


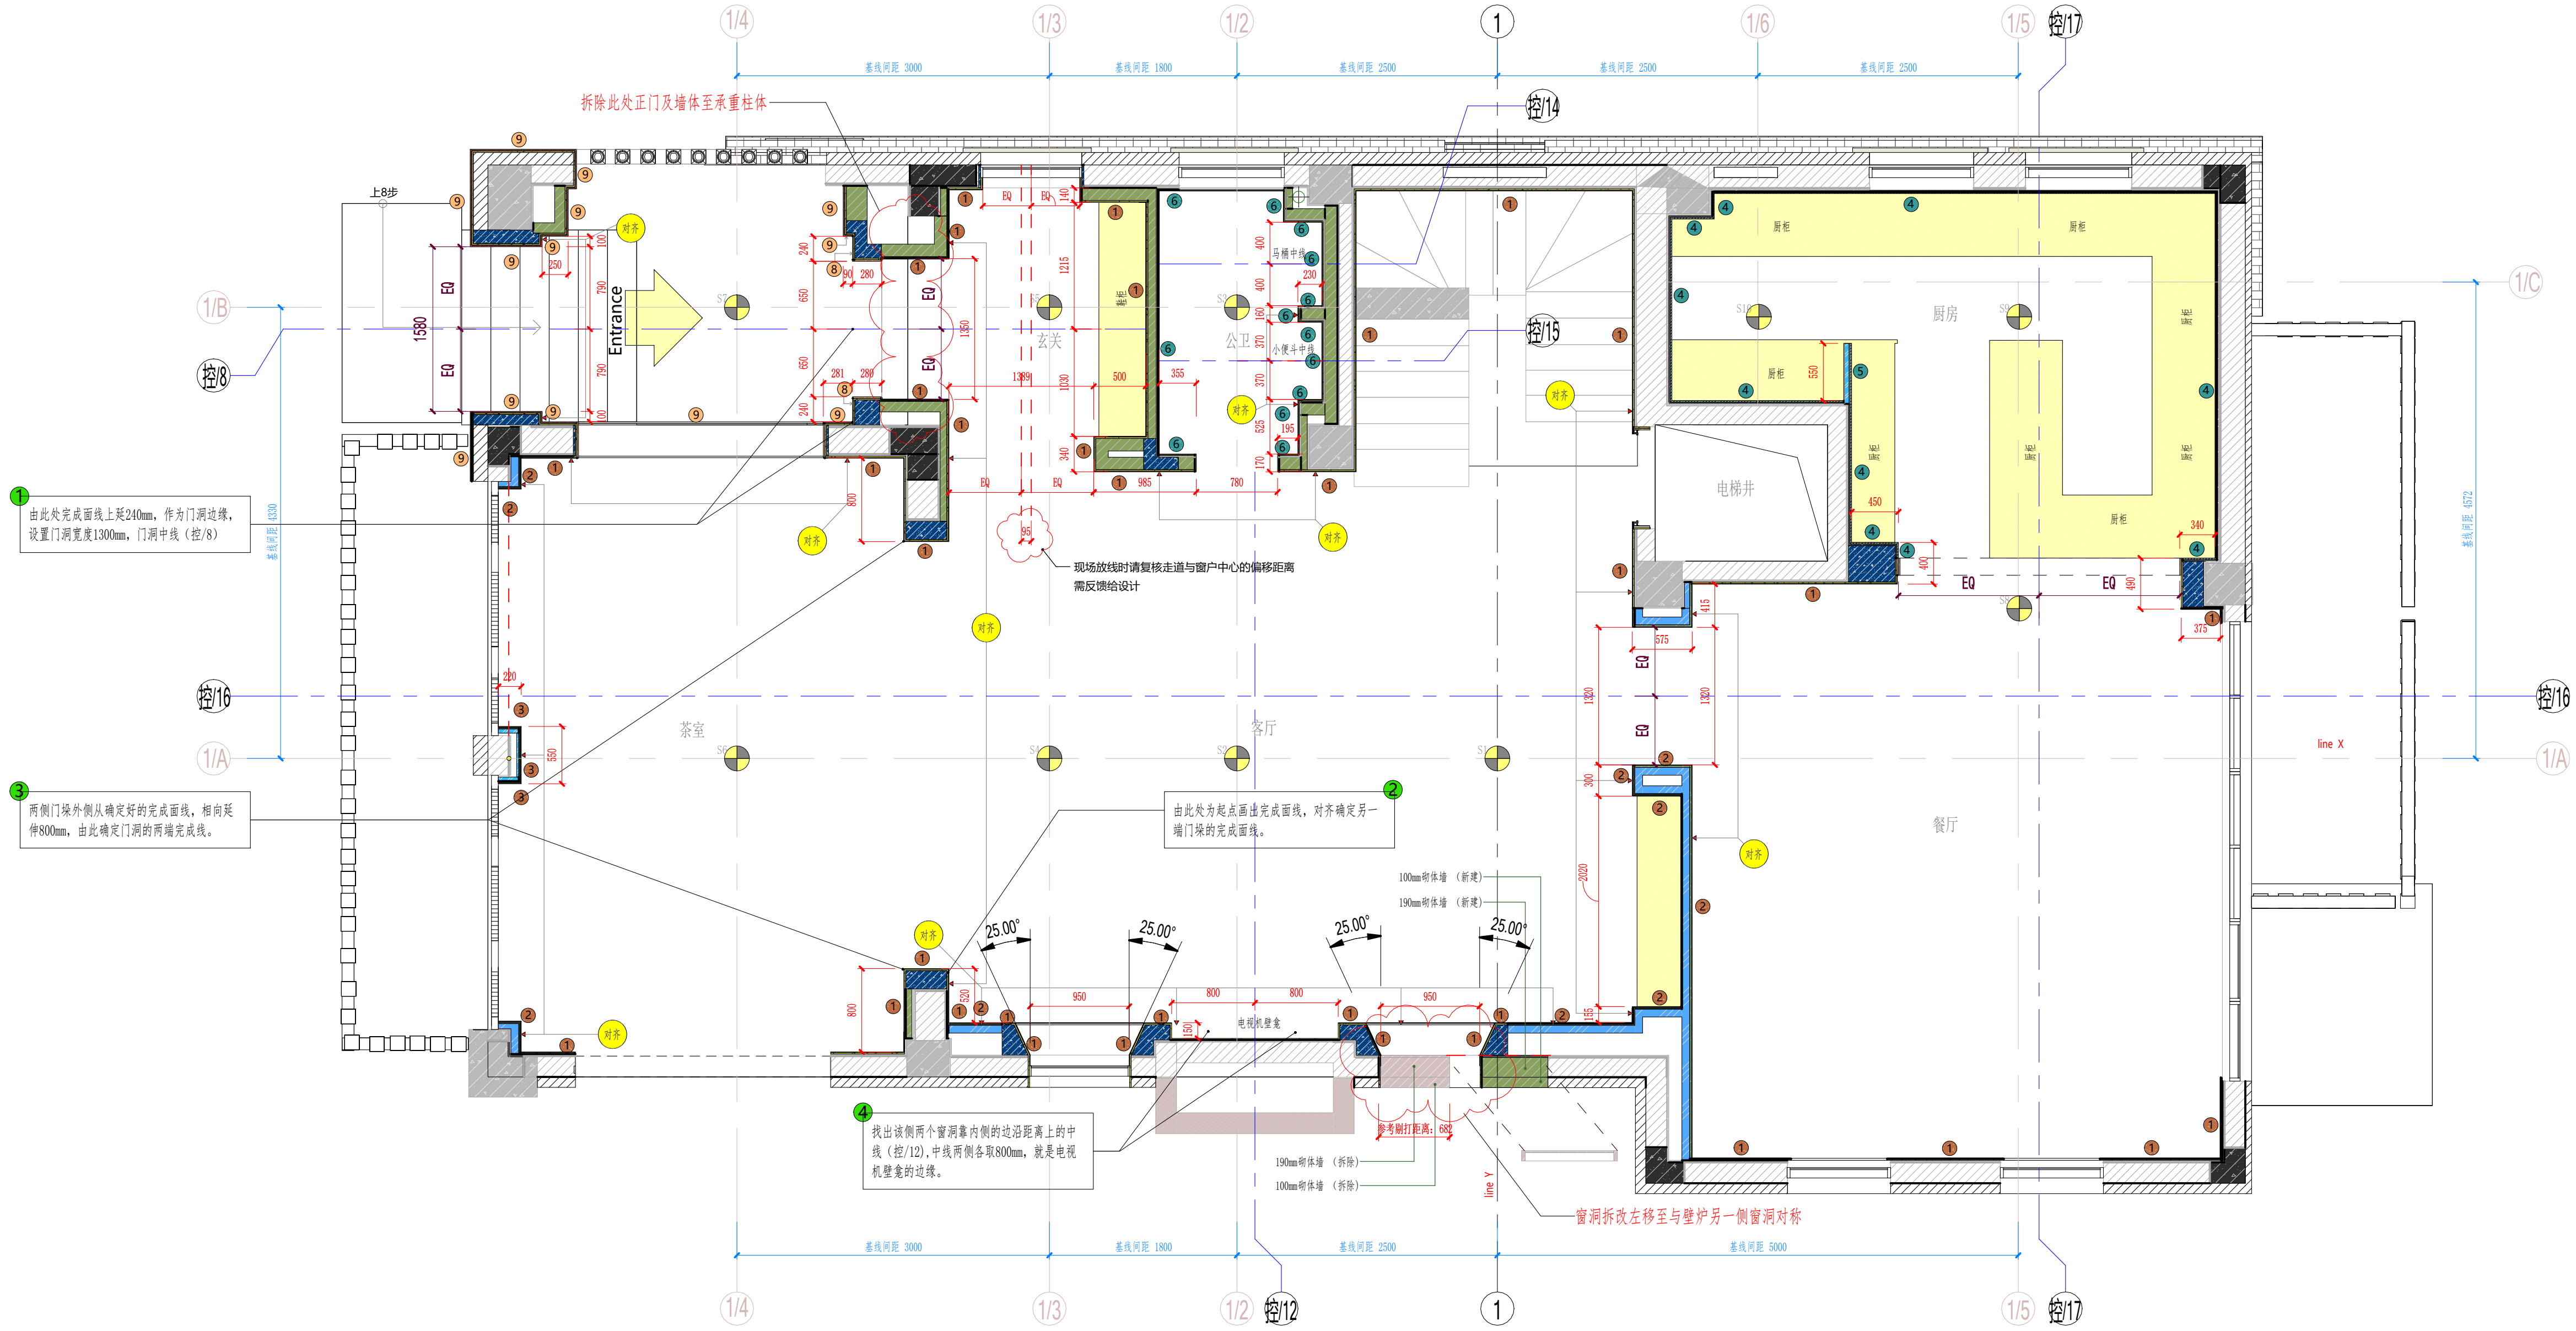




LEGEND - 完成面材质			注: 材质编号仅供参考使用					
编号	图例示意	完成面材质	编号	图例示意	完成面材质	编号	图例示意	完成面材质
①		涂料	⑤		人造石	⑧		外墙: 涂料 (控毛工艺)
②		涂料	⑥		涂料+人造石	⑨		

放线步骤说明:
步骤一: 参照完成面墙体图例中的外延厚度将原始墙体的完成面线弹出;
步骤二: 按照带边框的文字说明将相关控制线及找平线依照文字序号顺序放出;
步骤三: 依照图中每个区域的控制线将与其相关联的墙体完成面线分区放出;
步骤四: 将图纸标注的绿色复尺尺寸、控制线偏离基准线的距离复测并填入相关括号中, 拍照反馈BIM团队。

一号轴线为三层楼贯通轴线

放线步骤说明:

- 步骤一: 参照完成面墙体图例中的外延厚度将原始墙体的完成面线弹出;
- 步骤二: 按照带边框的文字说明将相关控制线及找平线按照文字序号顺序放出;
- 步骤三: 依照图中每个区域的控制线将与其相关联的墙体完成面线分区线放出;
- 步骤四: 将图纸标注的绿色复尺尺寸、控制线偏离基准线的距离复测并填入相关括号中, 拍照反馈 BIM 团队。

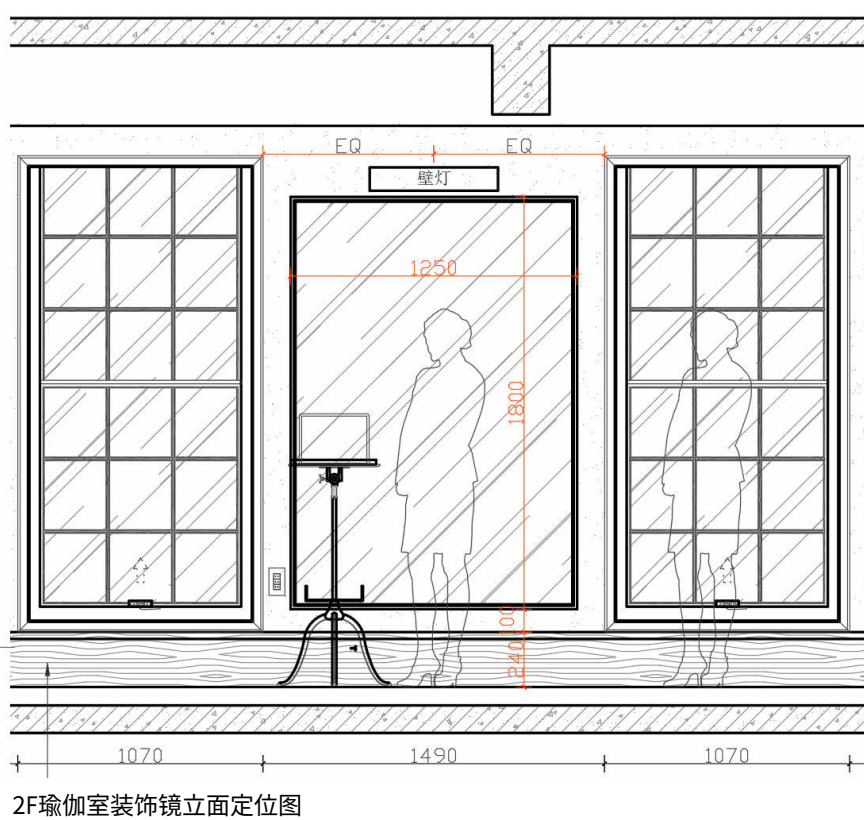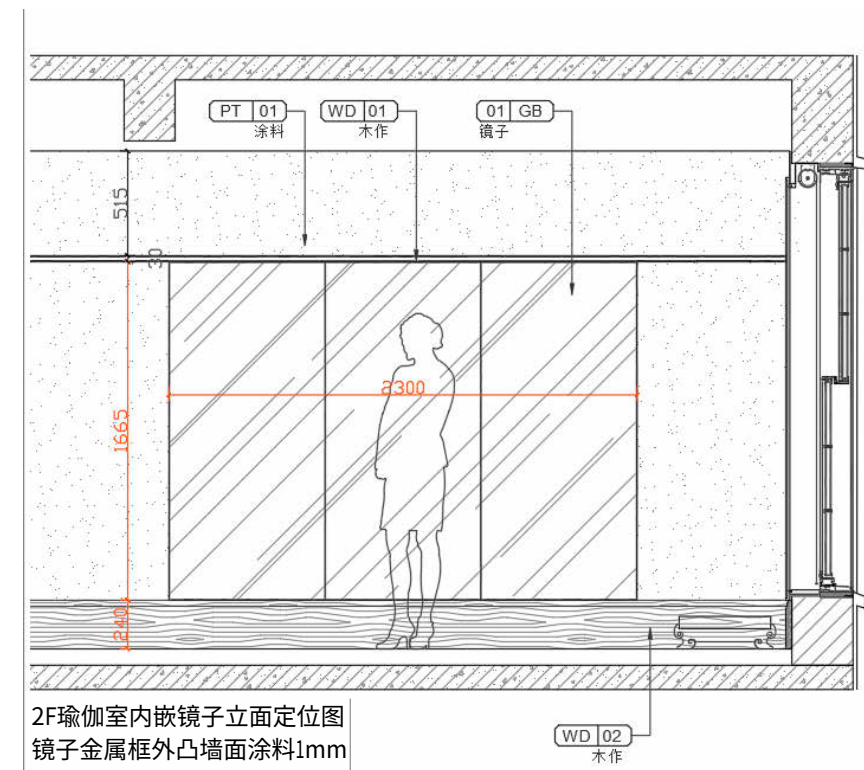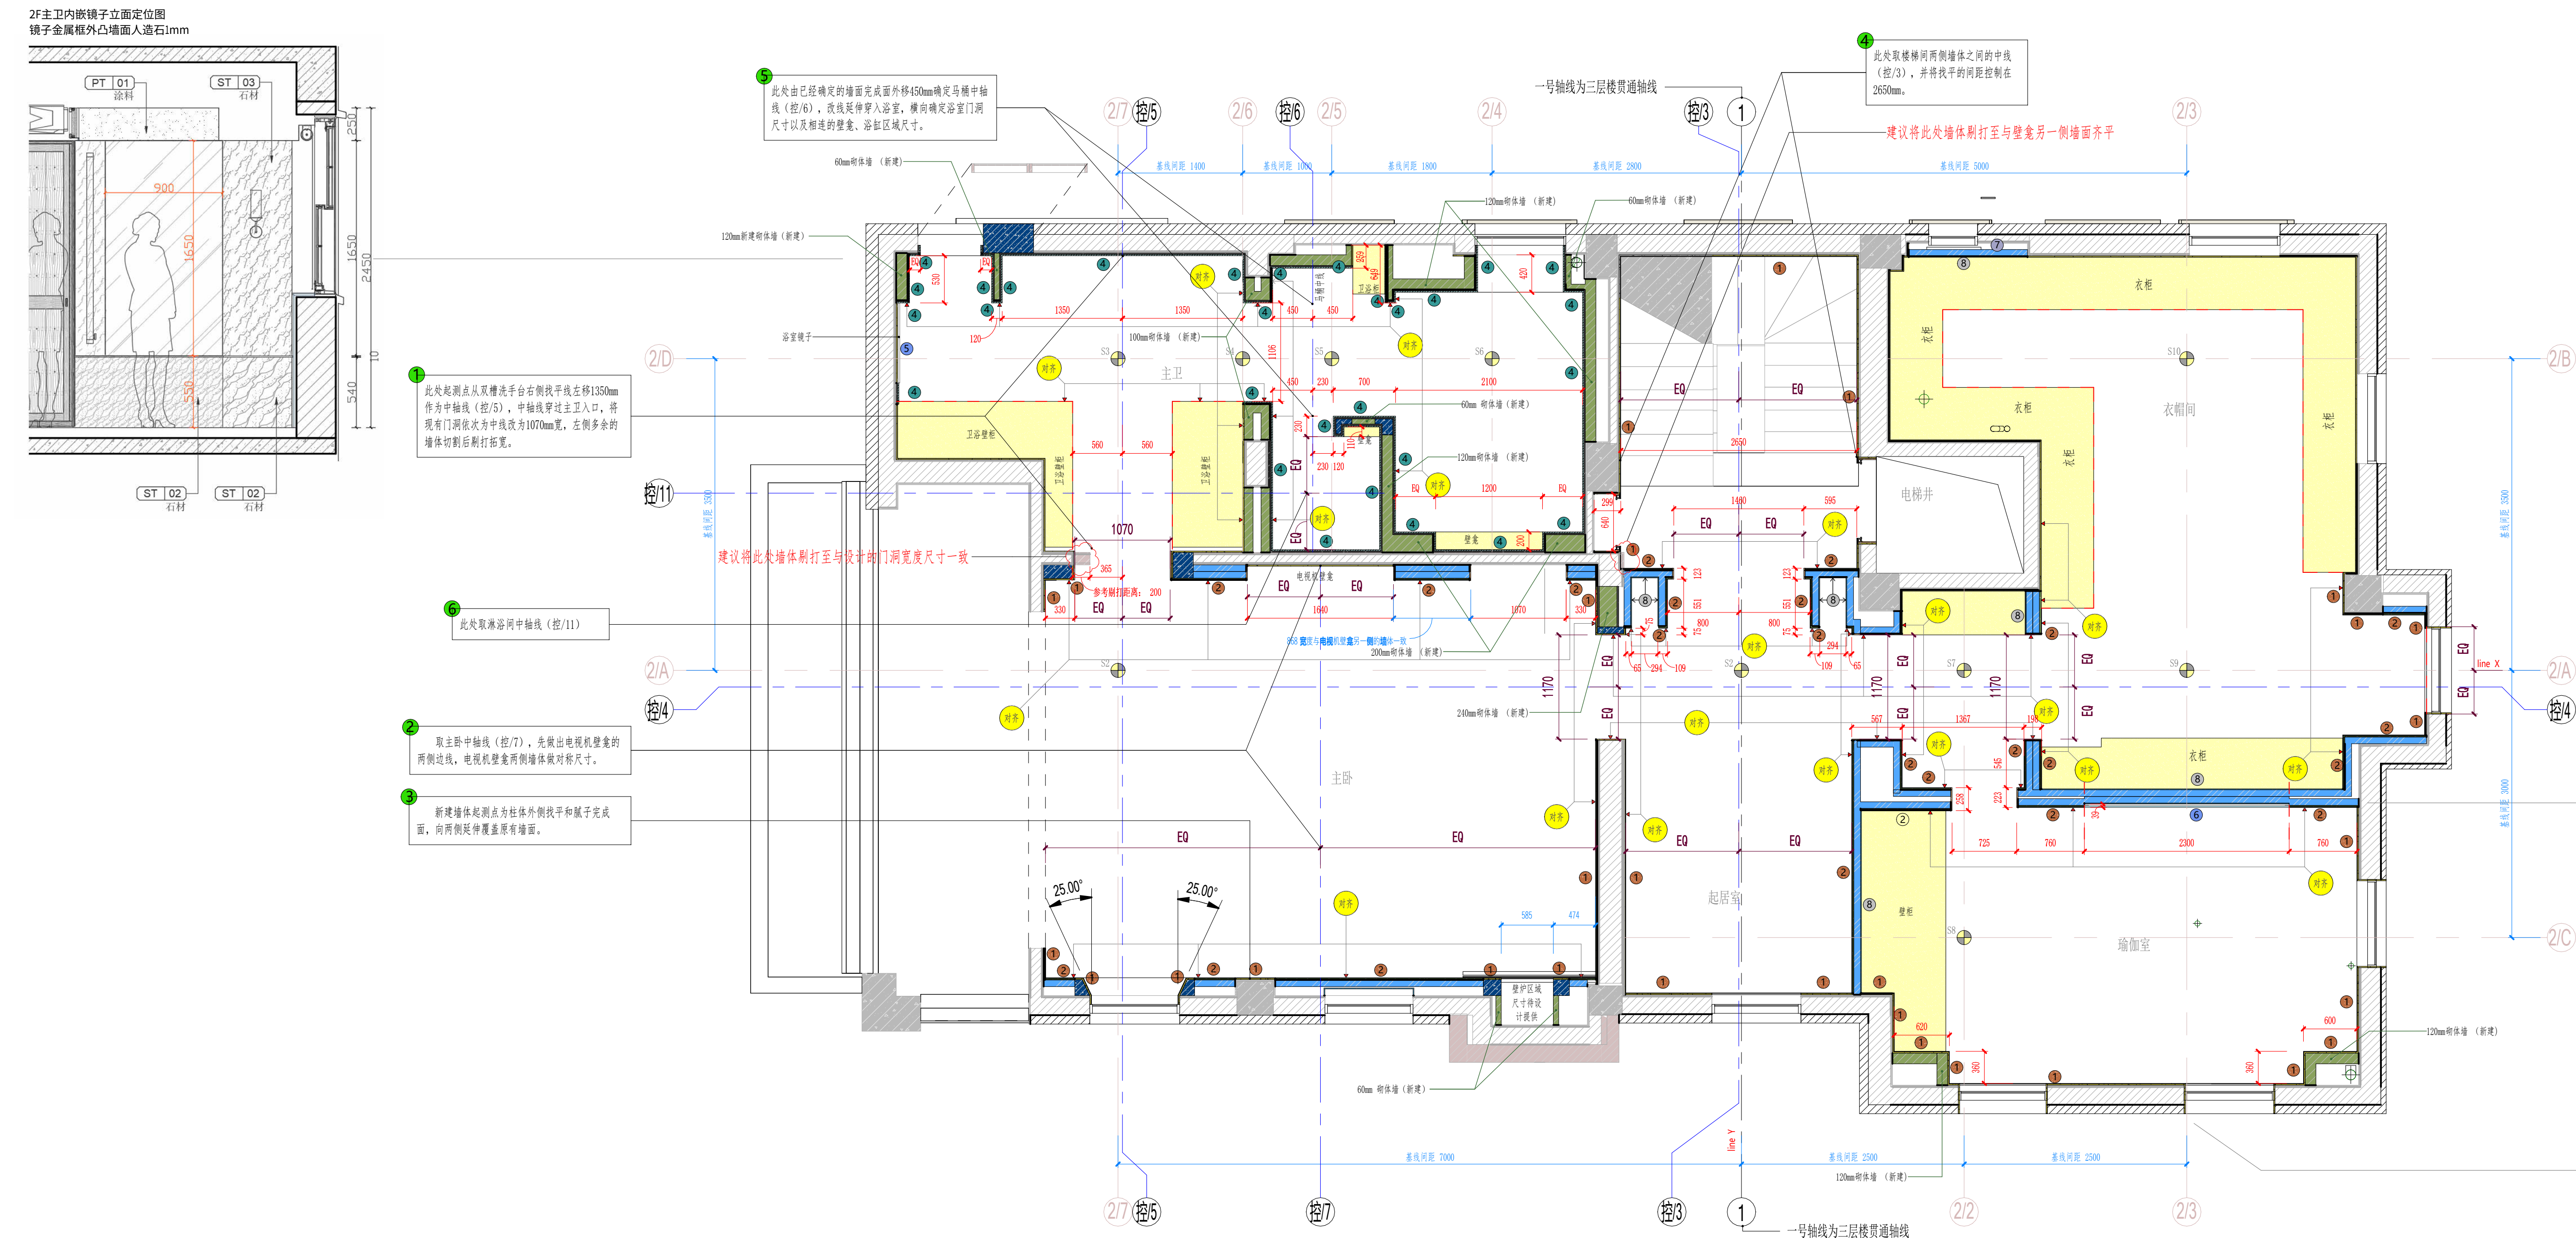

图例


LEGEND - 完成面材质

注：材质编号仅供3F使用

编号	图例示意	完成面材质	编号	图例示意	完成面材质
①		涂料	⑥		人造石
②		涂料	⑦		墙布
③		涂料	⑧		白色免漆板
④		木饰面	⑨		金属板
⑤		人造石			

放线步骤说明:

- 步骤一: 参照完成面墙体图例中的外延厚度将原始墙体的完成面线弹出;
- 步骤二: 按照带边框的文字说明将相关控制线及找平线依照文字序号顺序放出;
- 步骤三: 依照图中每个区域的控制线将与其相关联的墙体完成面线分区域放出;
- 步骤四: 将图纸标注的绿色复尺尺寸、控制线偏离基准线的距离复测并填入相关括号中, 拍照反馈BIM团队。

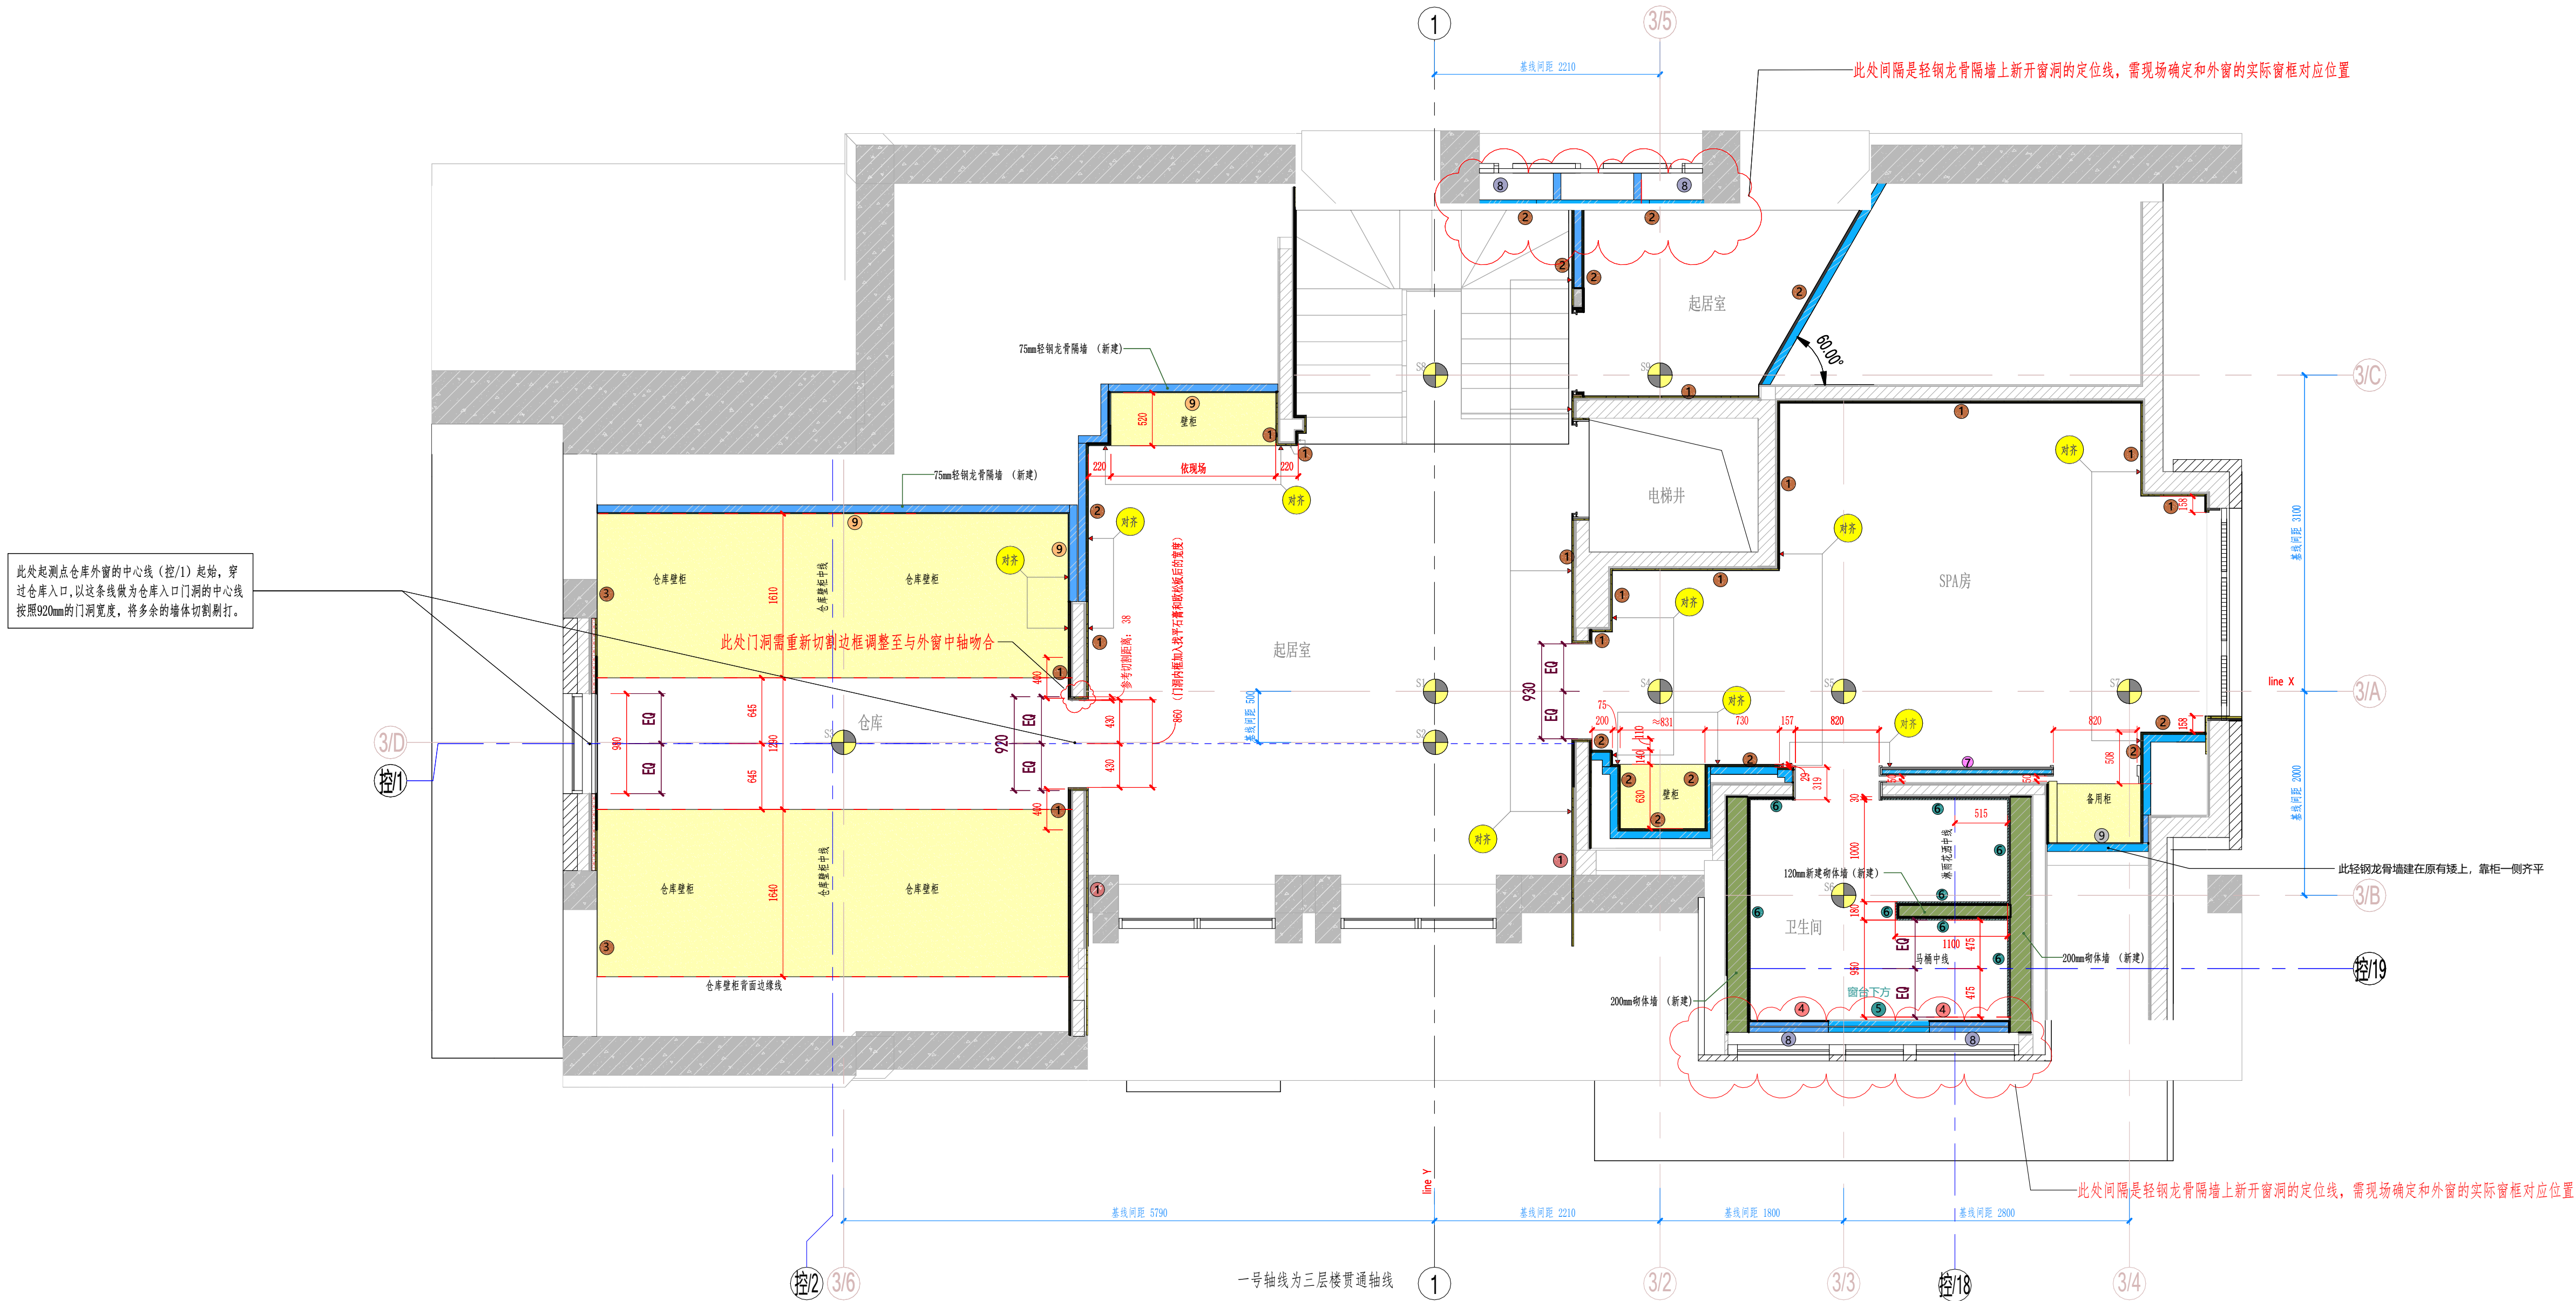图纸编号
Drawing No.

3F.PL-02

图纸名称
Drawing Name.

3F墙面完成面放线平面图

比例
Scale

1:40@A2

项目
Project

巨鹿路880号

项目编号
Project No.

2026

注释
Notes

- 1.本图纸如与现场尺寸有误差, 请施工人员与项目负责人联系。
- 2.施工前施工人员应认真查阅此图, 如有不明尺寸, 按现场测量为准。
- 3.本图纸必须经甲乙双方认可并签字方可作为施工依据。

日期
Date

2026/07/29

修订
Revision

1

盖章:

正式施工图
2026-07-30