


LEGEND 图例A 完成面说明

类别	编号	图例示意图
PT 肌理漆完成面	①	肌理漆 归方找平层 基层
	②	方型 龙骨板 肌理漆完成面
	③	肌理漆 归方找平层 基层
WD 木饰面完成面	④	基层墙体 归方找平层 5mm金属挂件 木饰面
	⑤	20~40mm龙骨 12mm金属挂件 5mm金属挂件 木饰面
	⑥	基层墙体 归方找平层 木饰面
ST 石材完成面	⑦	基层墙体 归方找平层 石材完成面
	⑧	基层墙体 归方找平层 石材完成面
	⑨	归方找平层 防水砂浆 轻骨料FC-A-01 石材完成面 轻骨料FC-A-01 轻骨料FC-A-01 轻骨料FC-A-01
	⑩	归方找平层 防水砂浆 轻骨料FC-A-04 石材完成面 轻骨料FC-A-04 轻骨料FC-A-04 轻骨料FC-A-04
	⑪	基层墙体 归方找平层 石材完成面
CT 瓷砖完成面	⑫	基层墙体 归方找平层 瓷砖完成面
MT 金属完成面	⑬	基层墙体 归方找平层 15mm金属挂件 金属完成面
GL 镜子/玻璃完成面	⑭	基层墙体 归方找平层 15mm金属挂件 镜子/玻璃完成面
WP 墙纸完成面	⑮	基层墙体 归方找平层 墙纸
	⑯	方型 龙骨板 墙纸
	⑰	归方找平层 防水砂浆 轻骨料FC-A-04 墙纸完成面 轻骨料FC-A-04 轻骨料FC-A-04 轻骨料FC-A-04
	⑱	归方找平层 防水砂浆 轻骨料FC-A-01 墙纸完成面 轻骨料FC-A-01 轻骨料FC-A-01 轻骨料FC-A-01
	⑲	基层墙体 归方找平层 墙纸
	⑳	基层墙体 归方找平层 墙纸
归方找平	㉑	基层墙体 归方找平层

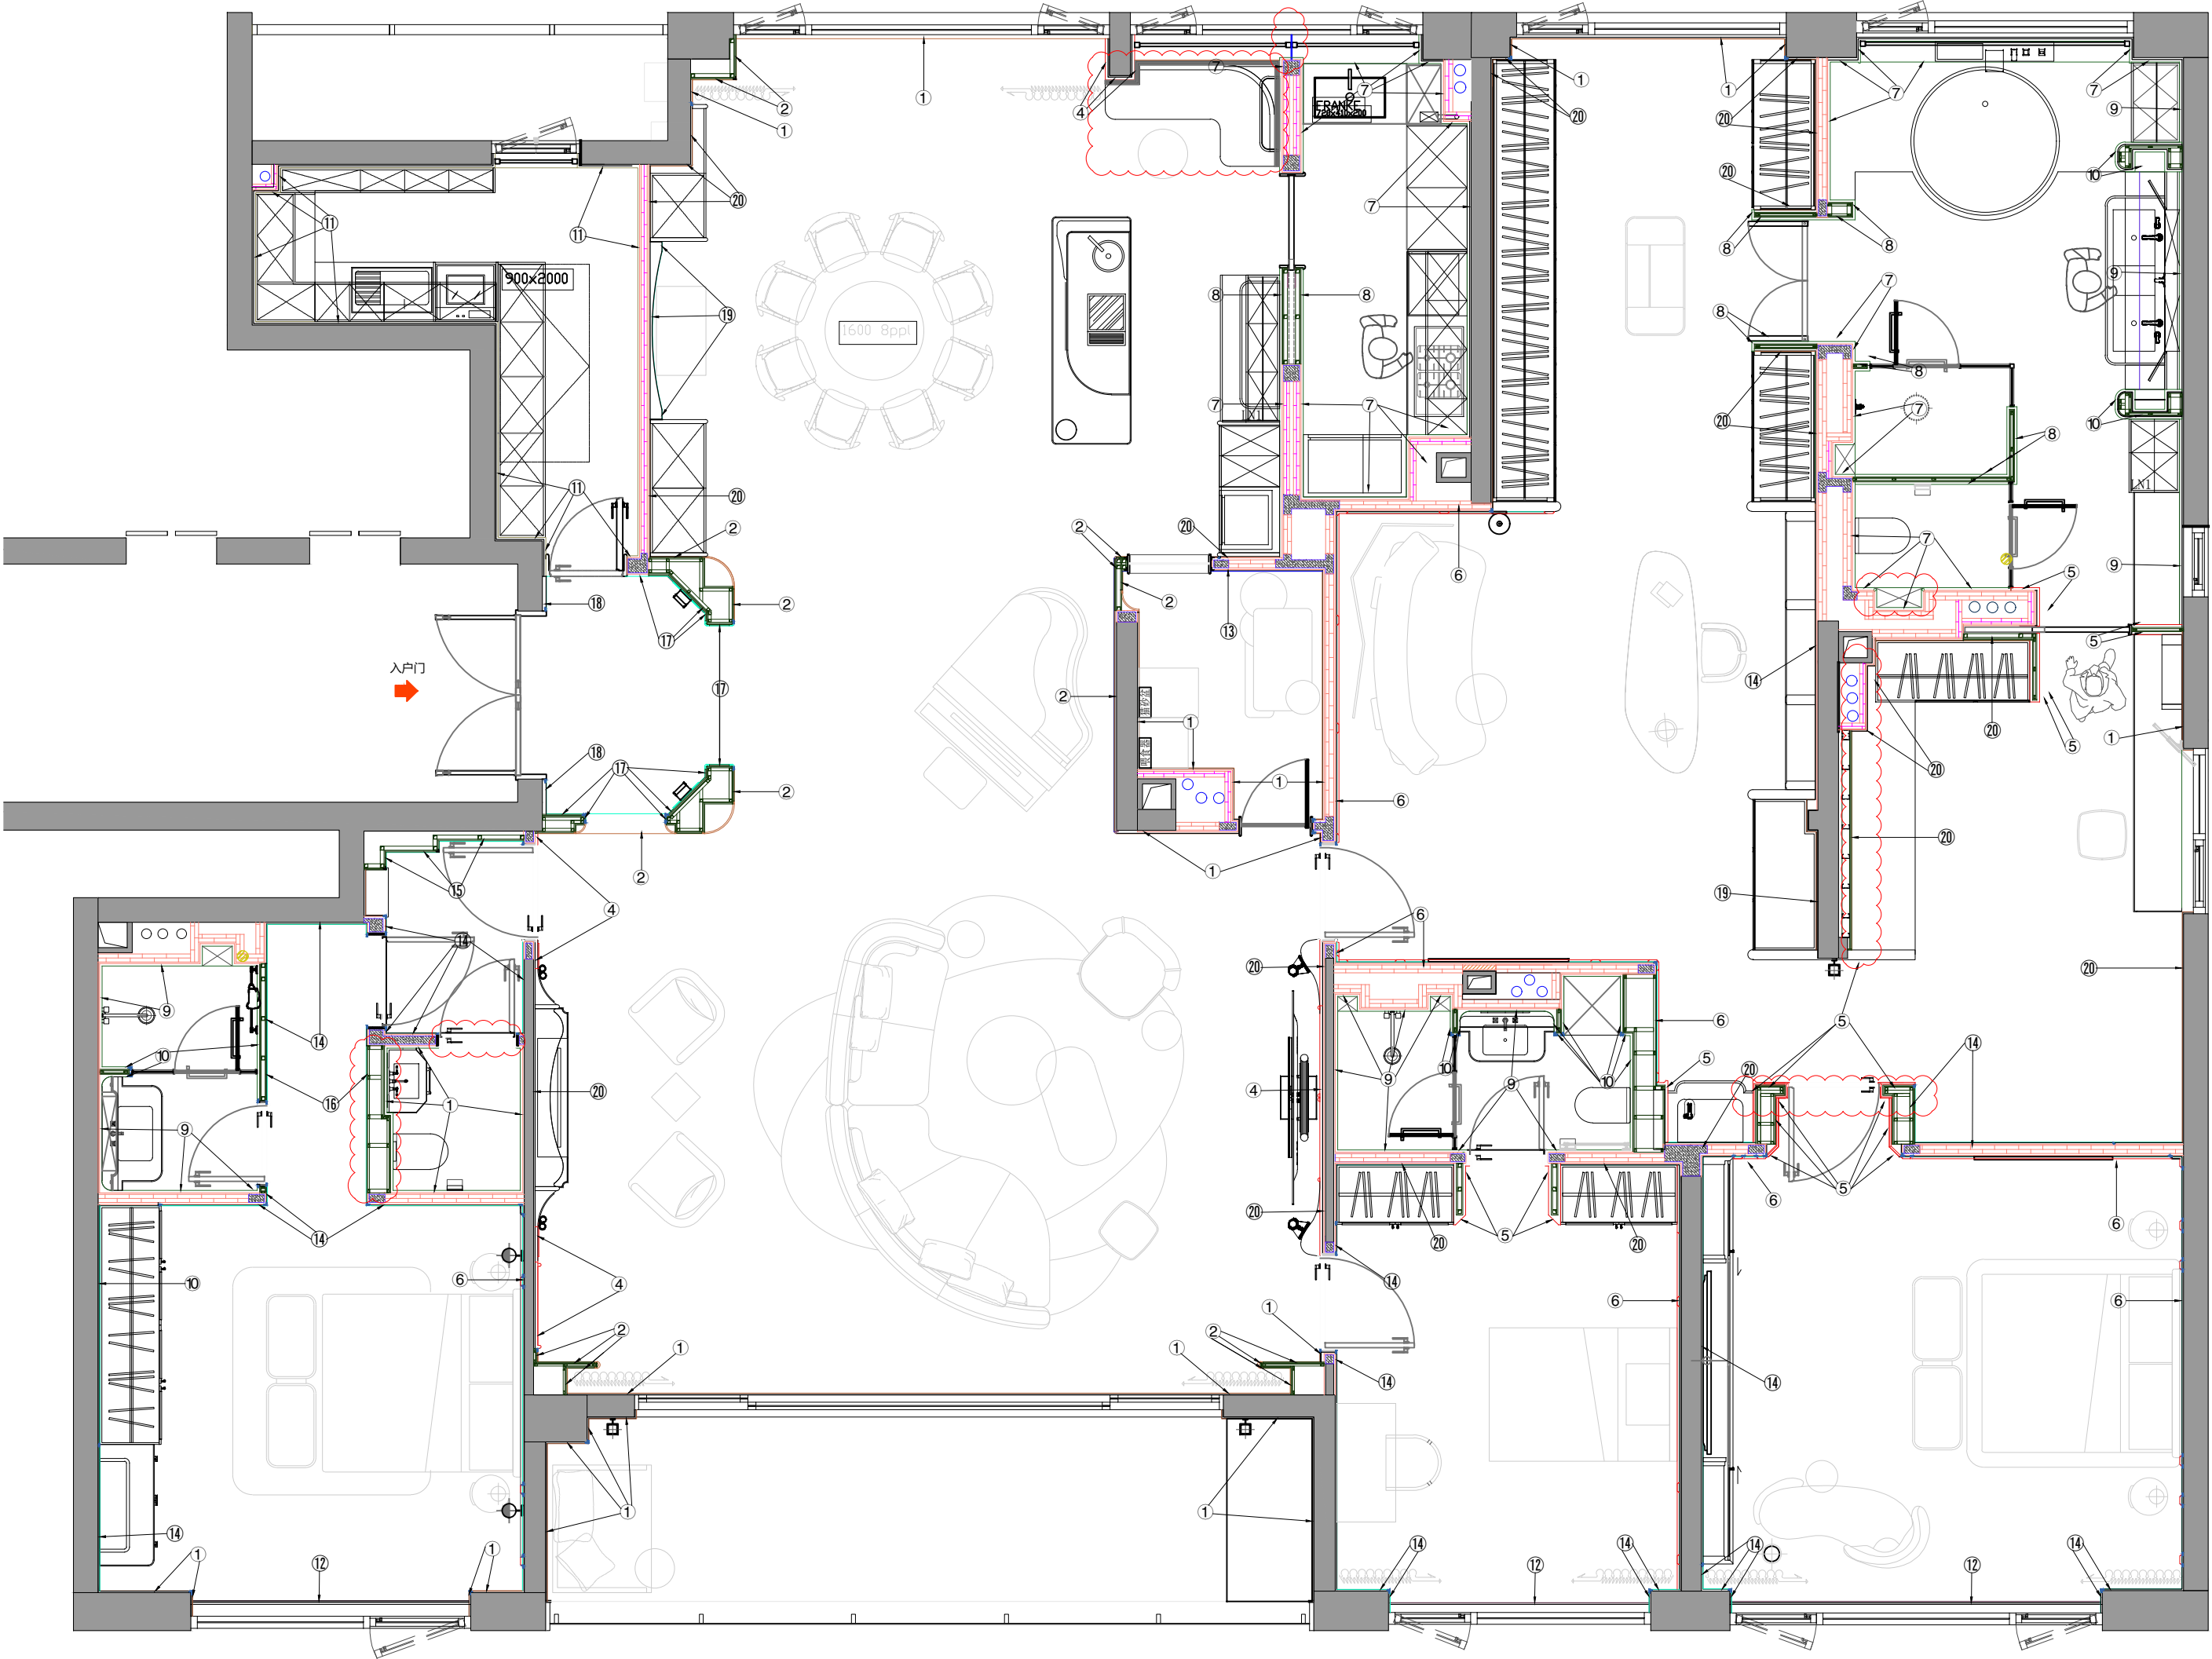

西南244°



ELIBORN

图例	材质名称 (墙体完成面)
—	肌理漆
—	木饰面
—	石材
—	瓷砖
—	金属
—	镜子/玻璃
—	墙纸
—	归方找平

日期
Date 2026.01.25

修订
Revisions



项目
Project

华岸府

Scale 1:60 @A2

墙面完成面分析平面图

Drawing No.
图纸编号

PL-02.1

Project No.
项目编号

© 2026


墙面完成面分析平面图

Scale比例 1:60@A2

注释
Notes

1. 本图纸尺寸如与现场尺寸有误差，请施工方与项目负责人联系。
2. 施工前施工方人员应认真查阅此图，如有不明尺寸，按现场测量为准。
3. 本图纸必须经甲乙双方认可并签字方可作为施工依据。

PL-02.1

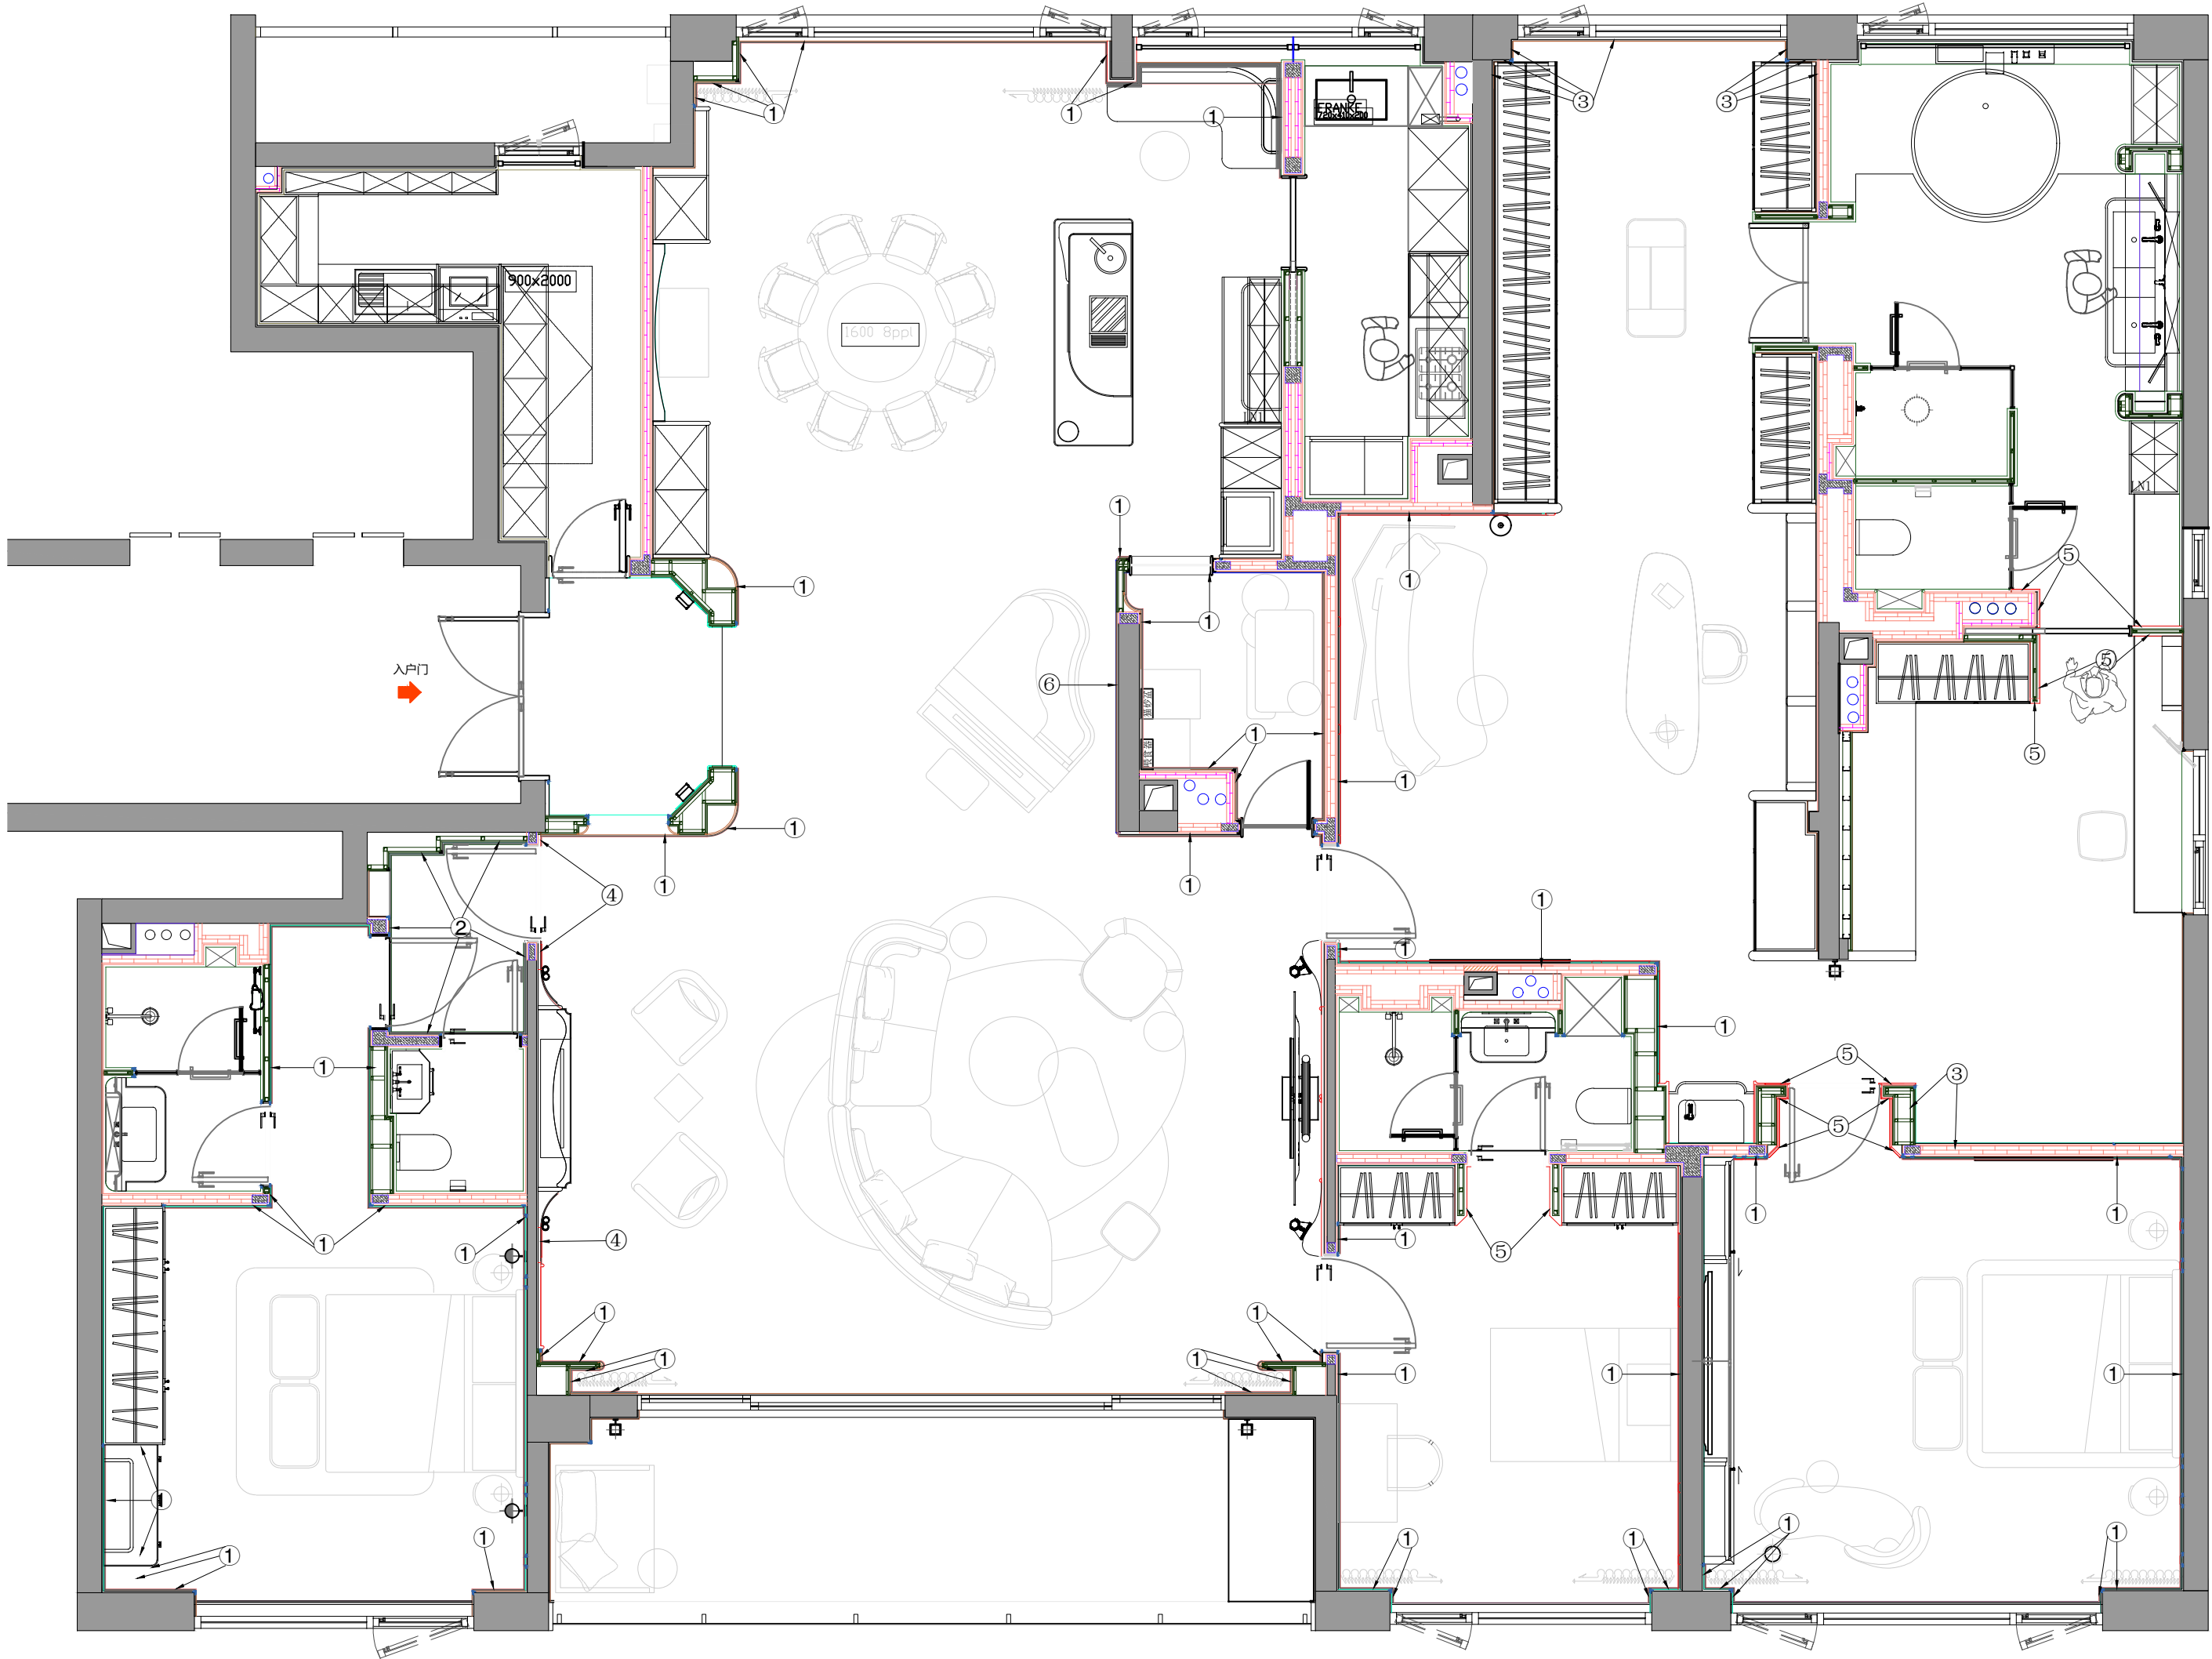

编号	图例示意	说明
①		踢脚白色哑光烤漆完成面 铝型材 YFC-A-01 白色哑光烤漆完成面
②		踢脚白色哑光烤漆完成面 铝型材 YFC-A-01 石材完成面
③		踢脚 不锈钢完成面 铝型材 YFC-A-01 不锈钢完成面
④		踢脚白色哑光烤漆完成面 白色哑光烤漆完成面
⑤		踢脚白色哑光烤漆完成面 白色哑光烤漆完成面
⑥		踢脚 镜面 铝型材 YFC-A-01 镜面完成面

日期
Date 2026.01.07

修订
Revisions

项目
Project

杭州华岸府

Scale 比例 1:60 @A2

踢脚线分析平面图

Drawing No.
图纸编号
PL-1.02

Project No.
项目编号
© 2025


踢脚线分析平面图

注释
Notes
1. 本图纸尺寸如与现场尺寸有误, 请施工人员与项目负责人联系。
2. 施工前施工人员应认真查阅此图, 如有不明确尺寸, 按现场测量为准。
3. 本图纸必须经甲乙双方认可并签字方可作为施工依据。

Scale比例 1:60@A2

LEGEND 图例A

编 号	图 例	名称
1	必要尺寸	必要尺寸
2	(依现场尺寸)	剩余的现场尺寸
3	墙体完成面厚度	墙体完成面厚度
4	* 现场核查	待现场核实的尺寸

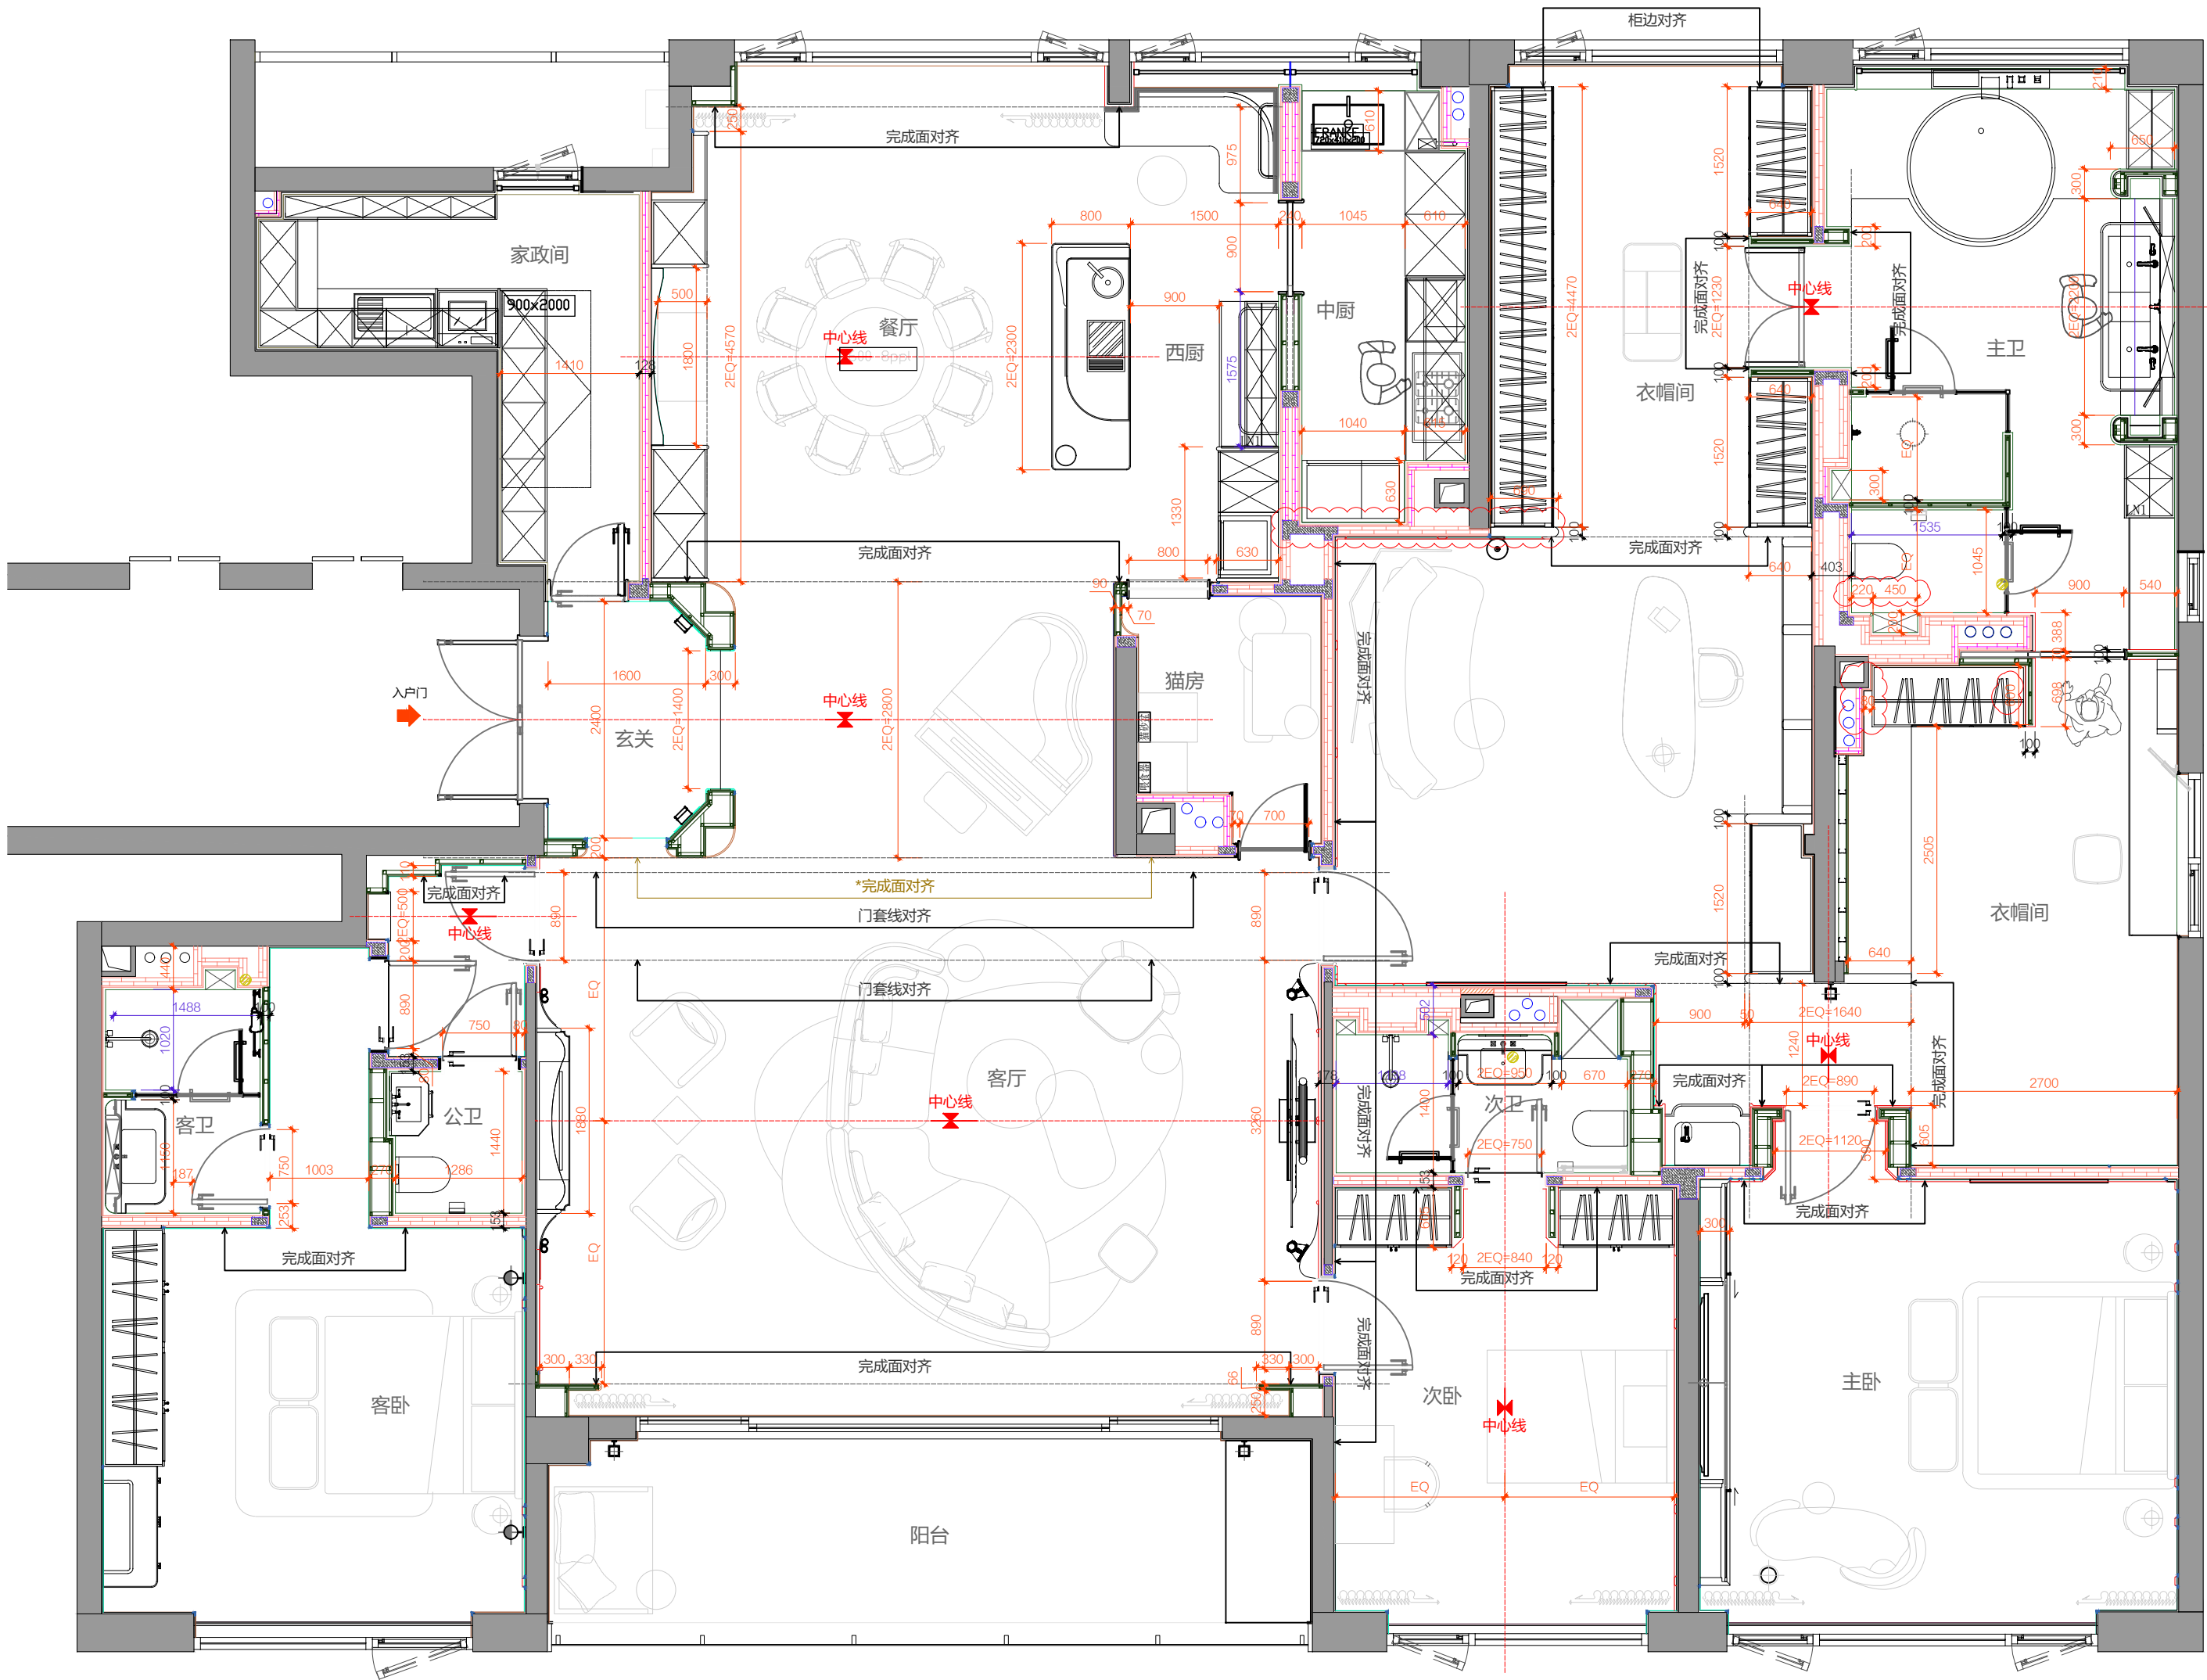

西南244°



ELIBORN

图 例	材质名称 (墙体完成面)
	艺术漆
	墙纸
	大理石
	瓷砖
	木饰面
	银镜
	不锈钢

日期
Date 2026.01.25

修订
Revisions



项目
Project

华岸府

Scale 1:60 @A2

墙面完成面放线平面图

Drawing No.
图纸编号

PL-02.2

Project No.
项目编号 © 2026

墙面完成面放线平面图

注释
Notes

1. 本图纸尺寸如与现场尺寸有误，请施工人员与项目负责人联系。
2. 施工前施工人员应认真查阅此图，如有不明确尺寸，按现场测量为准。
3. 本图纸必须经甲乙双方认可并签字方可作为施工依据。

Scale比例 1:60@A2

PL-02.2

基准线放线步骤说明：
步骤一,找到图上标注的基准线lineX的起点——起始点1 startpoint1（以入户门洞的中心点为起始点），使用激光水平仪打出起始于该点并垂直于门洞所在墙的激光线；

步骤二：在激光线的照射终点endpoint复核一下图上标注的终点复尺尺寸，并把实际复尺距离标在括号内；

步骤三：找到图上标注的基准线lineY的终点——LineY照射点 endpoint2（以指定窗洞中心点定位），使用激光水平仪从LineX上打出垂直于LineX并照射在LineY照射点endpoint2上；

步骤四：参照图纸上的基准点符号、基准线间距及其顺序符号（S1、S2、S3.....Sn），使用激光水平仪依次打出所有基线的激光线；

步骤五：参照现场打出的激光线，使用放线墨斗在天花板打出所有基准线的墨线，并在所有基准点喷涂基准符号。



图 例	材质名称 (墙体完成面)
---	基准线
●	基准线交汇点

日期
Date 2026.01.25

修订
Revisions

项目
Project

华岸府

Scale 1:60 @A2
比例

空间基准线定位平面图

Drawing No.
图纸编号
NW.PL-02.1

Project No.
项目编号
© 2026

空间基准线定位平面图

Scale比例 1:60@A2

注释
Notes
1. 本图纸尺寸如与现场尺寸有误，请施工人员与项目负责人联系。
2. 施工前施工人员应认真查阅此图，如有不明确尺寸，按现场测量为准。
3. 本图纸必须经甲乙双方认可并签字方可作为施工依据。



ELIBORN

LEGEND 图例

编 号	图 例	名 称
1		80mmPC砖墙
2		60mmPC砖墙
3		结构柱
4		抹灰层 (≈15mm)
5		钢架墙

日期
Date 2026.01.25

修订
Revisions

项目
Project

华岸府

Scale
比例 1:60 @A2

新建墙体类型平面图

Drawing No.
图纸编号

NW.PL-01

Project No.
项目编号 © 2026


新建墙体类型平面图

注释
Notes
1. 本图纸尺寸如与现场尺寸有误, 请施工人员与项目负责人联系。
2. 施工前施工人员应认真查阅此图, 如有不明确尺寸, 按现场测量为准。
3. 本图纸必须经甲乙双方认可并签字方可作为施工依据。


Scale比例 1:60@A2

1


NW.PL-01

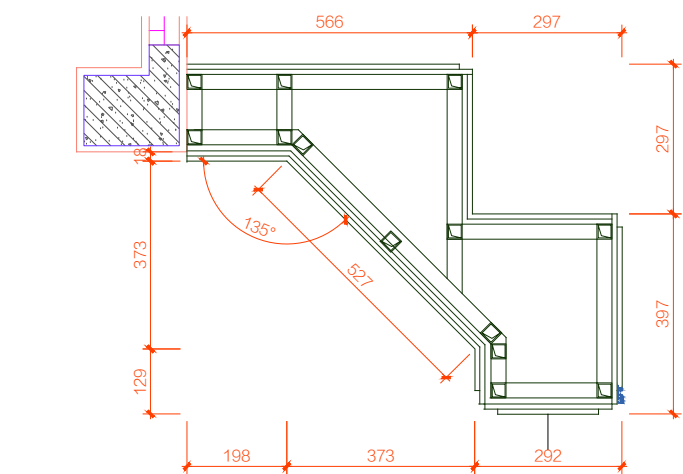


01
— 大样图 SCALE 1: 15

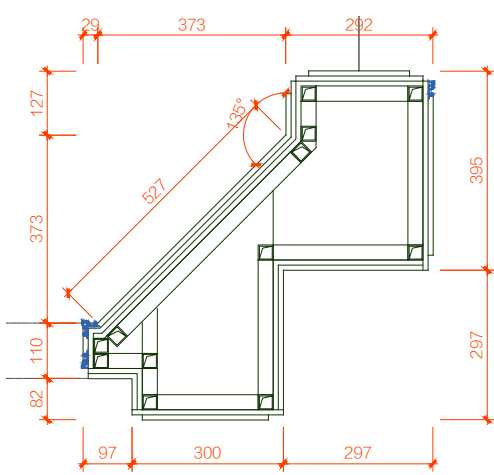

02
— 大样图 SCALE 1: 15

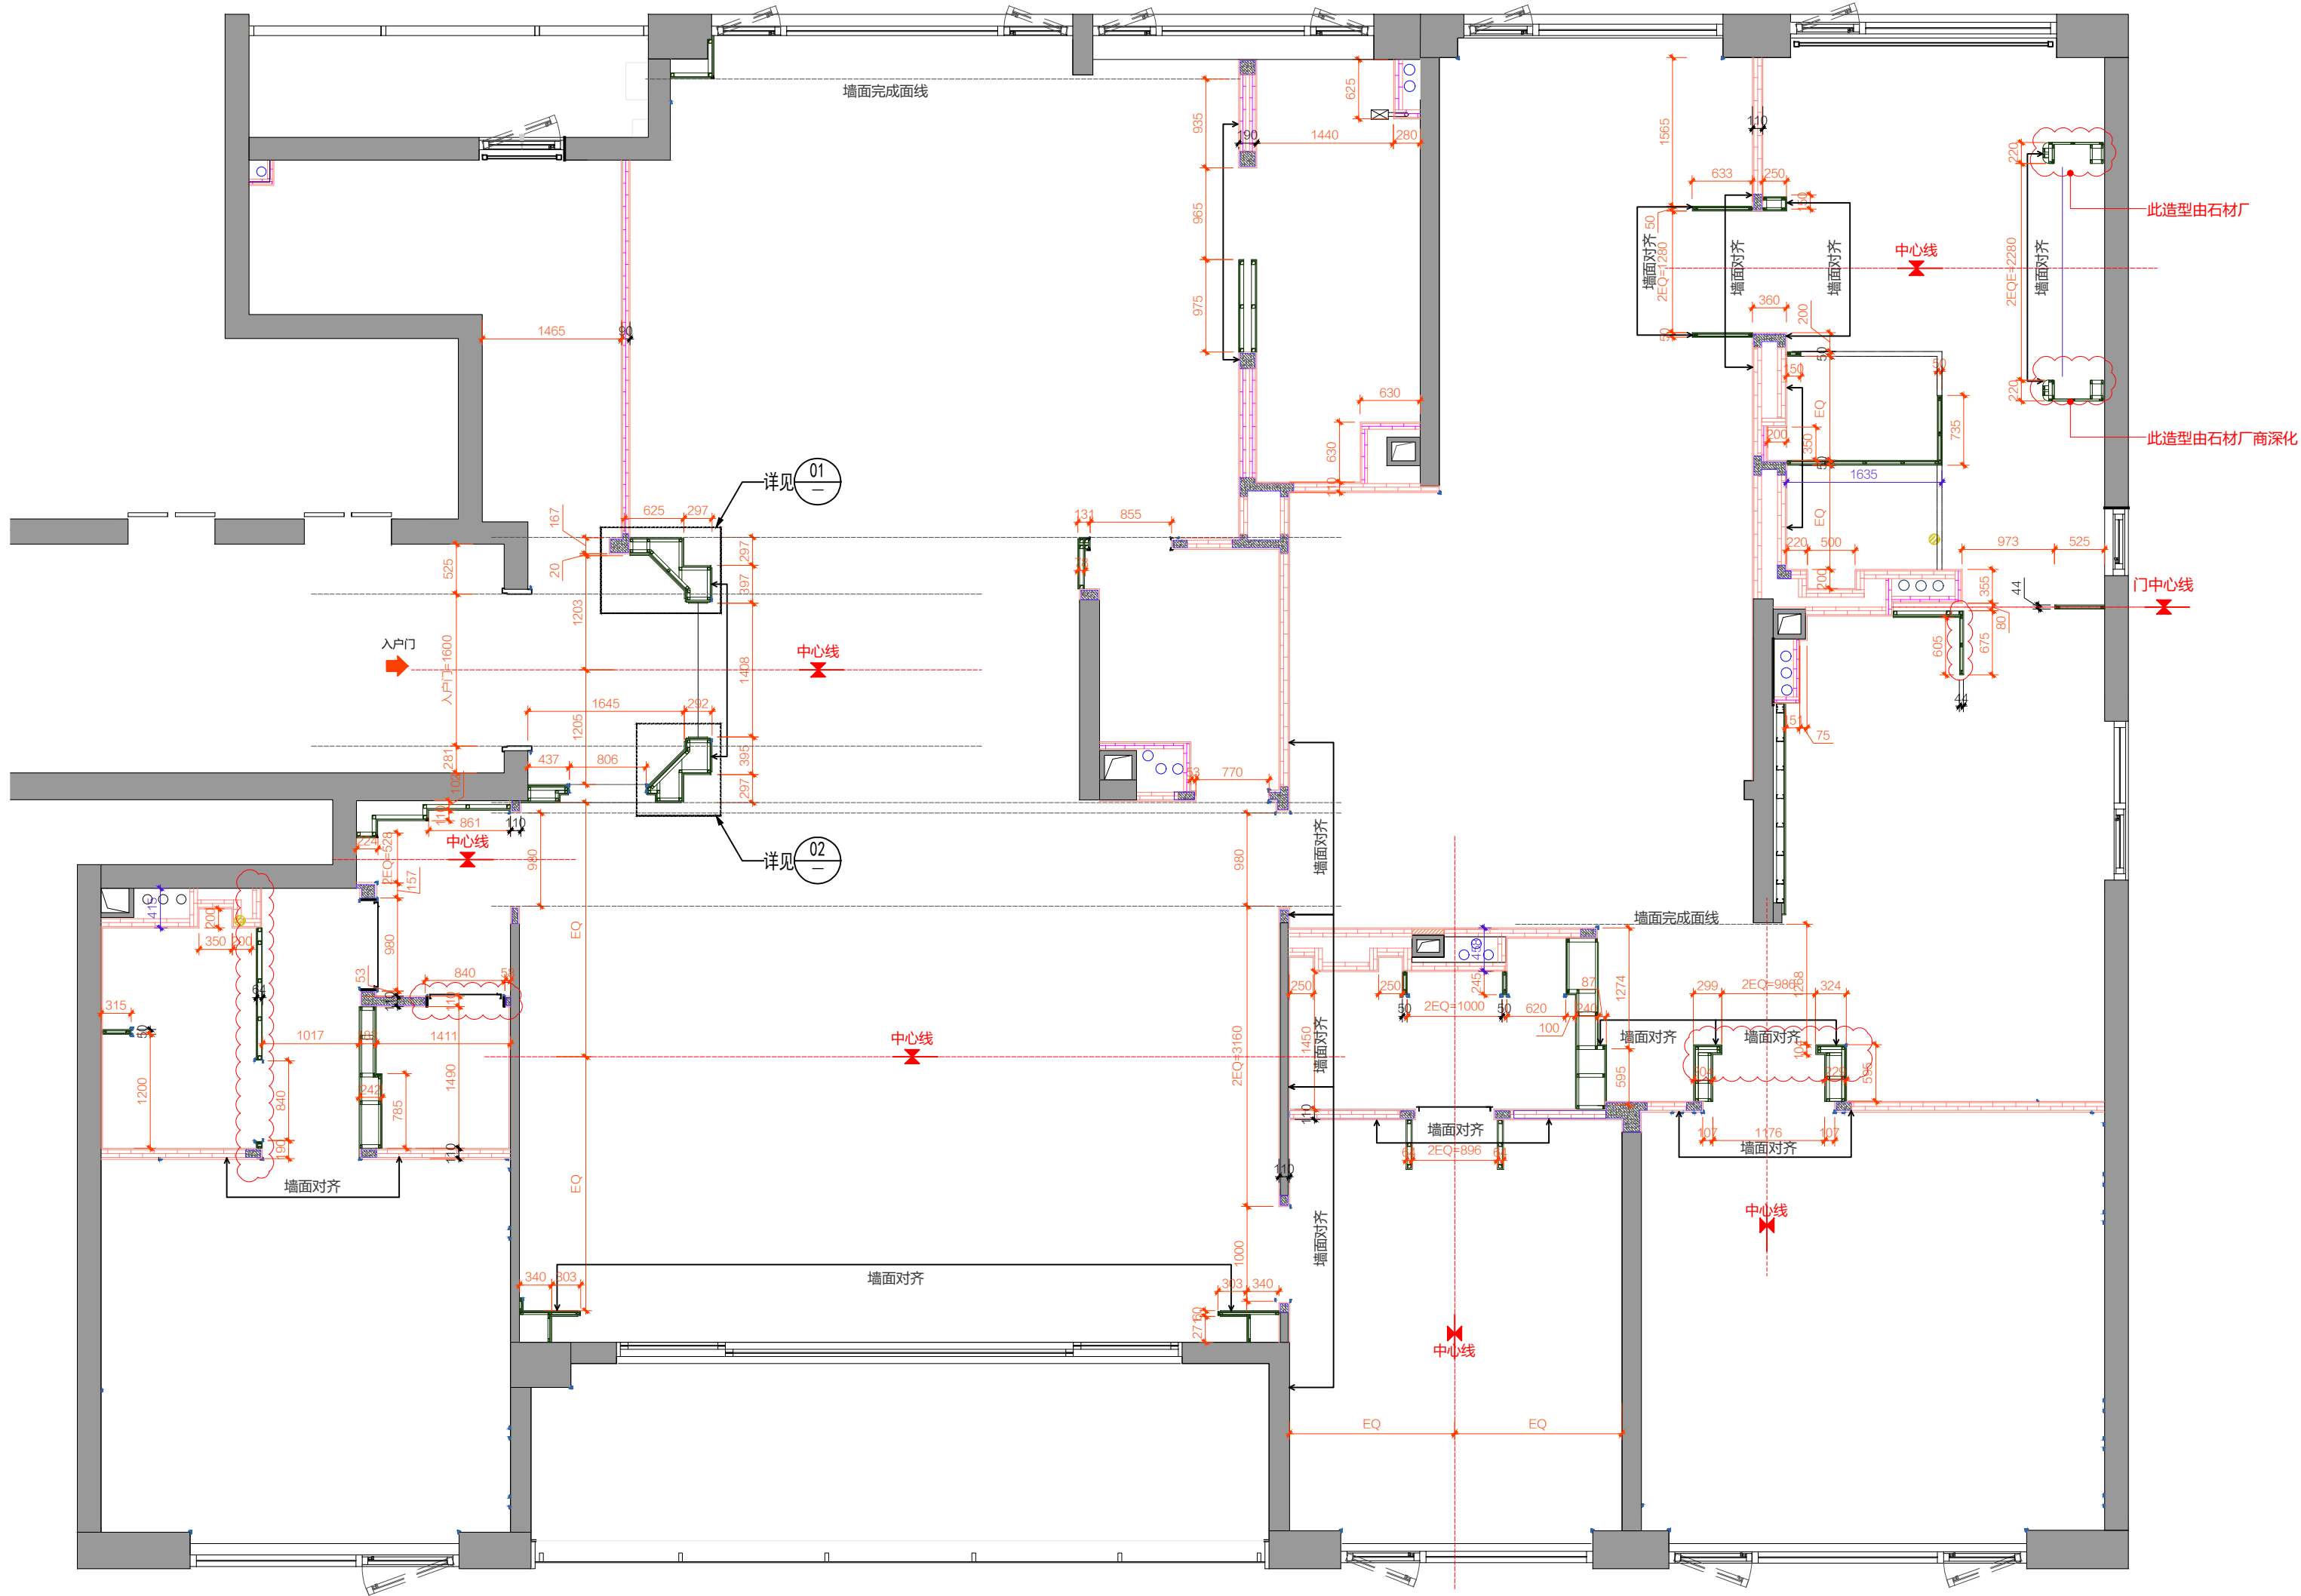

西南244°

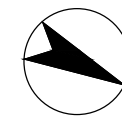

编 号	图 例	名称
1		必要尺寸
2		（依现场尺寸） 剩余的现场尺寸
3		墙体完成面厚度 墙体完成面厚度
4		* 现场核查 待现场核实的尺寸

日期
Date 2026.01.25

修订
Revisions

项目
Project

杭州华岸府

Scale 1:60 @A2
比例

新建墙体放线平面图

Drawing No.
图纸编号

NW.PL-02

Project No.
项目编号 © 2026

新建墙体放线平面图

注释
Notes
1. 本图纸尺寸如与现场尺寸有误，请施工人员与项目负责人联系。
2. 施工前施工人员应认真查阅此图，如有不明确尺寸，按现场测量为准。
3. 本图纸必须经甲乙双方认可并签字方可作为施工依据。

Scale比例 1:60@A2



LEGEND 图例

编 号	图 例	名称
1		原地面抬高
2		结构柱
3		混凝土导墙
4		混凝土导墙上加5mm钢板
5		混凝土止水坎
6		混凝土止水坎上加5mm钢板
7		不锈钢止水板

日期
Date 2026.01.25

修订
Revisions

项目
Project

华岸府

Scale
比例 1:60 @A2

混凝土导墙、止水坎平面图

Drawing No.
图纸编号

NW.PL-02

Project No.
项目编号 © 2026



ELIBORN

LEGEND 图例

编 号	图 例	名 称
1		原地面抬高
2		结构柱
3		混凝土导墙
4		混凝土导墙上加5mm钢板
5		混凝土止水坎
6		混凝土止水坎上加5mm钢板
7		不锈钢止水板

日期
Date 2026.01.25

修订
Revisions

项目
Project

华岸府

Scale
比例 1:60 @A2

混凝土导墙、止水坎平面图

Drawing No.
图纸编号
NW.PL-02

Project No.
项目编号 © 2026

混凝土导墙、止水坎平面图

注释
Notes
1. 本图纸尺寸如与现场尺寸有误，请施工人员与项目负责人联系。
2. 施工前施工人员应认真查阅此图，如有不明尺寸，按现场测量为准。
3. 本图纸必须经甲乙双方认可并签字方可作为施工依据。

Scale比例 1:60@A2

1

PL-1.01