

编号	图例	说明
1		原始墙、板、柱
2		混凝土导墙
3		过梁
4		构造柱
5		钢筋

正式施工图
2026-08-06

- 1.本图纸如与现场尺寸有误，请施工人员与项目负责人联系。
- 2.施工前施工人员应认真查阅此图，如有不明确尺寸，按现场测量为准。
- 3.本图纸必须经甲乙双方认可并签字方可作为施工依据。


修订
Revision



比例 1:40@A2
Scale

图纸编号
Drawing No.

1F.NW.PL-01
 项目编号 © 2026
 Project No.

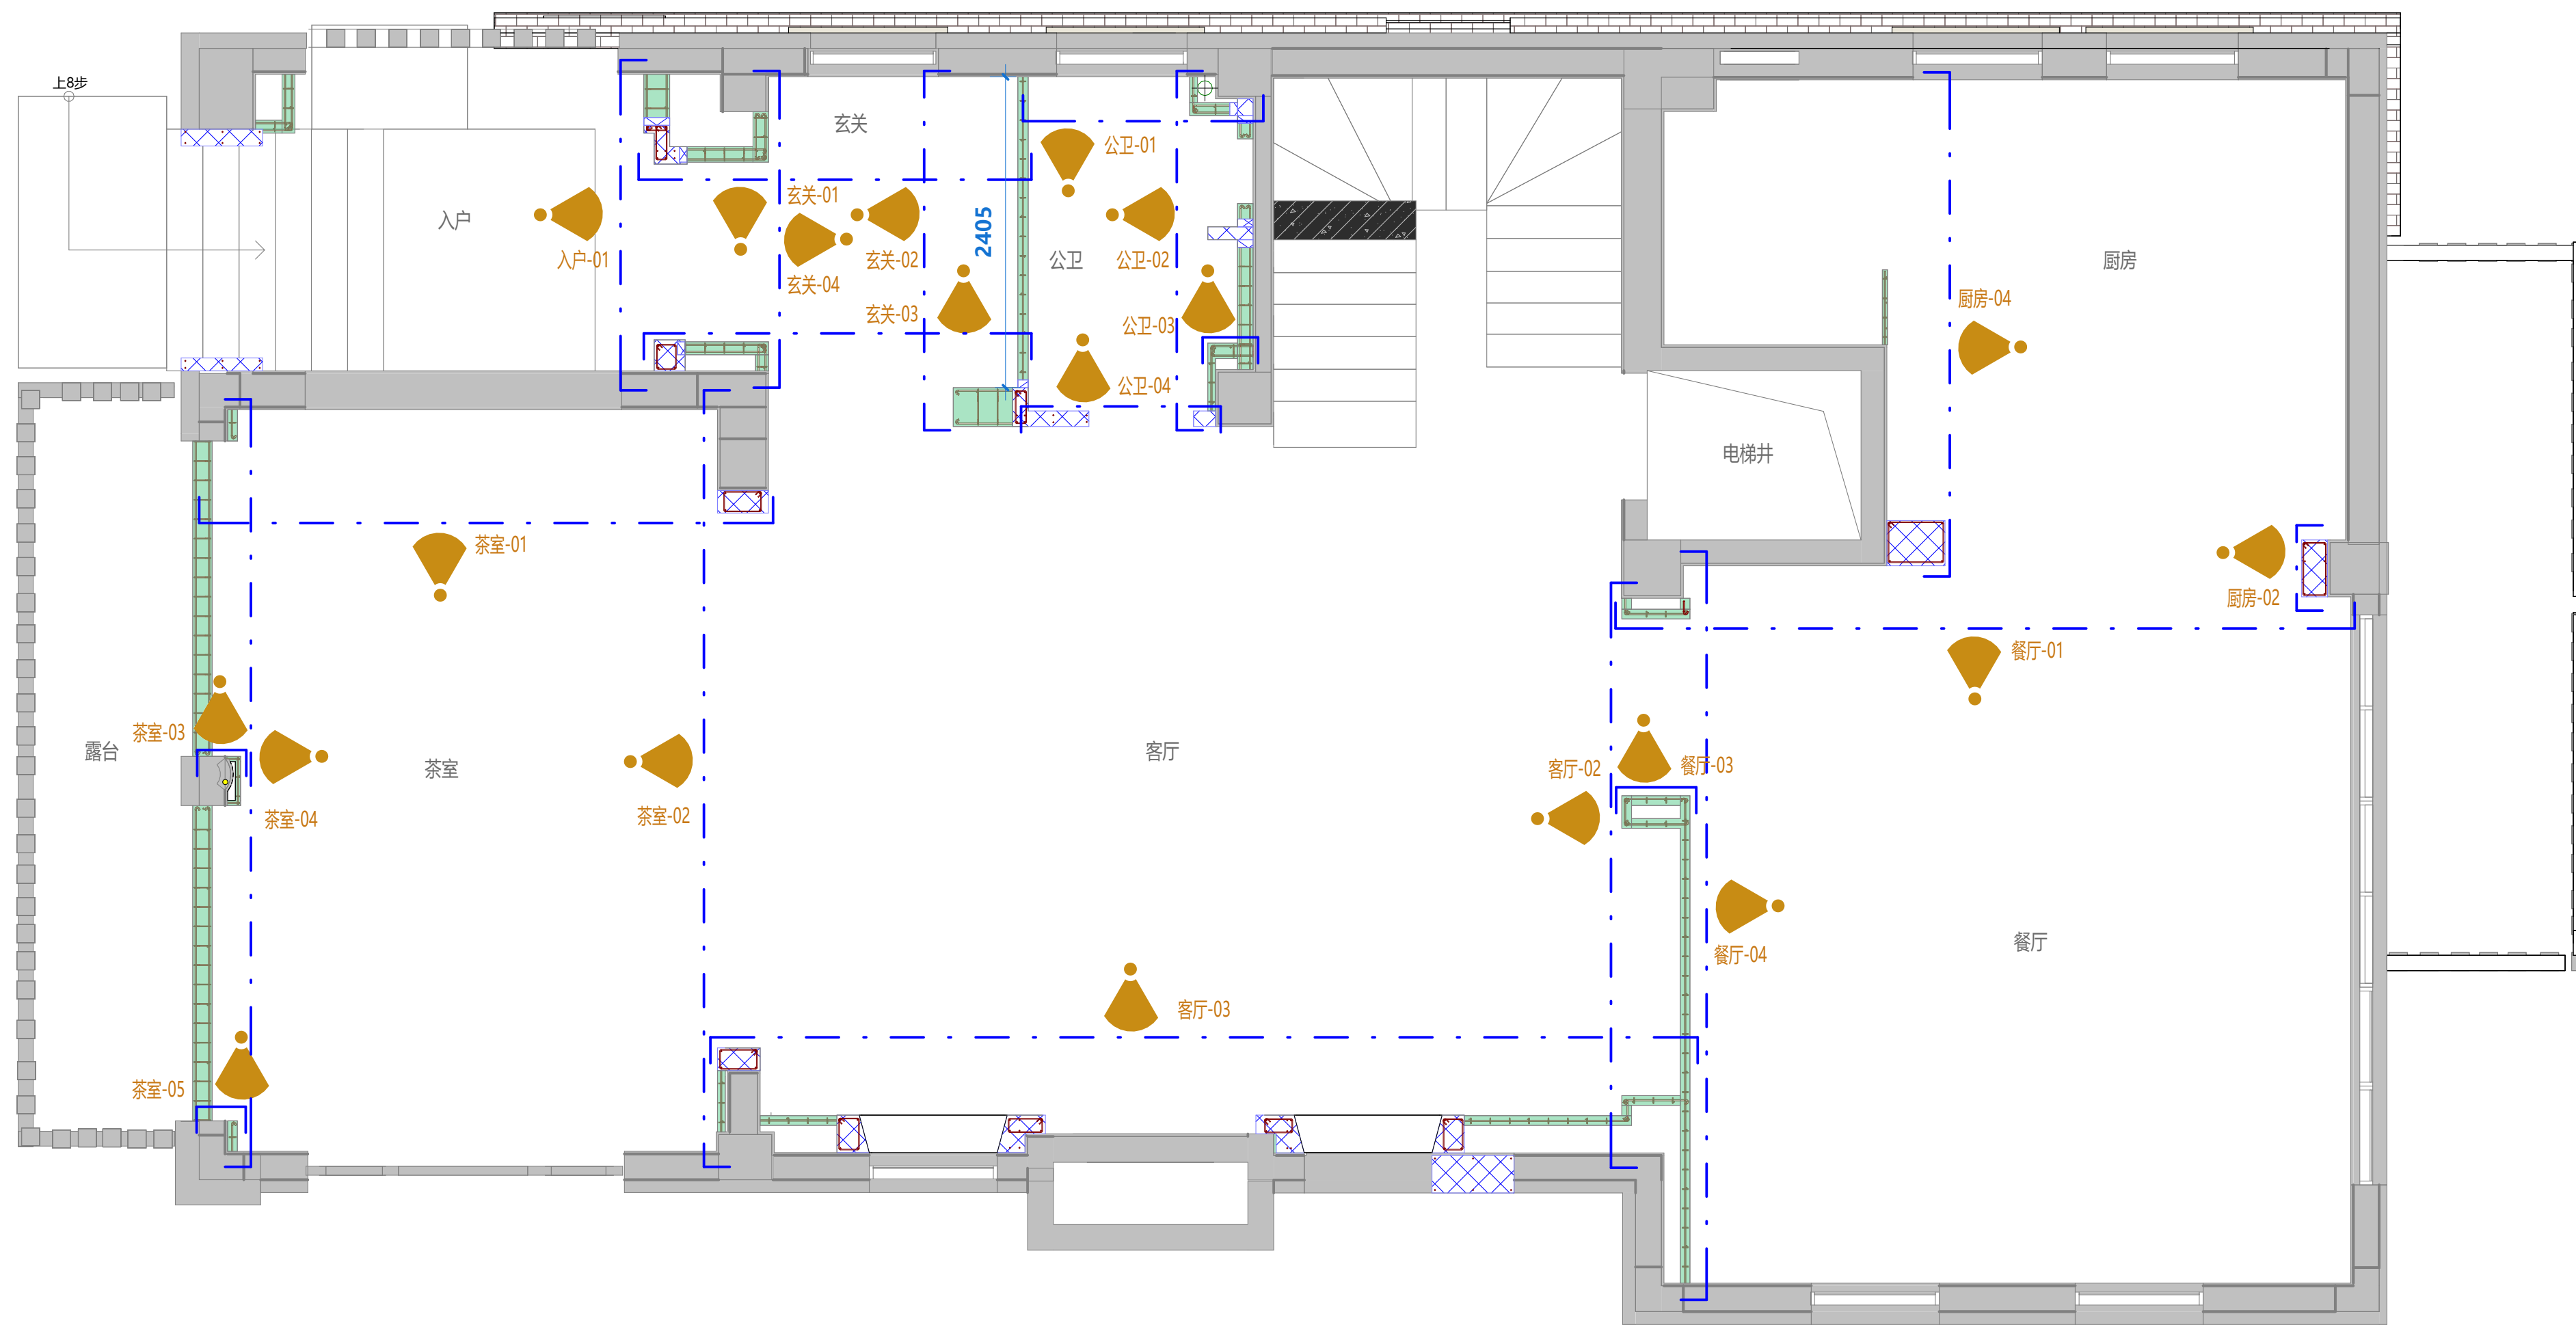

LEGEND图例

编号	图例	说明
1		原始墙、板、柱
2		混凝土导墙
3		过梁
4		构造柱
5		钢筋

盖章

正式施工图
2026-08-06

注释
Notes

- 1.本图纸如与现场尺寸有误，请施工人员与项目负责人联系。
- 2.施工前施工人员应认真查阅此图，如有不明确尺寸，按现场测量为准。
- 3.本图纸必须经甲乙双方认可并签字方可作为施工依据。

日期
Date

07/29/26

修订
Revision项目
Project

巨鹿路880号

比例
Scale

1:40@A2

1F导墙索引图

图纸编号
Drawing No.

1F.NW.PL-02

项目编号
Project No.

© 2026

LEGEND图例

编号	图例	说明
1		原始墙、板、柱
2		混凝土导墙
3		过梁
4		构造柱
5		钢筋

盖章:

正式施工图
2026-08-06

注释

Notes

- 1.本图纸如与现场尺寸有誤，請施工人員與項目負責人联系。
- 2.施工前施工人員应认真查阅此圖，如有不明尺寸，按现场測量为准。
- 3.本圖紙必須經甲乙雙方认可并簽字方可作为施工依据。

日期

Date

08/01/26

修订

Revision

项目

Project

巨鹿路880号

图纸名称

Drawing Name.

1F入户、玄关导墙钢筋立面图

比例

Scale

图纸编号











Drawing No.

1F.NW.PL-02.1

项目编号


Project No.

© 2026

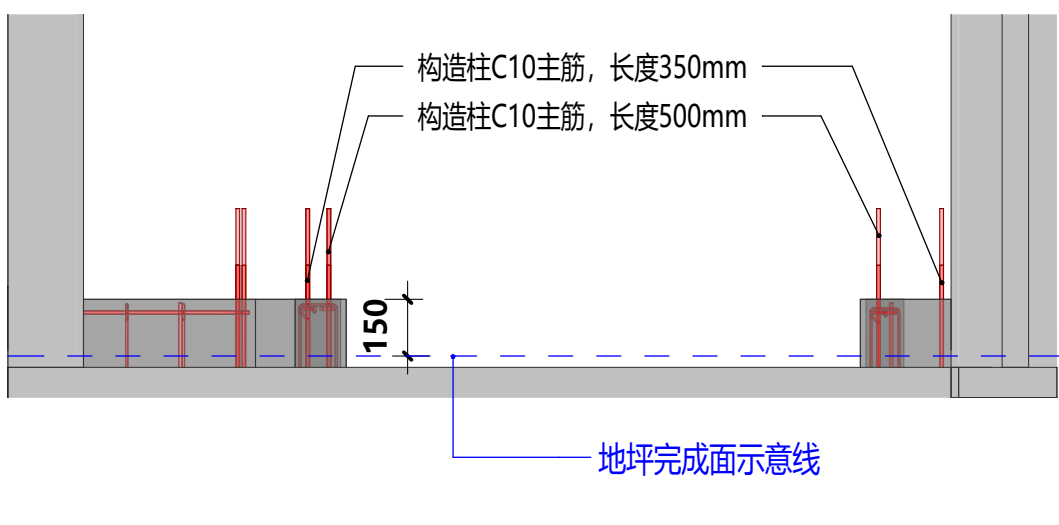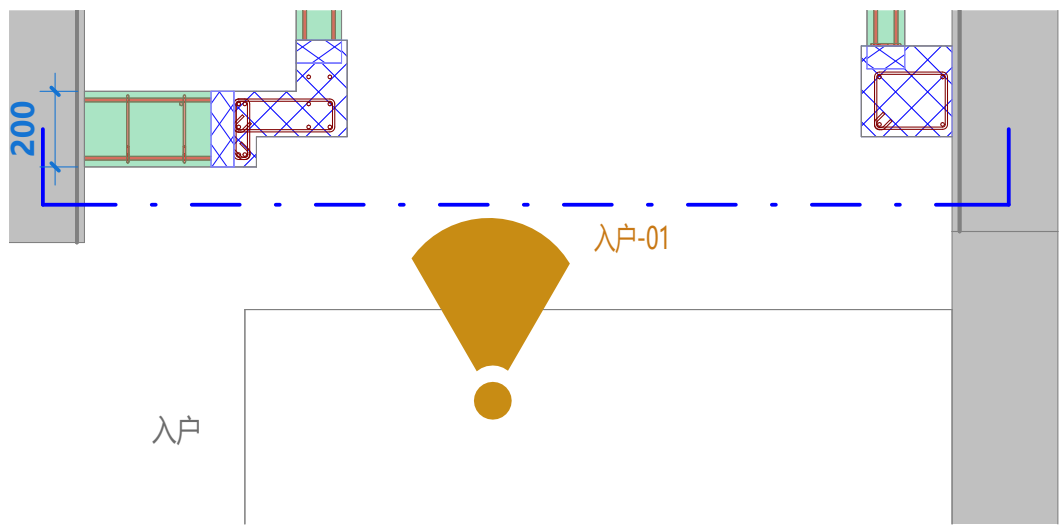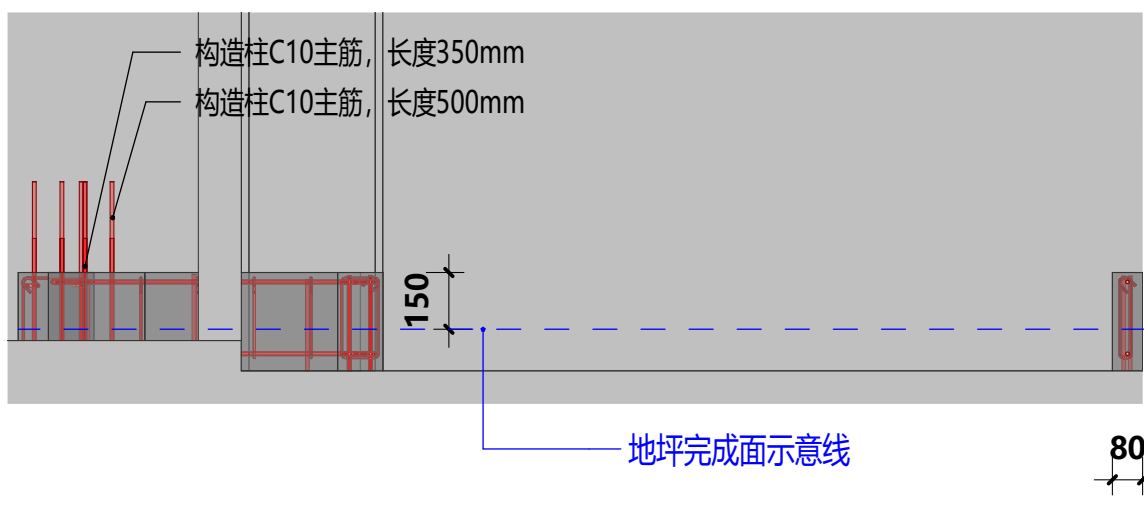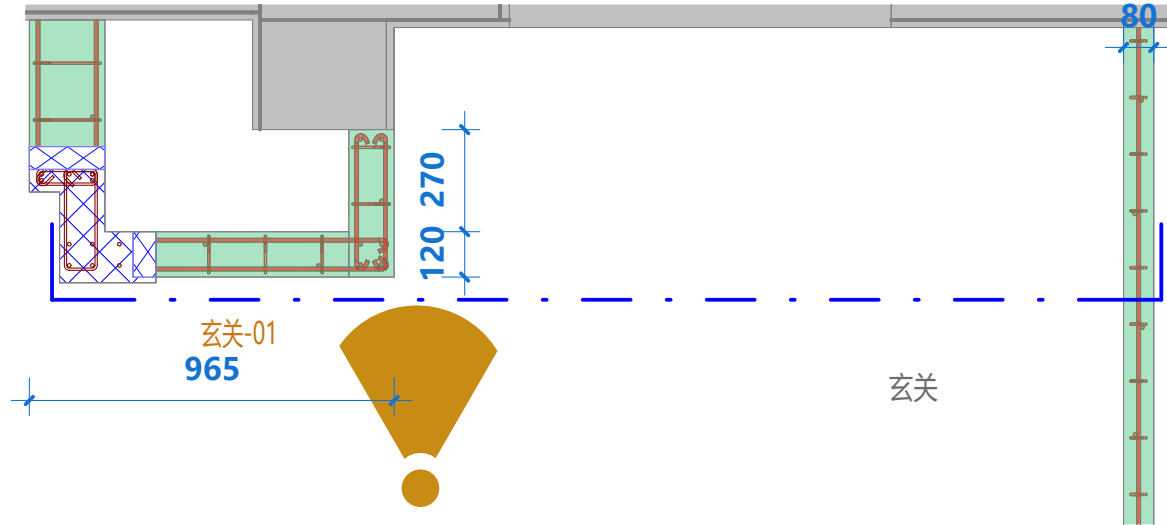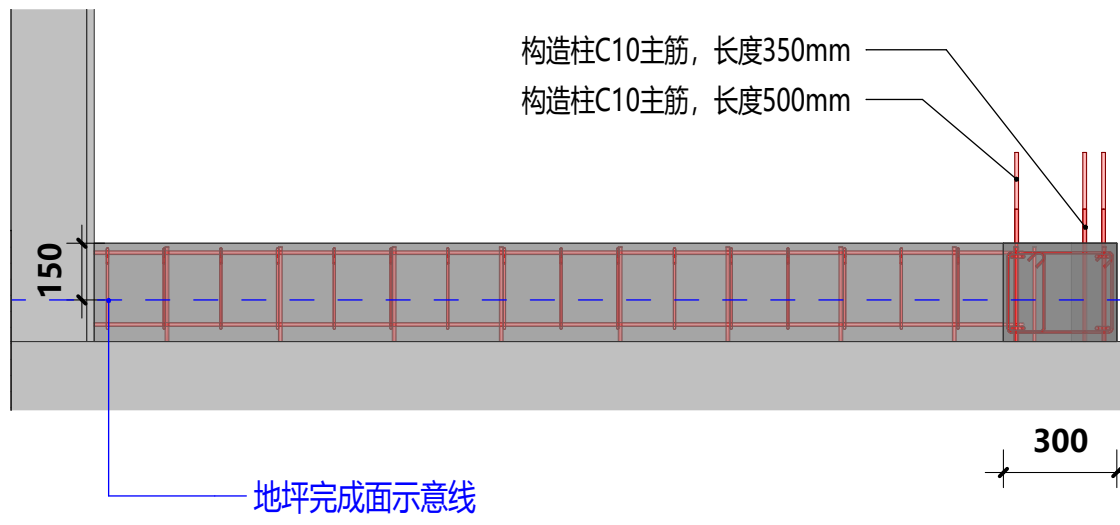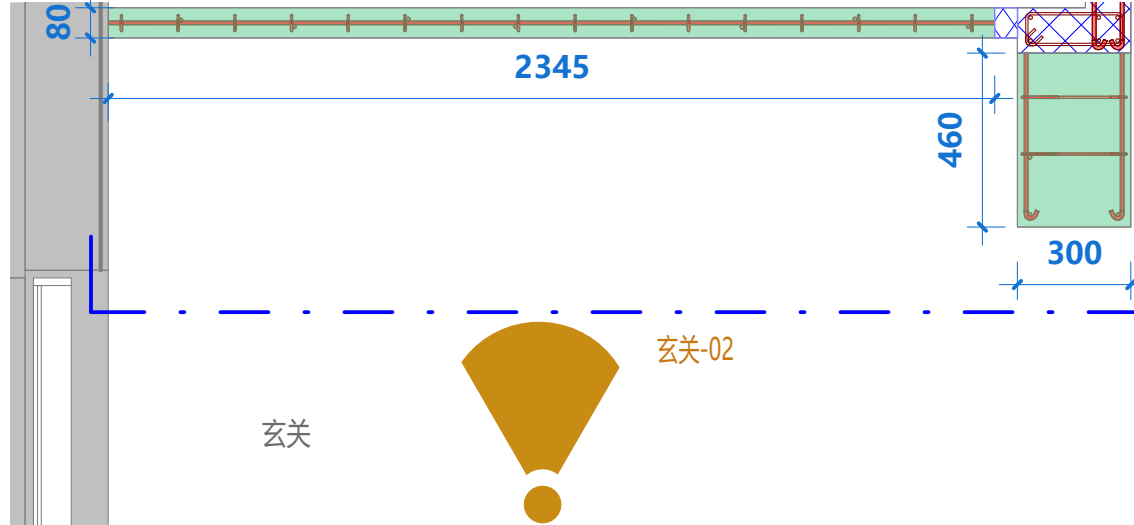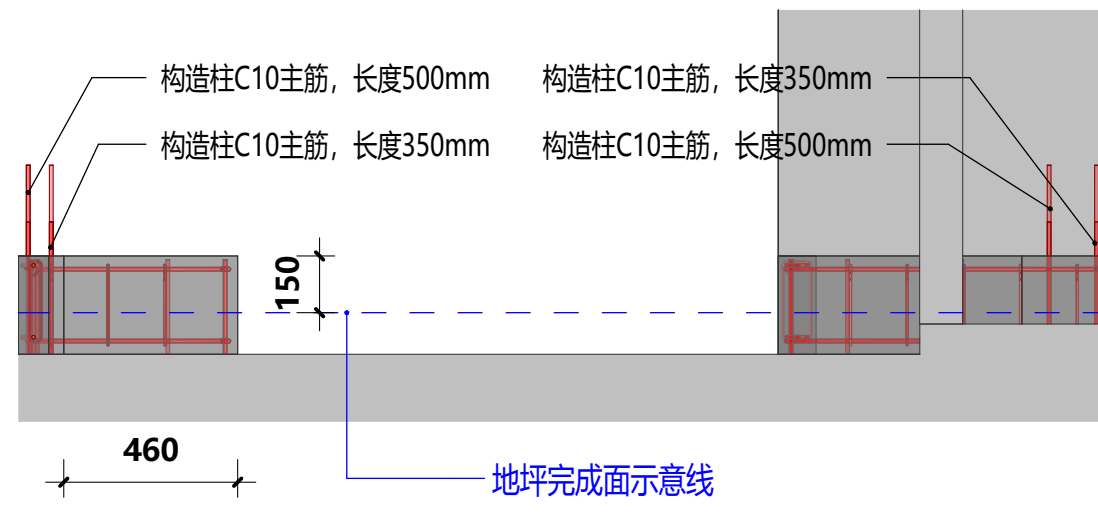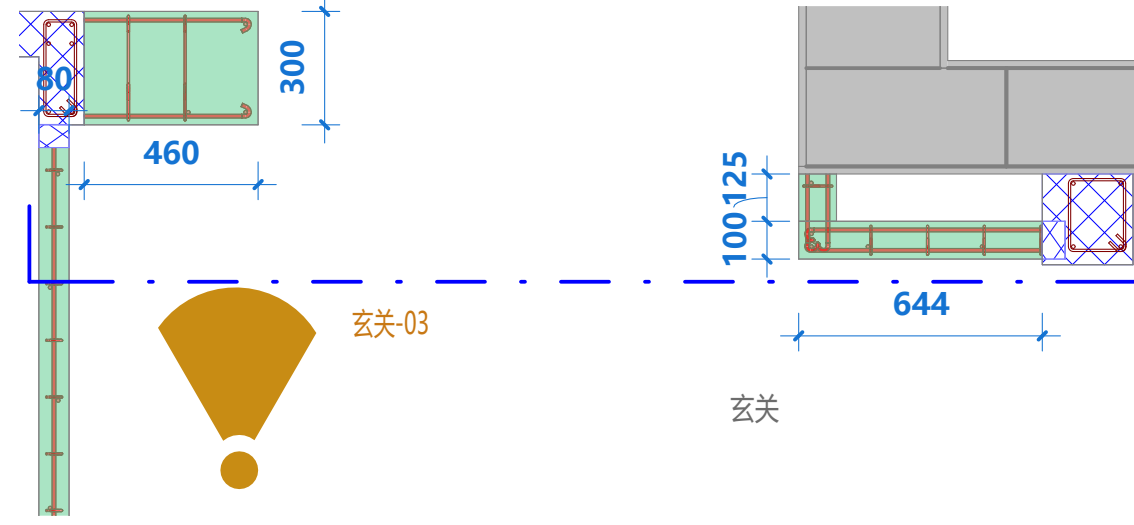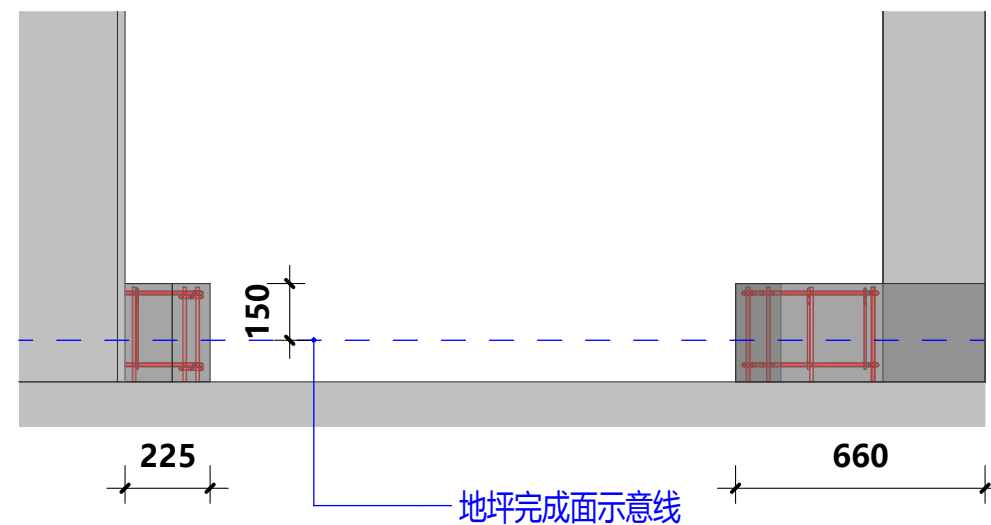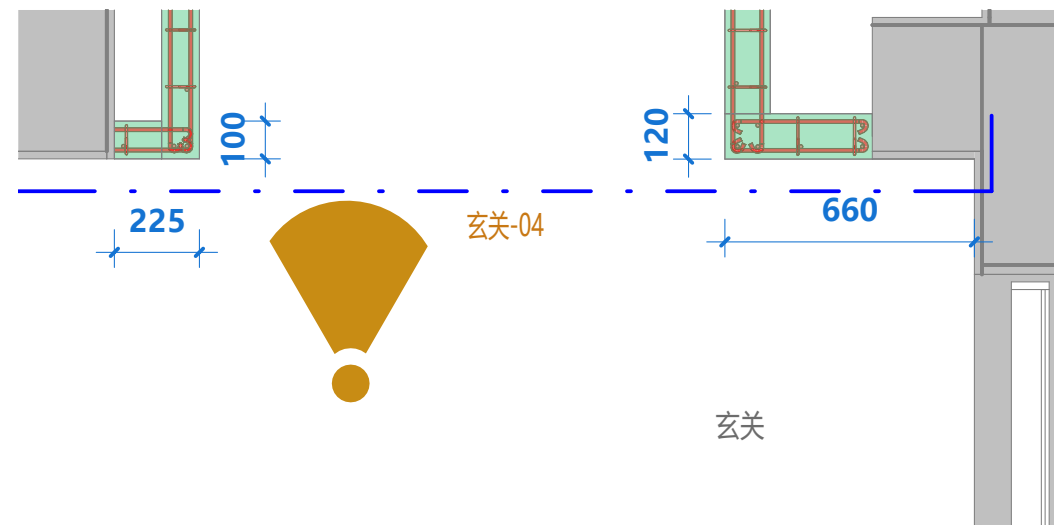


1	1F入户混凝土导墙、构造柱钢筋立面图1	2	1F玄关混凝土导墙、构造柱钢筋立面图1	3	1F玄关混凝土导墙、构造柱钢筋立面图2	4	1F玄关混凝土导墙、构造柱钢筋立面图3	5	1F玄关混凝土导墙、构造柱钢筋立面图4
入户-01	Scale比例 1:20@A2	玄关-01	Scale比例 1:20@A2	玄关-02	Scale比例 1:20@A2	玄关-03	Scale比例 1:20@A2	玄关-04	Scale比例 1:20@A2


导墙节点正视图

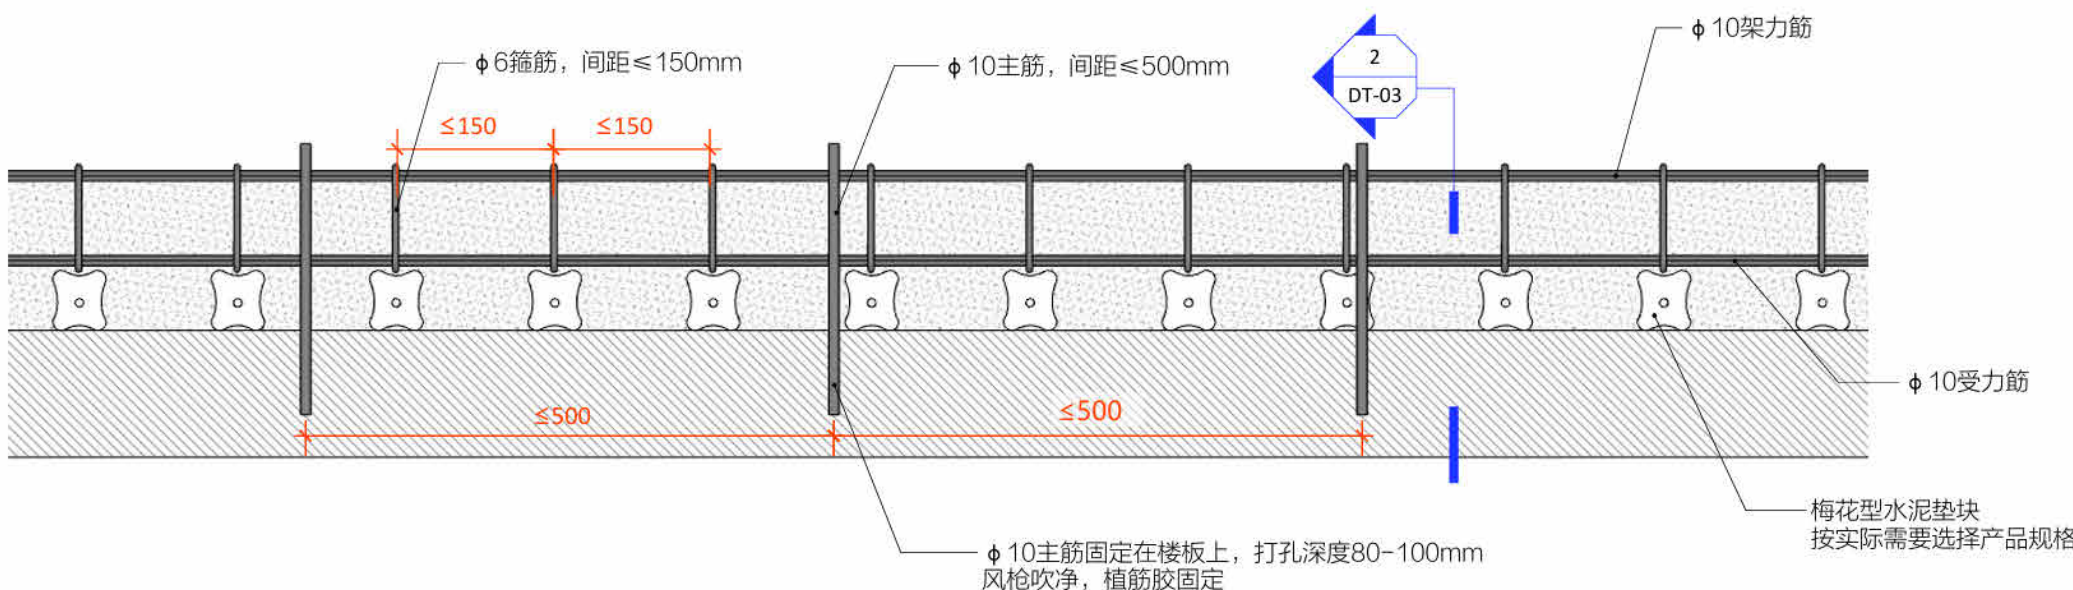


DT-03.2A导墙节点图


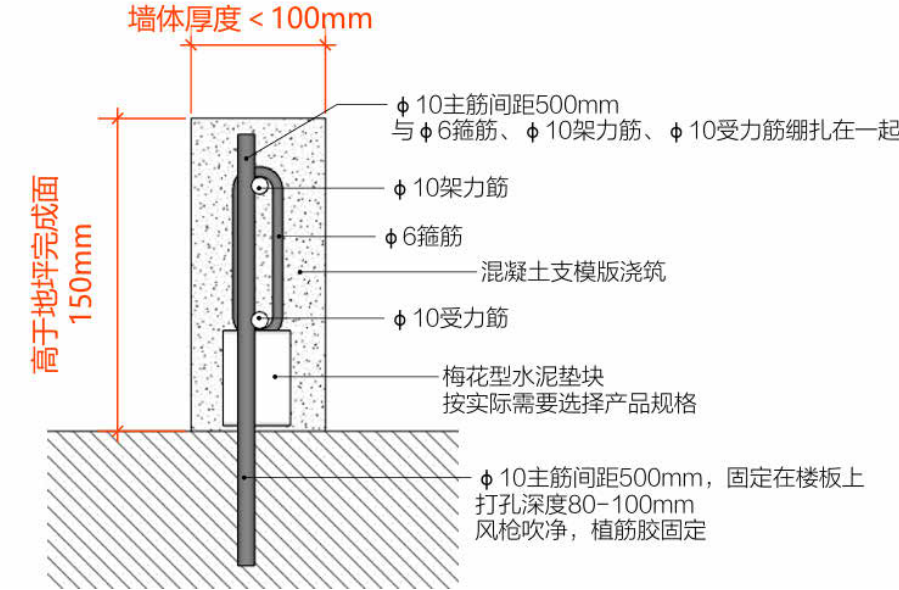


DT-03.2B导墙节点图

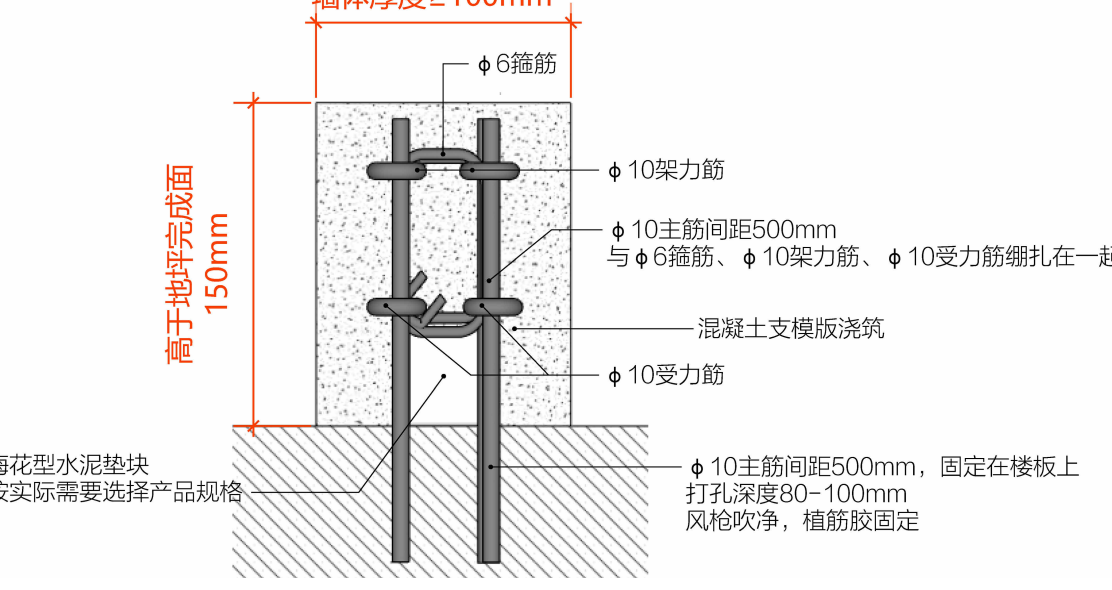

DT-04构造柱节点图

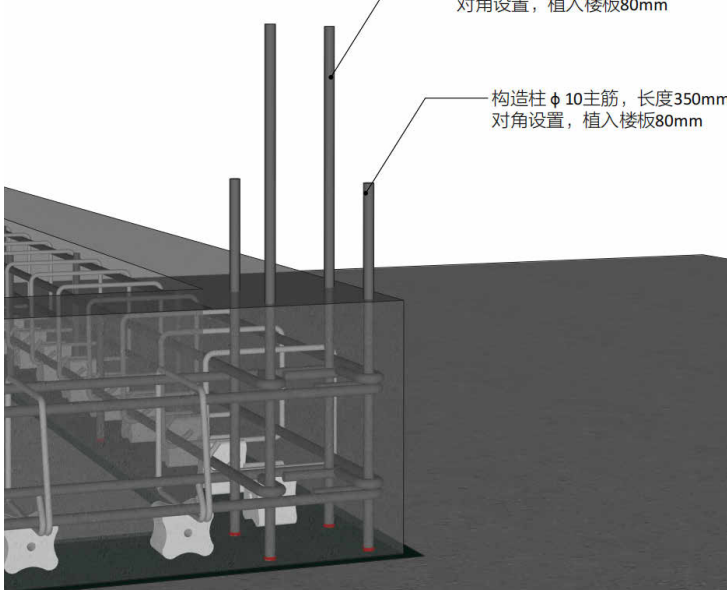

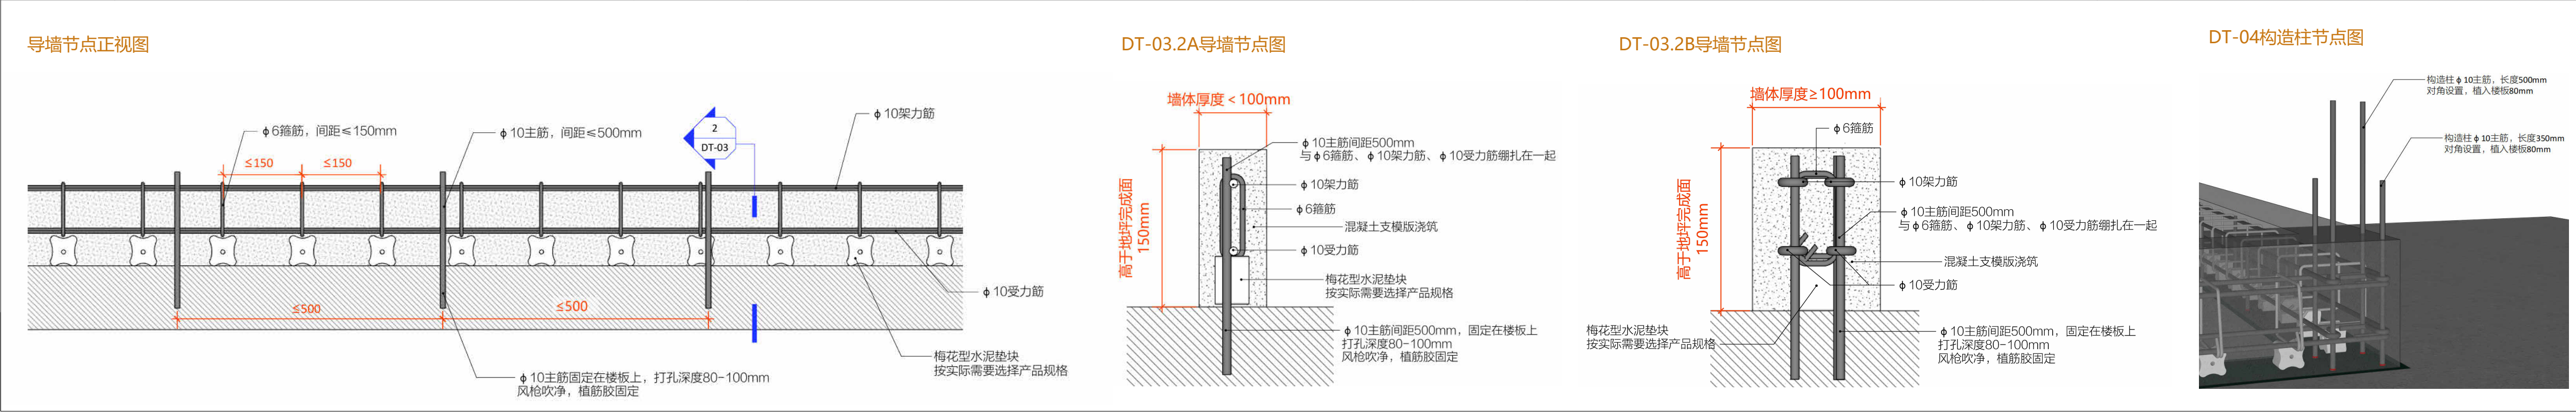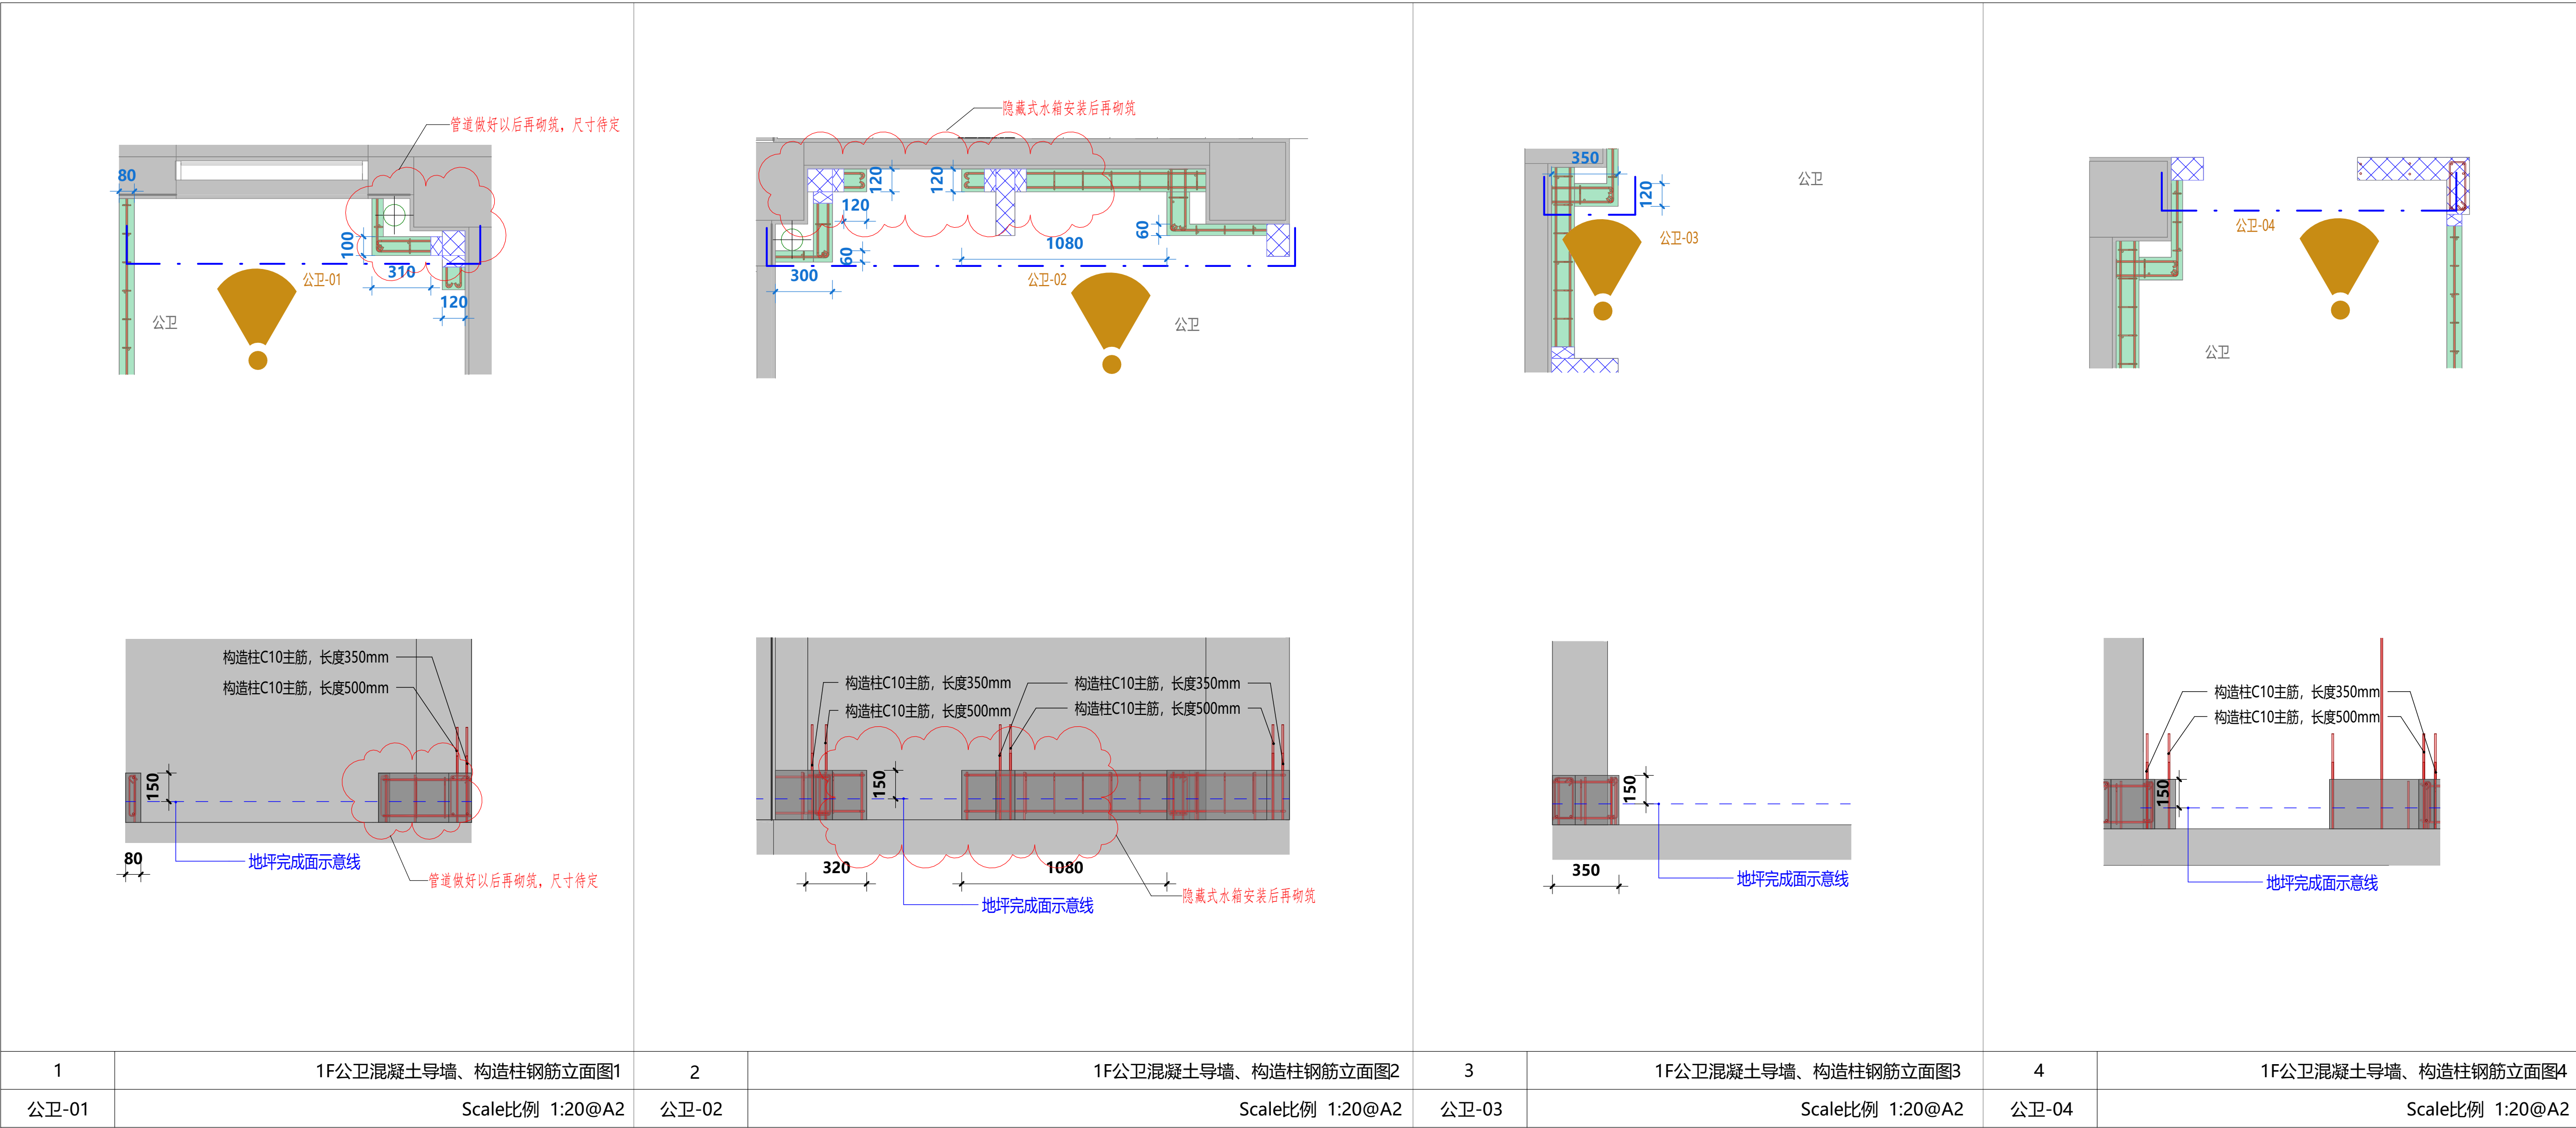

LEGEND图例

编号	图例	说明
1		原始墙、板、柱
2		混凝土导墙
3		过梁
4		构造柱
5		钢筋

盖章:

正式施工图
2026-08-06

注释
Notes

1.本图纸如与现场尺寸有误差, 请施工人员与项目负责人联系。
2.施工前施工人员应认真查阅此图, 如有不明尺寸, 按现场测量为准。
3.本图纸必须经甲乙双方认可并签字方可作为施工依据。

日期 Date	08/01/26
修订 Revision	

项目
Project

巨鹿路880号

图纸名称
Drawing Name.

1F公卫导墙钢筋立面











比例
Scale

图纸编号
Drawing No.

1F.NW.PL-02.2

项目编号
Project No.

© 2026

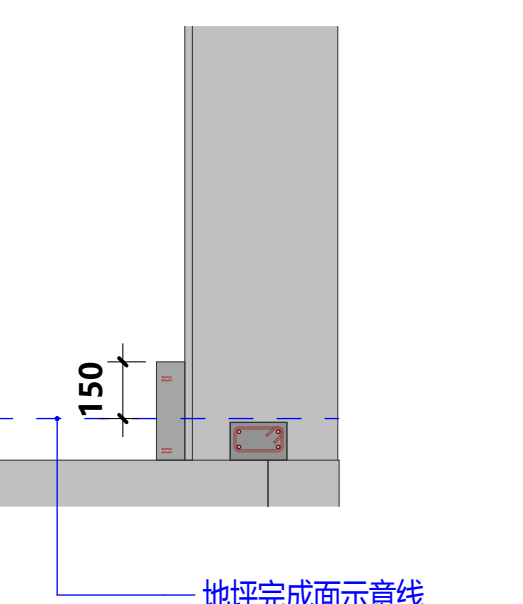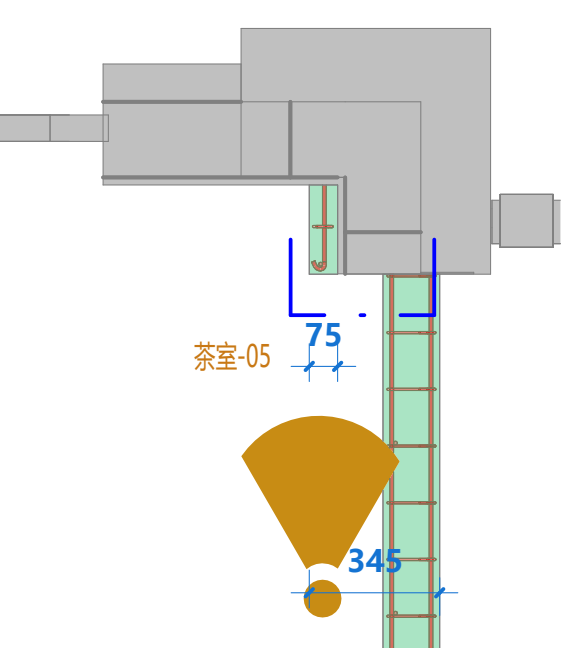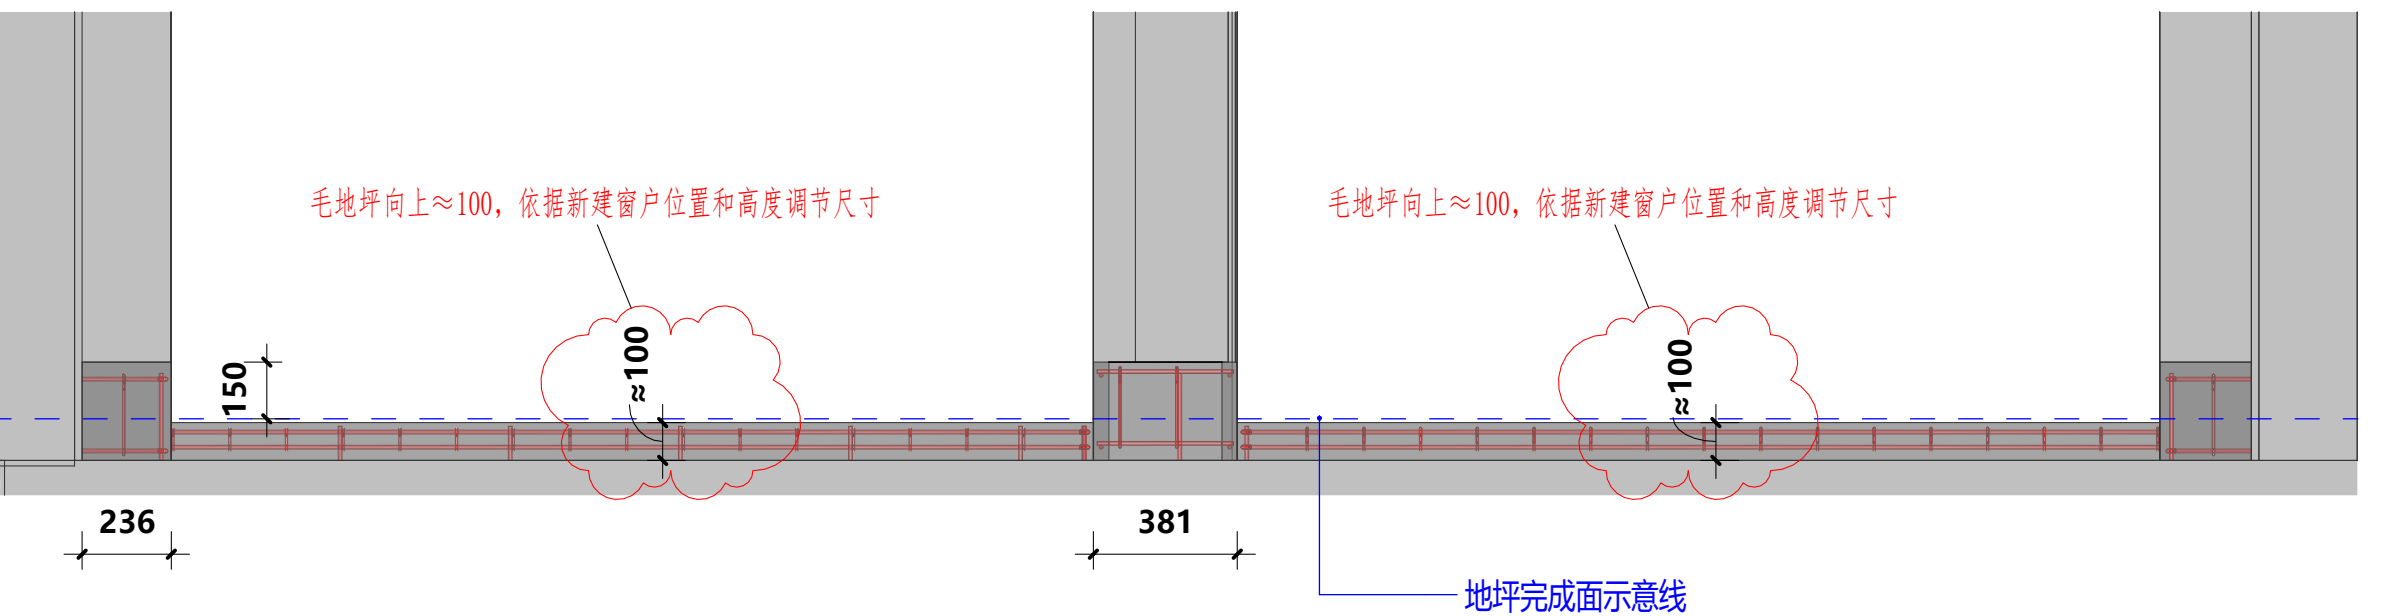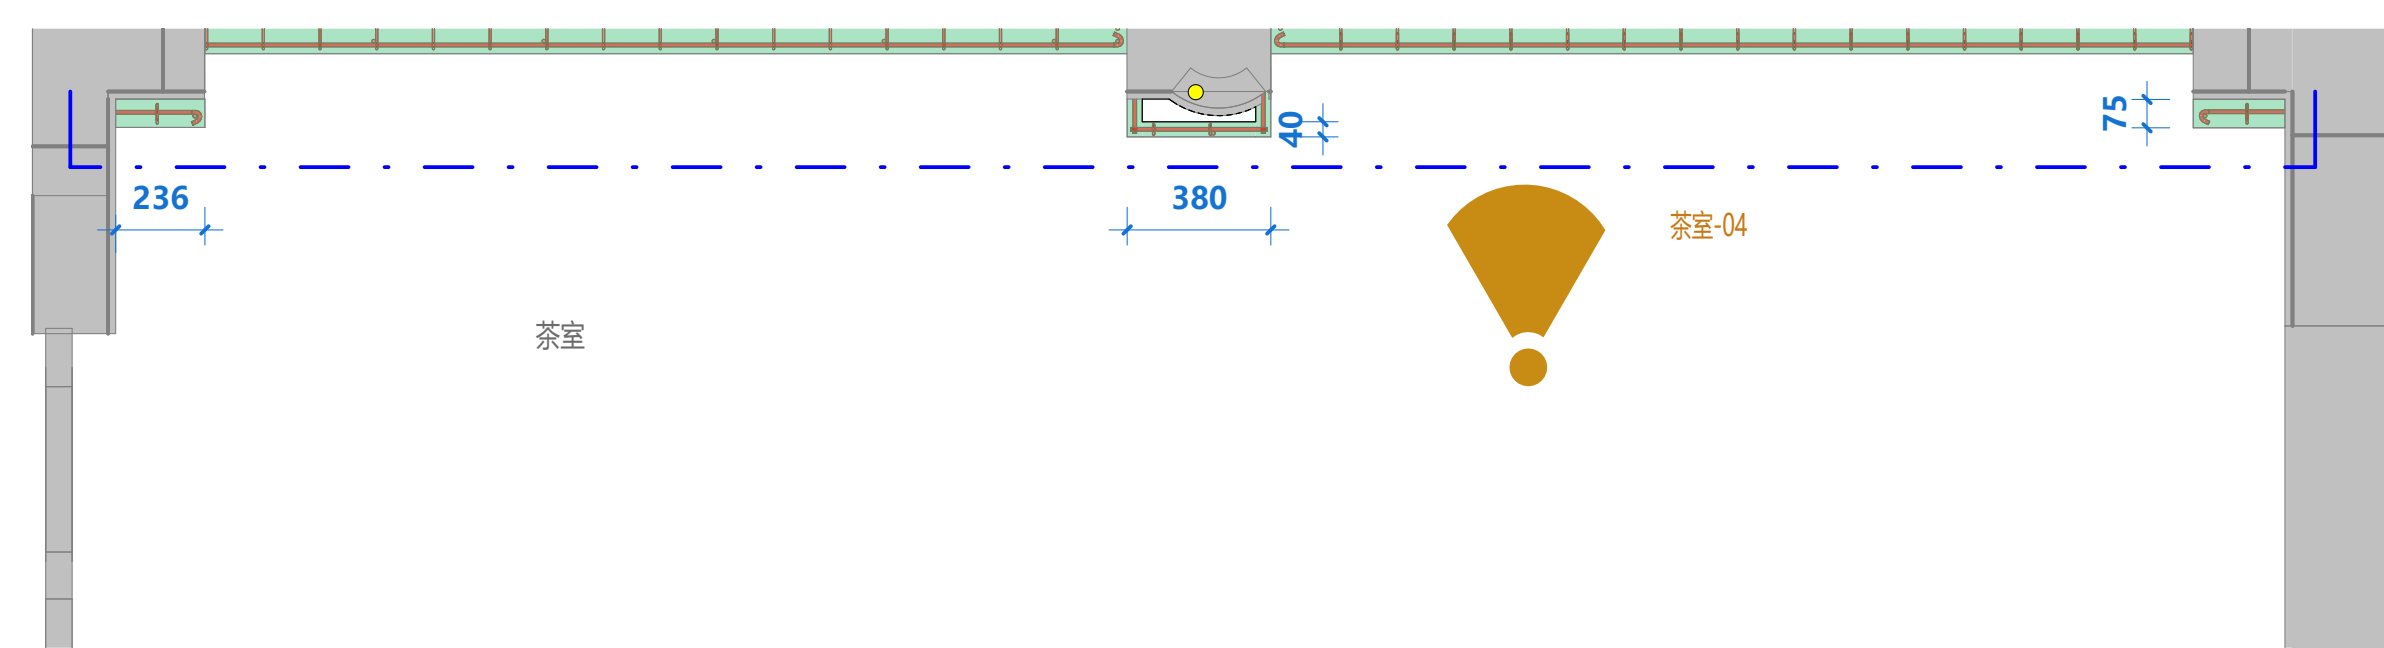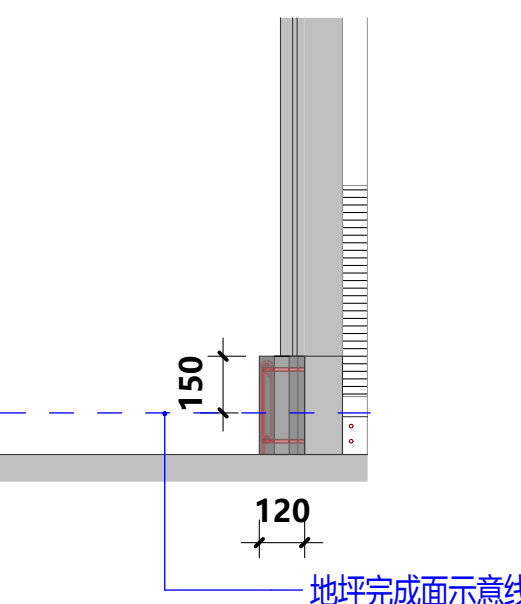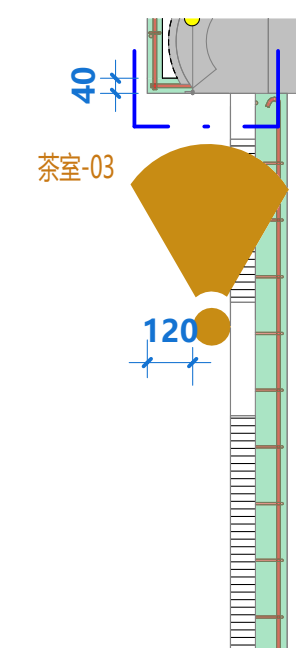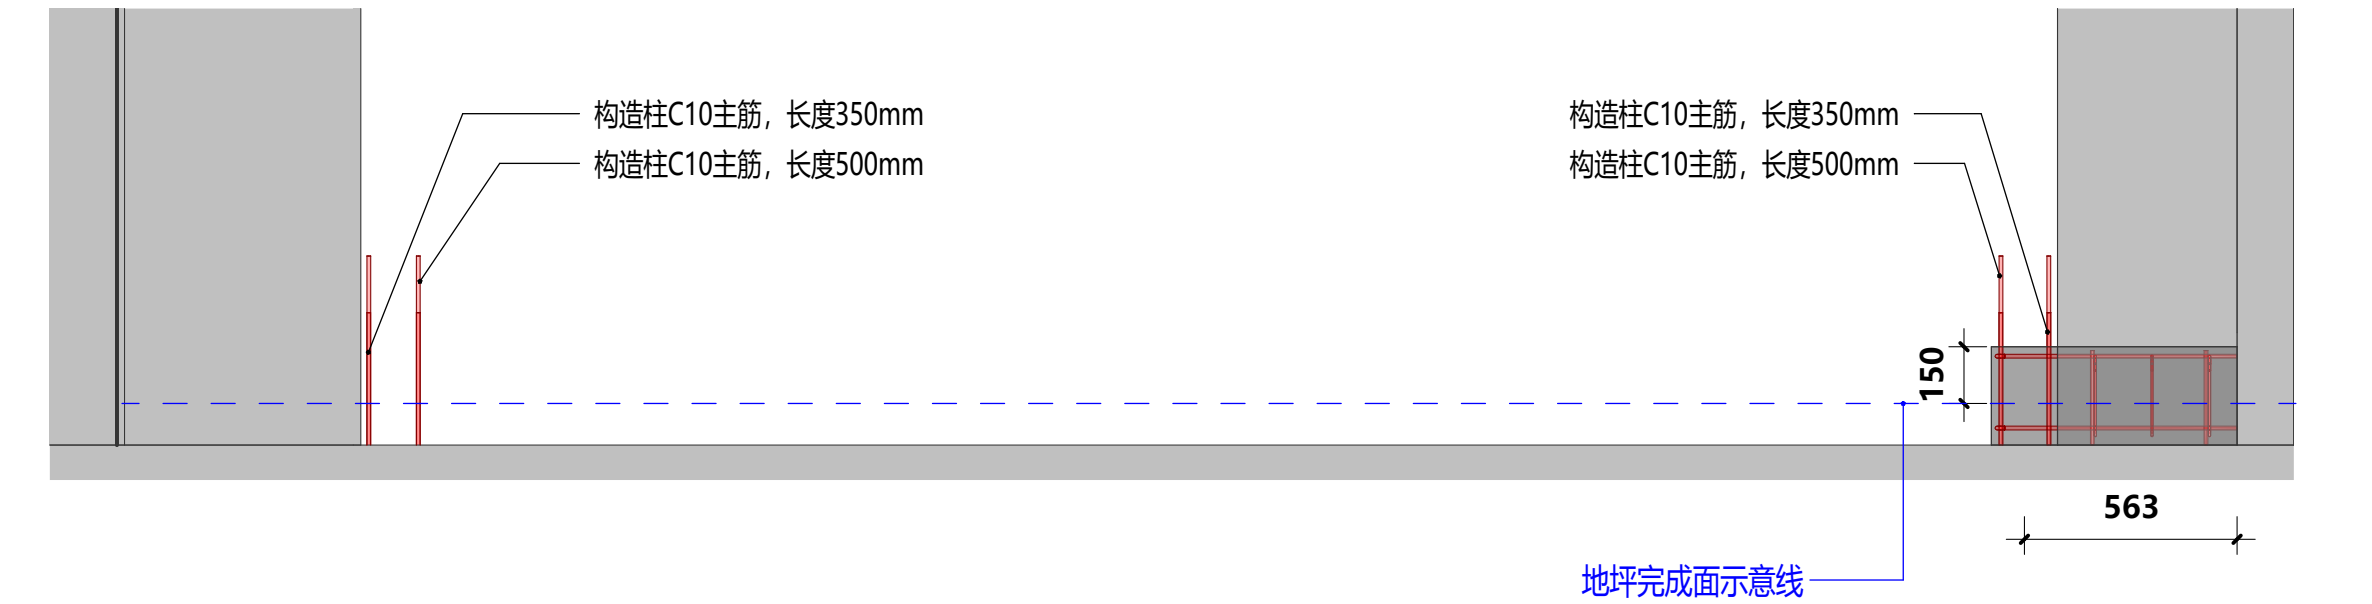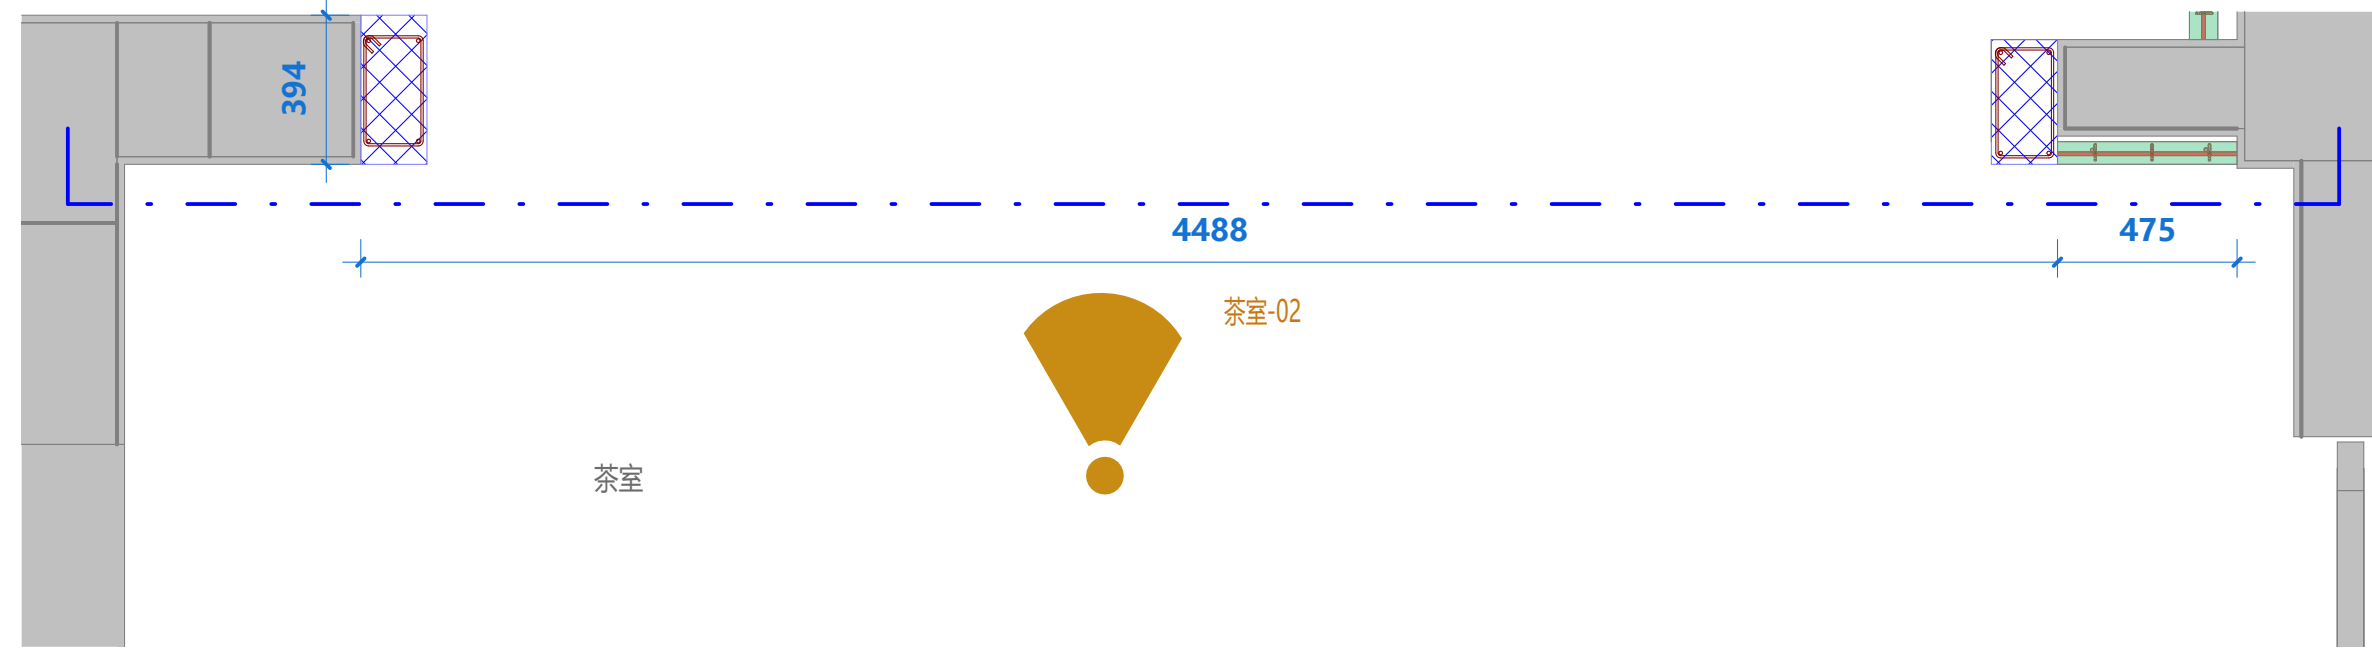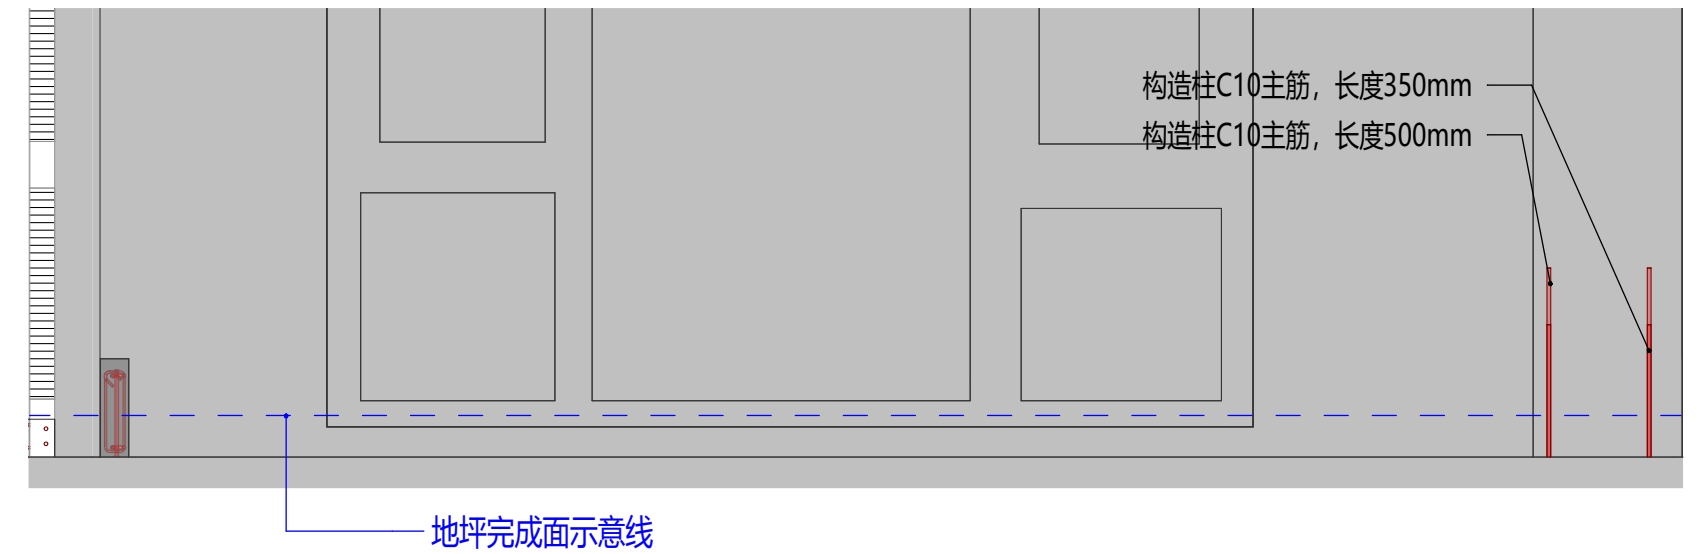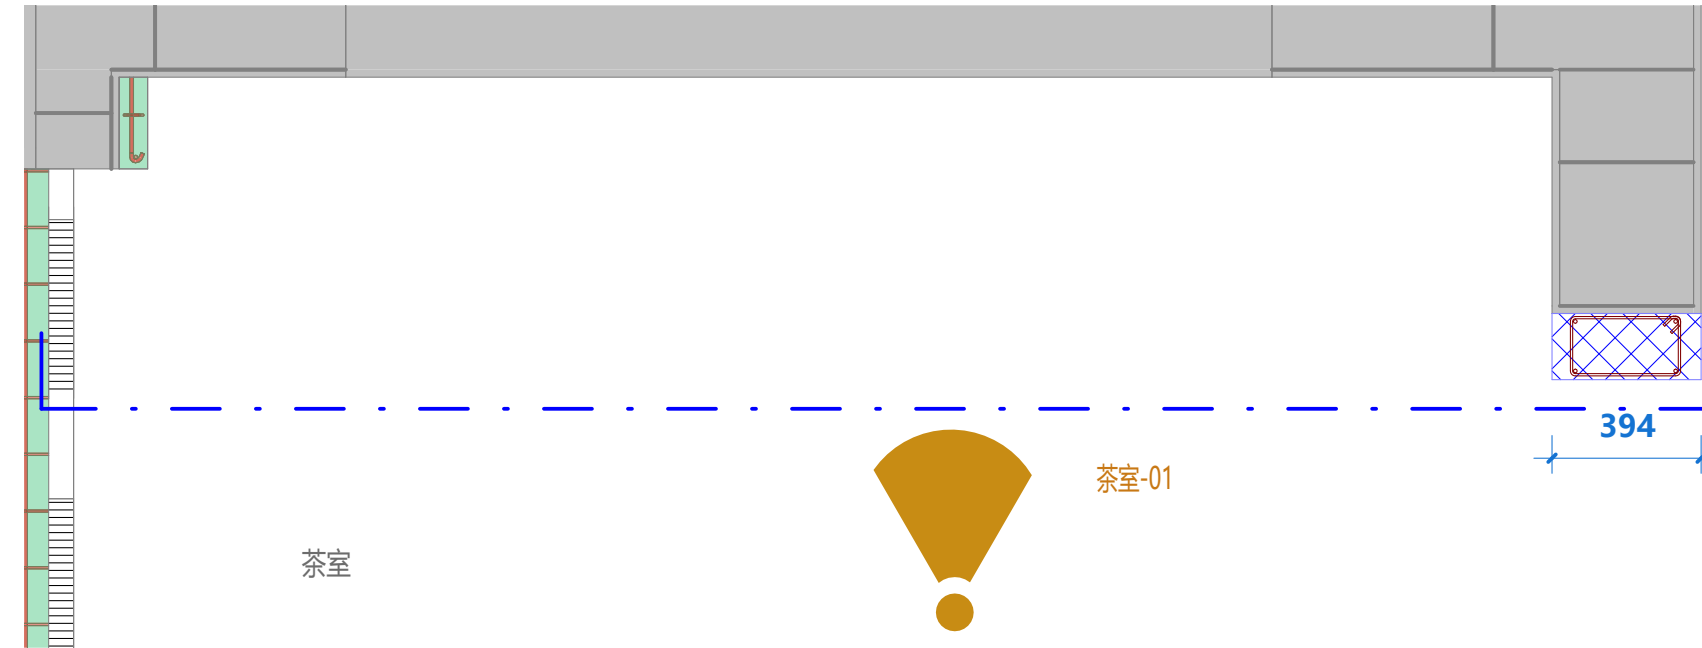

LEGEND图例

编号	图例	说明
1		原始墙、板、柱
2		混凝土墙
3		过梁
4		构造柱
5		钢筋

盖章:

正式施工图
2026-08-06

注释

Notes

1. 本图根据设计提供尺寸绘制, 请施工人员在施工过程中, 严格按照设计尺寸施工。
2. 施工过程中如有变更, 请及时与设计单位沟通, 并经设计单位确认后, 方可进行施工。
3. 本图仅供参考, 不作为施工依据。

日期

Date

08/01/26

修订

Revision

1

项目

Project

巨鹿路880号

图名

Drawing Name

1F茶室导墙钢筋立面

比例

Scale

图号

Drawing No.


1F.NW.PL-02.3

项目编号


Project No.

© 2026


导墙节点正视图

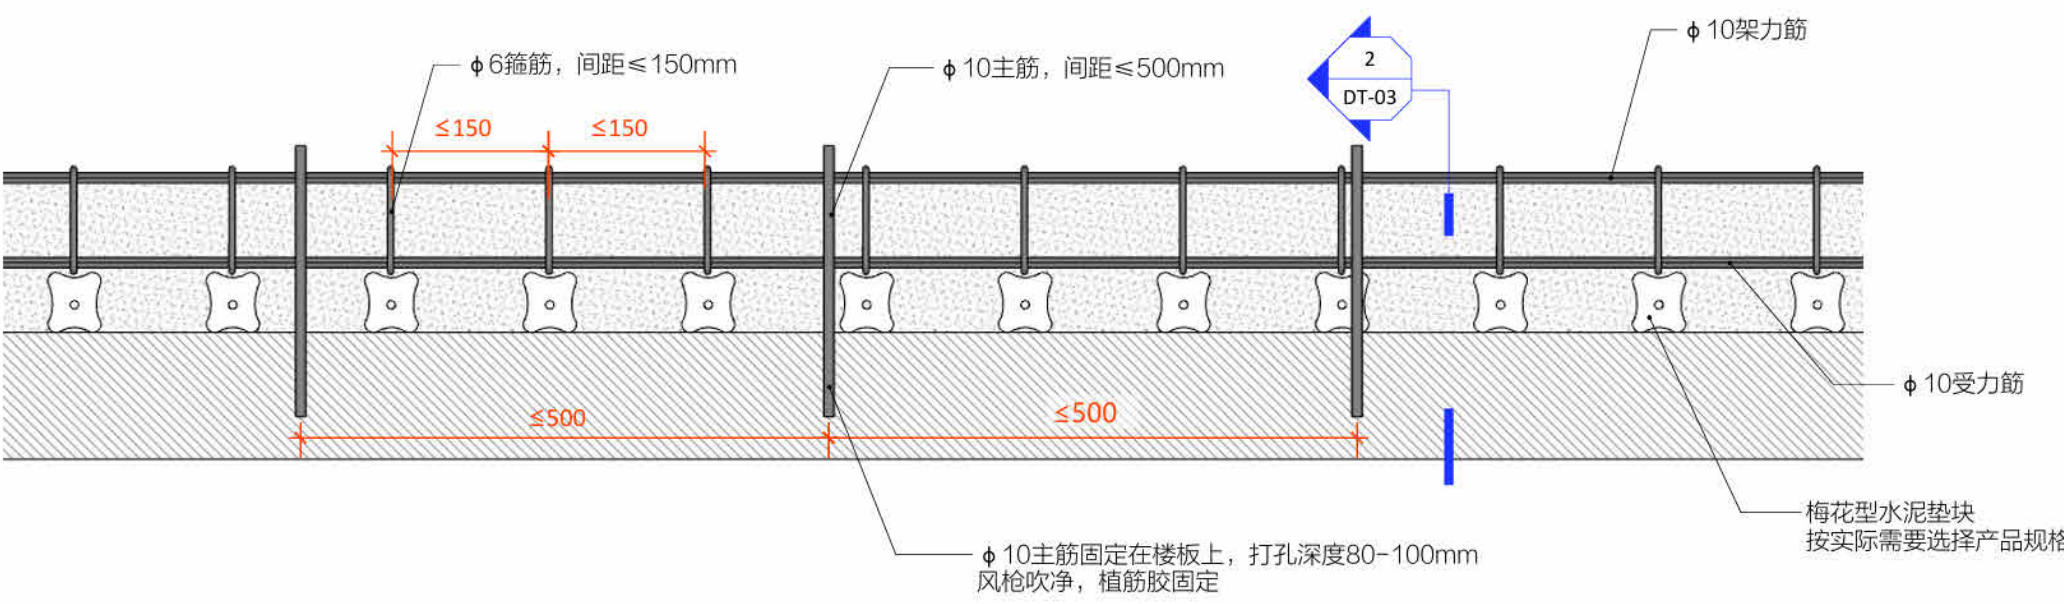


DT-03.2A导墙节点图

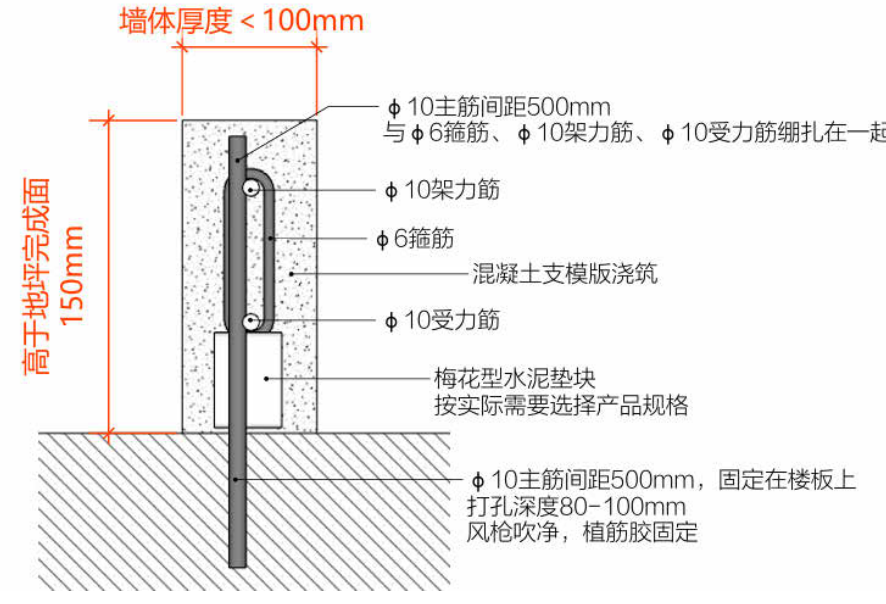


DT-03.2B导墙节点图

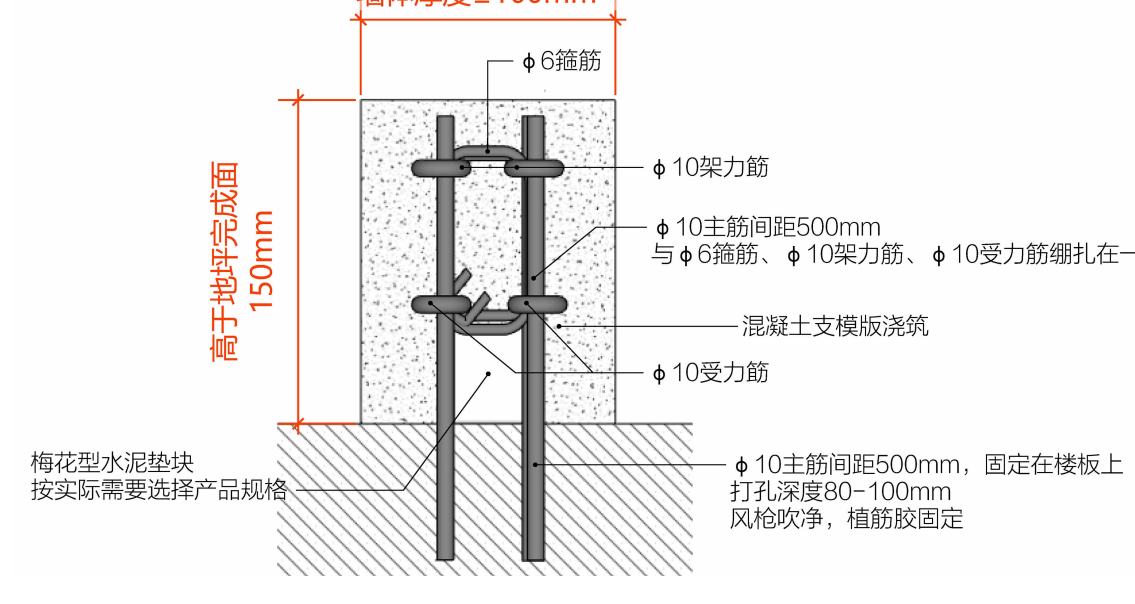


DT-04构造柱节点图


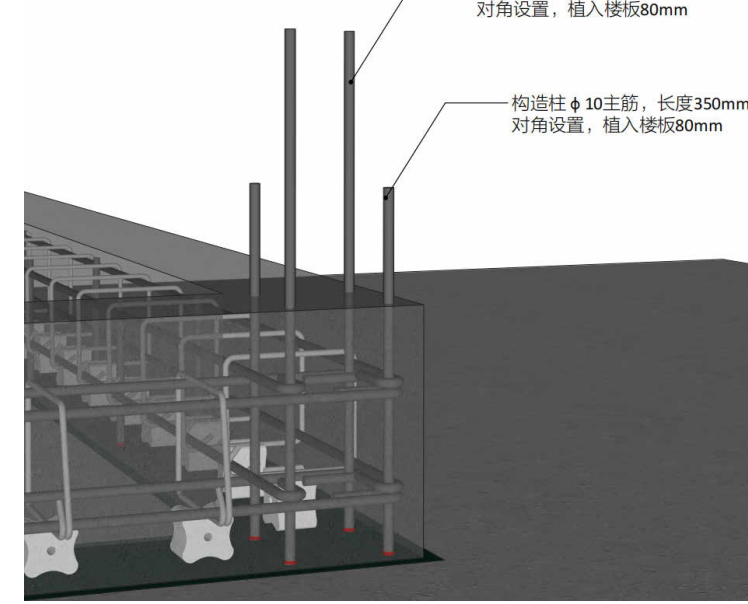


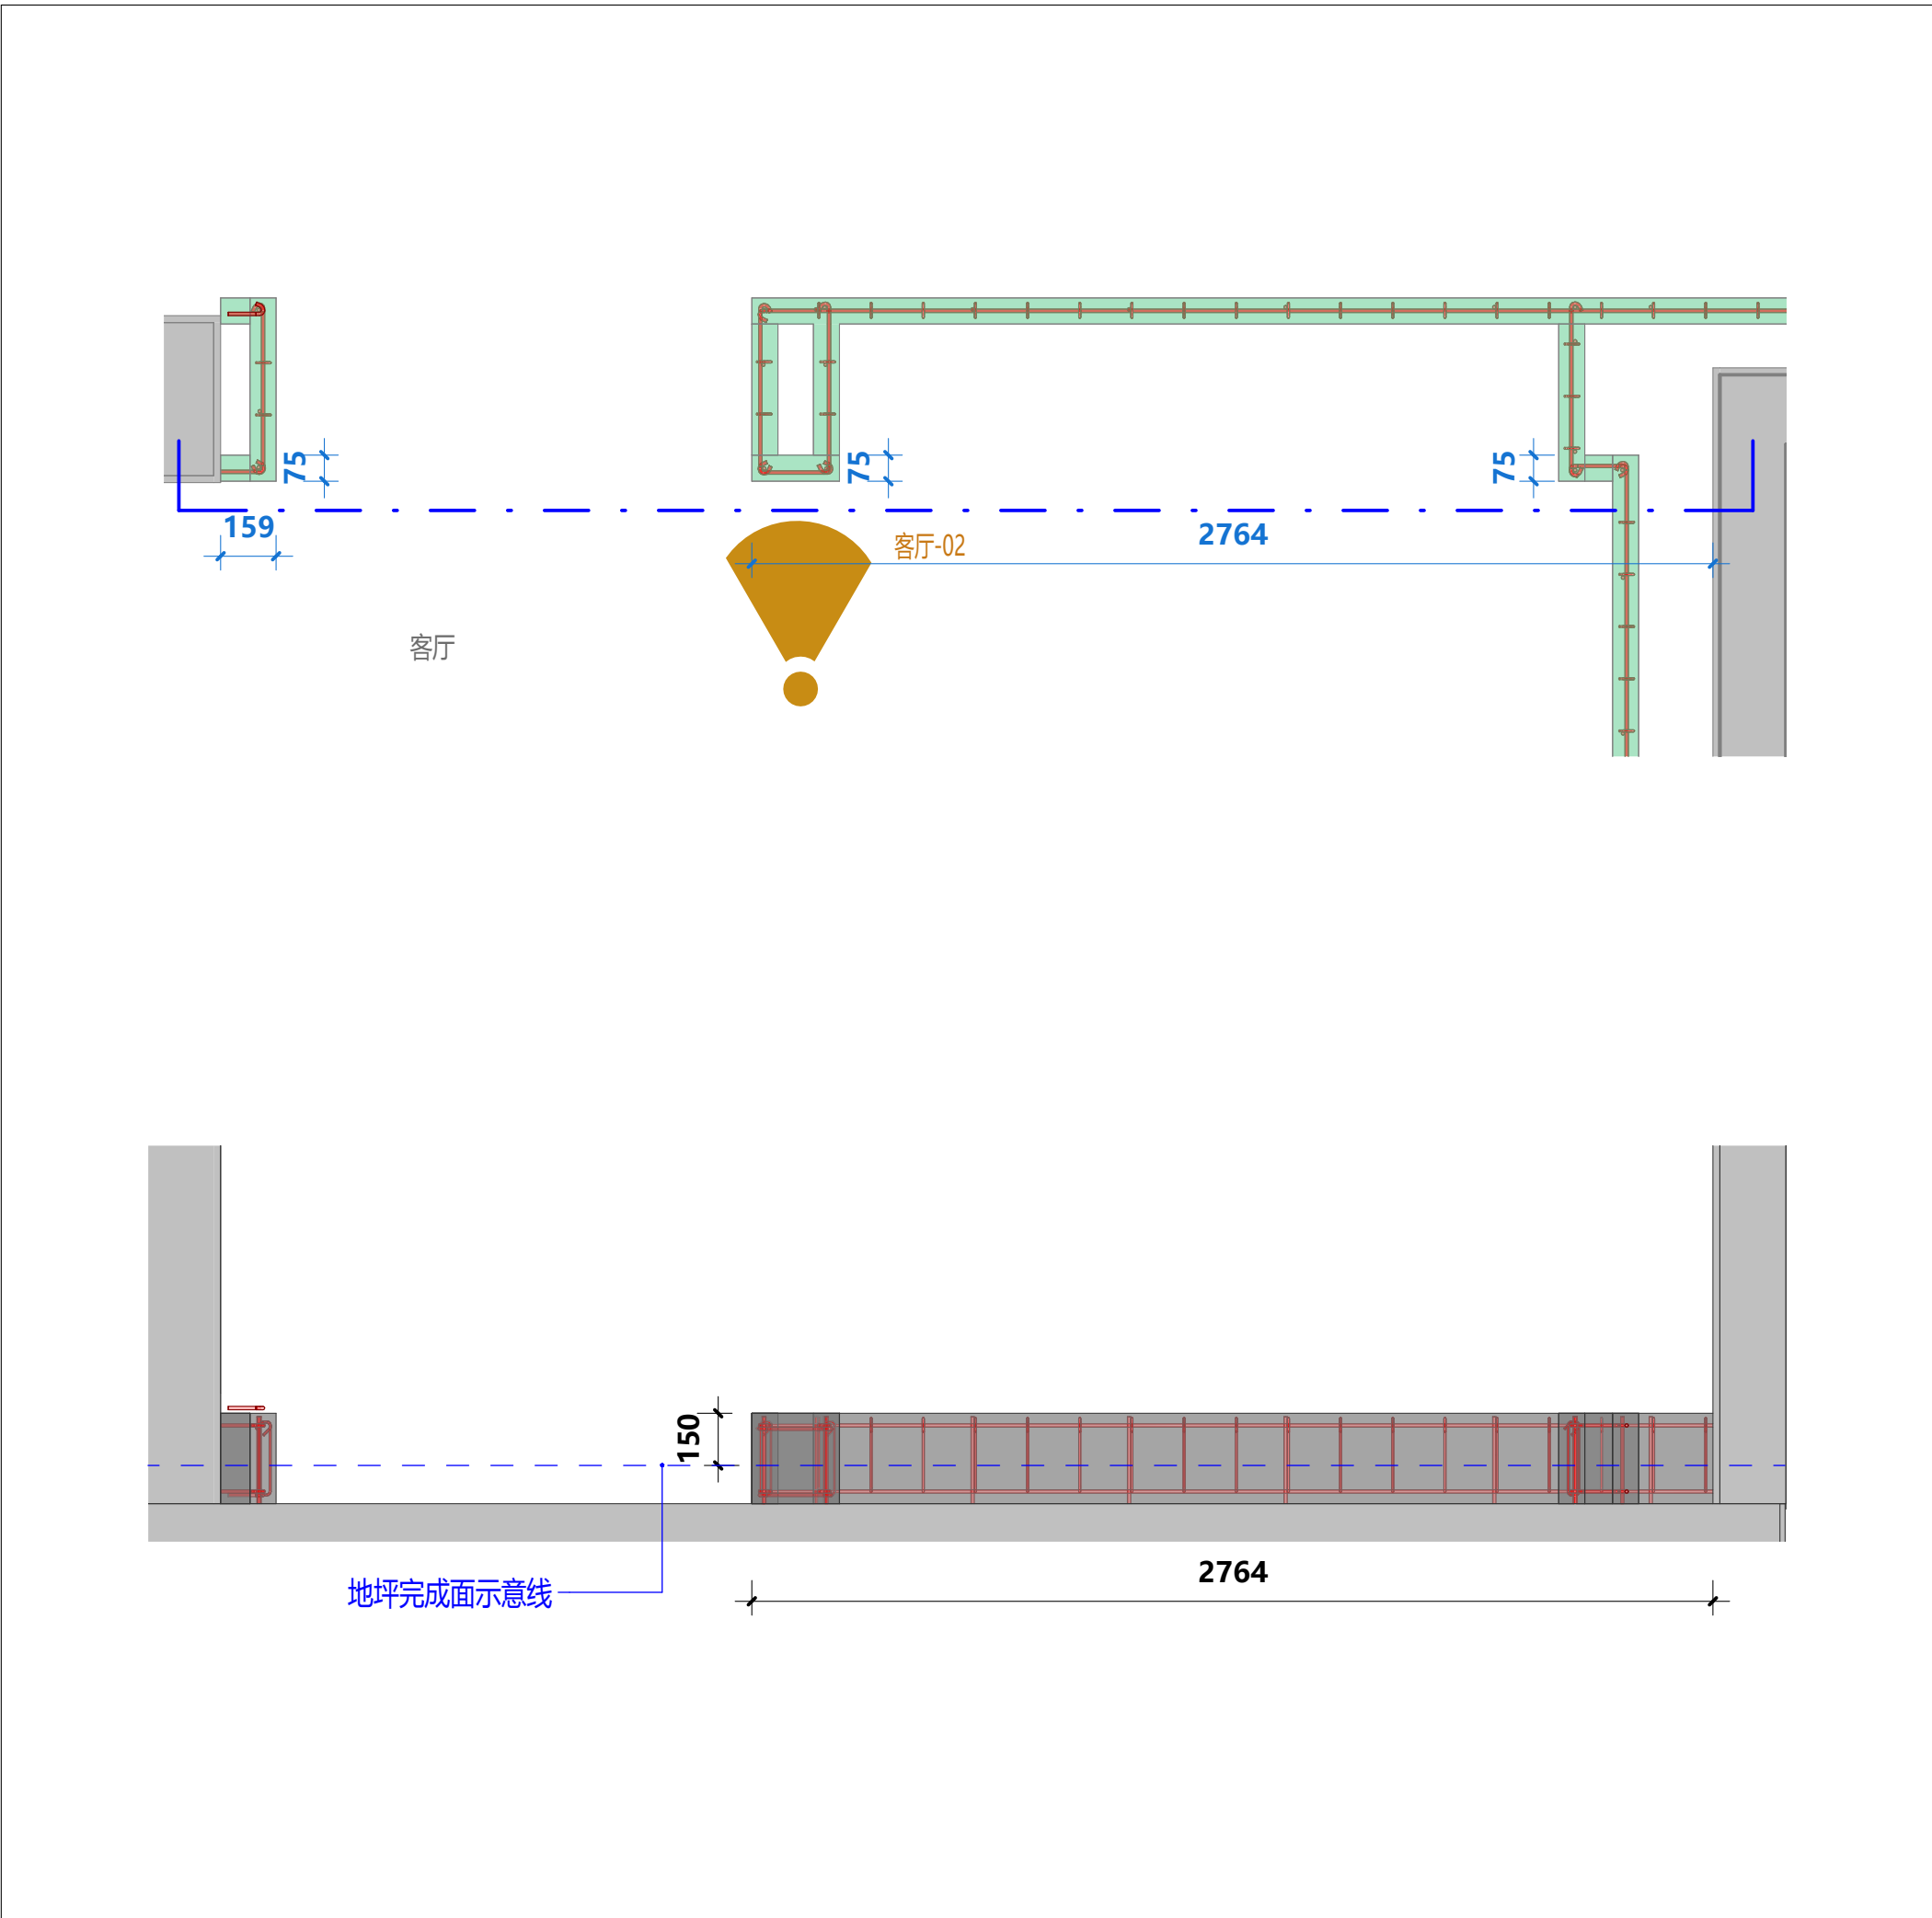

1 客厅-01 1F客厅混凝土导墙、构造柱钢筋立面图1 Scale比例 1:20@A2

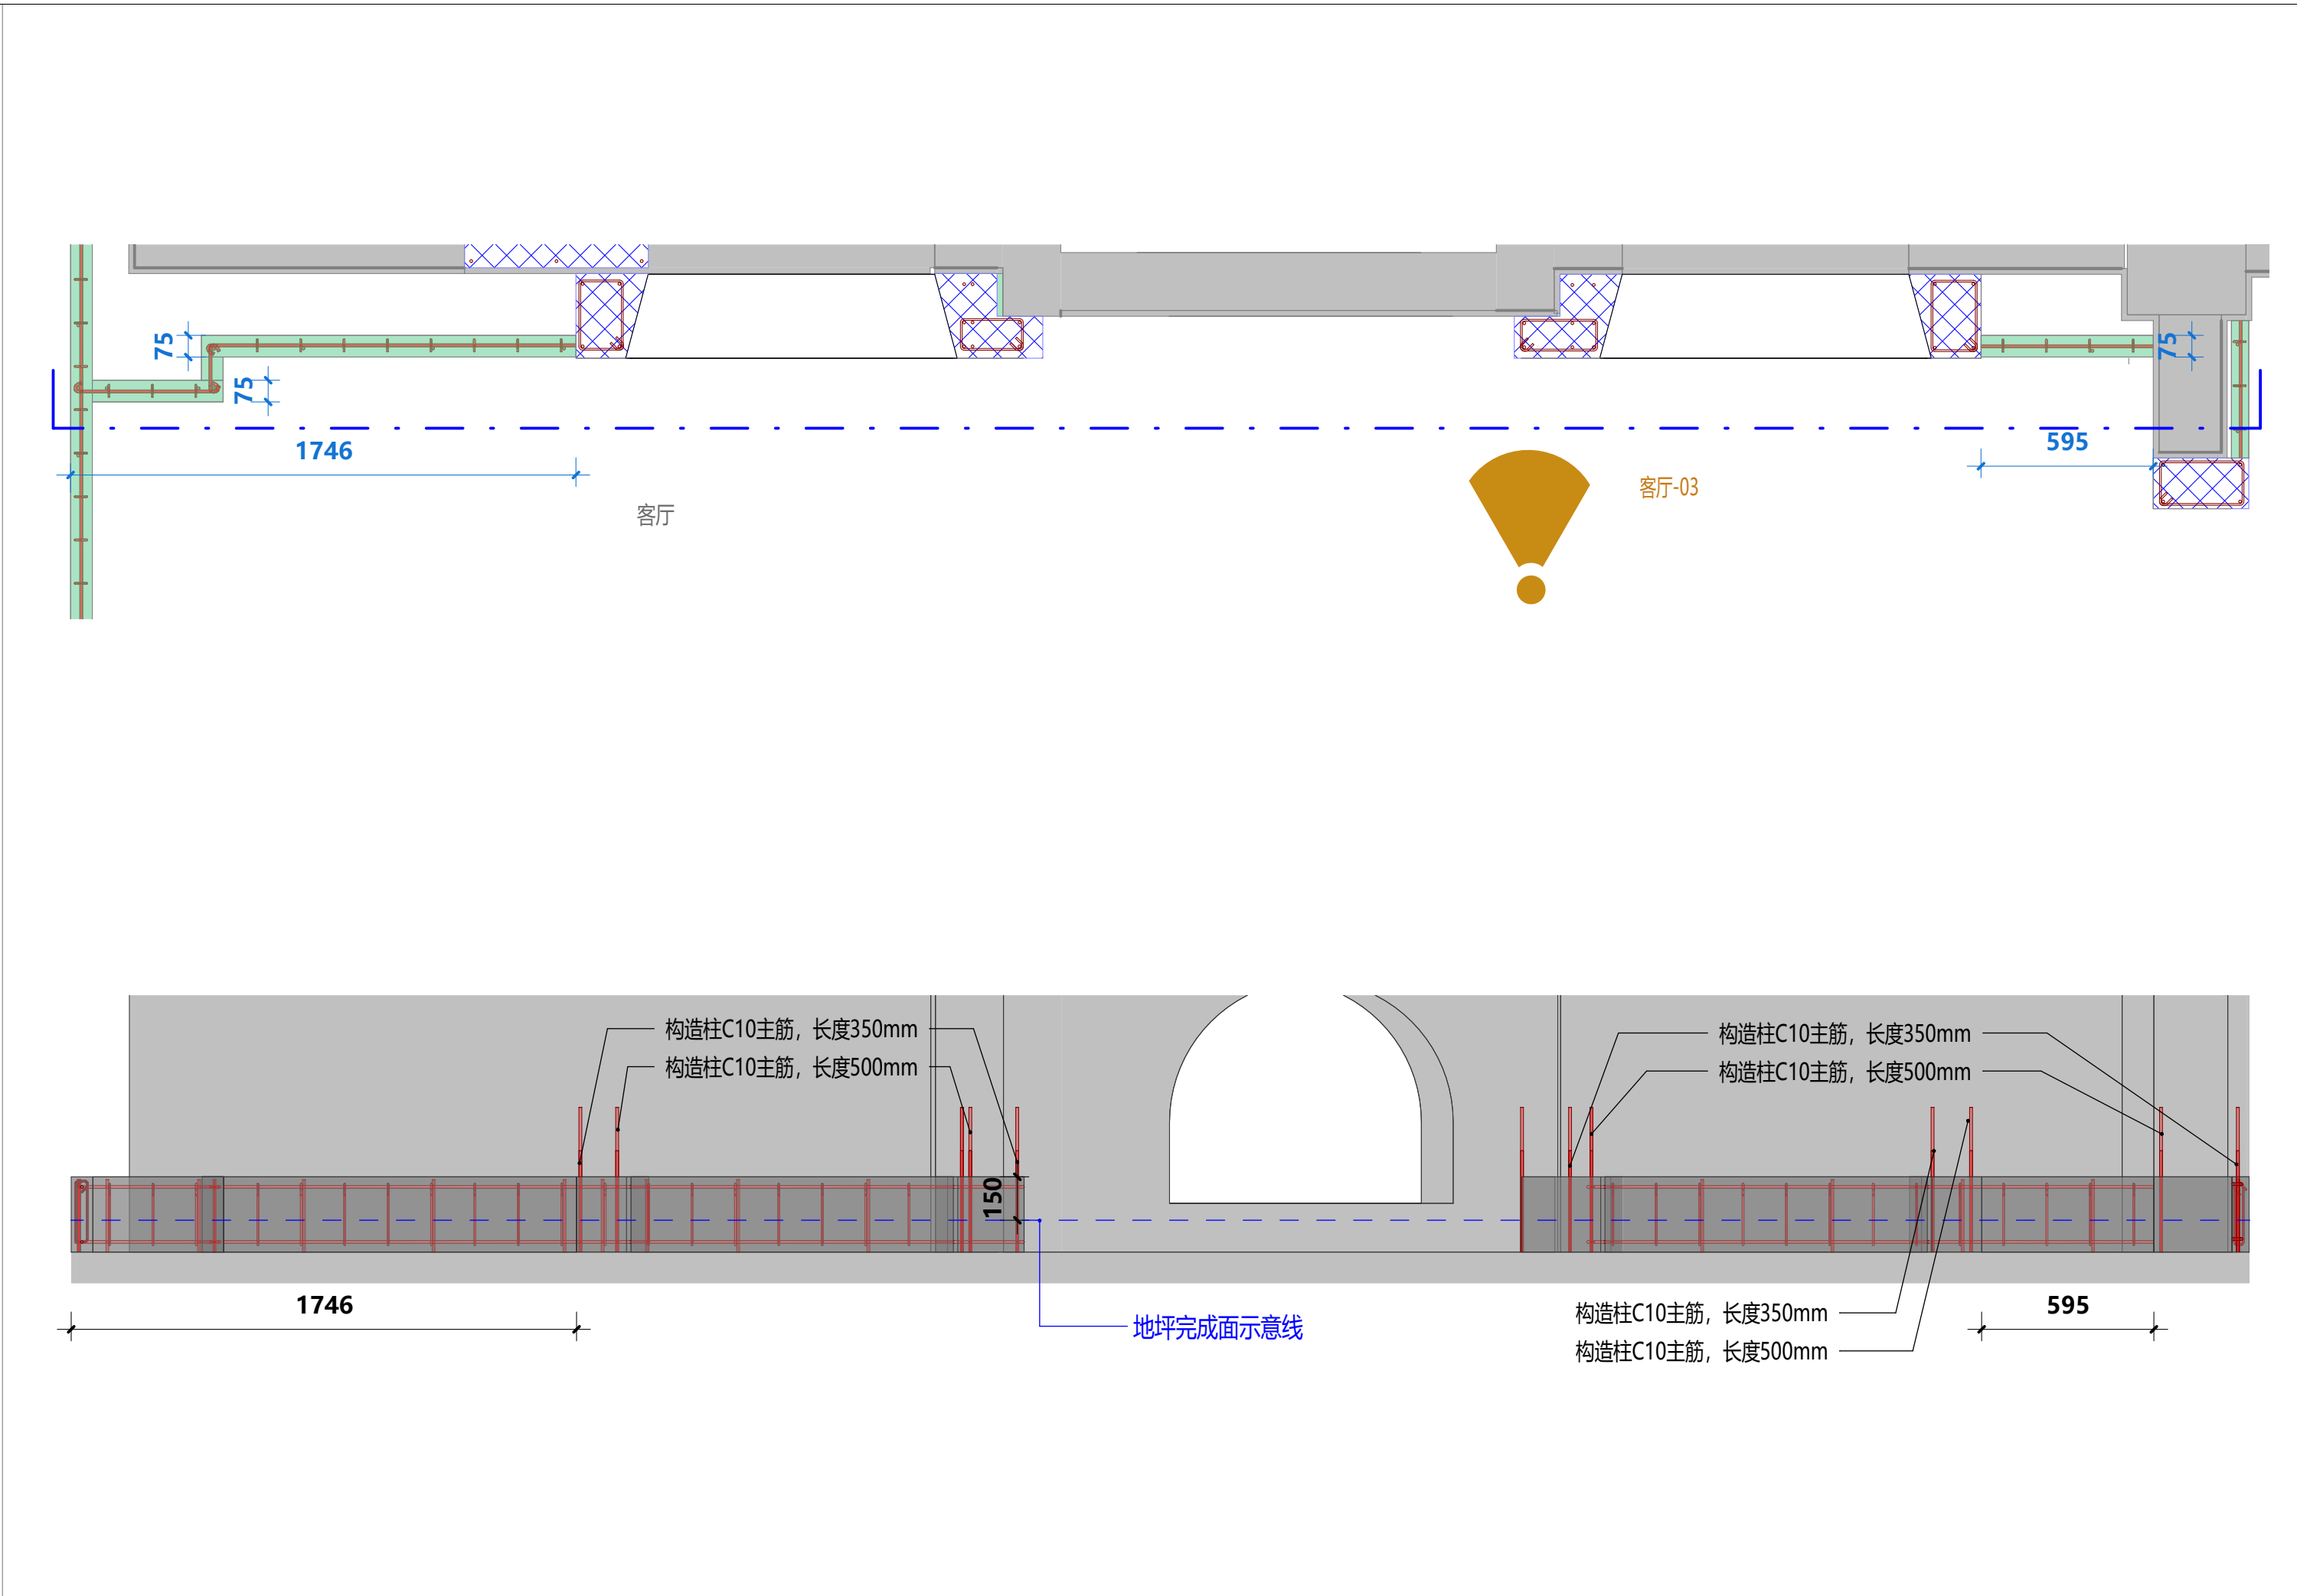

2 客厅-02 1F客厅混凝土导墙、构造柱钢筋立面图2 Scale比例 1:20@A2

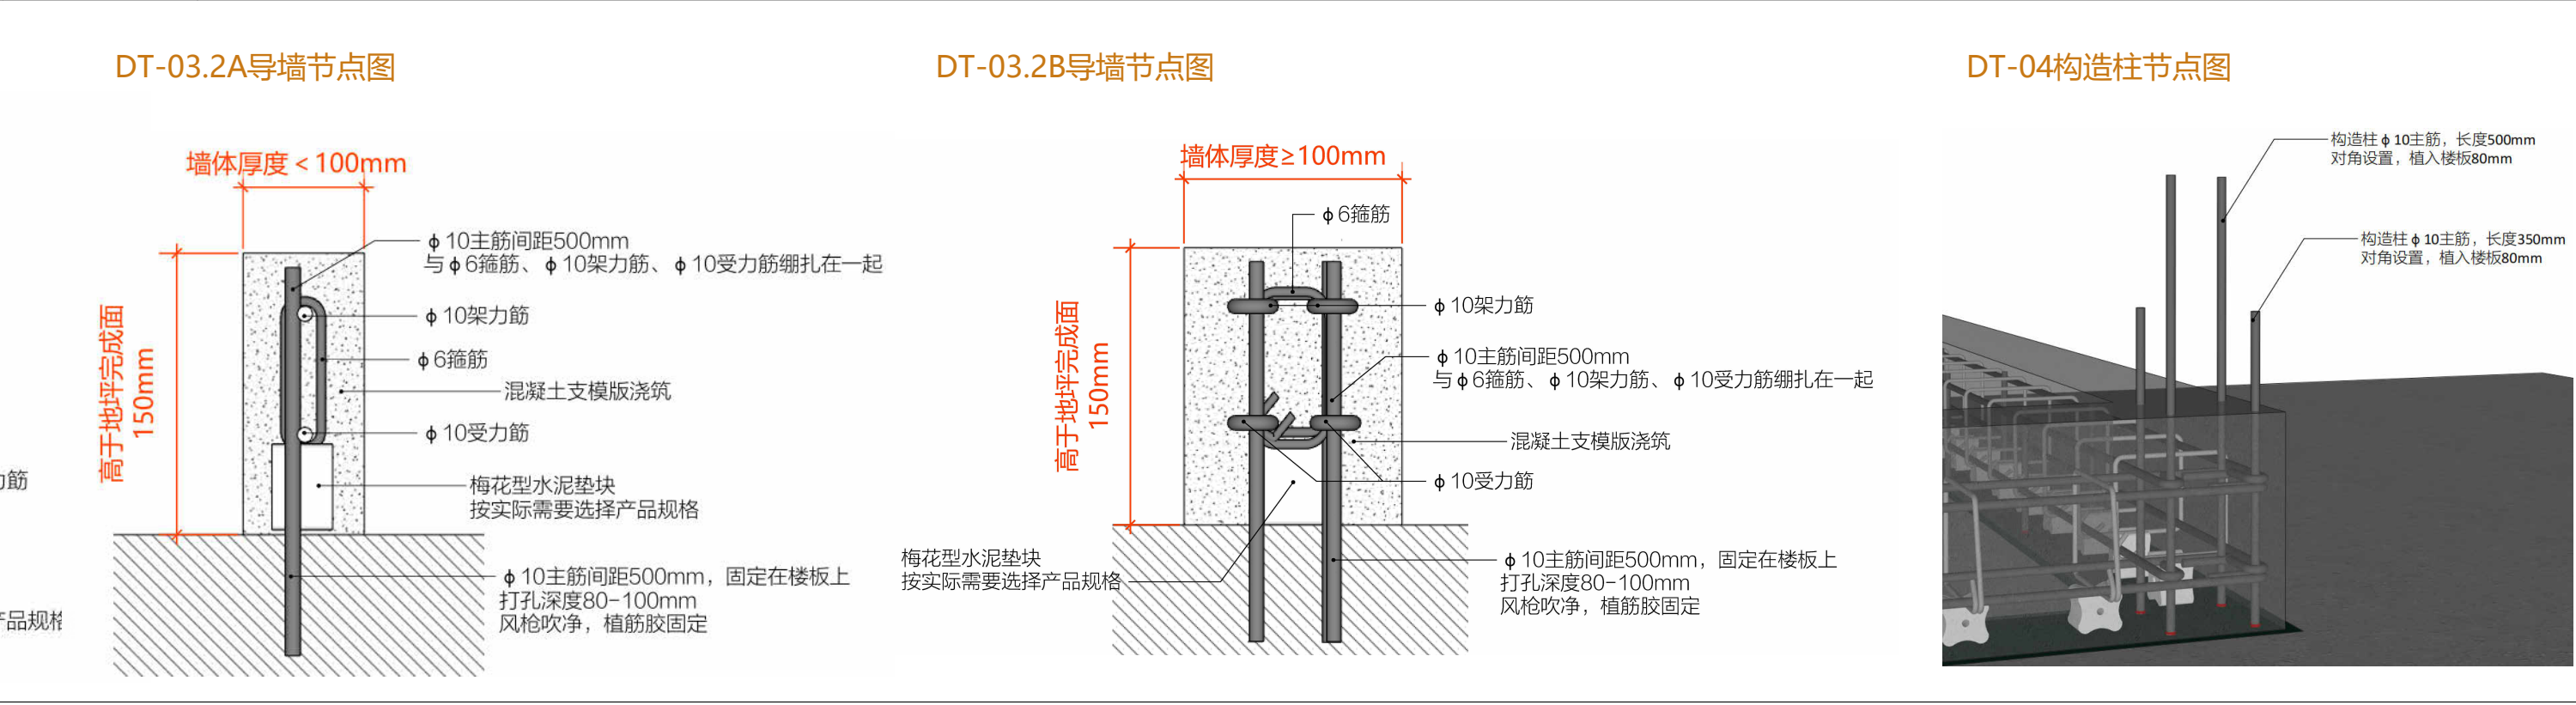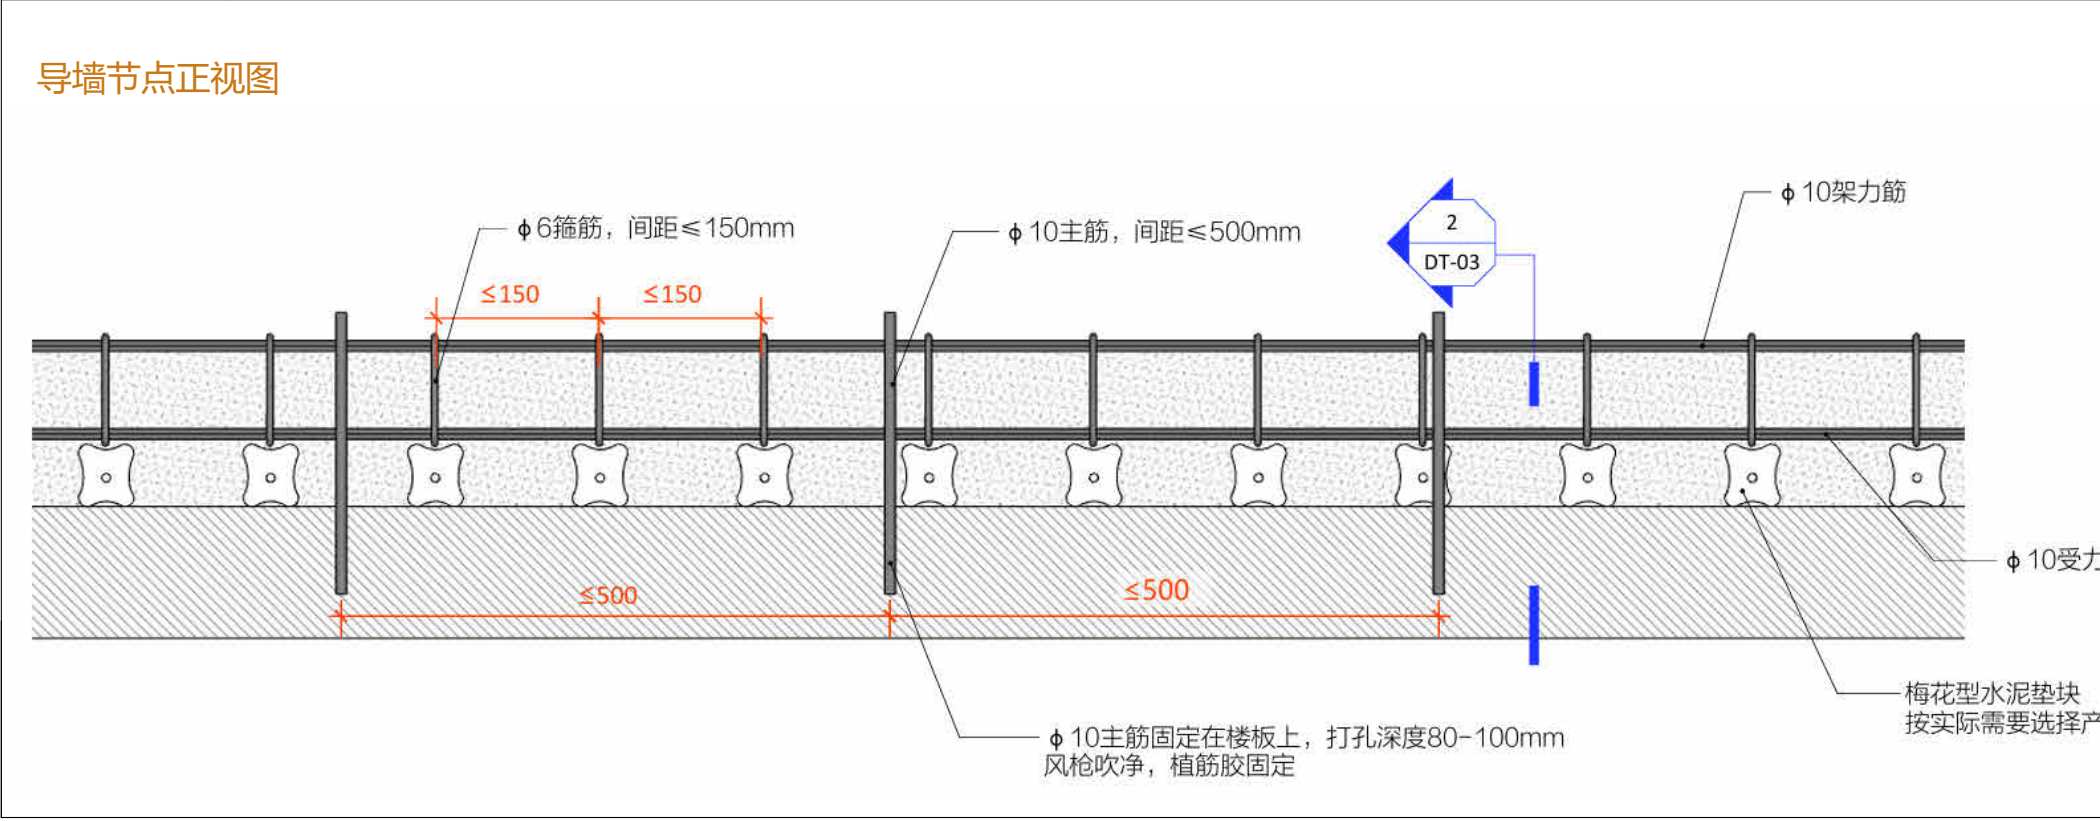

LEGEND图例

编号	图例	说明
1		原始墙、板、柱
2		混凝土导墙
3		过梁
4		构造柱
5		钢筋

盖章:

正式施工图
2026-08-06

注释
Notes

1. 本图纸如与现场尺寸有误差, 请施工人员与项目负责人联系。
2. 施工前施工人员应认真查阅此图, 如有不明确尺寸, 按现场测量为准。
3. 本图纸必须经甲乙双方认可并签字方可作为施工依据。

日期
Date

08/01/26

修订
Revision

项目
Project

巨鹿路880号

图纸名称
Drawing Name.

1F客厅导墙钢筋立面

比例
Scale

1:20@A2

图纸编号
Drawing No.

1F.NW.PL-02.4

项目编号
Project No.

© 2026

LEGEND图例

编号	图例	说明
1		原始墙、板、柱
2		混凝土导墙
3		过梁
4		构造柱
5		钢筋

盖章:

正式施工图
2026-08-06

注释

Notes

- 1.本图纸如与现场尺寸有誤，請施工人員與項目負責人联系。
- 2.施工前施工人員應認真阅此圖，如有不明確尺寸，按現場測量為準。
- 3.本图紙必須經甲乙雙方認可并簽字方可作为施工依据。

日期

Date

08/01/26

修订

Revision

1

项目

Project

巨鹿路880号

图纸名称

Drawing Name.

1F餐厅导墙钢筋立面

比例

Scale

1:20@A2

图纸编号



Drawing No.

1F.NW.PL-02.5

项目编号

Project No.


© 2026

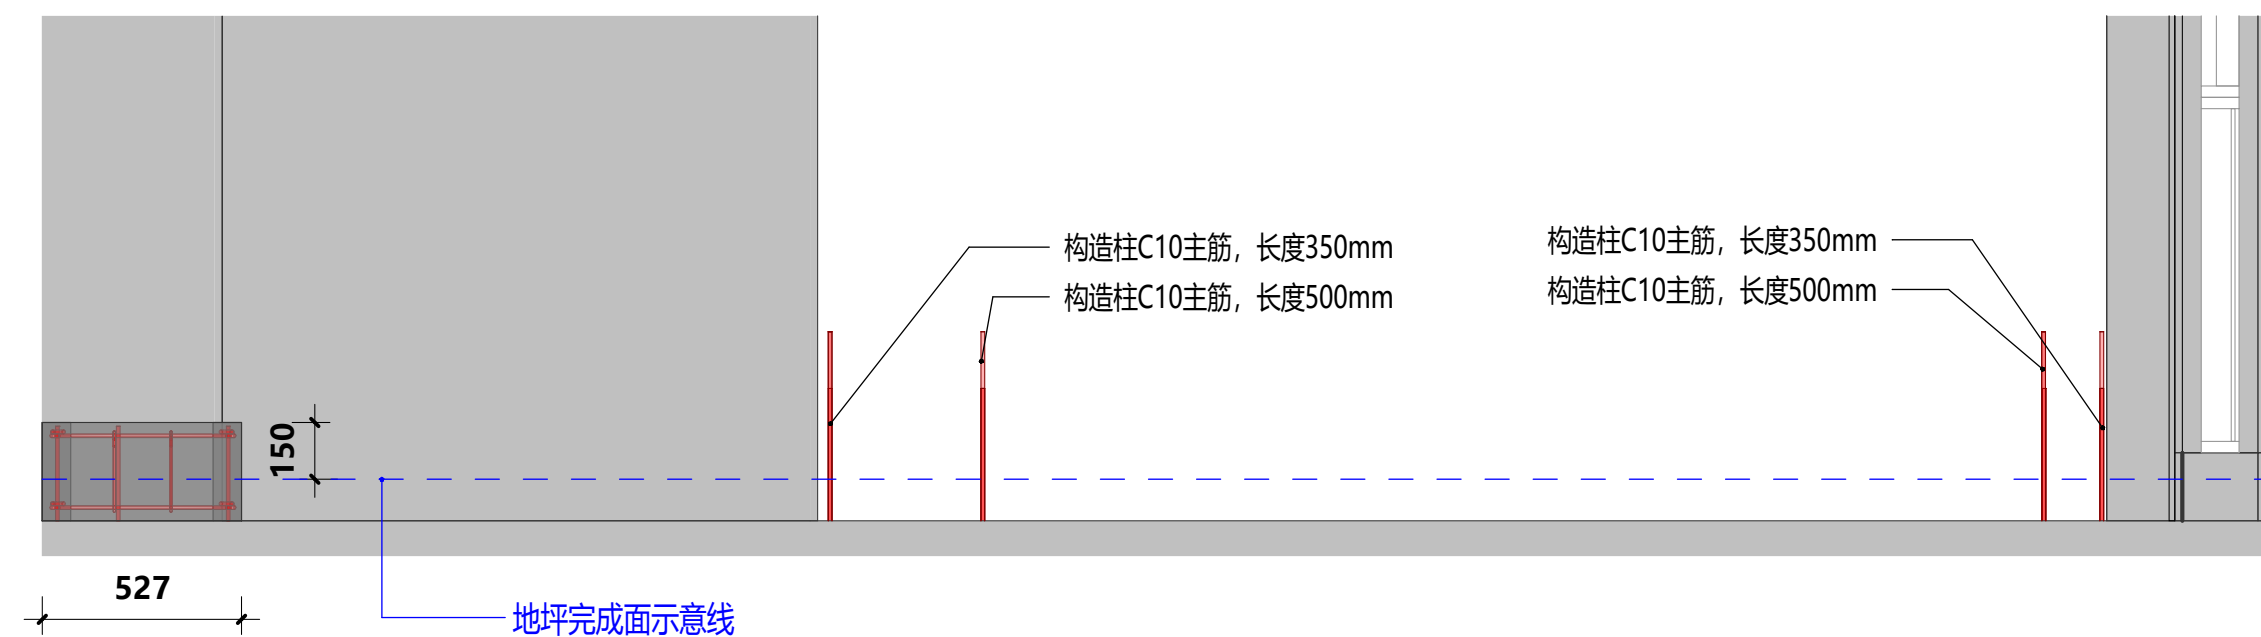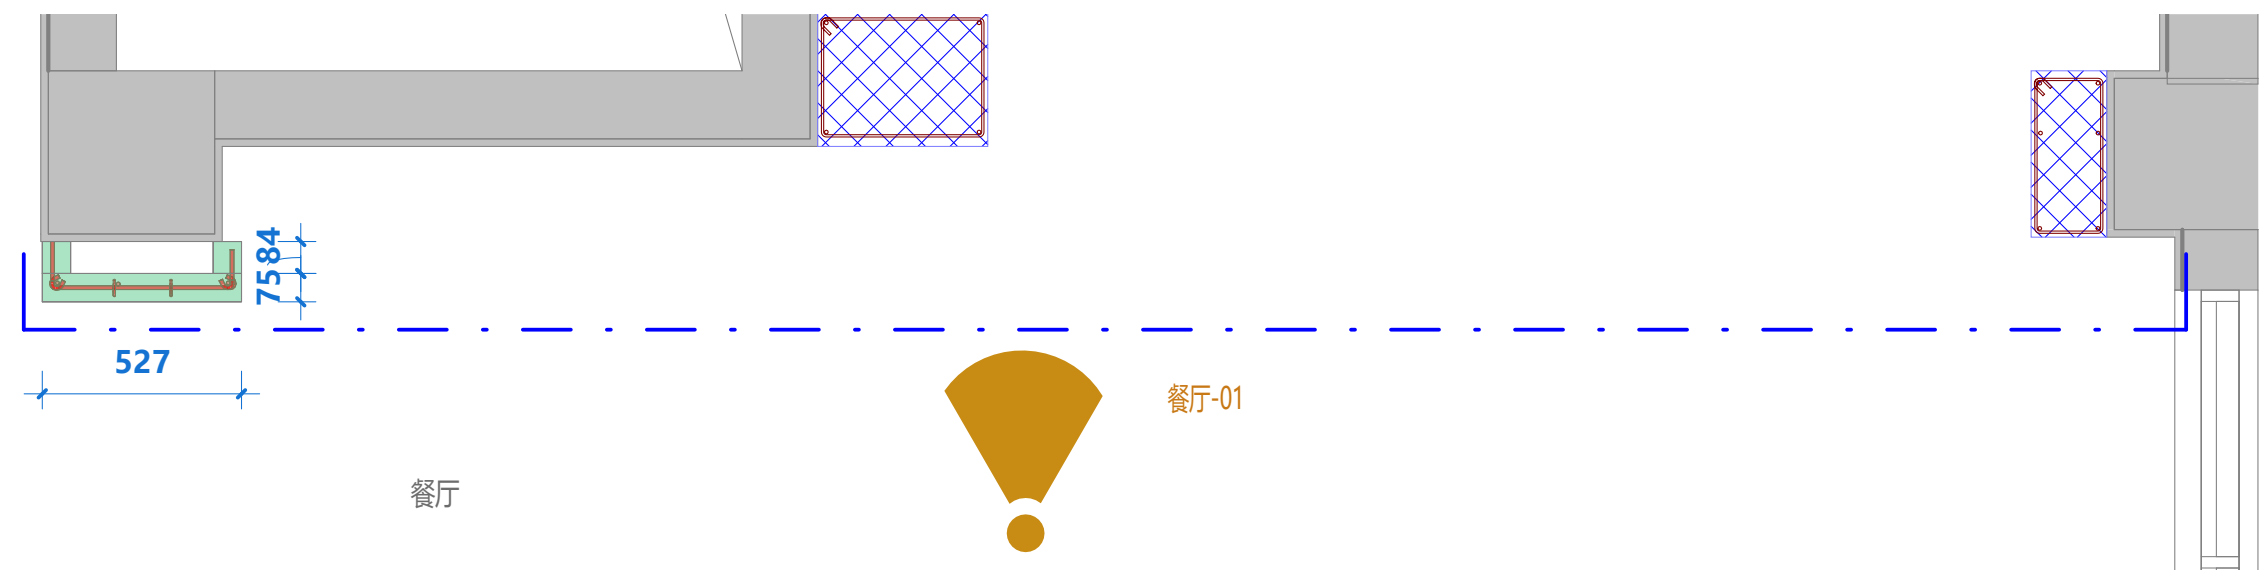


1F餐厅混凝土导墙、构造柱钢筋立面图1

Scale比例 1:20@A2

导墙节点正视图

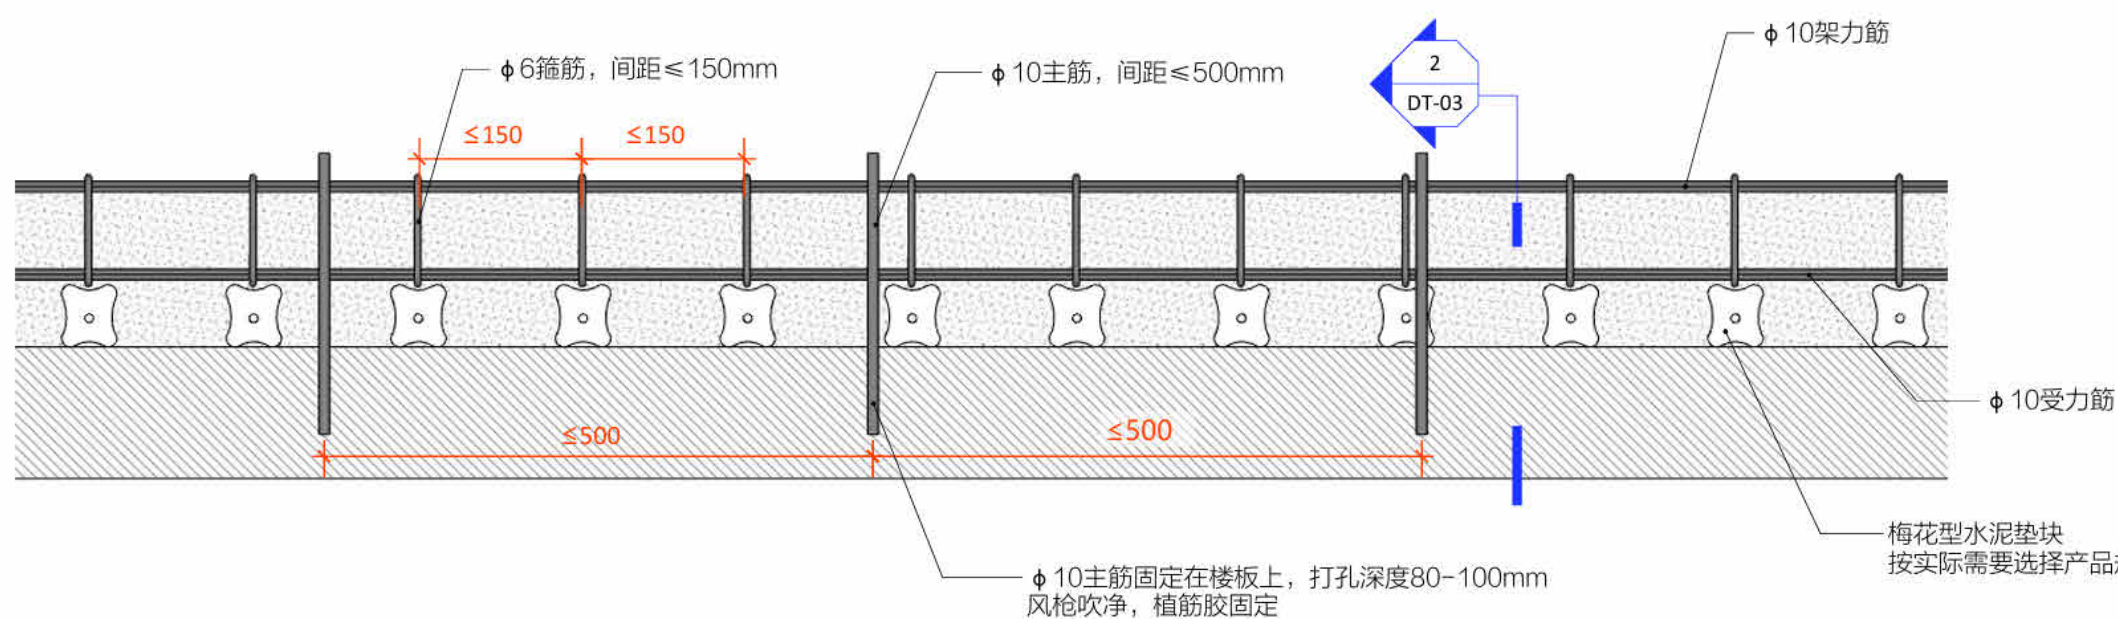


DT-03.2A导墙节点图

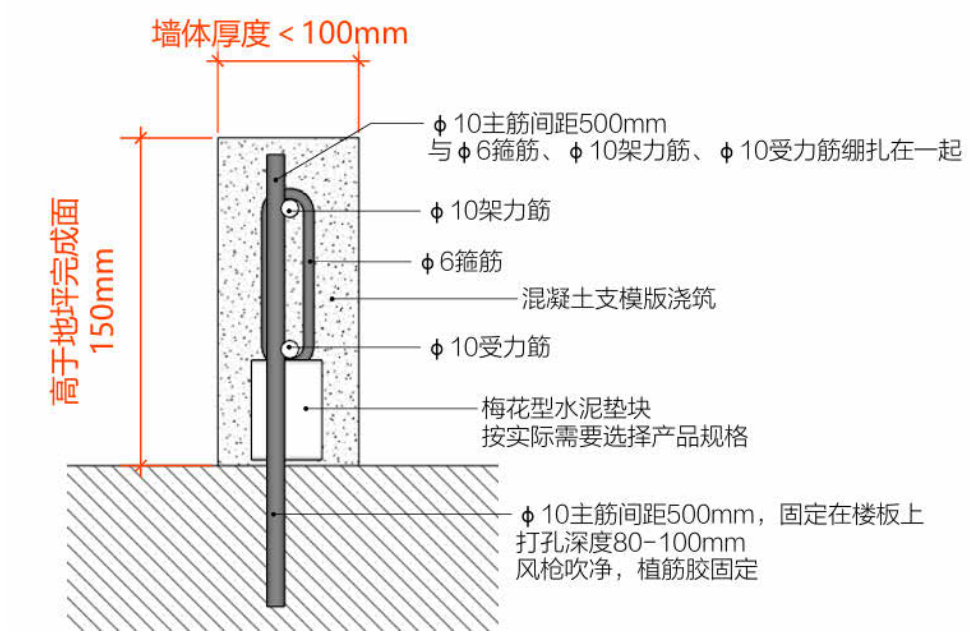

1F餐厅混凝土导墙、构造柱钢筋立面图3

Scale比例 1:20@A2


DT-03.2B导墙节点图

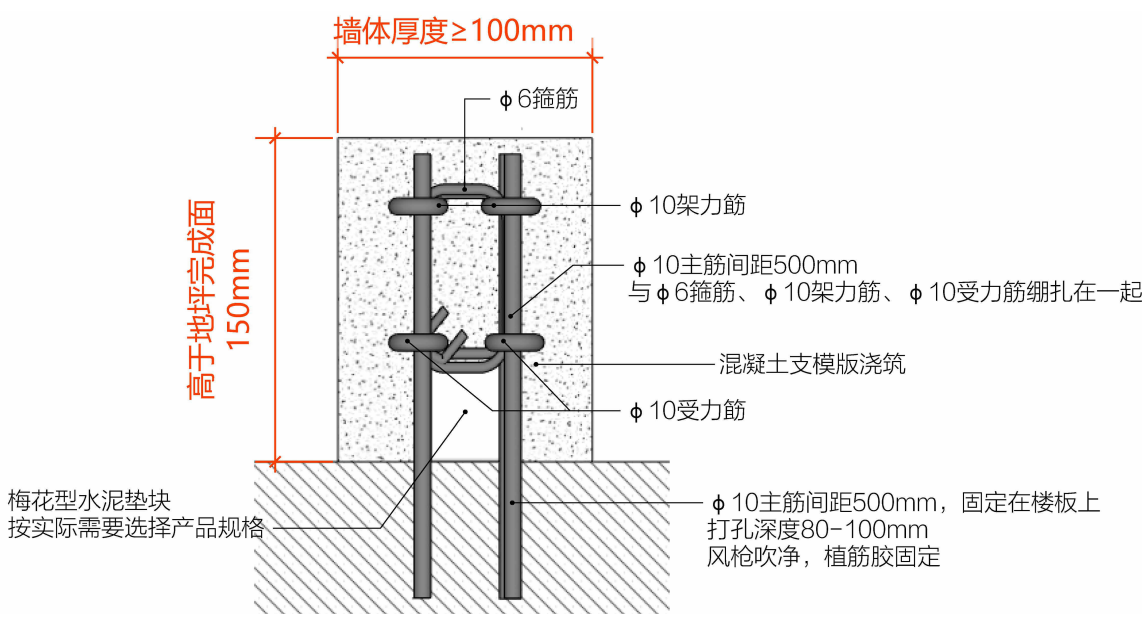


1F餐厅混凝土导墙、构造柱钢筋立面图4


Scale比例 1:20@A2

DT-04构造柱节点图




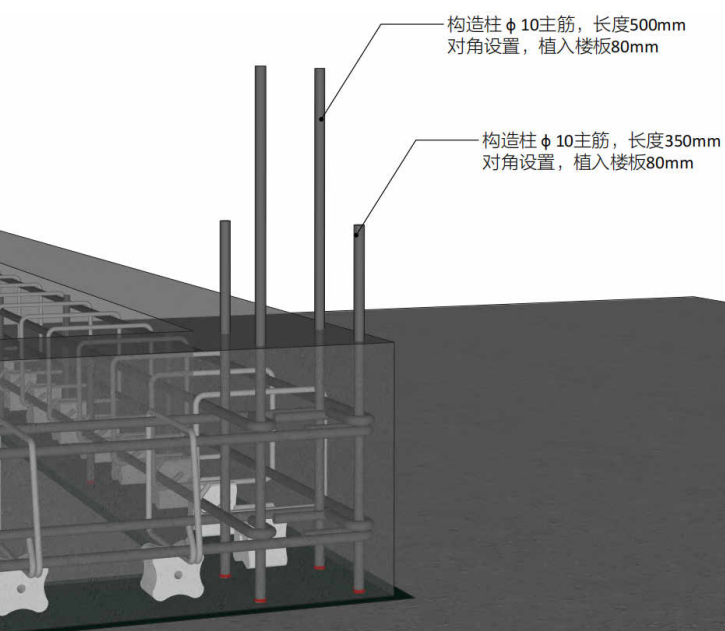


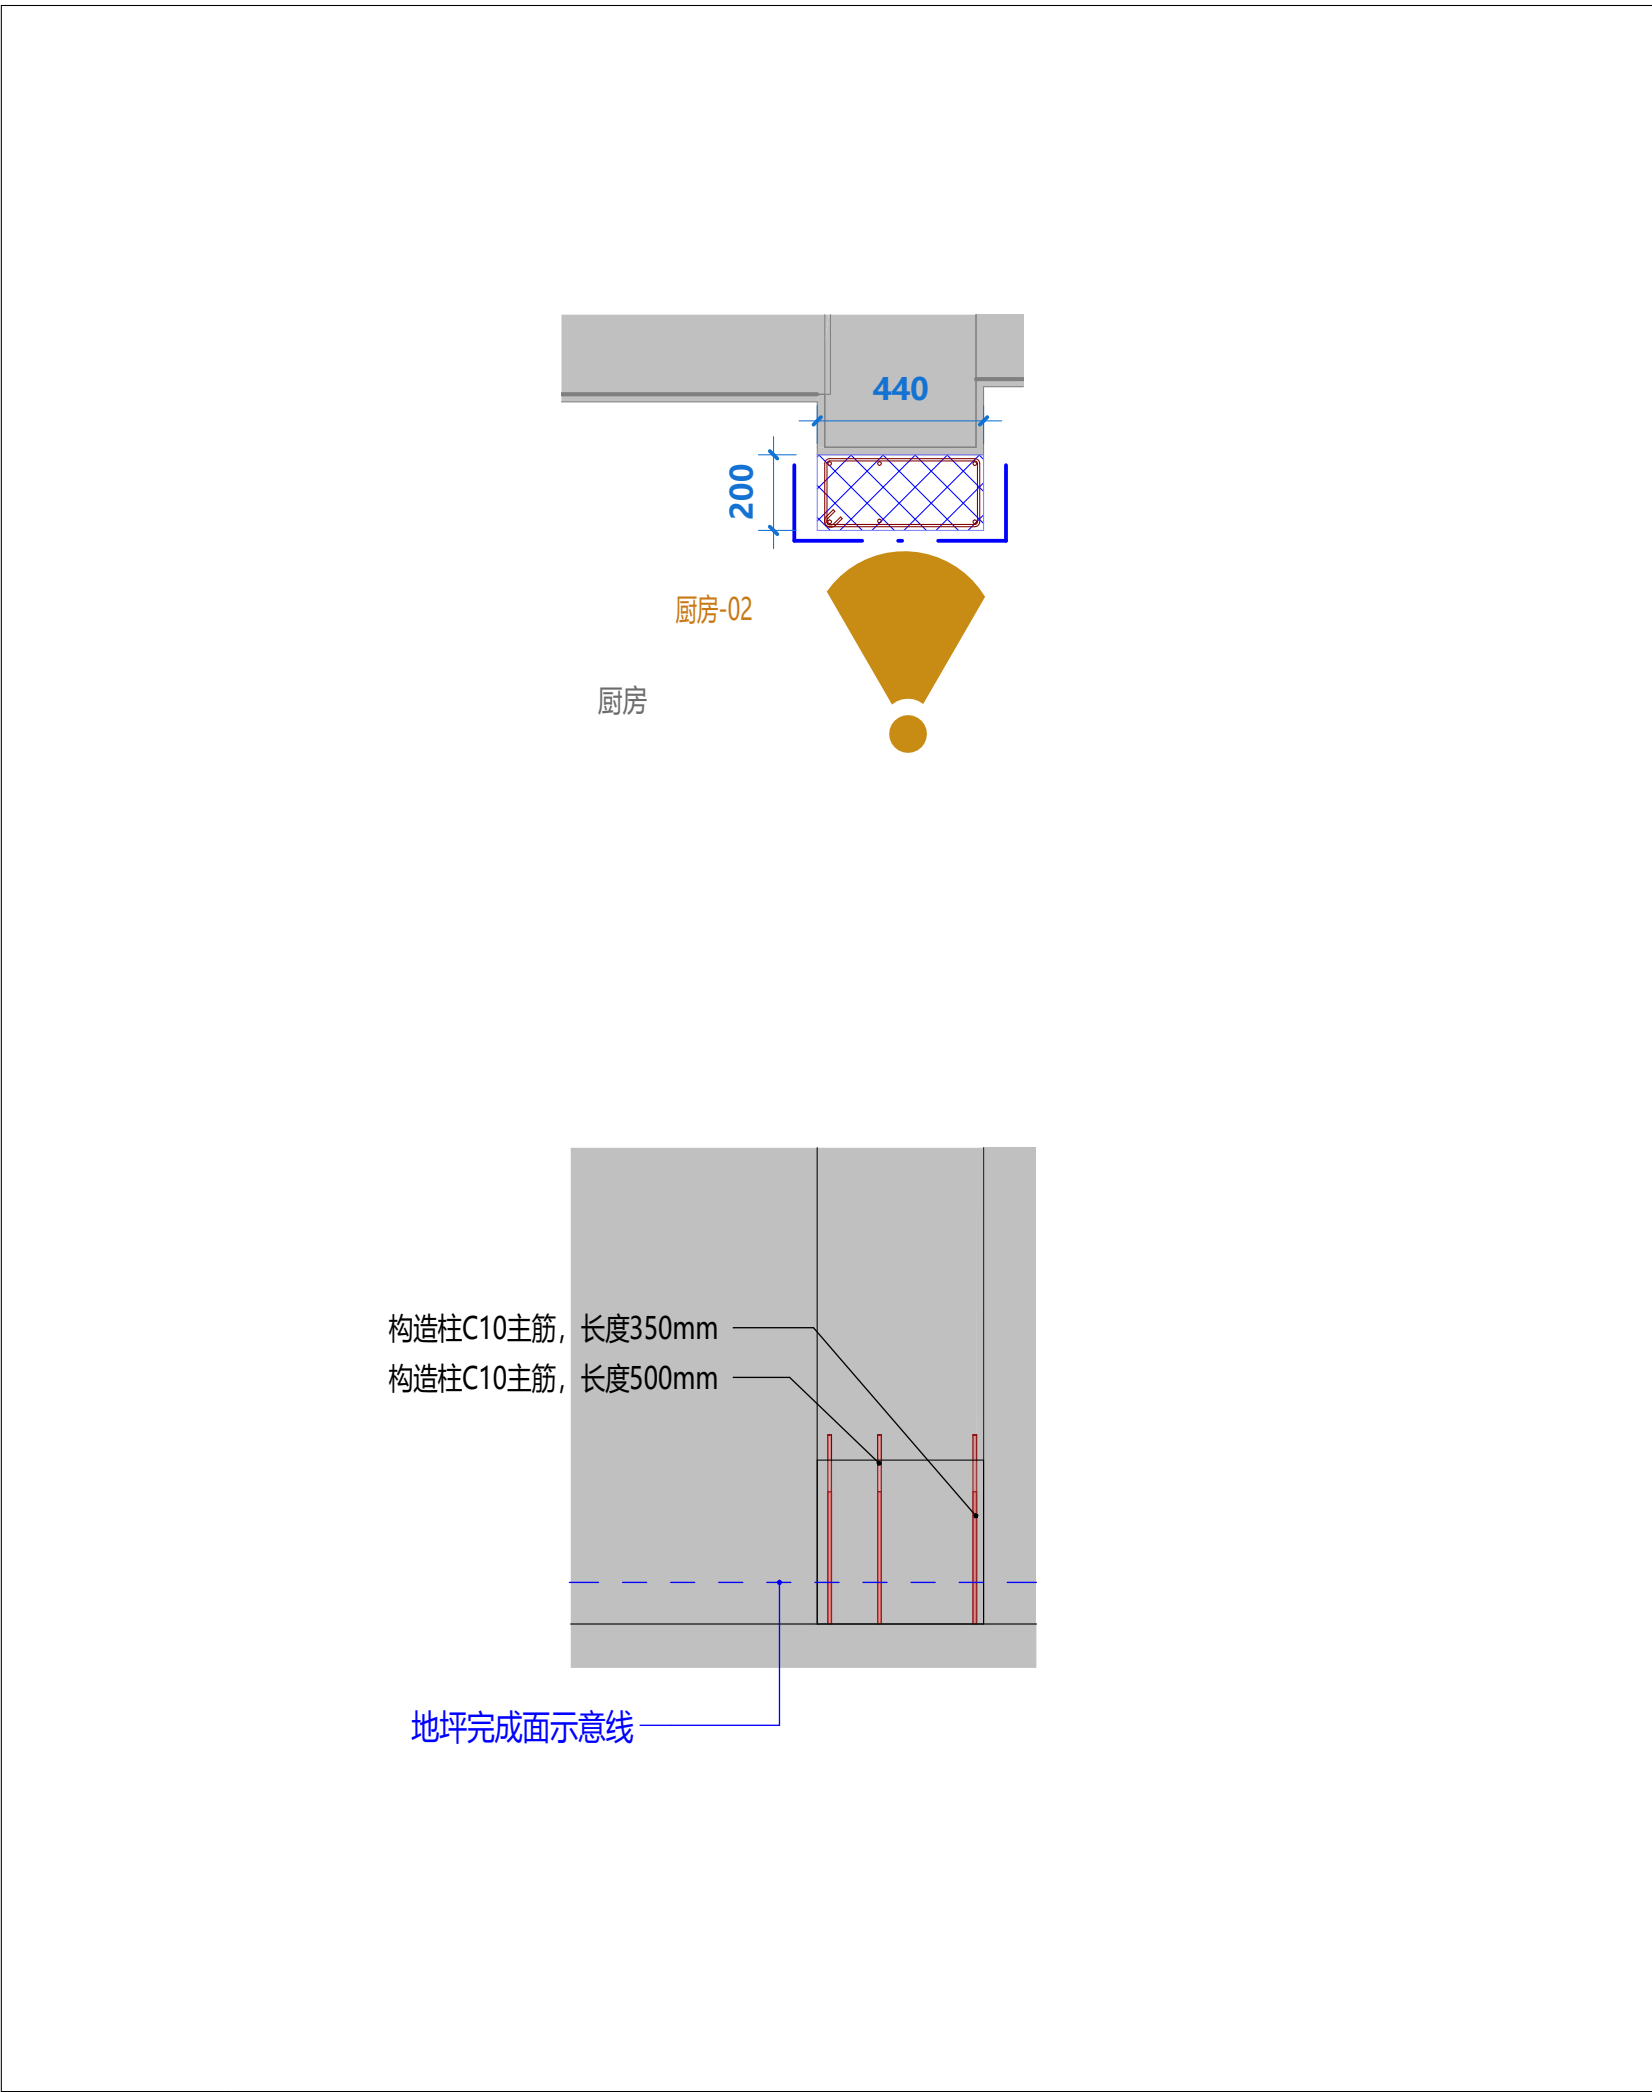

1 1F厨房混凝土导墙、构造柱钢筋立面图2
厨房-02 Scale比例 1:20@A2

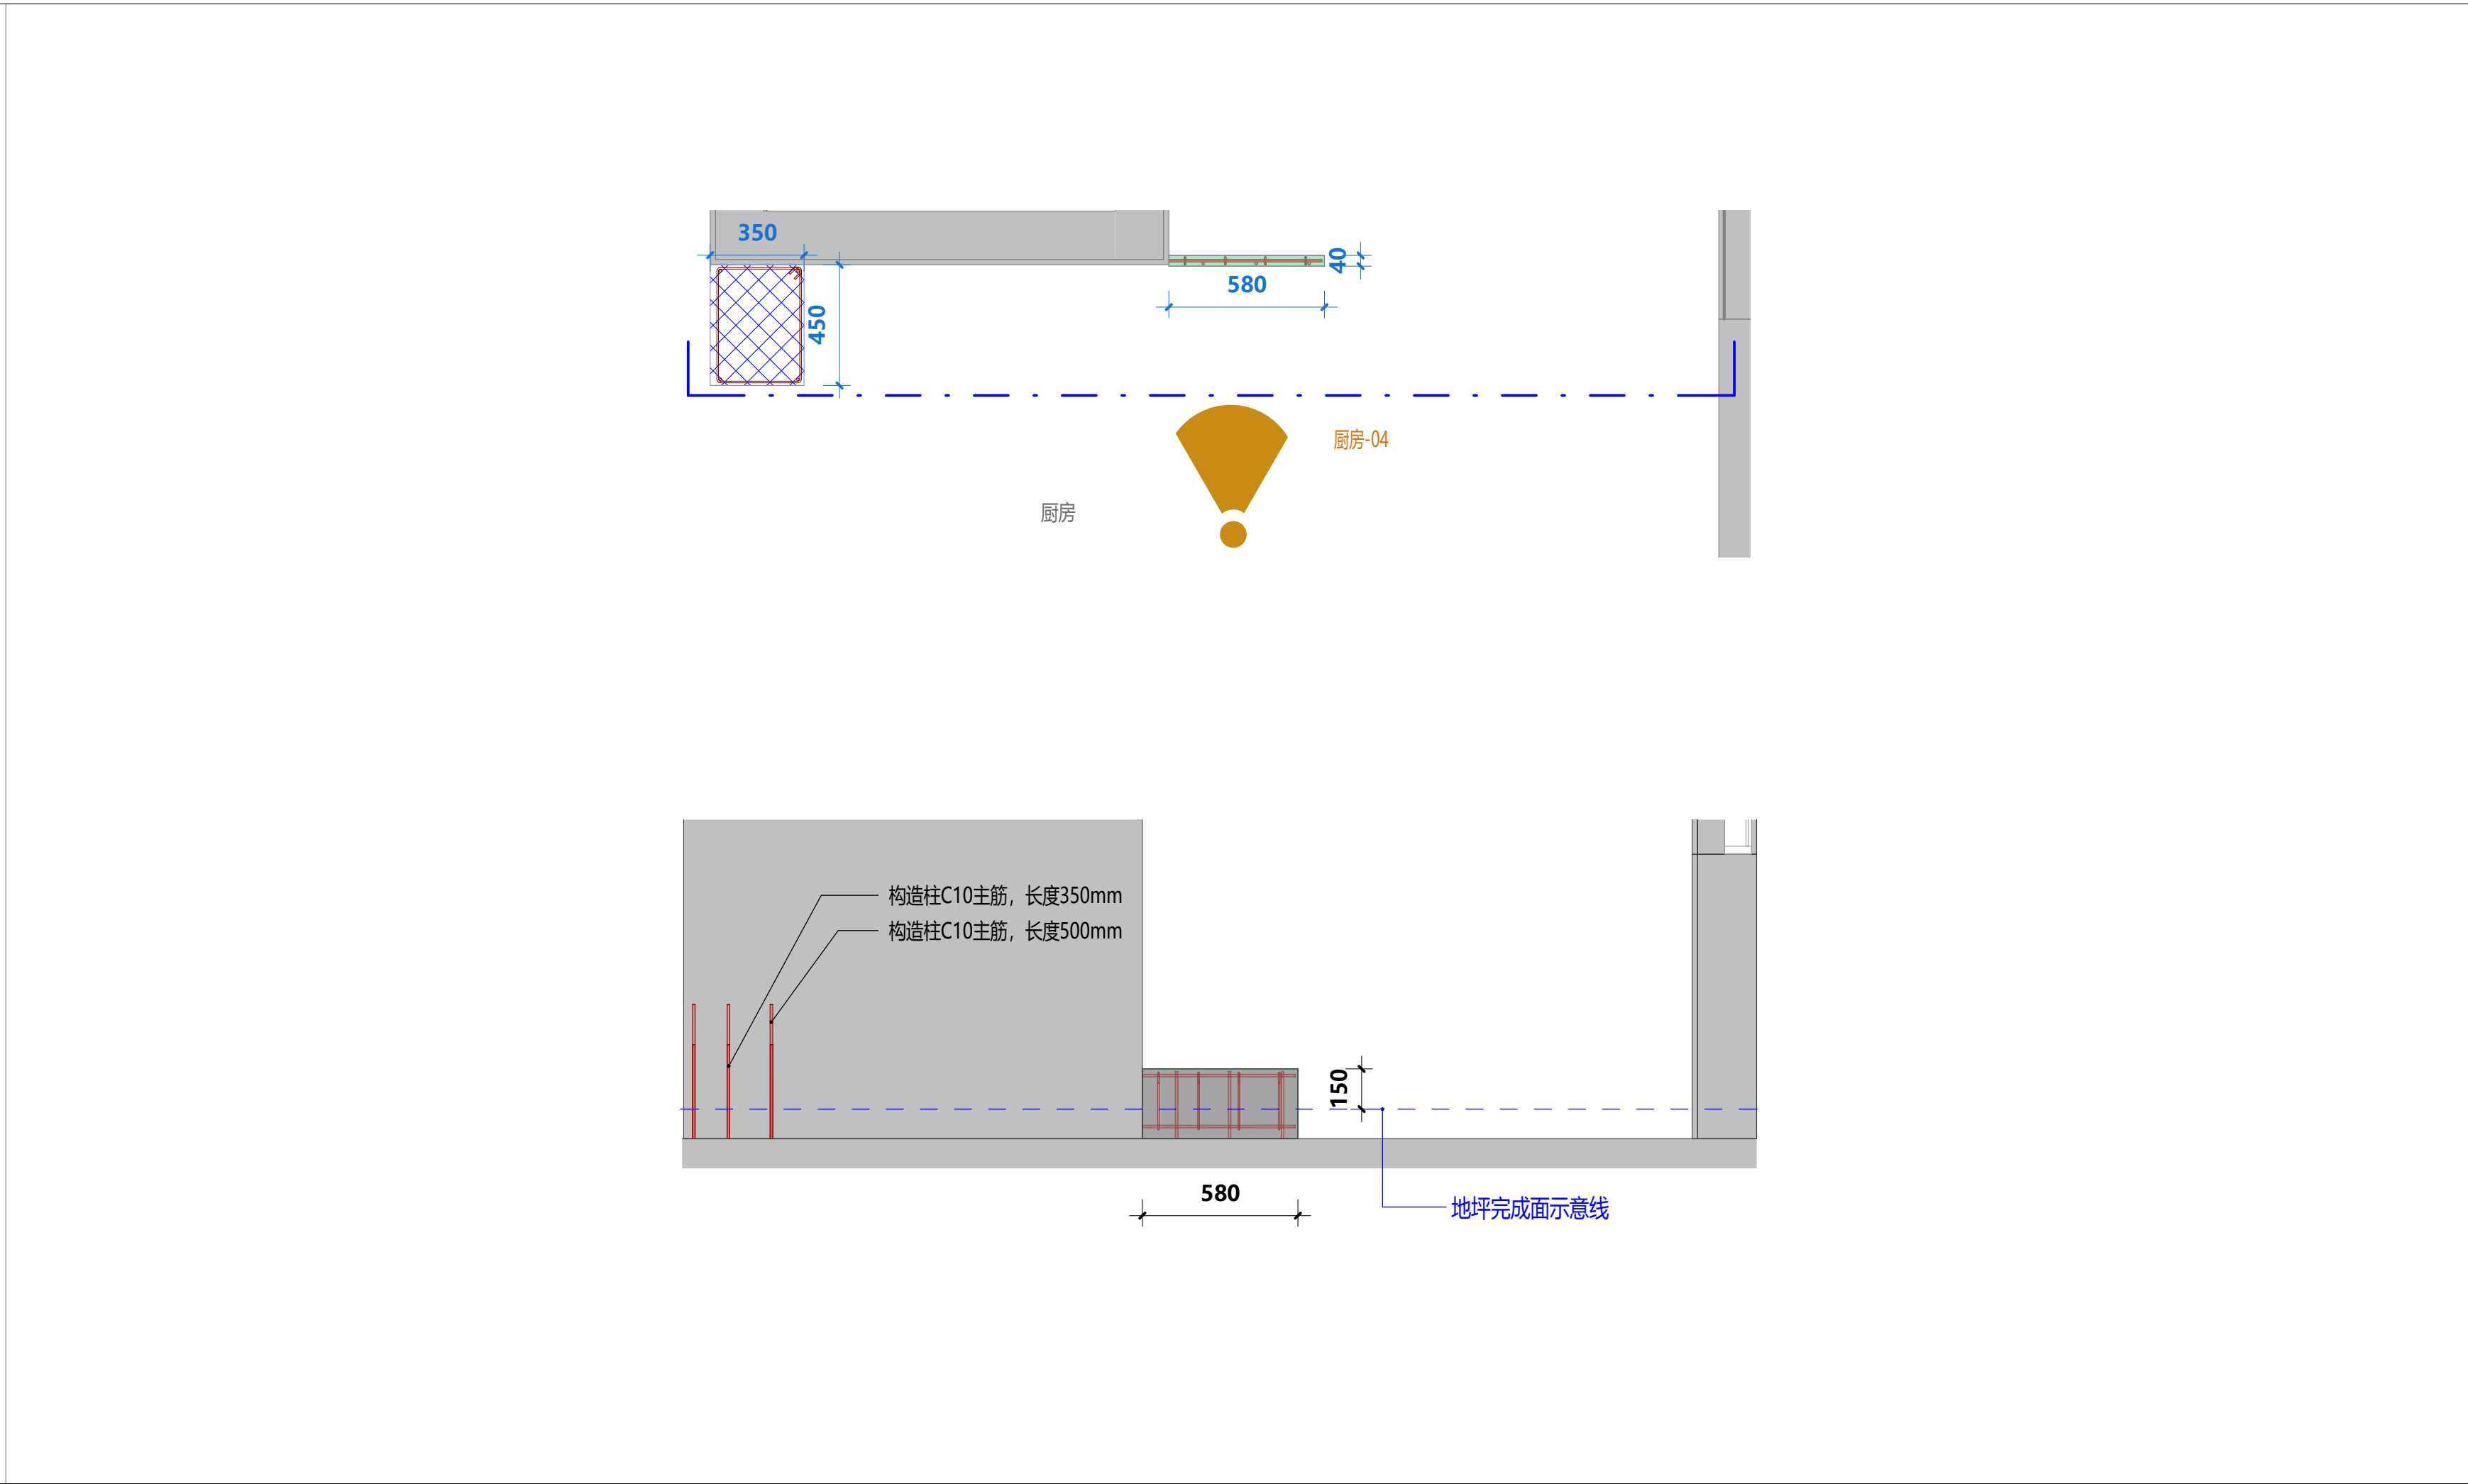

2 1F厨房混凝土导墙、构造柱钢筋立面图4
厨房-04 Scale比例 1:20@A2

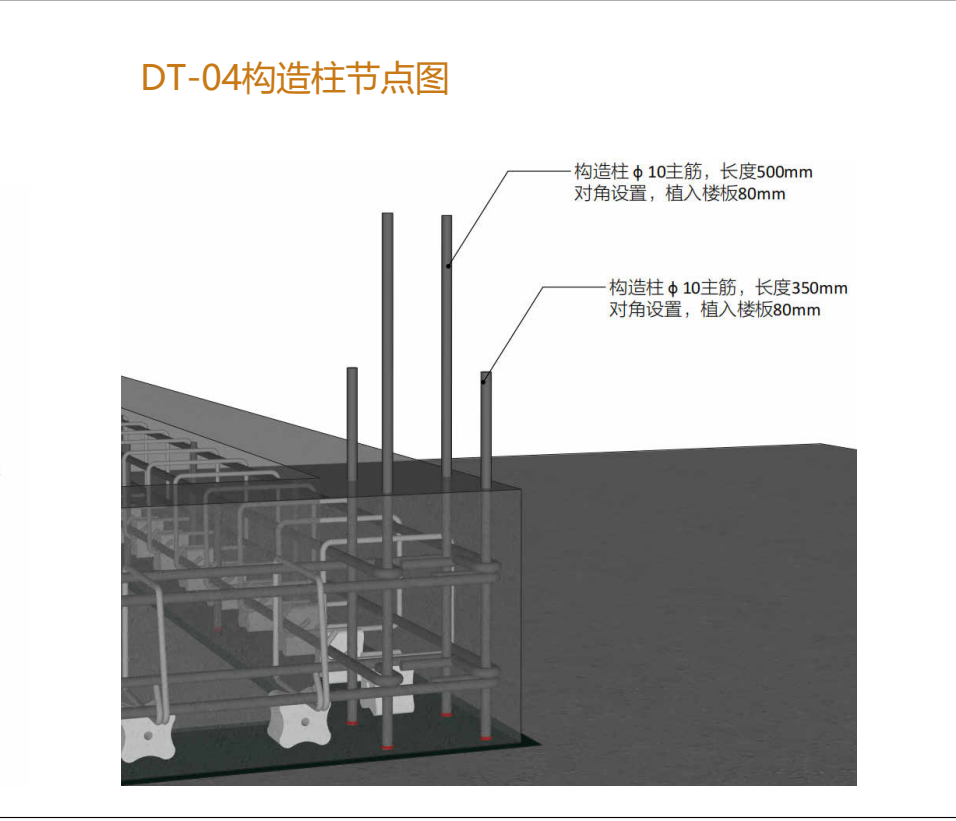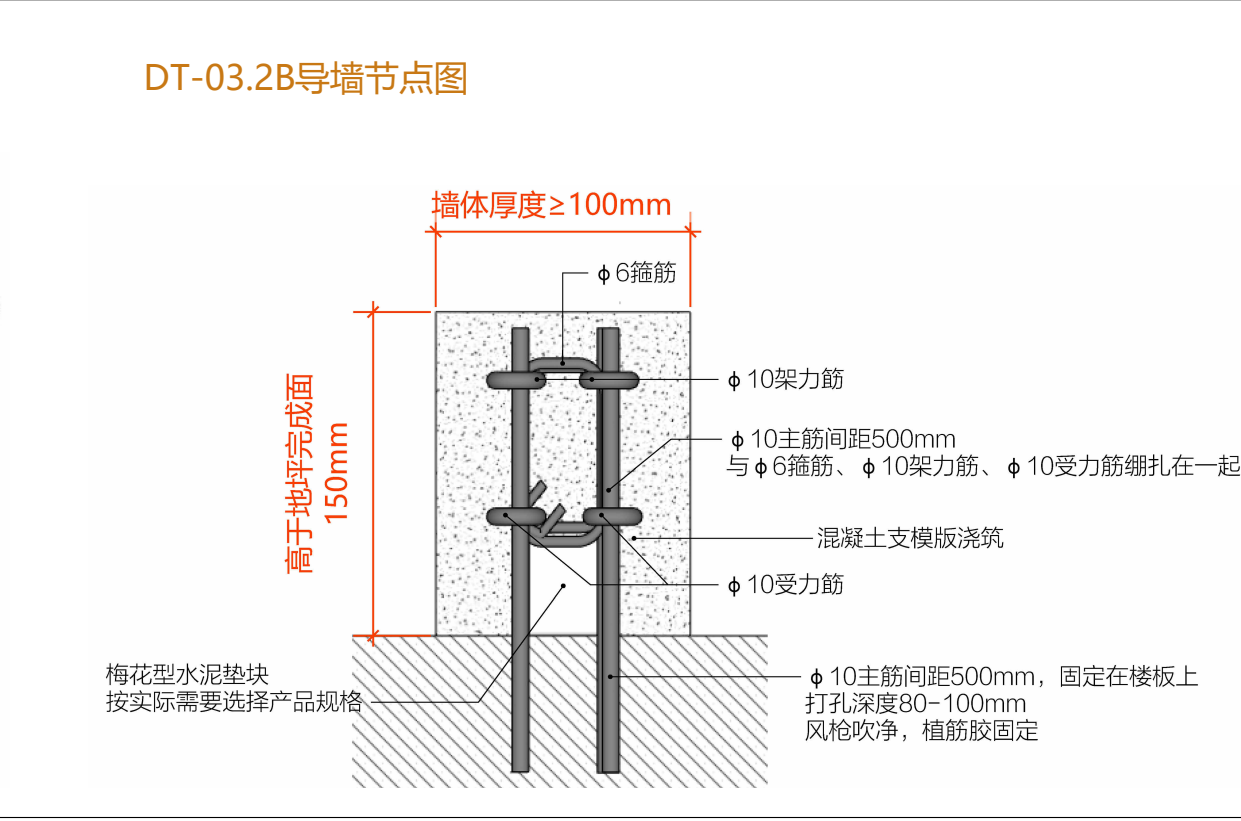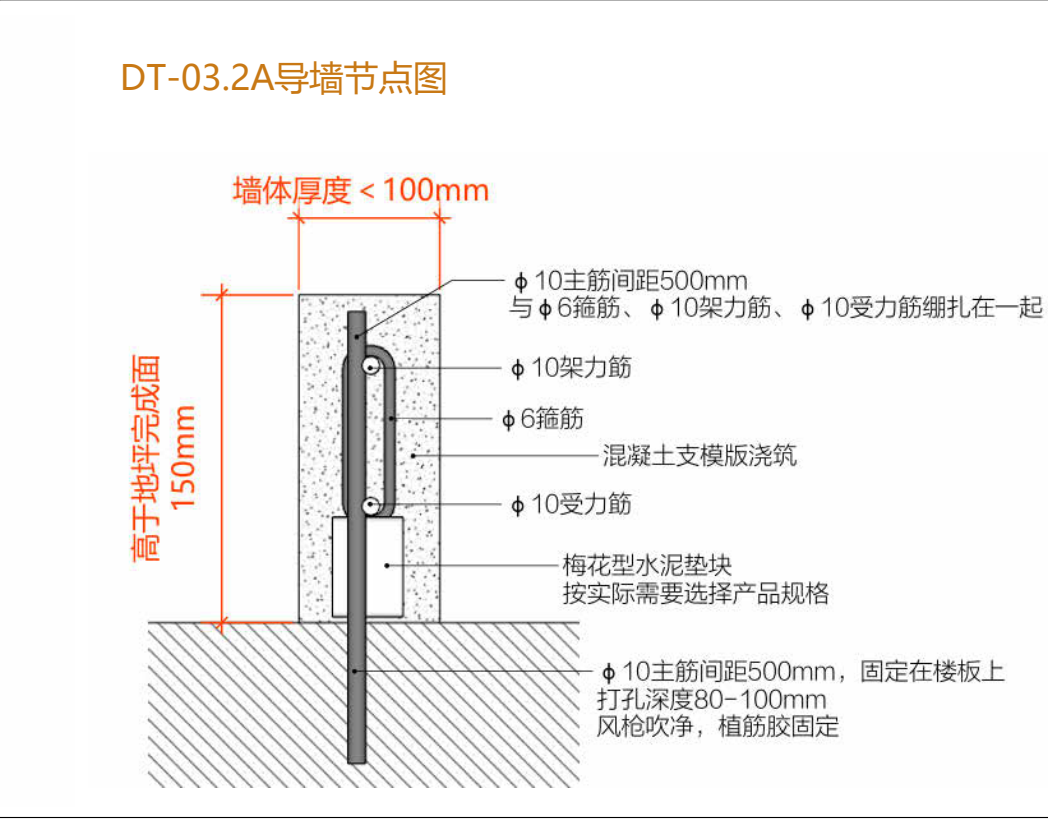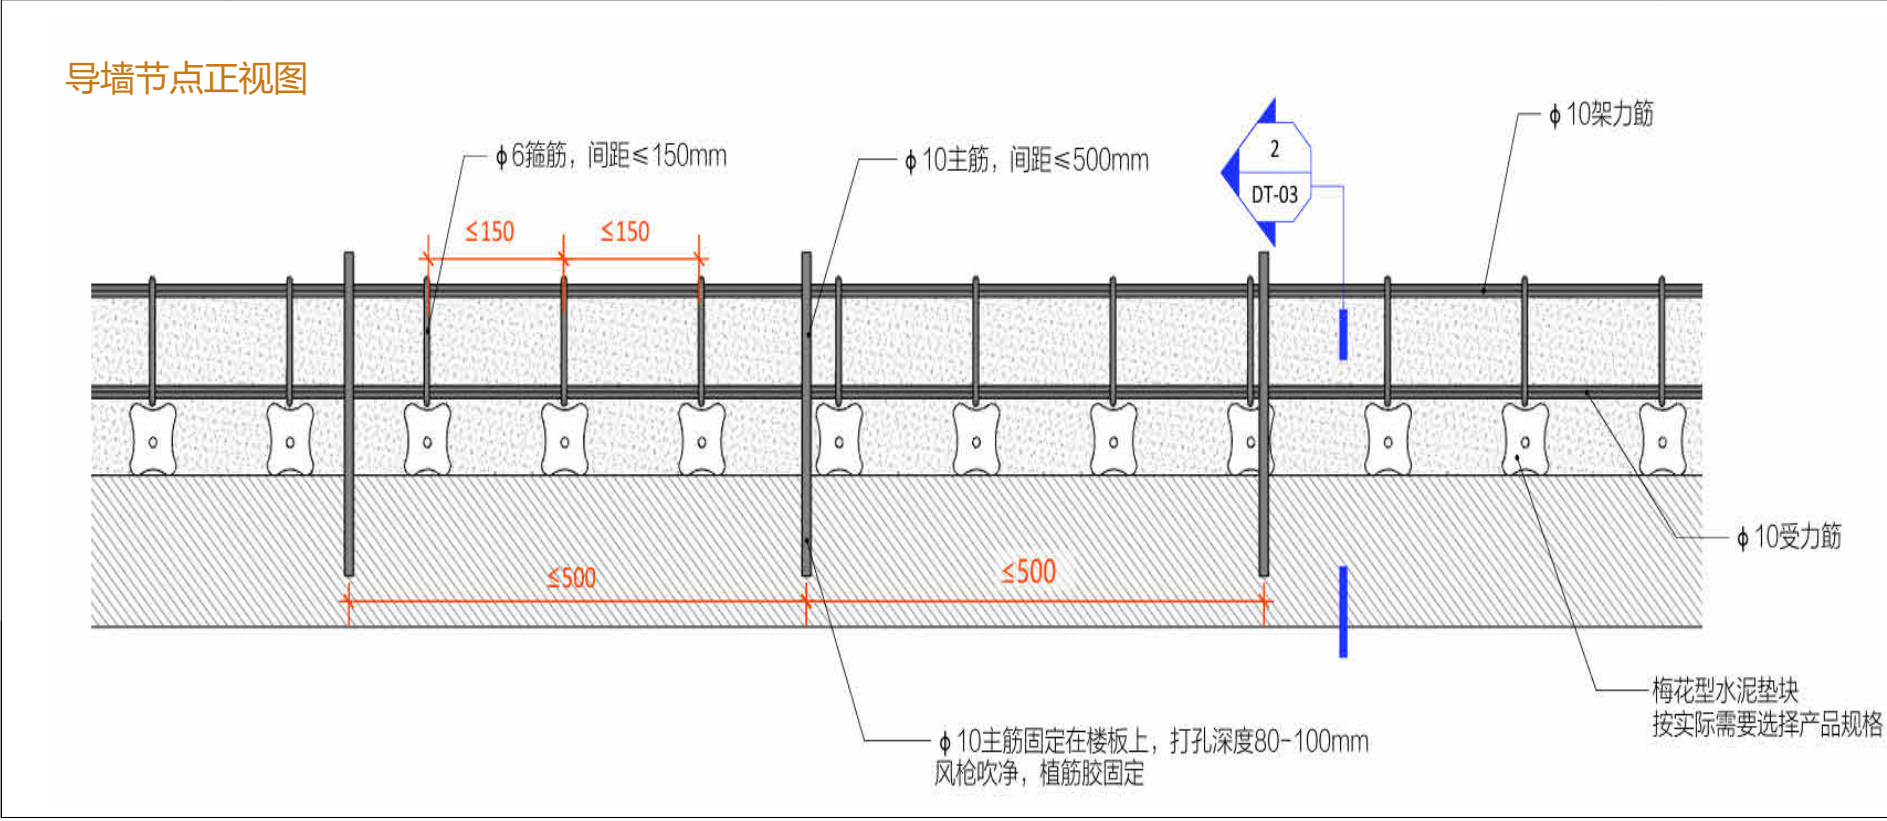

LEGEND图例

编号	图例	说明
1		原始墙、板、柱
2		混凝土导墙
3		过梁
4		构造柱
5		钢筋

盖章:

正式施工图
2026-08-06

注释
Notes

1 本图纸如与现场尺寸有誤, 请施工人员与项目负责人联系。
2 施工前施工人员应认真查阅此图, 如有不明尺寸, 按现场测量为准。
3 本图纸必须经甲乙双方认可并签字方可作为施工依据。

日期 Date	08/01/26
修订 Revision	

项目
Project

巨鹿路880号

图纸名称
Drawing Name.

1F厨房导墙钢筋立面

比例
Scale

1:20@A2

图纸编号
Drawing No.

1F.NW.PL-02.9

项目编号
Project No.

© 2026