


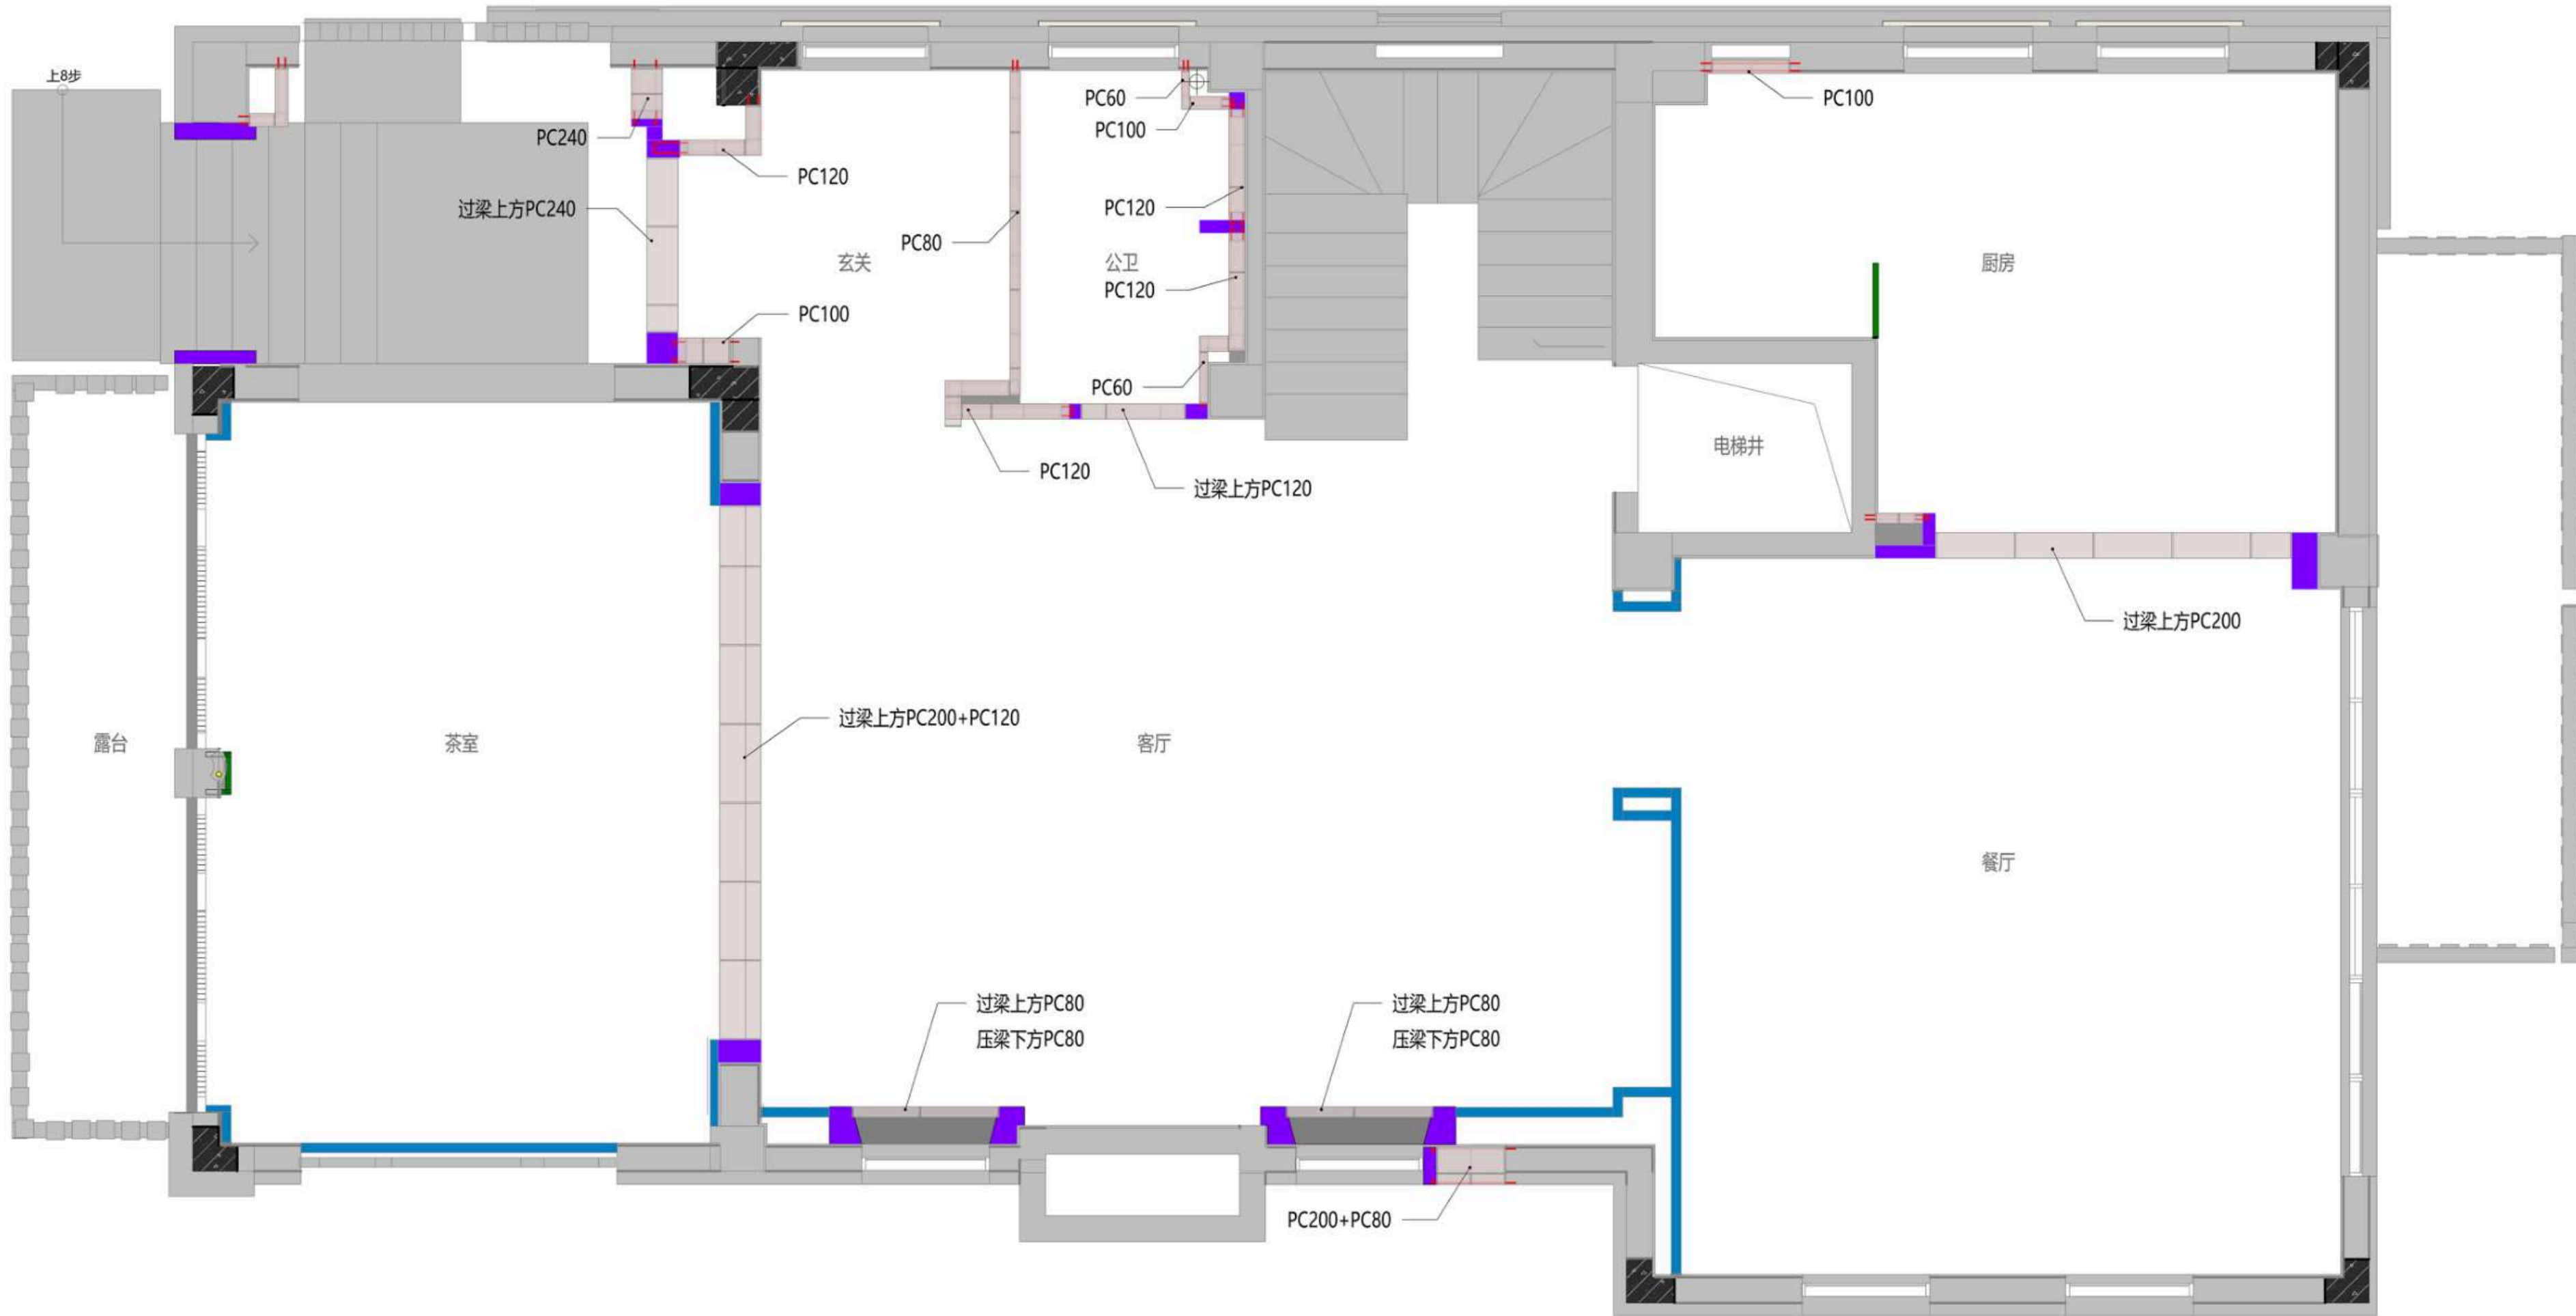

LEGEND图例

编号	图例	说明
1		原始墙、板、柱
2		混凝土导墙
3		砌块砖
4		构造柱
5		过梁
6		轻钢龙骨
7		钢架墙

盖章

正式施工图
2026-08-13

注释
Notes

1. 本图纸如与现场尺寸有误, 请施工人员与项目负责人联系。
2. 施工前施工人员应认真查阅此图, 如有不明确尺寸, 按现场测量为准。
3. 本图纸必须经甲乙双方认可并签字方可作为施工依据。

日期
Date 08/13/26

修订
Revision

1

项目
Project 巨鹿路880号


比例
Scale 1:40@A2

1F新建墙体类型平面图

图纸编号
Drawing No.

1F.NW.PL-04

项目编号
Project No. © 2026

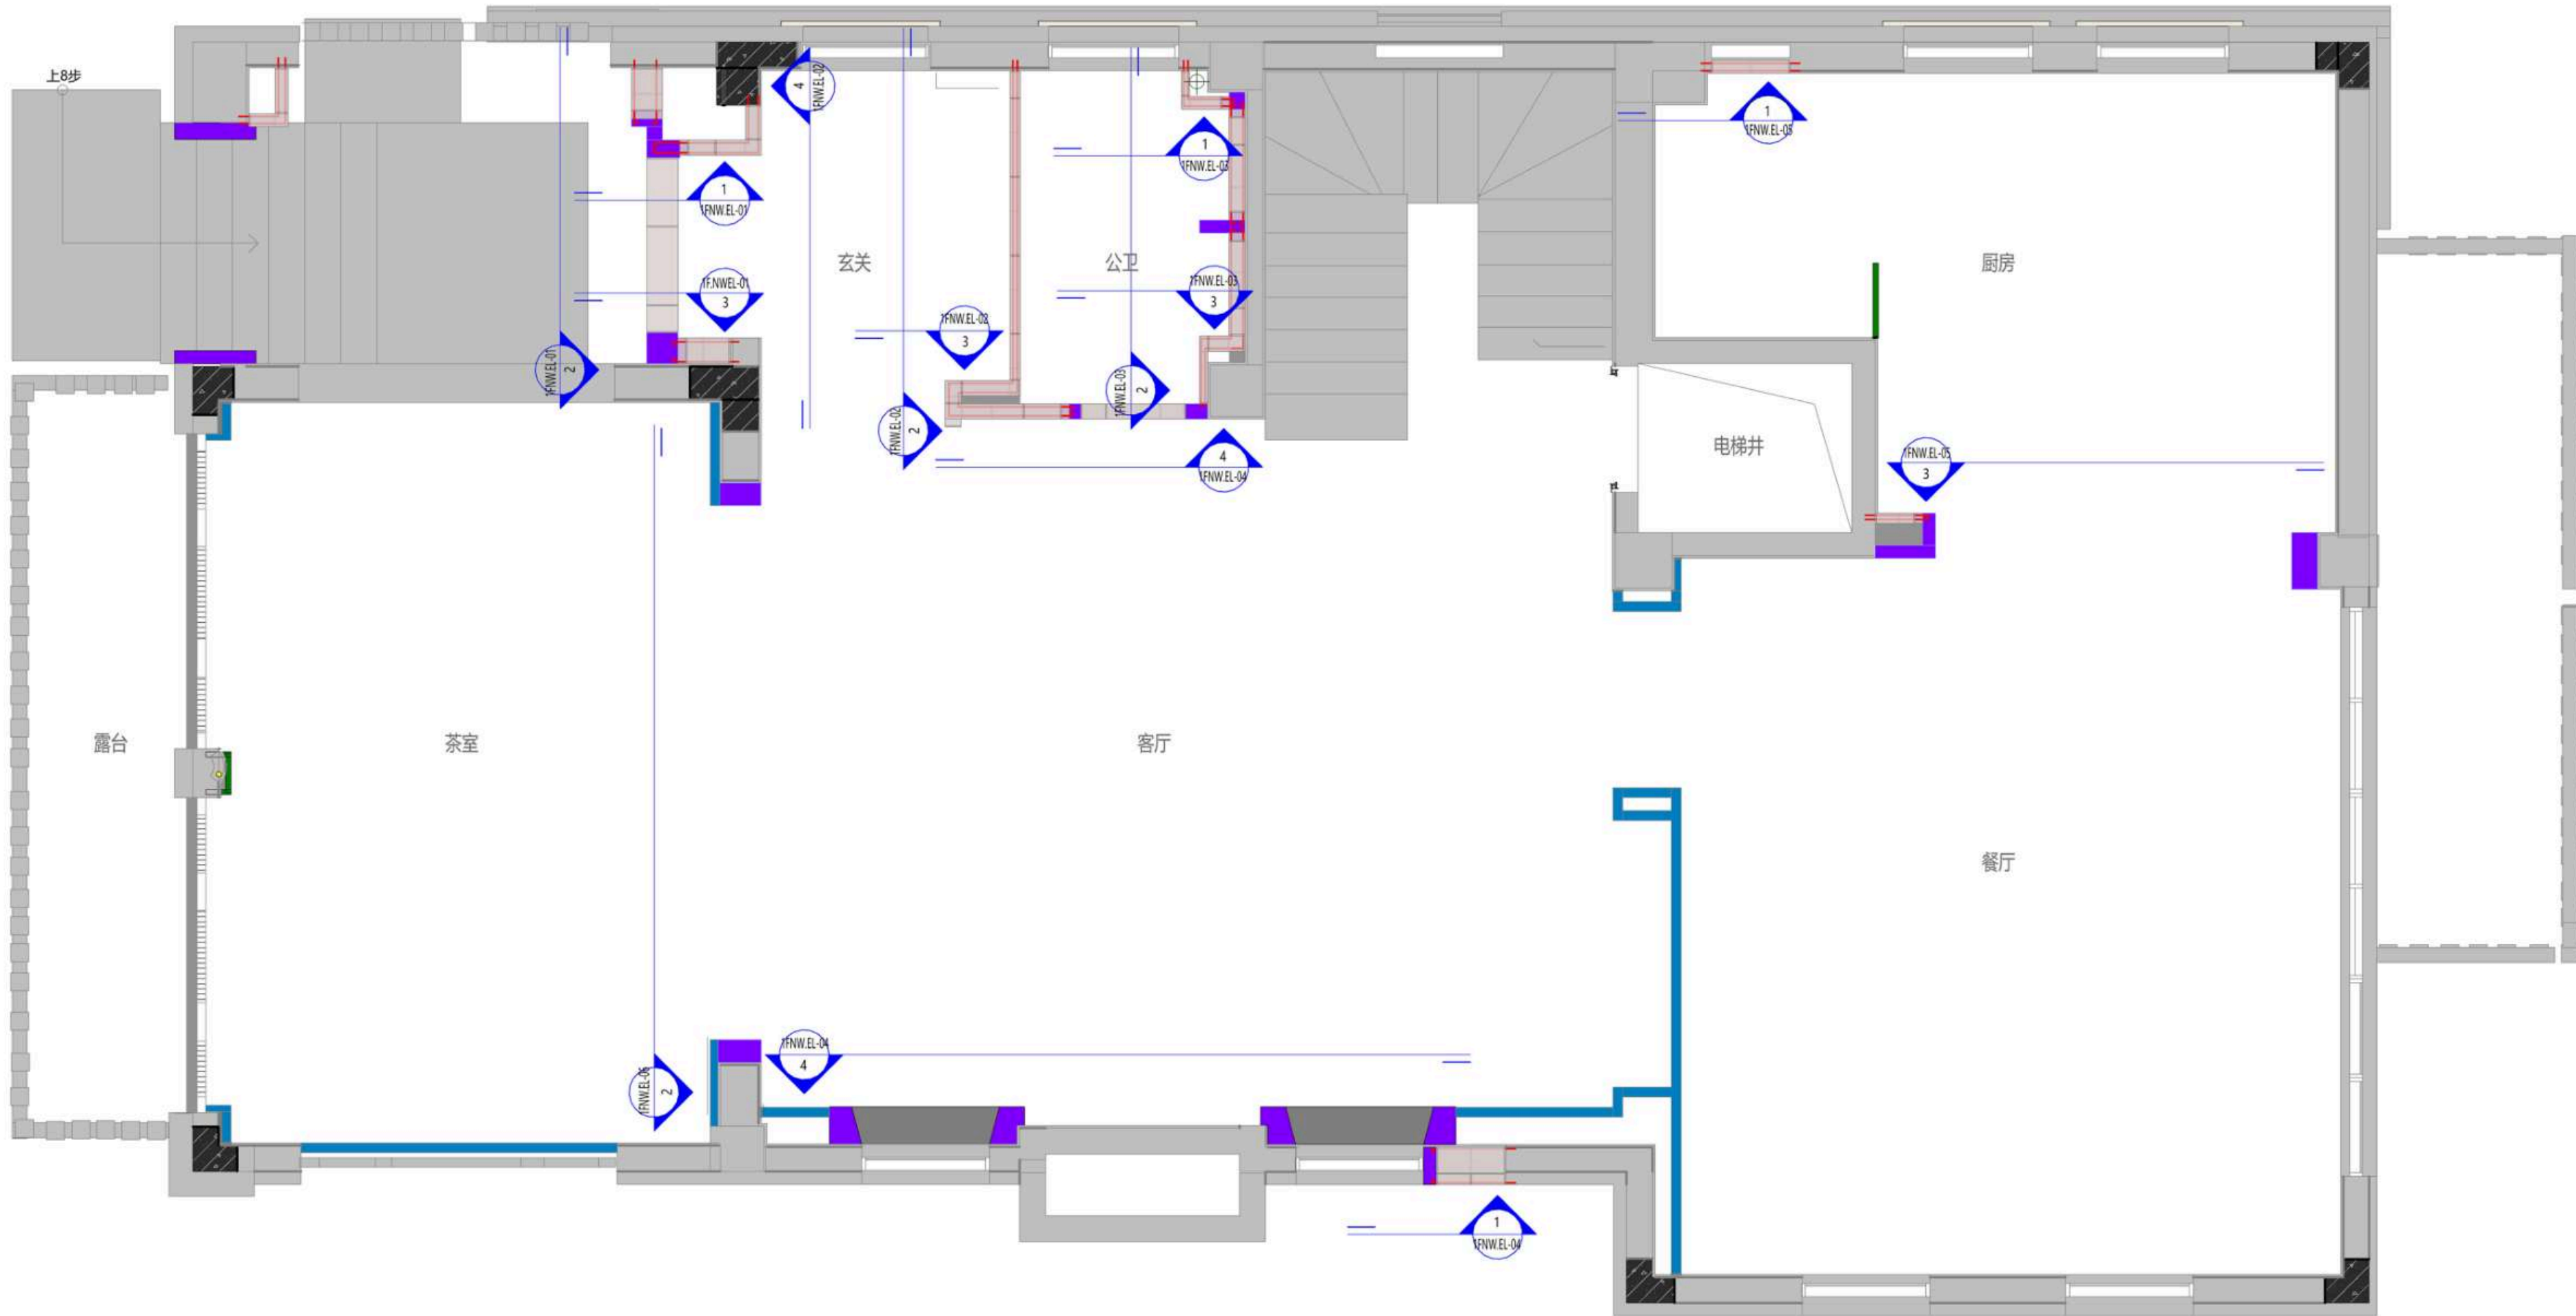

LEGEND图例

编号	图例	说明
1		原始墙、板、柱
2		混凝土导墙
3		砌块砖
4		构造柱
5		过梁
6		轻钢龙骨
7		钢架墙

盖章

正式施工图

2026-08-13

注释
Notes

1. 本图纸如与现场尺寸有误, 请施工人员与项目负责人联系。
2. 施工前施工人员应认真查阅此图, 如有不明确尺寸, 按现场测量为准。
3. 本图纸必须经甲乙双方认可并签字方可作为施工依据。

日期

Date

08/13/26

修订

Revision

项目

Project

巨鹿路880号

比例

Scale

1:40@A2

1F新建墙体索引图

图纸编号


Drawing No.

1F.NW.PL-05

项目编号

Project No.

© 2026

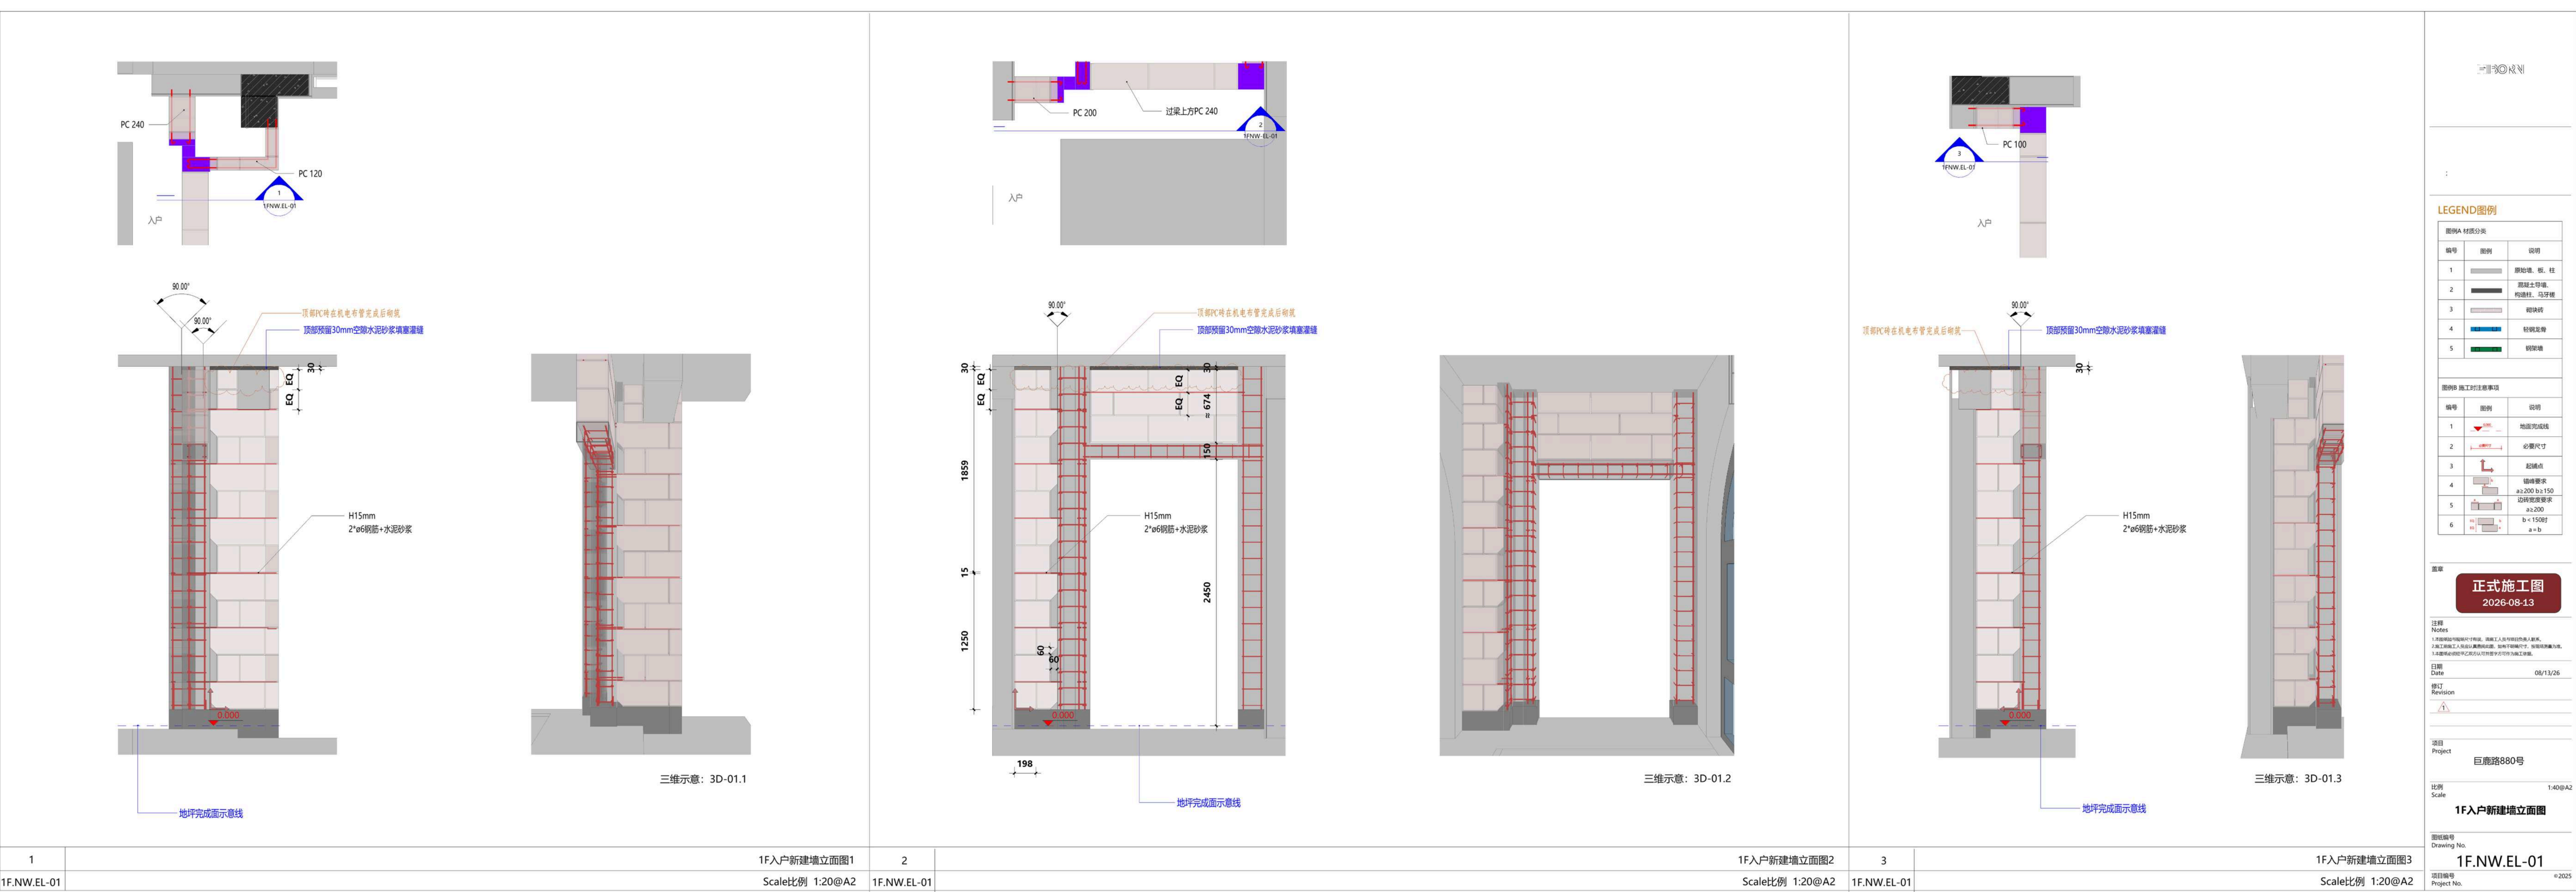

LEGEND图例

图例A 材质分类		
编号	图例	说明
1		原始墙、板、柱
2		混凝土导墙、构造柱、马牙槎
3		砌块砖
4		轻钢龙骨
5		钢架墙

图例B 施工时注意事项

编号	图例	说明
1		地面完成线
2		必要尺寸
3		起铺点
4		错缝要求 a≥200 b≥150
5		边砖宽度要求 a≥200
6		b < 150时 a = b

盖章

正式施工图
2026-08-13

注释

- Notes
- 1.本图纸所有标注尺寸均按国家现行标准执行，如遇特殊情况以设计人意见为准。
 - 2.施工时须按国家现行标准执行，如遇特殊情况以设计人意见为准。
 - 3.本图纸必须经甲方签字认可并加盖公章后方可作为施工依据。

日期
Date

08/13/26

修订
Revision

项目
Project

巨鹿路880号

比例
Scale

1:40@A2










1F入户新建墙立面图

图纸编号
Drawing No.

项目编号
Project No.

1F.NW.EL-01

© 2025

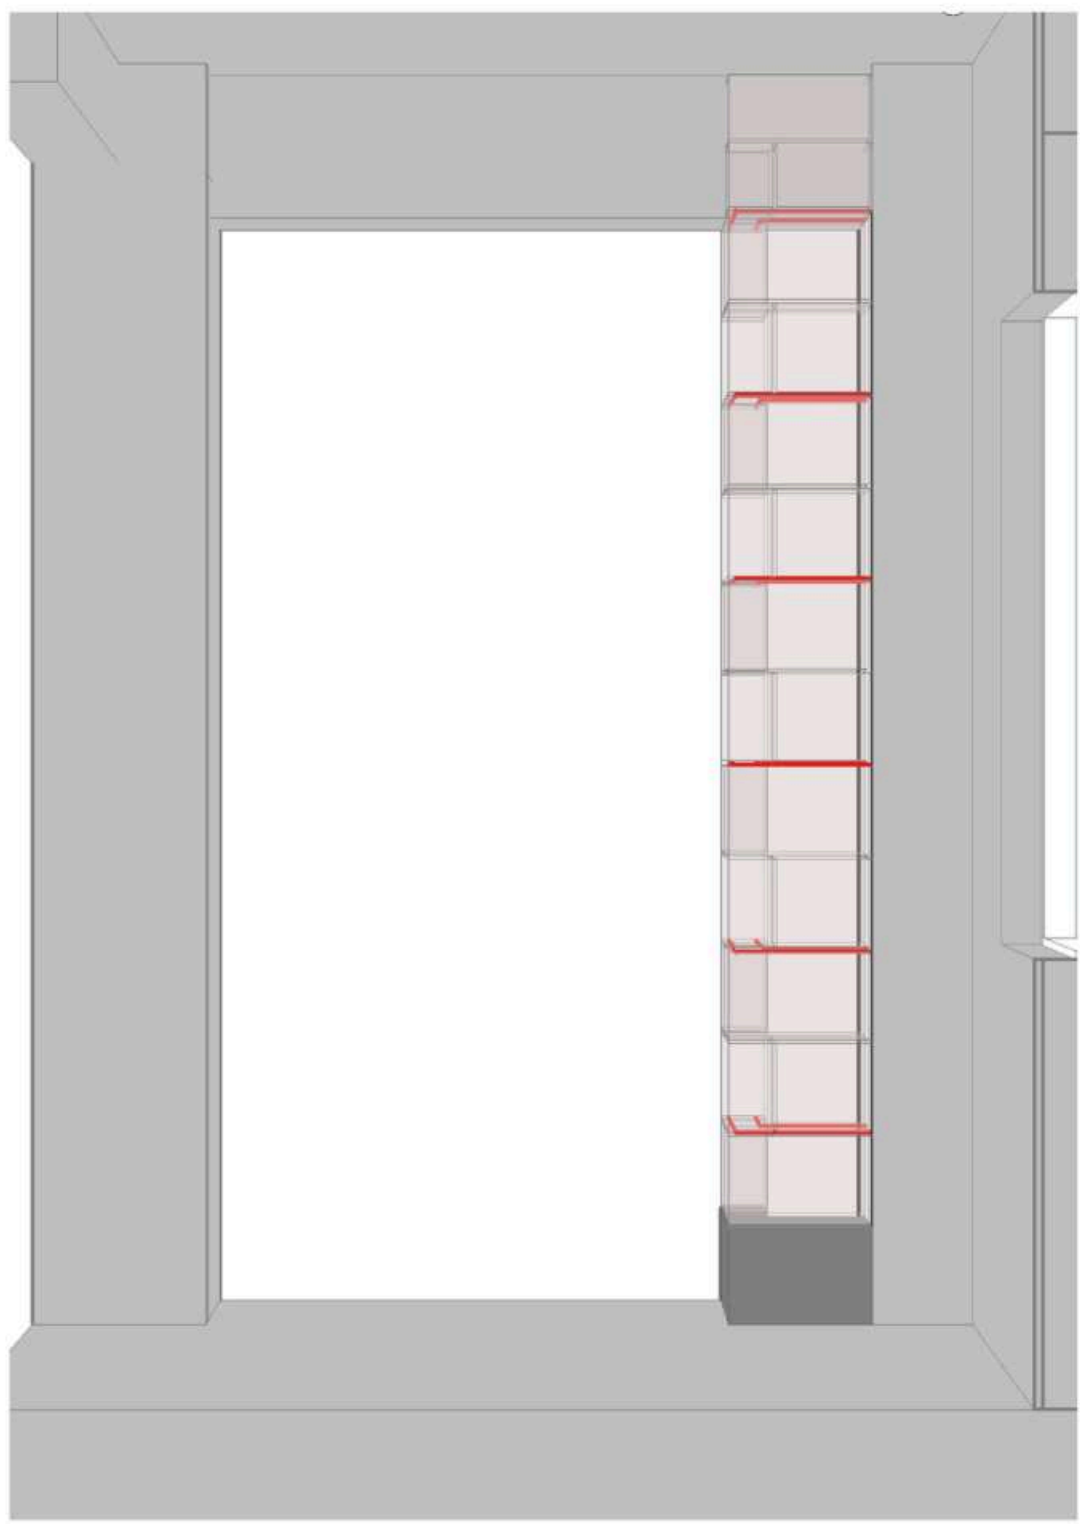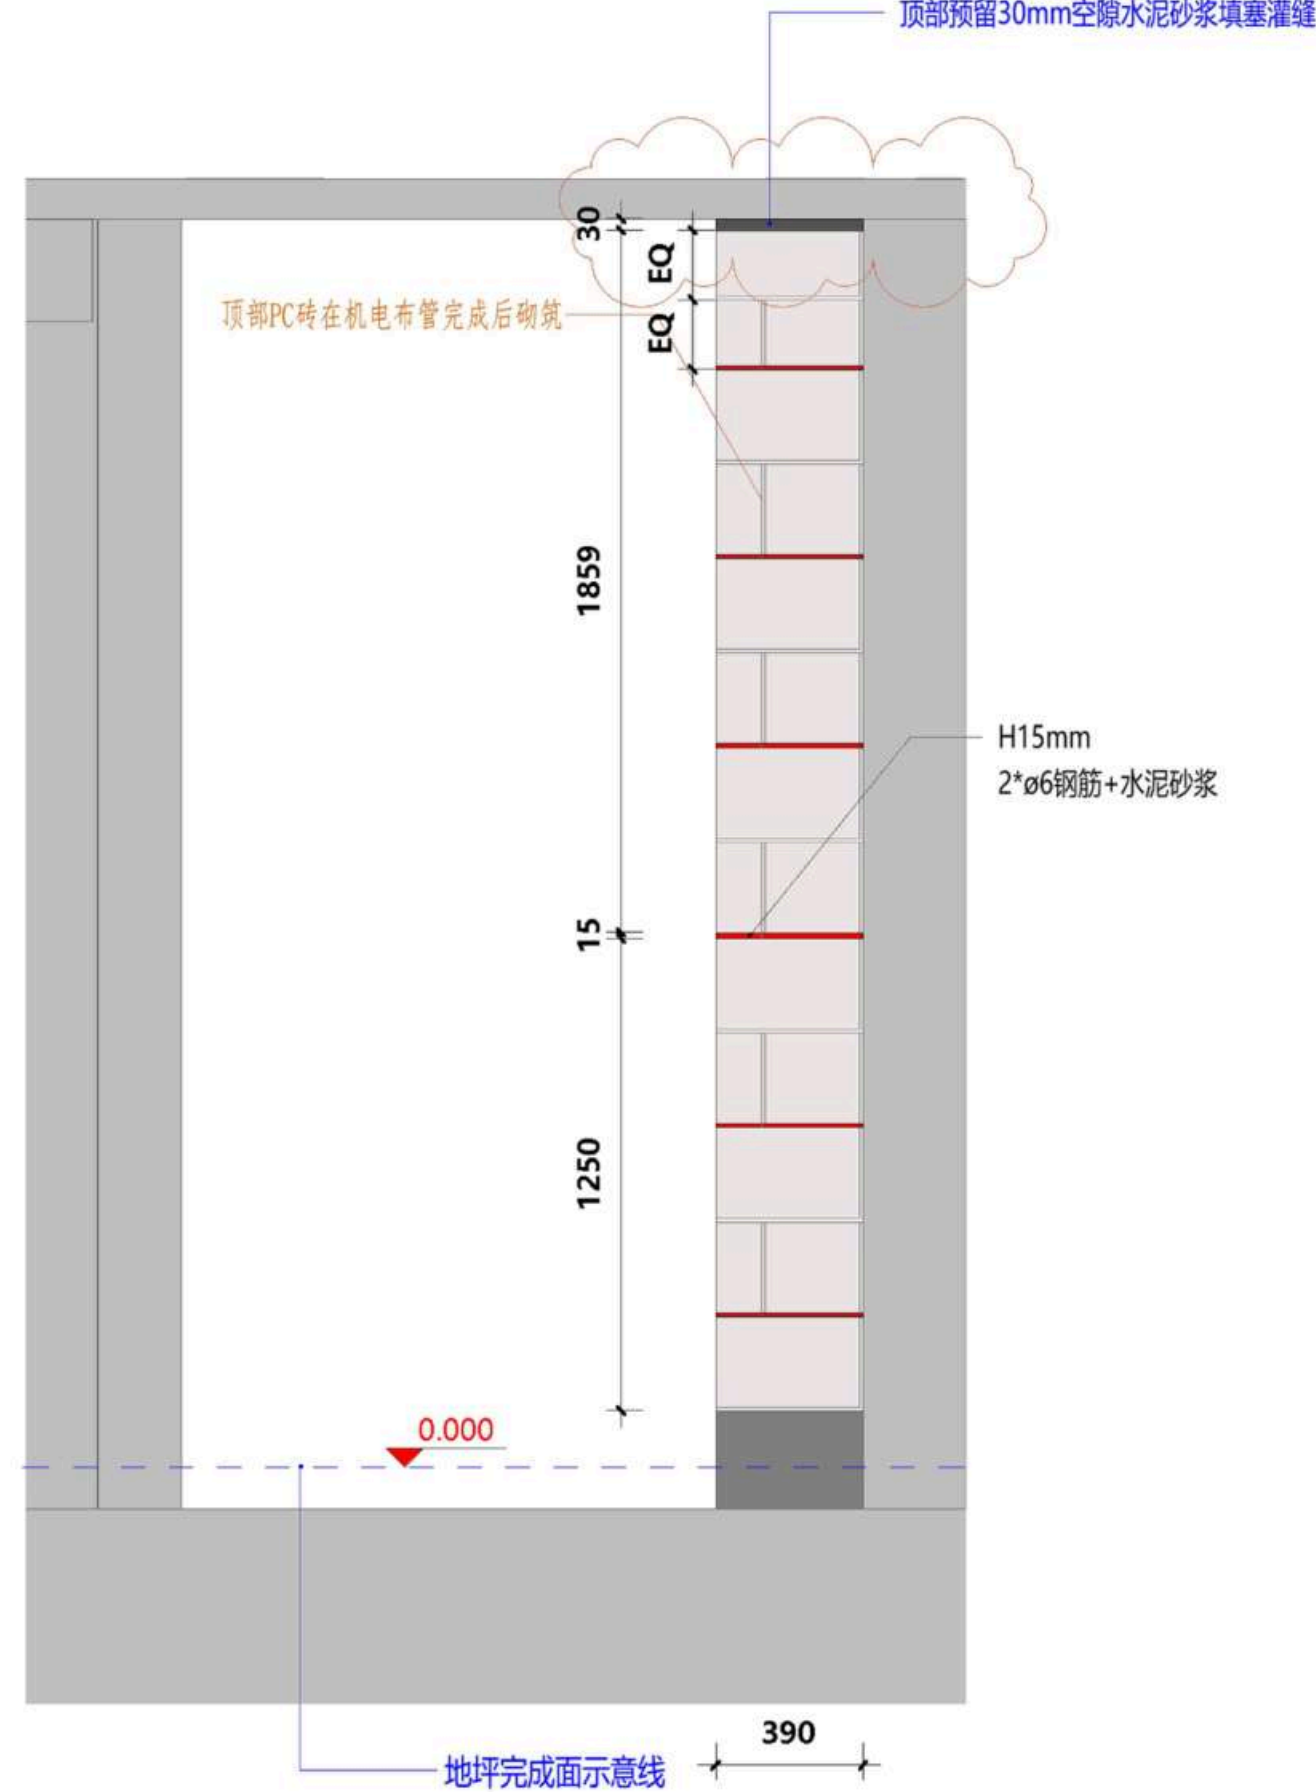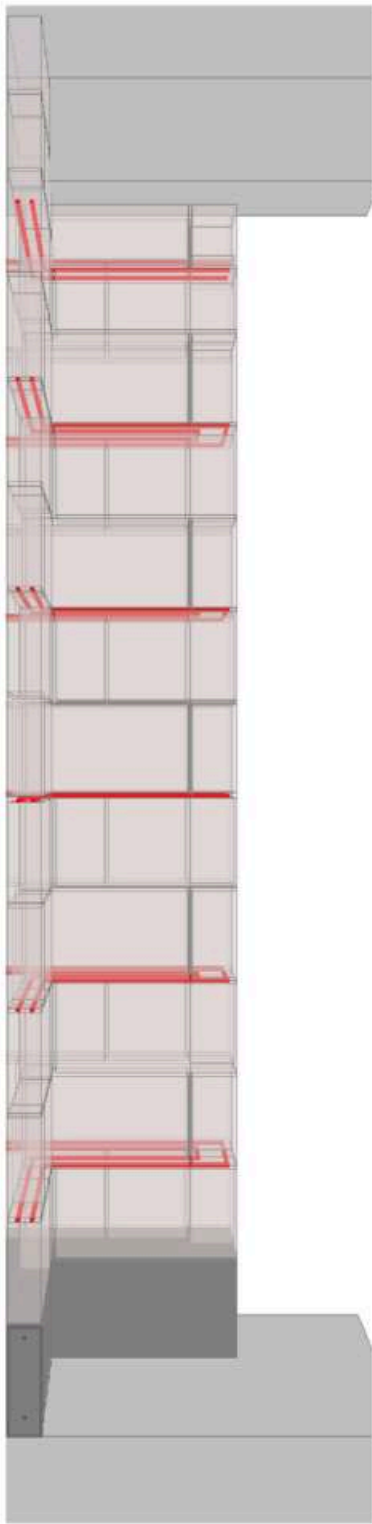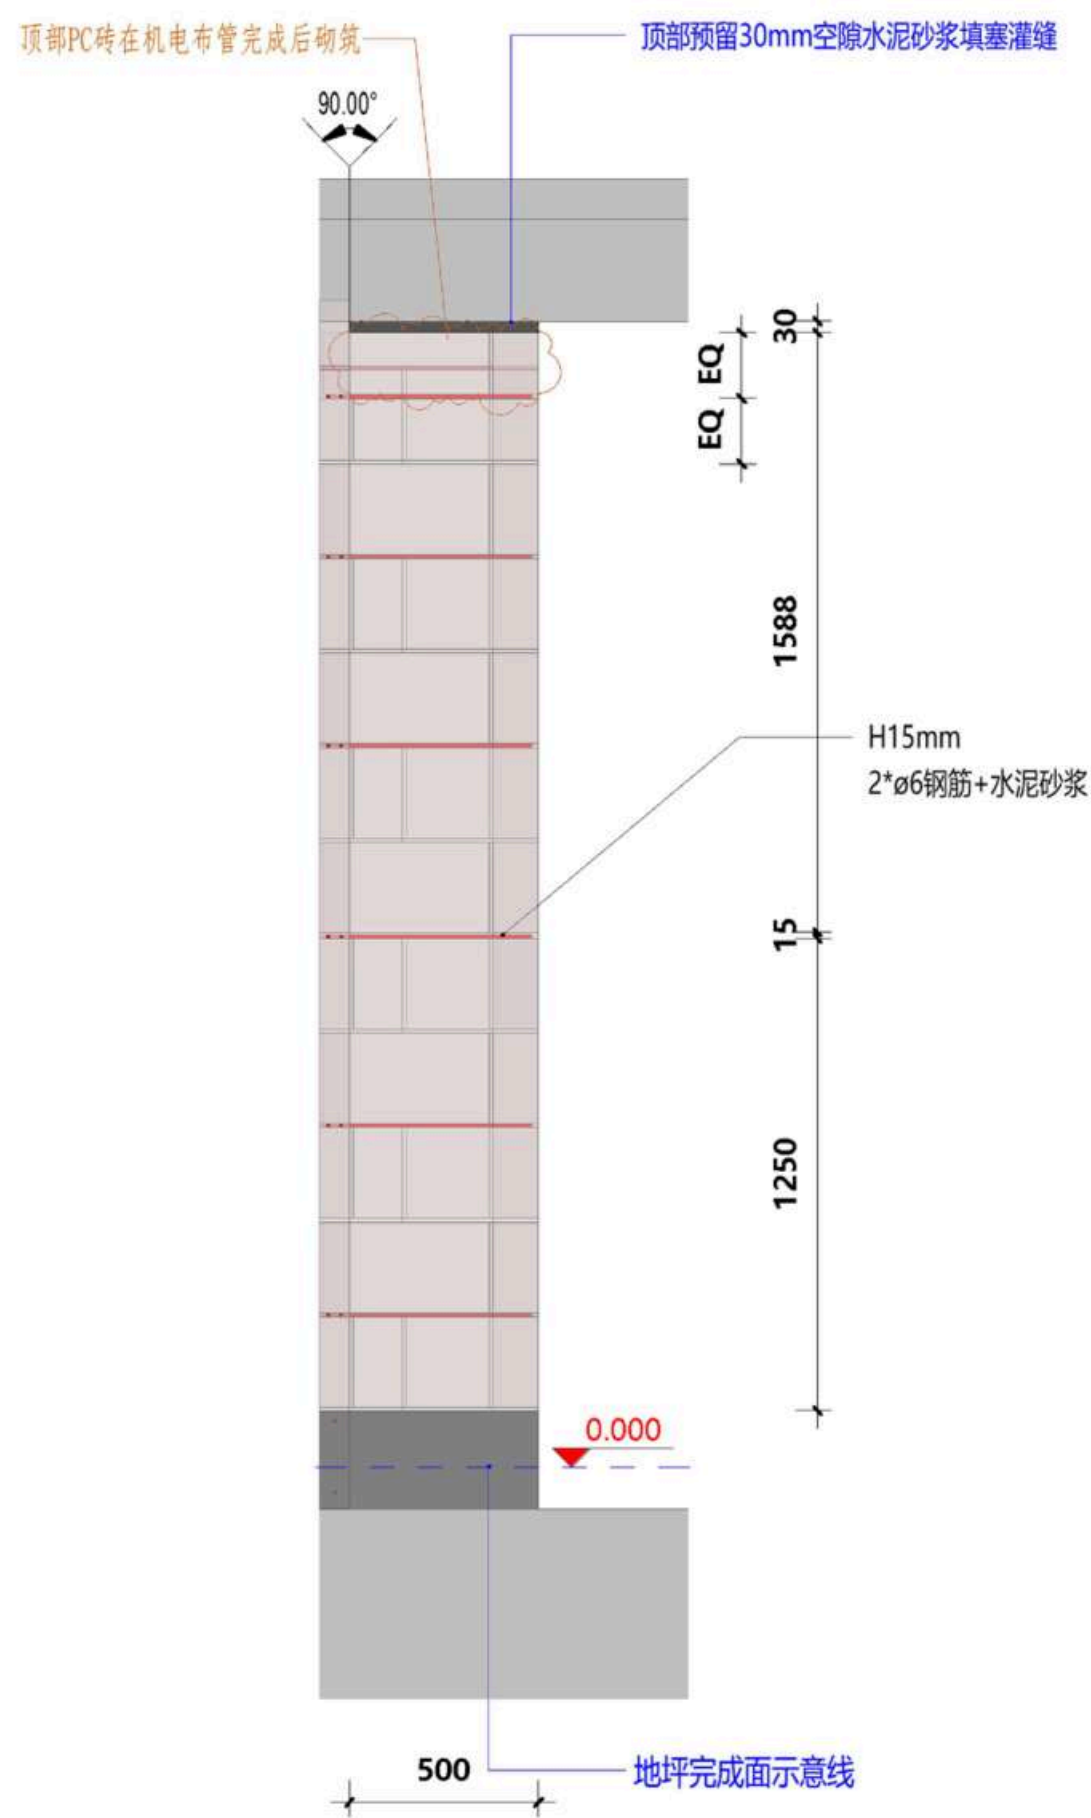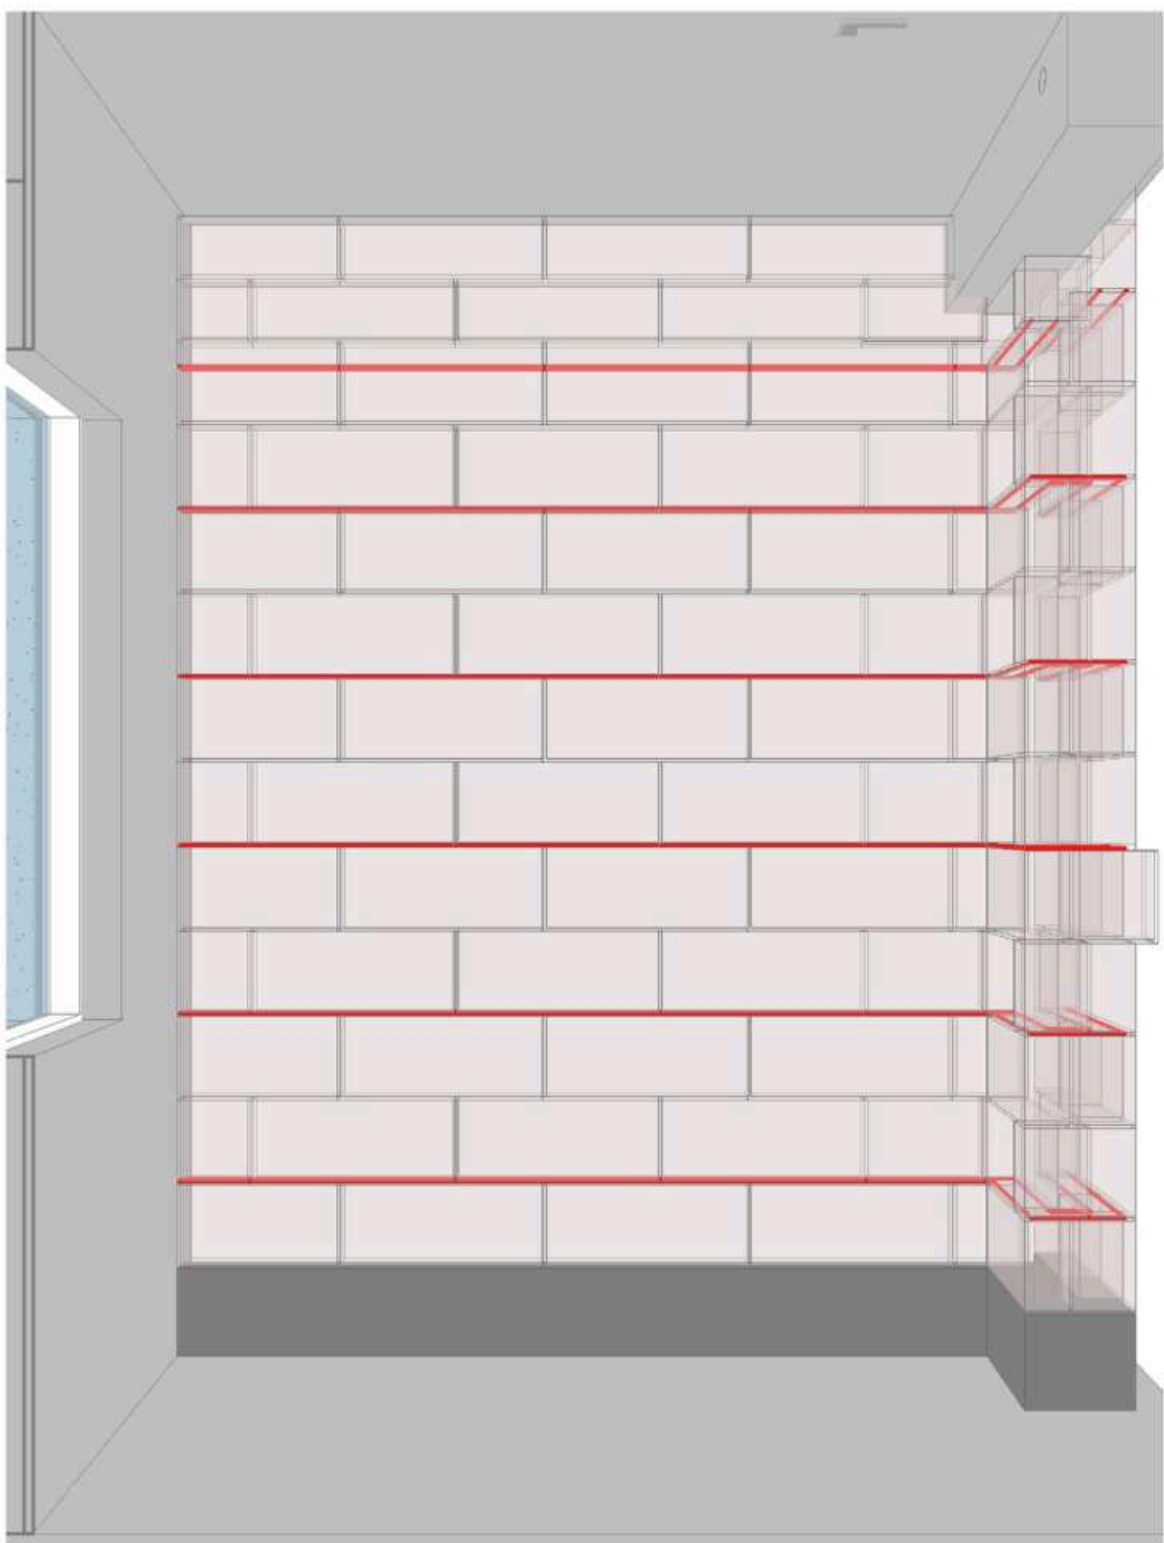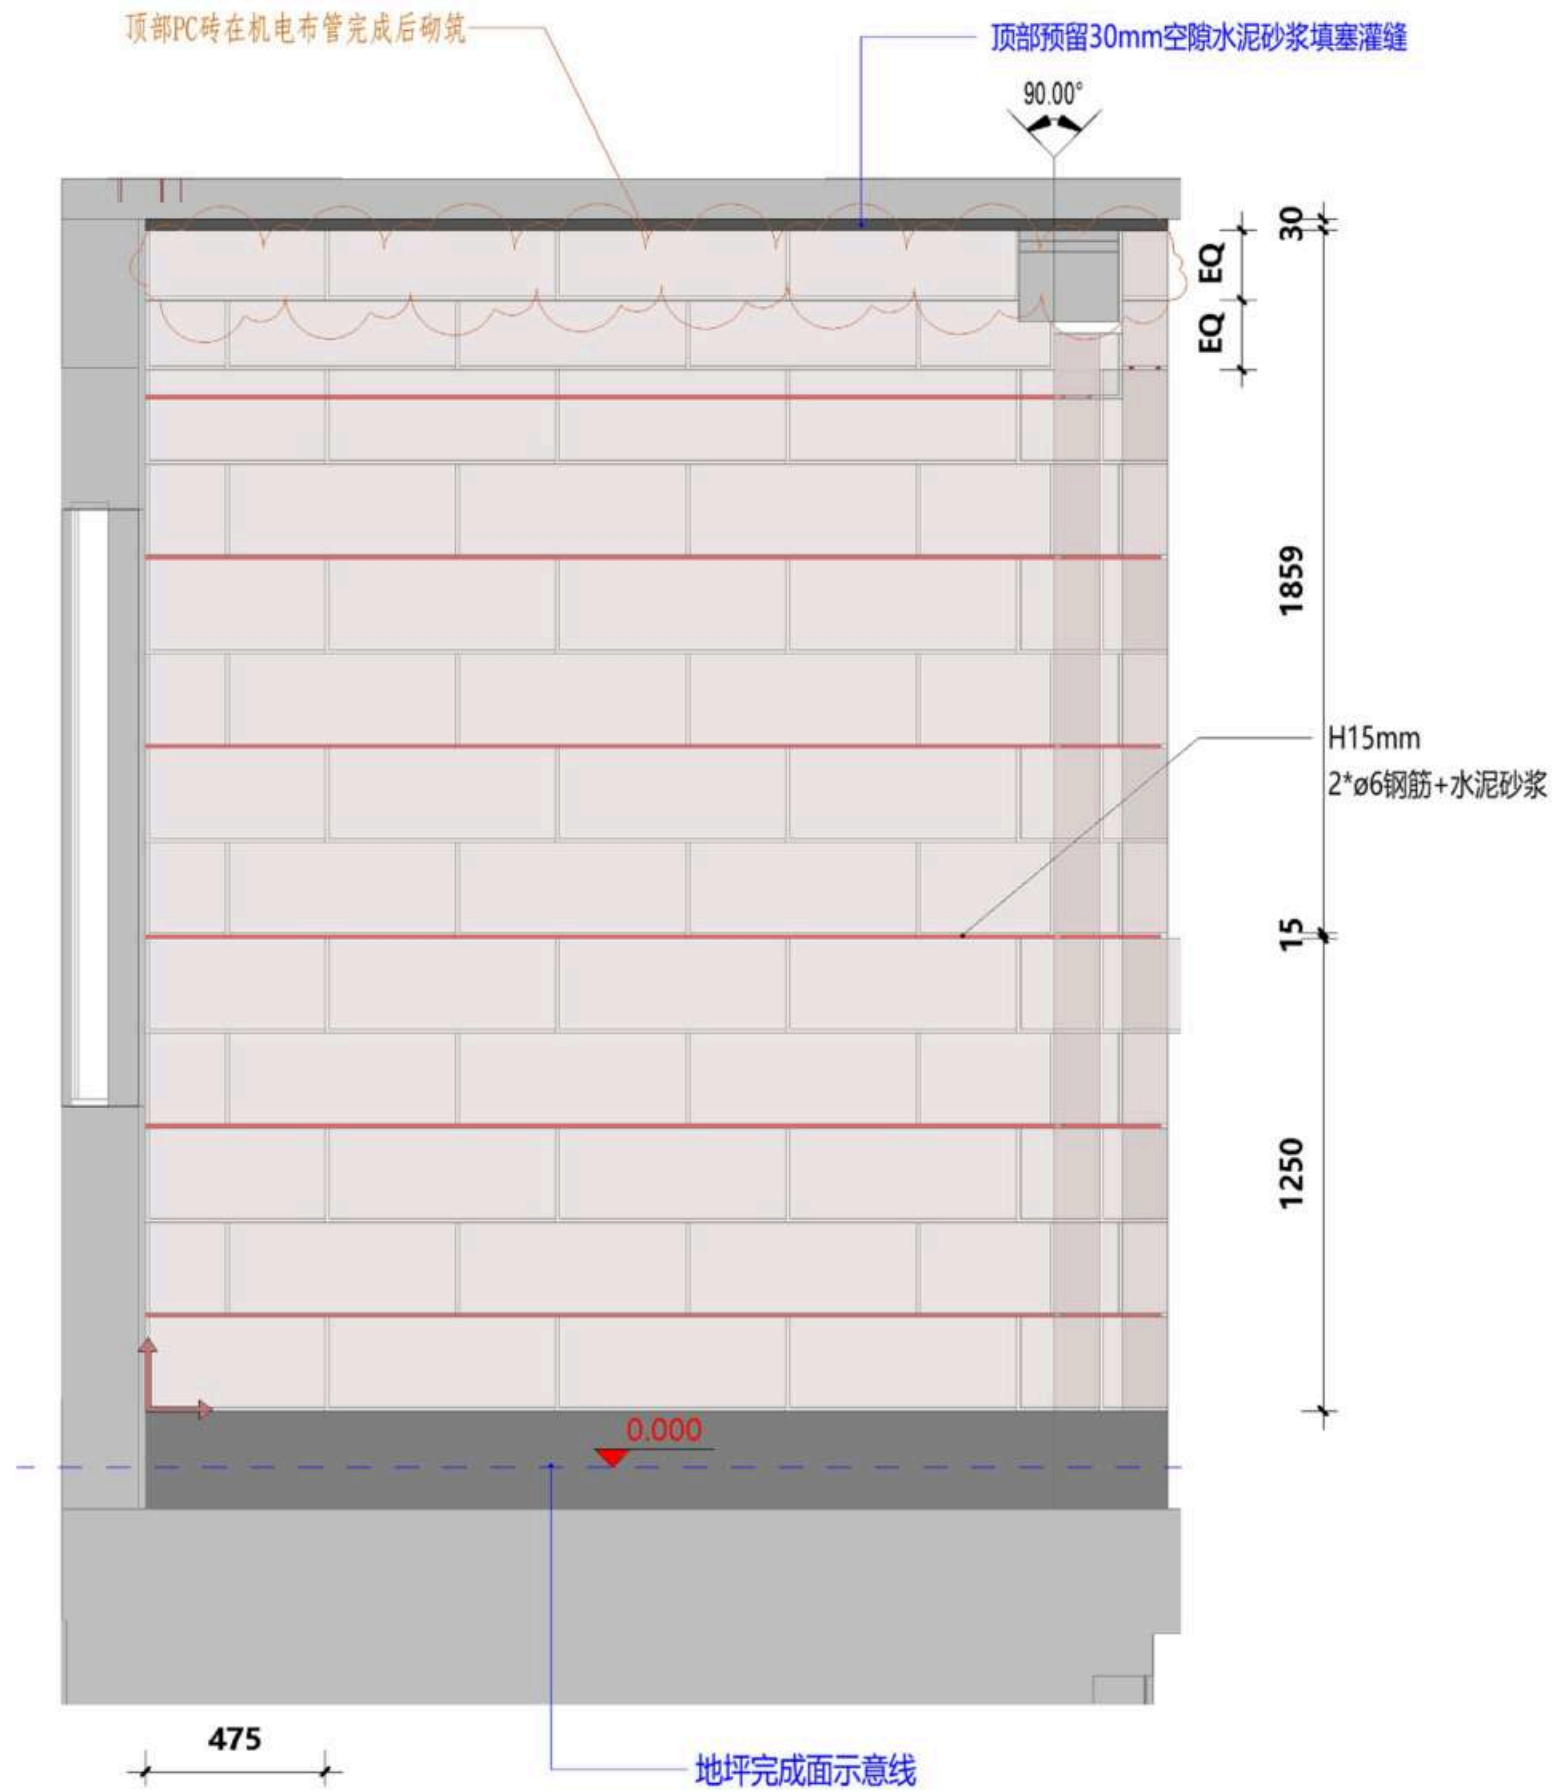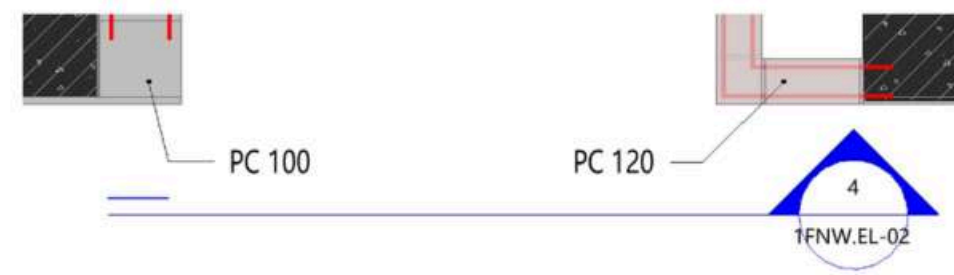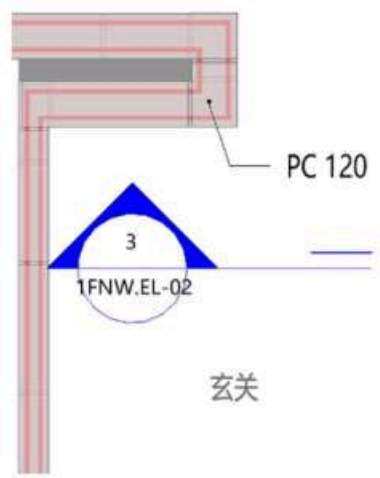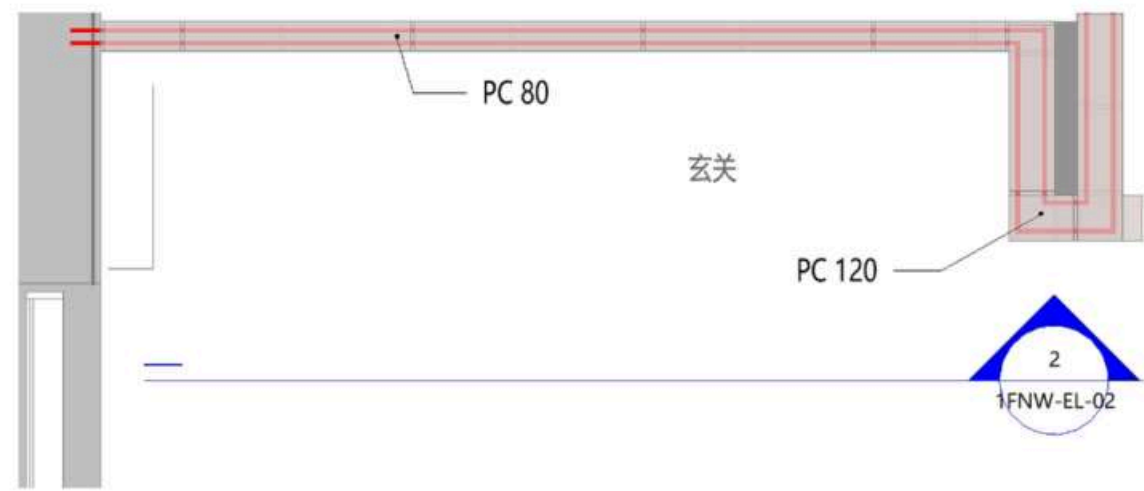

ELFORN

LEGEND图例

图例A 材质分类		
编号	图例	说明
1		原始墙、板、柱
2		混凝土导墙、构造柱、马牙槎
3		砌块砖
4		轻钢龙骨
5		钢架墙

图例B 施工时注意事项

编号	图例	说明
1		地面完成线
2		必要尺寸
3		起铺点
4		错缝要求 a≥200 b≥150
5		边砖宽度要求 a≥200
6		b < 150时 a = b

盖章

正式施工图
2026-08-13

注释

Notes
1.本图仅供参考，不作为施工依据。 2.施工过程中如有变更，请及时与设计师沟通。 3.本图仅供参考，不作为施工依据。

日期
Date

08/13/26

修订
Revision

项目

Project

巨鹿路880号

比例
Scale

1:40@A2

1F玄关新建墙立面图

图纸编号
Drawing No.

1F.NW.EL-02

项目编号
Project No.

© 2025

2

1F.NW.EL-02

1F玄关新建墙立面图2

Scale比例 1:20@A2

3

1F.NW.EL-02

1F玄关新建墙立面图3



Scale比例 1:20@A2

4



1F.NW.EL-02

1F玄关新建墙立面图4



Scale比例 1:20@A2

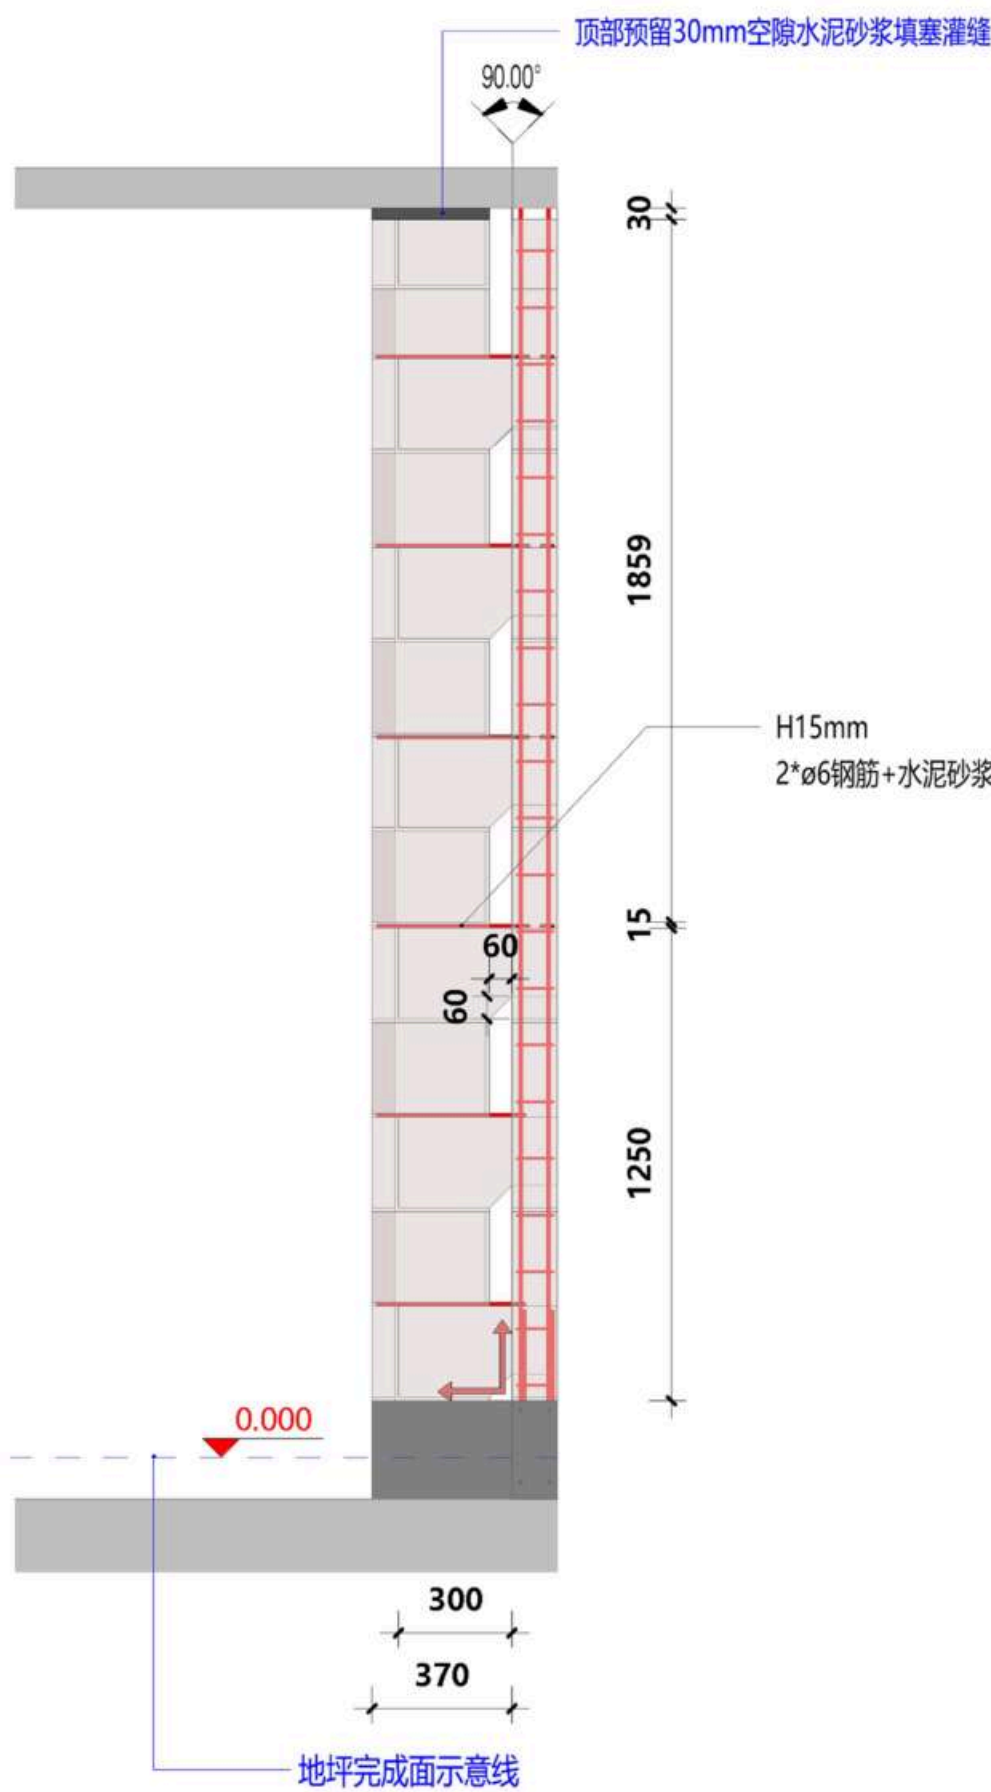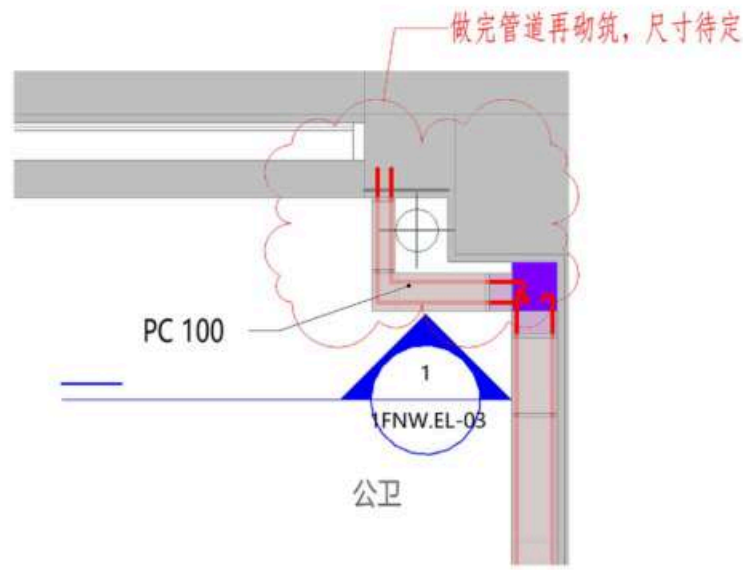

三维示意: 3D-03.1

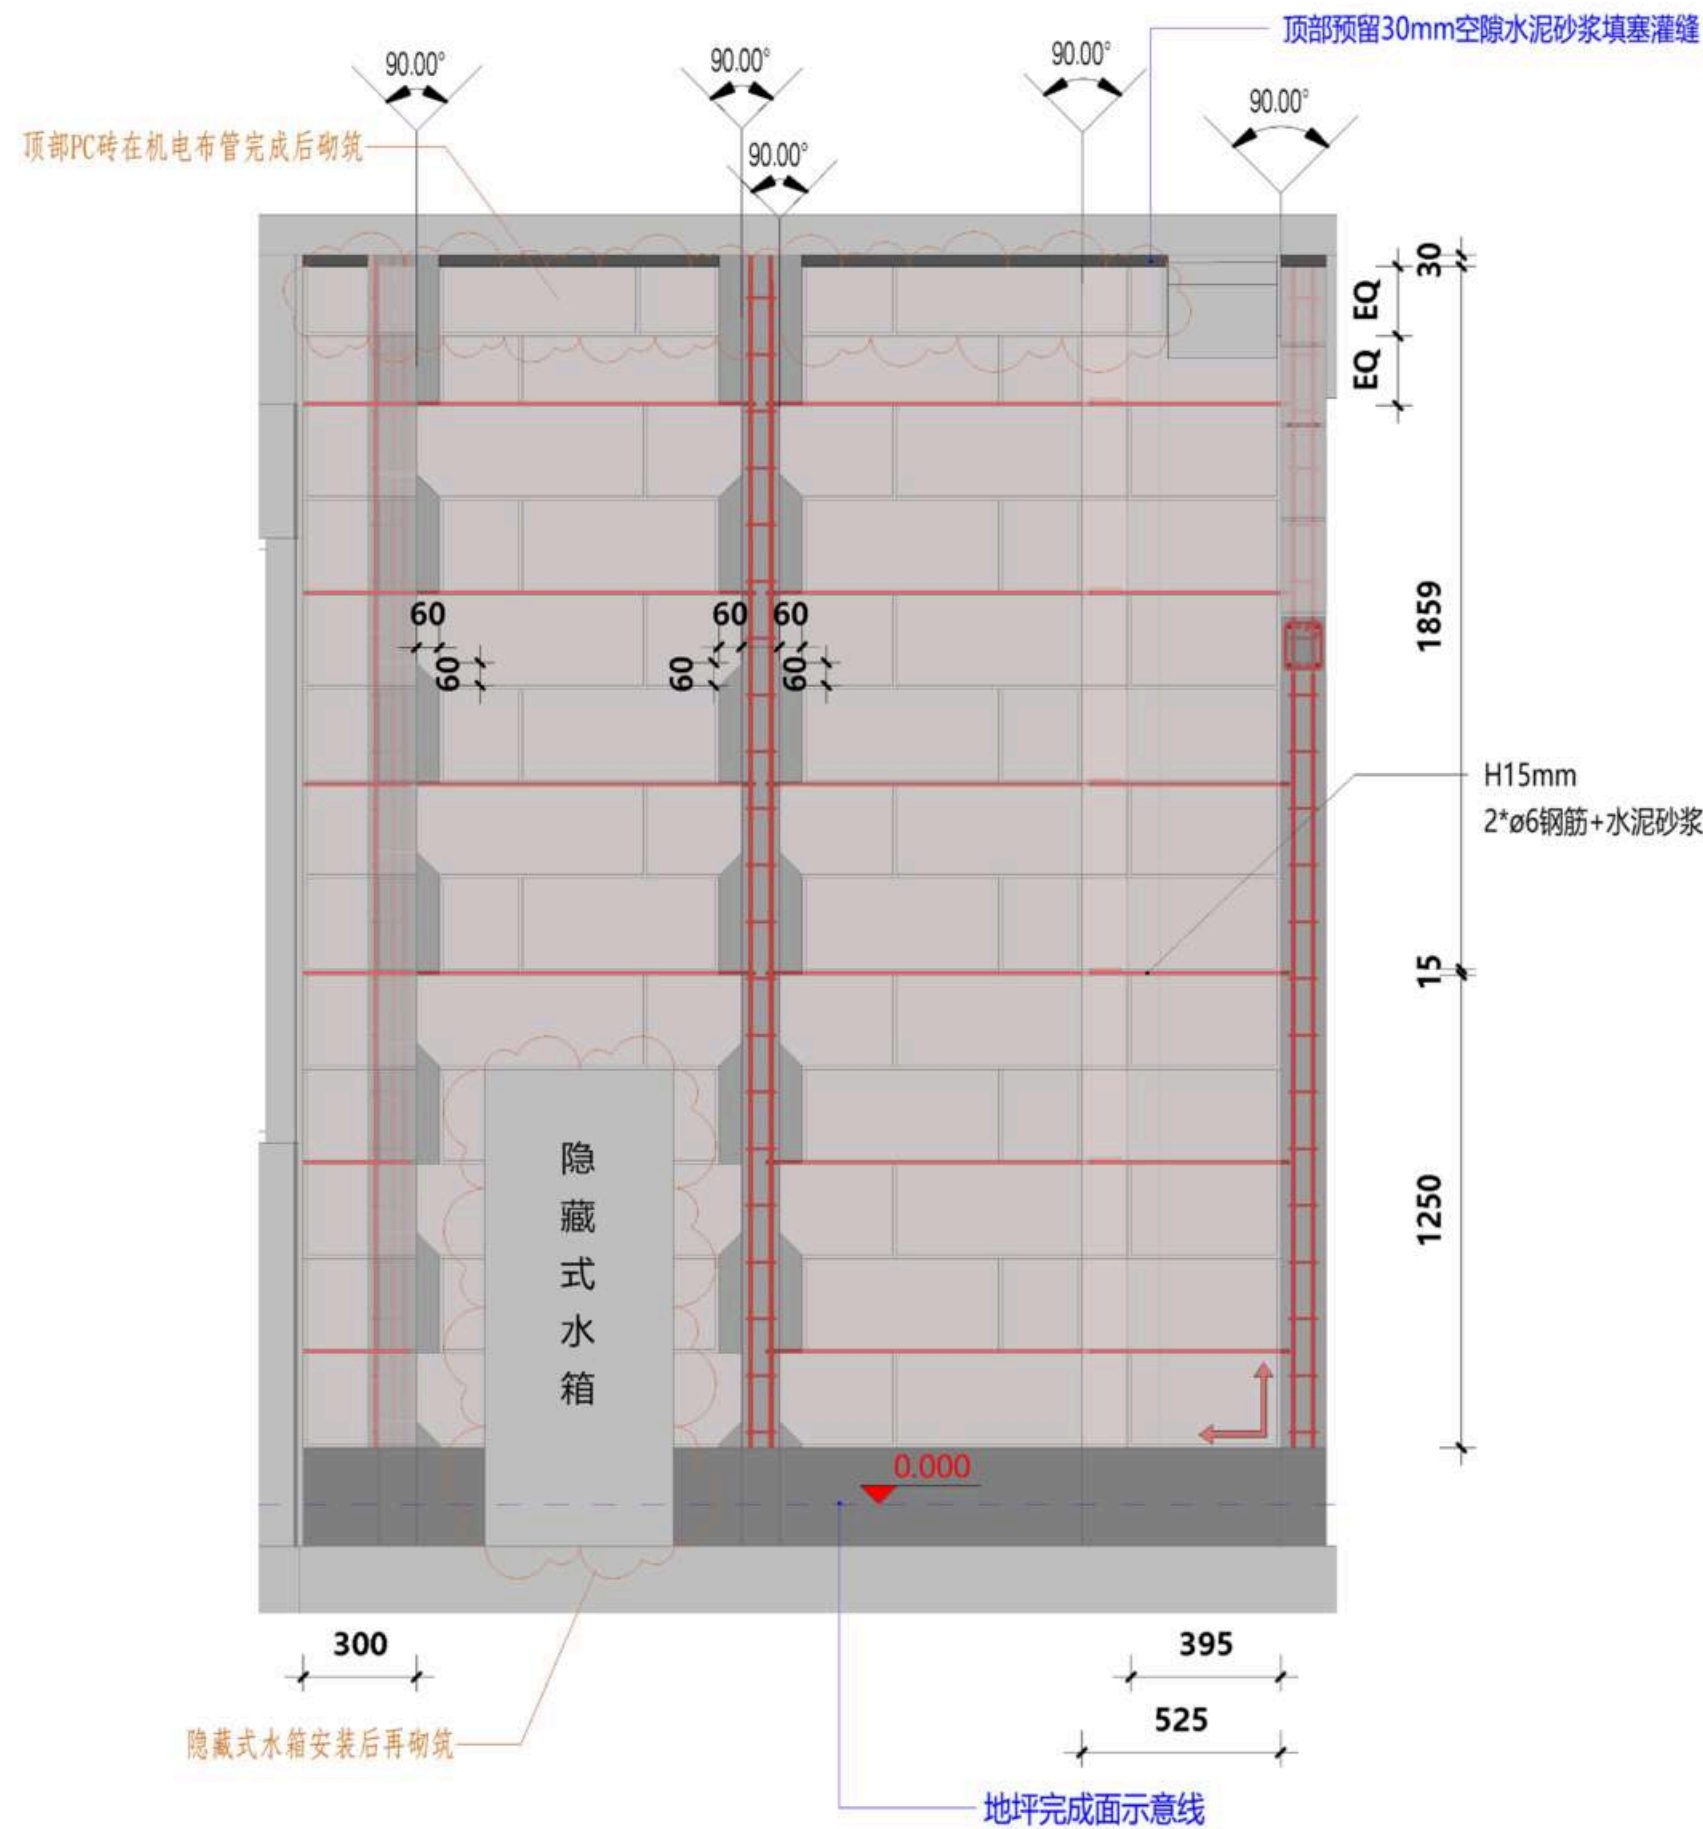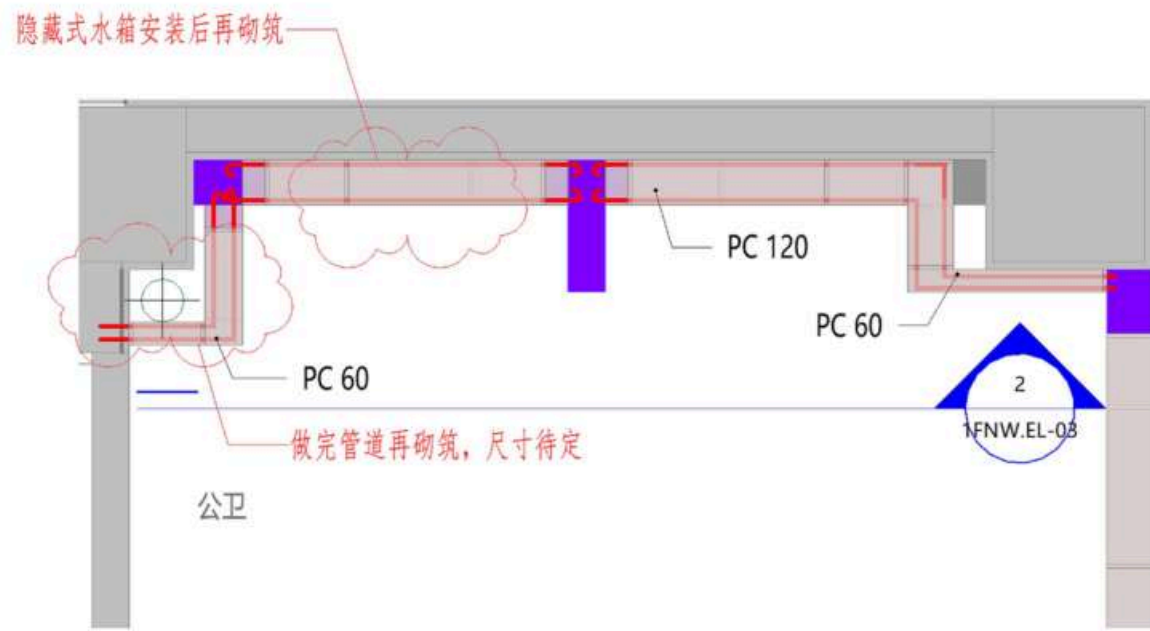

三维示意: 3D-03.2

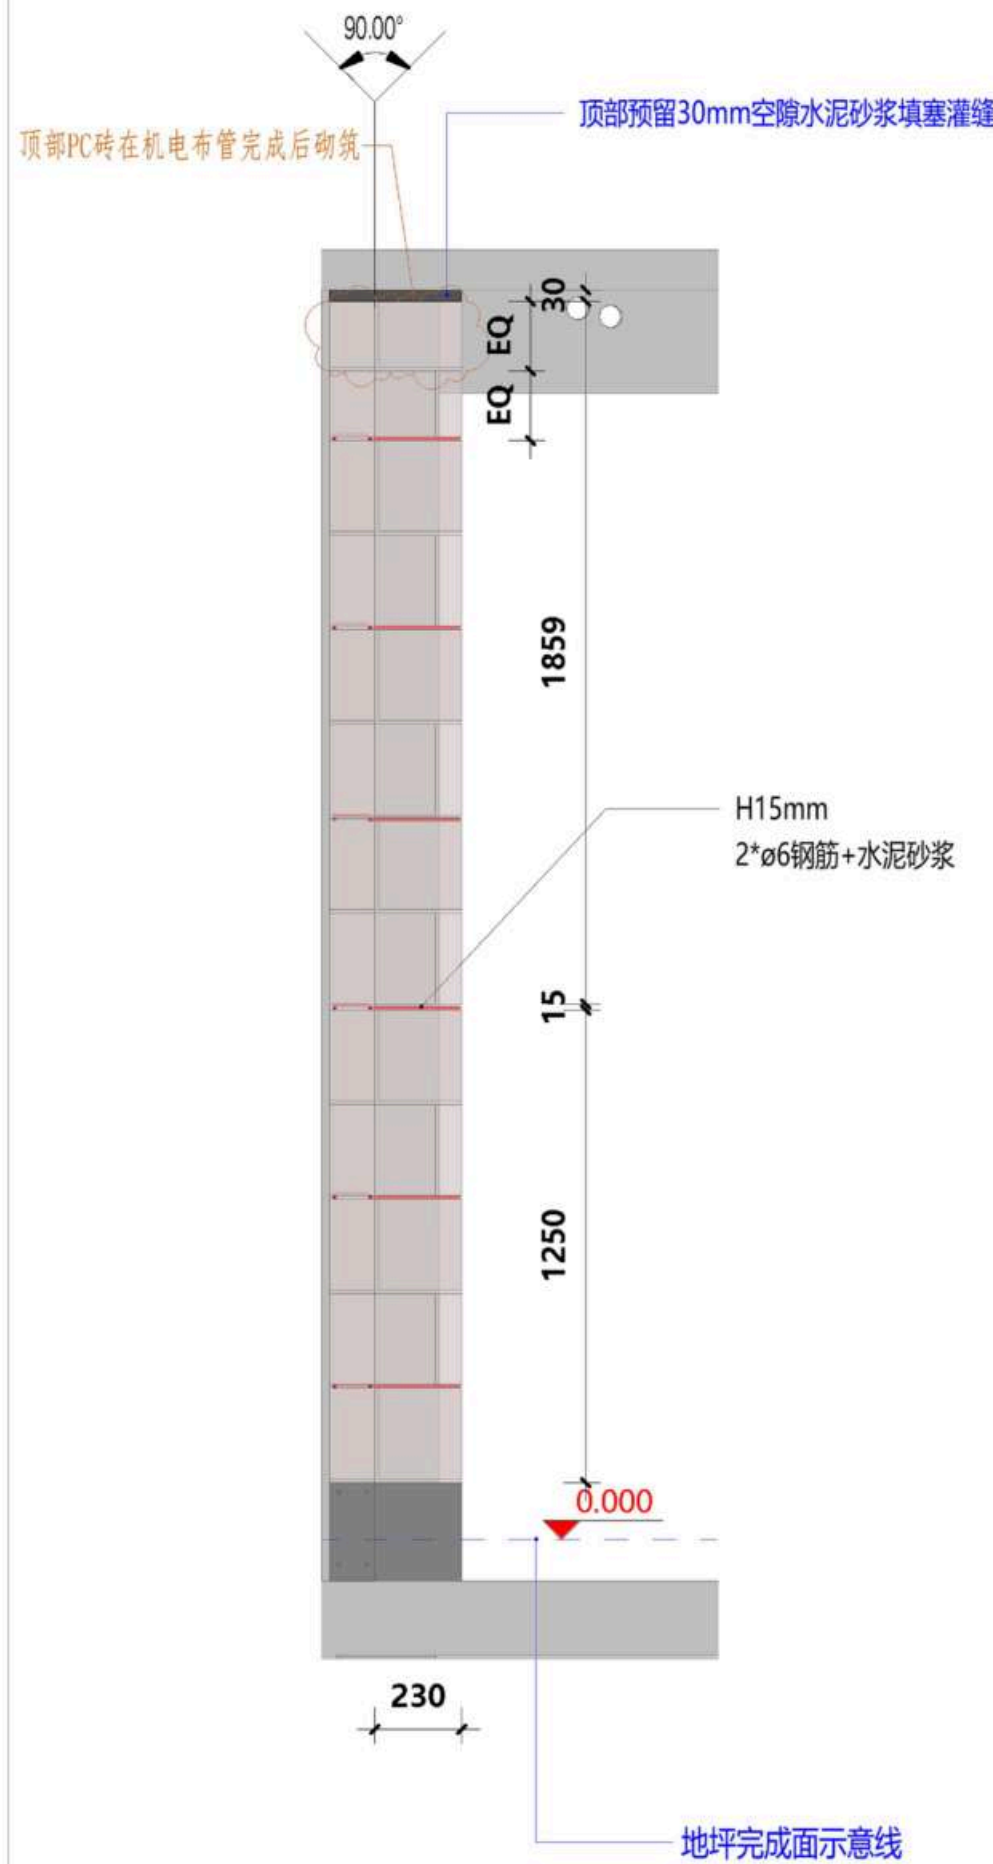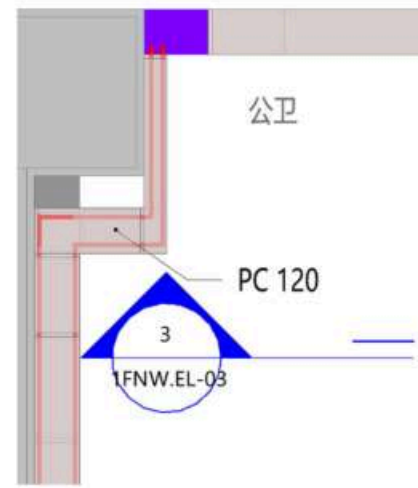

三维示意: 3D-03.3

图例

LEGEND图例

图例A 材质分类		
编号	图例	说明
1		原始墙、板、柱
2		混凝土导墙、构造柱、马牙槎
3		砌块砖
4		轻钢龙骨
5		钢架墙

图例B 施工注意事项

编号	图例	说明
1		地面完成线
2		必要尺寸
3		起铺点
4		错缝要求 a≥200 b≥150
5		边砖宽度要求 a≥200
6		b < 150时 a = b

盖章

正式施工图
2026-08-13

注释

Notes

- 1.本图与现场尺寸有异, 请施工人员与项目负责人联系。
- 2.施工前施工人应确认现场情况, 如有不明之处, 按现场测量为准。
- 3.本图必须经甲方双方认可并签字后方可作为施工依据。

日期

Date

08/13/26

修订

Revision

1

项目

Project

巨鹿路880号

比例

Scale

1:40@A2

1F公卫新建墙立面图

图底编号



Drawing No.

1F.NW.EL-03



项目编号

Project No.



©2025

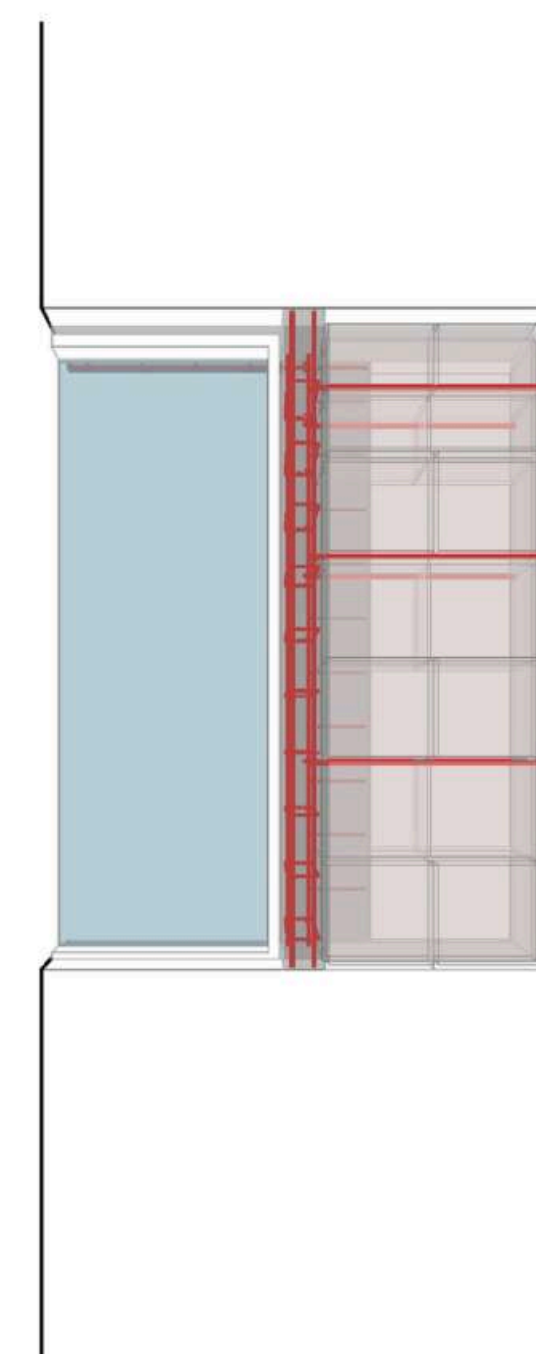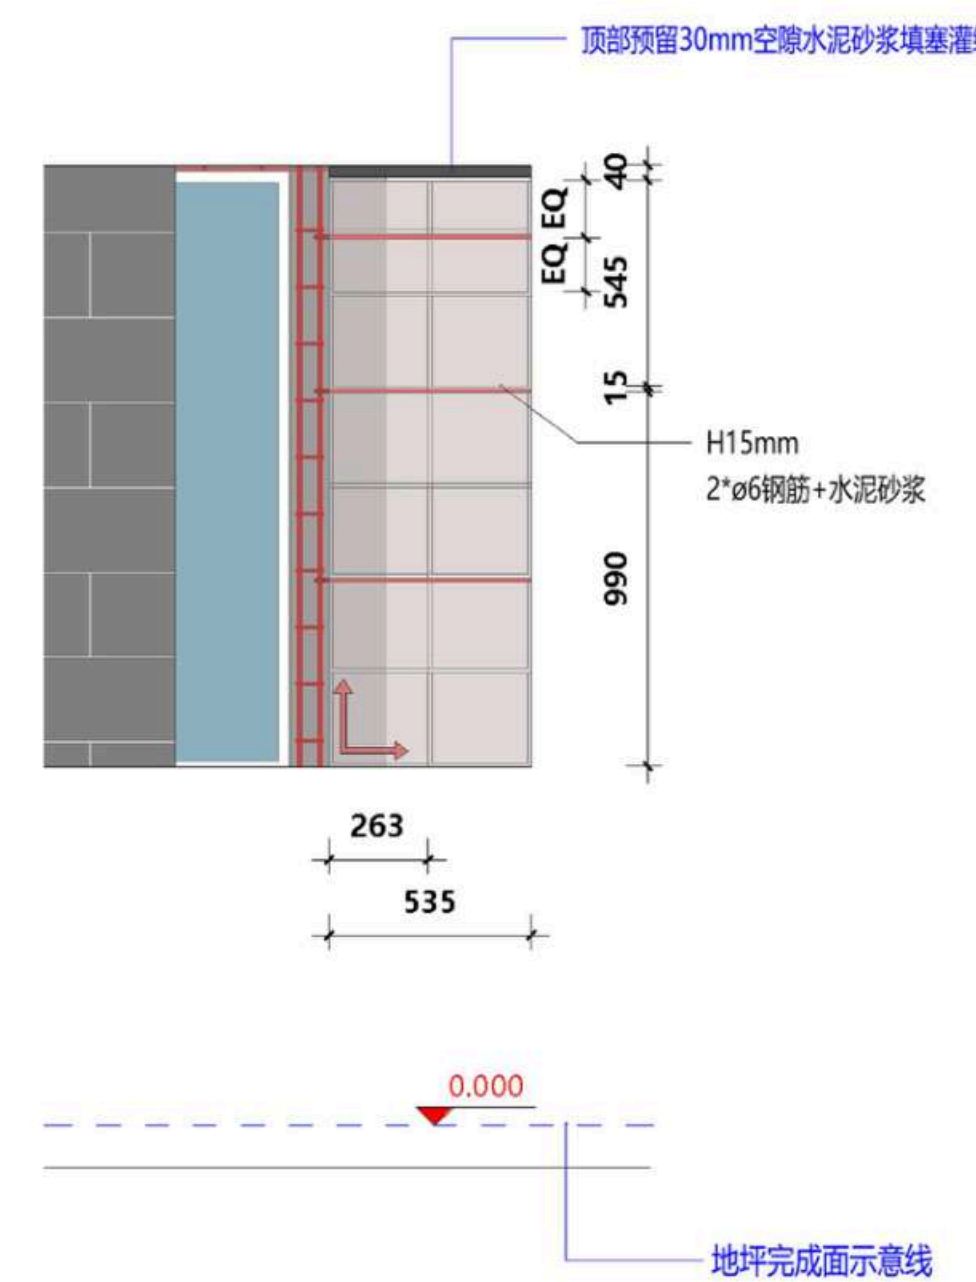

三维示意: 3D-04.1

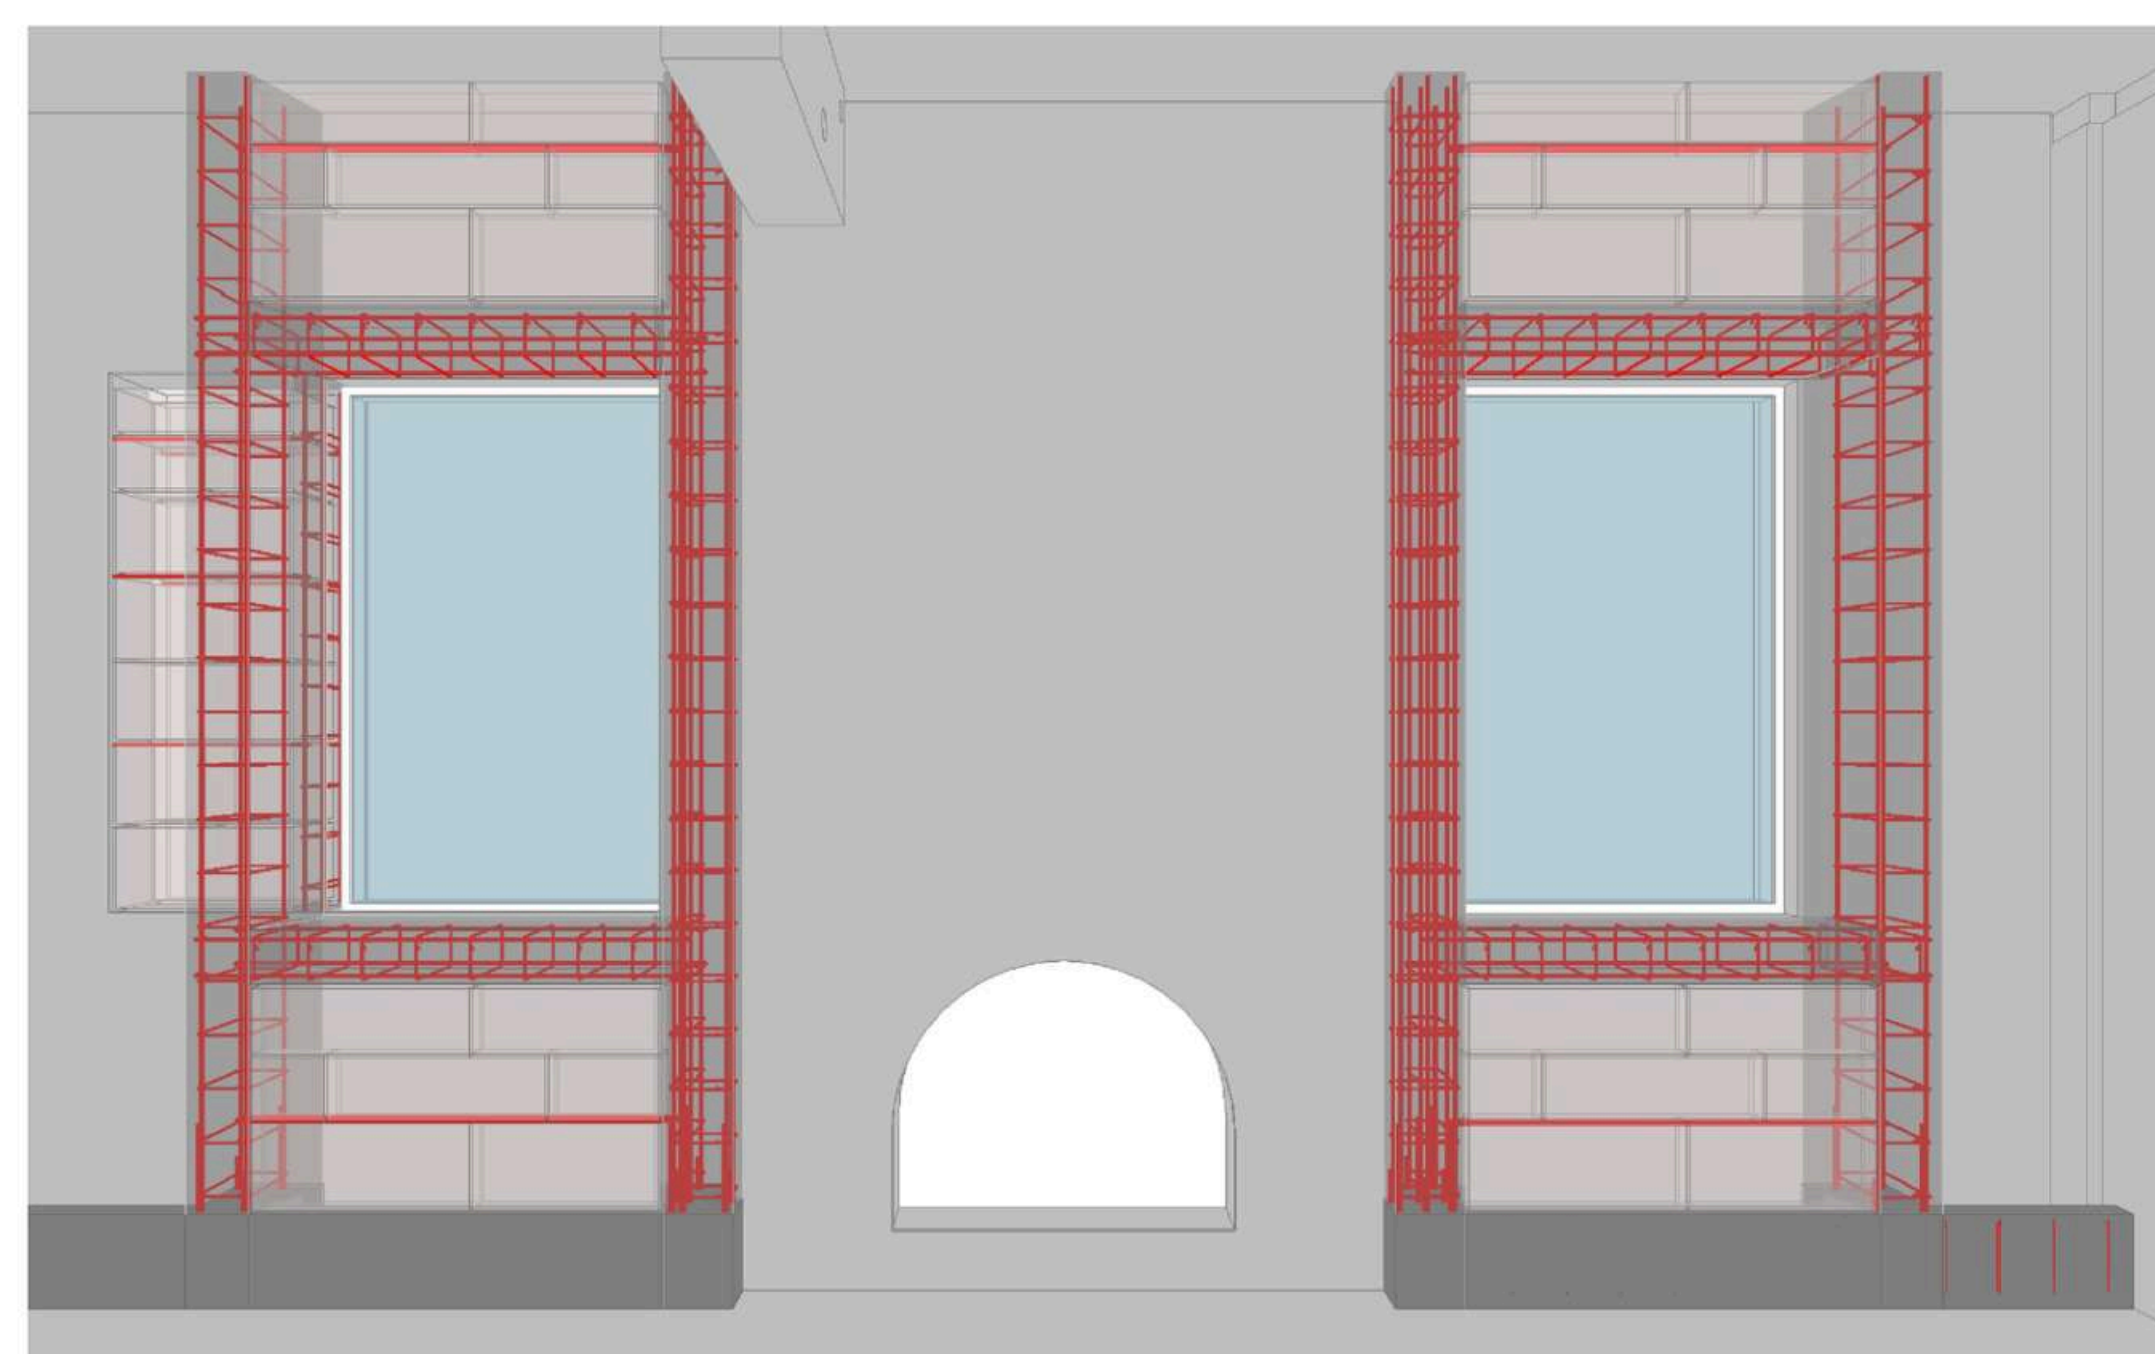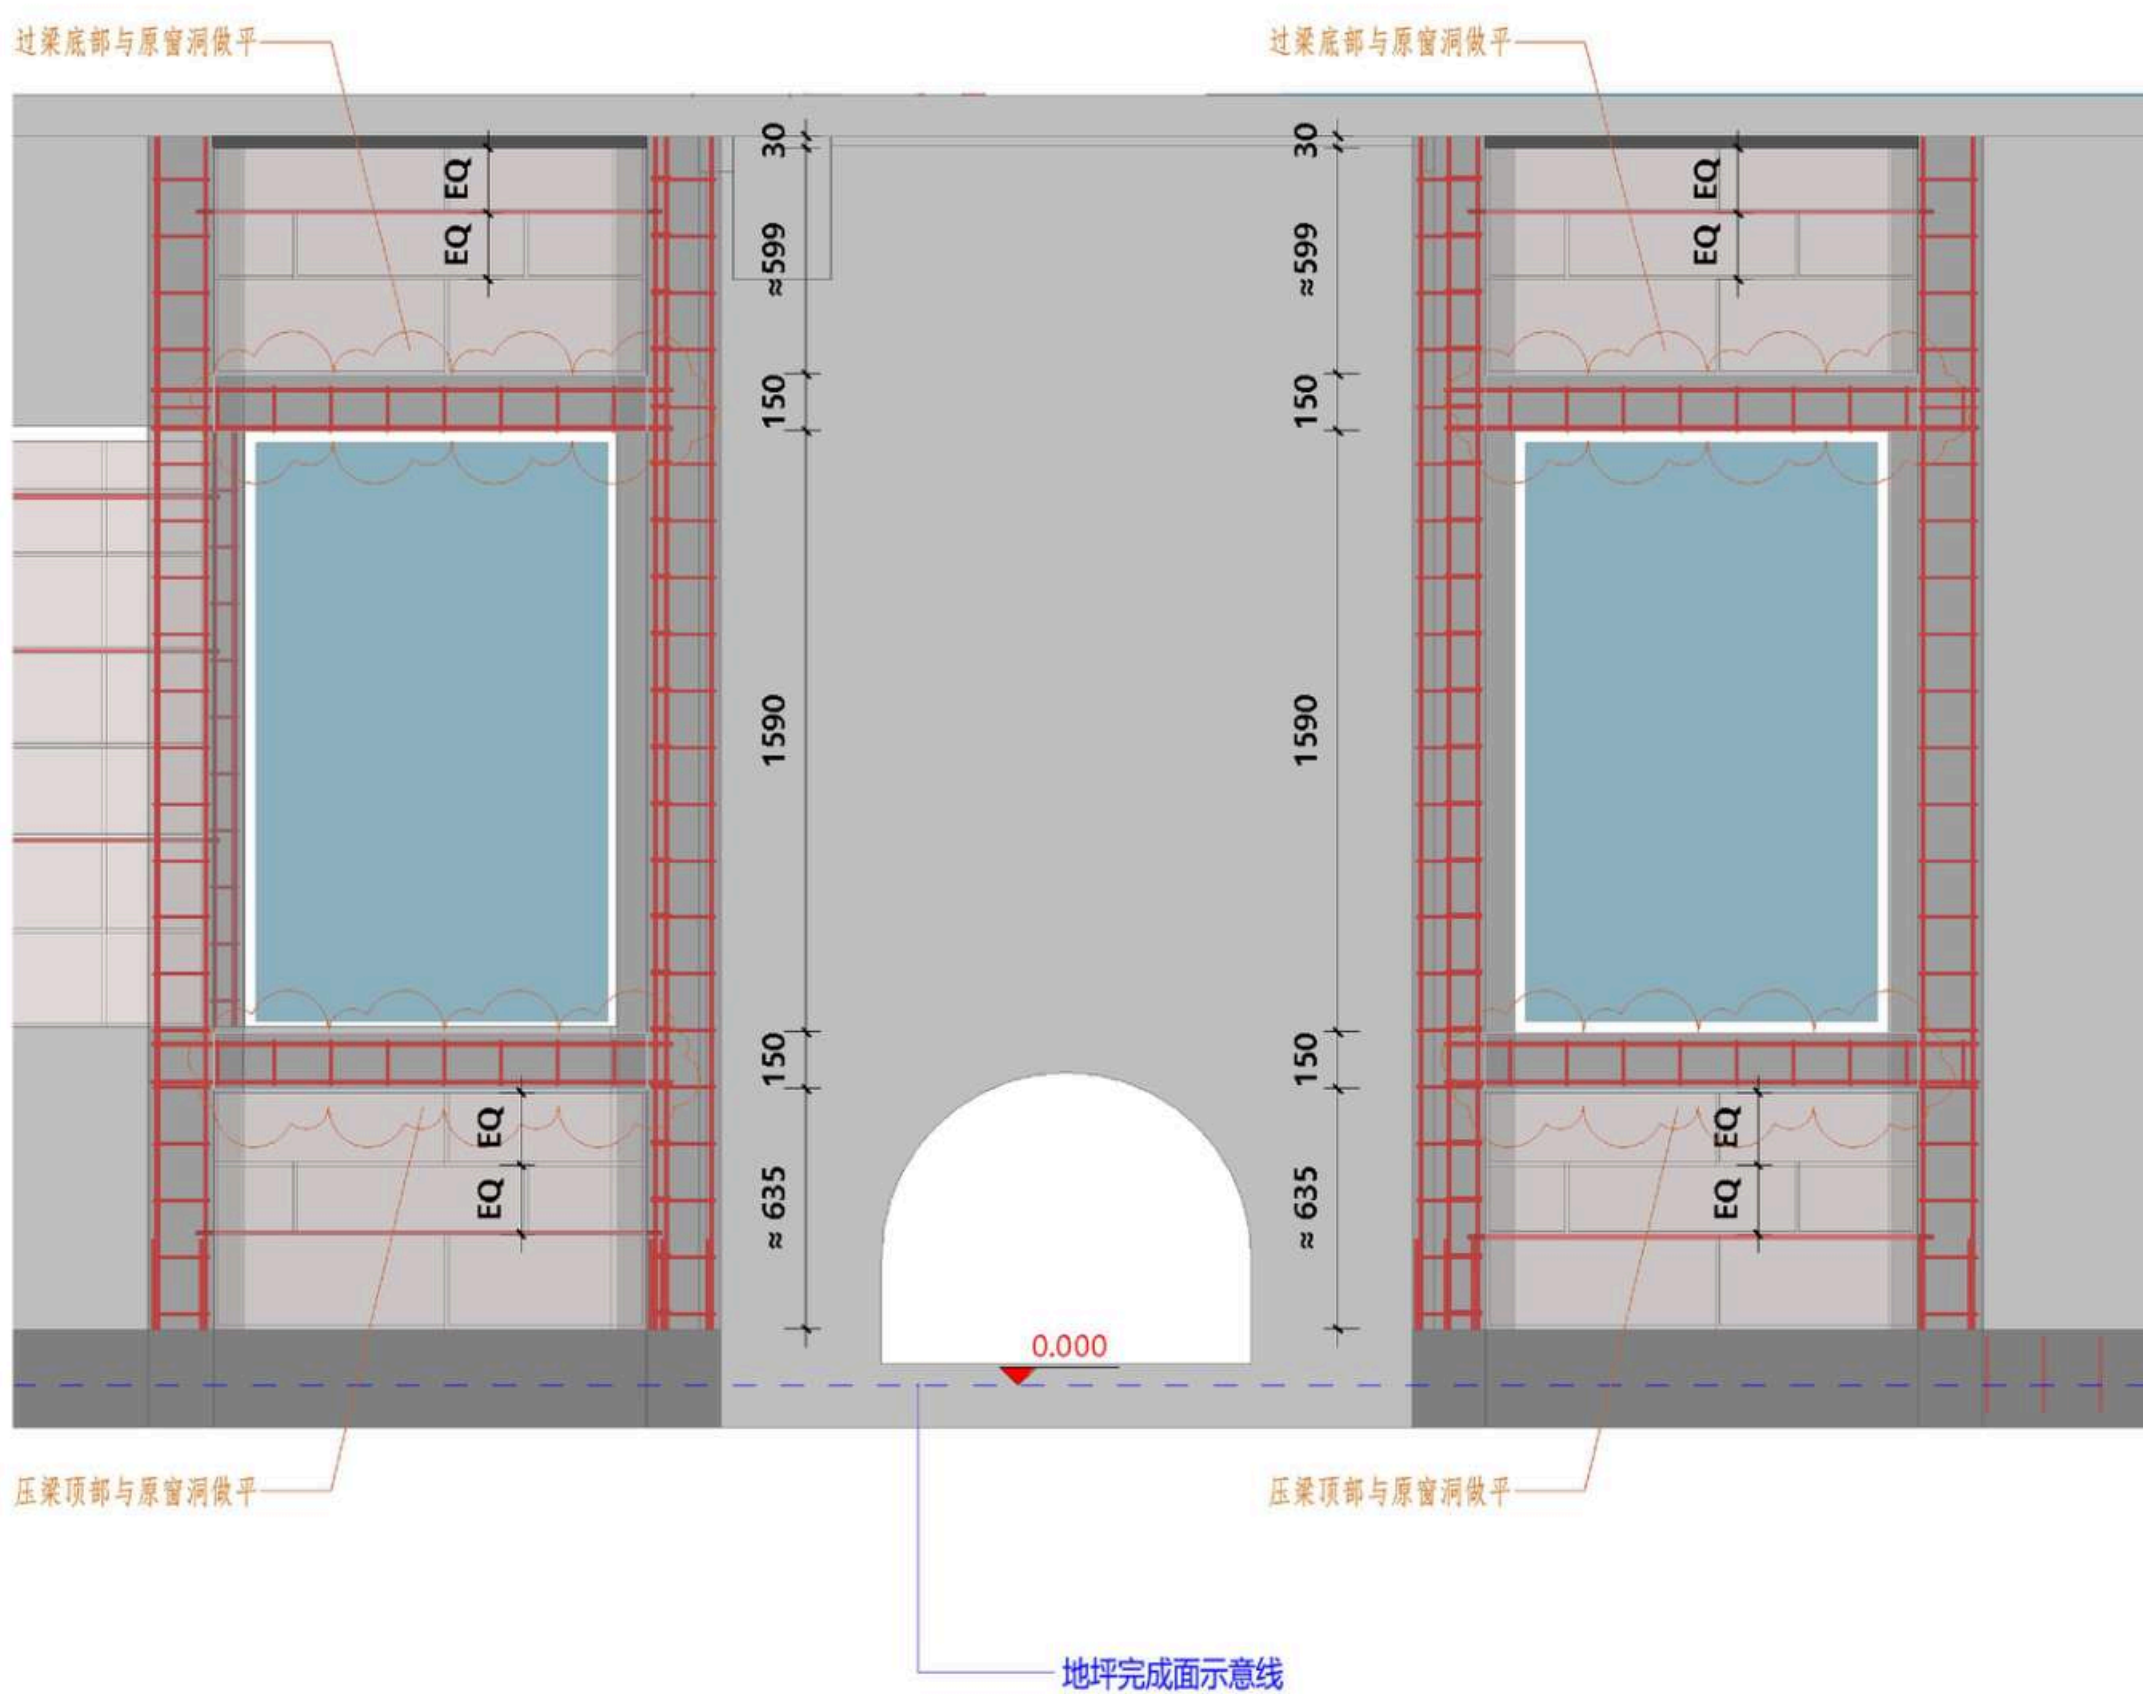

三维示意: 3D-04.3

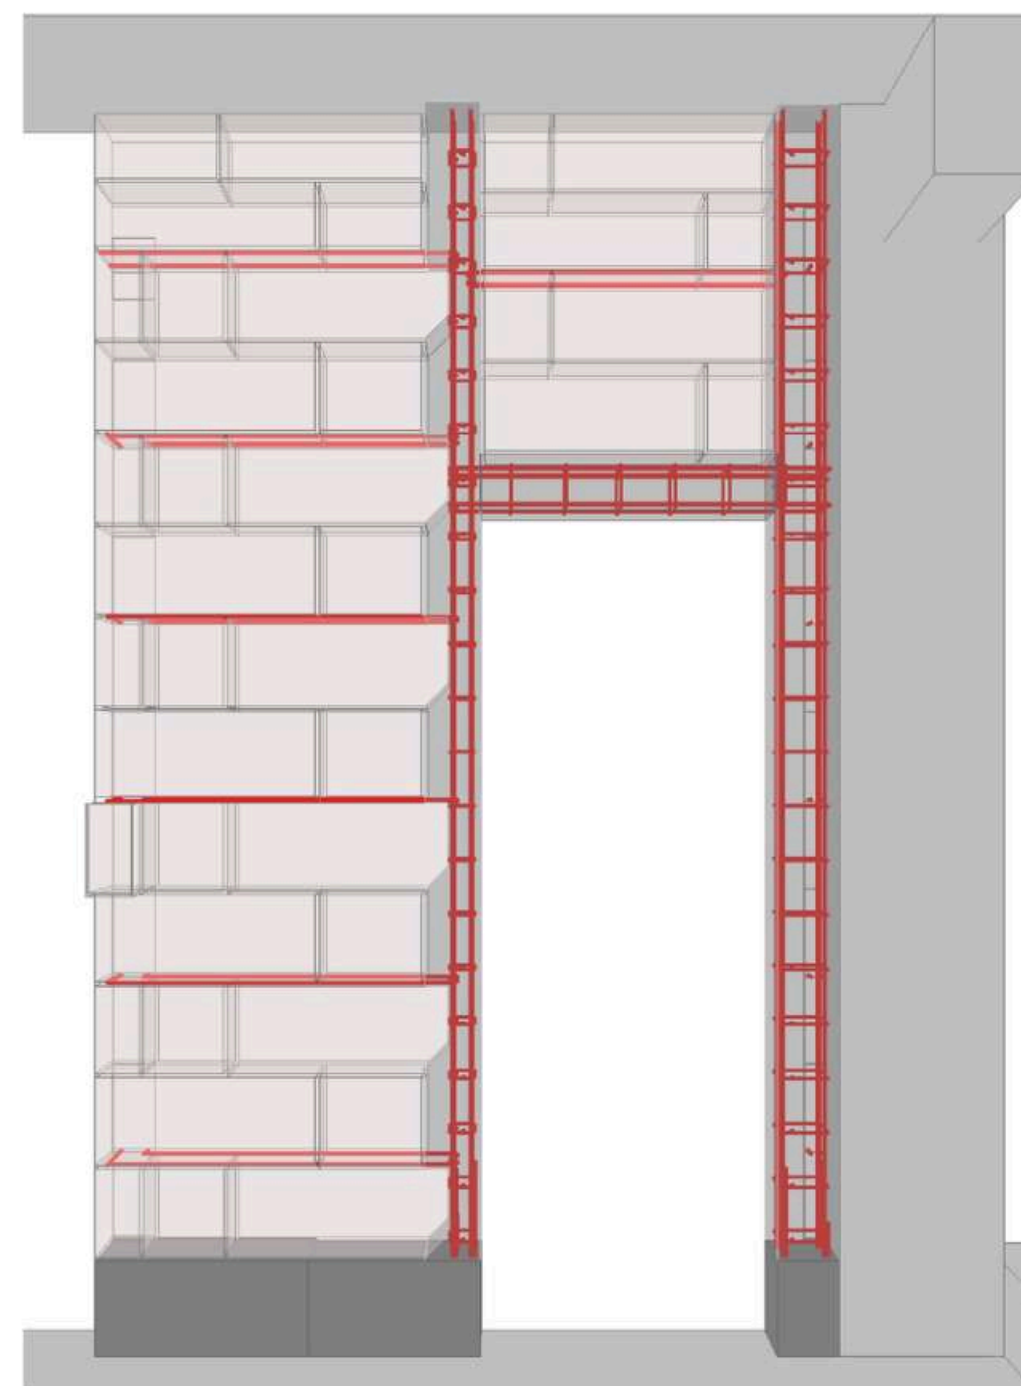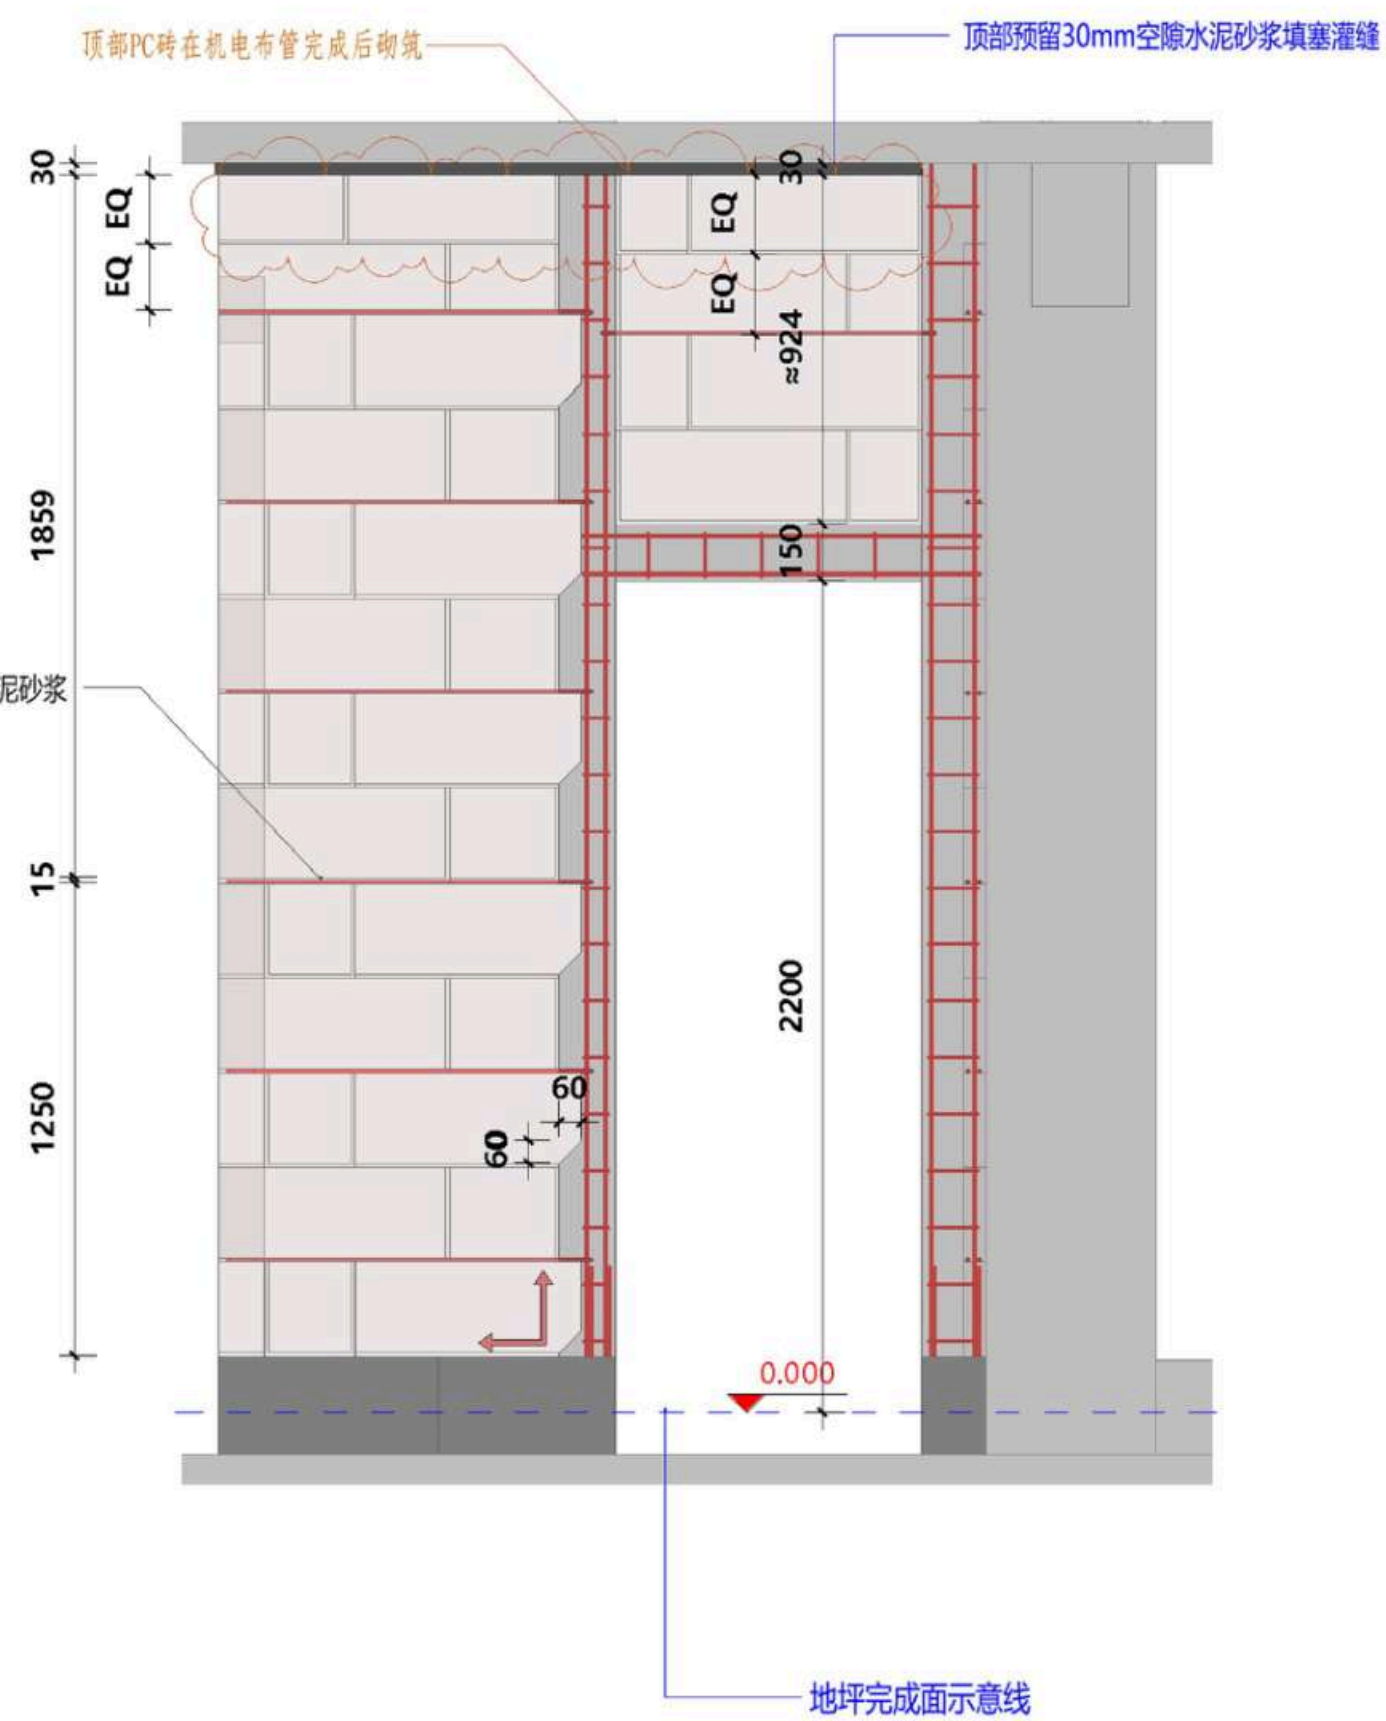

三维示意：3D-04.4

LEGEND图例

编号	图例	说明
1		原始墙、板、柱
2		混凝土外墙、构造柱、马牙砖
3		砌块砖
4		轻钢龙骨
5		钢架墙

图例B 施工时注意事项

编号	图例	说明
1		地面完成线
2		必要尺寸
3		起锚点
4		错缝要求 $a \geq 200$ 且 $b \geq 150$
5		边砖宽度要求 $a \geq 200$
6		$b < 150$ 时 $a = b$

監章

正式施工图
2026-08-13

注释

Note

3. 本图必须经甲乙双方认可并签字方可作为施工依据。

日期

Date _____

Revis

1

1

项目	
----	--

Project

10

100

Scale

10

10




STONY A

Drawn



10

1	2	
---	---	---	---	---	---	---	---	---	----	----	-----	-----	

Project

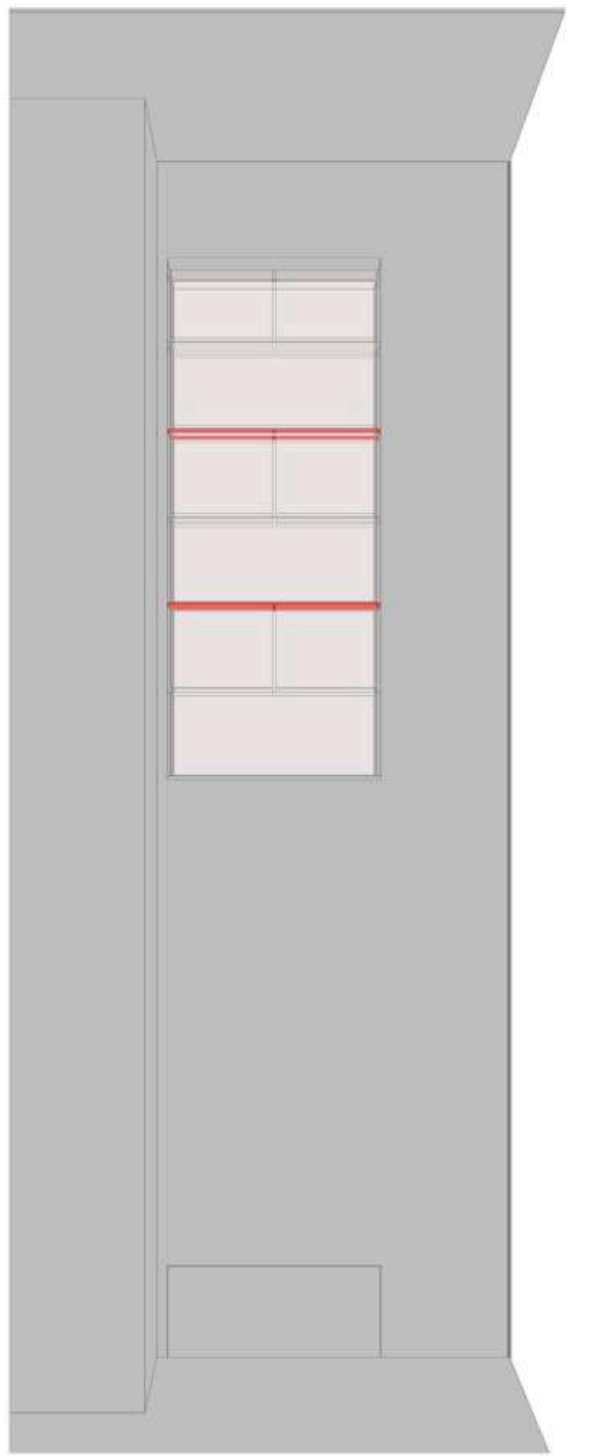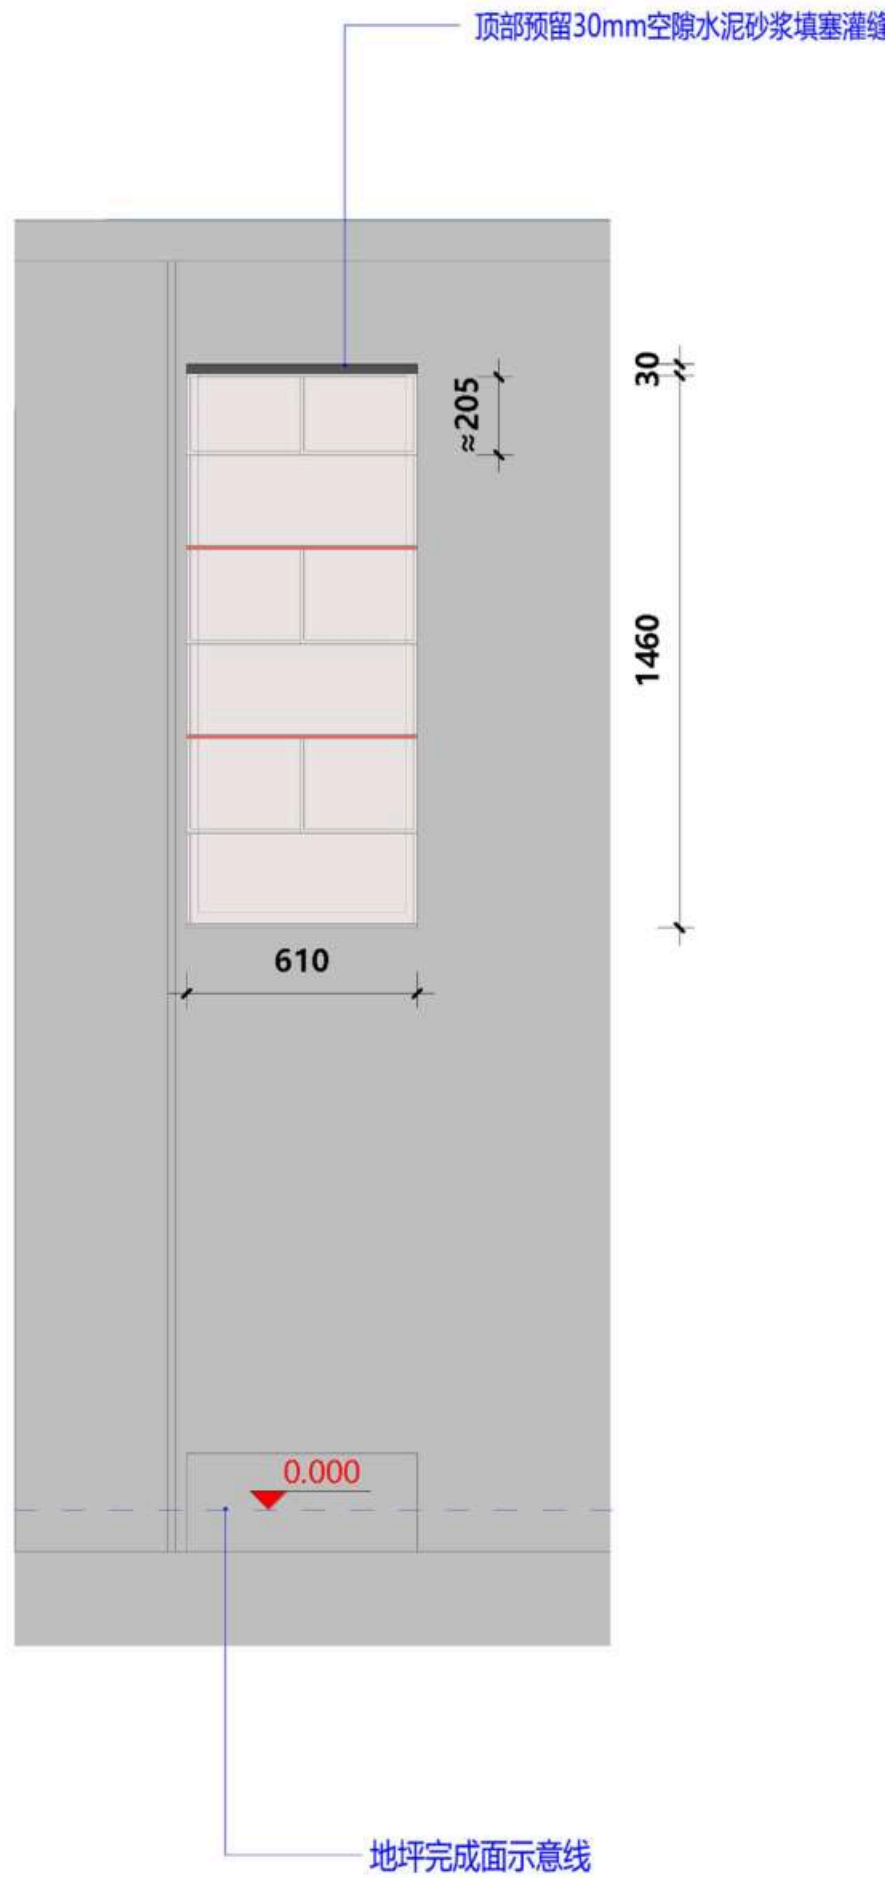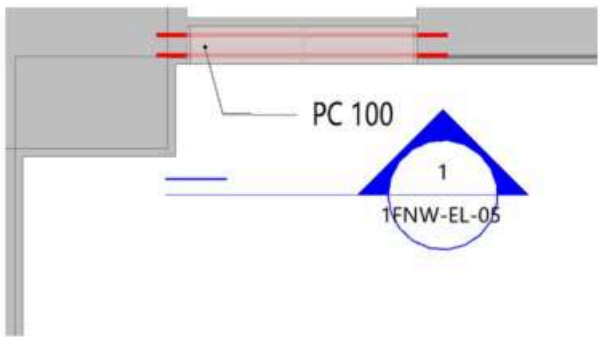

三维示意: 3D-05.1

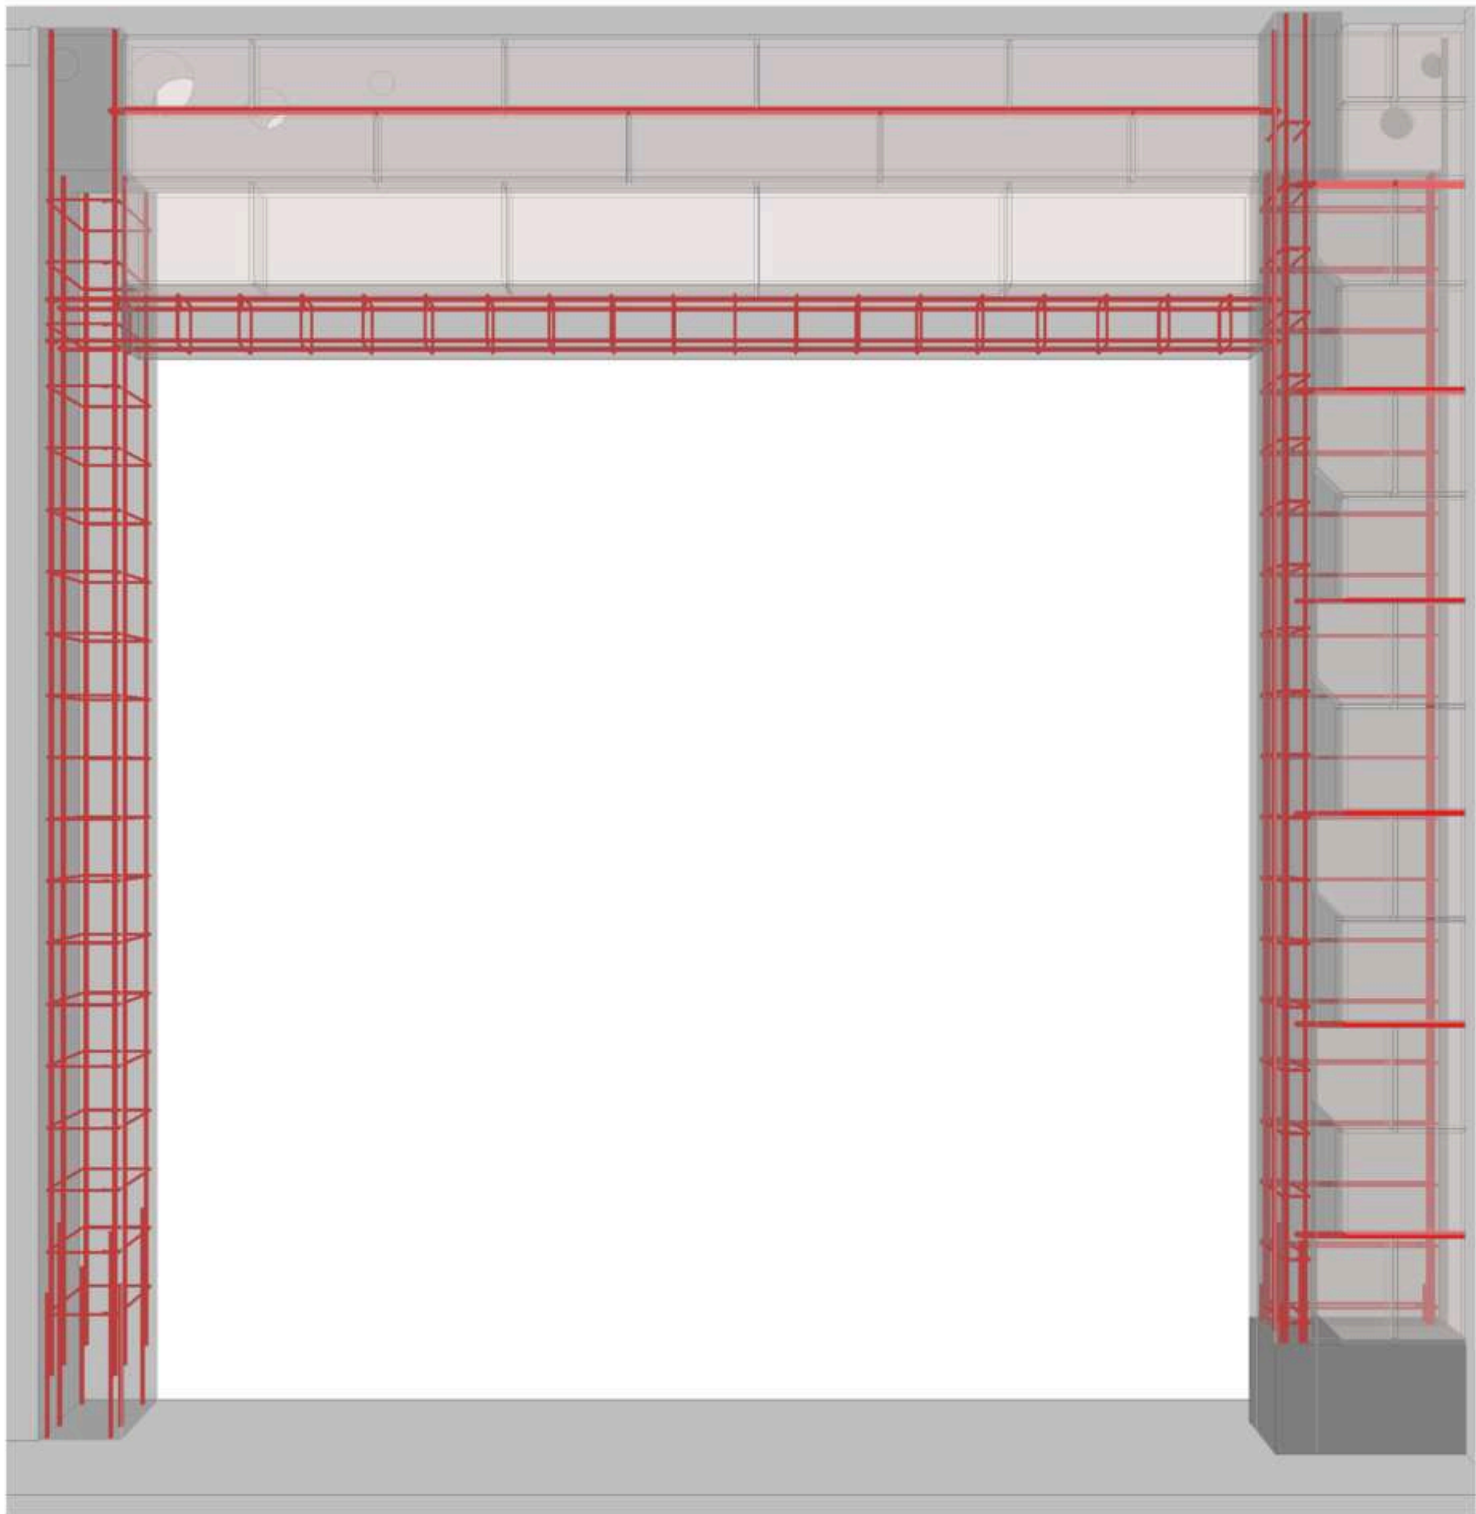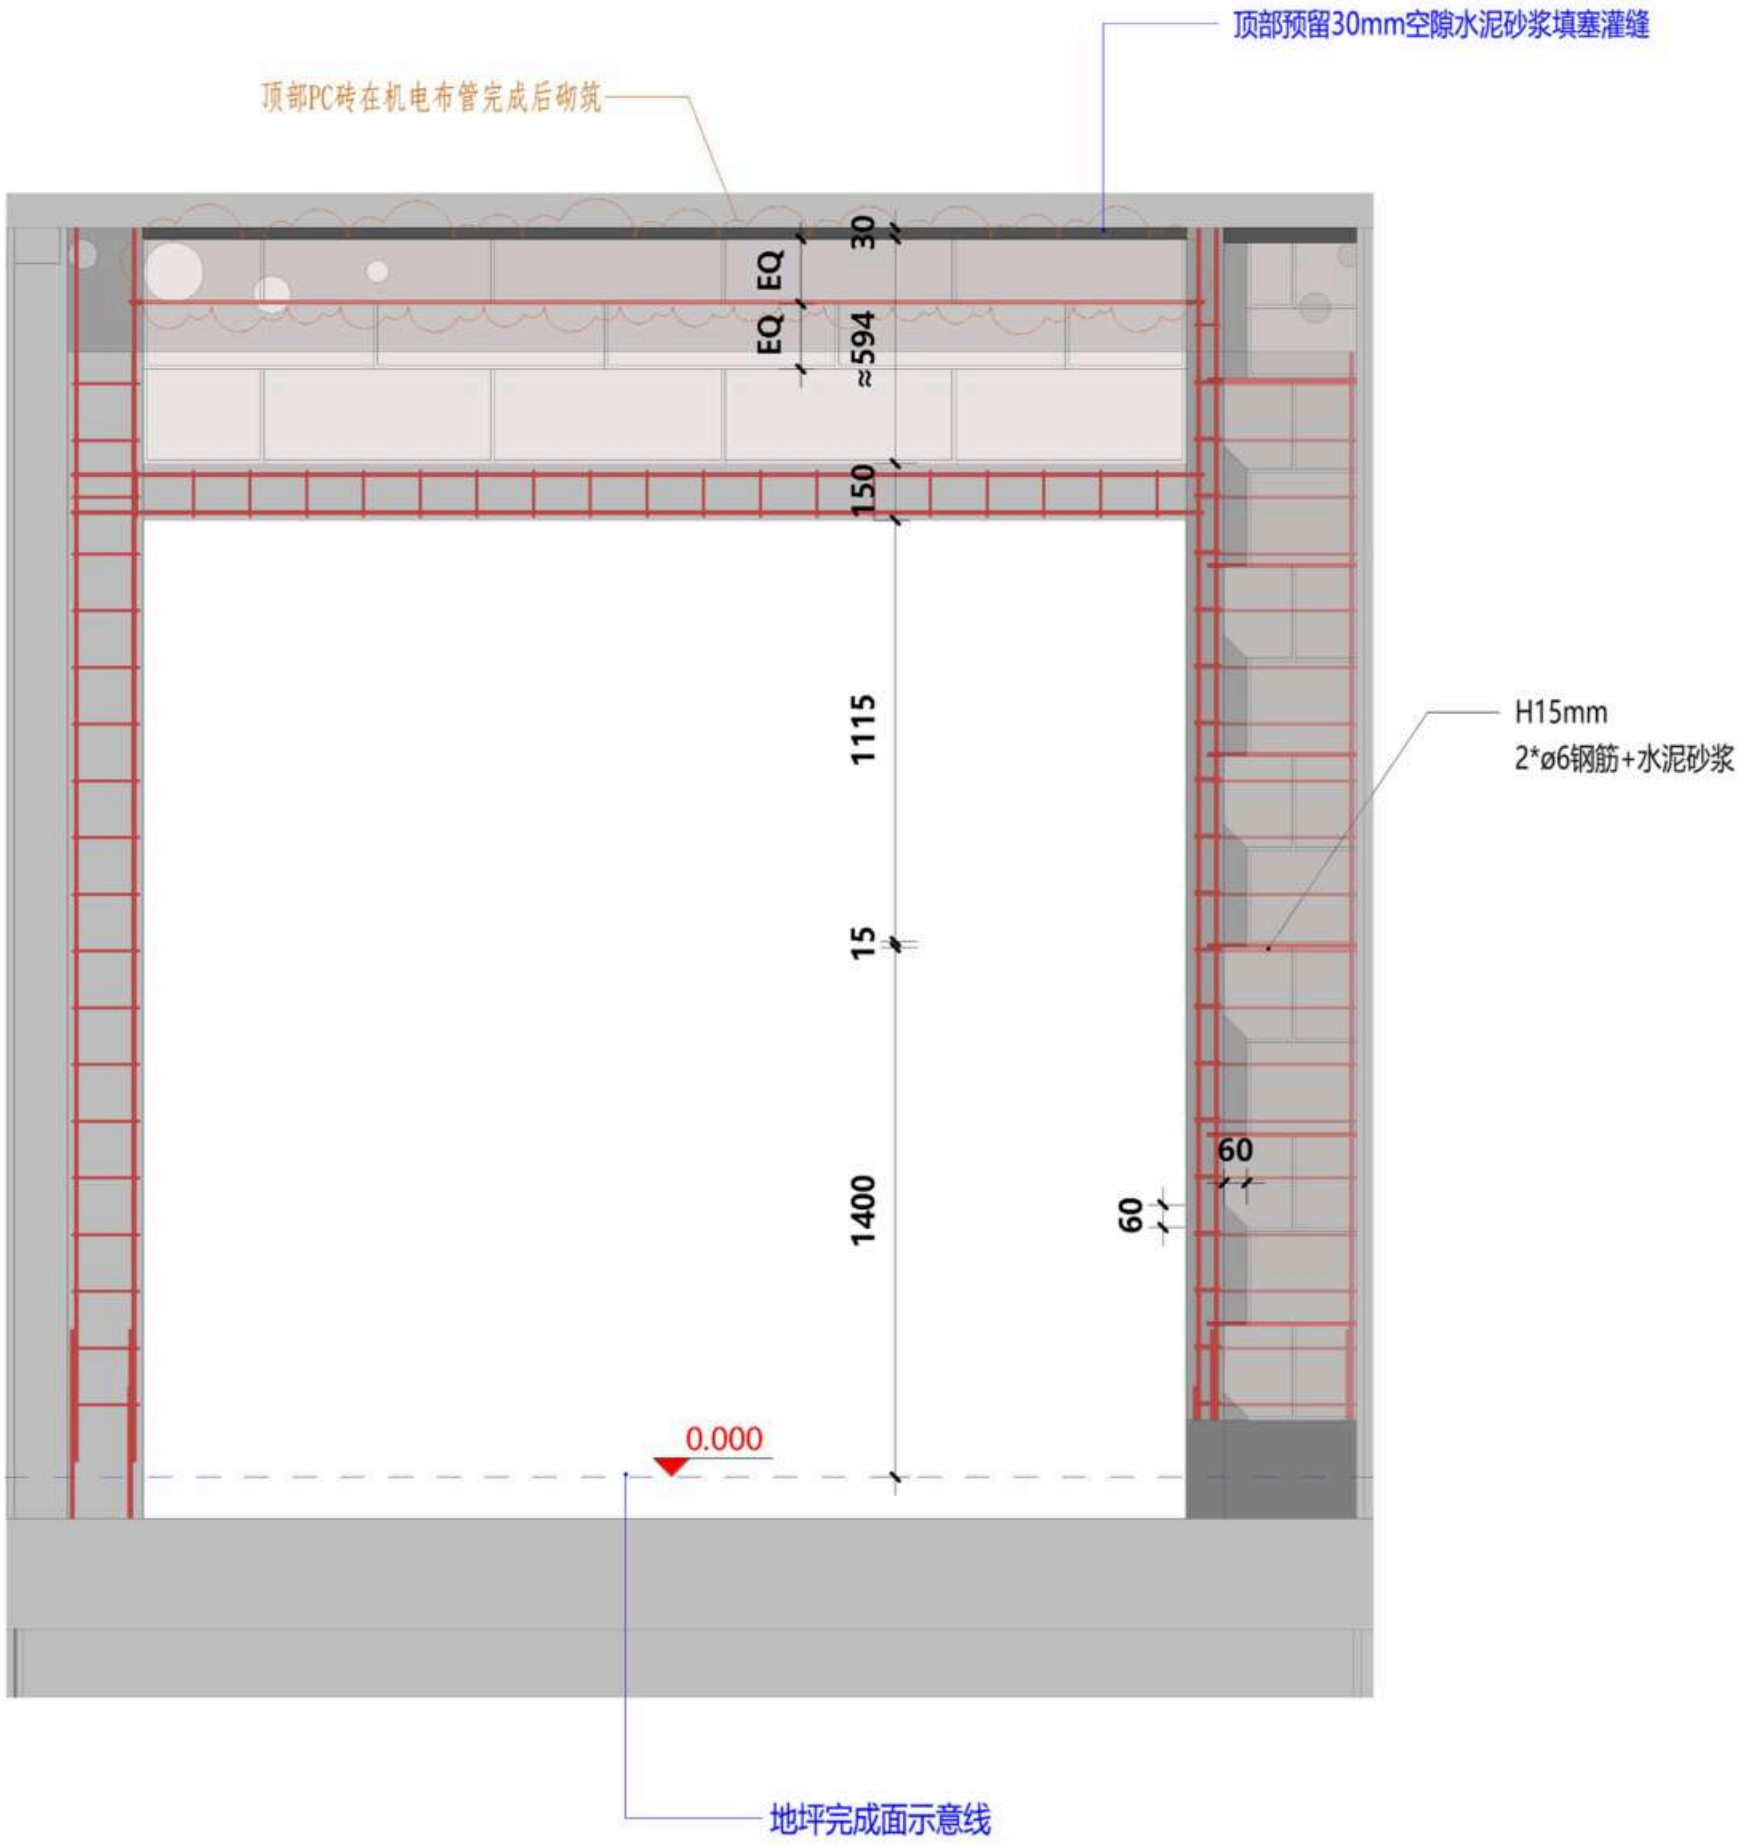

三维示意: 3D-05.3

11130RN

LEGEND图例

图例A 材质分类		
编号	图例	说明
1		原始墙、板、柱
2		混凝土导墙、构造柱、马牙槎
3		砌块砖
4		轻钢龙骨
5		钢架墙

图例B 施工时注意事项

编号	图例	说明
1		地面完成线
2		必要尺寸
3		起铺点
4		错缝要求 a≥200 b≥150
5		边砖宽度要求 a≥200
6		b < 150时 a = b

盖章

正式施工图
2026-08-13

注释

Notes

- 本图仅供参考，不作为施工依据。请施工人员在施工过程中，如有不明之处，请及时与项目负责人联系。
- 施工过程中，如有发现质量问题，请及时与项目负责人联系。
- 本图仅供参考，不作为施工依据。请施工人员在施工过程中，如有不明之处，请及时与项目负责人联系。

日期

Date

08/13/26

修订

Revision

1

项目

Project

巨鹿路880号

比例

Scale

1:20@A2

1F厨房新建墙立面图

图底编号

Drawing No.

1F.NW.EL-05

项目编号

Project No.

©2025

1

1F.NW.EL-05

1F厨房新建墙立面图1

Scale比例 1:20@A2

3

1F.NW.EL-05

1F厨房新建墙立面图3

Scale比例 1:20@A2

LEGEND图例

图例A 材质分类		
编号	图例	说明
1		原始墙、板、柱
2		混凝土导墙、构造柱、马牙槎
3		砌块砖
4		轻钢龙骨
5		钢架墙

图例B 施工时注意事项		
编号	图例	说明
1		地面完成线
2		必要尺寸
3		起铺点
4		错缝要求 $a \geq 200$ $b \geq 150$
5		边砖宽度要求 $a \geq 200$
6		$b < 150$ 时 $a = b$

盖章

正式施工图
2026-08-13

注释

Notes

1.本图纸如与现场尺寸有误, 请施工人员与项目负责人联系。
2.施工前施工人员应认真查阅此图, 如有不明尺寸, 按现场测量为准。
3.本图纸必须经甲乙双方认可并签字方可作为施工依据。

日期

Date

08/13/26

修订

Revision

1

项目

Project

巨鹿路880号

比例

Scale

1:20@A2

1F茶室新建墙立面

图纸编号



Drawing No.

1F.NW.EL-06

项目编号

Project No.

©2025

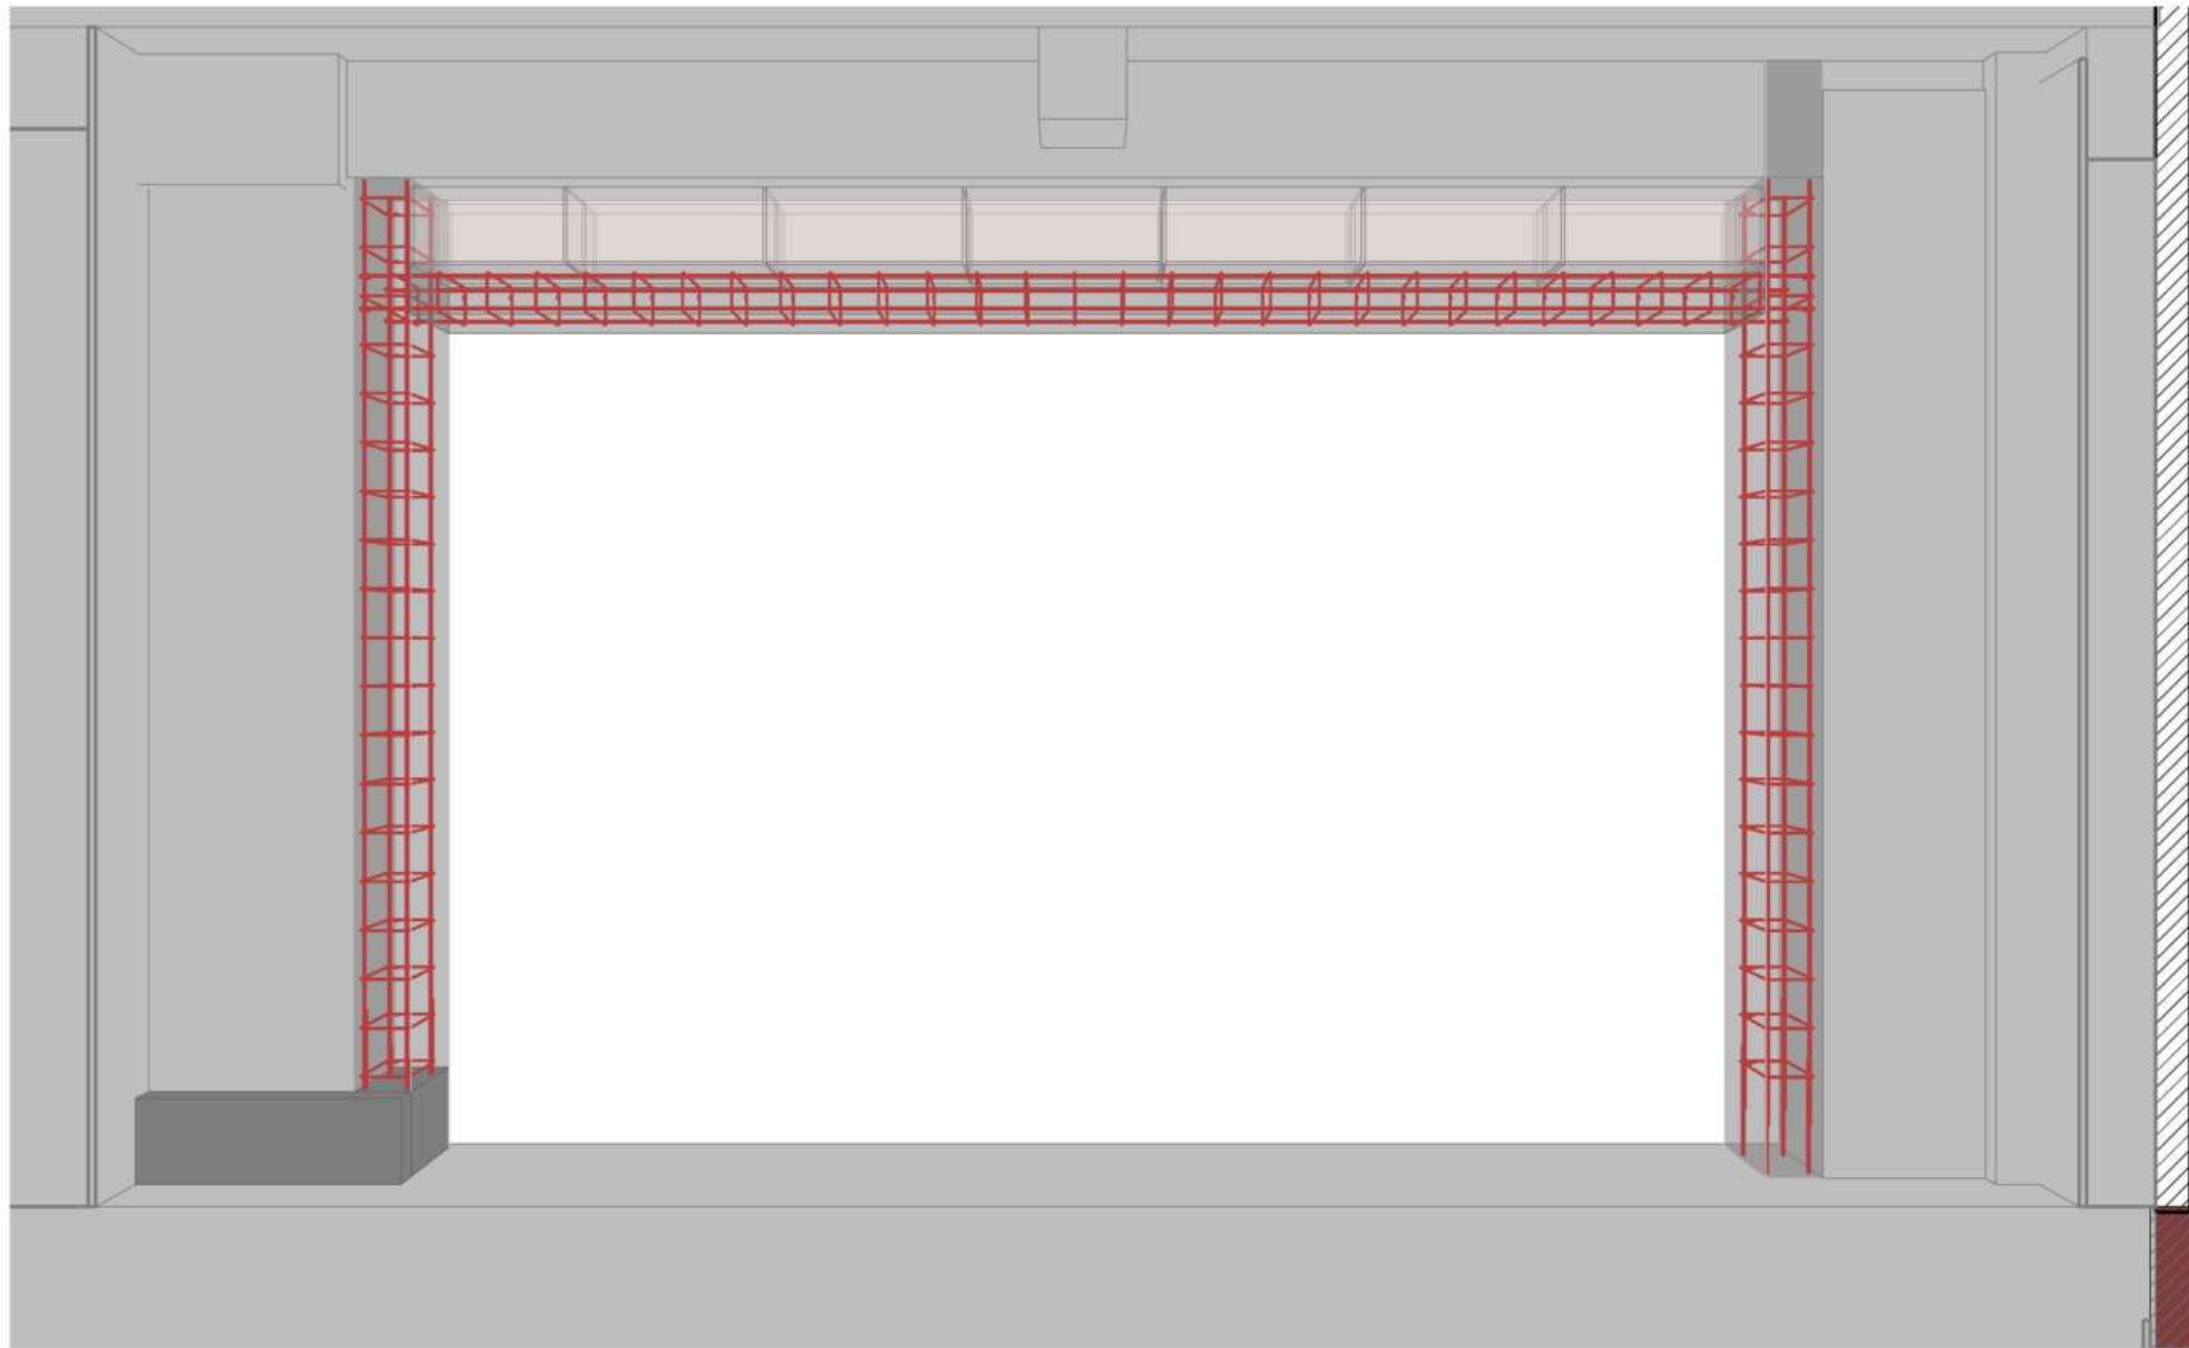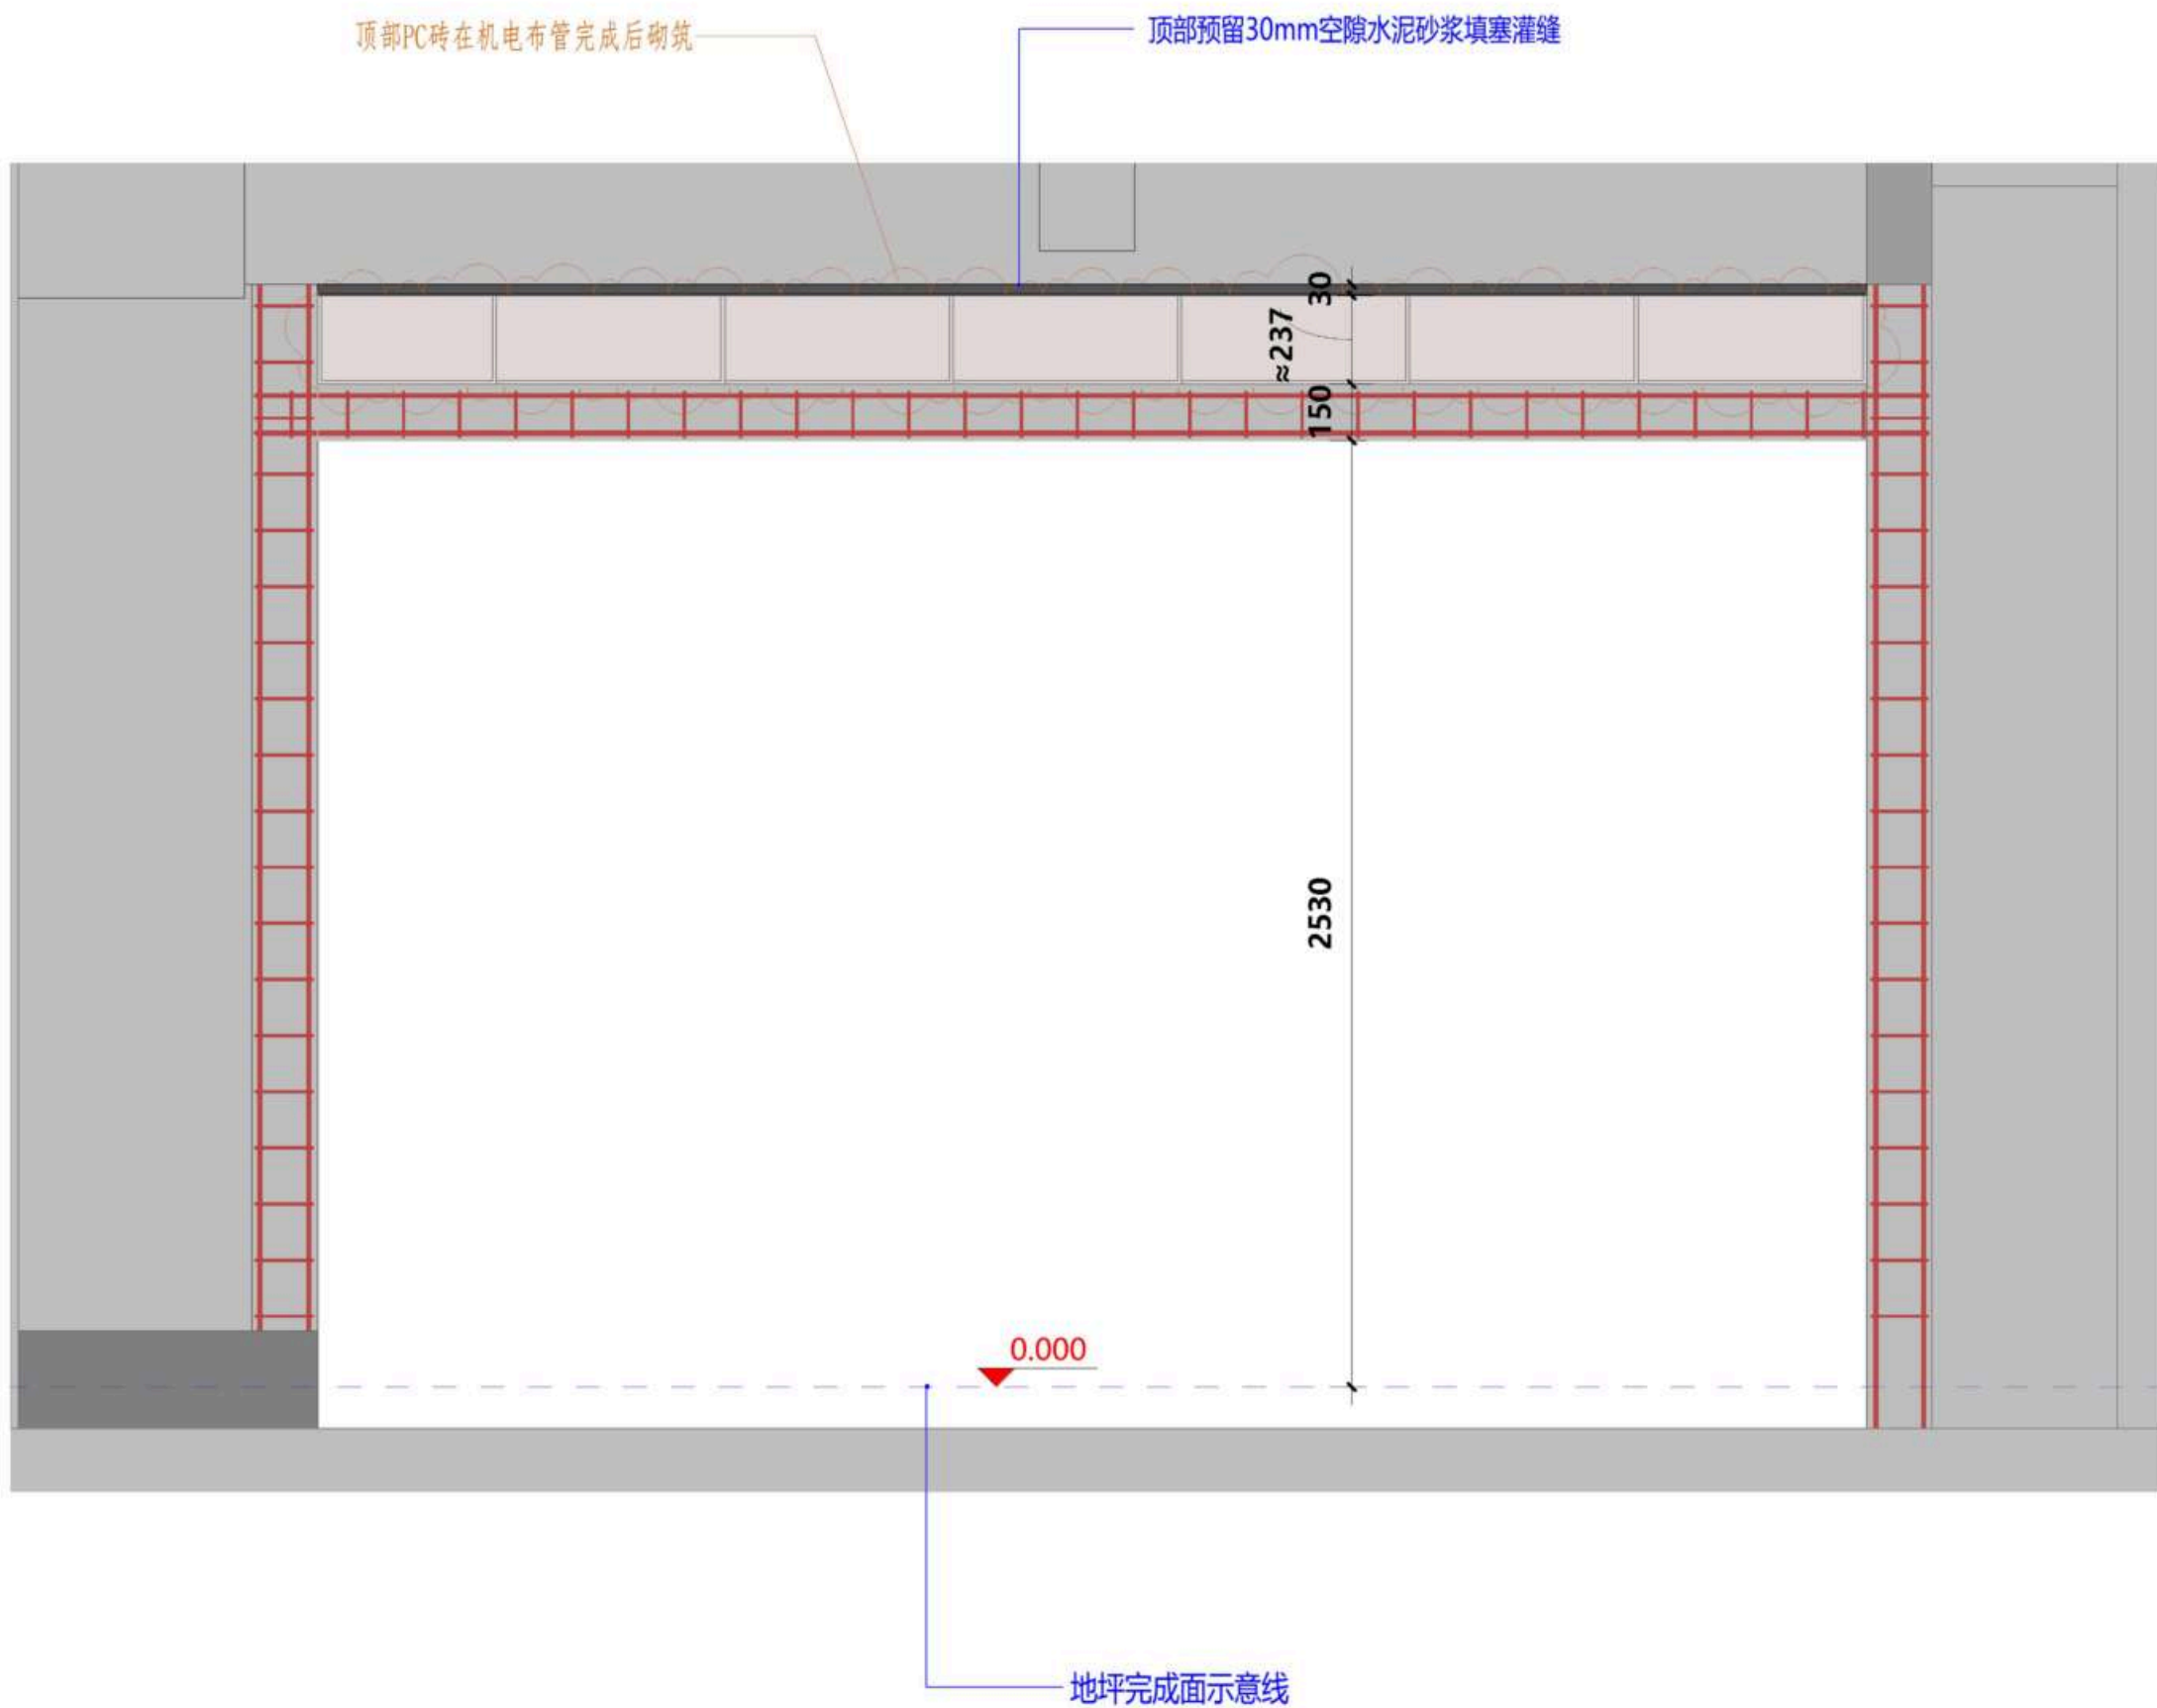

三维示意: 3D-06.2