



LEGEND图例

编号	图例	说明
1		原始墙、板、柱
2		混凝土导墙
3		砌块砖
4		构造柱
5		过梁
6		轻钢龙骨
7		钢架墙

盖章

正式施工图
2026-08-21

注释

Notes

- 本图纸如与现场尺寸有误，请施工人员与项目负责人联系。
- 施工前施工人员应认真查阅此图，如有不明尺寸，按现场测量为准。
- 本图纸必须经甲乙双方认可并签字方可作为施工依据。

日期

Date

08/21/26

修订

Revision

项目

Project

巨鹿路880号

比例

Scale

1:40@A2

1F轻钢龙骨钢架墙平面图

图纸编号


Drawing No.

1F.NW.PL-07

项目编号

Project No.

© 2026

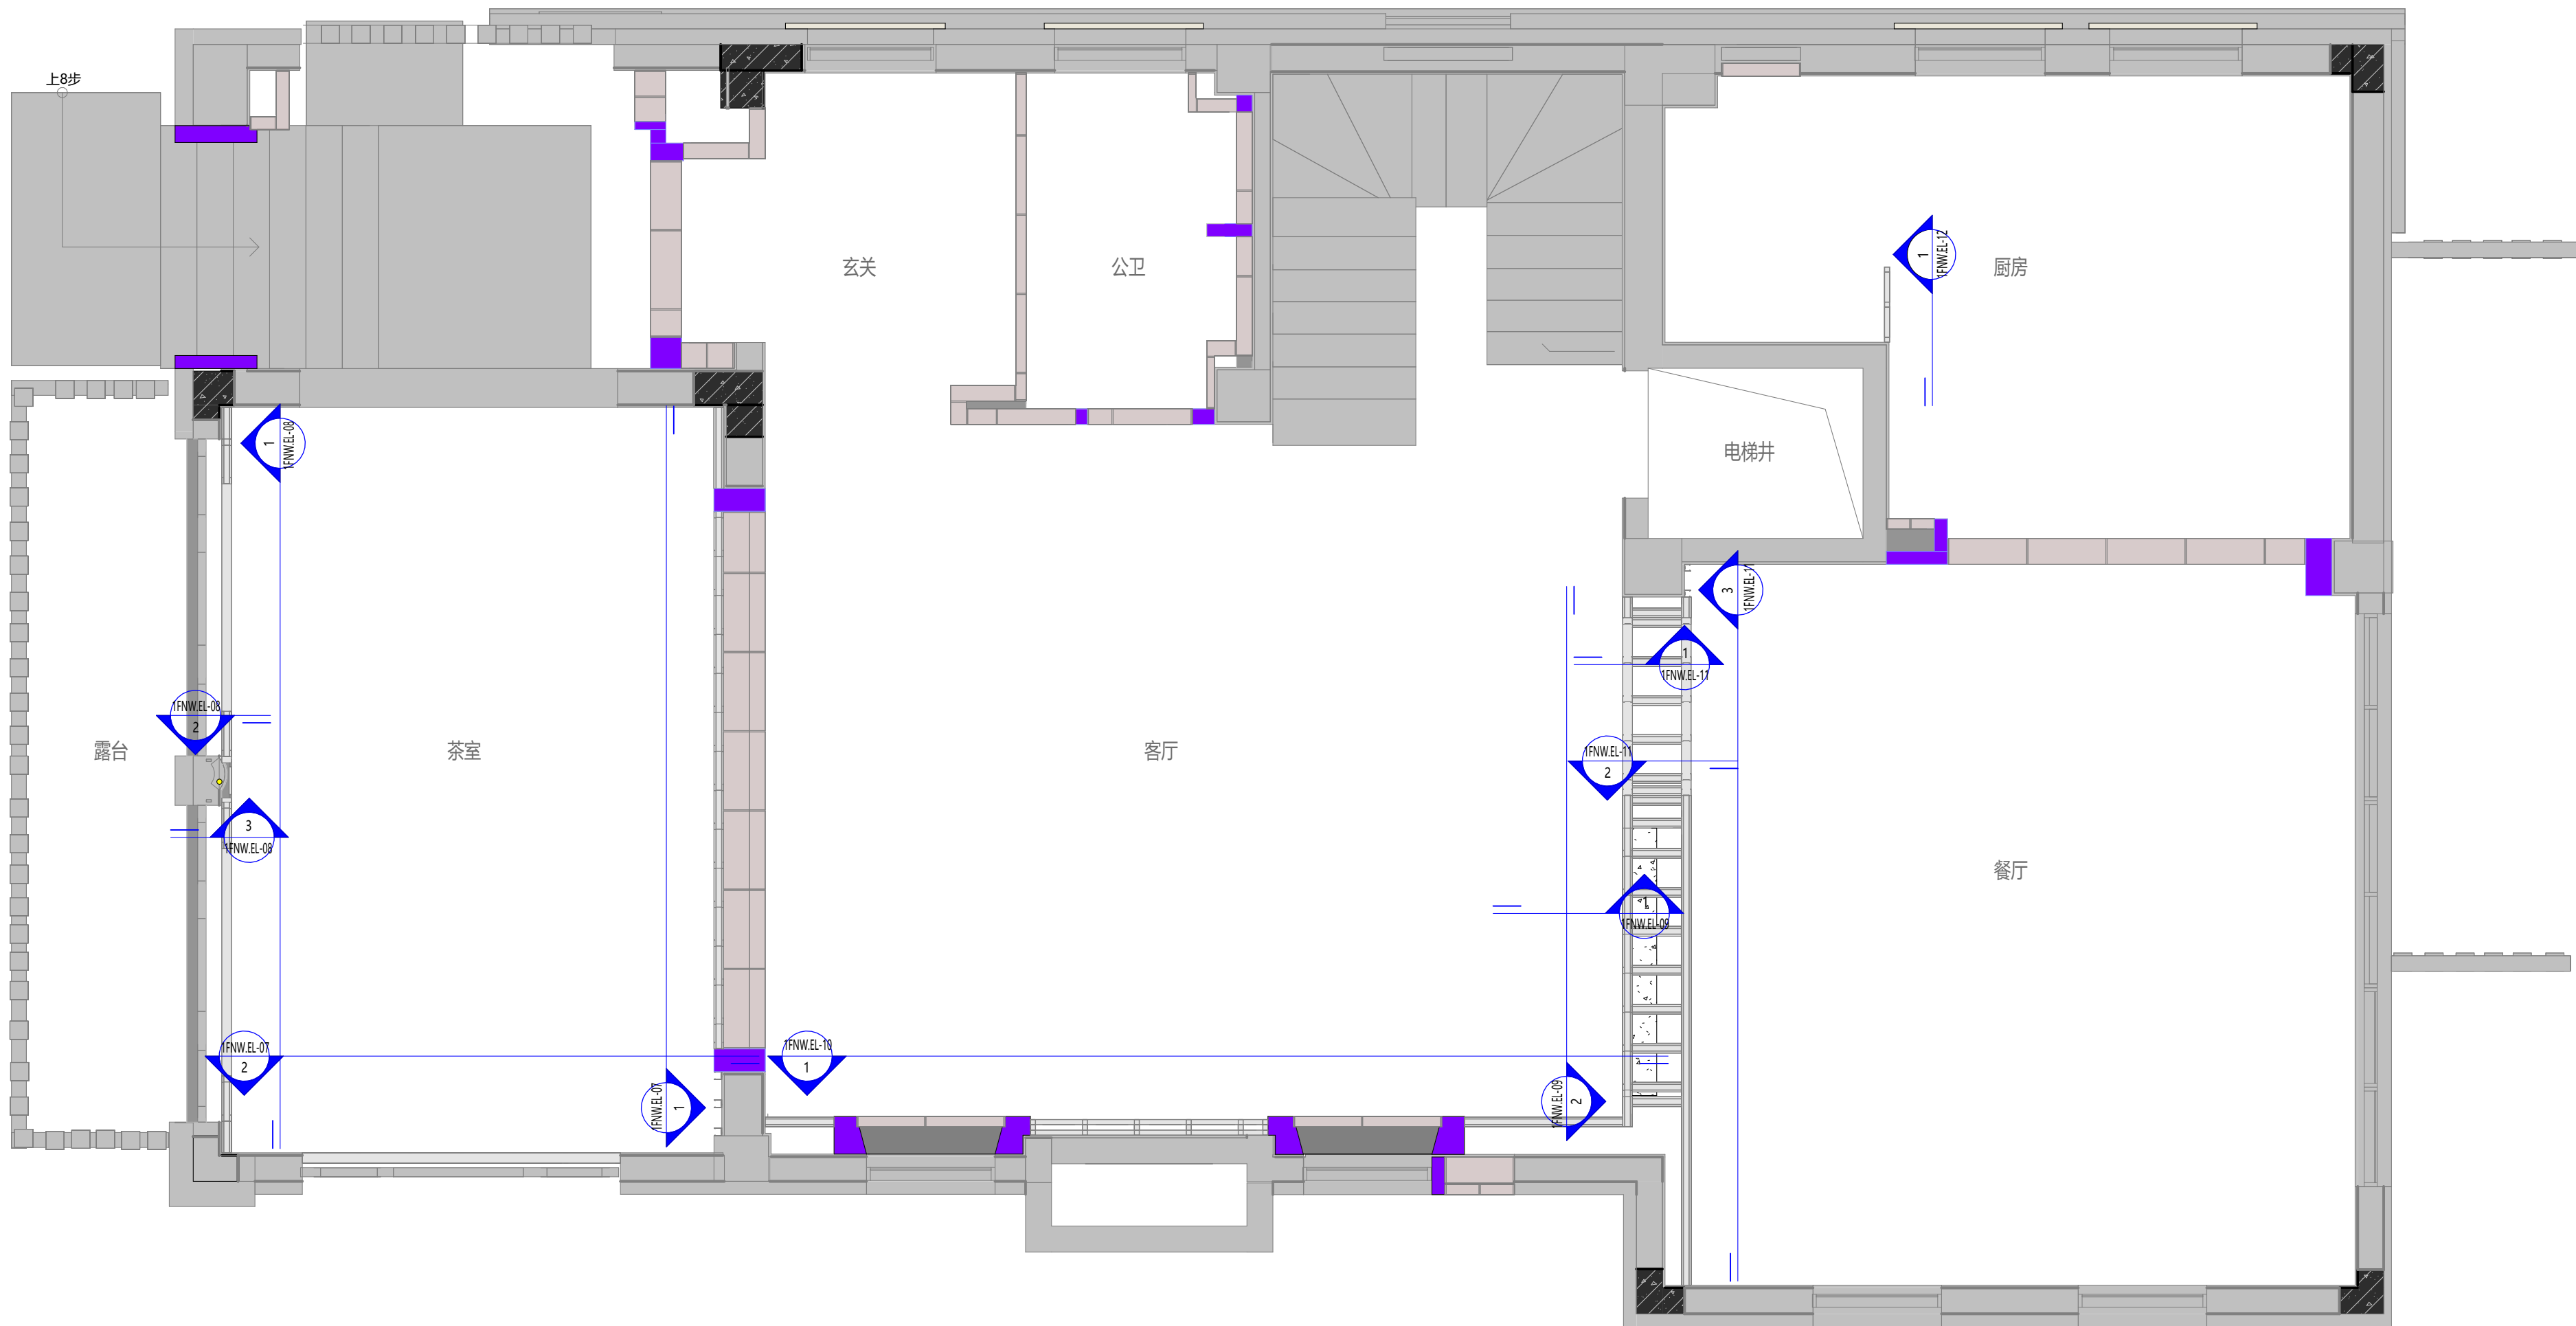

LEGEND图例

编号	图例	说明
1		原始墙、板、柱
2		混凝土导墙
3		砌块砖
4		构造柱
5		过梁
6		轻钢龙骨
7		钢架墙

盖章

正式施工图
2026-08-21注释
Notes

- 1.本图纸如与现场尺寸有误，请施工人员与项目负责人联系。
- 2.施工前施工人员应认真查阅此图，如有不明确尺寸，按现场测量为准。
- 3.本图纸必须经甲乙双方认可并签字方可作为施工依据。

日期
Date 08/21/26修订
Revision

1

项目
Project

巨鹿路880号




比例
Scale 1:40@A2

1F轻钢龙骨钢架墙索引图




图纸编号
Drawing No.

1F.NW.PL-08

项目编号
Project No. © 2026

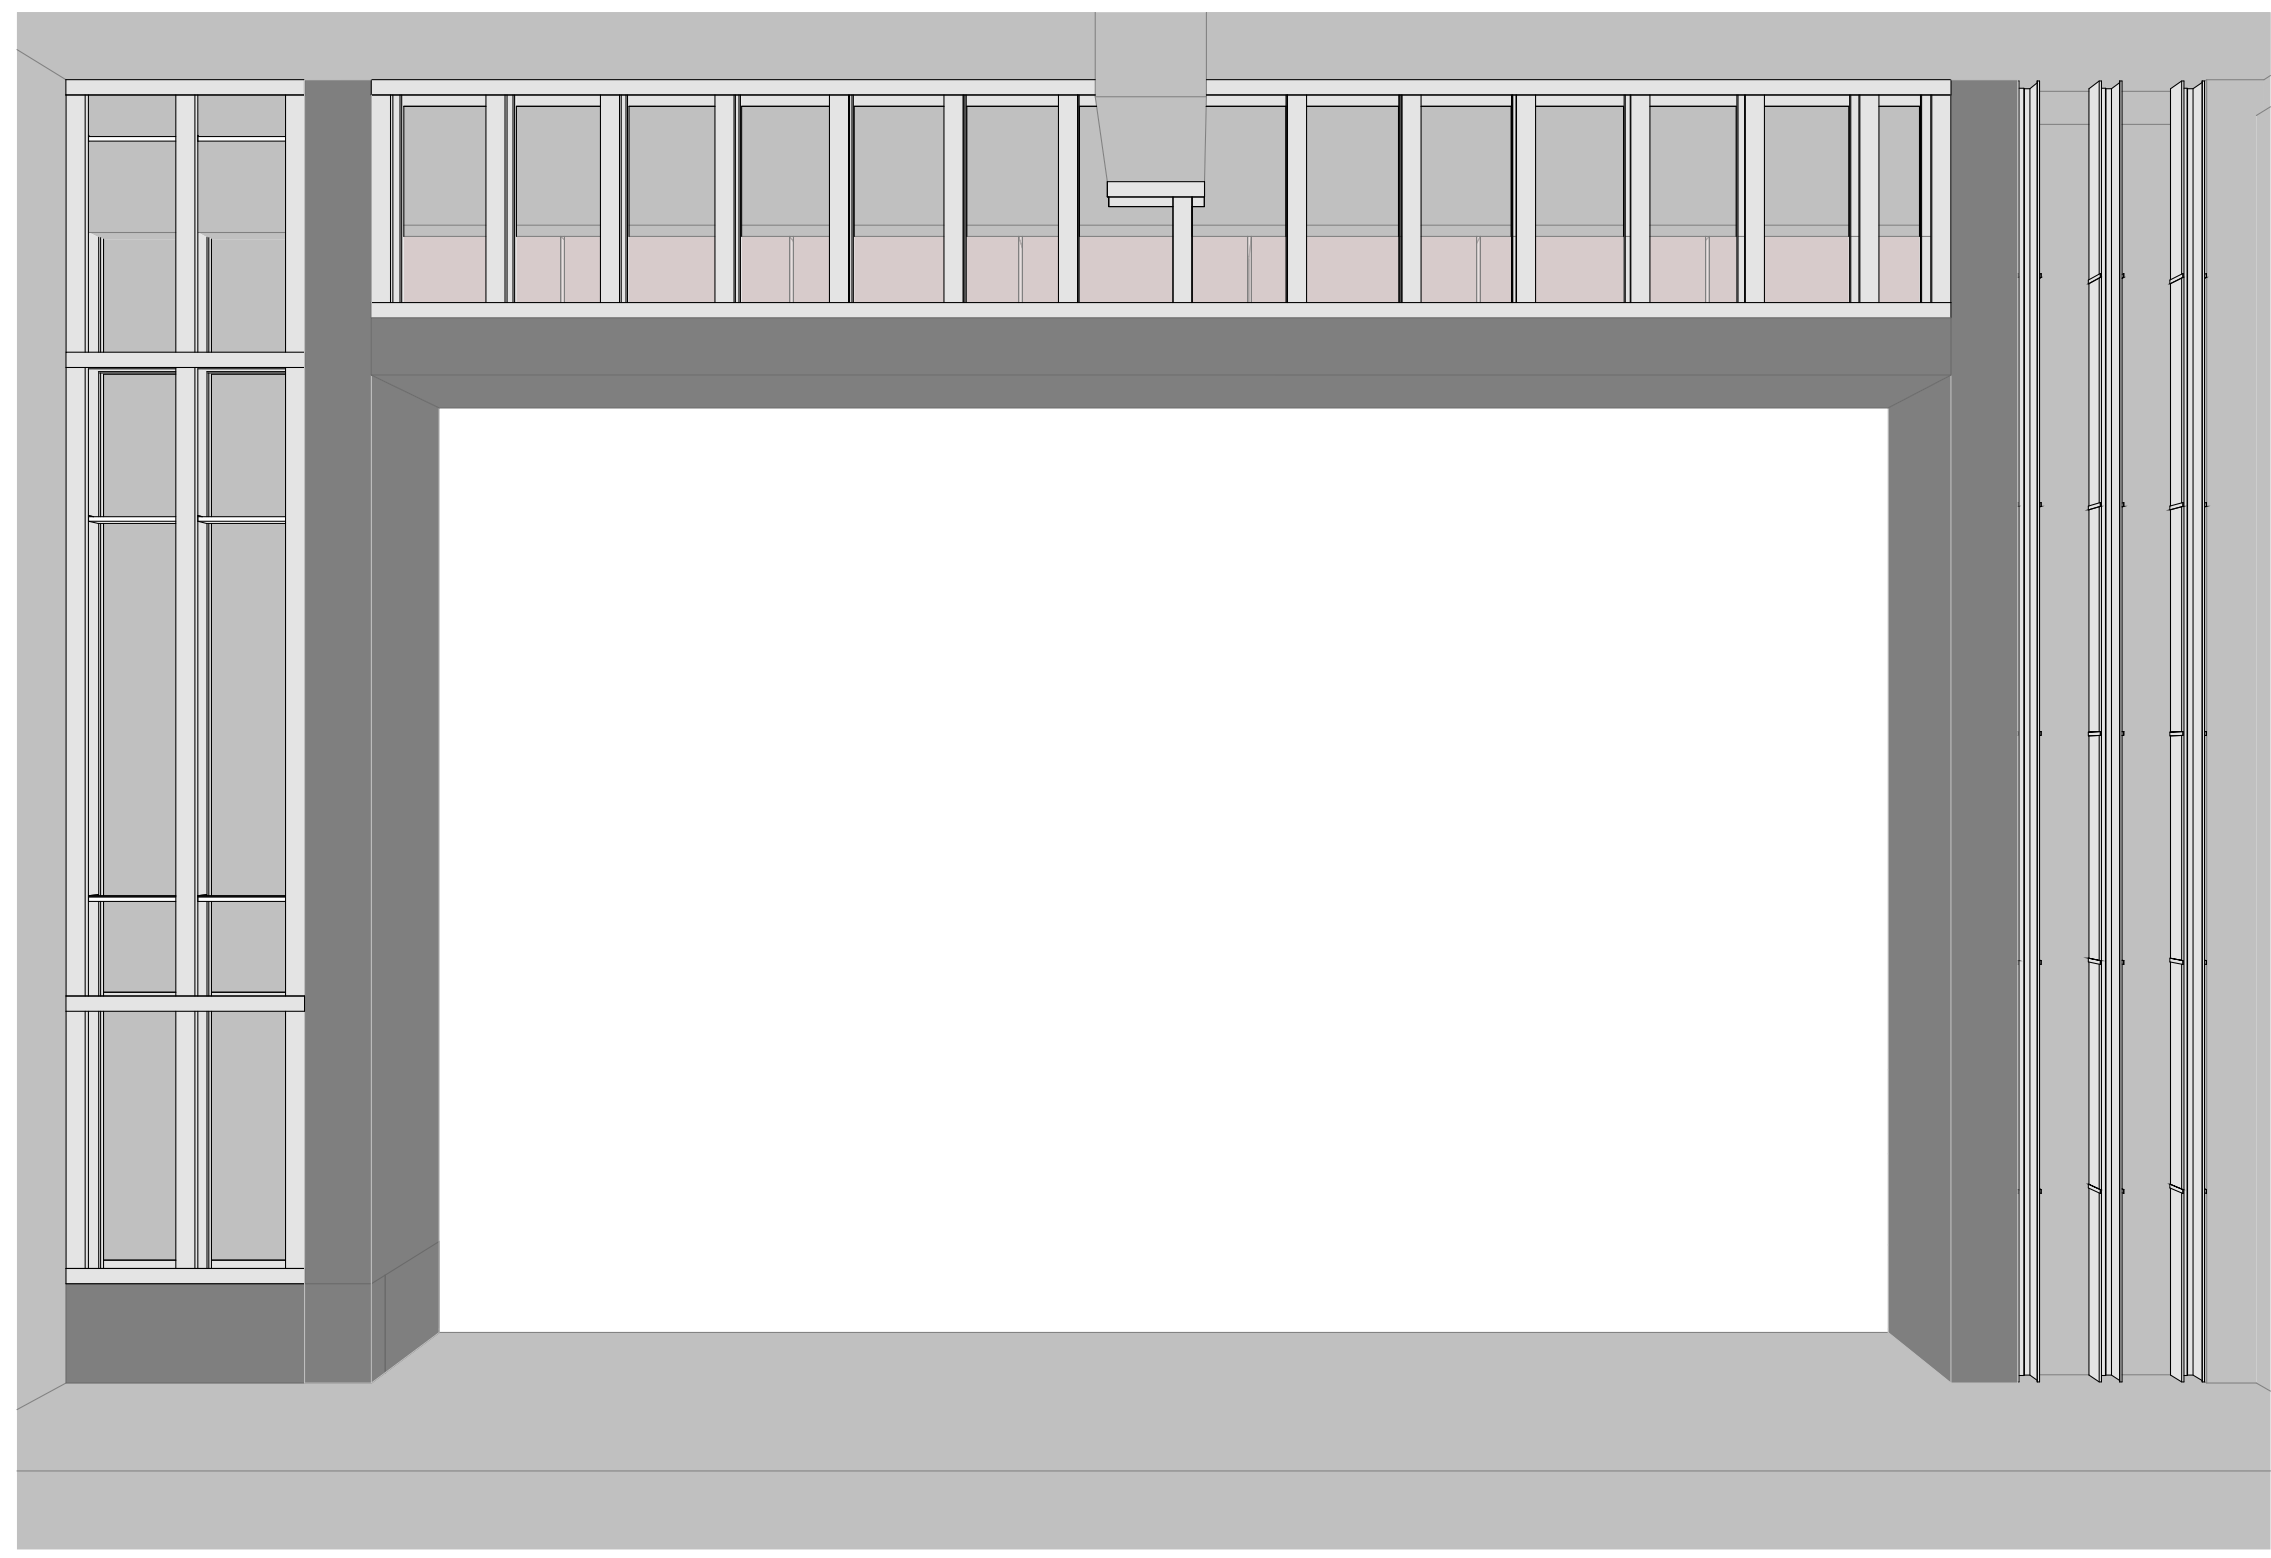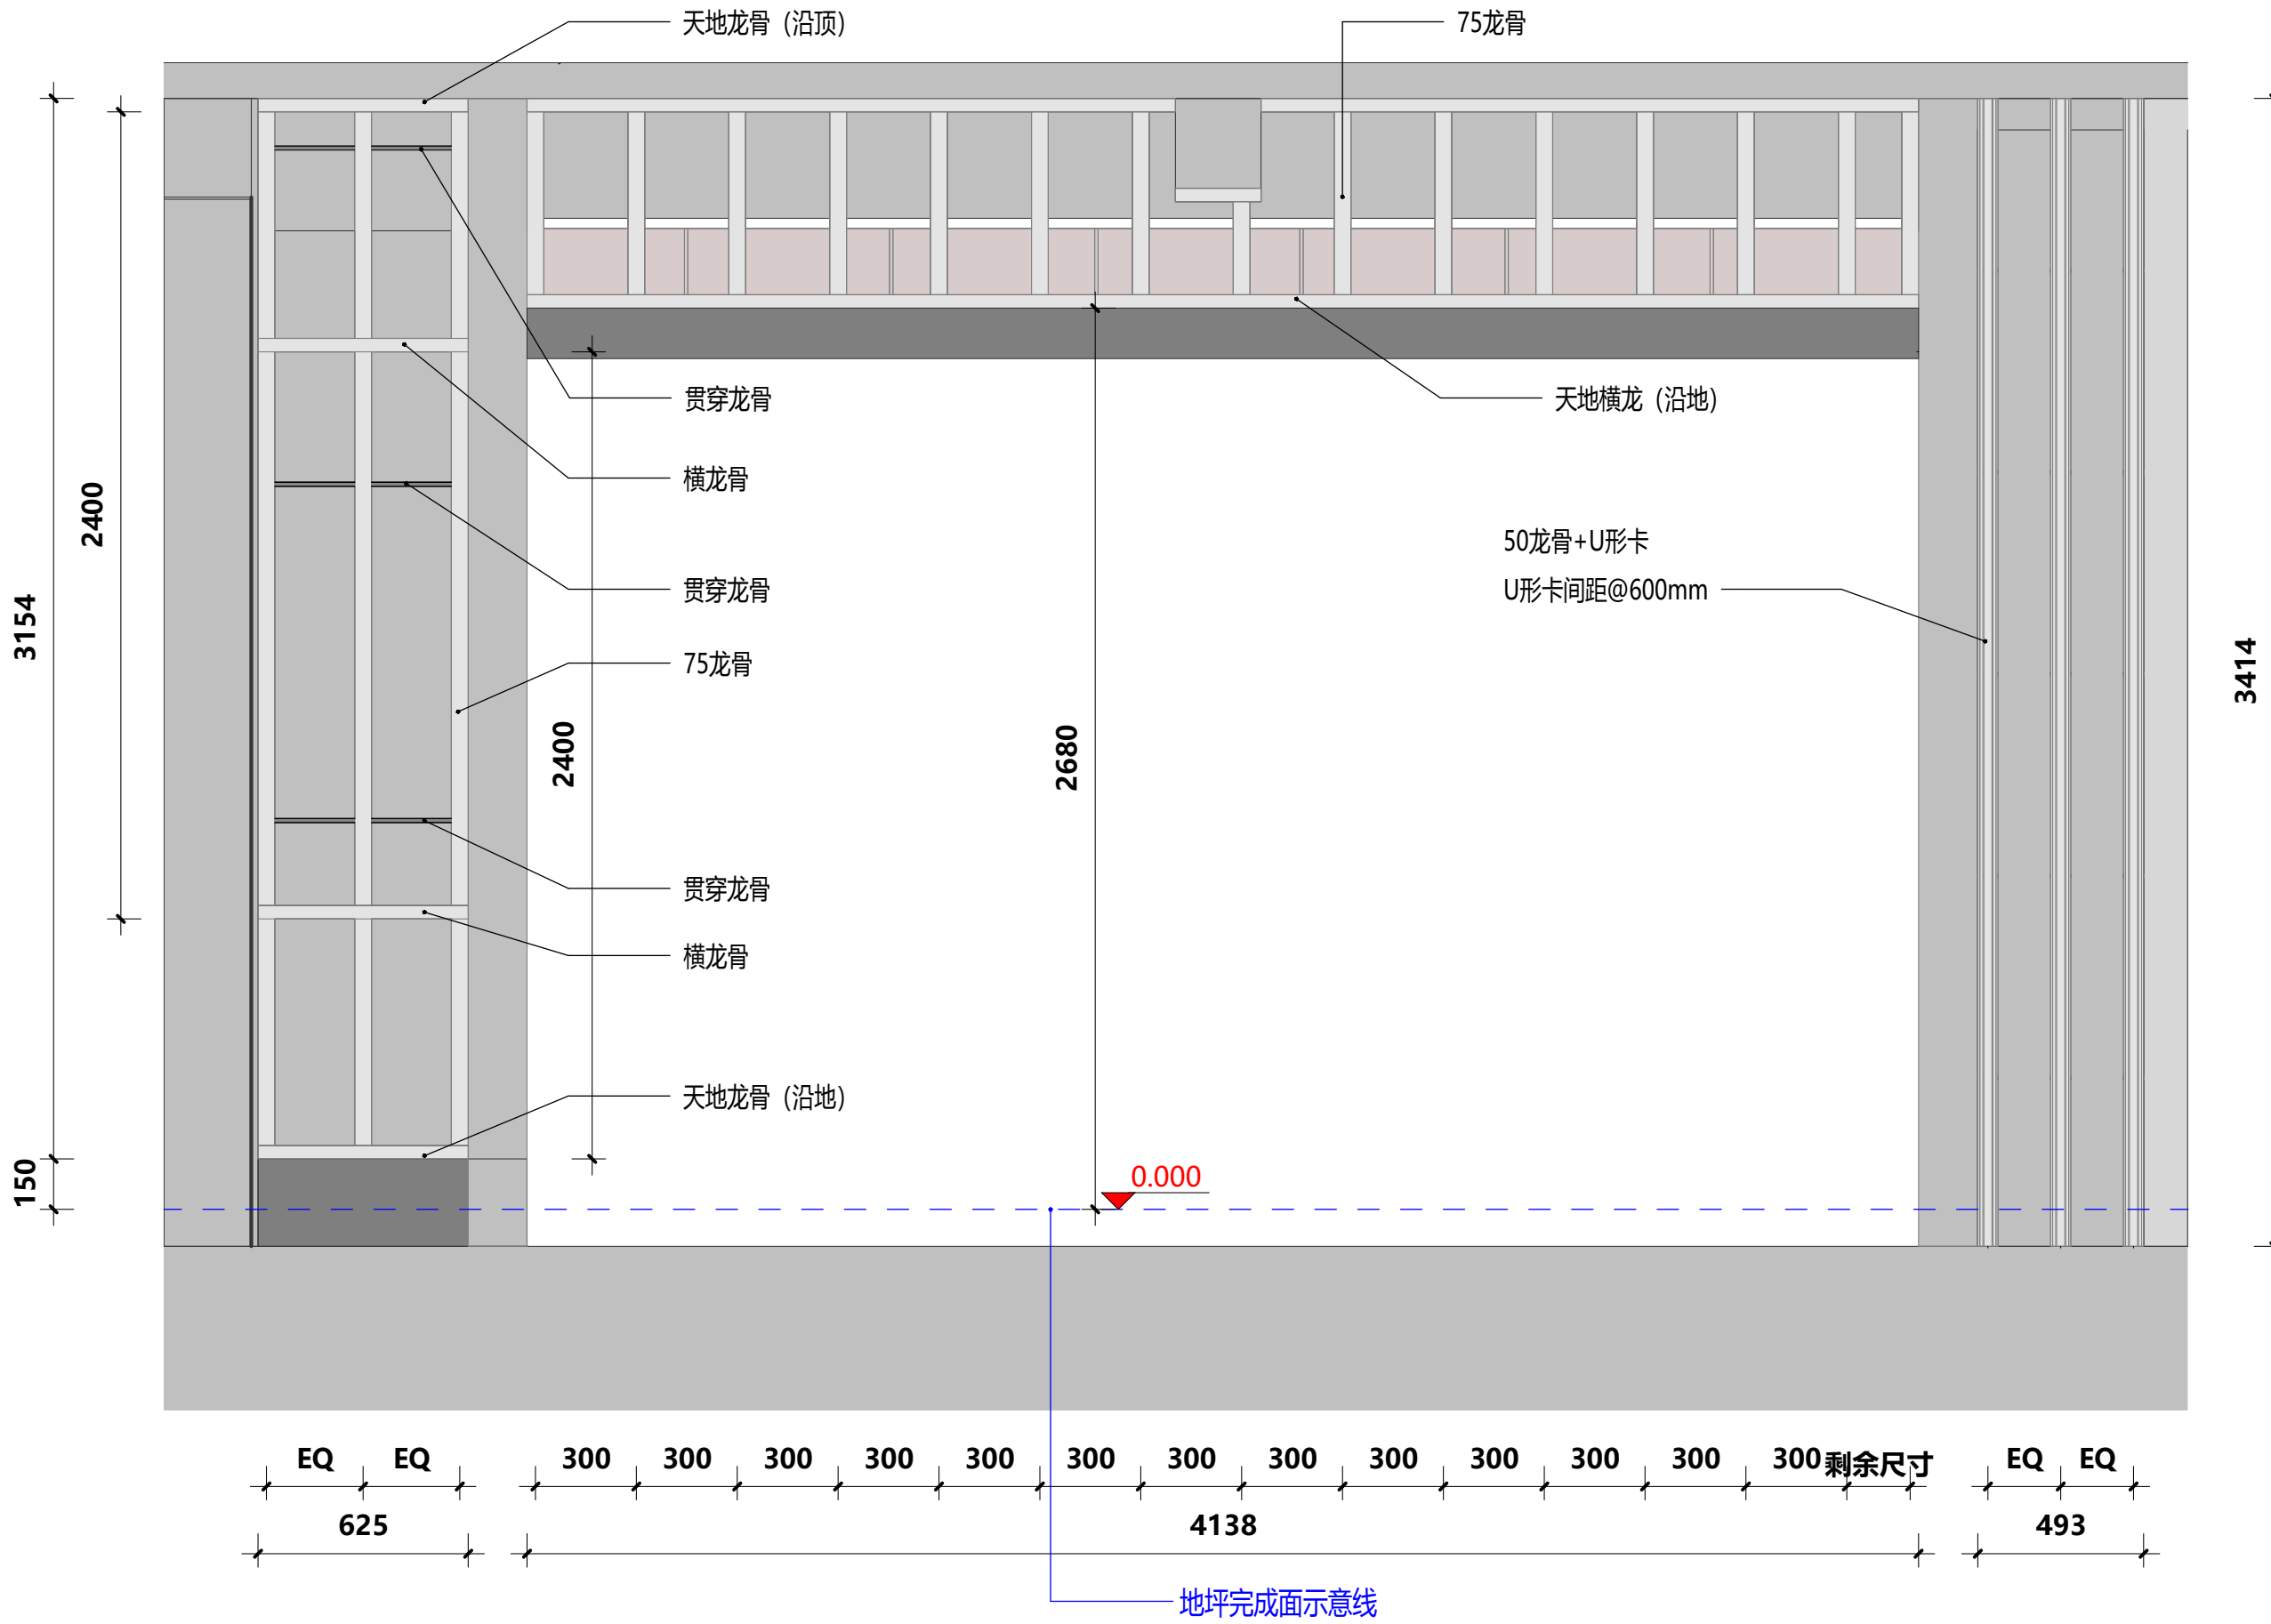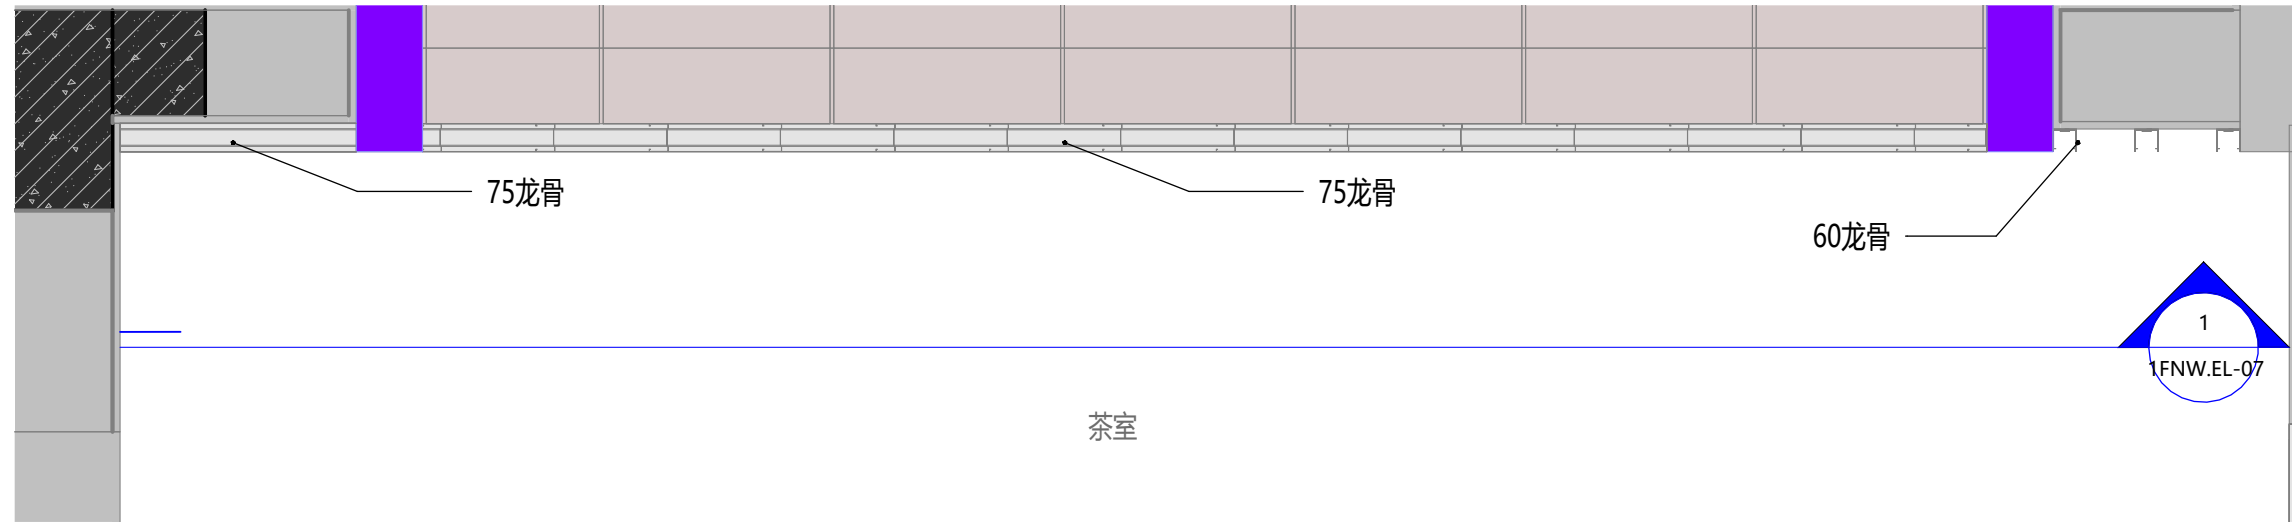

三维示意：3D-07.1

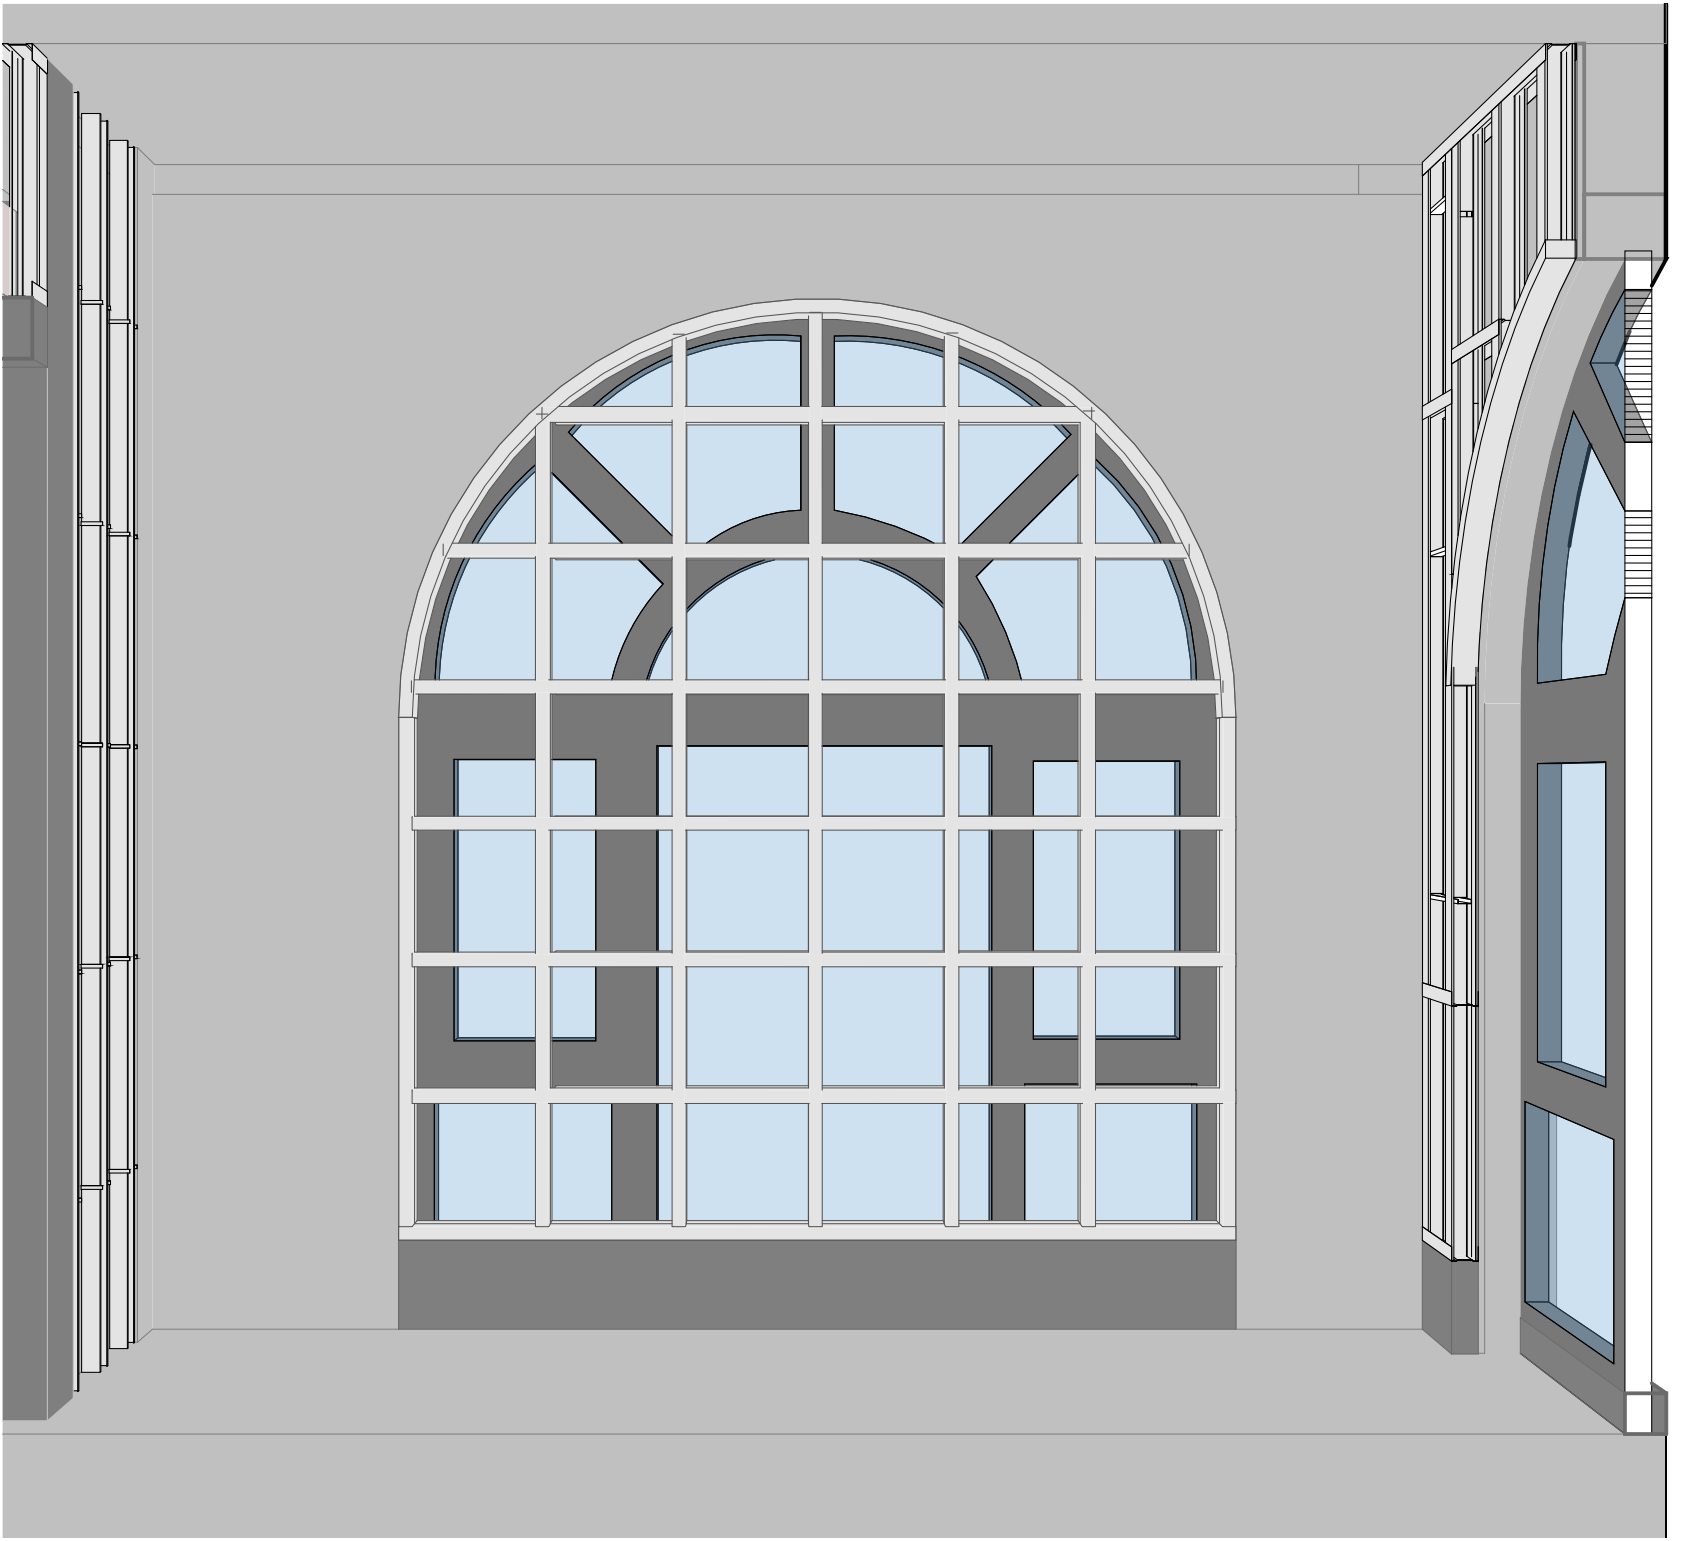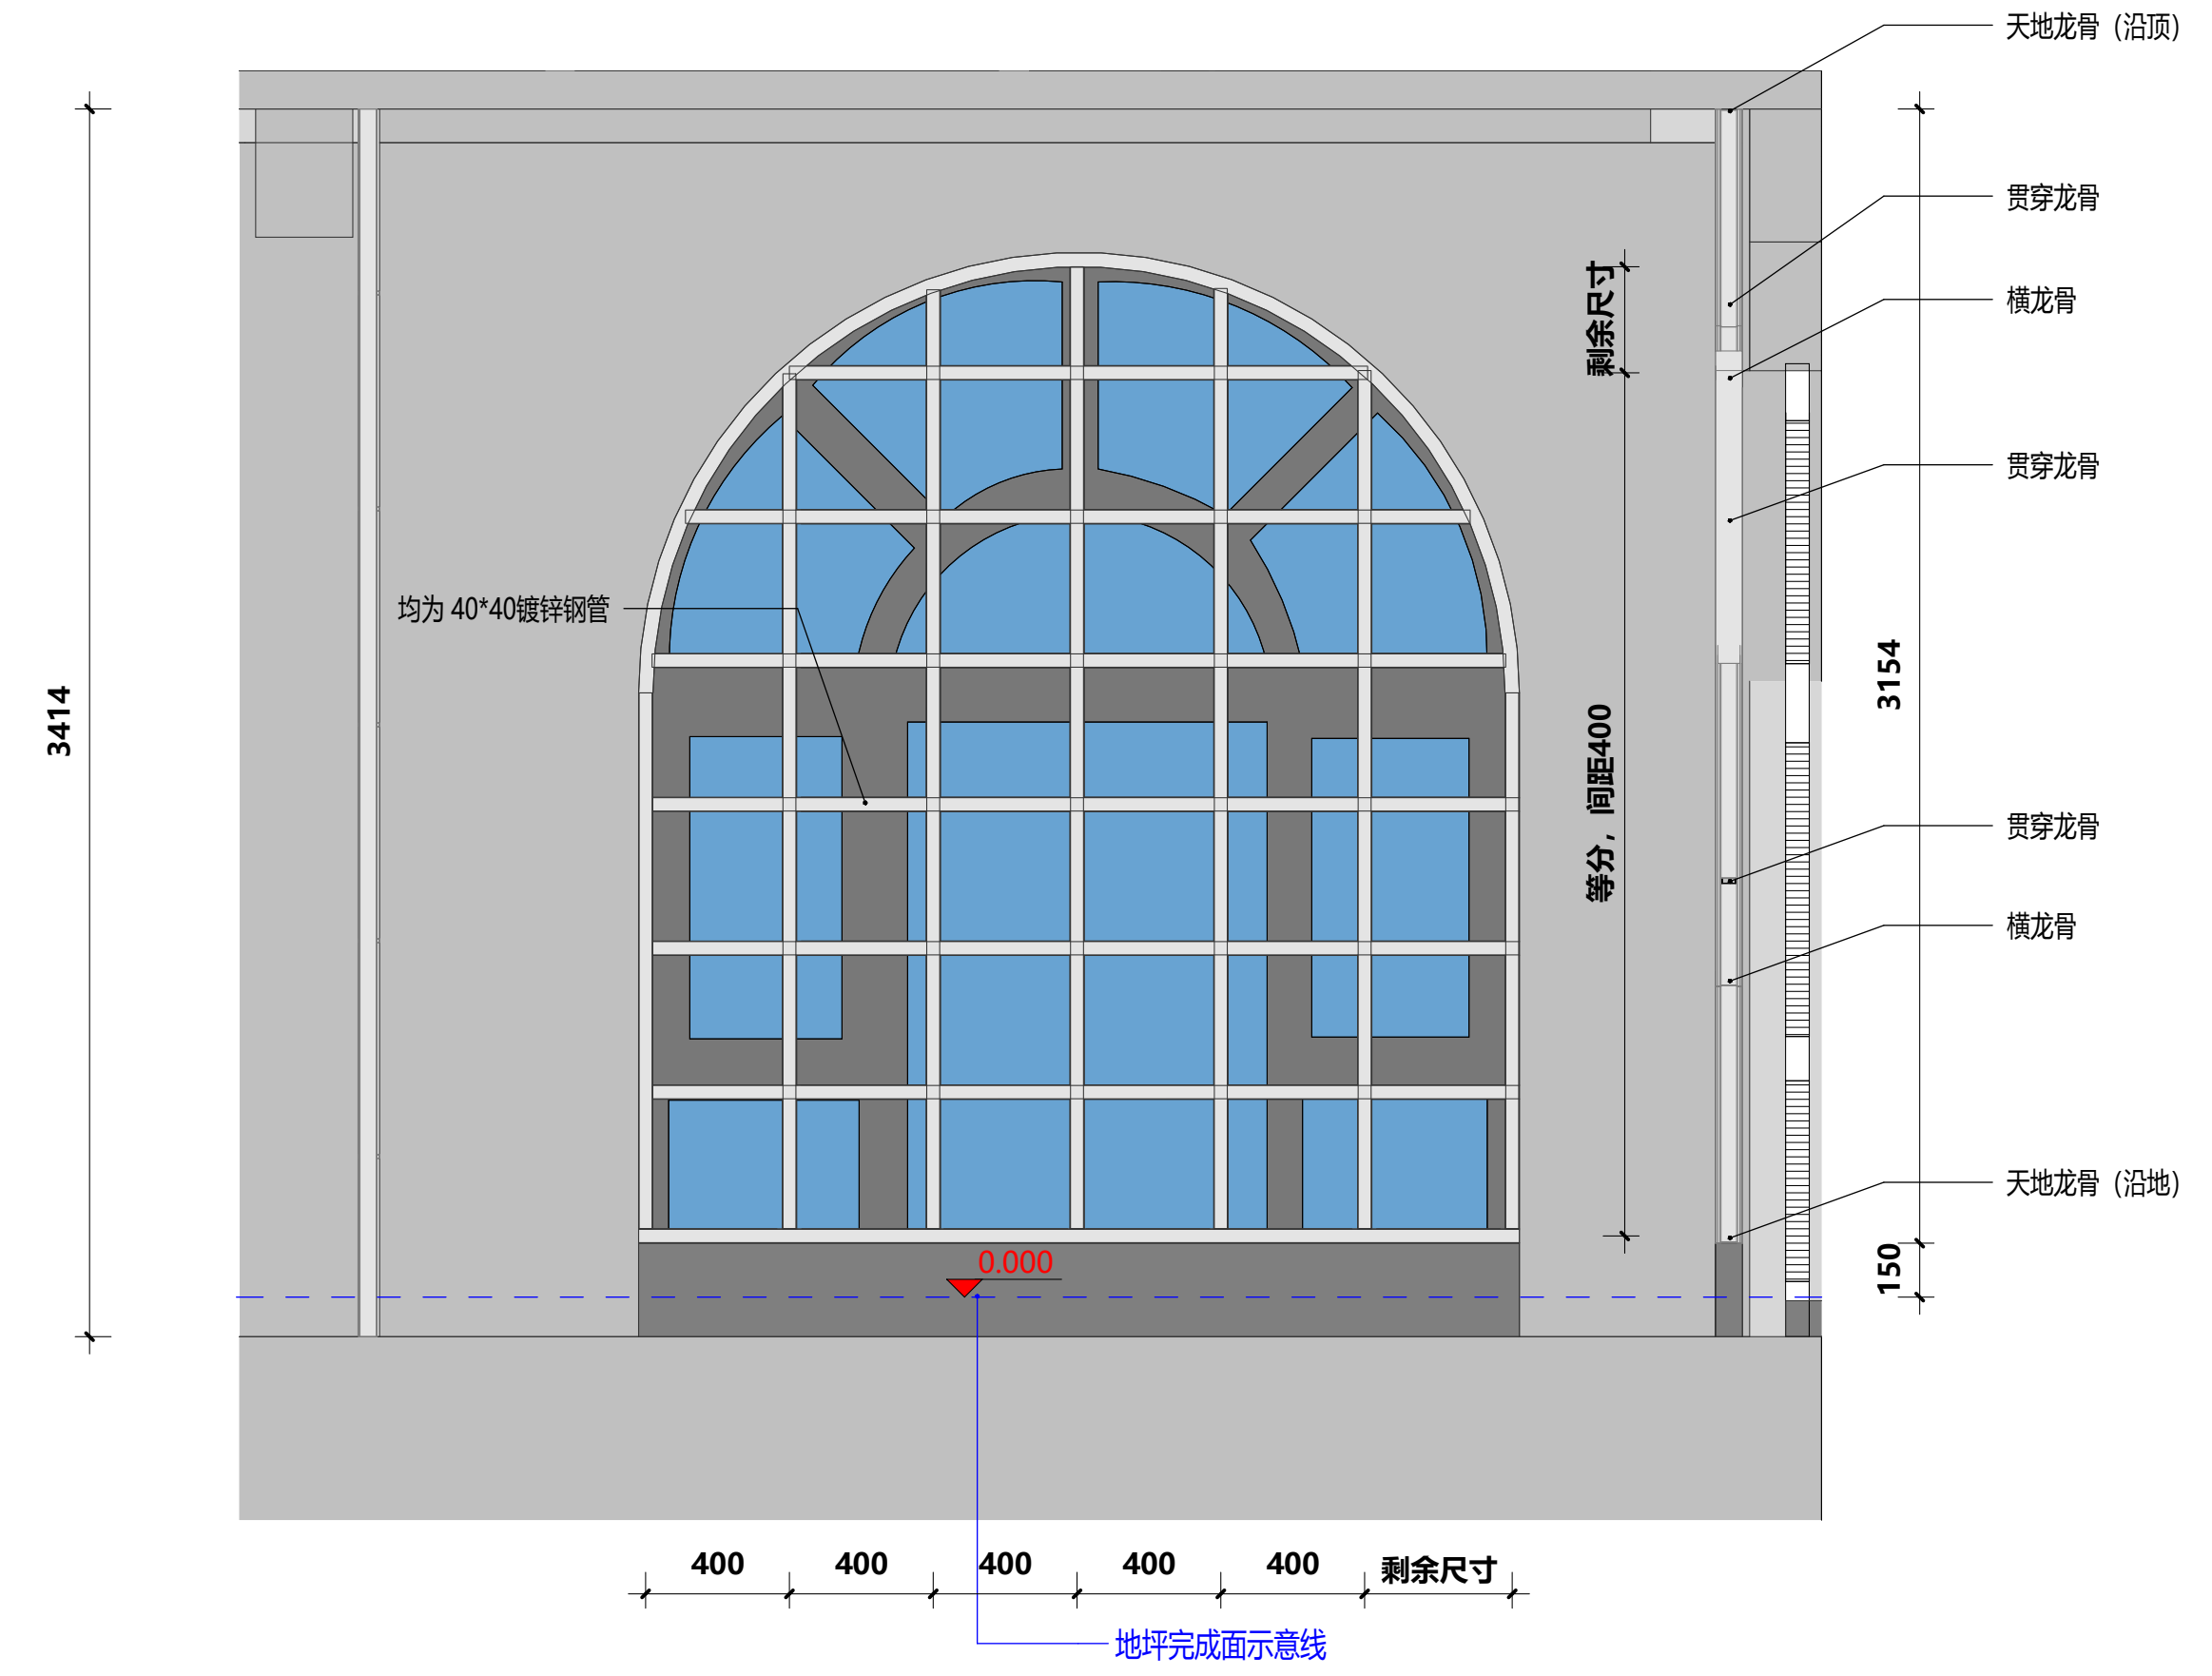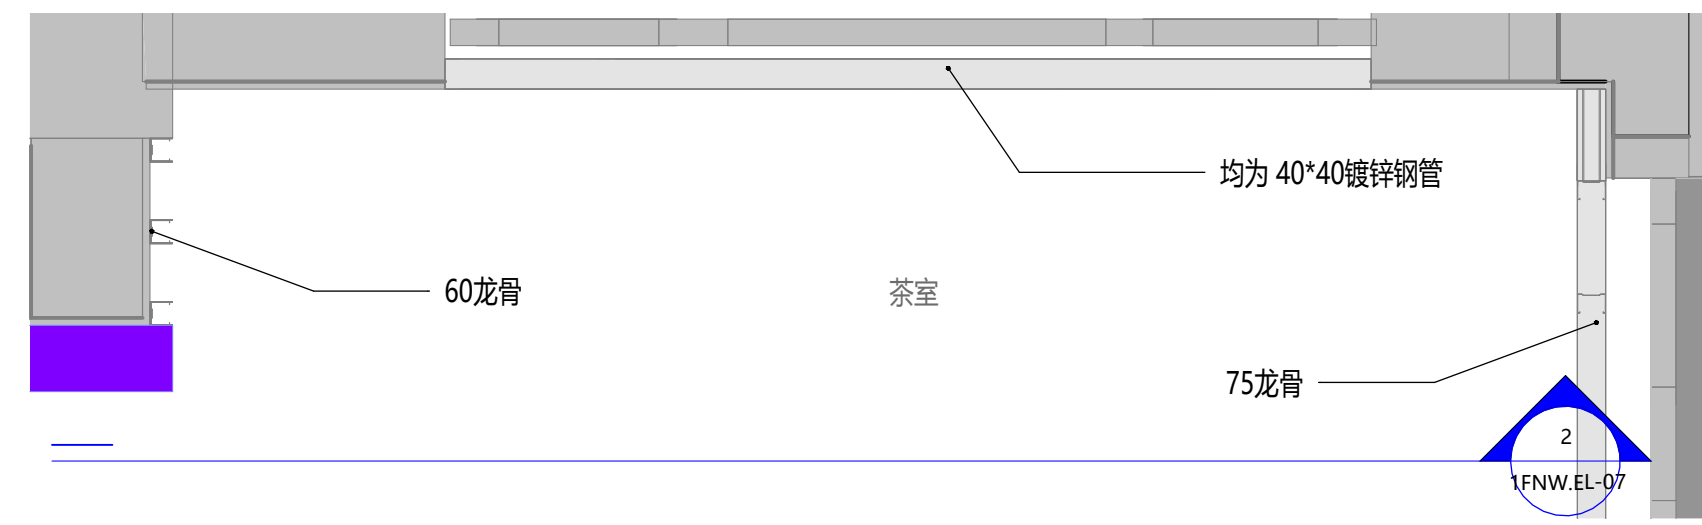

三维示意：3D-07.2

图例A 材质分类		
编号	图例	说明
1		原始墙、板、柱
2		混凝土外墙、构造柱、马牙槎
3		砌块墙
4		轻钢龙骨
5		钢架墙

图例B 施工时注意事项		
编号	图例	说明
1		地面完成线
2		必要尺寸
3		起始点
4		错缝要求 a≥200 b≥150
5		边砖宽度要求 a≥200 b < 150mm
6		a = b

盖章
正式施工图
2026-08-21

注释
Notes
1.本图按设计标准尺寸制作，施工过程中如有变更，须经设计人员同意后方可实施。
2.施工过程中如发现质量问题，应及时向监理单位报告，不得擅自处理。
3.本图经设计确认后，方可作为施工依据。

日期
Date
08/21/26
修订
Revision


项目
Project
巨鹿路880号

比例
Scale
1:20@A2


1F茶室轻钢龙骨钢架墙立面图一

图纸编号
Drawing No.
1F.NW.EL-07


项目编号
Project No.
© 2025

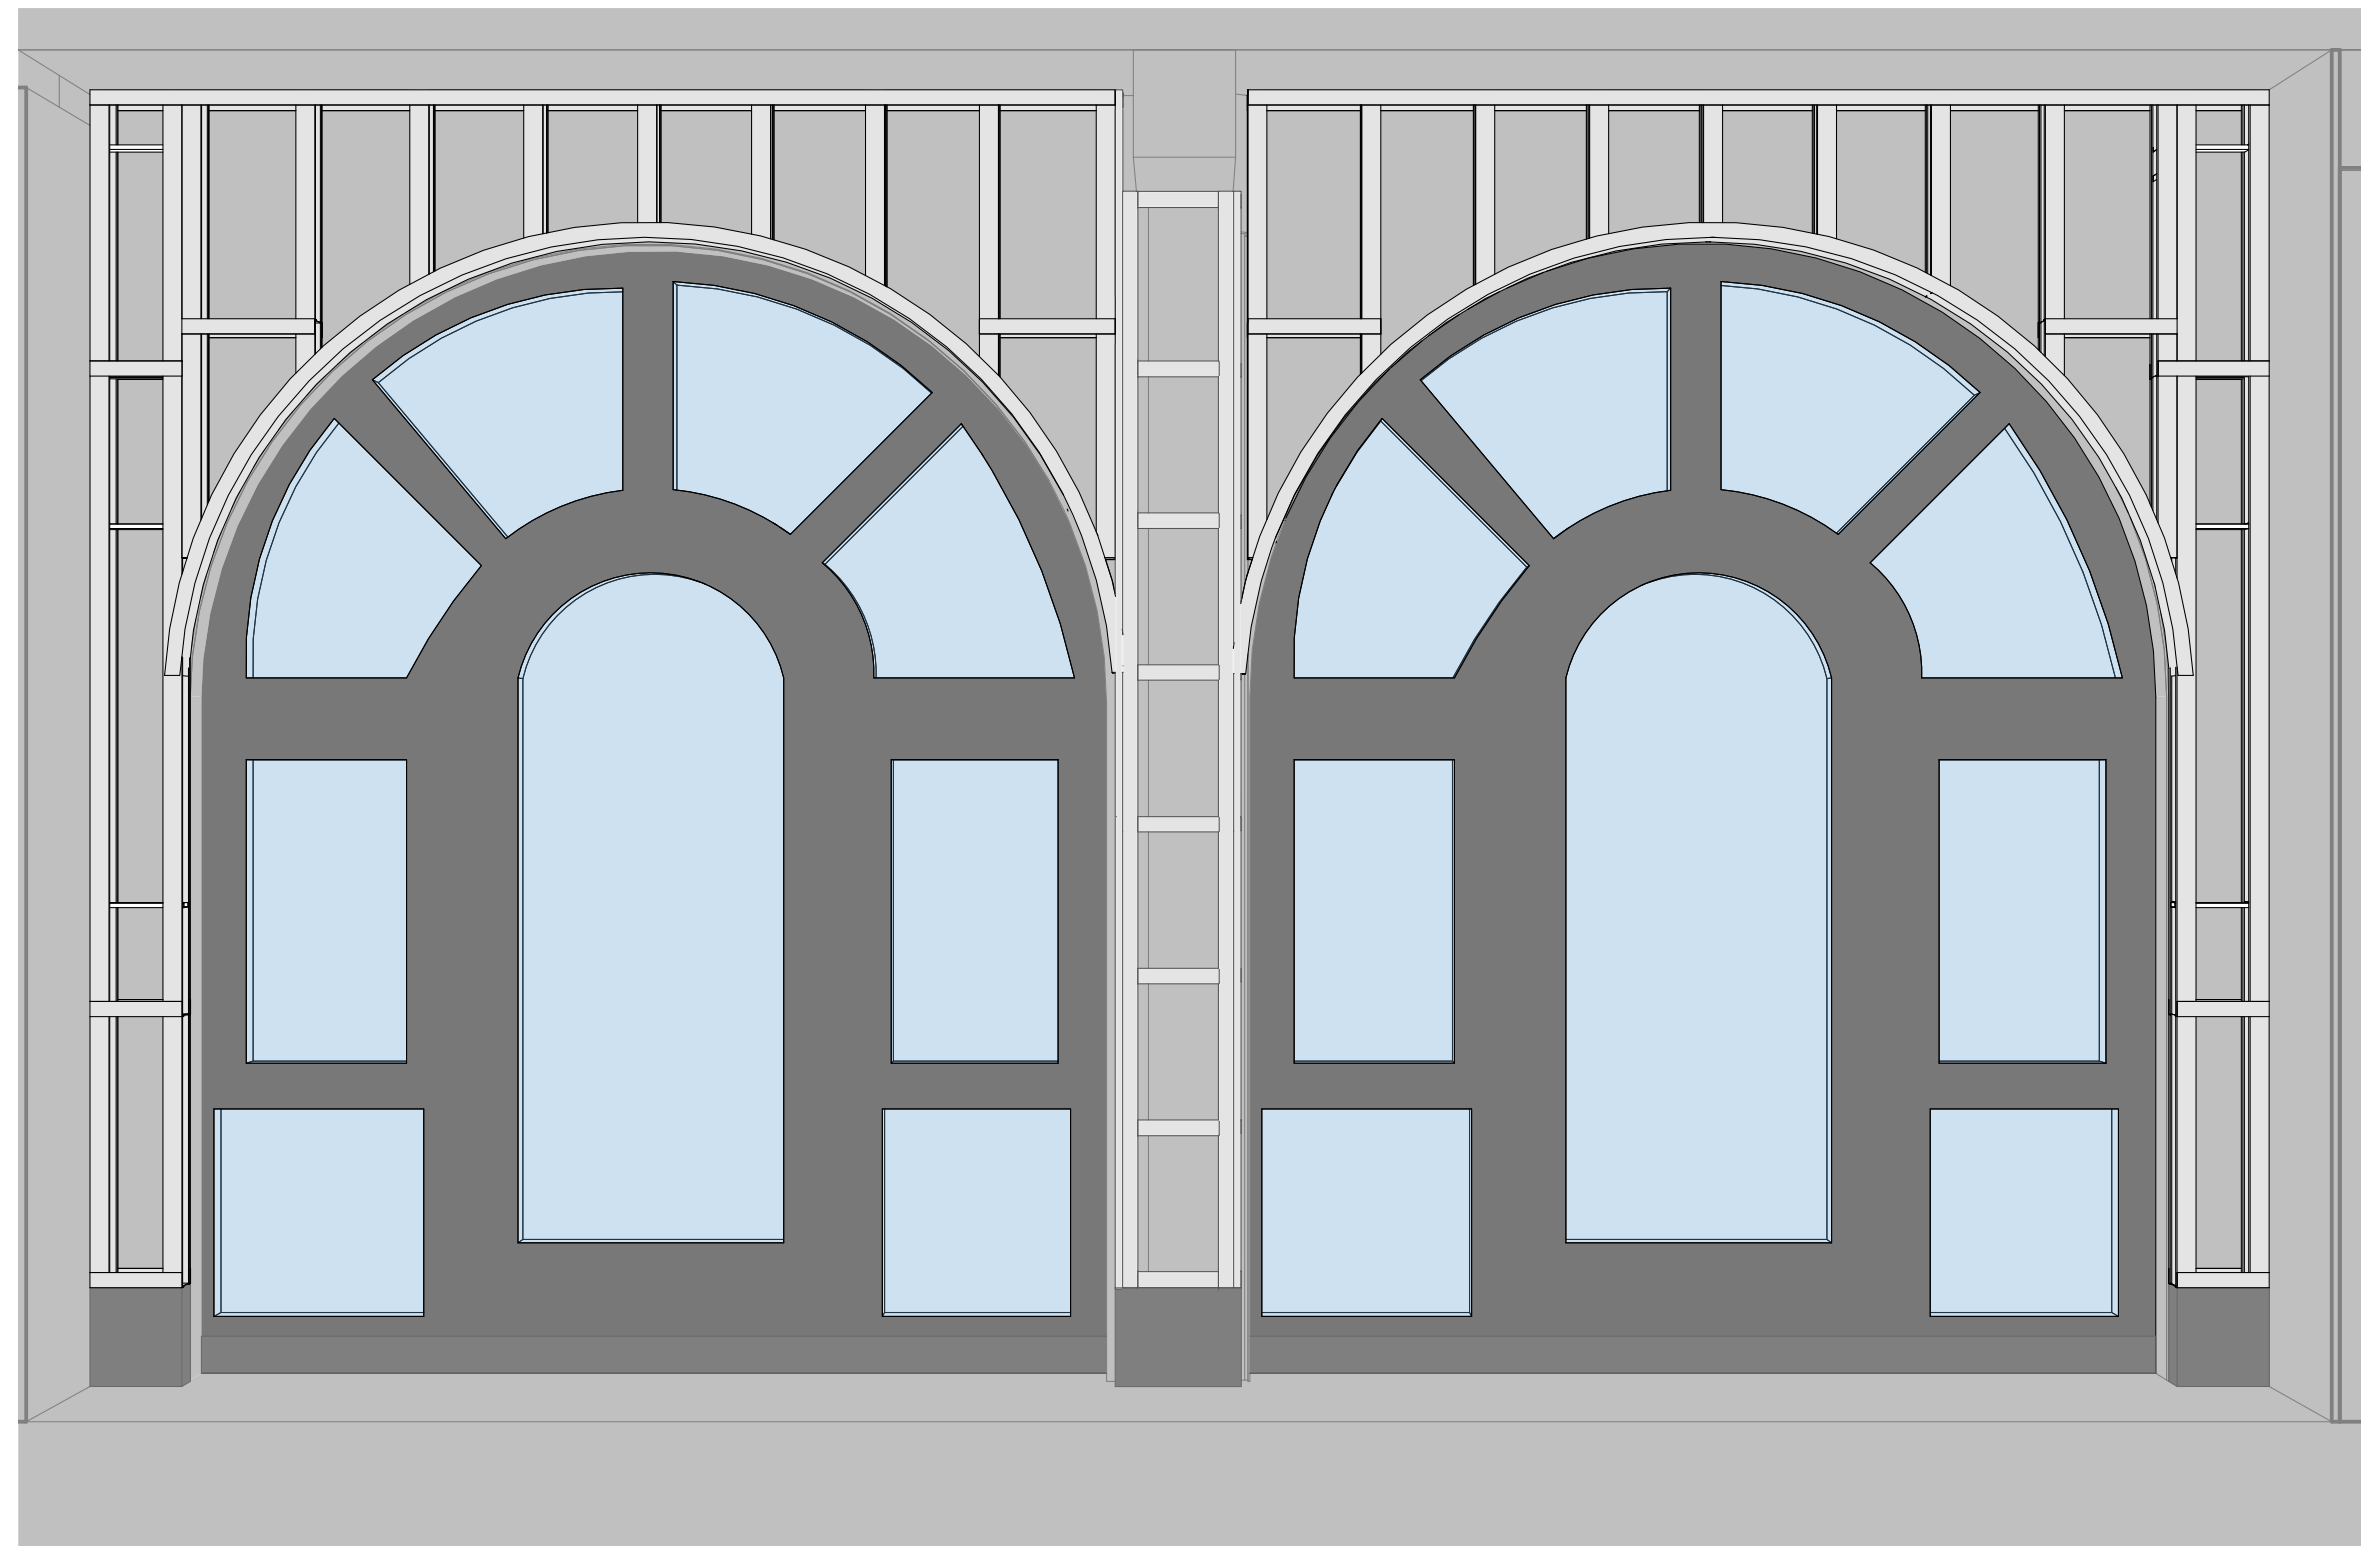

Scale比例 1:20@A2


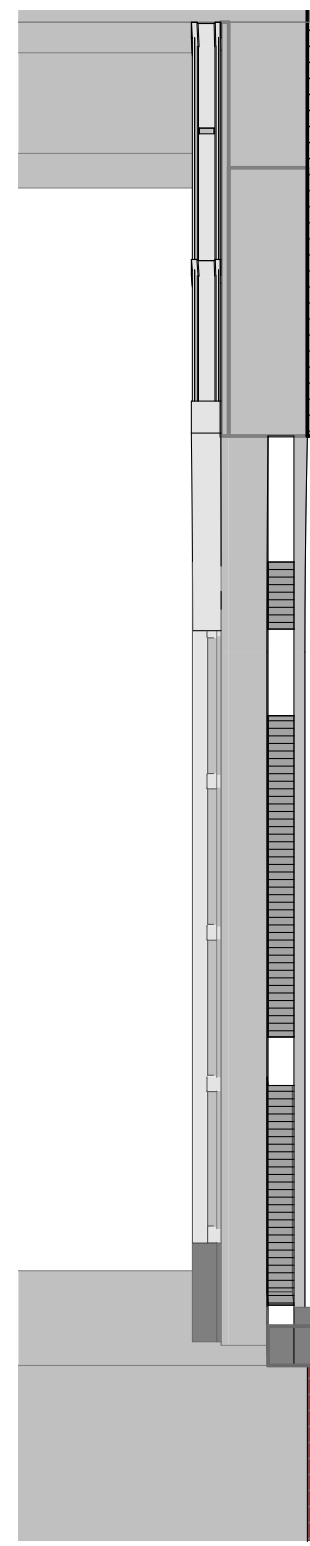




Scale比例 1:20@A2



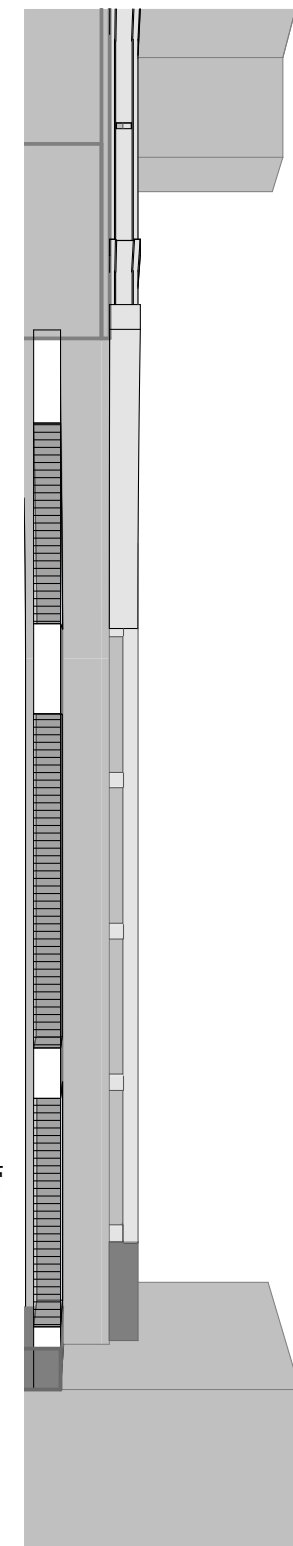


Scale比例 1:20@A2

项目编号
Project No.

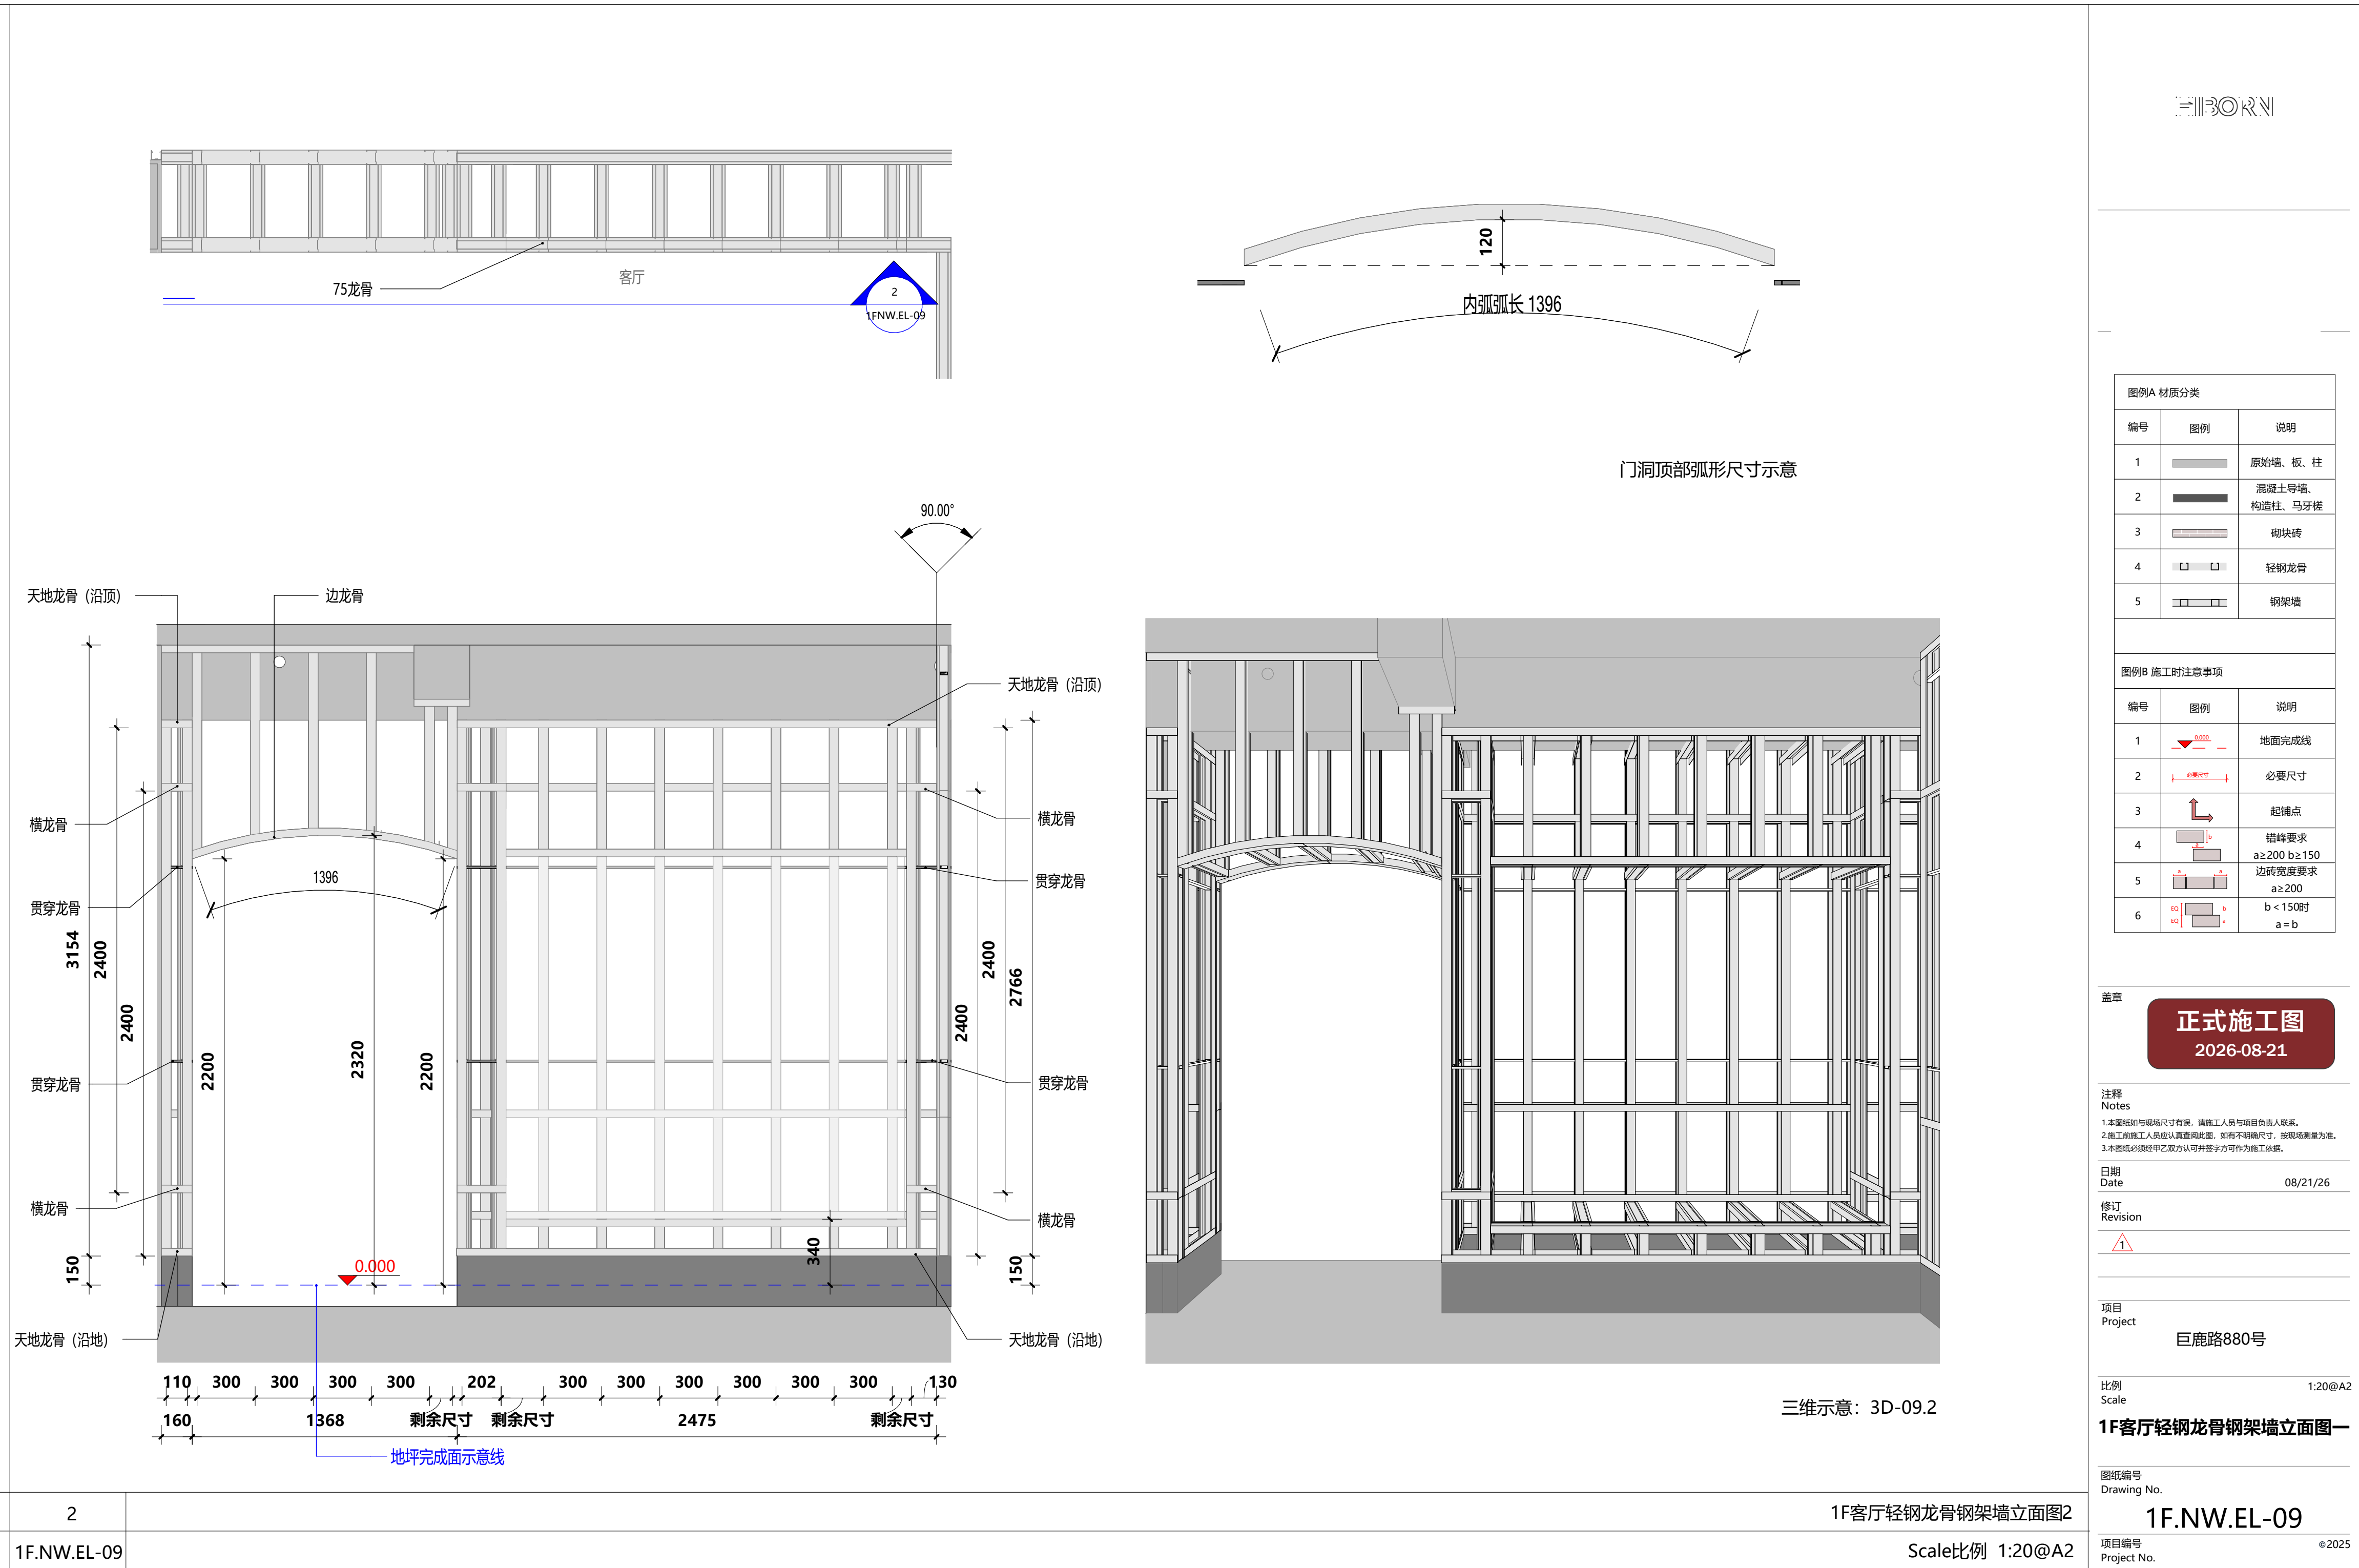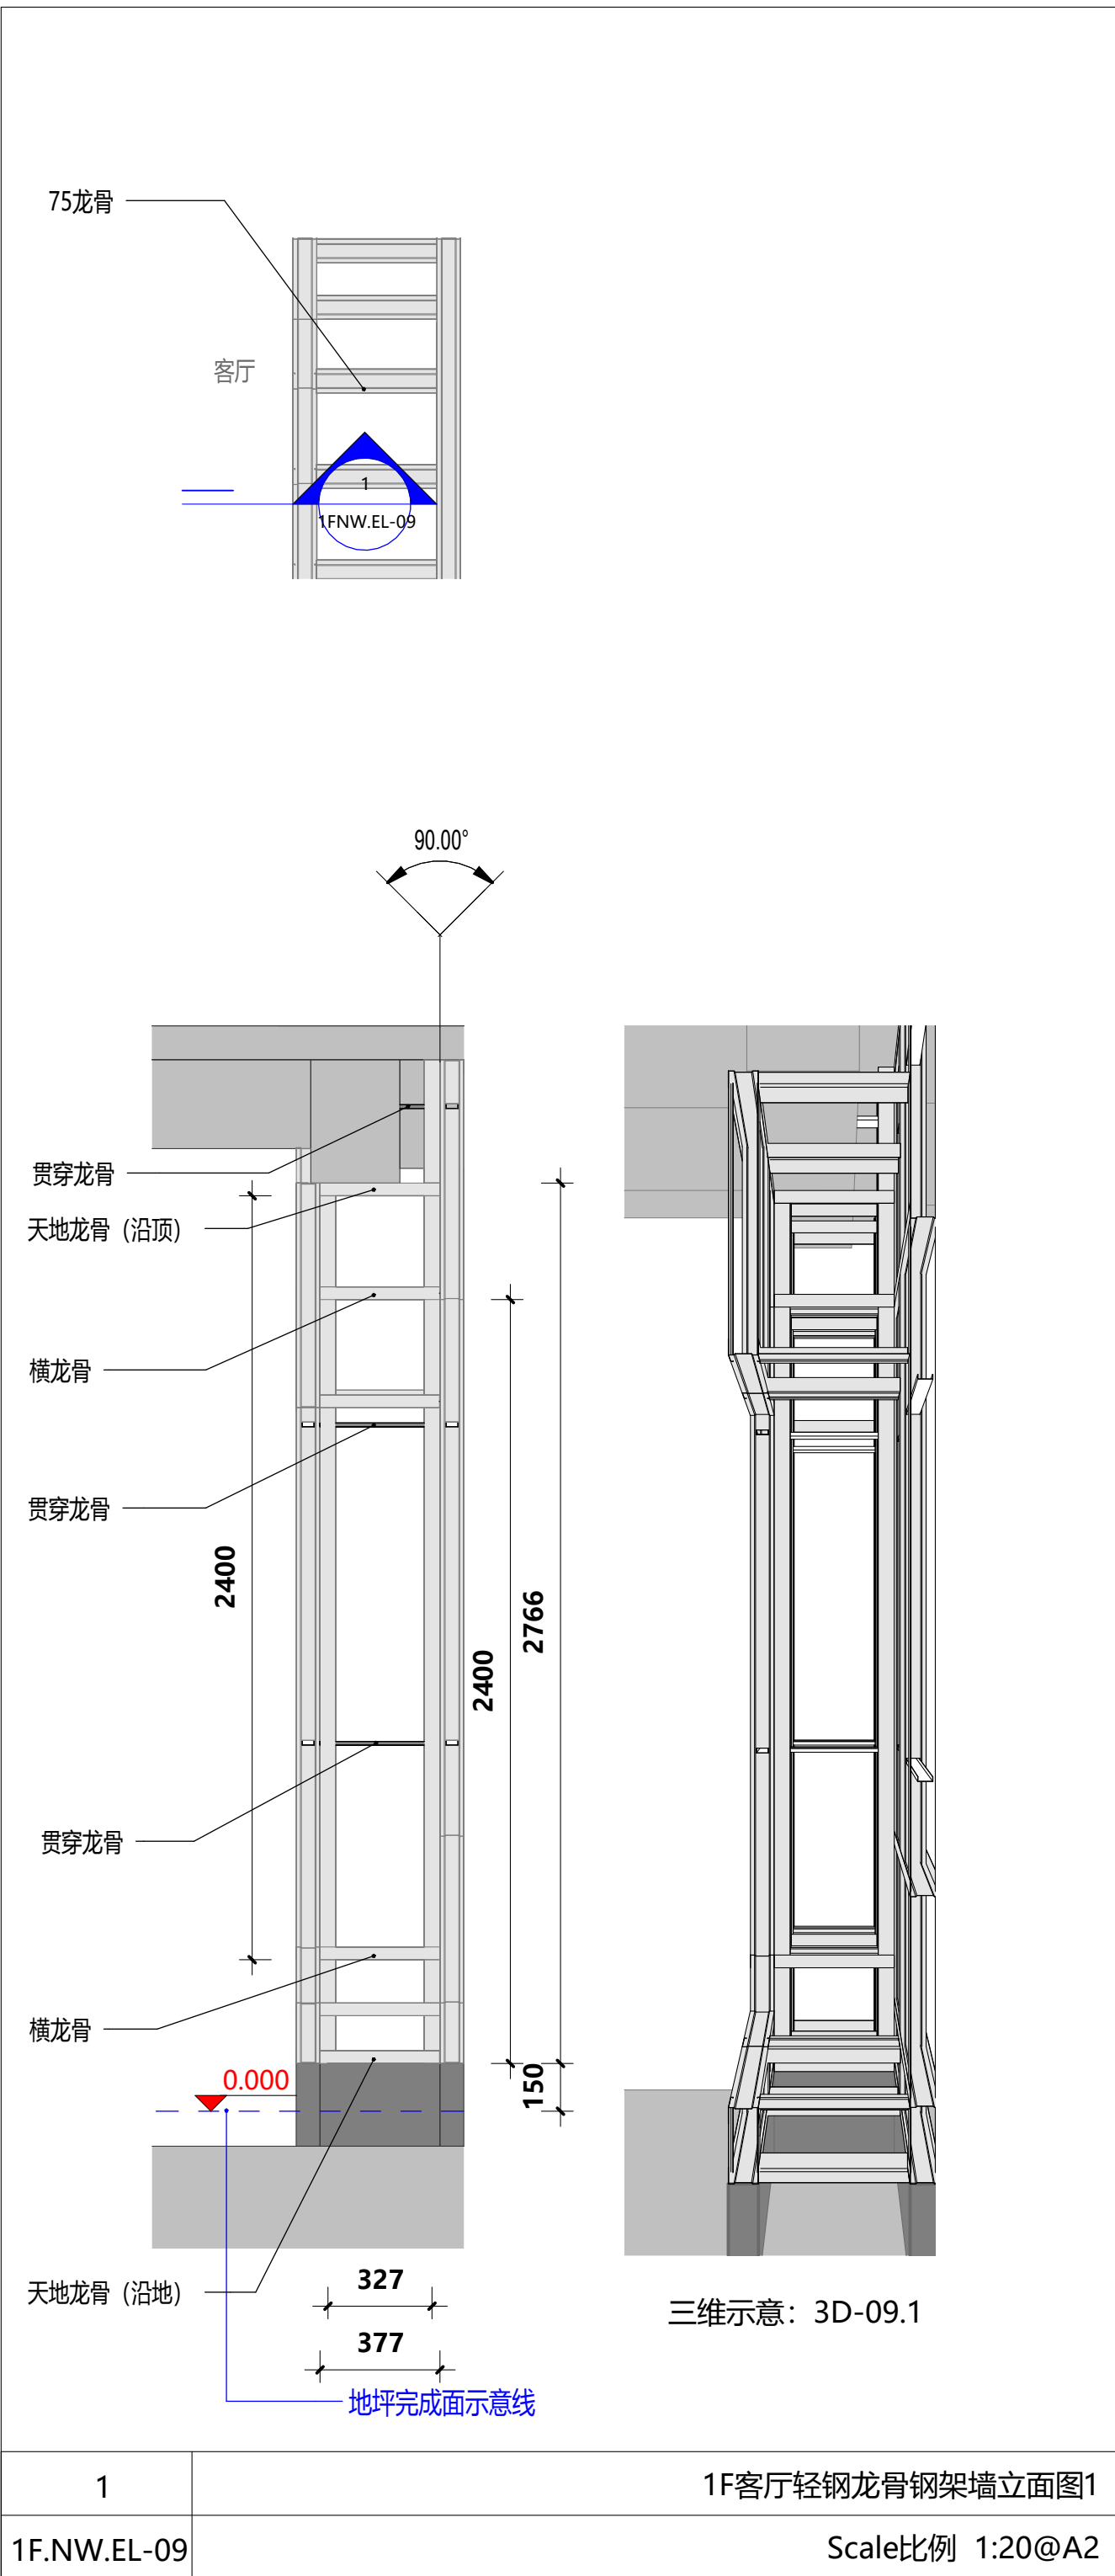

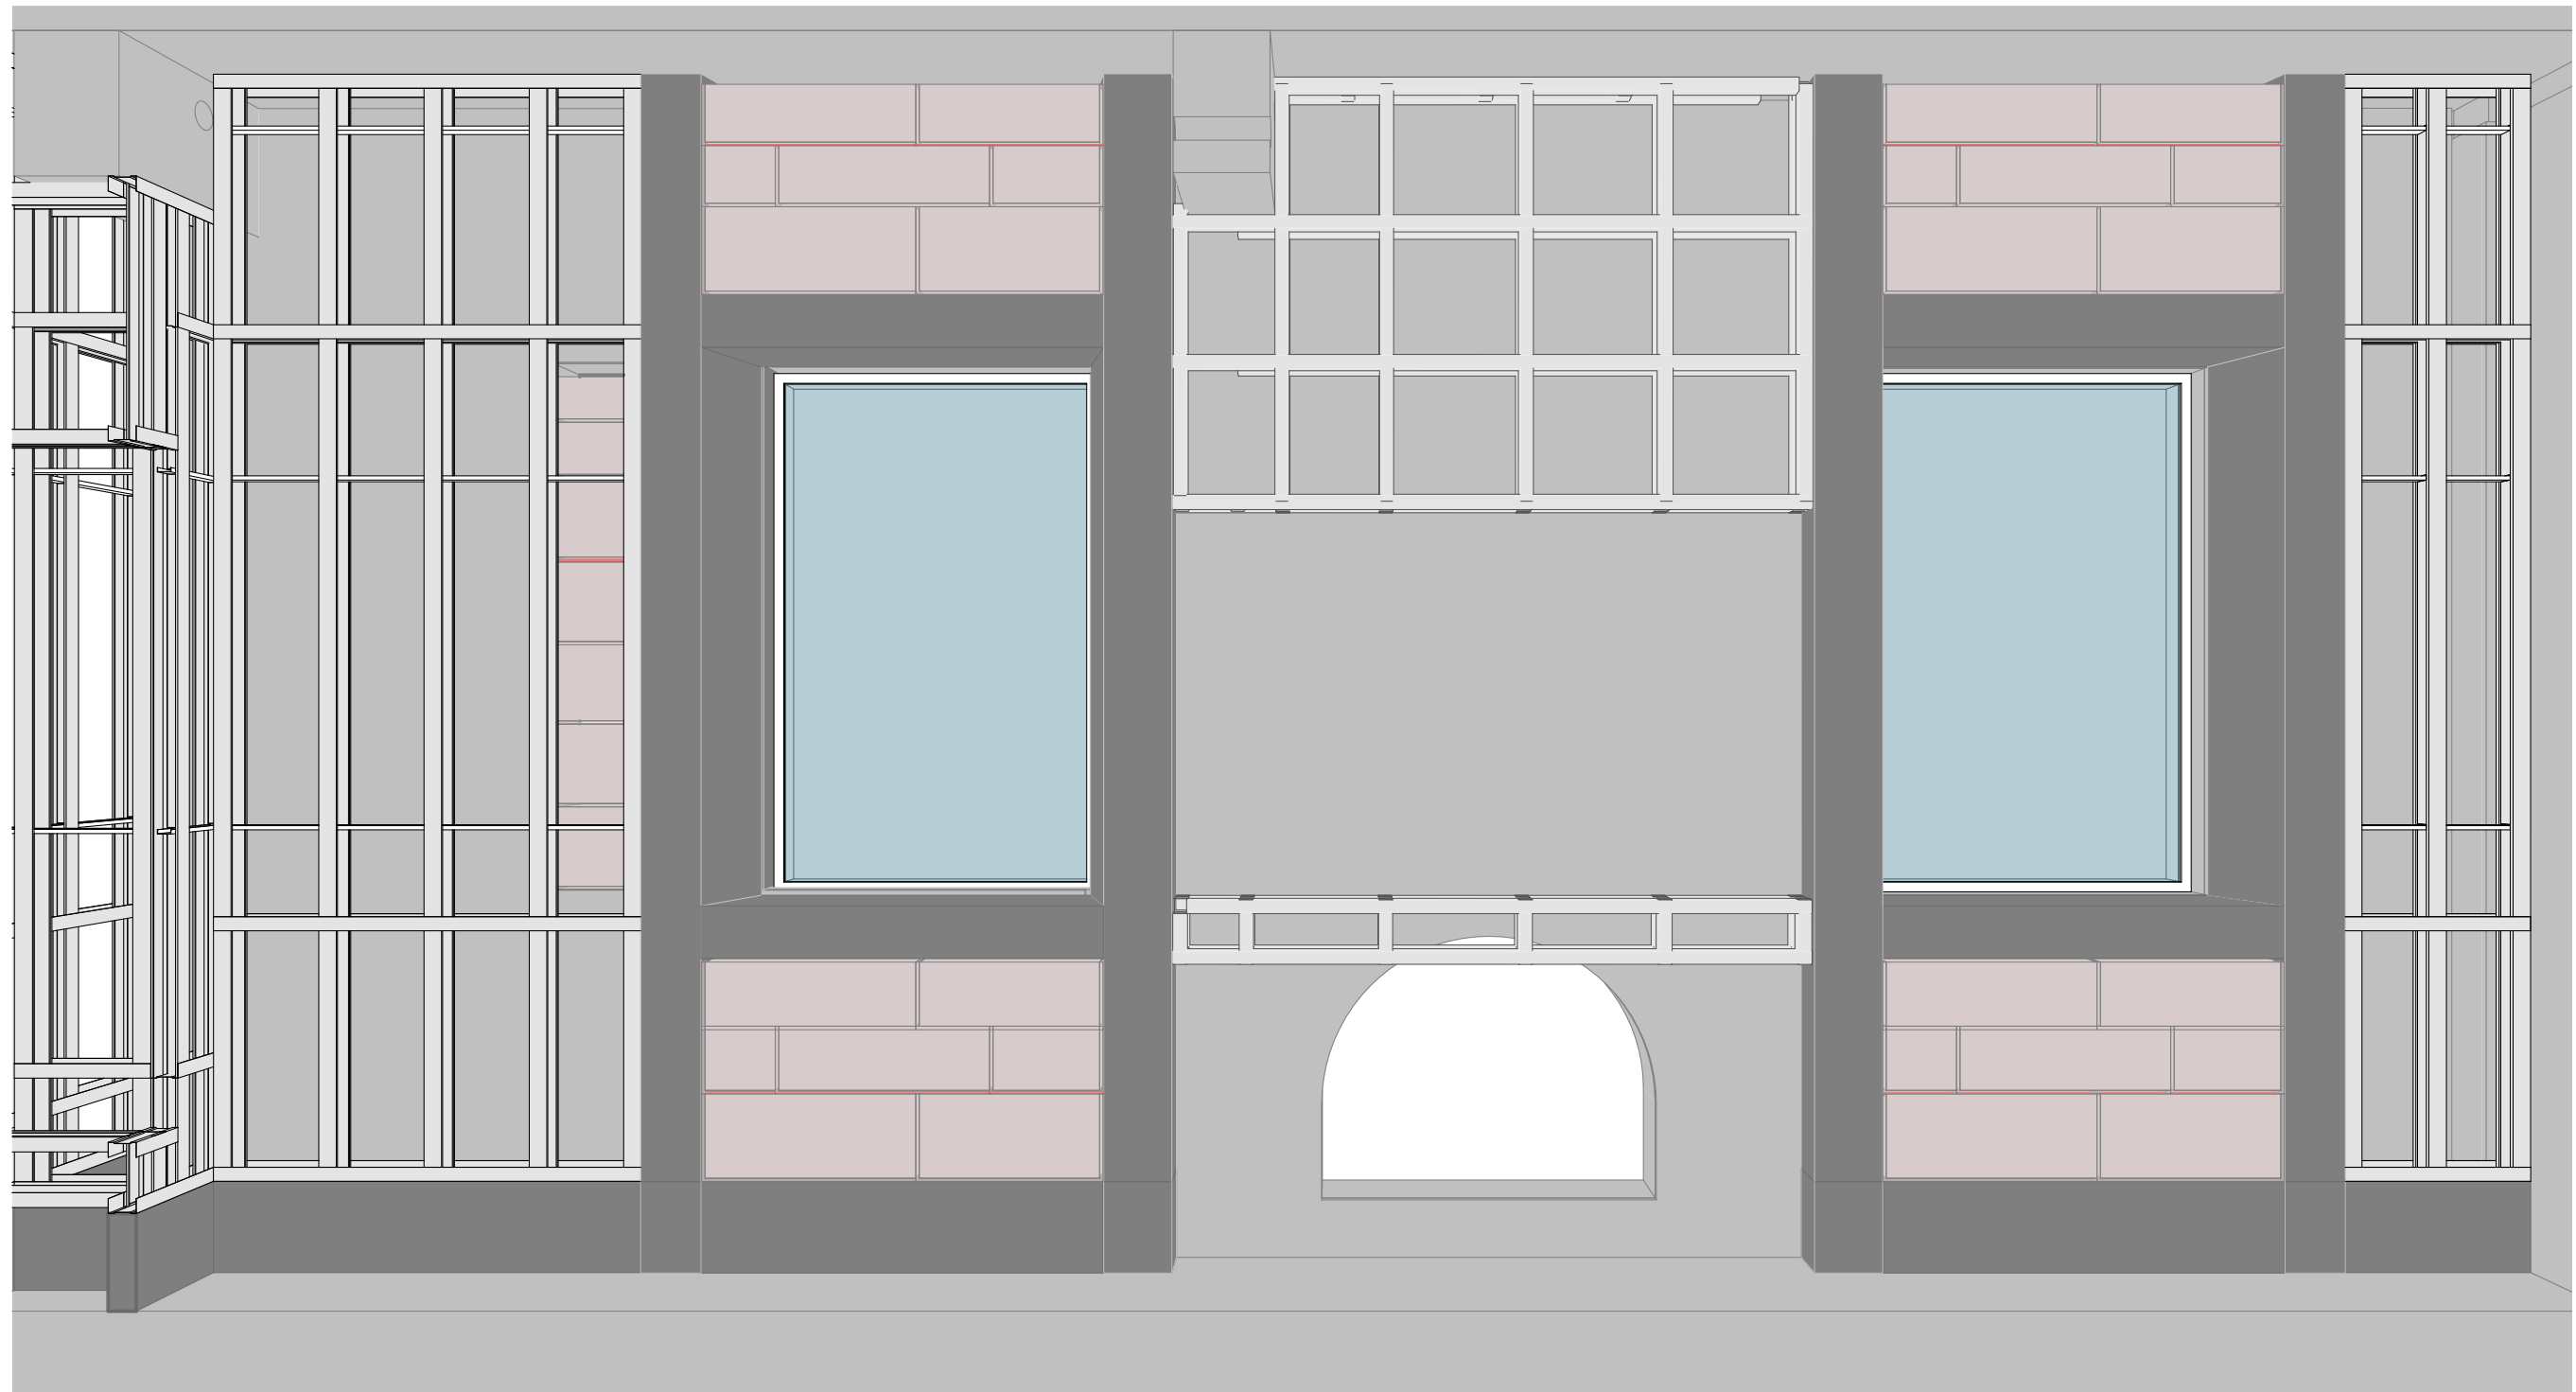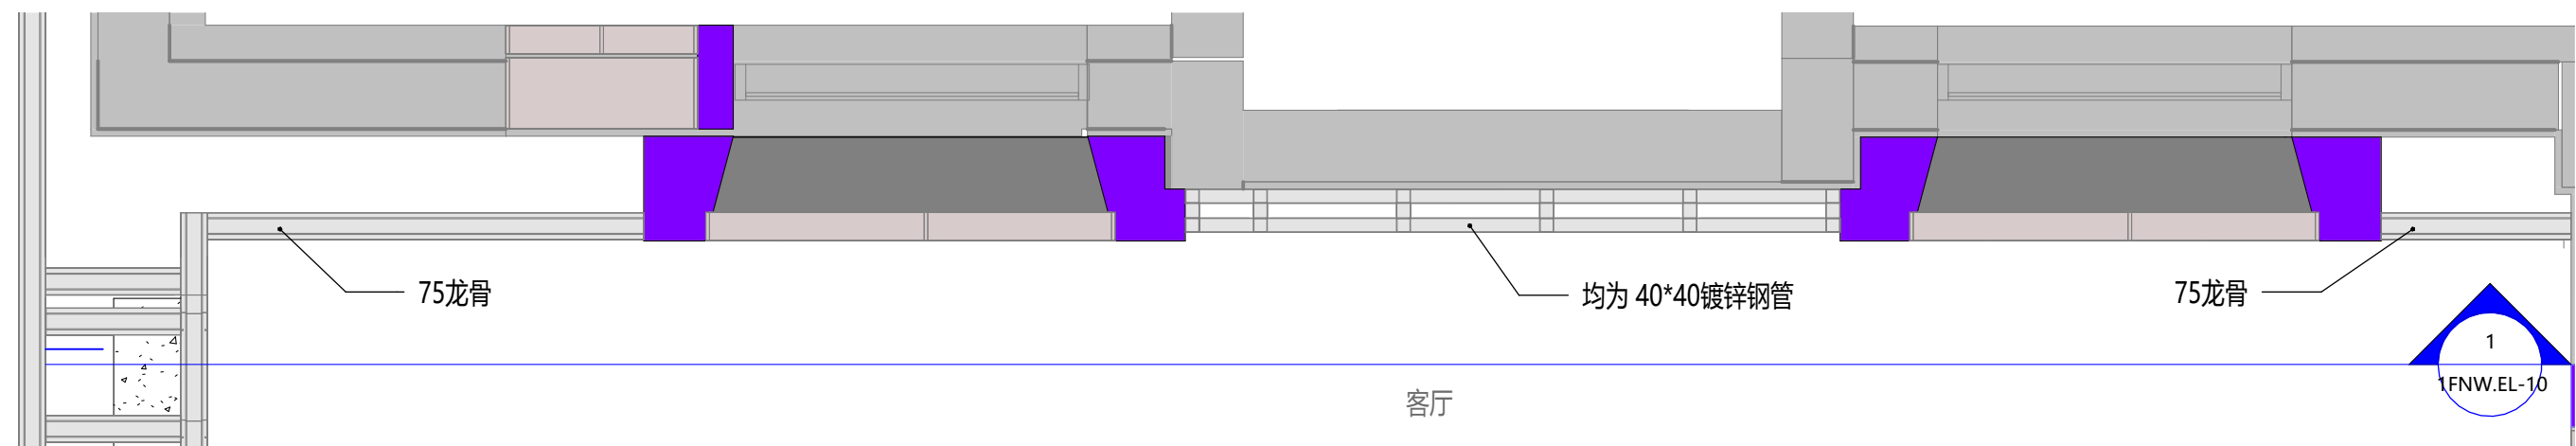

   编号	图例	说明
1		地面完成线
2		必要尺寸
3		起铺点
4		错缝要求 $a \geq 200$ $b \geq 150$
5		边砖宽度要求 $a \geq 200$
6		$b < 150$ 时 $a = b$

正式施工图
2026-08-21

Notes

1. 本图如与现场尺寸有误, 请施工人员和项目负责人联系。
2. 施工前施工人员应认真查阅此图, 如有不明确尺寸, 按现场测量为准。
3. 本图必须经甲乙双方认可并签字方可作为施工依据。

日期
Date 08/21/26

修订
Revision



Project 巨鹿路880号




比例	1:200
Scale	

1F客厅轻钢龙骨钢架墙立面图.

图纸编号
Drawing No.

1F.NW.EL-10

项目编号 ②
Project No.

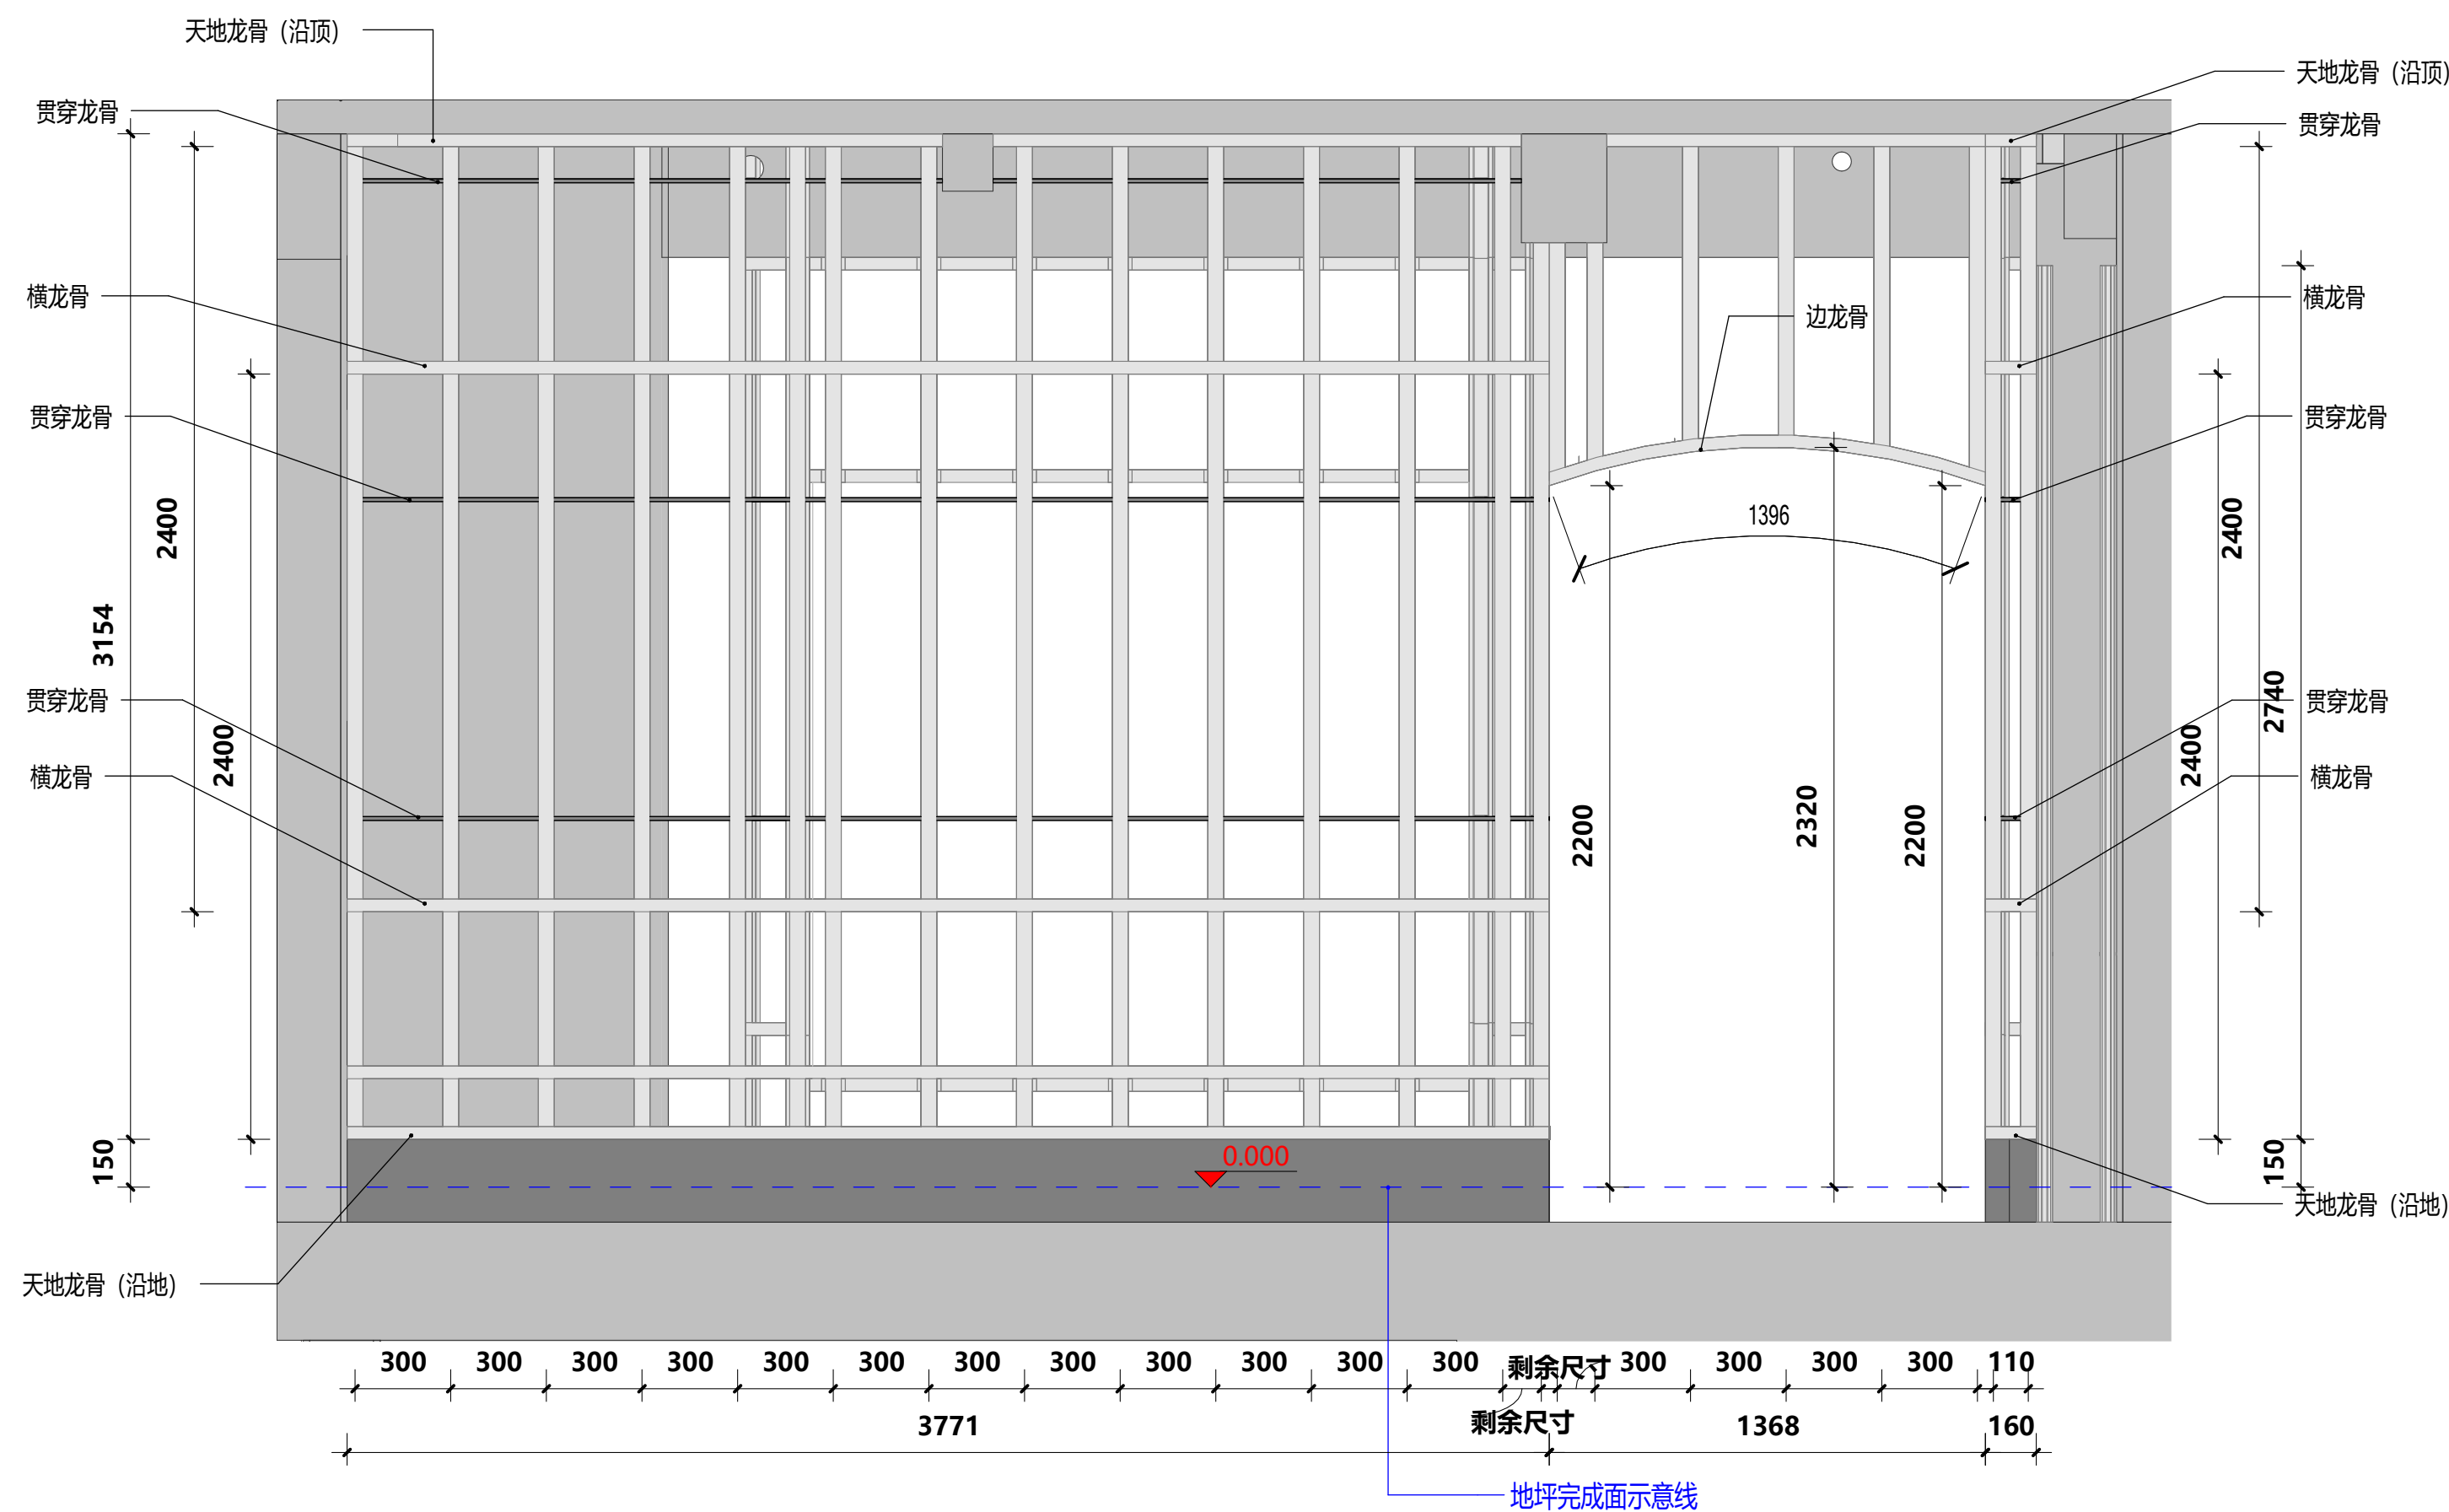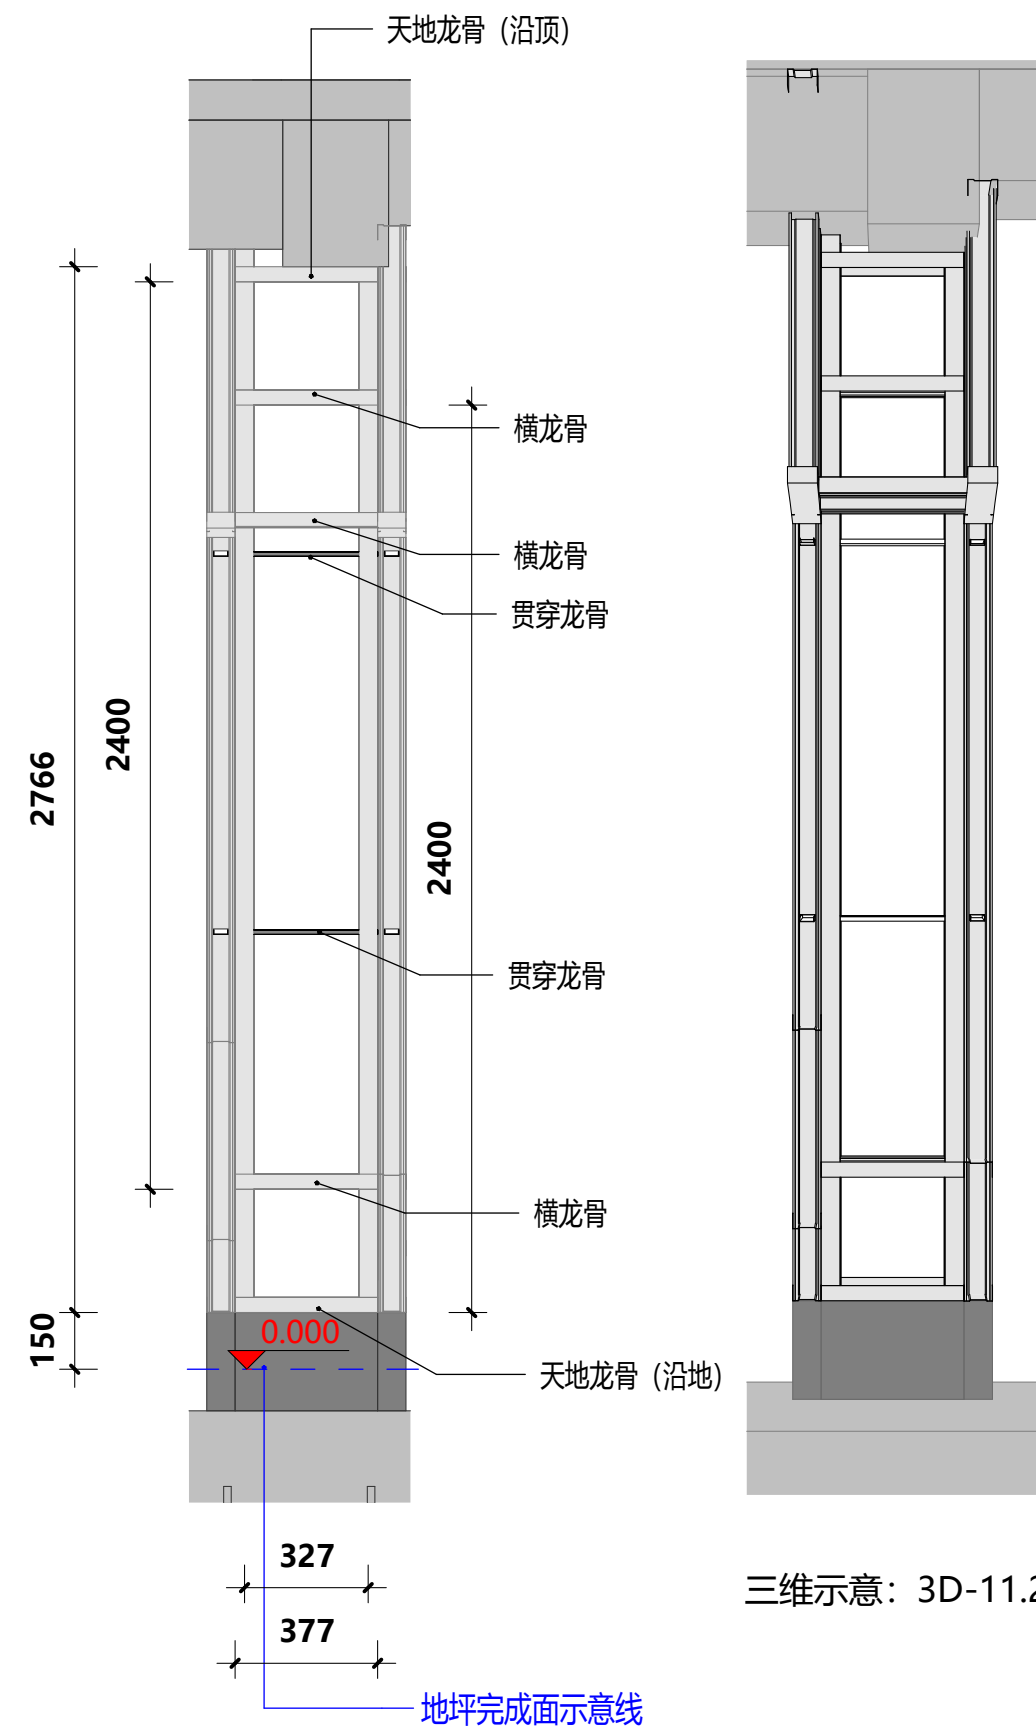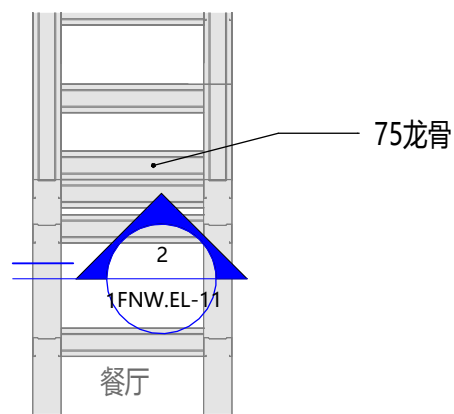

三维示意: 3D-11.3

编号	图例	说明
1		地面完成线
2		必要尺寸
3		起铺点
4		错缝要求 $a \geq 200 \text{ b} \geq 150$
5		边砖宽度要求 $a \geq 200$
6		$b < 150$ 时 $a = b$

五章

正式施工图
2026-08-21

主釋
later

本图经如与现场尺寸有误。请施工人员与项目负责人联系。
施工前施工人员应认真查阅此图，如有不明确尺寸，按现场测量为准。
本图纸必须经甲乙双方认可并签字方可作为施工依据。

日期
Date 08/21/26

television

項目
Project

巨鹿路880号

比例	1:20
----	------

cale

1F餐厅轻钢龙骨钢架墙立面图

— **КТО ШИРОКО ИЛИ ДЛИННО**


Drawing No.

15 DMM/EL 11

1F.NW.EL-11

项目编号 ②2

Project No.

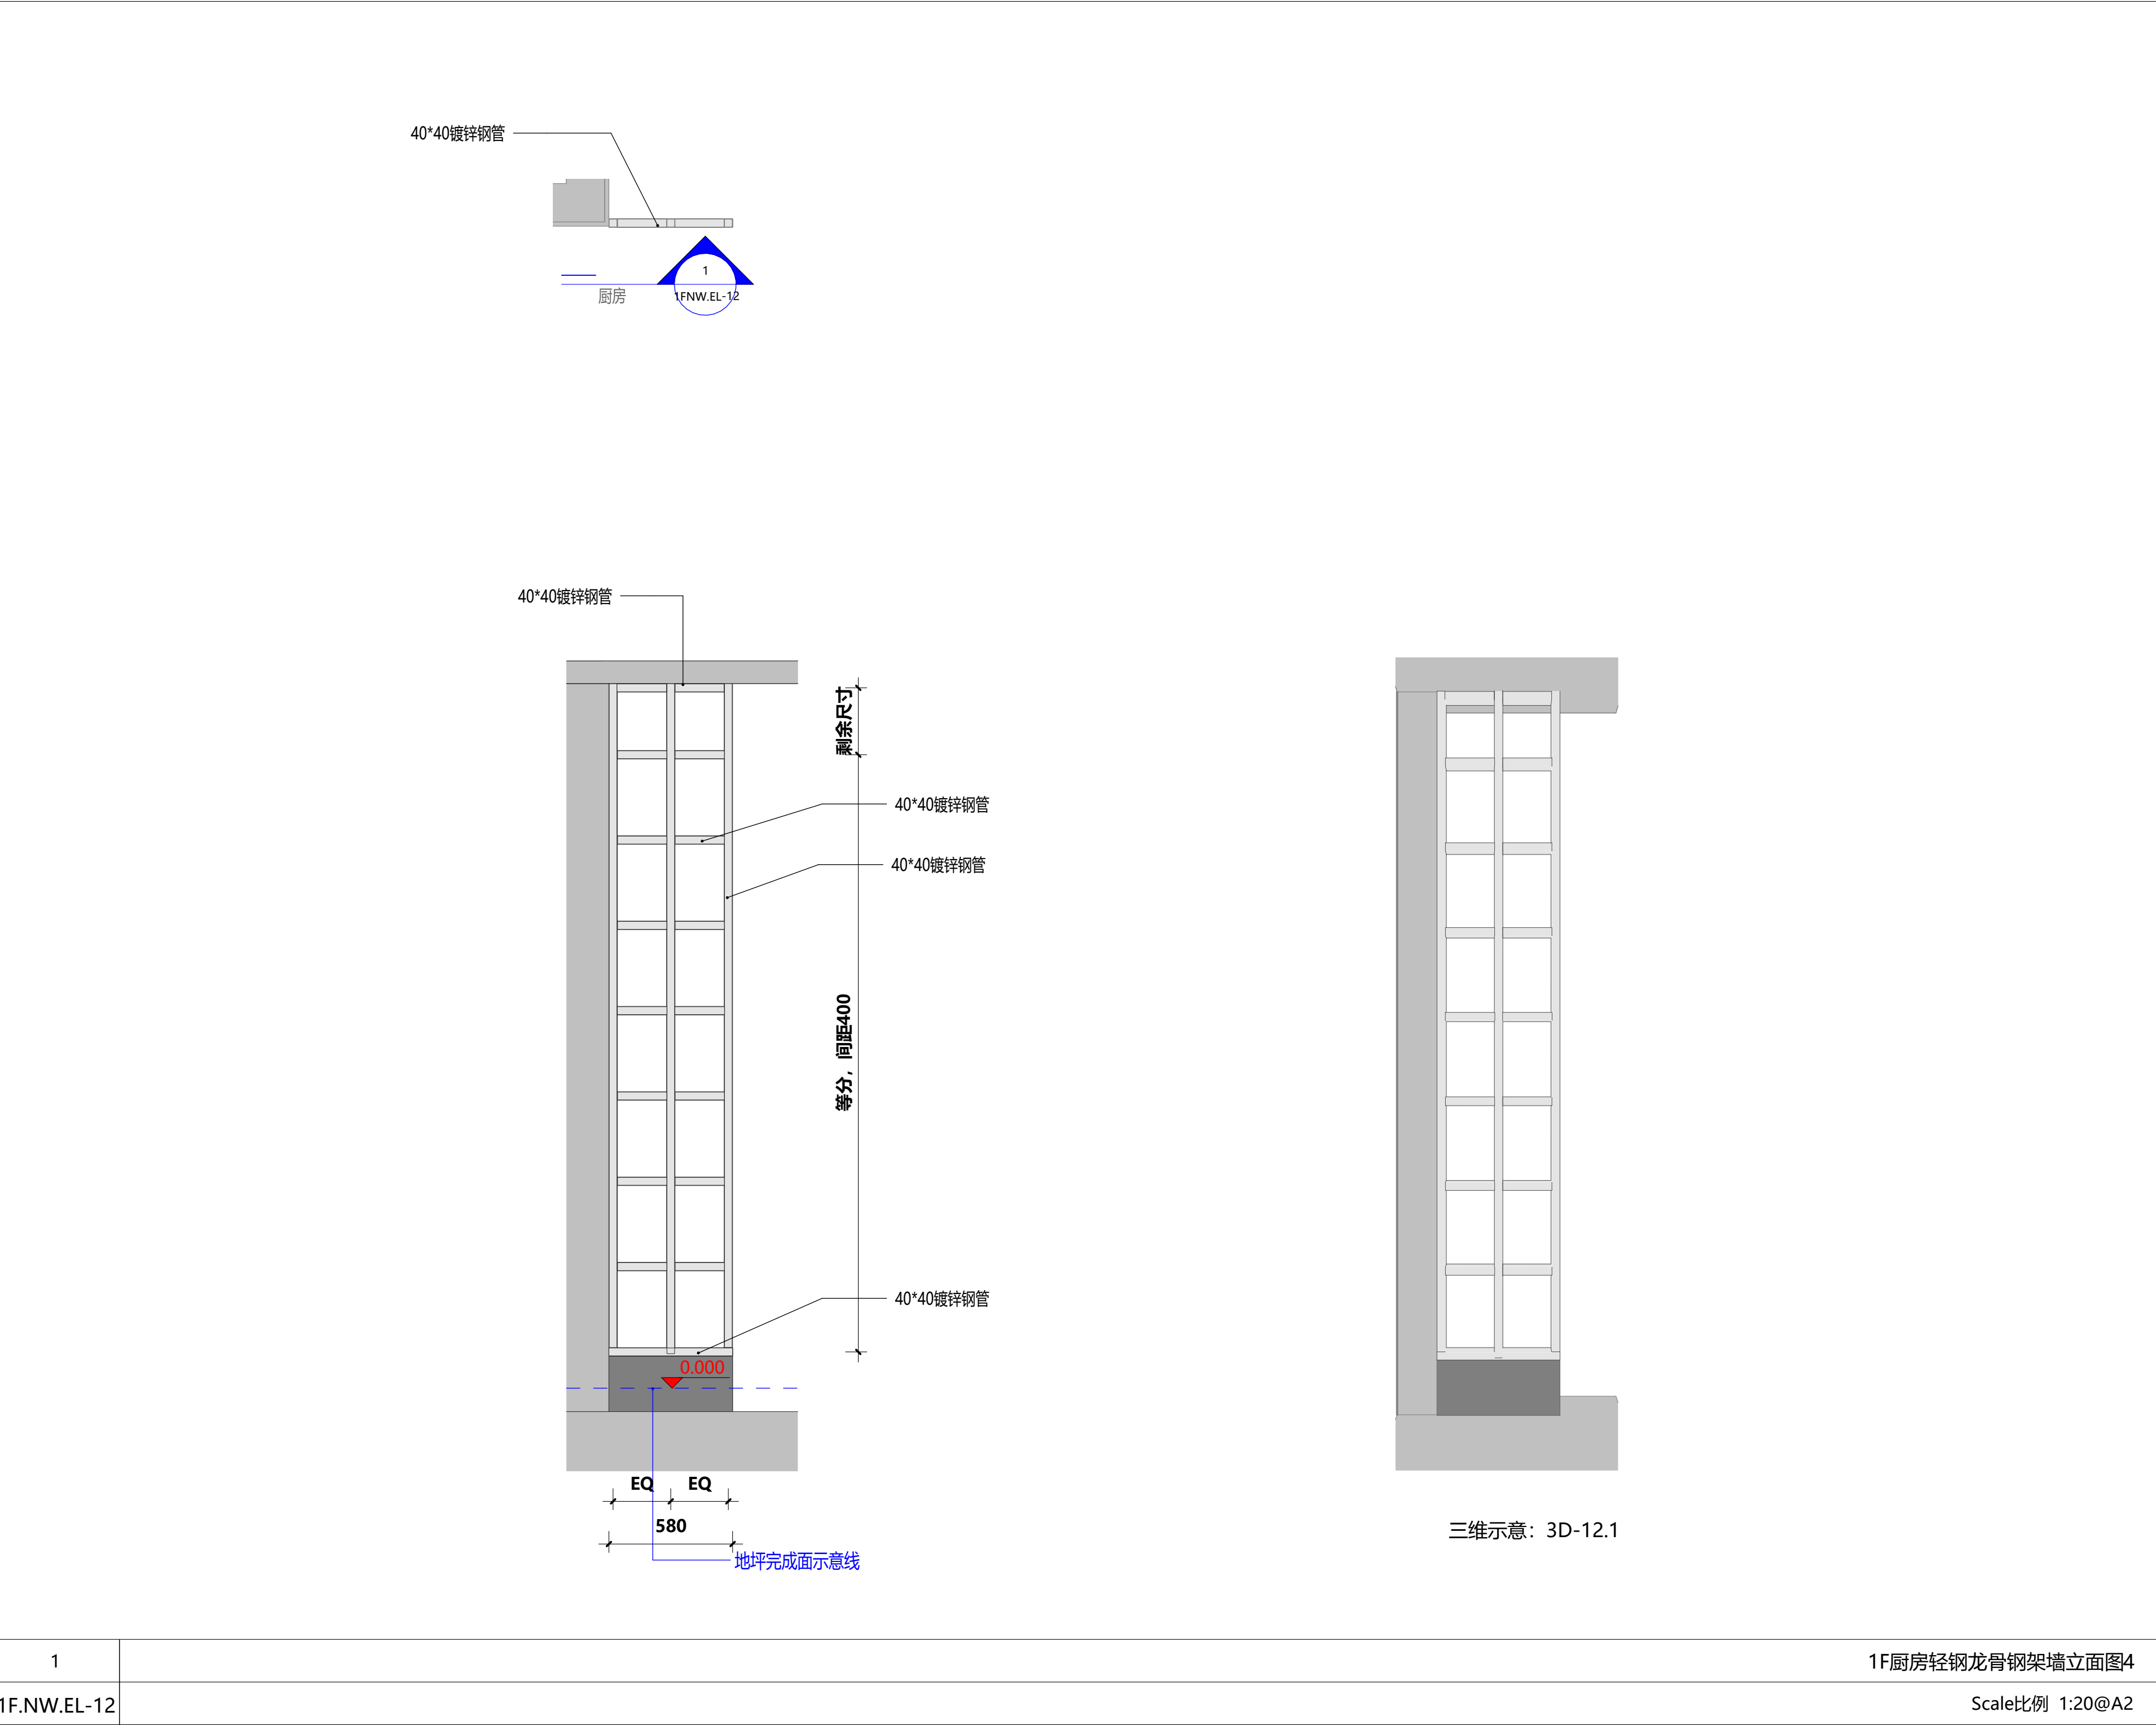

图例A 材质分类		
编号	图例	说明
1		原始墙、板、柱
2		混凝土导墙、构造柱、马牙槎
3		砌块砖
4		轻钢龙骨
5		钢架墙

图例B 施工时注意事项		
编号	图例	说明
1		地面完成线
2		必要尺寸
3		起铺点
4		错峰要求 $a \geq 200$ $b \geq 150$
5		边砖宽度要求 $a \geq 200$
6		$b < 150$ 时 $a = b$

盖章

正式施工图
2026-08-21

注释
Notes

1.本图纸如与现场尺寸有误，请施工人员与项目负责人联系。
2.施工前施工人员应认真查阅此图，如有不明确尺寸，按现场测量为准。
3.本图纸必须经甲乙双方认可并签字方可作为施工依据。

日期
Date

08/21/26

修订
Revision

1

Project
项目

巨鹿路880号

Scale
比例

1:20@A2

1F厨房轻钢龙骨钢架墙立面图

Drawing No.
图纸编号

1F.NW.EL-12

Project No.
项目编号

© 2025