


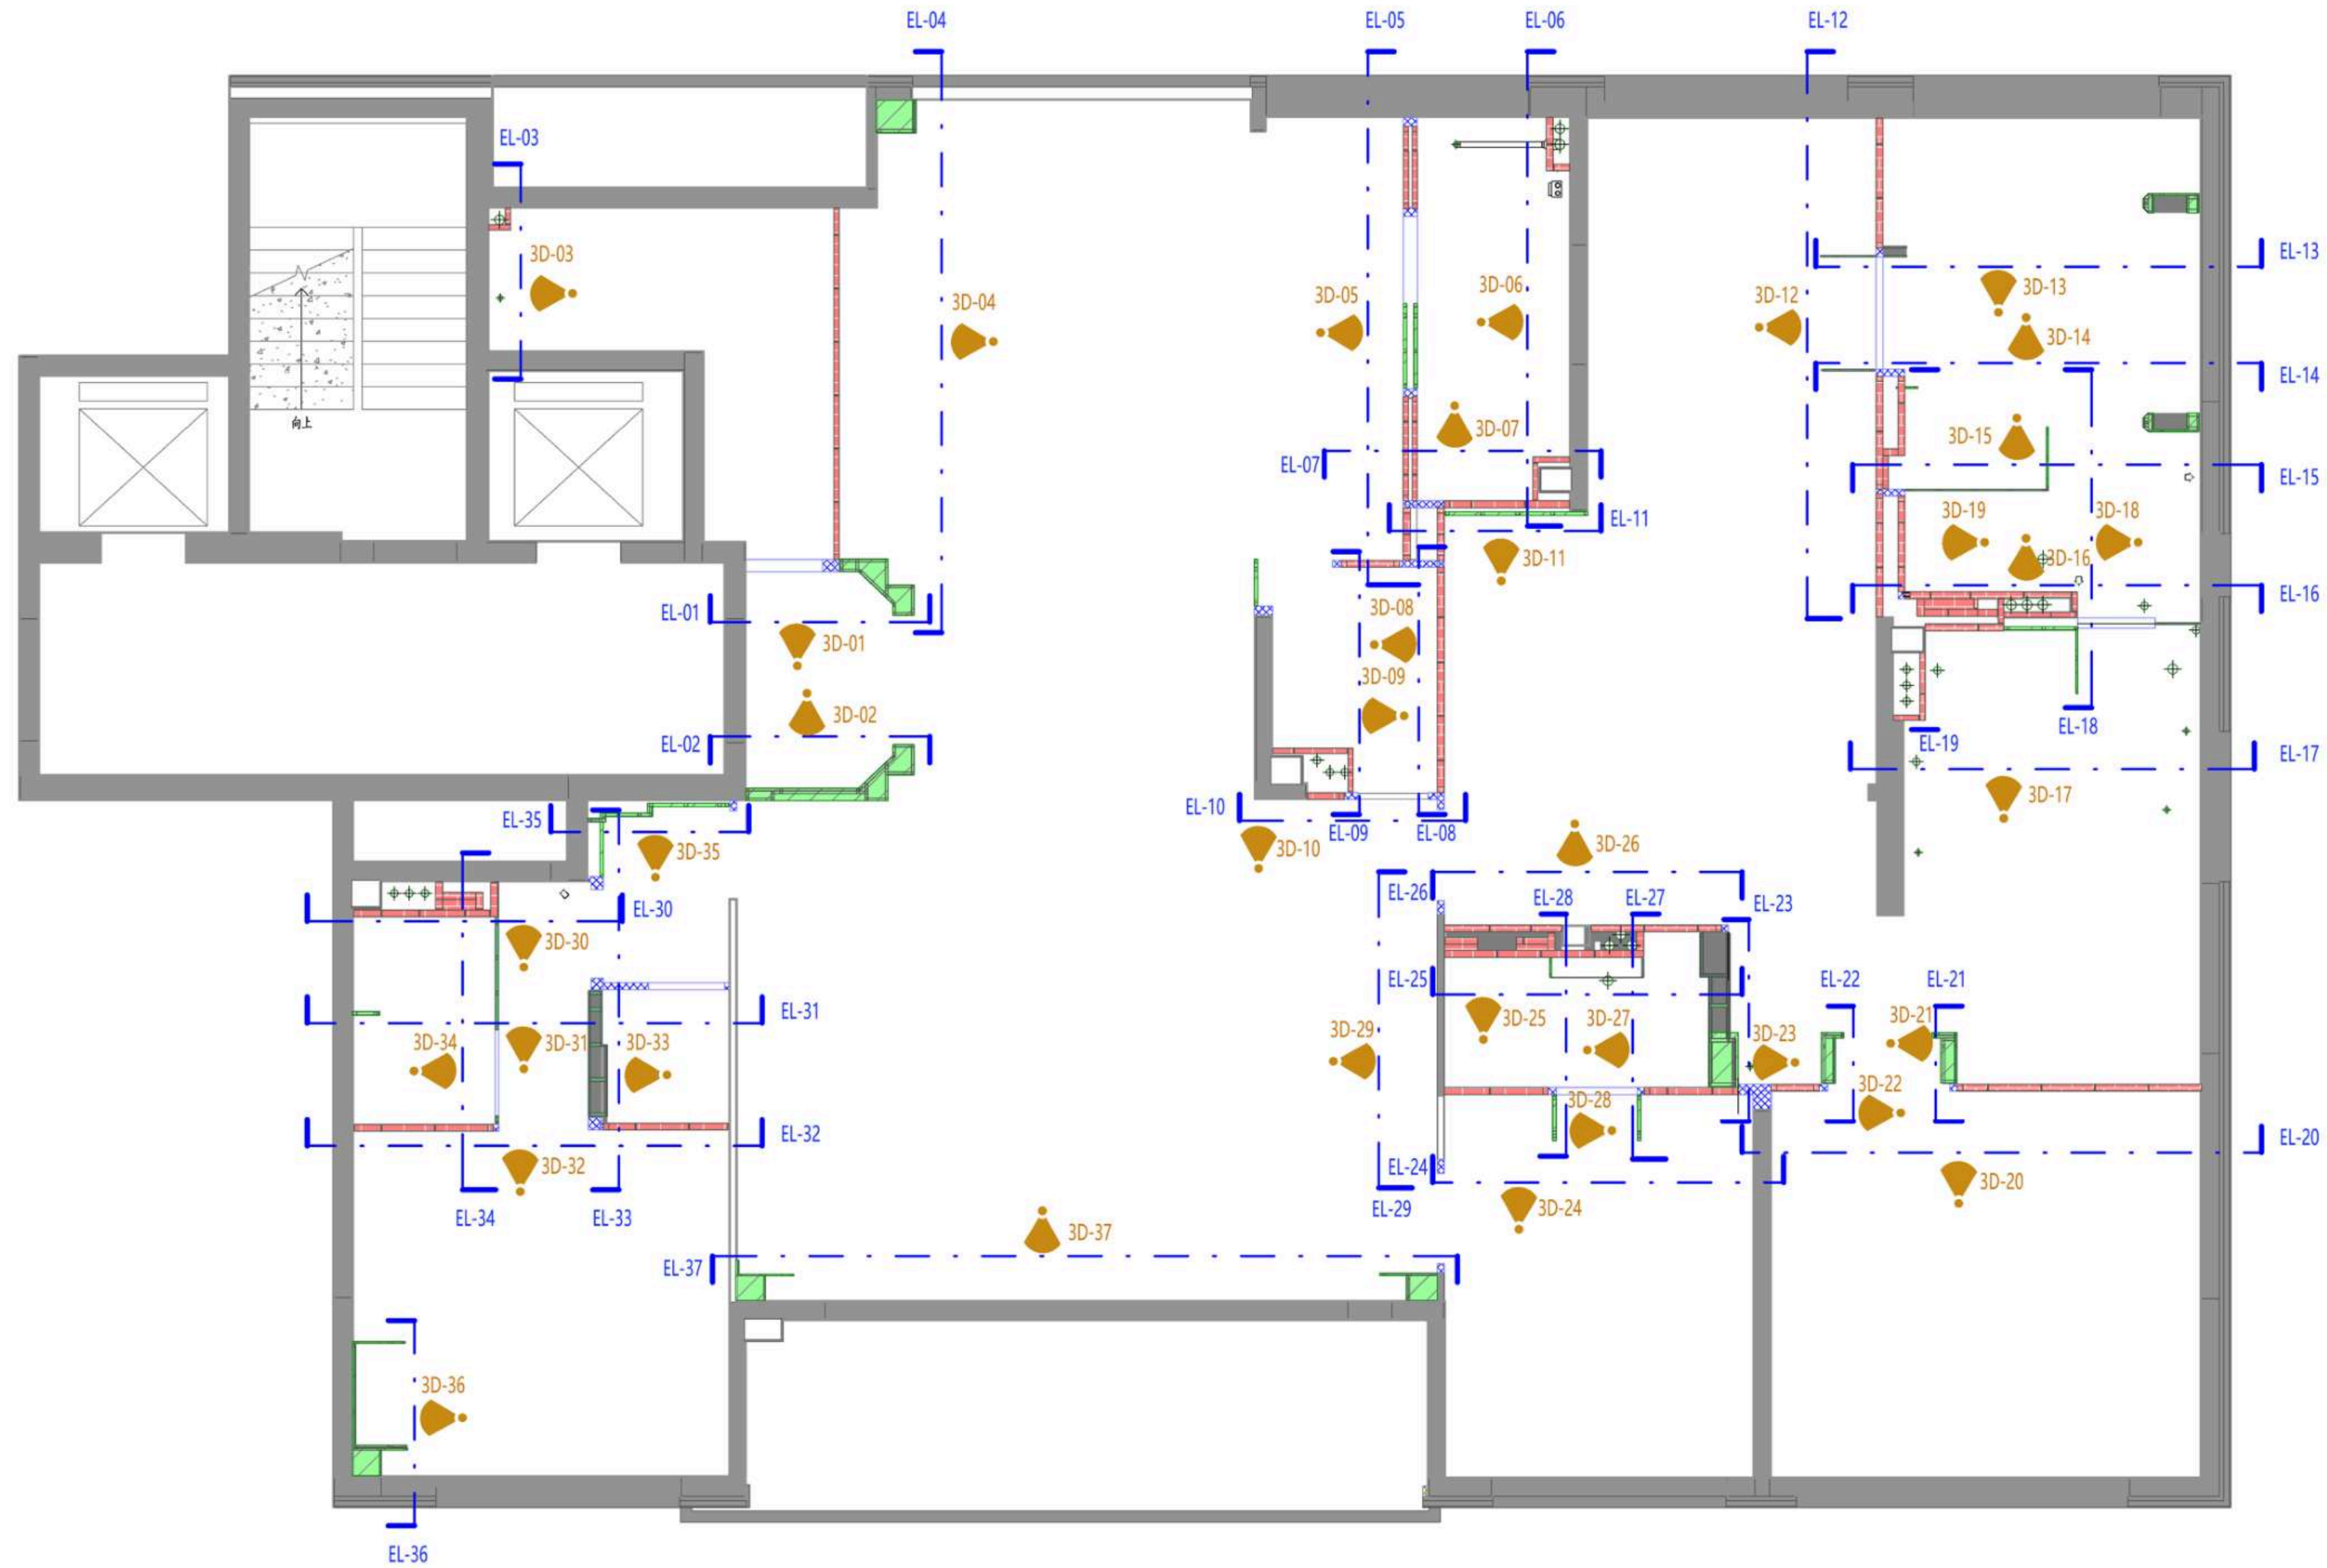

LEGEND图例

编号	图例	说明
1		原始墙、板、柱
2		结构柱
3		PC砖
4		红砖
5		钢架墙

日期
Date 01/07/26

修订
Revision

项目
Project

潮映华岸府3-801

Scale
比例 1:60@A2


PC墙立面索引图

Drawing No.
图纸编号

4-NW-04

Project No.
项目编号

©2025

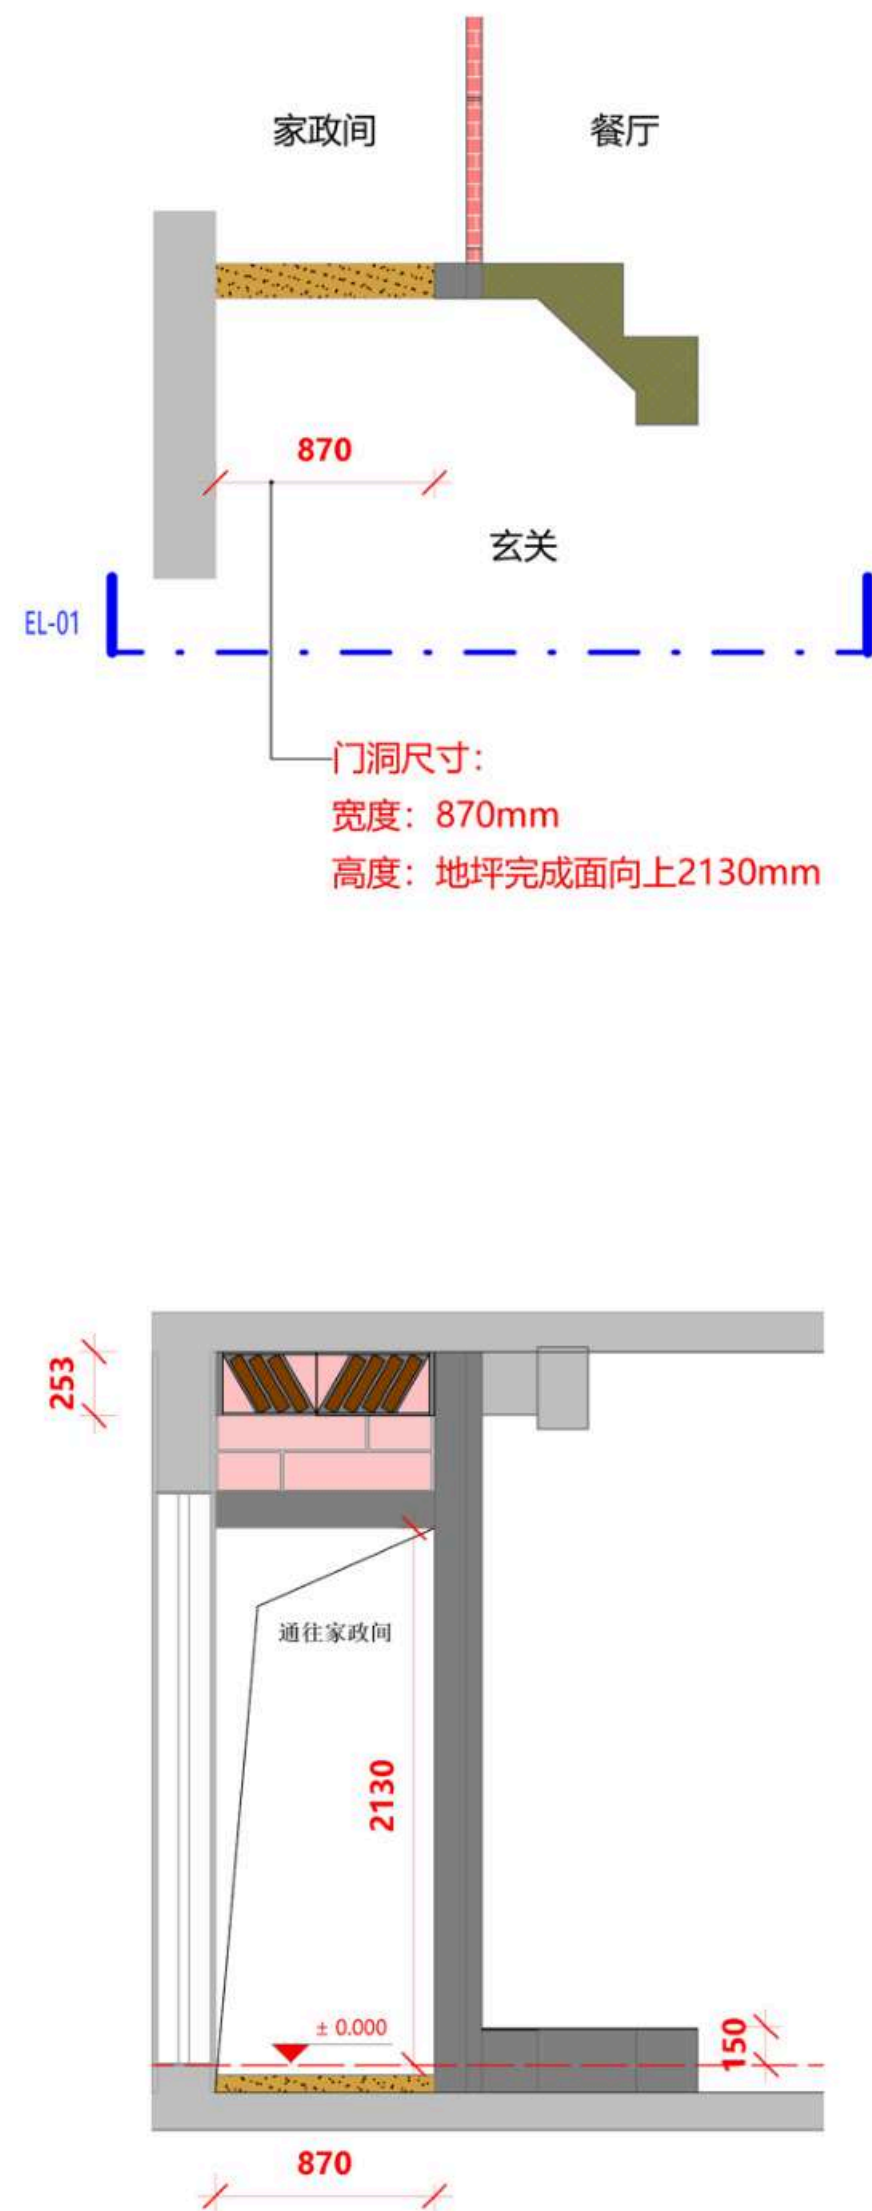

ELBORN

LEGEND图例

图例A 材质分类		
编号	图例	说明
1		原始墙、板、柱
2		混凝土导墙、结构柱、马牙槎
3		PC砖
4		红砖
5		钢架墙
6		止水坎
7		混凝土止水坎上加5mm钢板

图例B 施工时注意事项		
编号	图例	说明
1		地面完成线
2		必要尺寸
3		起铺点
4		错峰要求 $a \geq 200$ $b \geq 150$
5		边砖宽度要求 $a \geq 200$
6		$b < 150$ 时 $a = b$

日期
Date 01/07/26

修订
Revision

项目
Project
潮映华府3-801

Scale
比例 1:30@A2
PC砖墙01

Drawing No.
图纸编号
5-PCW-01




Project No.
项目编号
©2025

正式施工图
2026-01-27

1
EL-01
PC砖墙立面图01
Scale比例 1 : 30@A2

1
3D-01
PC砖墙三维示意图01
Scale比例 1:30@A2

注释
Notes
1.本图纸如与现场尺寸有误, 请施工人员与项目负责人联系。
2.施工前施工人员应认真查阅此图, 如有不明确尺寸, 按现场测量为准。
3.本图纸必须经甲乙双方认可并签字方可作为施工依据。

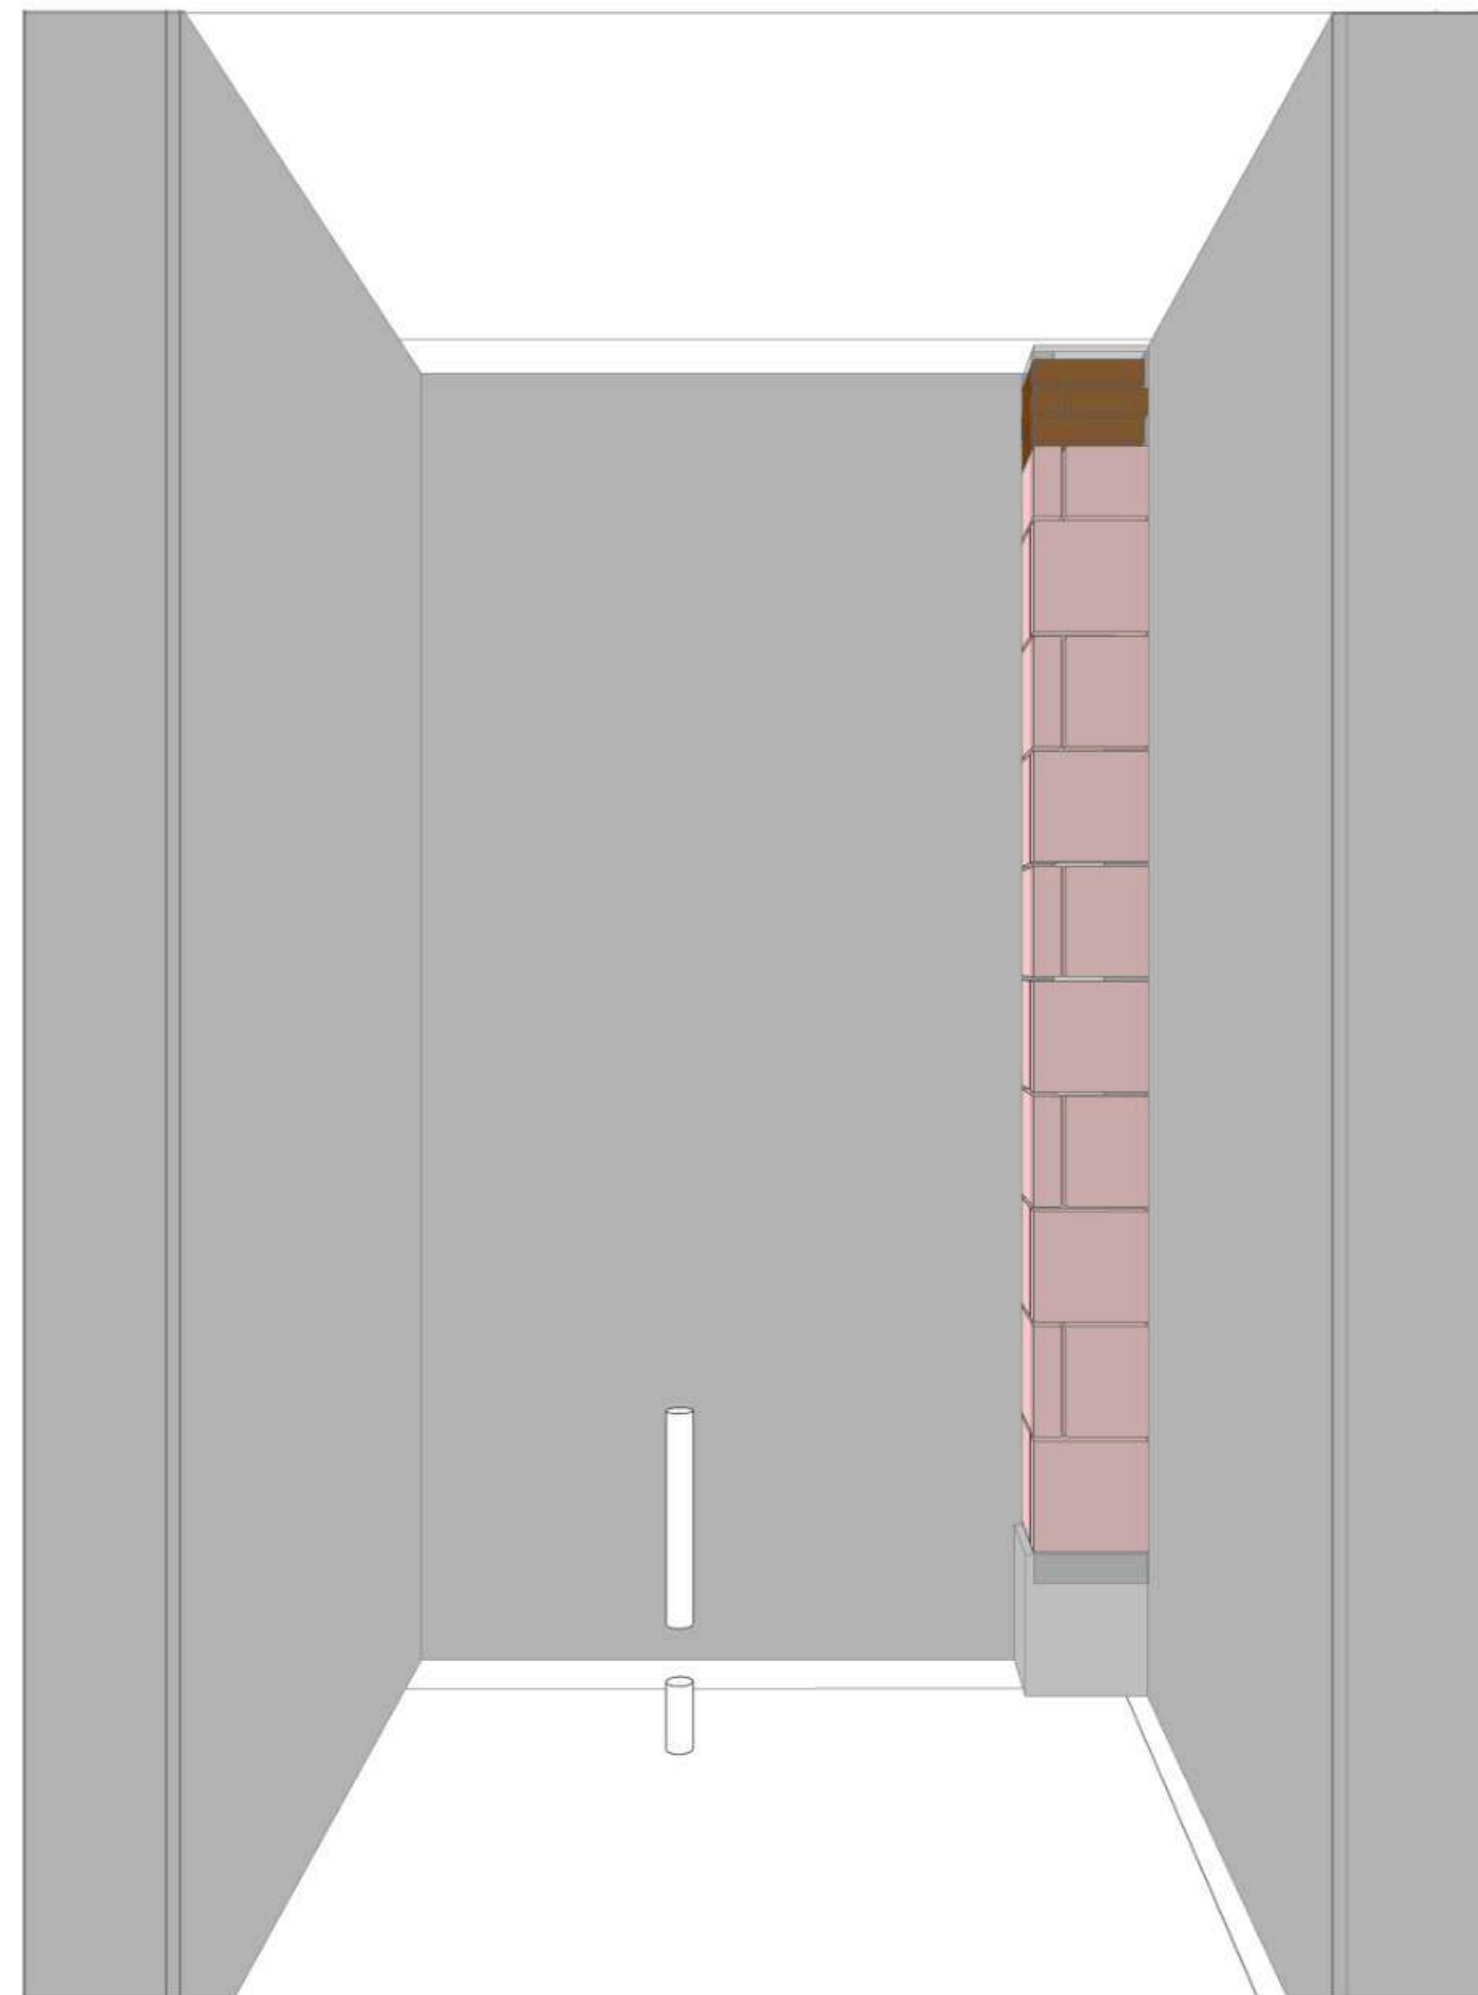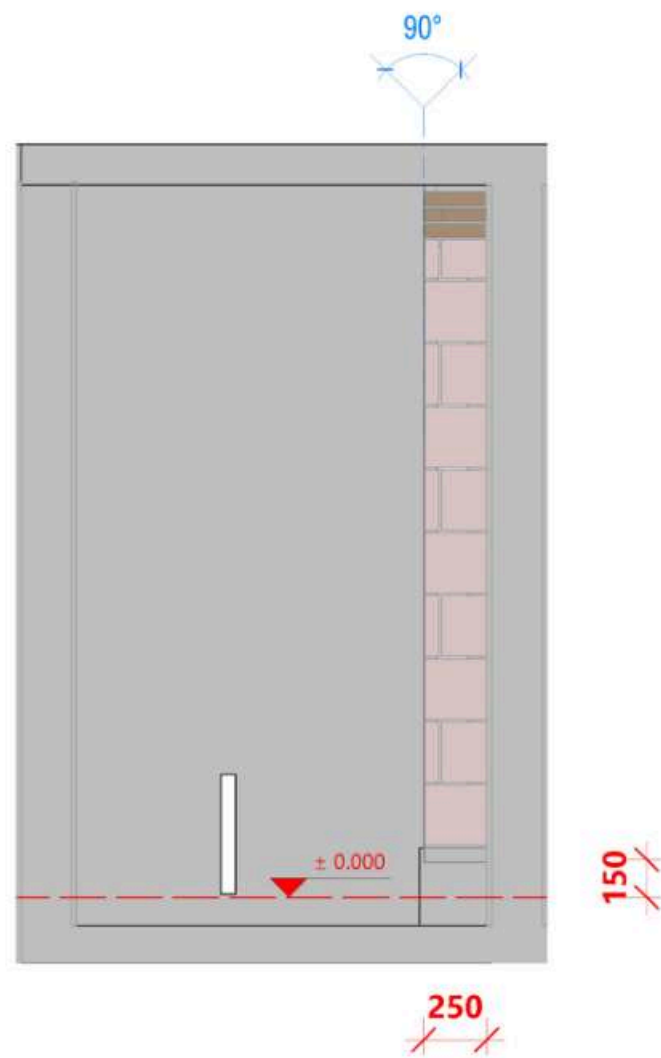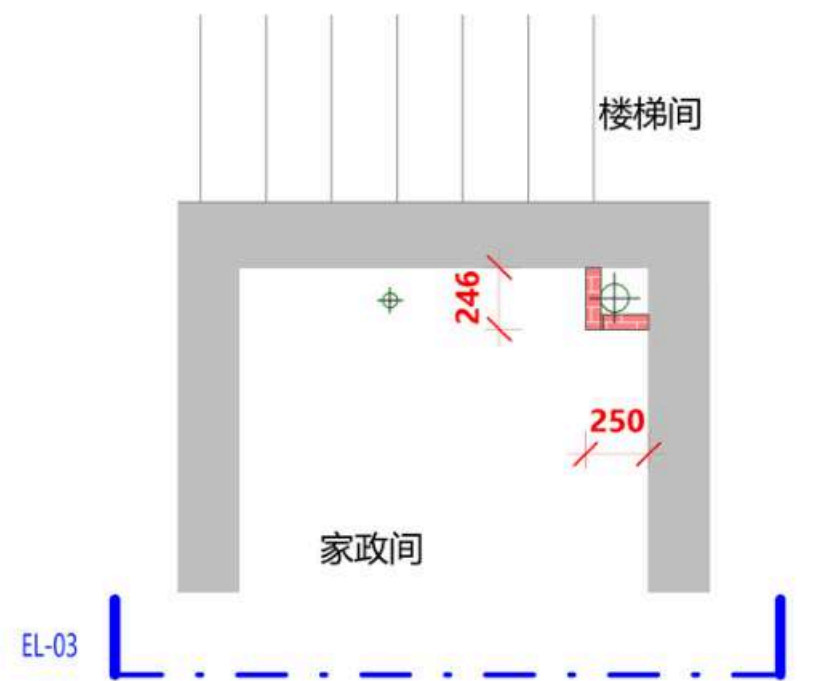

正式施工图
2026-01-27

ELBORN

LEGEND图例

图例A 材质分类		
编号	图例	说明
1		原始墙、板、柱
2		混凝土导墙、结构柱、马牙槎
3		PC砖
4		红砖
5		钢架墙
6		止水坎
7		混凝土止水坎上加5mm钢板
图例B 施工时注意事项		
编号	图例	说明
1		地面完成线
2		必要尺寸
3		起铺点
4		错峰要求 $a \geq 200$ $b \geq 150$
5		边砖宽度要求 $a \geq 200$
6		$b < 150$ 时 $a = b$

日期
Date 01/08/26

修订
Revision

项目
Project
潮映华府3-801

Scale
比例 1:30@A2
PC砖墙03

Drawing No.
图纸编号
6-PCW-03

Project No.
项目编号
©2025

1
EL-03
PC砖墙立面图03
Scale比例 1 : 30@A2

1
3D-03
PC砖墙三维示意图03
Scale比例 1:30@A2

注释
Notes
1.本图纸如与现场尺寸有误，请施工人员与项目负责人联系。
2.施工前施工人员应认真查阅此图，如有不明确尺寸，按现场测量为准。
3.本图纸必须经甲乙双方认可并签字方可作为施工依据。

LEGEND图例

图例A 材质分类		
编号	图例	说明
1		原始墙、板、柱
2		混凝土导墙、结构柱、马牙槎
3		PC砖
4		红砖
5		钢架墙
6		止水坎
7		混凝土止水坎上加5mm钢板

图例B 施工时注意事项		
编号	图例	说明
1		地面完成线
2		必要尺寸
3		起铺点
4		错缝要求 $a \geq 200$ $b \geq 150$
5		边砖宽度要求 $a \geq 200$
6		$b < 150$ 时 $a = b$

日期
Date 01/08/26

修订
Revision


项目
Project 潮映华府3-801

Scale
比例 1:30@A2



PC砖墙04

Drawing No.
图纸编号 7-PCW-04

Project No.
项目编号 ©2025

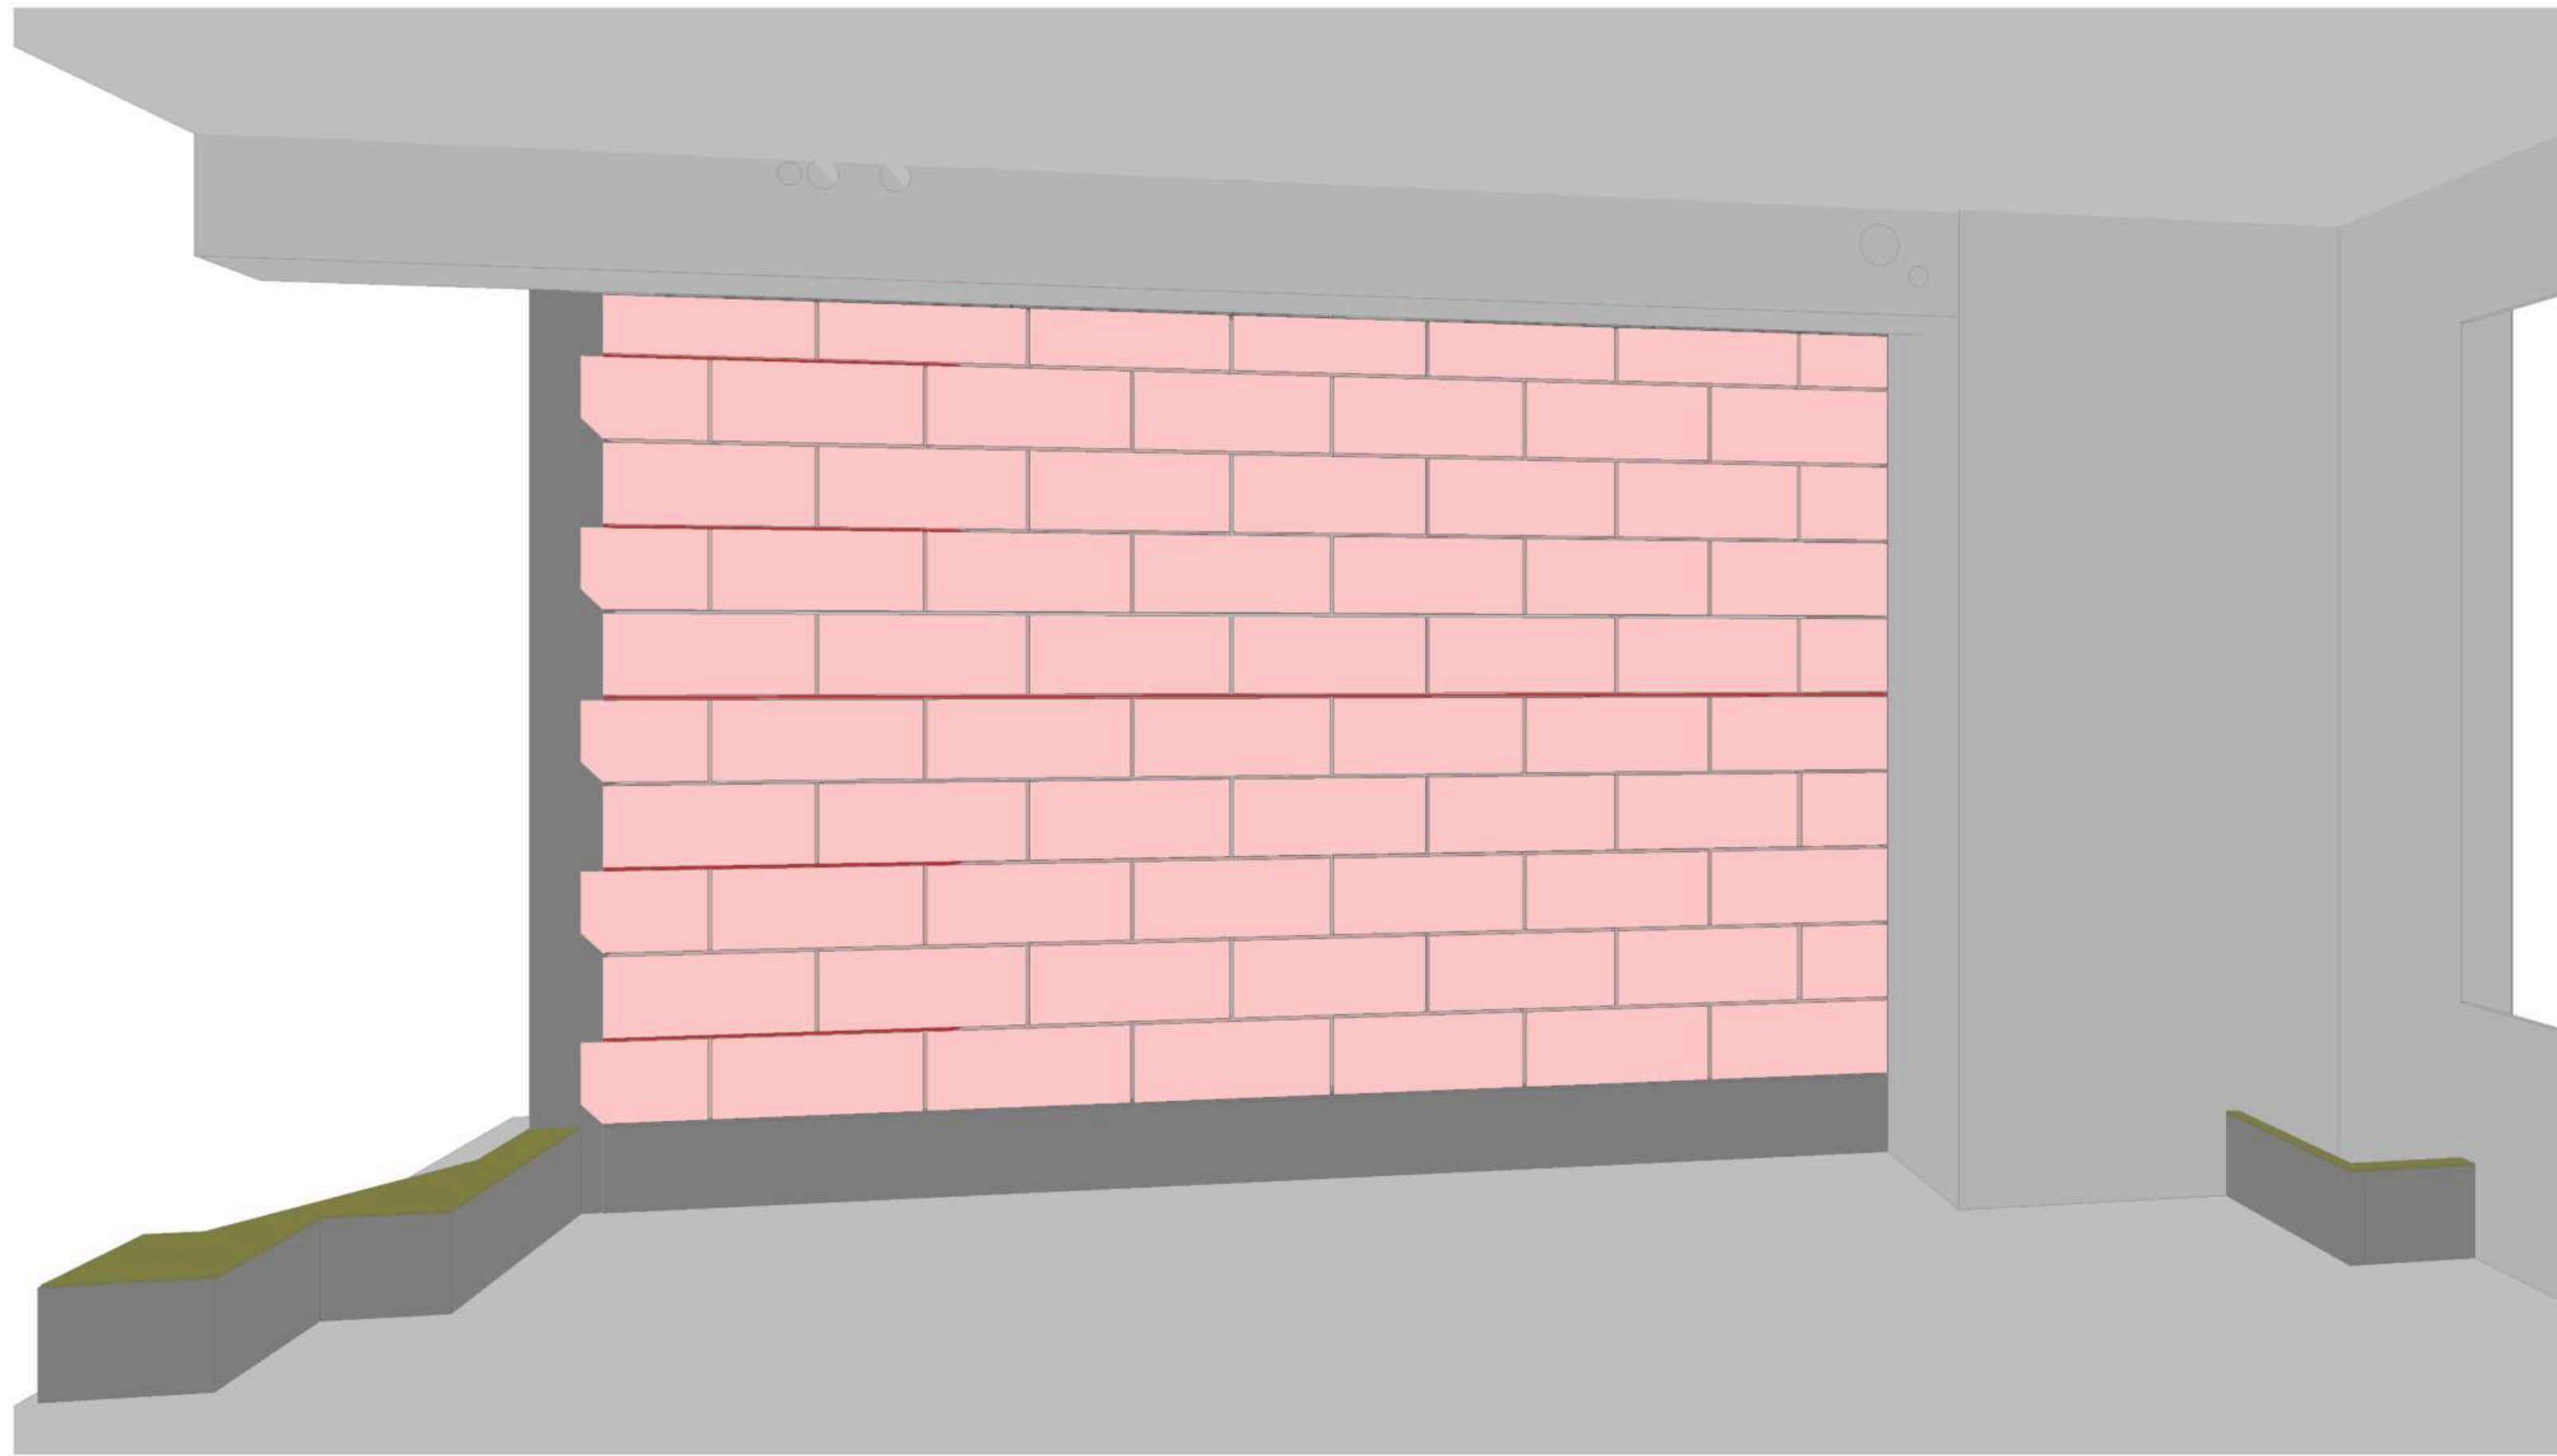

正式施工图
2026-01-27

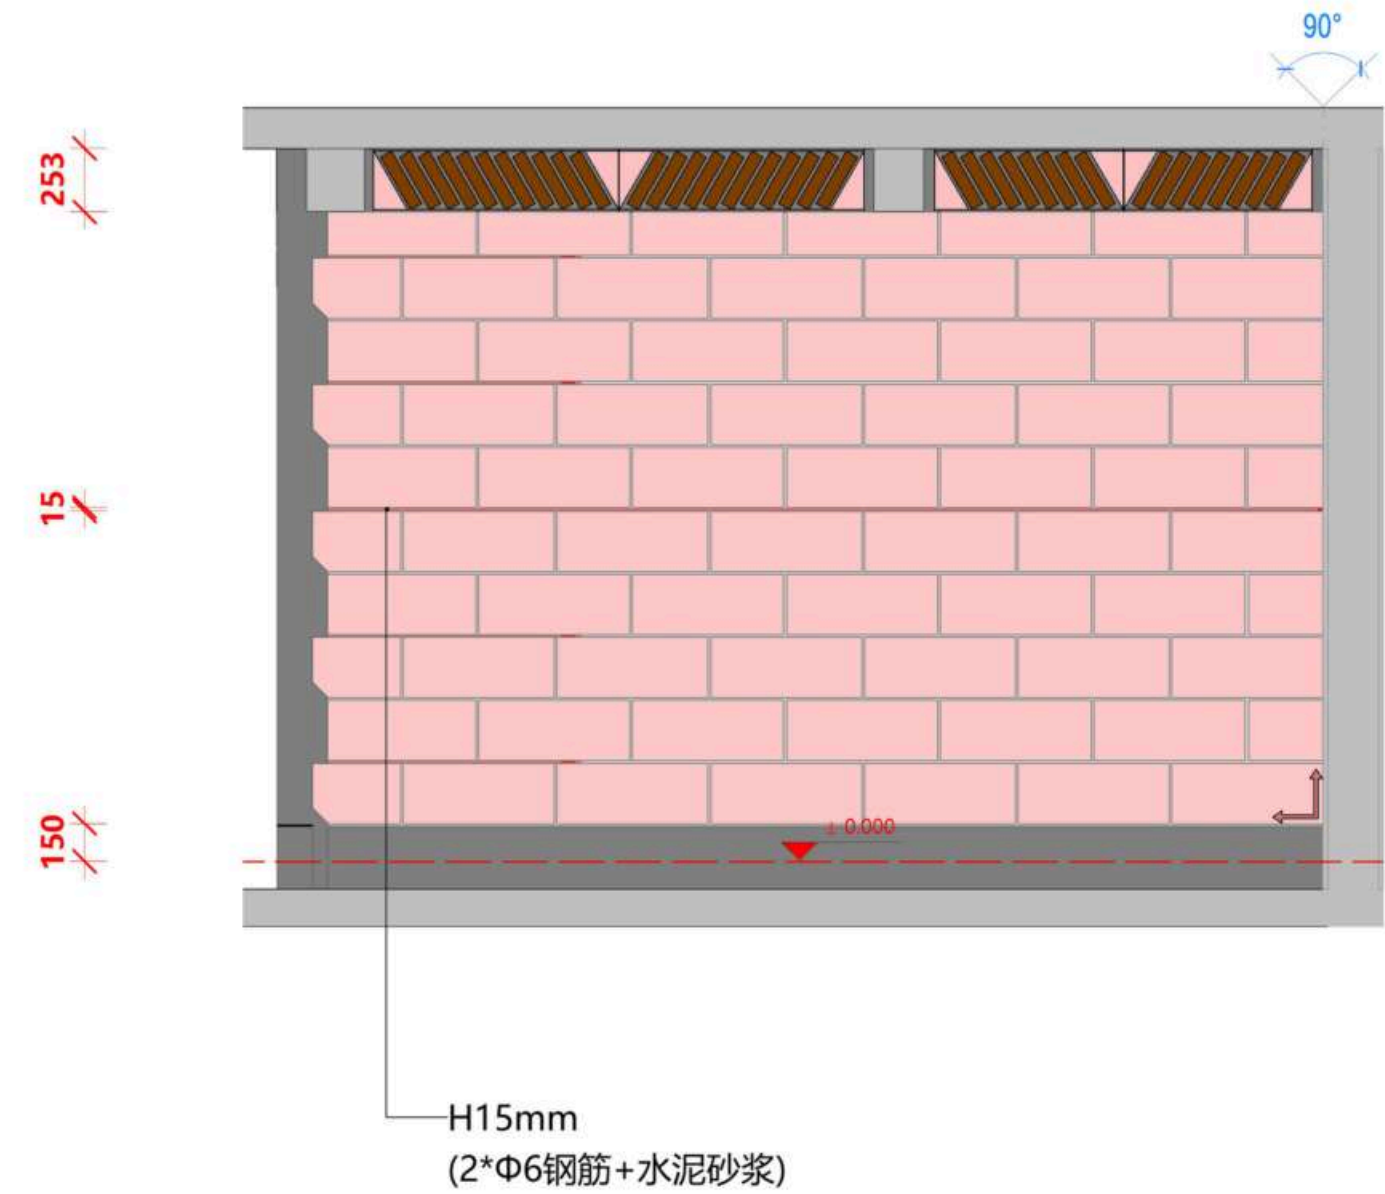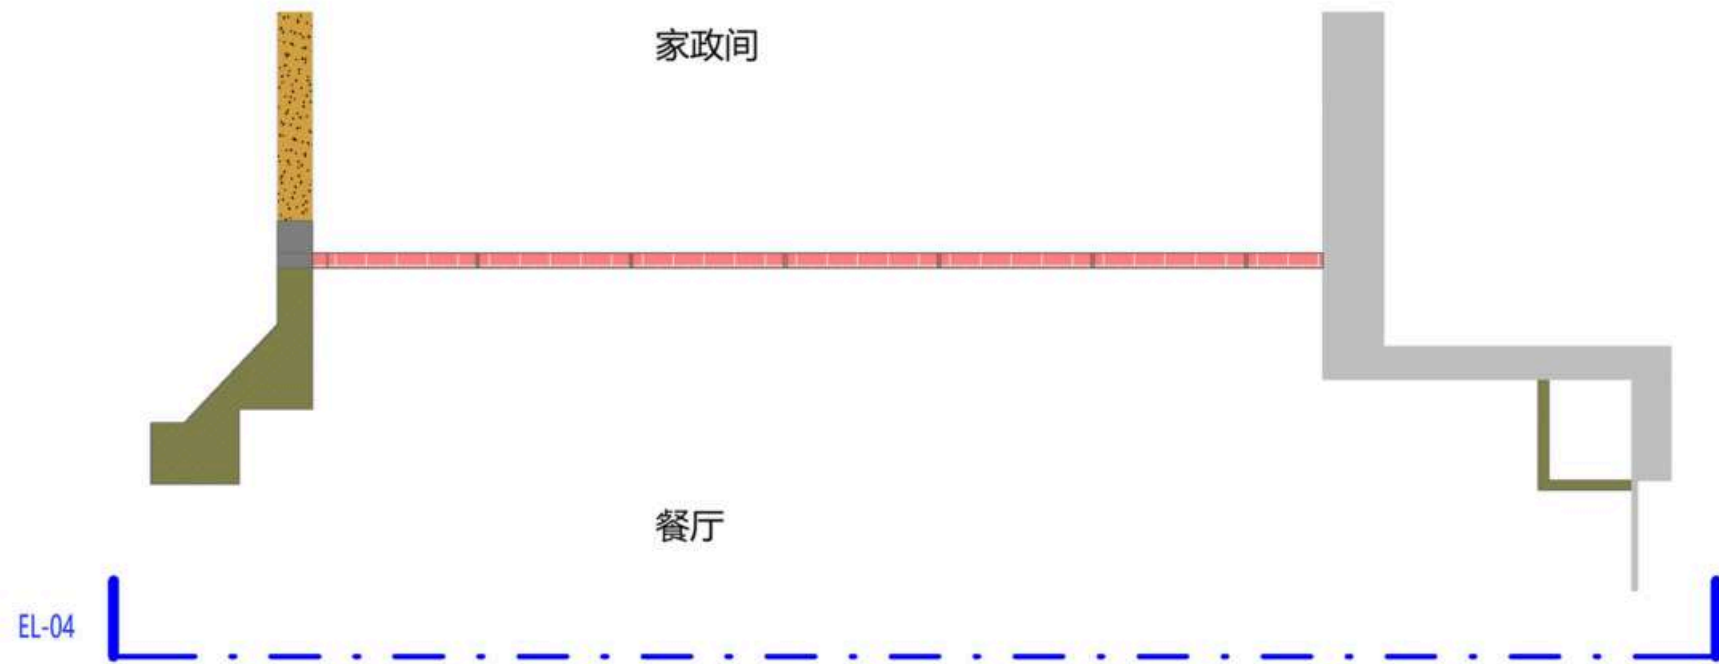

PC砖墙立面图04

Scale比例 1 : 30@A2

1

3D-04

PC砖墙三维示意图04

Scale比例 1:30@A2

注释

Notes
1.本图纸如与现场尺寸有误,请施工人员与项目负责人联系。
2.施工前施工人员应认真查阅此图,如有不明确尺寸,按现场测量为准。
3.本图纸必须经甲乙双方认可并签字方可作为施工依据。

LEGEND图例

图例A 材质分类		
编号	图例	说明
1		原始墙、板、柱
2		混凝土导墙、结构柱、马牙槎
3		PC砖
4		红砖
5		钢架墙
6		止水坎
7		混凝土止水坎上加5mm钢板

图例B 施工时注意事项		
编号	图例	说明
1		地面完成线
2		必要尺寸
3		起铺点
4		错缝要求 $a \geq 200$ $b \geq 150$
5		边砖宽度要求 $a \geq 200$
6		$b < 150$ 时 $a = b$

日期
Date 01/08/26


修订
Revision

项目
Project
潮映华岸府3-801


Scale
比例 1:30@A2
PC砖墙06

Drawing No.
图纸编号
9-PCW-06

Project No.
项目编号
©2025

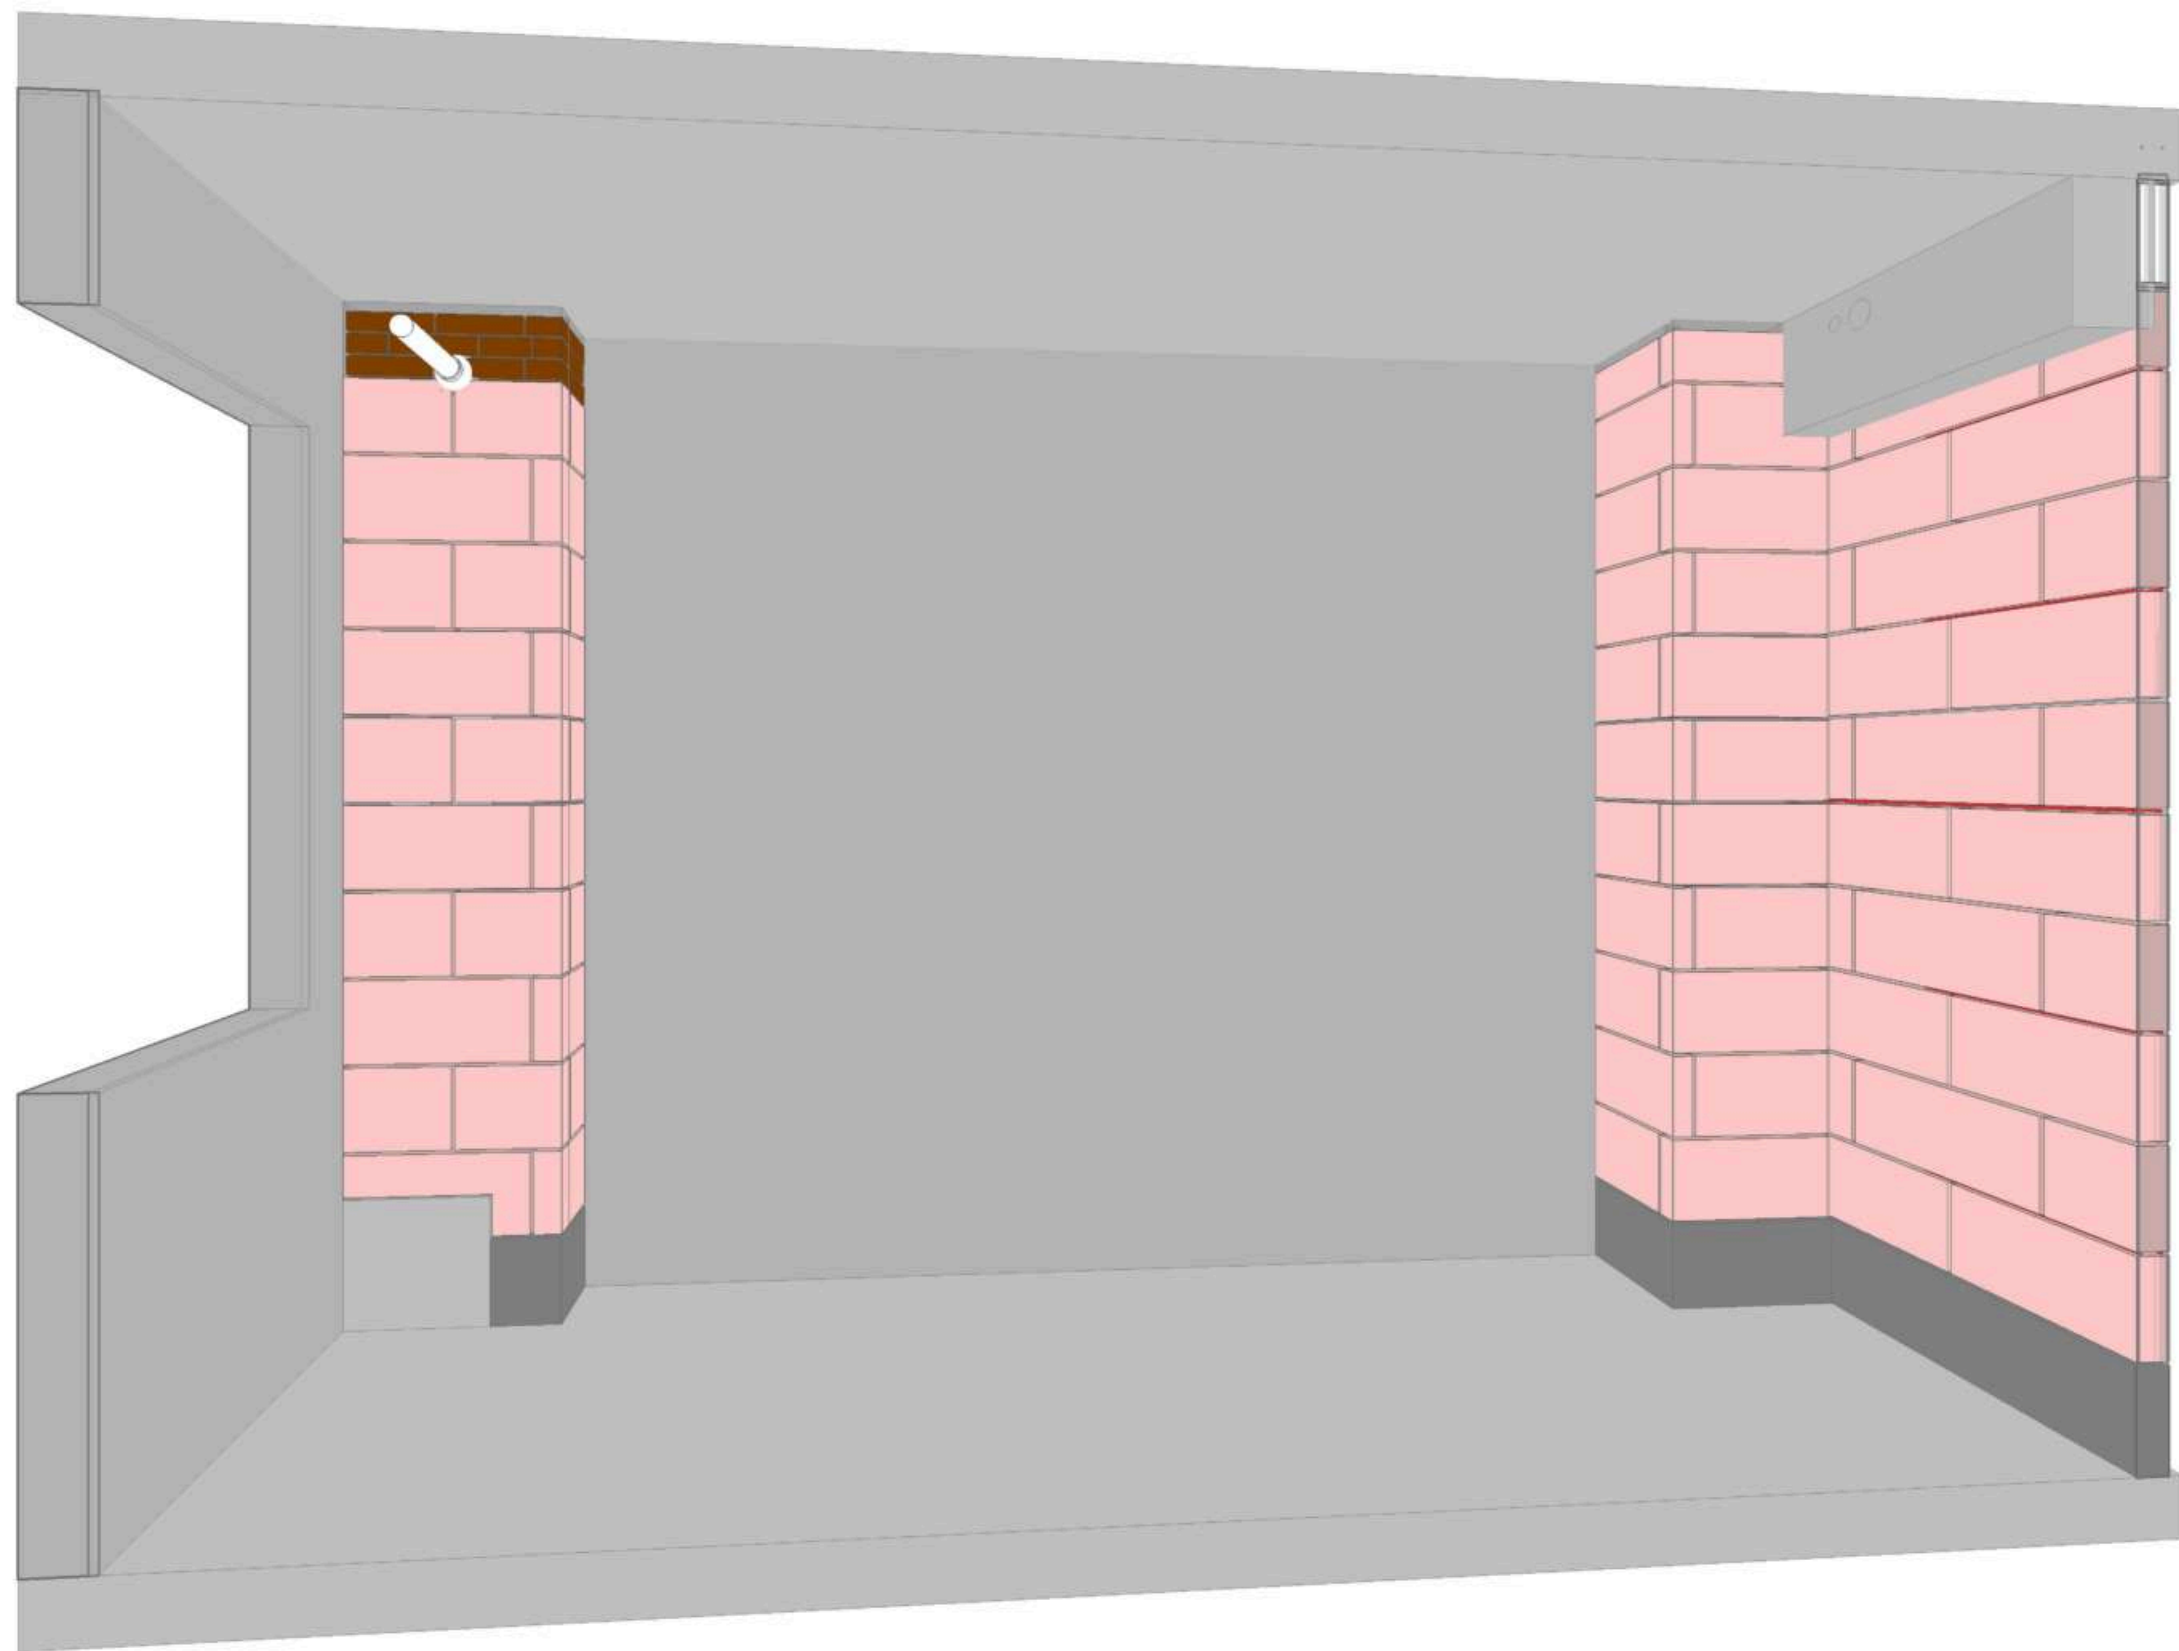

正式施工图
2026-01-27

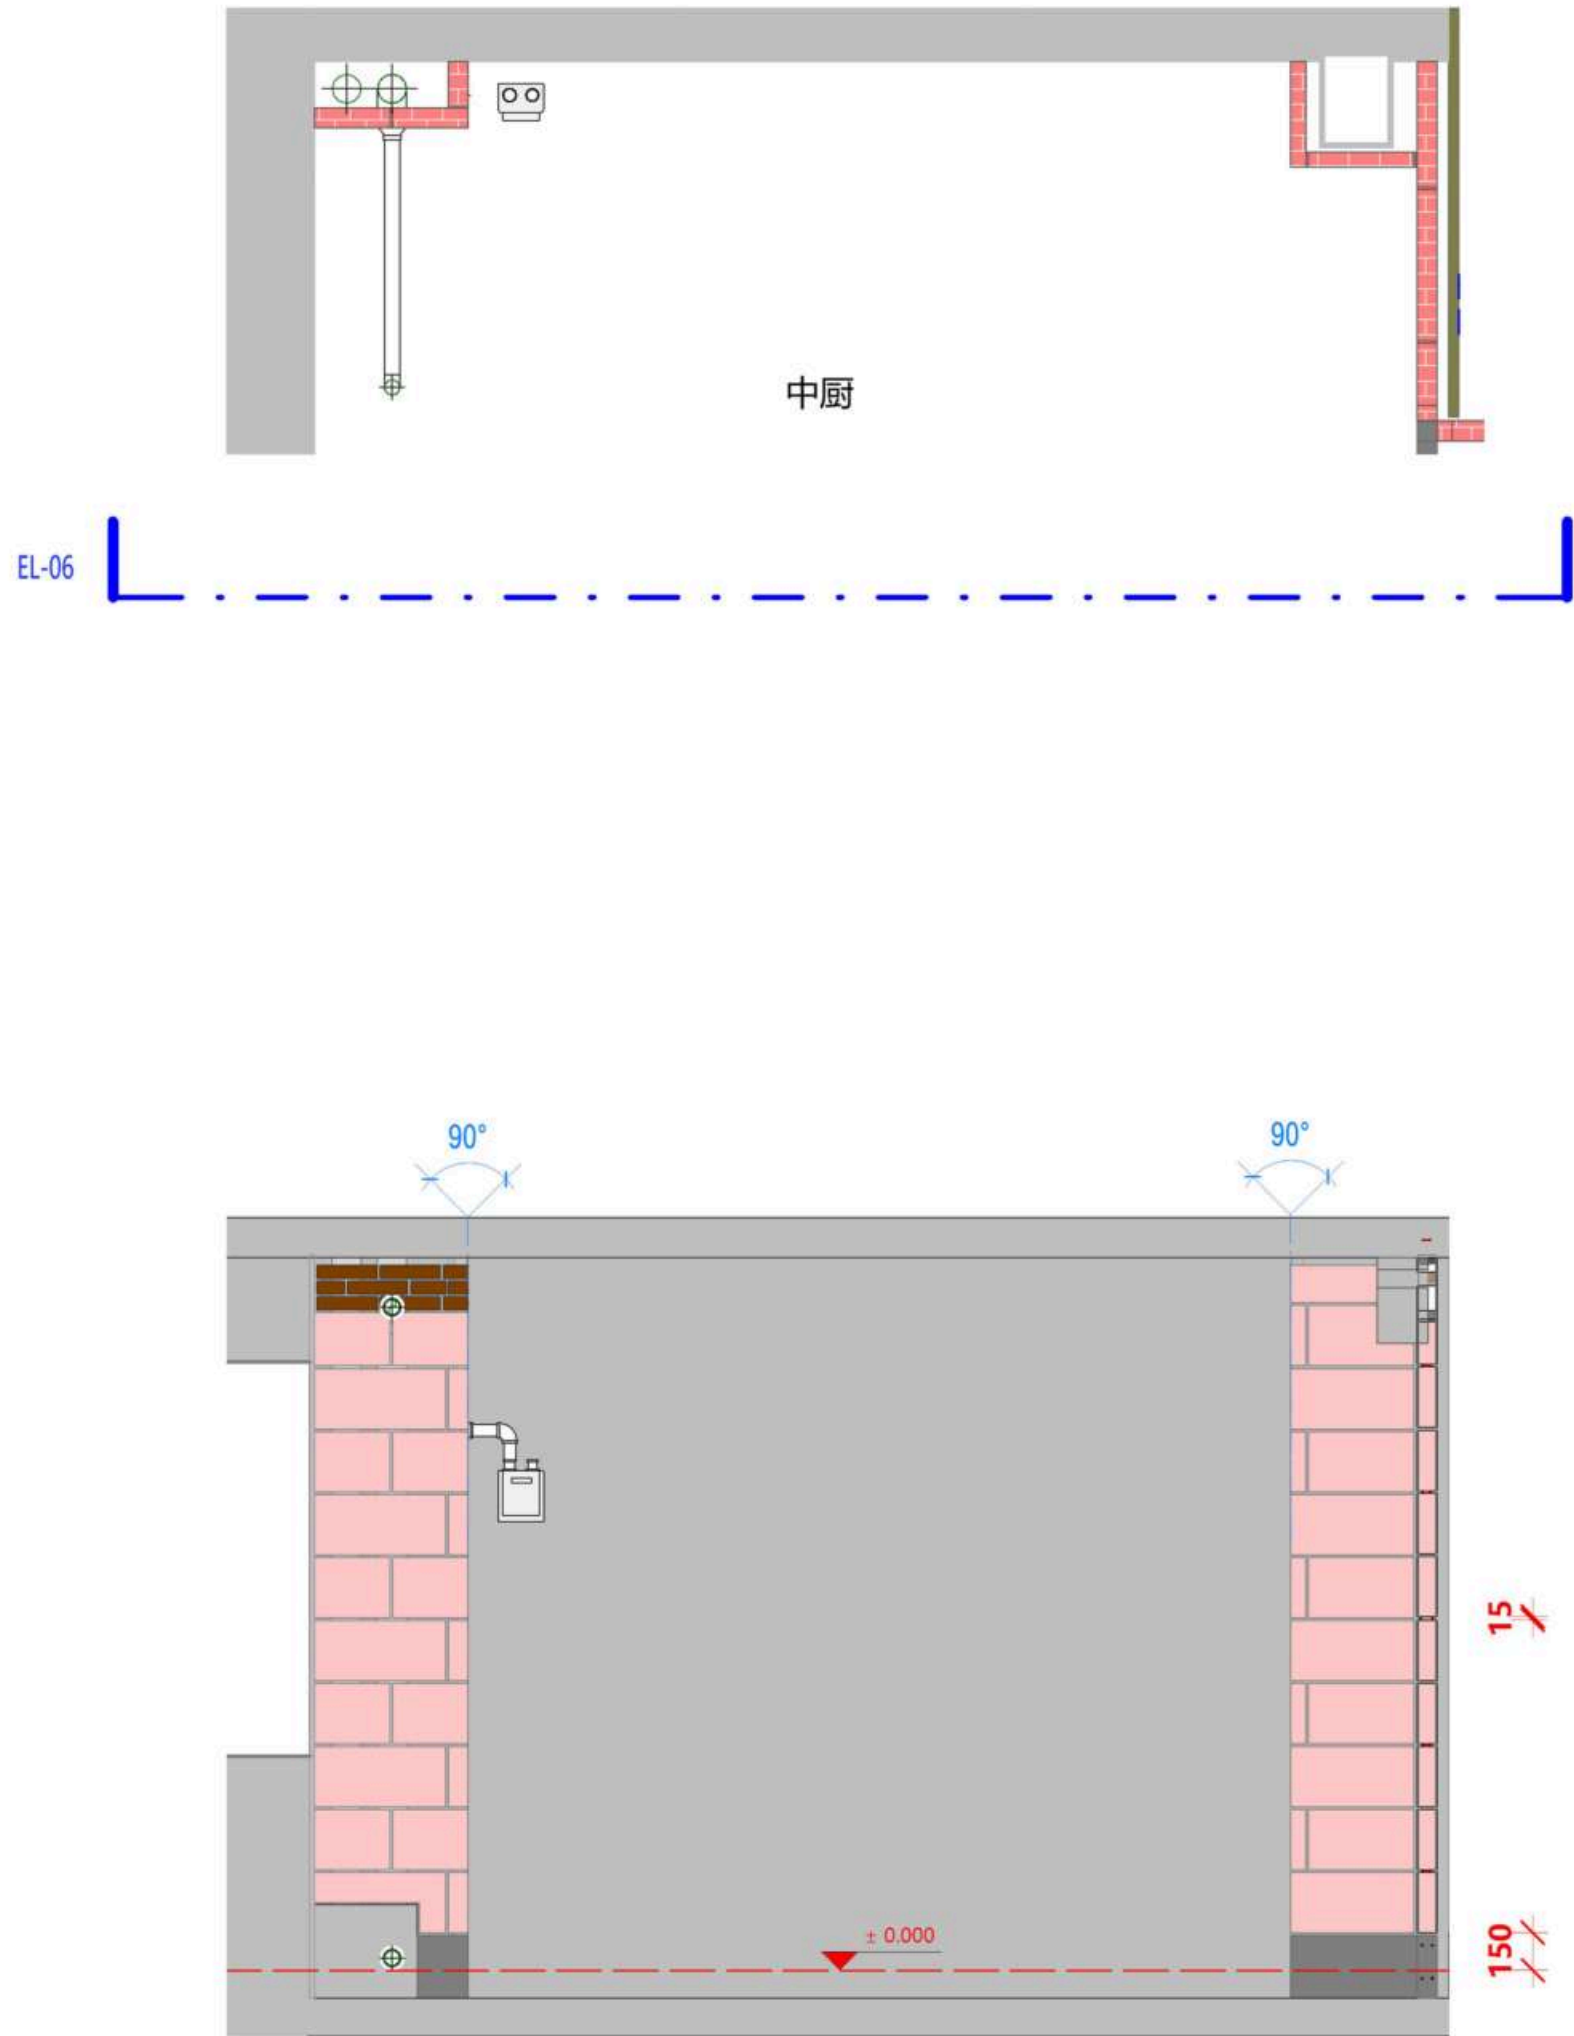

PC砖墙立面图06

Scale比例 1 : 30@A2

1

3D-06



PC砖墙三维示意图06

Scale比例 1:30@A2


注释
Notes
1.本图纸如与现场尺寸有误，请施工人员与项目负责人联系。
2.施工前施工人员应认真查阅此图，如有不明确尺寸，按现场测量为准。
3.本图纸必须经甲乙双方认可并签字方可作为施工依据。

1

EL-06

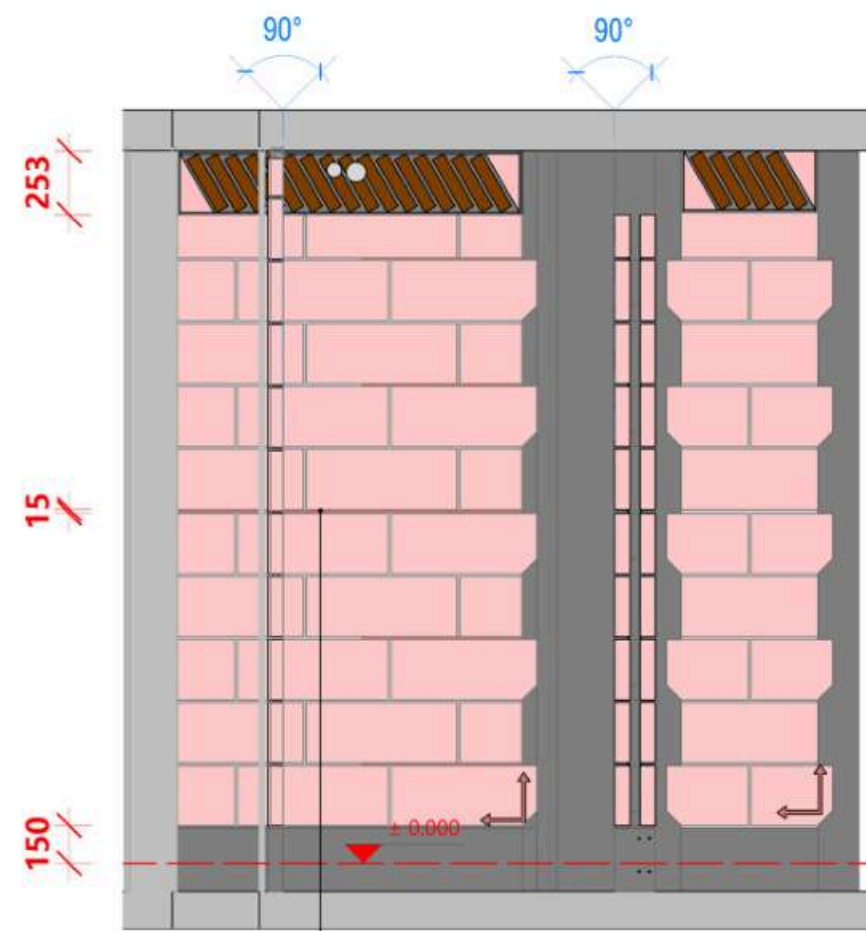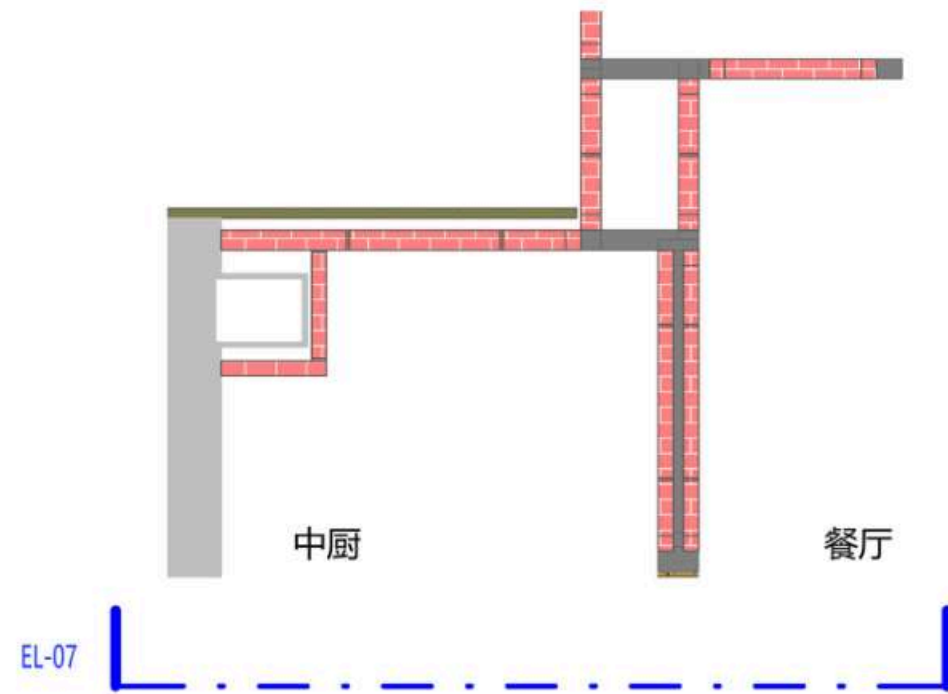

H15mm
(2*Φ6钢筋+水泥砂浆)

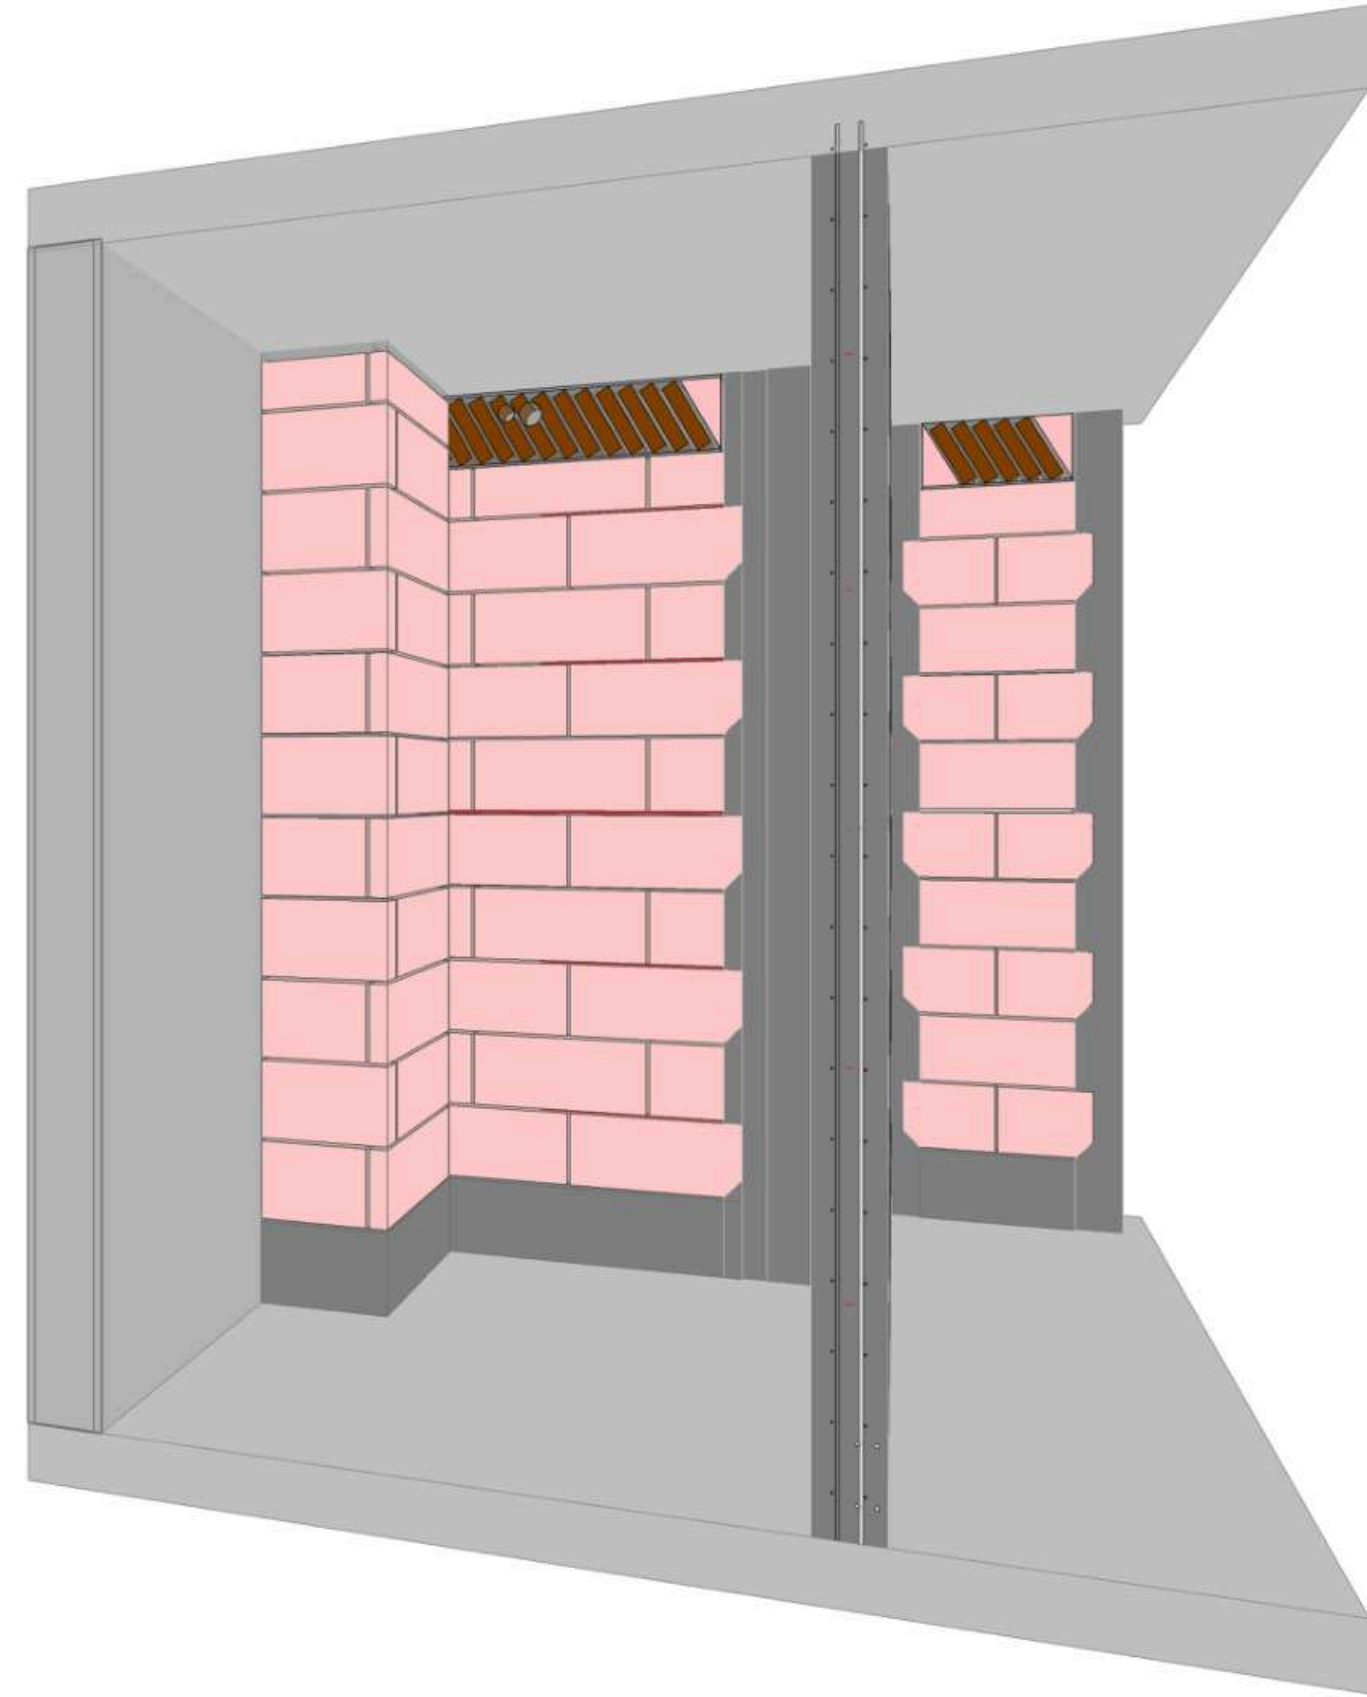

LEGEND图例

图例A 材质分类		
编号	图例	说明
1		原始墙、板、柱
2		混凝土导墙、结构柱、马牙槎
3		PC砖
4		红砖
5		钢架墙
6		止水坎
7		混凝土止水坎上加5mm钢板

图例B 施工时注意事项		
编号	图例	说明
1		地面完成线
2		必要尺寸
3		起铺点
4		错峰要求 $a \geq 200$ $b \geq 150$
5		边砖宽度要求 $a \geq 200$
6		$b < 150$ 时 $a = b$

日期
Date 01/08/26

修订
Revision

项目
Project

潮映华府3-801

Scale
比例 1:30@A2

PC砖墙07

Drawing No.
图纸编号

10-PCW-07

Project No.
项目编号

©2025

正式施工图
2026-01-27

PC砖墙立面图07

Scale比例 1 : 30@A2

1



3D-07

PC砖墙三维示意图07


Scale比例 1:30@A2

注释
Notes

- 1.本图纸如与现场尺寸有误，请施工人员与项目负责人联系。
- 2.施工前施工人员应认真查阅此图，如有不明确尺寸，按现场测量为准。
- 3.本图纸必须经甲乙双方认可并签字方可作为施工依据。

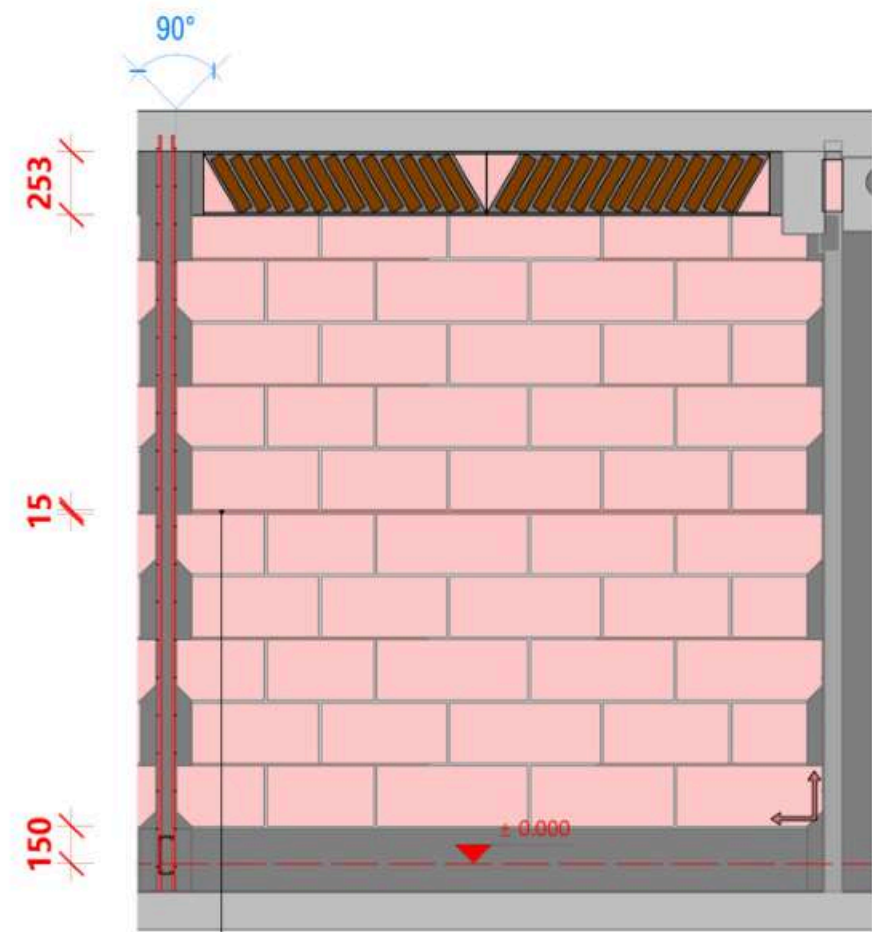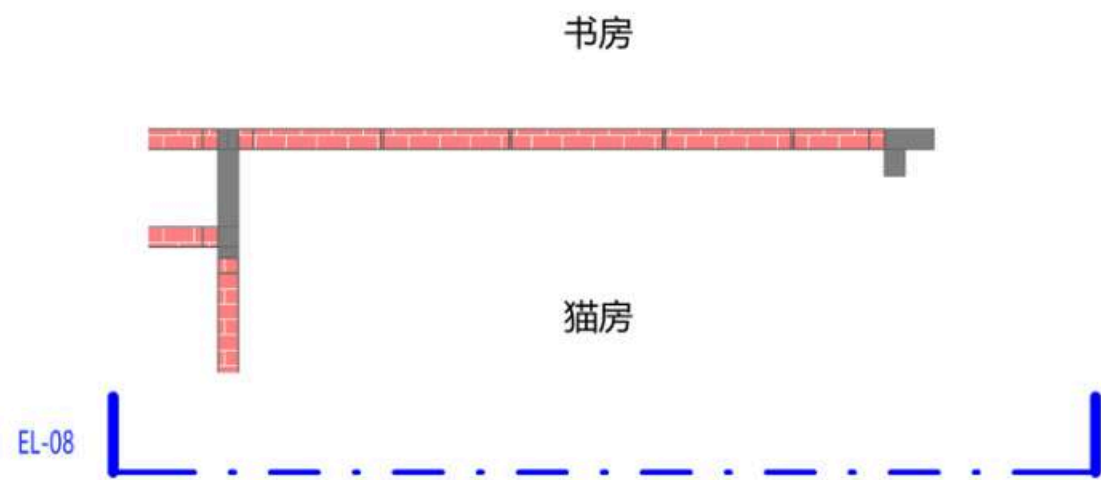

H15mm
(2*Φ6钢筋+水泥砂浆)

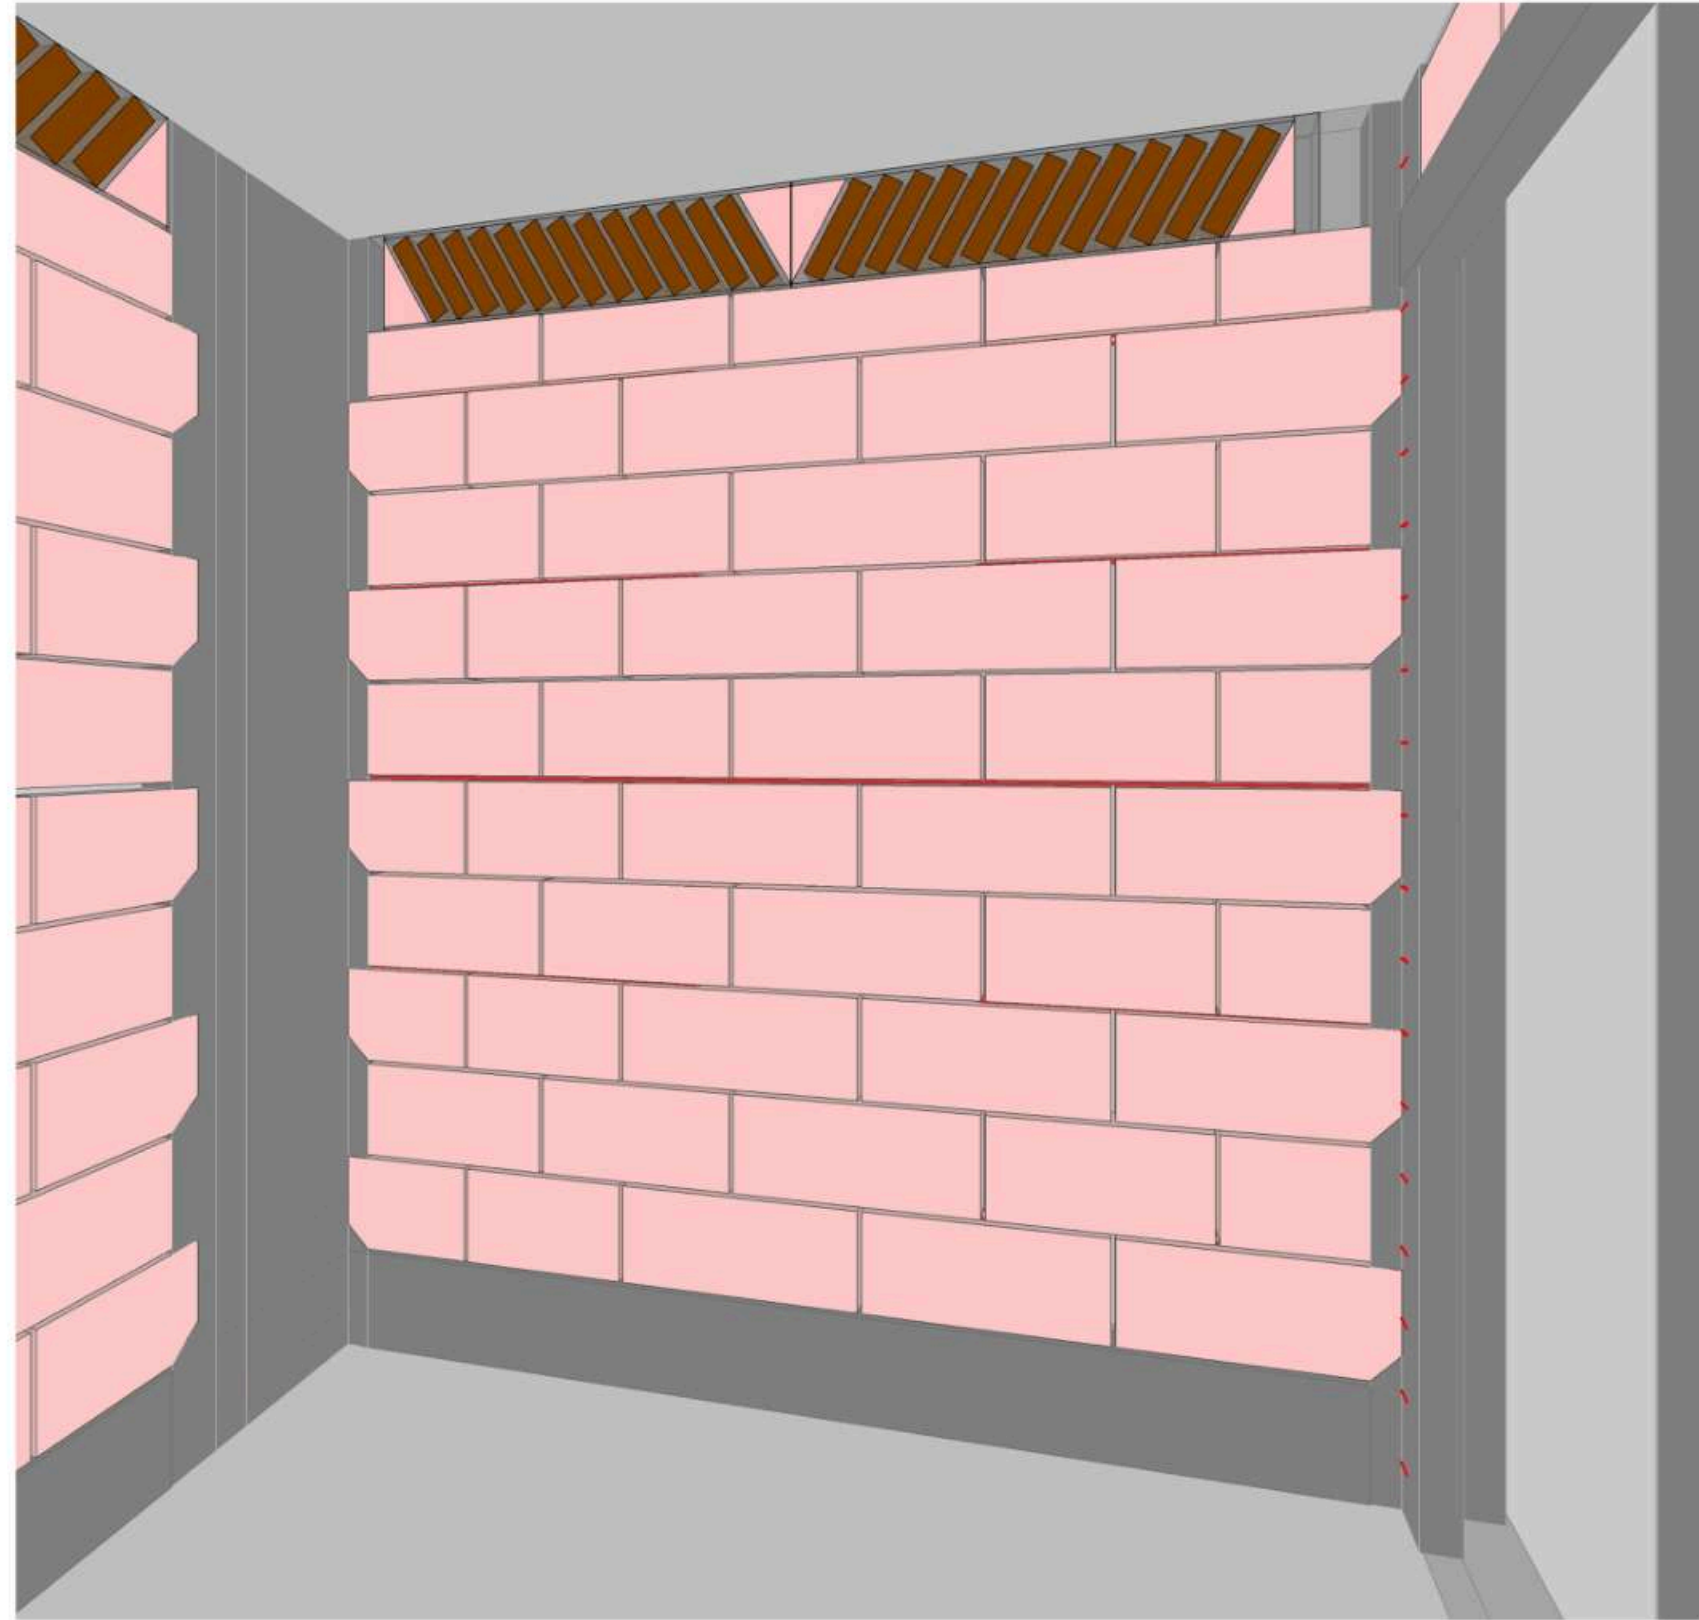

LEGEND图例

图例A 材质分类		
编号	图例	说明
1		原始墙、板、柱
2		混凝土导墙、结构柱、马牙槎
3		PC砖
4		红砖
5		钢架墙
6		止水坎
7		混凝土止水坎上加5mm钢板

图例B 施工时注意事项		
编号	图例	说明
1		地面完成线
2		必要尺寸
3		起铺点
4		错峰要求 $a \geq 200$ $b \geq 150$
5		边砖宽度要求 $a \geq 200$
6		$b < 150$ 时 $a = b$

日期
Date 01/08/26

修订
Revision

项目
Project

潮映华府3-801

Scale
比例 1:30@A2

PC砖墙08

Drawing No.
图纸编号

11-PCW-08

Project No.
项目编号

©2025

1

EL-08

PC砖墙立面图08

Scale比例 1 : 30@A2

1

3D-08

PC砖墙三维示意图08

Scale比例 1:30@A2



注释

Notes

1.本图纸如与现场尺寸有误, 请施工人员与项目负责人联系。
2.施工前施工人员应认真查阅此图, 如有不明确尺寸, 按现场测量为准。
3.本图纸必须经甲乙双方认可并签字方可作为施工依据。

正式施工图

2026-01-27

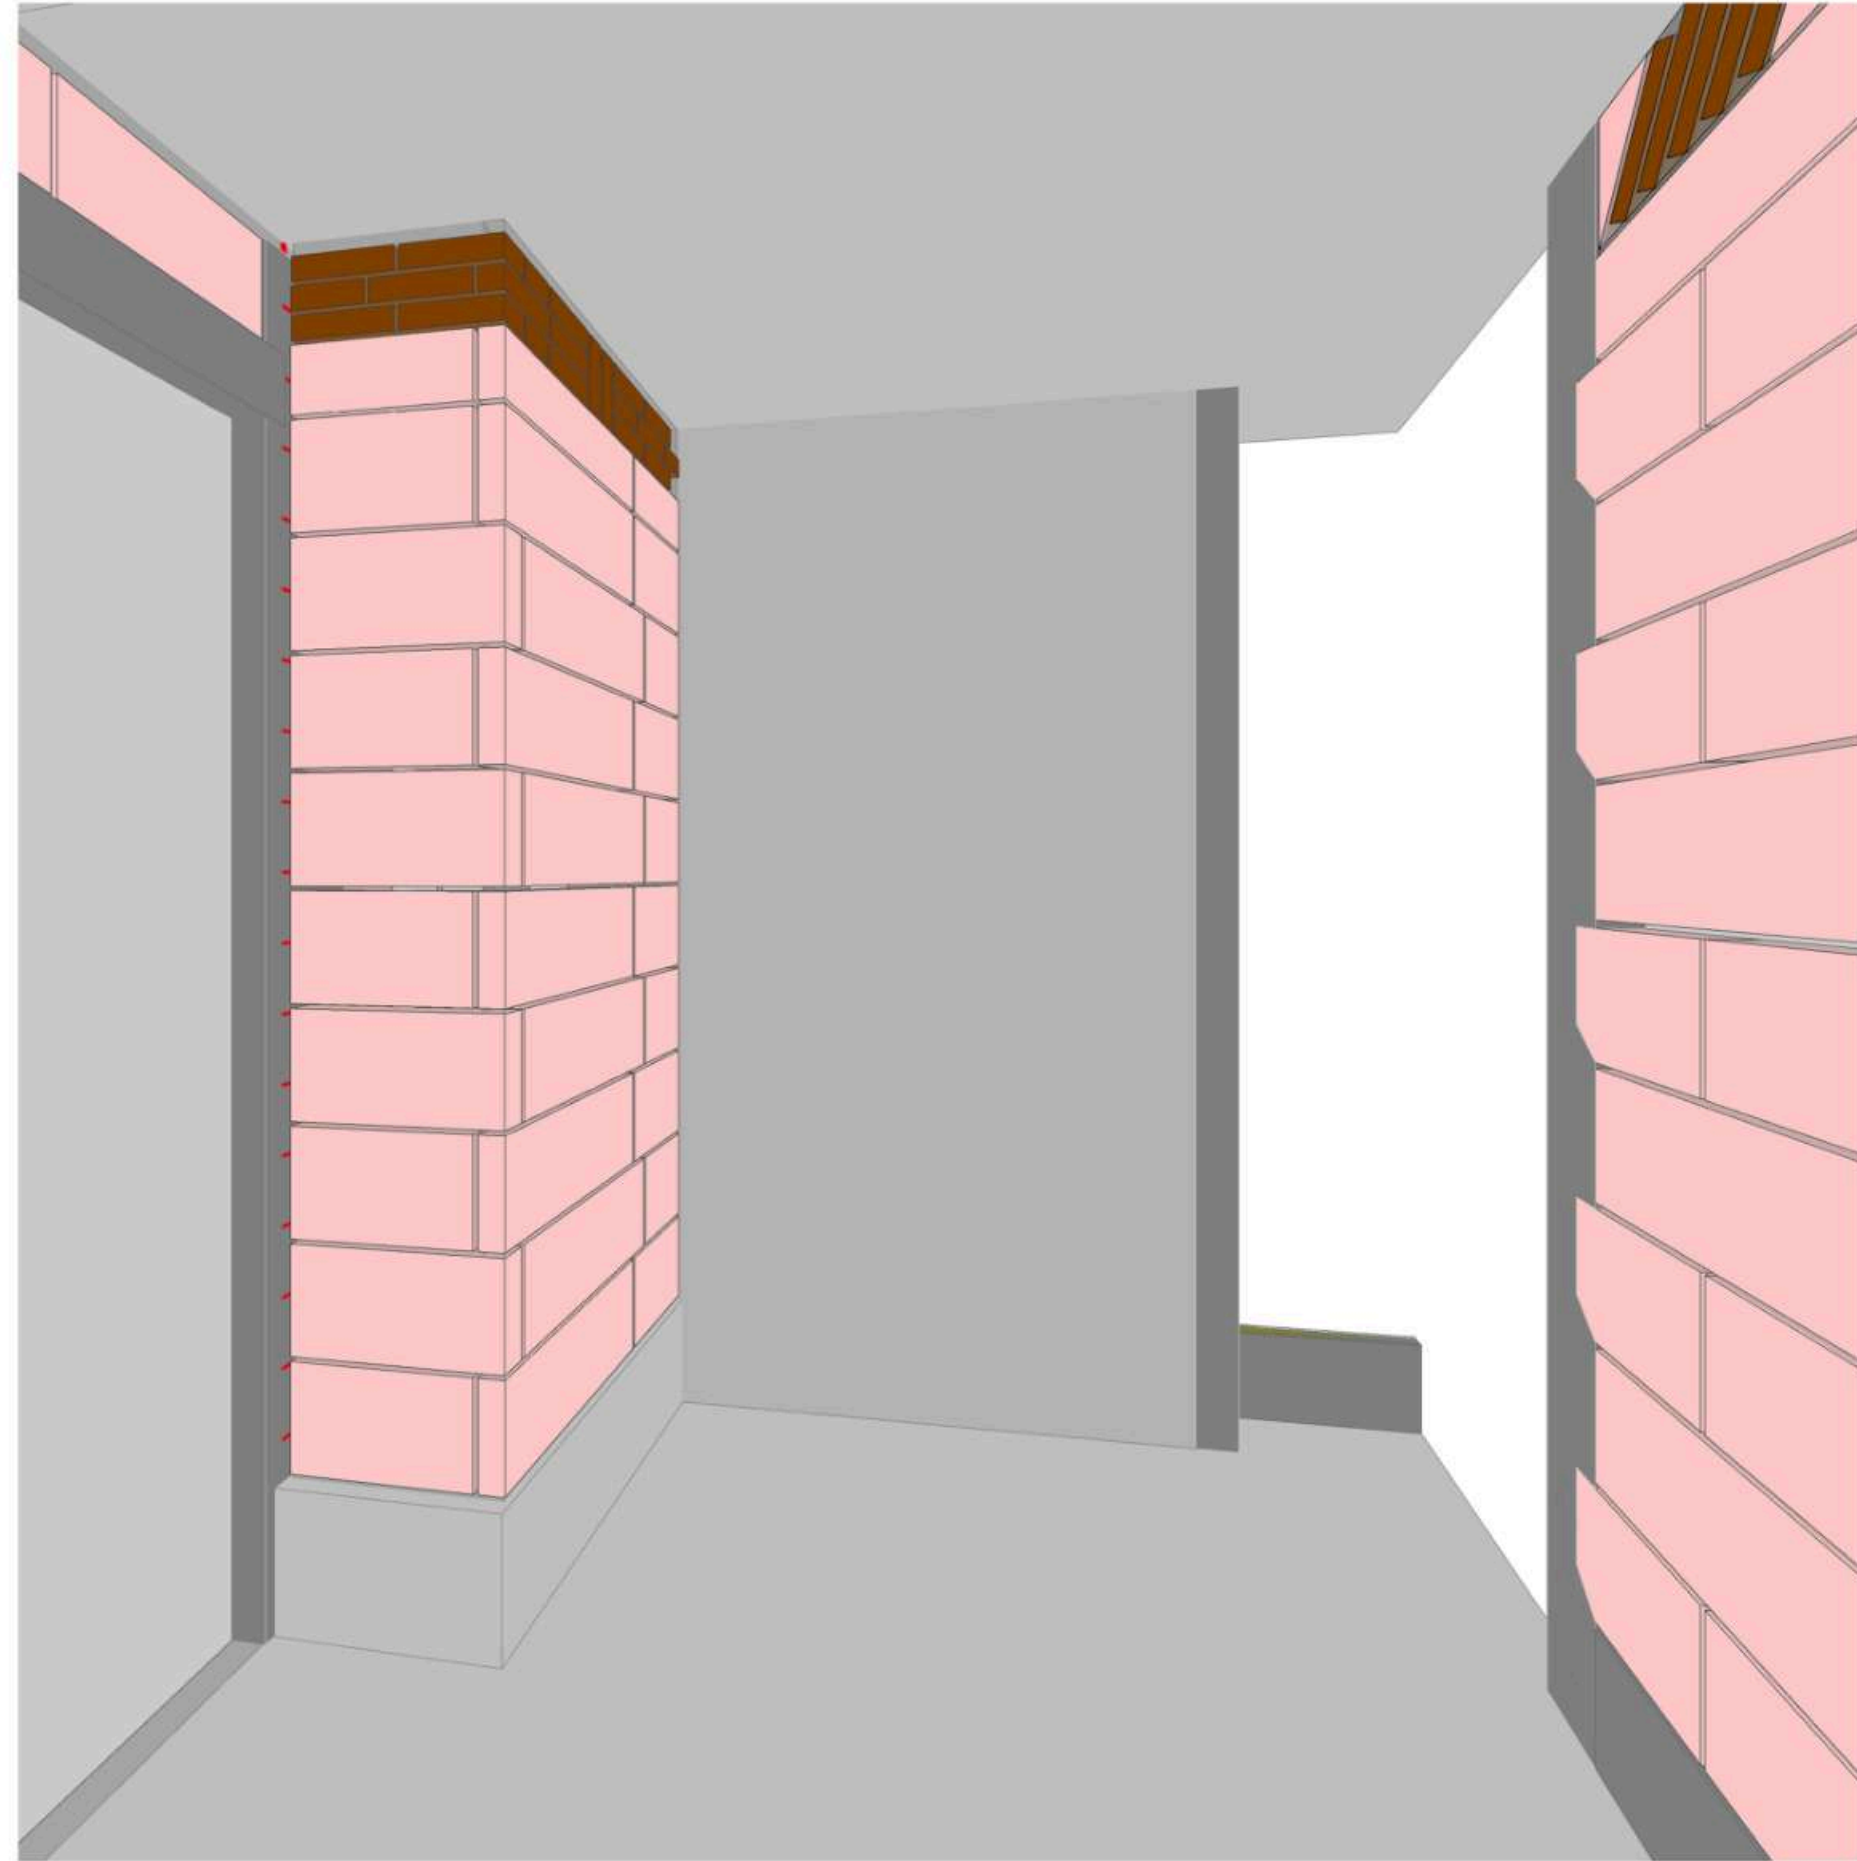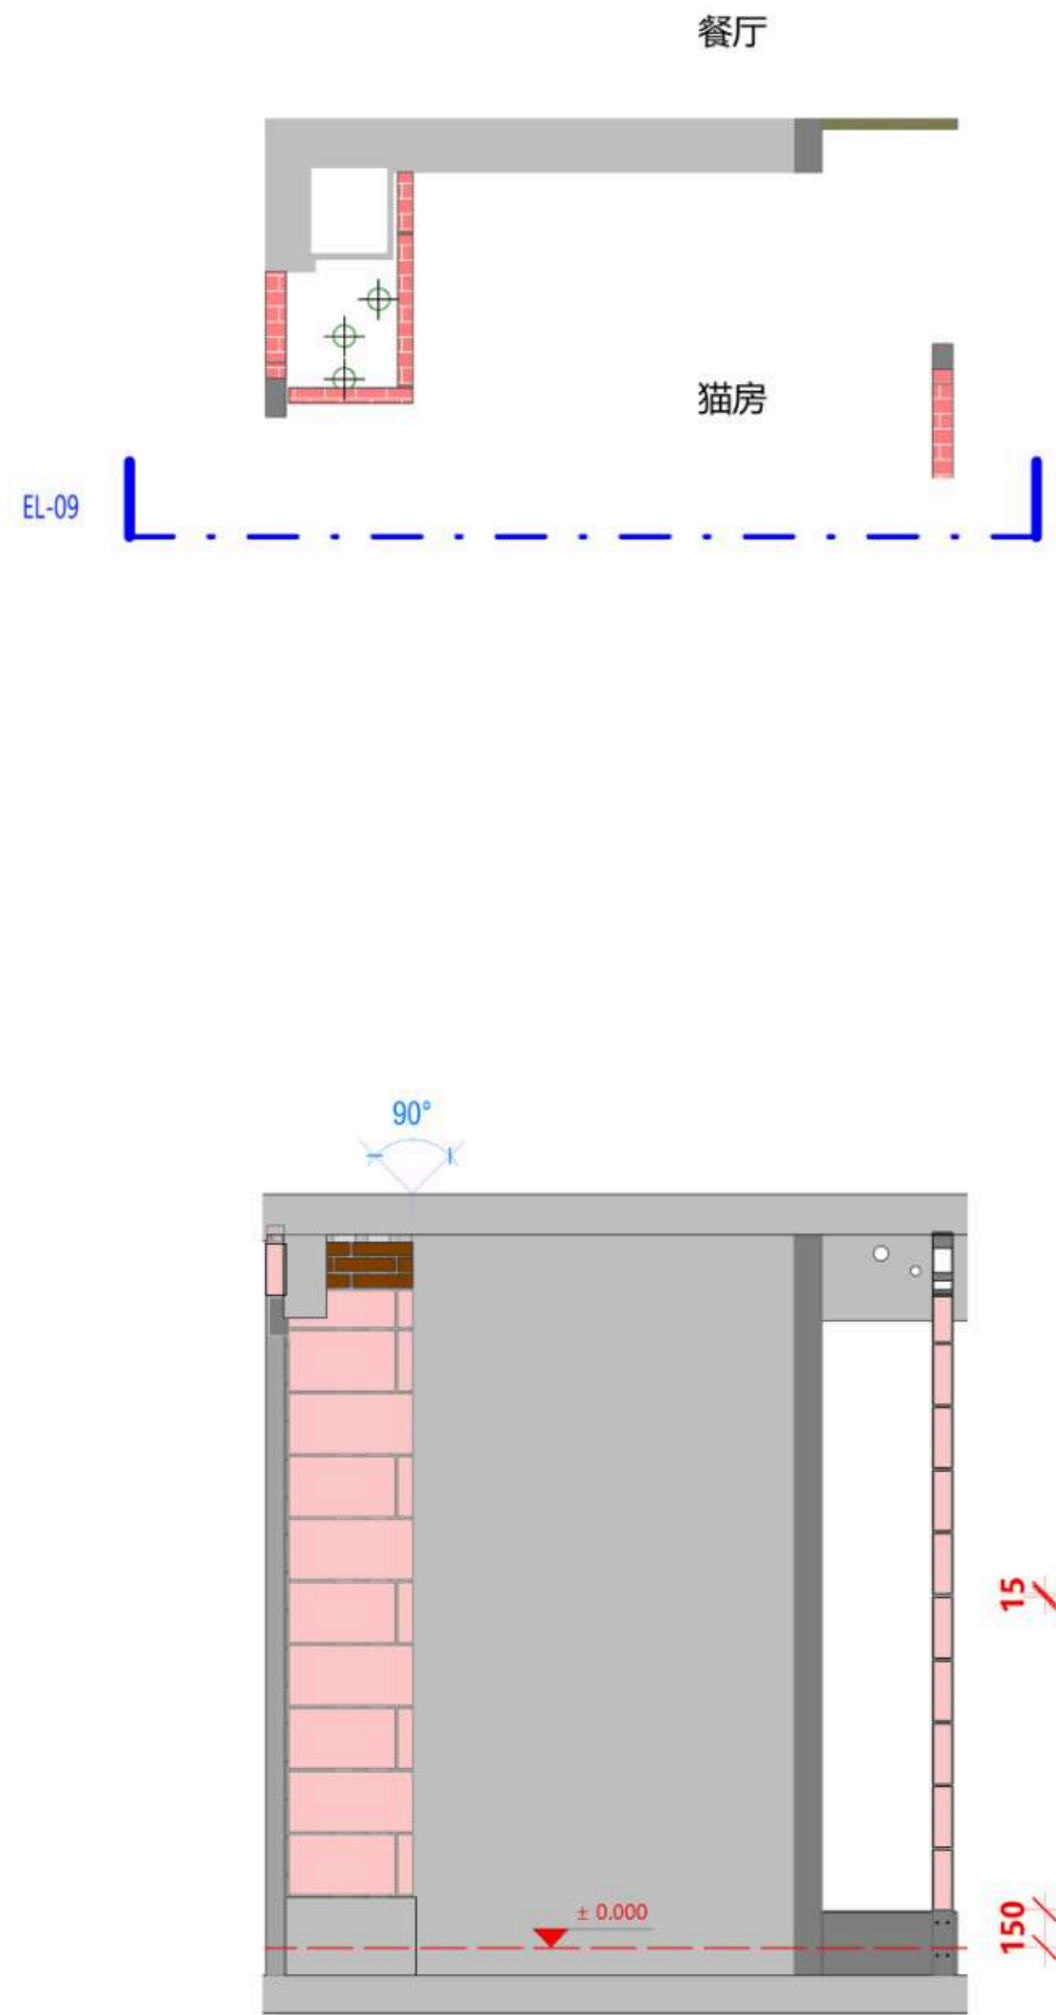

LEGEND图例

图例A 材质分类		
编号	图例	说明
1		原始墙、板、柱
2		混凝土导墙、结构柱、马牙槎
3		PC砖
4		红砖
5		钢架墙
6		止水坎
7		混凝土止水坎上加5mm钢板

图例B 施工时注意事项		
编号	图例	说明
1		地面完成线
2		必要尺寸
3		起铺点
4		错峰要求 $a \geq 200$ $b \geq 150$
5		边砖宽度要求 $a \geq 200$
6		$b < 150$ 时 $a = b$

日期
Date 01/08/26

修订
Revision

项目
Project
潮映华府3-801

Scale
比例 1:30@A2
PC砖墙09

Drawing No.
图纸编号
12-PCW-09



Project No.
项目编号
©2025

正式施工图
2026-01-27

1	PC砖墙立面图09
EL-09	Scale比例 1 : 30@A2

1	PC砖墙三维示意图09
3D-09	Scale比例 1:30@A2

注释 Notes
1.本图纸如与现场尺寸有误, 请施工人员与项目负责人联系。
2.施工前施工人员应认真查阅此图, 如有不明确尺寸, 按现场测量为准。
3.本图纸必须经甲乙双方认可并签字方可作为施工依据。

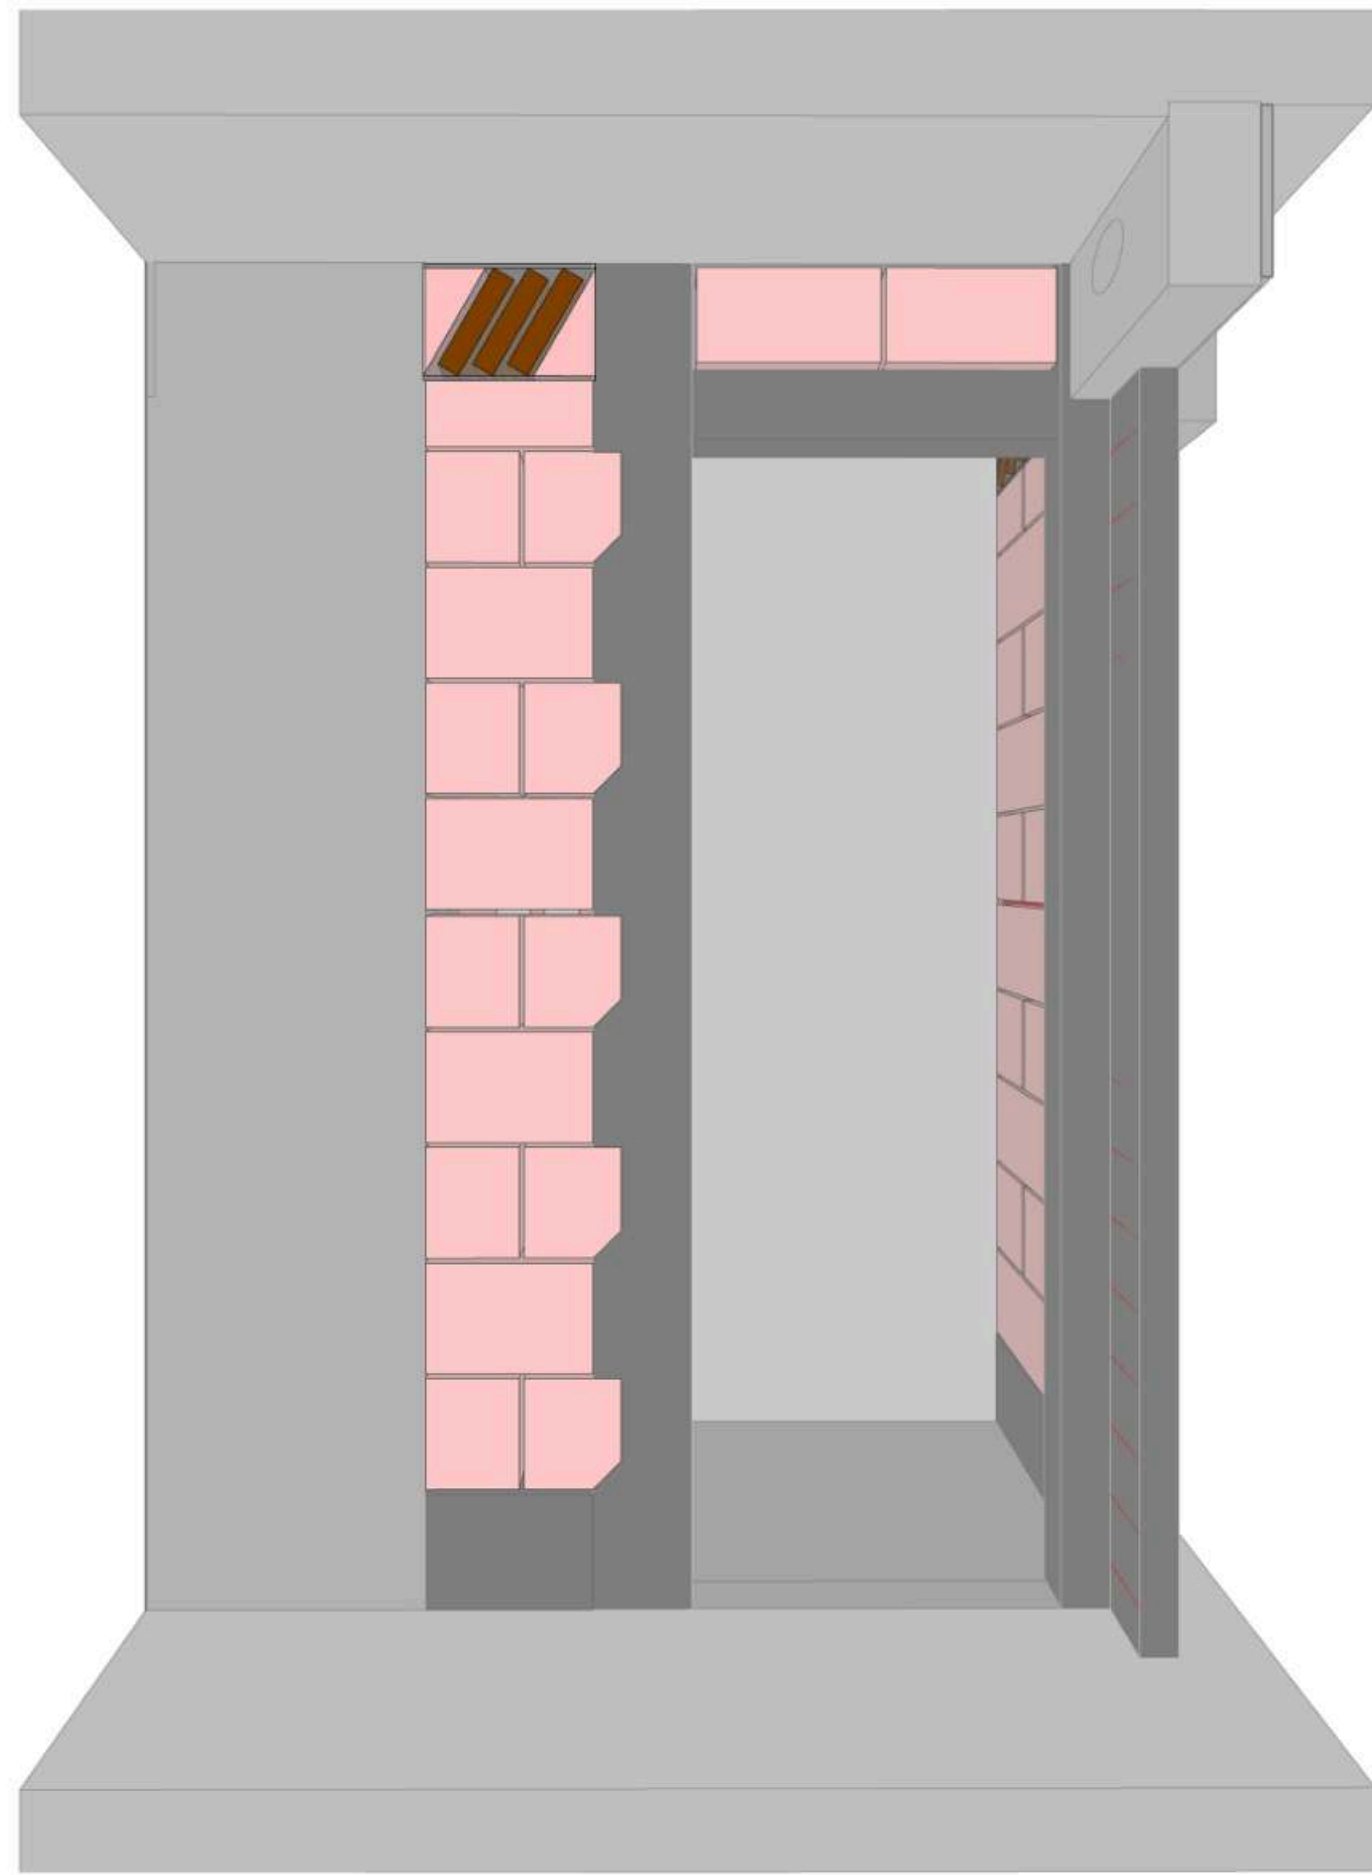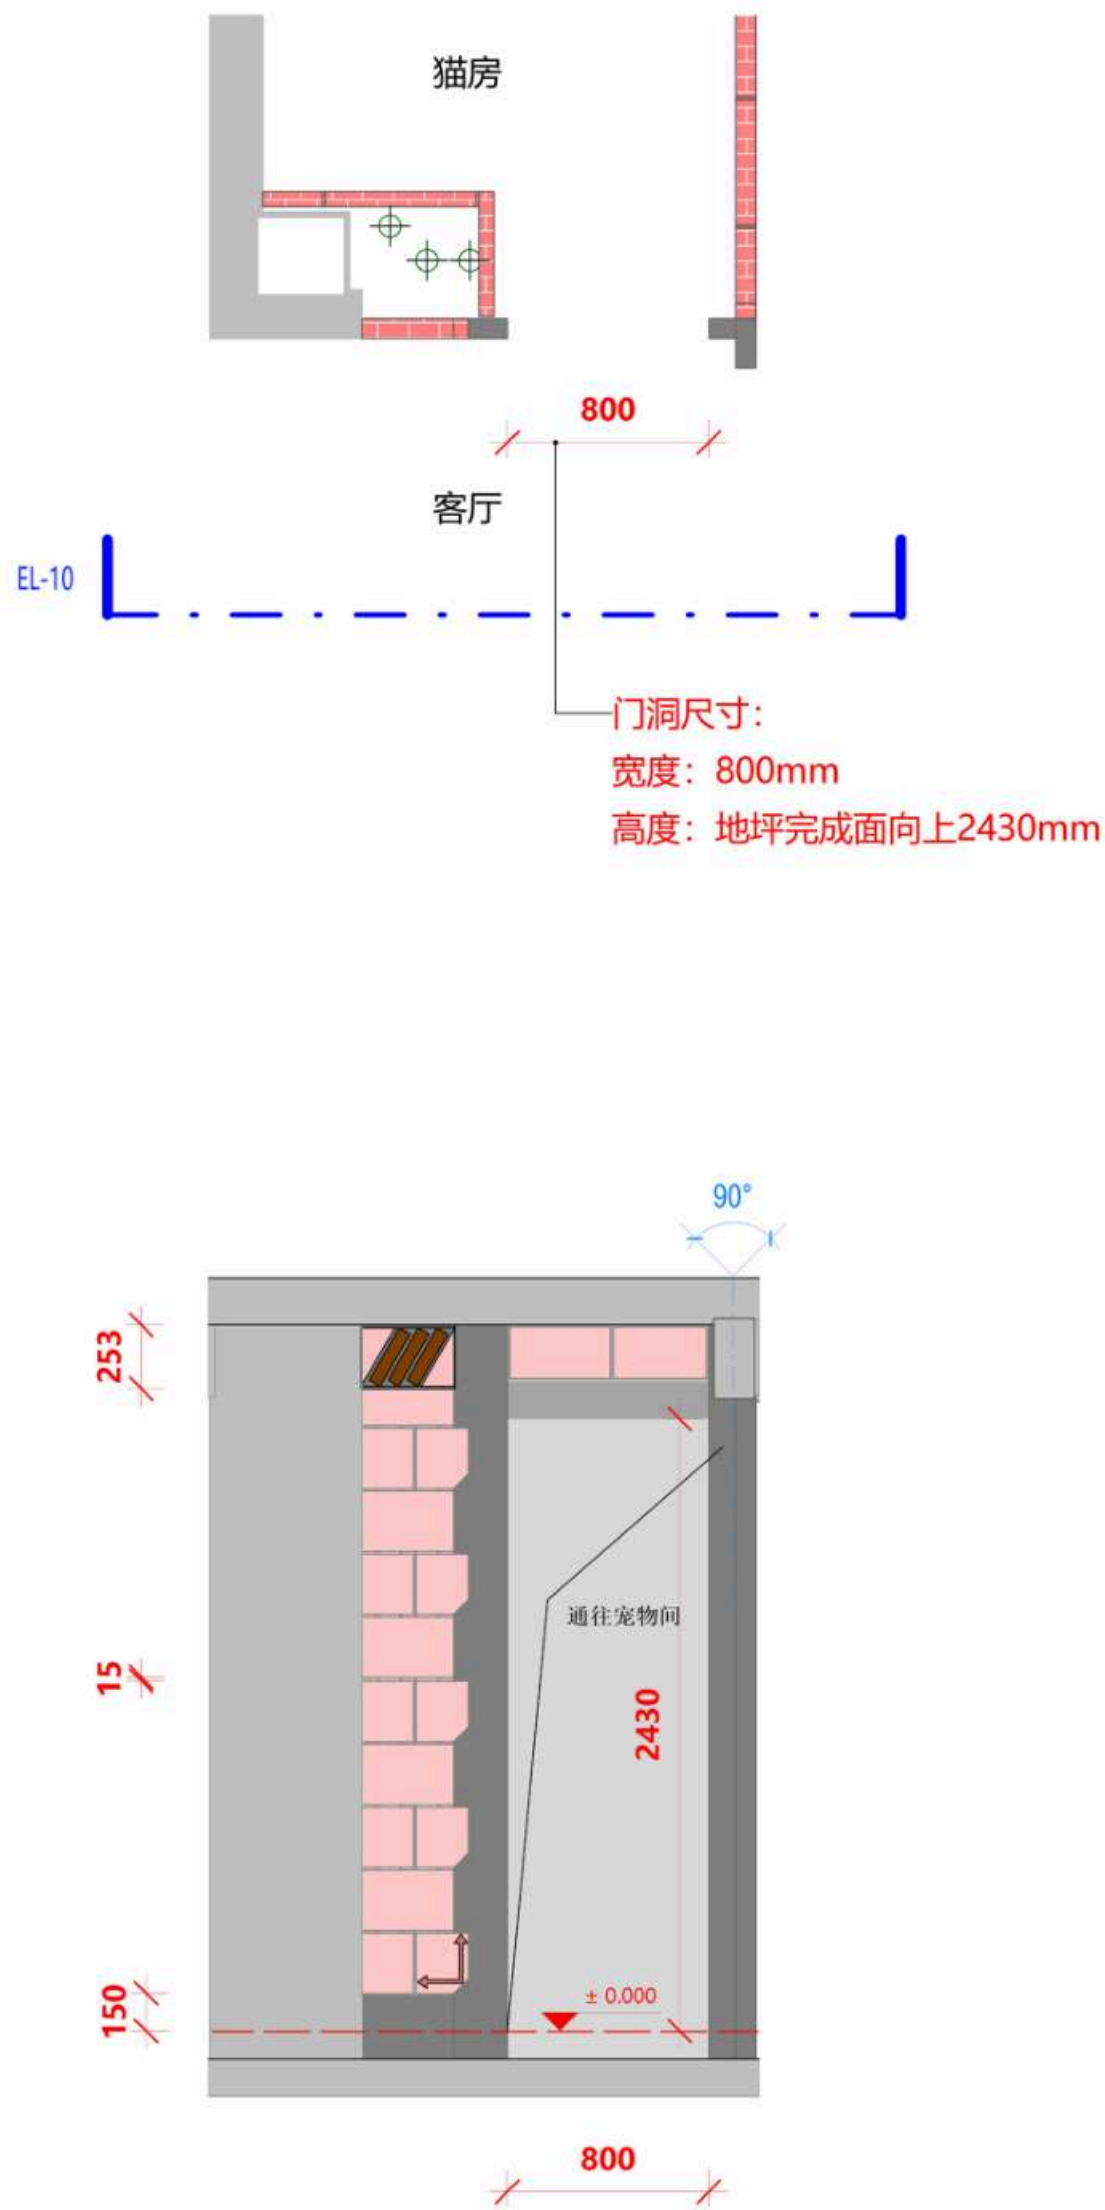

正式施工图
2026-01-27

ELBORN

LEGEND图例

图例A 材质分类		
编号	图例	说明
1		原始墙、板、柱
2		混凝土导墙、结构柱、马牙槎
3		PC砖
4		红砖
5		钢架墙
6		止水坎
7		混凝土止水坎上加5mm钢板
图例B 施工时注意事项		
编号	图例	说明
1		地面完成线
2		必要尺寸
3		起铺点
4		错峰要求 $a \geq 200$ $b \geq 150$
5		边砖宽度要求 $a \geq 200$
6		$b < 150$ 时 $a = b$

日期
Date 01/08/26

修订
Revision

项目
Project
潮映华府3-801

Scale
比例 1:30@A2
PC砖墙10

Drawing No.
图纸编号
13-PCW-10


Project No.
项目编号
©2025

1
EL-10
PC砖墙立面图10
Scale比例 1 : 30@A2



1
3D-10

PC砖墙三维示意图10
Scale比例 1:30@A2

注释
Notes
1.本图纸如与现场尺寸有误, 请施工人员与项目负责人联系。
2.施工前施工人员应认真查阅此图, 如有不明确尺寸, 按现场测量为准。
3.本图纸必须经甲乙双方认可并签字方可作为施工依据。

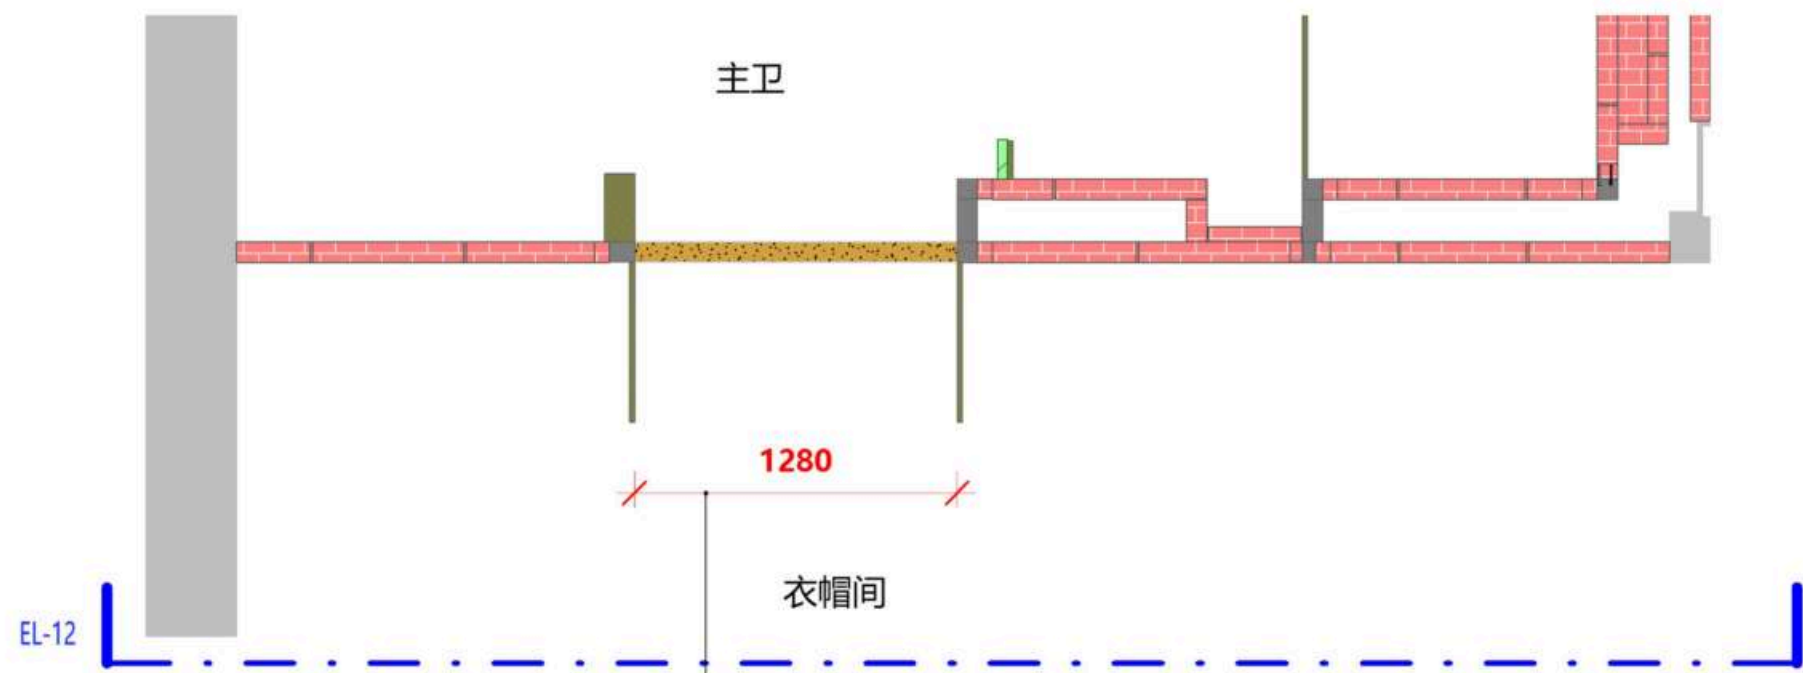

门洞尺寸:
宽度: 1280mm
高度: 地坪完成面向上2485mm
做不了过梁

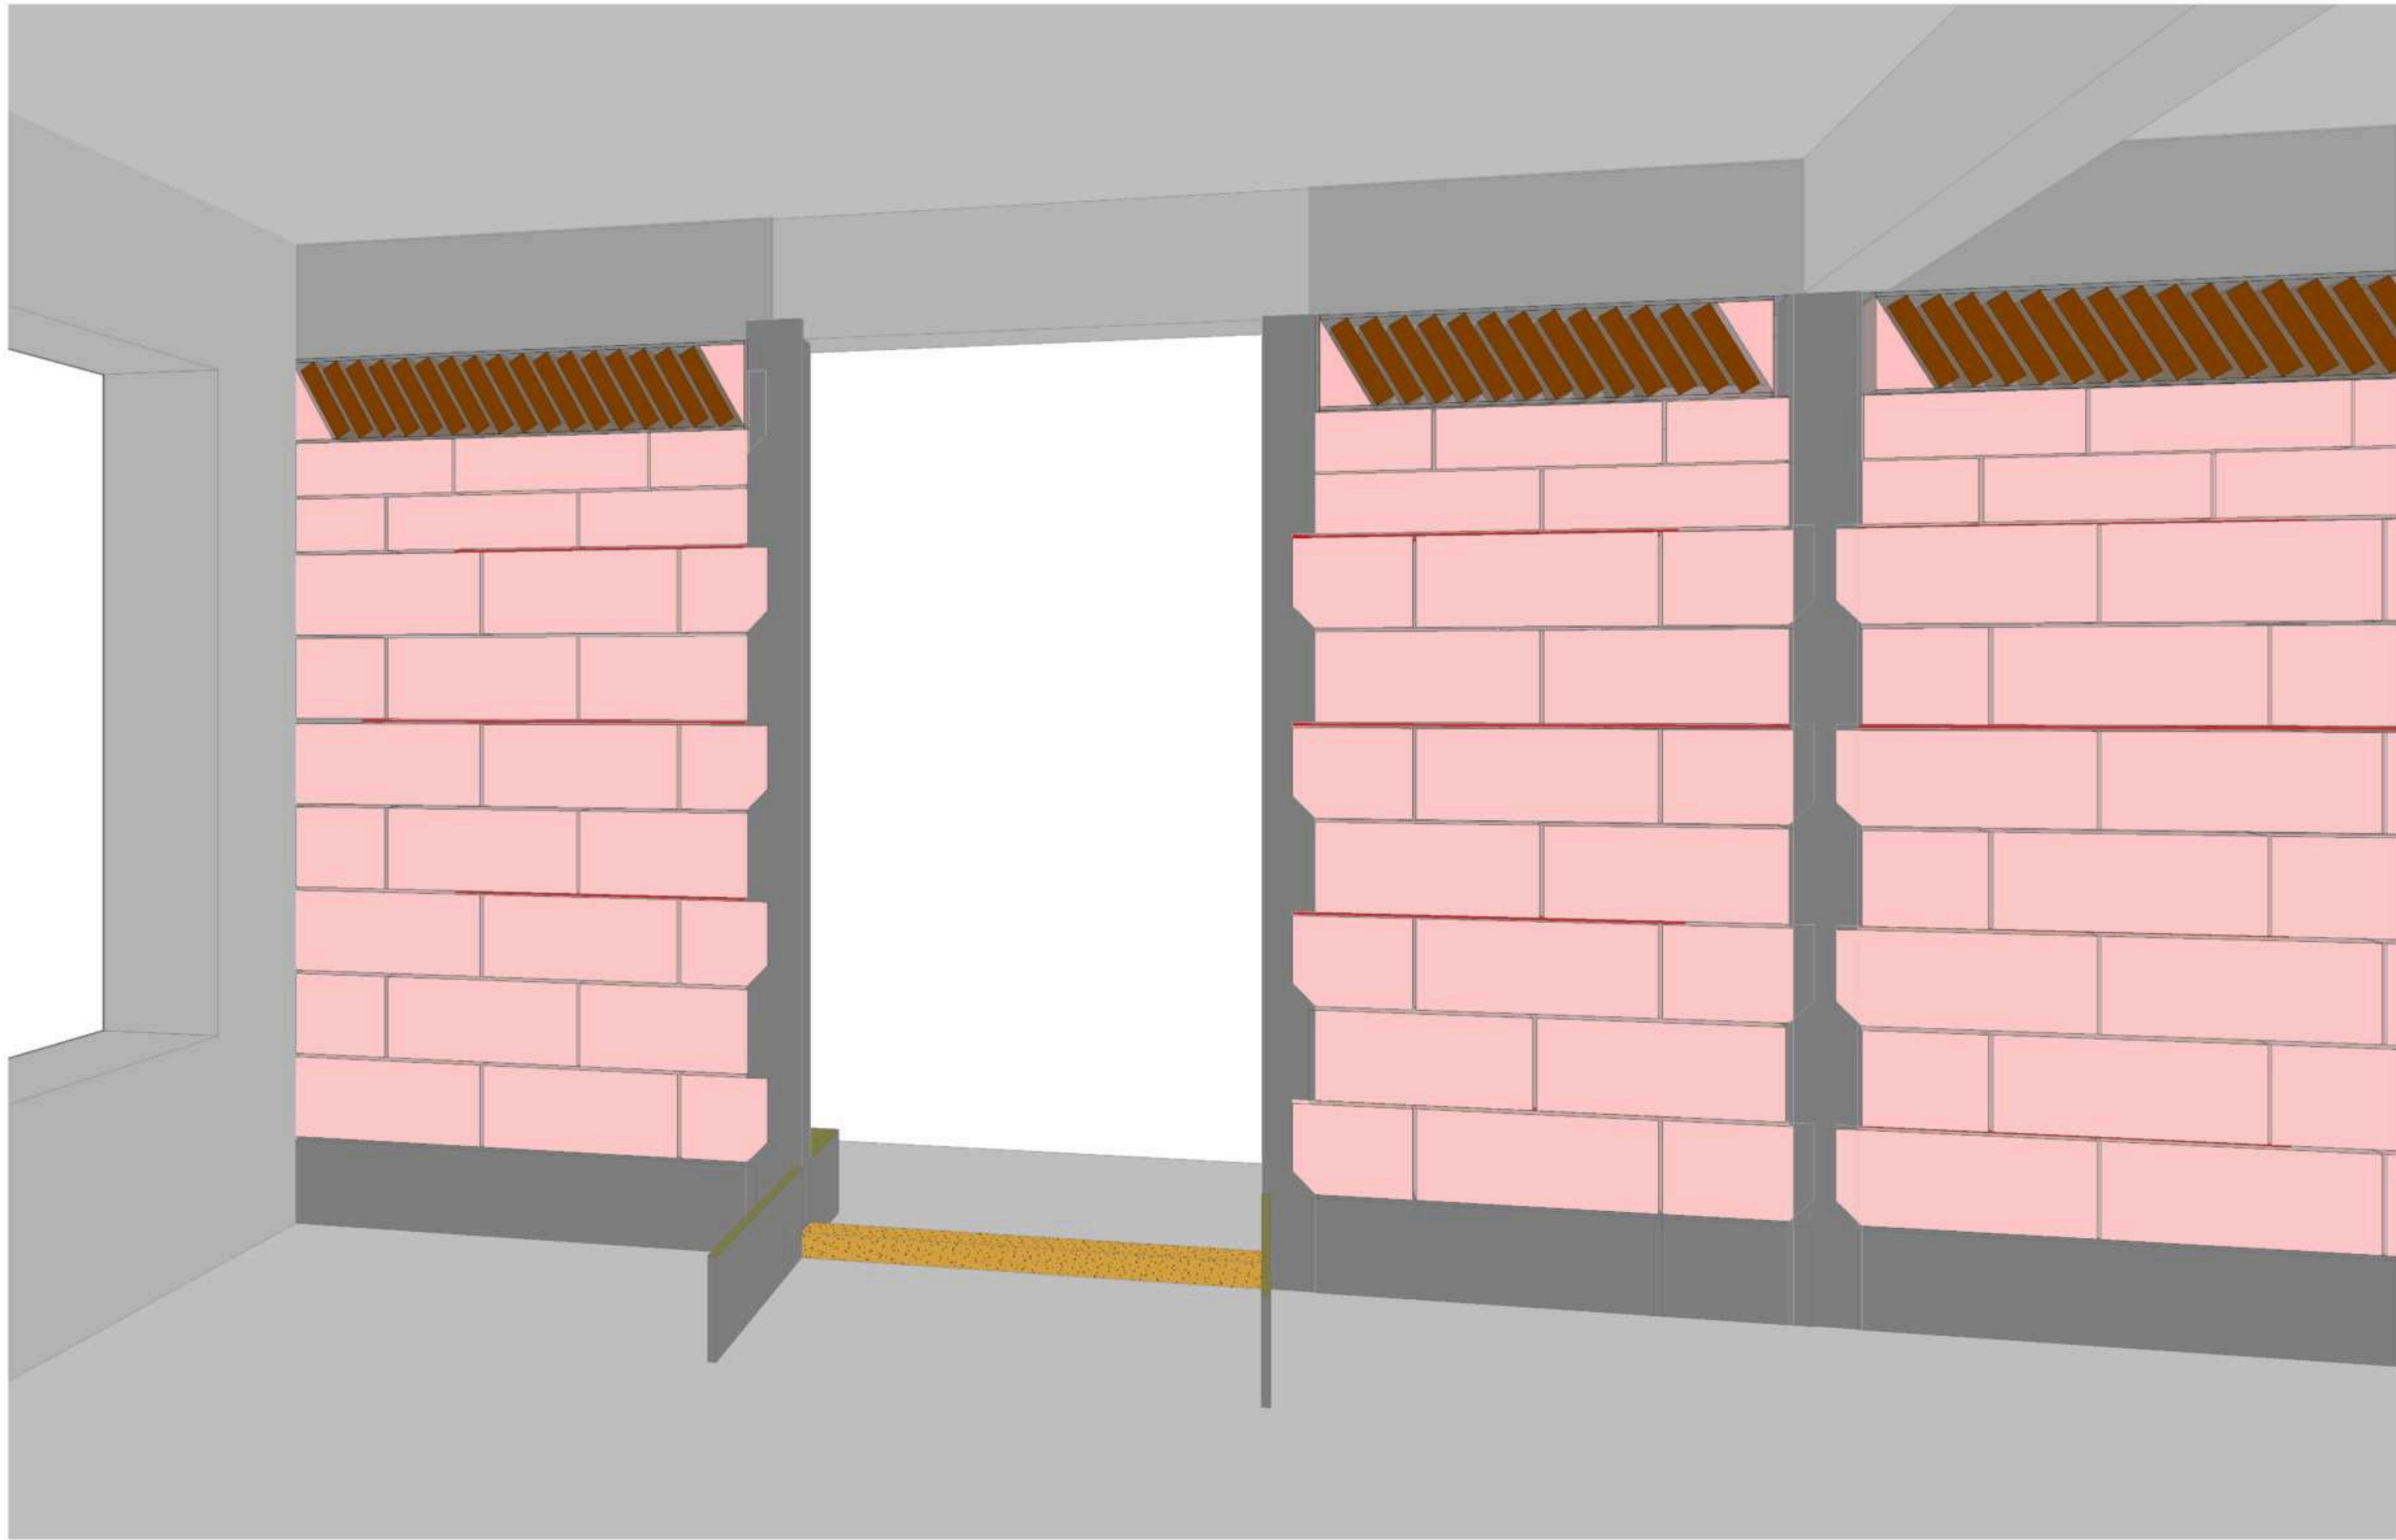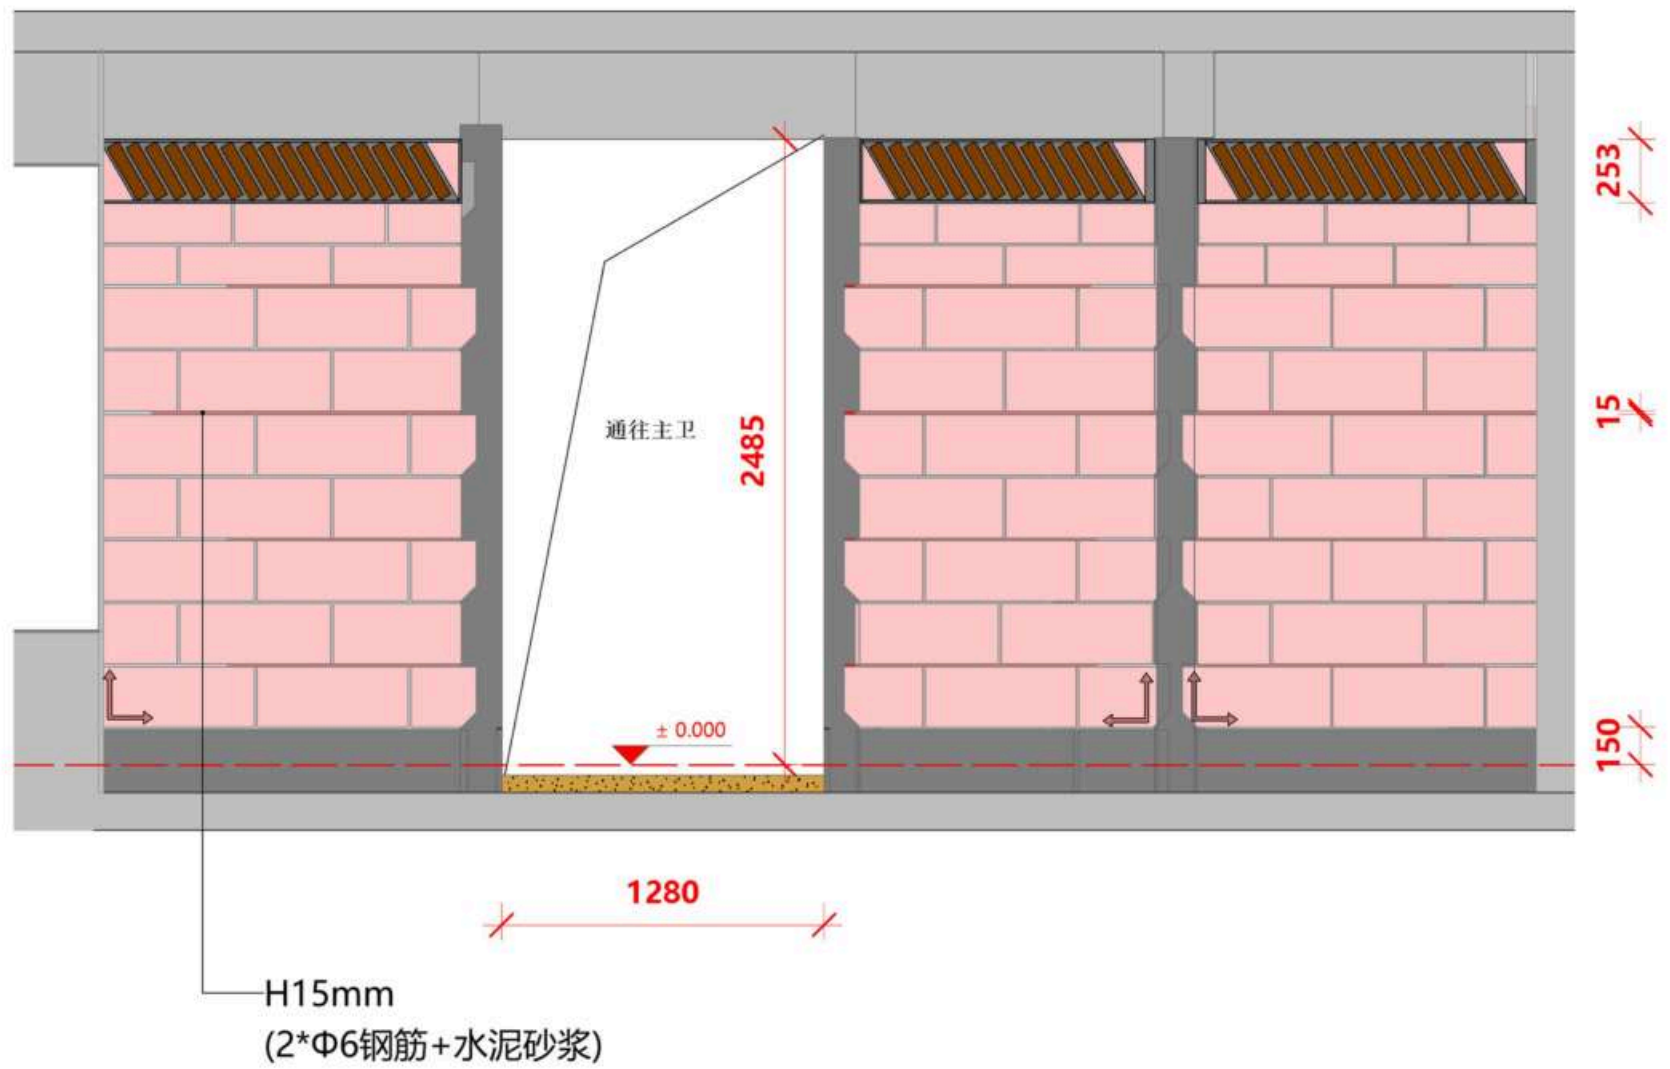

LEGEND图例

图例A 材质分类		
编号	图例	说明
1		原始墙、板、柱
2		混凝土导墙、结构柱、马牙槎
3		PC砖
4		红砖
5		钢架墙
6		止水坎
7		混凝土止水坎上加5mm钢板

图例B 施工时注意事项		
编号	图例	说明
1		地面完成线
2		必要尺寸
3		起铺点
4		错缝要求 a ≥ 200 b ≥ 150
5		边砖宽度要求 a ≥ 200
6		b < 150时 a = b

日期
Date 01/08/26

修订
Revision

项目
Project 潮映华府3-801

Scale
比例 1:30@A2

PC砖墙12

Drawing No.
图纸编号 14-PCW-12

Project No.
项目编号 ©2025

正式施工图
2026-01-27




PC砖墙三维示意图12
Scale比例 1:30@A2

注释
Notes
1.本图纸如与现场尺寸有误,请施工人员与项目负责人联系。
2.施工前施工人员应认真查阅此图,如有不明确尺寸,按现场测量为准。
3.本图纸必须经甲乙双方认可并签字方可作为施工依据。

PC砖墙立面图12
Scale比例 1 : 30@A2

1
3D-12

1
EL-12

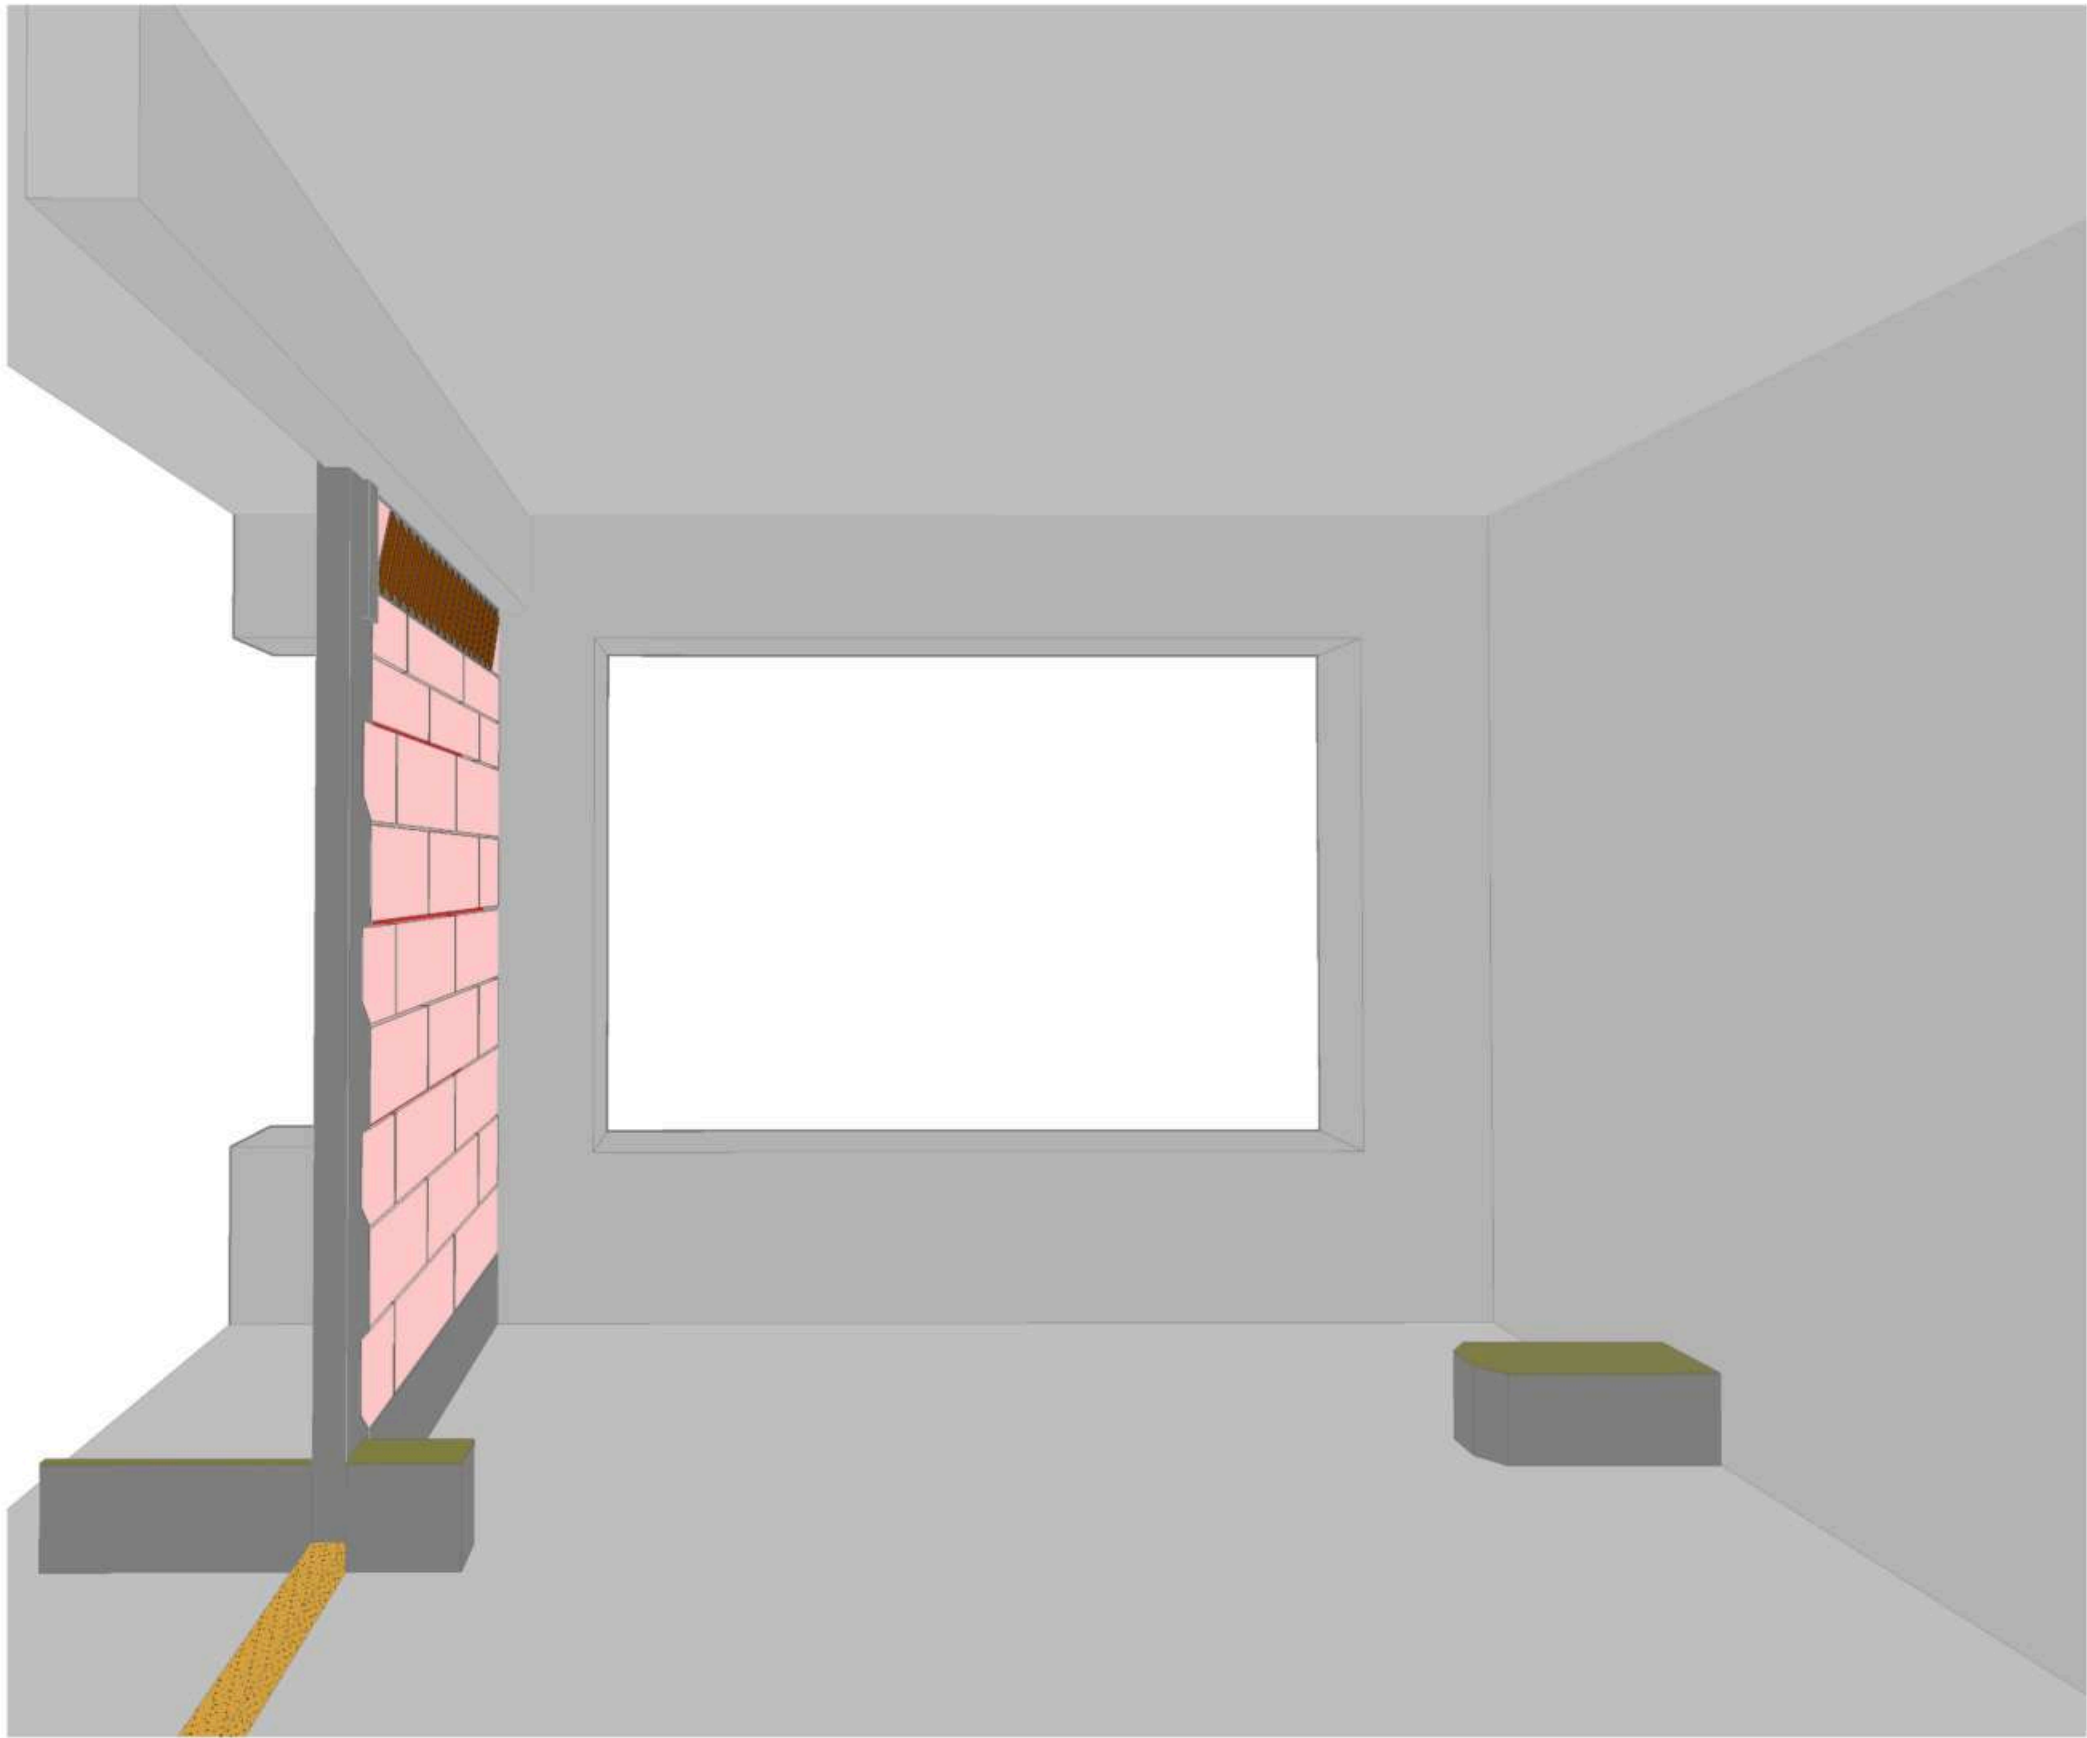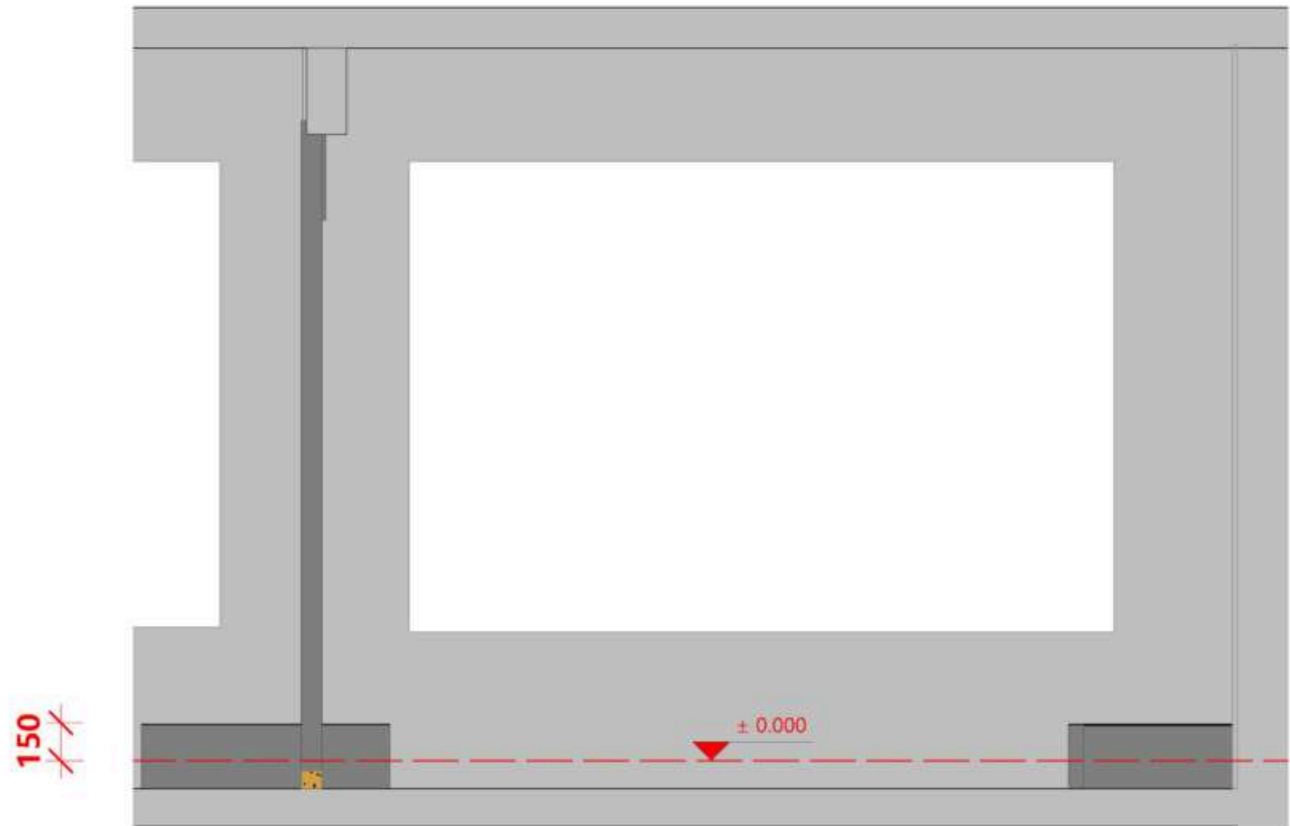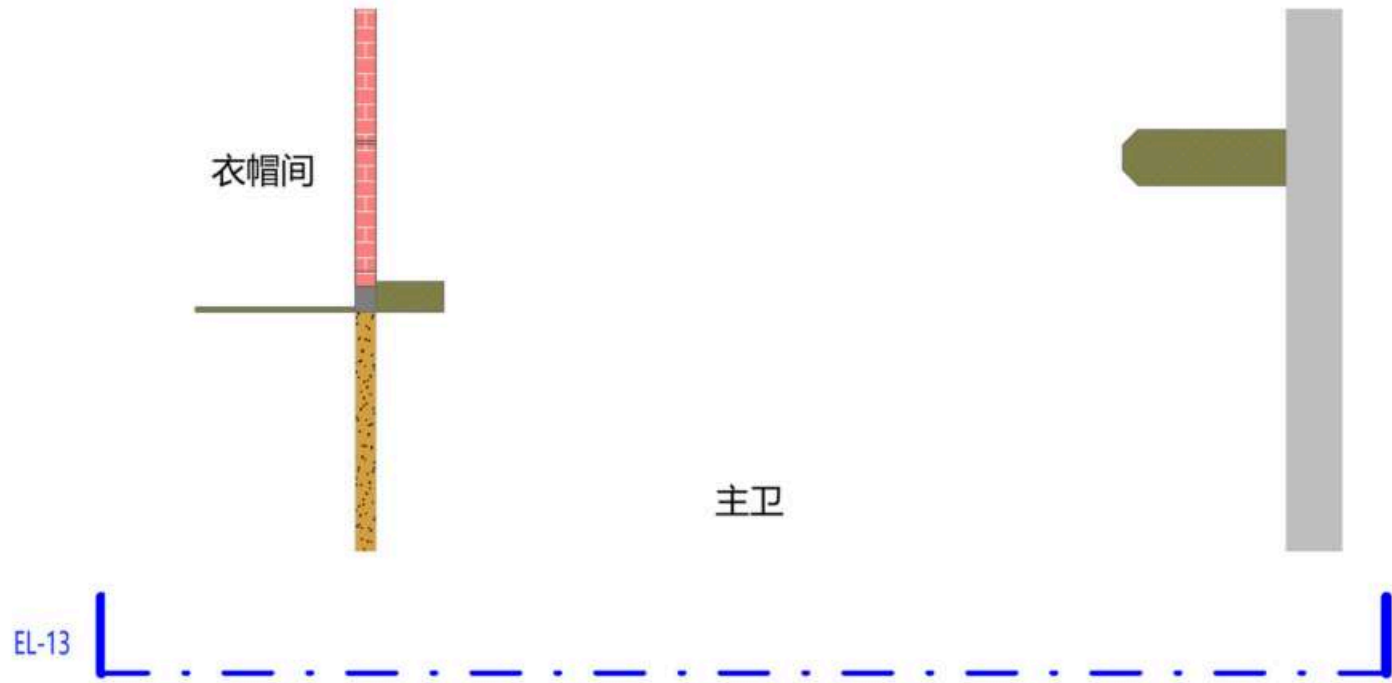

正式施工图
2026-01-27

ELBORN

LEGEND图例

图例A 材质分类		
编号	图例	说明
1		原始墙、板、柱
2		混凝土导墙、结构柱、马牙槎
3		PC砖
4		红砖
5		钢架墙
6		止水坎
7		混凝土止水坎上加5mm钢板

图例B 施工时注意事项		
编号	图例	说明
1		地面完成线
2		必要尺寸
3		起铺点
4		错缝要求 a≥200 b≥150
5		边砖宽度要求 a≥200
6		b < 150时 a = b

日期
Date 01/08/26

修订
Revision

项目
Project 潮映华府3-801

Scale
比例 1:30@A2

PC砖墙13

Drawing No.
图纸编号 15-PCW-13

Project No.
项目编号 ©2025

注释
Notes
1.本图纸如与现场尺寸有误，请施工人员与项目负责人联系。
2.施工前施工人员应认真查阅此图，如有不明确尺寸，按现场测量为准。
3.本图纸必须经甲乙双方认可并签字方可作为施工依据。

PC砖墙三维示意图13

Scale比例 1:30@A2

1




3D-13

PC砖墙立面图13

Scale比例 1 : 30@A2

1

EL-13

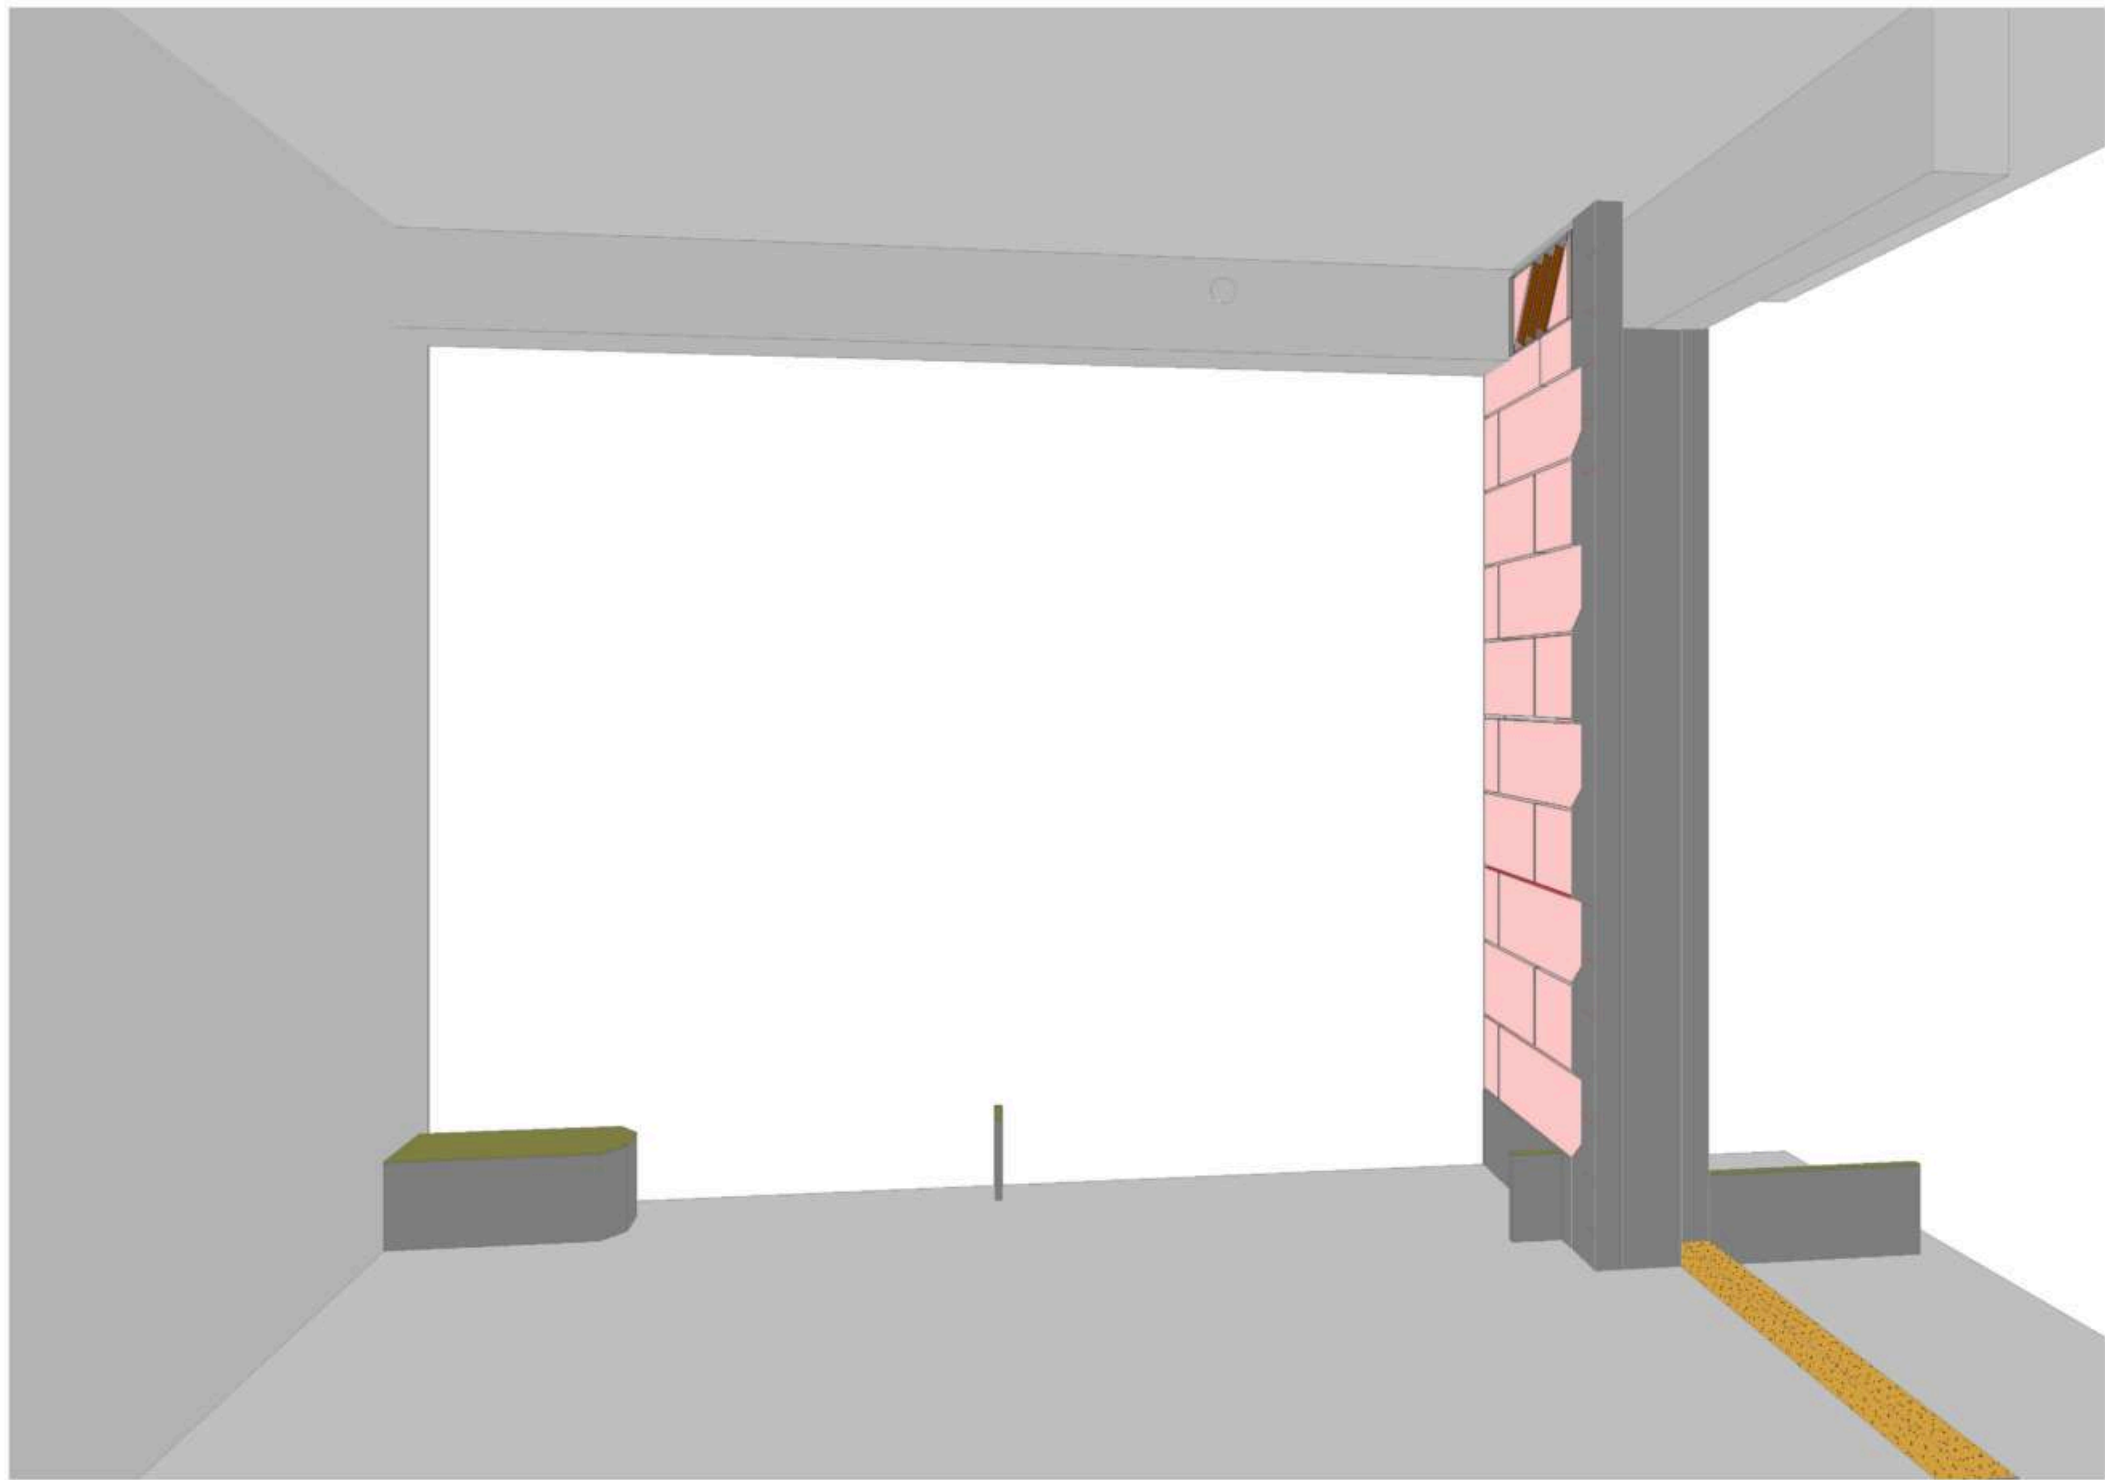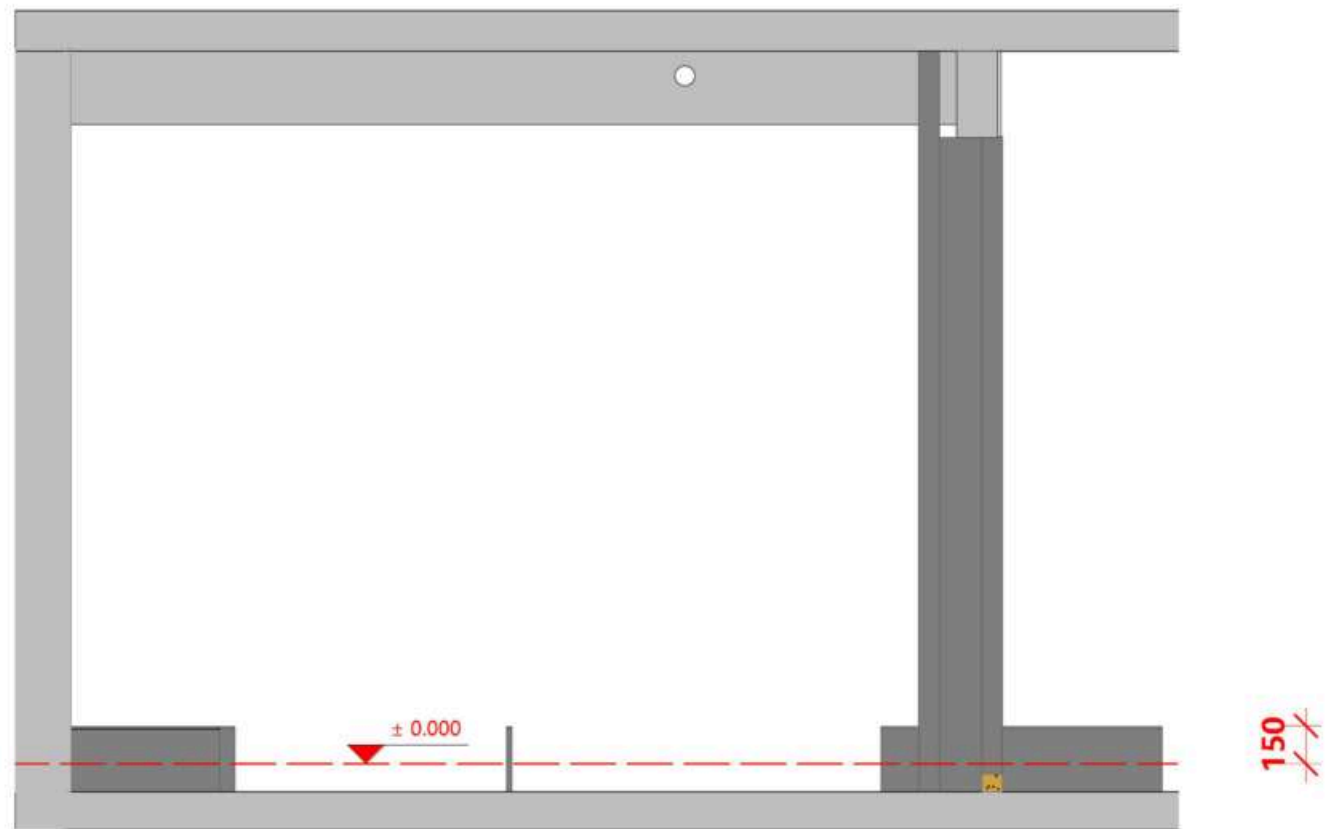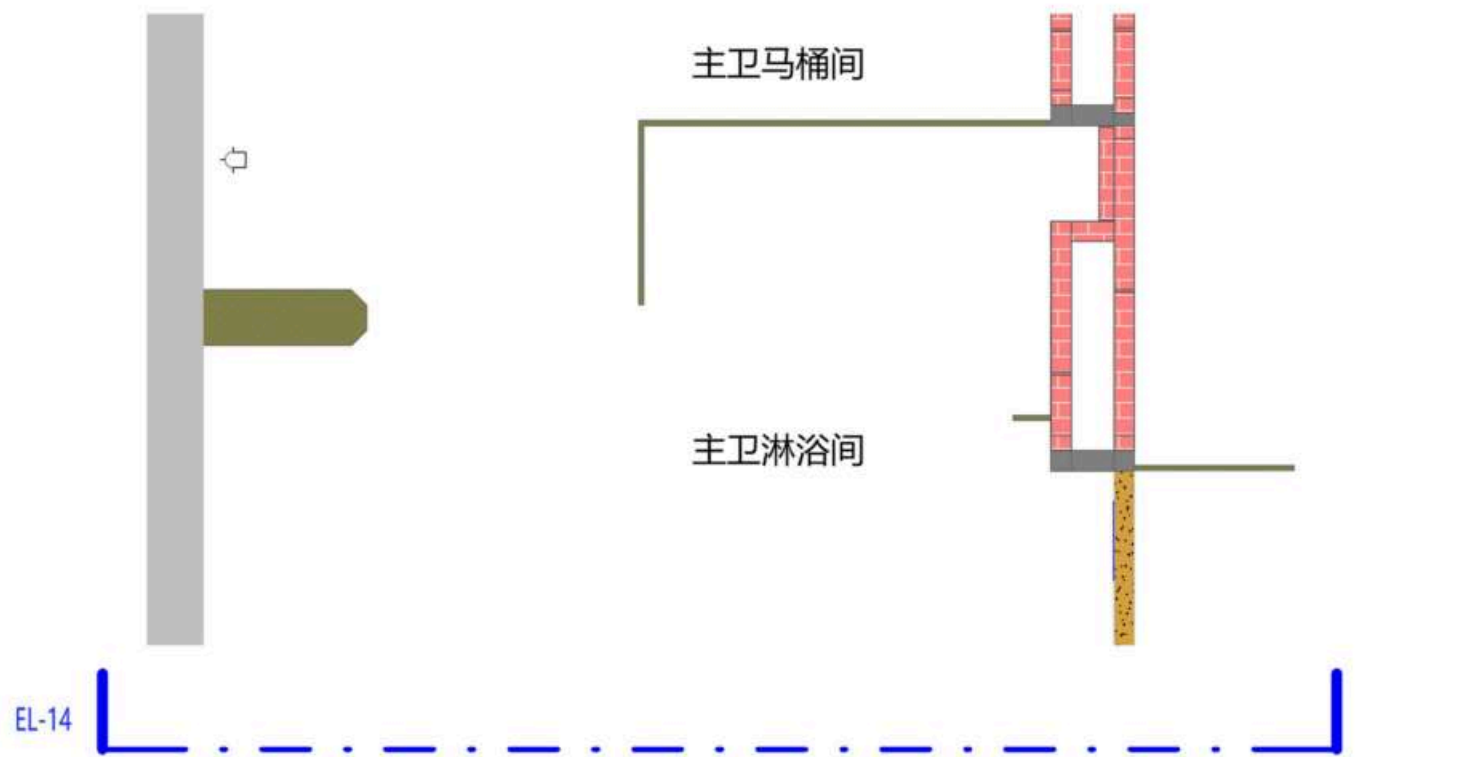

LEGEND图例

图例A 材质分类		
编号	图例	说明
1		原始墙、板、柱
2		混凝土导墙、结构柱、马牙槎
3		PC砖
4		红砖
5		钢架墙
6		止水坎
7		混凝土止水坎上加5mm钢板

图例B 施工时注意事项		
编号	图例	说明
1		地面完成线
2		必要尺寸
3		起铺点
4		错缝要求 a≥200 b≥150
5		边砖宽度要求 a≥200
6		b < 150时 a = b

日期
Date 01/08/26

修订
Revision

项目
Project 潮映华府3-801

Scale
比例 1:30@A2
PC砖墙14



Drawing No.
图纸编号 16-PCW-14

Project No.
项目编号 ©2025

正式施工图
2026-01-27

Scale比例 1:30@A2
PC砖墙三维示意图14

注释
Notes
1.本图纸如与现场尺寸有误，请施工人员与项目负责人联系。
2.施工前施工人员应认真查阅此图，如有不明确尺寸，按现场测量为准。
3.本图纸必须经甲乙双方认可并签字方可作为施工依据。

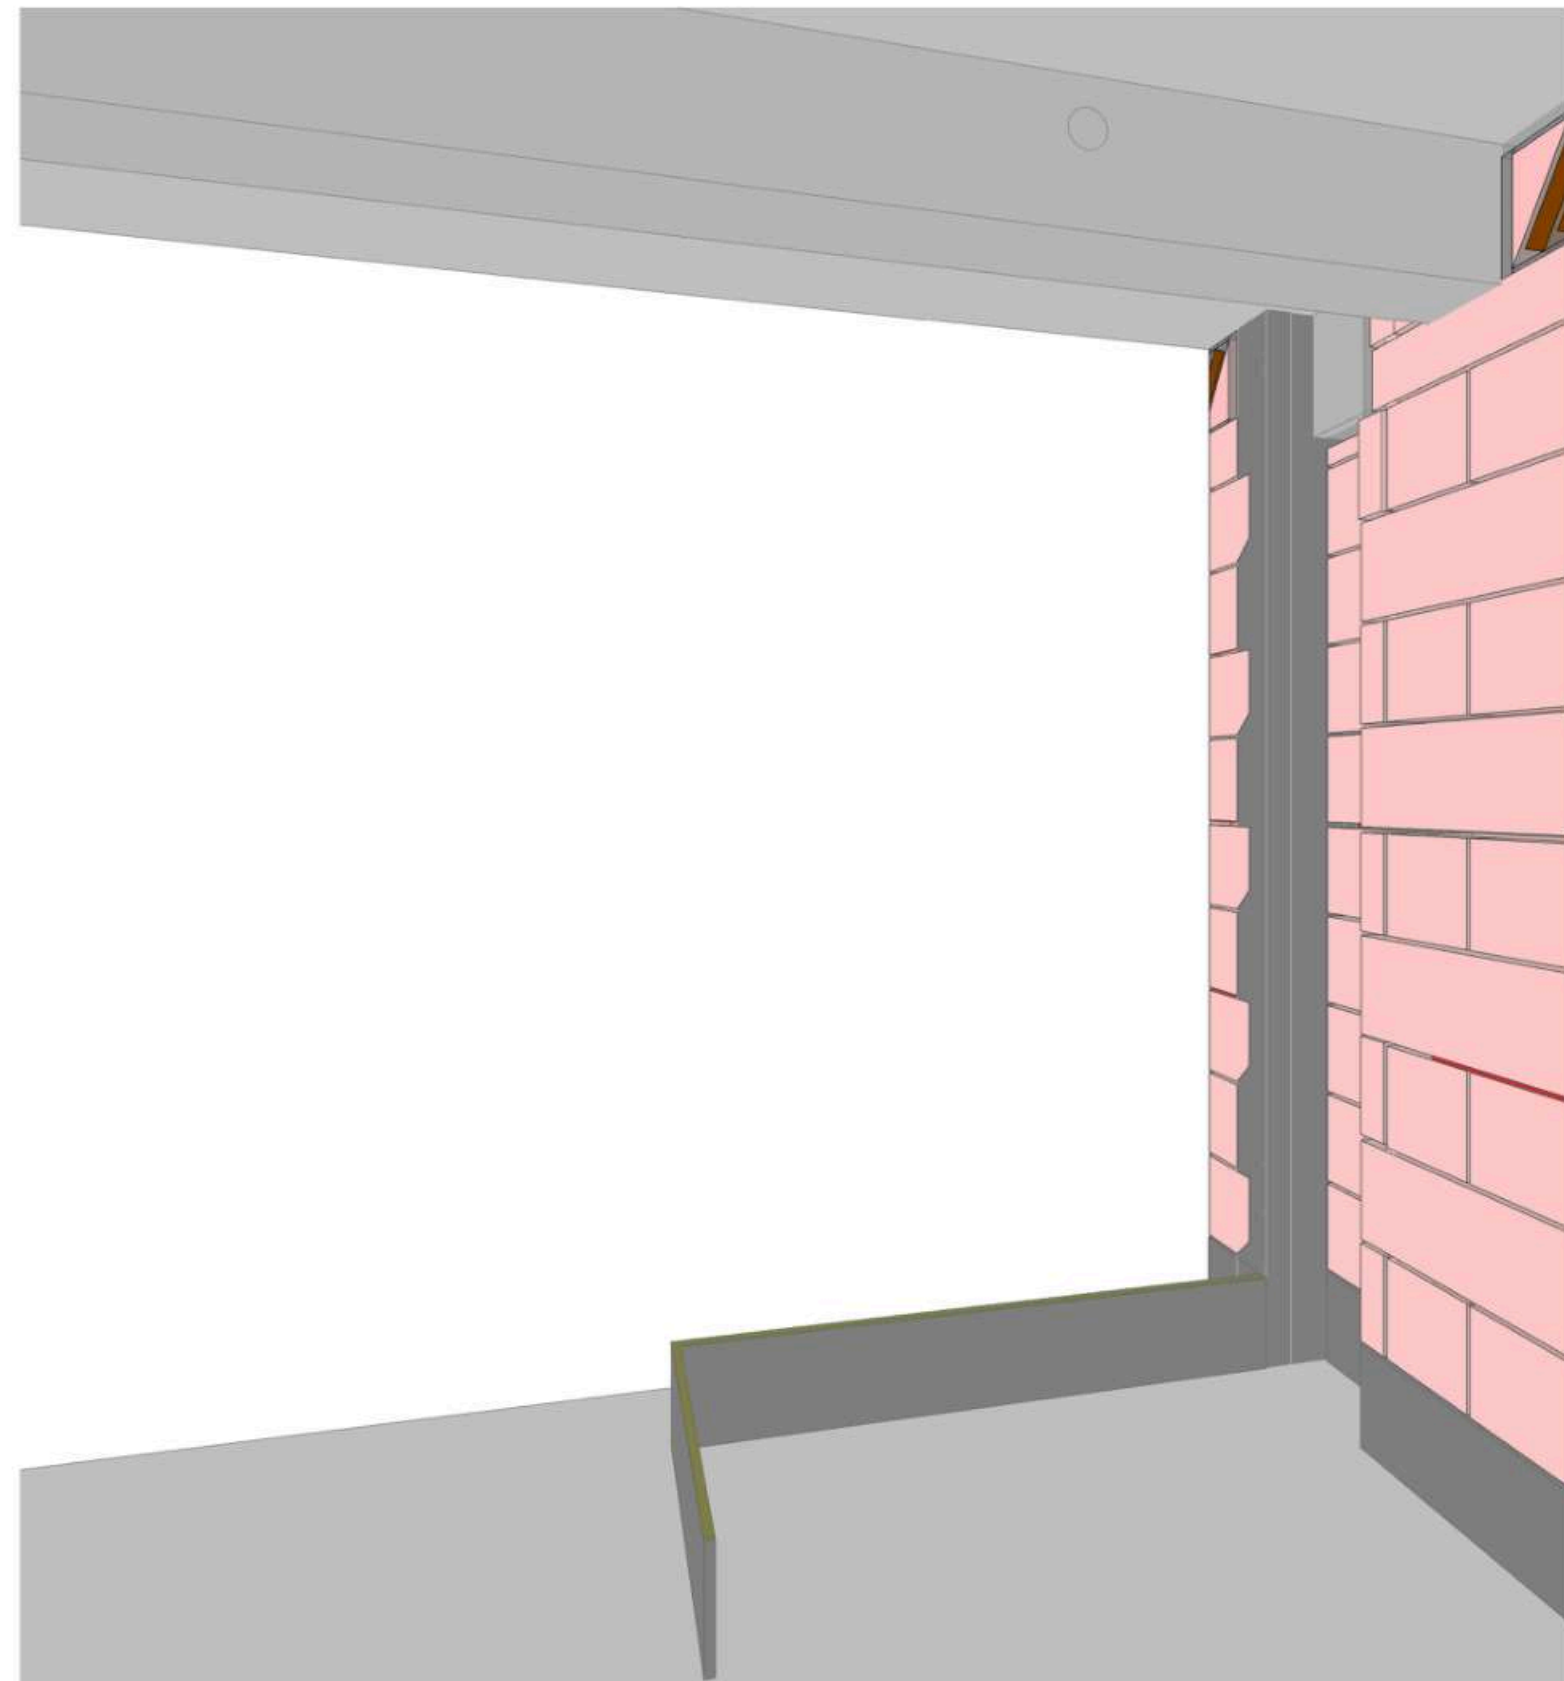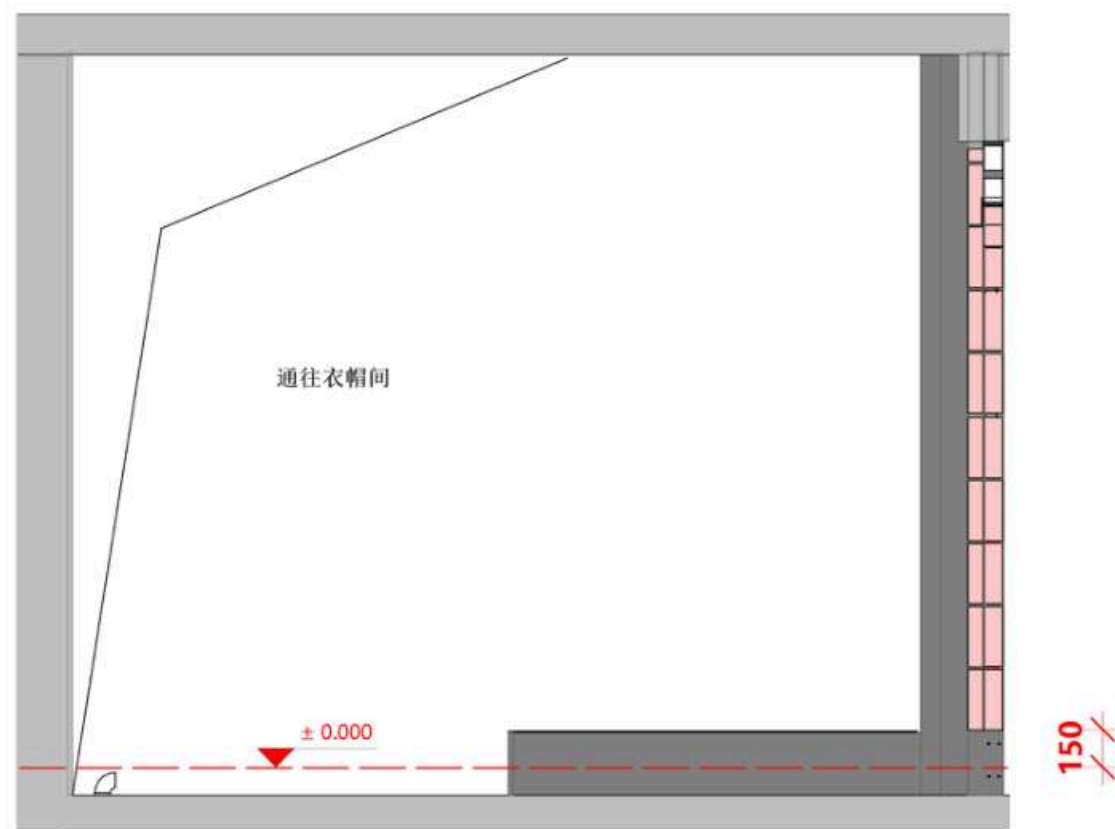

LEGEND图例

图例A 材质分类		
编号	图例	说明
1		原始墙、板、柱
2		混凝土导墙、结构柱、马牙槎
3		PC砖
4		红砖
5		钢架墙
6		止水坎
7		混凝土止水坎上加5mm钢板
图例B 施工时注意事项		
编号	图例	说明
1		地面完成线
2		必要尺寸
3		起铺点
4		错峰要求 $a \geq 200$ $b \geq 150$
5		边砖宽度要求 $a \geq 200$
6		$b < 150$ 时 $a = b$

日期
Date01/08/26修订
Revision项目
Project

潮映华岸府3-801

Scale
比例1:30@A2

PC砖墙15

Drawing No.
图纸编号

17-PCW-15




Project No.
项目编号©2025

1
EL-15
PC砖墙立面图15
Scale比例 1 : 30@A2

1
3D-15
PC砖墙三维示意图15
Scale比例 1:30@A2

注释
Notes
1.本图纸如与现场尺寸有误, 请施工人员与项目负责人联系。
2.施工前施工人员应认真查阅此图, 如有不明确尺寸, 按现场测量为准。
3.本图纸必须经甲乙双方认可并签字方可作为施工依据。

正式施工图
2026-01-27

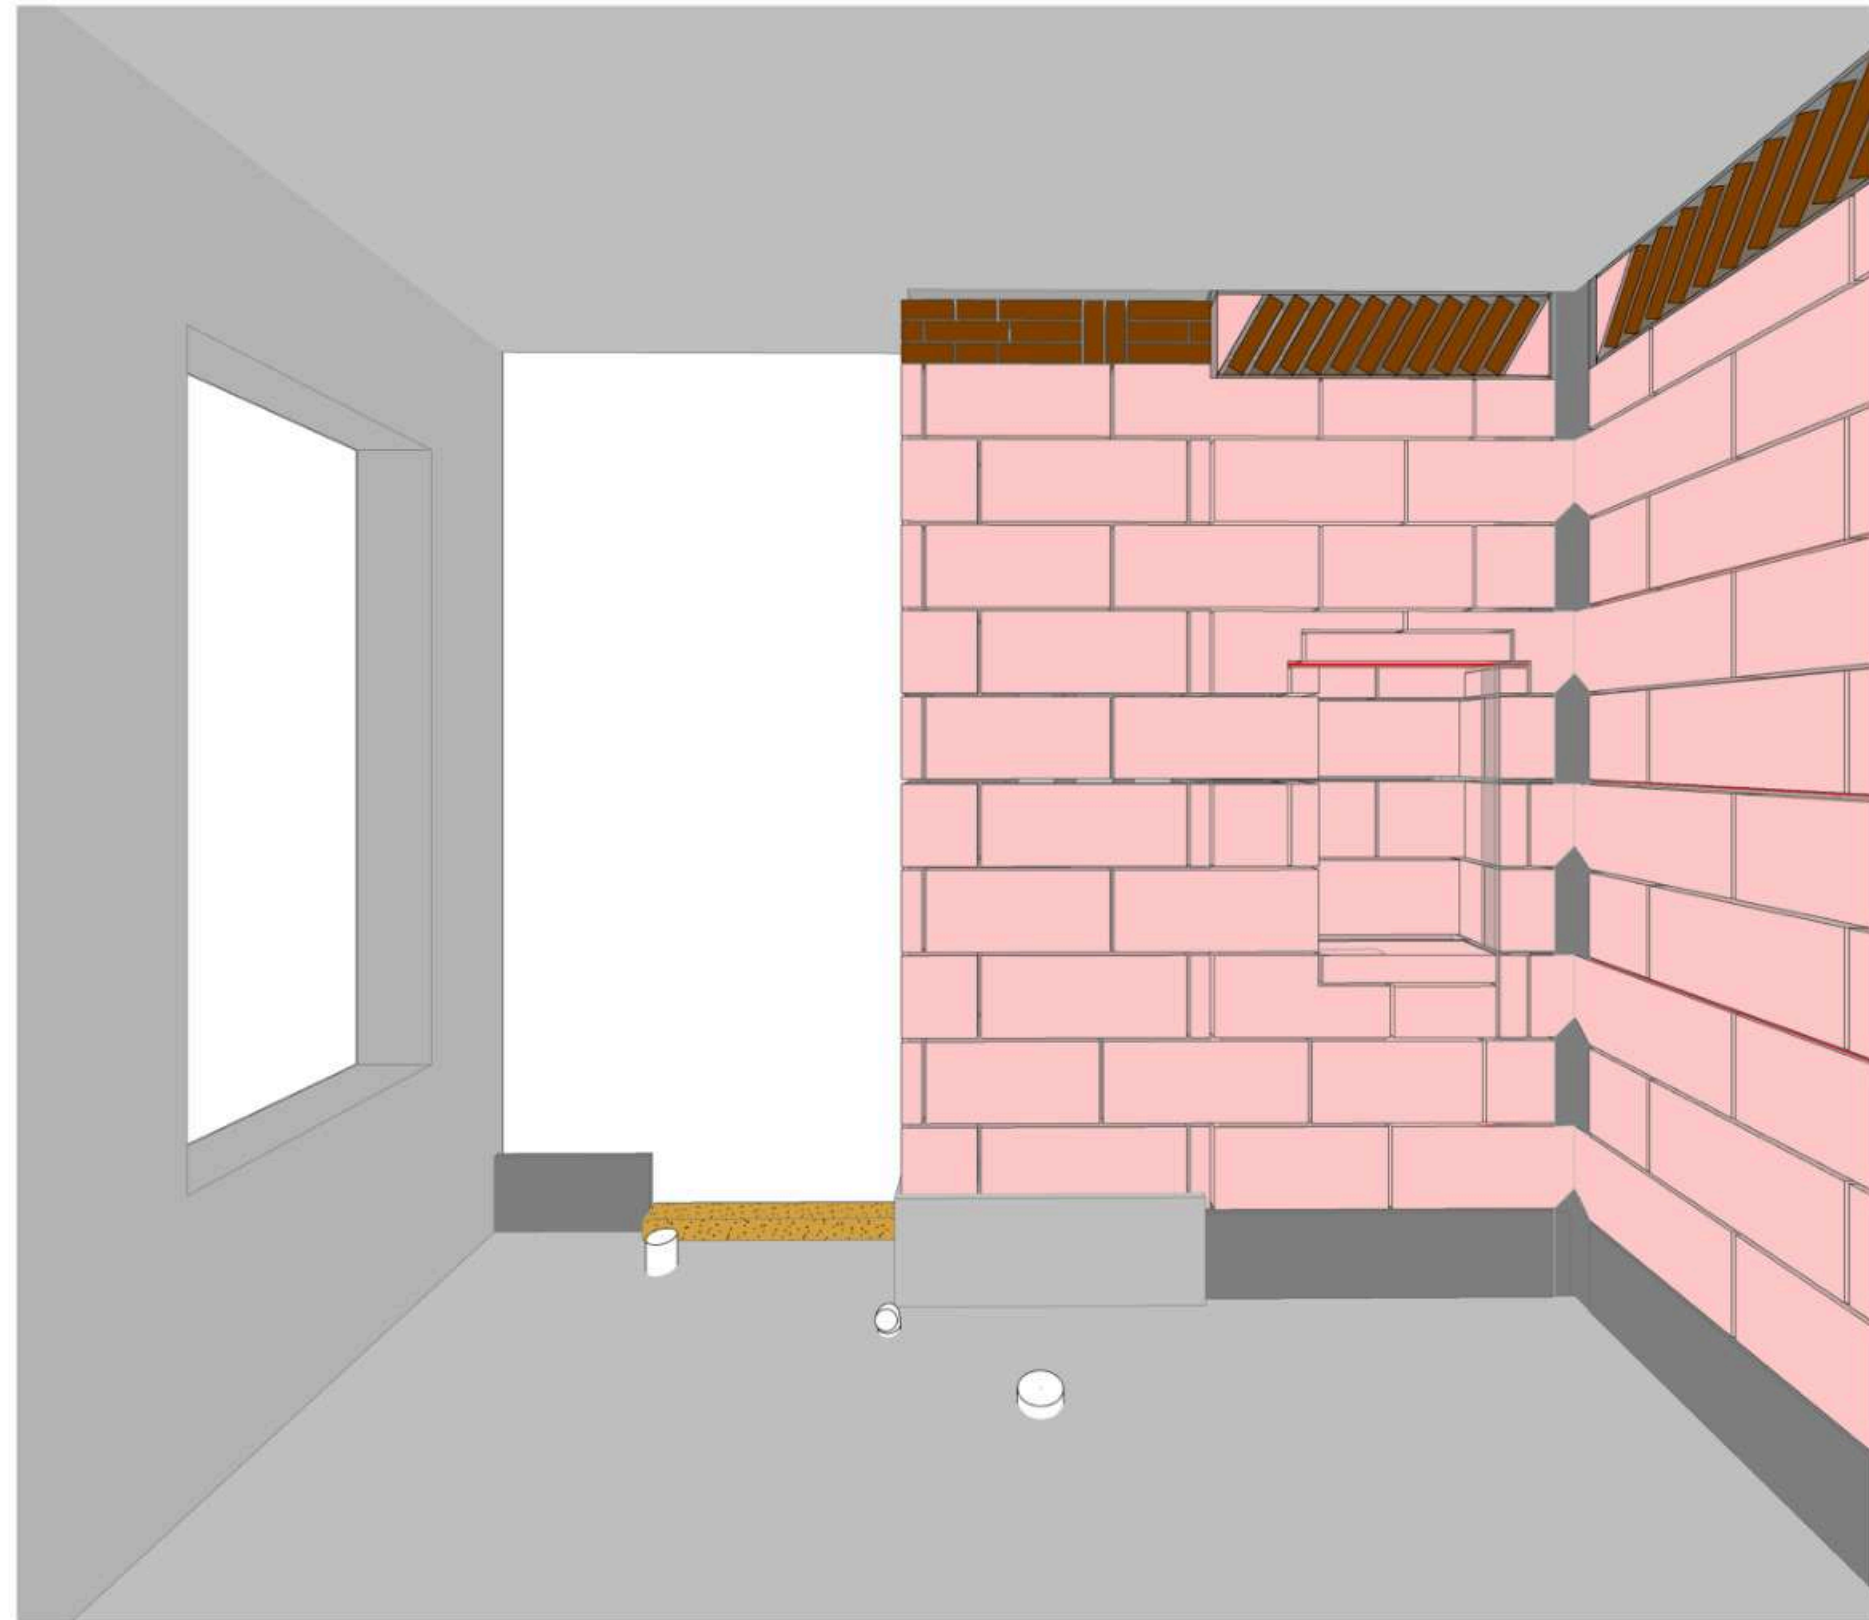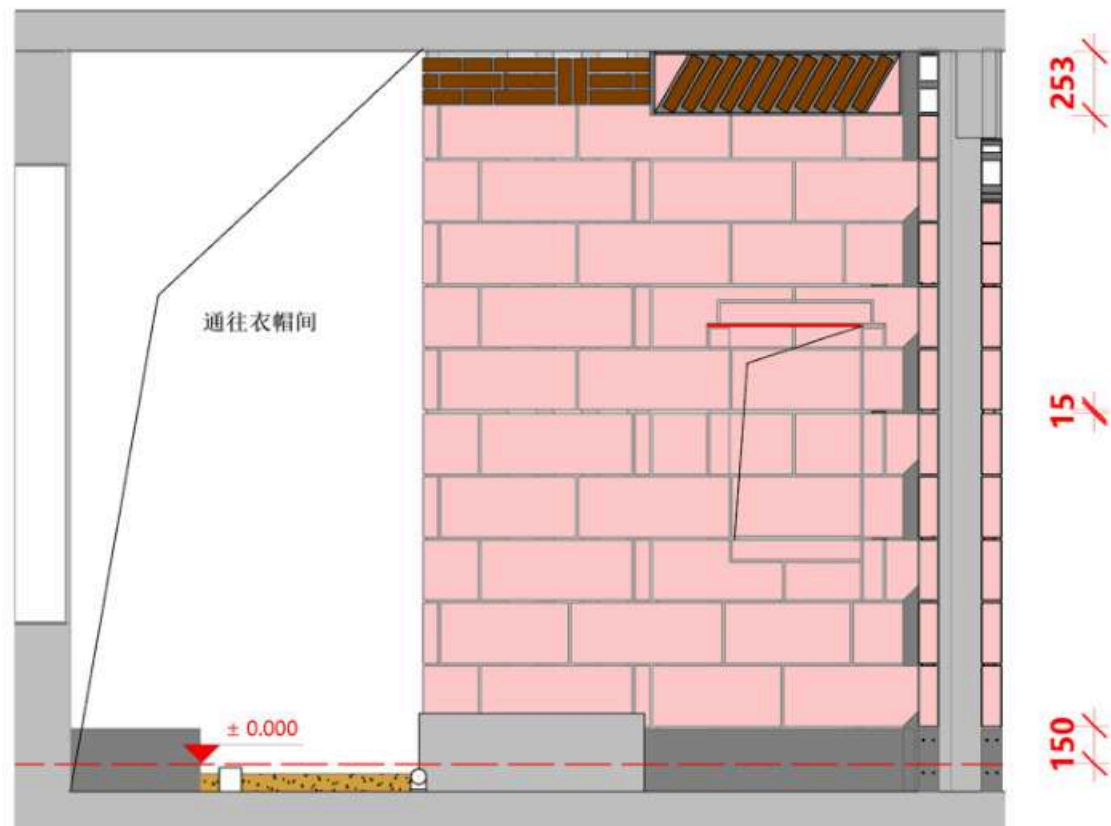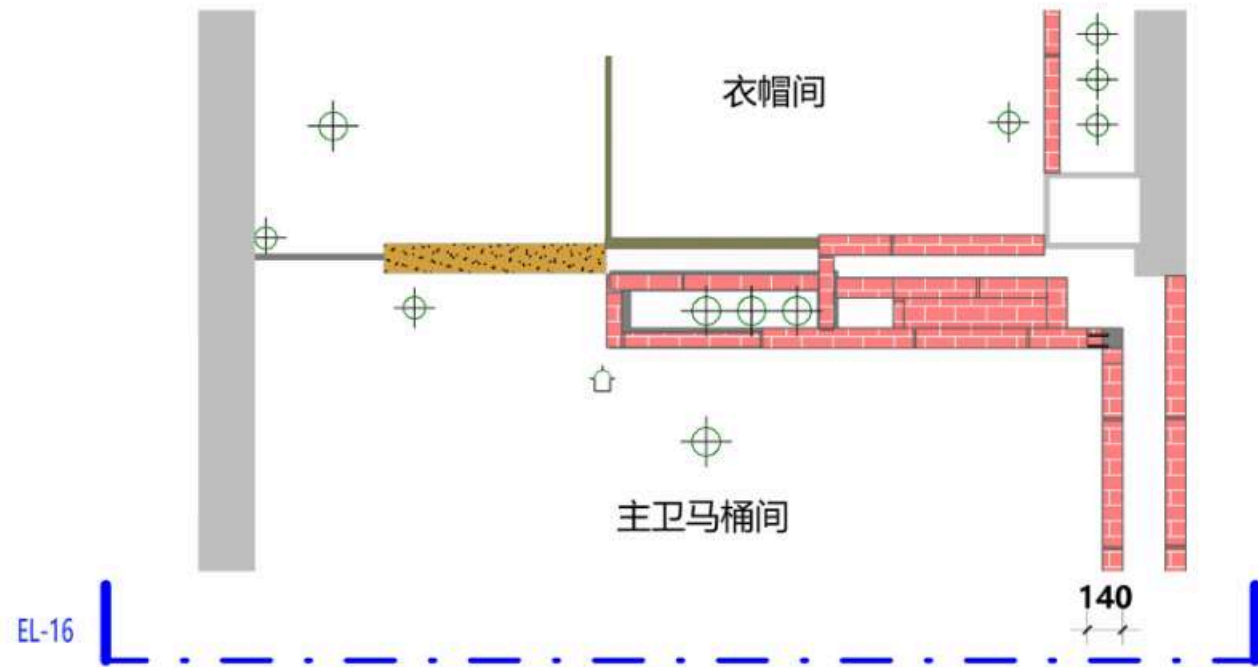

EL-16

LEGEND图例

图例A 材质分类		
编号	图例	说明
1		原始墙、板、柱
2		混凝土导墙、结构柱、马牙槎
3		PC砖
4		红砖
5		钢架墙
6		止水坎
7		混凝土止水坎上加5mm钢板

图例B 施工时注意事项		
编号	图例	说明
1		地面完成线
2		必要尺寸
3		起铺点
4		错峰要求 $a \geq 200$ $b \geq 150$
5		边砖宽度要求 $a \geq 200$
6		$b < 150$ 时 $a = b$

日期
Date

01/08/26

修订
Revision

项目
Project

潮映华府3-801

Scale
比例

1:30@A2

PC砖墙16

Drawing No.
图纸编号

18-PCW-16

Project No.
项目编号

©2025

1

EL-16

PC砖墙立面图16

Scale比例 1 : 30@A2

1

3D-16

PC砖墙三维示意图16

Scale比例 1:30@A2




注释

Notes

1.本图纸如与现场尺寸有误,请施工人员与项目负责人联系。
2.施工前施工人员应认真查阅此图,如有不明确尺寸,按现场测量为准。
3.本图纸必须经甲乙双方认可并签字方可作为施工依据。

正式施工图

2026-01-27

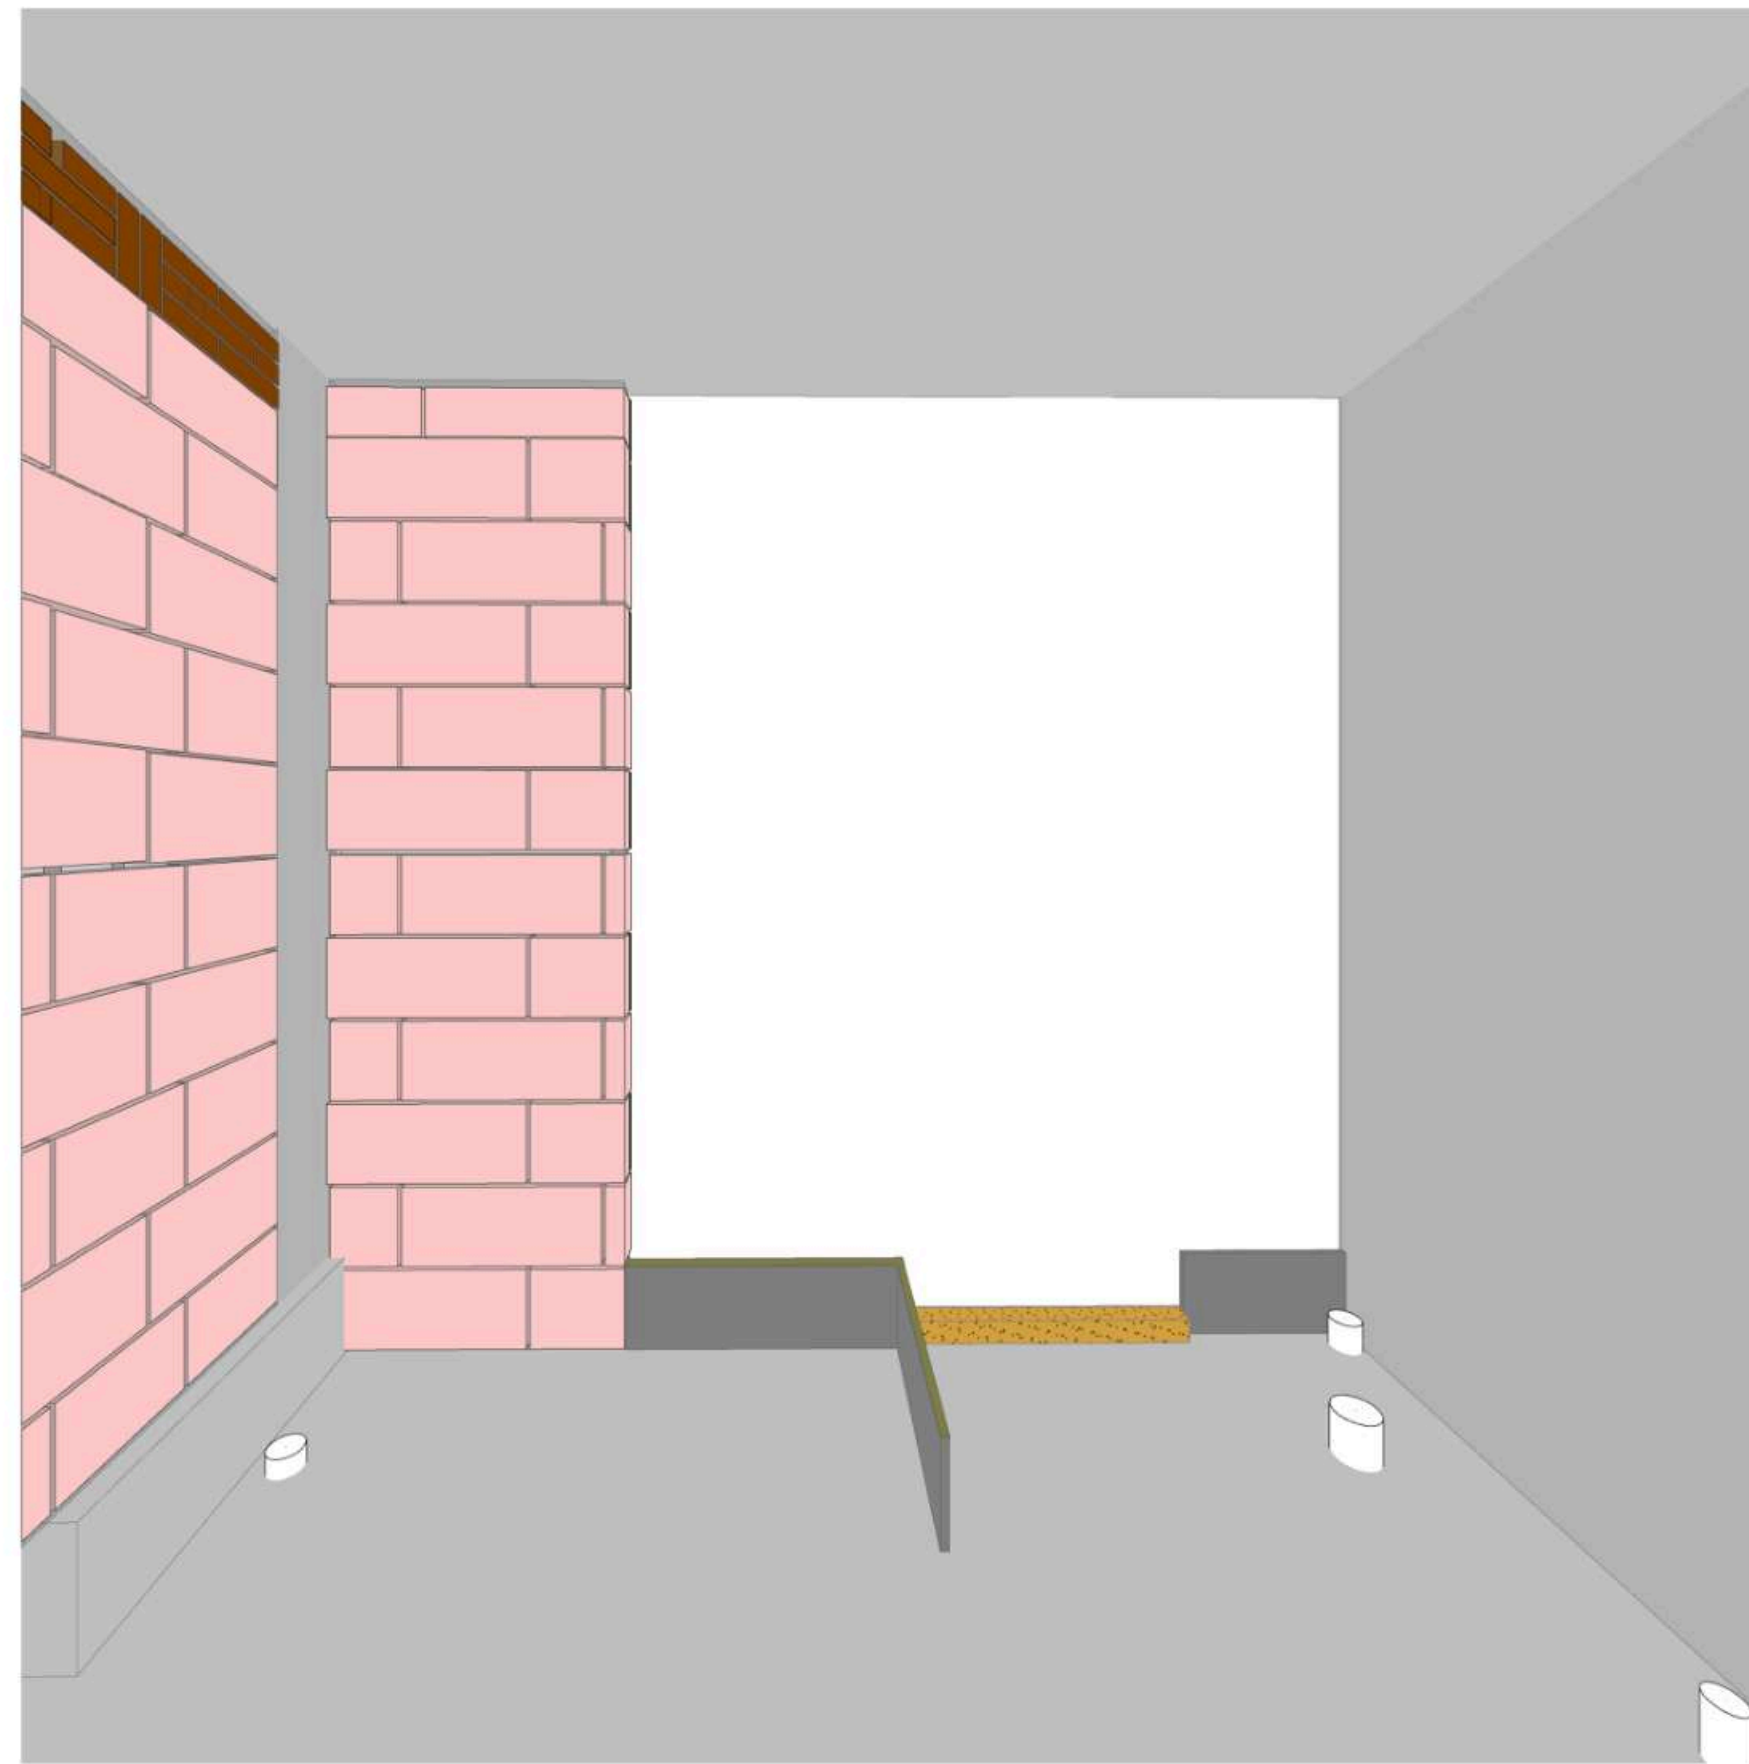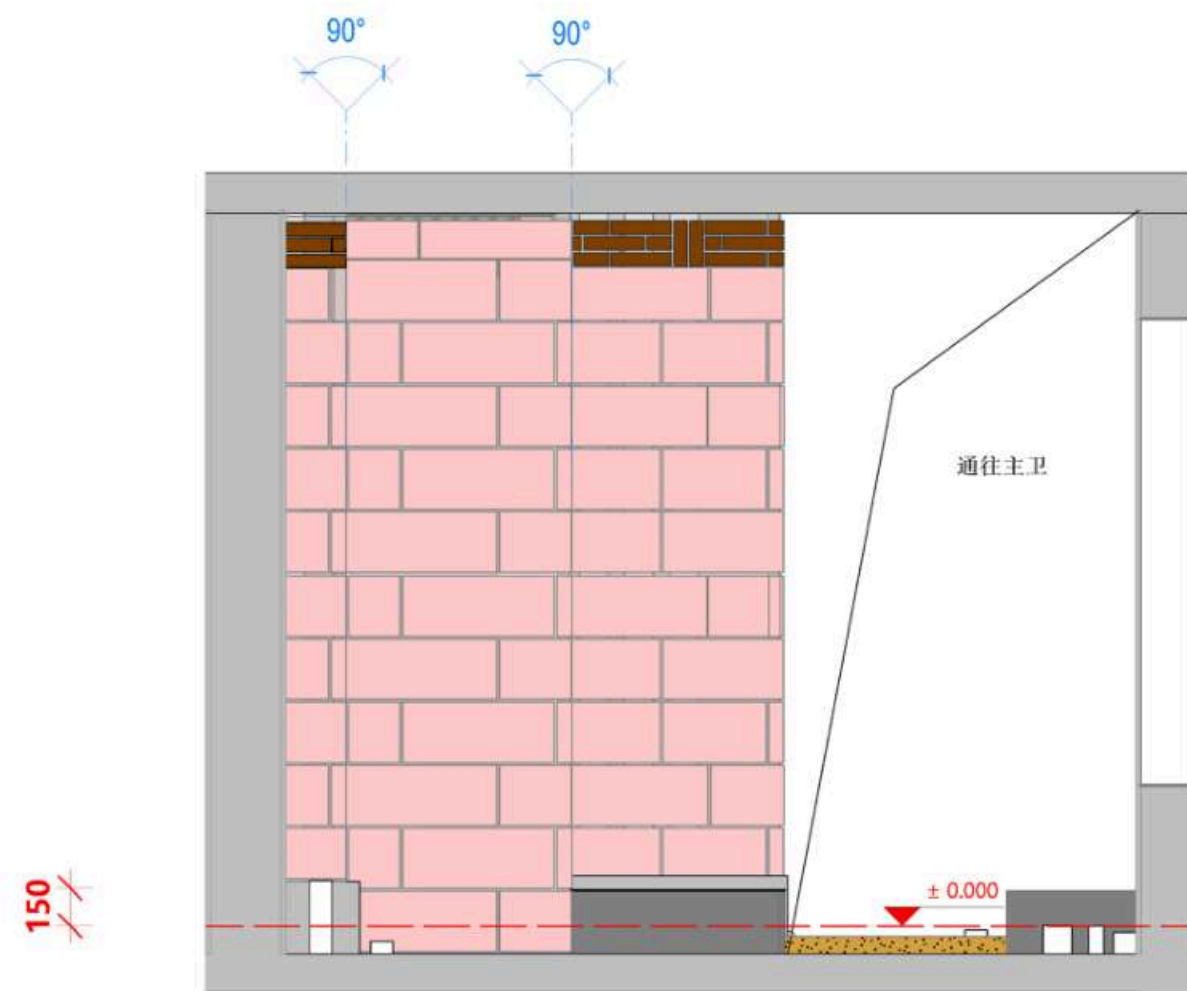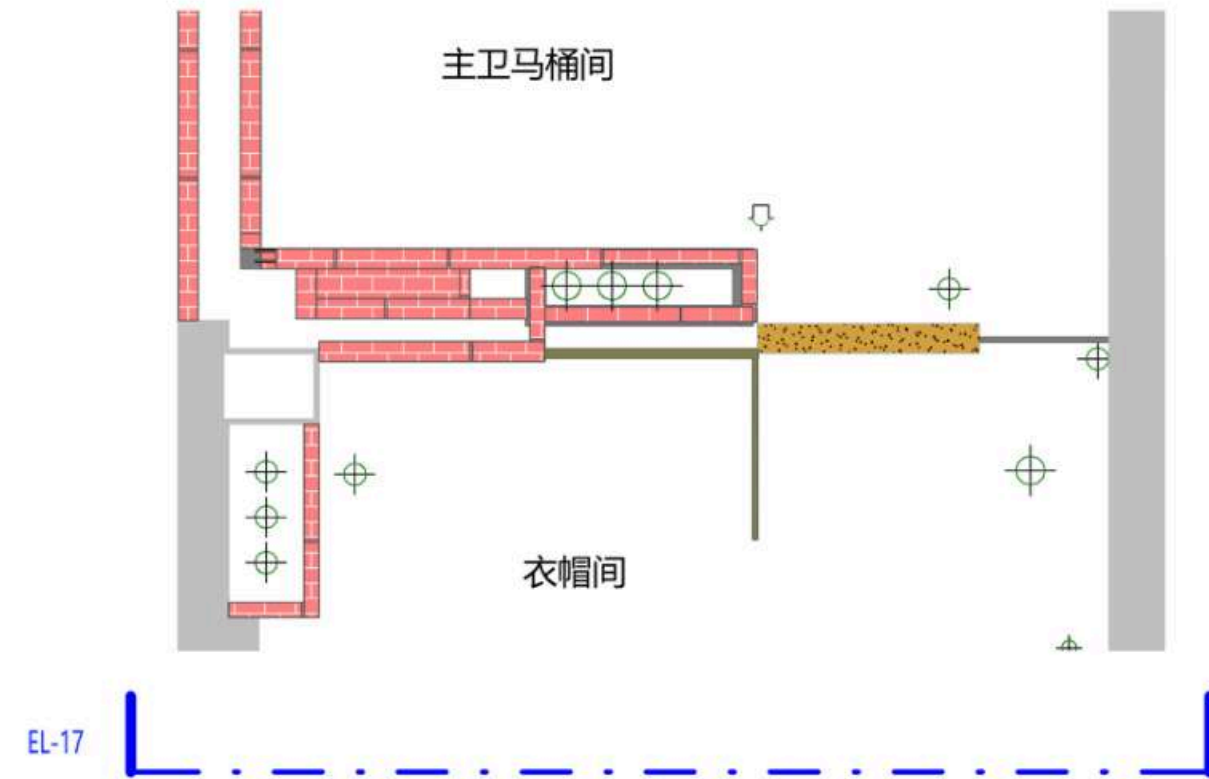

LEGEND图例

图例A 材质分类		
编号	图例	说明
1		原始墙、板、柱
2		混凝土导墙、结构柱、马牙槎
3		PC砖
4		红砖
5		钢架墙
6		止水坎
7		混凝土止水坎上加5mm钢板

图例B 施工时注意事项		
编号	图例	说明
1		地面完成线
2		必要尺寸
3		起铺点
4		错峰要求 $a \geq 200$ $b \geq 150$
5		边砖宽度要求 $a \geq 200$
6		$b < 150$ 时 $a = b$

日期
Date

01/08/26

修订
Revision

项目
Project

潮映华府3-801

Scale
比例

1:30@A2

正式施工图

2026-01-27

PC砖墙17

Drawing No.
图纸编号

19-PCW-17

Project No.
项目编号

©2025

1

PC砖墙立面图17

EL-17

Scale比例 1 : 30@A2

1



3D-17

PC砖墙三维示意图17

Scale比例 1:30@A2

注释
Notes

1.本图纸如与现场尺寸有误, 请施工人员与项目负责人联系。
2.施工前施工人员应认真查阅此图, 如有不明确尺寸, 按现场测量为准。
3.本图纸必须经甲乙双方认可并签字方可作为施工依据。

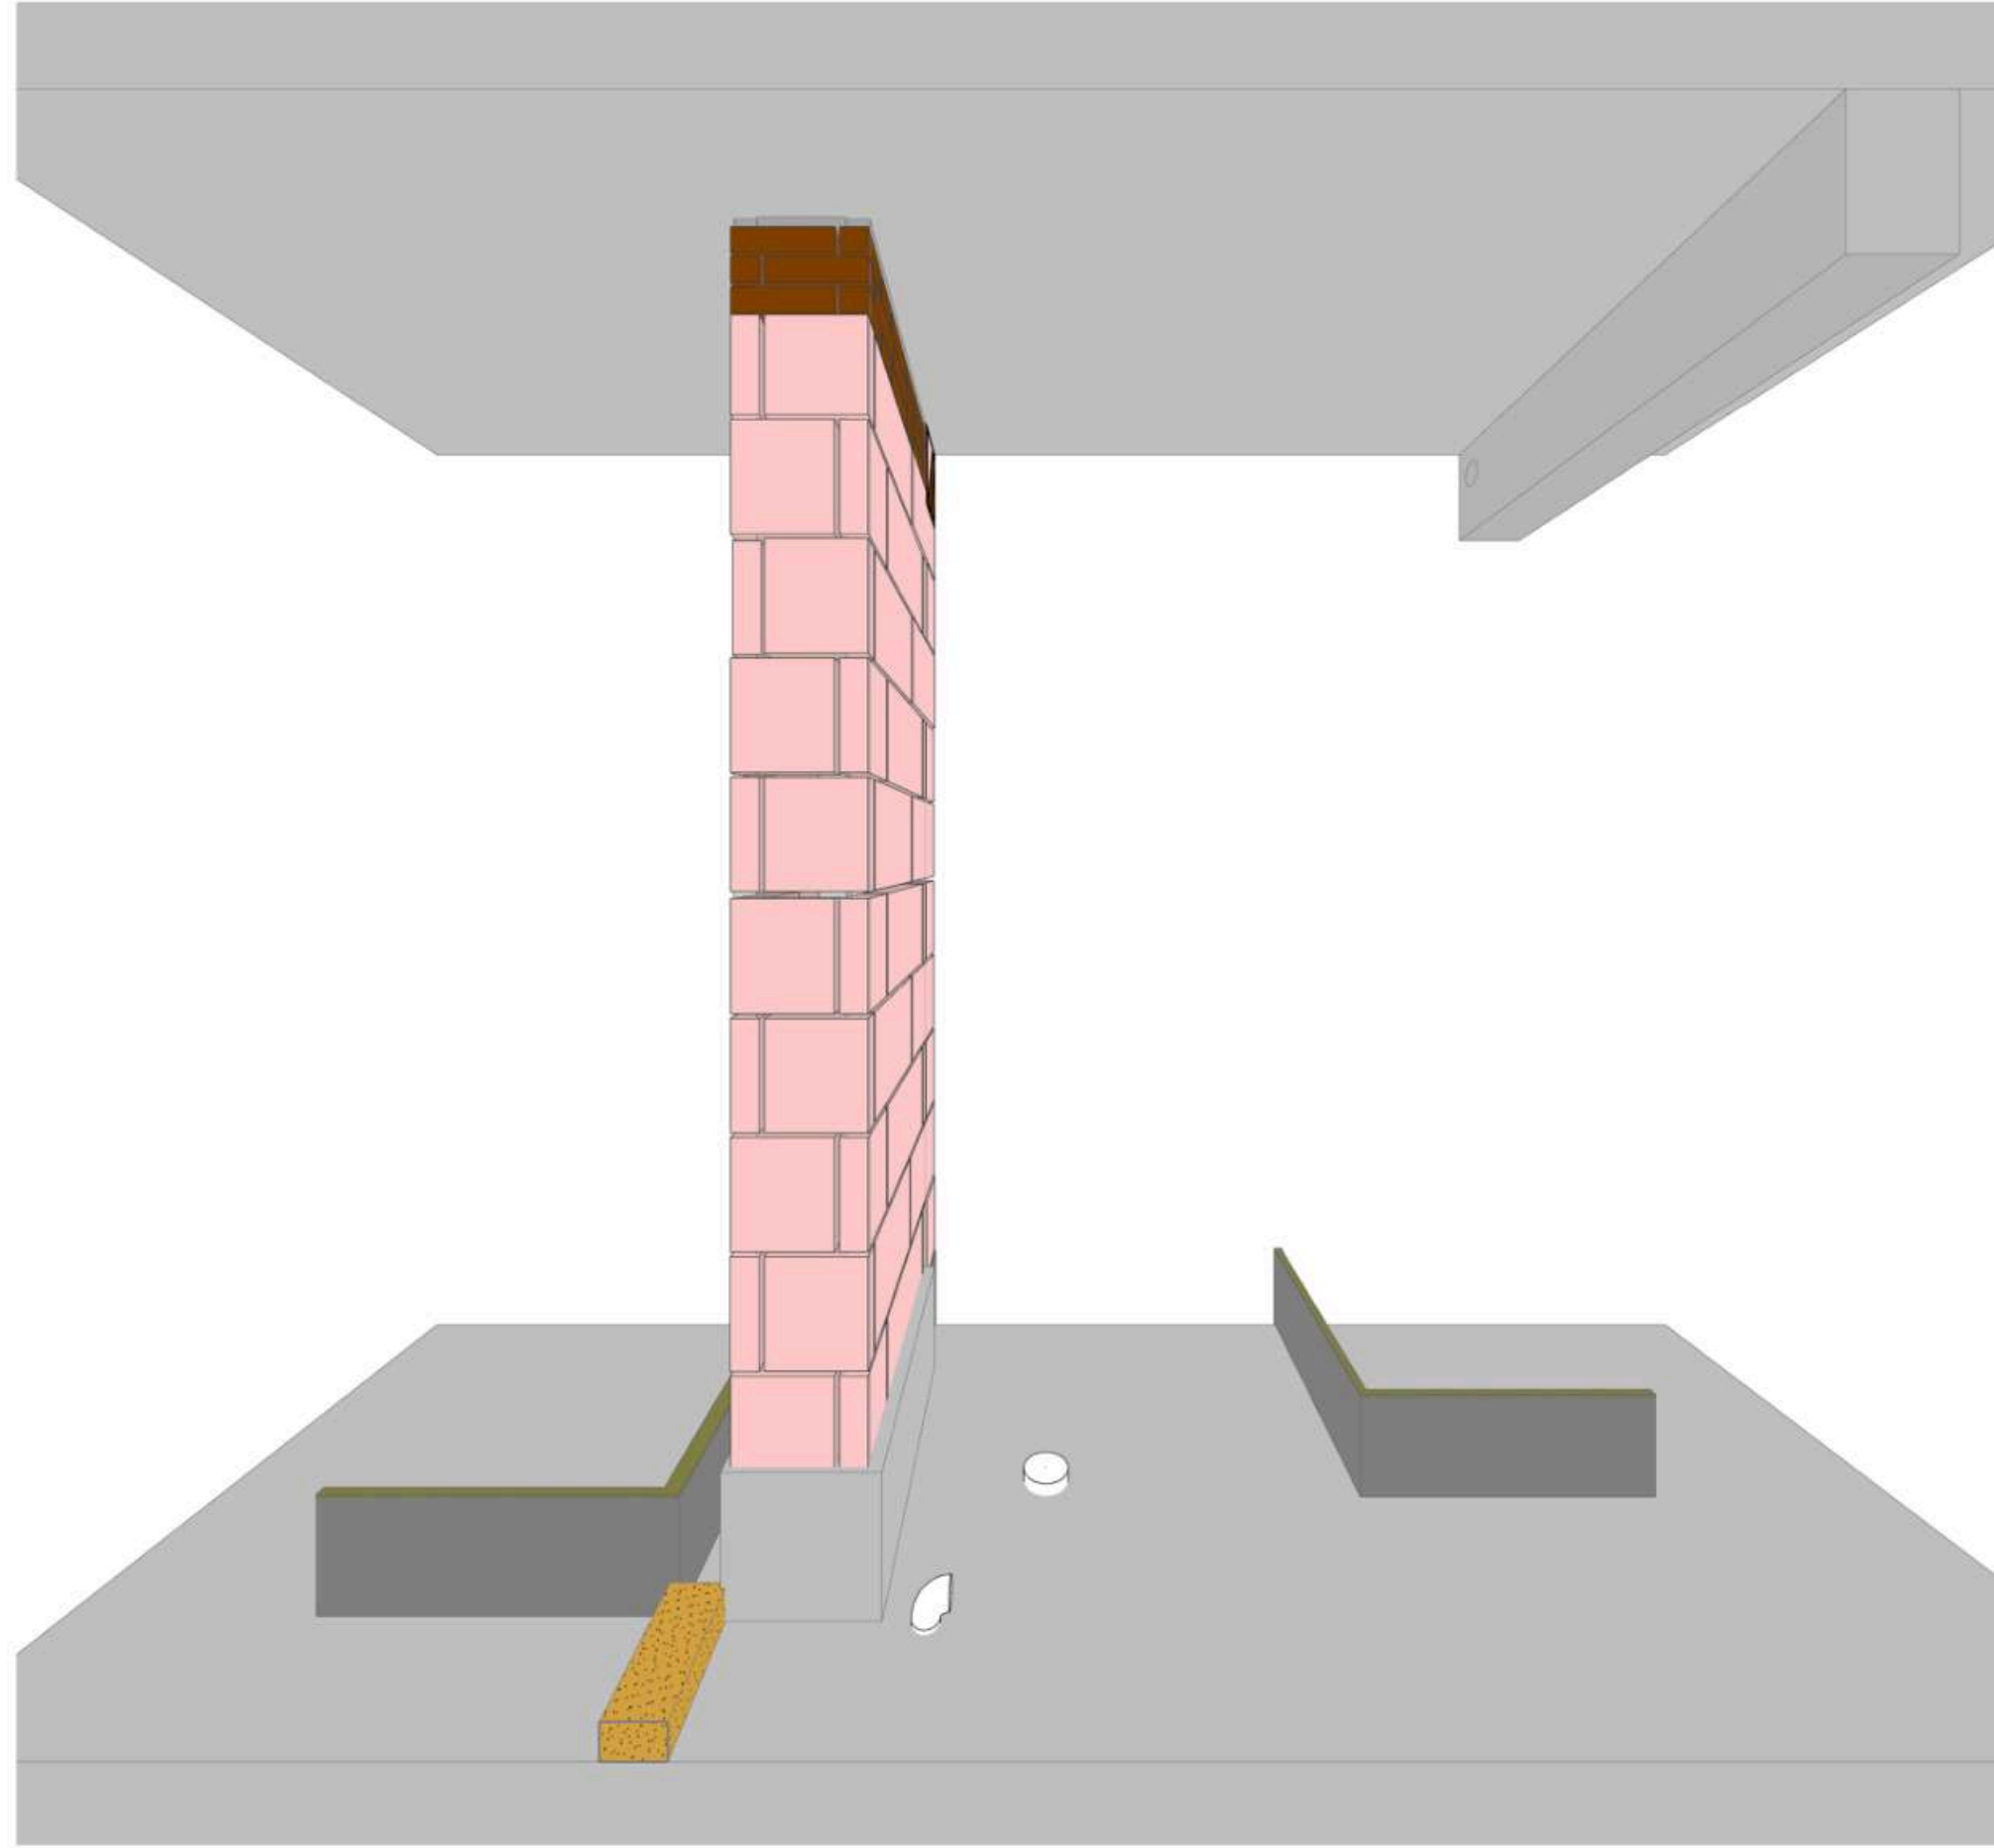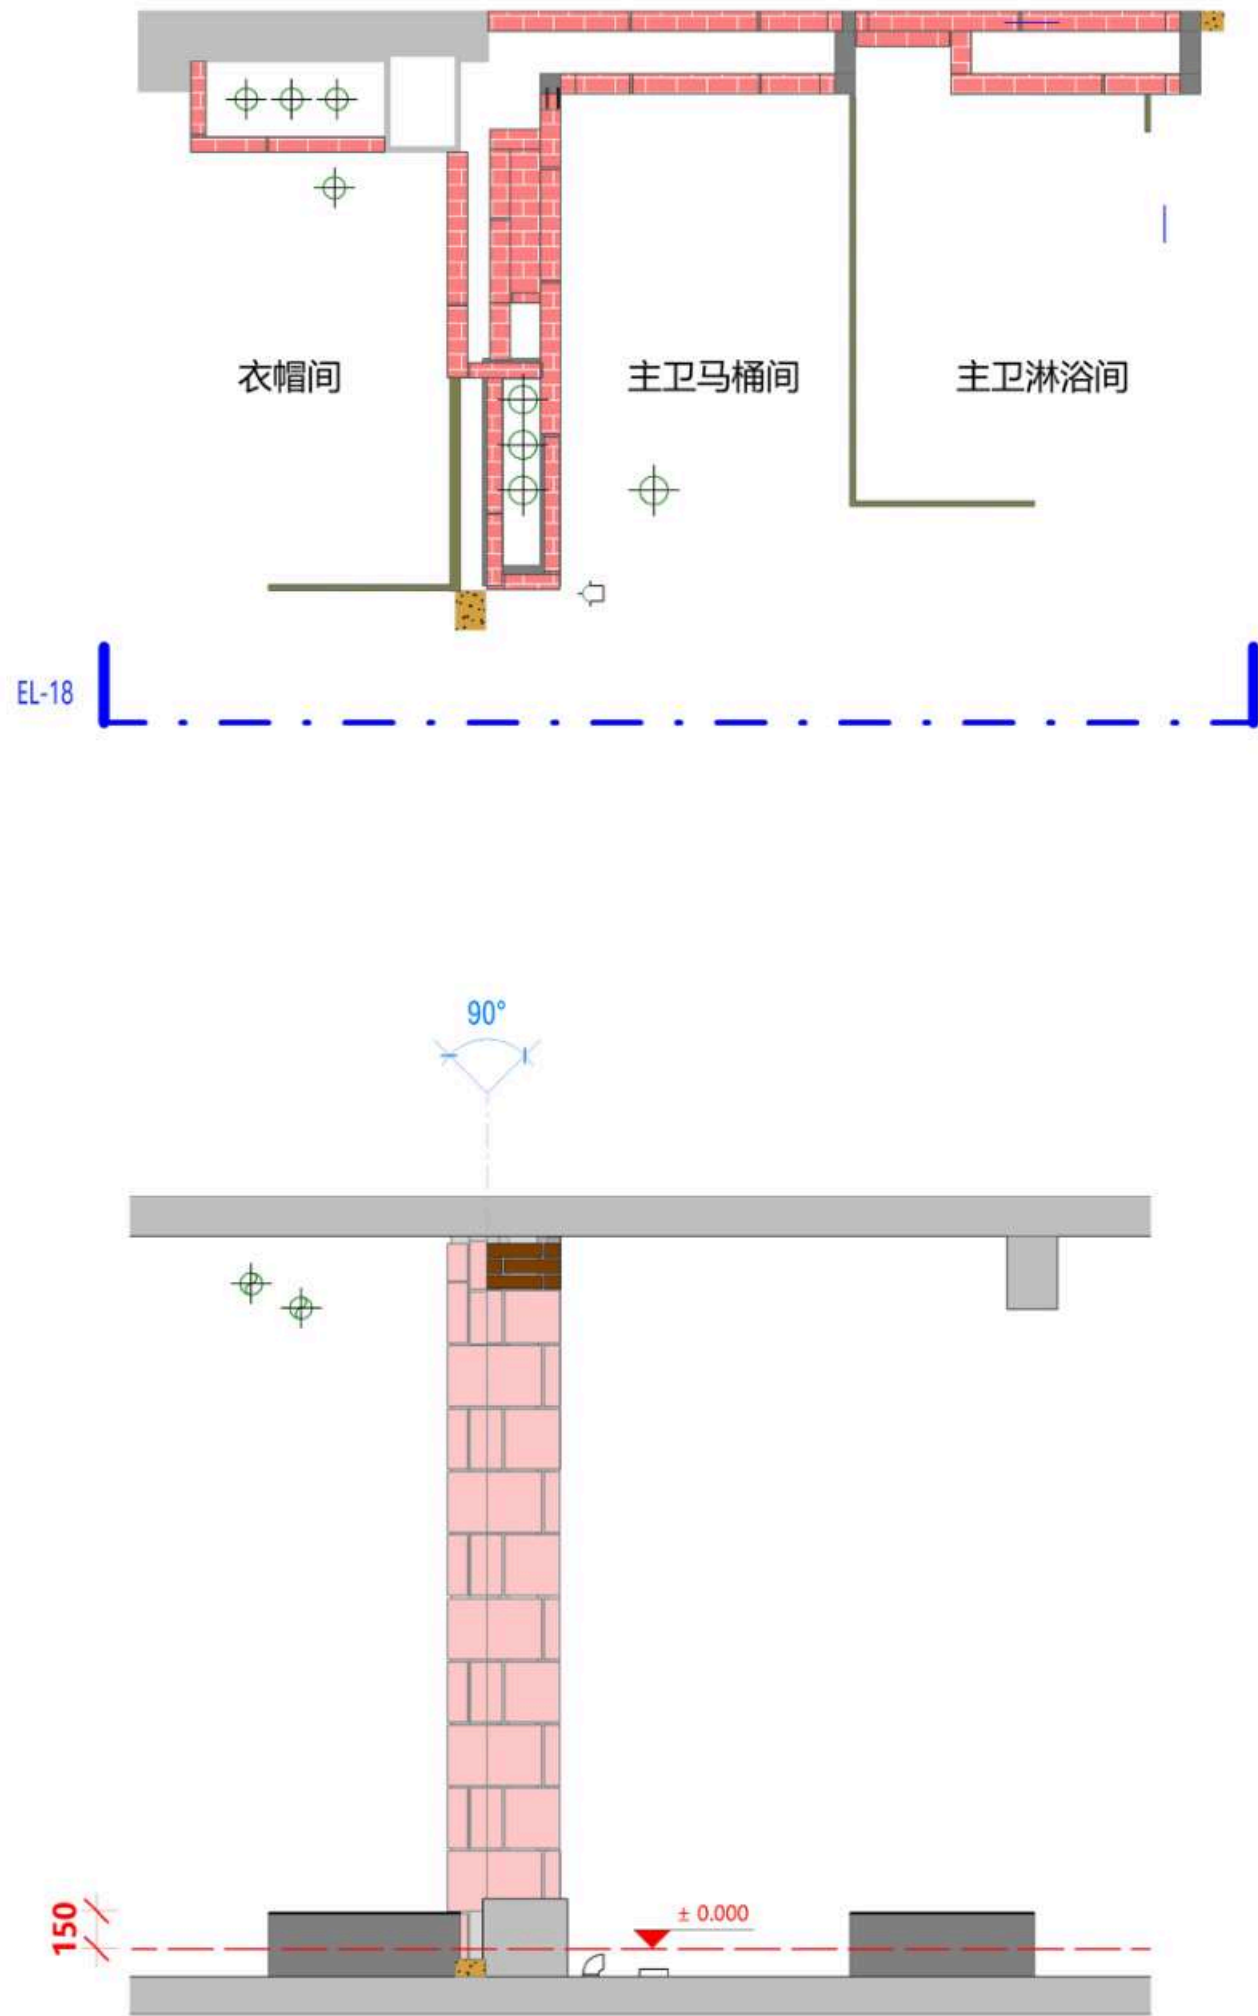

ELBORNI

LEGEND图例

图例A 材质分类		
编号	图例	说明
1		原始墙、板、柱
2		混凝土导墙、结构柱、马牙槎
3		PC砖
4		红砖
5		钢架墙
6		止水坎
7		混凝土止水坎上加5mm钢板
图例B 施工时注意事项		
编号	图例	说明
1		地面完成线
2		必要尺寸
3		起铺点
4		错峰要求 $a \geq 200$ $b \geq 150$
5		边砖宽度要求 $a \geq 200$
6		$b < 150$ 时 $a = b$

日期
Date 01/08/26

修订
Revision

项目
Project
潮映华府3-801

Scale
比例 1:30@A2
PC砖墙18

Drawing No.
图纸编号
20-PCW-18




Project No.
项目编号
©2025

正式施工图
2026-01-27

1
EL-18
PC砖墙立面图18
Scale比例 1 : 30@A2

1
3D-18
PC砖墙三维示意图18
Scale比例 1:30@A2

注释
Notes
1.本图纸如与现场尺寸有误，请施工人员与项目负责人联系。
2.施工前施工人员应认真查阅此图，如有不明确尺寸，按现场测量为准。
3.本图纸必须经甲乙双方认可并签字方可作为施工依据。

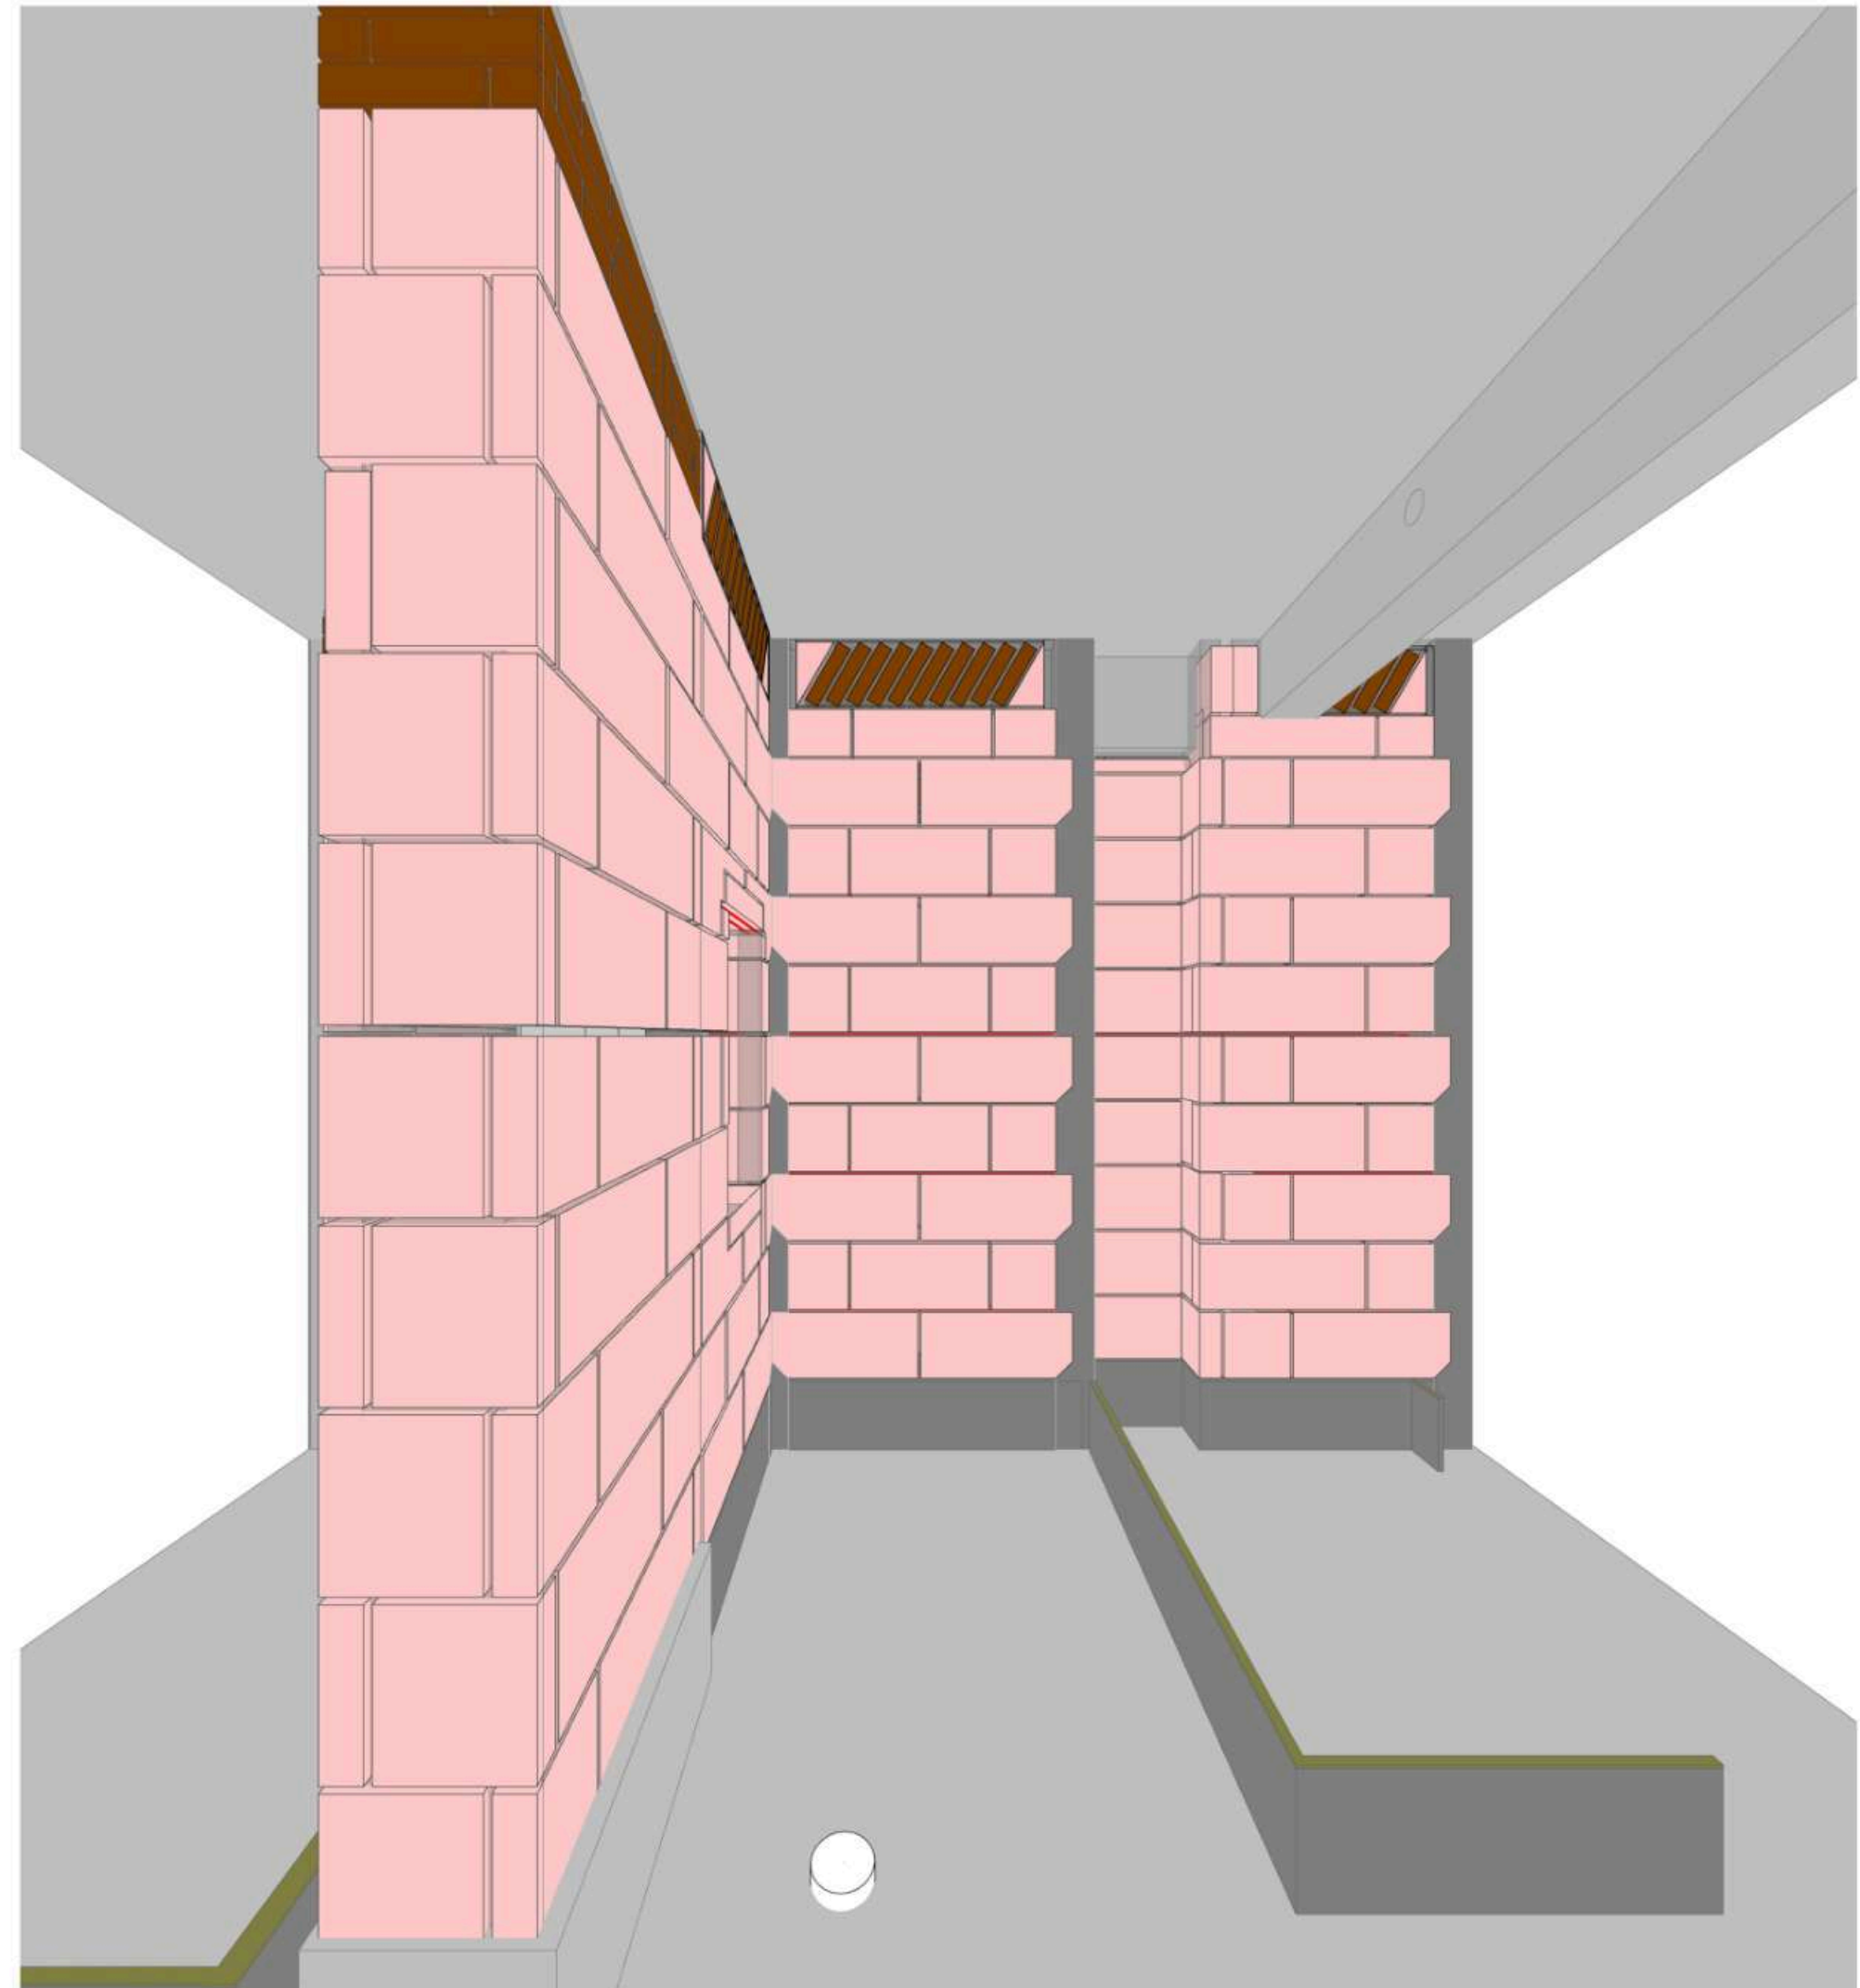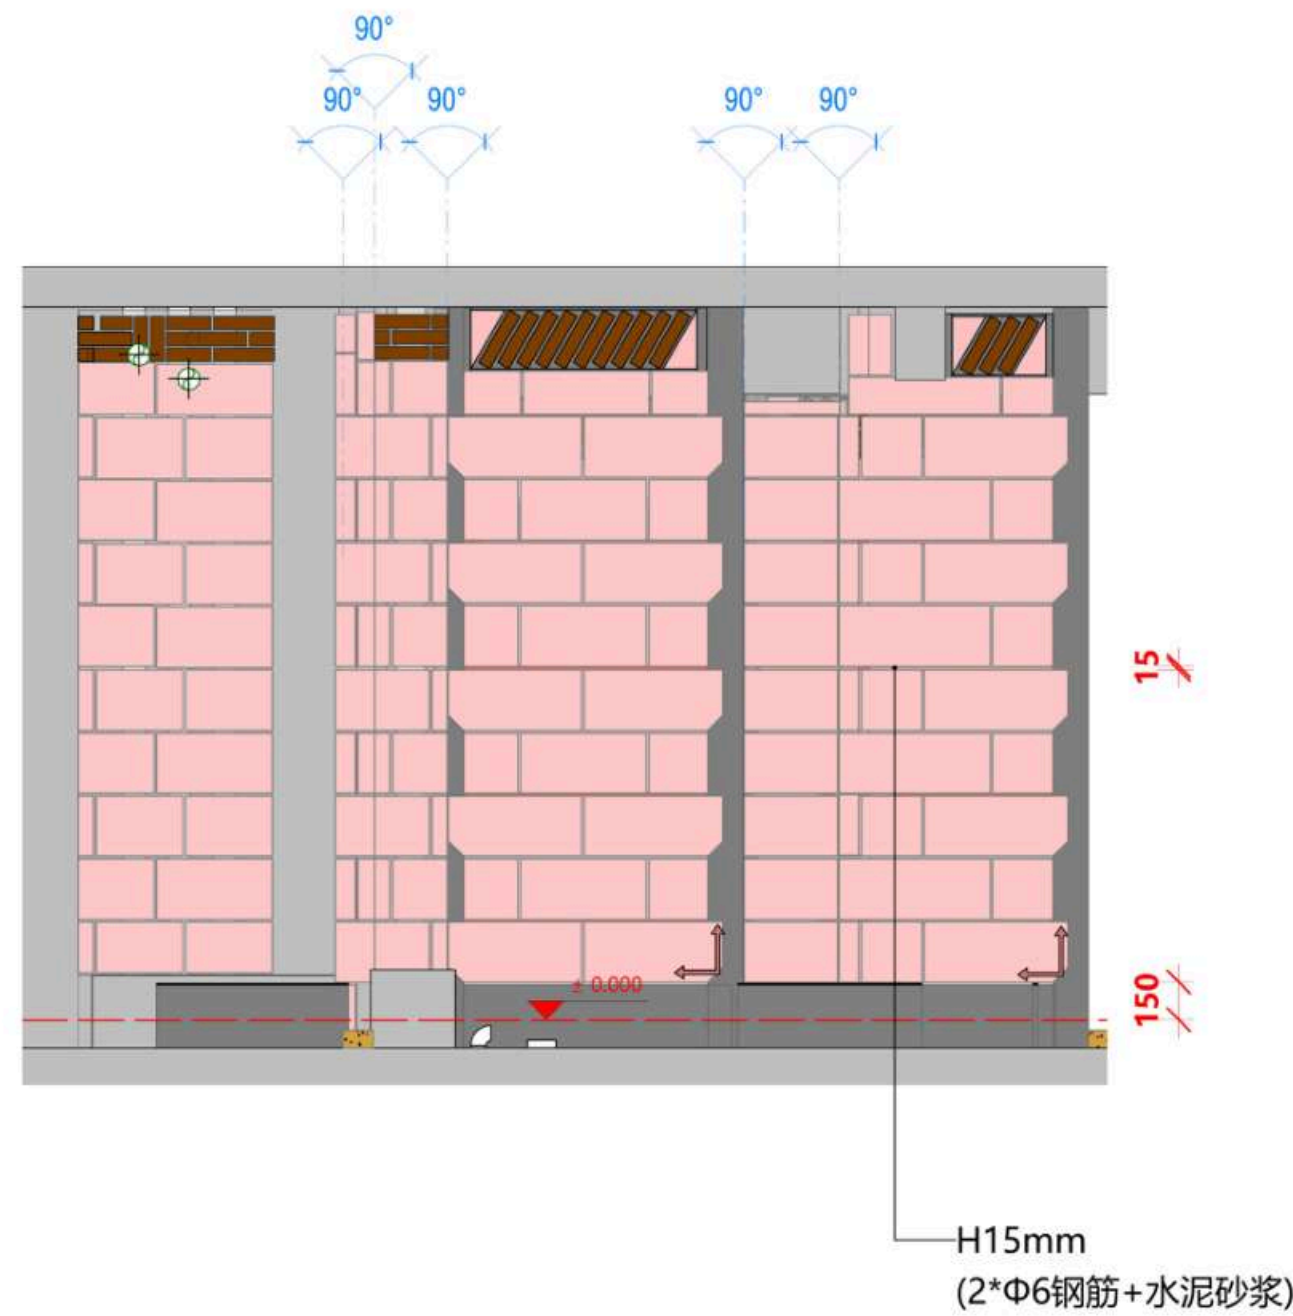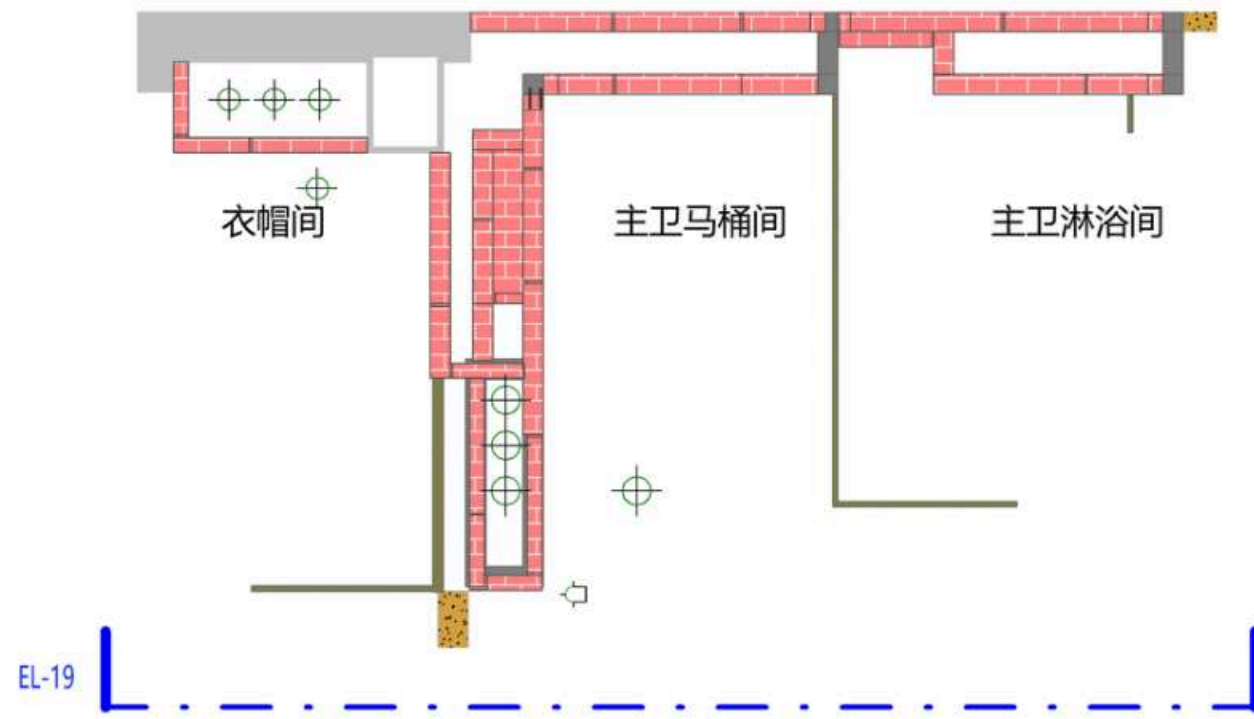

ELBORNI

LEGEND图例

图例A 材质分类		
编号	图例	说明
1		原始墙、板、柱
2		混凝土导墙、结构柱、马牙槎
3		PC砖
4		红砖
5		钢架墙
6		止水坎
7		混凝土止水坎上加5mm钢板

图例B 施工时注意事项		
编号	图例	说明
1		地面完成线
2		必要尺寸
3		起铺点
4		错峰要求 $a \geq 200$ $b \geq 150$
5		边砖宽度要求 $a \geq 200$
6		$b < 150$ 时 $a = b$

日期
Date

01/08/26

修订
Revision

项目
Project

潮映华府3-801

Scale
比例

1:30@A2

正式施工图

2026-01-27

PC砖墙19

Drawing No.
图纸编号

21-PCW-19

Project No.
项目编号

©2025

1

PC砖墙立面图19

EL-19

Scale比例 1 : 30@A2



1

PC砖墙三维示意图19


Scale比例 1:30@A2

注释
Notes

1.本图纸如与现场尺寸有误差, 请施工人员与项目负责人联系。
2.施工前施工人员应认真查阅此图, 如有不明确尺寸, 按现场测量为准。
3.本图纸必须经甲乙双方认可并签字方可作为施工依据。

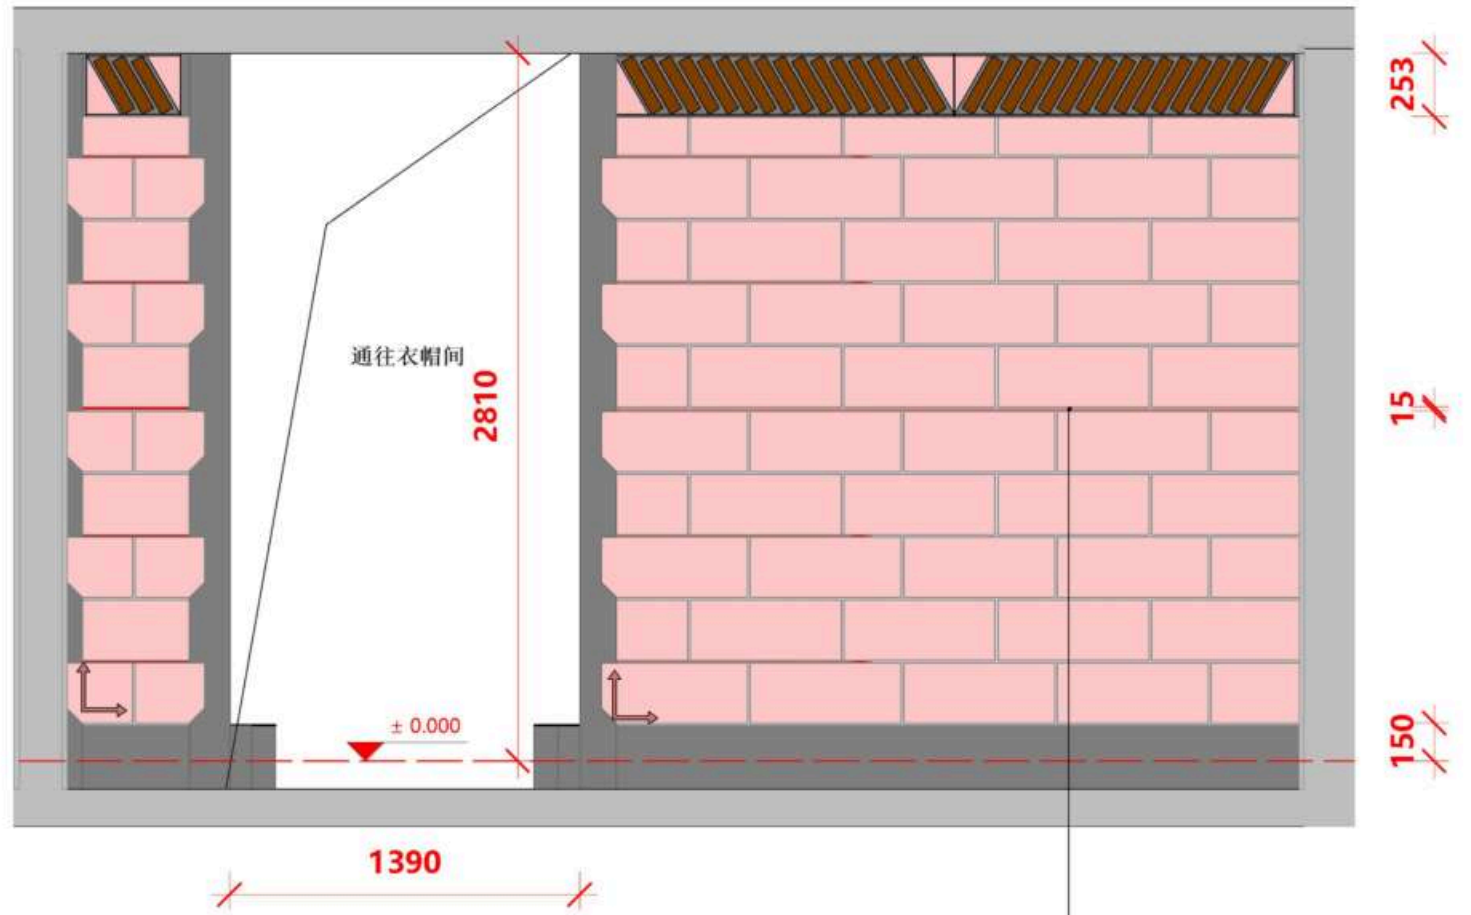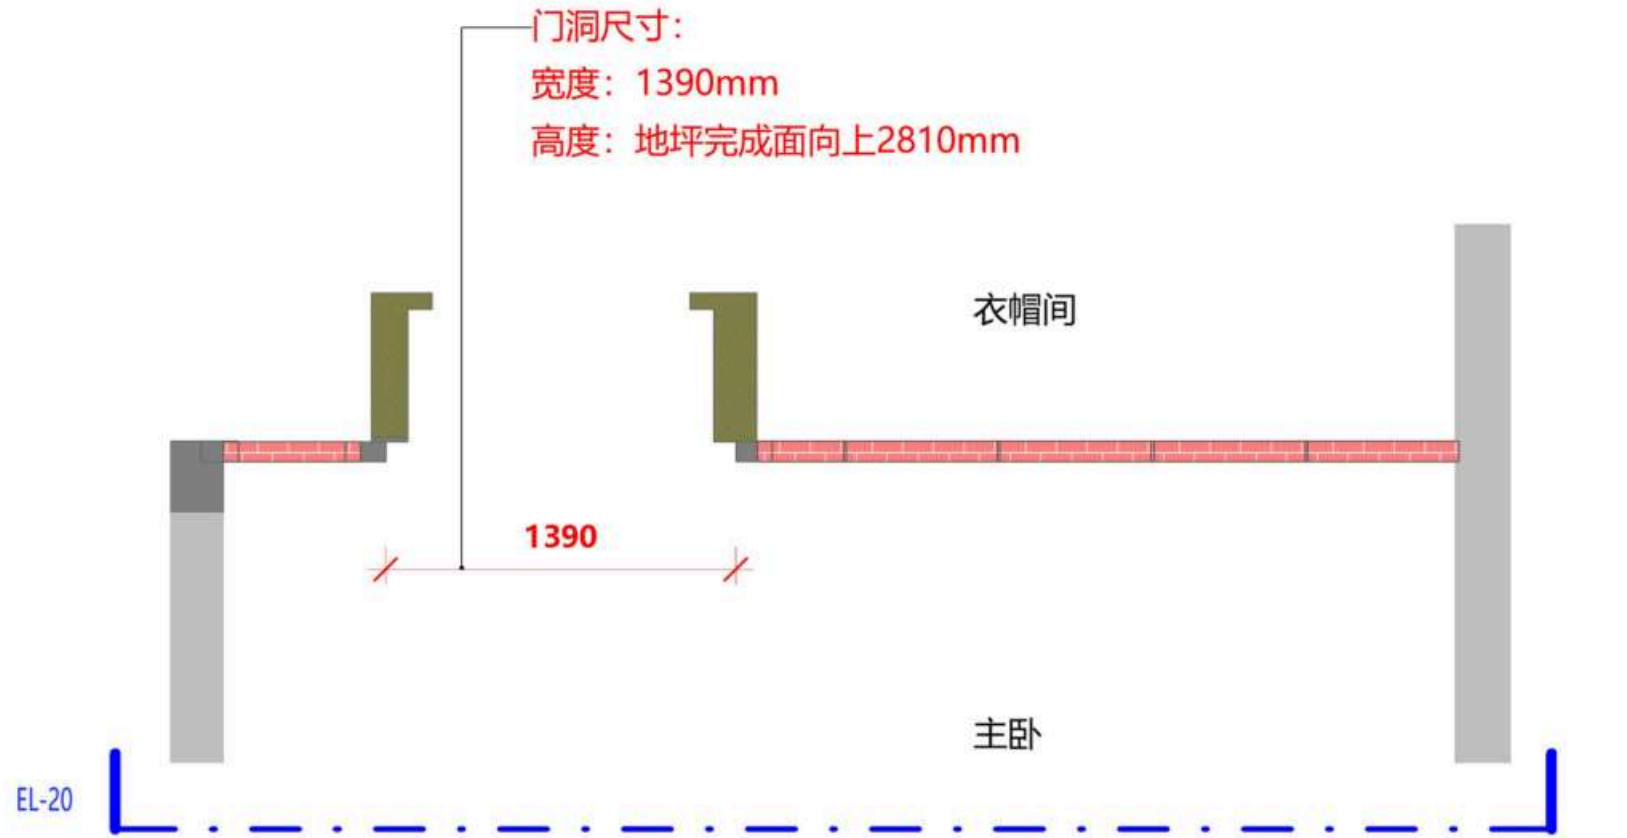

H15mm
(2*Φ6钢筋+水泥砂浆)

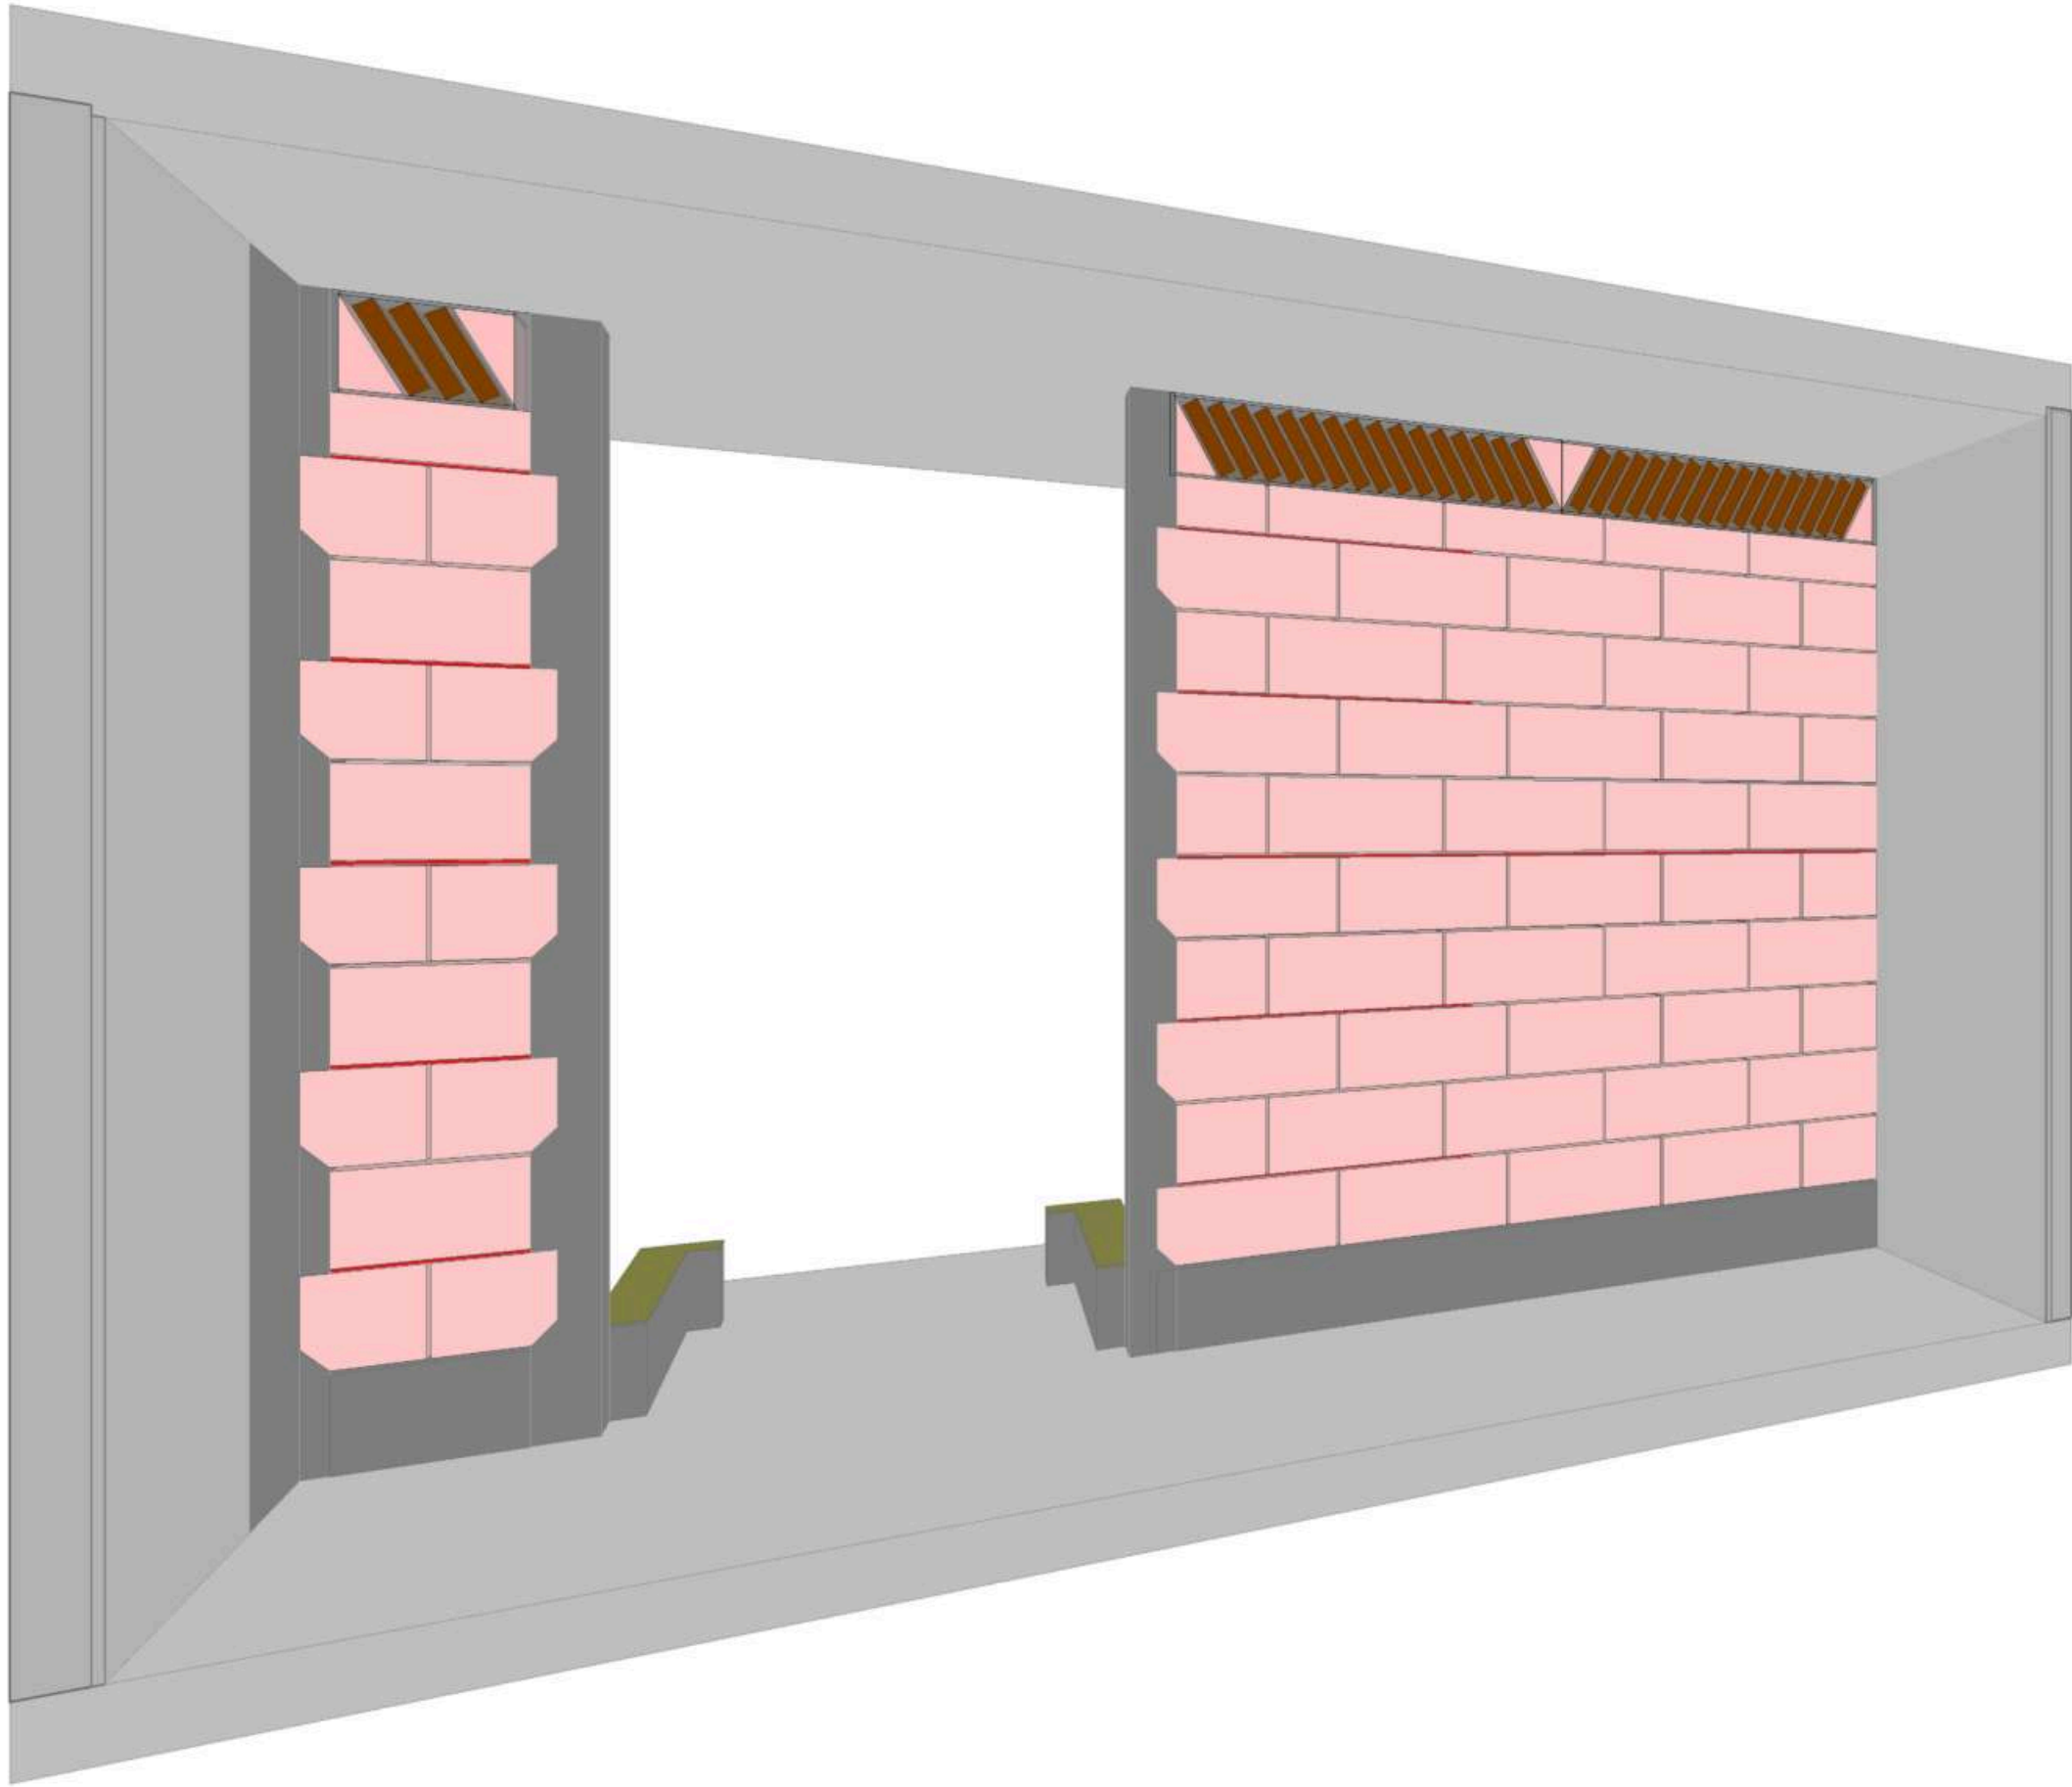

ELBORNI

LEGEND图例

图例A 材质分类		
编号	图例	说明
1		原始墙、板、柱
2		混凝土导墙、结构柱、马牙槎
3		PC砖
4		红砖
5		钢架墙
6		止水坎
7		混凝土止水坎上加5mm钢板

图例B 施工时注意事项		
编号	图例	说明
1		地面完成线
2		必要尺寸
3		起铺点
4		错缝要求 a≥200 b≥150
5		边砖宽度要求 a≥200
6		b < 150时 a = b

日期
Date 01/08/26

修订
Revision

项目
Project 潮映华府3-801

Scale
比例 1:30@A2

PC砖墙20

Drawing No.
图纸编号 22-PCW-20

Project No.
项目编号 ©2025

正式施工图
2026-01-27

PC砖墙三维示意图20

Scale比例 1:30@A2

注释
Notes
1.本图纸如与现场尺寸有误,请施工人员与项目负责人联系。
2.施工前施工人员应认真查阅此图,如有不明确尺寸,按现场测量为准。
3.本图纸必须经甲乙双方认可并签字方可作为施工依据。

PC砖墙立面图20




Scale比例 1 : 30@A2

1

3D-20

1

EL-20

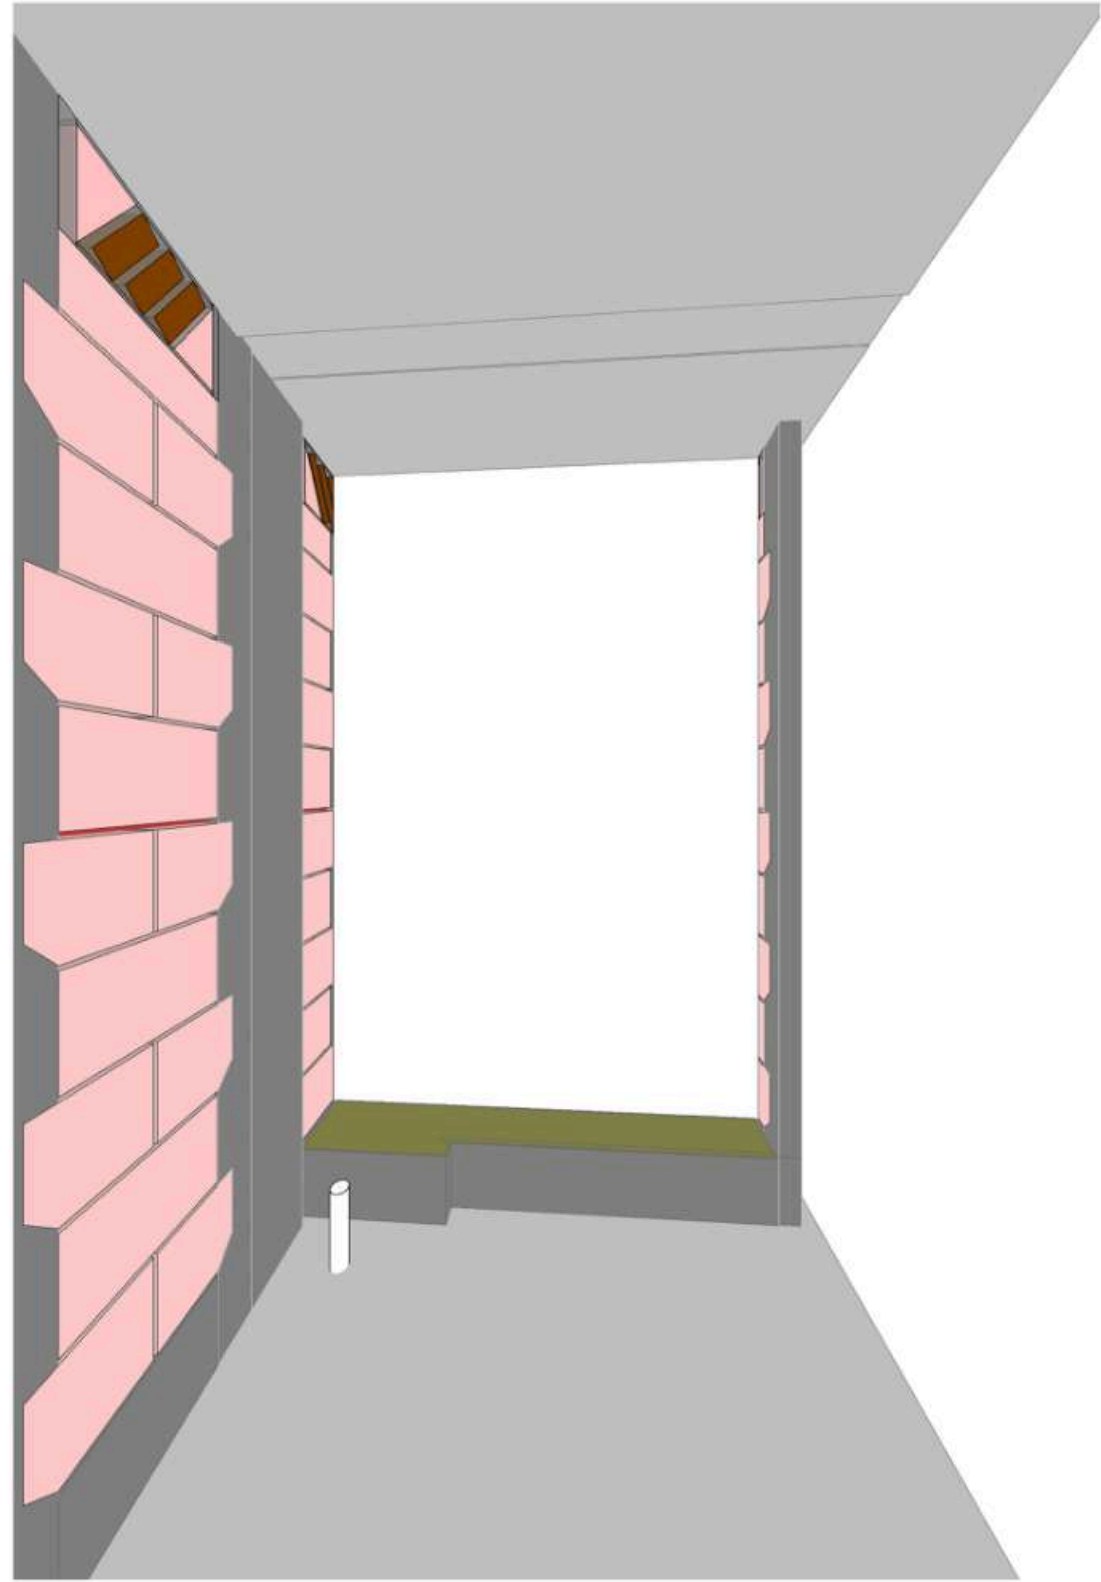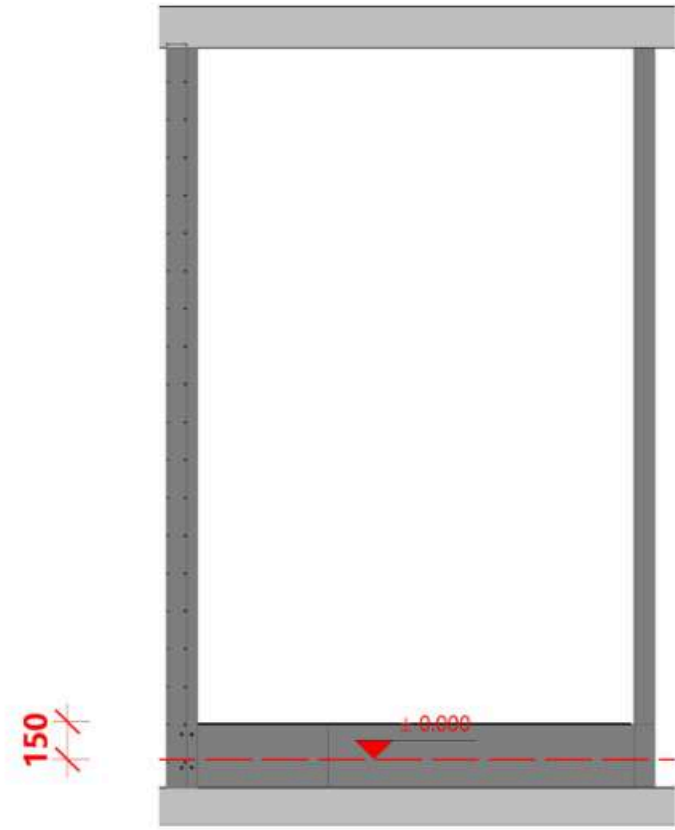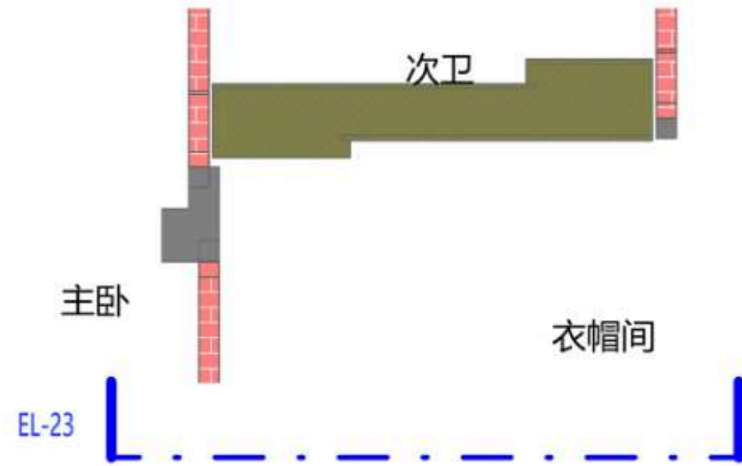

LEGEND图例

图例A 材质分类		
编号	图例	说明
1		原始墙、板、柱
2		混凝土导墙、结构柱、马牙槎
3		PC砖
4		红砖
5		钢架墙
6		止水坎
7		混凝土止水坎上加5mm钢板
图例B 施工时注意事项		
编号	图例	说明
1		地面完成线
2		必要尺寸
3		起铺点
4		错峰要求 $a \geq 200$ $b \geq 150$
5		边砖宽度要求 $a \geq 200$
6		$b < 150$ 时 $a = b$

日期
Date 01/11/26

修订
Revision

项目
Project

潮映华府3-801

Scale
比例 1:30@A2

PC砖墙23

Drawing No.
图纸编号

23-PCW-23

Project No.
项目编号

©2025

正式施工图

2026-01-27

PC砖墙立面图23

Scale比例 1 : 30@A2

1

3D-23




PC砖墙三维示意图23

Scale比例 1:30@A2

注释

Notes

- 1.本图纸如与现场尺寸有误，请施工人员与项目负责人联系。
- 2.施工前施工人员应认真查阅此图，如有不明确尺寸，按现场测量为准。
- 3.本图纸必须经甲乙双方认可并签字方可作为施工依据。

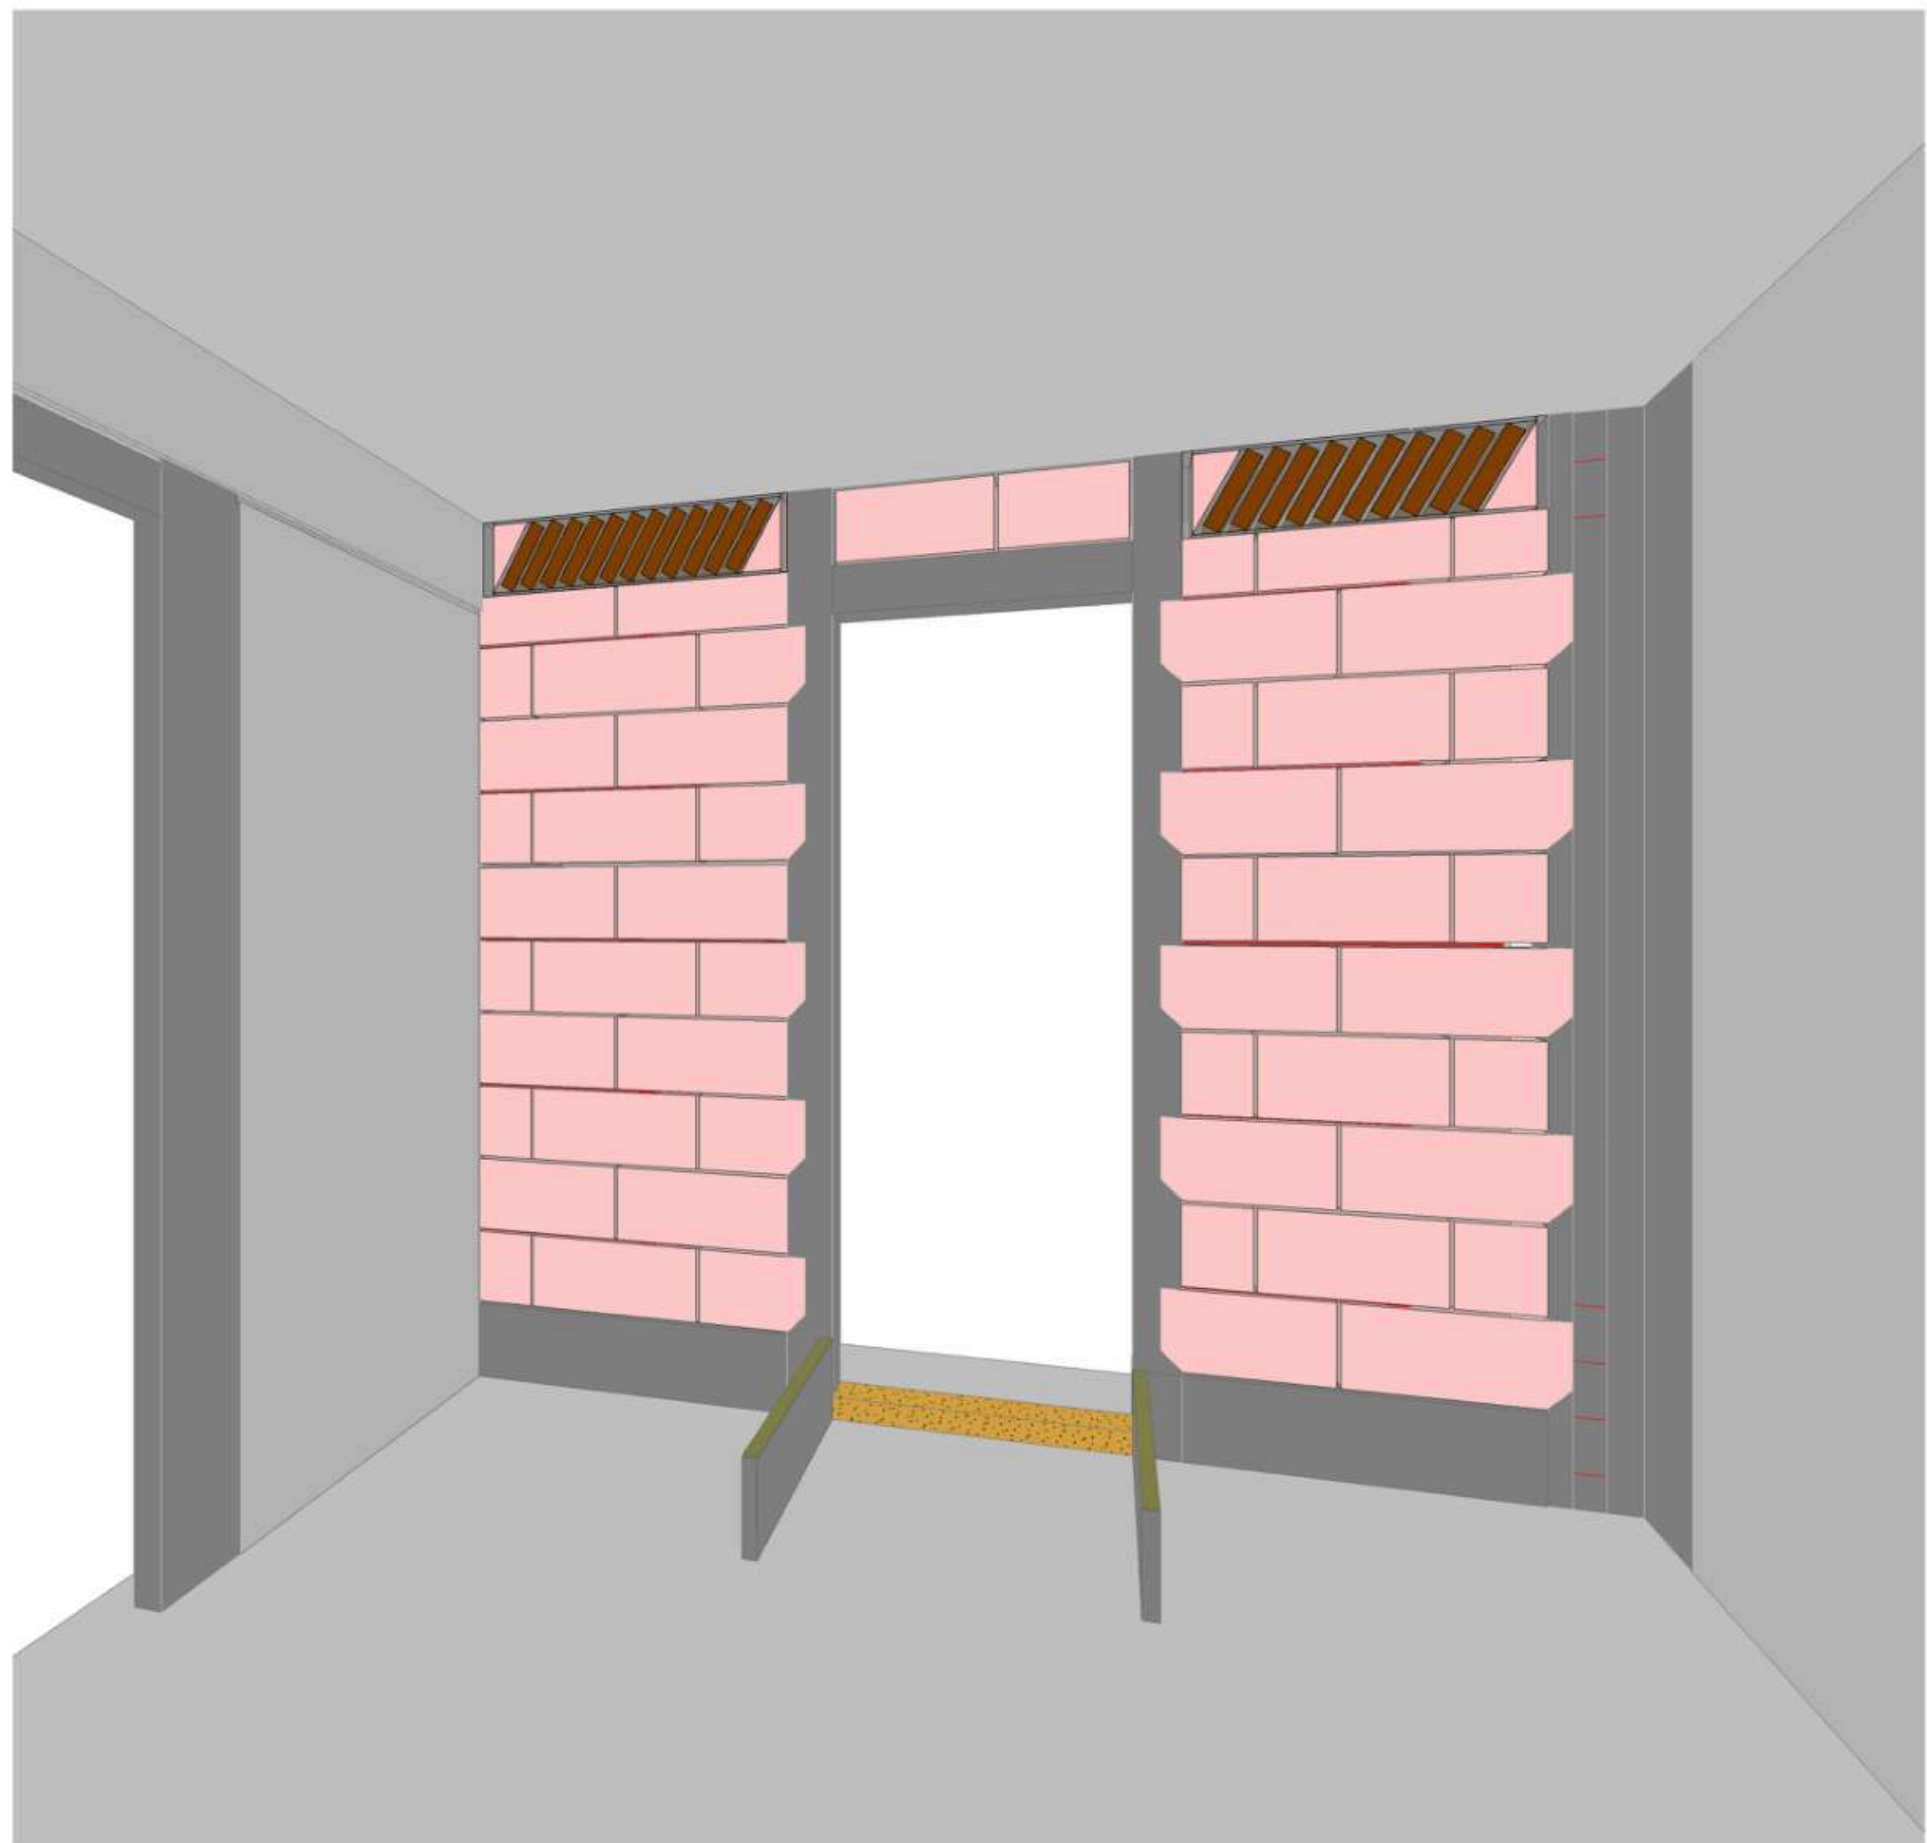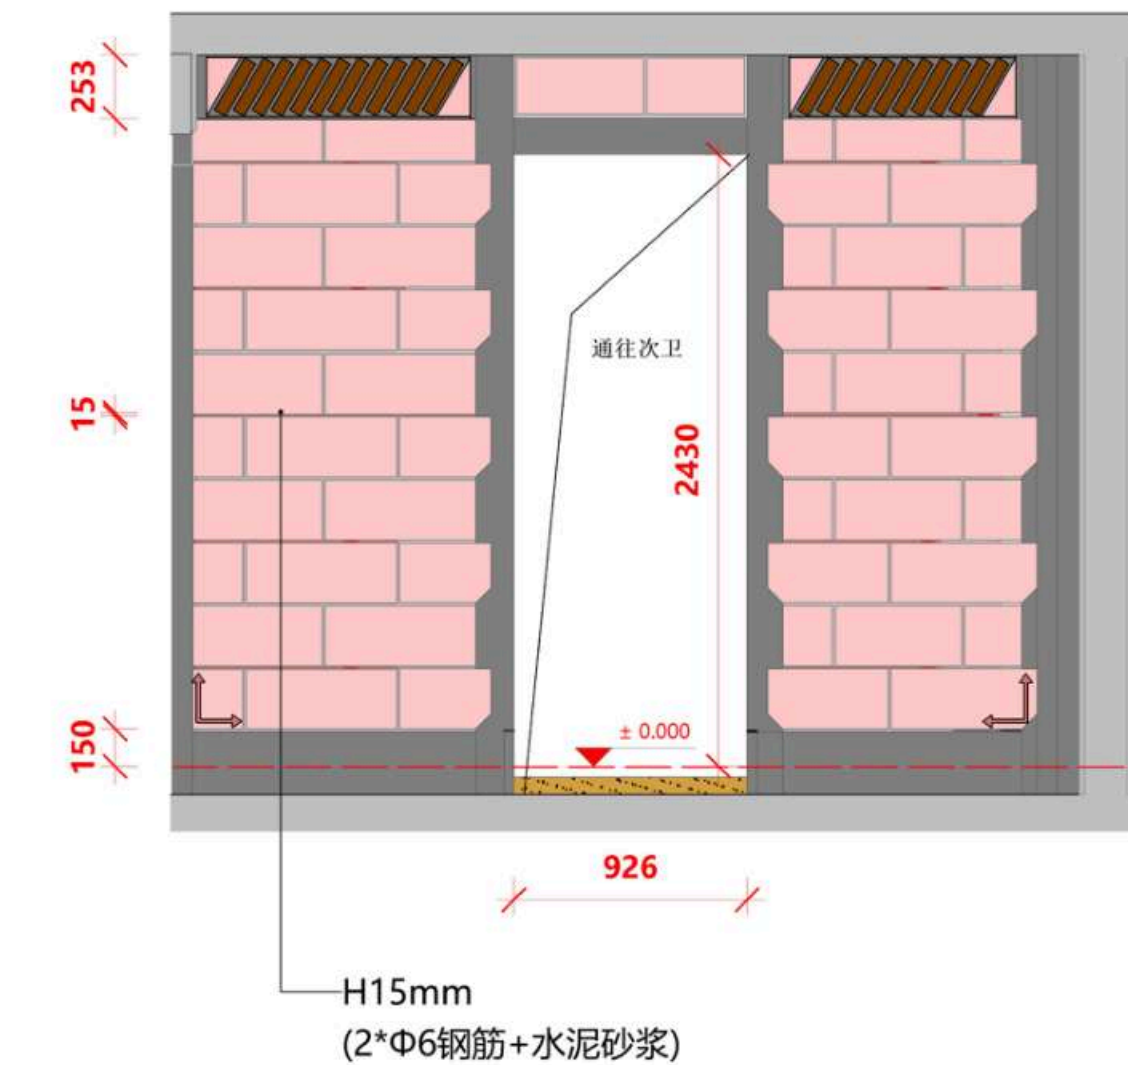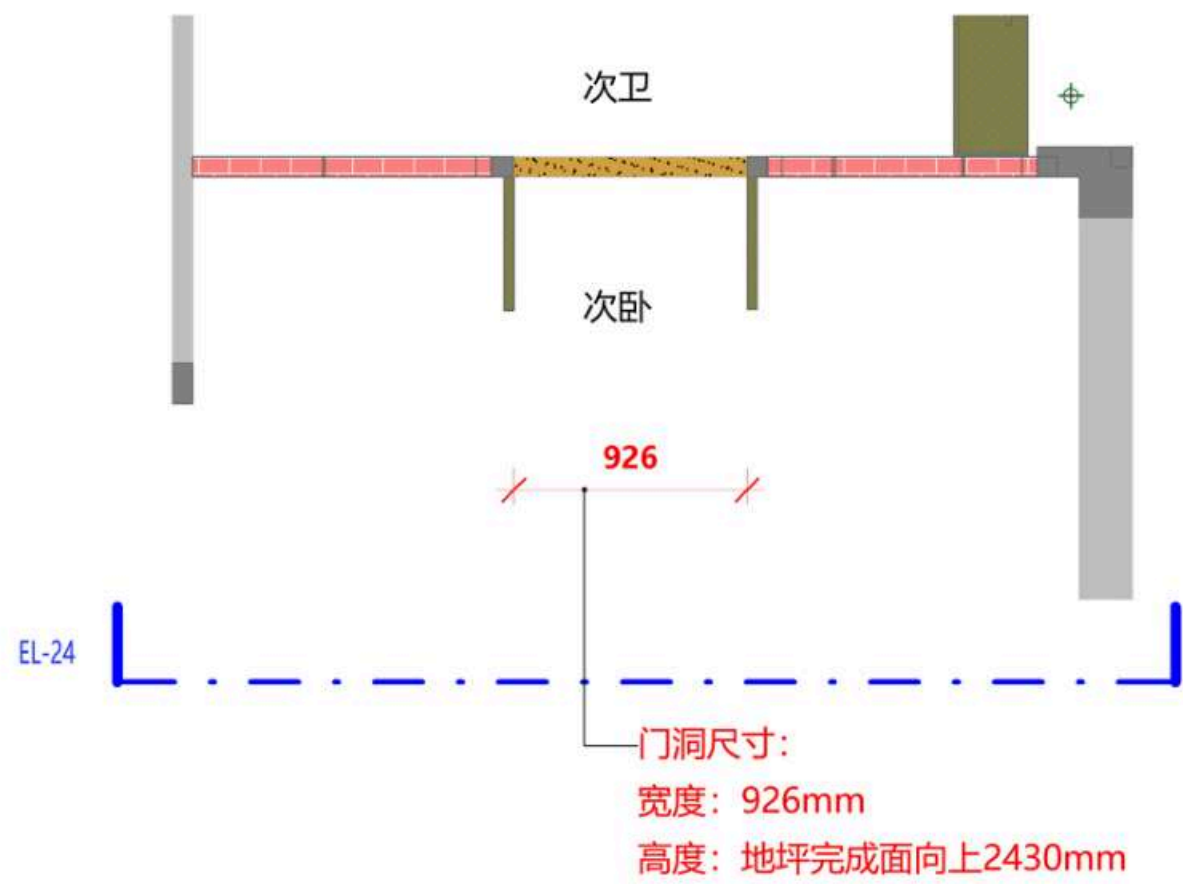

LEGEND图例

图例A 材质分类		
编号	图例	说明
1		原始墙、板、柱
2		混凝土导墙、结构柱、马牙槎
3		PC砖
4		红砖
5		钢架墙
6		止水坎
7		混凝土止水坎上加5mm钢板

图例B 施工时注意事项		
编号	图例	说明
1		地面完成线
2		必要尺寸
3		起铺点
4		错峰要求 $a \geq 200$ $b \geq 150$
5		边砖宽度要求 $a \geq 200$
6		$b < 150$ 时 $a = b$

日期
Date 01/11/26

修订
Revision



项目
Project
潮映华府3-801

Scale
比例 1:30@A2
PC砖墙24


Drawing No.
图纸编号
24-PCW-24

Project No.
项目编号
©2025

正式施工图
2026-01-27

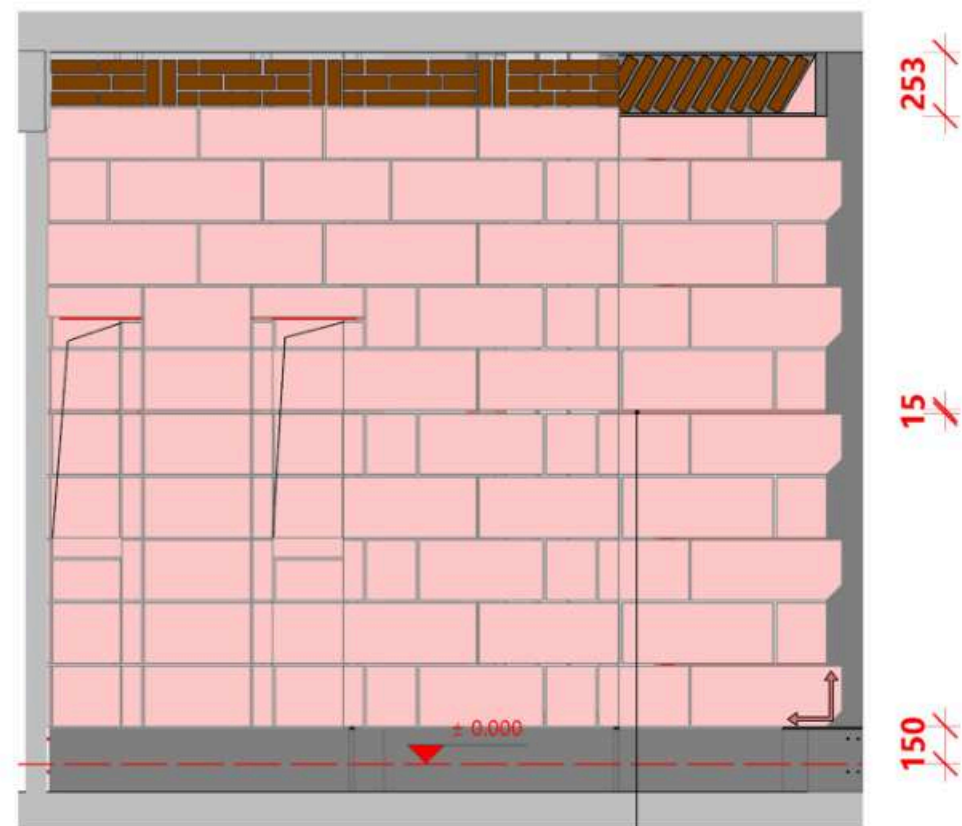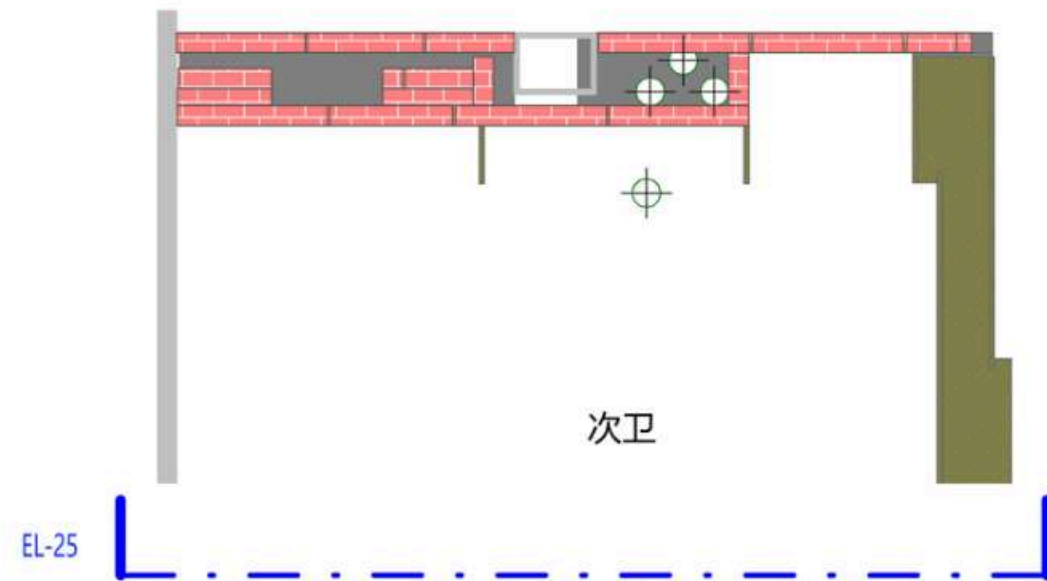

H15mm
(2*Φ6钢筋+水泥砂浆)

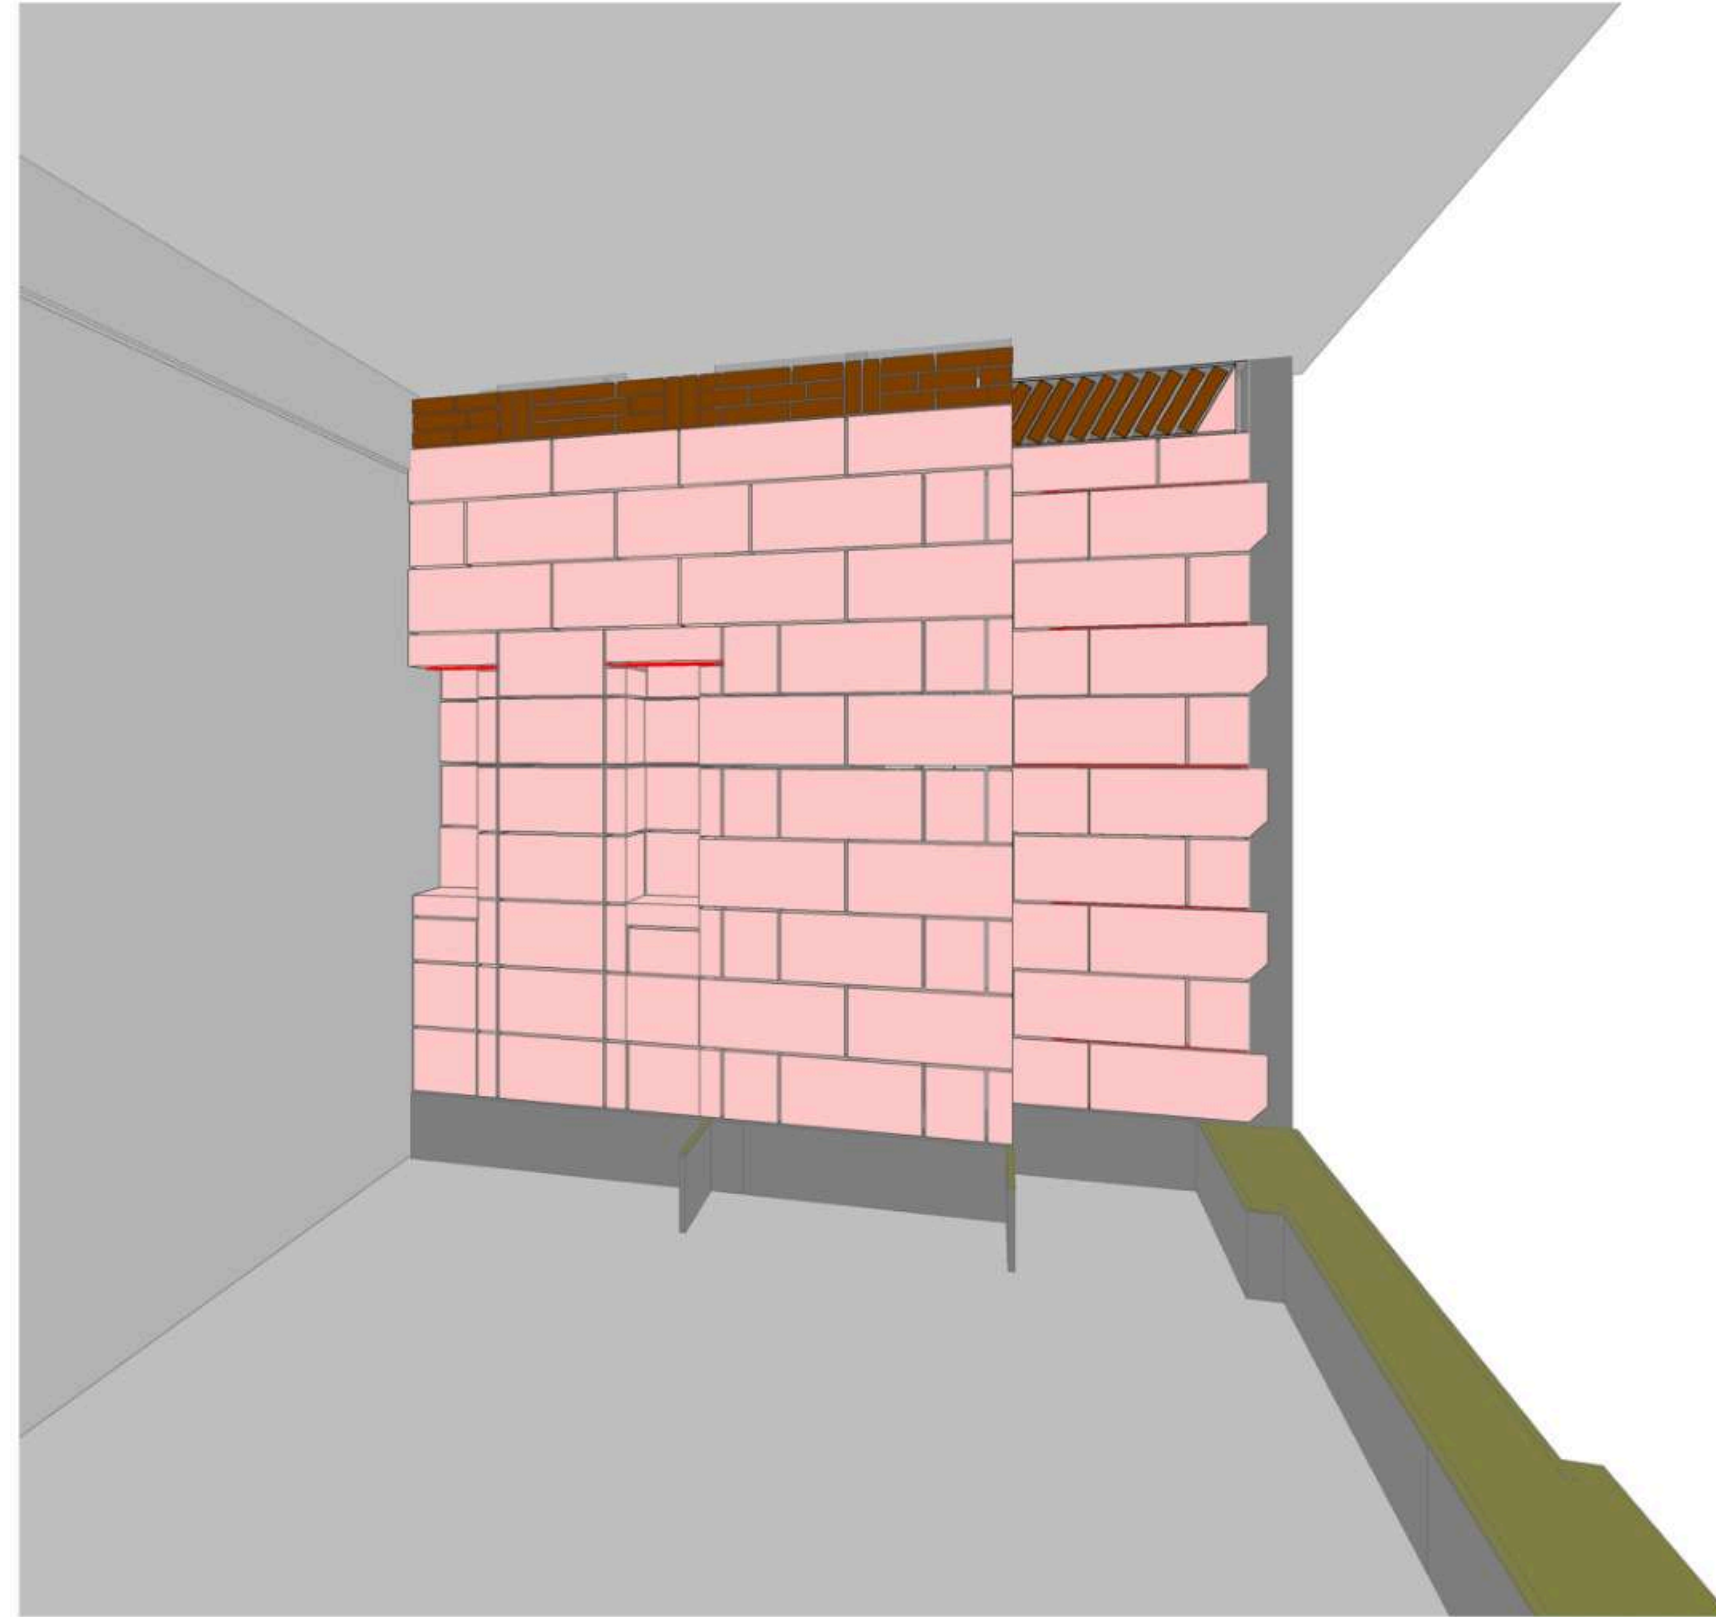

LEGEND图例

图例A 材质分类		
编号	图例	说明
1		原始墙、板、柱
2		混凝土导墙、结构柱、马牙槎
3		PC砖
4		红砖
5		钢架墙
6		止水坎
7		混凝土止水坎上加5mm钢板

图例B 施工时注意事项		
编号	图例	说明
1		地面完成线
2		必要尺寸
3		起铺点
4		错峰要求 $a \geq 200$ $b \geq 150$
5		边砖宽度要求 $a \geq 200$
6		$b < 150$ 时 $a = b$

日期
Date 01/11/26

修订
Revision

项目
Project

潮映华府3-801

Scale
比例 1:30@A2

PC砖墙25

Drawing No.
图纸编号

25-PCW-25

Project No.
项目编号

©2025

正式施工图

2026-01-27

1

EL-25

PC砖墙立面图25

Scale比例 1:30@A2

1


3D-25

PC砖墙三维示意图25

Scale比例 1:30@A2


注释
Notes

1.本图纸如与现场尺寸有误,请施工人员与项目负责人联系。
2.施工前施工人员应认真查阅此图,如有不明确尺寸,按现场测量为准。
3.本图纸必须经甲乙双方认可并签字方可作为施工依据。

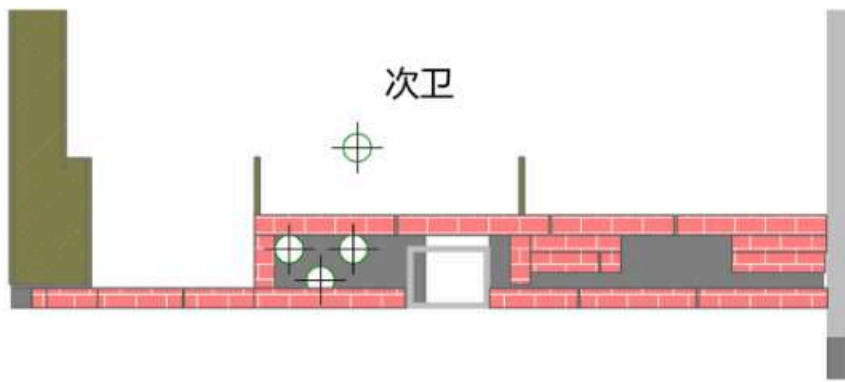


书房

EL-26

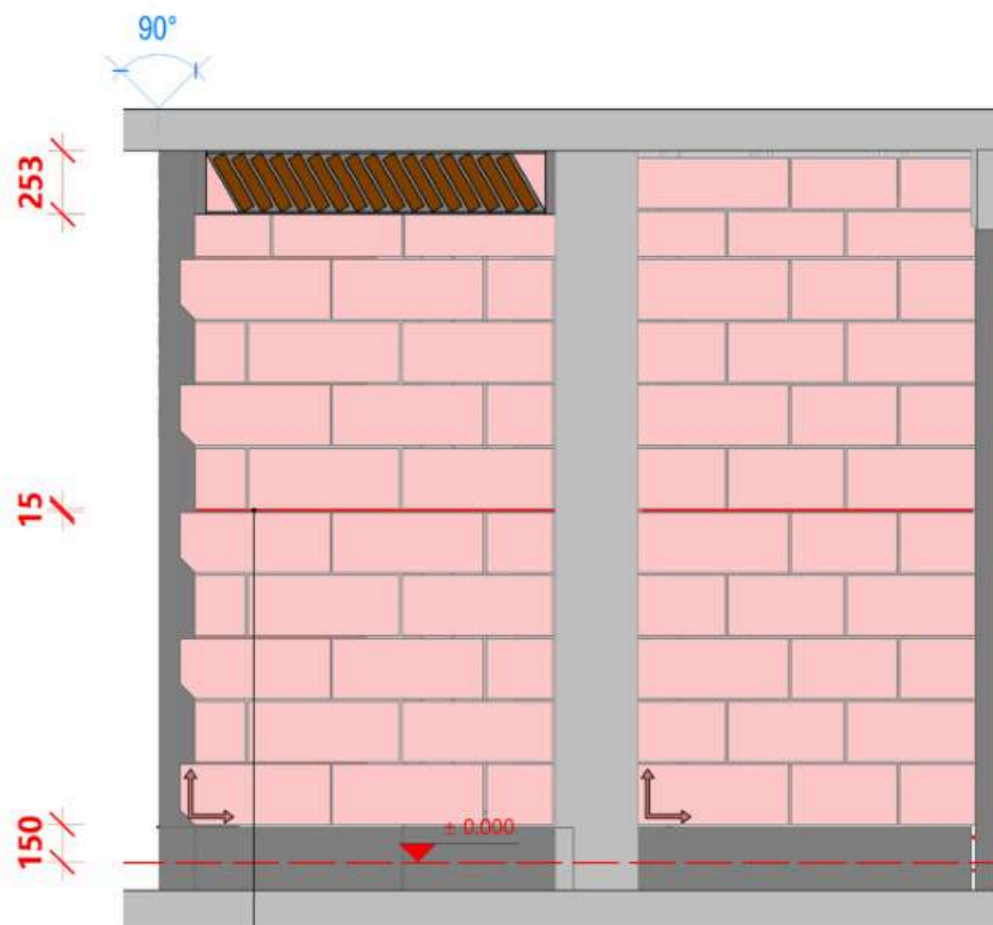

H15mm
(2*Φ6钢筋+水泥砂浆)

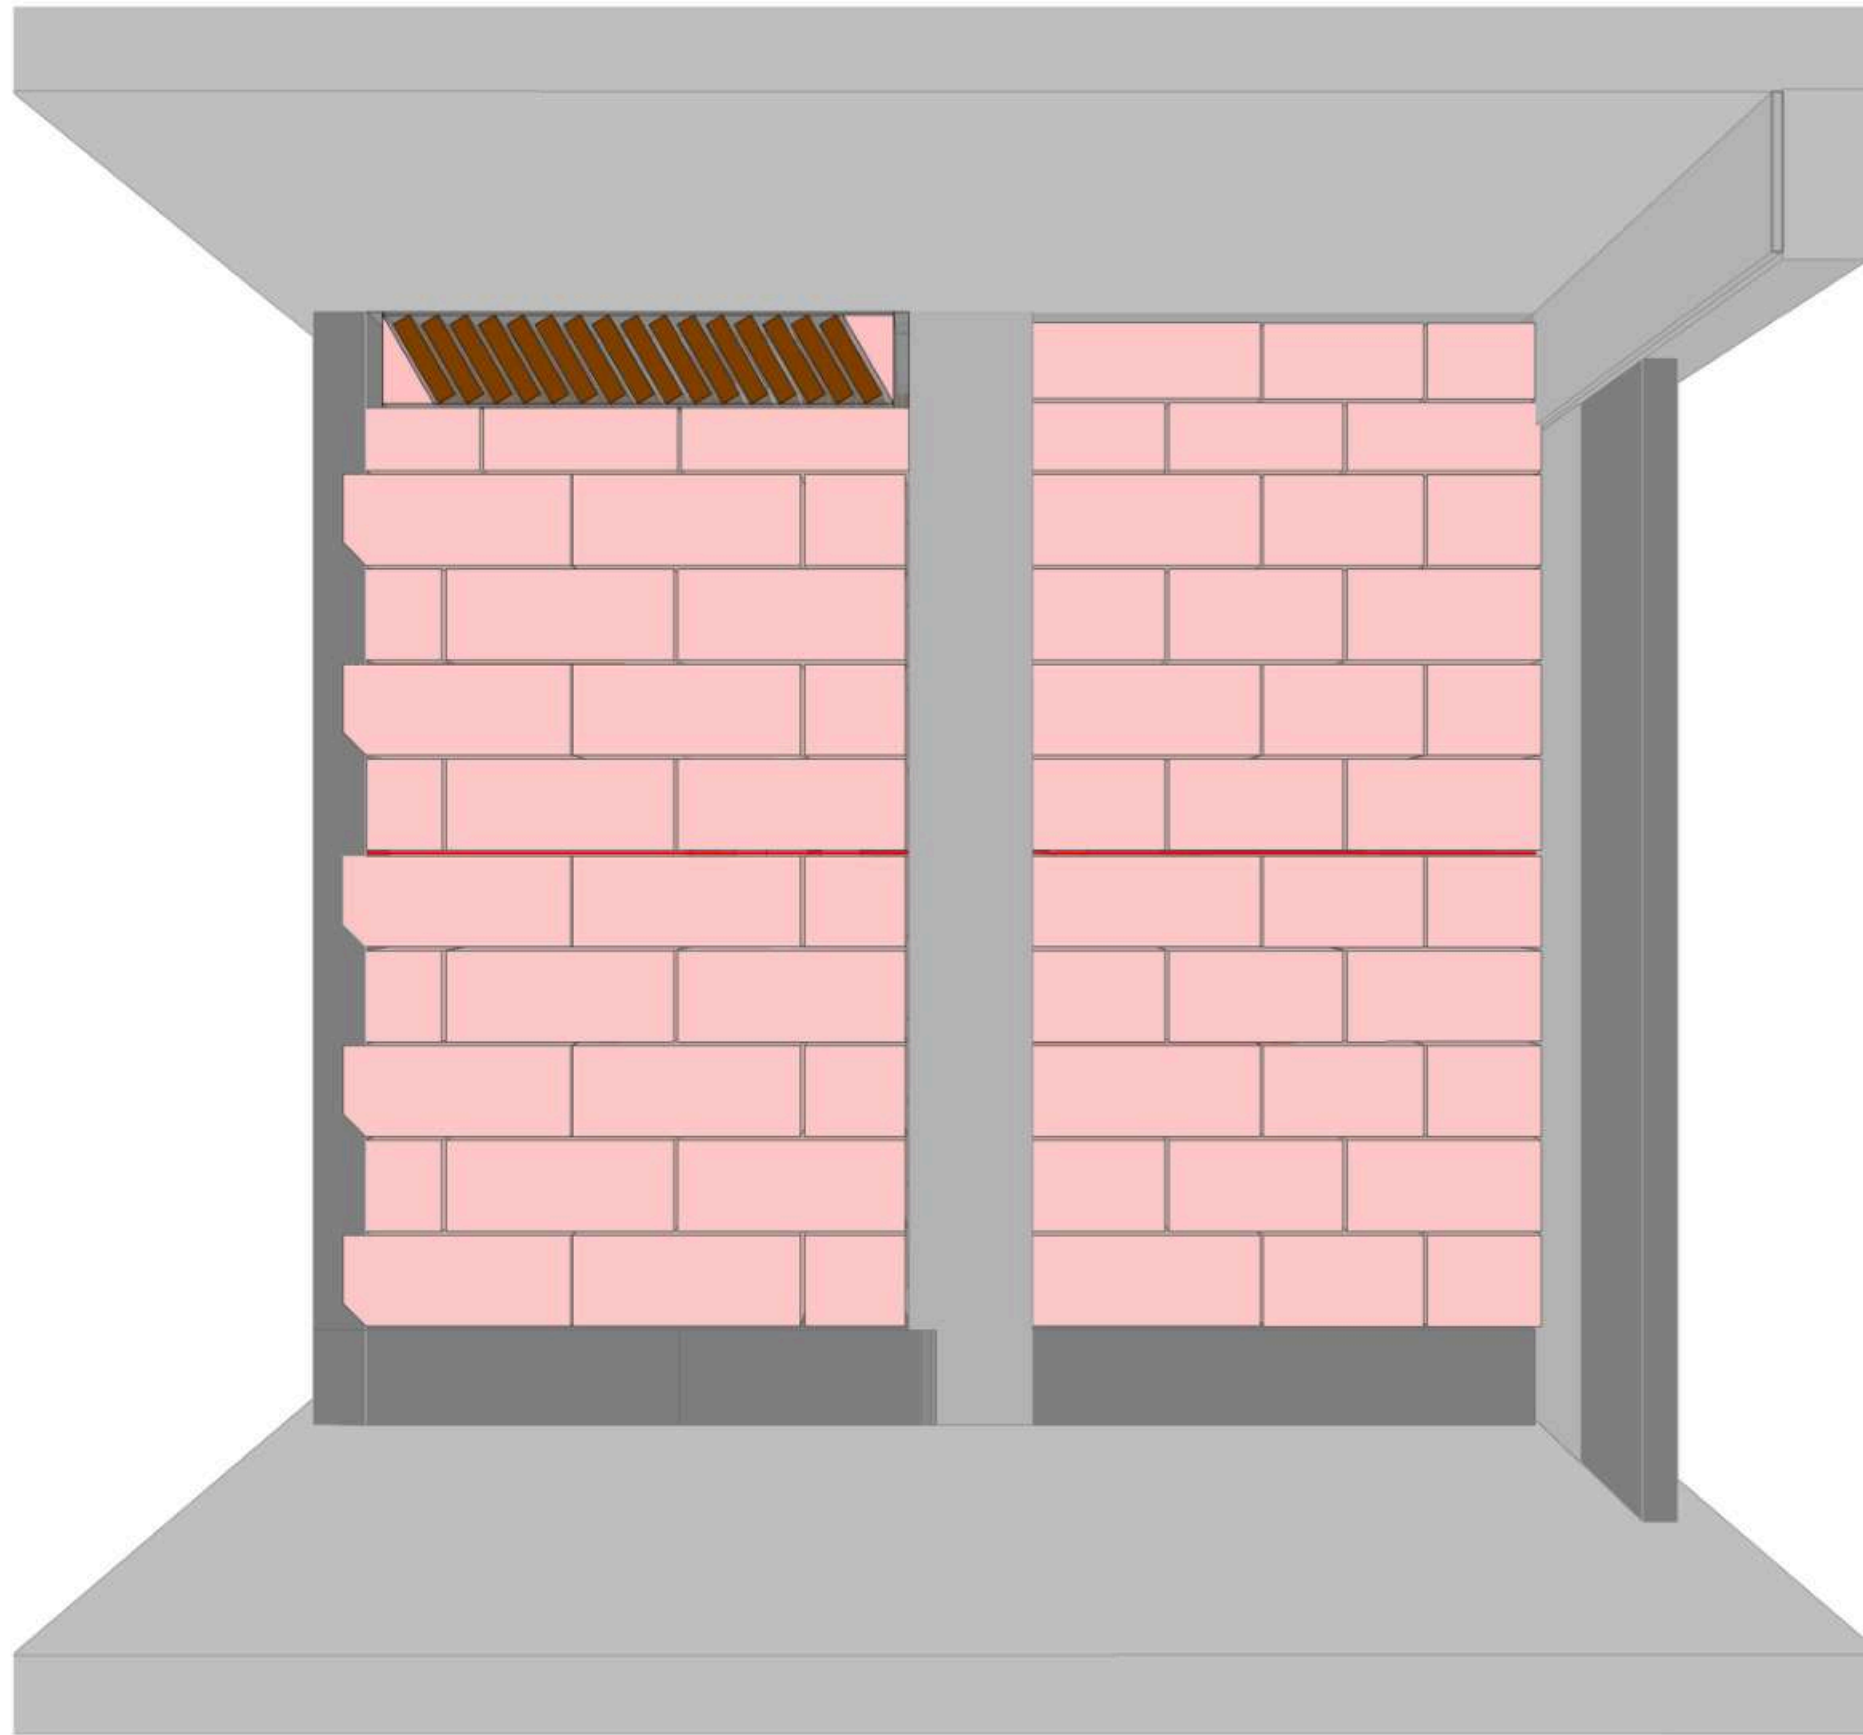

正式施工图
2026-01-27

ELIBORNI

LEGEND图例

图例A 材质分类		
编号	图例	说明
1		原始墙、板、柱
2		混凝土导墙、结构柱、马牙槎
3		PC砖
4		红砖
5		钢架墙
6		止水坎
7		混凝土止水坎上加5mm钢板

图例B 施工时注意事项		
编号	图例	说明
1		地面完成线
2		必要尺寸
3		起铺点
4		错峰要求 $a \geq 200$ $b \geq 150$
5		边砖宽度要求 $a \geq 200$
6		$b < 150$ 时 $a = b$

日期
Date 01/11/26

修订
Revision

项目
Project

潮映华府3-801

Scale
比例 1:30@A2

PC砖墙26

Drawing No.
图纸编号

26-PCW-26

Project No.
项目编号

©2025

1

EL-26

PC砖墙立面图26

Scale比例 1 : 30@A2

1

3D-26


PC砖墙三维示意图26




Scale比例 1:30@A2

注释

Notes

- 1.本图纸如与现场尺寸有误，请施工人员与项目负责人联系。
- 2.施工前施工人员应认真查阅此图，如有不明确尺寸，按现场测量为准。
- 3.本图纸必须经甲乙双方认可并签字方可作为施工依据。

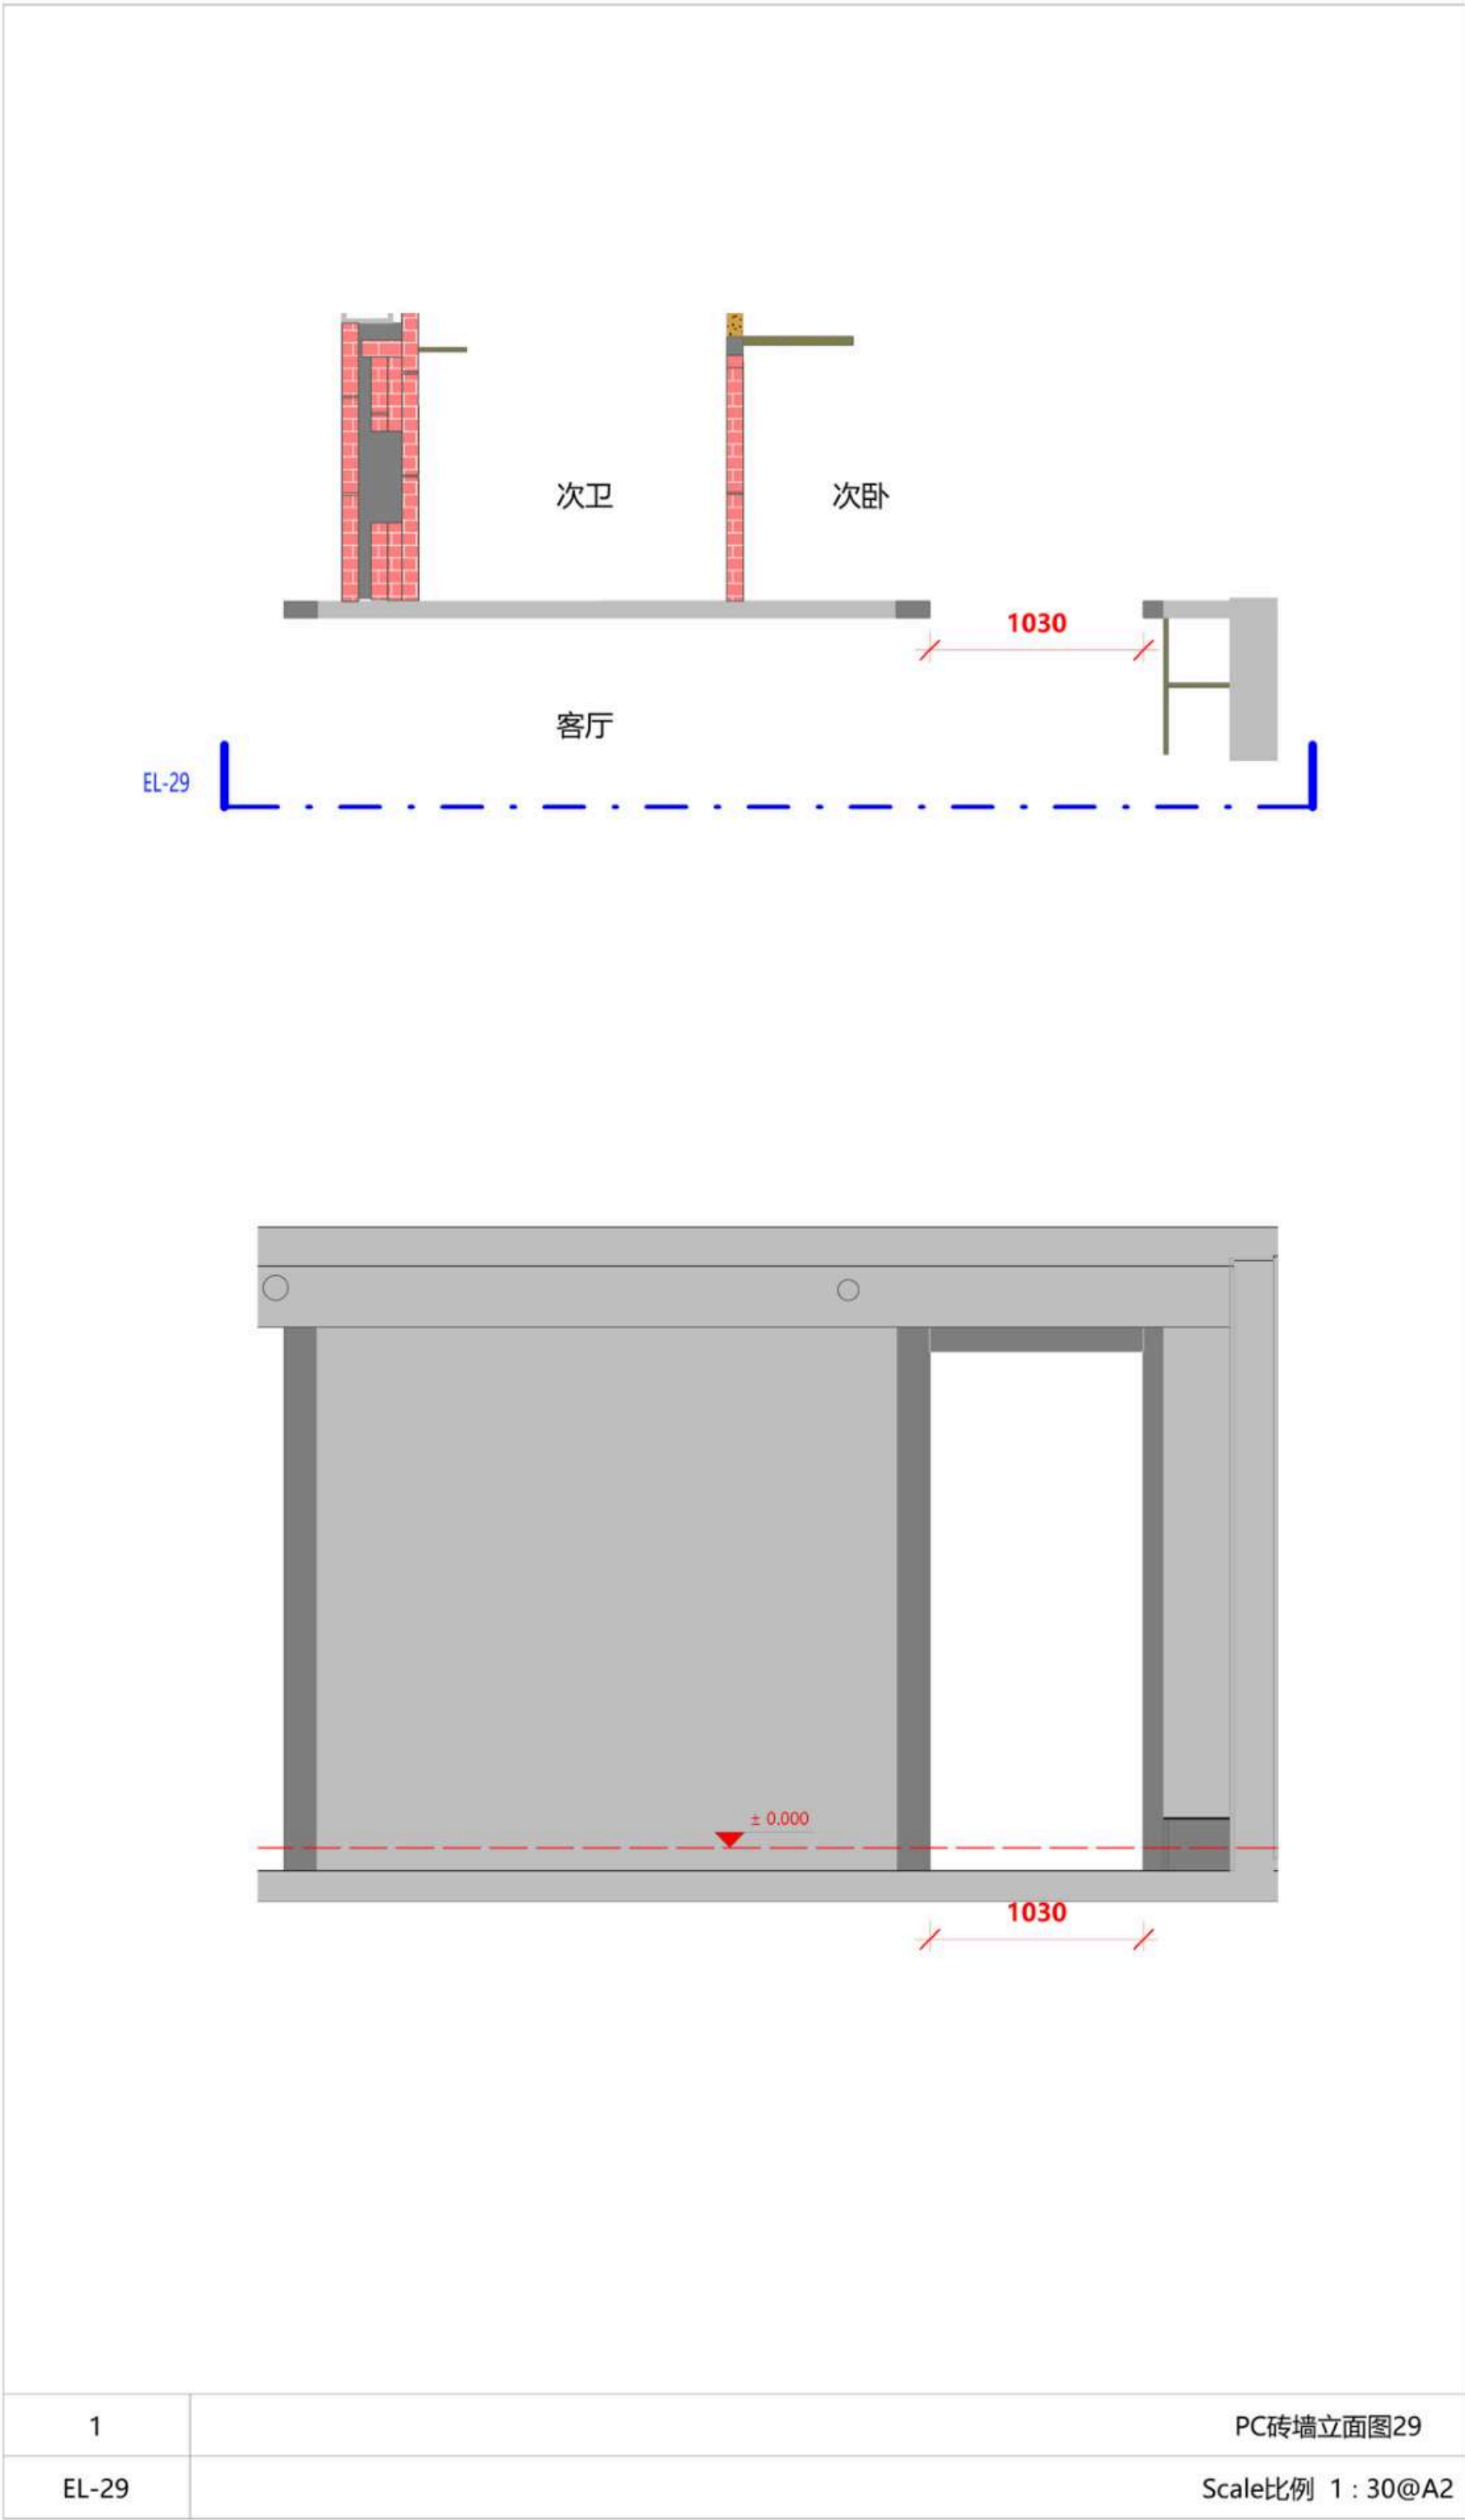

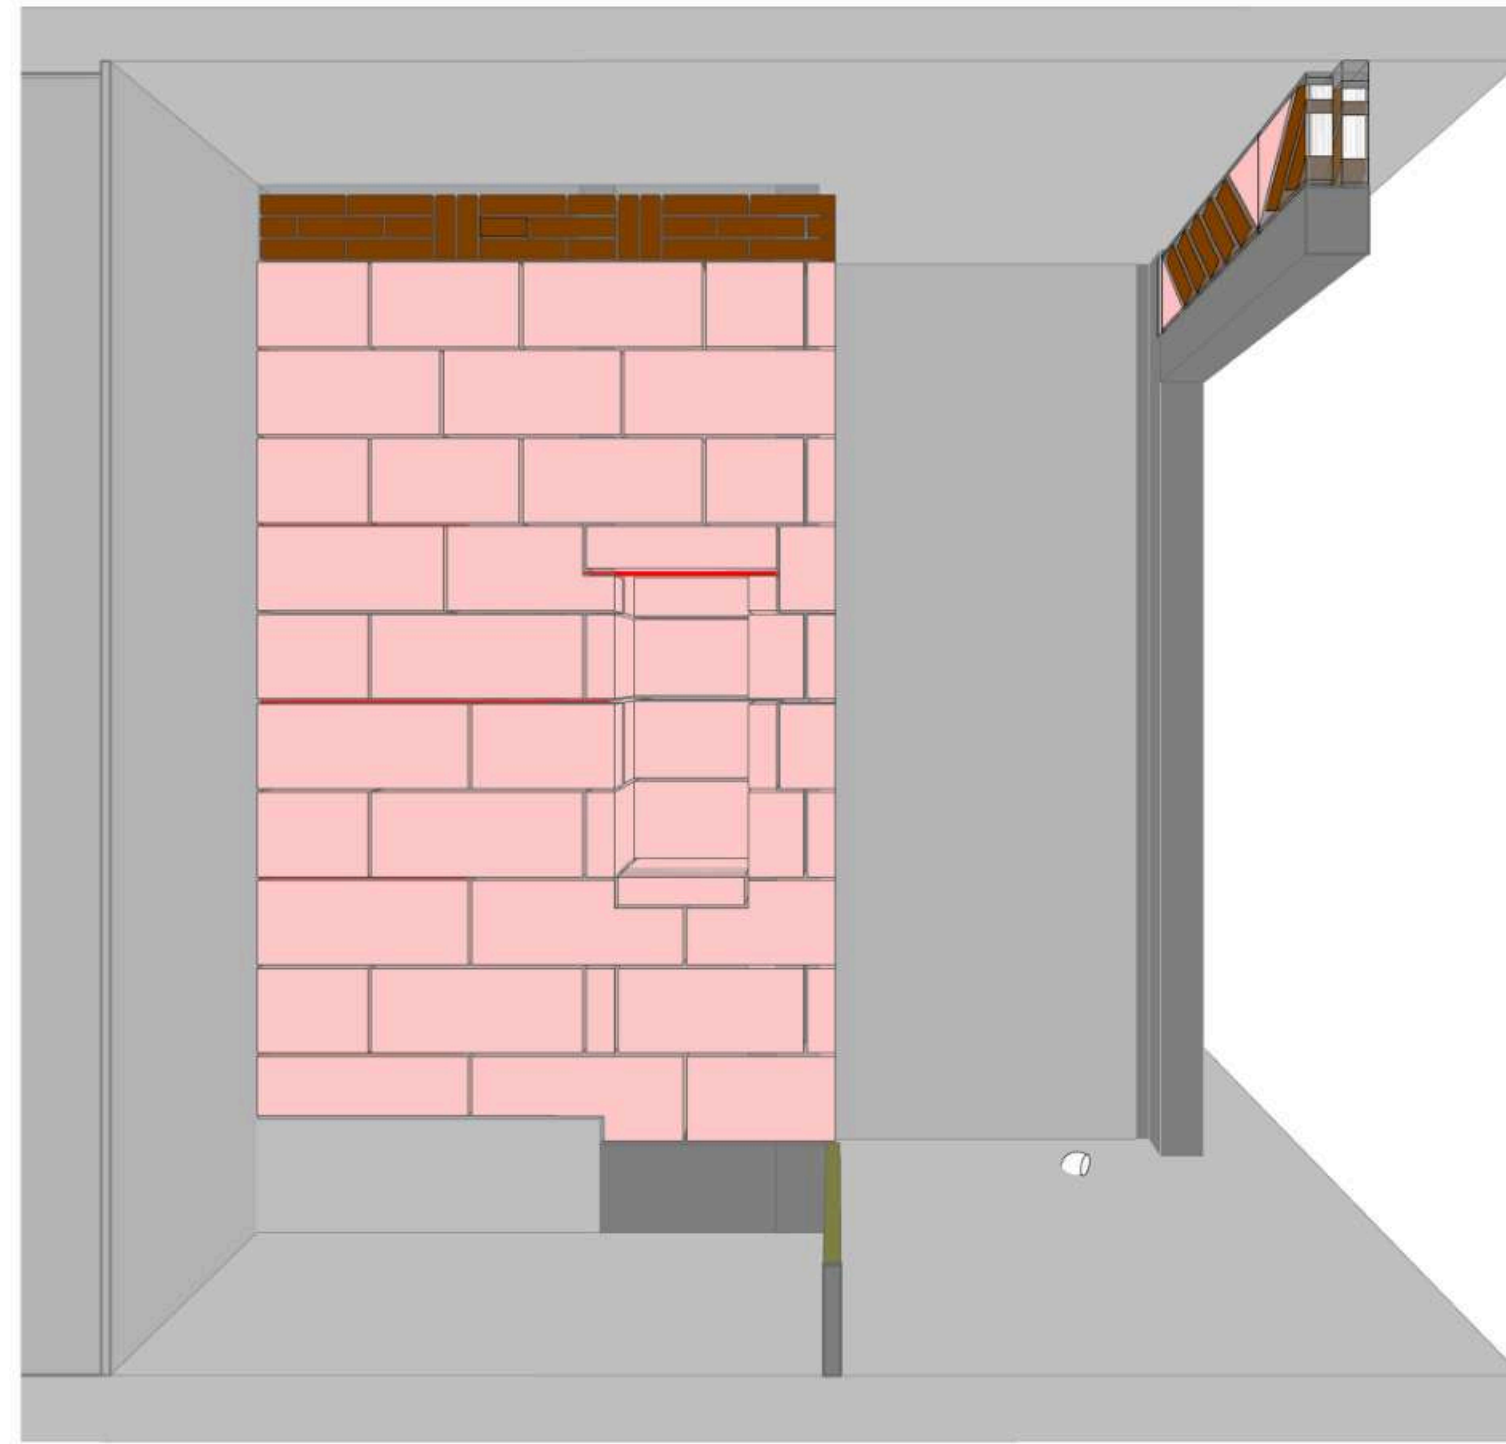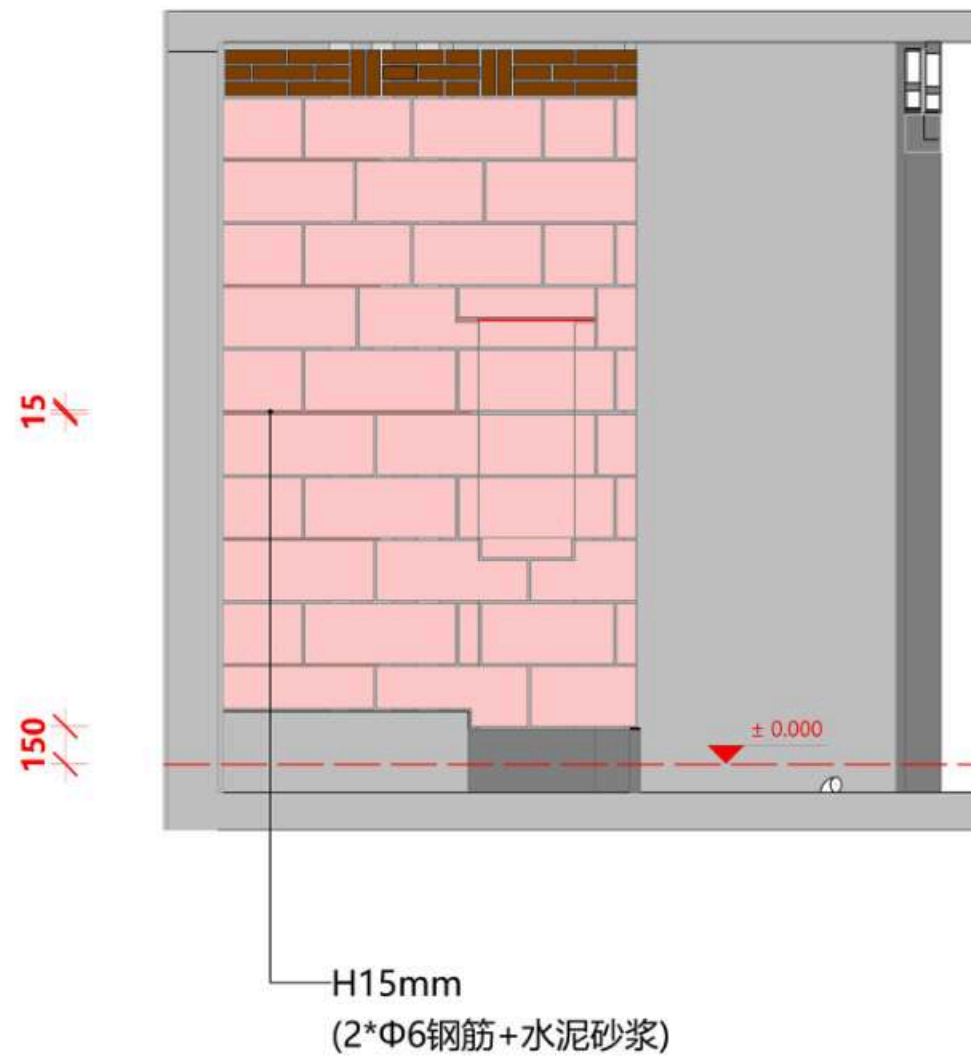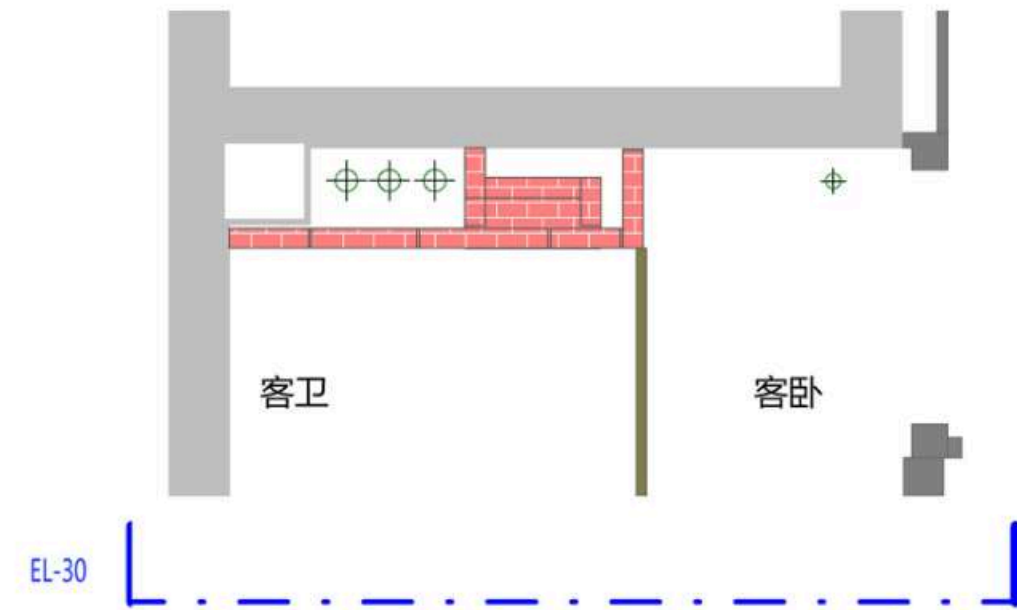

LEGEND图例

图例A 材质分类		
编号	图例	说明
1		原始墙、板、柱
2		混凝土导墙、结构柱、马牙槎
3		PC砖
4		红砖
5		钢架墙
6		止水坎
7		混凝土止水坎上加5mm钢板

图例B 施工时注意事项		
编号	图例	说明
1		地面完成线
2		必要尺寸
3		起铺点
4		错峰要求 $a \geq 200$ $b \geq 150$
5		边砖宽度要求 $a \geq 200$
6		$b < 150$ 时 $a = b$

日期
Date01/11/26修订
Revision项目
Project
潮映华府3-801Scale
比例1:30@A2
PC砖墙30Drawing No.
图纸编号
28-PCW-30Project No.
项目编号
©2025正式施工图
2026-01-27

PC砖墙立面图30

Scale比例 1 : 30@A2

1



3D-30

PC砖墙三维示意图30

Scale比例 1:30@A2

注释
Notes

- 1.本图纸如与现场尺寸有误，请施工人员与项目负责人联系。
- 2.施工前施工人员应认真查阅此图，如有不明确尺寸，按现场测量为准。
- 3.本图纸必须经甲乙双方认可并签字方可作为施工依据。

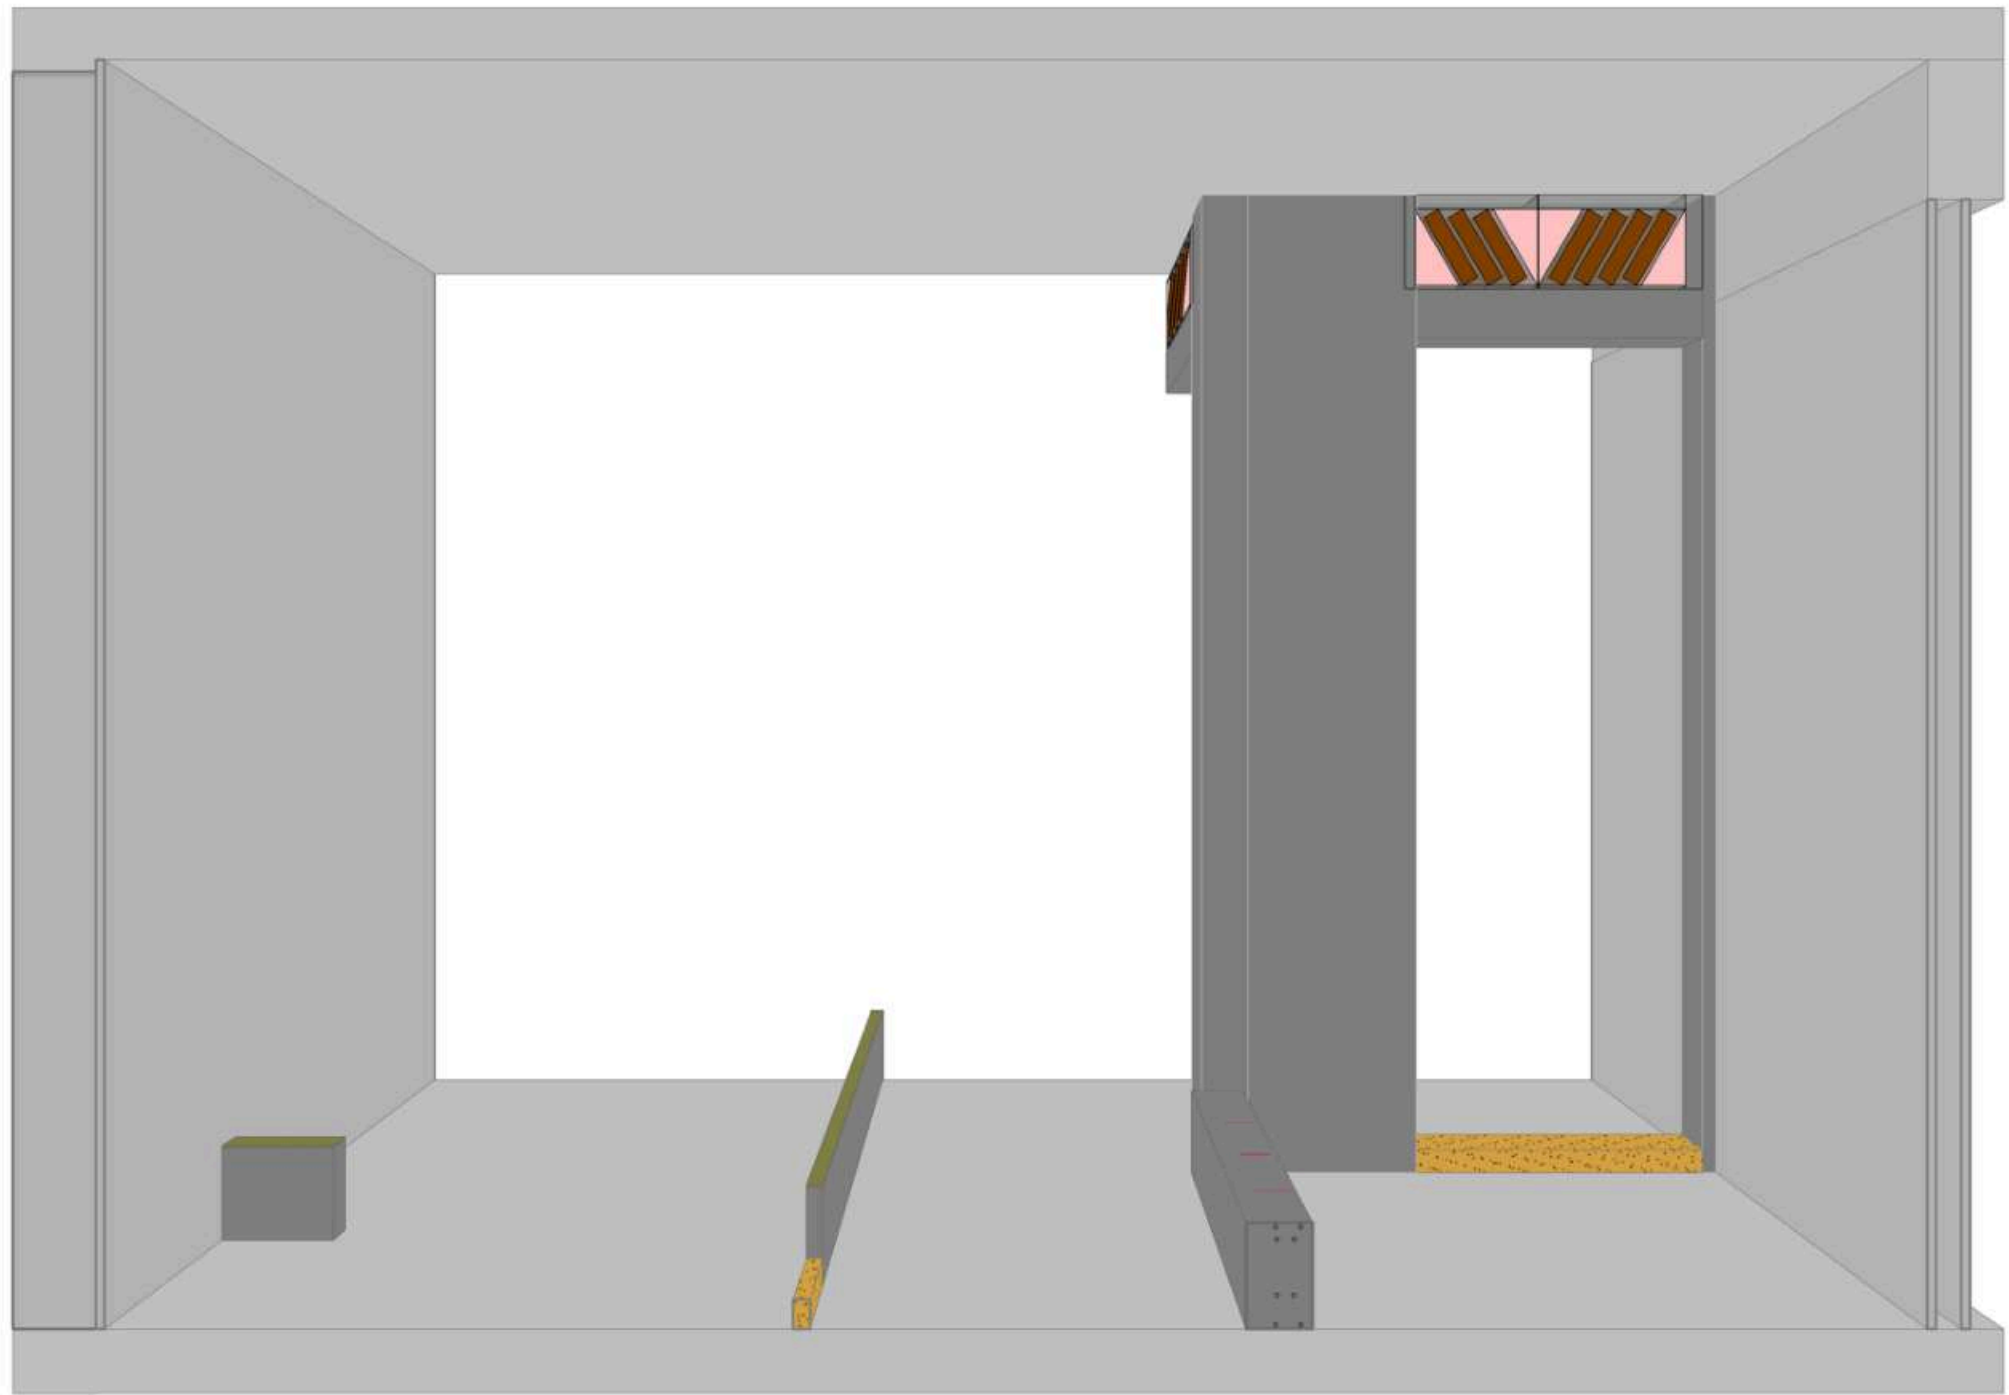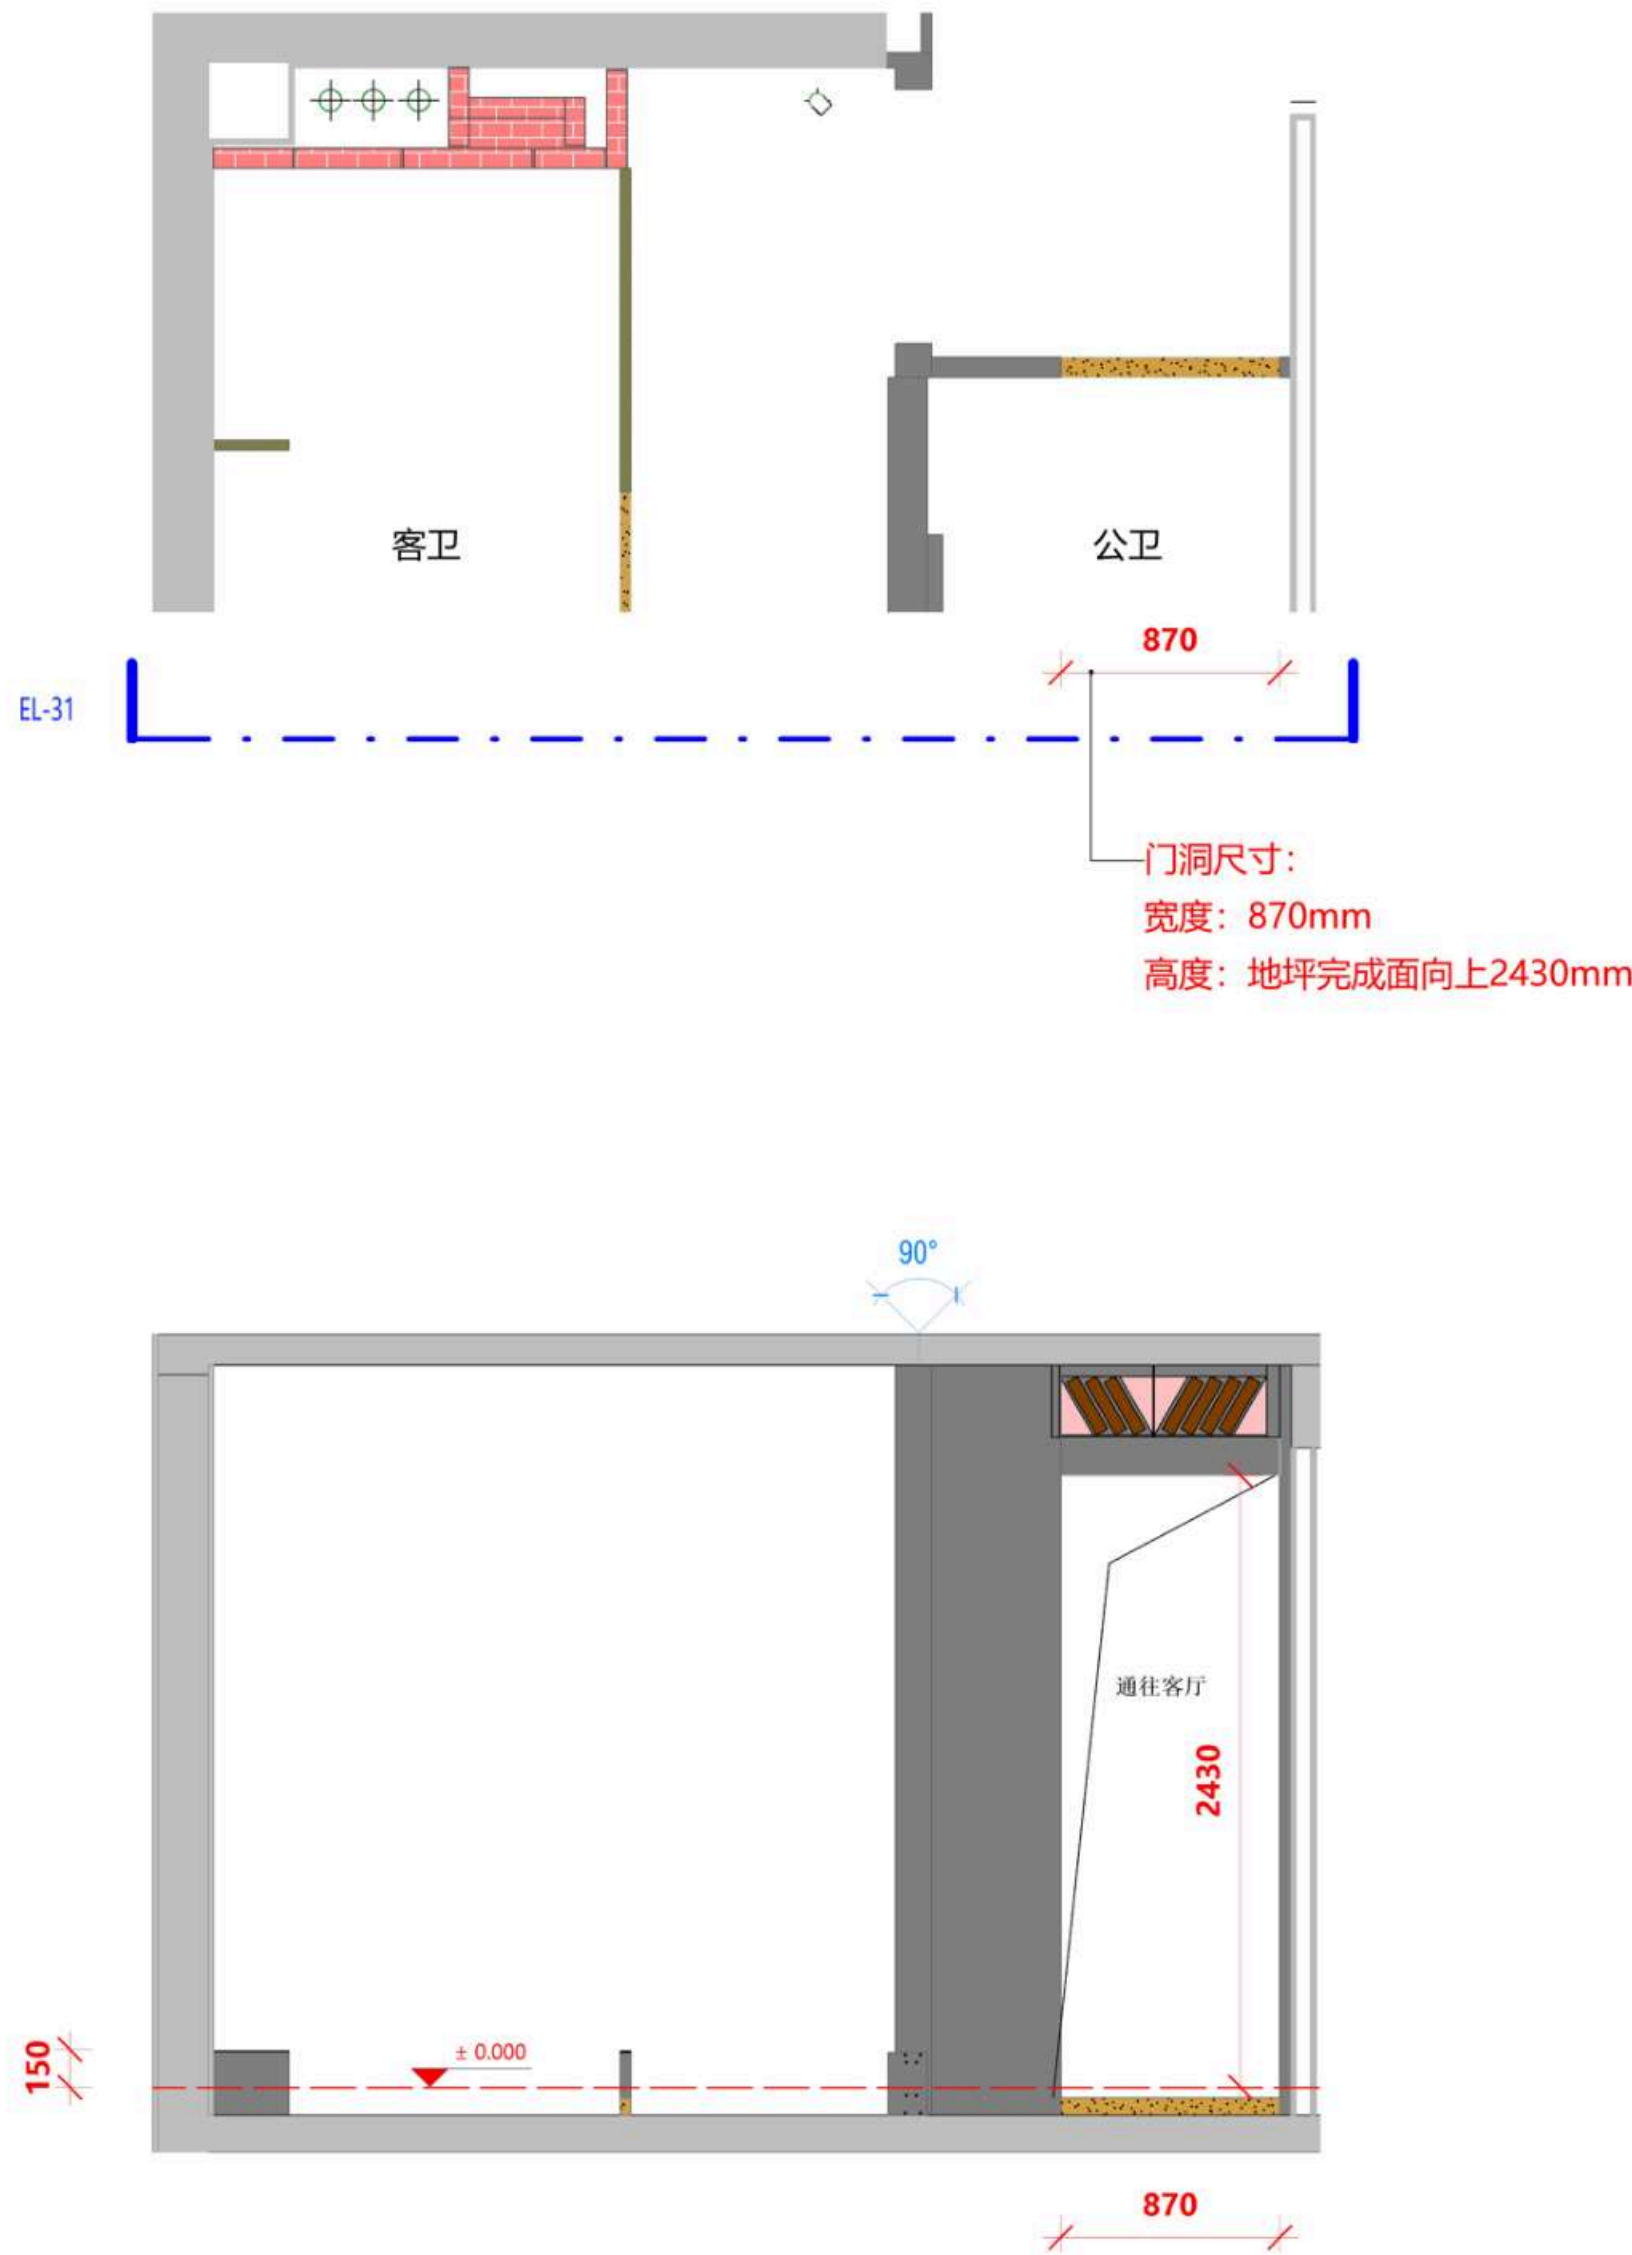

ELBORNI

LEGEND图例

图例A 材质分类		
编号	图例	说明
1		原始墙、板、柱
2		混凝土墙、结构柱、马牙槎
3		PC砖
4		红砖
5		钢架墙
6		止水坎
7		混凝土止水坎上加5mm钢板
图例B 施工时注意事项		
编号	图例	说明
1		地面完成线
2		必要尺寸
3		起铺点
4		错缝要求 $a \geq 200$ $b \geq 150$
5		边砖宽度要求 $a \geq 200$
6		$b < 150$ 时 $a = b$

日期
Date 01/11/26

修订
Revision

项目
Project

潮映华府3-801

Scale
比例 1:30@A2

PC砖墙31

Drawing No.
图纸编号

29-PCW-31

Project No.
项目编号

©2025

正式施工图

2026-01-27

PC砖墙立面图31

Scale比例 1:30@A2




PC砖墙三维示意图31

Scale比例 1:30@A2

注释

Notes

- 1.本图纸如与现场尺寸有误差, 请施工人员与项目负责人联系。
- 2.施工前施工人员应认真查阅此图, 如有不明确尺寸, 按现场测量为准。
- 3.本图纸必须经甲乙双方认可并签字方可作为施工依据。

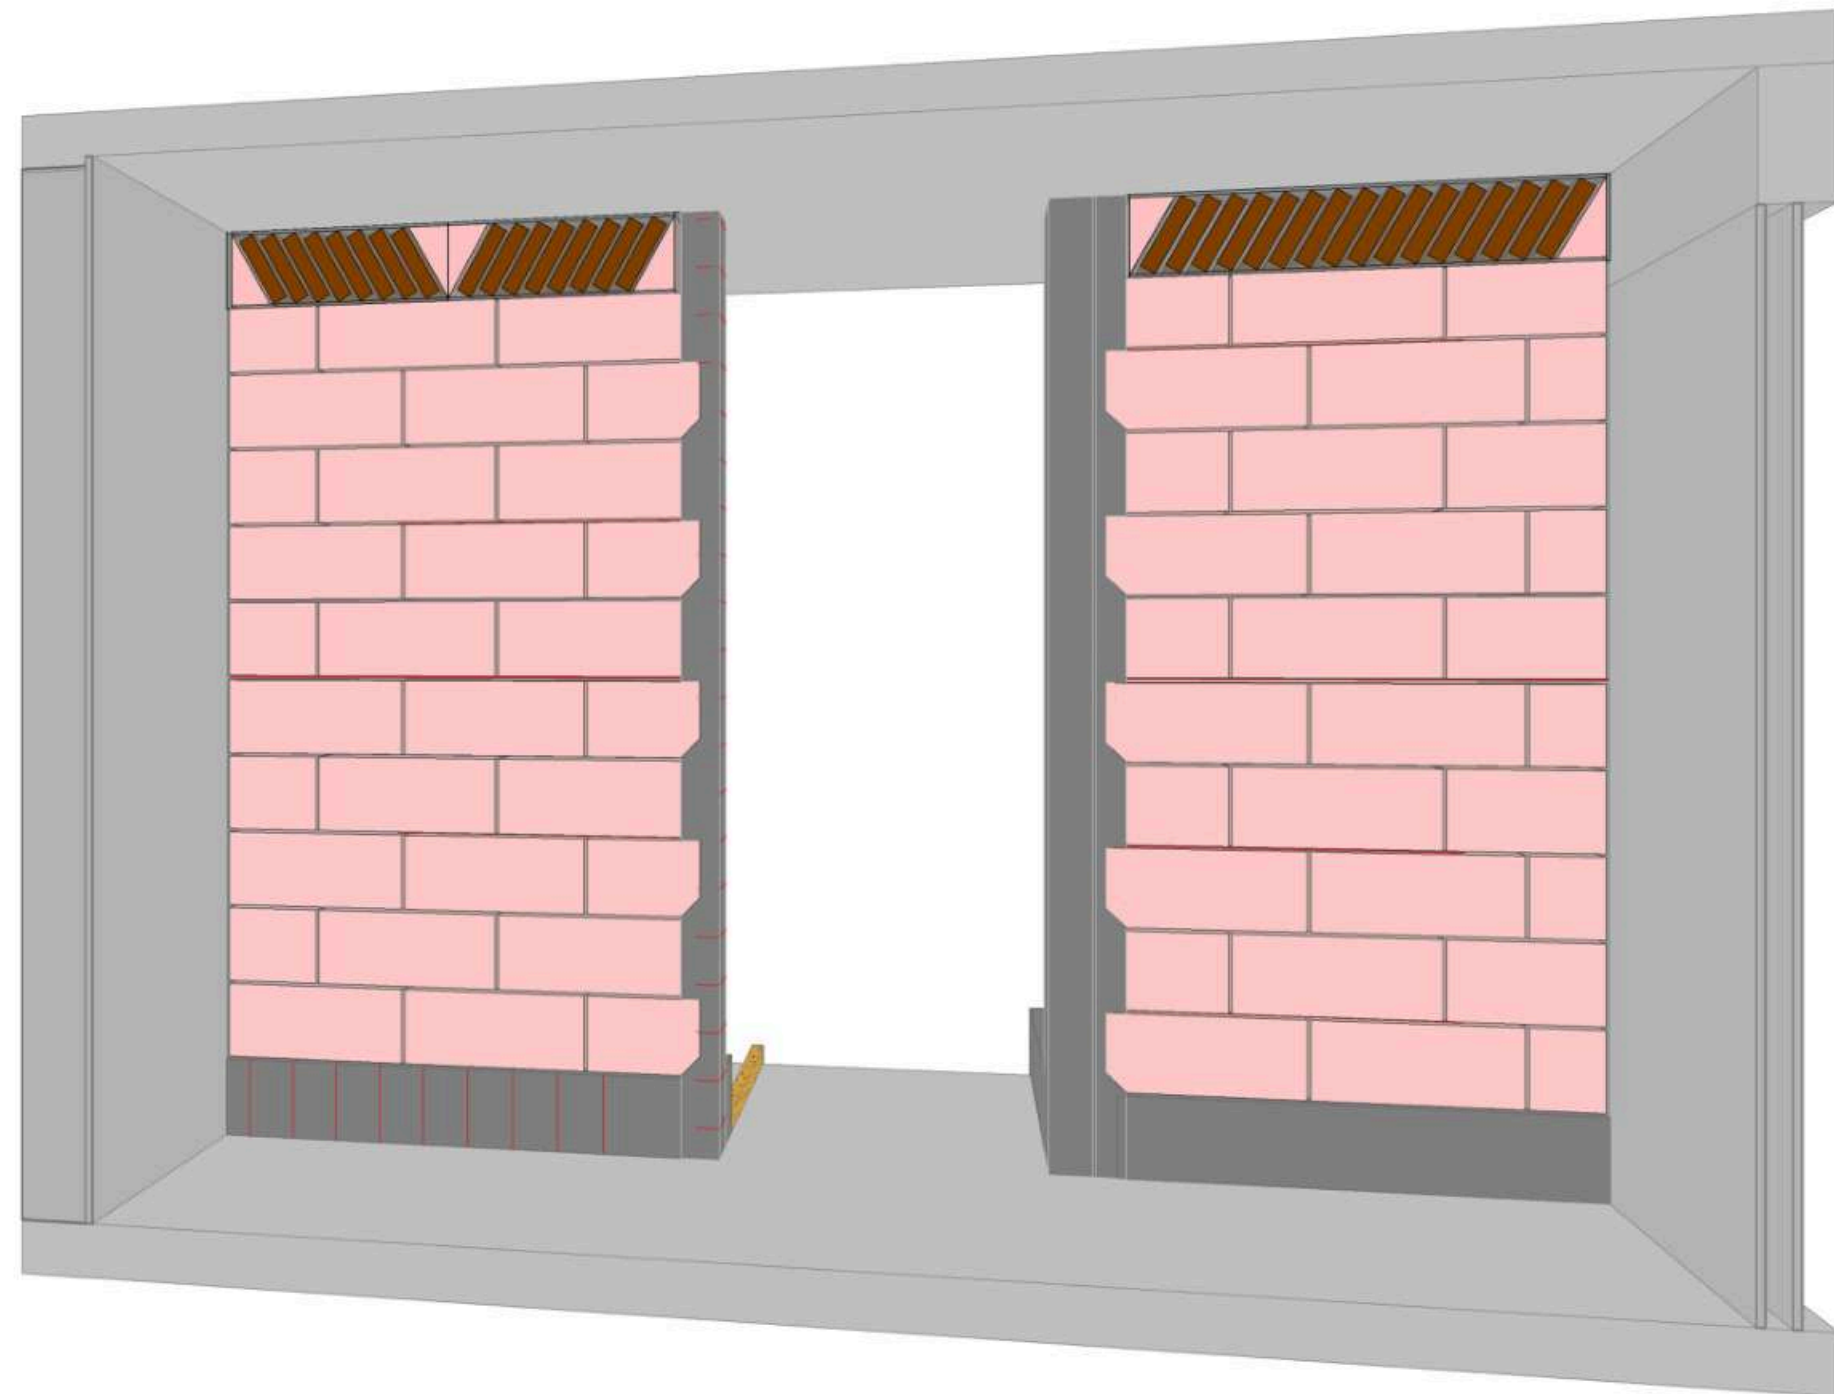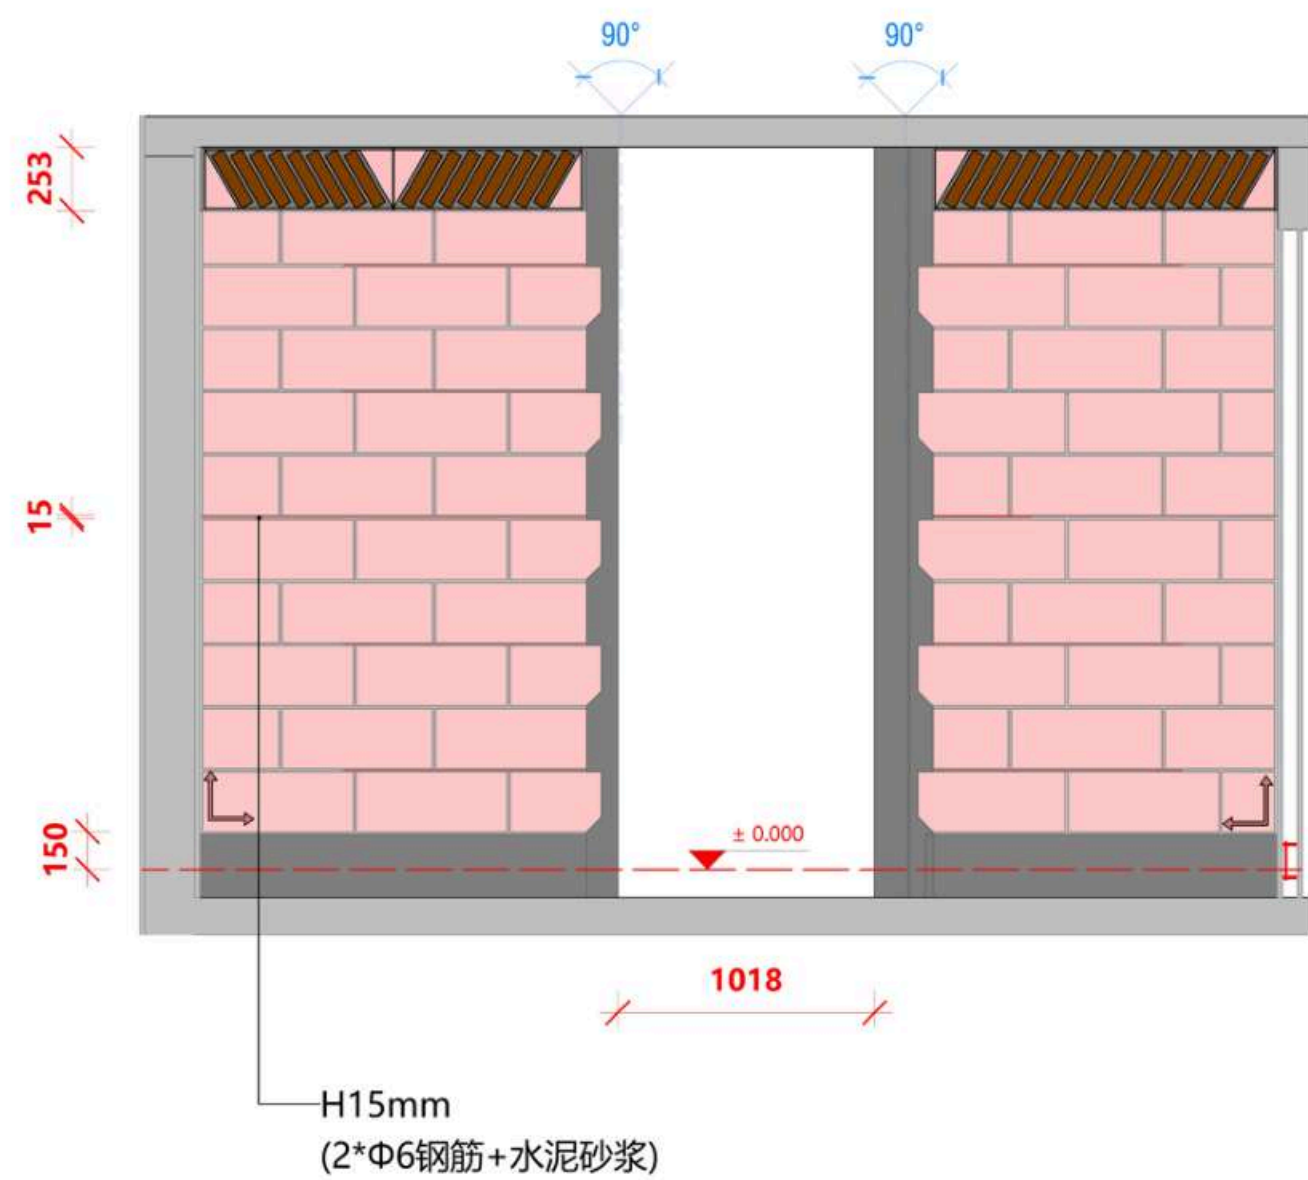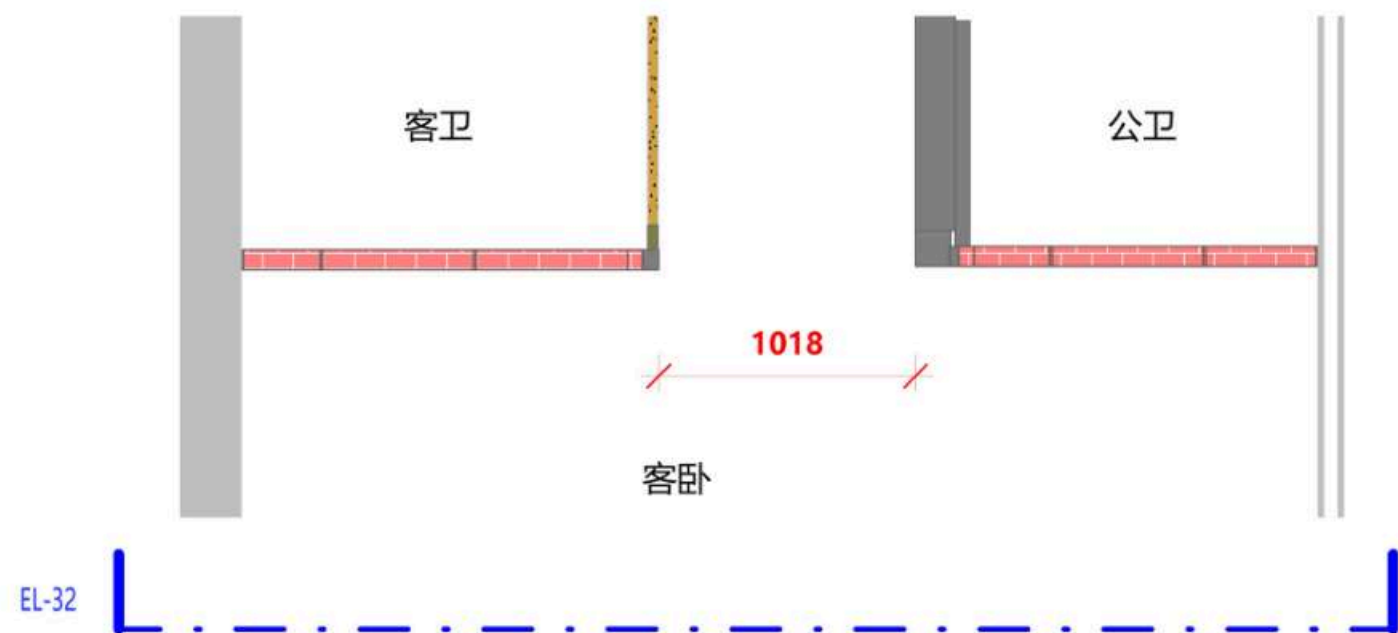

ELBORNI

LEGEND图例

图例A 材质分类		
编号	图例	说明
1		原始墙、板、柱
2		混凝土导墙、结构柱、马牙槎
3		PC砖
4		红砖
5		钢架墙
6		止水坎
7		混凝土止水坎上加5mm钢板

图例B 施工时注意事项		
编号	图例	说明
1		地面完成线
2		必要尺寸
3		起铺点
4		错峰要求 $a \geq 200$ $b \geq 150$
5		边砖宽度要求 $a \geq 200$
6		$b < 150$ 时 $a = b$

日期
Date 01/11/26

修订
Revision

项目
Project
潮映华府3-801

Scale
比例 1:30@A2
PC砖墙32

Drawing No.
图纸编号
30-PCW-32




Project No.
项目编号
©2025

1 PC砖墙立面图32
EL-32 Scale比例 1 : 30@A2

1 PC砖墙三维示意图32
3D-32 Scale比例 1:30@A2

注释
Notes
1.本图纸如与现场尺寸有误，请施工人员与项目负责人联系。
2.施工前施工人员应认真查阅此图，如有不明确尺寸，按现场测量为准。
3.本图纸必须经甲乙双方认可并签字方可作为施工依据。

正式施工图
2026-01-27

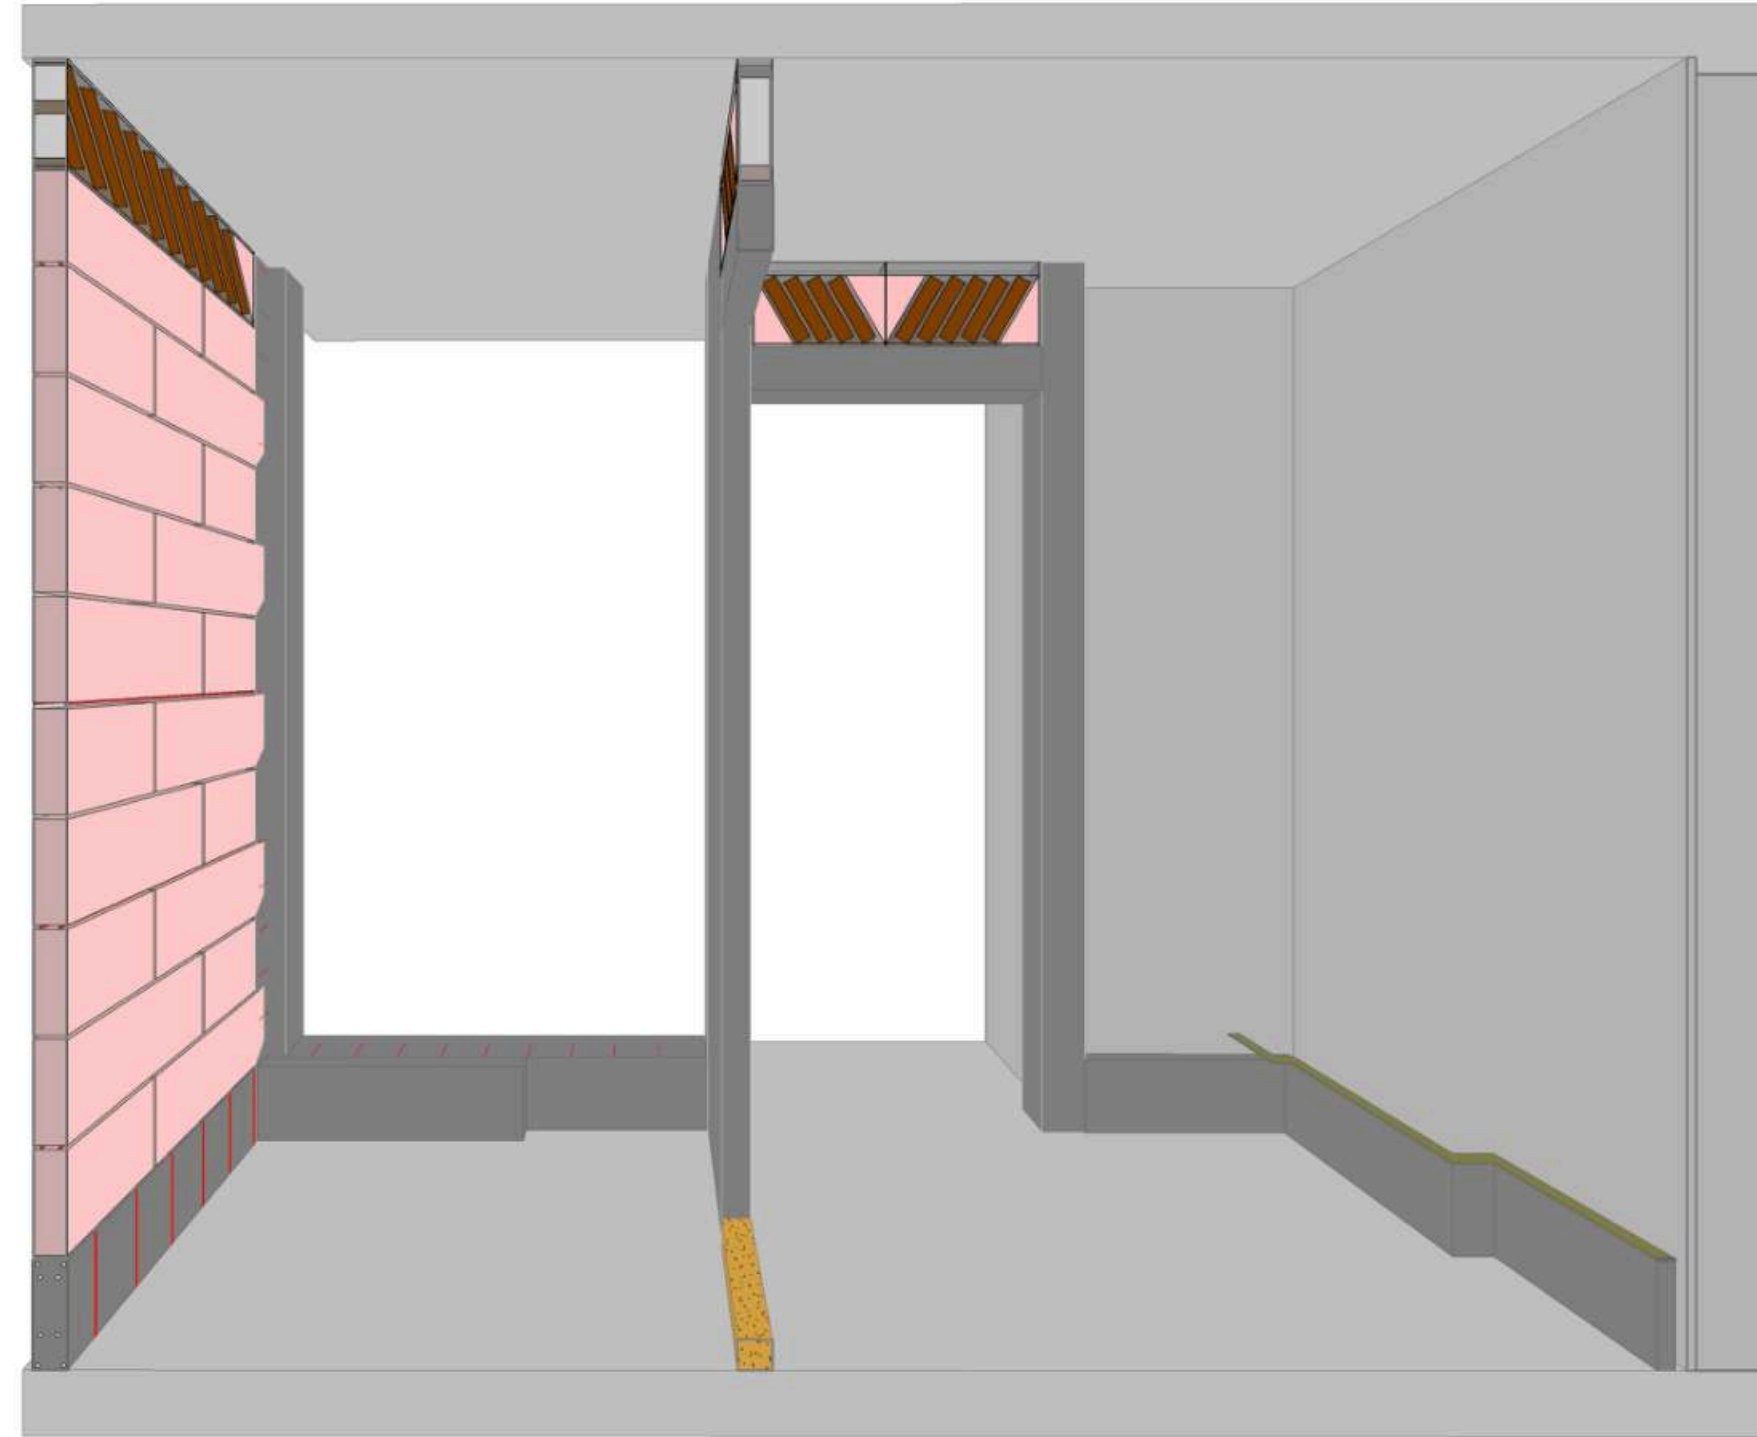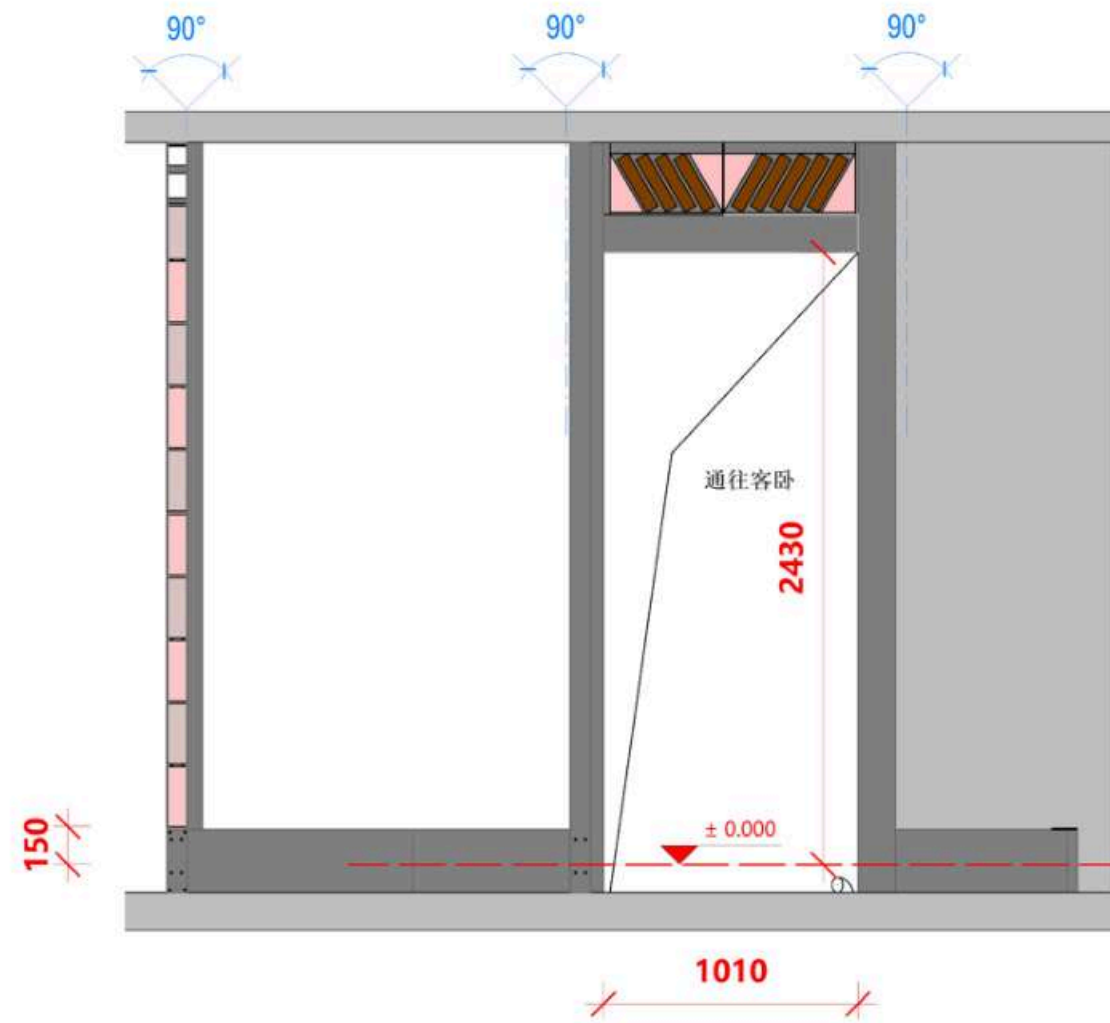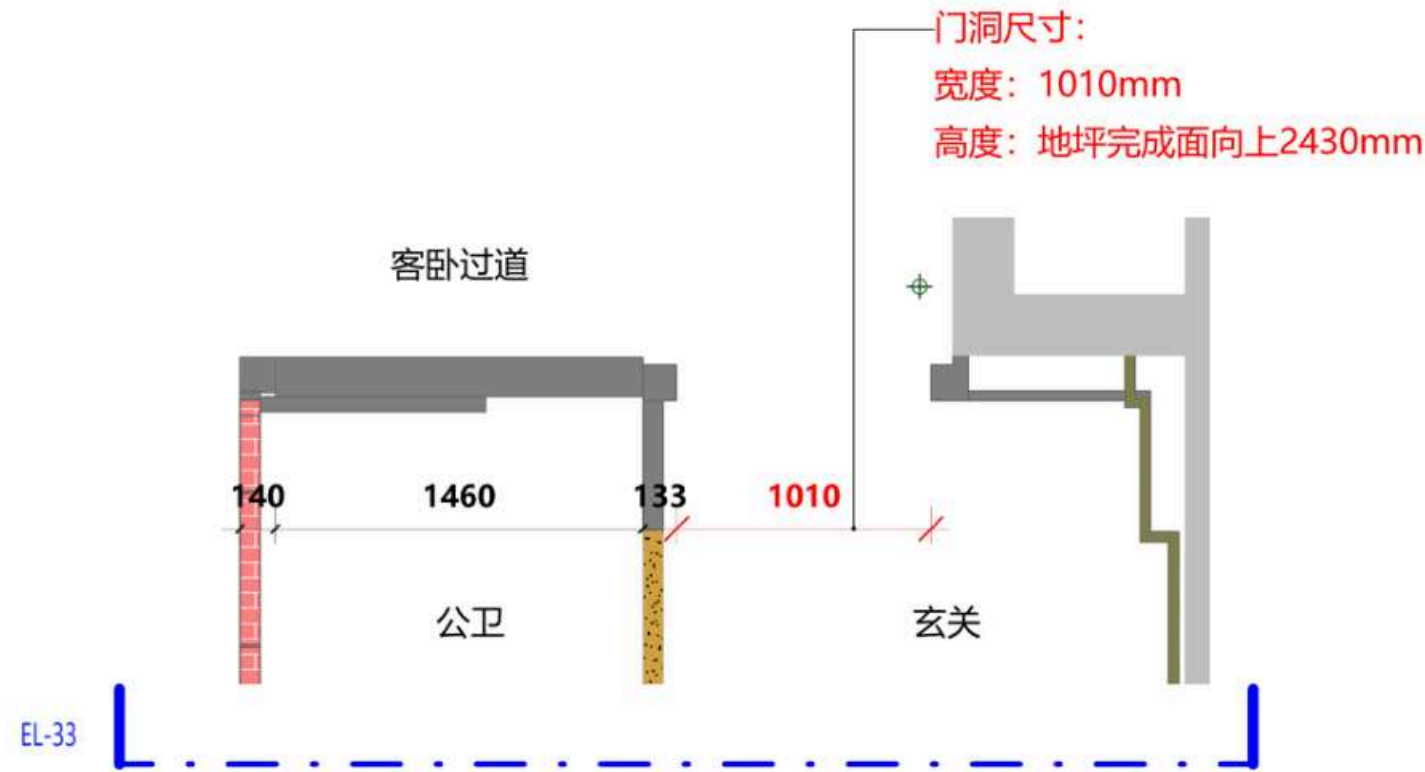

ELBORN

LEGEND图例

图例A 材质分类		
编号	图例	说明
1		原始墙、板、柱
2		混凝土墙、结构柱、马牙槎
3		PC砖
4		红砖
5		钢架墙
6		止水坎
7		混凝土止水坎上加5mm钢板

图例B 施工时注意事项		
编号	图例	说明
1		地面完成线
2		必要尺寸
3		起铺点
4		错峰要求 $a \geq 200$ $b \geq 150$
5		边砖宽度要求 $a \geq 200$
6		$b < 150$ 时 $a = b$

日期
Date 01/11/26

修订
Revision

项目
Project

潮映华府3-801

Scale
比例 1:30@A2

PC砖墙33

Drawing No.
图纸编号

31-PCW-33

Project No.
项目编号

©2025

正式施工图

2026-01-27

1

EL-33

PC砖墙立面图33

Scale比例 1 : 30@A2

1




3D-33

PC砖墙三维示意图33

Scale比例 1:30@A2

注释
Notes

- 1.本图纸如与现场尺寸有误差, 请施工人员与项目负责人联系。
- 2.施工前施工人员应认真查阅此图, 如有不明确尺寸, 按现场测量为准。
- 3.本图纸必须经甲乙双方认可并签字方可作为施工依据。

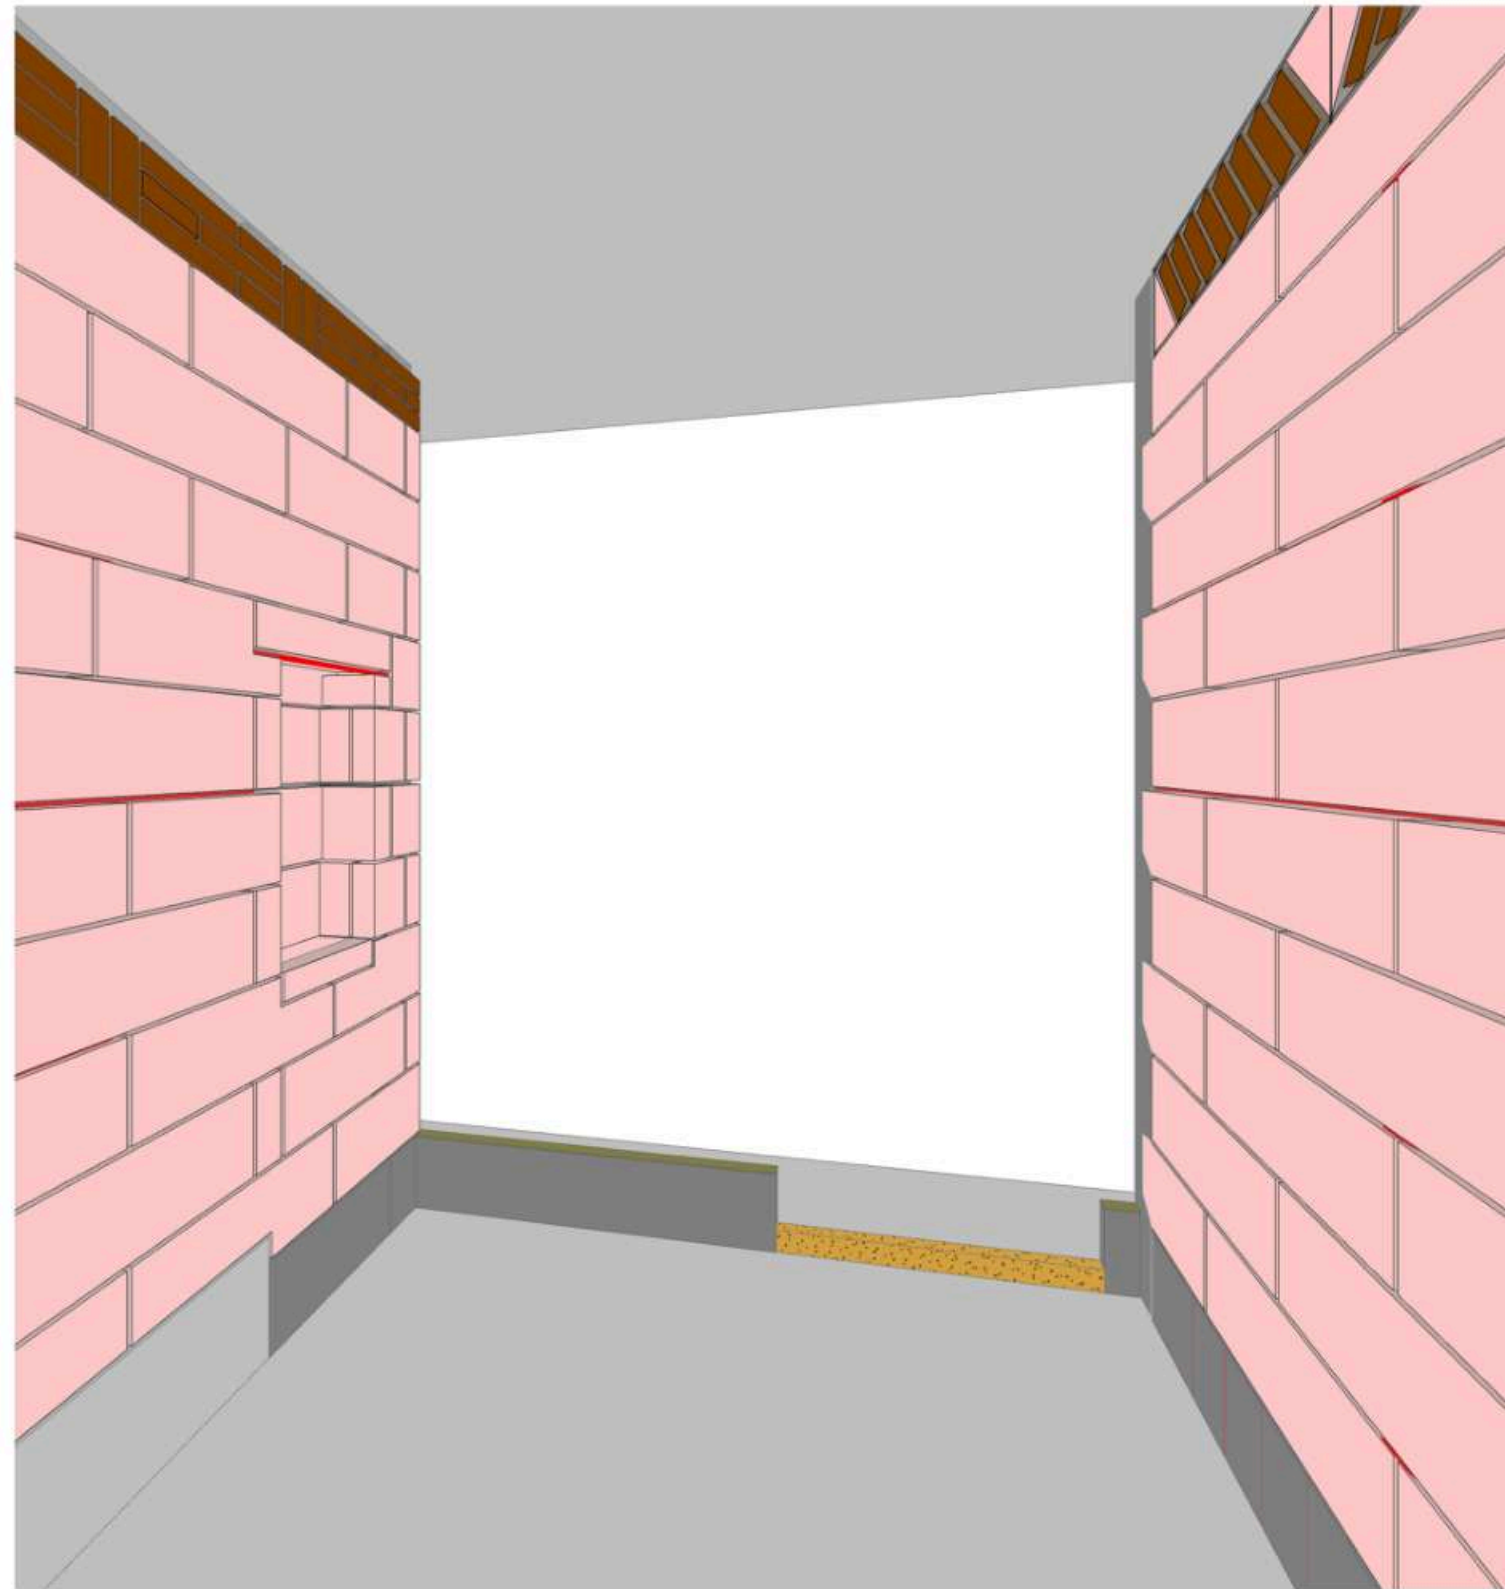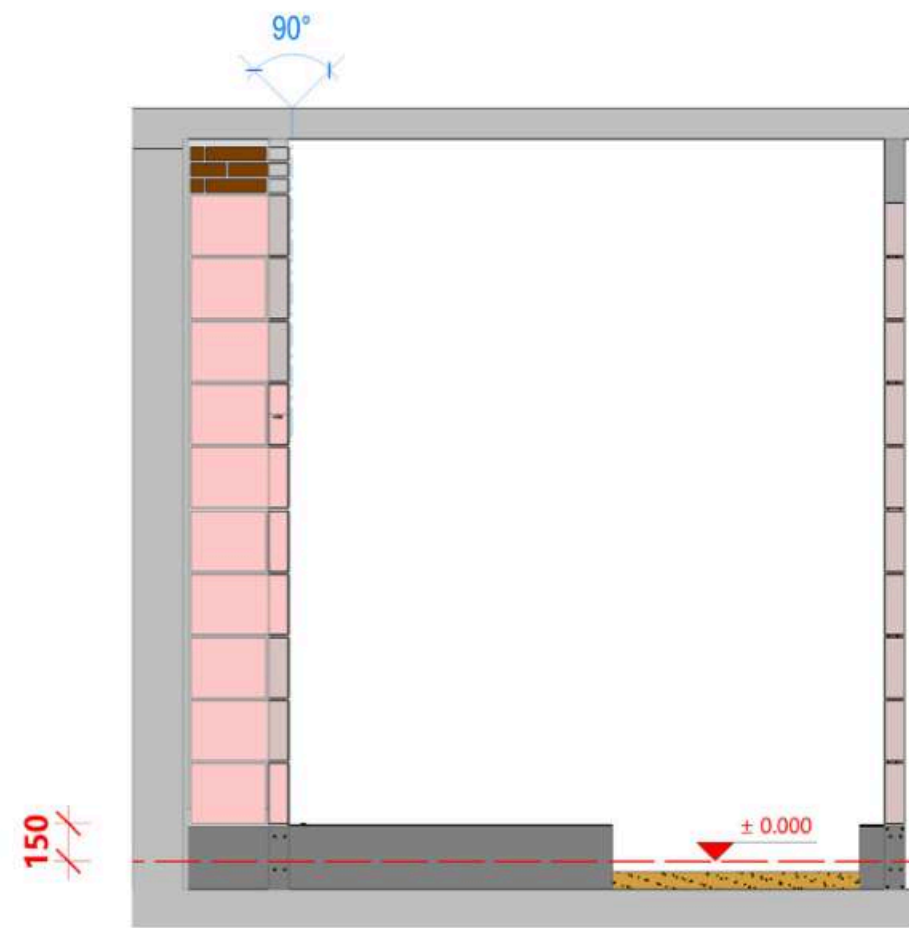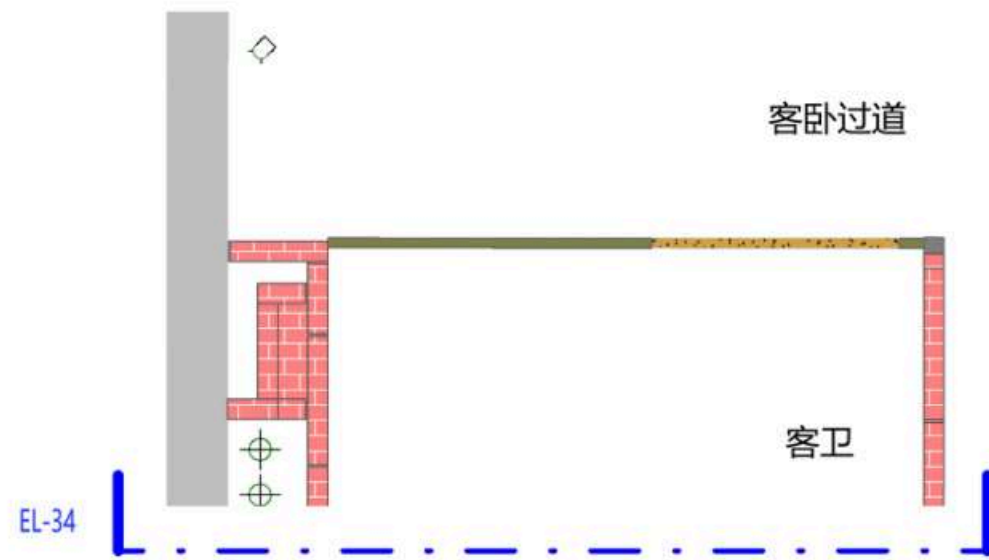

LEGEND图例

图例A 材质分类		
编号	图例	说明
1		原始墙、板、柱
2		混凝土导墙、结构柱、马牙槎
3		PC砖
4		红砖
5		钢架墙
6		止水坎
7		混凝土止水坎上加5mm钢板
图例B 施工时注意事项		
编号	图例	说明
1		地面完成线
2		必要尺寸
3		起铺点
4		错峰要求 $a \geq 200$ $b \geq 150$
5		边砖宽度要求 $a \geq 200$
6		$b < 150$ 时 $a = b$

日期
Date 01/11/26

修订
Revision

项目
Project

潮映华府3-801

Scale
比例 1:30@A2

PC砖墙34

Drawing No.
图纸编号

32-PCW-34

Project No.
项目编号

©2025

正式施工图

2026-01-27

1

EL-34

PC砖墙立面图34

Scale比例 1 : 30@A2

1

3D-34

PC砖墙三维示意图34

Scale比例 1:30@A2

注释

Notes

1.本图纸如与现场尺寸有误，请施工人员与项目负责人联系。
2.施工前施工人员应认真查阅此图，如有不明确尺寸，按现场测量为准。
3.本图纸必须经甲乙双方认可并签字方可作为施工依据。