


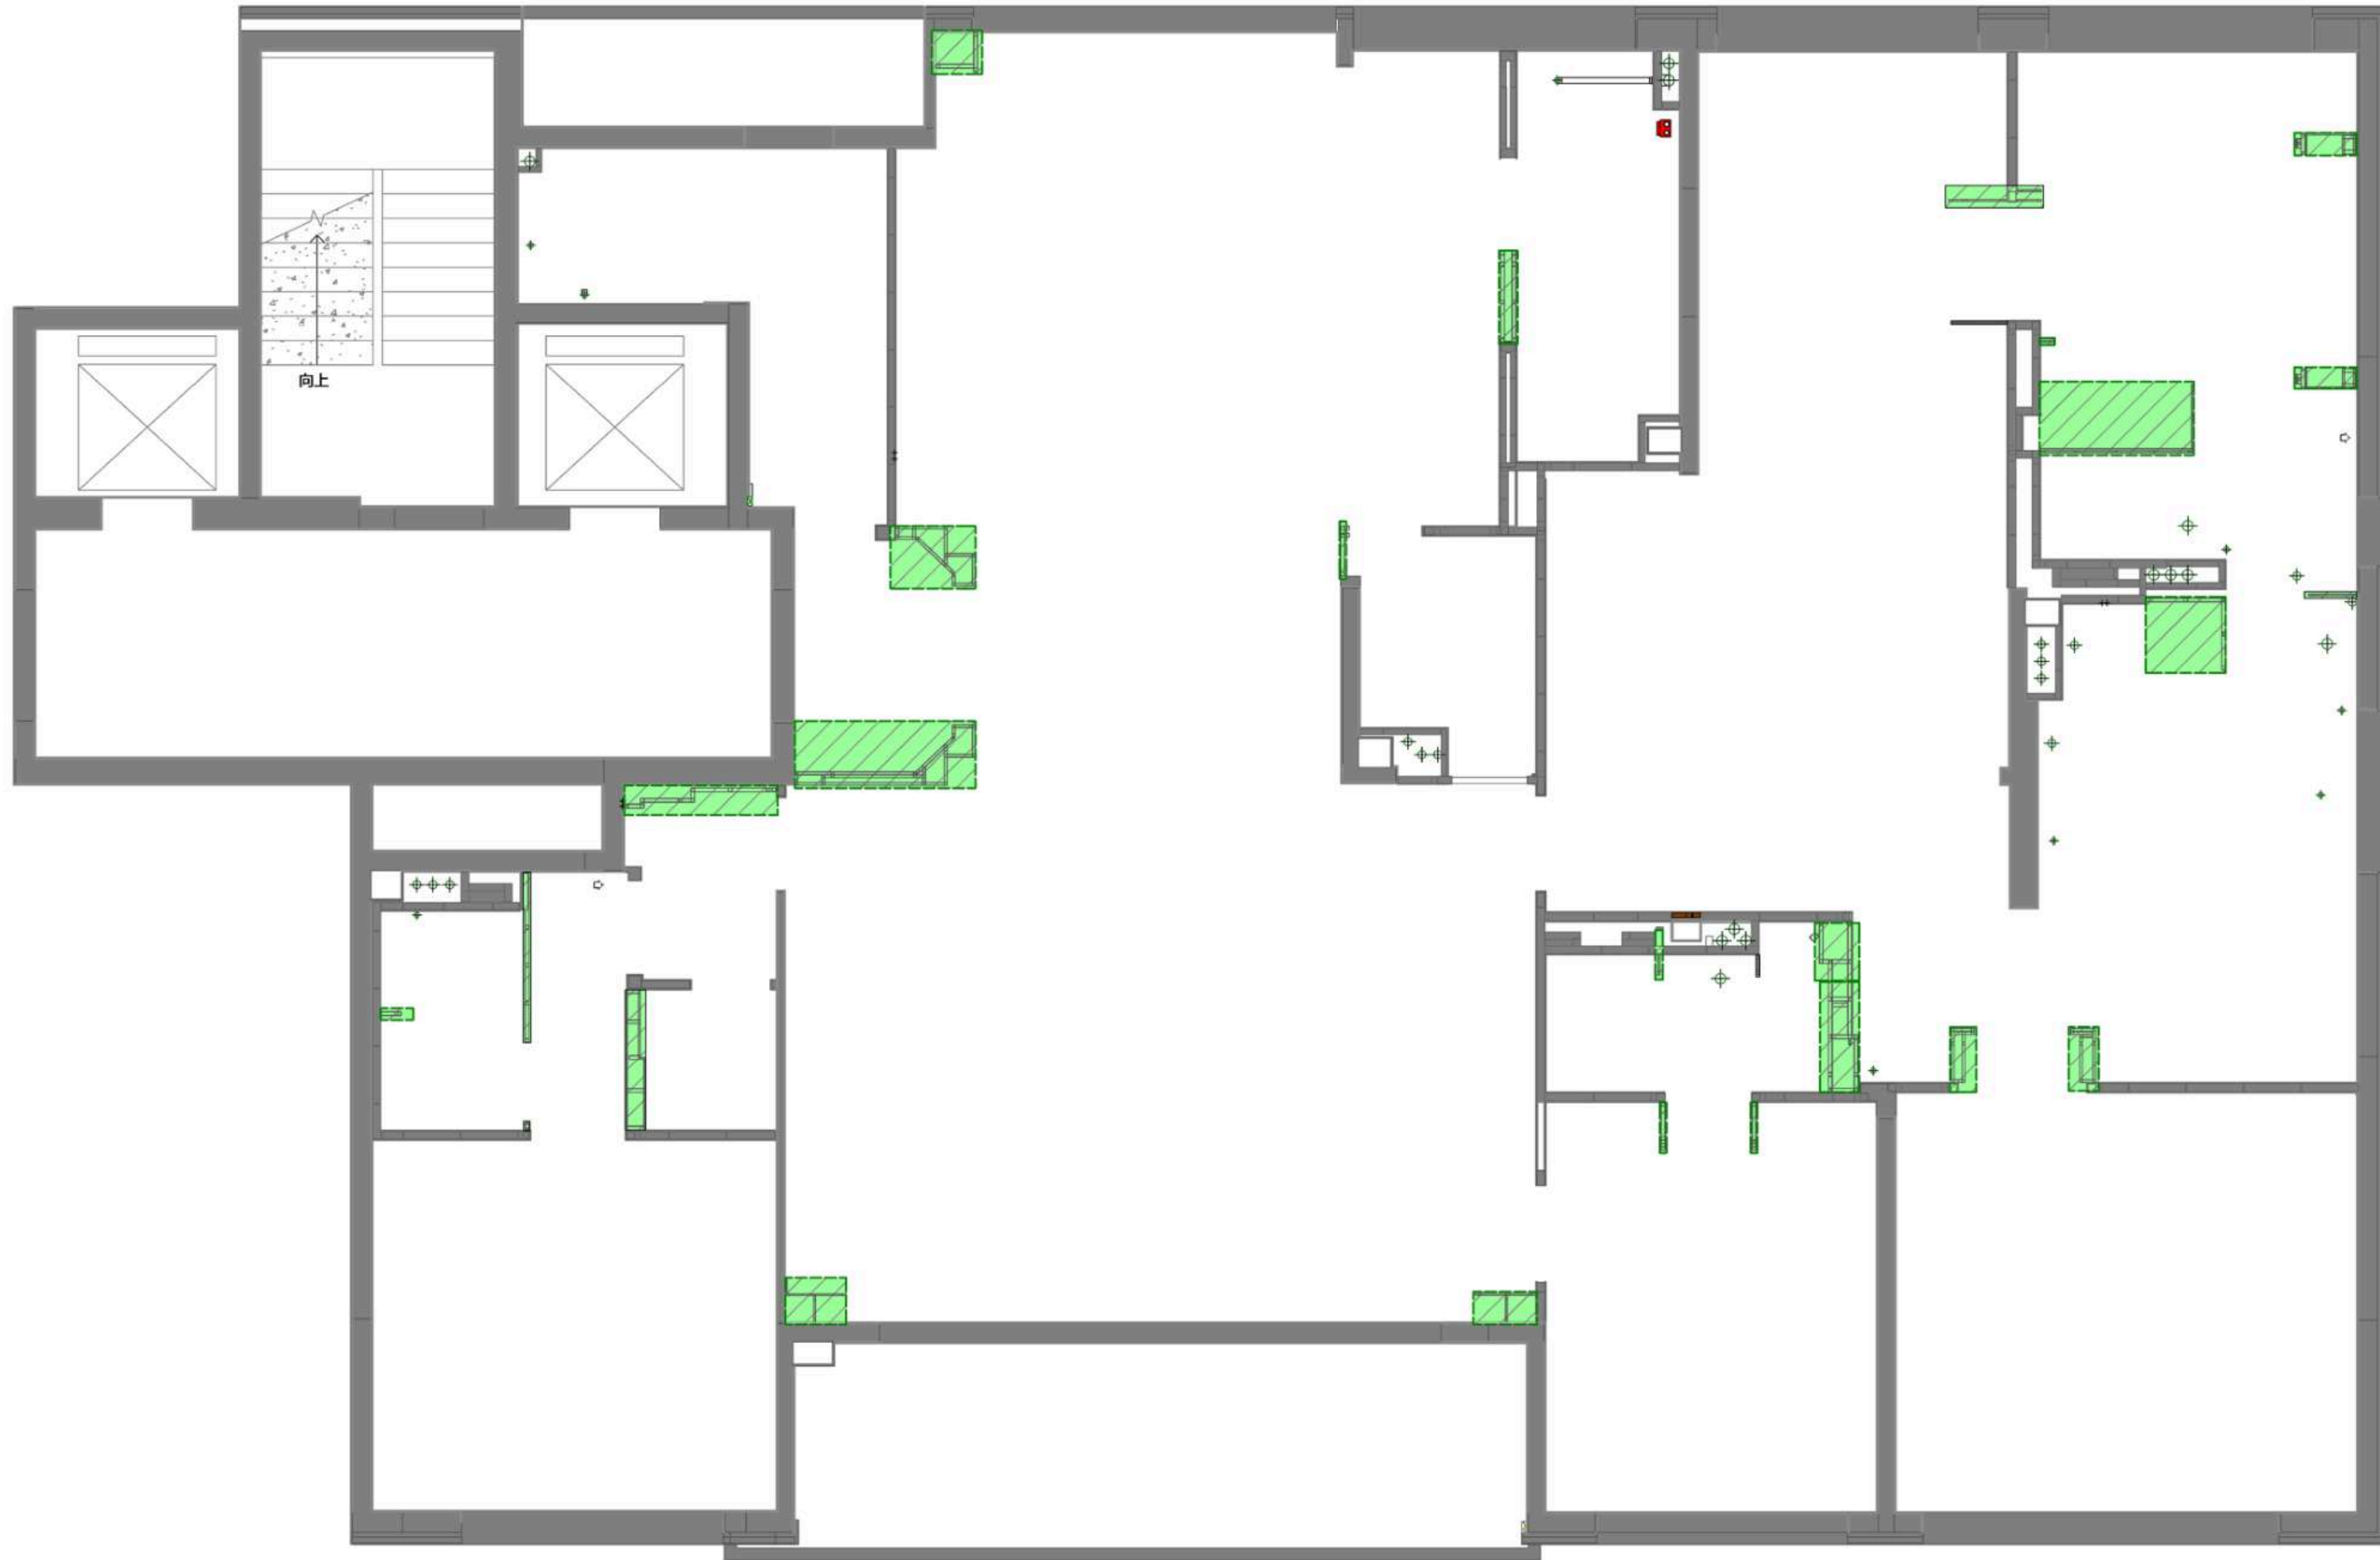

LEGEND图例

编号	图例	说明
1		加气块砖墙
2		抹灰层 (≈15mm)
3		结构柱
4		钢架墙

日期
Date

01/11/26

修订
Revision

项目
Project

潮映华府3-801

Scale
比例

1:60@A2


钢架墙平面示意图

Drawing No.
图纸编号

33-NW-05

Project No.
项目编号

©2025

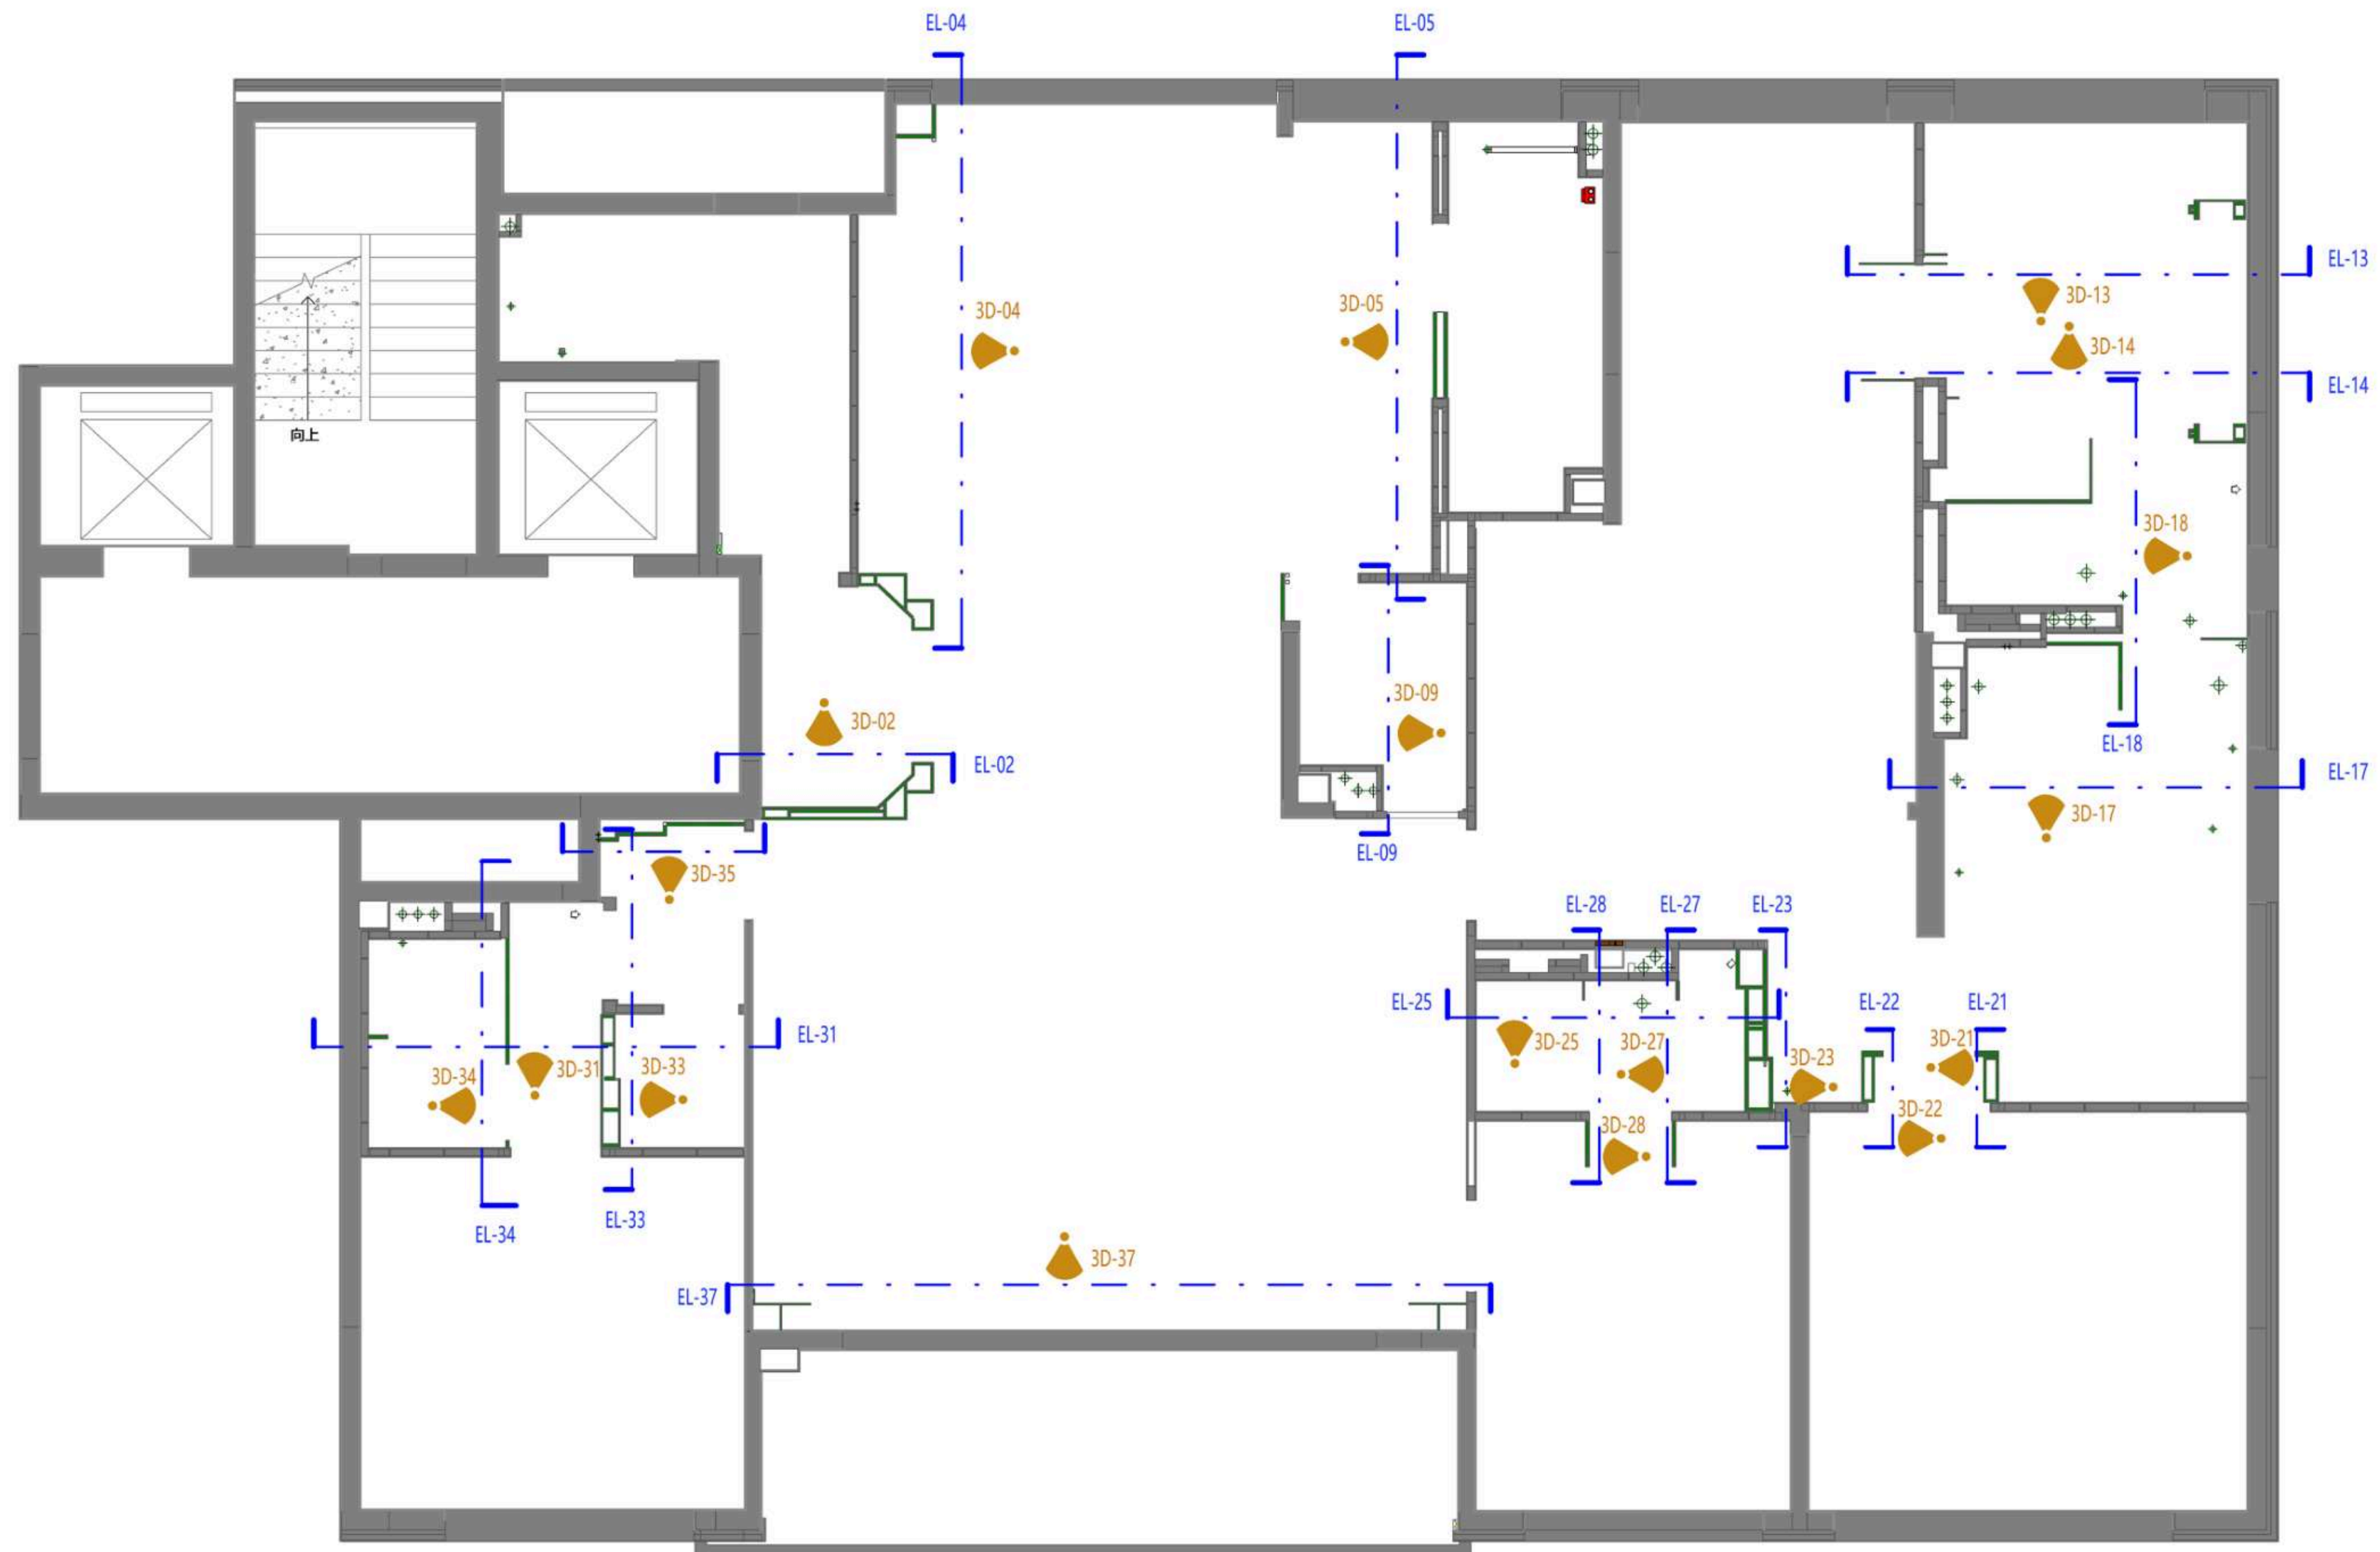

LEGEND图例

编号	图例	说明
1		加气块砖墙
2		抹灰层 (≈15mm)
3		结构柱
4		钢架墙

日期
Date 01/11/26

修订
Revision

项目
Project
潮映华岸府3-801

Scale
比例 1:60@A2
钢架墙立面索引图

Drawing No.
图纸编号 34-NW-06

Project No.
项目编号 ©2025




钢架墙立面索引图

Scale比例 1:60@A2

注释

Notes

- 1.本图纸如与现场尺寸有误, 请施工人员与项目负责人联系。
- 2.施工前施工人员应认真查阅此图, 如有不明确尺寸, 按现场测量为准。
- 3.本图纸必须经甲乙双方认可并签字方可作为施工依据。

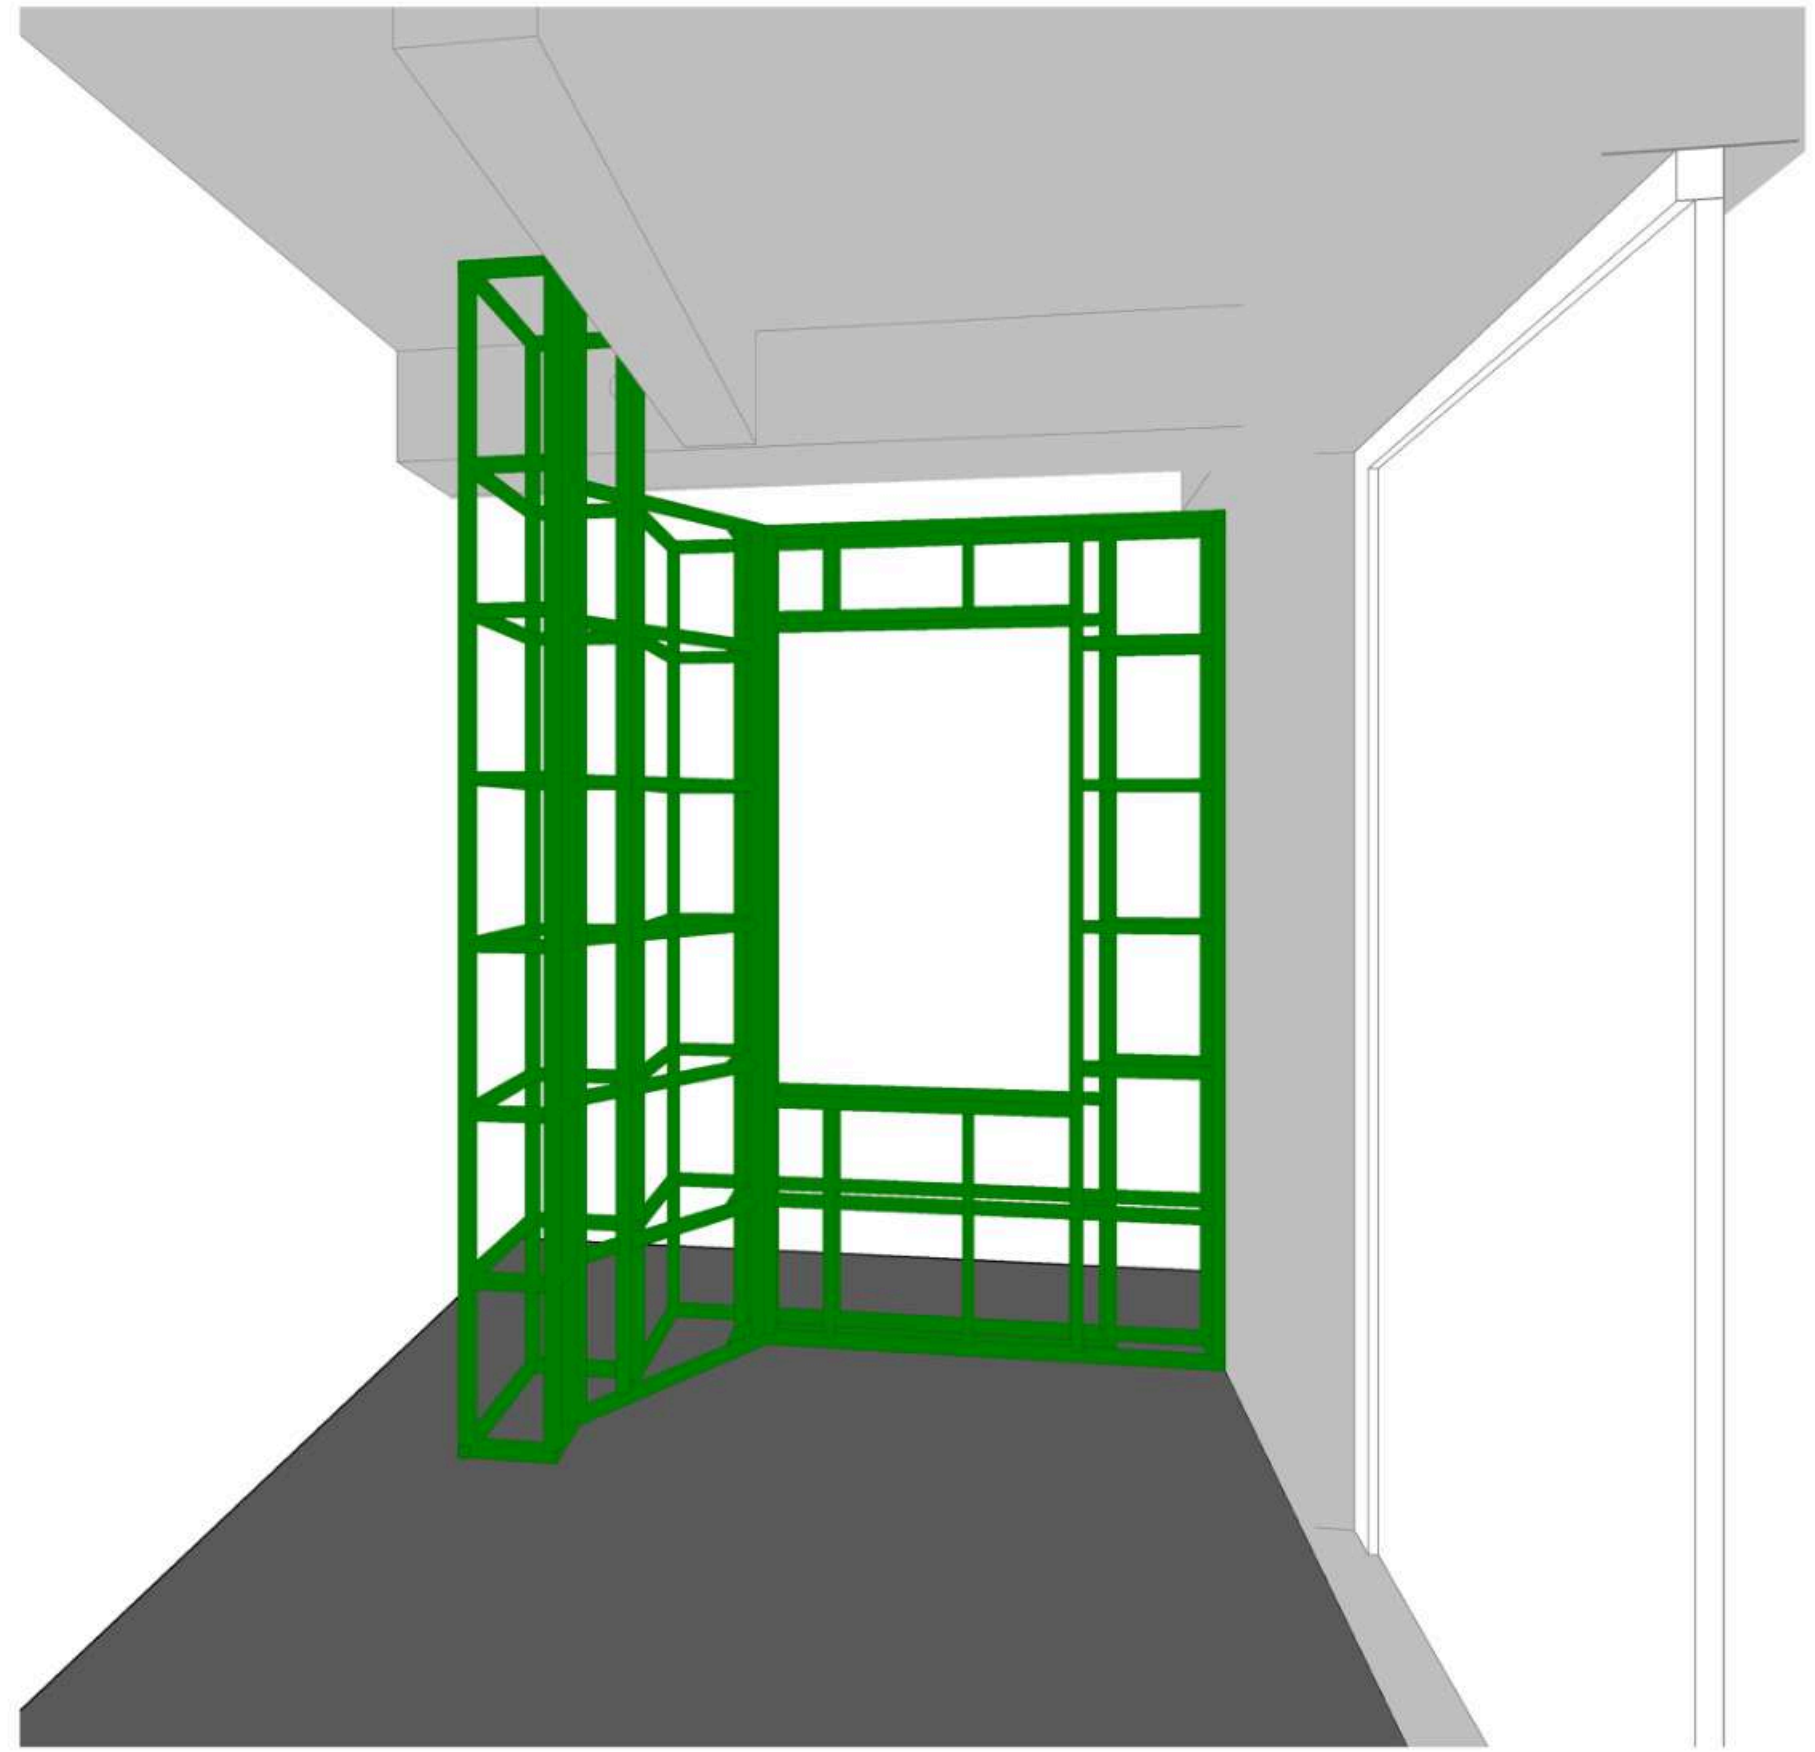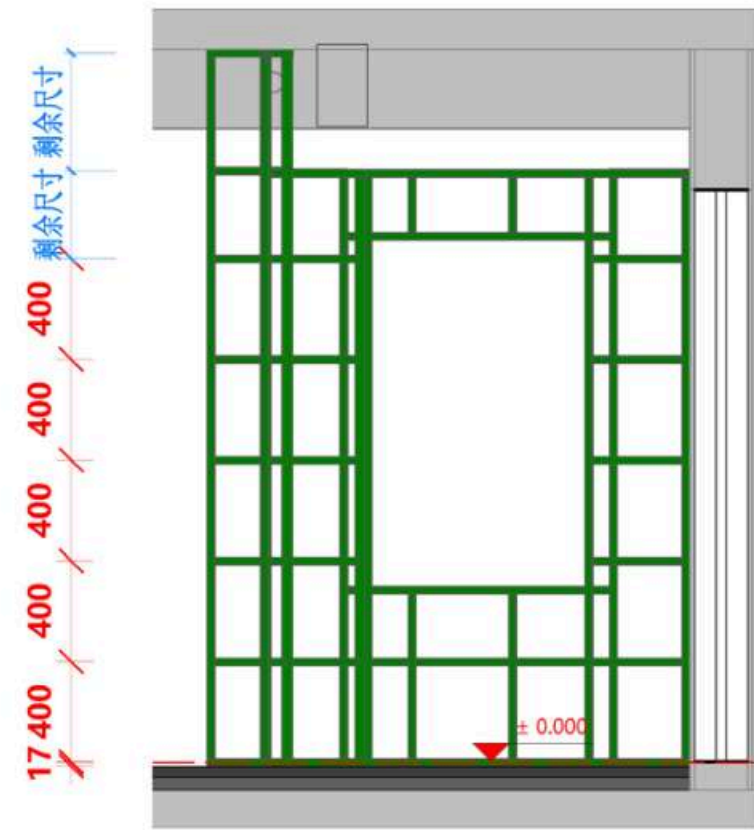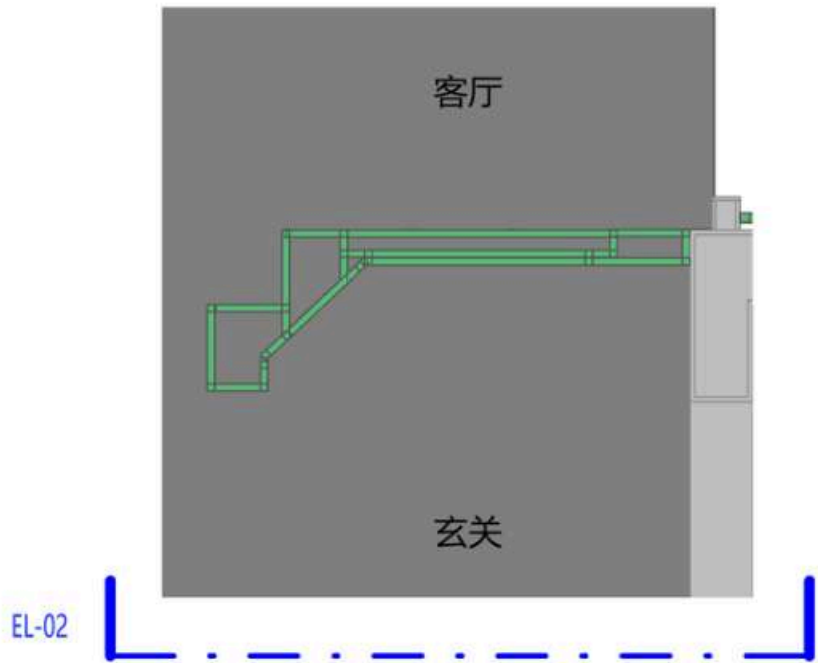

三和

LEGEND图例

编号	图例	说明
1		抹灰层 (≈15mm)
2		混凝土止水坎上 加5mm钢板
3		钢架墙

日期
Date

01/11/26

修订
Revision

项目
Project

潮映华岸府3-801

Scale
比例

1:30@A2

钢架墙02

Drawing No.
图纸编号

35-SW-02

Project No.
项目编号

©2025

1

EL-02

钢架墙立面图02

Scale比例 1 : 30@A2

1

3D-02



钢架墙三维图02

Scale比例 1:30@A2

注释

Notes

- 1.本图纸如与现场尺寸有误, 请施工人员与项目负责人联系。
- 2.施工前施工人员应认真查阅此图, 如有不明确尺寸, 按现场测量为准。
- 3.本图纸必须经甲乙双方认可并签字方可作为施工依据。

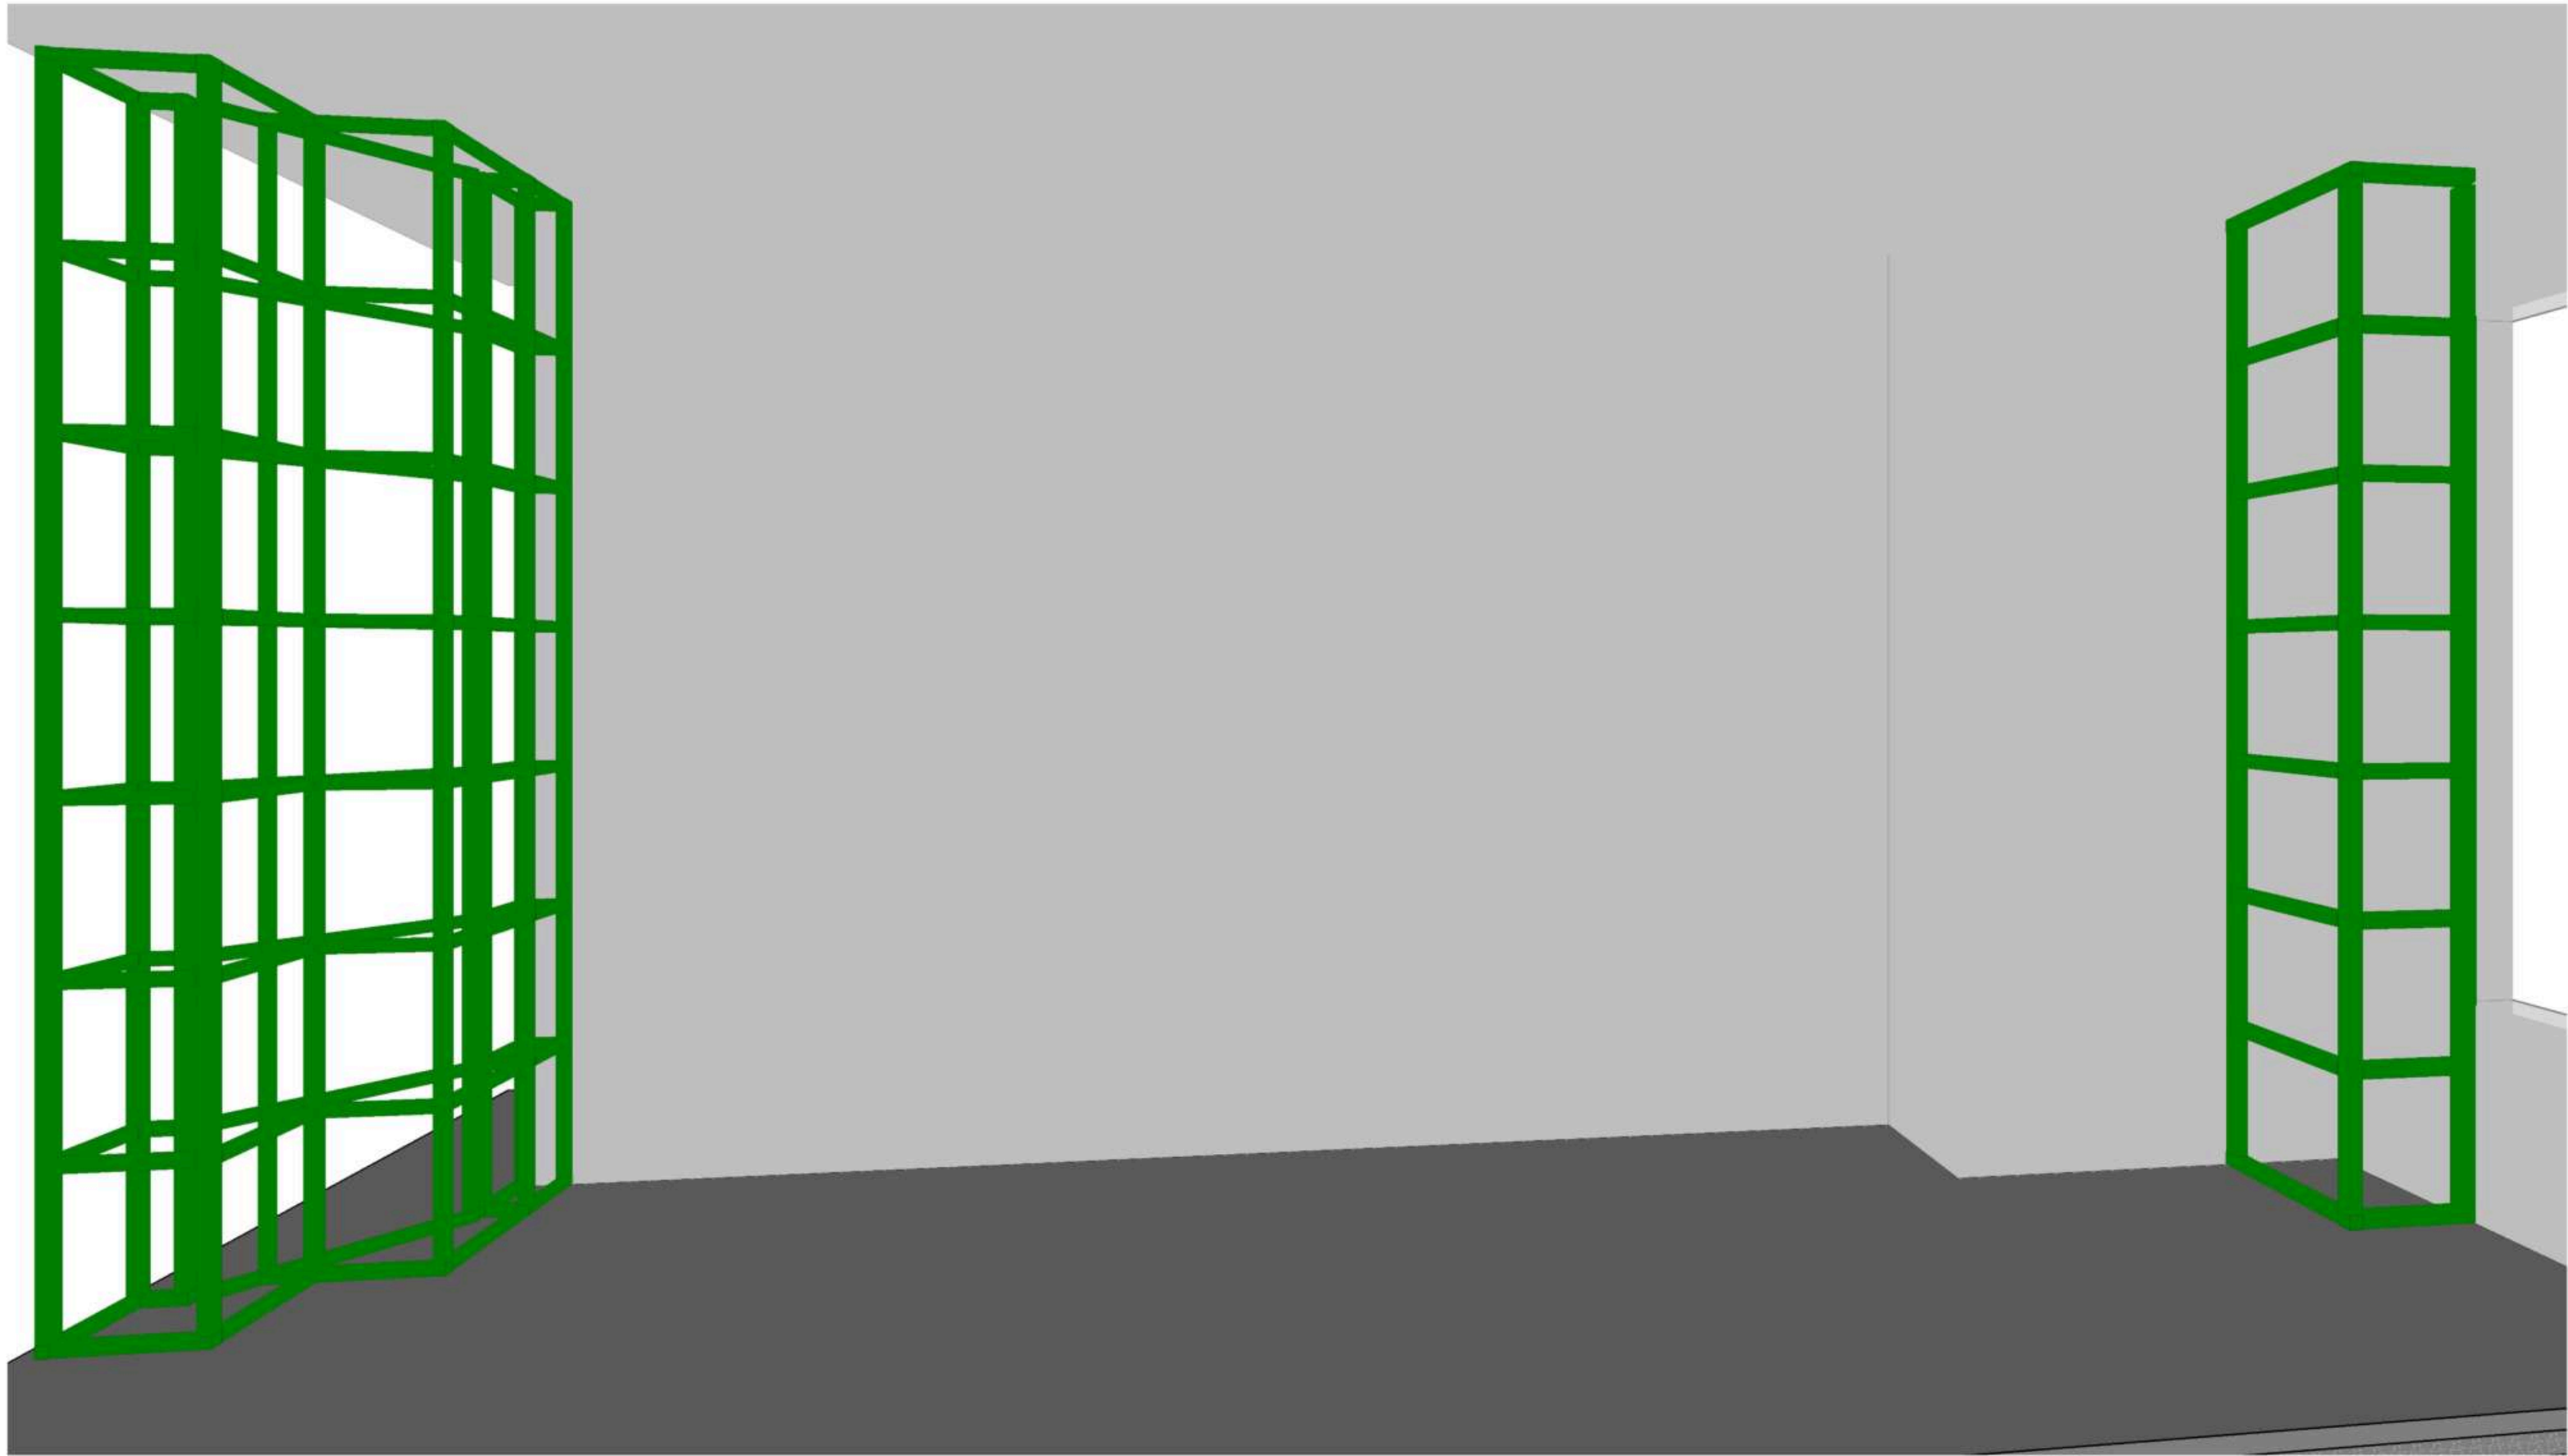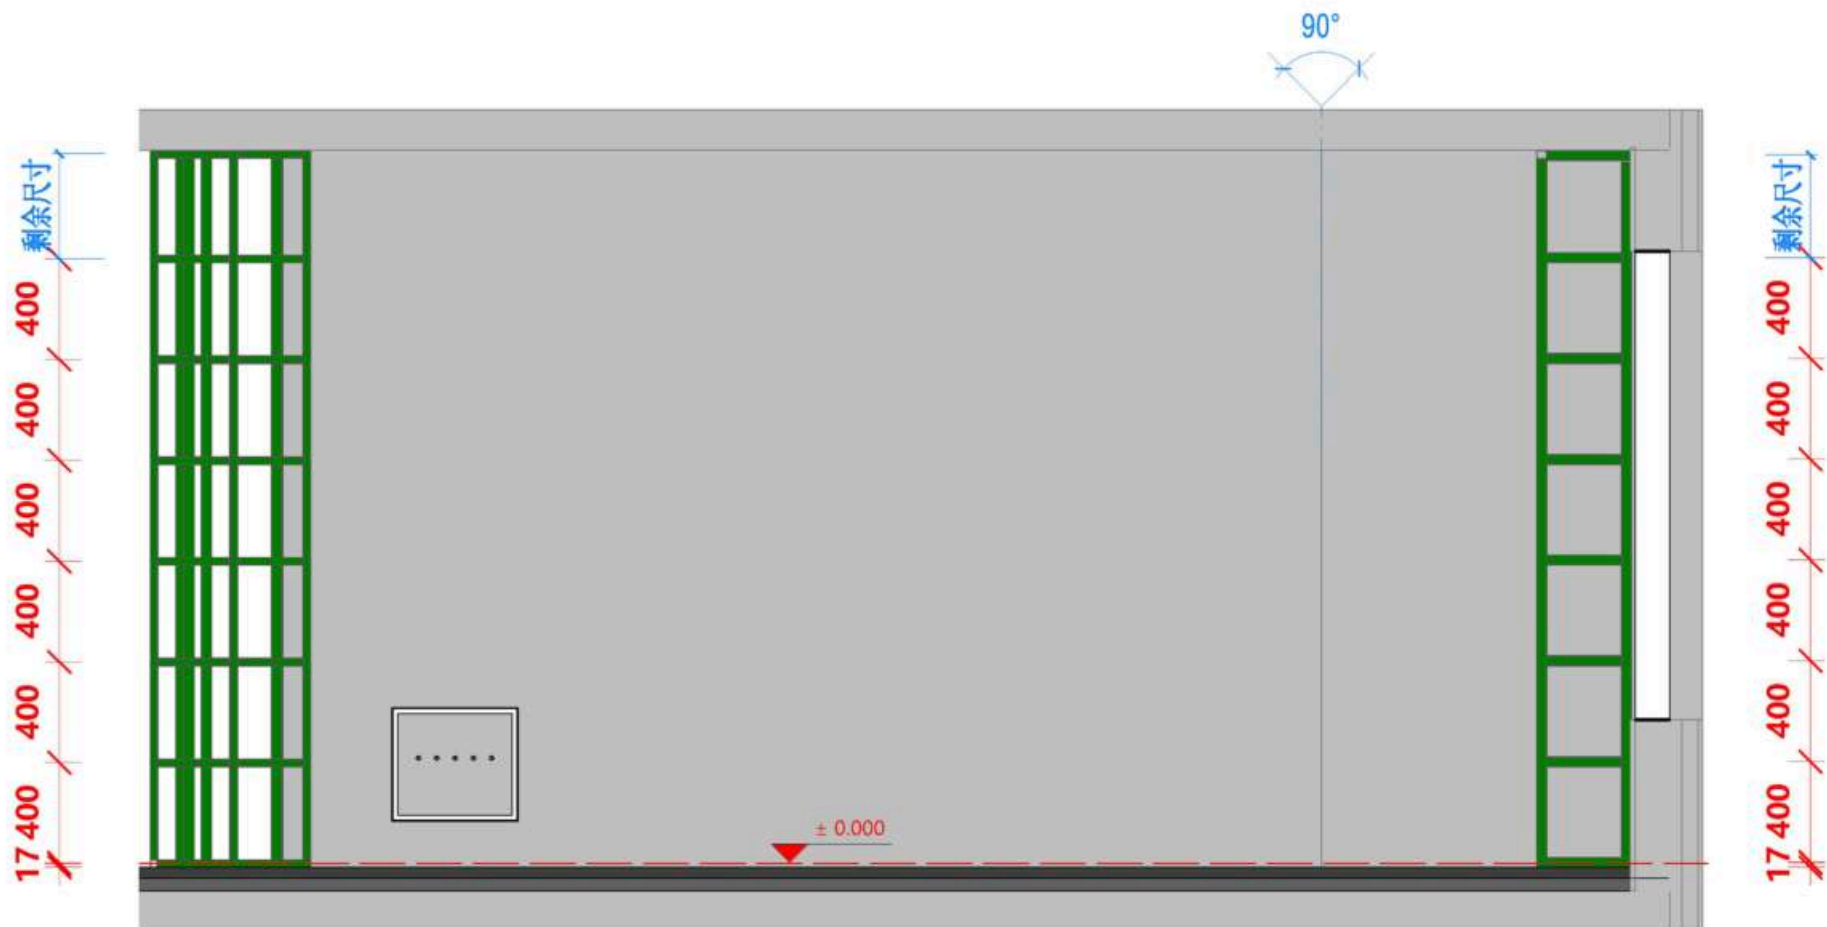

ELBORNI

LEGEND图例

编号	图例	说明
1		抹灰层 (≈15mm)
2		混凝土止水坎上 加5mm钢板
3		钢架墙

日期
Date 01/11/26

修订
Revision

项目
Project 潮映华府3-801

Scale
比例 1:30@A2

钢架墙04

Drawing No.
图纸编号 36-SW-04




Project No.
项目编号 ©2025

1 钢架墙立面图04
EL-04 Scale比例 1 : 30@A2

1 3D-04

钢架墙三维图04
Scale比例 1:30@A2

注释
Notes
1.本图纸如与现场尺寸有误，请施工人员与项目负责人联系。
2.施工前施工人员应认真查阅此图，如有不明确尺寸，按现场测量为准。
3.本图纸必须经甲乙双方认可并签字方可作为施工依据。

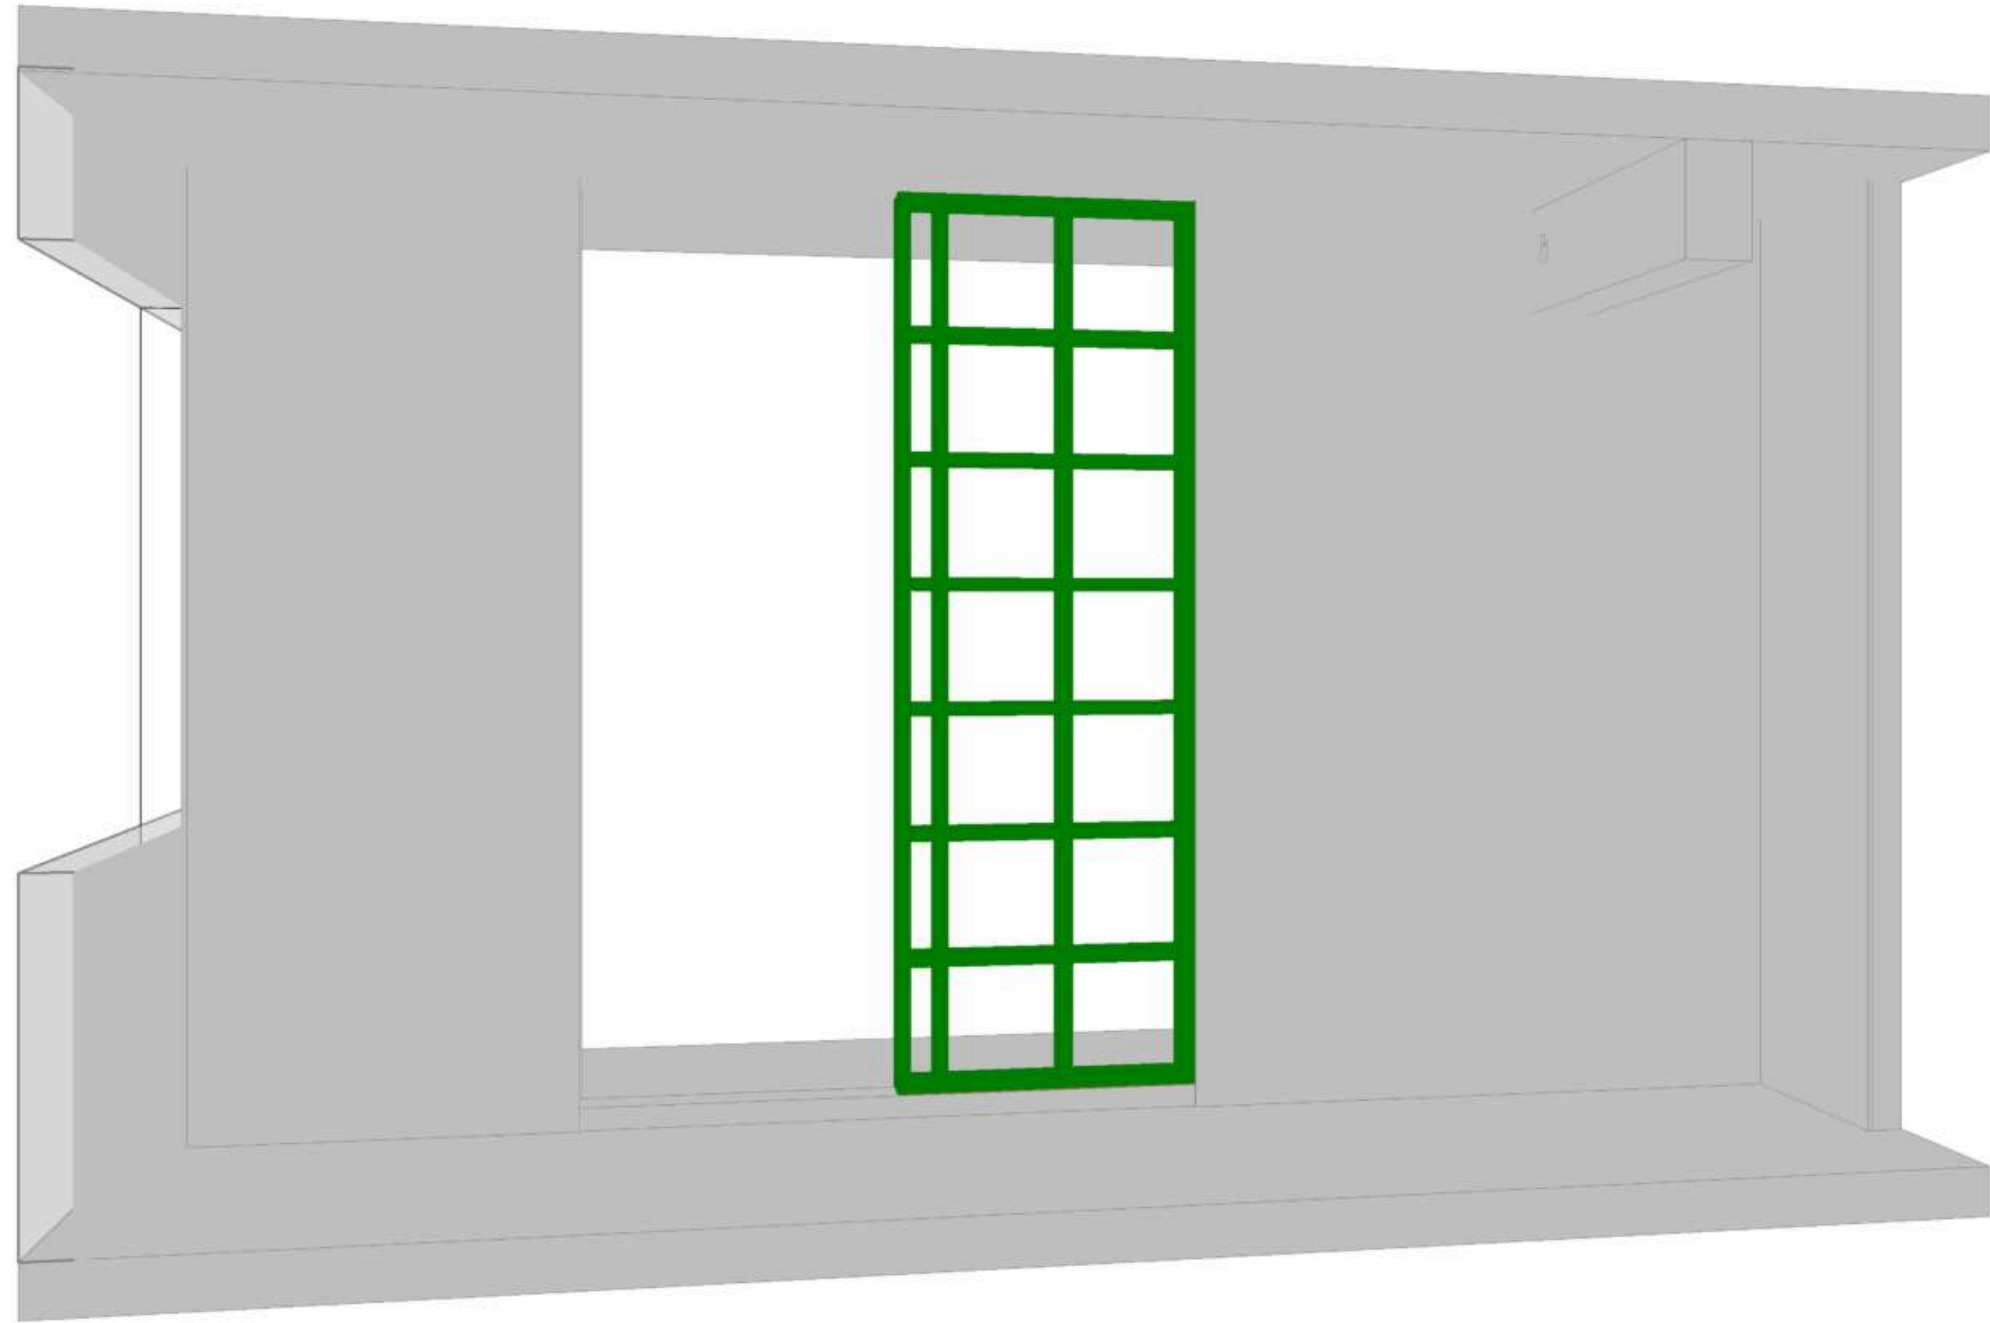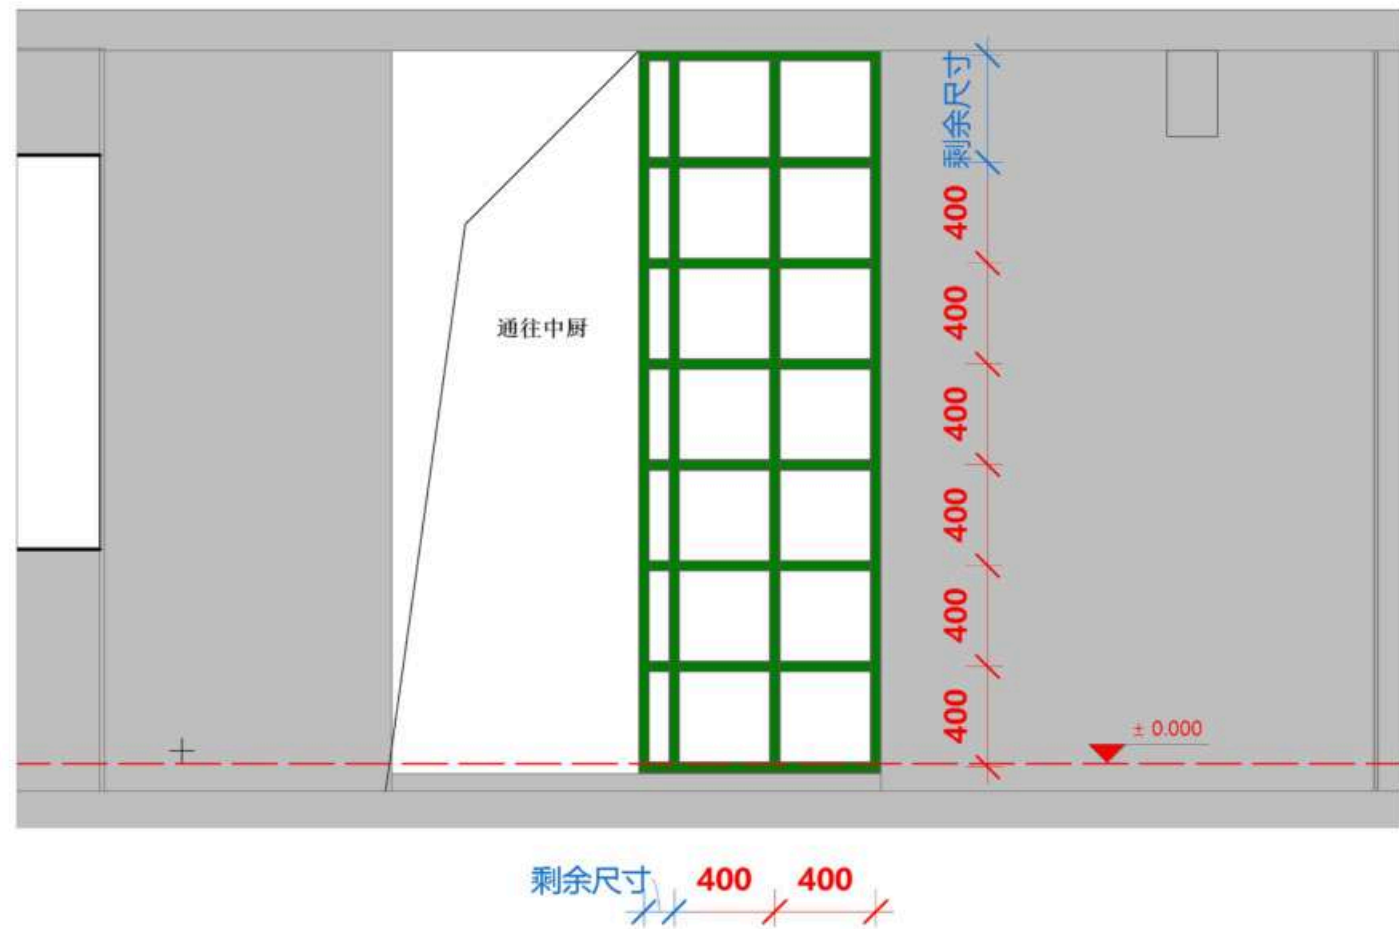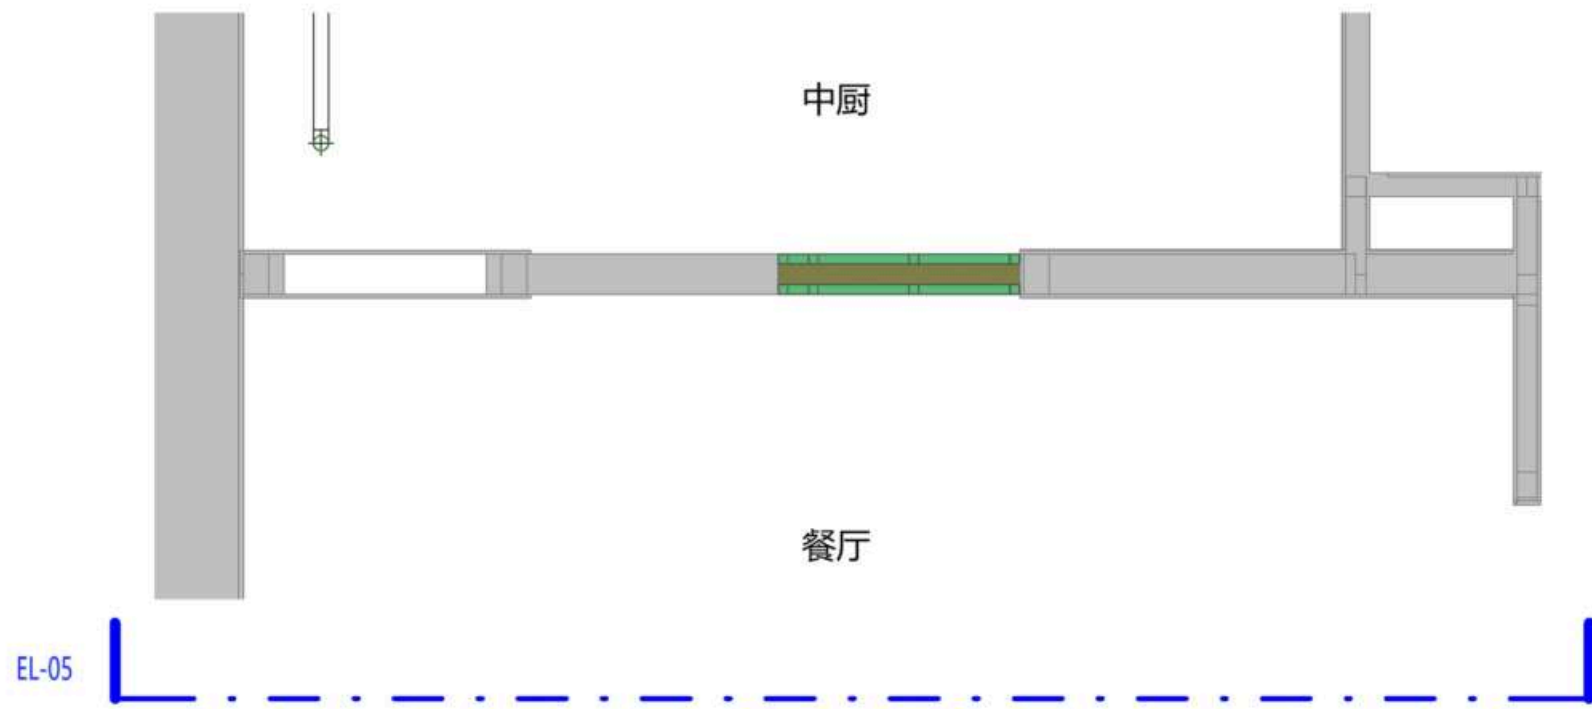

LIBORNI

LEGEND图例

编号	图例	说明
1		抹灰层 (≈15mm)
2		混凝土止水坎上 加5mm钢板
3		钢架墙

日期
Date

01/11/26

修订
Revision

项目
Project

潮映华岸府3-801

Scale
比例

1:30@A2

钢架墙05

Drawing No.
图纸编号

37-SW-05

Project No.
项目编号

©2025

1

EL-05

钢架墙立面图05

Scale比例 1 : 30@A2

1

3D-05




钢架墙三维图05

Scale比例 1:30@A2

注释

Notes

1.本图纸如与现场尺寸有误，请施工人员与项目负责人联系。
2.施工前施工人员应认真查阅此图，如有不明确尺寸，按现场测量为准。
3.本图纸必须经甲乙双方认可并签字方可作为施工依据。

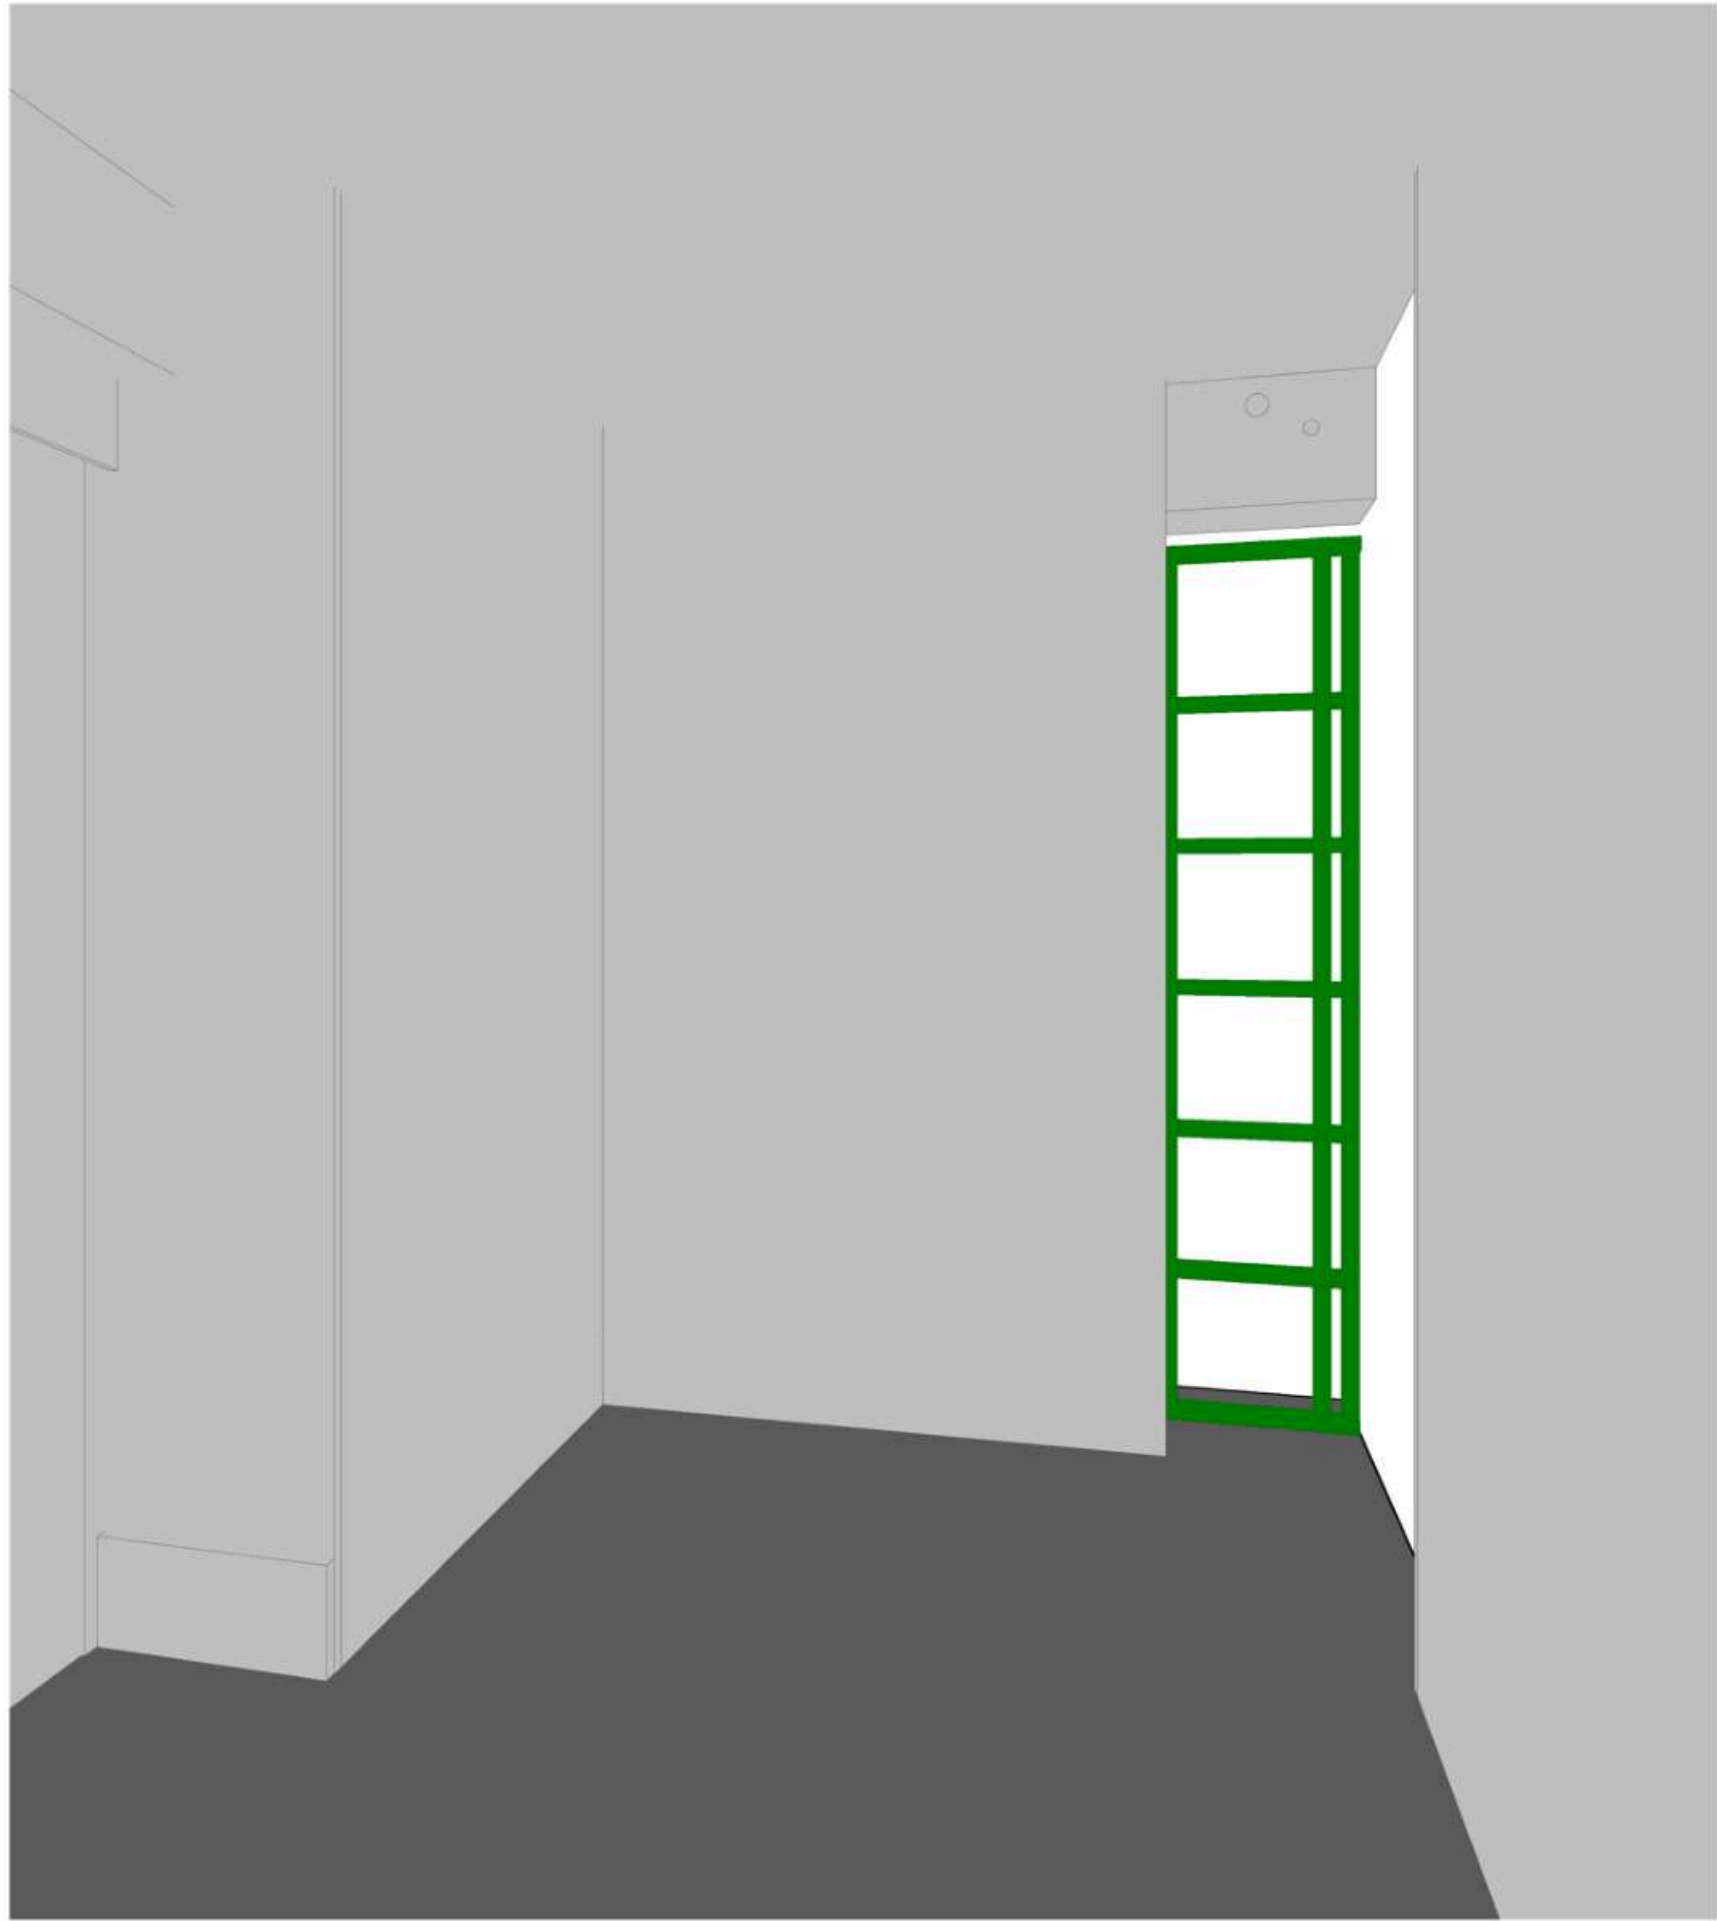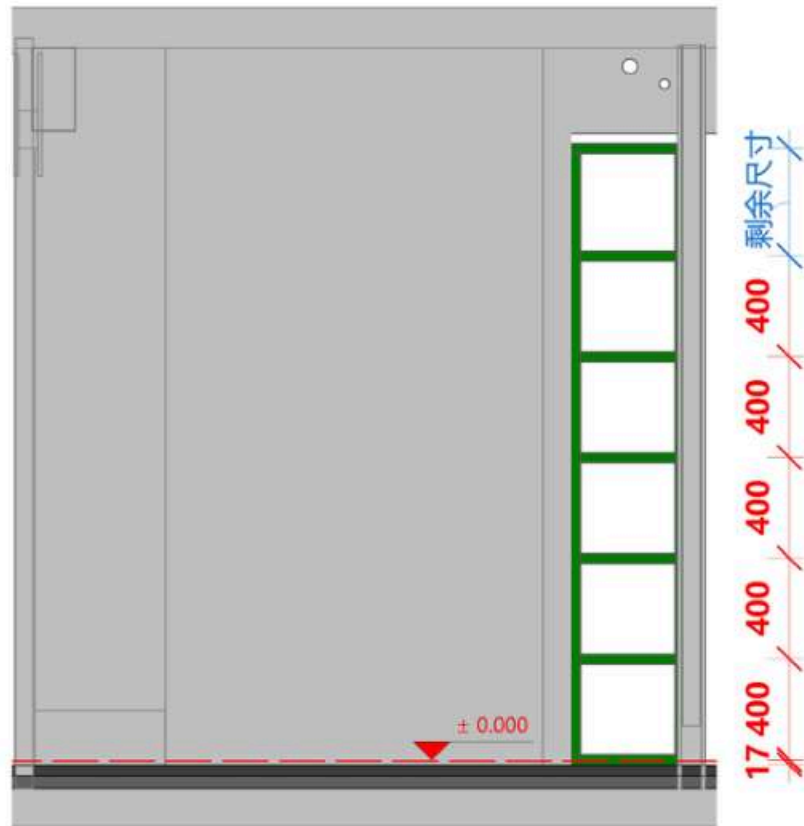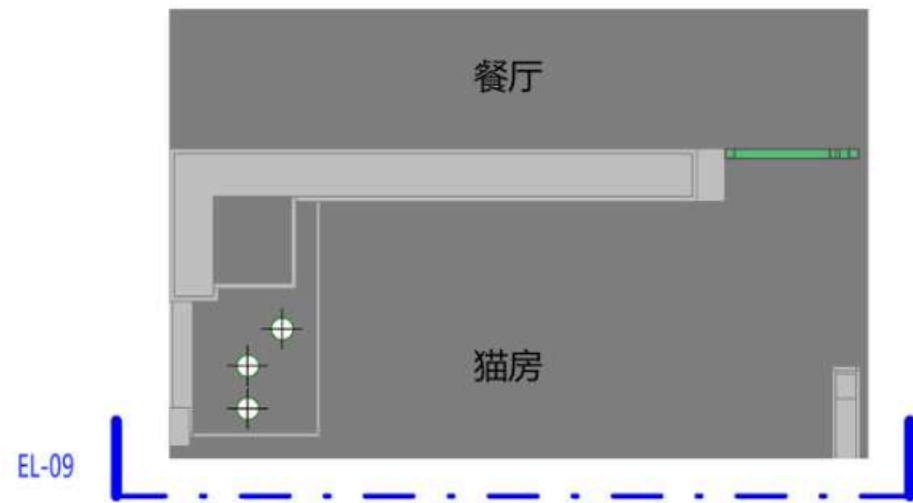

LEGEND图例

编号	图例	说明
1		抹灰层 (≈15mm)
2		混凝土止水坎上 加5mm钢板
3		钢架墙

日期
Date 01/11/26

修订
Revision

项目
Project
潮映华府3-801

Scale
比例 1:30@A2
钢架墙09

Drawing No.
图纸编号 38-SW-09

Project No.
项目编号 ©2025

1

EL-09

钢架墙立面图09

Scale比例 1 : 30@A2

1

3D-09



钢架墙三维图09

Scale比例 1:30@A2

注释

Notes

- 1.本图纸如与现场尺寸有误, 请施工人员与项目负责人联系。
- 2.施工前施工人员应认真查阅此图, 如有不明确尺寸, 按现场测量为准。
- 3.本图纸必须经甲乙双方认可并签字方可作为施工依据。

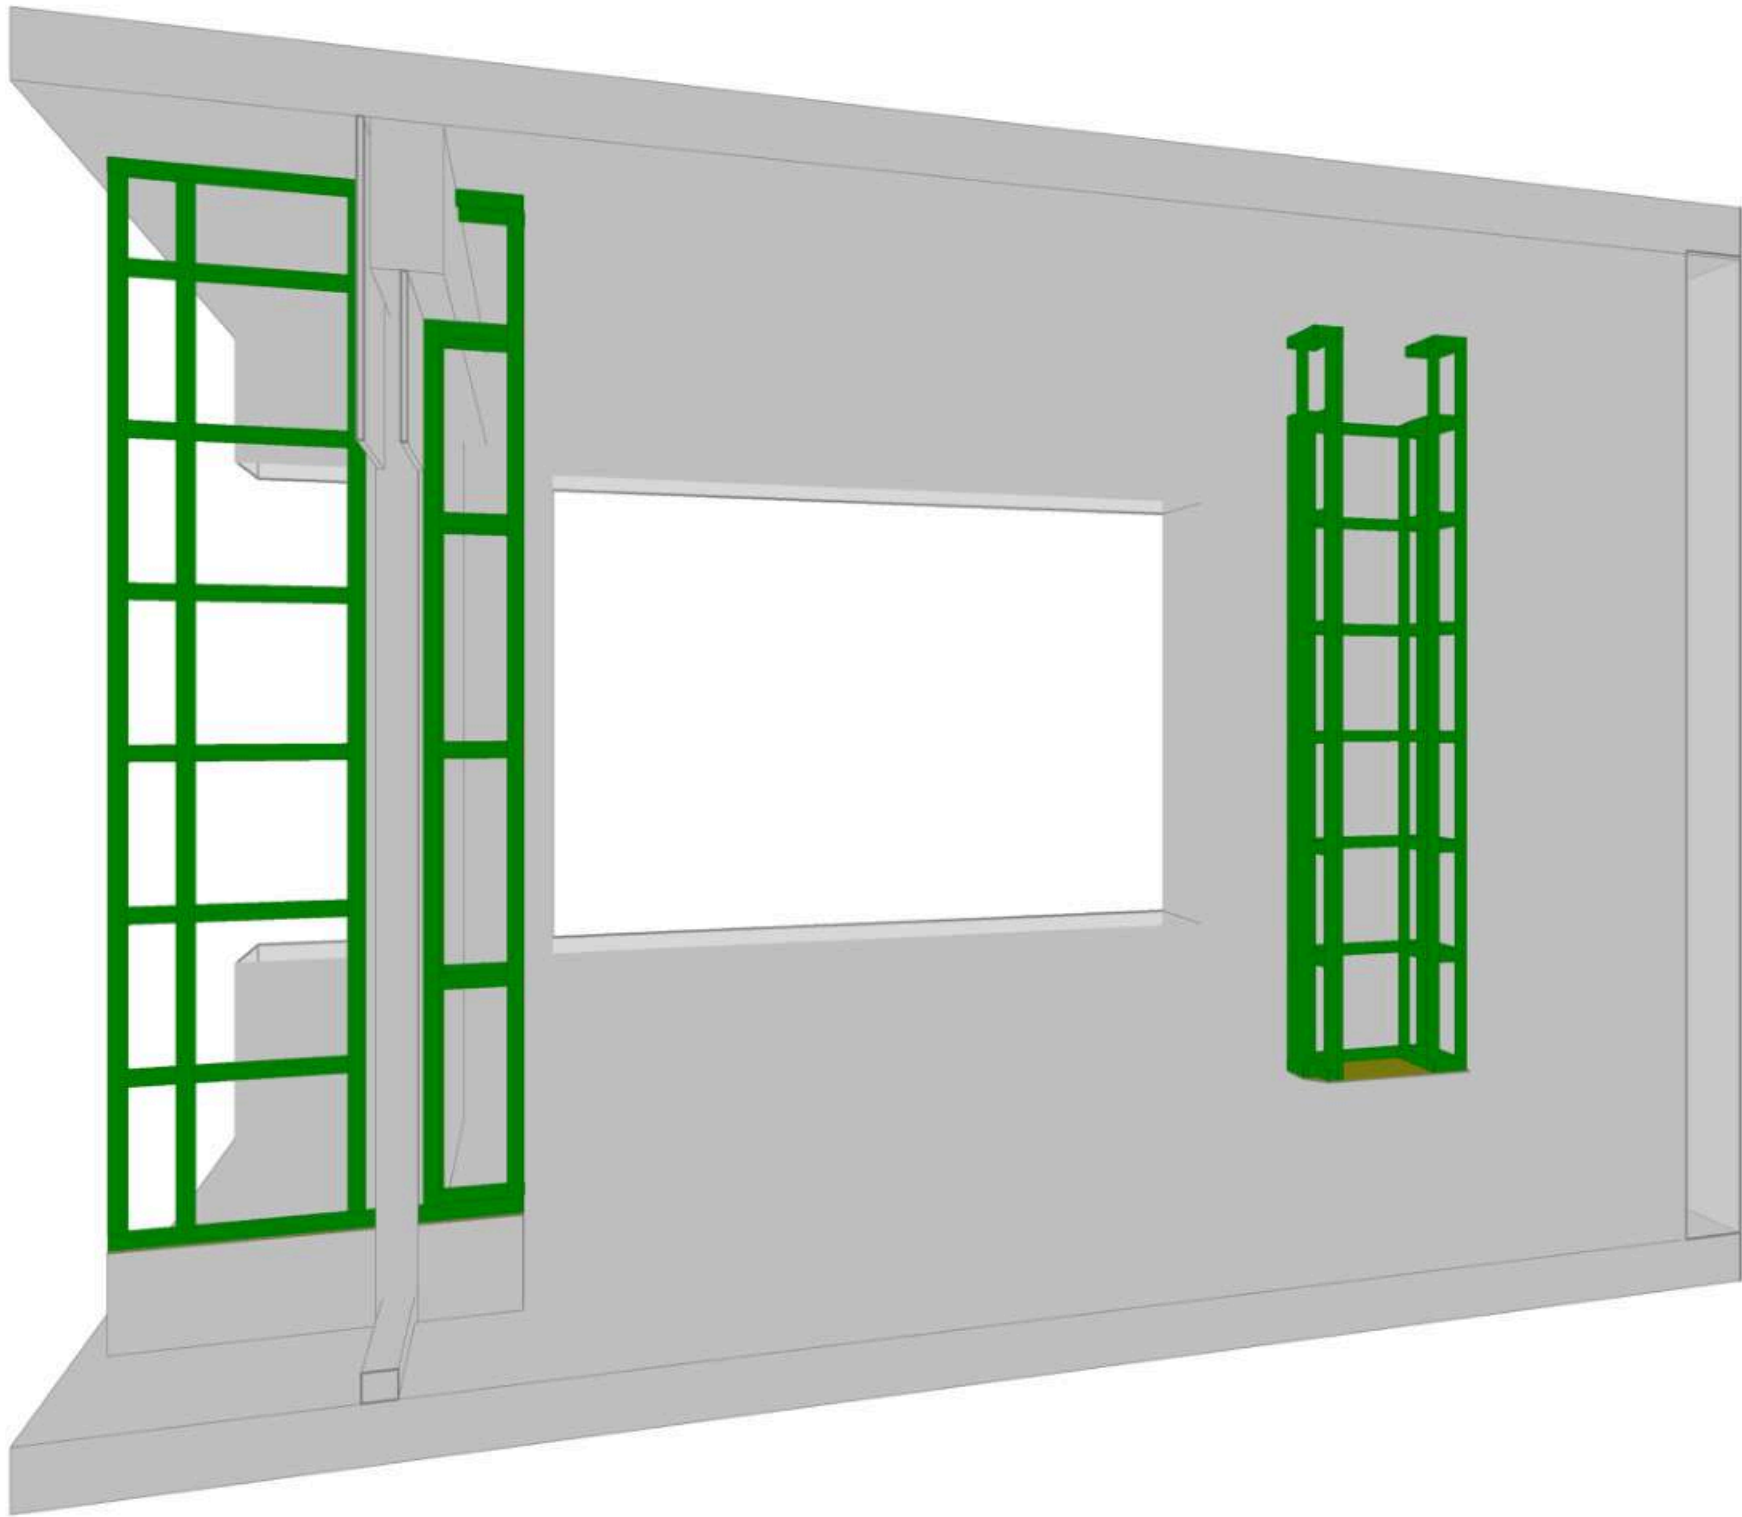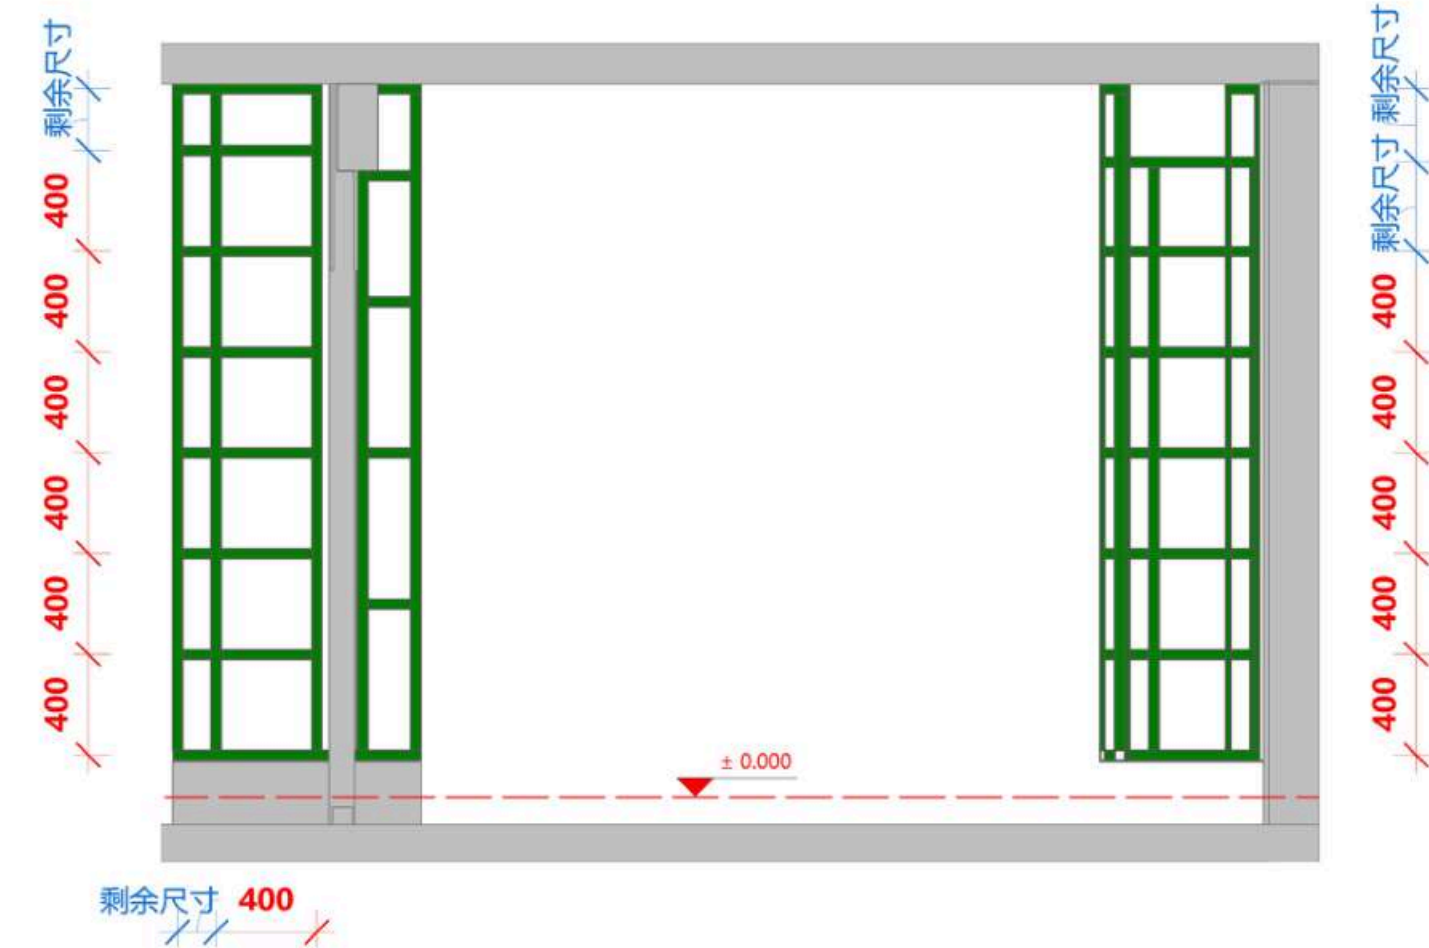

LEGEND图例

编号	图例	说明
1		抹灰层 (≈15mm)
2		混凝土止水坎上 加5mm钢板
3		钢架墙

日期
Date

01/11/26

修订
Revision

项目
Project

潮映华府3-801

Scale
比例

1:30@A2

钢架墙13

Drawing No.
图纸编号

40-SW-13

Project No.
项目编号

©2025

1

EL-13

钢架墙立面图13

Scale比例 1 : 30@A2

1

3D-13




钢架墙三维图13

Scale比例 1:30@A2

注释

Notes

- 1.本图纸如与现场尺寸有误差, 请施工人员与项目负责人联系。
- 2.施工前施工人员应认真查阅此图, 如有不明确尺寸, 按现场测量为准。
- 3.本图纸必须经甲乙双方认可并签字方可作为施工依据。

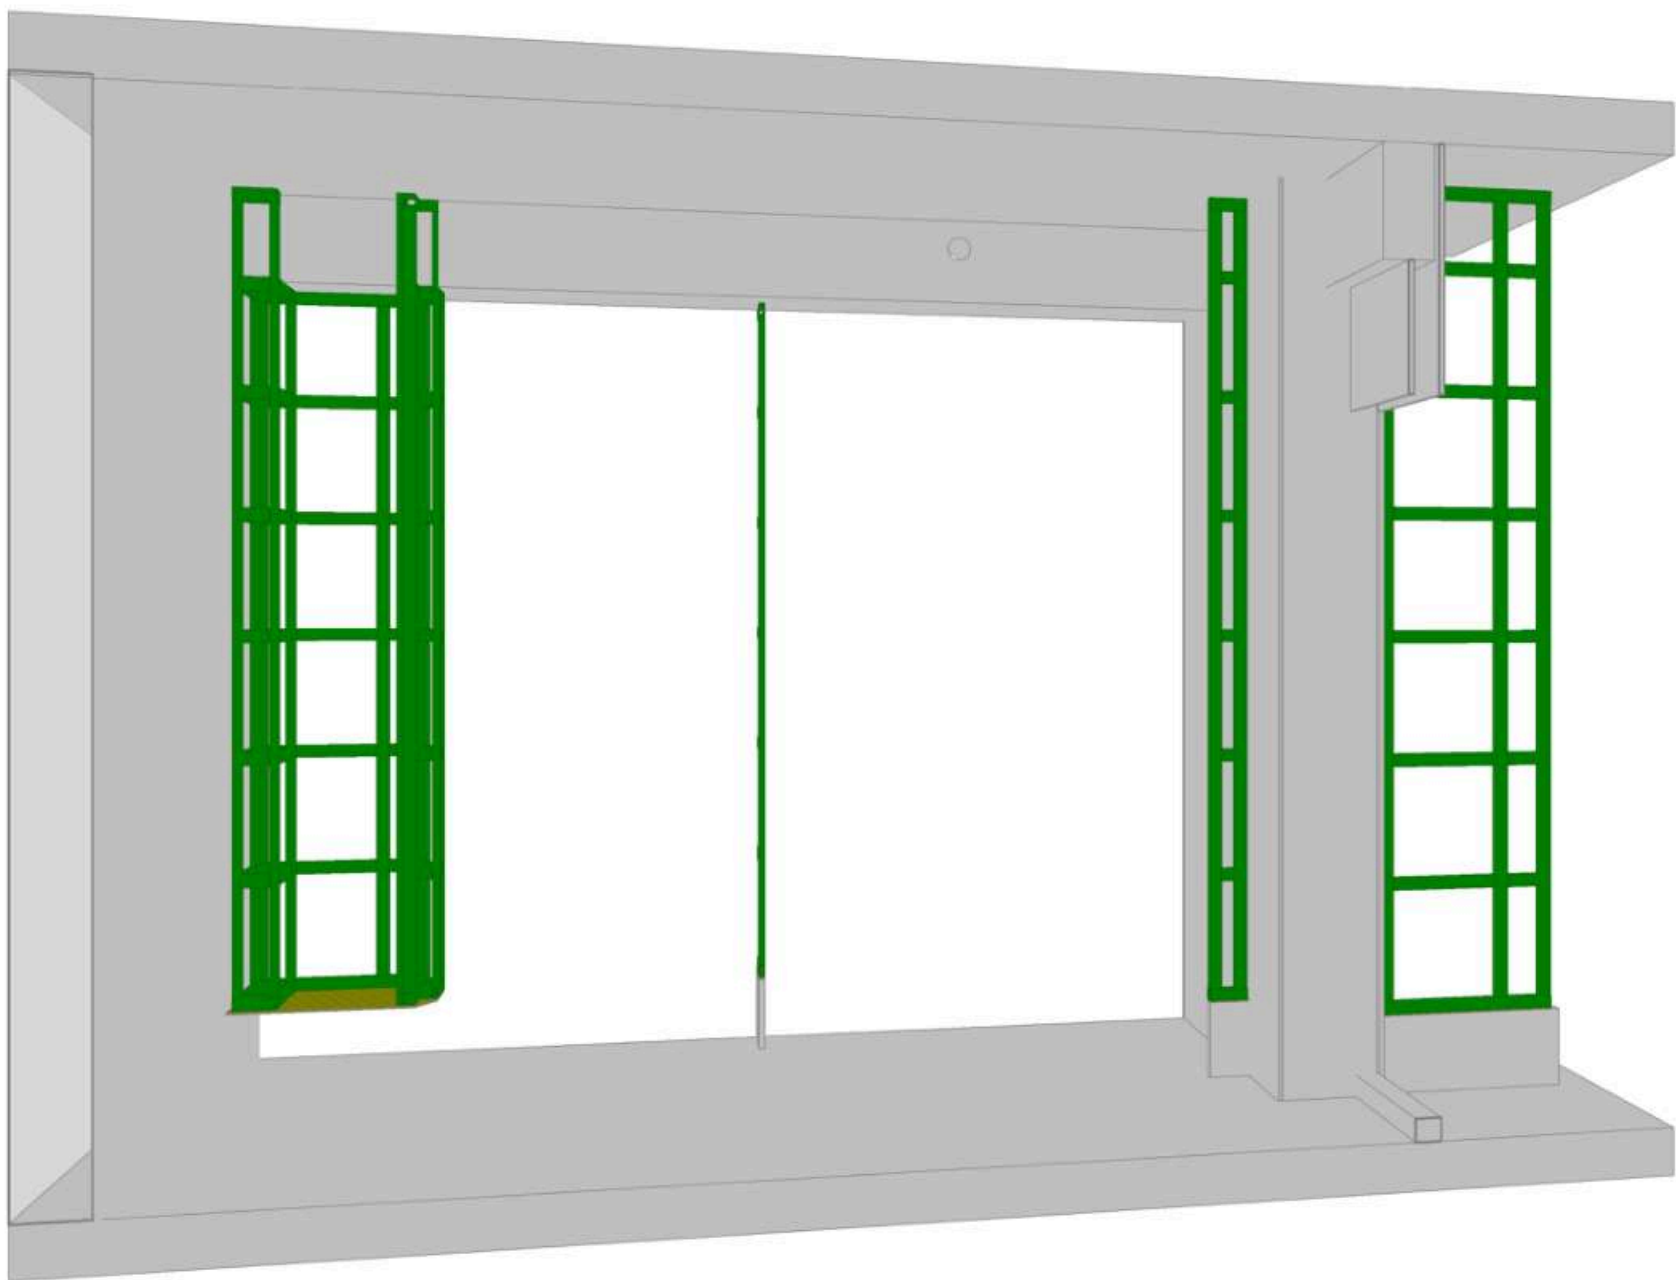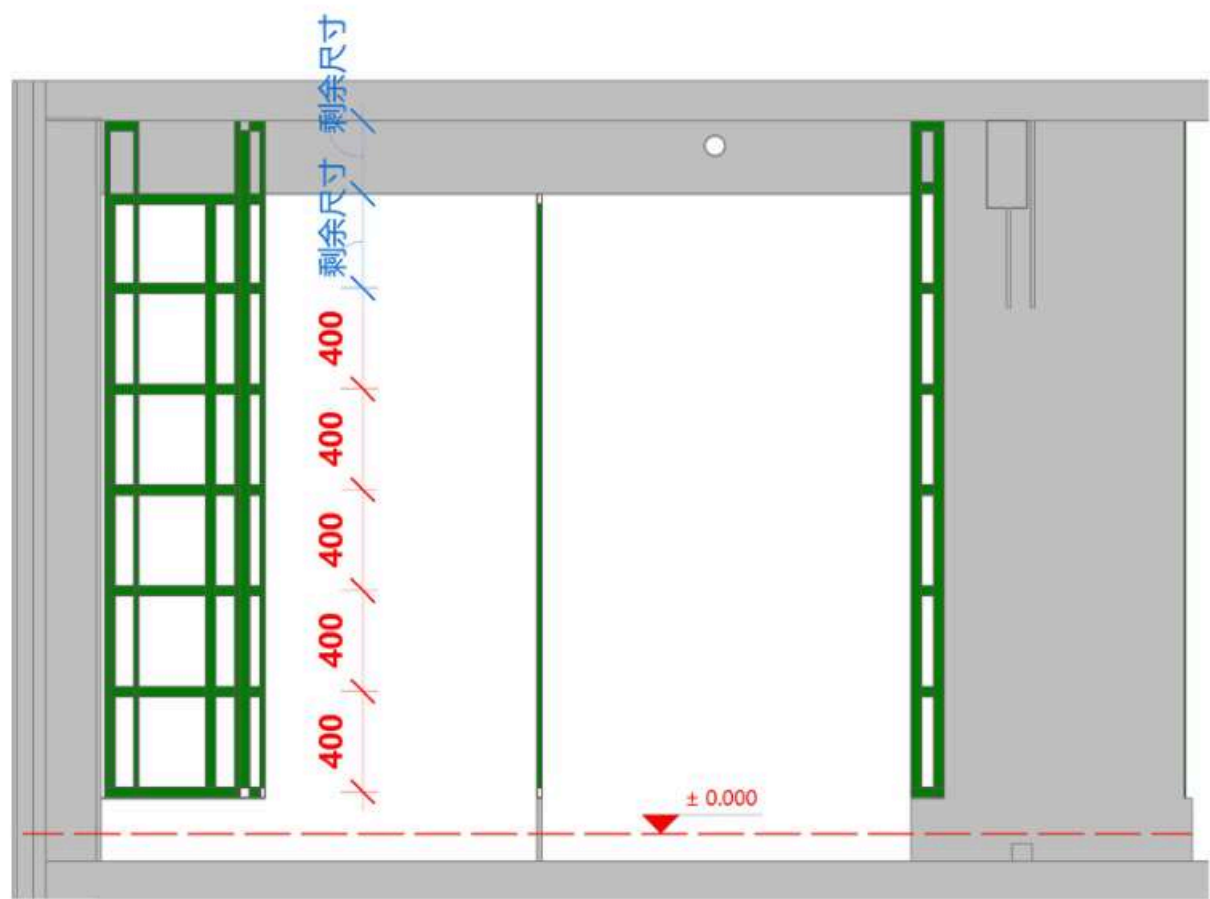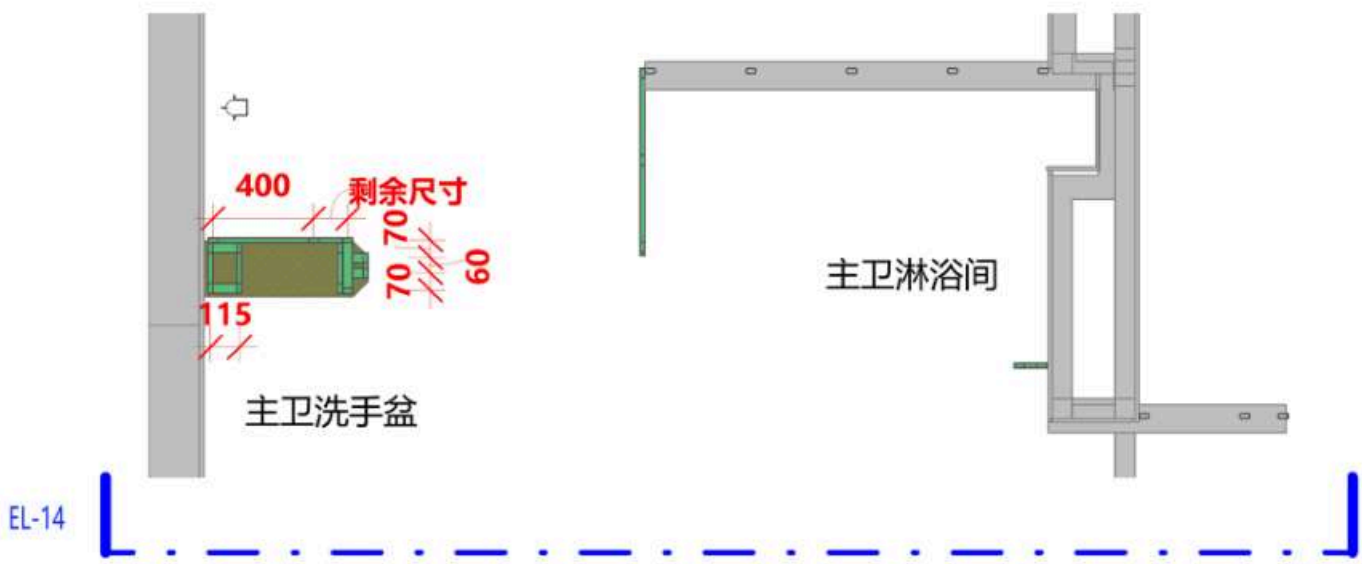

EL-14

LEGEND图例

编号	图例	说明
1		抹灰层 (≈15mm)
2		混凝土止水坎上 加5mm钢板
3		钢架墙

日期
Date

01/11/26

修订
Revision

项目
Project

潮映华府3-801

Scale
比例

1:30@A2

钢架墙14

Drawing No.
图纸编号

41-SW-14

Project No.
项目编号

©2025

1

钢架墙立面图14

Scale比例 1 : 30@A2

EL-14

1

钢架墙三维图14

Scale比例 1:30@A2

3D-14

注释

Notes

1.本图纸如与现场尺寸有误差, 请施工人员与项目负责人联系。
2.施工前施工人员应认真查阅此图, 如有不明确尺寸, 按现场测量为准。
3.本图纸必须经甲乙双方认可并签字方可作为施工依据。

LEGEND图例

编号	图例	说明
1		抹灰层 (≈15mm)
2		混凝土止水坎上 加5mm钢板
3		钢架墙

日期
Date

01/11/26

修订

Revision

项目

Project

潮映华府3-801

Scale

比例

1:30@A2

钢架墙17

Drawing No.




图纸编号

42-SW-17

Project No.

项目编号

©2025

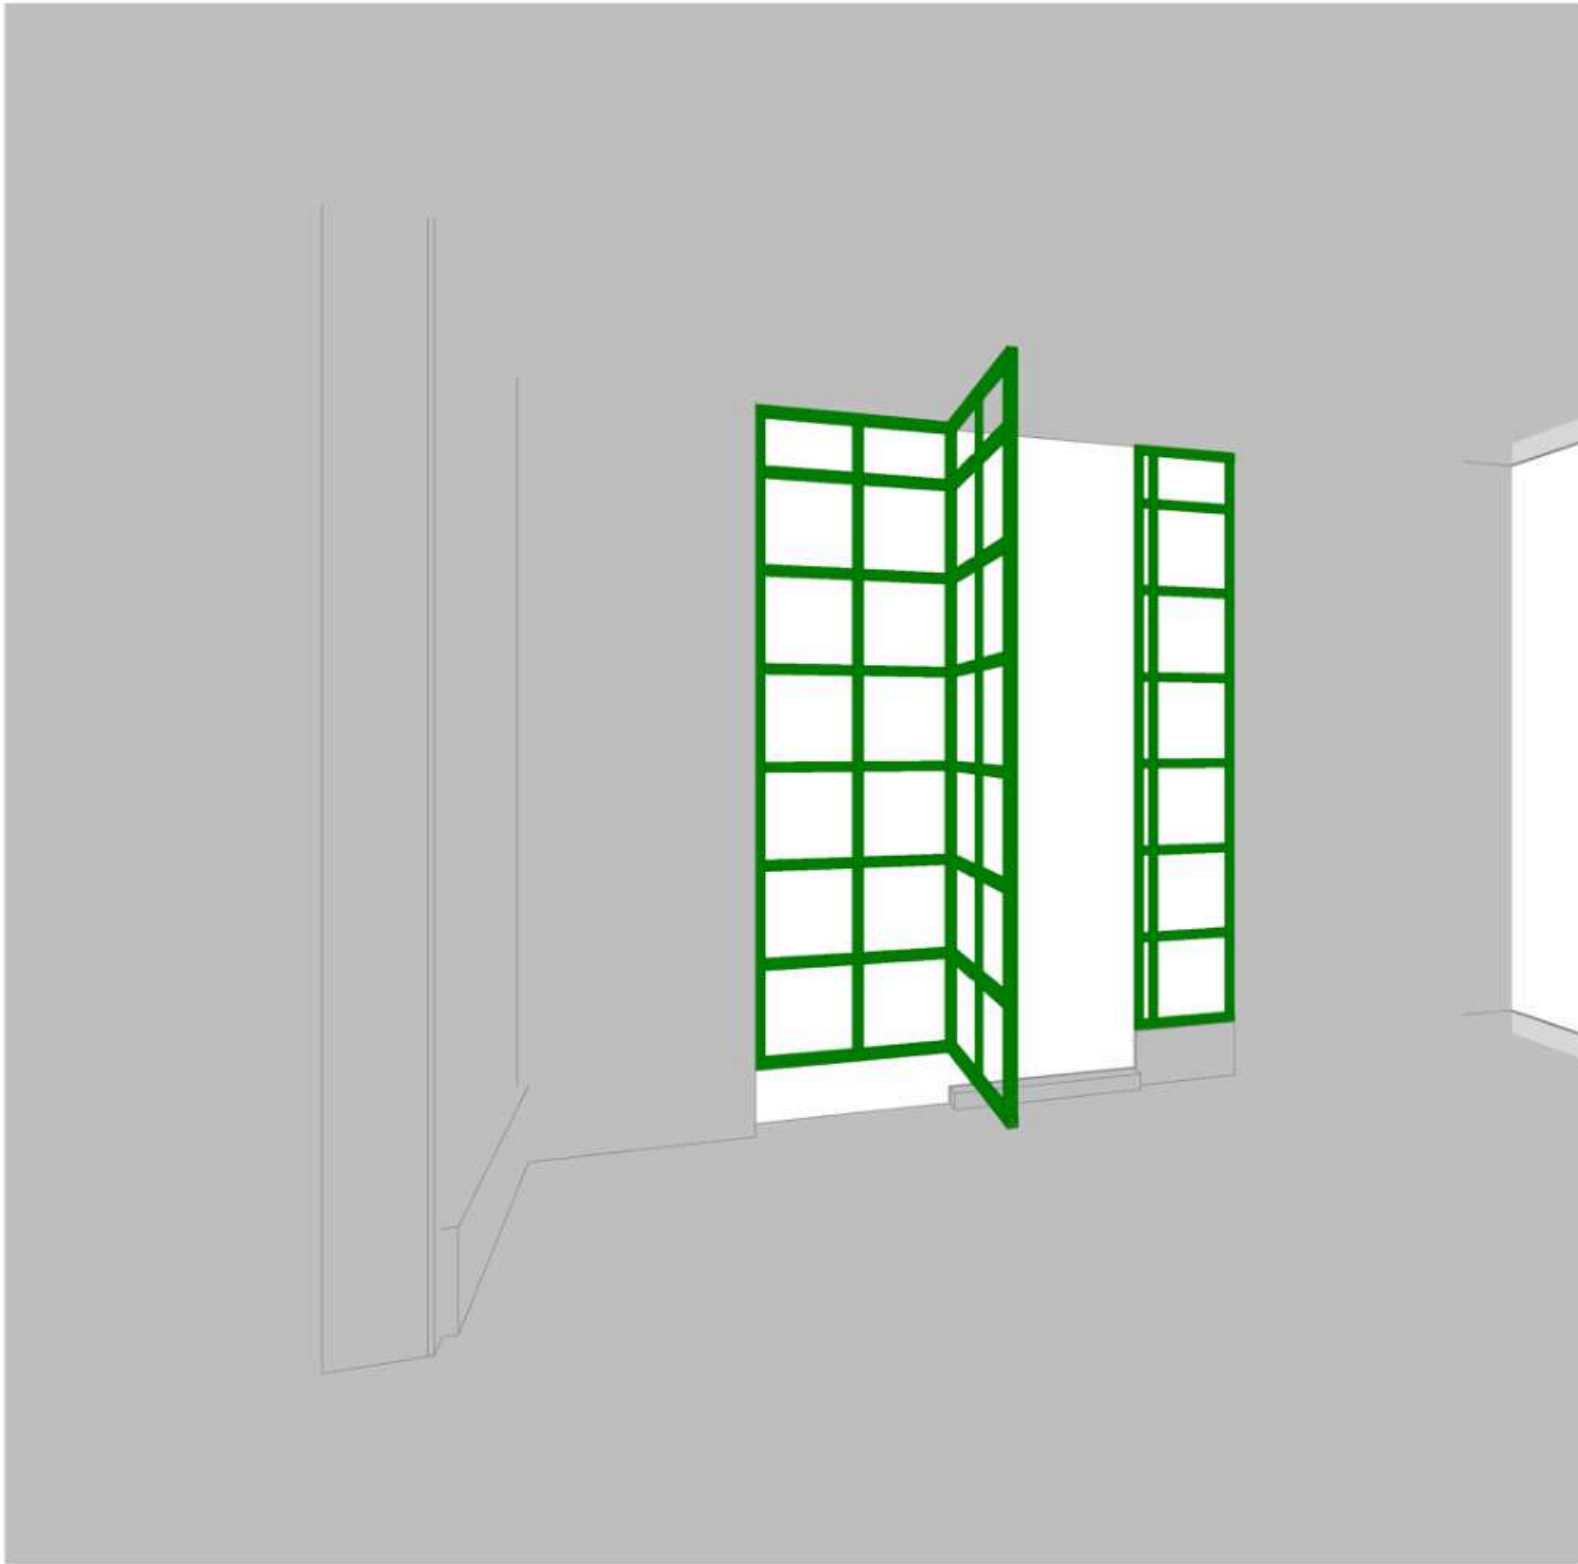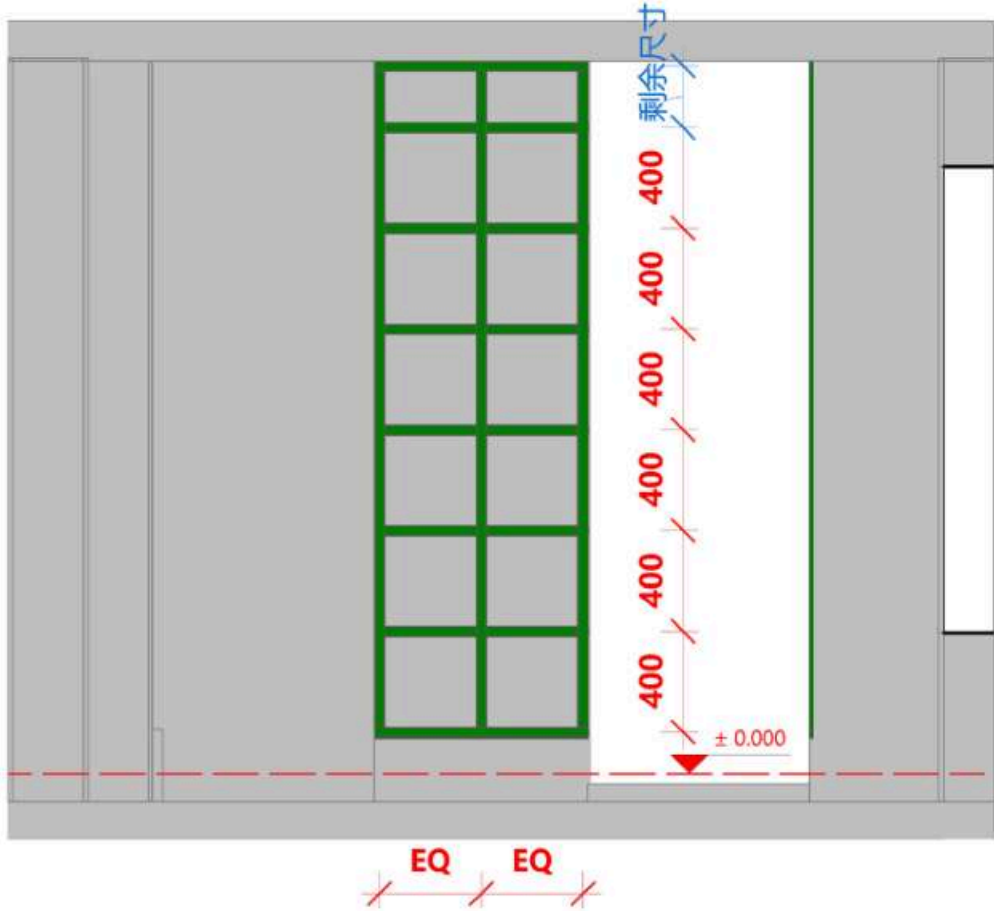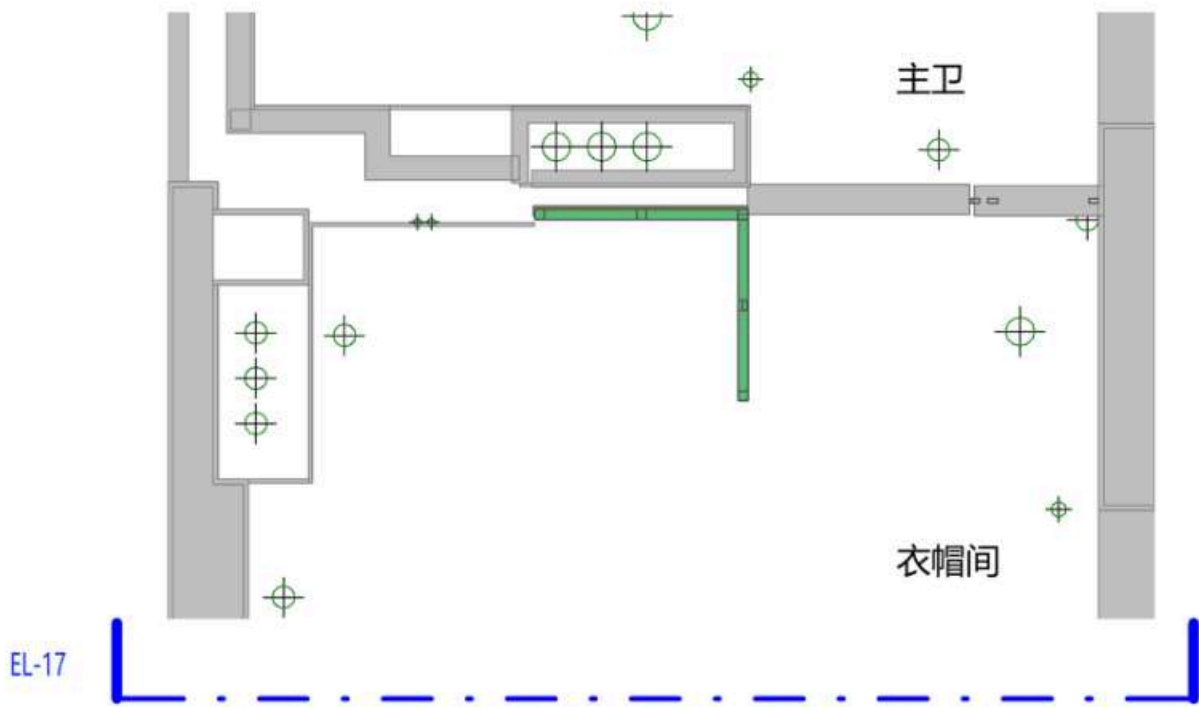

1

钢架墙立面图17

Scale比例 1 : 30@A2

1



钢架墙三维图17

Scale比例 1:30@A2

注释

Notes

- 1.本图纸如与现场尺寸有误, 请施工人员与项目负责人联系。
- 2.施工前施工人员应认真查阅此图, 如有不明确尺寸, 按现场测量为准。
- 3.本图纸必须经甲乙双方认可并签字方可作为施工依据。

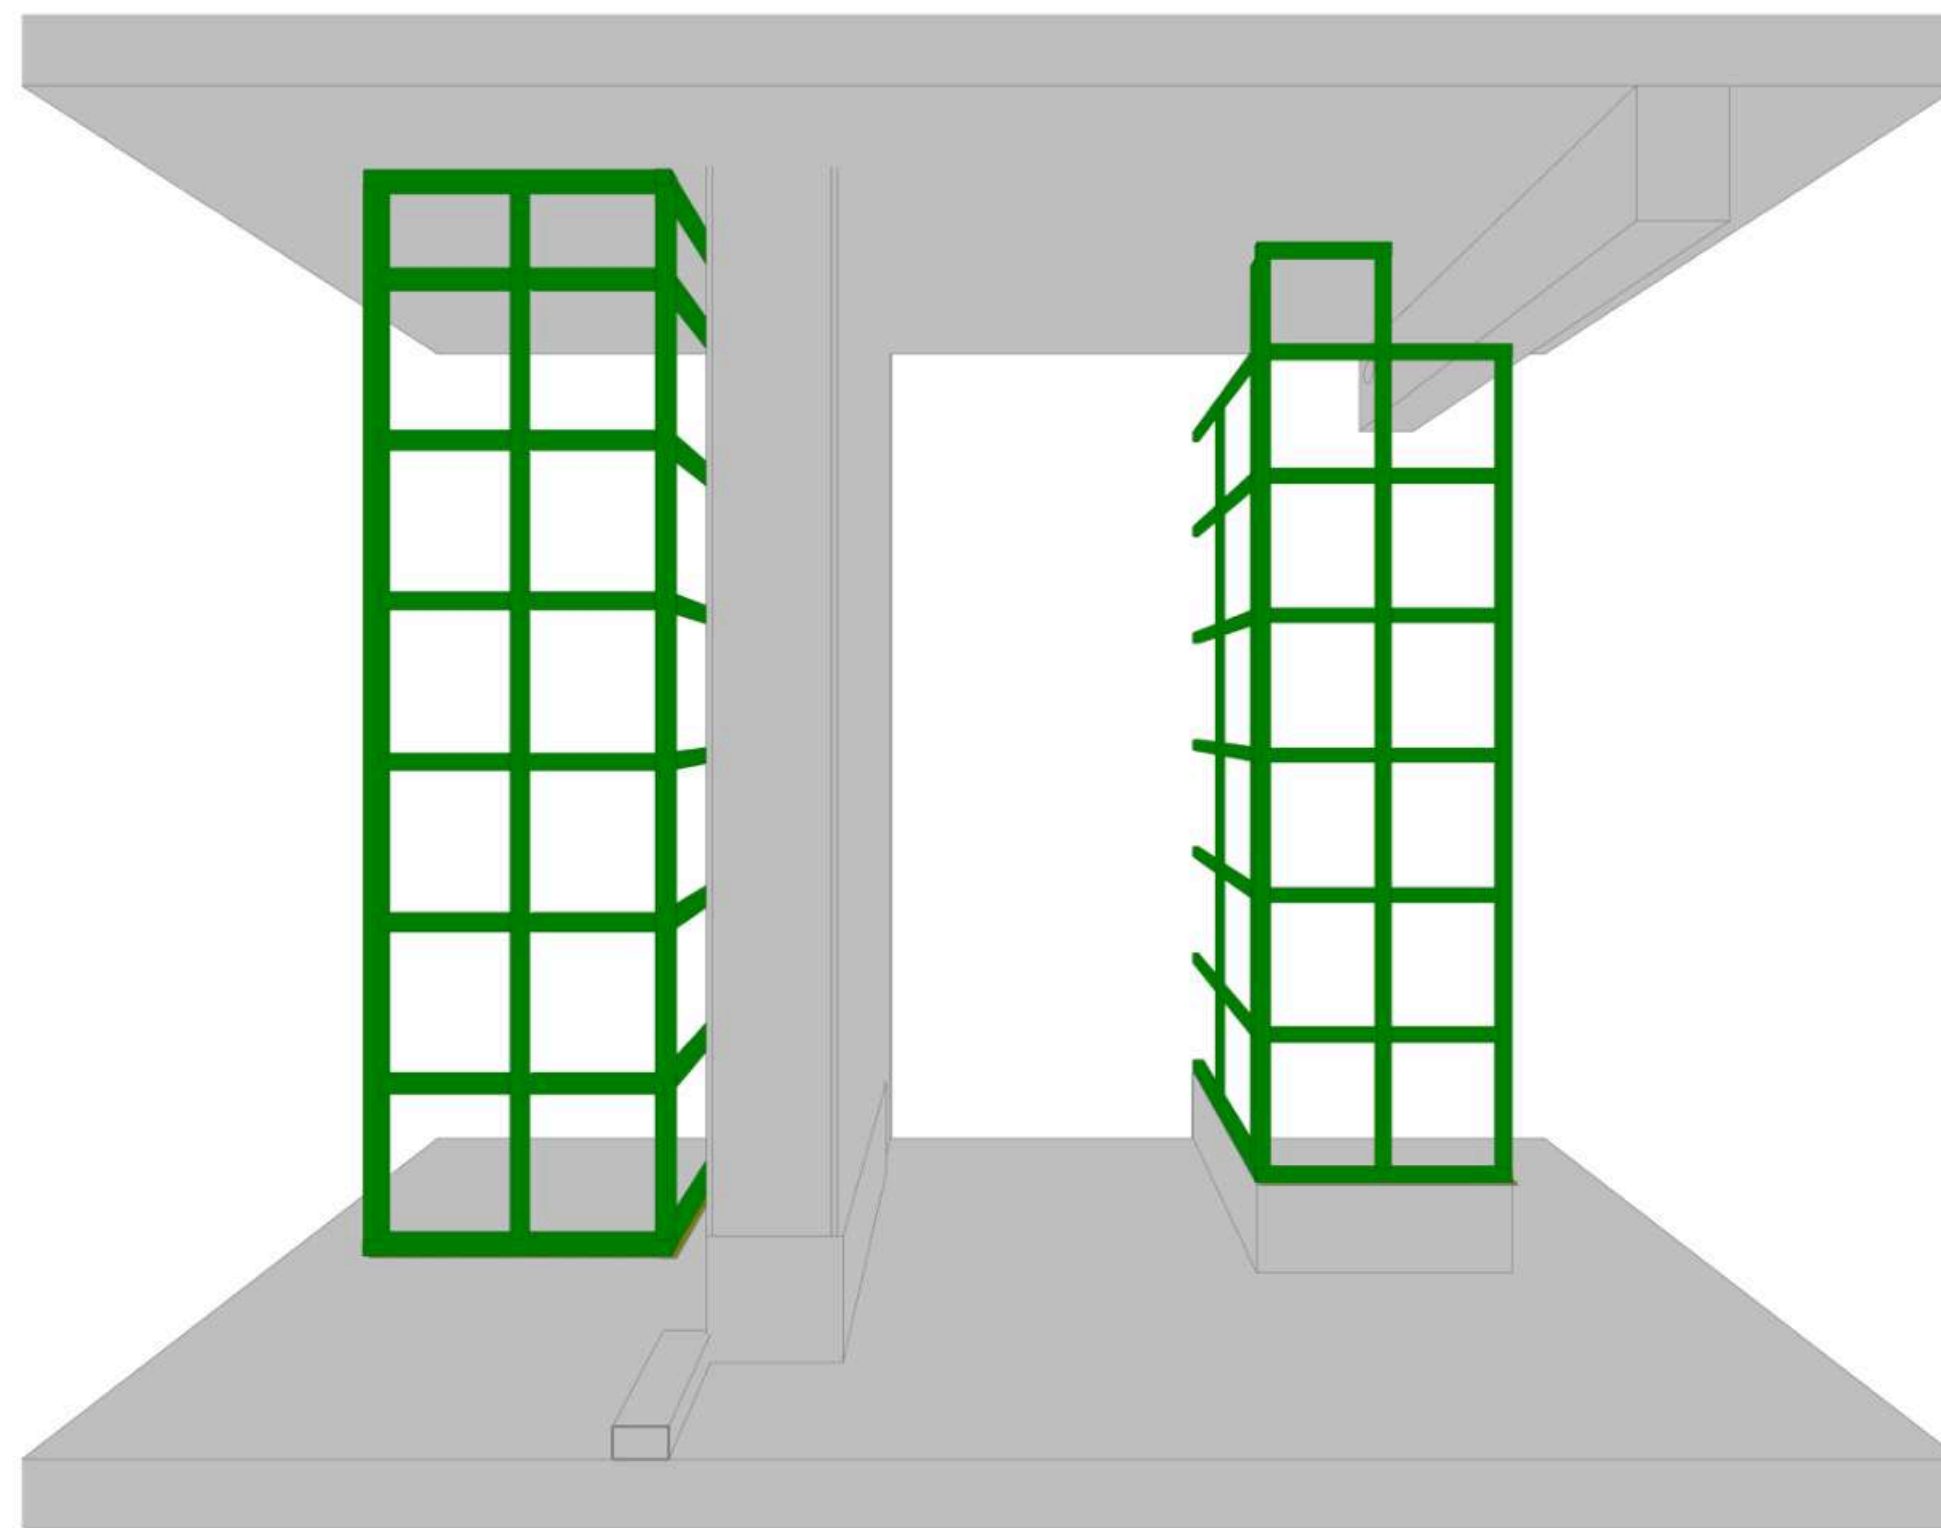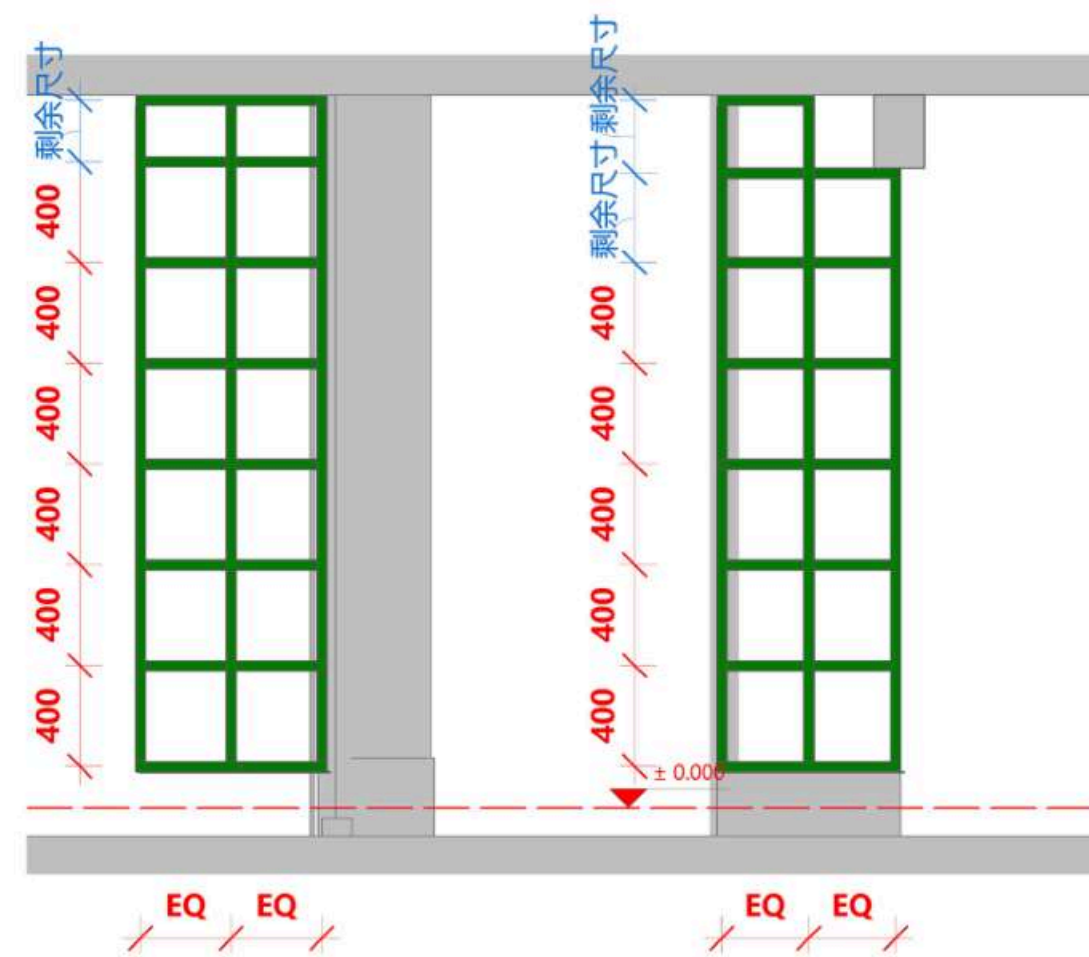

LEGEND图例

编号	图例	说明
1		抹灰层 (≈15mm)
2		混凝土止水坎上 加5mm钢板
3		钢架墙

日期
Date

01/11/26

修订
Revision

项目
Project

潮映华府3-801

Scale
比例

1:30@A2

钢架墙18

Drawing No.
图纸编号

43-SW-18

Project No.
项目编号

©2025

1

EL-18

钢架墙立面图18

Scale比例 1 : 30@A2

1


3D-18

钢架墙三维图18

Scale比例 1:30@A2

注释
Notes

1.本图纸如与现场尺寸有误, 请施工人员与项目负责人联系。
2.施工前施工人员应认真查阅此图, 如有不明确尺寸, 按现场测量为准。
3.本图纸必须经甲乙双方认可并签字方可作为施工依据。

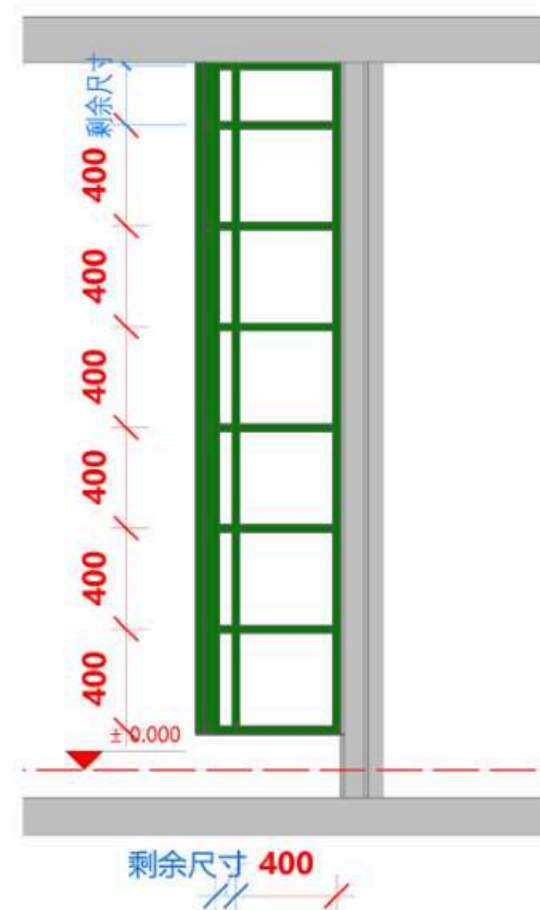


编号	图例	说明
1		抹灰层 (≈15mm)
2		混凝土止水坎上 加5mm钢板
3		钢架墙

Project No. © 2025
项目编号

注释
Notes

- 1.本图纸如与现场尺寸有误，请施工人员与项目负责人联系。
- 2.施工前施工人员应认真查阅此图，如有不明确尺寸，按现场测量为准。
- 3.本图纸必须经甲乙双方认可并签字方可作为施工依据。

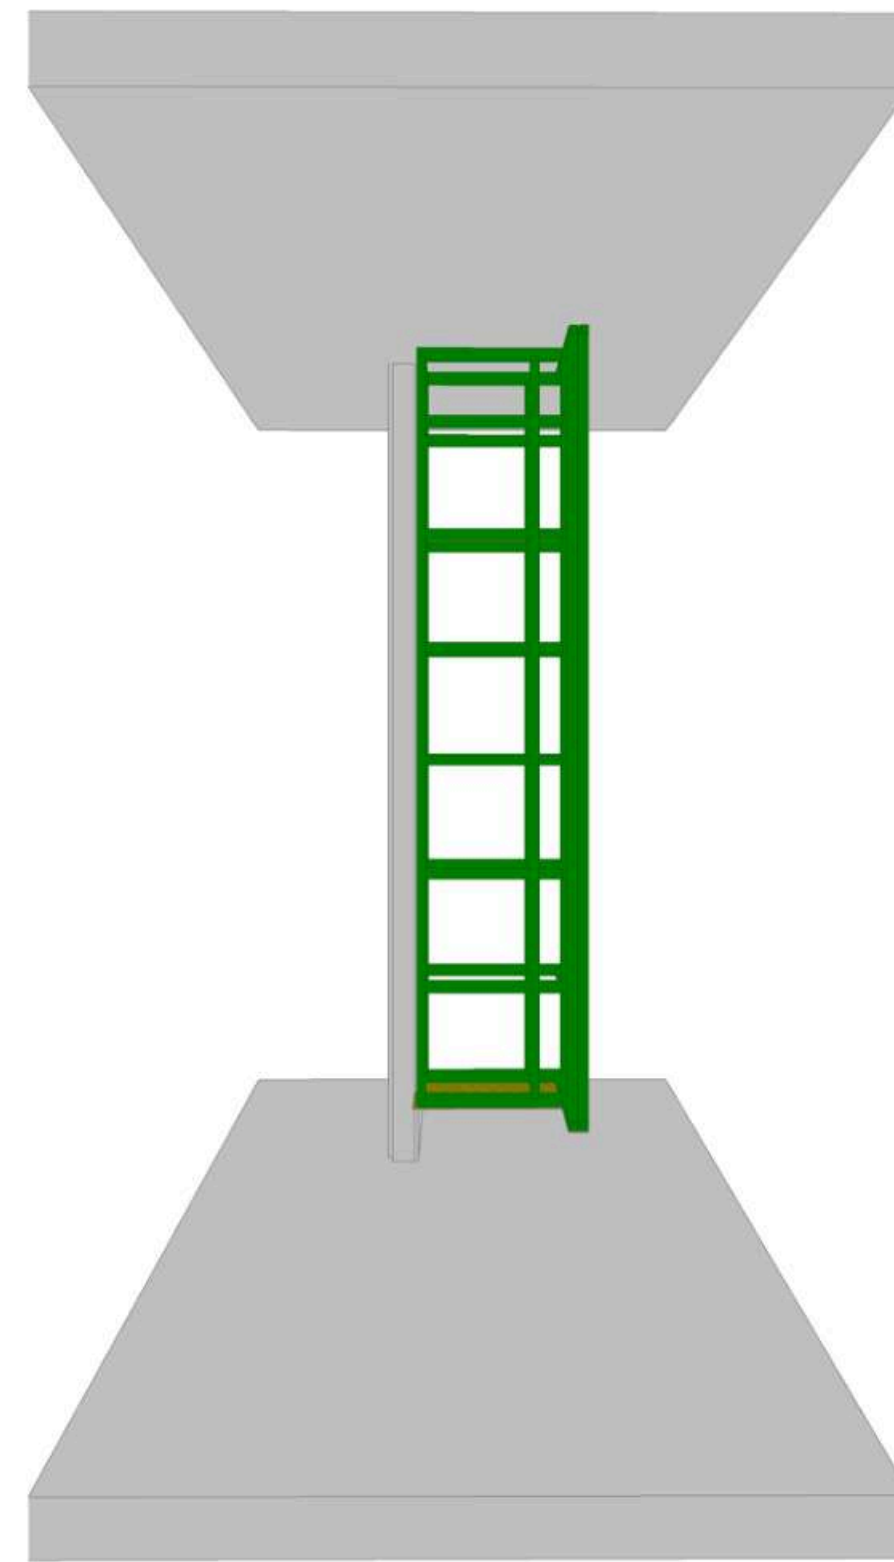

⇒|||30KRN|

LEGEND图例

编号	图例	说明
1		抹灰层 (≈15mm)
2		混凝土止水坎上 加5mm钢板
3		钢架墙

日期
Date 01/11/26

修订
Revision

项目 Project	
---------------	--

潮映华岸府3-801

Scale	1:30@A
比例	



钢架墙22

Drawing No.
图纸编号

45-SW-22

Project No. ©2025
项目编号

1	钢架墙立面图22	1	钢架墙三维图22	注释 Notes 1.本图纸如与现场尺寸有误，请施工人员与项目负责人联系。 2.施工前施工人员应认真查阅此图，如有不明确尺寸，按现场测量为准。 3.本图纸必须经甲乙双方认可并签字方可作为施工依据。	45-SW-22
EL-22	Scale比例 1 : 30@A2	3D-22	Scale比例 1:30@A2		Project No. © 2025 项目编号

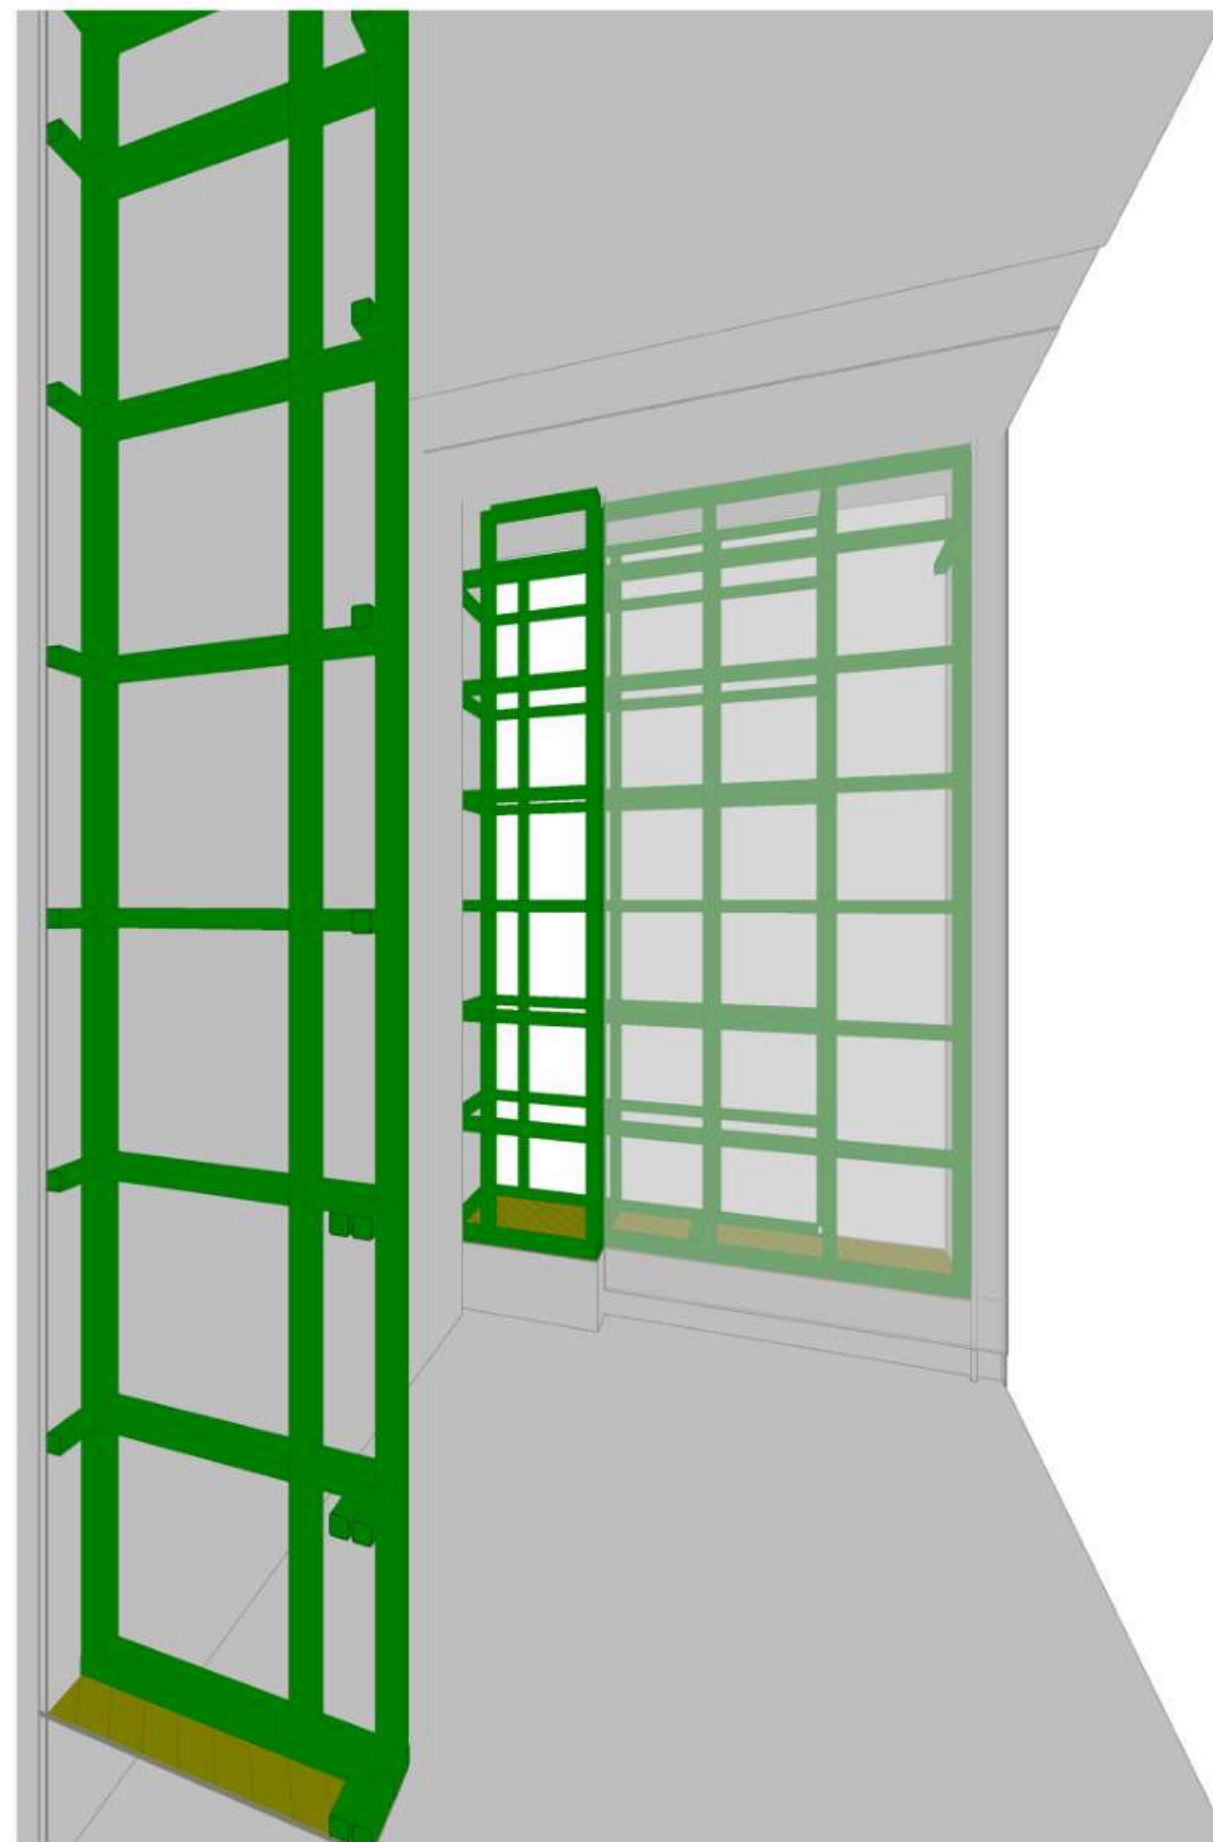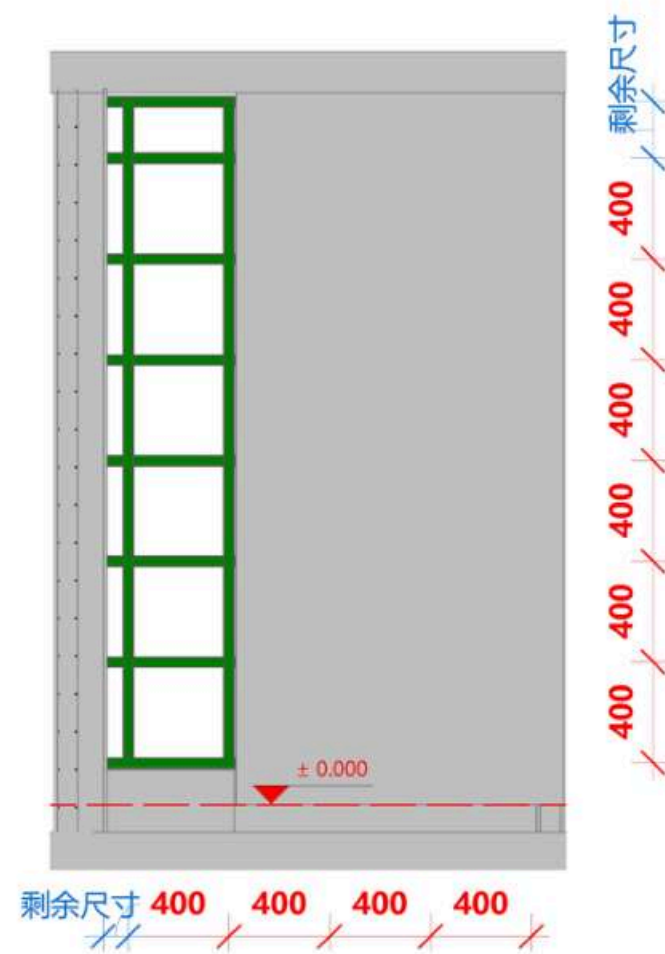

LEGEND图例

编号	图例	说明
1		抹灰层 (≈15mm)
2		混凝土止水坎上 加5mm钢板
3		钢架墙

日期
Date

01/11/26

修订
Revision

项目
Project

潮映华府3-801

Scale
比例

1:30@A2

钢架墙23

Drawing No.
图纸编号

46-SW-23

Project No.
项目编号

©2025

1

EL-23

钢架墙立面图23

Scale比例 1 : 30@A2

1

3D-23

钢架墙三维图23

Scale比例 1:30@A2

注释

Notes

- 1.本图纸如与现场尺寸有误，请施工人员与项目负责人联系。
- 2.施工前施工人员应认真查阅此图，如有不明确尺寸，按现场测量为准。
- 3.本图纸必须经甲乙双方认可并签字方可作为施工依据。

LEGEND图例

编号	图例	说明
1		抹灰层 (≈15mm)
2		混凝土止水坎上 加5mm钢板
3		钢架墙

日期
Date

01/11/26

修订

Revision

项目

Project

潮映华府3-801

Scale

比例

1:30@A2

钢架墙25

Drawing No.



图纸编号

47-SW-25

Project No.

项目编号

©2025

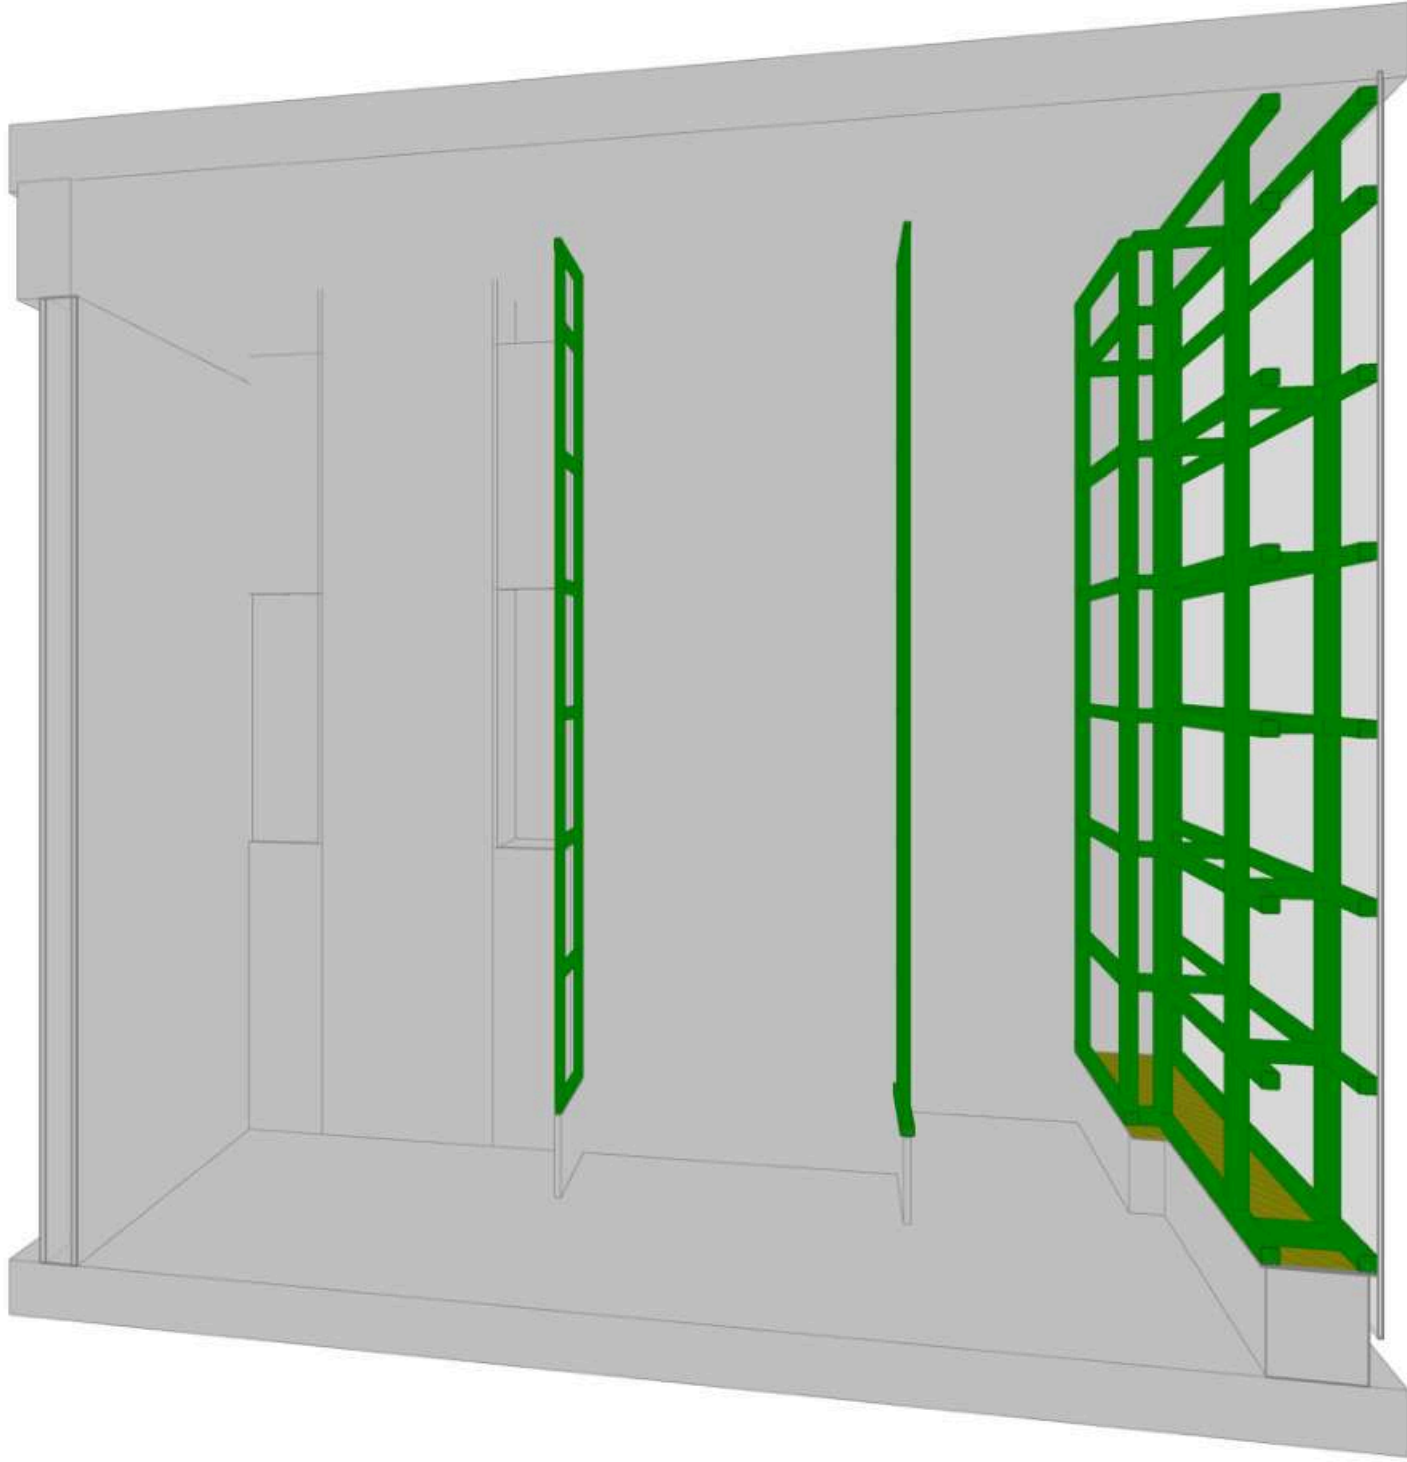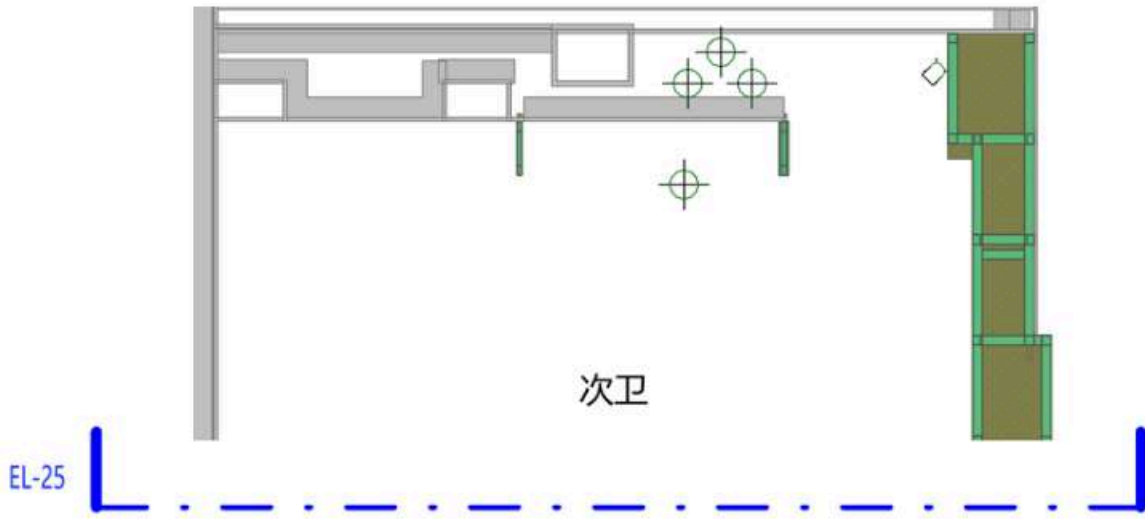

1

EL-25

钢架墙立面图25

Scale比例 1 : 30@A2

1

3D-25




钢架墙三维图25

Scale比例 1:30@A2

注释

Notes

- 1.本图纸如与现场尺寸有误，请施工人员与项目负责人联系。
- 2.施工前施工人员应认真查阅此图，如有不明确尺寸，按现场测量为准。
- 3.本图纸必须经甲乙双方认可并签字方可作为施工依据。

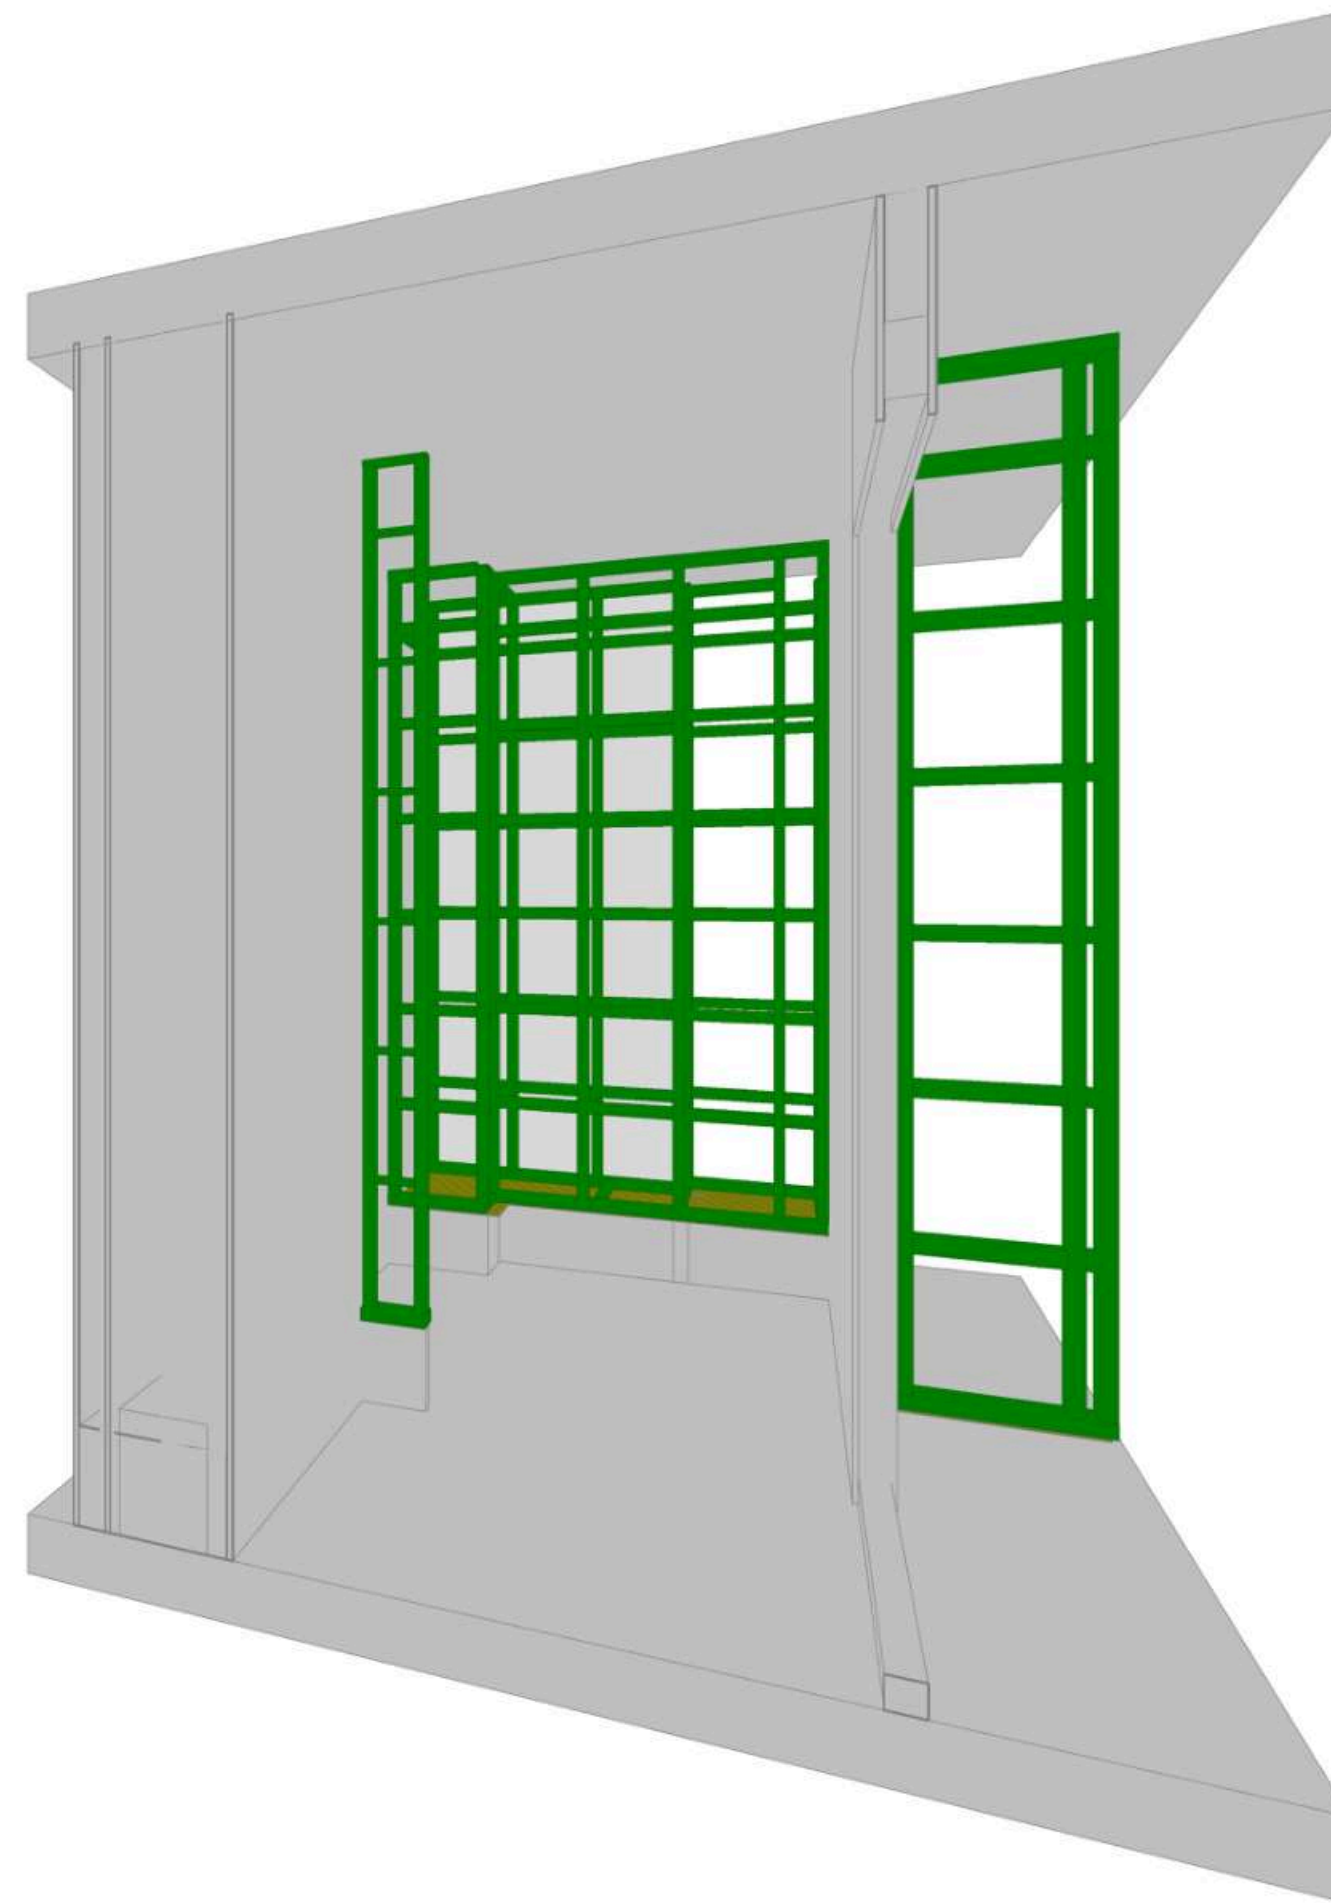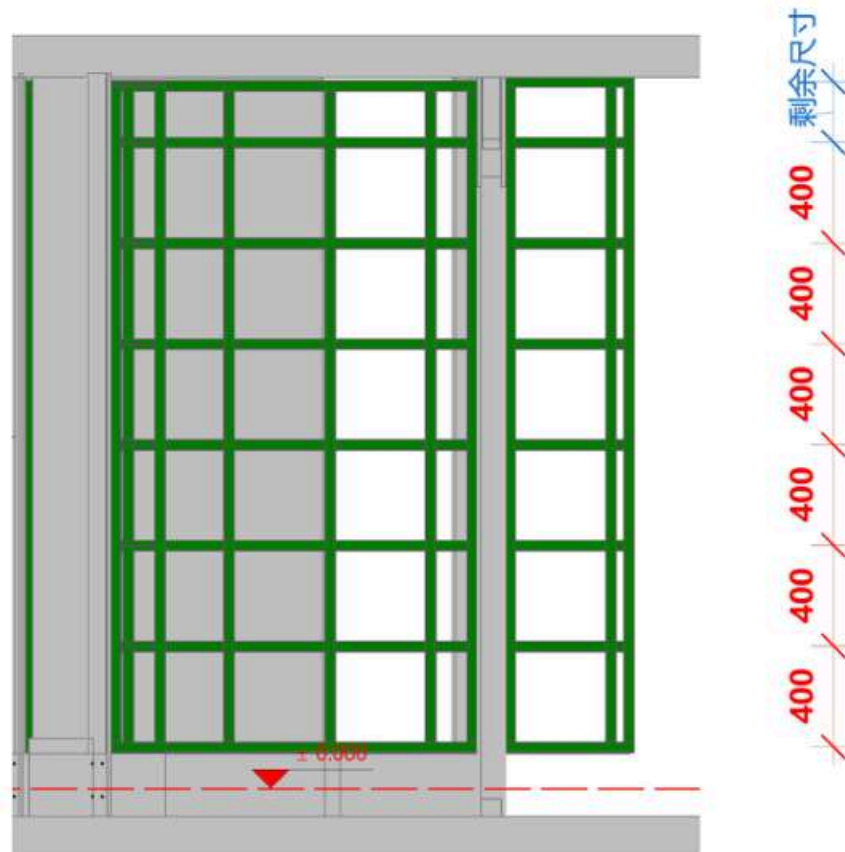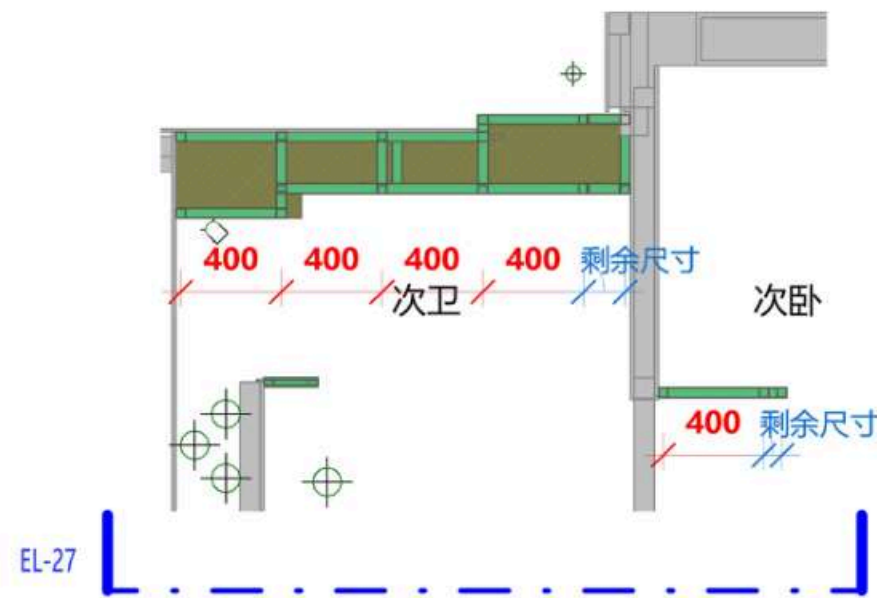

LEGEND图例

编号	图例	说明
1		抹灰层 (≈15mm)
2		混凝土止水坎上 加5mm钢板
3		钢架墙

日期
Date

01/11/26

修订
Revision

项目
Project

潮映华岸府3-801

Scale
比例

1:30@A2

钢架墙27

Drawing No.
图纸编号

48-SW-27

Project No.
项目编号

©2025

1

EL-27

钢架墙立面图27

Scale比例 1 : 30@A2

1




3D-27

钢架墙三维图27

Scale比例 1:30@A2

注释
Notes

- 1.本图纸如与现场尺寸有误，请施工人员与项目负责人联系。
- 2.施工前施工人员应认真查阅此图，如有不明确尺寸，按现场测量为准。
- 3.本图纸必须经甲乙双方认可并签字方可作为施工依据。

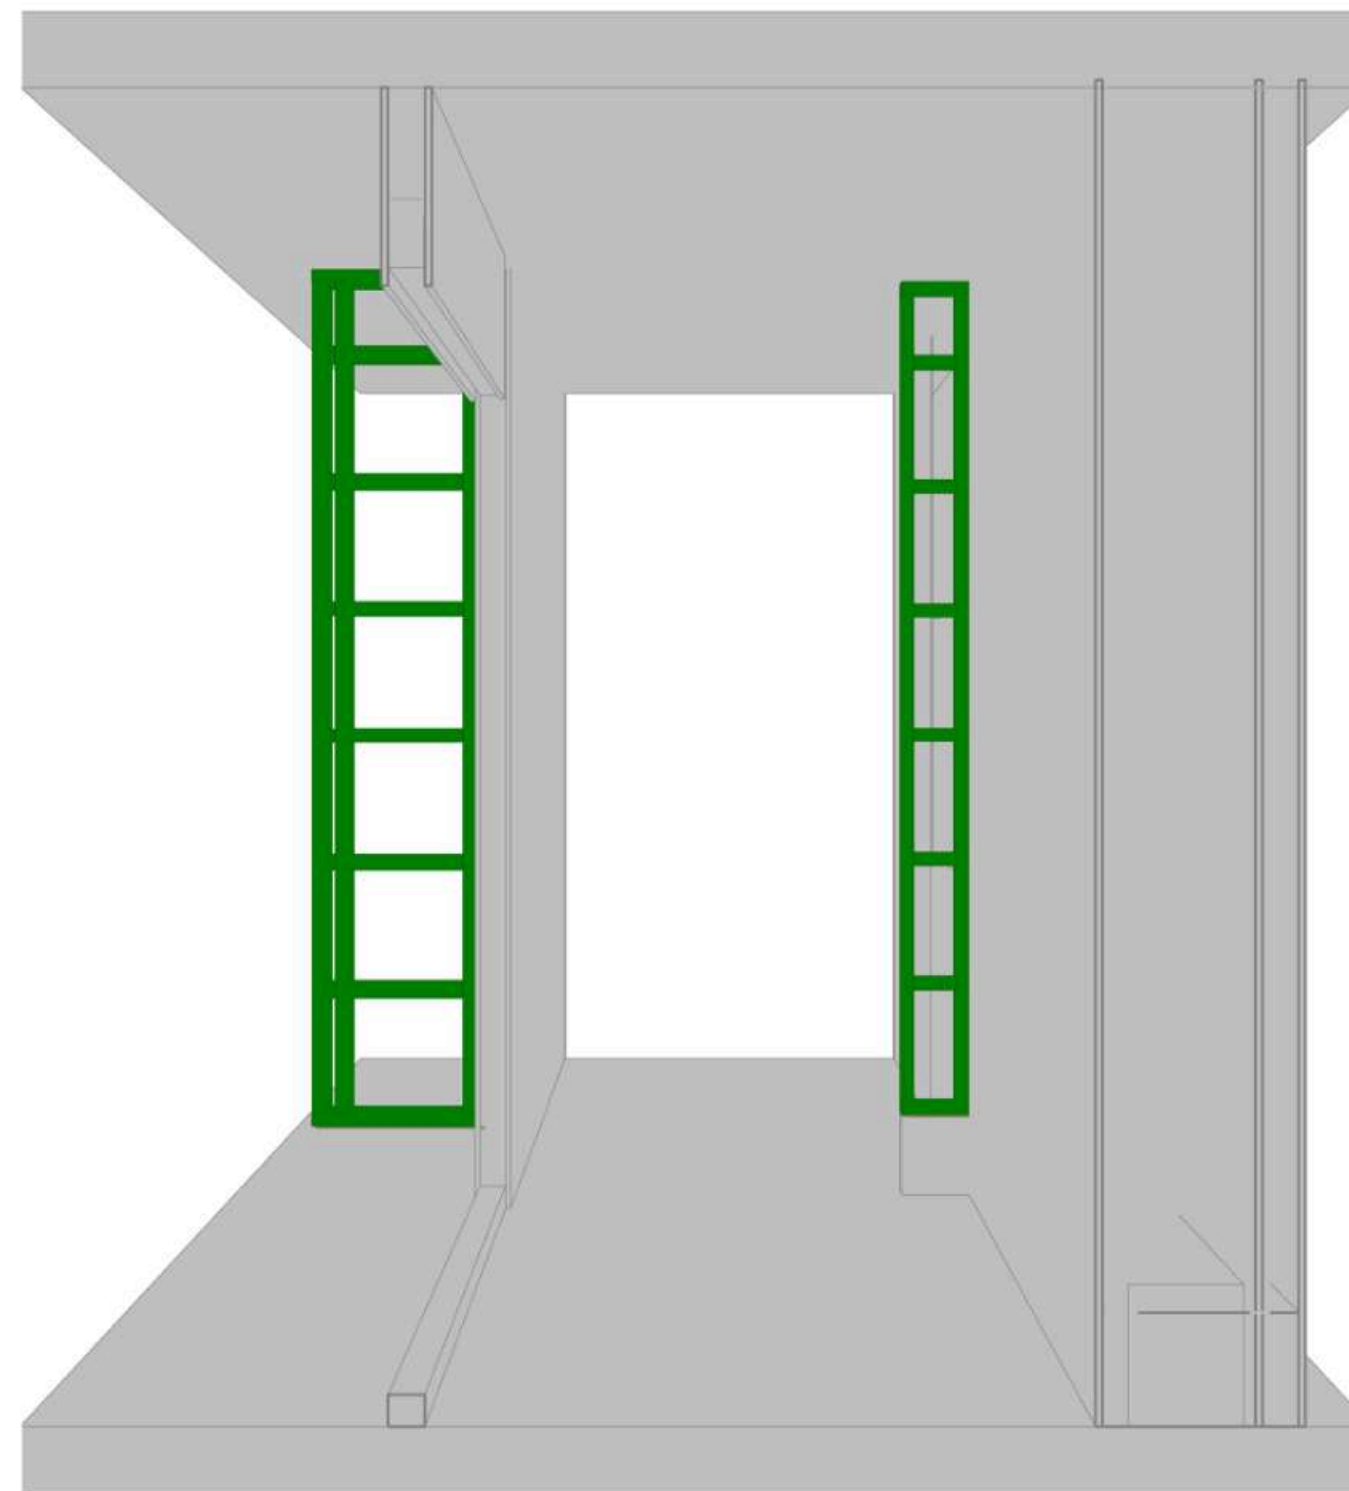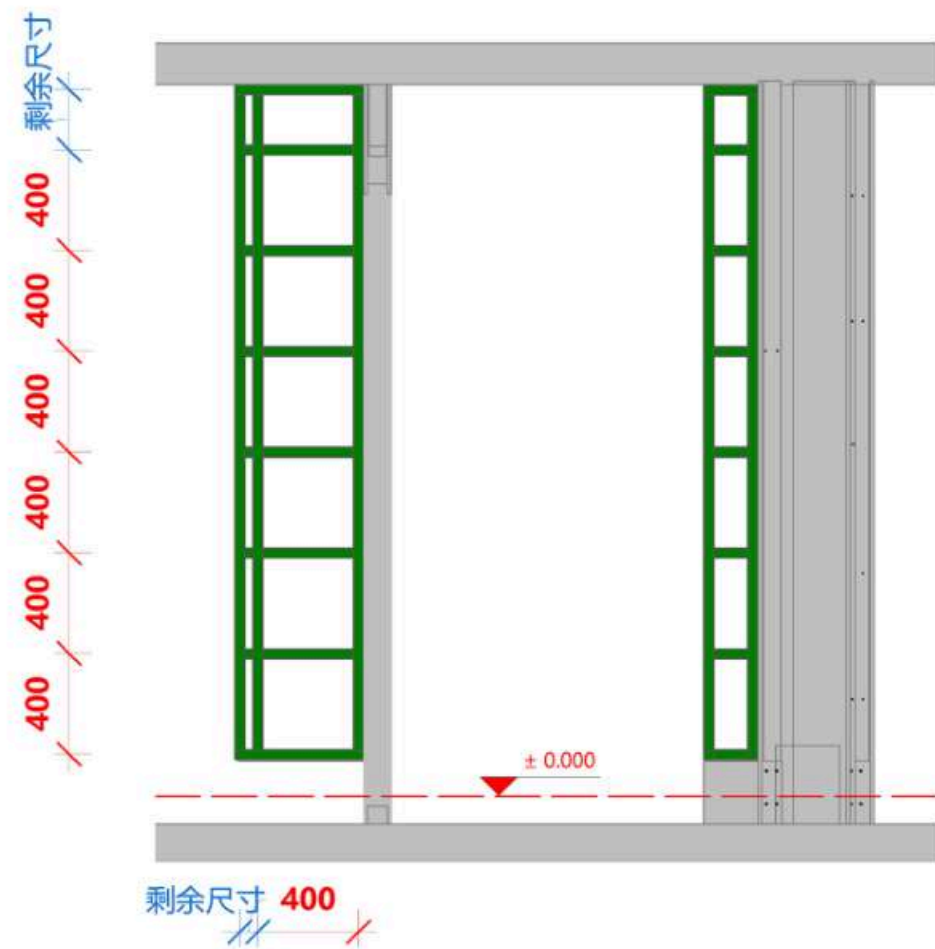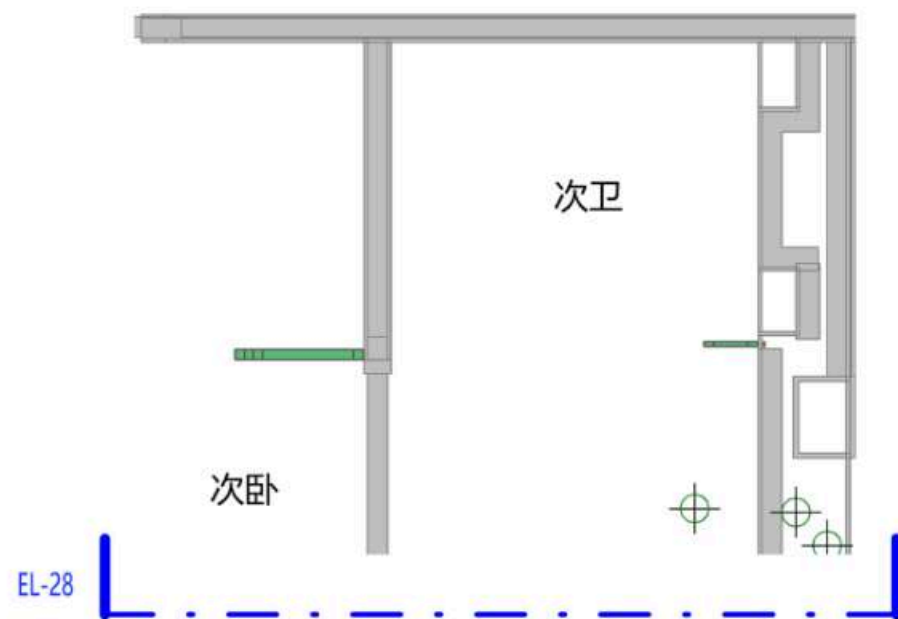

三和

LEGEND图例

编号	图例	说明
1		抹灰层 (≈15mm)
2		混凝土止水坎上 加5mm钢板
3		钢架墙

日期
Date

01/11/26

修订
Revision

项目
Project

潮映华府3-801

Scale
比例

1:30@A2

钢架墙28

Drawing No.
图纸编号

49-SW-28

Project No.
项目编号

©2025

1

EL-28

钢架墙立面图28

Scale比例 1 : 30@A2

1



3D-28

钢架墙三维图28

Scale比例 1:30@A2

注释 Notes

- 1.本图纸如与现场尺寸有误, 请施工人员与项目负责人联系。
- 2.施工前施工人员应认真查阅此图, 如有不明确尺寸, 按现场测量为准。
- 3.本图纸必须经甲乙双方认可并签字方可作为施工依据。

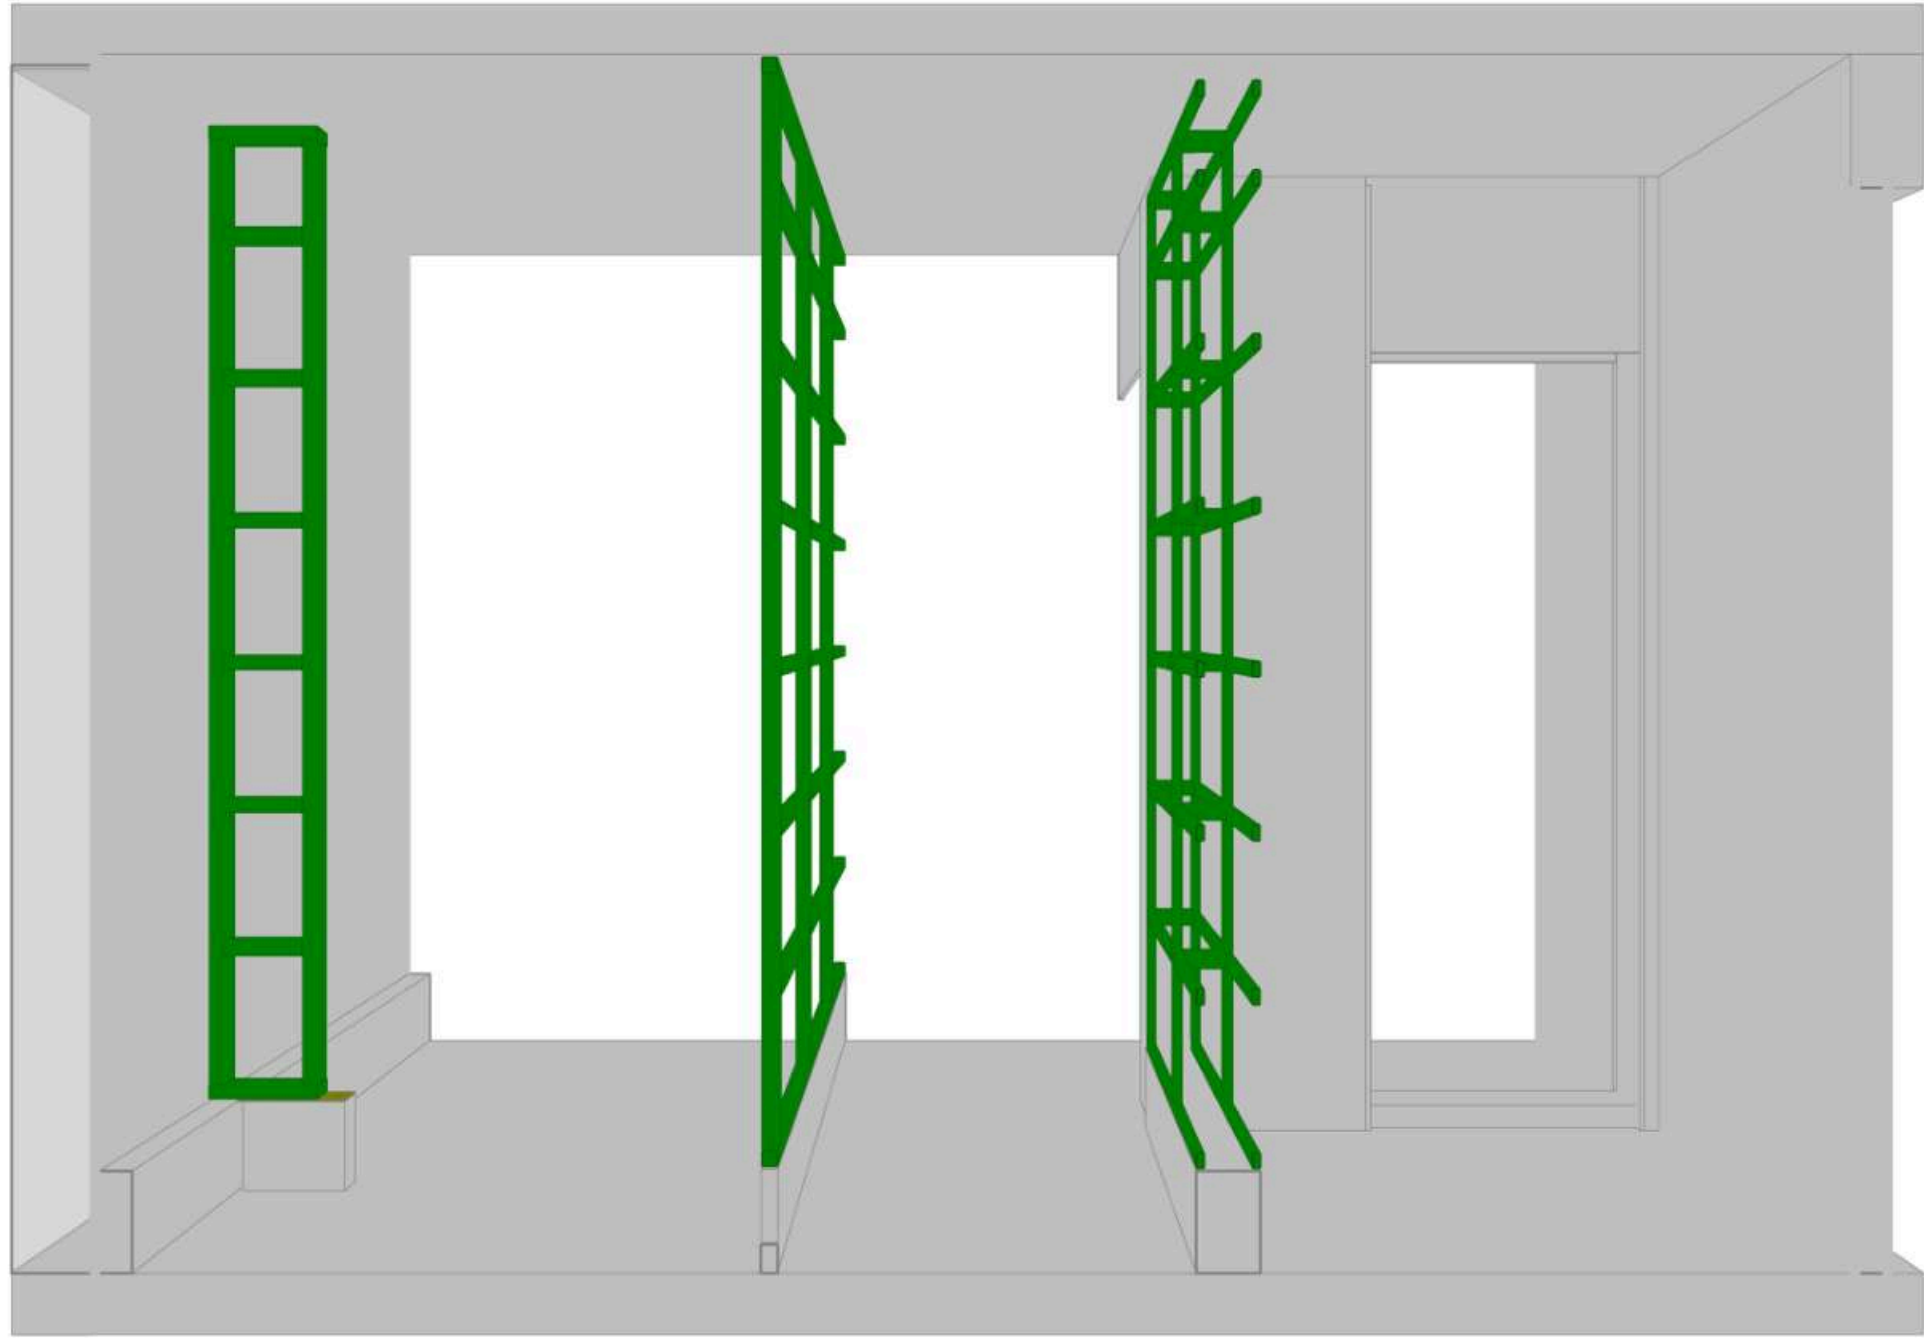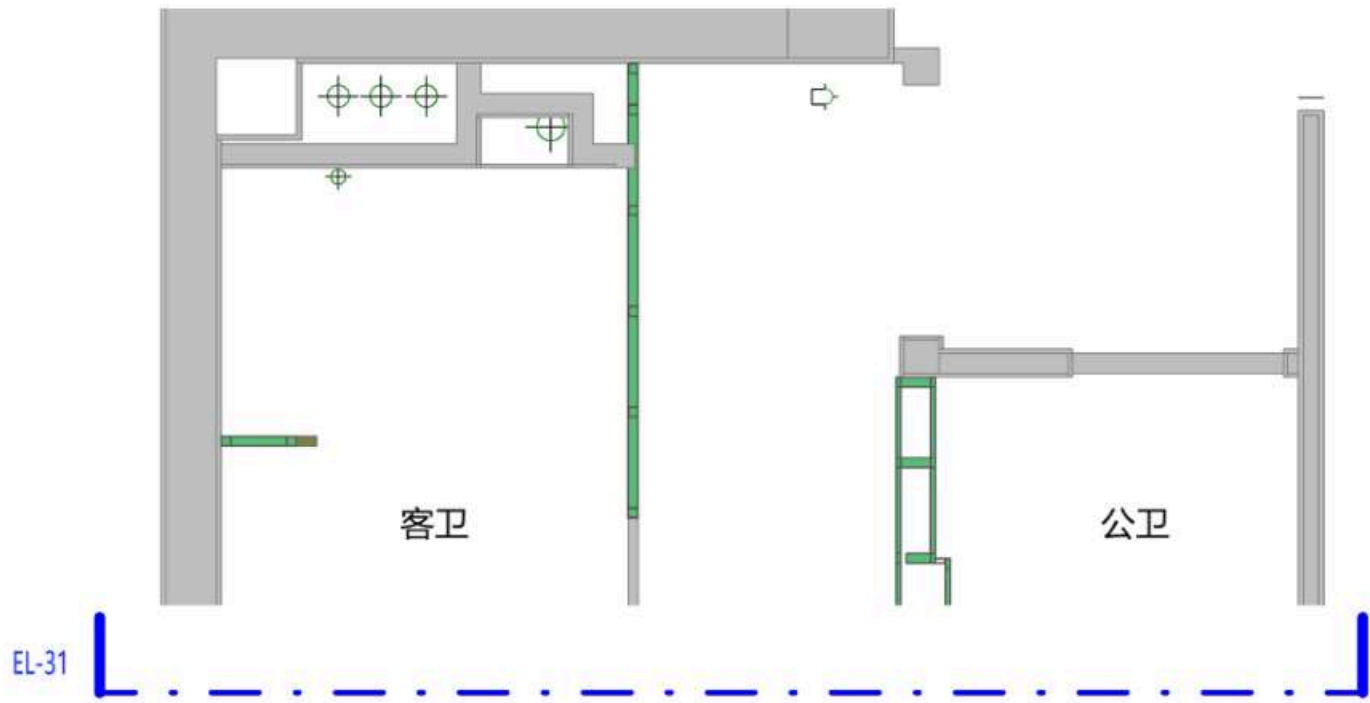

LEGEND图例

编号	图例	说明
1		抹灰层 (≈15mm)
2		混凝土止水坎上 加5mm钢板
3		钢架墙

日期
Date 01/11/26

修订
Revision

项目
Project

潮映华府3-801

Scale
比例 1:30@A2

钢架墙31

Drawing No.
图纸编号

50-SW-31

Project No.
项目编号

©2025

1

EL-31

钢架墙立面图31

Scale比例 1 : 30@A2

1

3D-31




钢架墙三维图31

Scale比例 1:30@A2

注释

Notes

- 1.本图纸如与现场尺寸有误差, 请施工人员与项目负责人联系。
- 2.施工前施工人员应认真查阅此图, 如有不明确尺寸, 按现场测量为准。
- 3.本图纸必须经甲乙双方认可并签字方可作为施工依据。

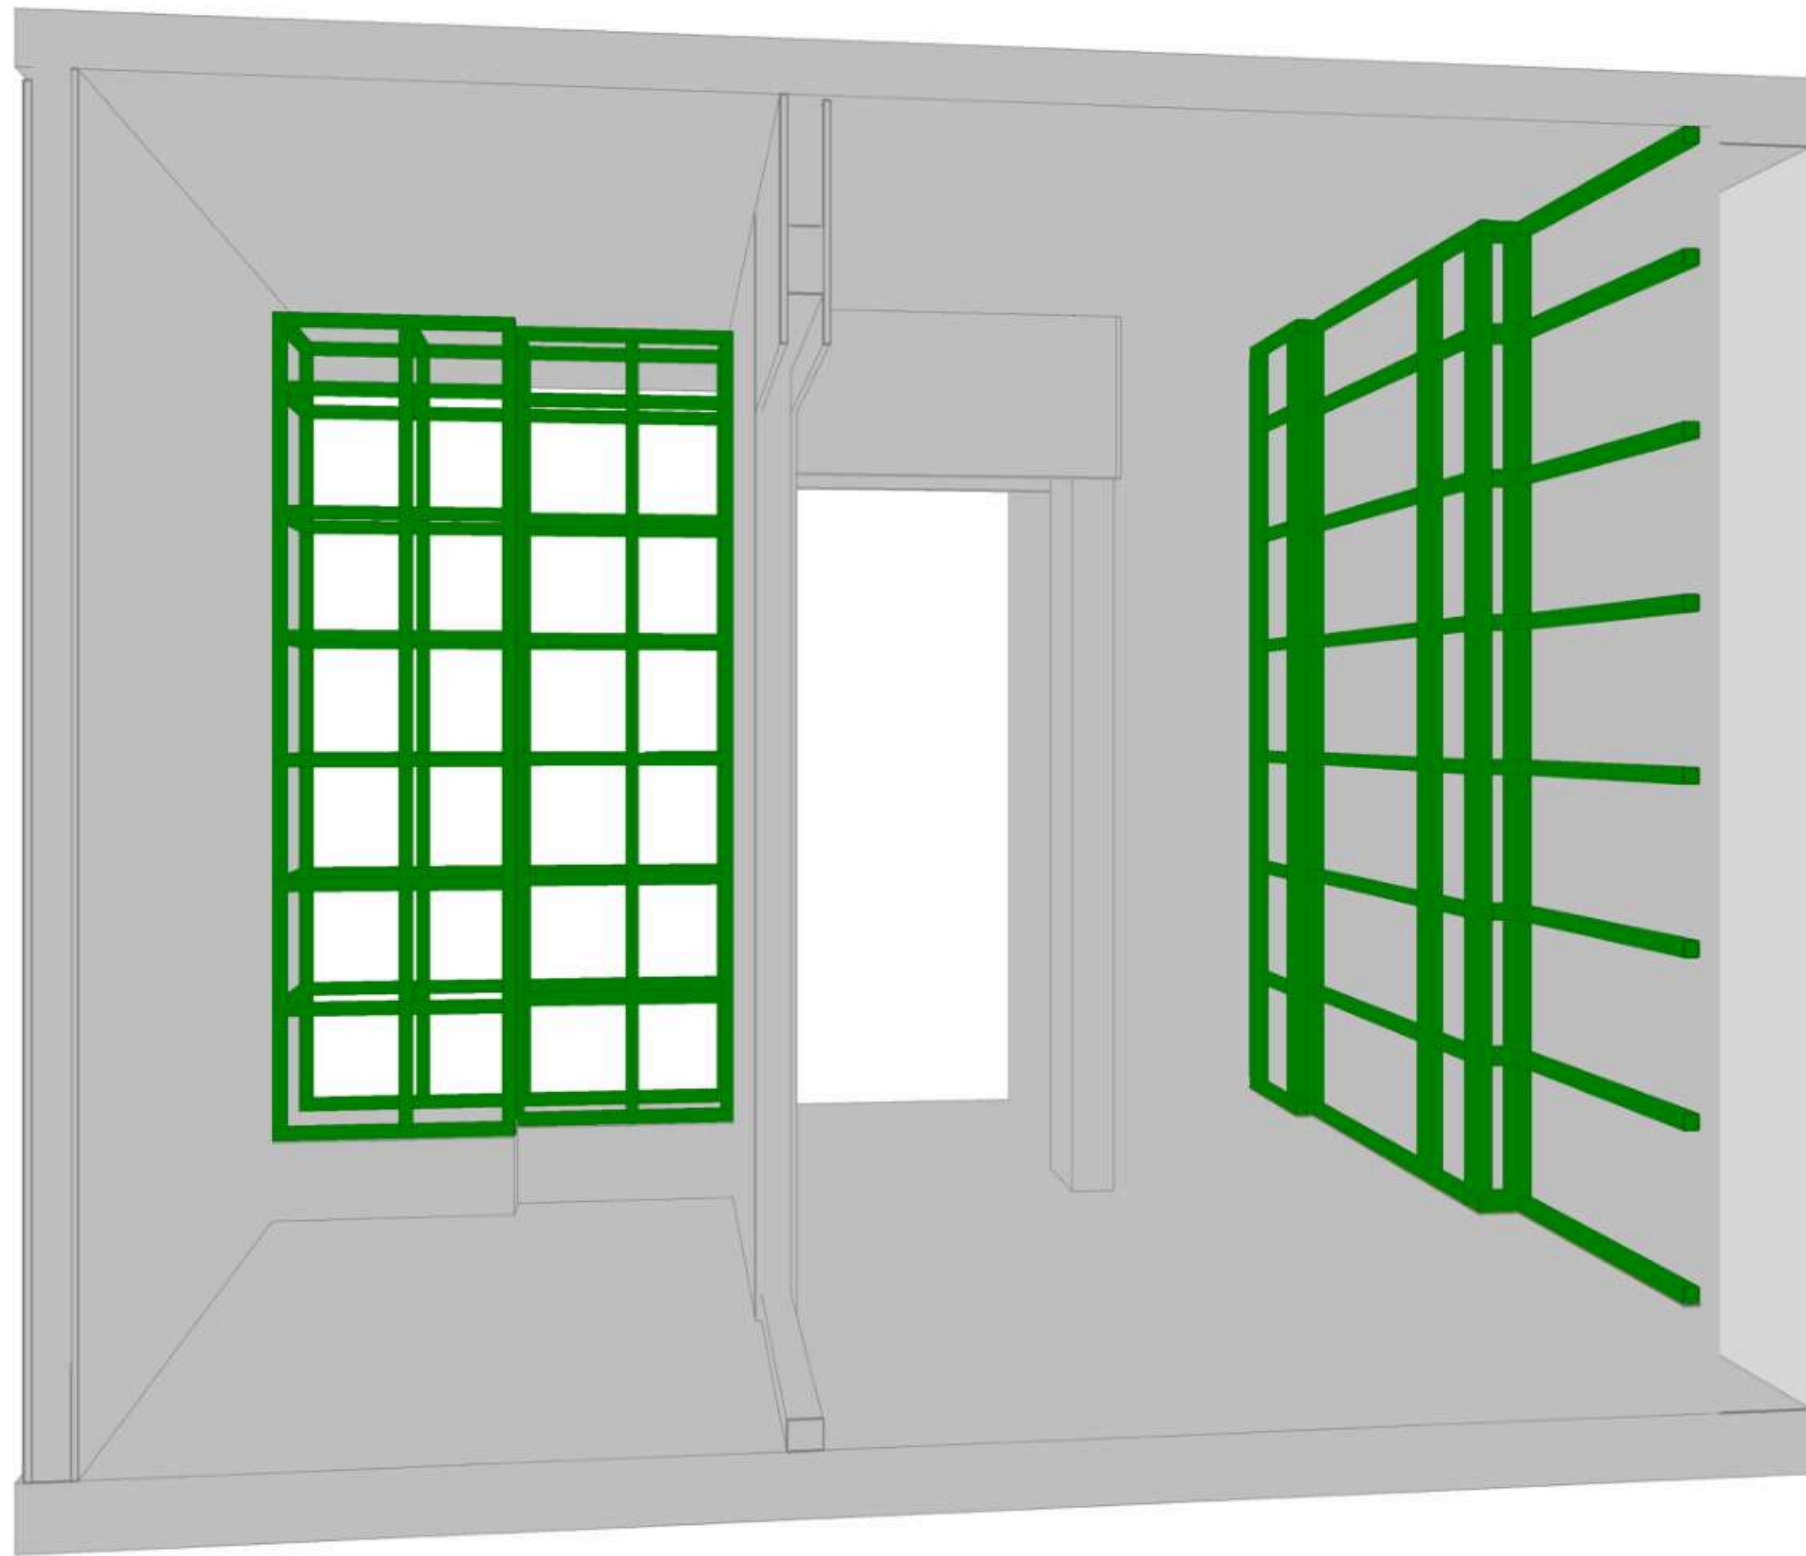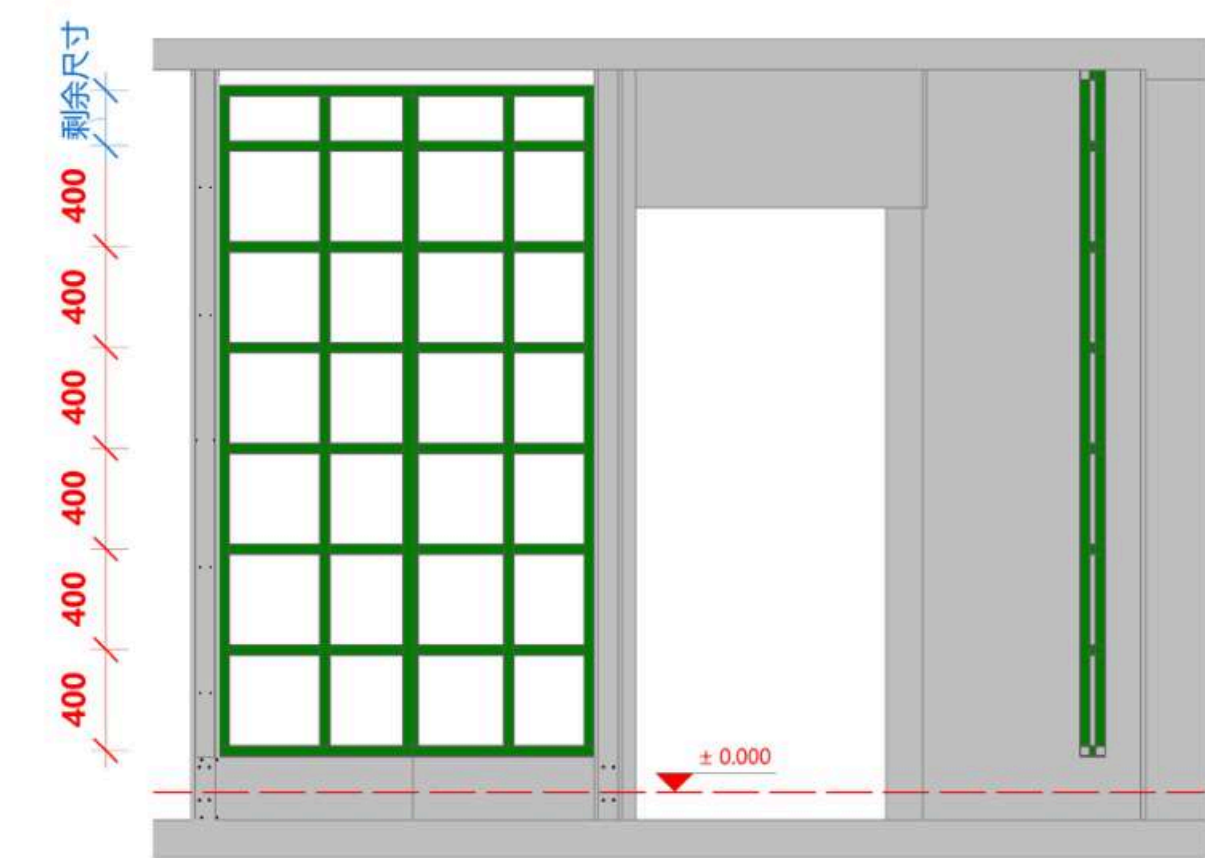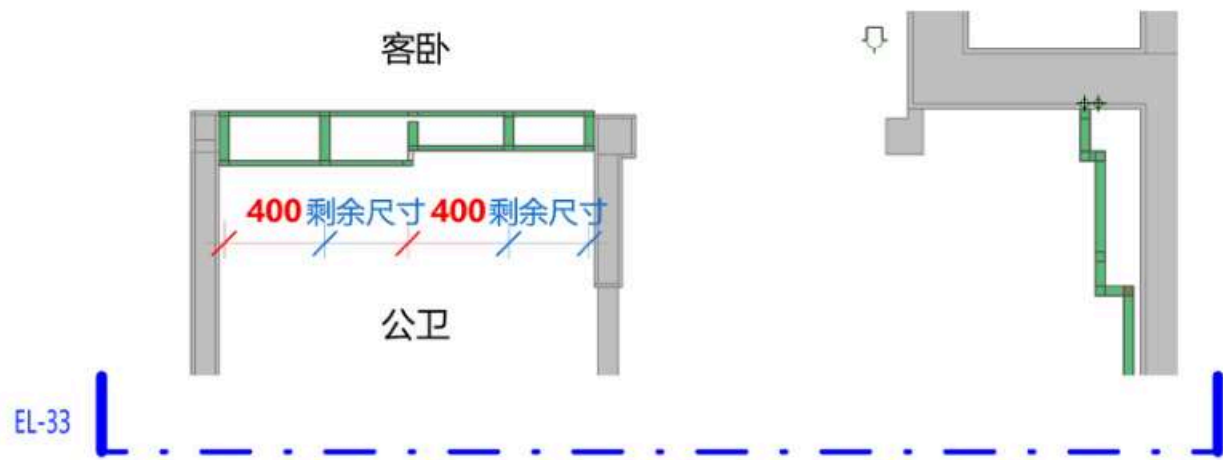

LEGEND图例

编号	图例	说明
1		抹灰层 (≈15mm)
2		混凝土止水坎上 加5mm钢板
3		钢架墙

日期
Date

01/11/26

修订
Revision

项目
Project

潮映华府3-801

Scale
比例

1:30@A2

钢架墙33

Drawing No.
图纸编号

51-SW-33

Project No.
项目编号

©2025

1

EL-33

钢架墙立面图33

Scale比例 1 : 30@A2

1


3D-33

钢架墙三维图33

Scale比例 1:30@A2

注释
Notes

- 1.本图纸如与现场尺寸有误差, 请施工人员与项目负责人联系。
- 2.施工前施工人员应认真查阅此图, 如有不明确尺寸, 按现场测量为准。
- 3.本图纸必须经甲乙双方认可并签字方可作为施工依据。

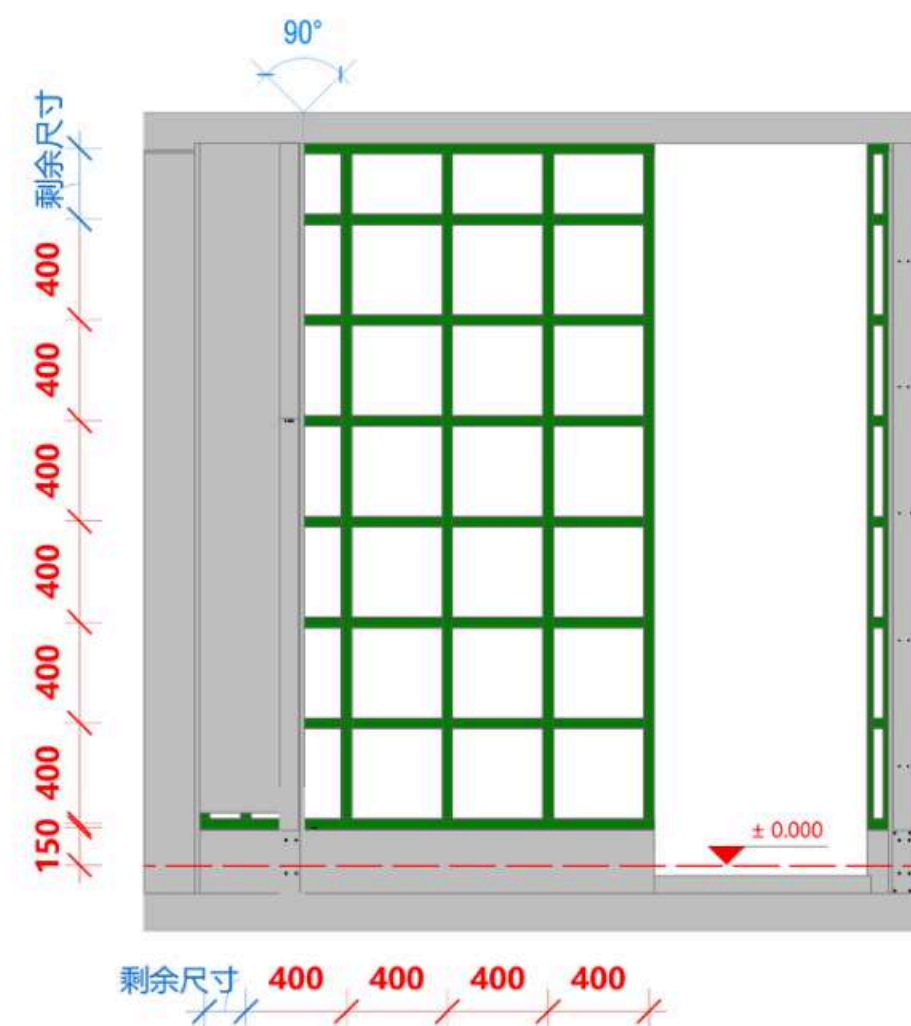


Project No. © 2025
项目编号

Scale比例 1:30@A2

Notes

1. 本图纸如与现场尺寸有误, 请施工人员与项目负责人联系。
2. 施工前施工人员应认真查阅此图, 如有不明确尺寸, 按现场测量为准。
3. 本图纸必须经甲乙双方认可并签字方可作为施工依据。

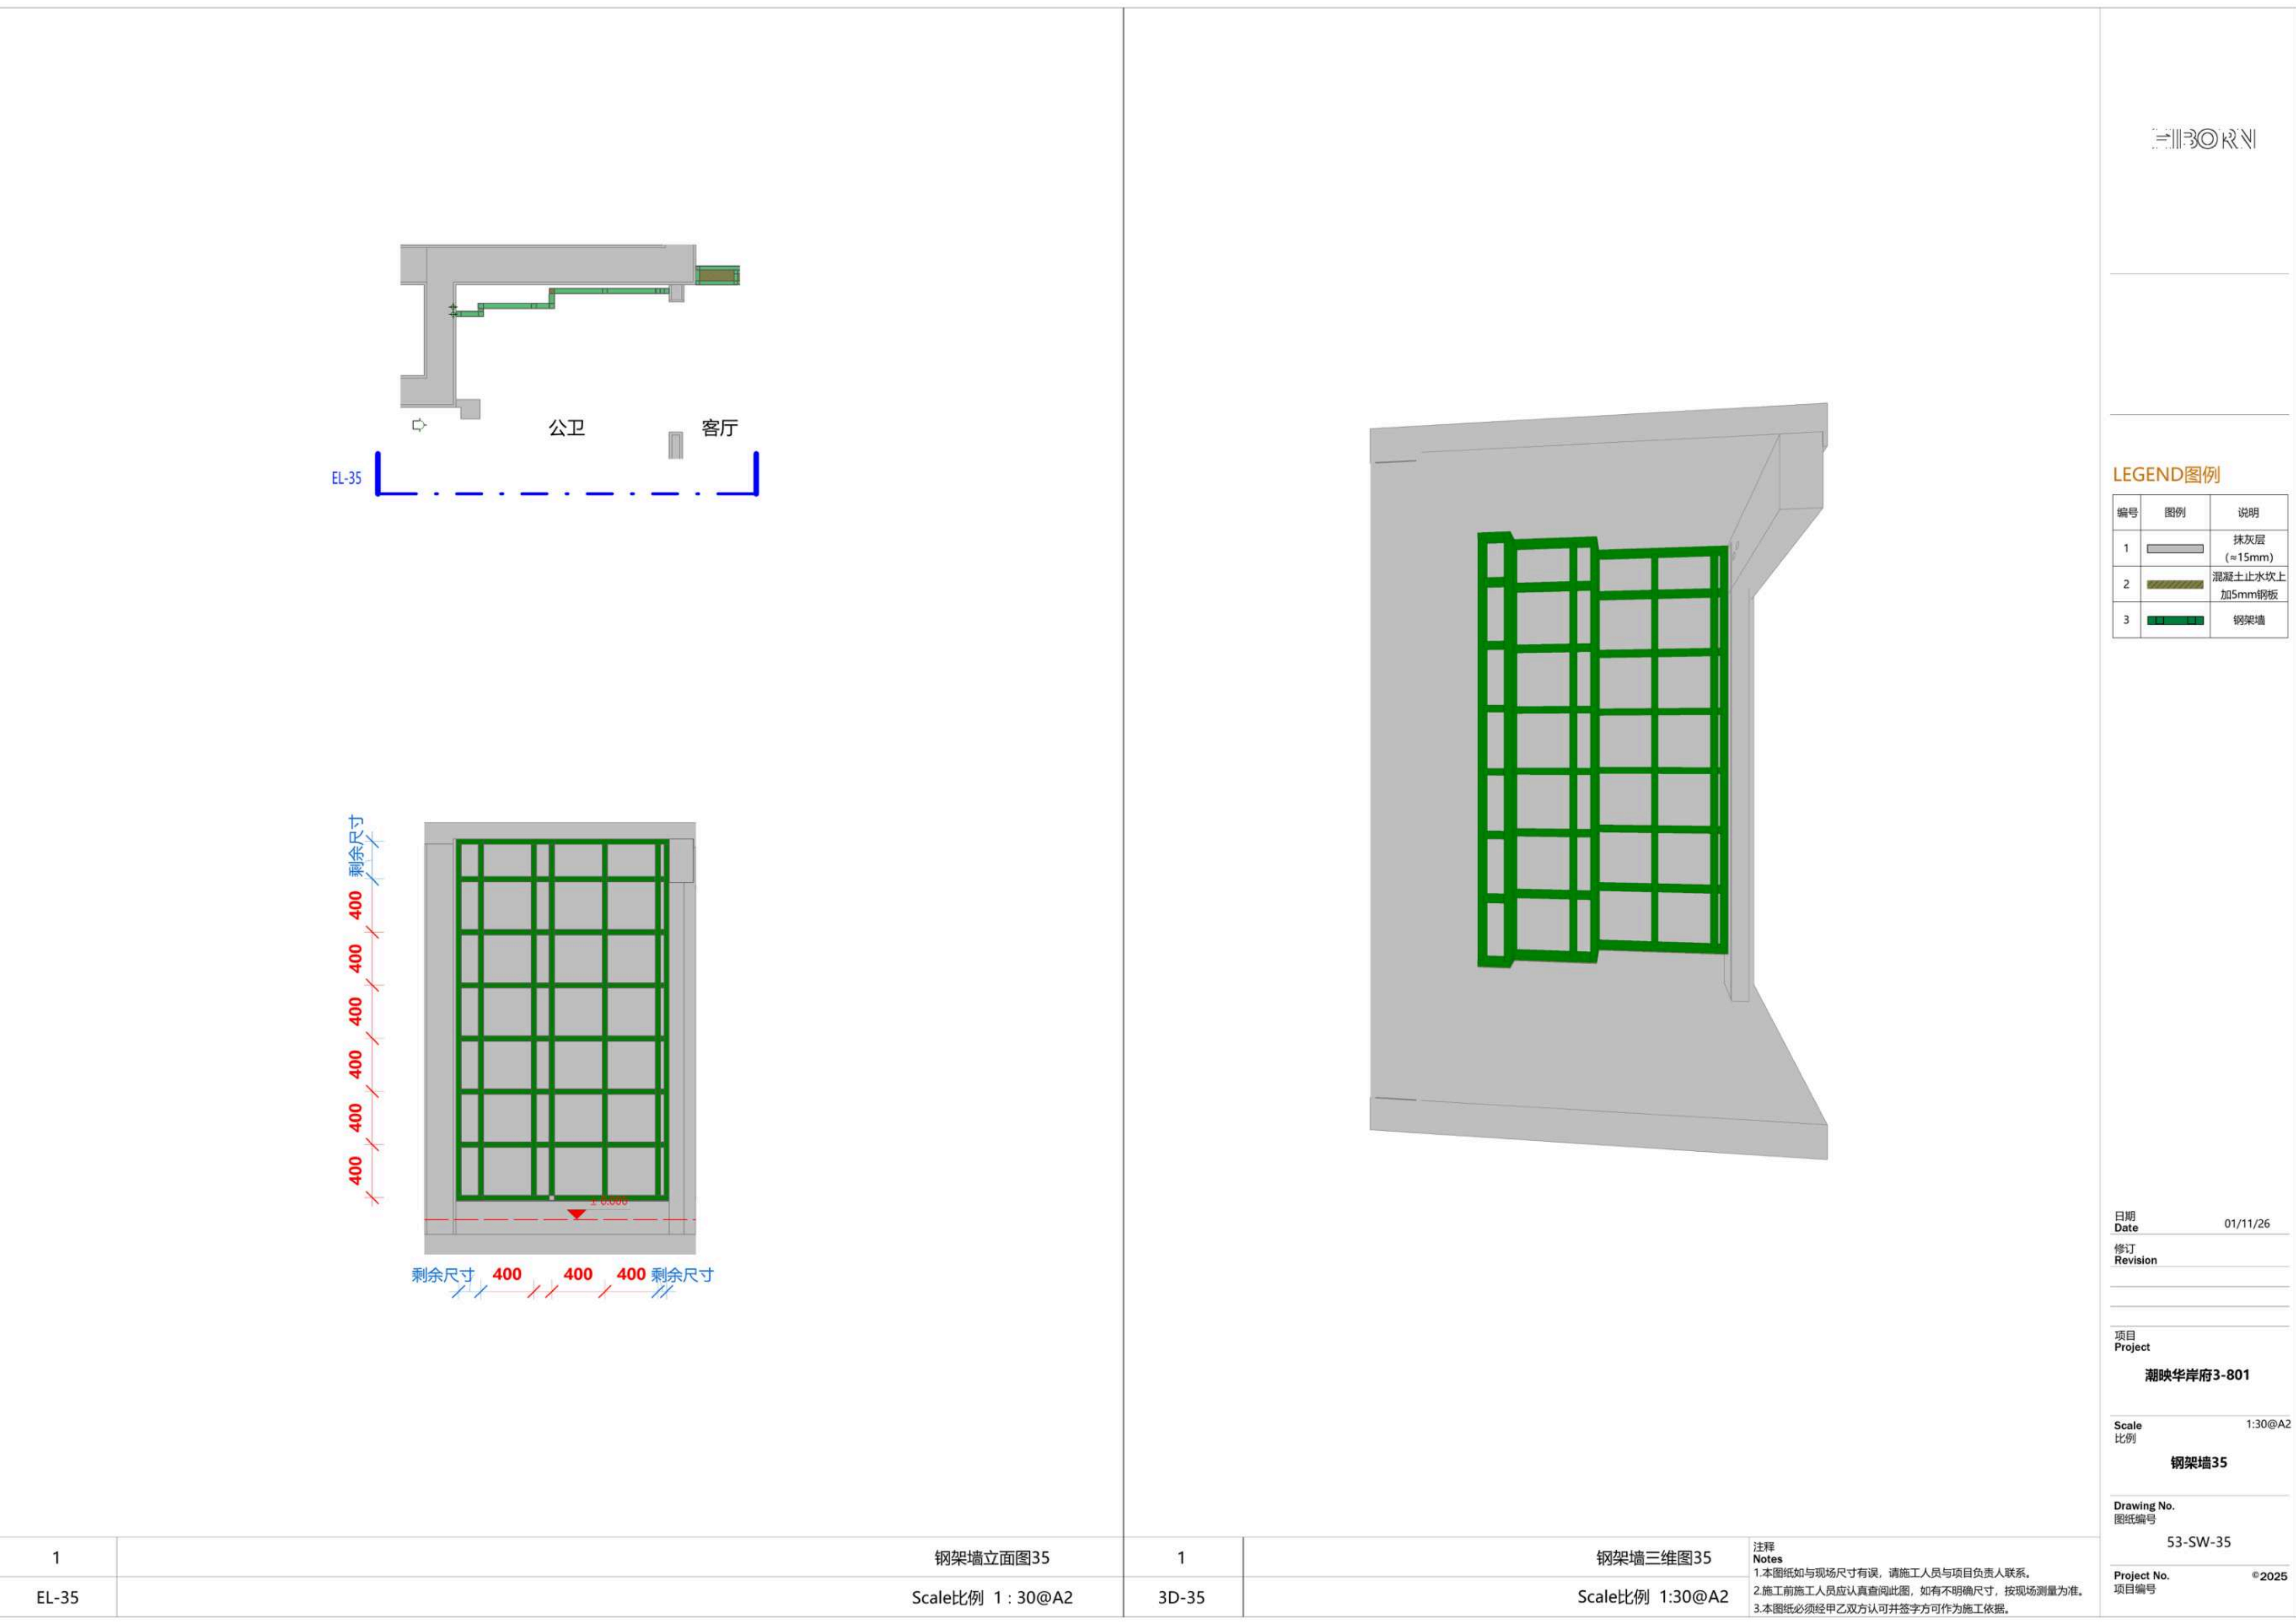

LEGEND图例

编号	图例	说明
1		抹灰层 (≈15mm)
2		混凝土止水坎上 加5mm钢板
3		钢架墙

日期
Date 01/11/26

修订
Revision


项目
Project
潮映华岸府3-801

Scale
比例 1:30@A2
钢架墙35

Drawing No.
图纸编号 53-SW-35

Project No.
项目编号 ©2025

1	钢架墙立面图35	1	钢架墙三维图35	注释 Notes
EL-35	Scale比例 1 : 30@A2	3D-35	Scale比例 1:30@A2	1.本图纸如与现场尺寸有误, 请施工人员与项目负责人联系。 2.施工前施工人员应认真查阅此图, 如有不明确尺寸, 按现场测量为准。 3.本图纸必须经甲乙双方认可并签字方可作为施工依据。

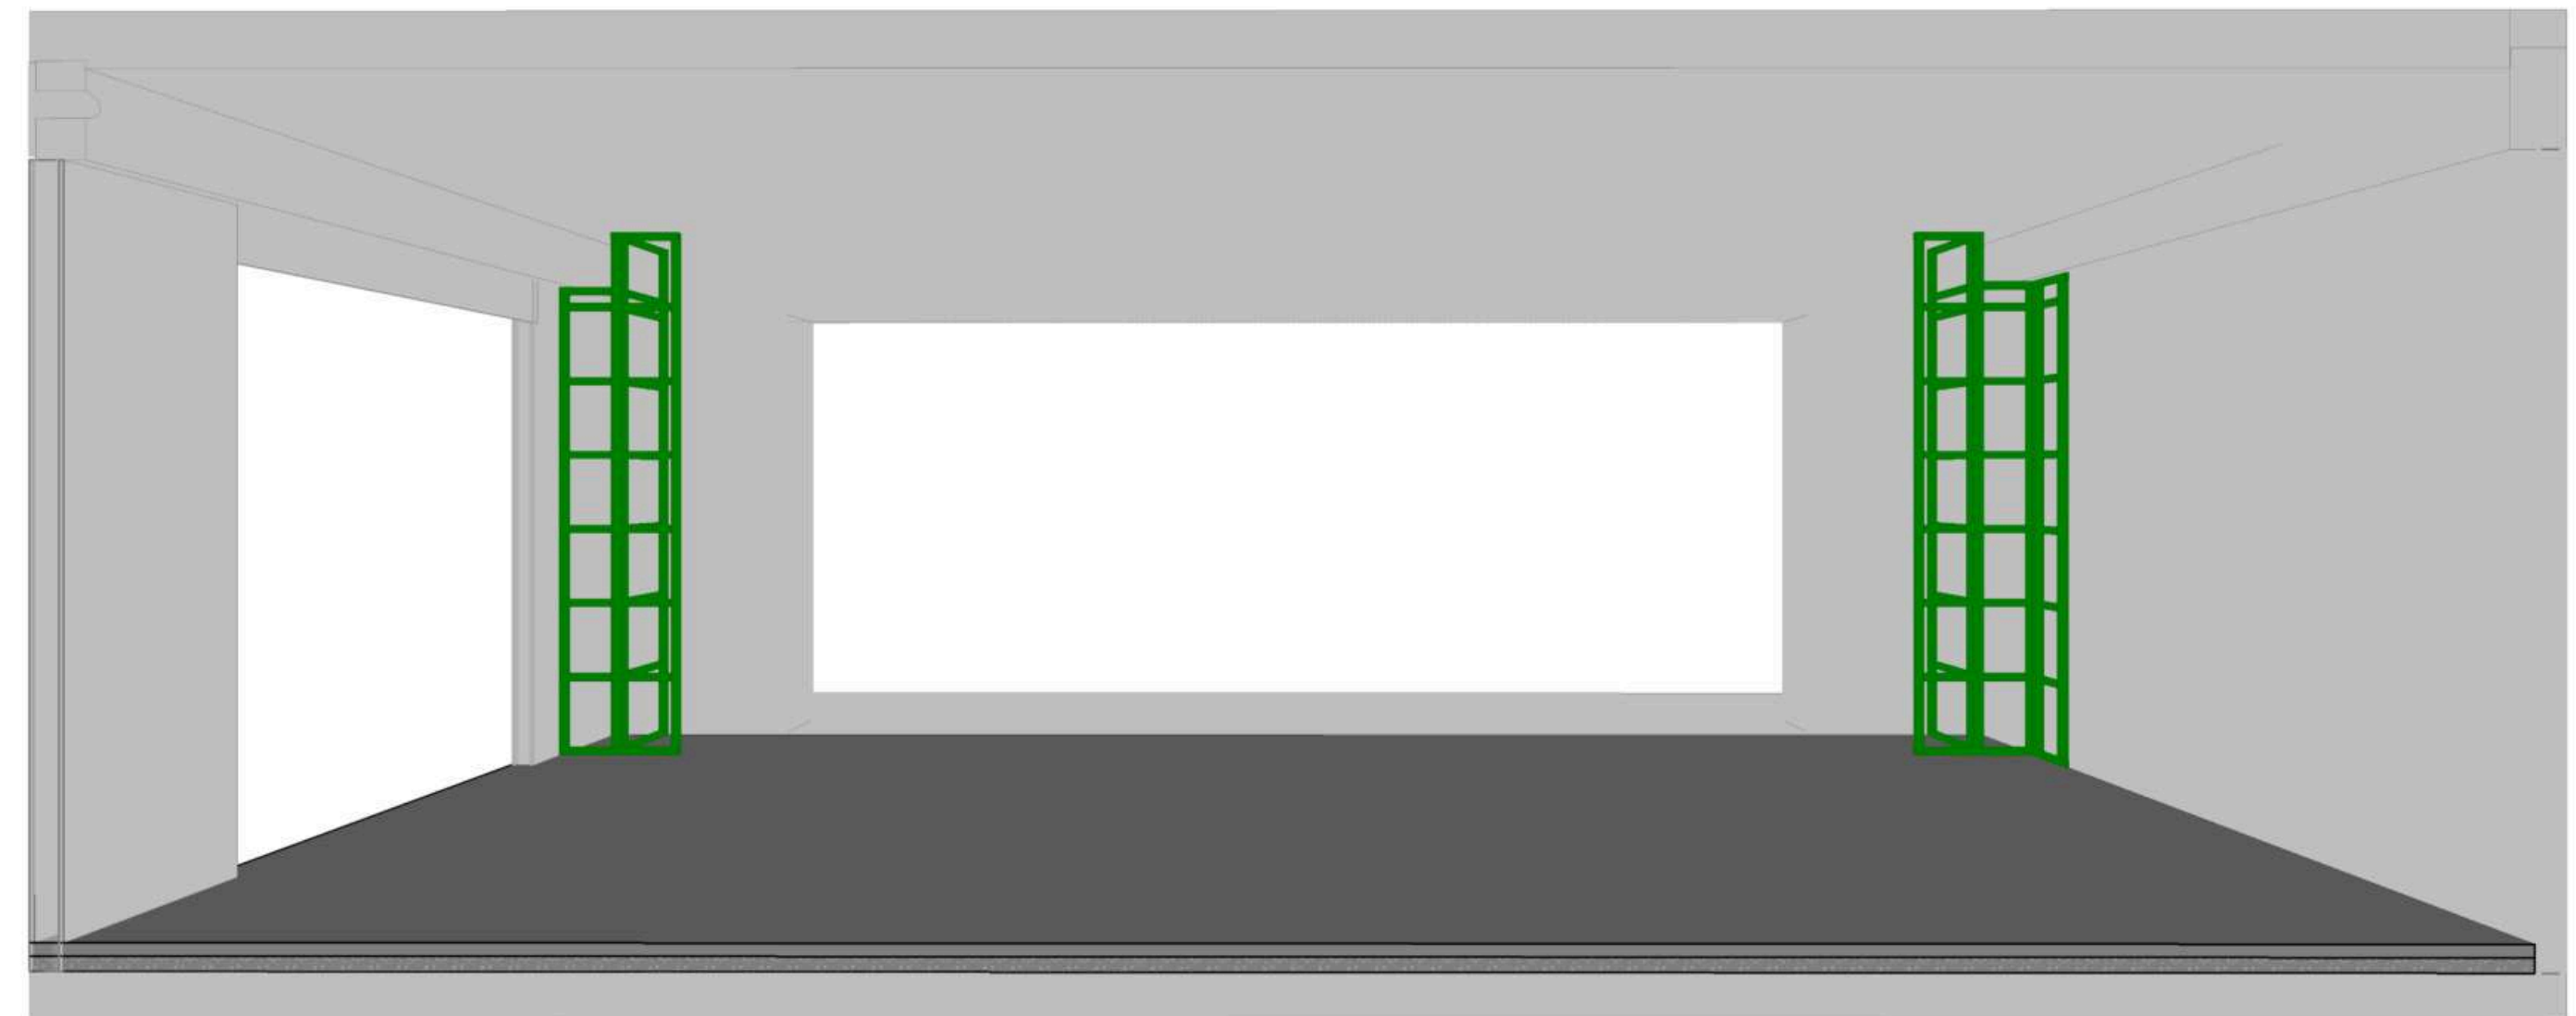
$$\Rightarrow ||\beta \otimes \mathbb{R}N||$$

LEGEND图例

号	图例	说明
		抹灰层 (≈15mm)
		混凝土止水坎上 加5mm钢板
		钢架墙

01/11/26

Division

Project

映华岸府3-801

ale	1:30@A2
-----	---------

架墙37

Drawing No.
紙编号

-SW-37

Subject No.
目编号

2025

1

EL-37

钢架墙立面图37

Scale比例 1 : 30@A2

1

3D-37

钢架墙三维图37

Scale比例 1:30@A2

注释
Notes

- 1.本图纸如与现场尺寸有误,请施工人员与项目负责人联系。
- 2.施工前施工人员应认真查阅此图,如有不明确尺寸,按现场测量为准。
- 3.本图纸必须经甲乙双方认可并签字方可作为施工依据。