杭州潮映华岸府3-801
墙面及踢脚铝型材深化图

出图日期：2026年3月12日

DRAWINGS LIST 图纸目录

PROJECT 项目名称：杭州华岸府

DQG.NO 图号	TITLE 内容	SCALE 比例	DATE/日期	REV.修订
AP-01	墙面铝型材分析平面图	1 : 60@A2	2026.3.12	
AP-02	踢脚铝型材分析平面图	1 : 60@A2	2026.3.12	
AP.EL-索引	墙面及踢脚铝型材立面索引图	1 : 60@A2	2026.3.12	
AP.EL-01	玄关、家政间 墙面及踢脚铝型材	1 : 30@A2	2026.3.12	
AP.EL-02	客厅一 墙面及踢脚铝型材	1 : 30@A2	2026.3.12	
AP.EL-03	客厅二 墙面及踢脚铝型材	1 : 30@A2	2026.3.12	
AP.EL-04	餐厅一 墙面及踢脚铝型材	1 : 30@A2	2026.3.12	
AP.EL-05	餐厅二 墙面及踢脚铝型材	1 : 30@A2	2026.3.12	
AP.EL-06	猫房、阳台 墙面及踢脚铝型材	1 : 30@A2	2026.3.12	
AP.EL-07	客卧入户、客卧过道 墙面及踢脚铝型材	1 : 30@A2	2026.3.12	
AP.EL-08	客卫、公卫 墙面及踢脚铝型材	1 : 30@A2	2026.3.12	
AP.EL-09	客卧 墙面及踢脚铝型材	1 : 30@A2	2026.3.12	
AP.EL-10	次卧 墙面及踢脚铝型材	1 : 30@A2	2026.3.12	
AP.EL-11	次卫 墙面及踢脚铝型材	1 : 30@A2	2026.3.12	
AP.EL-12	书房 墙面及踢脚铝型材	1 : 30@A2	2026.3.12	

DQG.NO 图号	TITLE 内容	SCALE 比例	DATE/日期	REV.修订
AP.EL-13	衣帽间、主卫 墙面及踢脚铝型材	1 : 30@A2	2026.3.12	
AP.EL-14	主卧 墙面及踢脚铝型材	1 : 30@A2	2026.3.12	

盖章

注释
Notes

1.本图纸如与现场尺寸有误，请施工人员与项目负责人联系。
2.施工前施工人员应认真查阅此图，如有不明确尺寸，按现场测量为准。
3.本图纸必须经甲乙双方认可并签字方可作为施工依据。

日期
Date 03/04/26

修订
Revision

△1

项目
Project
潮映华岸府3-801

比例
Scale
图纸目录

图纸编号
Drawing No.
AP-目录

项目编号
Project No.

©2025

图例 A
LEGEND A-石膏基冲筋找平铝型材

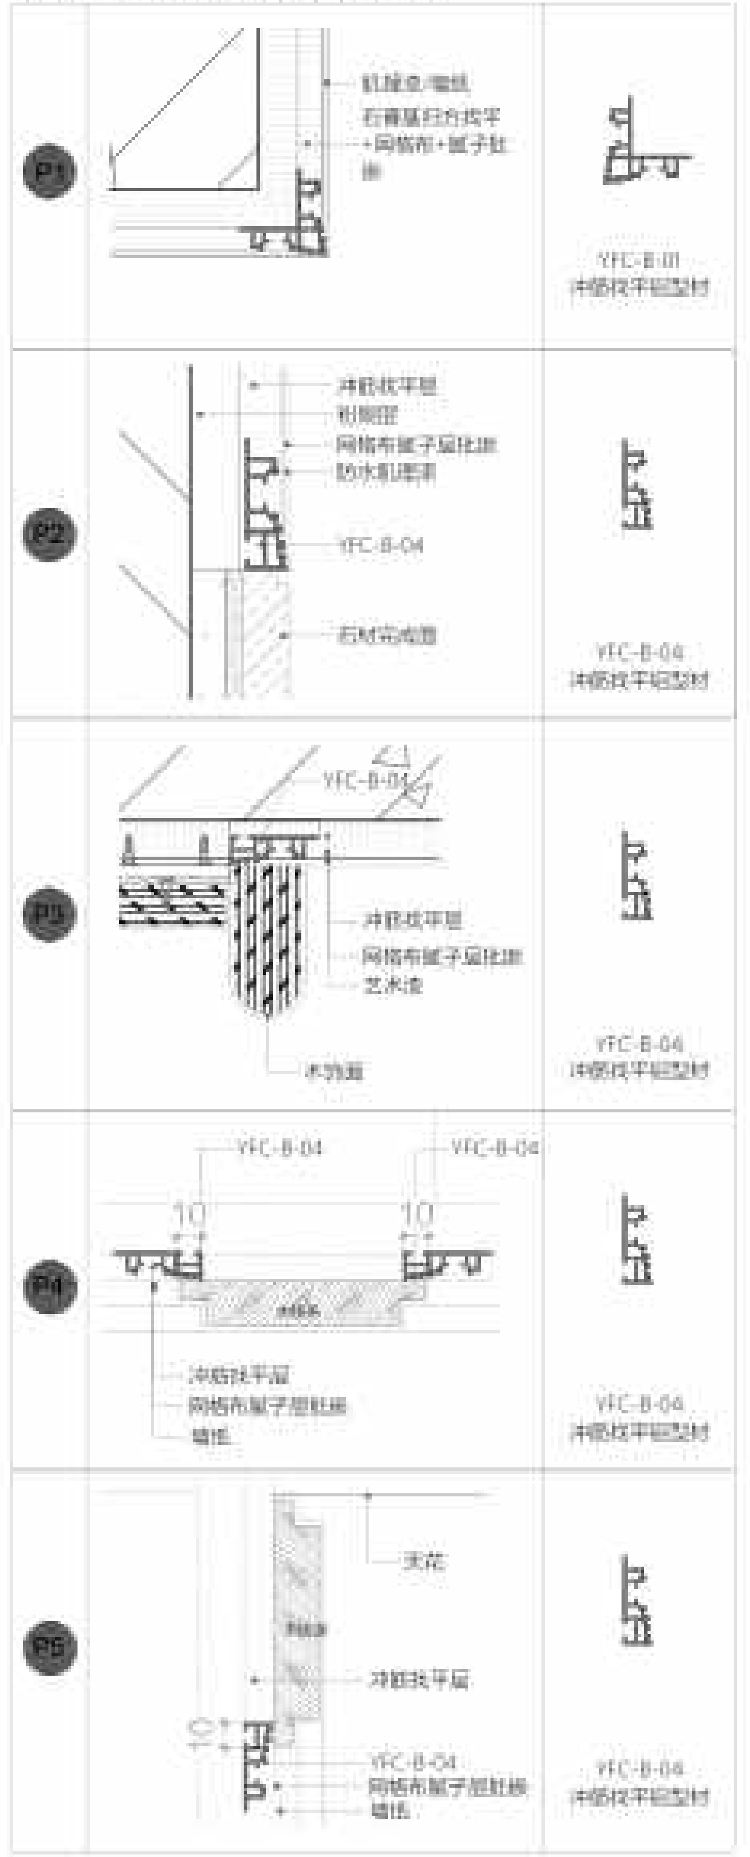
P1
肌理漆/墙纸
石膏基归方找平
+网格布+腻子批
嵌
YFC-B-01
冲筋找平铝型材
P2
冲筋找平层
粉刷层
网格布腻子层批嵌
防水乳液涂
YFC-B-04
石材完成面
YFC-B-04
冲筋找平铝型材
P3
YFC-B-04
冲筋找平层
网格布腻子层批嵌
艺术漆
木饰面
YFC-B-04
冲筋找平铝型材
P4
YFC-B-04
YFC-B-04
10
10
冲筋找平层
网格布腻子层批嵌
墙纸
YFC-B-04
冲筋找平铝型材
P5
天花
冲筋找平层
YFC-B-04
网格布腻子层批嵌
墙纸
YFC-B-04
冲筋找平铝型材

图例 B
LEGEND B-柜边石膏基冲筋找平铝型材

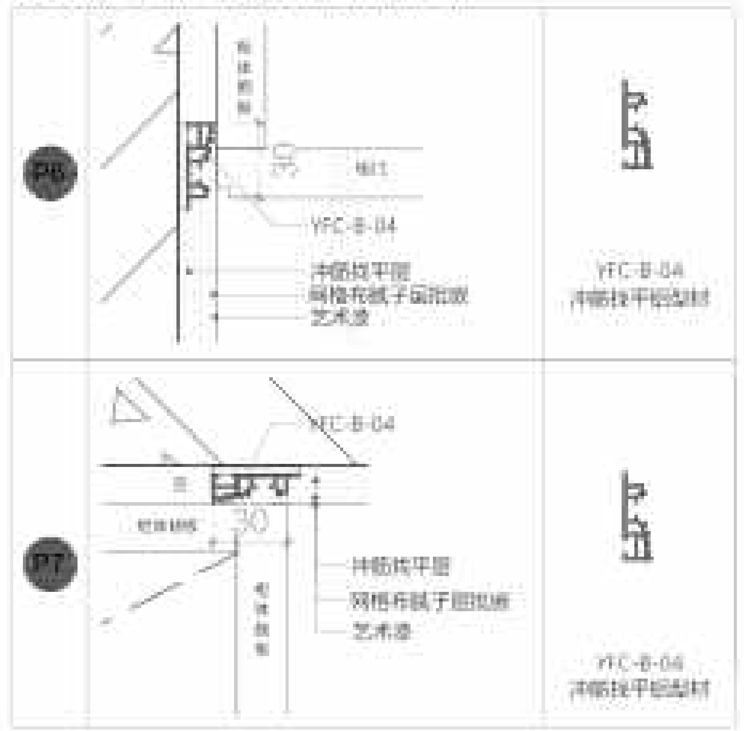
P6
YFC-B-04
冲筋找平层
网格布腻子层批嵌
艺术漆
YFC-B-04
冲筋找平铝型材
P7
YFC-B-04
30
冲筋找平层
网格布腻子层批嵌
艺术漆
YFC-B-04
冲筋找平铝型材

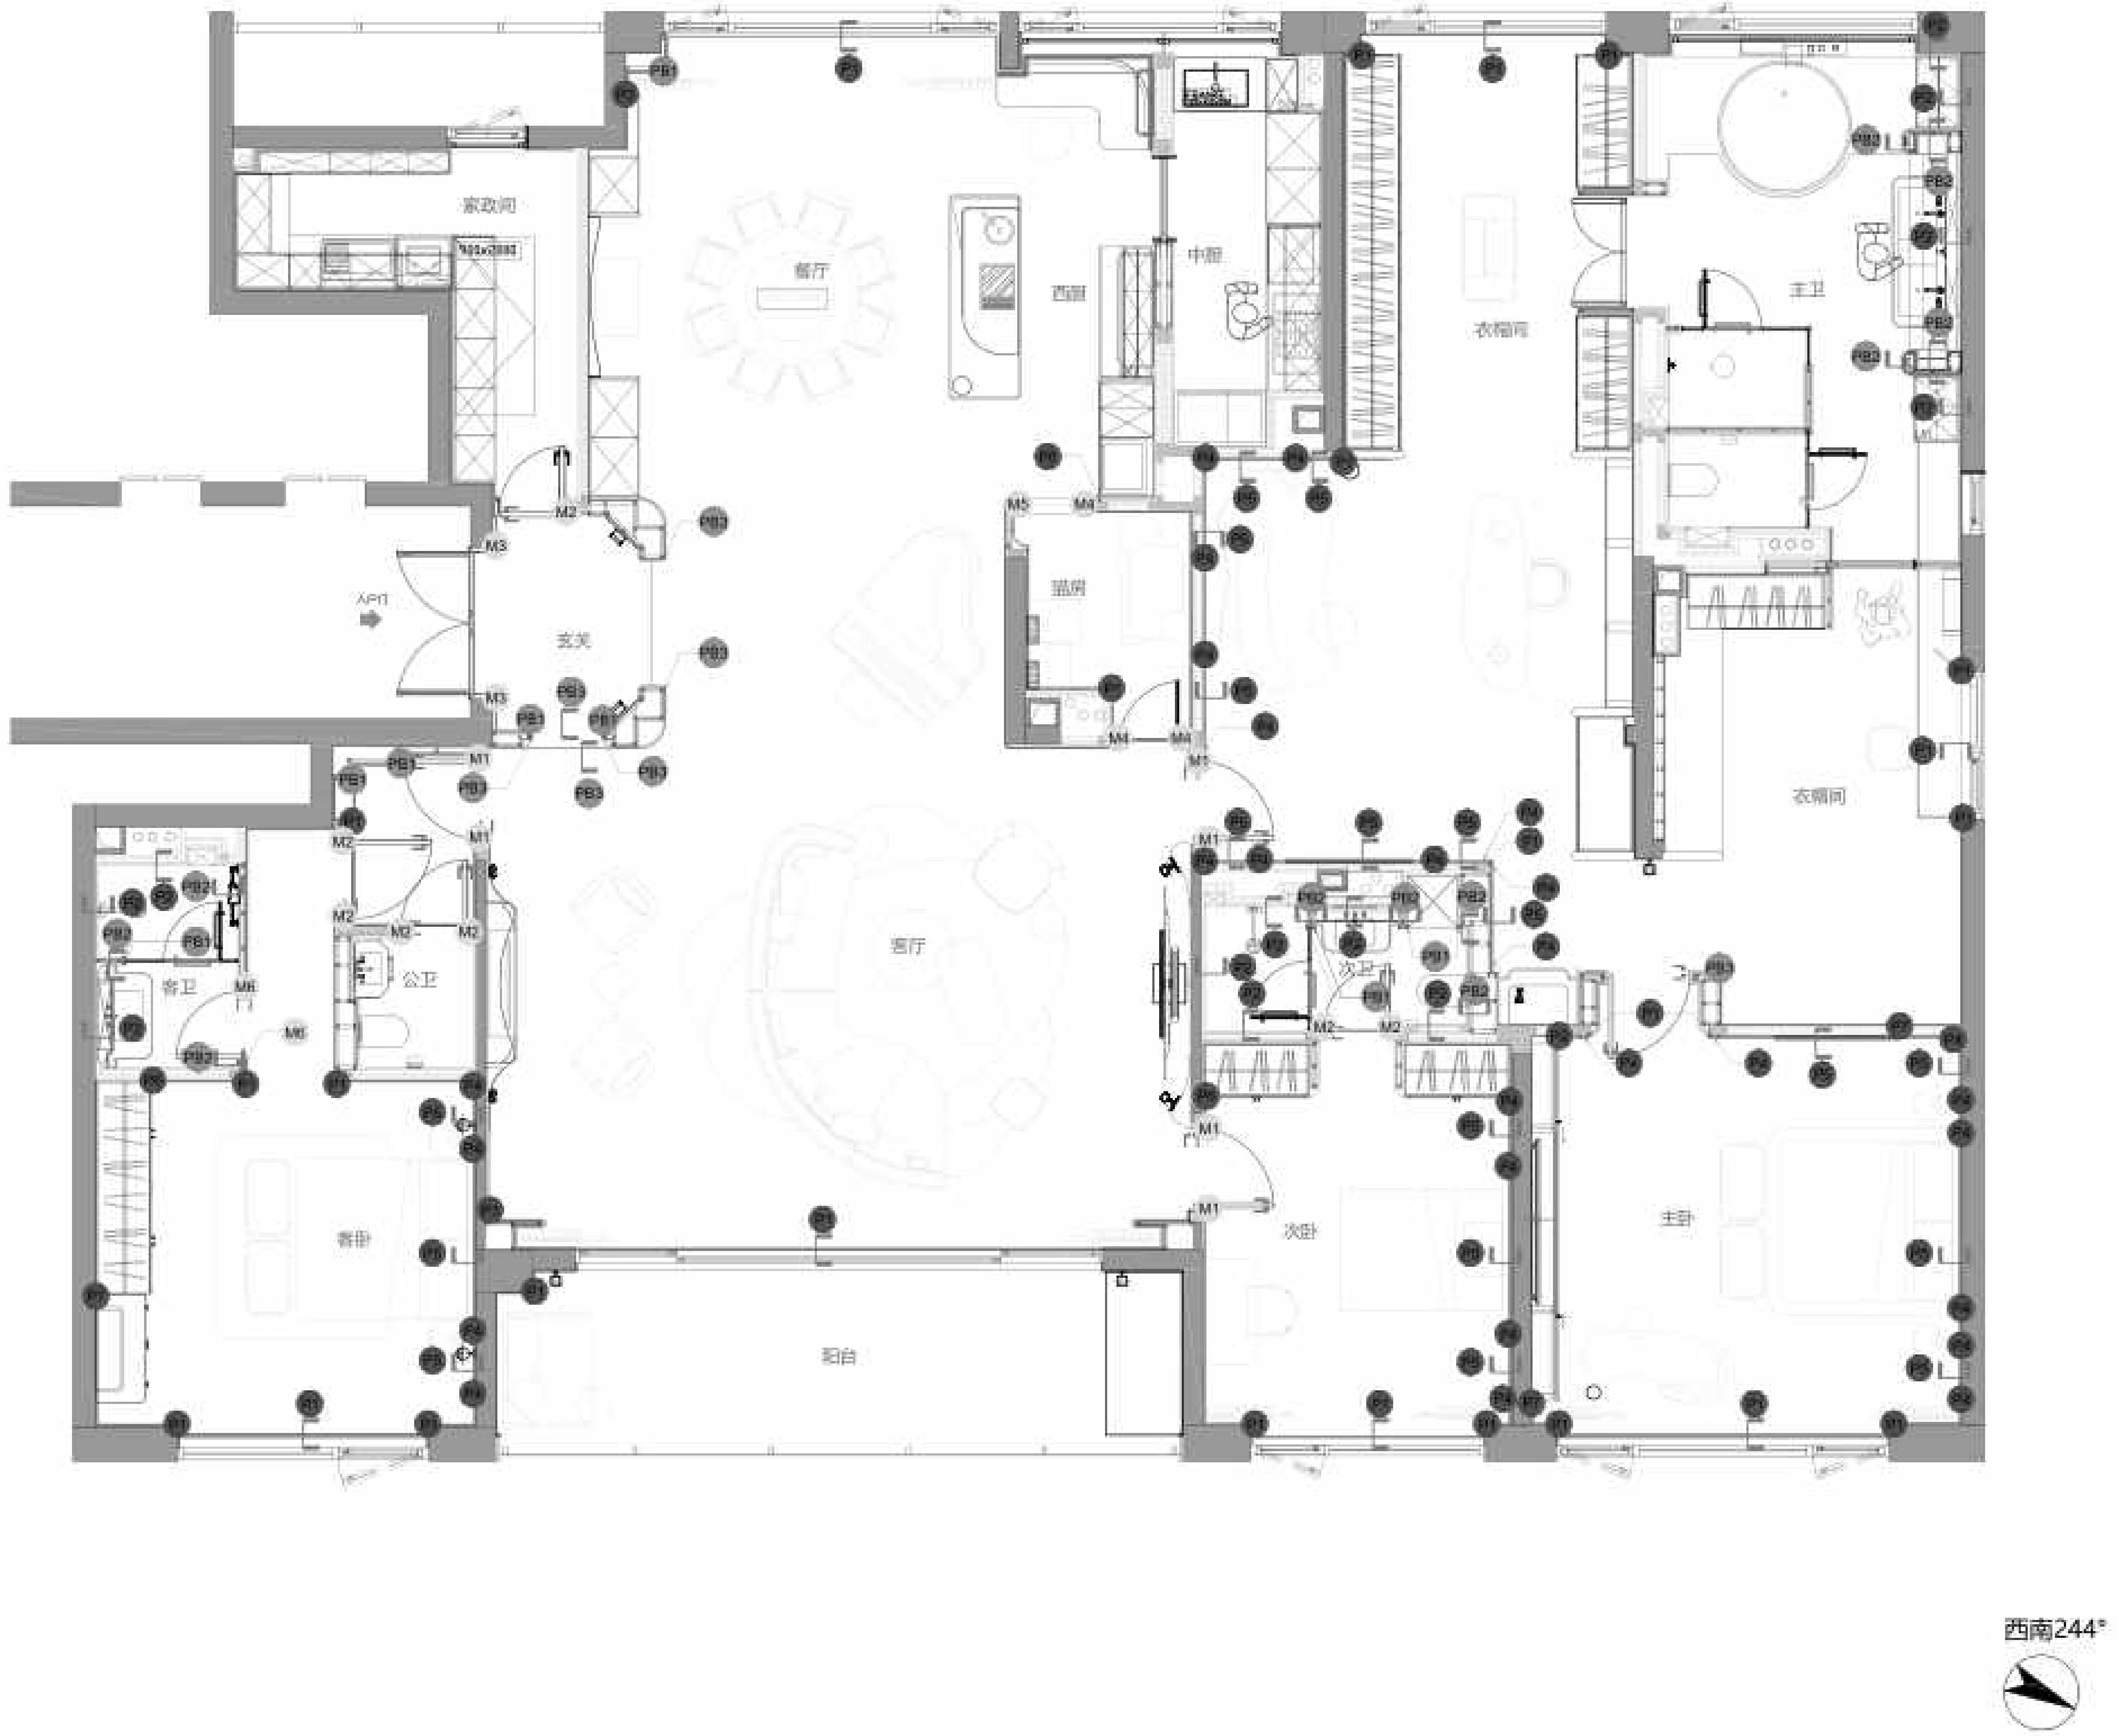
家政间
餐厅
西厨
中厨
衣帽间
主卫
佣房
API
玄关
客卫
公卫
客厅
次卫
客卧
次卧
主卧
衣帽间
阳台
西南244°

图例 C
LEGEND C-石膏板归方找平铝型材

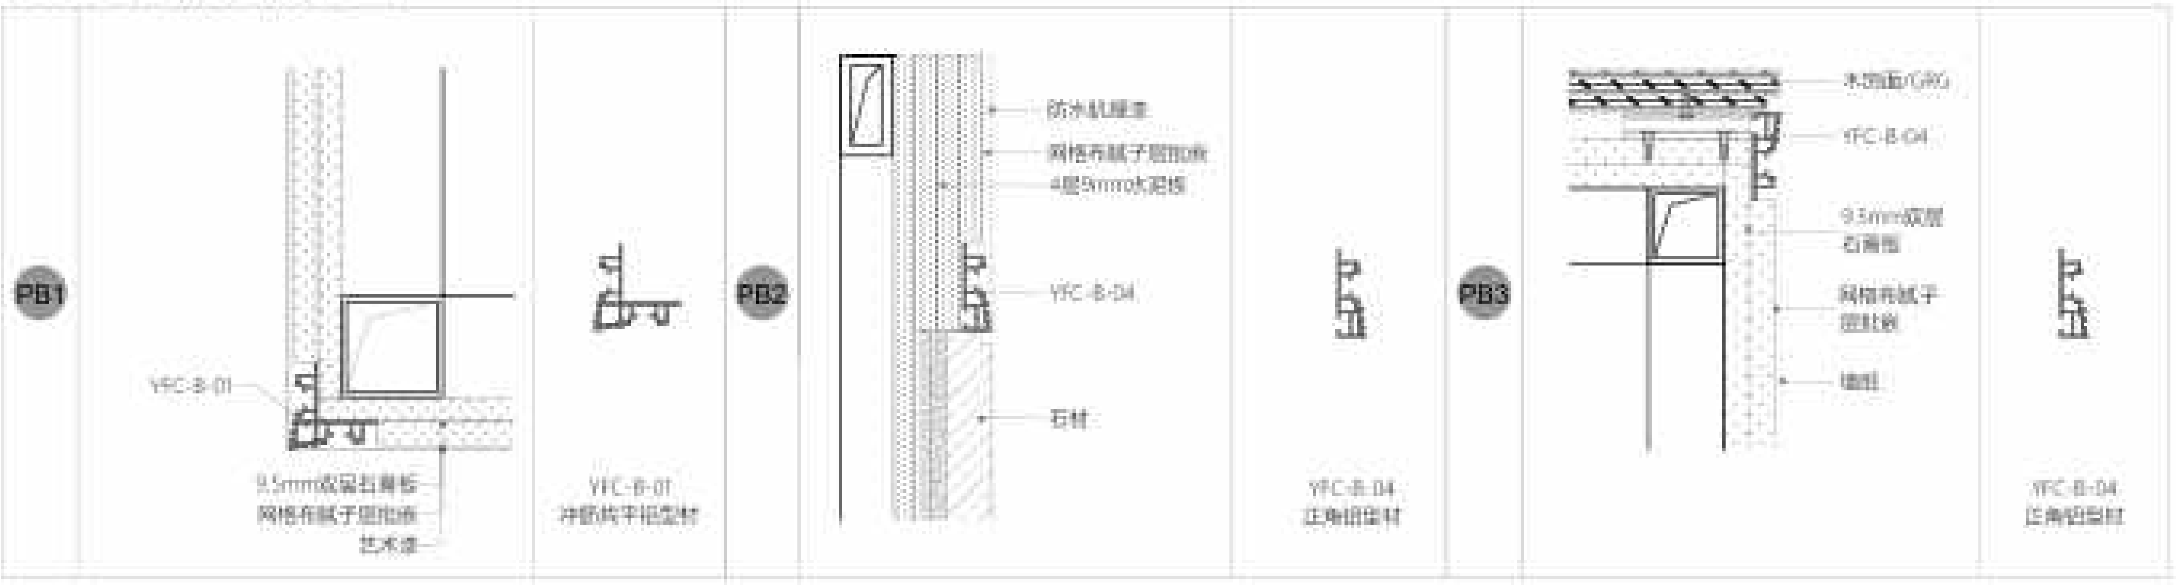
PB1
YFC-B-01
9.5mm双层石膏板
网格布腻子层批嵌
艺术漆
YFC-B-01
冲筋找平铝型材
PB2
防水乳胶漆
网格布腻子层批嵌
4层9mm水泥板
YFC-B-04
石材
YFC-B-04
正角铝型材
PB3
木饰面/GRG
YFC-B-04
9.5mm双层
石膏板
网格布腻子
层批嵌
墙纸
YFC-B-04
正角铝型材

图例 D
LEGEND D-门边铝型材

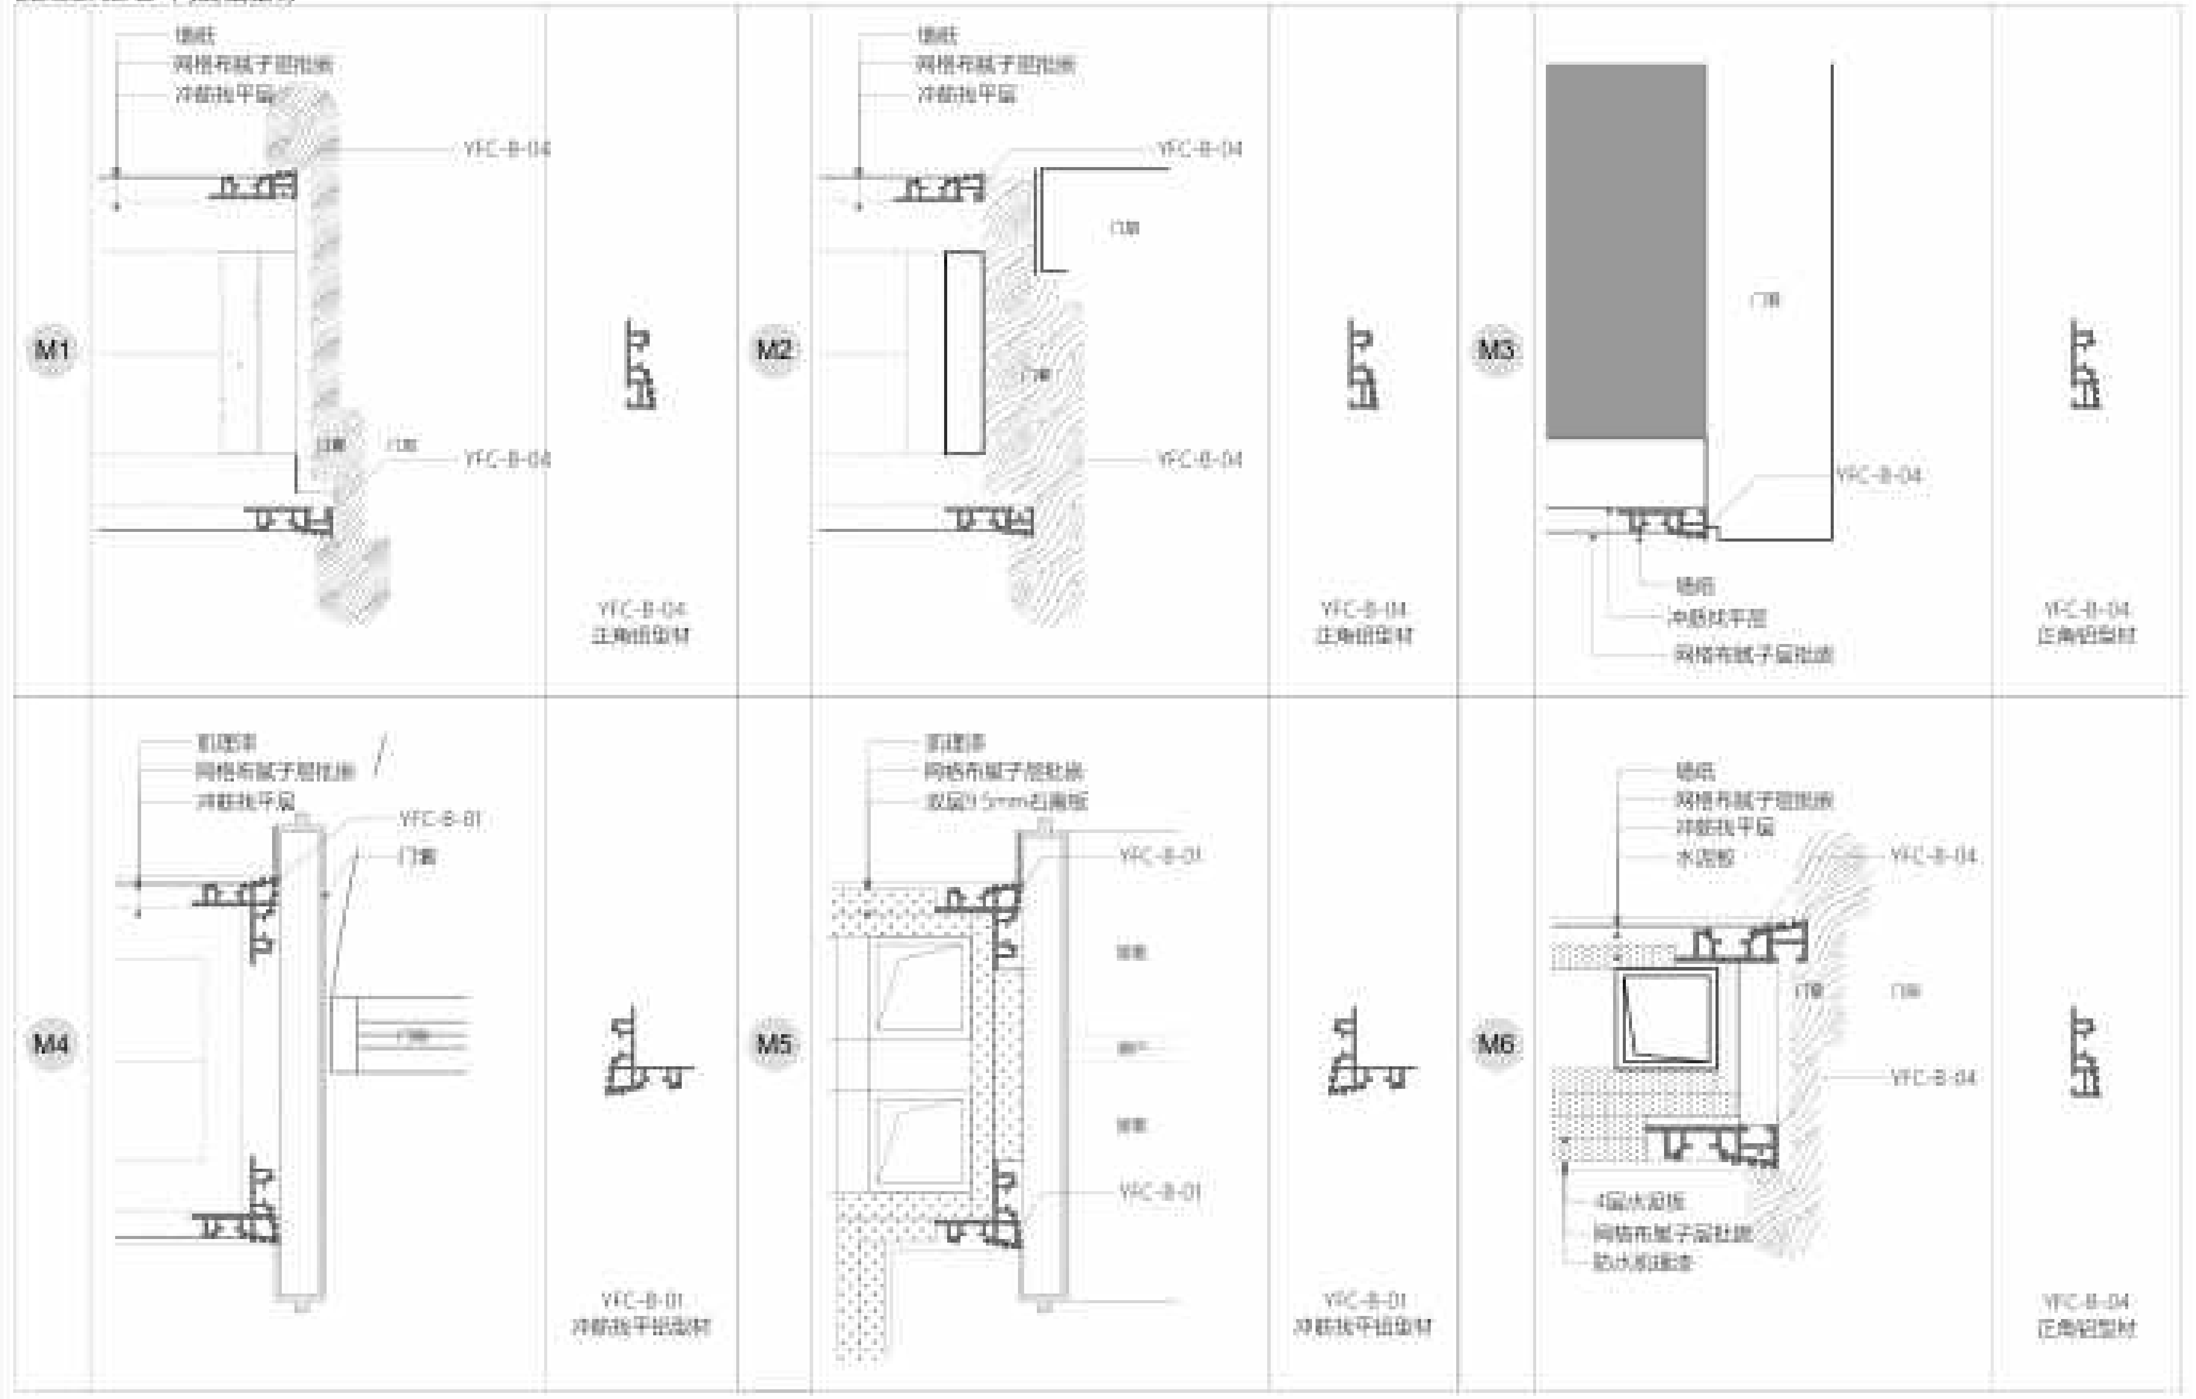
M1
墙纸
网格布腻子层批嵌
冲筋找平层
YFC-B-04
门套
YFC-B-04
YFC-B-04
正角铝型材
M2
墙纸
网格布腻子层批嵌
冲筋找平层
YFC-B-04
门套
YFC-B-04
YFC-B-04
正角铝型材
M3
门套
YFC-B-04
墙纸
冲筋找平层
网格布腻子层批嵌
YFC-B-04
正角铝型材
M4
肌理漆
网格布腻子层批嵌
冲筋找平层
YFC-B-01
门套
YFC-B-01
冲筋找平铝型材
M5
肌理漆
网格布腻子层批嵌
双层9.5mm石膏板
YFC-B-01
YFC-B-01
YFC-B-01
冲筋找平铝型材
M6
墙纸
网格布腻子层批嵌
冲筋找平层
水泥板
YFC-B-04
门套
YFC-B-04
4层水泥板
网格布腻子层批嵌
防水乳胶漆
YFC-B-04
正角铝型材

图纸编号 Drawing No.	图纸名称 Drawing Name	比例 Scale	项目 Project	项目编号 Project No.	注释 Notes	日期 Date	盖章:
AP-01	**墙面铝型材分析平面图**	1:60 @A2	**华岸府**	© 2026	1. 本图纸尺寸如与现场尺寸有误，请施工人员与项目负责人联系。 2. 施工前施工人员应认真查阅此图，如有不明确尺寸，按现场测量为准。 3. 本图纸必须经甲乙双方认可并签字方可作为施工依据。	2026.03.02 修订 Revisions ⚠	

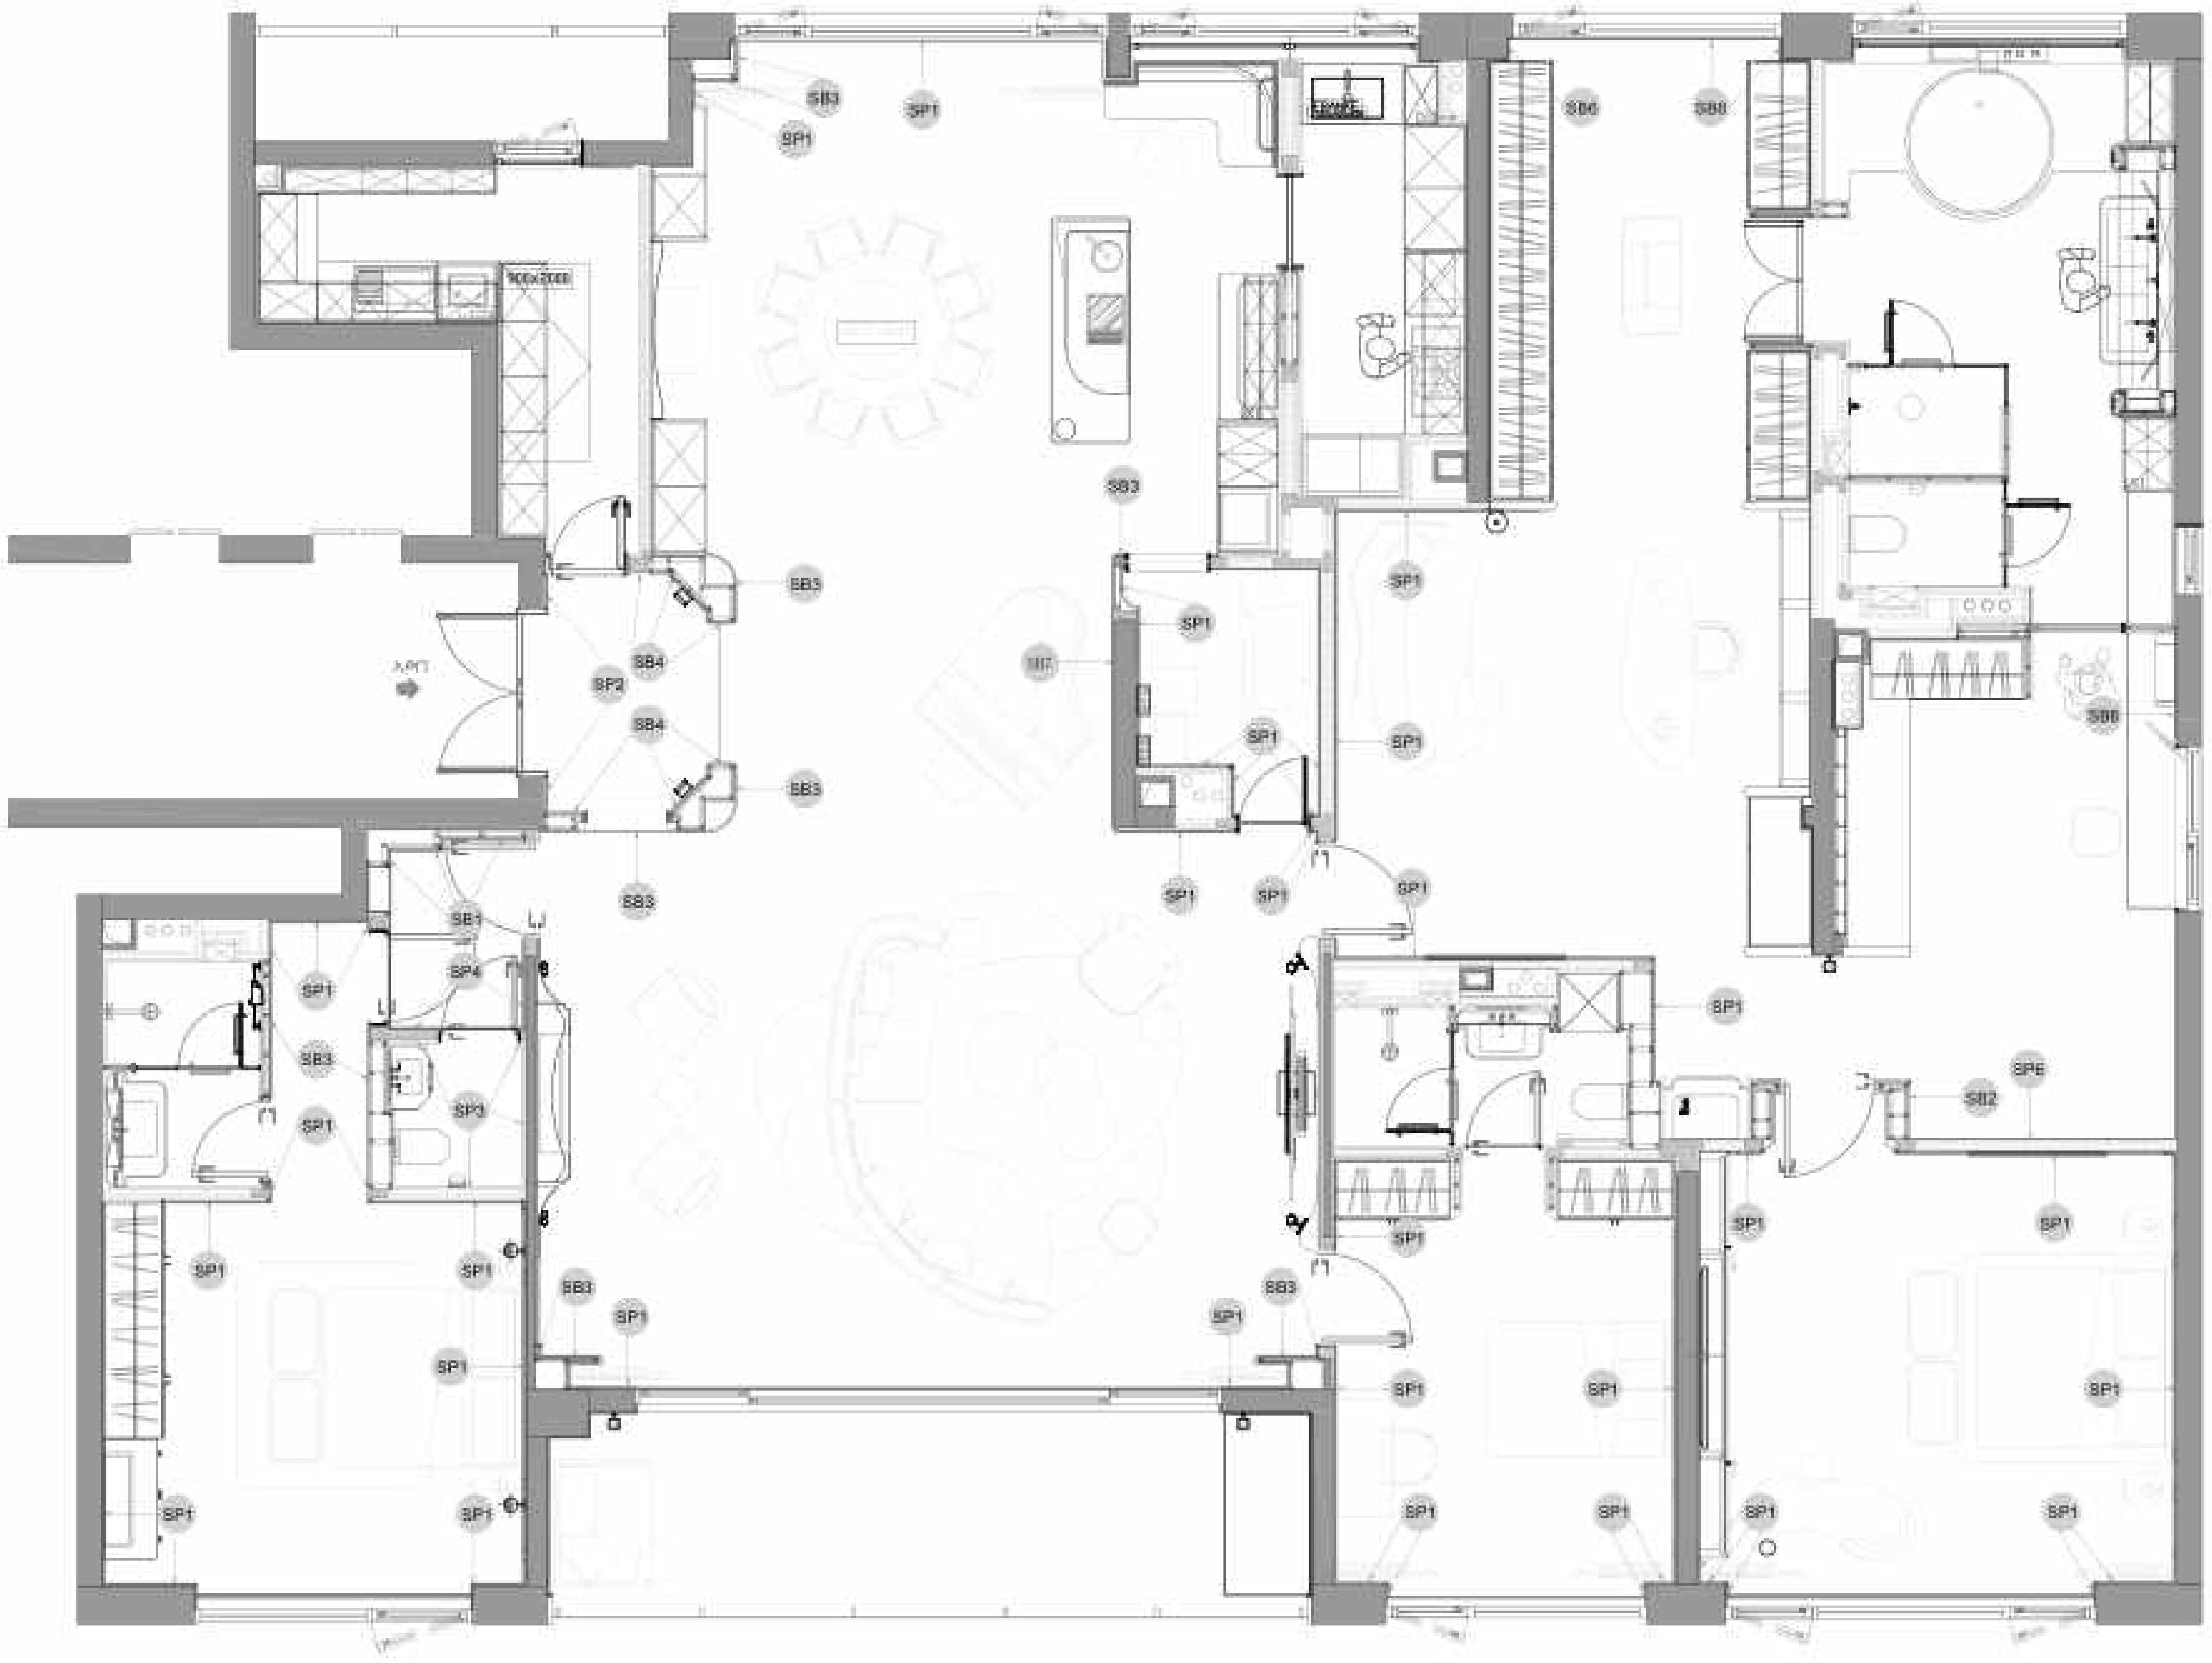
SB3
SP1
SB6
SB8
900x2000
入户门
SP2
SB4
SB7
SP3
SP4
SB1
SB2
SP6

图例 E
LEGEND E-踢脚铝型材

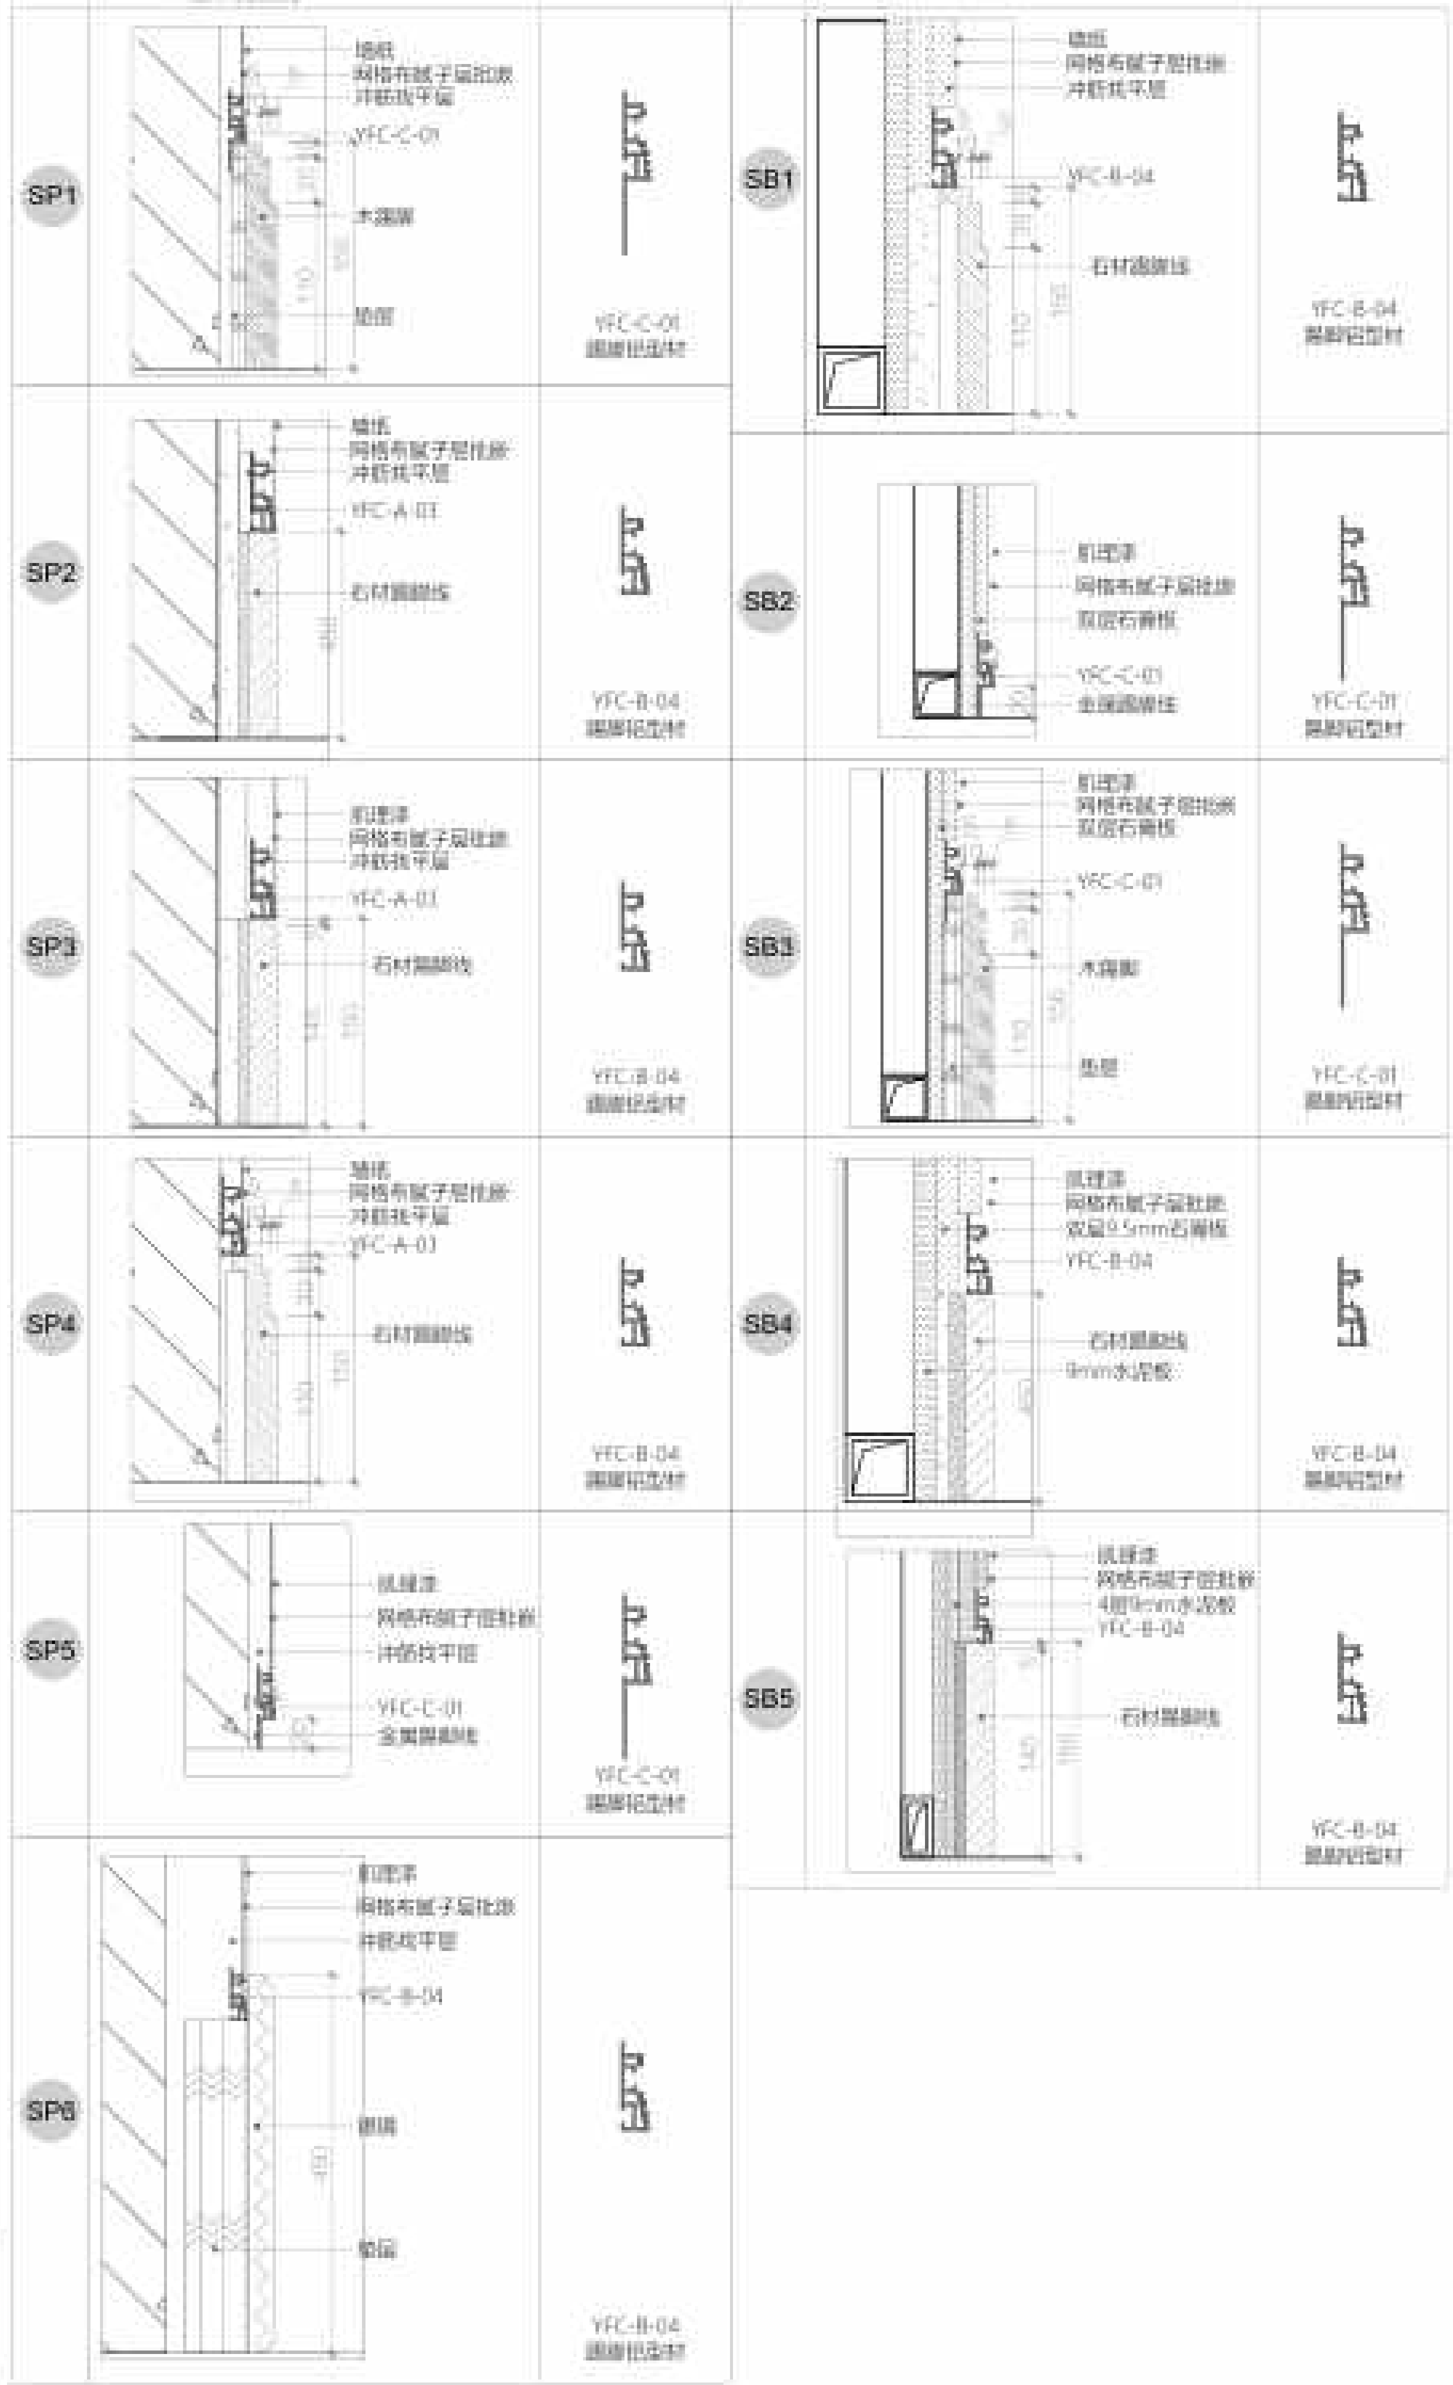
SP1
墙纸
网格布腻子层批嵌
冲筋找平层
YFC-C-01
木踢脚
垫层
YFC-C-01
踢脚铝型材
SB1
墙纸
网格布腻子层批嵌
冲筋找平层
YFC-B-04
石材踢脚线
YFC-B-04
踢脚铝型材
SP2
墙纸
网格布腻子层批嵌
冲筋找平层
YFC-A-01
石材踢脚线
YFC-B-04
踢脚铝型材
SB2
肌理漆
网格布腻子层批嵌
双层石膏板
YFC-C-01
金属踢脚线
YFC-C-01
踢脚铝型材
SP3
肌理漆
网格布腻子层批嵌
冲筋找平层
YFC-A-01
石材踢脚线
YFC-B-04
踢脚铝型材
SB3
肌理漆
网格布腻子层批嵌
双层石膏板
YFC-C-01
木踢脚
垫层
YFC-C-01
踢脚铝型材
SP4
墙纸
网格布腻子层批嵌
冲筋找平层
YFC-A-01
石材踢脚线
YFC-B-04
踢脚铝型材
SB4
肌理漆
网格布腻子层批嵌
双层9.5mm石膏板
YFC-B-04
石材踢脚线
9mm水泥板
YFC-B-04
踢脚铝型材
SP5
肌理漆
网格布腻子层批嵌
冲筋找平层
YFC-C-01
金属踢脚线
YFC-C-01
踢脚铝型材
SB5
肌理漆
网格布腻子层批嵌
4层9mm水泥板
YFC-B-04
石材踢脚线
YFC-B-04
踢脚铝型材
SP6
肌理漆
网格布腻子层批嵌
冲筋找平层
YFC-B-04
踢脚
垫层
YFC-B-04
踢脚铝型材

图纸编号 Drawing No.	图纸名称 Drawing Name	比例 Scale	项目 Project	项目编号 Project No.	注释 Notes	日期 Date	签章:
AP-02	**踢脚铝型材分析平面图**	1:60 @A2	**华岸府**	© 2026	1. 本图纸尺寸如与现场尺寸有误，请施工人员与项目负责人联系。 2. 施工前施工人员应认真查阅此图，如有不明确尺寸，按现场测量为准。 3. 本图纸必须经甲乙双方认可并签字后方可作为施工依据。	2026.03.02 修订 Revisions ⚠	

图例 A
LEGEND A-石膏基冲筋找平铝型材

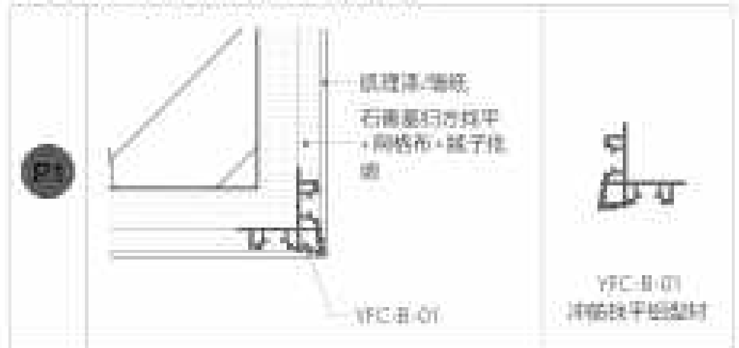
P1
肌理漆/墙纸
石膏基归方找平
+网格布+腻子批嵌
YFC-B-01
YFC-B-01
冲筋找平铝型材

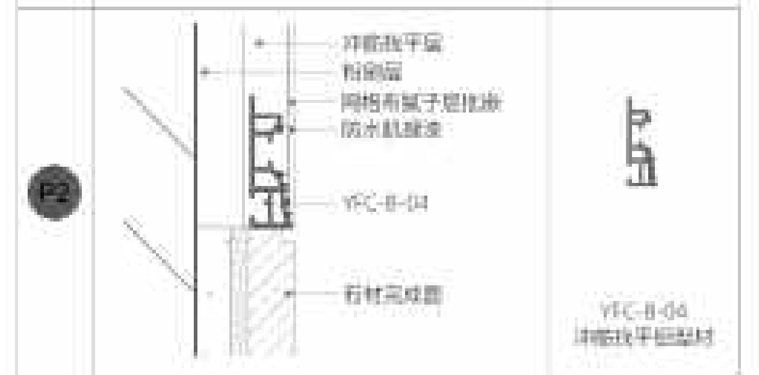
P2
冲筋找平层
粉刷层
网格布腻子层批嵌
防水肌理漆
YFC-B-04
石材完成面
YFC-B-04
冲筋找平铝型材

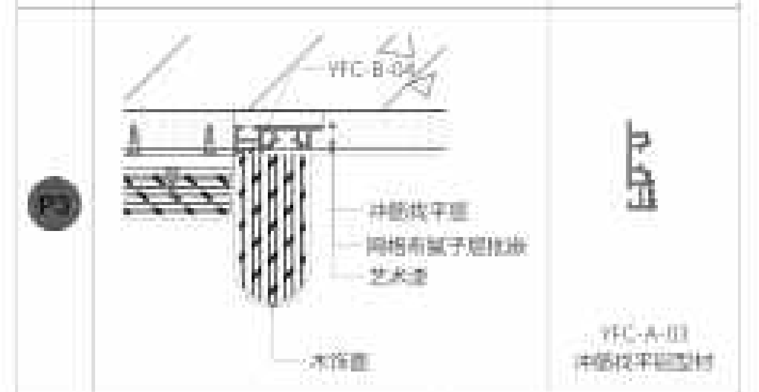
P3
YFC-B-04
冲筋找平层
网格布腻子层批嵌
艺术漆
木饰面
YFC-A-03
冲筋找平铝型材

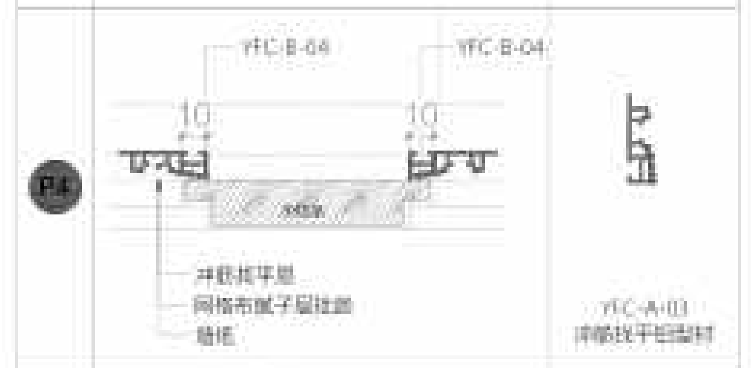
P4
YFC-B-04
YFC-B-04
10
10
冲筋找平层
网格布腻子层批嵌
墙纸
YFC-A-03
冲筋找平铝型材

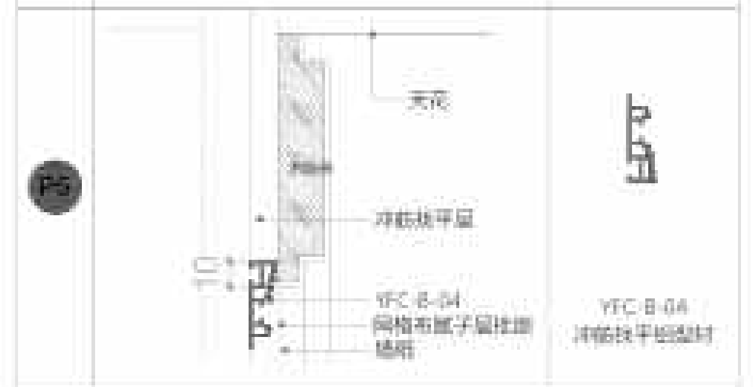
P5
天花
冲筋找平层
10
YFC-B-04
网格布腻子层批嵌
墙纸
YFC-B-04
冲筋找平铝型材

图例 B
LEGEND B-柜边石膏基冲筋找平铝型材

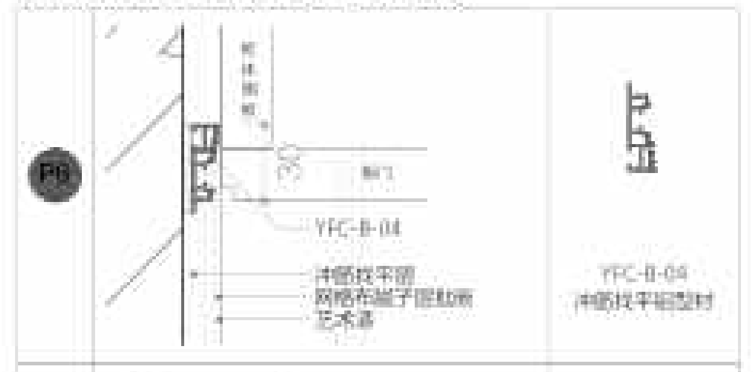
P6
柜体侧板
柜门
20
YFC-B-04
冲筋找平层
网格布腻子层批嵌
艺术漆
YFC-B-04
冲筋找平铝型材

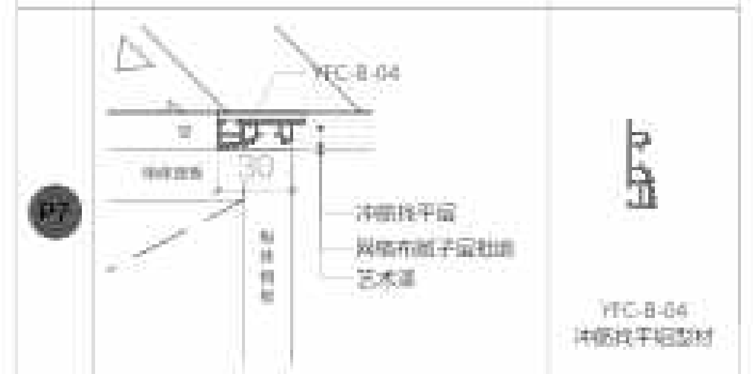
P7
YFC-B-04
30
柜体顶板
柜体侧板
冲筋找平层
网格布腻子层批嵌
艺术漆
YFC-B-04
冲筋找平铝型材

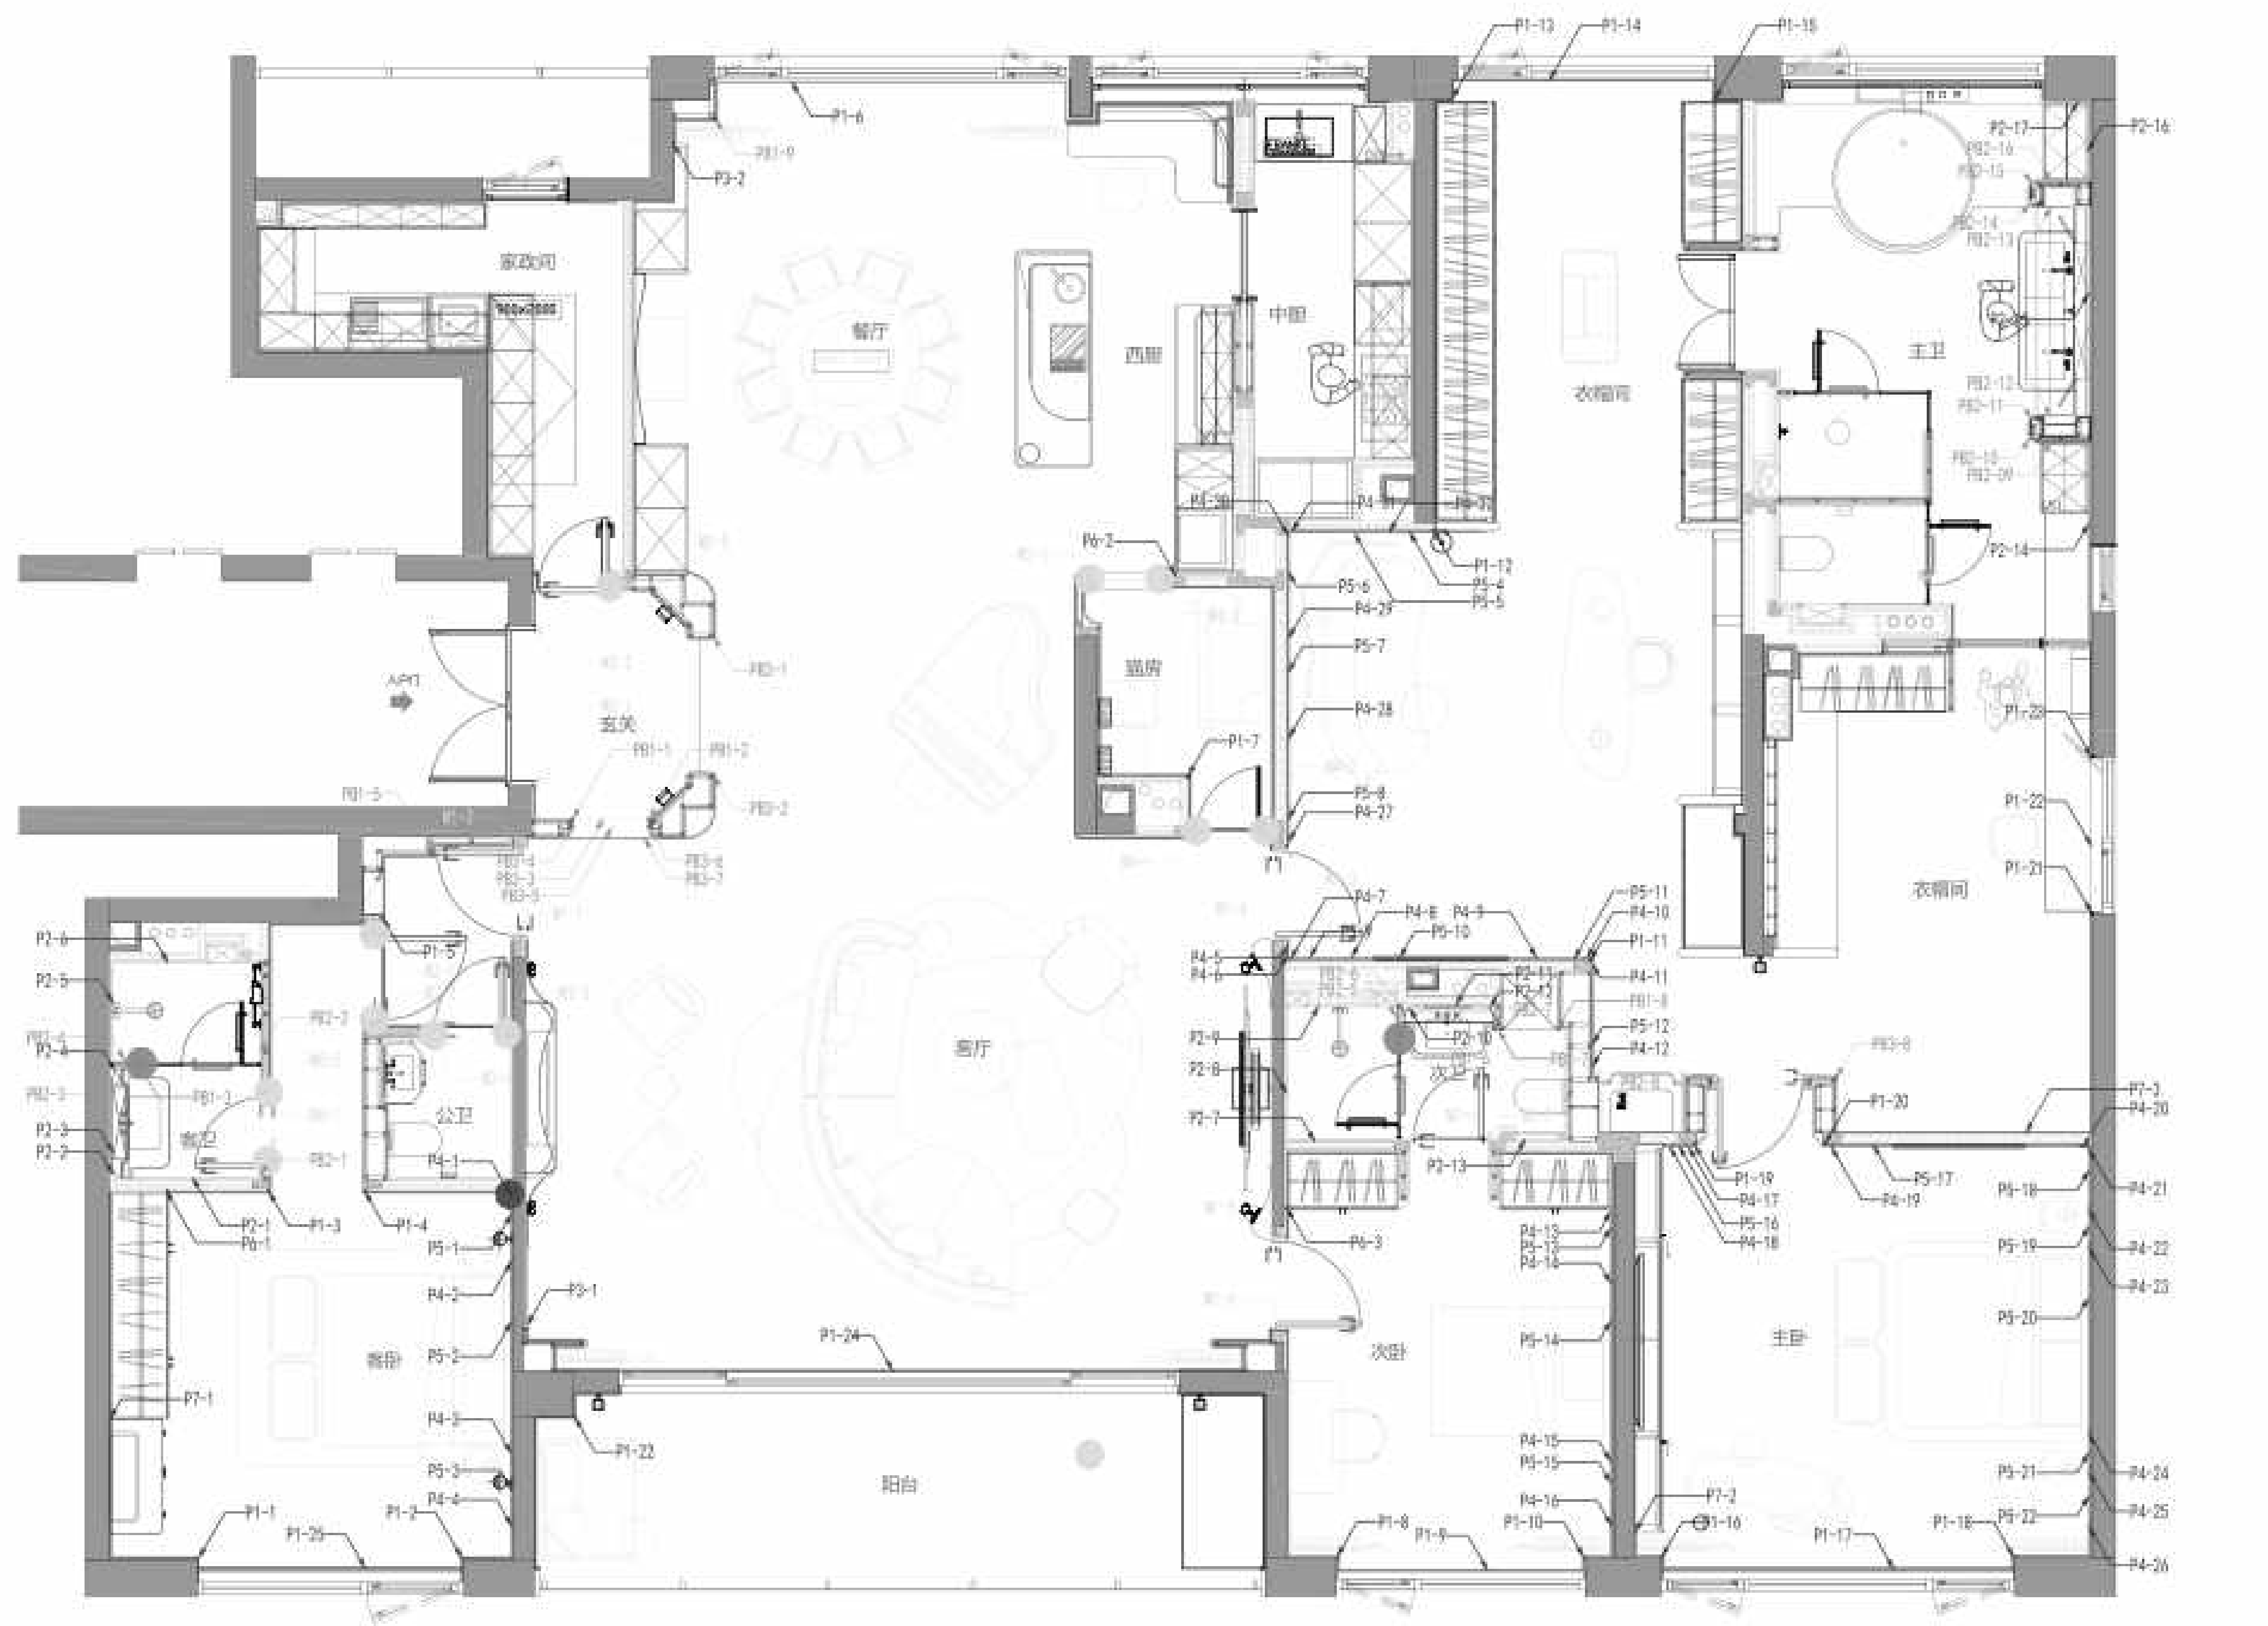
家政间
餐厅
西厨
中厨
衣帽间
主卫
玄关
猫房
衣帽间
客厅
客卫
公卫
次卫
客卧
阳台
次卧
主卧
P1-6
PB1-9
P3-2
P1-13
P1-14
P1-15
P2-17
P2-16
PB2-16
PB2-15
PB2-14
PB2-13
PB2-12
PB2-11
PB2-10
PB2-09
P2-14
P6-2
P4-30
P4-31
P1-12
P5-4
P5-5
P5-6
P4-29
P5-7
P4-28
P1-7
P5-8
P4-27
P1-22
P1-21
PB3-1
PB1-1
PB1-2
PB3-2
PB1-5
PB3-6
PB3-7
PB3-4
PB3-3
PB3-5
P1-5
P2-6
P2-5
PB2-4
P2-4
PB2-3
P2-3
P2-2
PB2-2
PB1-3
PB2-1
P2-1
P6-1
P1-3
P1-4
P5-1
P4-1
P4-2
P3-1
P5-2
P7-1
P4-3
P5-3
P4-4
P1-1
P1-25
P1-2
P1-22
P1-24
P4-7
P4-8
P4-9
P5-10
P4-5
P4-6
P5-11
P4-10
P1-11
P4-11
PB1-8
P2-11
P2-12
P5-12
P4-12
P2-10
P2-9
P2-8
P2-7
P2-13
P6-3
P4-13
P5-13
P4-14
P5-14
P4-15
P5-15
P4-16
P5-16
P1-8
P1-9
P1-10
P7-2
P1-16
P1-17
P1-18
PB3-8
P1-30
P1-19
P4-17
P5-16
P4-18
P5-17
P4-19
P7-3
P4-20
P4-21
P5-18
P5-19
P4-22
P4-23
P5-20
P5-21
P4-24
P4-25
P5-22
P4-26

西南244°

图例 C
LEGEND C-石膏板归方找平铝型材

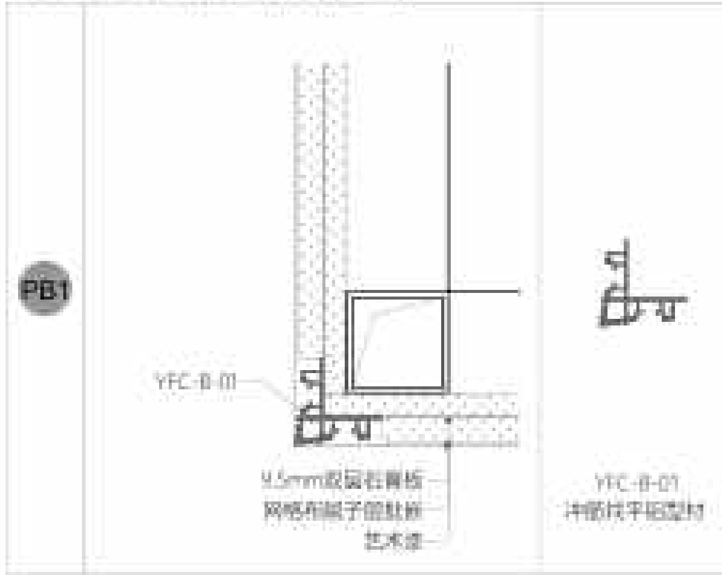
PB1
YFC-B-01
9.5mm双层石膏板
网格布腻子层批嵌
艺术漆
YFC-B-01
冲筋找平铝型材

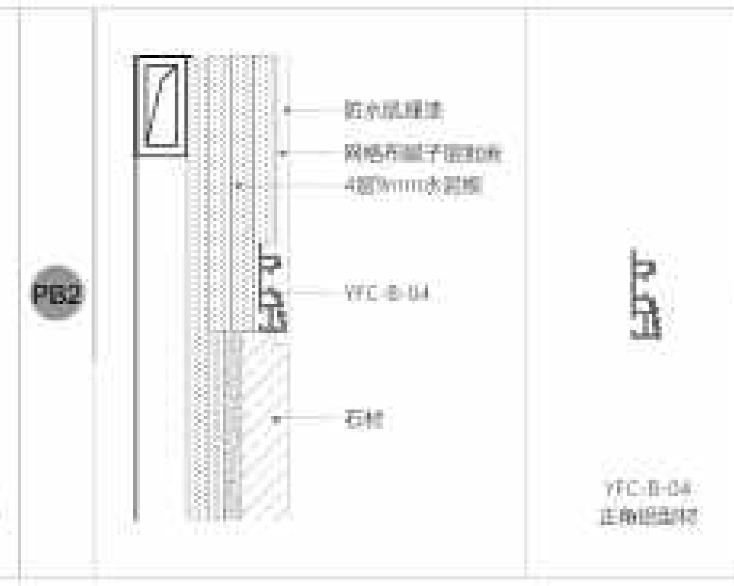
PB2
防水肌理漆
网格布腻子层批嵌
4层9mm水泥板
YFC-B-04
石材
YFC-B-04
正角铝型材

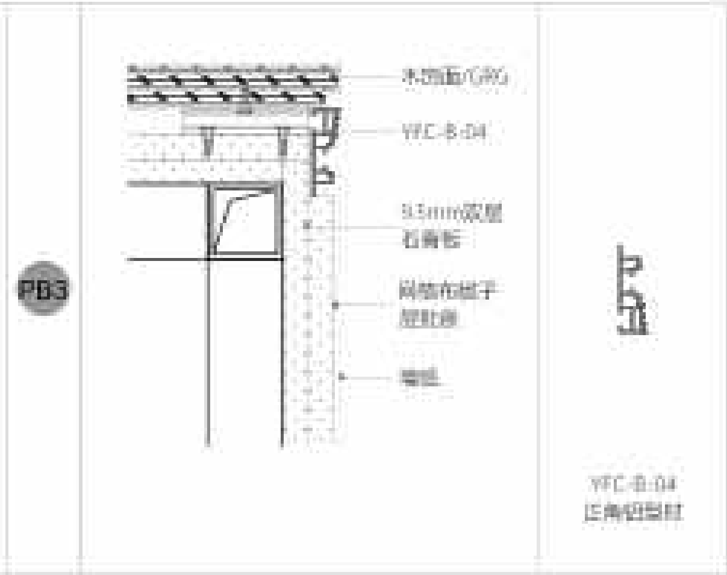
PB3
木饰面/GRG
YFC-B-04
9.5mm双层
石膏板
网格布腻子
层批嵌
墙纸
YFC-B-04
正角铝型材

图例 D
LEGEND D-门边铝型材

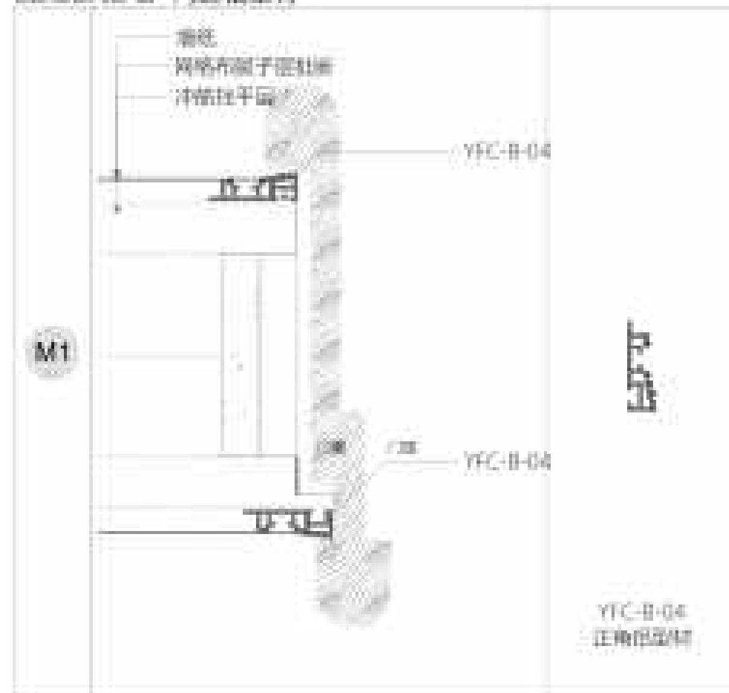
M1
墙纸
网格布腻子层批嵌
冲筋找平层
YFC-B-04
门套
YFC-B-04
YFC-B-04
正角铝型材

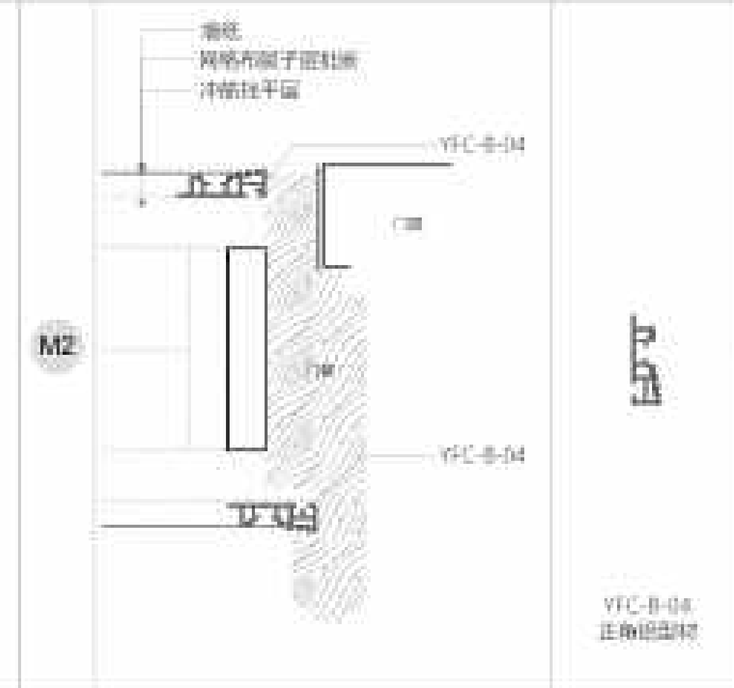
M2
墙纸
网格布腻子层批嵌
冲筋找平层
YFC-B-04
门套
门套
YFC-B-04
YFC-B-04
正角铝型材

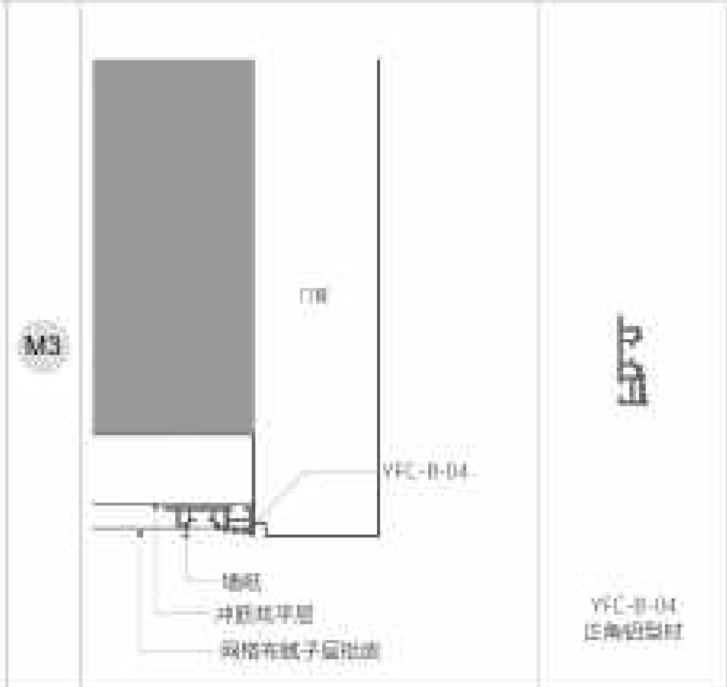
M3
门套
YFC-B-04
墙纸
冲筋找平层
网格布腻子层批嵌
YFC-B-04
正角铝型材

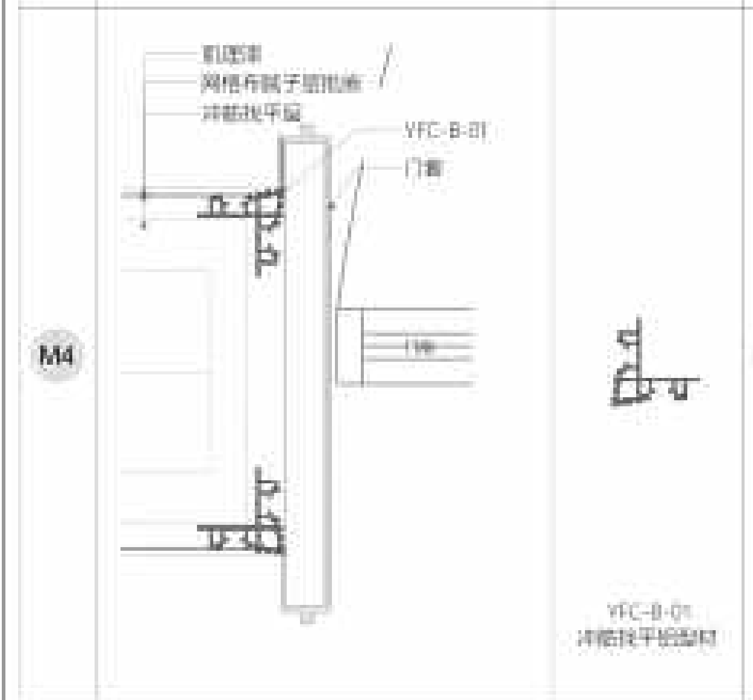
M4
乳胶漆
网格布腻子层批嵌
冲筋找平层
YFC-B-01
门套
门套
YFC-B-01
冲筋找平铝型材

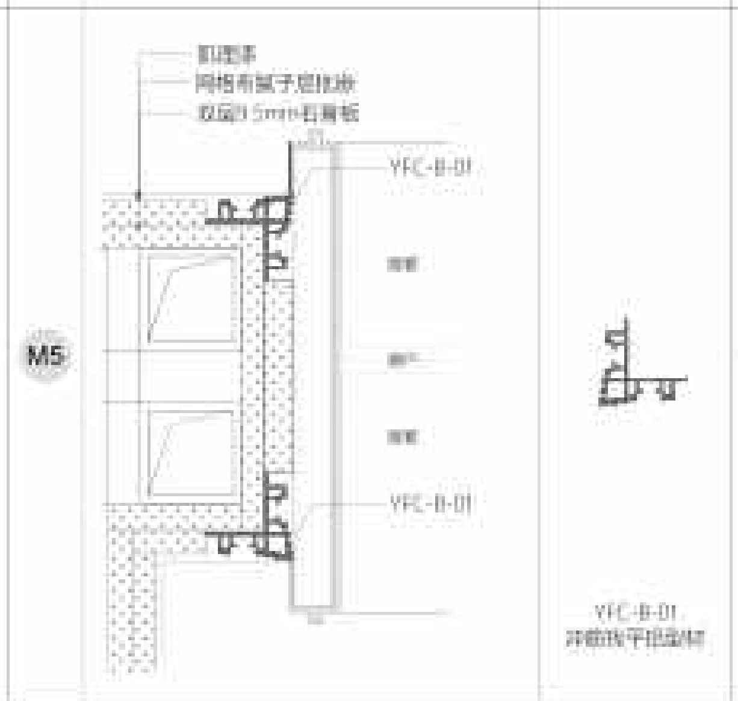
M5
乳胶漆
网格布腻子层批嵌
双层9.5mm石膏板
YFC-B-01
墙体
墙体
YFC-B-01
YFC-B-01
冲筋找平铝型材

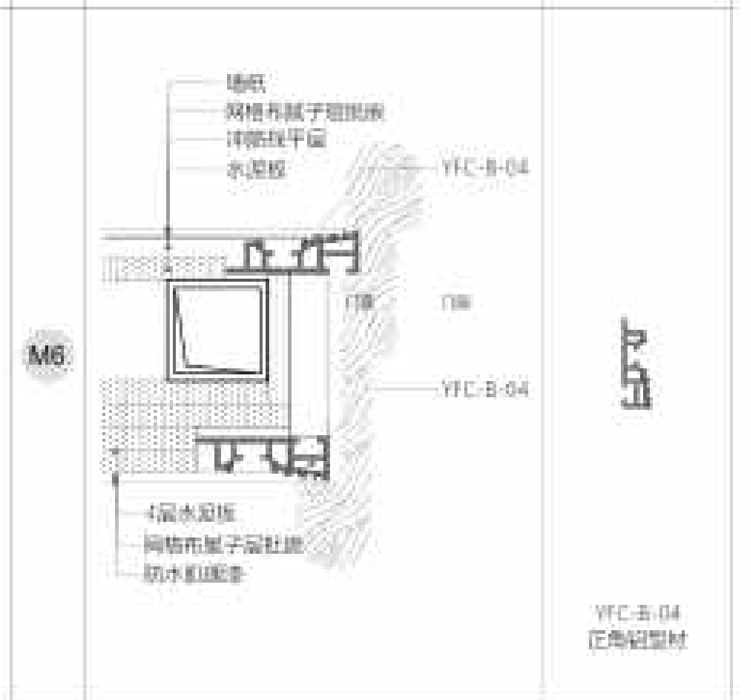
M6
墙纸
网格布腻子层批嵌
冲筋找平层
水泥板
YFC-B-04
门套
门套
YFC-B-04
4层水泥板
网格布腻子层批嵌
防水肌理漆
YFC-B-04
正角铝型材

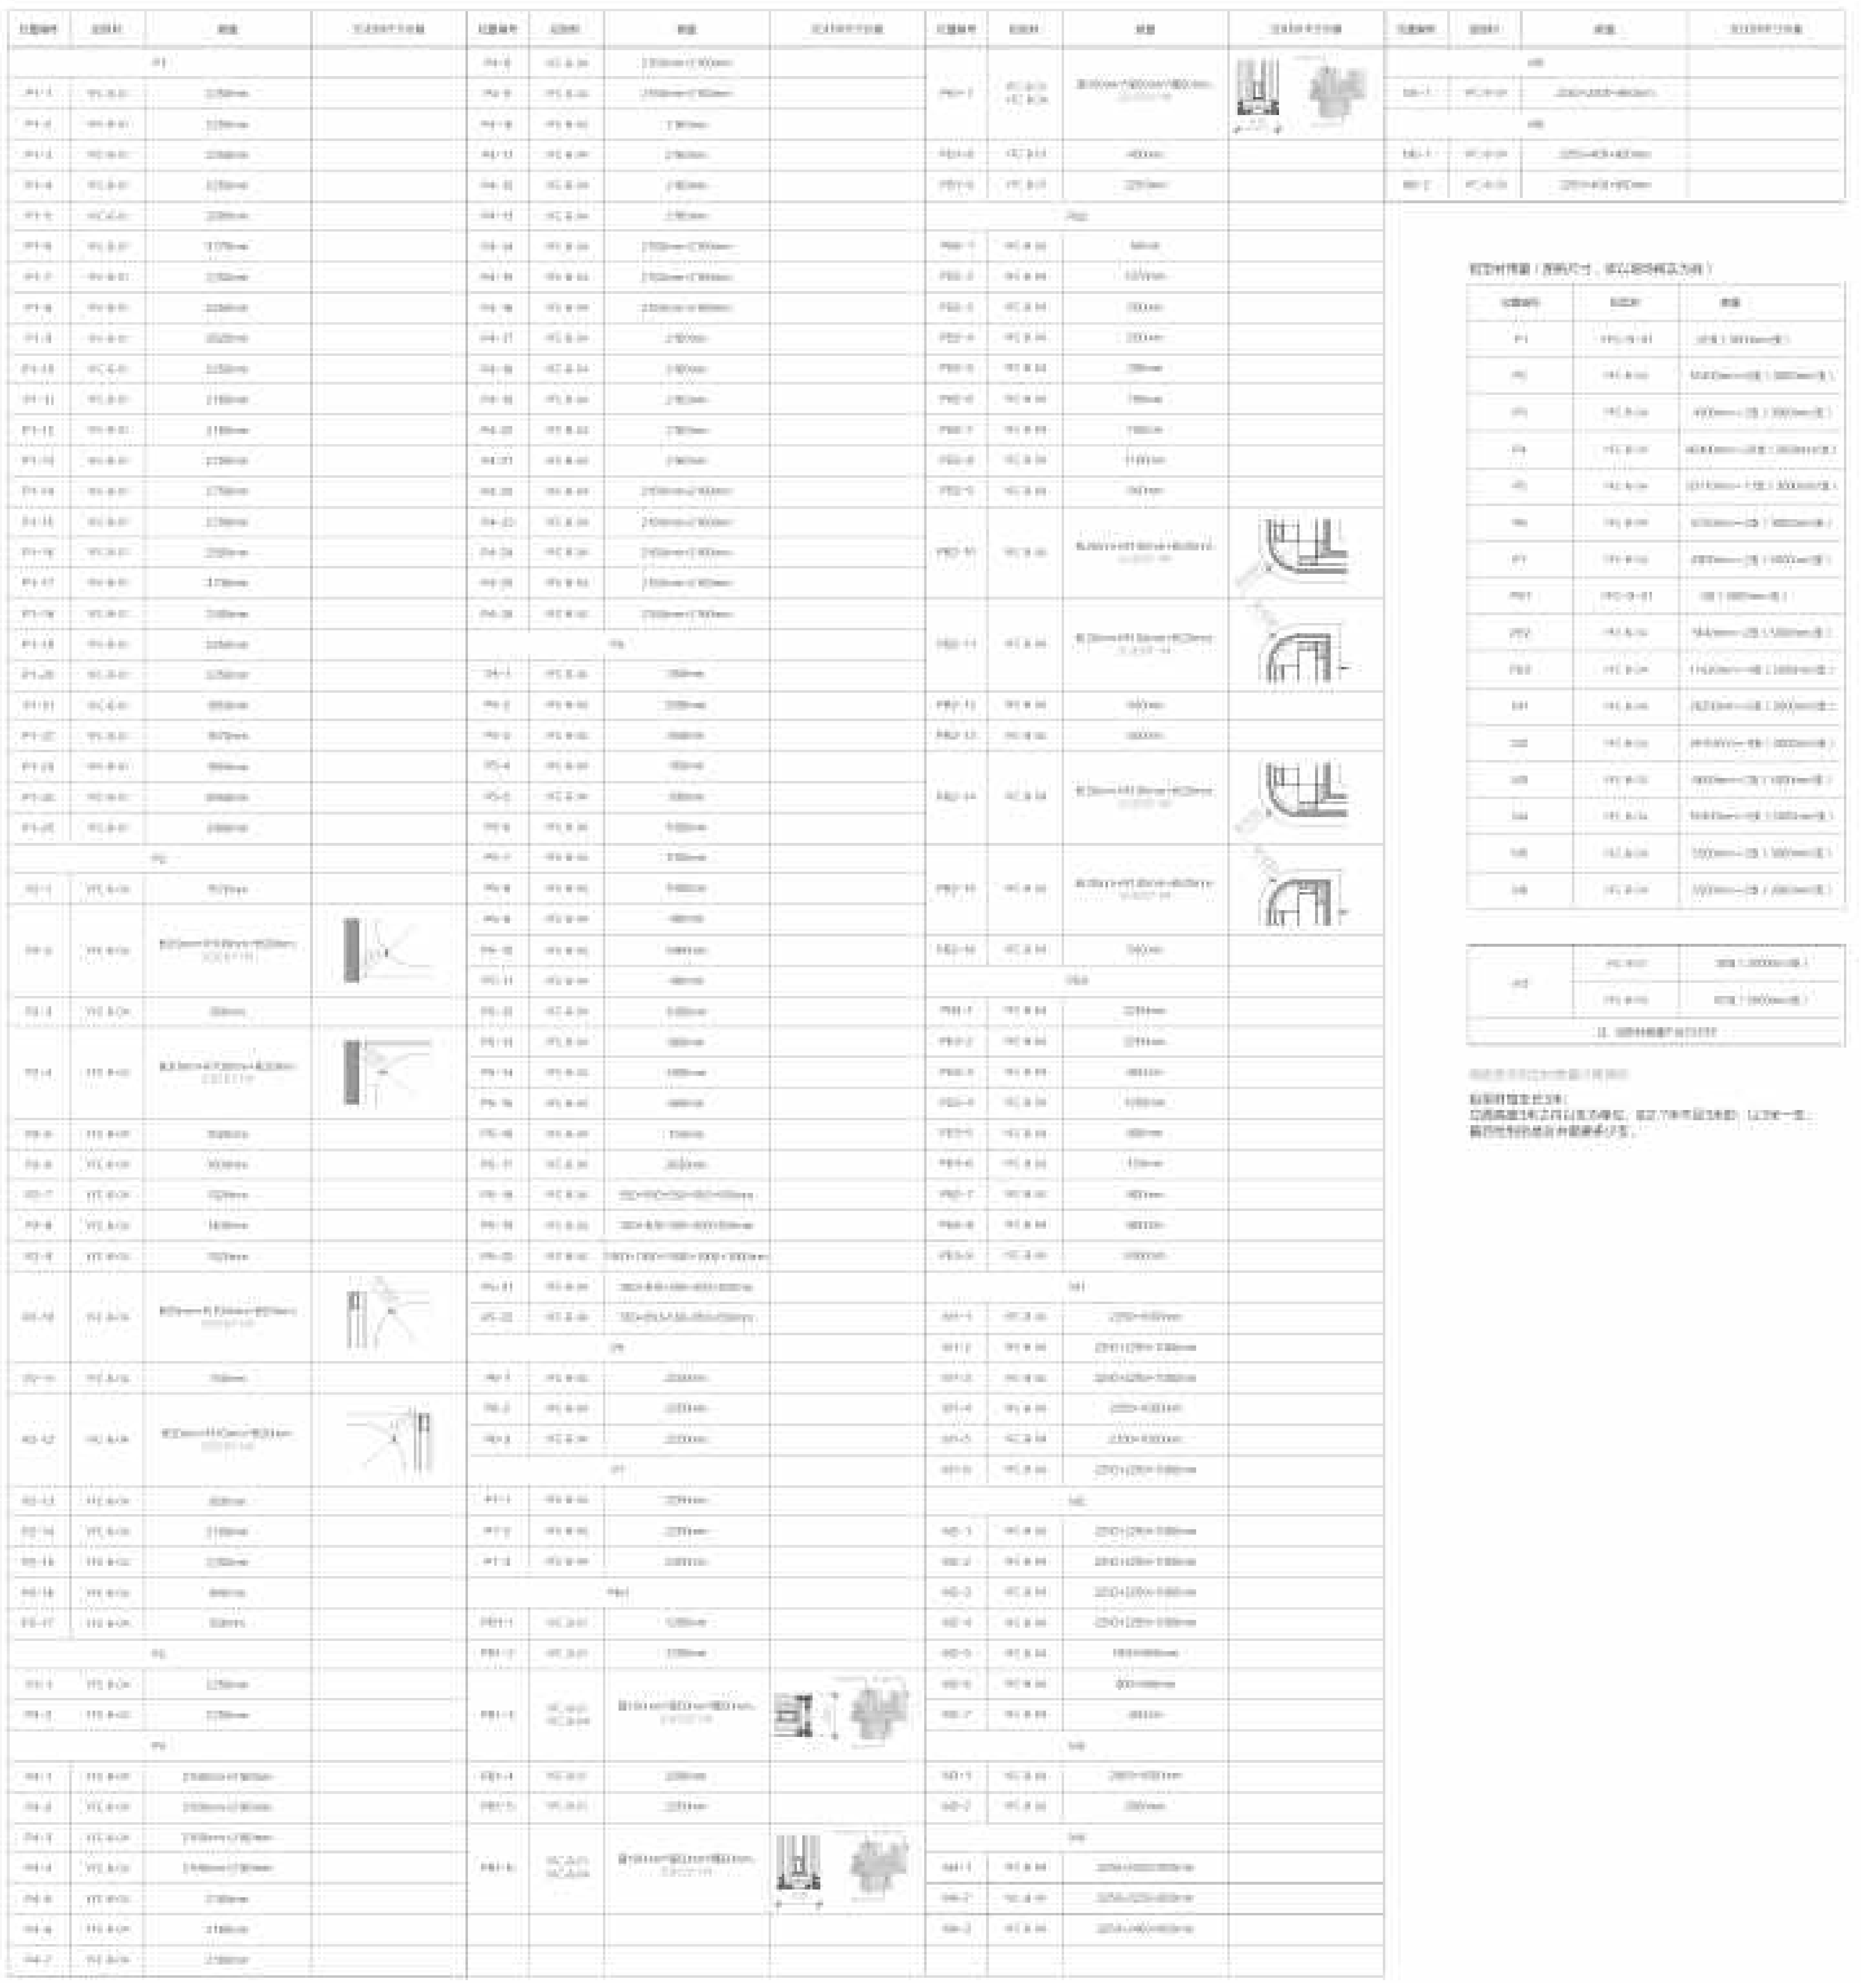

图纸编号 Drawing No.	图纸名称 Drawing Name	比例 Scale	项目 Project	项目编号 Project No.	注释 Notes	日期 Date	盖章:
AP-01	**墙面铝型材分析平面图**	1:60 @A2	**华岸府**	© 2026	1. 本图纸尺寸如与现场尺寸有误，请施工人员与项目负责人联系。 2. 施工前施工人员应认真查阅此图，如有不明确尺寸，按现场测量为准。 3. 本图纸必须经甲乙双方认可并签字方可作为施工依据。	2026.02.04 修订 Revisions ⚠	

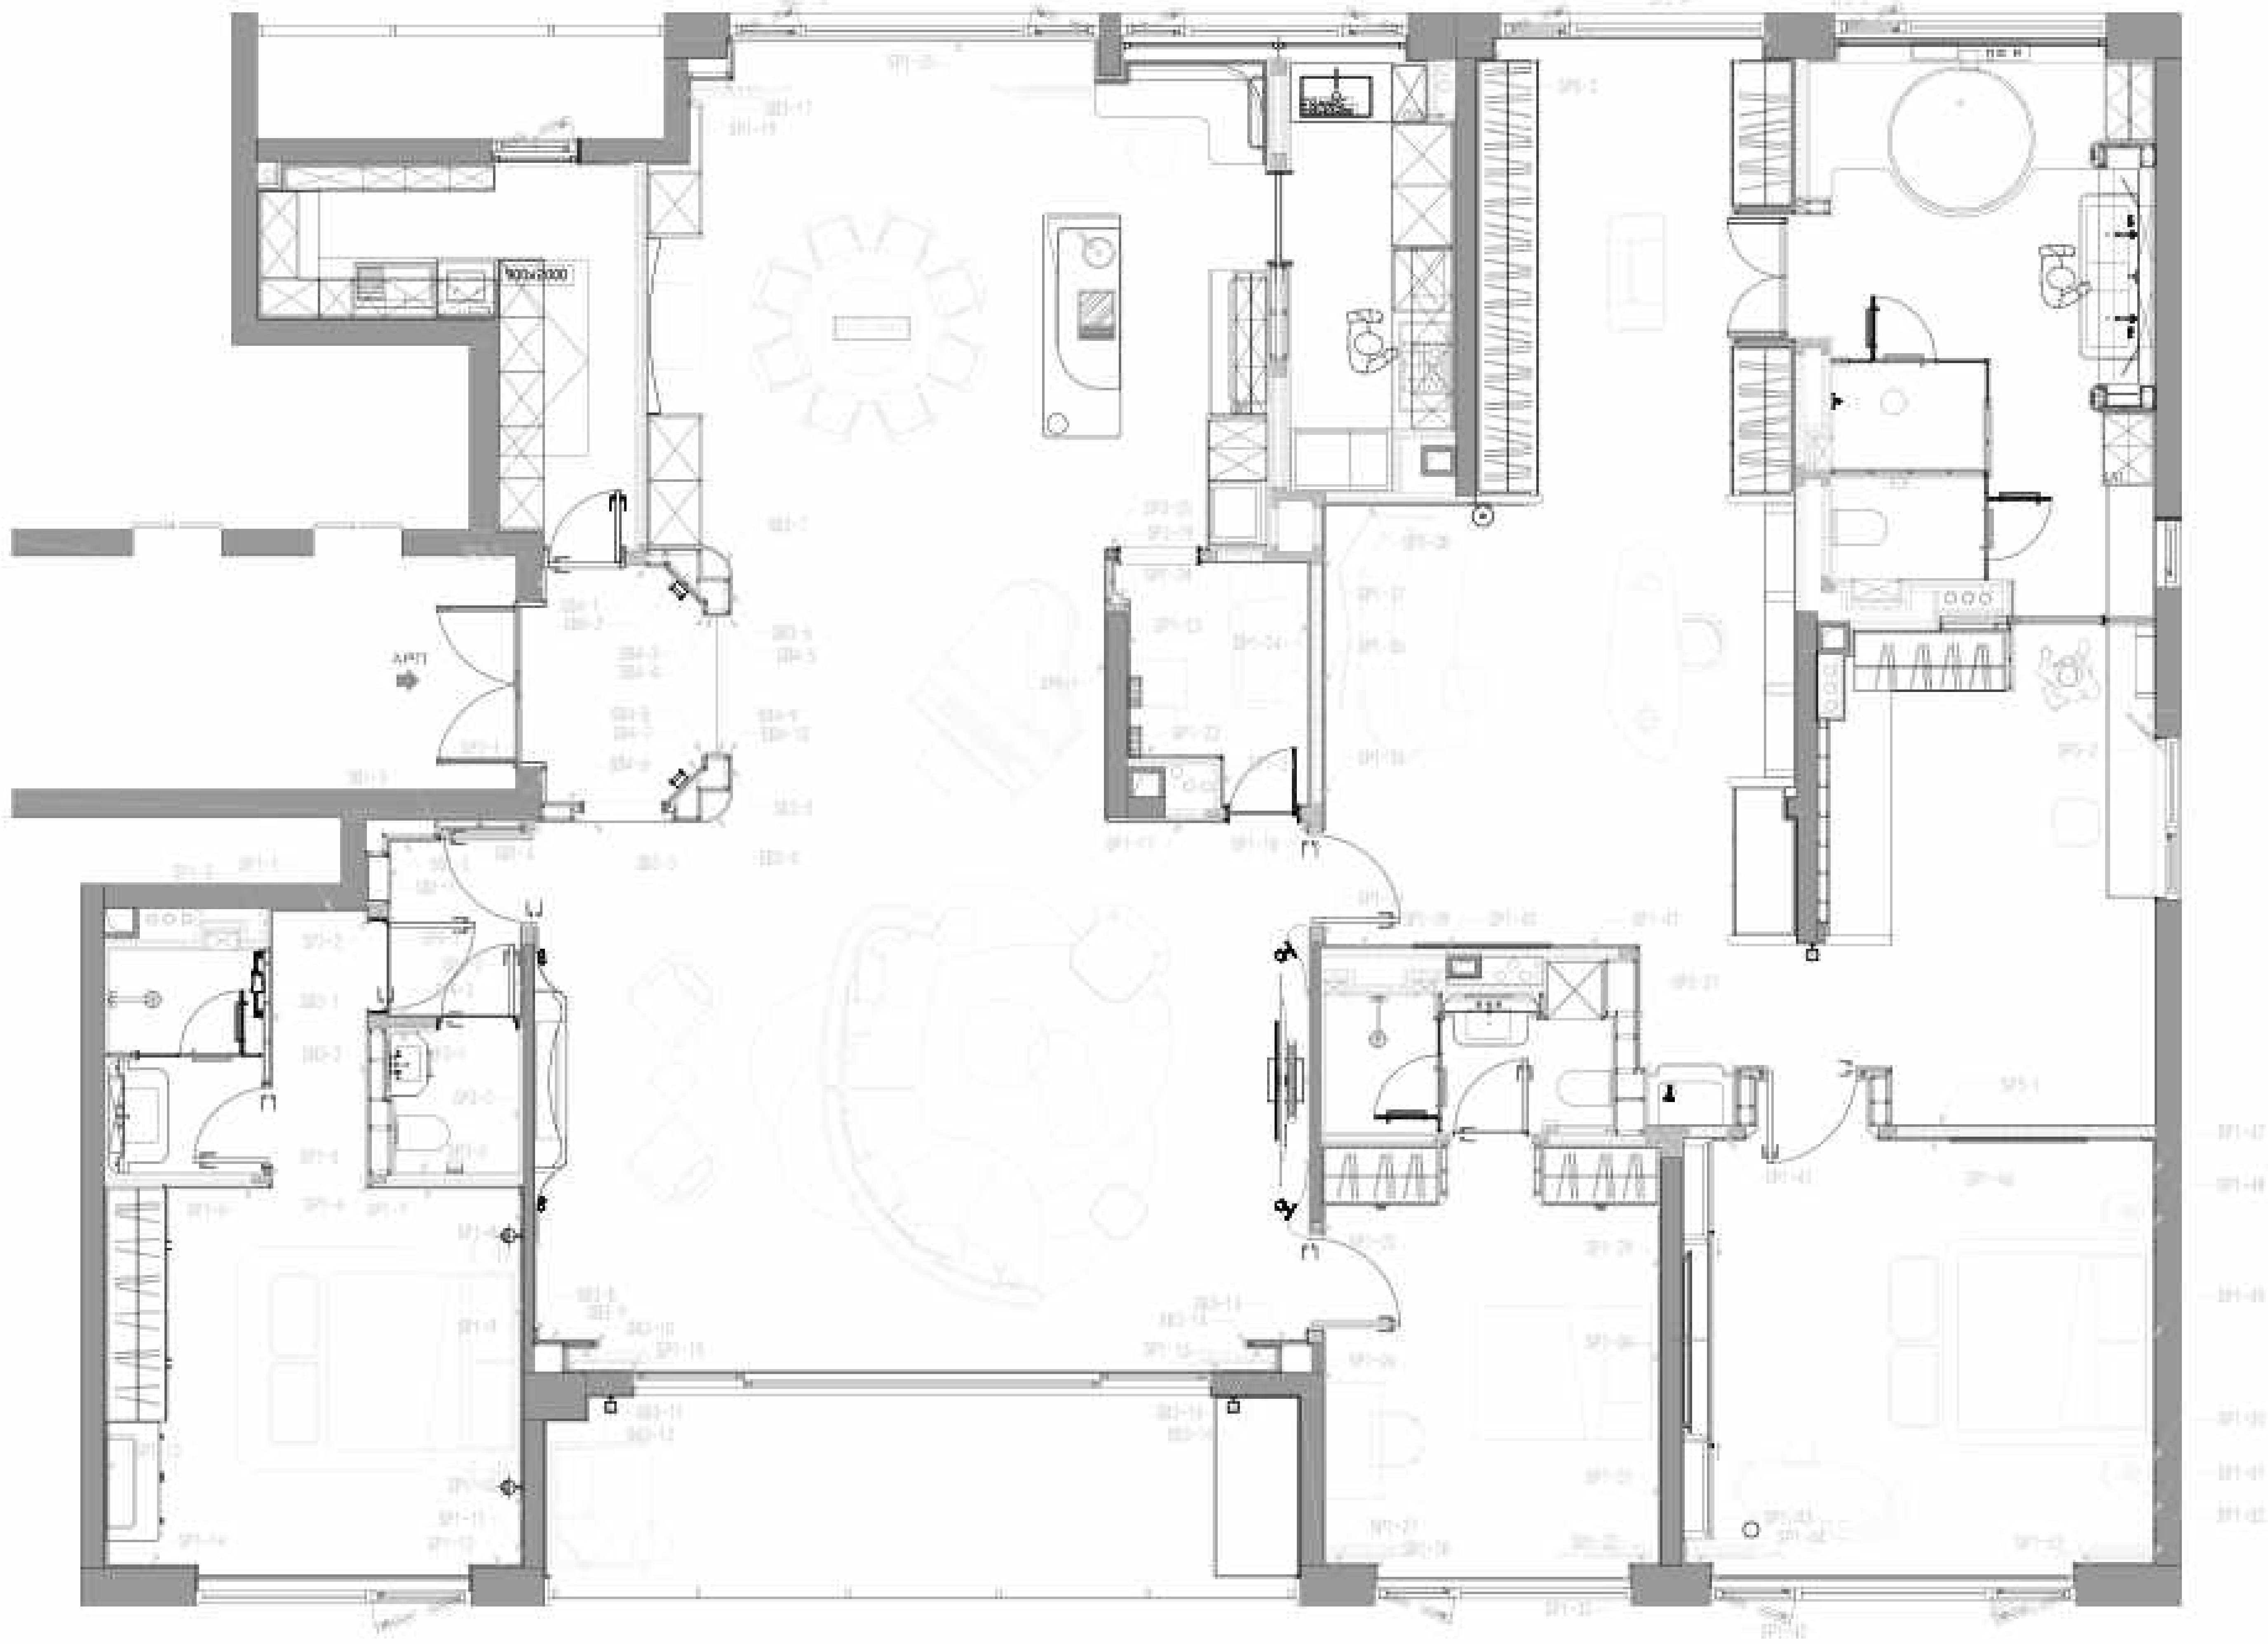
900x2000
APT1

图例 E
LEGEND E-踢脚铝型材

SP1
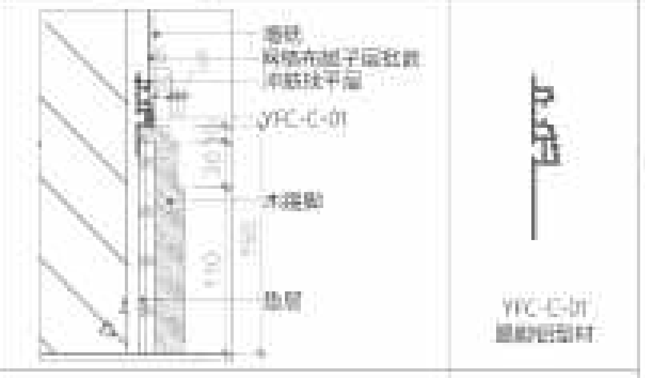
墙纸
网格布腻子层批嵌
冲筋找平层
YFC-C-01
木踢脚
垫层
YFC-C-01
踢脚铝型材

SP2
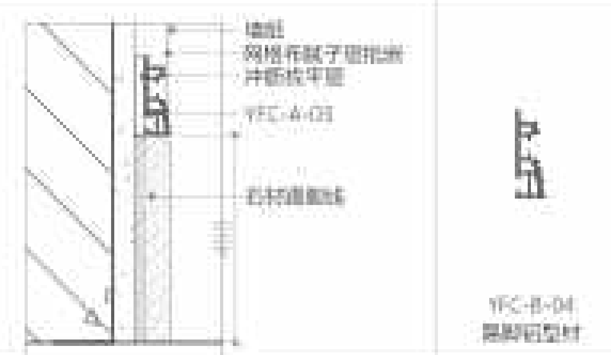
墙纸
网格布腻子层批嵌
冲筋找平层
YFC-A-03
石材踢脚线
YFC-B-04
踢脚铝型材

SP3
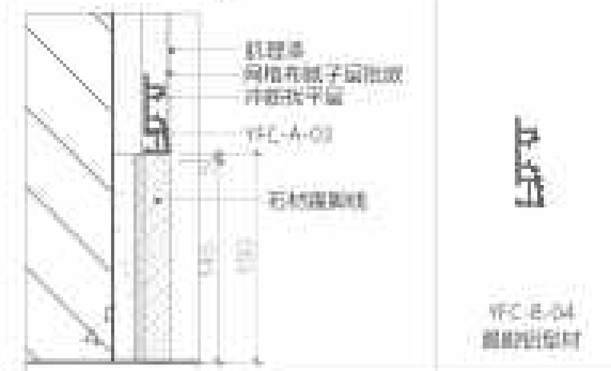
肌理漆
网格布腻子层批嵌
冲筋找平层
YFC-A-03
石材踢脚线
YFC-B-04
踢脚铝型材

SP4
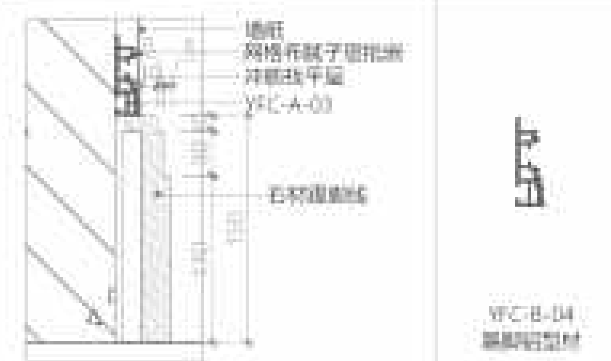
墙纸
网格布腻子层批嵌
冲筋找平层
YFC-A-03
石材踢脚线
YFC-B-04
踢脚铝型材

SP5
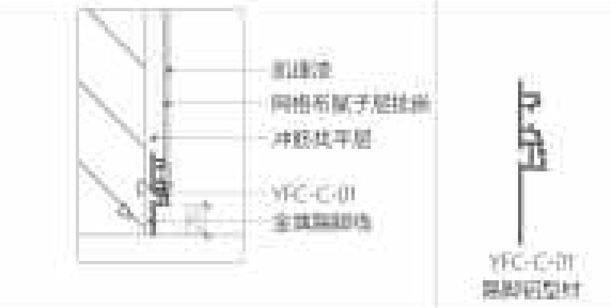
肌理漆
网格布腻子层批嵌
冲筋找平层
YFC-C-01
金属踢脚线
YFC-C-01
踢脚铝型材

SP6
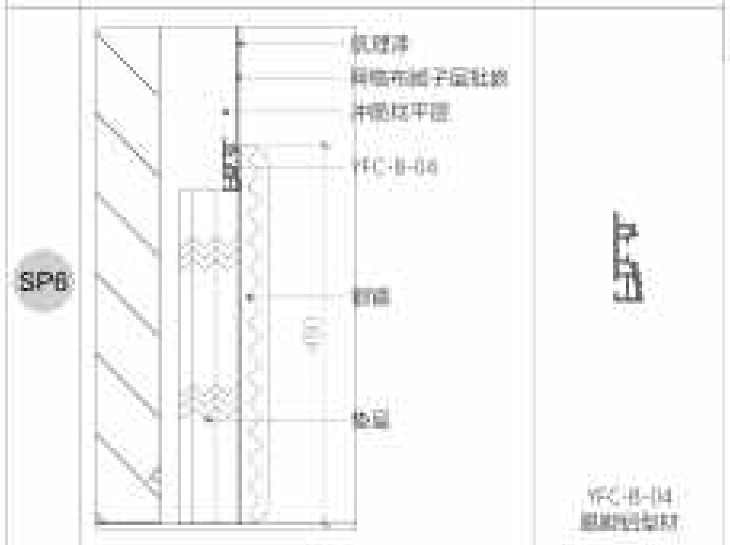
肌理漆
网格布腻子层批嵌
冲筋找平层
YFC-B-04
踢脚
垫层
YFC-B-04
踢脚铝型材

SB1
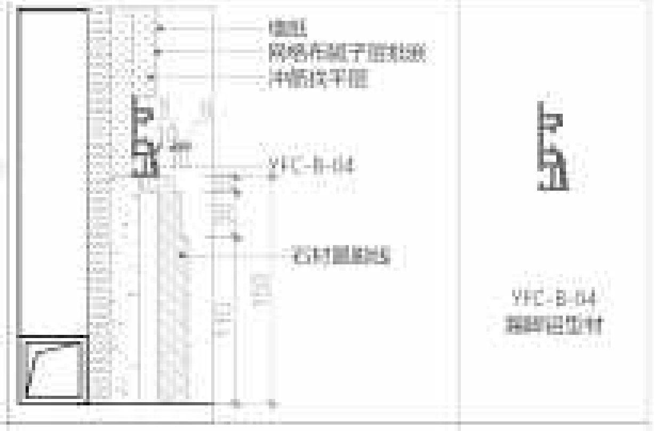
墙纸
网格布腻子层批嵌
冲筋找平层
YFC-B-04
石材踢脚线
YFC-B-04
踢脚铝型材

SB2
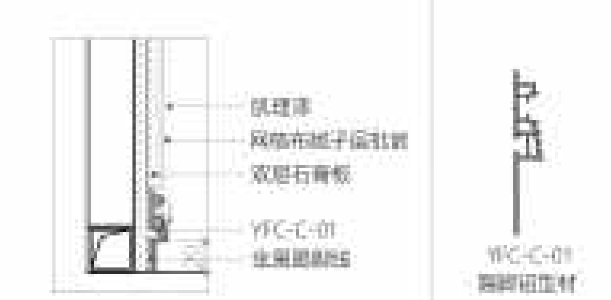
肌理漆
网格布腻子层批嵌
双层石膏板
YFC-C-01
金属踢脚线
YFC-C-01
踢脚铝型材

SB3
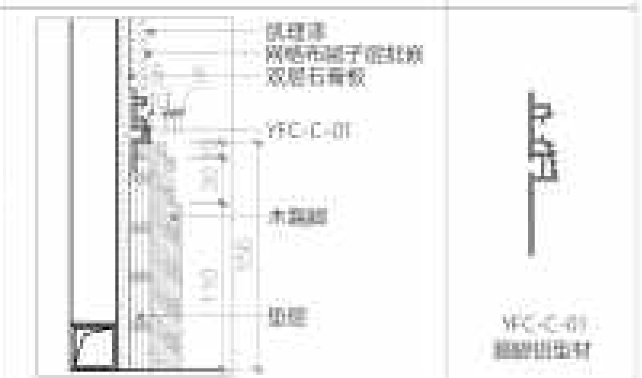
肌理漆
网格布腻子层批嵌
双层石膏板
YFC-C-01
木踢脚
垫层
YFC-C-01
踢脚铝型材

SB4
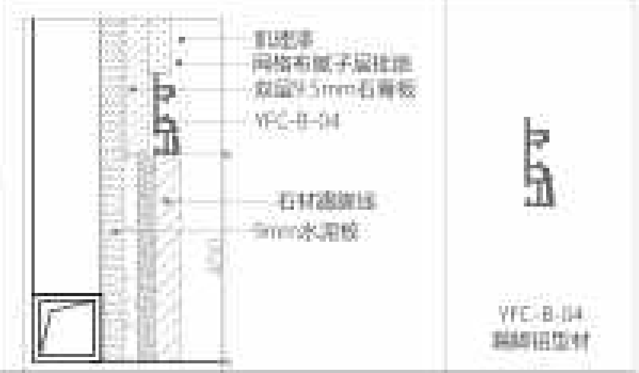
肌理漆
网格布腻子层批嵌
双层9.5mm石膏板
YFC-B-04
石材踢脚线
9mm水泥板
YFC-B-04
踢脚铝型材

SB5
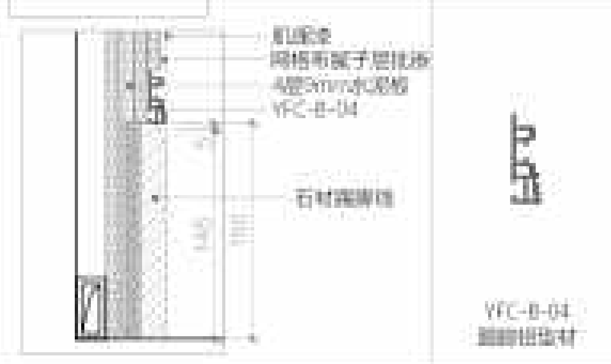
肌理漆
网格布腻子层批嵌
4层9mm水泥板
YFC-B-04
石材踢脚线
YFC-B-04
踢脚铝型材

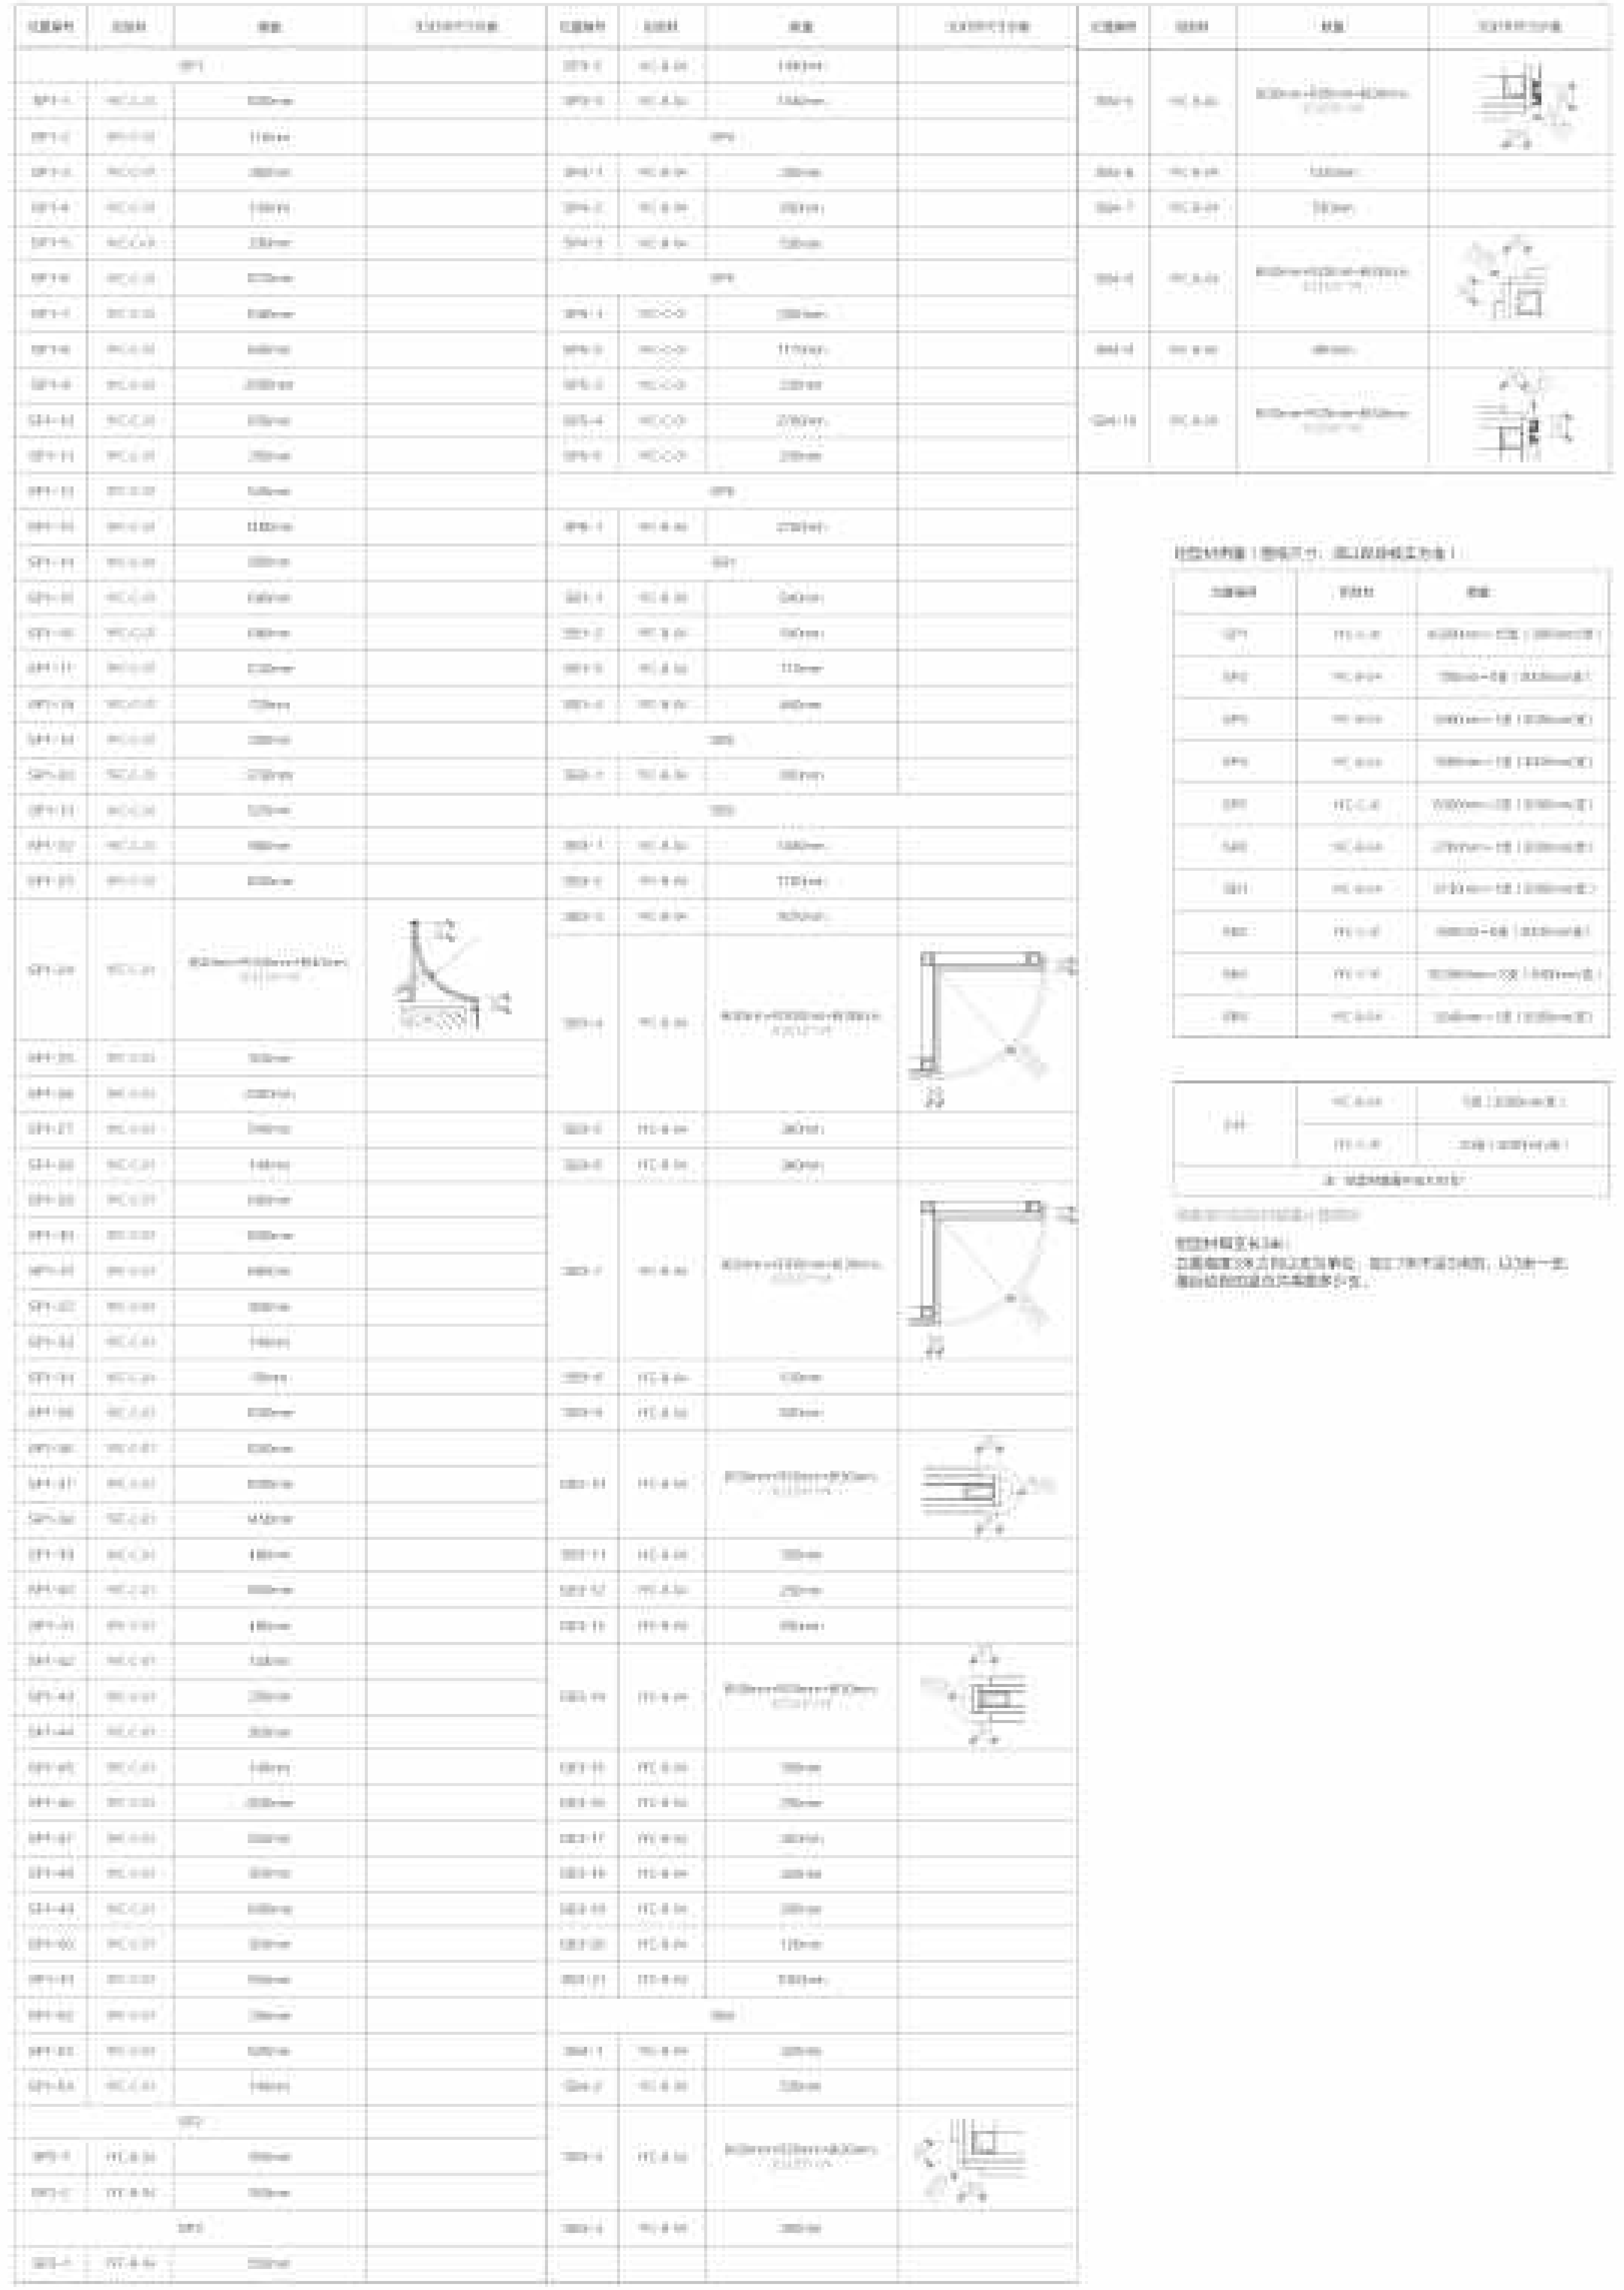

图纸编号 Drawing No.	图纸名称 Drawing Name	比例 Scale	项目 Project	项目编号 Project No.	注释 Notes	日期 Date	签章
AP-02	**踢脚铝型材分析平面图**	1:60 @A2	**华岸府**	© 2026	1. 本图纸尺寸如与现场尺寸有误，请施工人员与项目负责人联系。 2. 施工前施工人员应认真查阅此图，如有不明确尺寸，按现场测量为准。 3. 本图纸必须经甲乙双方认可并签字方可作为施工依据。	2026.03.02 修订 Revisions ⚠	

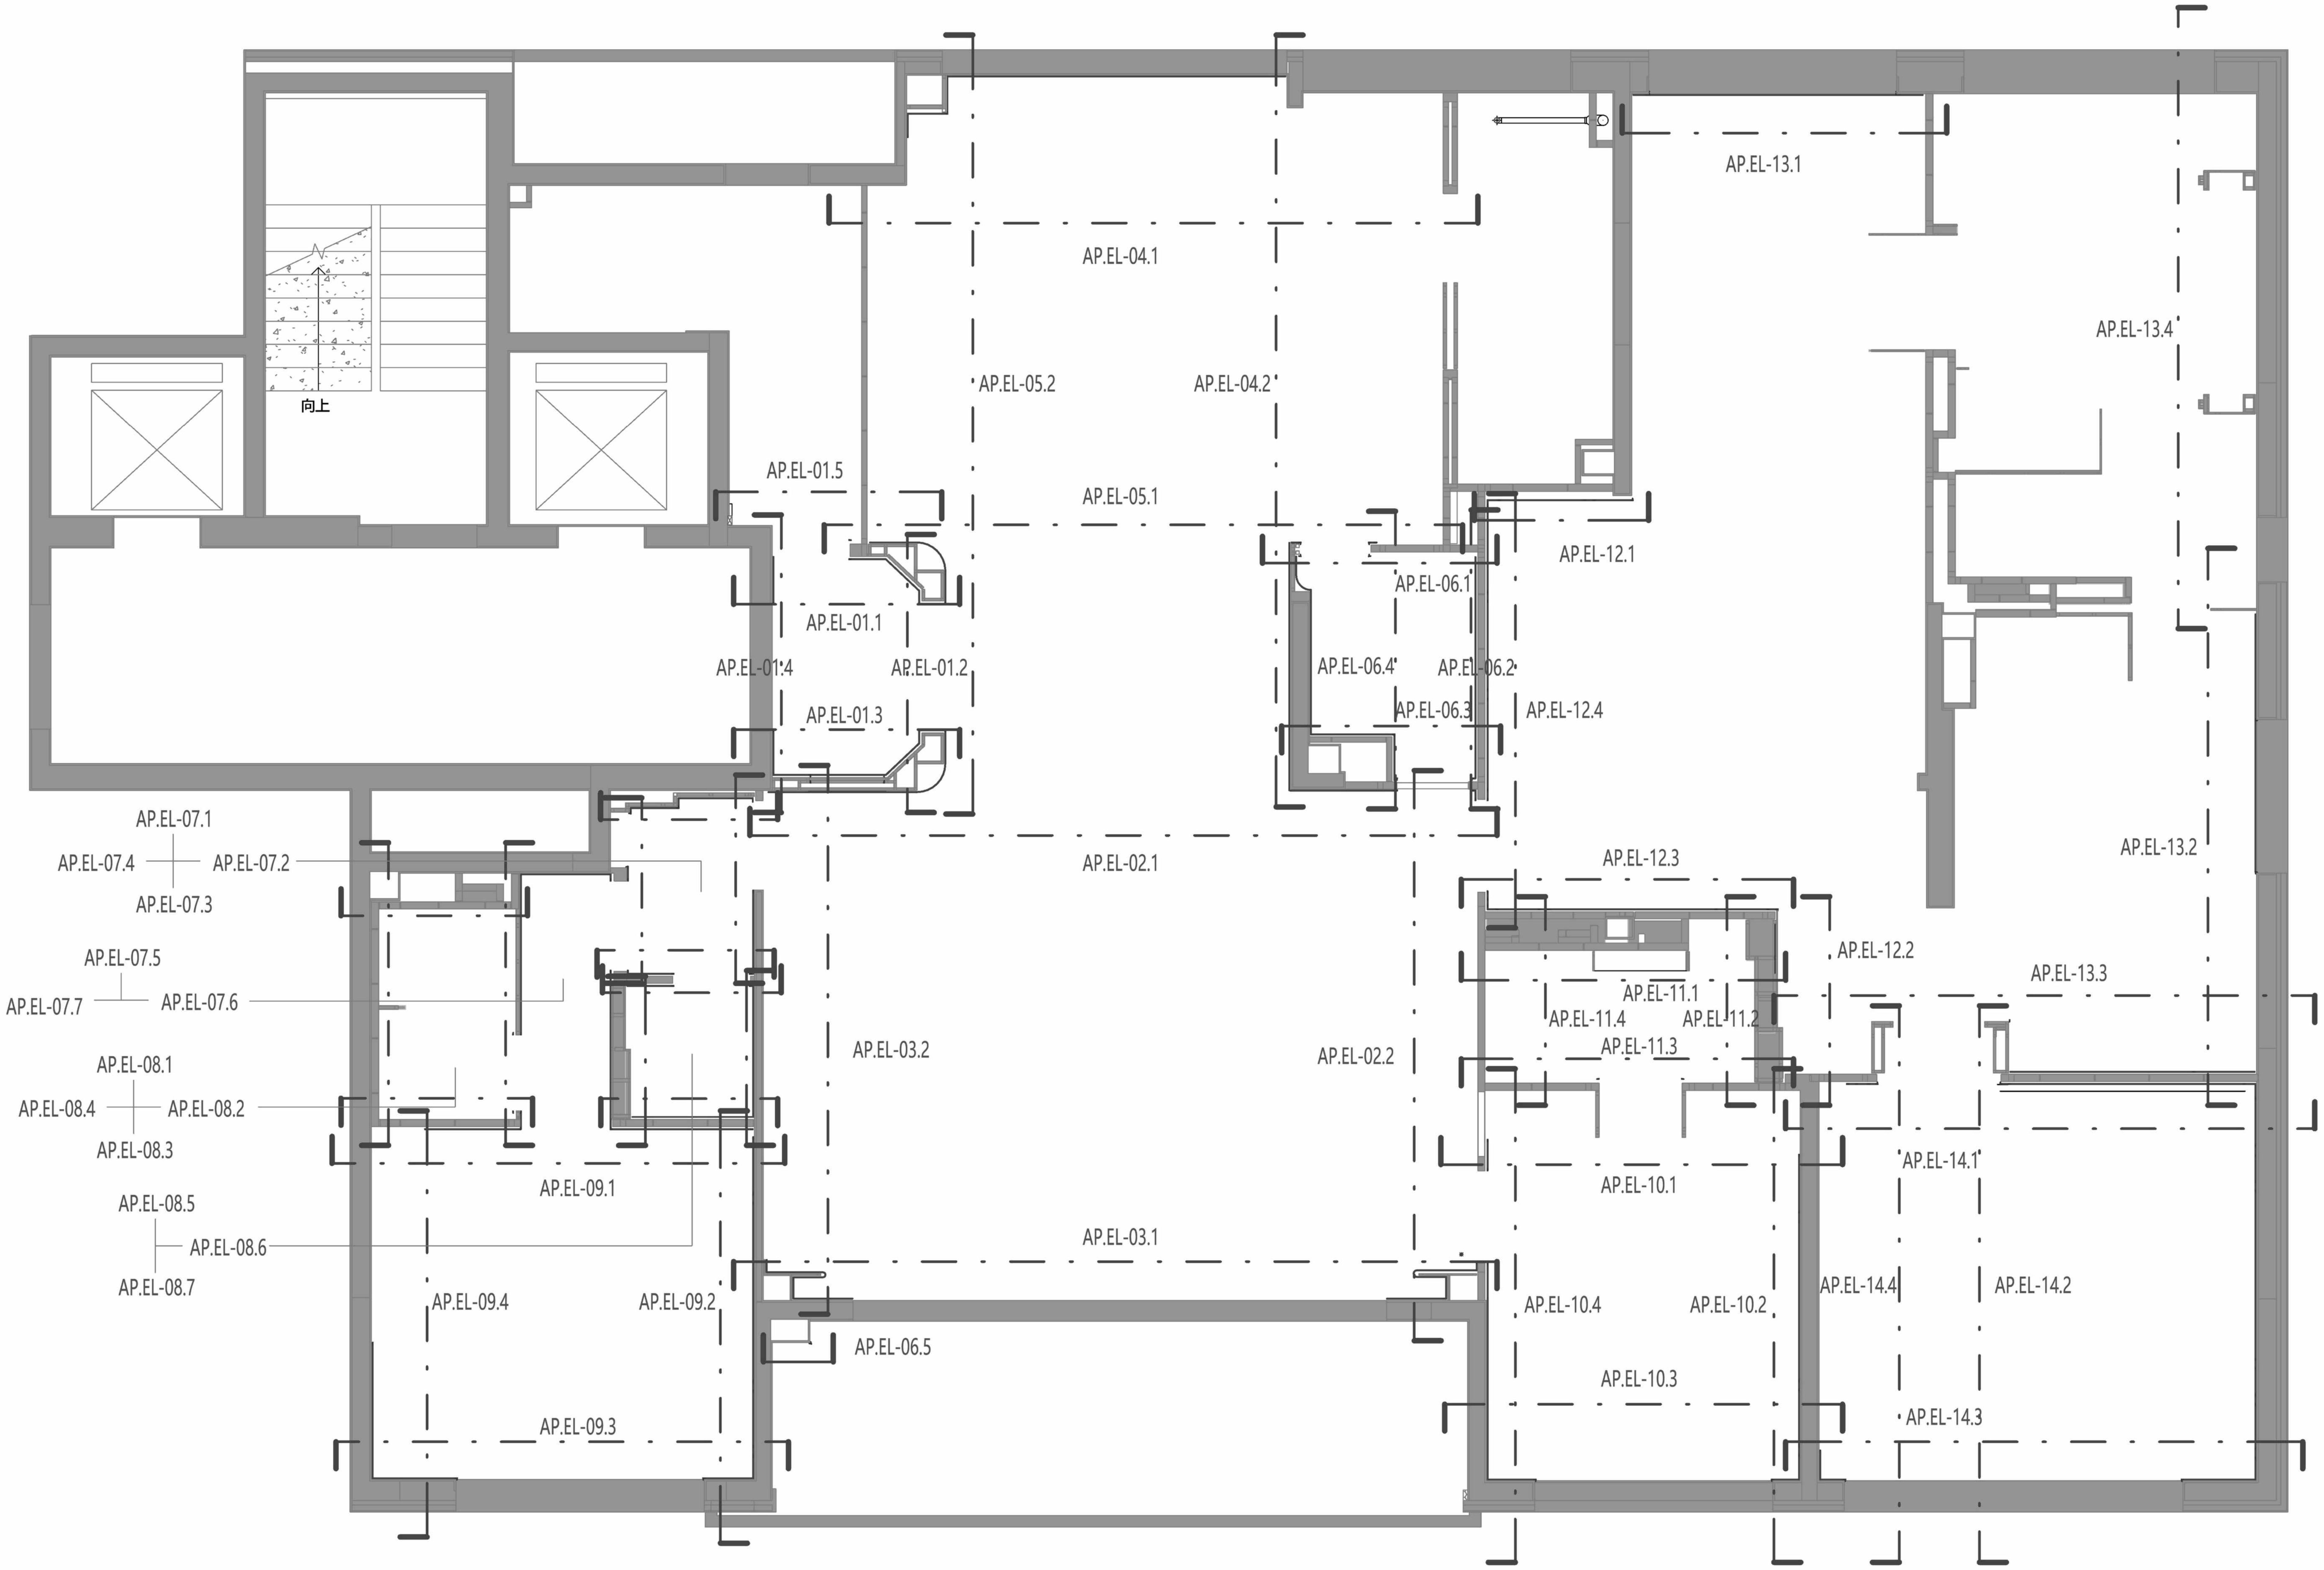
向上
AP.EL-13.1
AP.EL-04.1
AP.EL-13.4
AP.EL-05.2
AP.EL-04.2
AP.EL-01.5
AP.EL-05.1
AP.EL-12.1
AP.EL-06.1
AP.EL-01.1
AP.EL-01.4
AP.EL-01.2
AP.EL-06.4
AP.EL-06.2
AP.EL-06.3
AP.EL-12.4
AP.EL-01.3
AP.EL-07.1
AP.EL-07.4
AP.EL-07.2
AP.EL-07.3
AP.EL-02.1
AP.EL-12.3
AP.EL-13.2
AP.EL-07.5
AP.EL-07.7
AP.EL-07.6
AP.EL-12.2
AP.EL-13.3
AP.EL-11.1
AP.EL-11.4
AP.EL-11.2
AP.EL-11.3
AP.EL-03.2
AP.EL-02.2
AP.EL-08.1
AP.EL-08.4
AP.EL-08.2
AP.EL-08.3
AP.EL-14.1
AP.EL-09.1
AP.EL-10.1
AP.EL-08.5
AP.EL-08.6
AP.EL-08.7
AP.EL-03.1
AP.EL-14.4
AP.EL-14.2
AP.EL-09.4
AP.EL-09.2
AP.EL-10.4
AP.EL-10.2
AP.EL-06.5
AP.EL-10.3
AP.EL-14.3
AP.EL-09.3

1

墙面及踢脚铝型材立面索引图

Scale比例 1:60@A2

盖章

注释
Notes

1.本图纸如与现场尺寸有误，请施工人员与项目负责人联系。
2.施工前施工人员应认真查阅此图，如有不明确尺寸，按现场测量为准。
3.本图纸必须经甲乙双方认可并签字方可作为施工依据。

日期
Date 03/04/26

修订
Revision

△1

项目
Project
潮映华岸府3-801

比例
Scale 1:60@A2

墙面及踢脚铝型材立面索引图

图纸编号
Drawing No.
AP.EL-索引

项目编号
Project No.
©2025

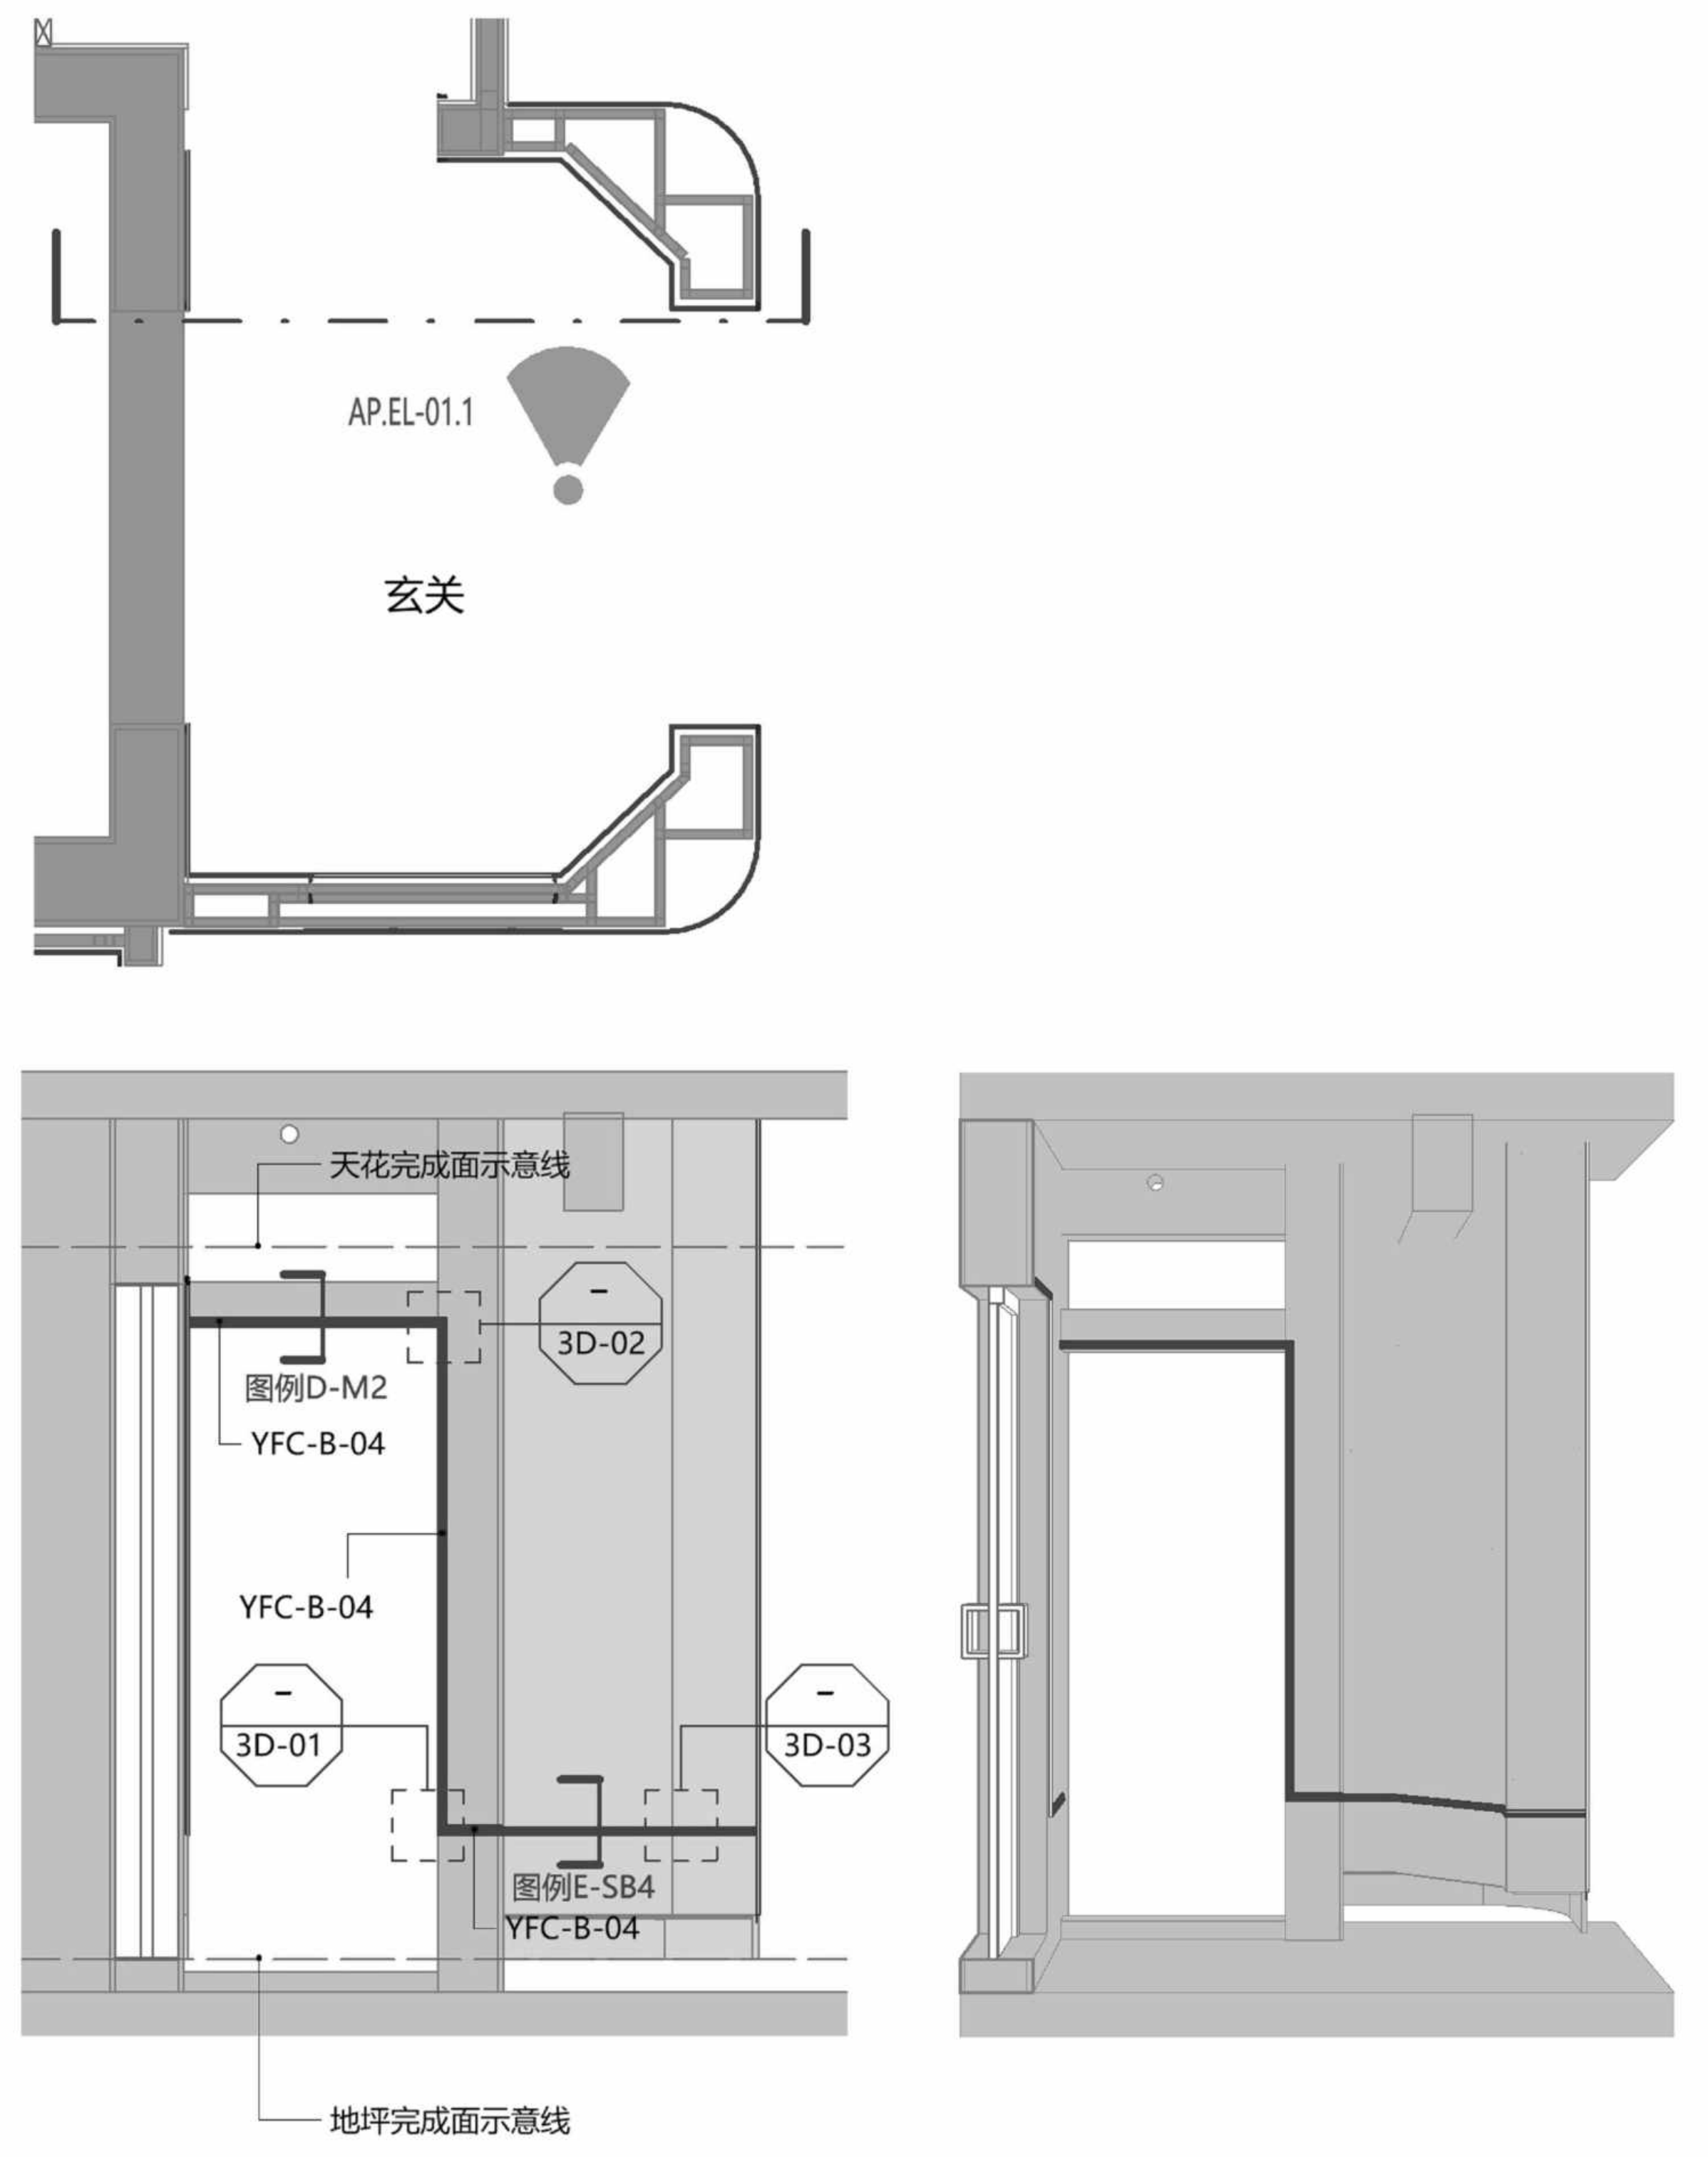
AP.EL-01.1
玄关
天花完成面示意线
图例D-M2
YFC-B-04
3D-02
YFC-B-04
3D-01
3D-03
图例E-SB4
YFC-B-04
地坪完成面示意线

1
玄关 墙面及踢脚铝型材立面图1
Scale比例 1 : 30@A2

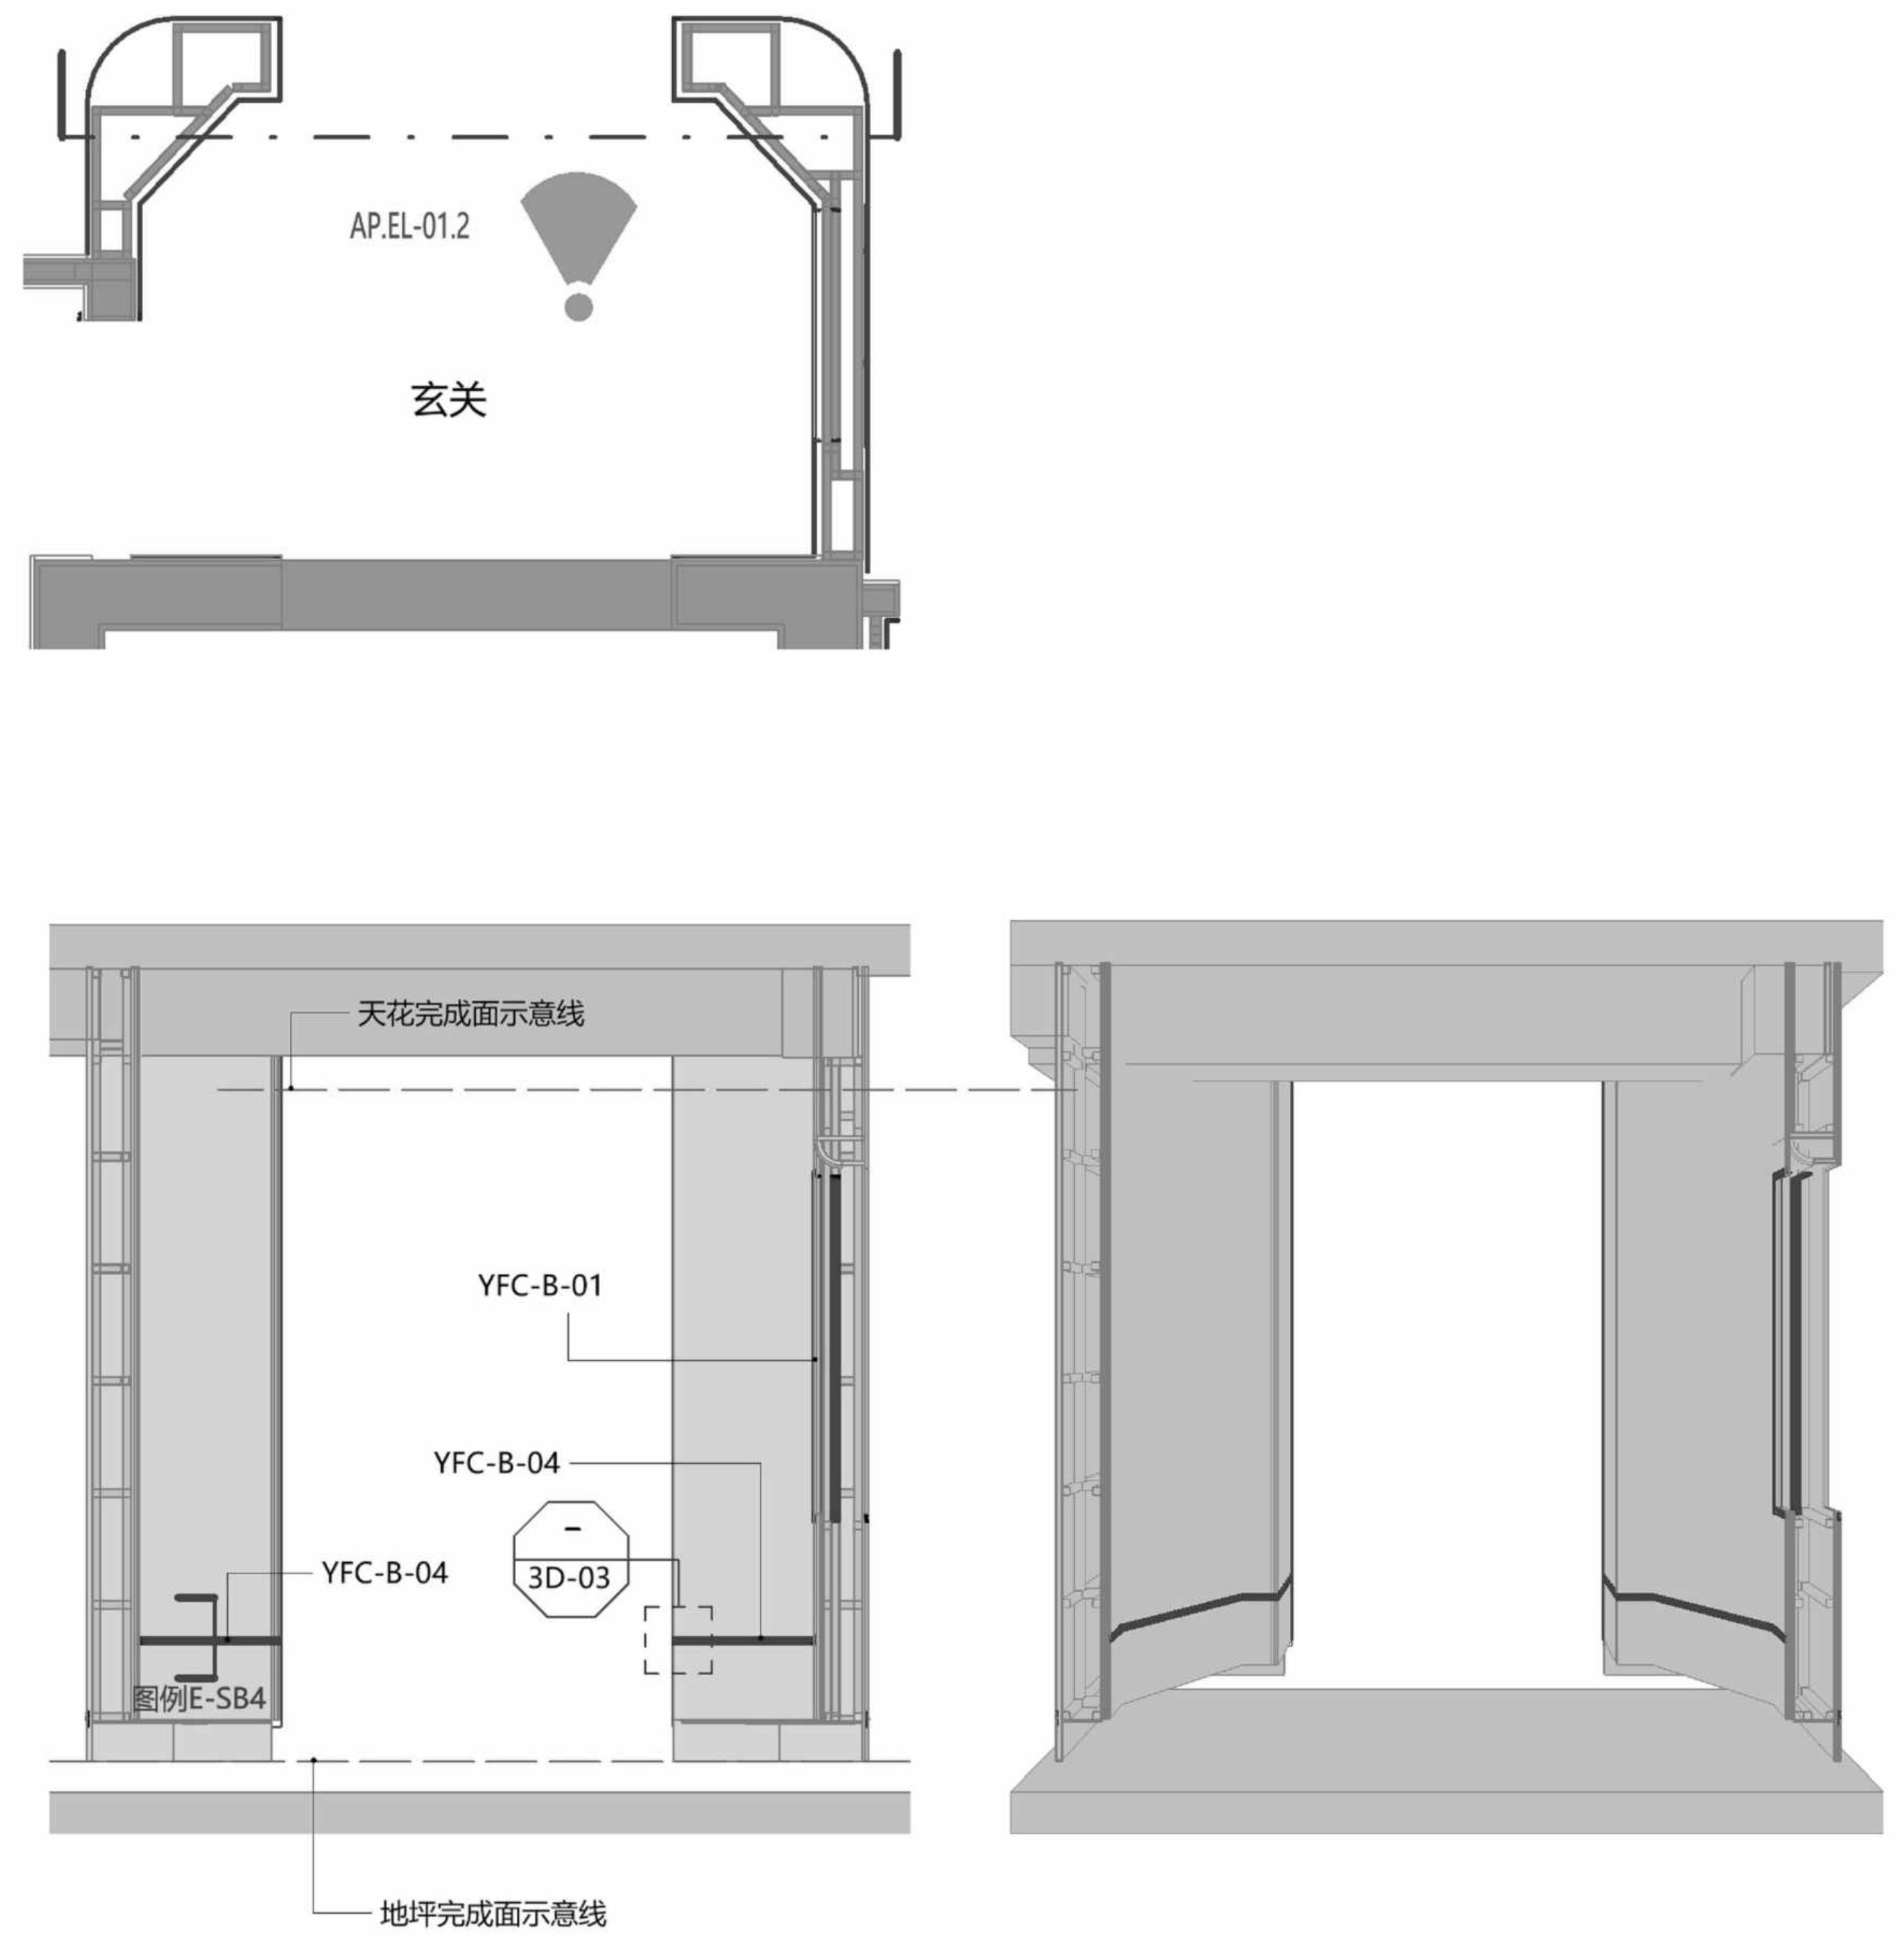
AP.EL-01.2
玄关
天花完成面示意线
YFC-B-01
YFC-B-04
YFC-B-04
3D-03
图例E-SB4
地坪完成面示意线

2
玄关 墙面及踢脚铝型材立面图2
Scale比例 1 : 30@A2

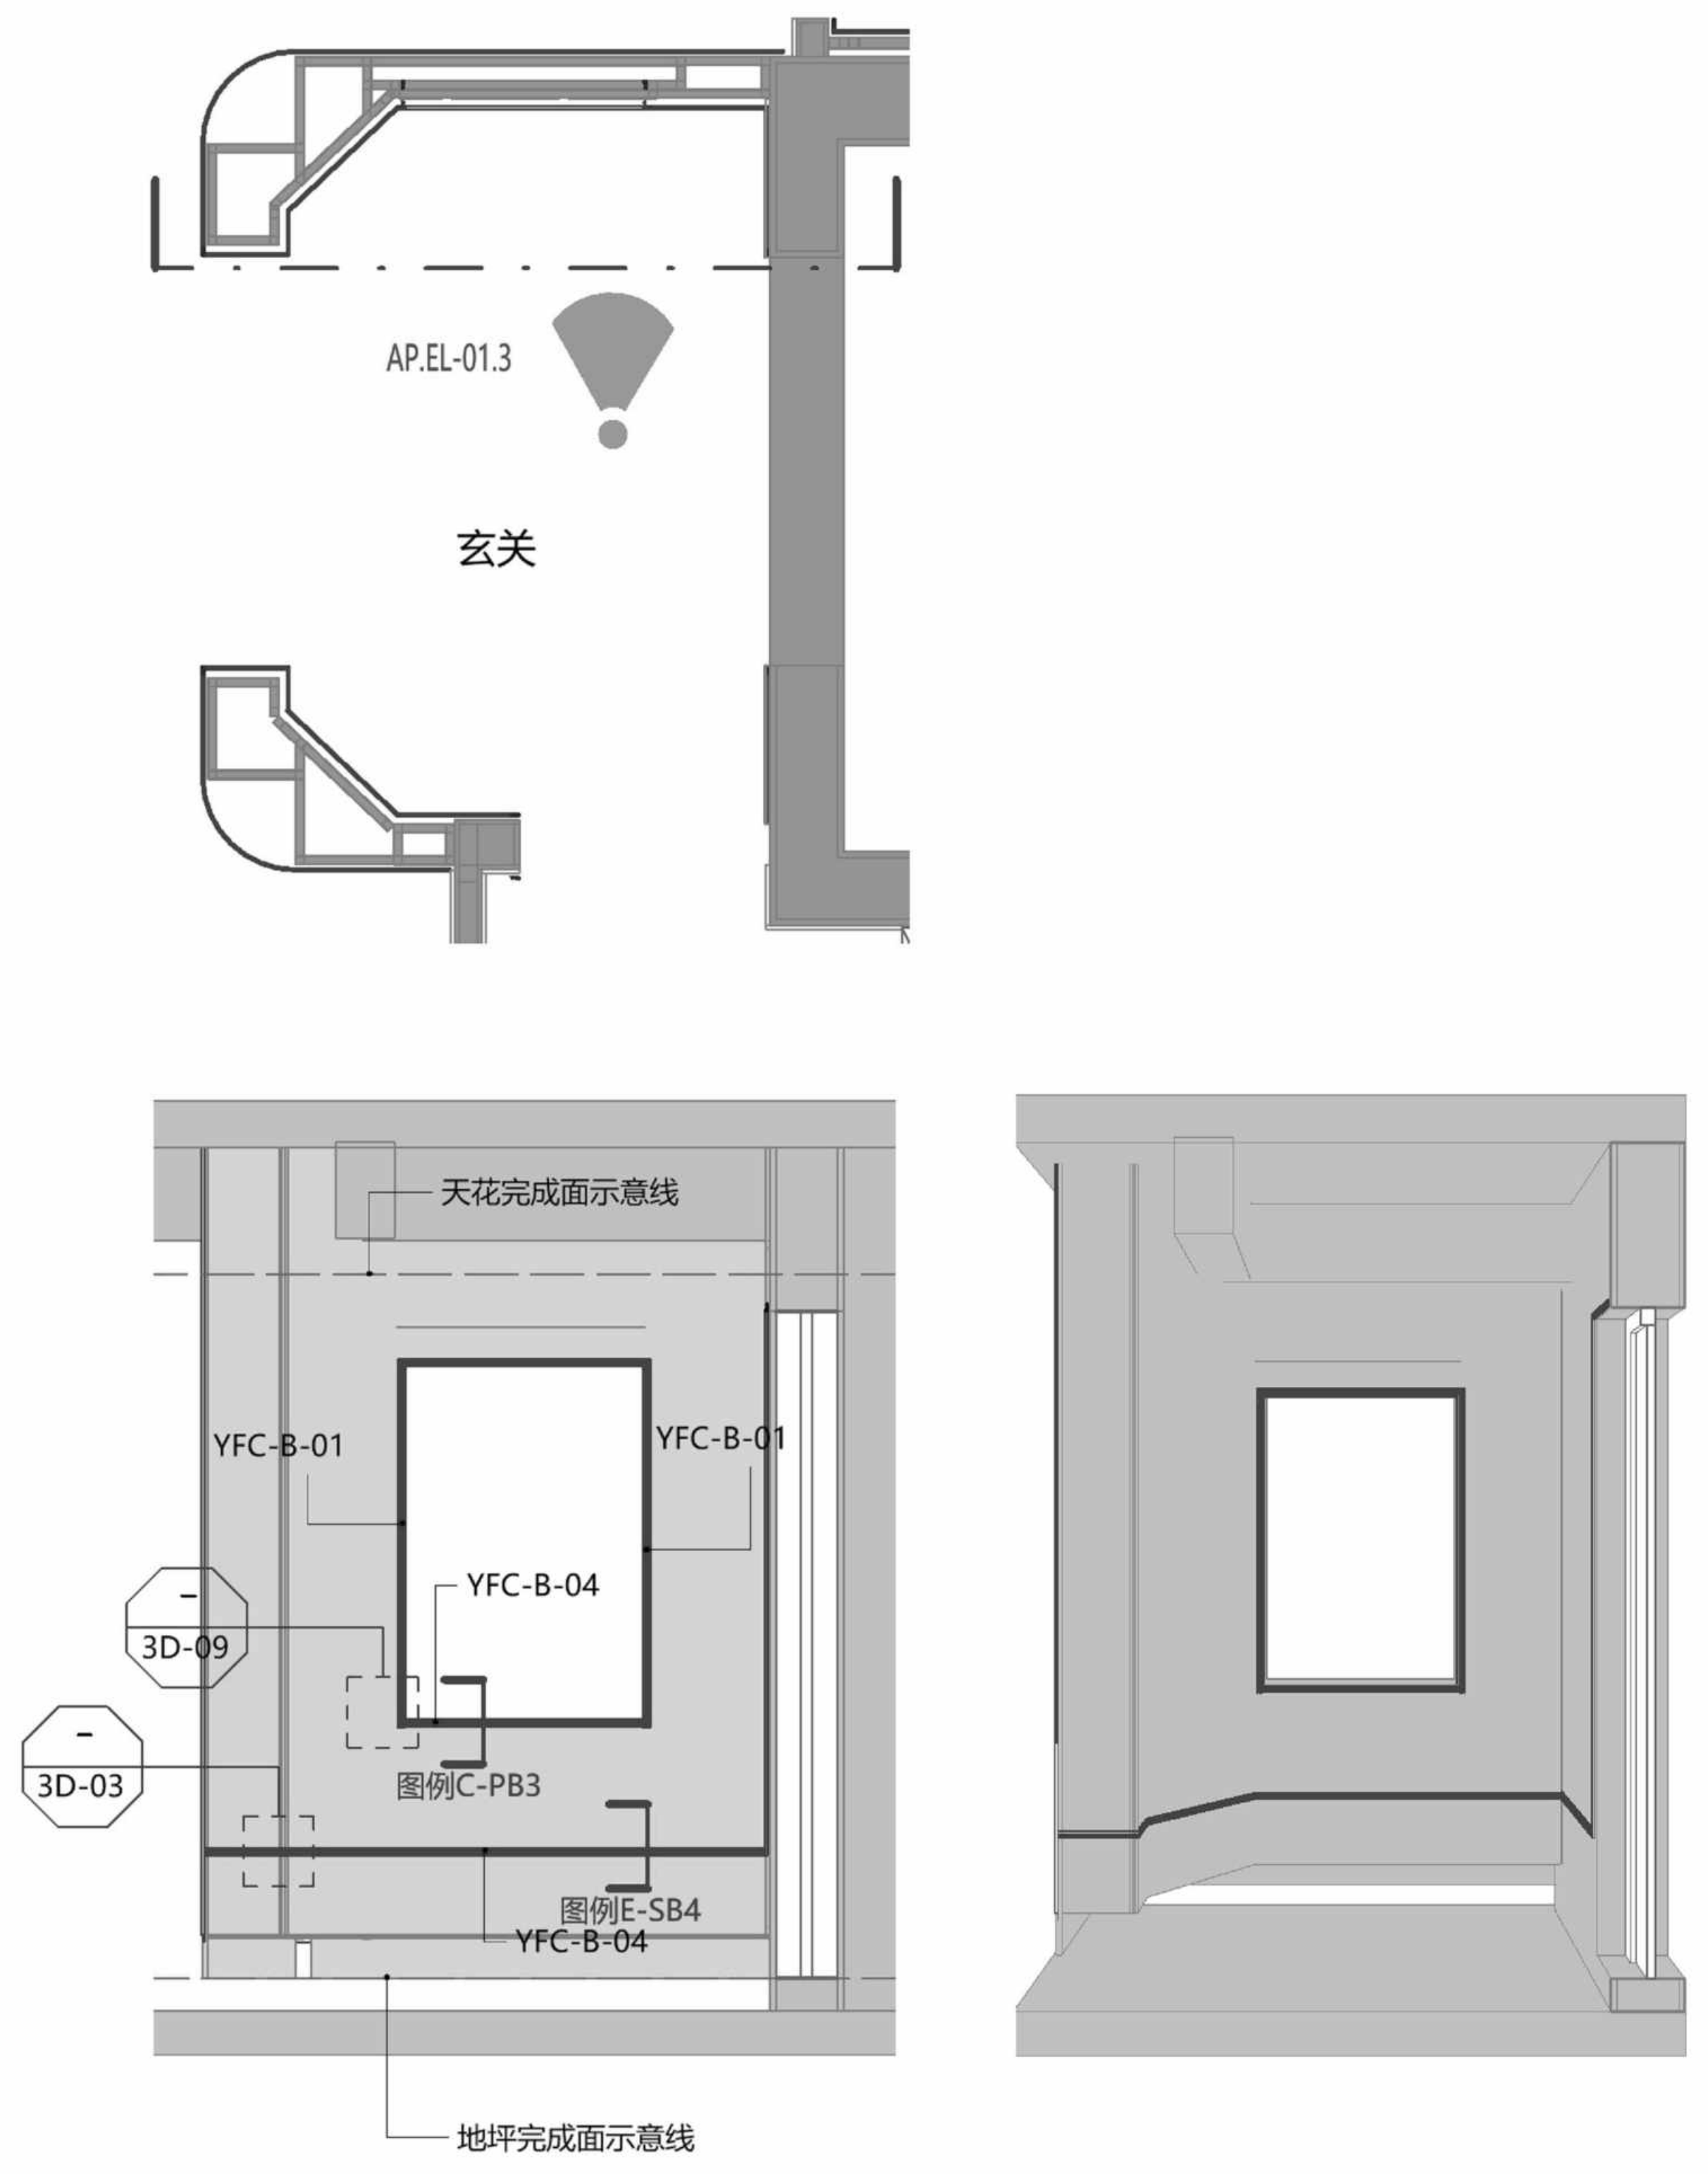
AP.EL-01.3
玄关
天花完成面示意线
YFC-B-01
YFC-B-01
YFC-B-04
3D-09
3D-03
图例C-PB3
图例E-SB4
YFC-B-04
地坪完成面示意线

3
玄关 墙面及踢脚铝型材立面图3
Scale比例 1 : 30@A2

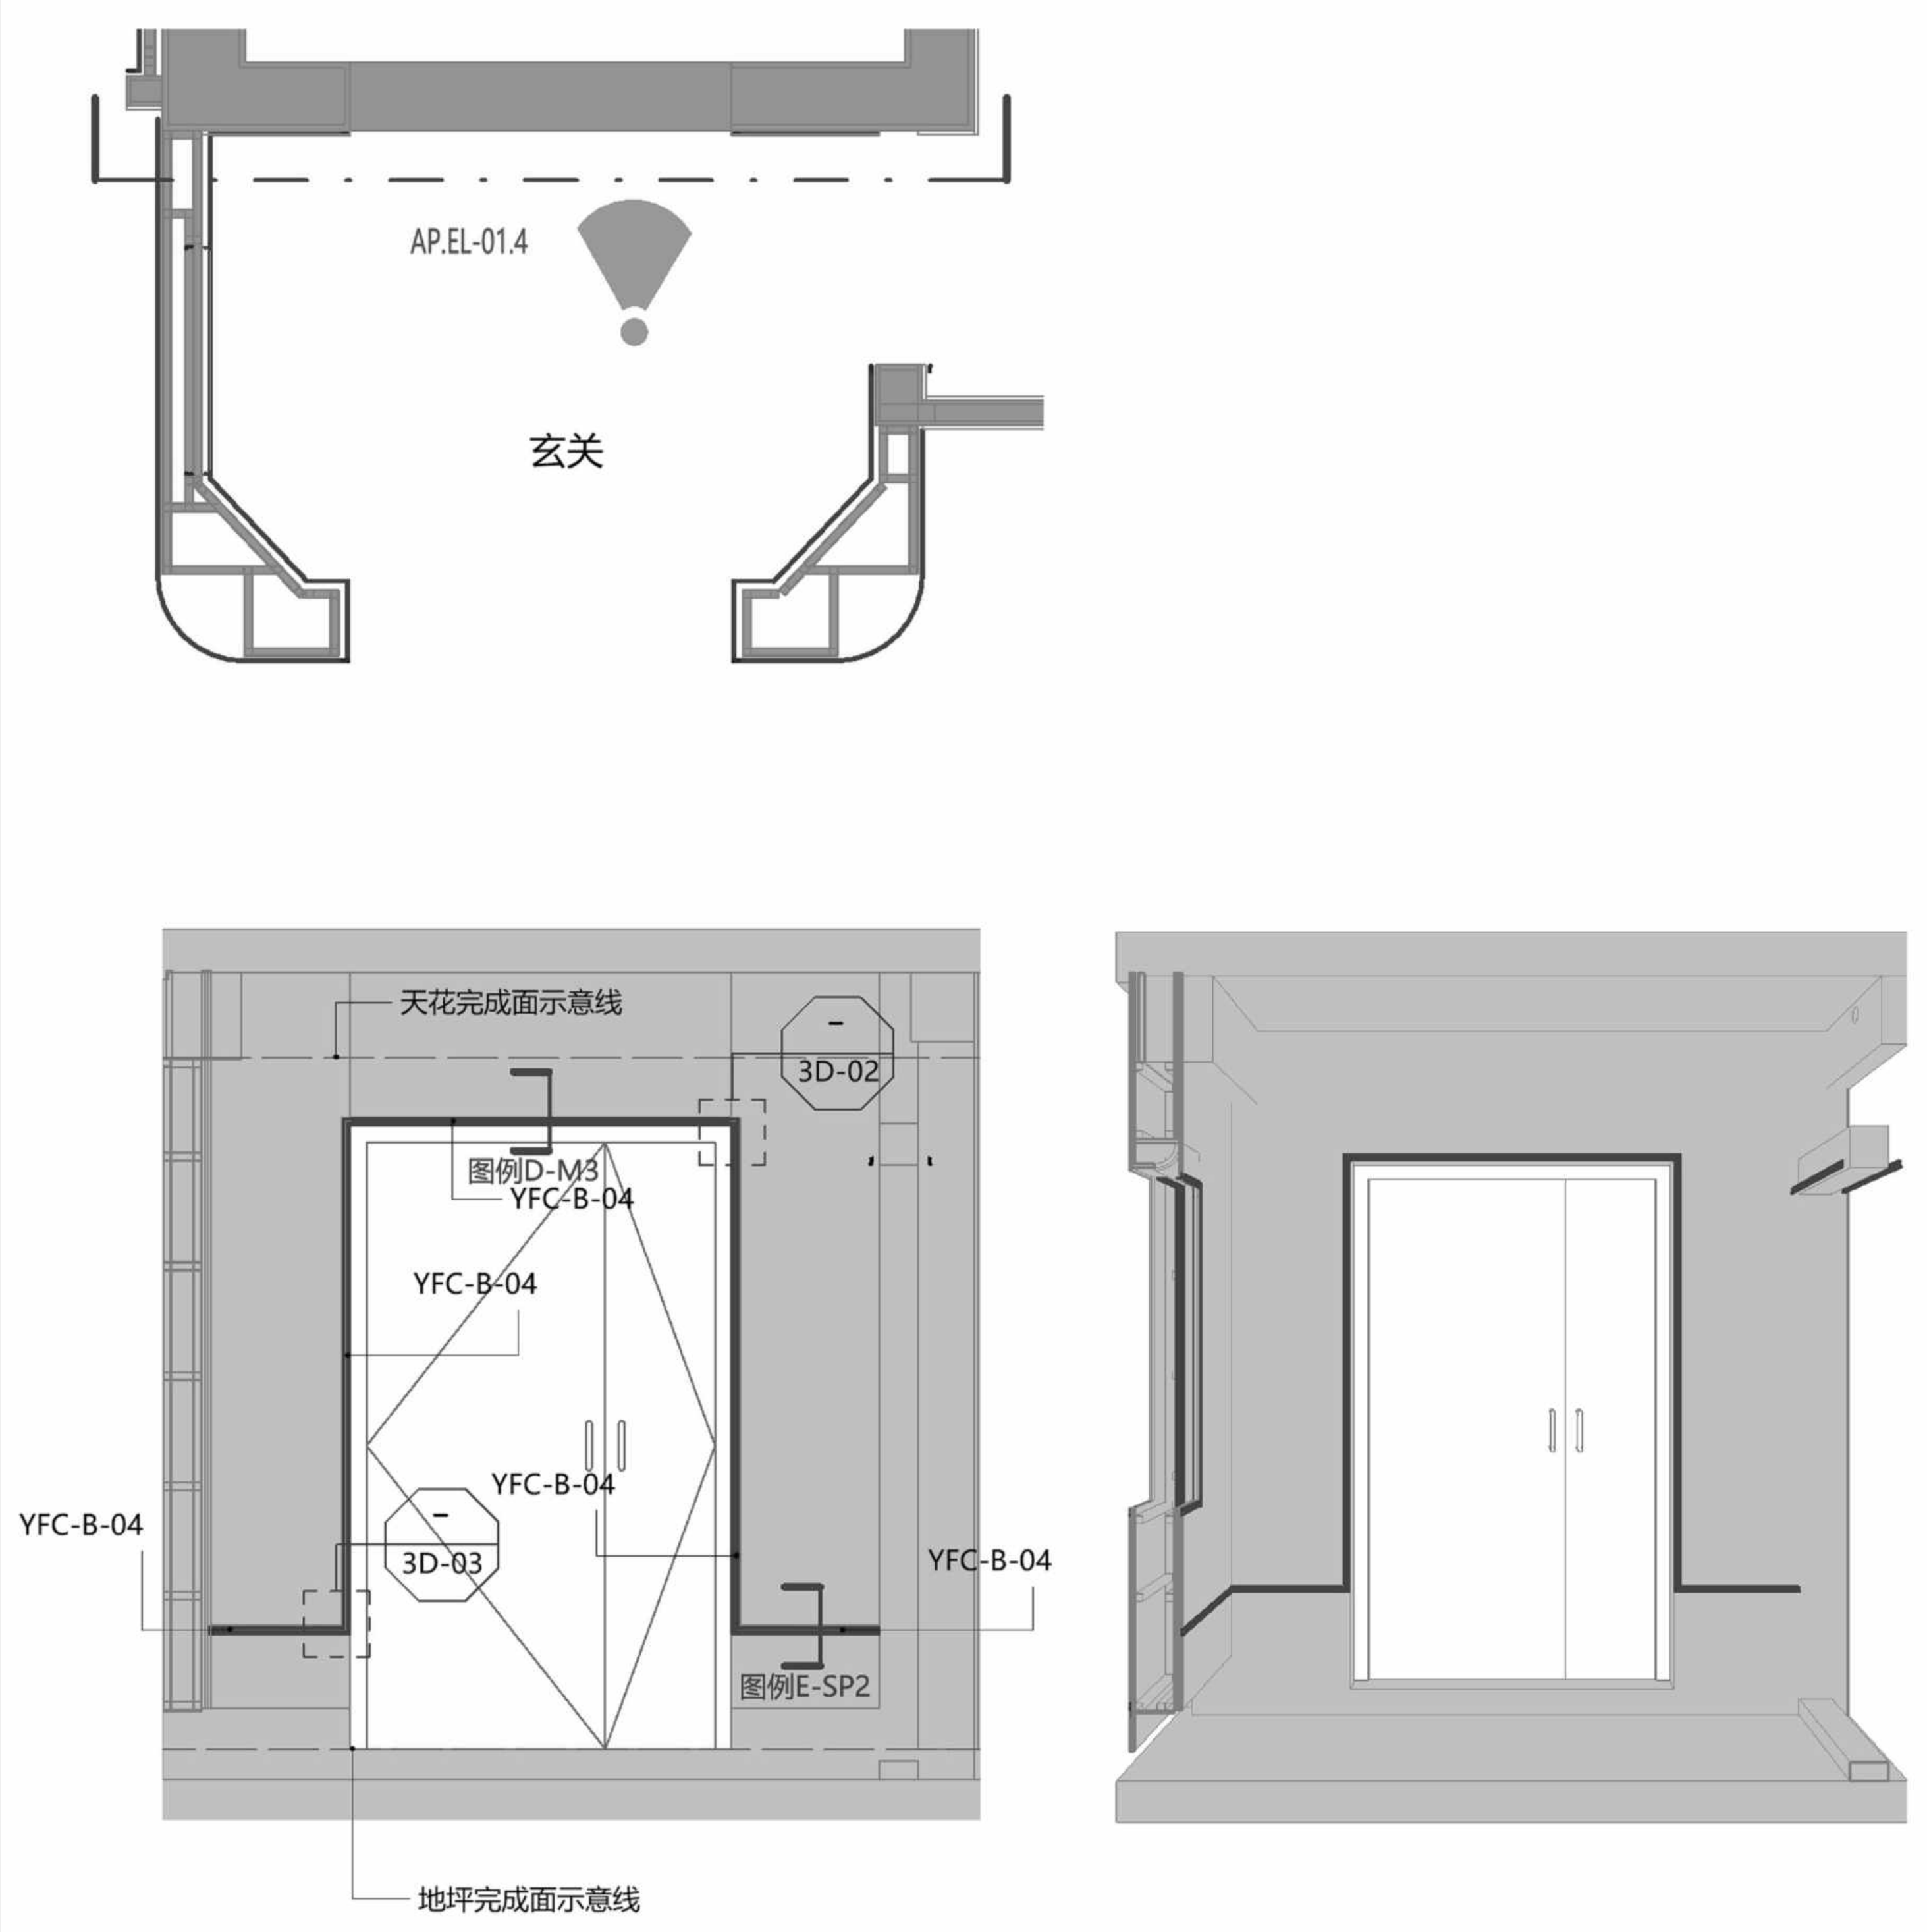
AP.EL-01.4
玄关
天花完成面示意线
3D-02
图例D-M3
YFC-B-04
YFC-B-04
YFC-B-04
YFC-B-04
3D-03
图例E-SP2
YFC-B-04
地坪完成面示意线

4
玄关 墙面及踢脚铝型材立面图4
Scale比例 1 : 30@A2

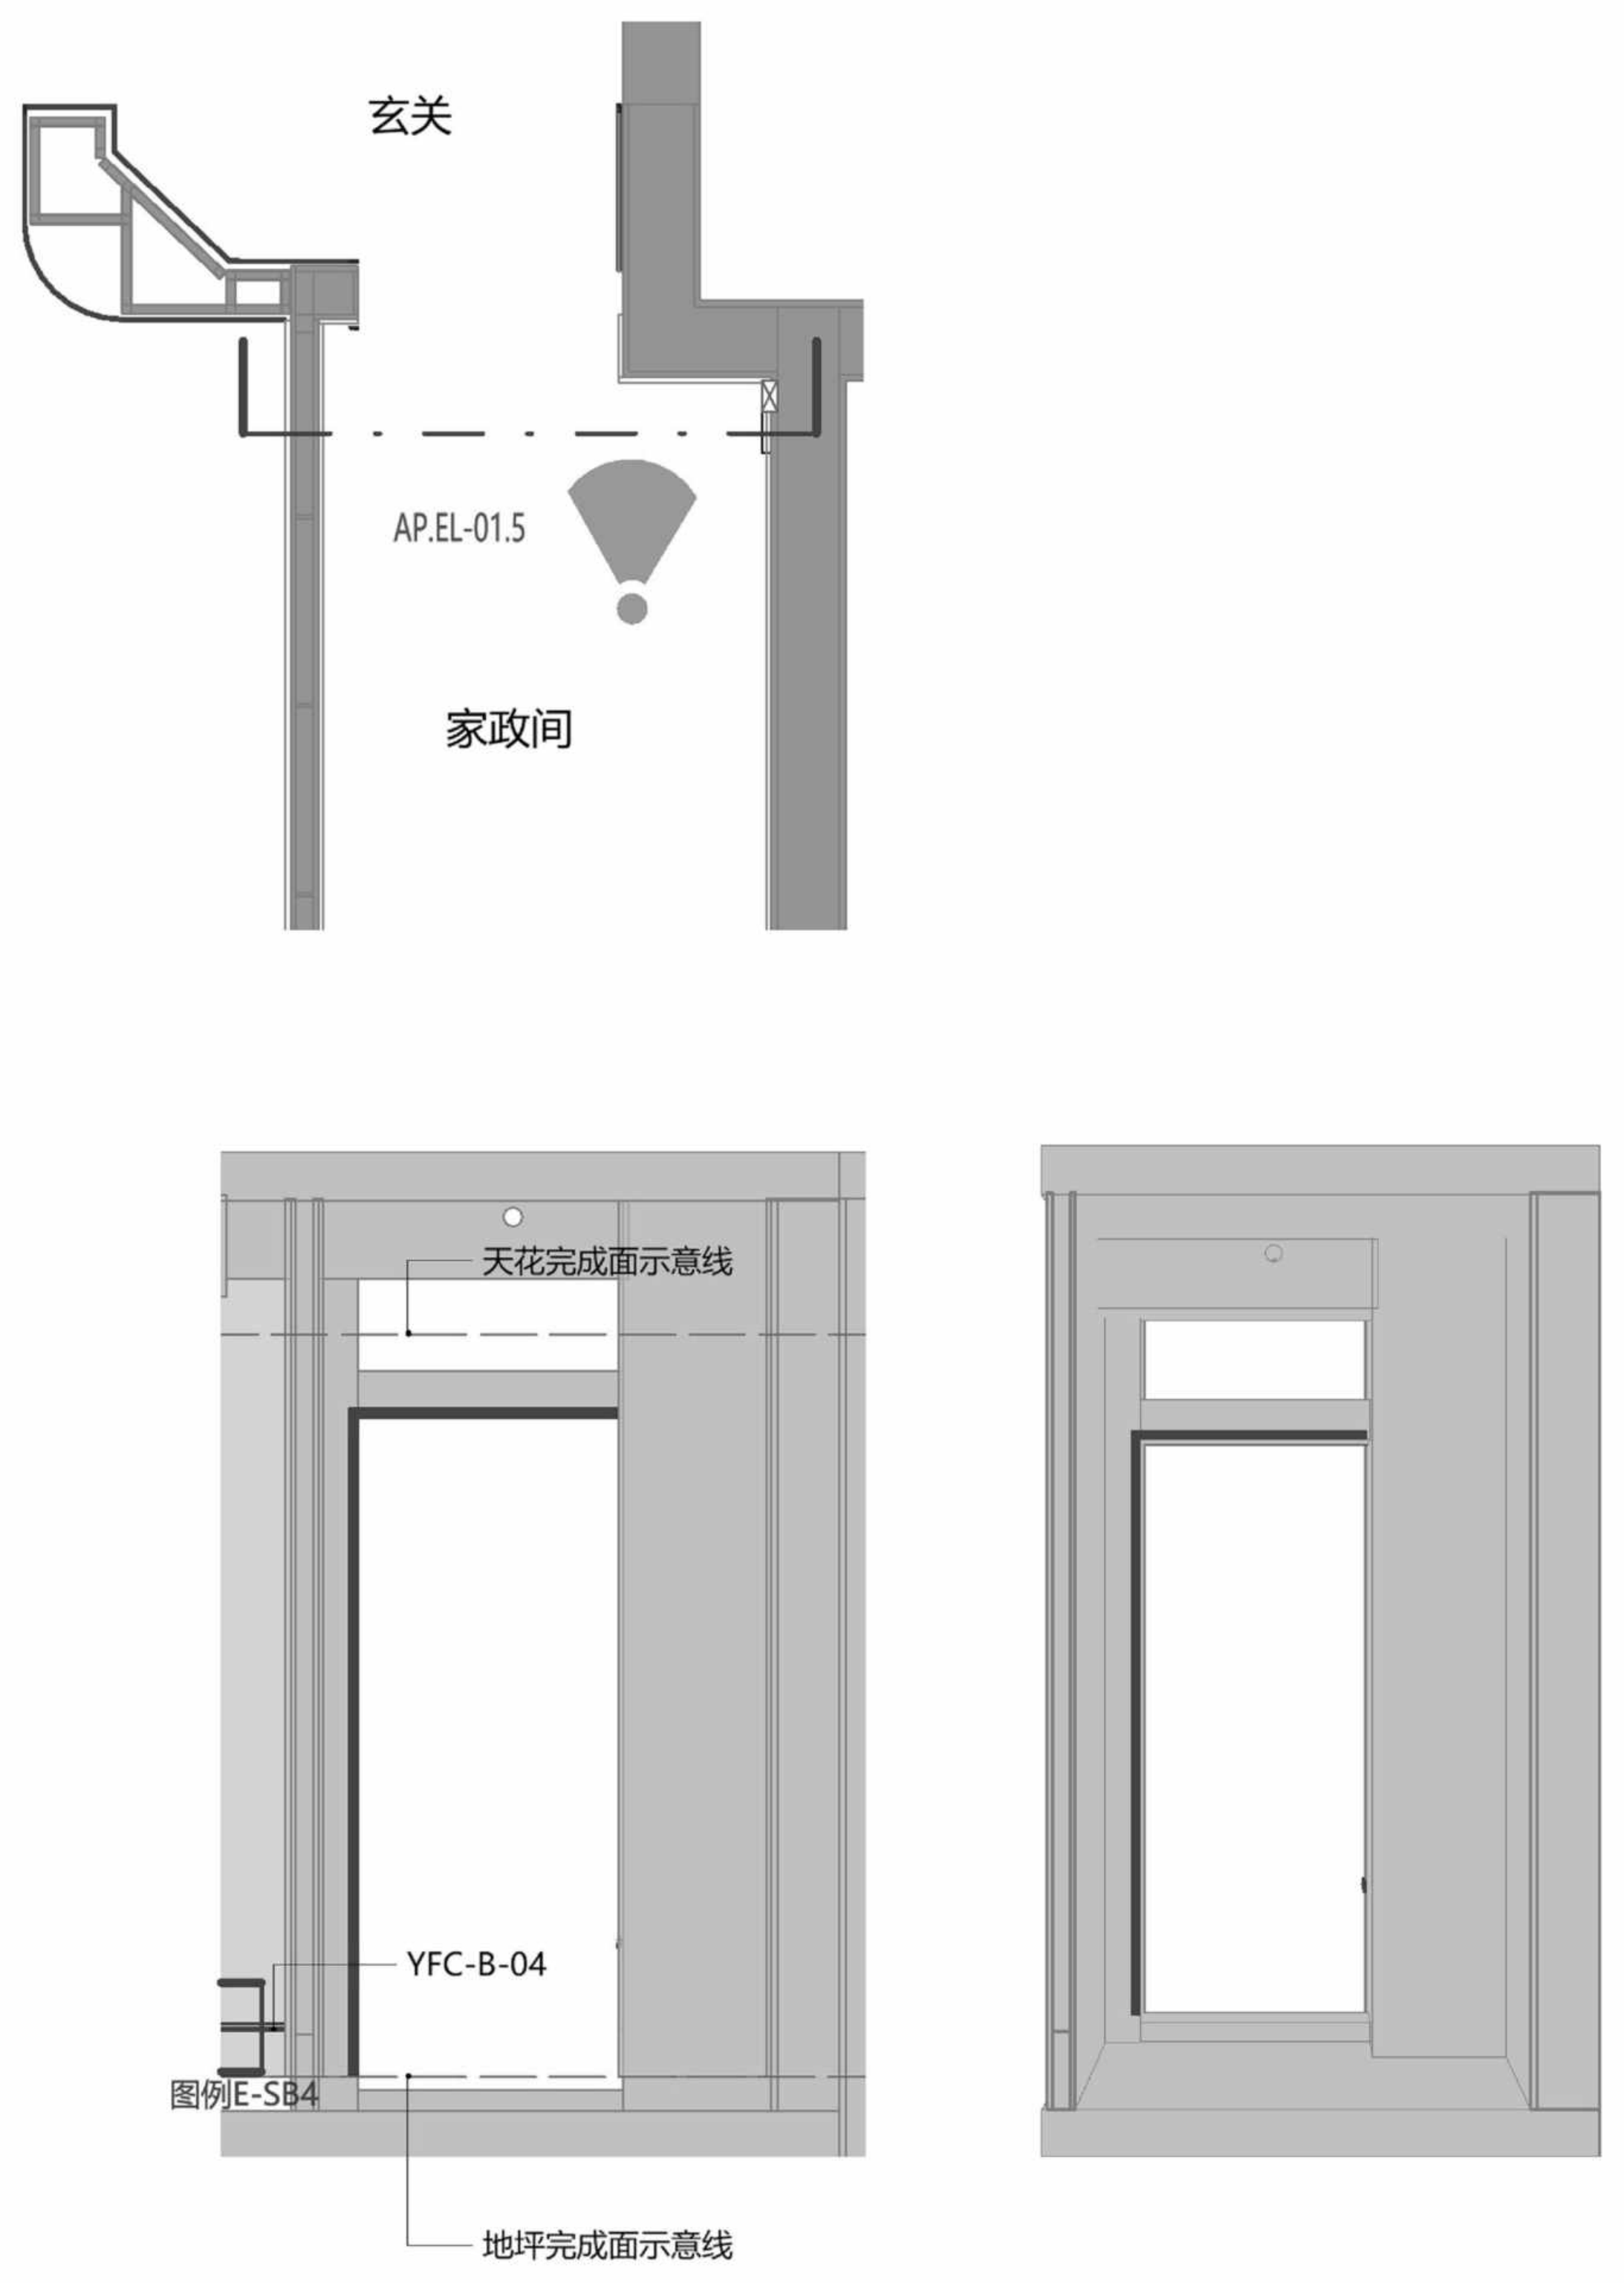
玄关
AP.EL-01.5
家政间
天花完成面示意线
YFC-B-04
图例E-SB4
地坪完成面示意线

5
家政间 墙面及踢脚铝型材立面图
Scale比例 1 : 30@A2

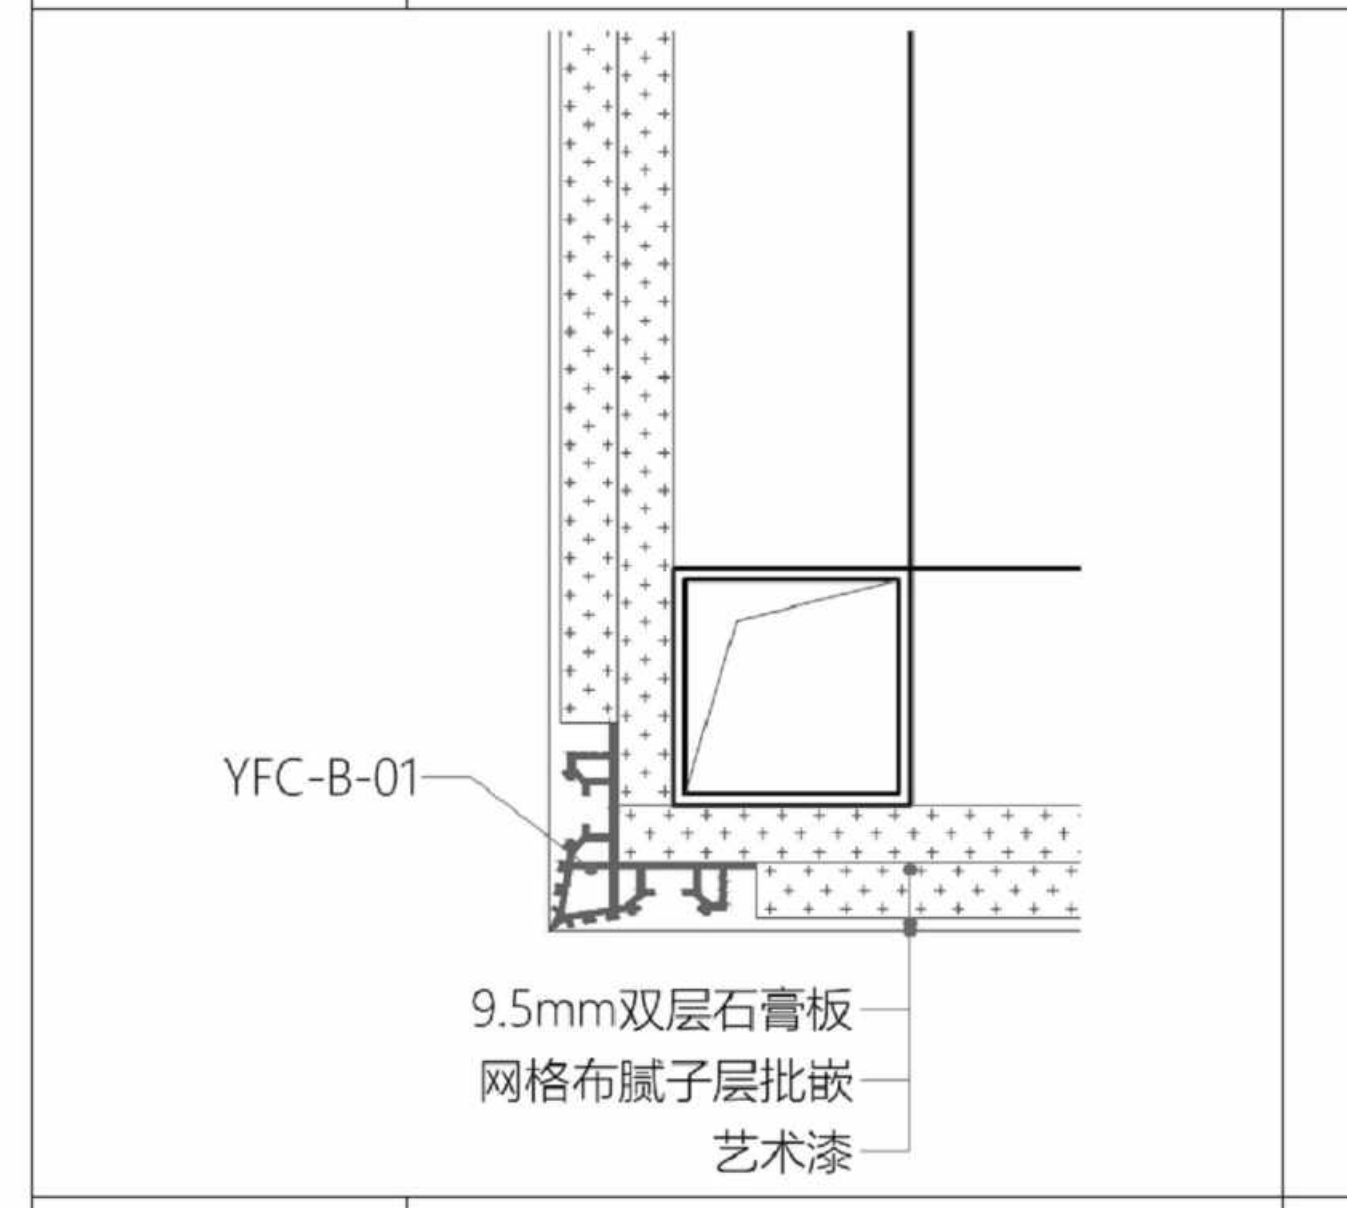
YFC-B-01
9.5mm双层石膏板
网格布腻子层批嵌
艺术漆

图例C-PB1
墙面-石膏基找平铝型材
Scale比例 1 : 1@A2

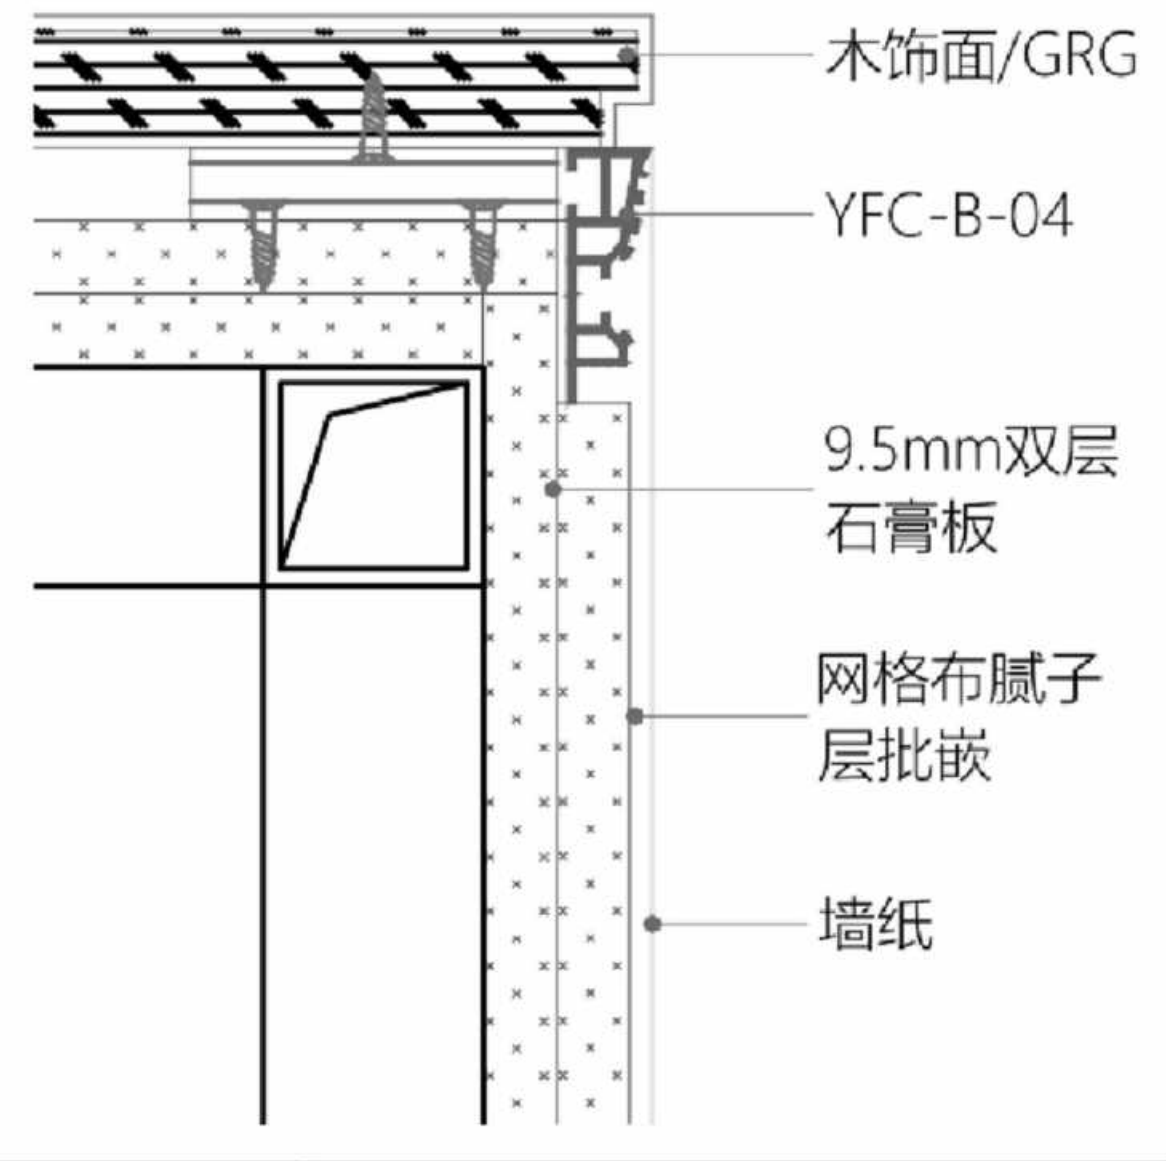
木饰面/GRG
YFC-B-04
9.5mm双层石膏板
网格布腻子层批嵌
墙纸

图例C-PB2
墙面-石膏基找平铝型材
Scale比例 1 : 1@A2

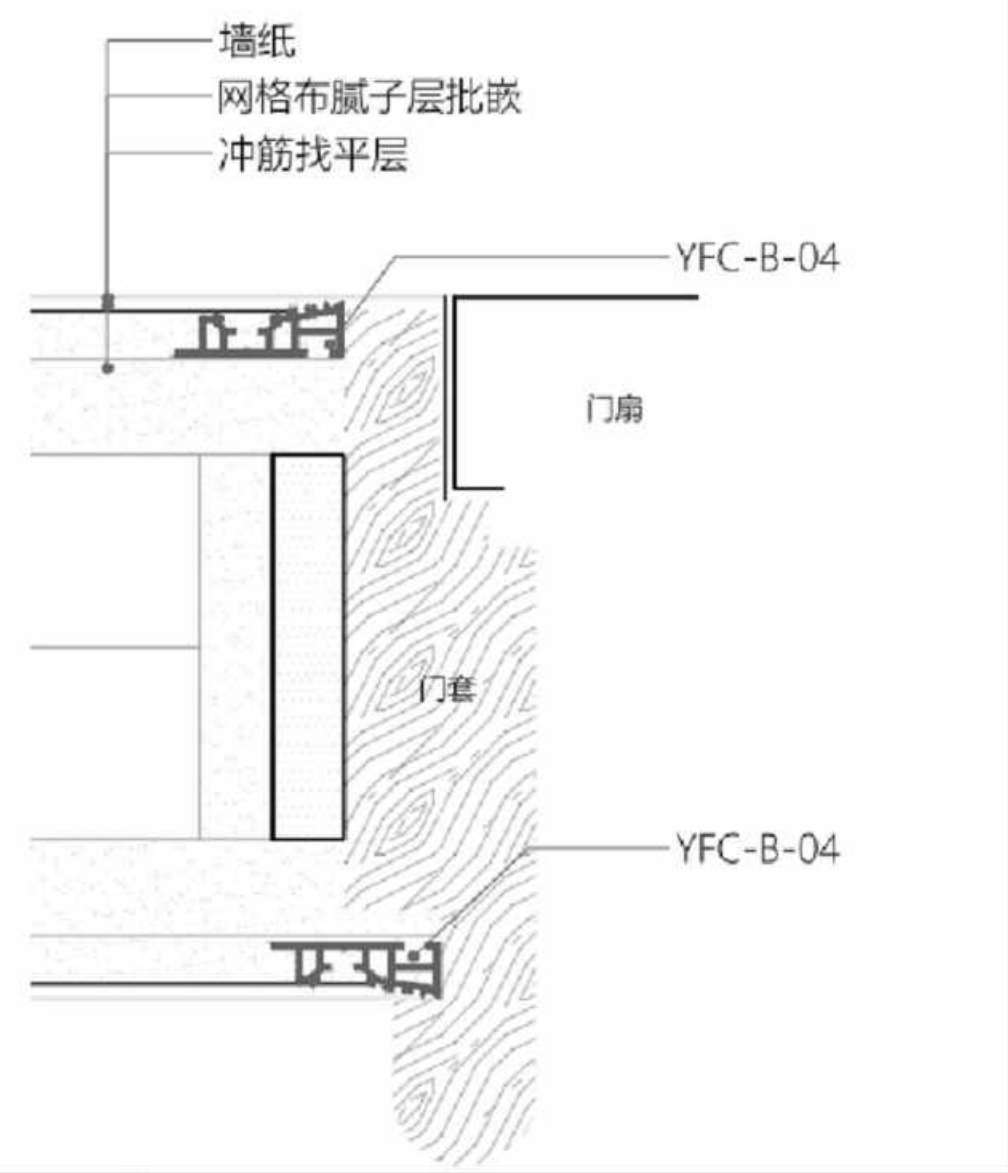
墙纸
网格布腻子层批嵌
冲筋找平层
YFC-B-04
门扇
门套
YFC-B-04

图例D-M2
门边-石膏基找平铝型材
Scale比例 1 : 1@A2

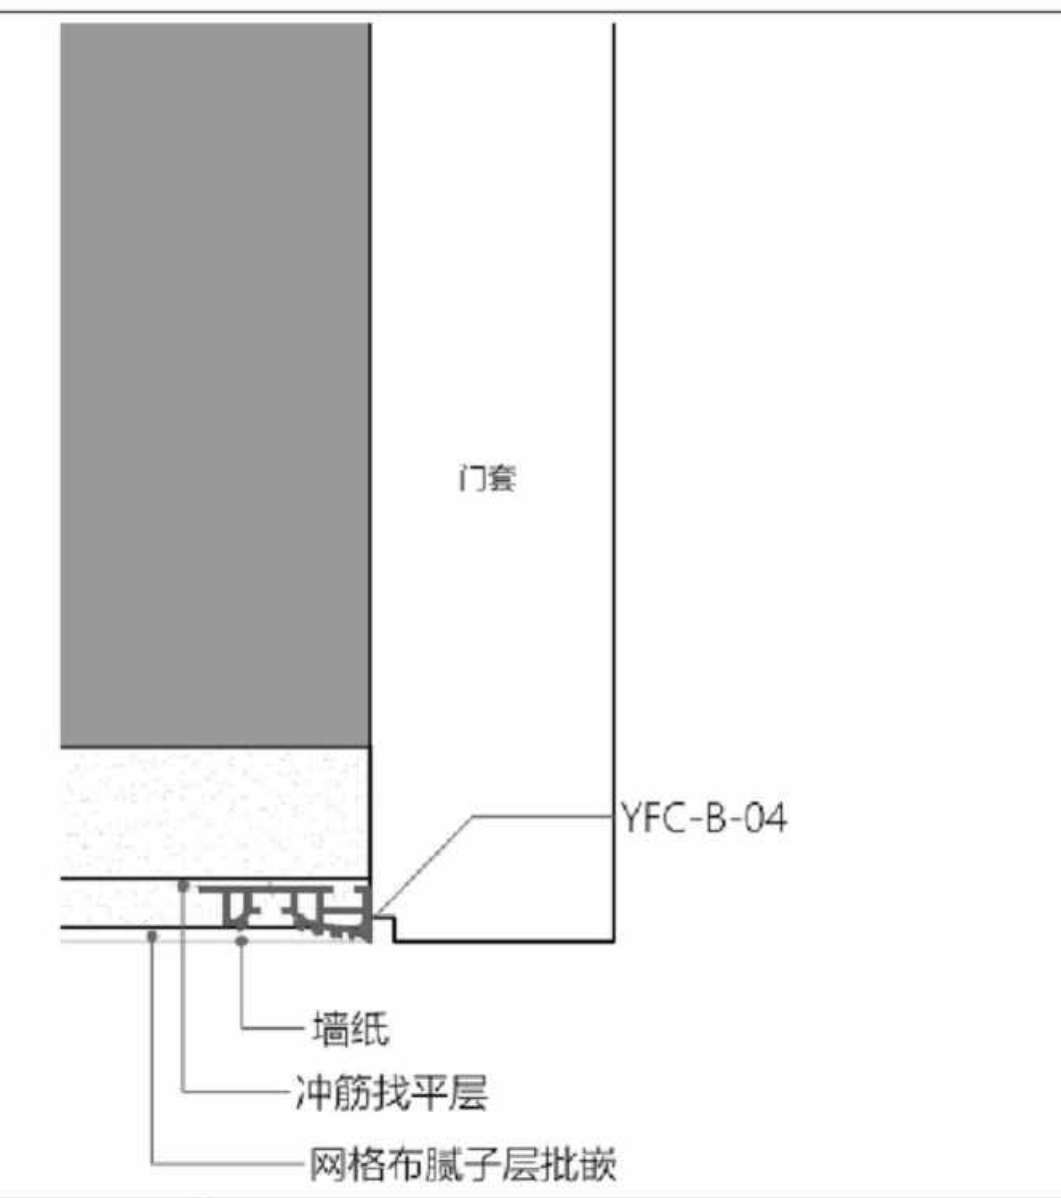
门套
YFC-B-04
墙纸
冲筋找平层
网格布腻子层批嵌

图例D-M3
门边-石膏基找平铝型材
Scale比例 1 : 1@A2

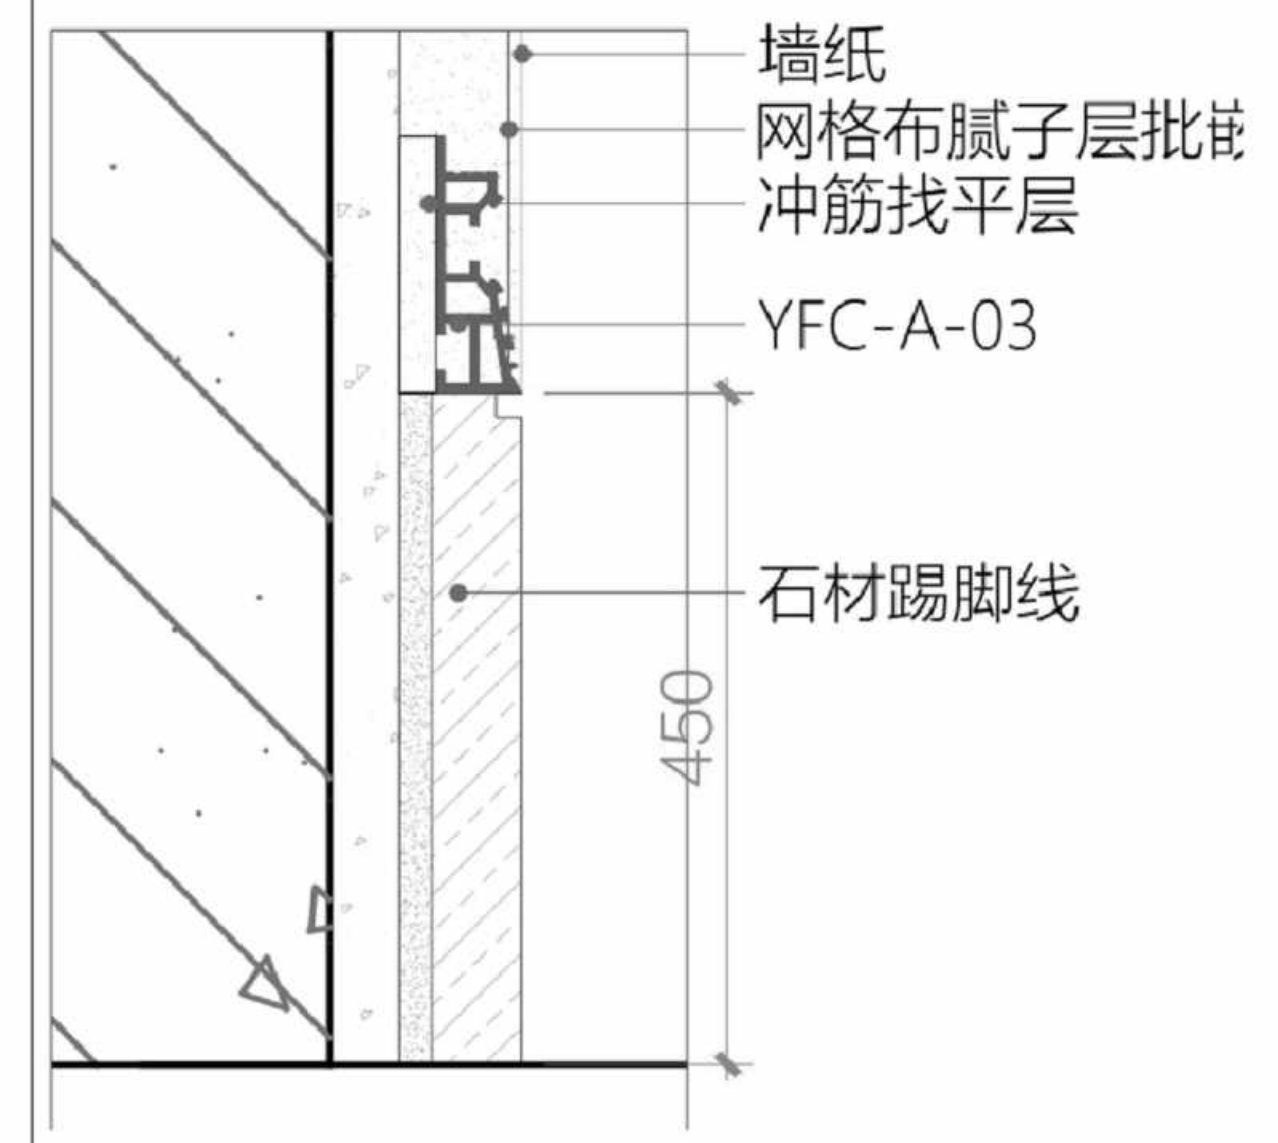
墙纸
网格布腻子层批嵌
冲筋找平层
YFC-A-03
石材踢脚线
450

图例E-SP2
踢脚-石膏基找平铝型材
Scale比例 1 : 1@A2

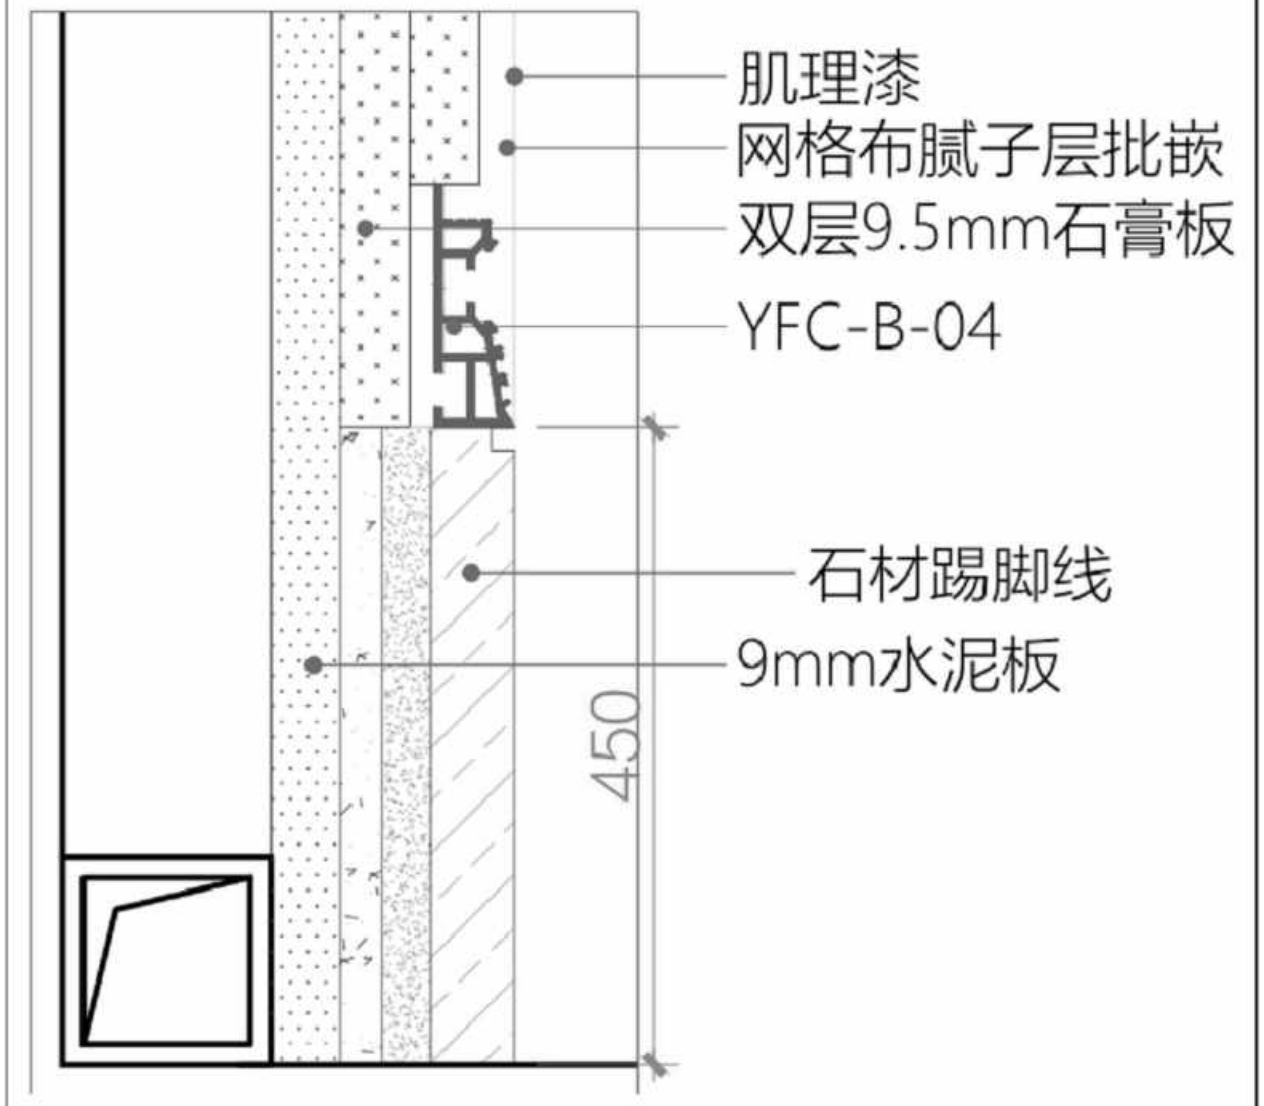
肌理漆
网格布腻子层批嵌
双层9.5mm石膏板
YFC-B-04
石材踢脚线
9mm水泥板
450

图例E-SB4
踢脚-石膏基找平铝型材
Scale比例 1 : 1@A2

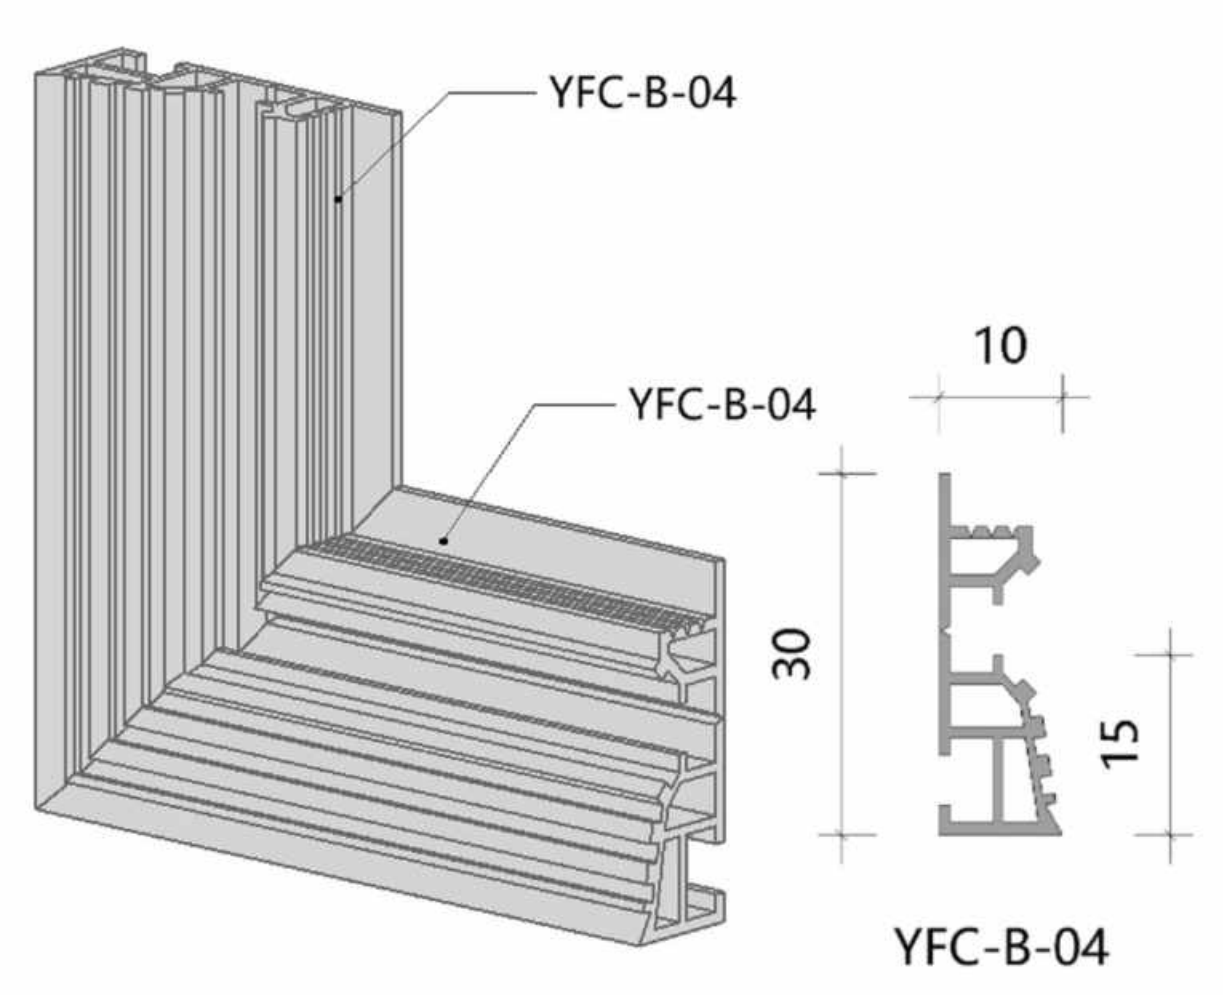
YFC-B-04
YFC-B-04
10
30
15
YFC-B-04

3D-01
转角铝型材-拼接跟通
转角数量：1

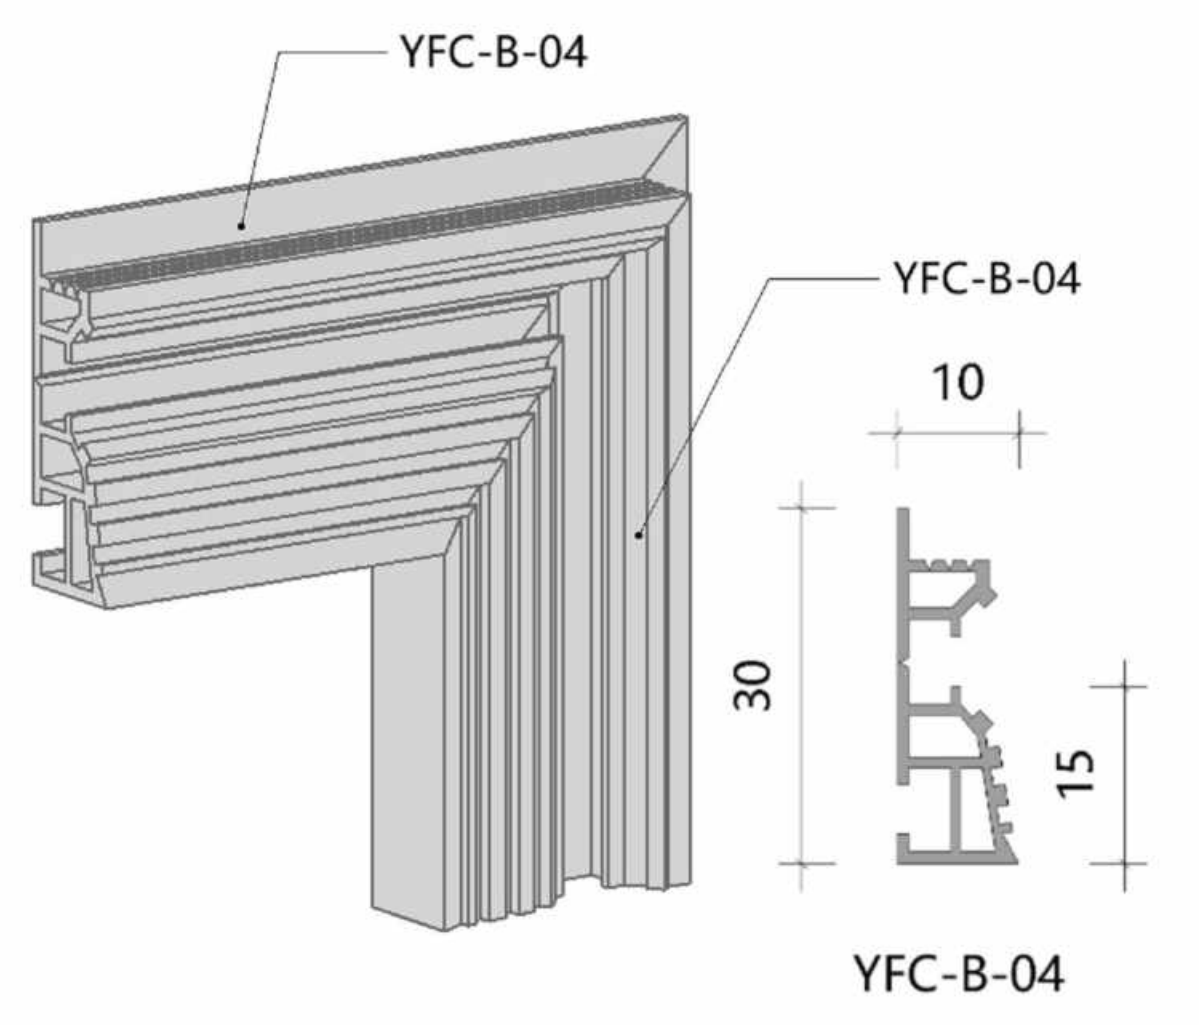
YFC-B-04
YFC-B-04
10
30
15
YFC-B-04

3D-02
转角铝型材-拼接跟通
转角数量：2

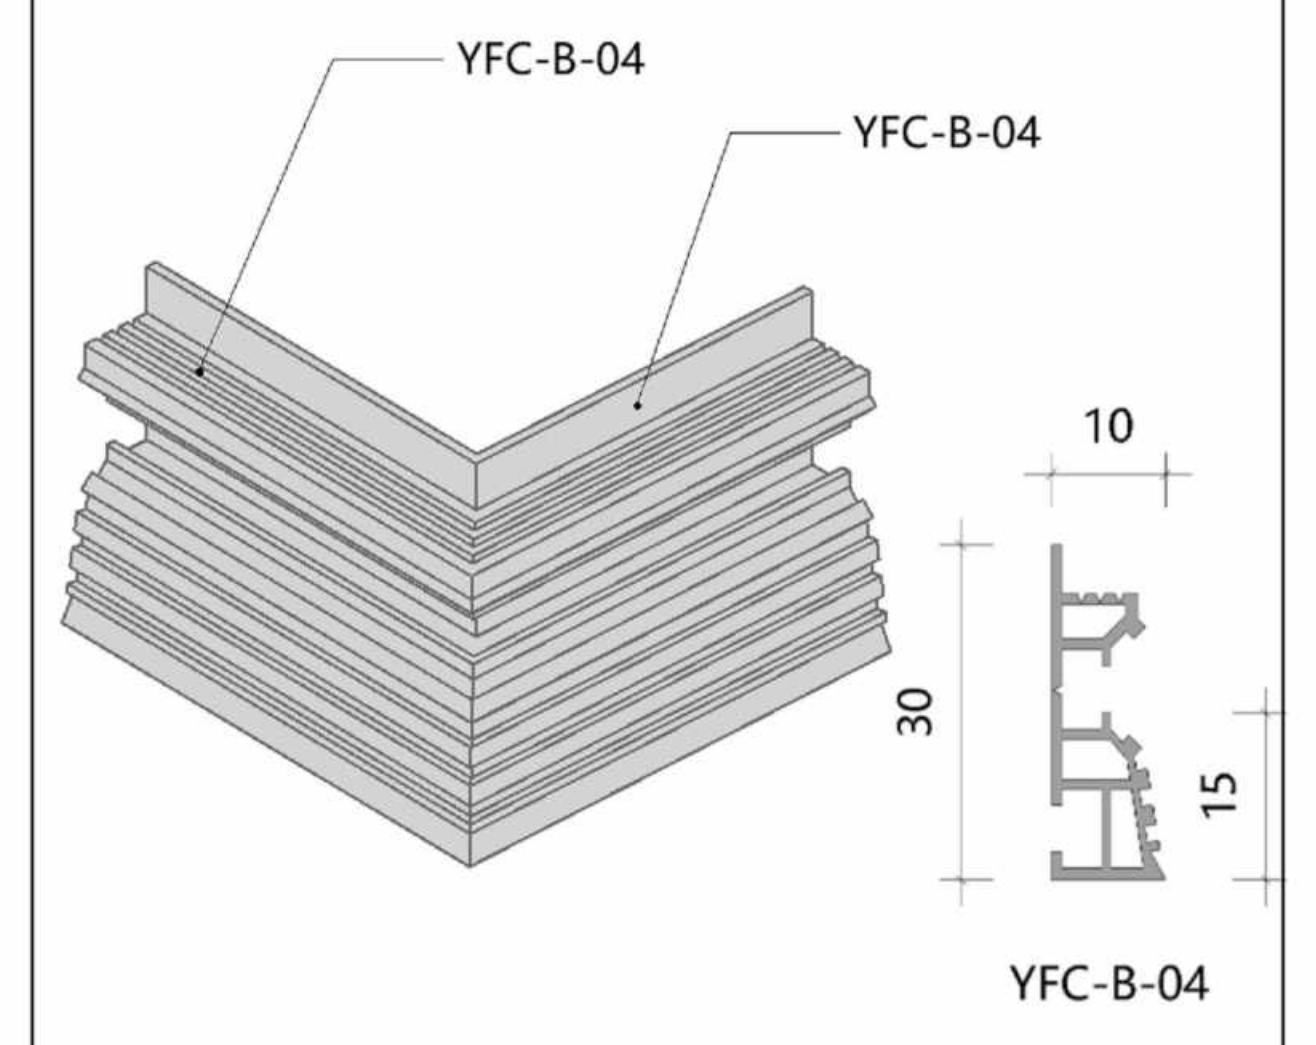
YFC-B-04
YFC-B-04
10
30
15
YFC-B-04

3D-03
转角铝型材-拼接跟通
转角数量：4

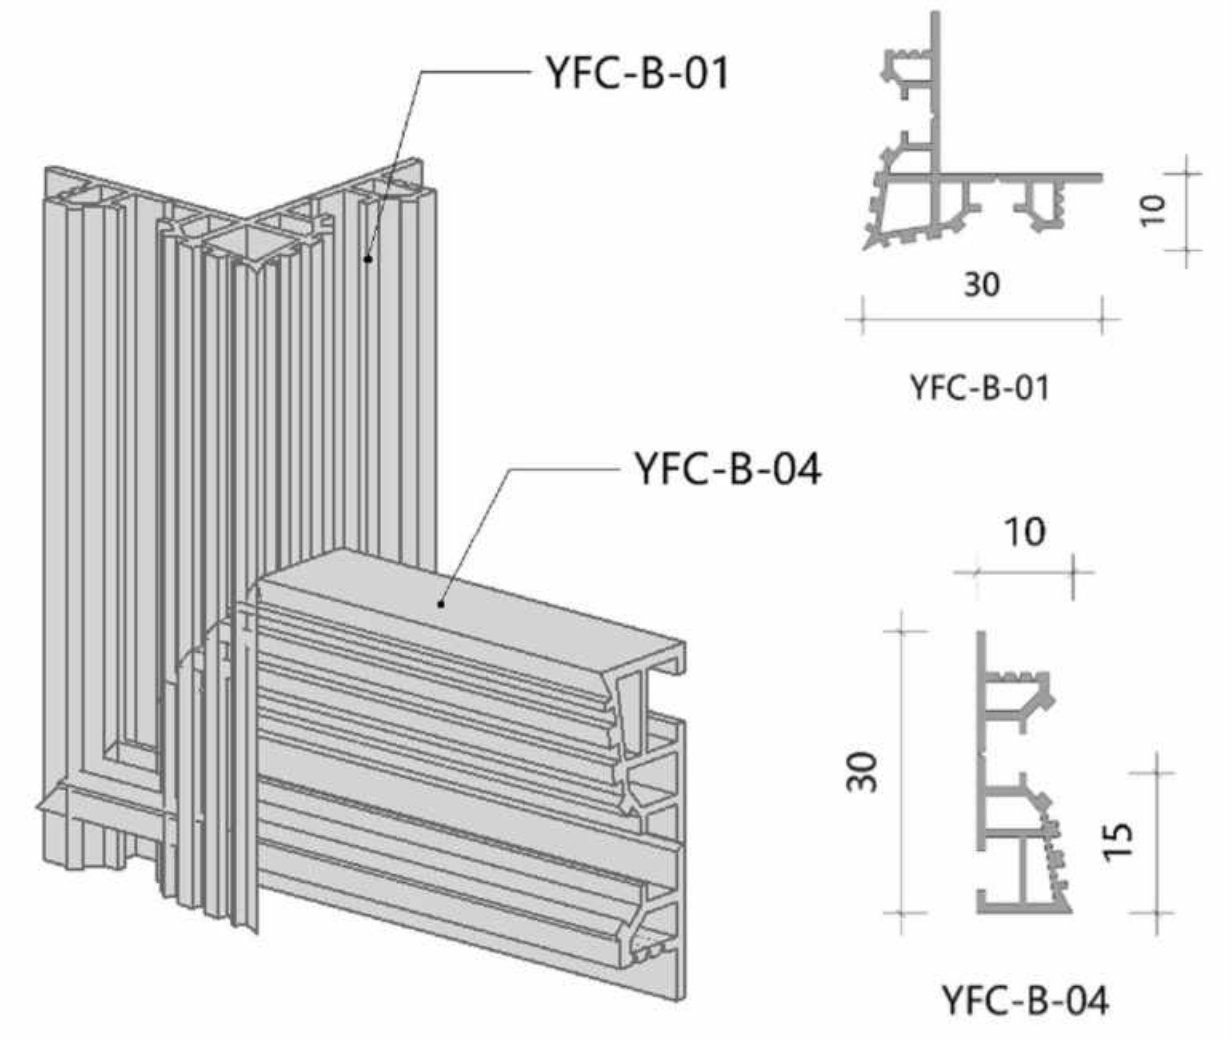
YFC-B-01
20
10
30
YFC-B-01
YFC-B-04
10
30
15
YFC-B-04

3D-09
转角铝型材-拼接跟通
转角数量：1

EIBORN

盖章

注释
Notes
1.本图纸如与现场尺寸有误，请施工人员与项目负责人联系。
2.施工前施工人员应认真查阅此图，如有不明确尺寸，按现场测量为准。
3.本图纸必须经甲乙双方认可并签字方可作为施工依据。

日期
Date 03/04/26

修订
Revision
1

项目
Project
潮映华岸府3-801

比例
Scale 1：30@A2

玄关、家政间
墙面及踢脚铝型材

图纸编号
Drawing No.
AP.EL-01

项目编号
Project No.
©2025

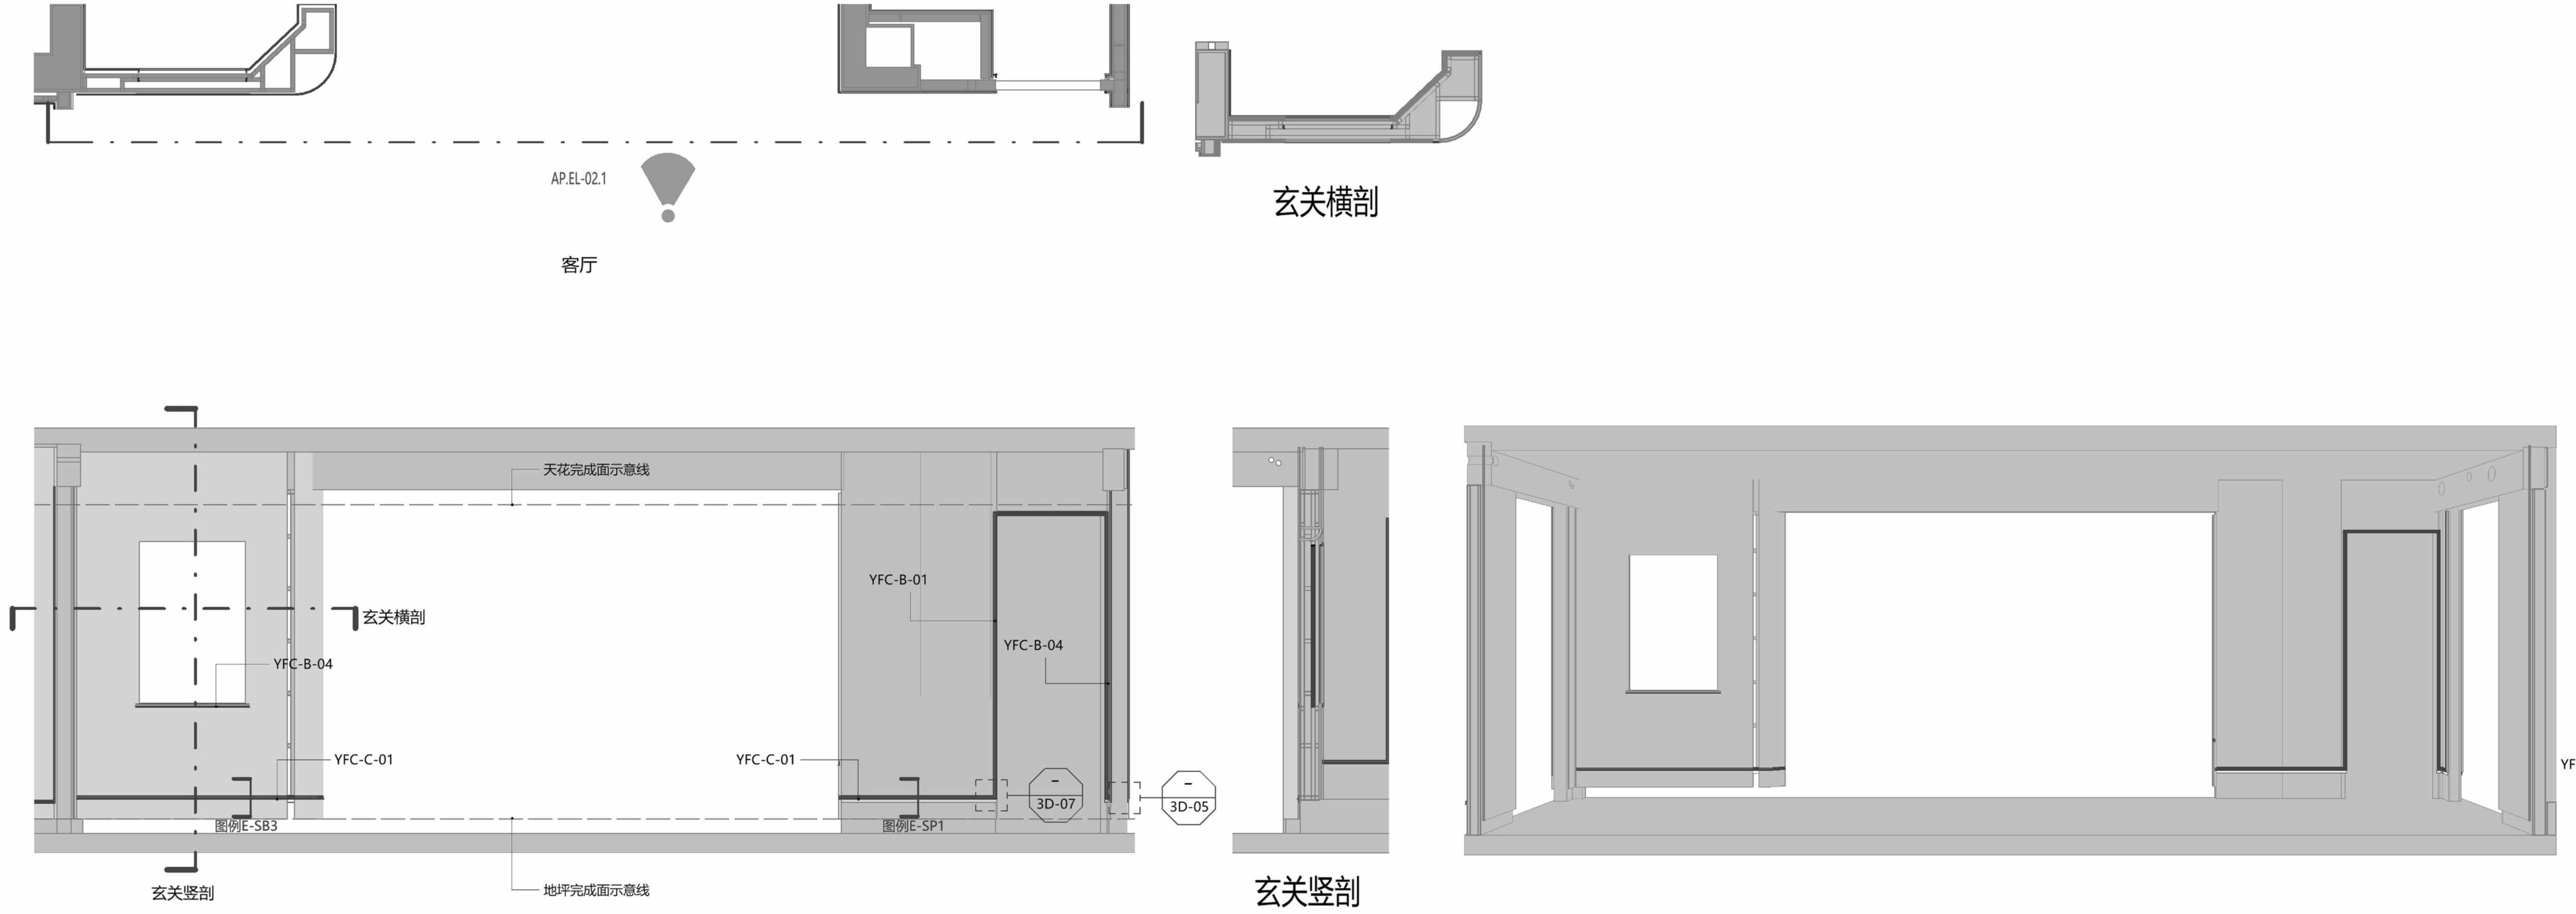
AP.EL-02.1
客厅
玄关横剖
天花完成面示意线
玄关横剖
YFC-B-04
YFC-C-01
YFC-B-01
YFC-B-04
YFC-C-01
3D-07
3D-05
图例E-SB3
图例E-SP1
玄关竖剖
地坪完成面示意线
玄关竖剖

1

客厅一 墙面及踢脚铝型材立面图1

Scale比例 1：30@A2

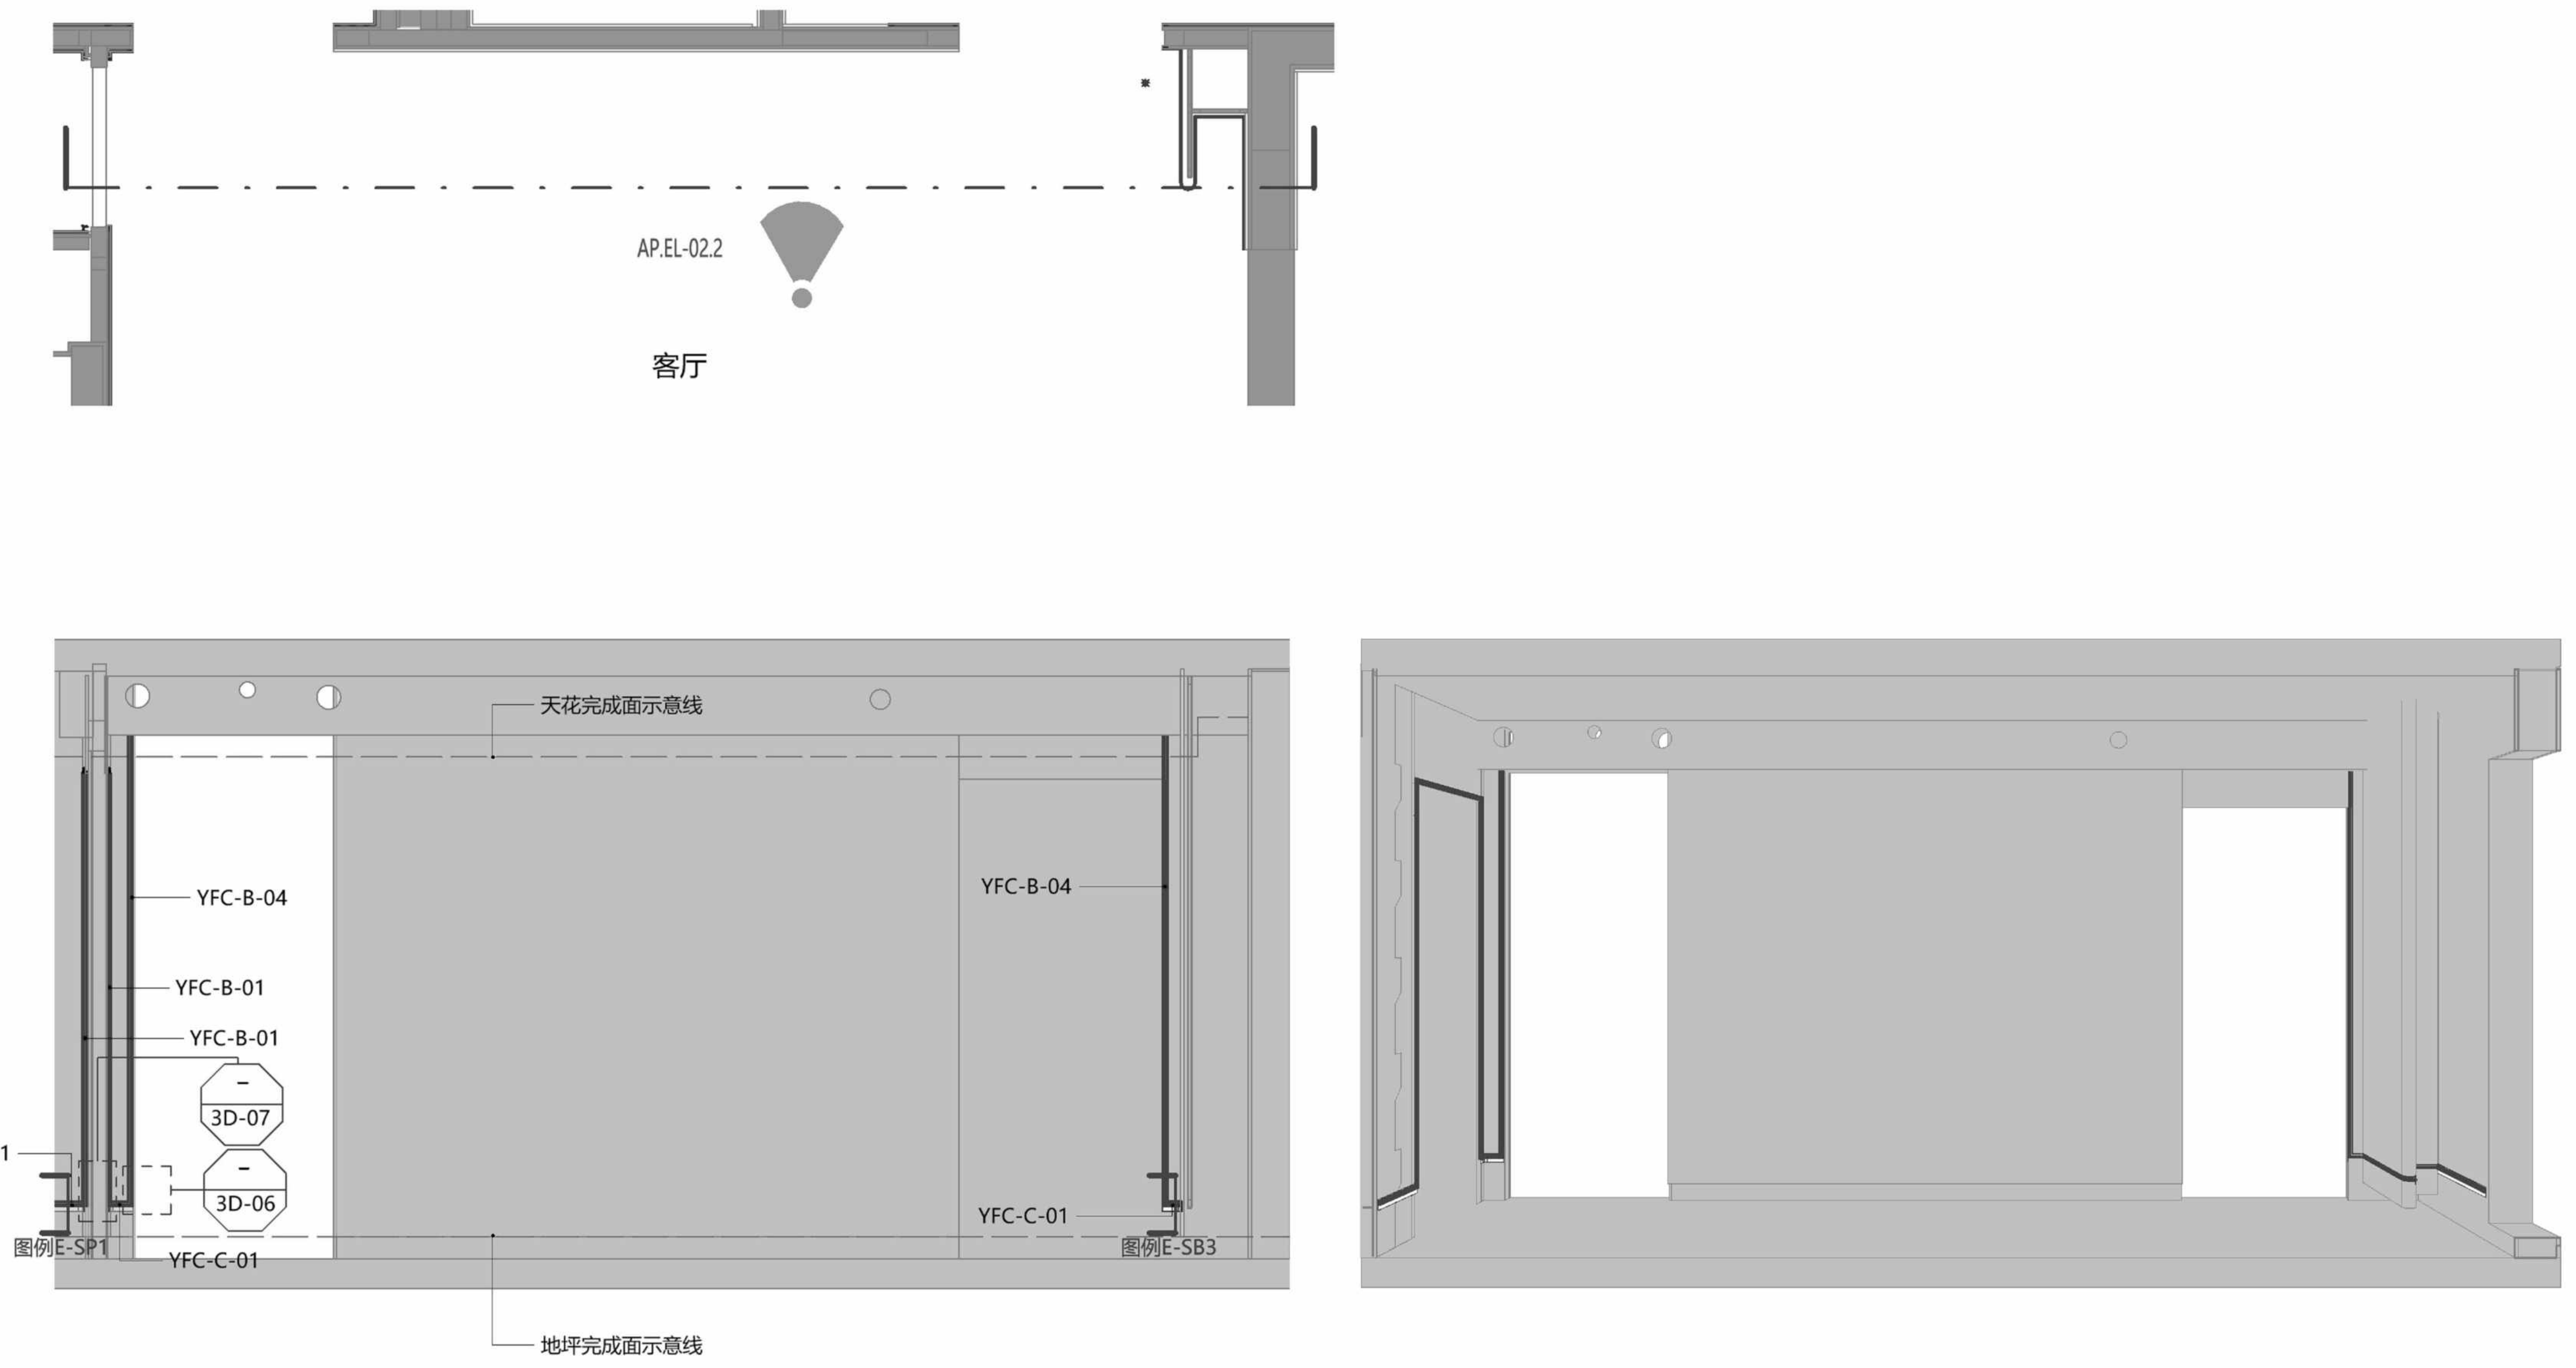
AP.EL-02.2
客厅
天花完成面示意线
YFC-B-04
YFC-B-01
YFC-B-01
3D-07
YFC-C-01
3D-06
图例E-SP1
YFC-C-01
YFC-B-04
YFC-C-01
图例E-SB3
地坪完成面示意线

2

客厅一 墙面及踢脚铝型材立面图2

Scale比例 1：30@A2

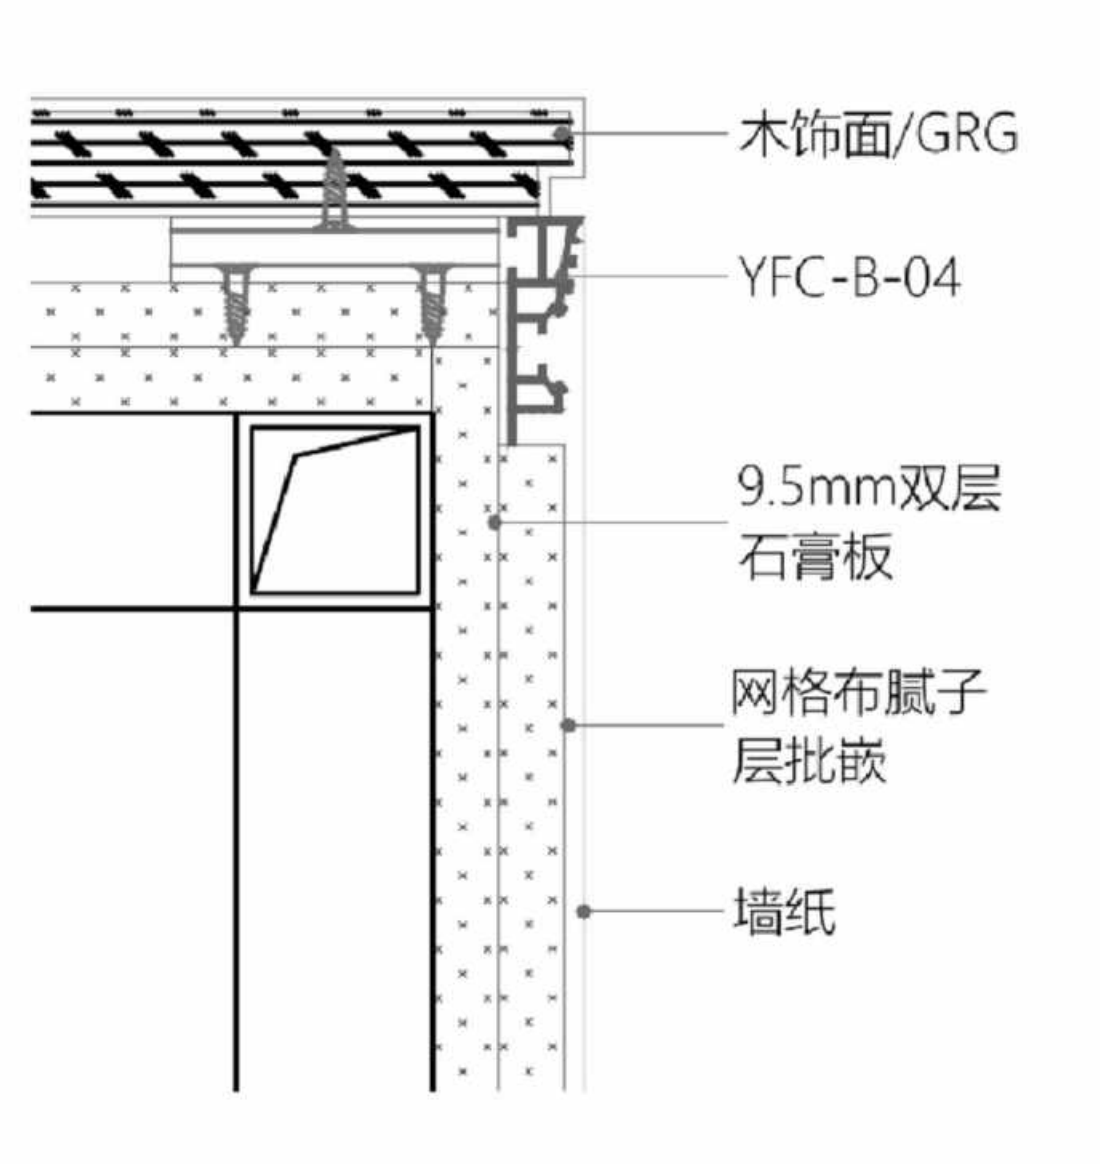
木饰面/GRG
YFC-B-04
9.5mm双层石膏板
网格布腻子层批嵌
墙纸

图例C-PB2

墙面-石膏基找平铝型材

Scale比例 1：1@A2

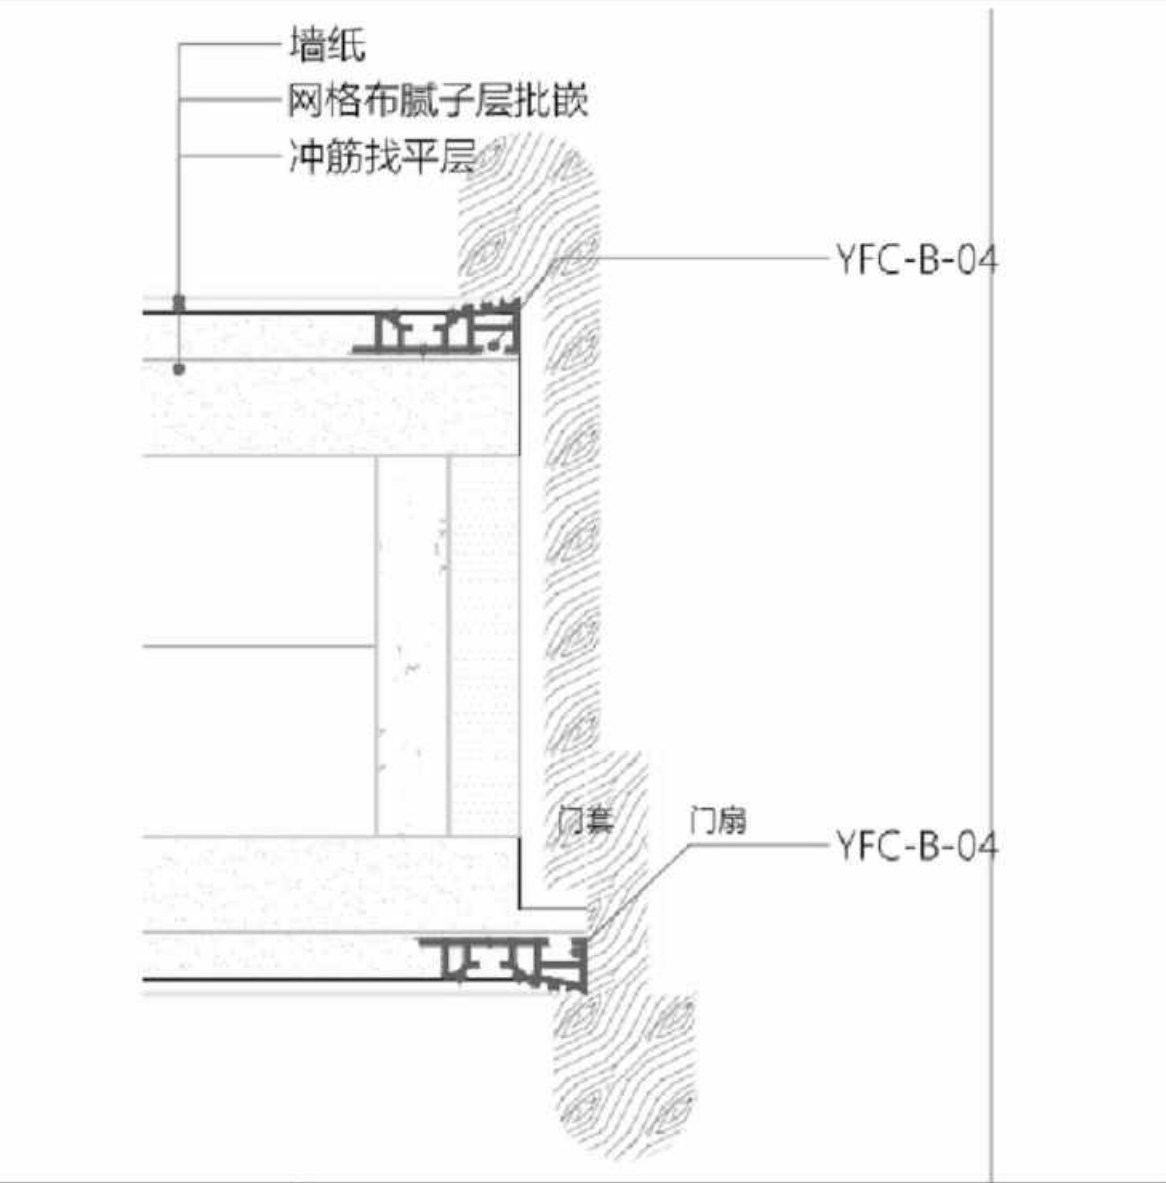
墙纸
网格布腻子层批嵌
冲筋找平层
YFC-B-04
门套
门扇
YFC-B-04

图例D-M1

门边-石膏基找平铝型材

Scale比例 1：1@A2

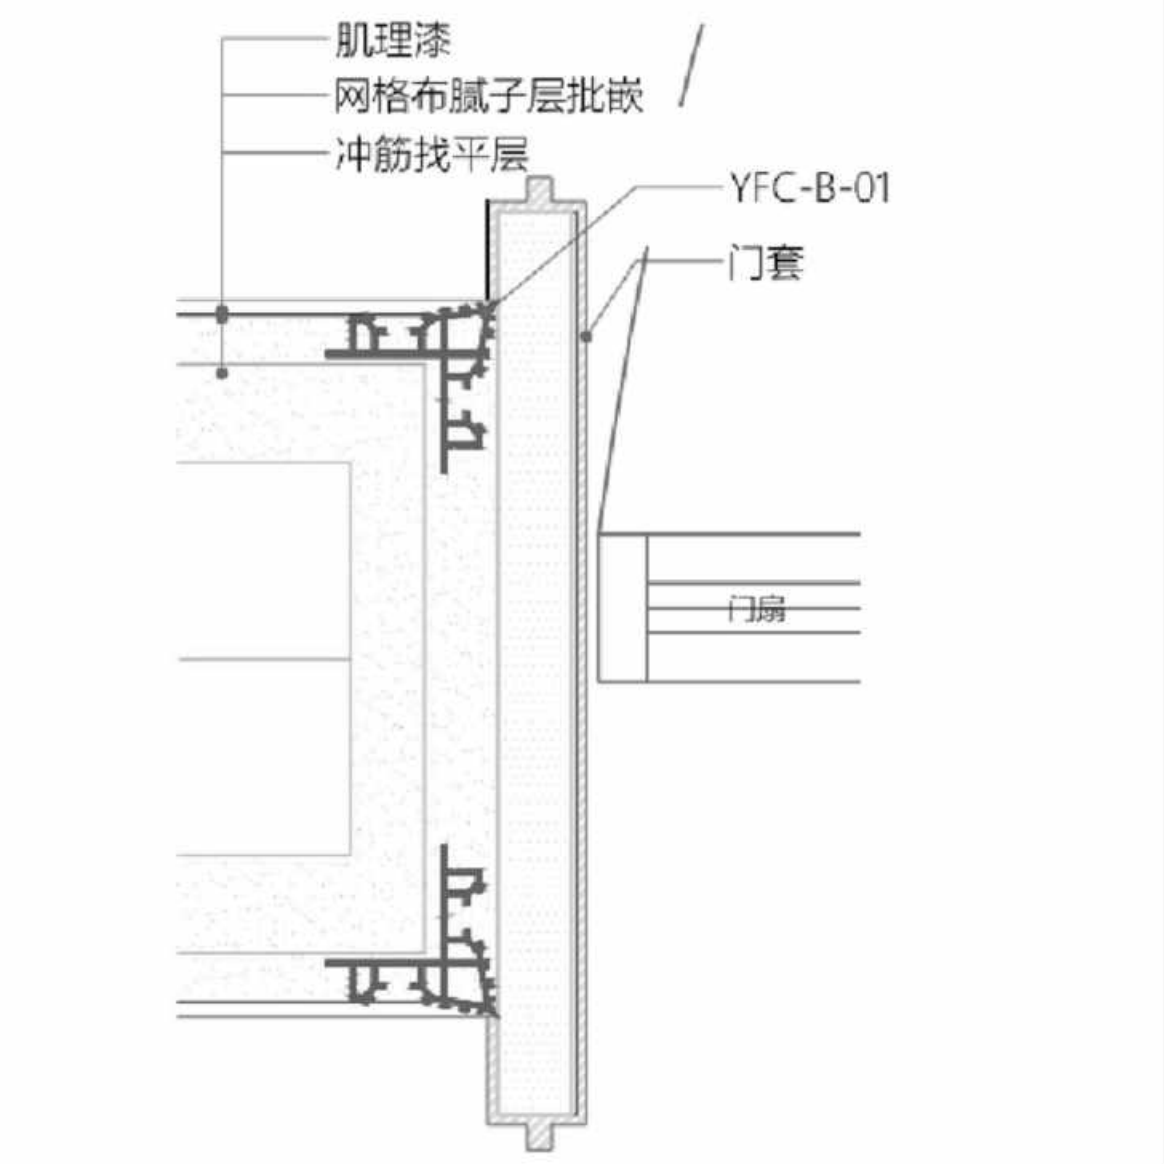
肌理漆
网格布腻子层批嵌
冲筋找平层
YFC-B-01
门套
门扇

图例D-M4

门边-石膏基找平铝型材

Scale比例 1：1@A2

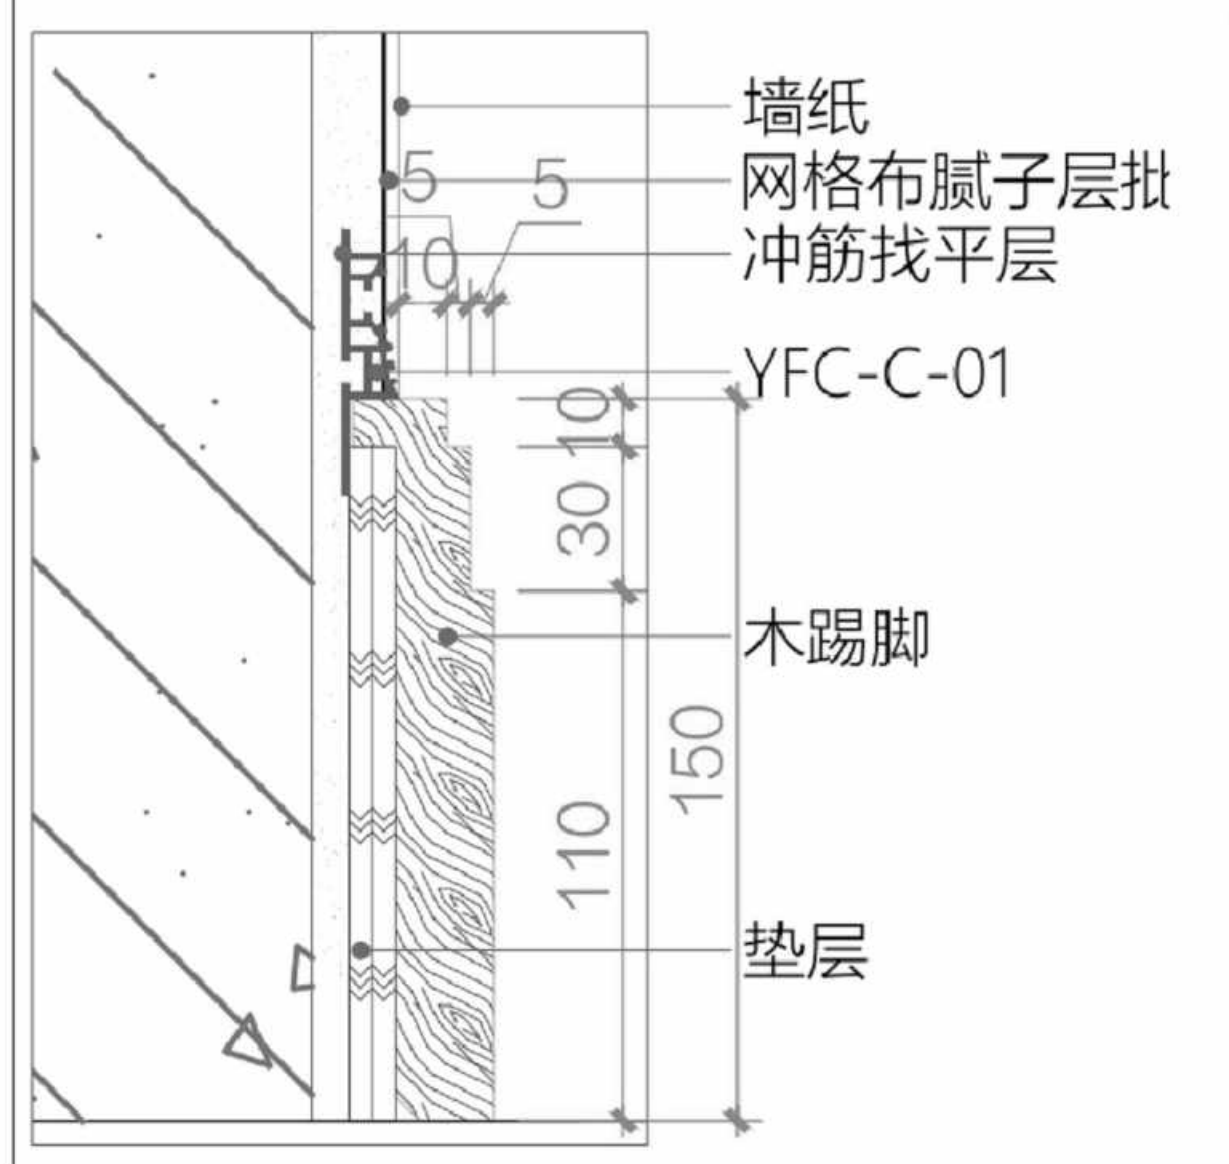
墙纸
网格布腻子层批
冲筋找平层
YFC-C-01
木踢脚
垫层
5
5
10
10
30
150
110

图例E-SP1

踢脚-石膏基找平铝型材

Scale比例 1：1@A2

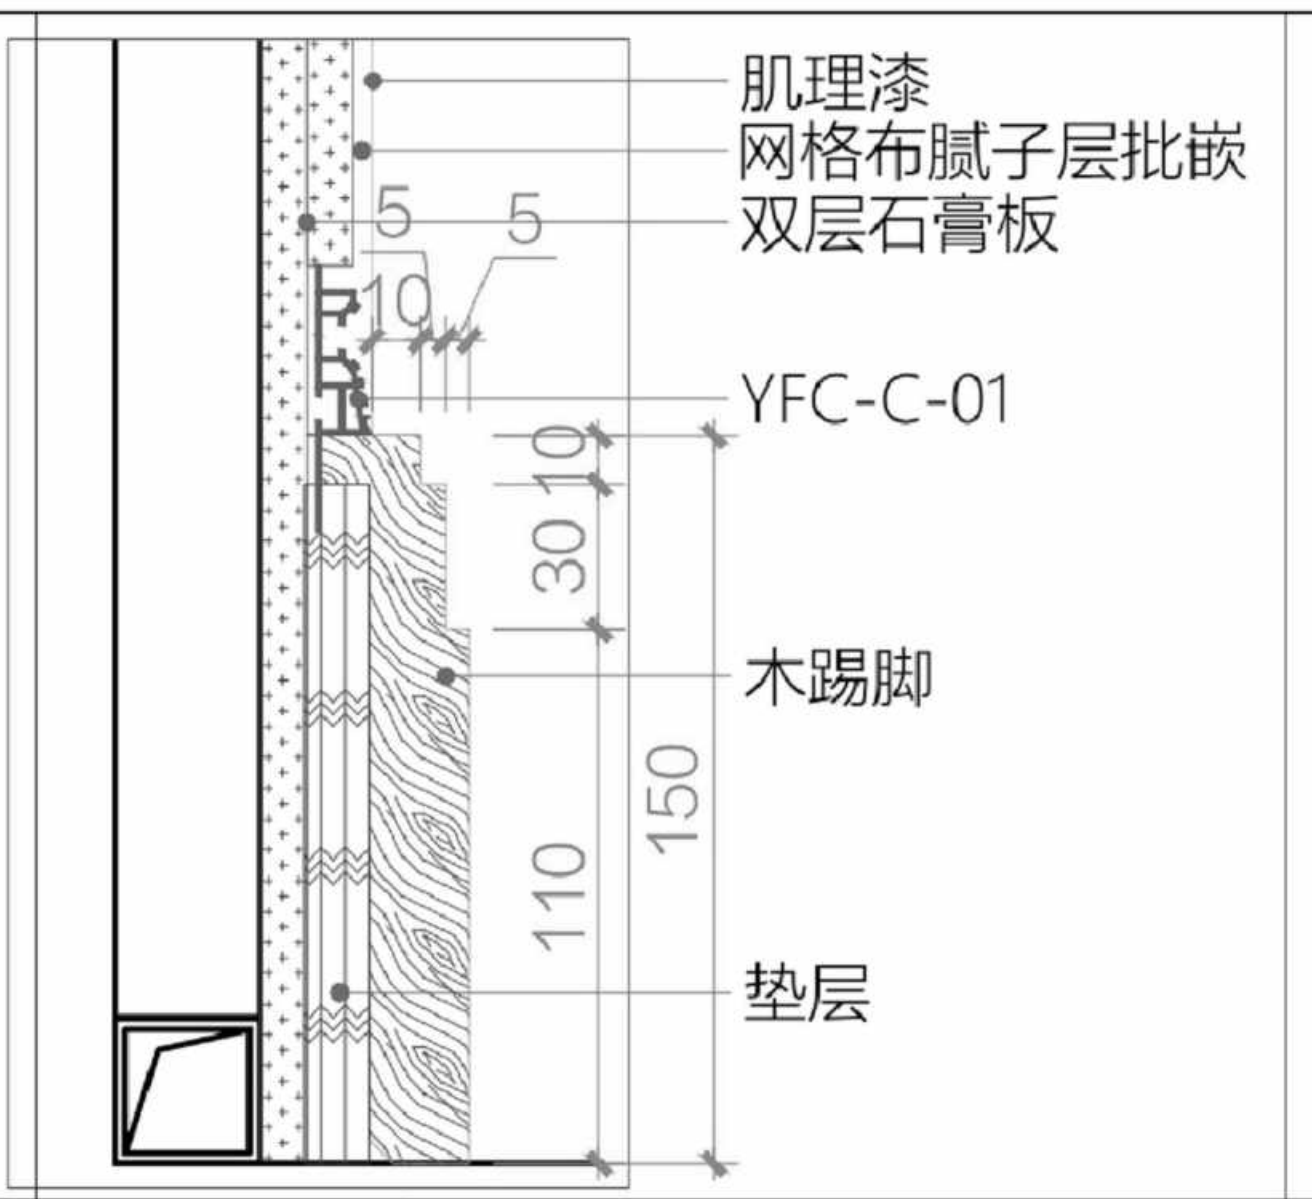
肌理漆
网格布腻子层批嵌
双层石膏板
YFC-C-01
木踢脚
垫层
5
5
10
10
30
150
110

图例E-SB3

踢脚-石膏基找平铝型材

Scale比例 1：1@A2

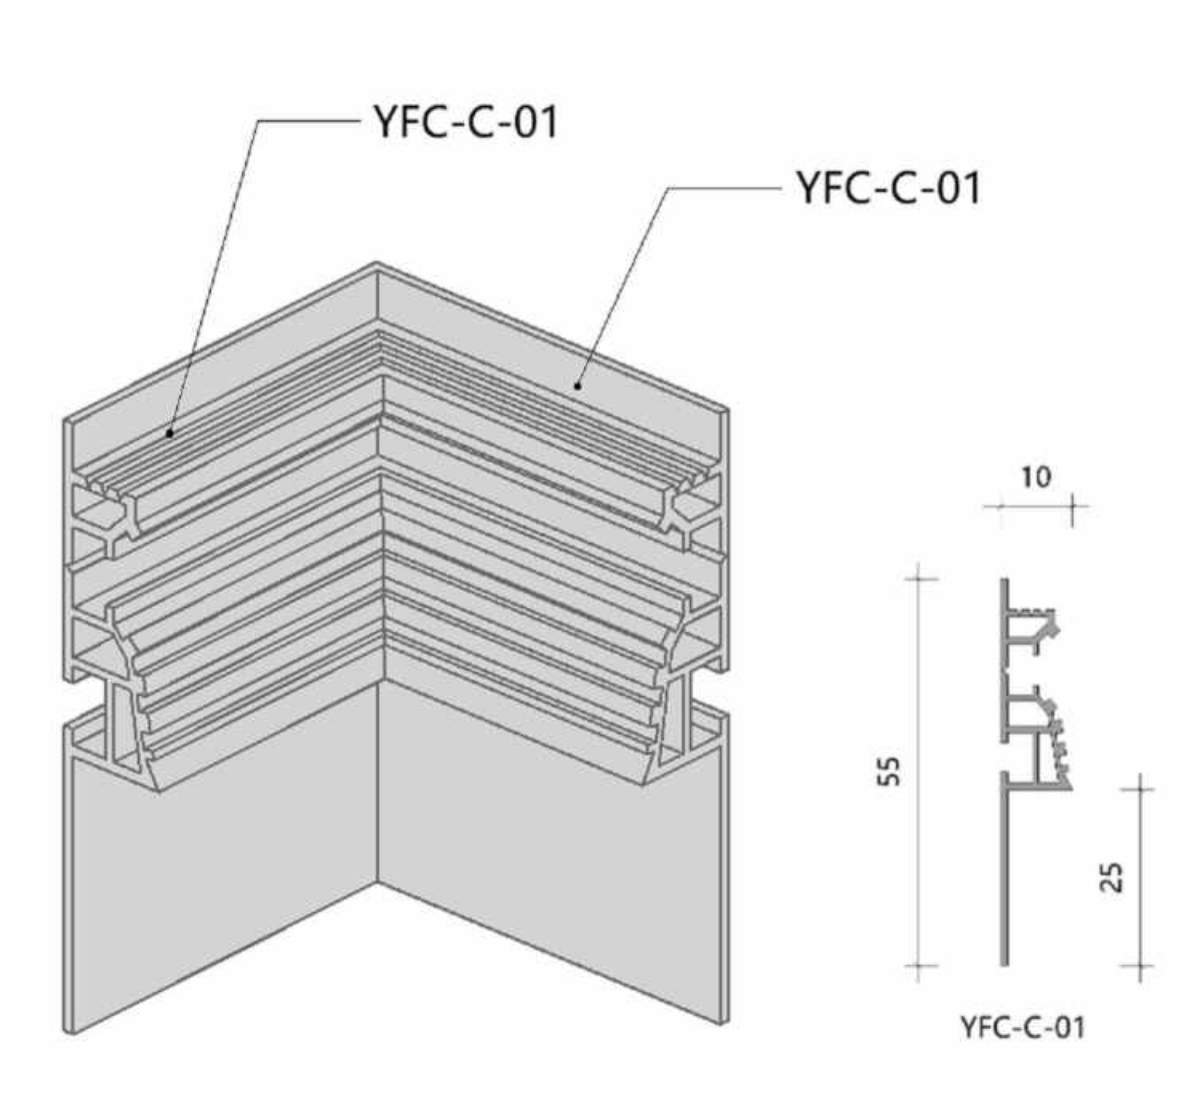
YFC-C-01
YFC-C-01
10
55
25
YFC-C-01

3D-05

转角铝型材-拼接跟通

转角数量：1

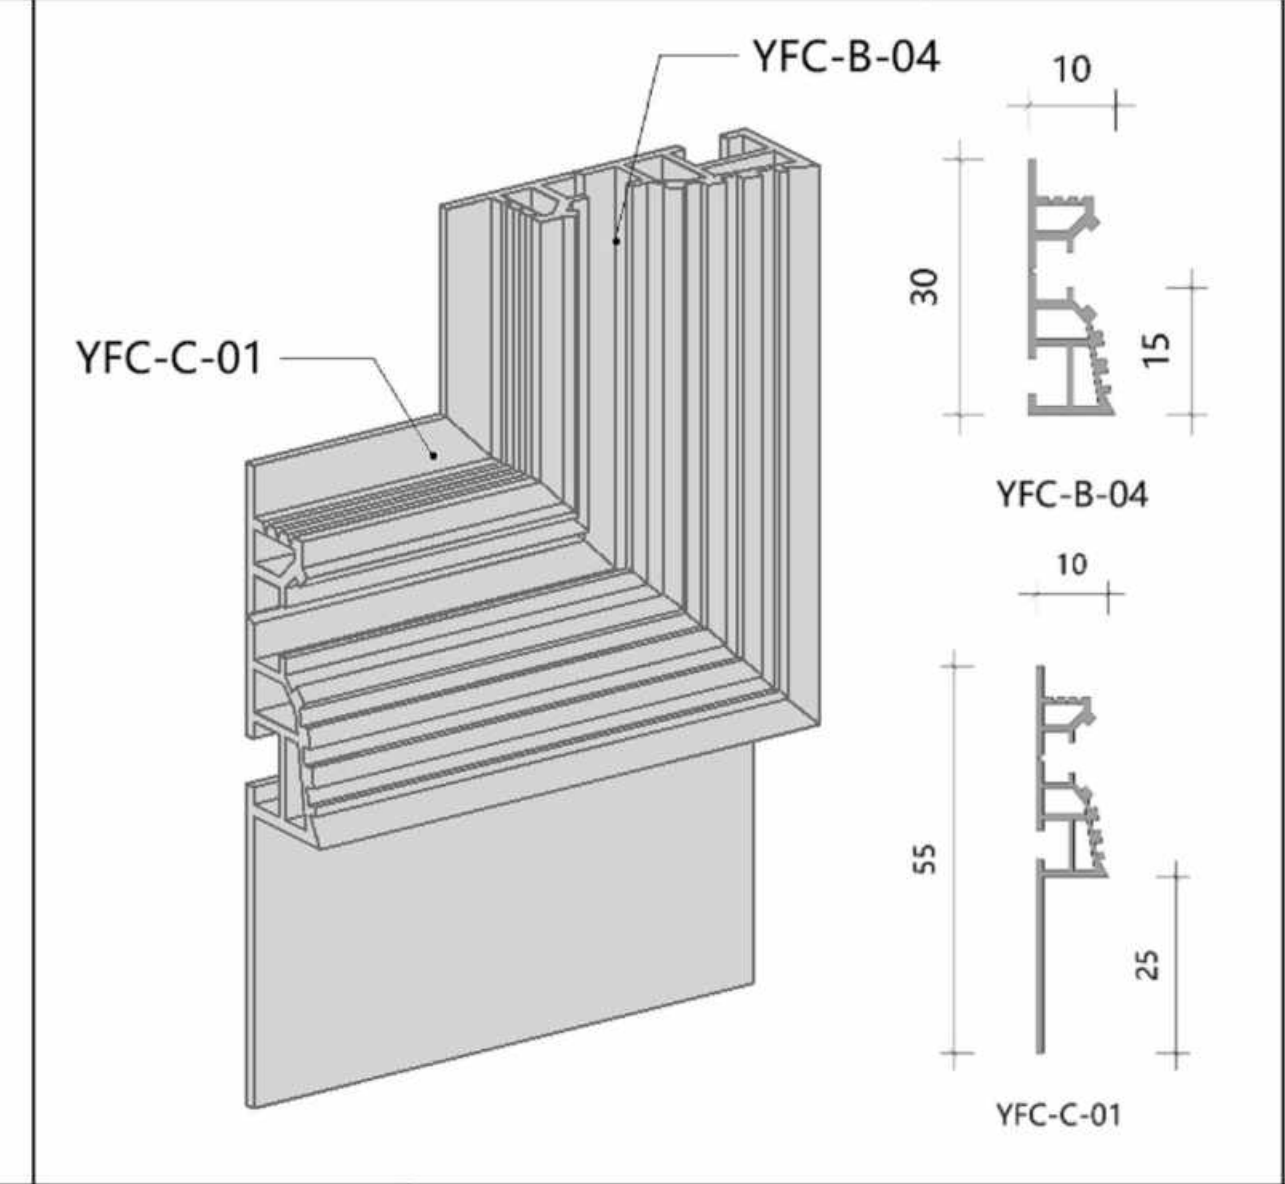
YFC-B-04
YFC-C-01
10
30
15
YFC-B-04
10
55
25
YFC-C-01

3D-06

转角铝型材-拼接跟通

转角数量：1

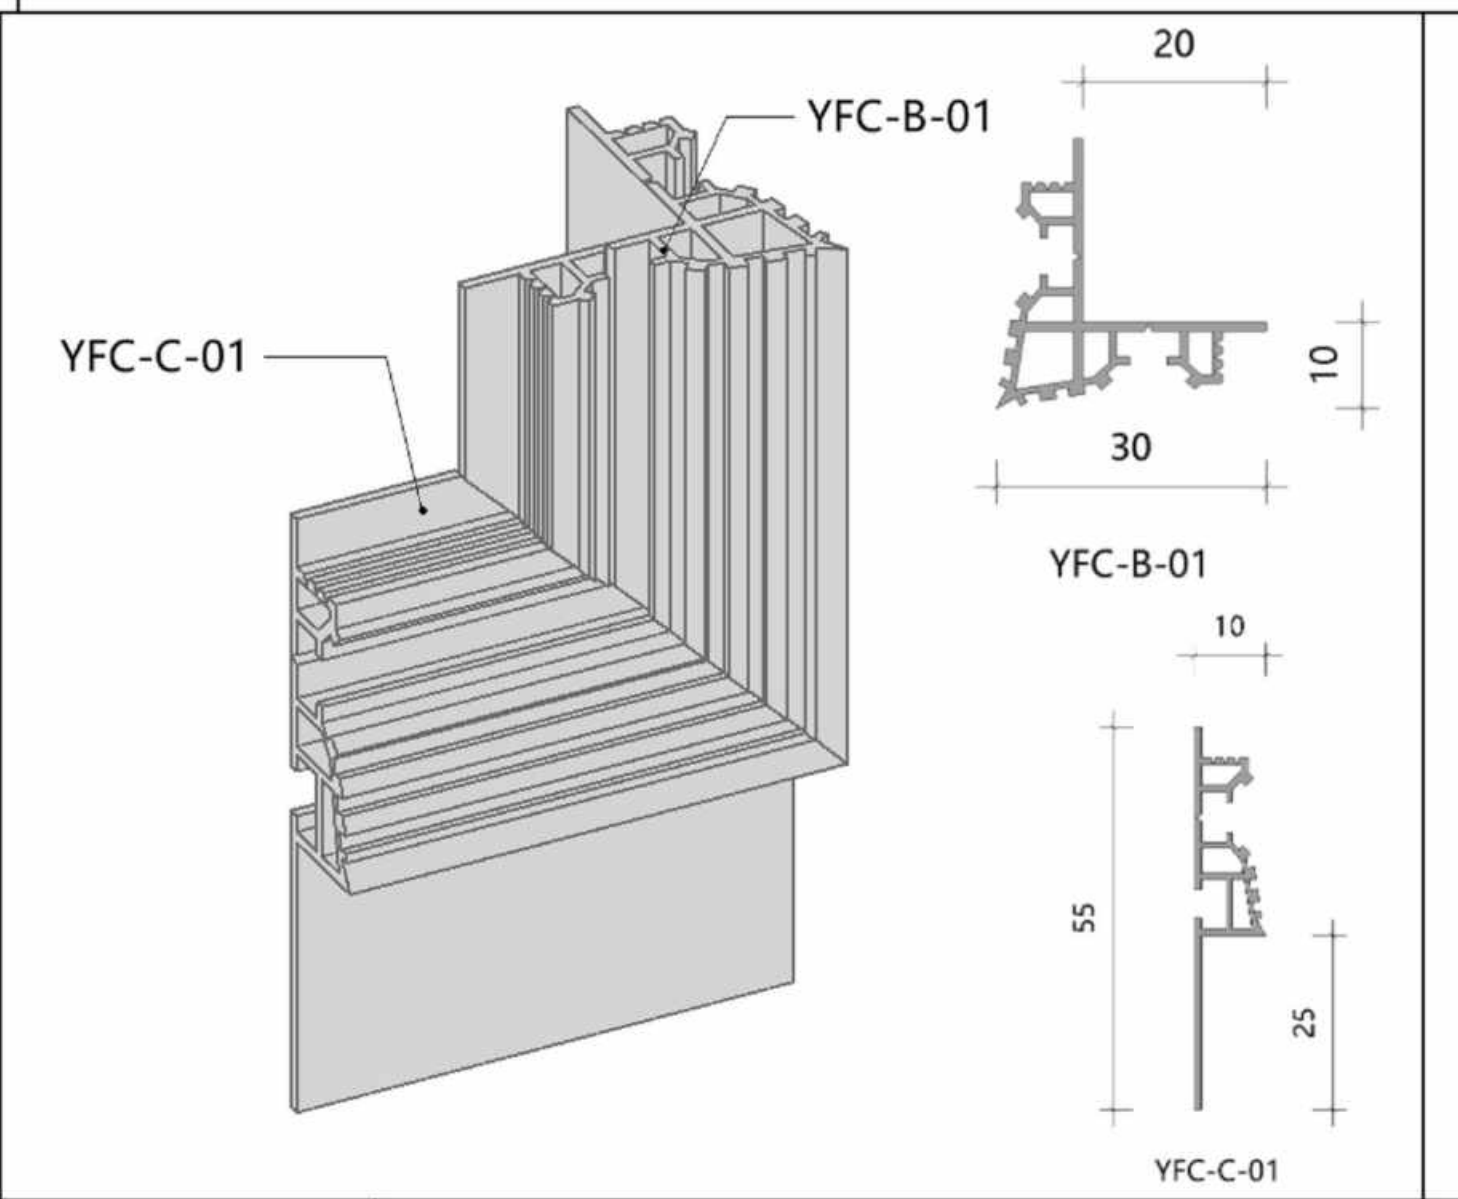
YFC-B-01
YFC-C-01
20
10
30
YFC-B-01
10
55
25
YFC-C-01

3D-07

转角铝型材-拼接跟通

转角数量：2

FIBORN

盖章

注释
Notes
1.本图纸如与现场尺寸有误，请施工人员与项目负责人联系。
2.施工前施工人员应认真查阅此图，如有不明确尺寸，按现场测量为准。
3.本图纸必须经甲乙双方认可并签字方可作为施工依据。

日期
Date 03/04/26

修订
Revision

1

项目
Project
潮映华岸府3-801

比例
Scale

客厅一

墙面及踢脚铝型材

图纸编号
Drawing No.
AP.EL-02

项目编号
Project No.

©2025

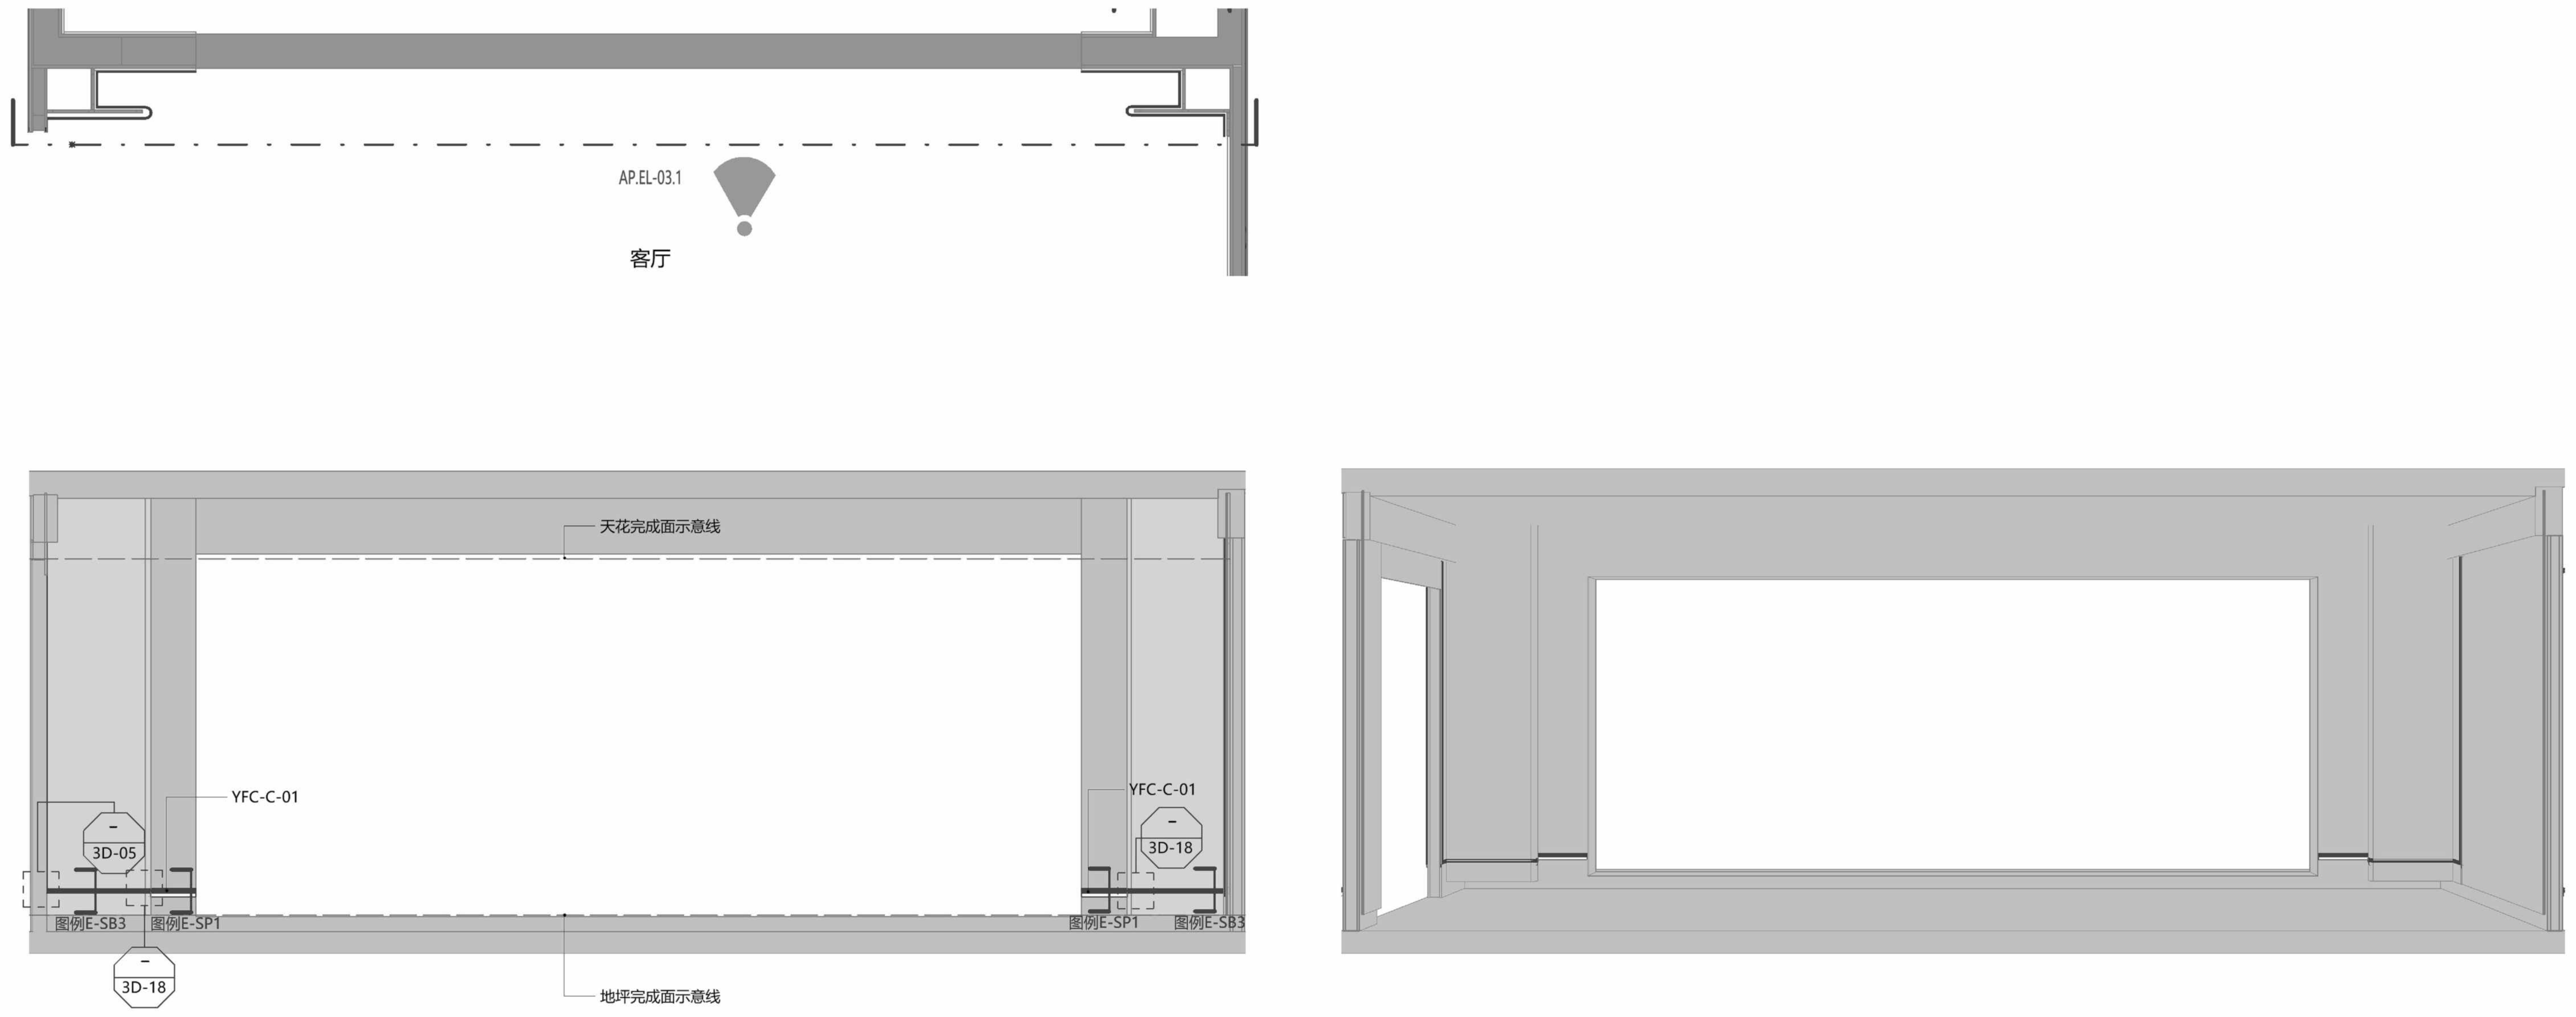
AP.EL-03.1
客厅
天花完成面示意线
YFC-C-01
3D-05
YFC-C-01
3D-18
图例E-SB3
图例E-SP1
图例E-SP1
图例E-SB3
3D-18
地坪完成面示意线

1

客厅二 墙面及踢脚铝型材立面图1

Scale比例 1 : 30@A2

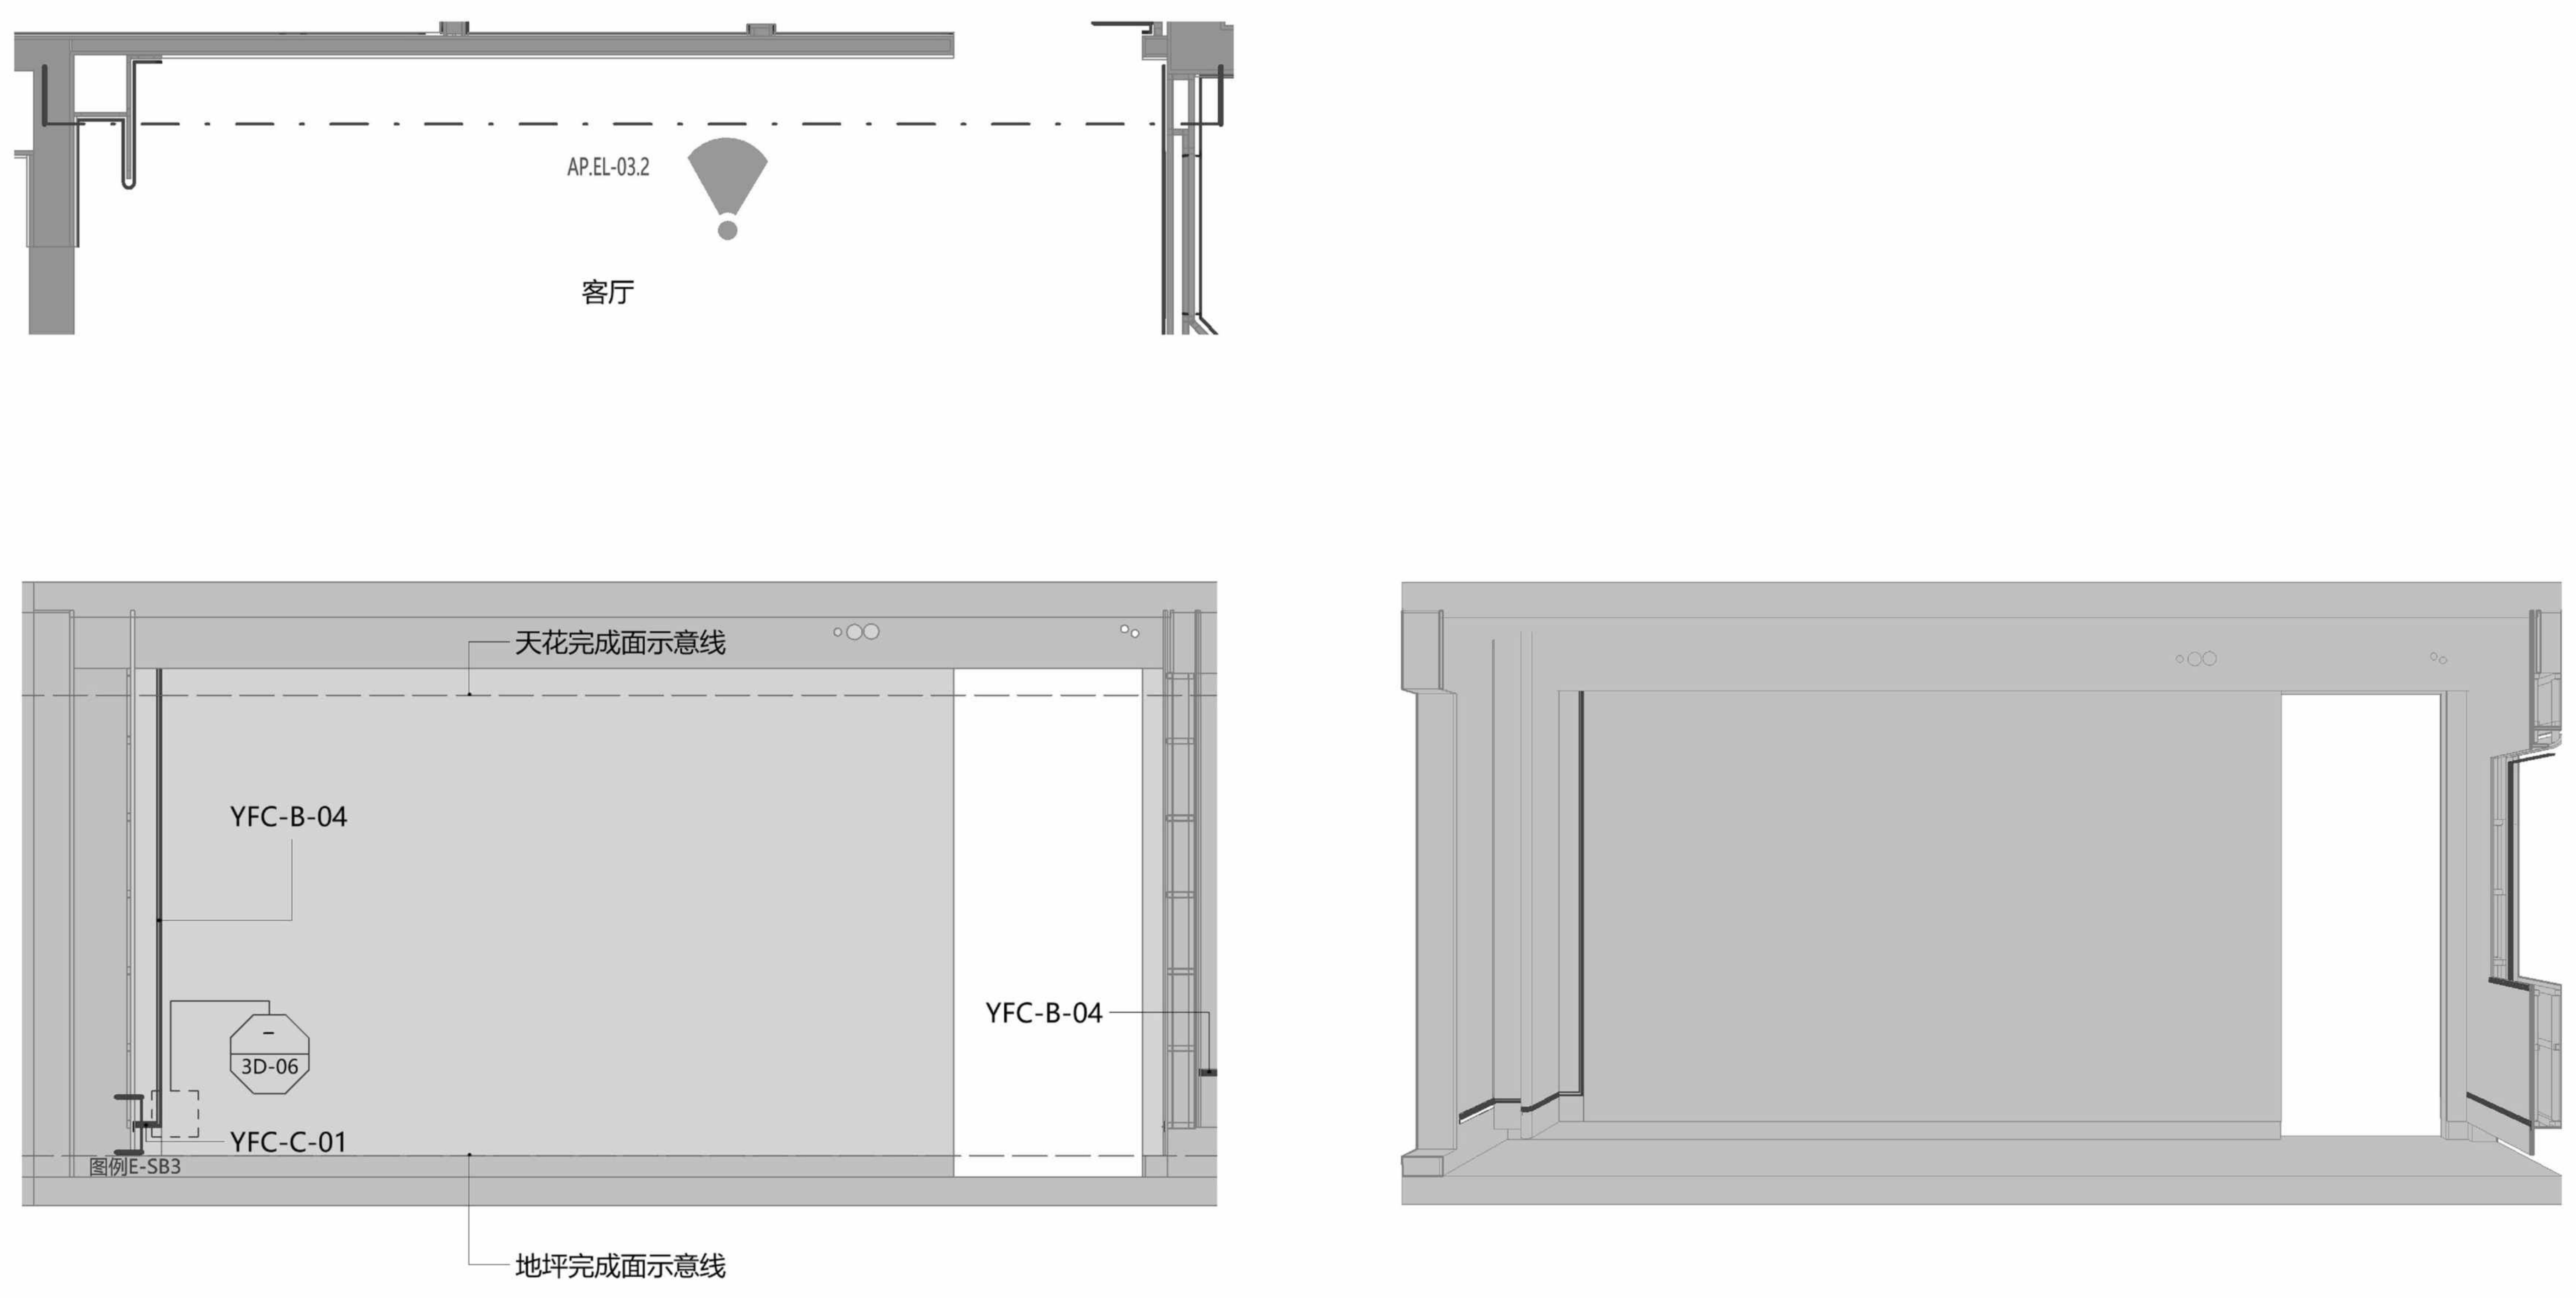
AP.EL-03.2
客厅
天花完成面示意线
YFC-B-04
3D-06
YFC-C-01
图例E-SB3
YFC-B-04
地坪完成面示意线

2

客厅二 墙面及踢脚铝型材立面图2

Scale比例 1 : 30@A2

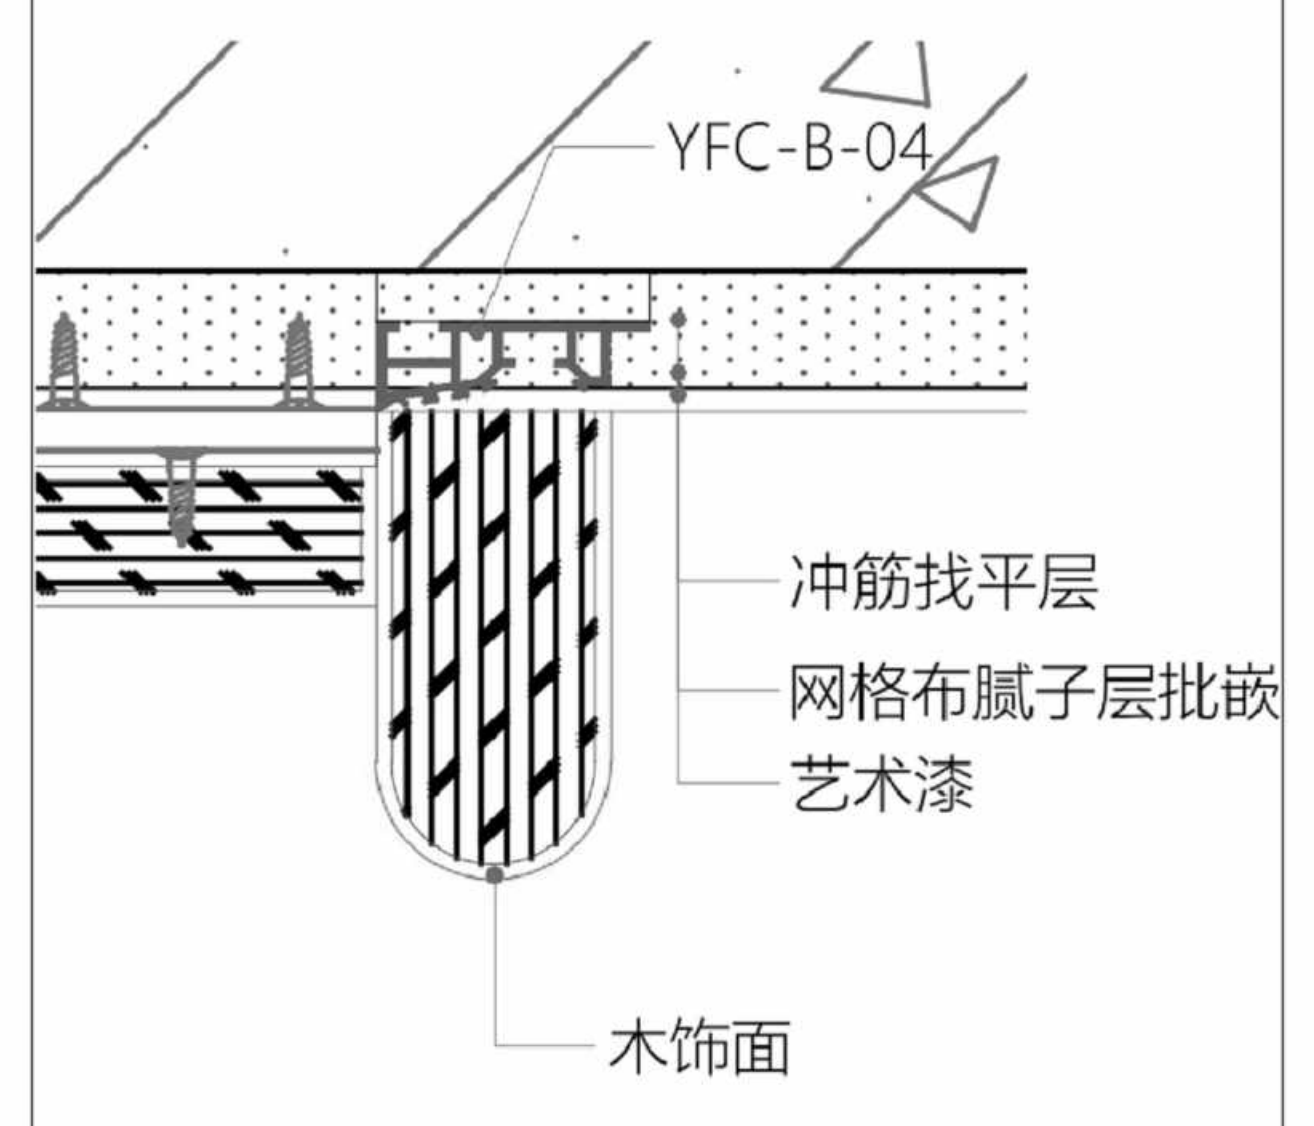
YFC-B-04
冲筋找平层
网格布腻子层批嵌
艺术漆
木饰面

图例A-P3

墙面-石膏基找平铝型材

Scale比例 1 : 1@A2

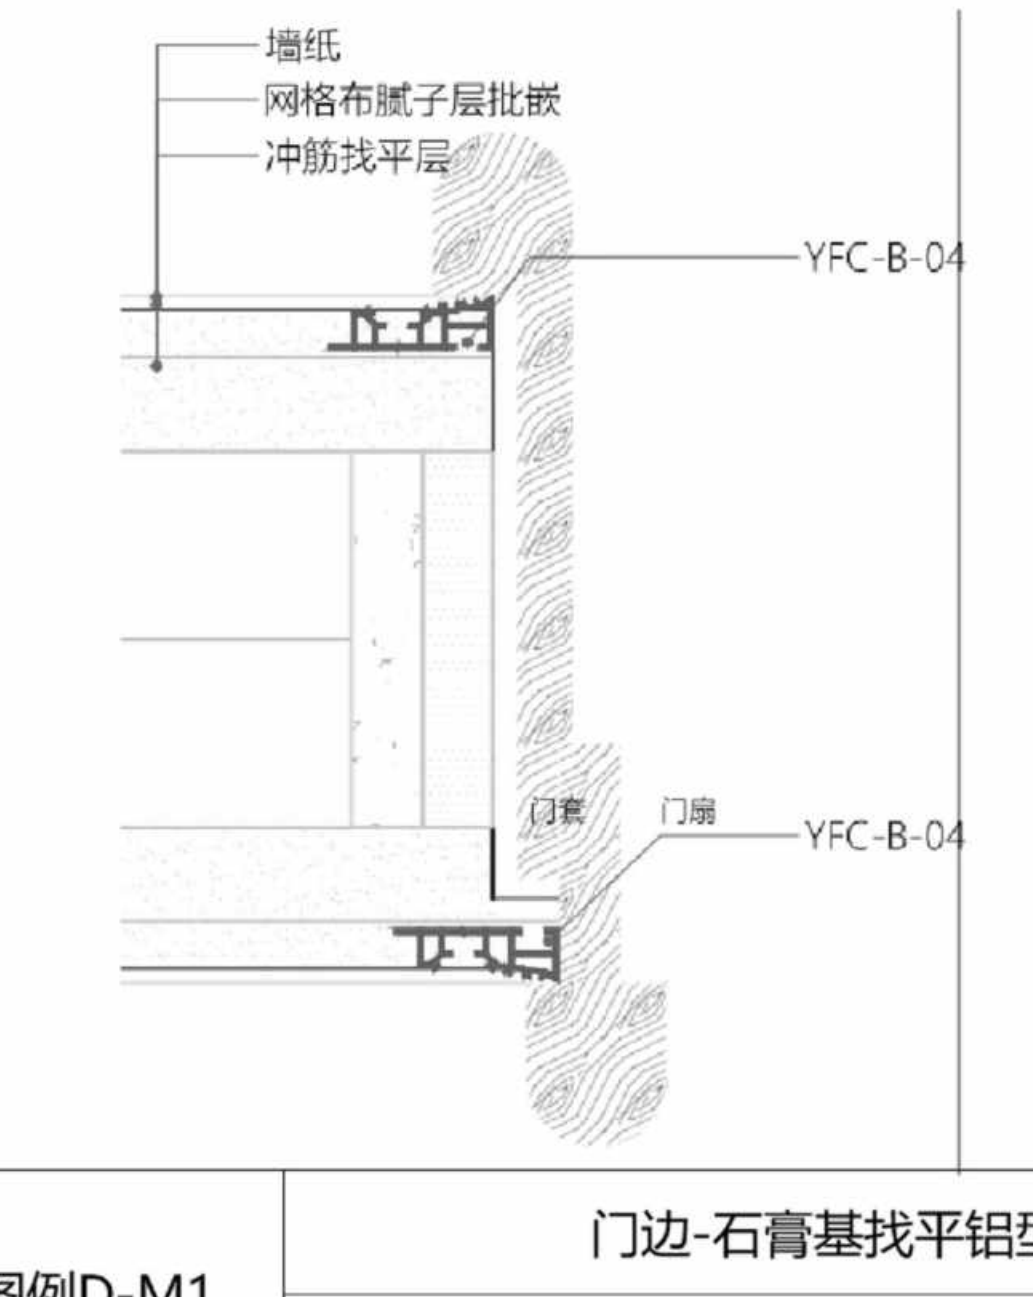
墙纸
网格布腻子层批嵌
冲筋找平层
YFC-B-04
门套
门扇
YFC-B-04

图例D-M1

门边-石膏基找平铝型材

Scale比例 1 : 1@A2

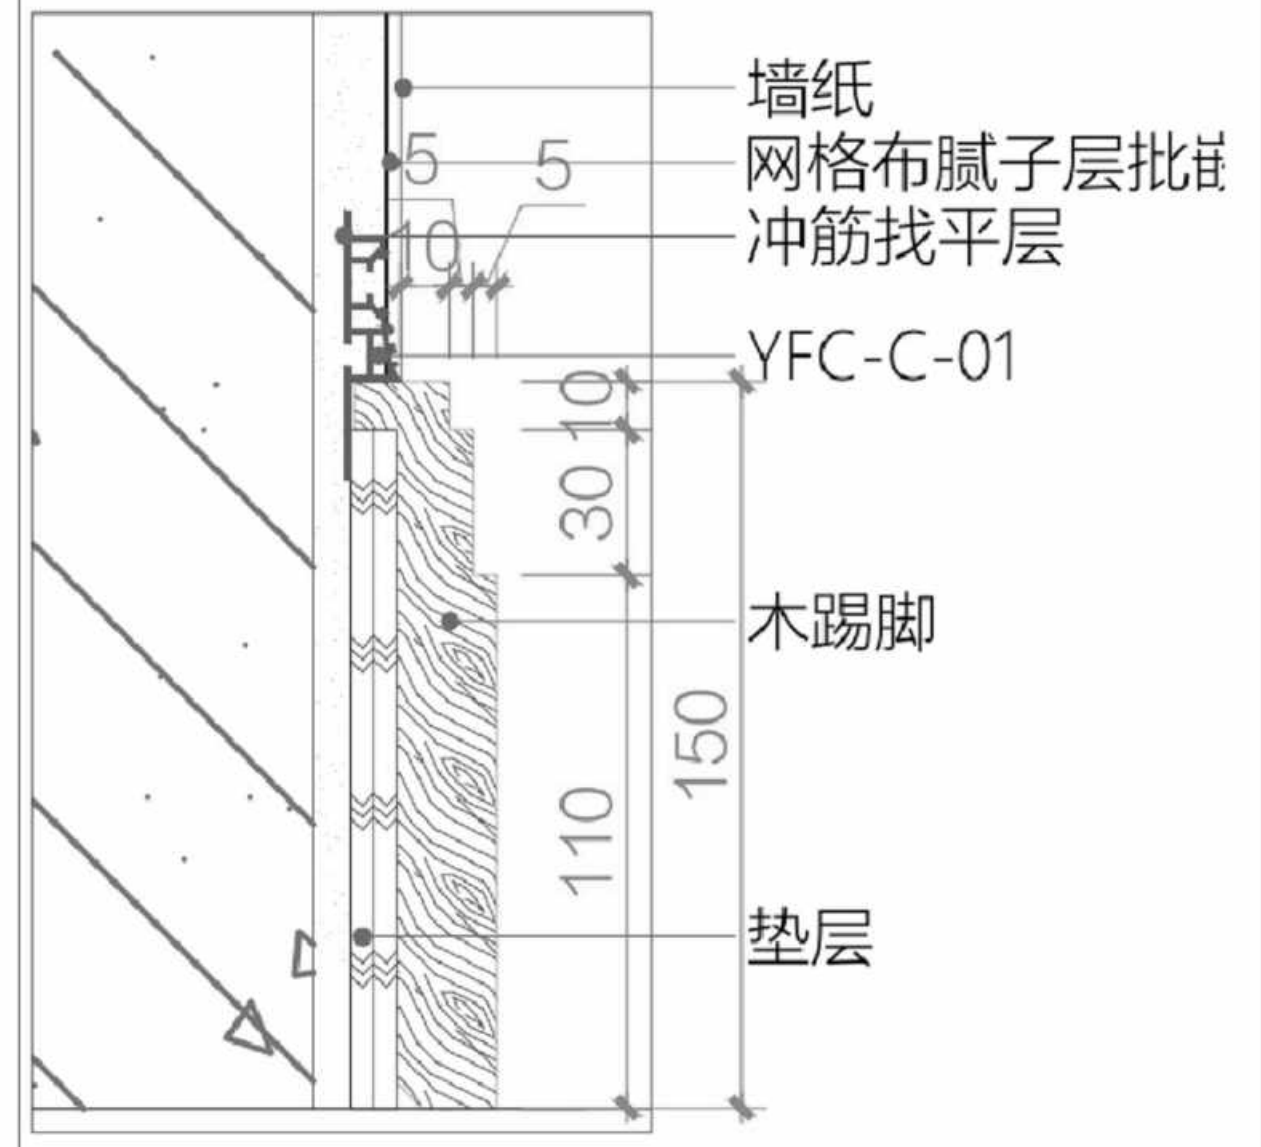
墙纸
5
5
网格布腻子层批嵌
10
冲筋找平层
YFC-C-01
10
30
木踢脚
150
110
垫层

图例E-SP1

门边-石膏基找平铝型材

Scale比例 1 : 1@A2

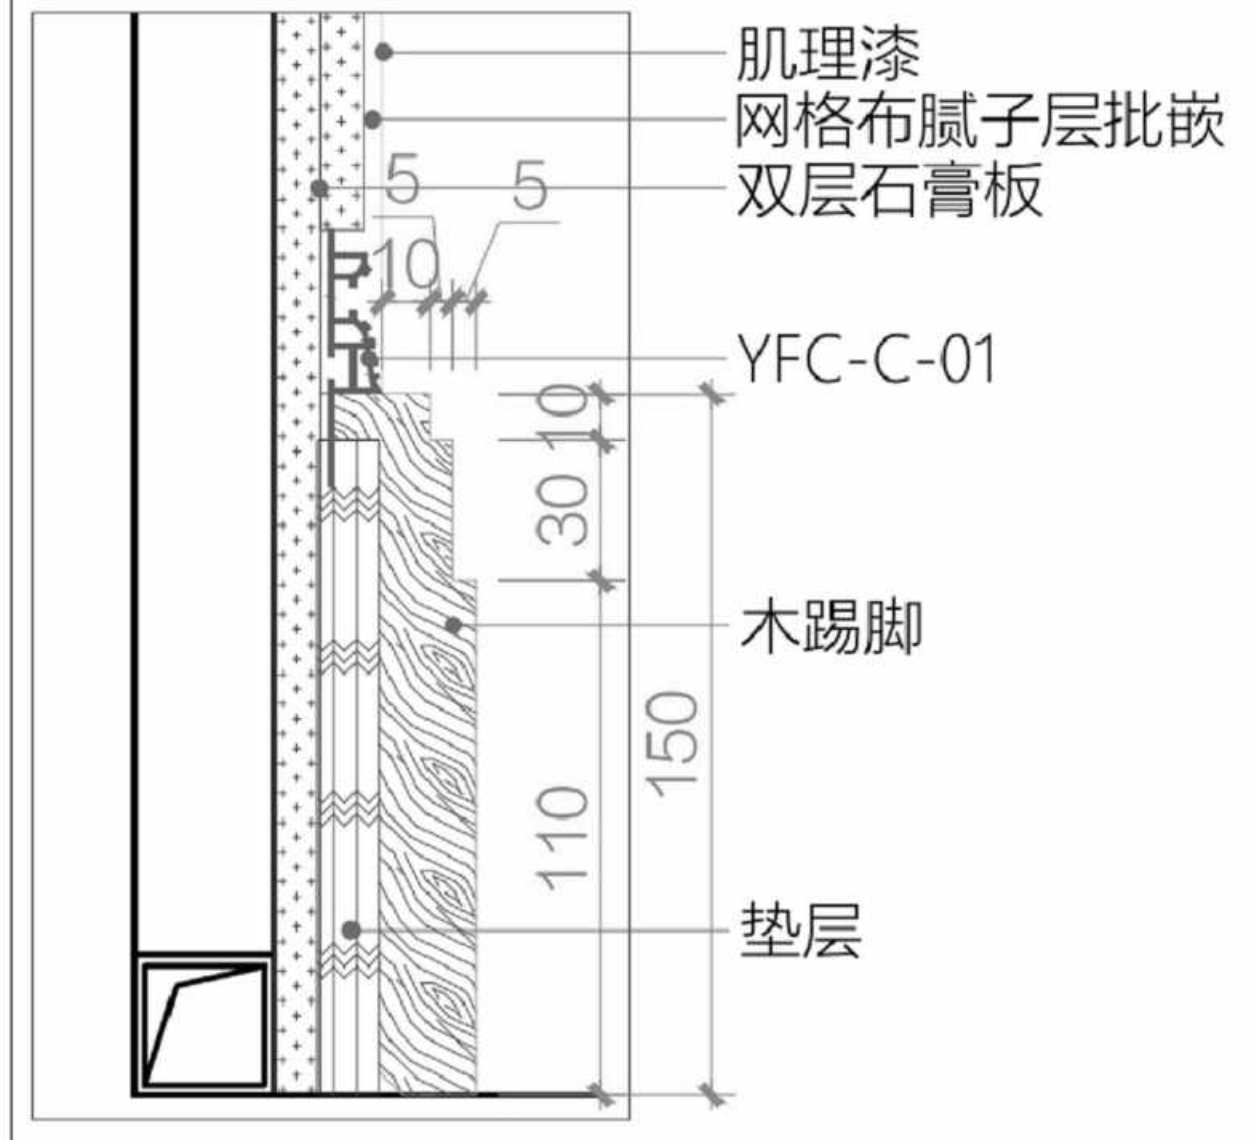
肌理漆
网格布腻子层批嵌
5
5
双层石膏板
10
YFC-C-01
10
30
木踢脚
150
110
垫层

图例E-SB3

踢脚-石膏基找平铝型材

Scale比例 1 : 1@A2

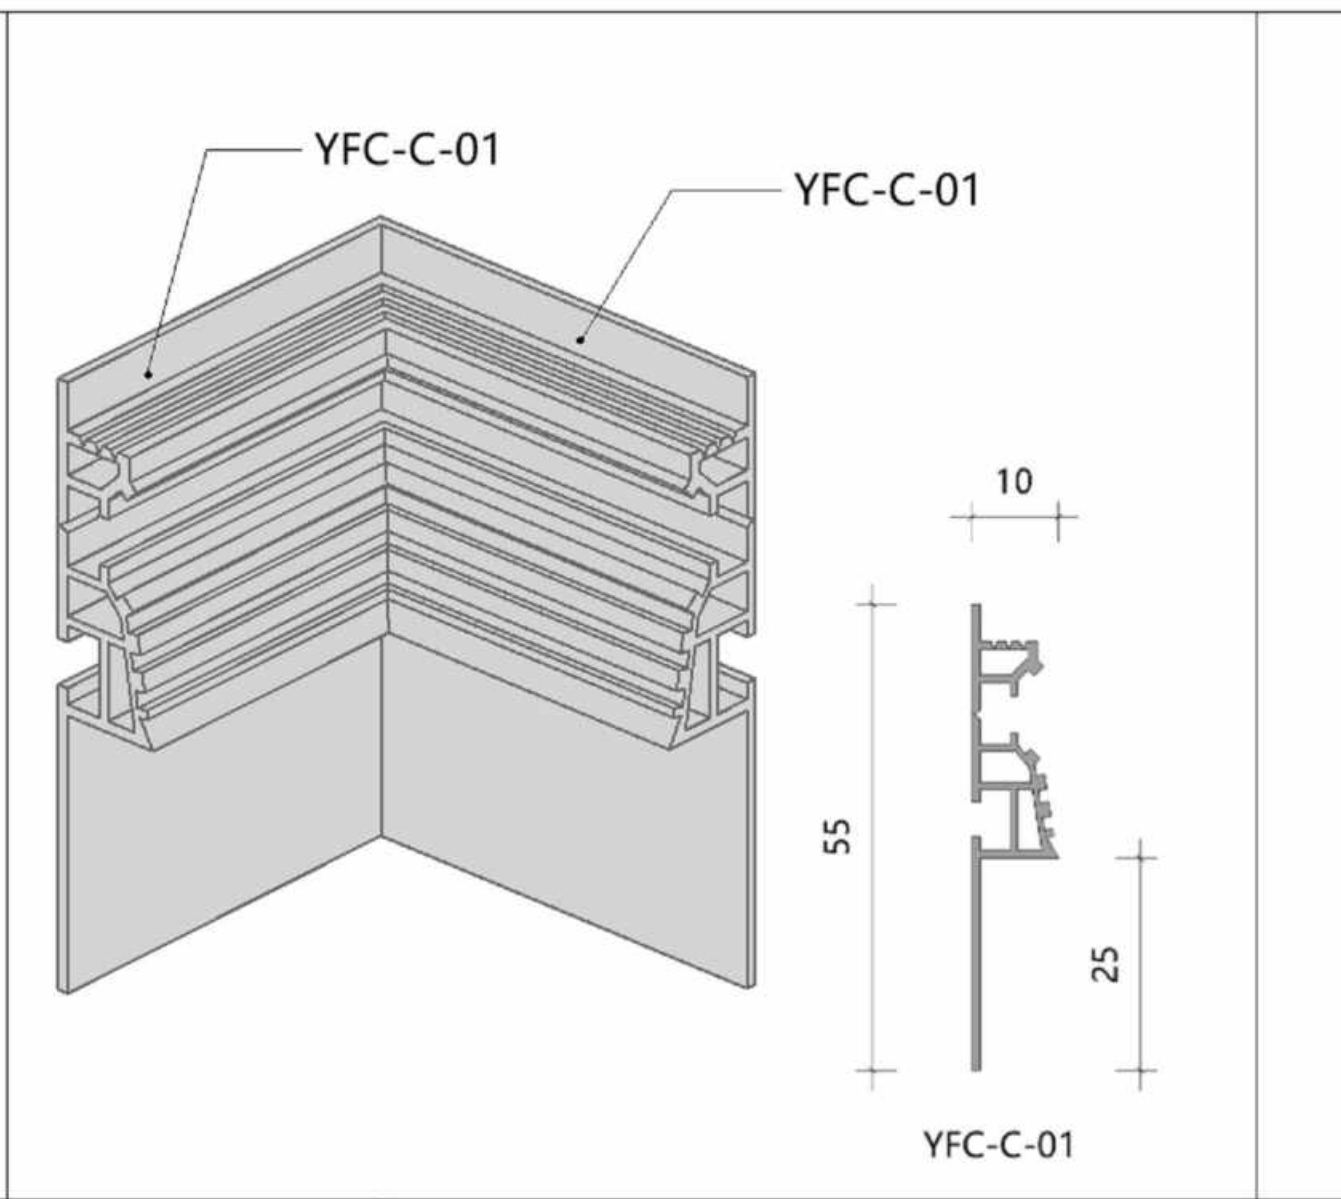
YFC-C-01
YFC-C-01
10
55
25
YFC-C-01

3D-05

转角铝型材-拼接跟通

转角数量：2

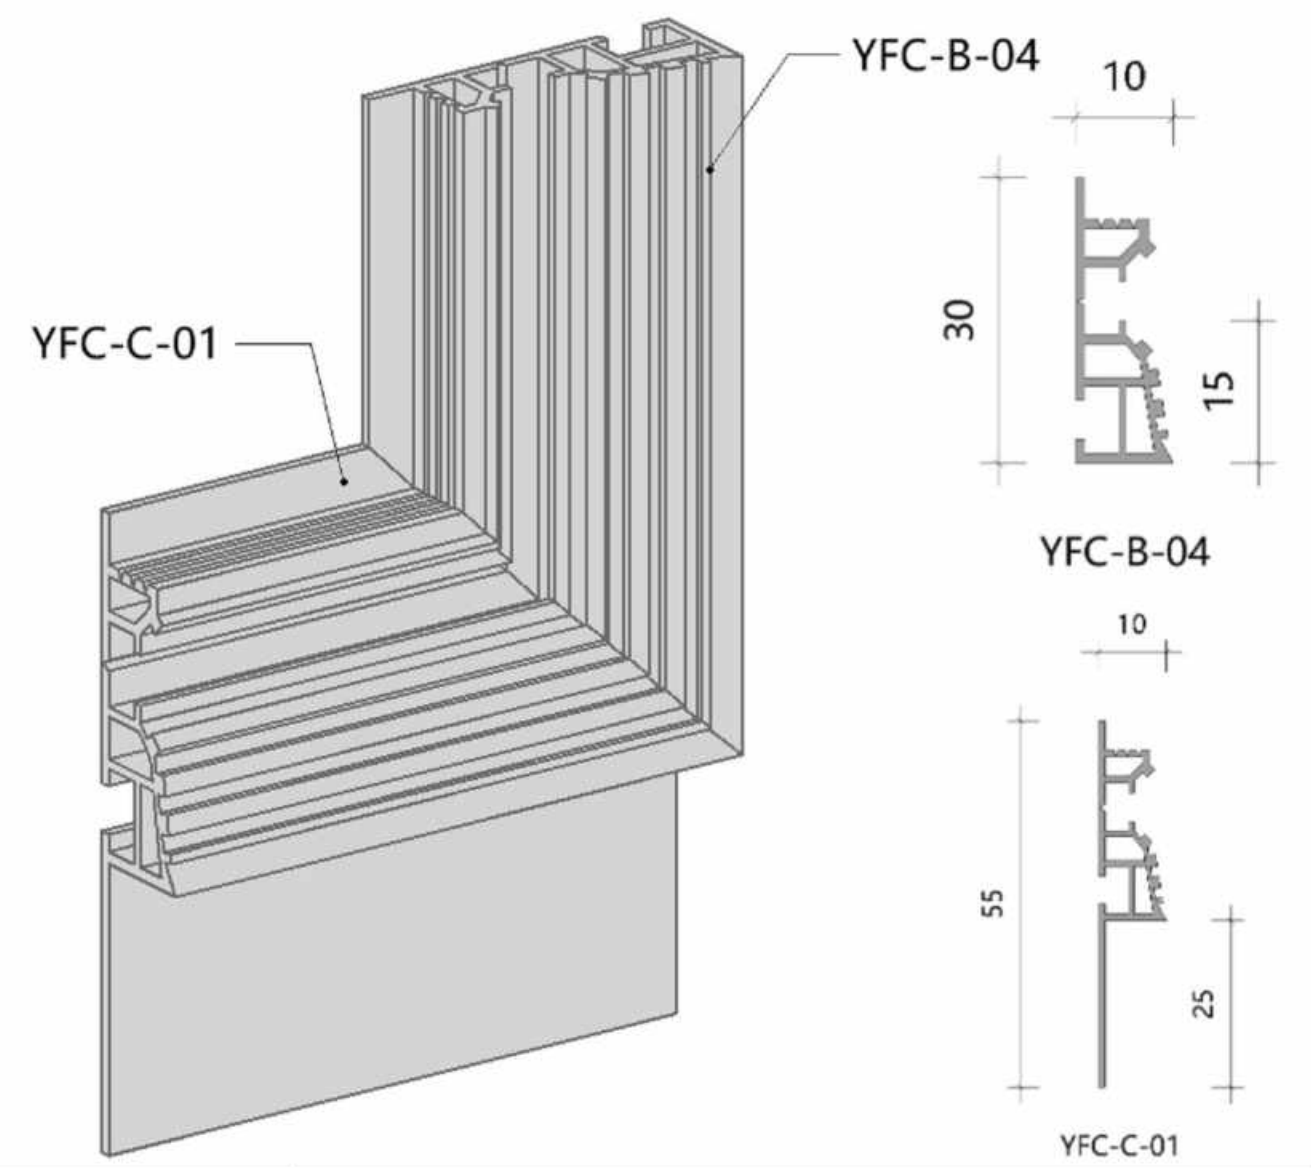
YFC-B-04
10
YFC-C-01
30
15
YFC-B-04
10
55
25
YFC-C-01

3D-06

转角铝型材-拼接跟通

转角数量：1

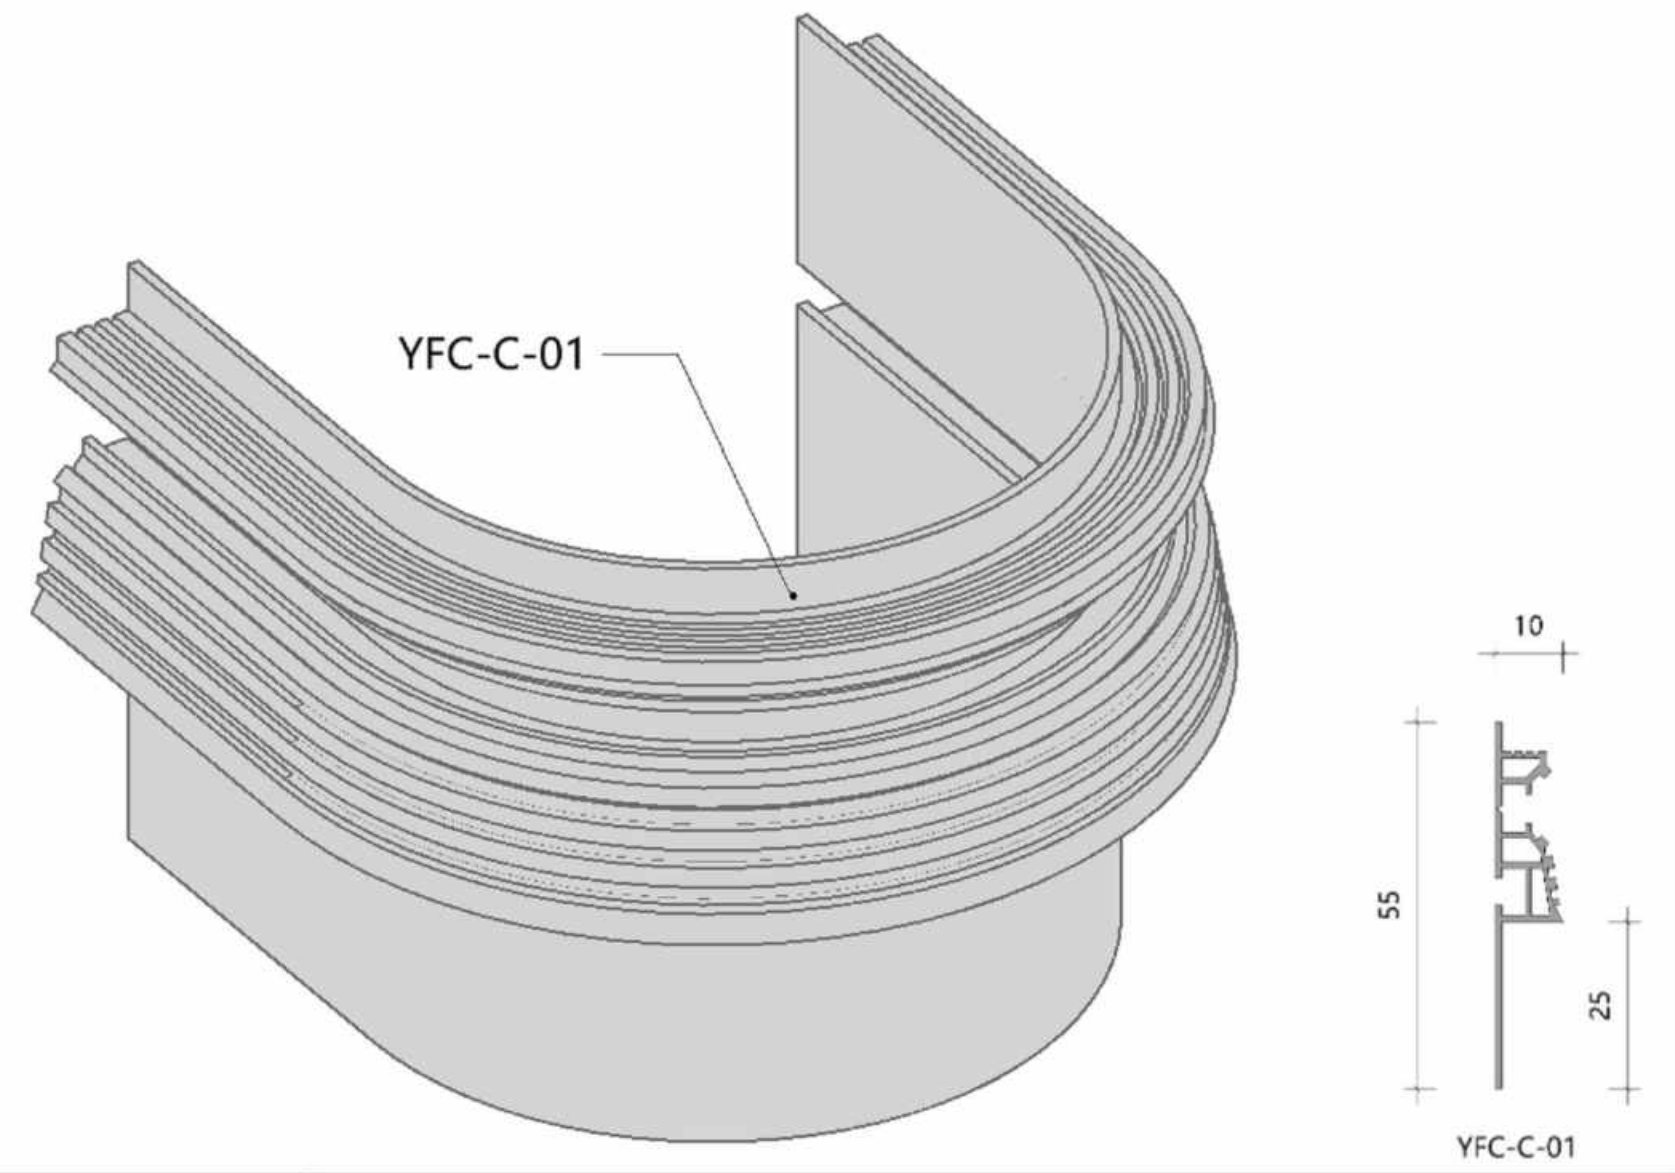
YFC-C-01
10
55
25
YFC-C-01

3D-18

转角铝型材-拼接跟通

转角数量：2

FIBORN

盖章

注释
Notes
1.本图纸如与现场尺寸有误，请施工人员与项目负责人联系。
2.施工前施工人员应认真查阅此图，如有不明确尺寸，按现场测量为准。
3.本图纸必须经甲乙双方认可并签字方可作为施工依据。

日期
Date 03/04/26

修订
Revision
1

项目
Project
潮映华岸府3-801

比例
Scale

客厅二
墙面及踢脚铝型材

图纸编号
Drawing No.
AP.EL-03

项目编号
Project No.

©2025

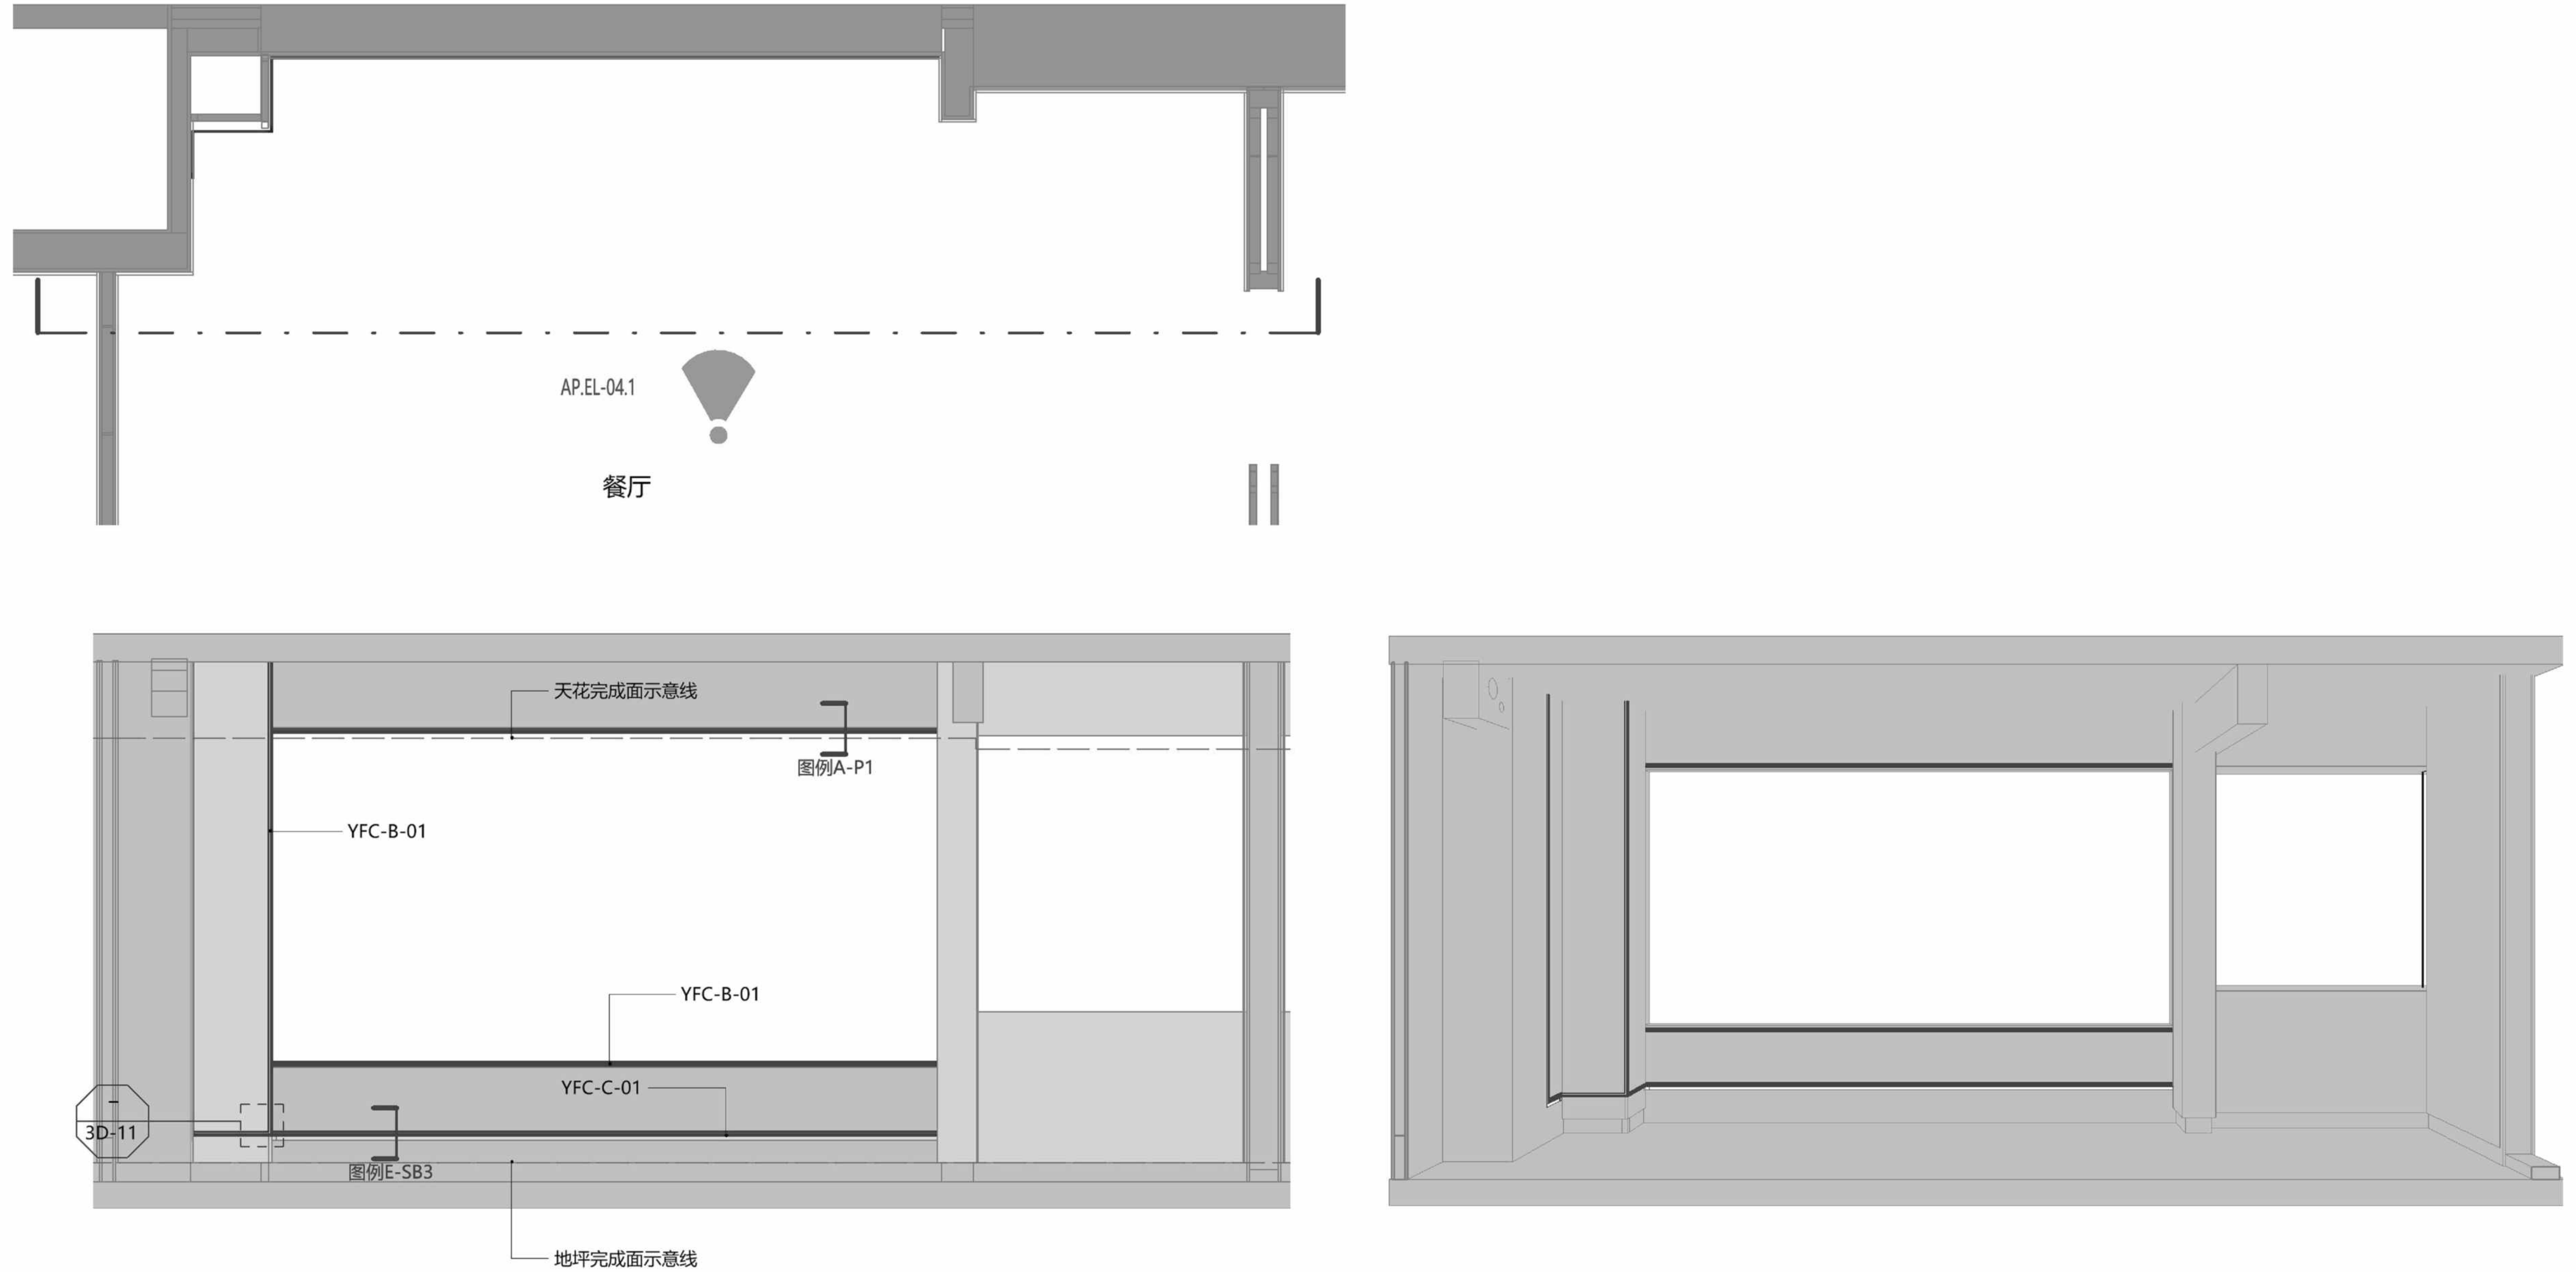
AP.EL-04.1
餐厅
天花完成面示意线
图例A-P1
YFC-B-01
YFC-B-01
YFC-C-01
3D-11
图例E-SB3
地坪完成面示意线

1

餐厅一 墙面及踢脚铝型材立面图1

Scale比例 1：30@A2

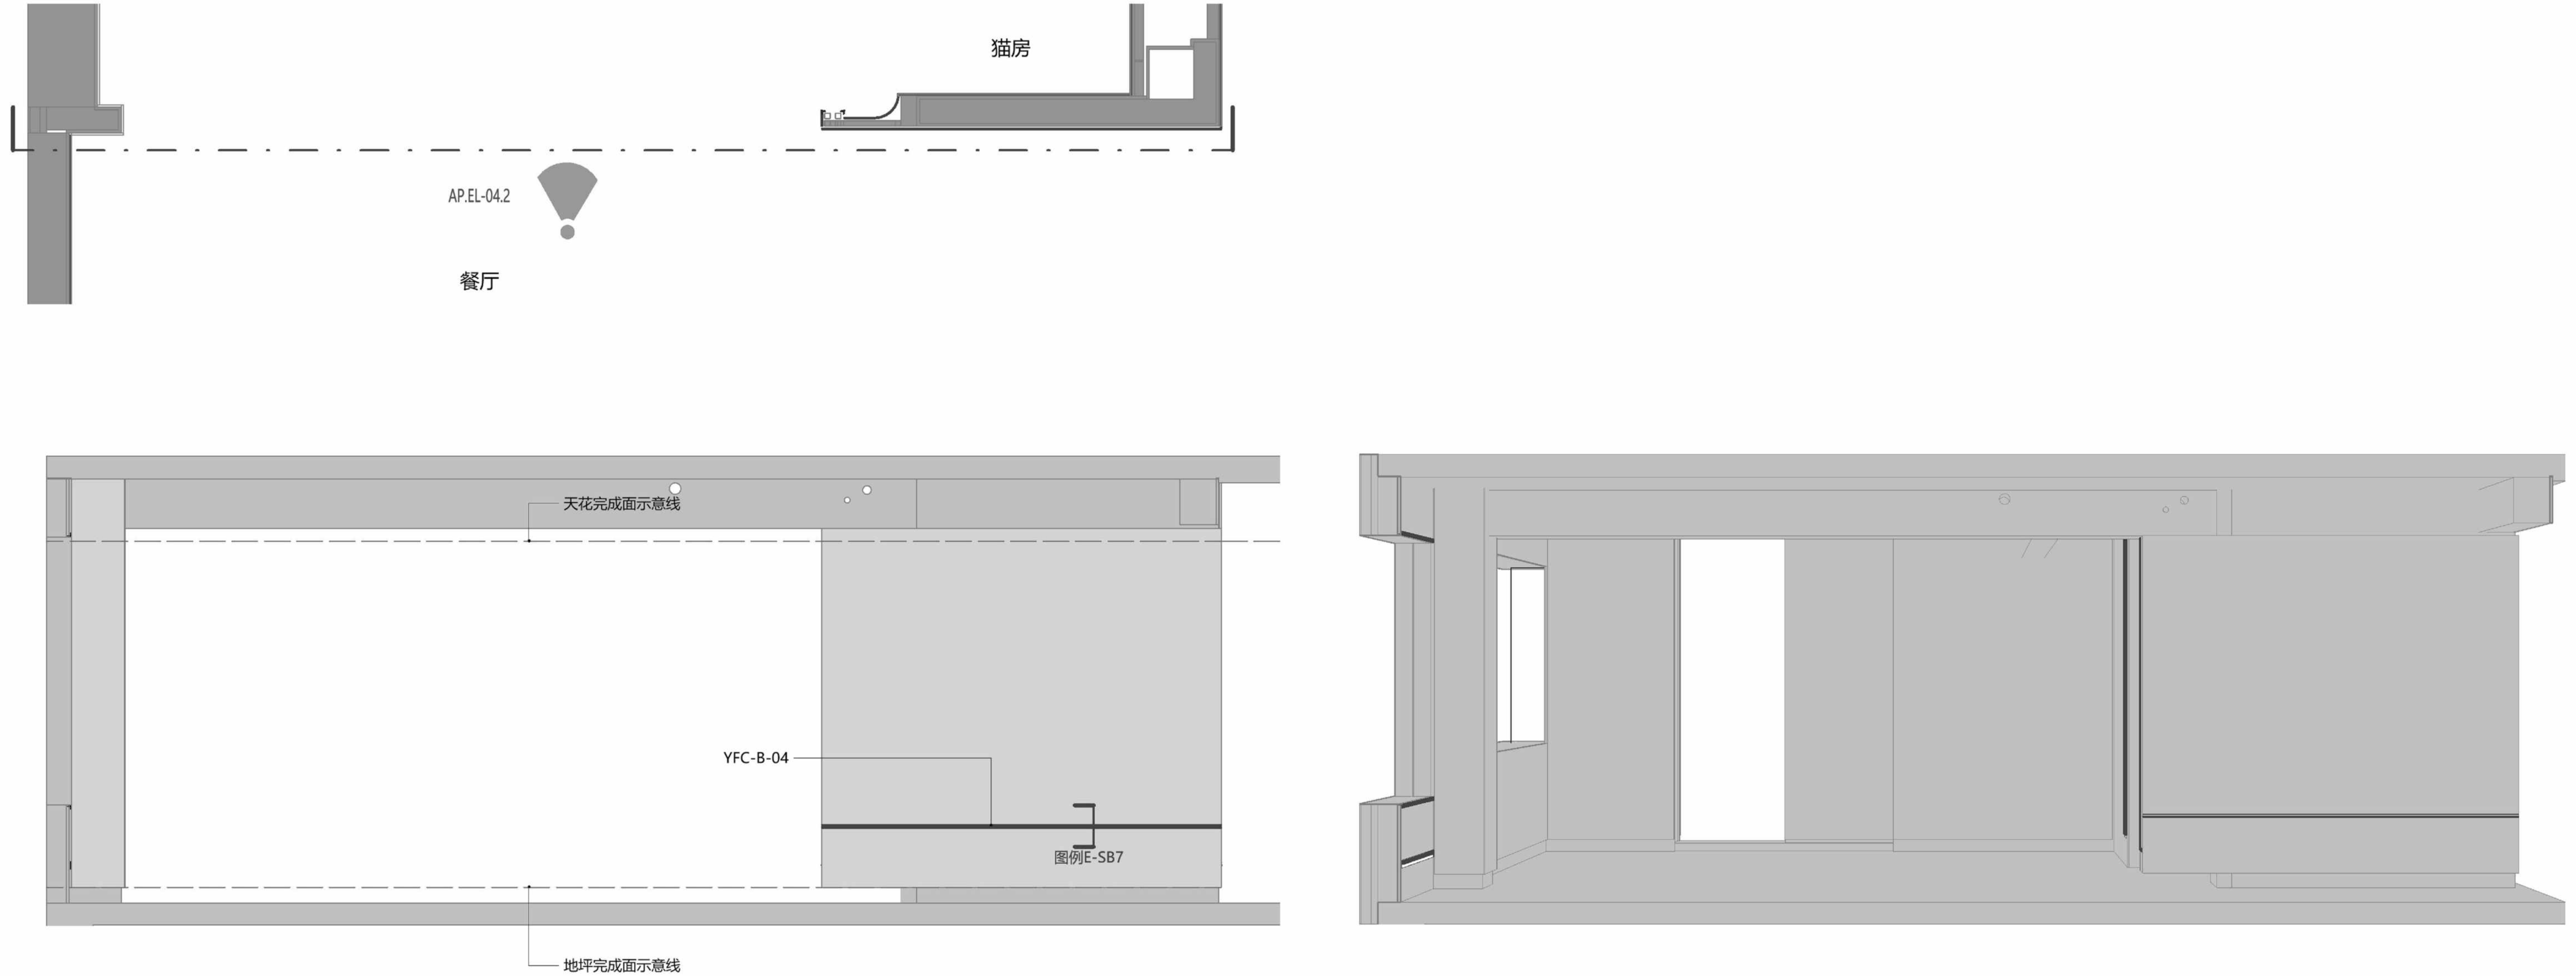
猫房
AP.EL-04.2
餐厅
天花完成面示意线
YFC-B-04
图例E-SB7
地坪完成面示意线

2

餐厅一 墙面及踢脚铝型材立面图2

Scale比例 1：30@A2

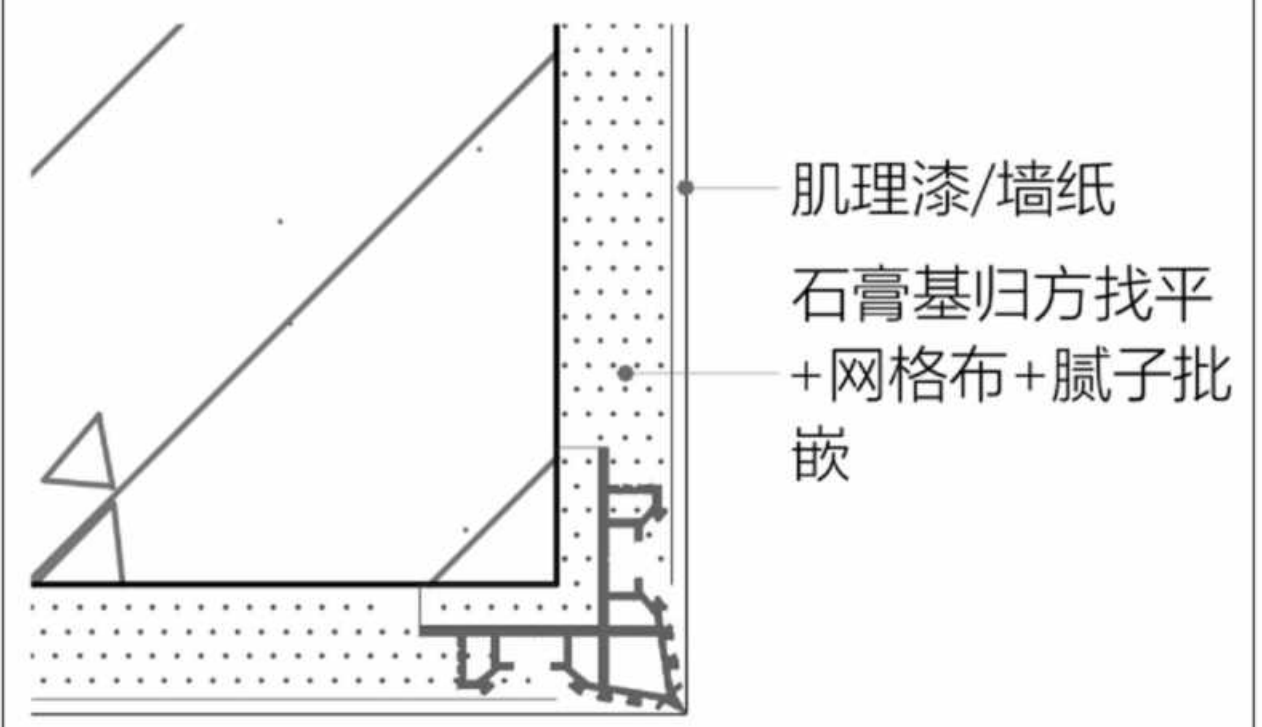
肌理漆/墙纸
石膏基归方找平+网格布+腻子批嵌

图例A-P1

墙面-石膏基找平铝型材

Scale比例 1：1@A2

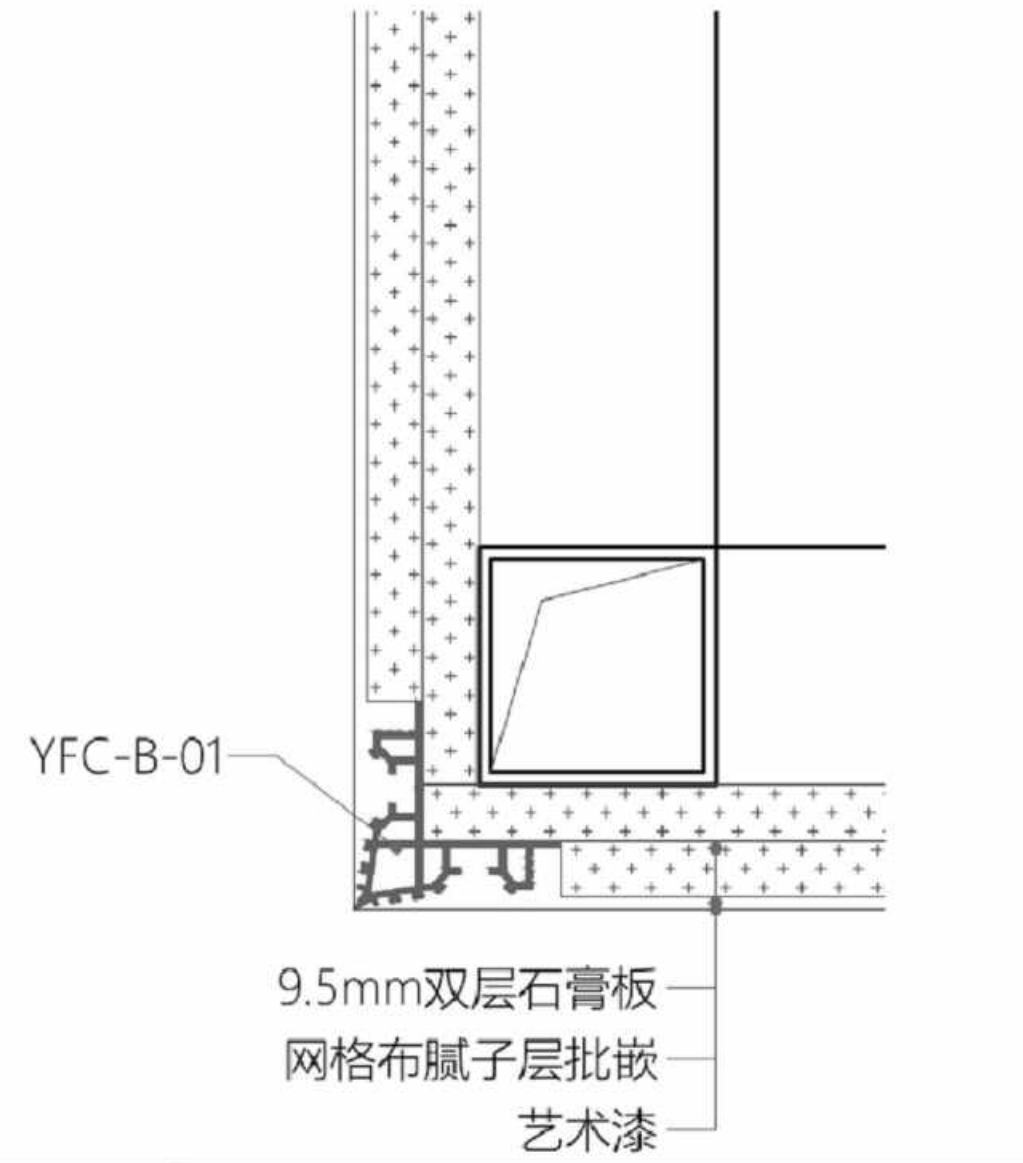
YFC-B-01
9.5mm双层石膏板
网格布腻子层批嵌
艺术漆

图例C-PB1

墙面-石膏基找平铝型材

Scale比例 1：1@A2

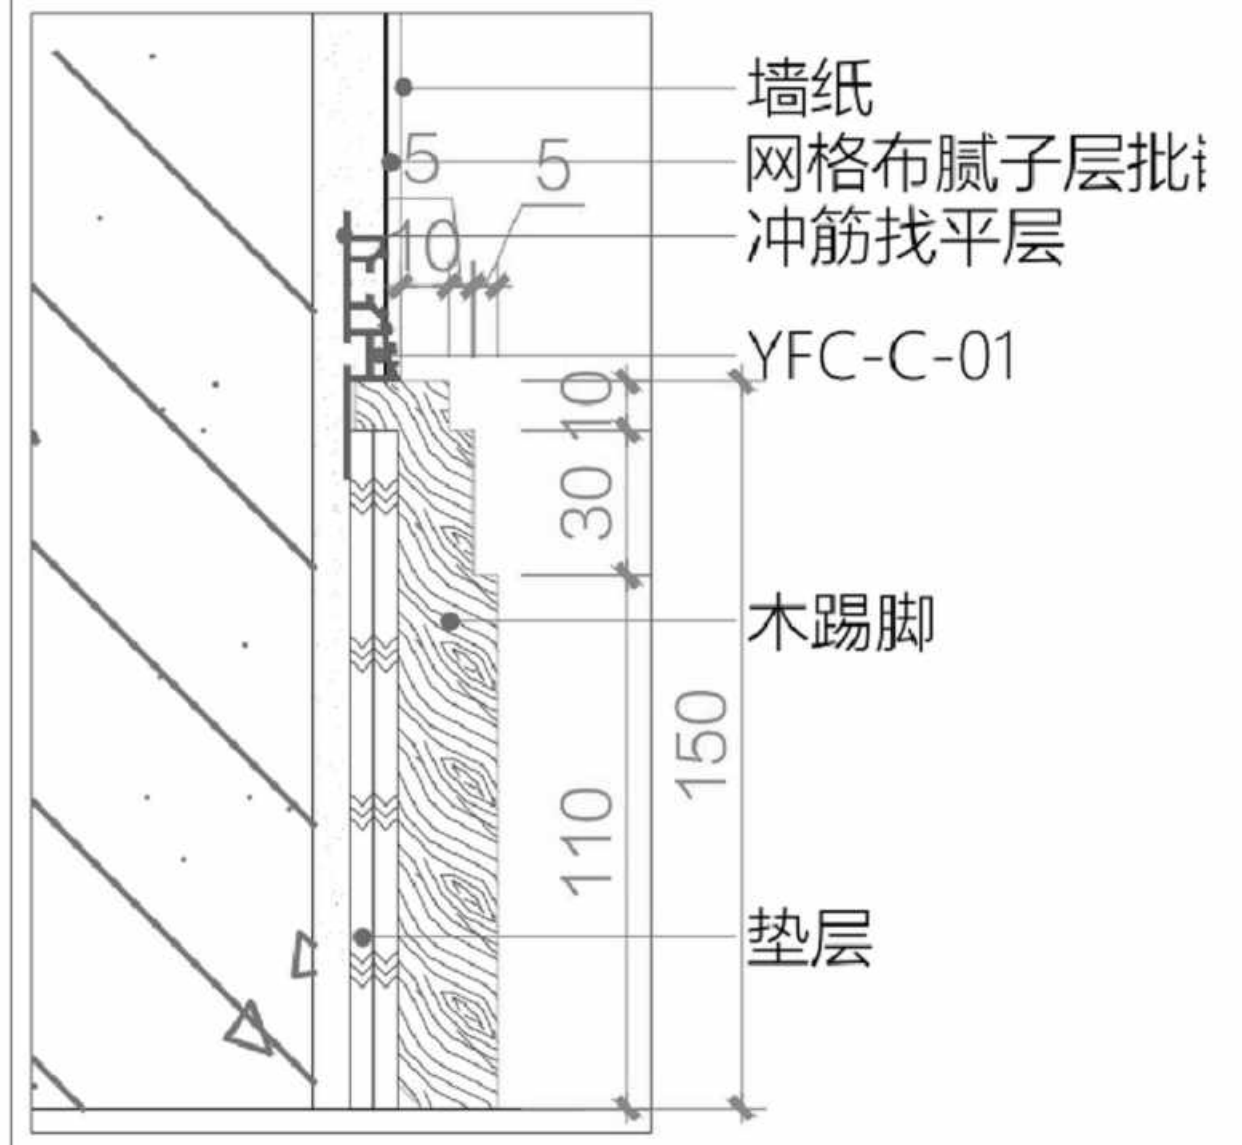
墙纸
网格布腻子层批i
冲筋找平层
5
5
10
YFC-C-01
10
30
110
150
木踢脚
垫层

图例E-SP1

踢脚-石膏基找平铝型材

Scale比例 1：1@A2

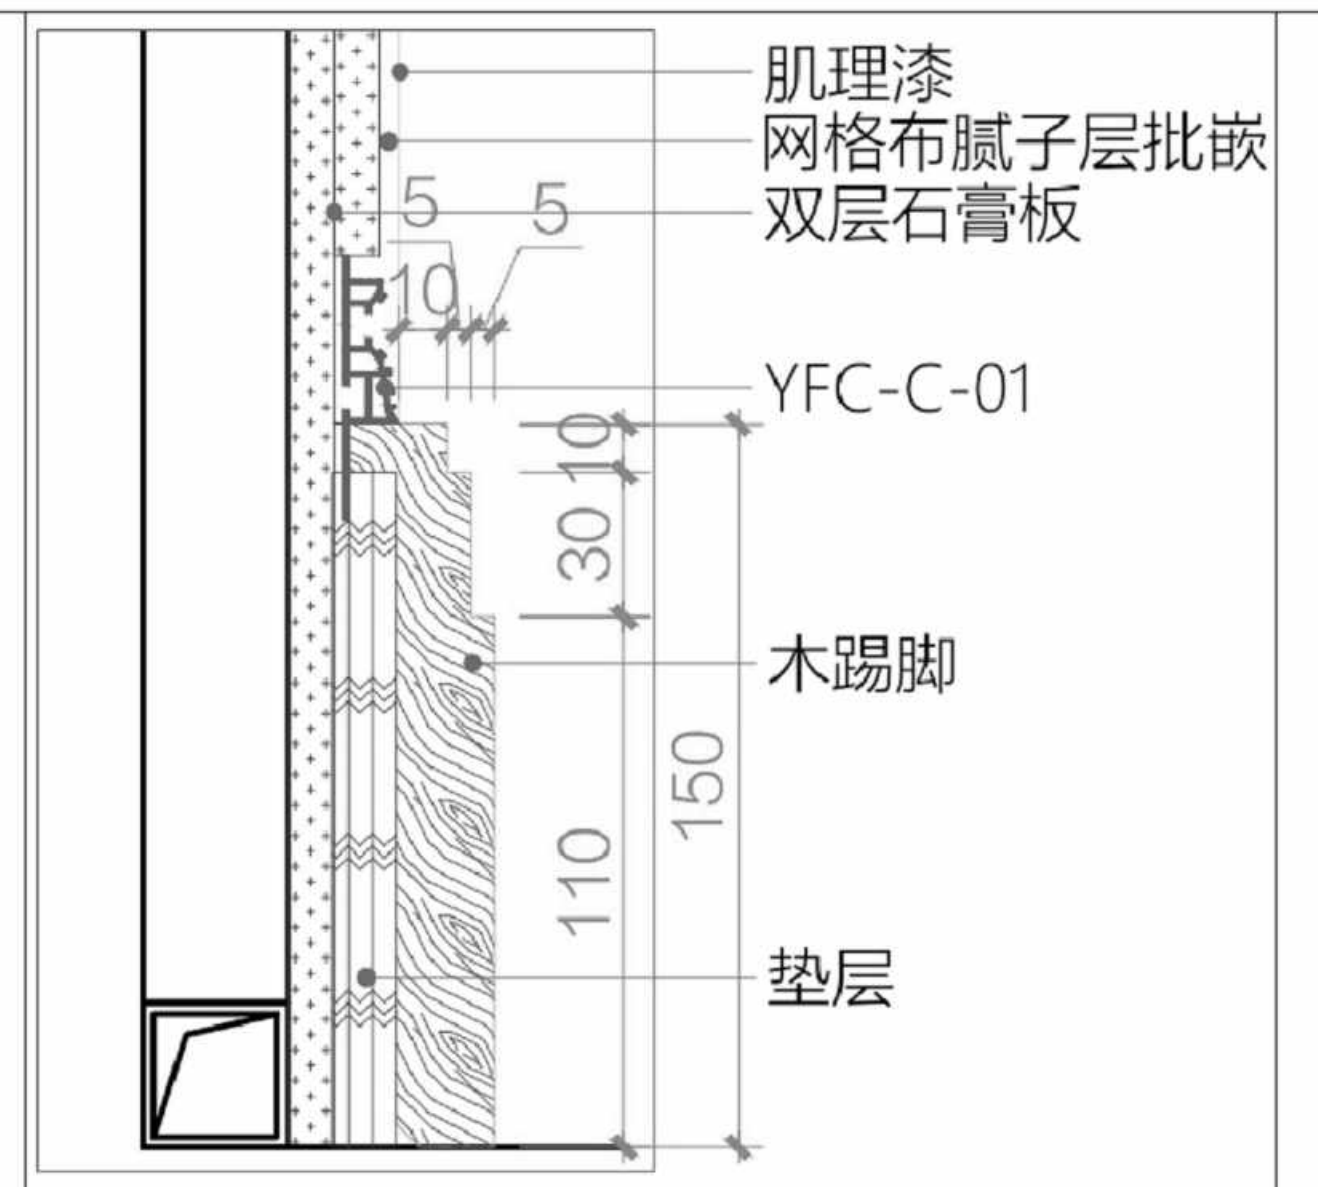
肌理漆
网格布腻子层批嵌
双层石膏板
5
5
10
YFC-C-01
10
30
110
150
木踢脚
垫层

图例E-SB3

踢脚-石膏基找平铝型材

Scale比例 1：1@A2

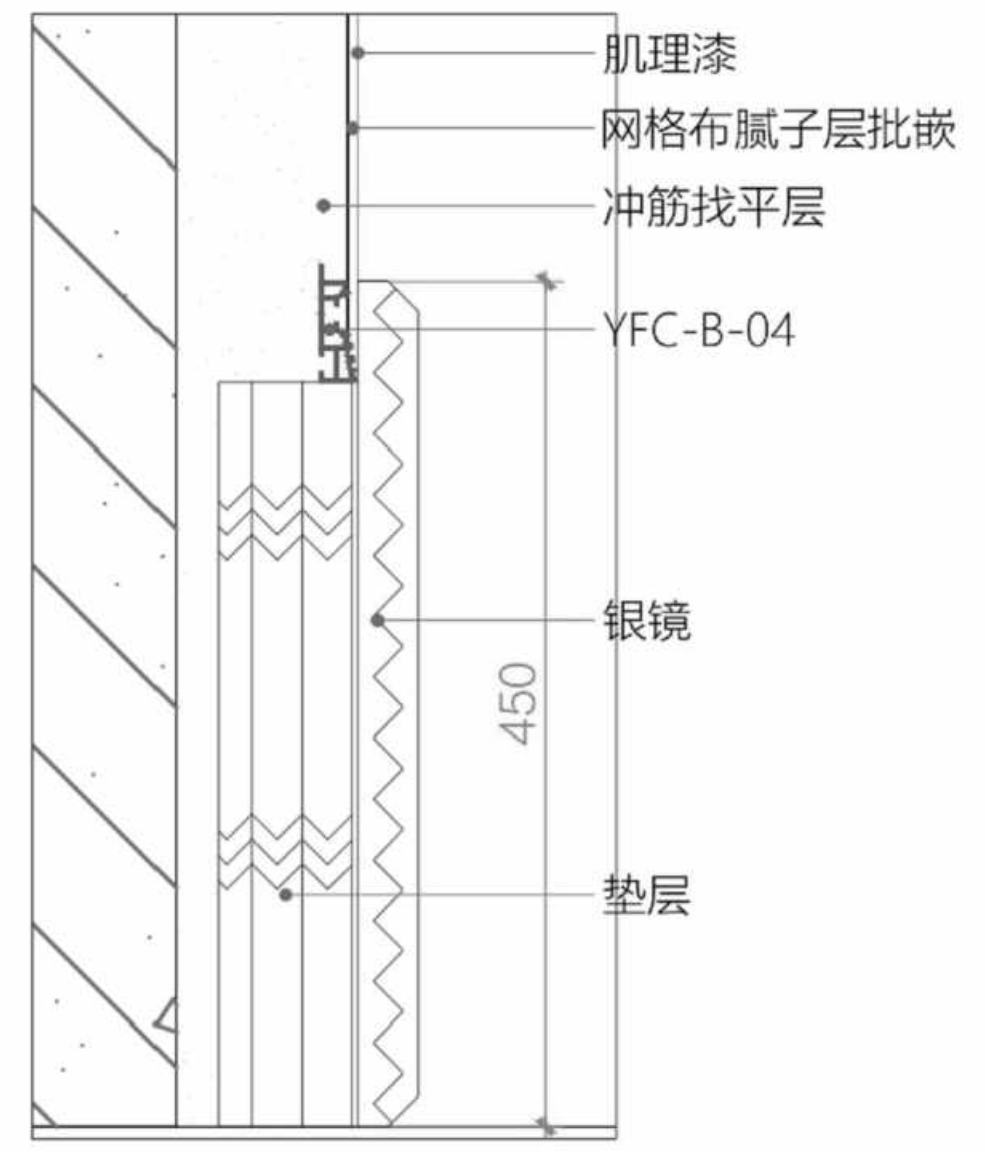
肌理漆
网格布腻子层批嵌
冲筋找平层
YFC-B-04
银镜
450
垫层

图例E-SB7

踢脚-石膏基找平铝型材

Scale比例 1：1@A2

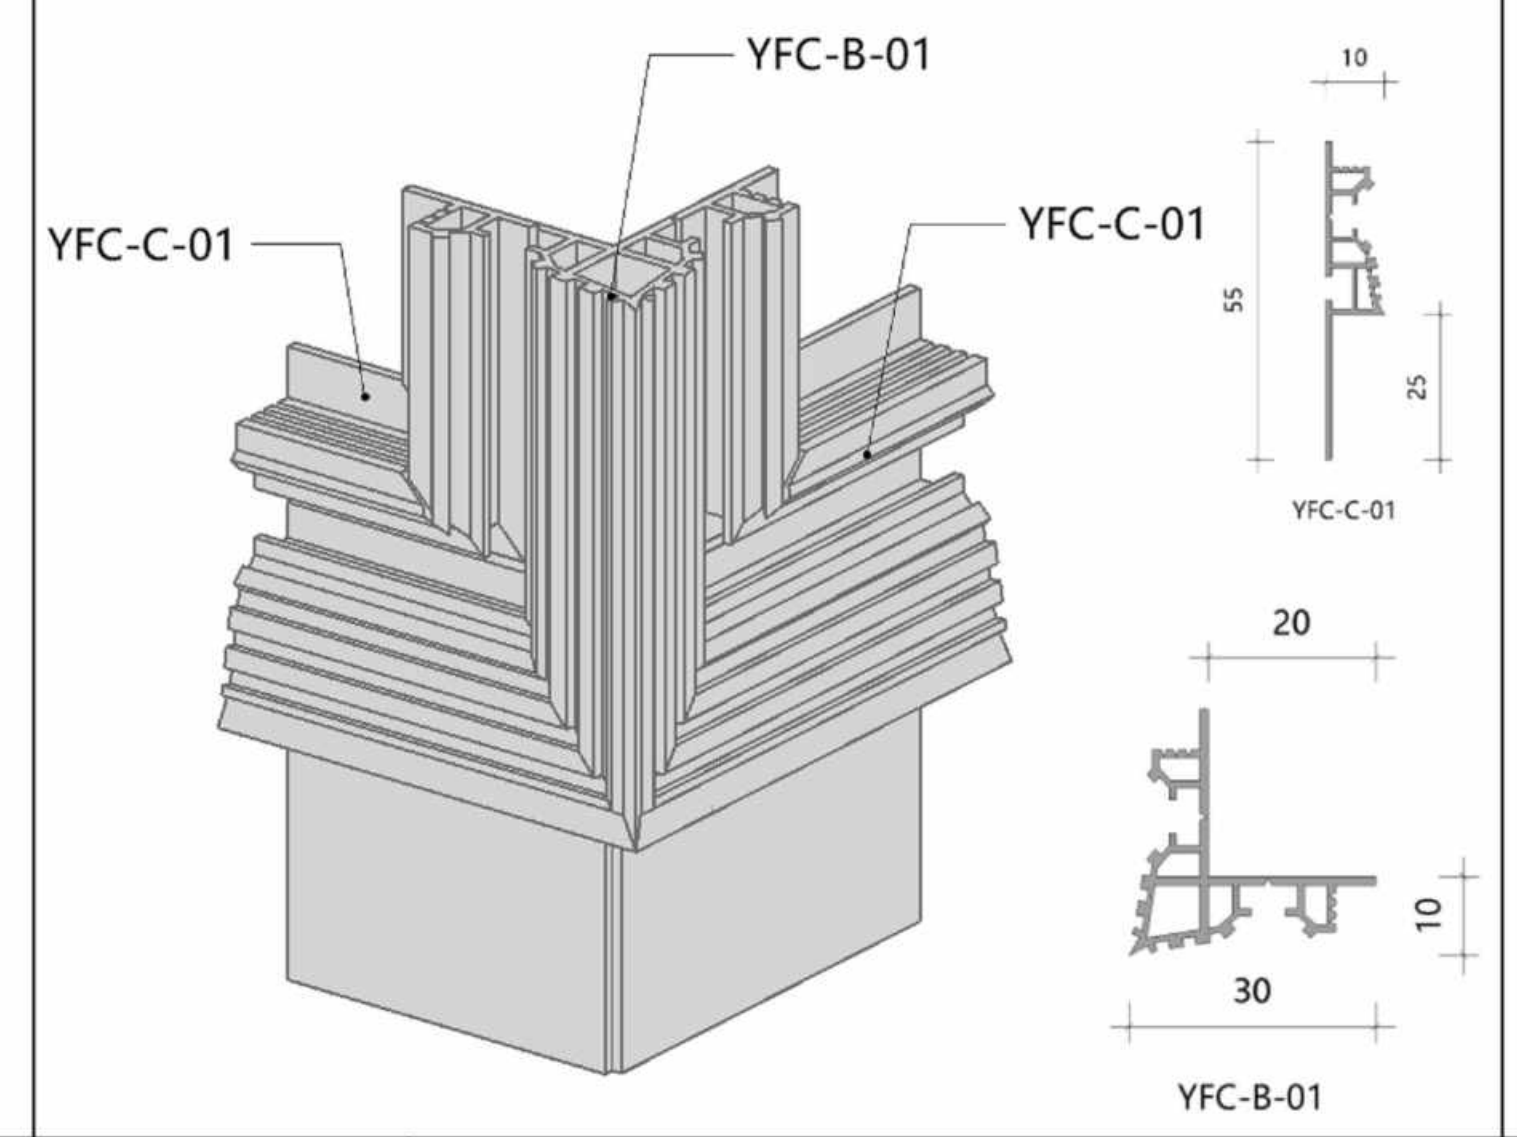
YFC-B-01
YFC-C-01
YFC-C-01
10
55
25
YFC-C-01
20
30
10
YFC-B-01

3D-11

转角铝型材-拼接跟通

转角数量：1

盖章

注释
Notes

1.本图纸如与现场尺寸有误，请施工人员与项目负责人联系。
2.施工前施工人员应认真查阅此图，如有不明确尺寸，按现场测量为准。
3.本图纸必须经甲乙双方认可并签字方可作为施工依据。

日期
Date 03/04/26

修订
Revision

1

项目
Project
潮映华岸府3-801

比例
Scale
餐厅一
墙面及踢脚铝型材

图纸编号
Drawing No.
AP.EL-04

项目编号
Project No.

©2025

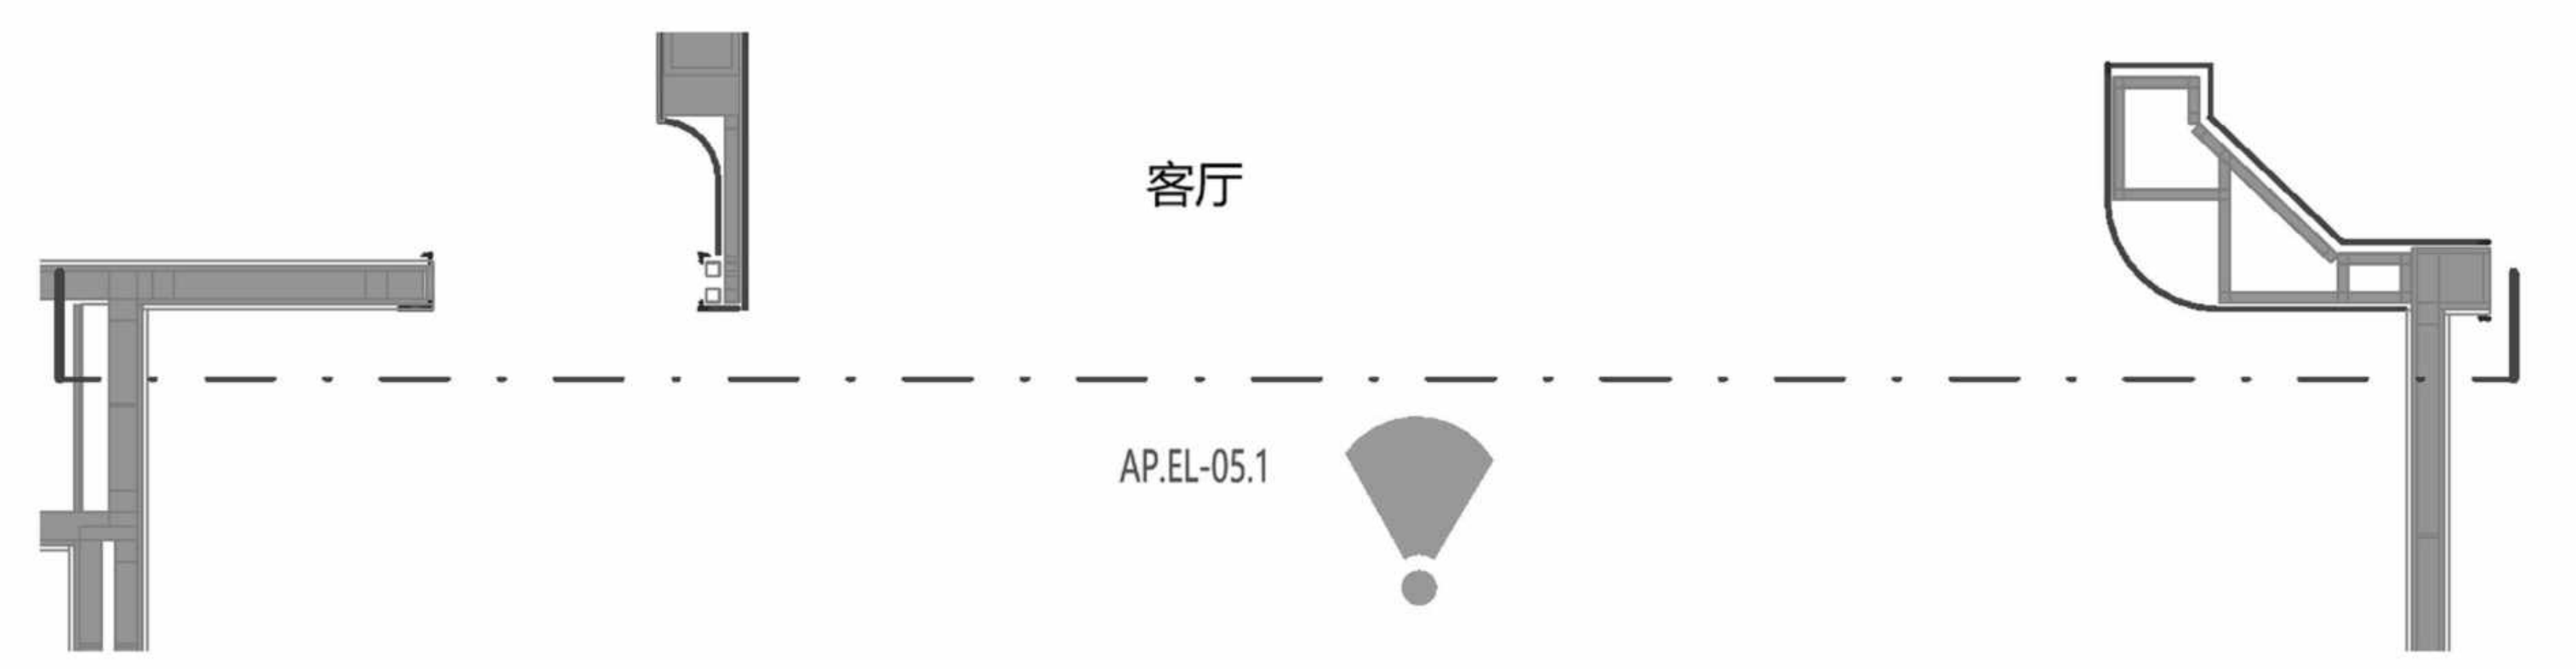
客厅
AP.EL-05.1
餐厅

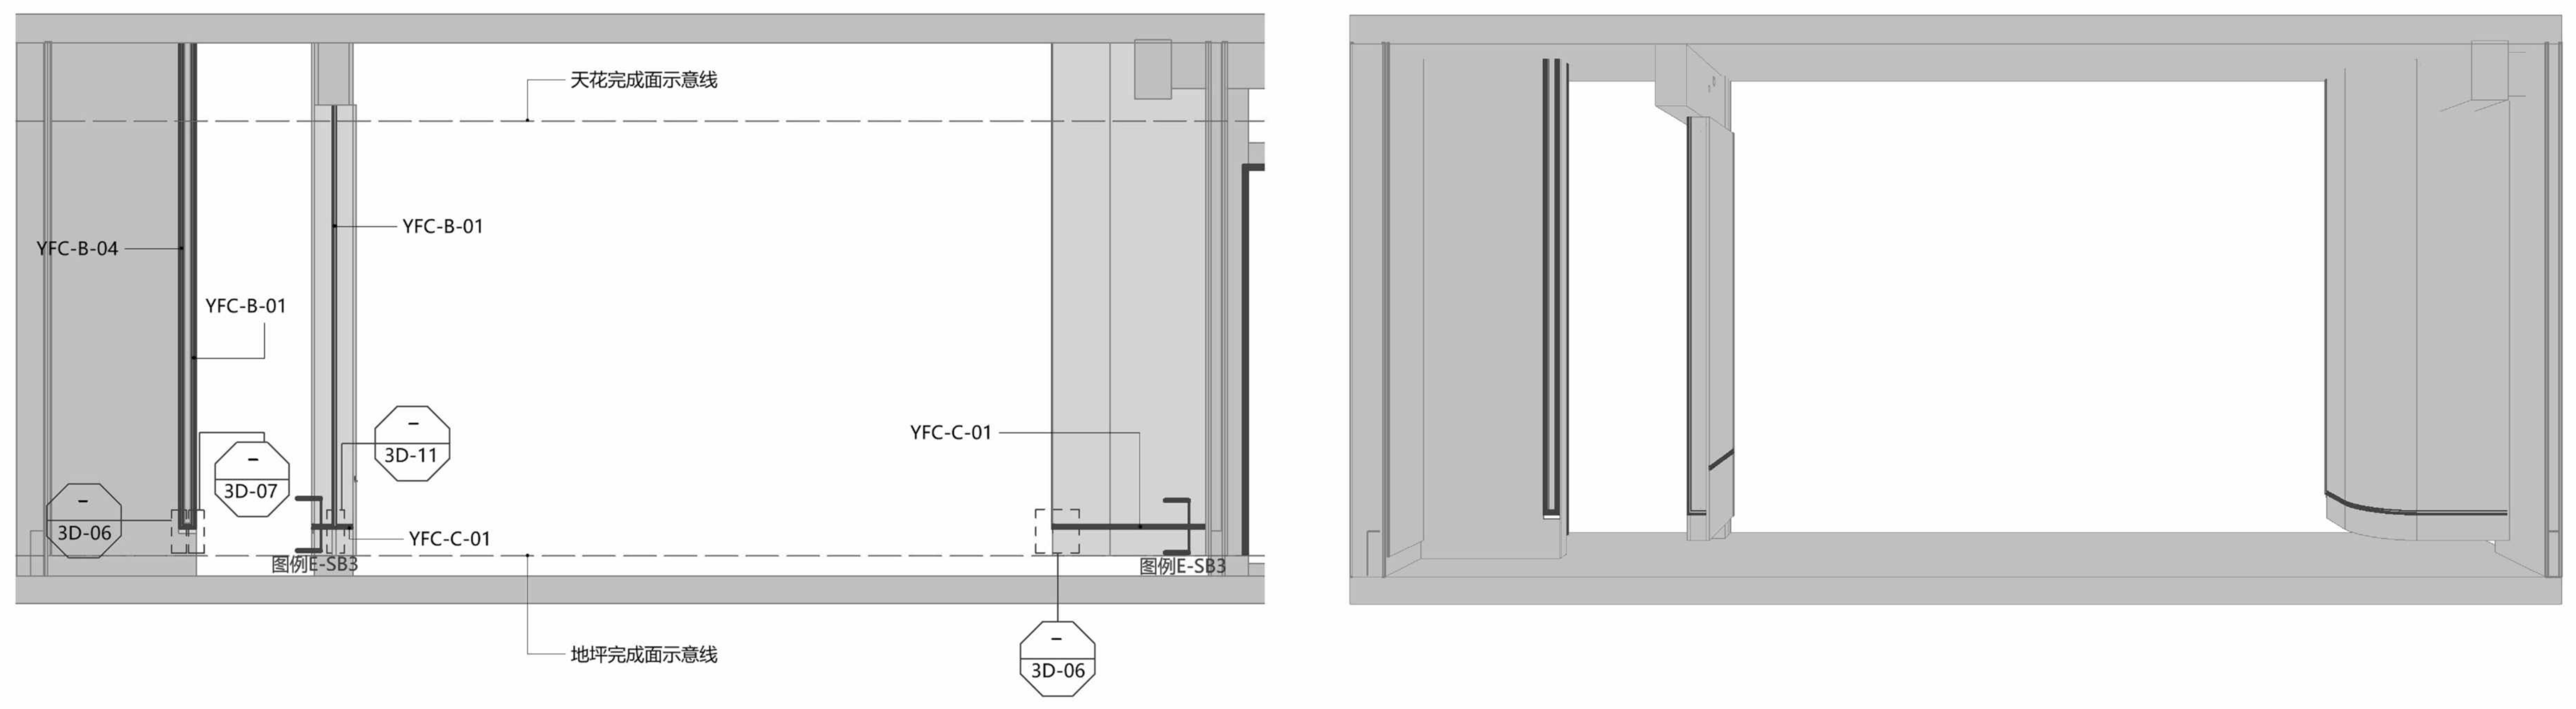
天花完成面示意线
YFC-B-04
YFC-B-01
YFC-B-01
3D-11
3D-07
3D-06
YFC-C-01
图例E-SB3
YFC-C-01
图例E-SB3
3D-06
地坪完成面示意线

1

餐厅二 墙面及踢脚铝型材立面图1

Scale比例 1：30@A2

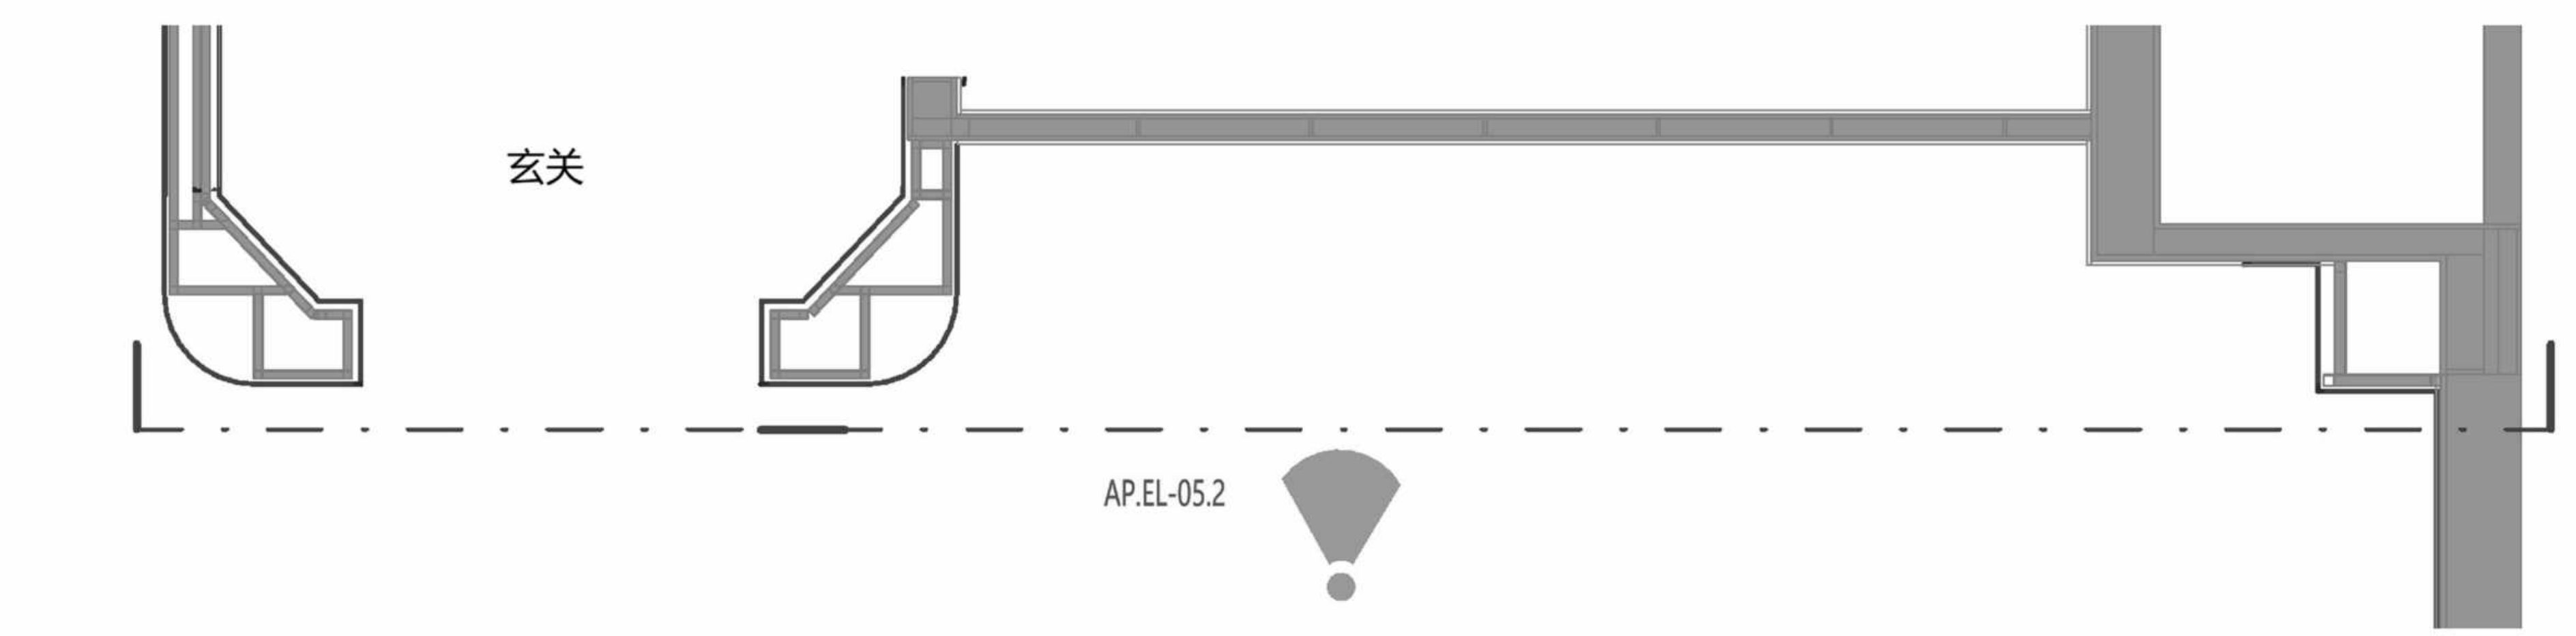
玄关
AP.EL-05.2
餐厅

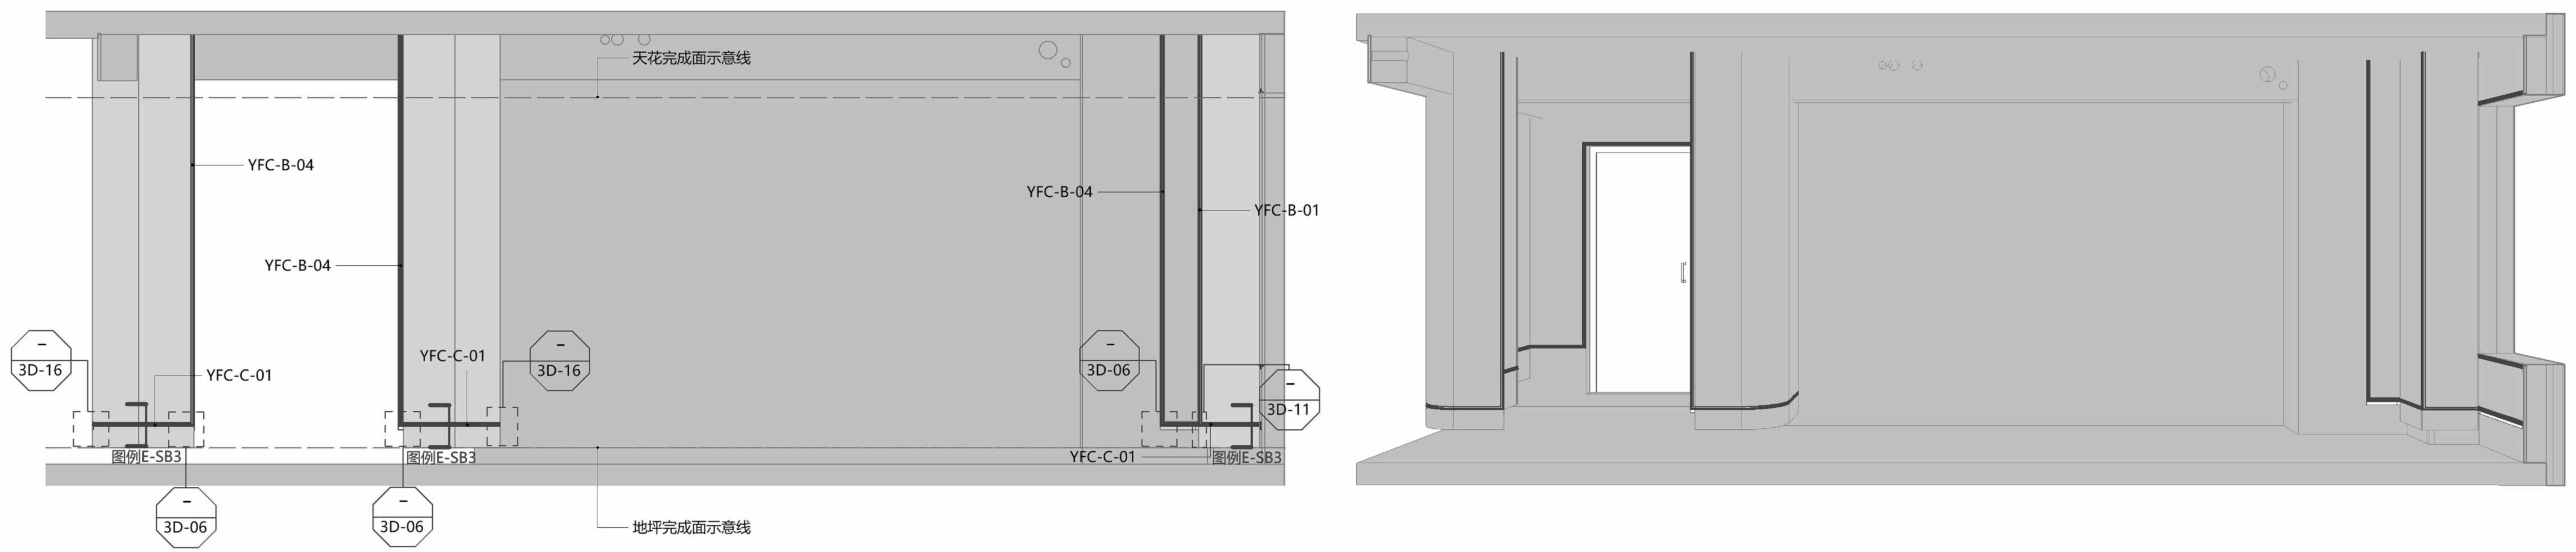
天花完成面示意线
YFC-B-04
YFC-B-04
3D-16
YFC-C-01
YFC-C-01
3D-16
YFC-B-04
YFC-B-01
3D-06
3D-11
YFC-C-01
图例E-SB3
图例E-SB3
图例E-SB3
3D-06
3D-06
地坪完成面示意线

2

餐厅二 墙面及踢脚铝型材立面图2

Scale比例 1：30@A2

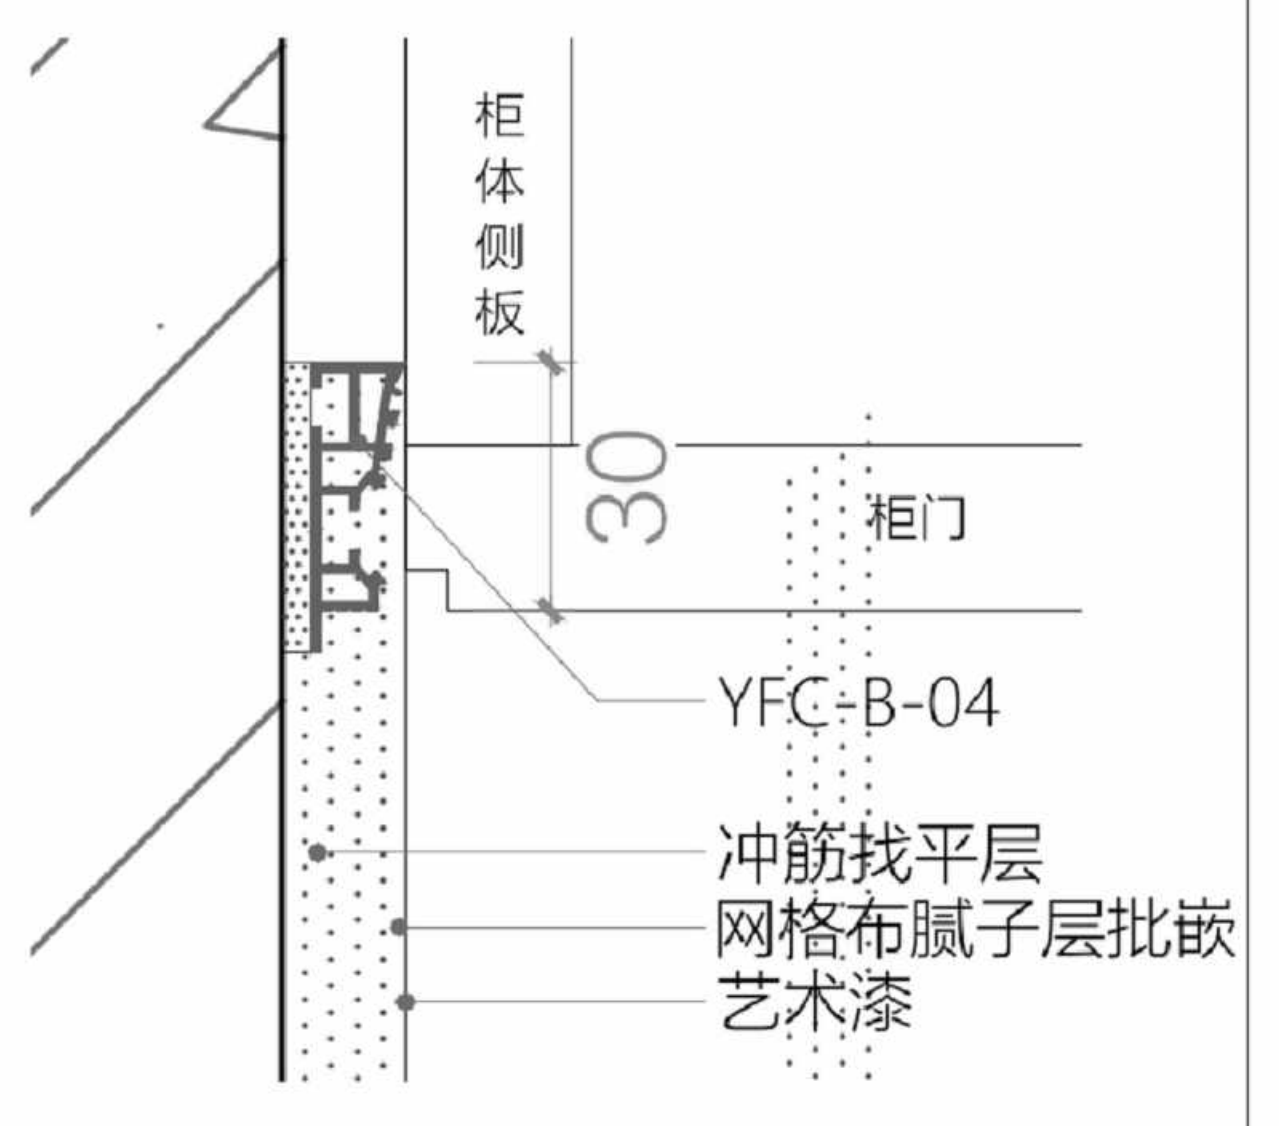
柜体侧板
30
柜门
YFC-B-04
冲筋找平层
网格布腻子层批嵌
艺术漆

图例B-P6 柜边-石膏基找平铝型材

Scale比例 1：1@A2

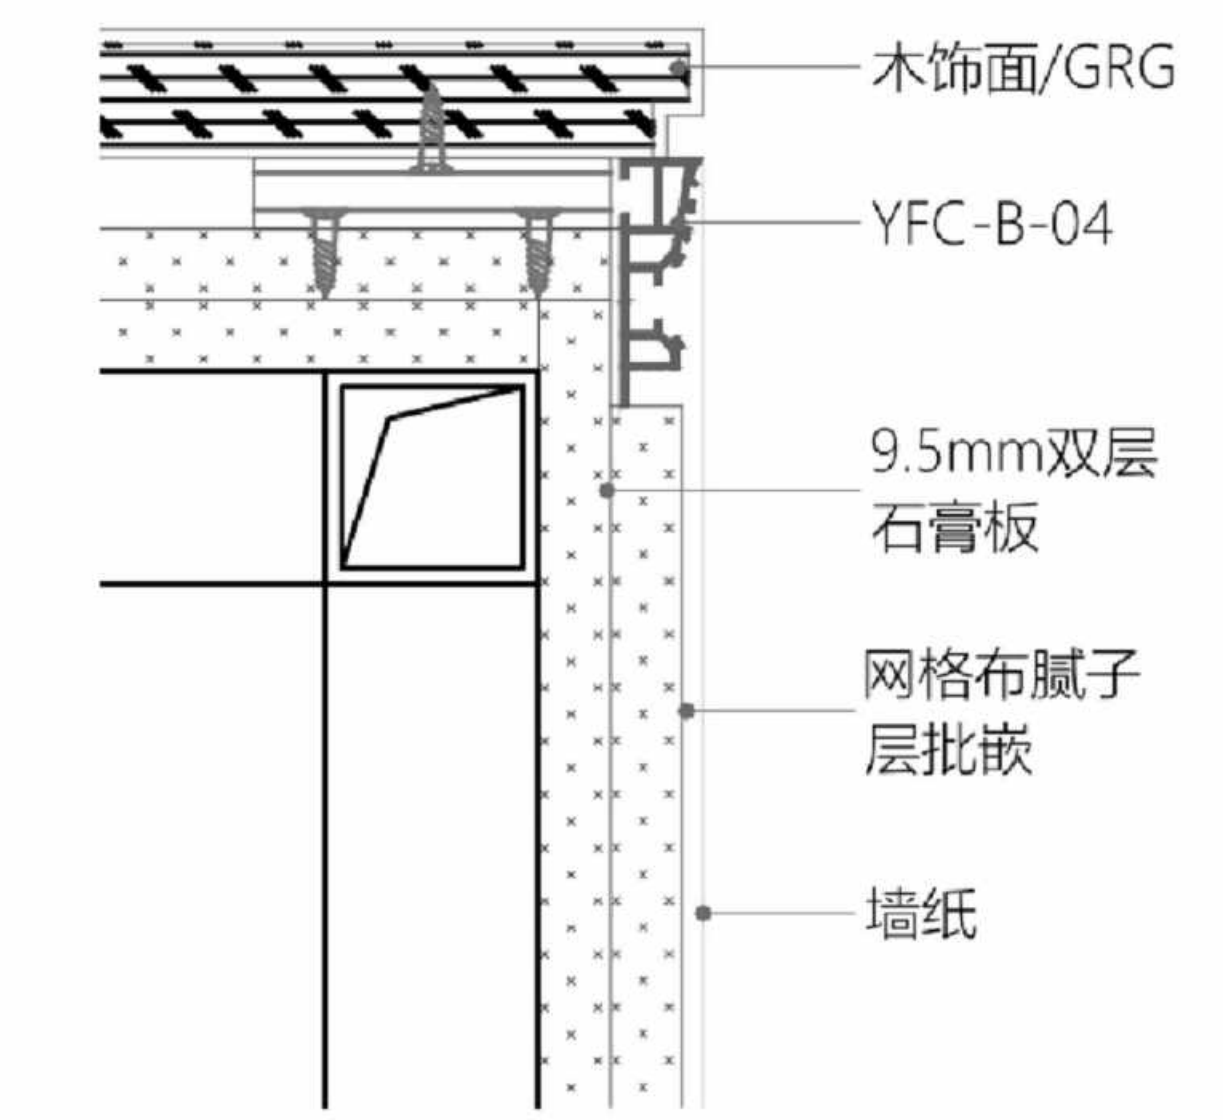
木饰面/GRG
YFC-B-04
9.5mm双层石膏板
网格布腻子层批嵌
墙纸

图例C-PB2 墙面-石膏基找平铝型材

Scale比例 1：1@A2

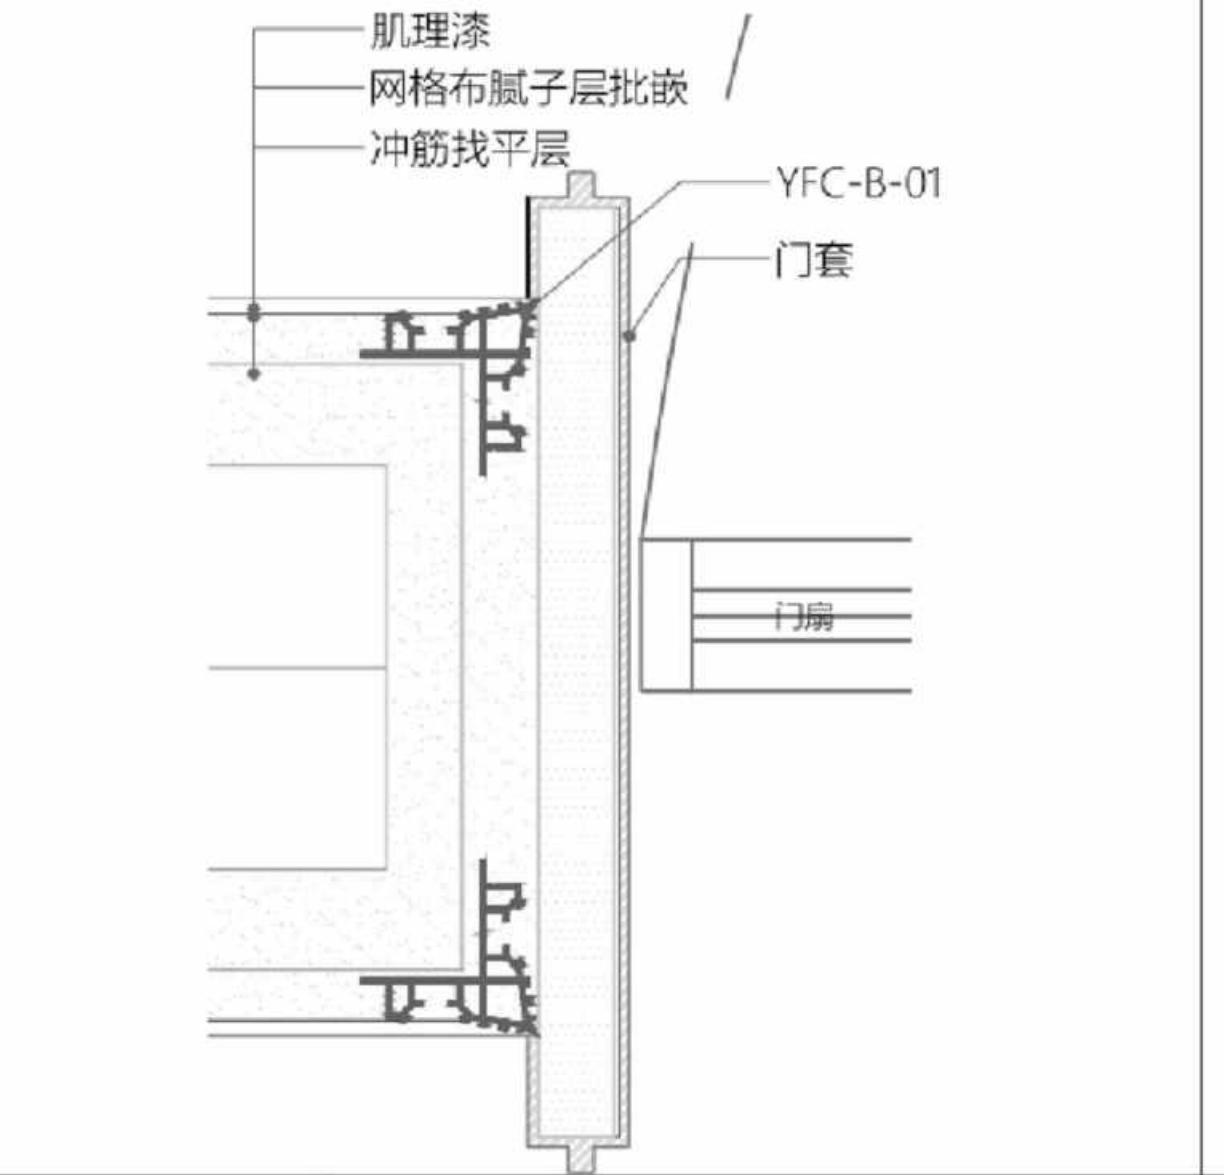
肌理漆
网格布腻子层批嵌
冲筋找平层
YFC-B-01
门套
门扇

图例D-M4 门边-石膏基找平铝型材

Scale比例 1：1@A2

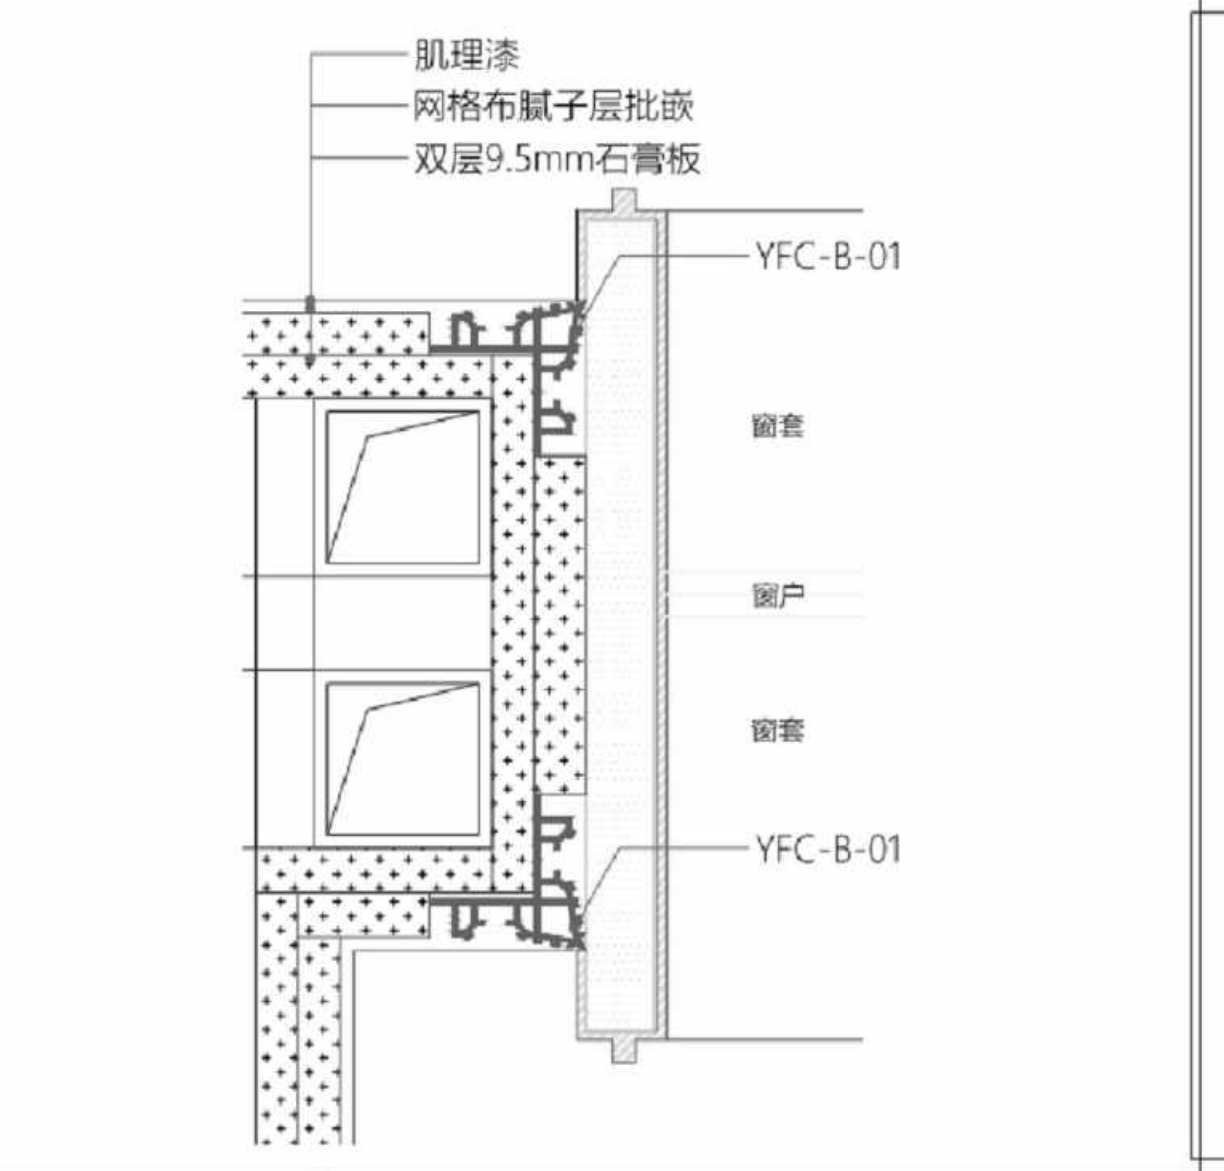
肌理漆
网格布腻子层批嵌
双层9.5mm石膏板
YFC-B-01
窗套
窗户
窗套
YFC-B-01

图例D-M5 门边-石膏基找平铝型材

Scale比例 1：1@A2

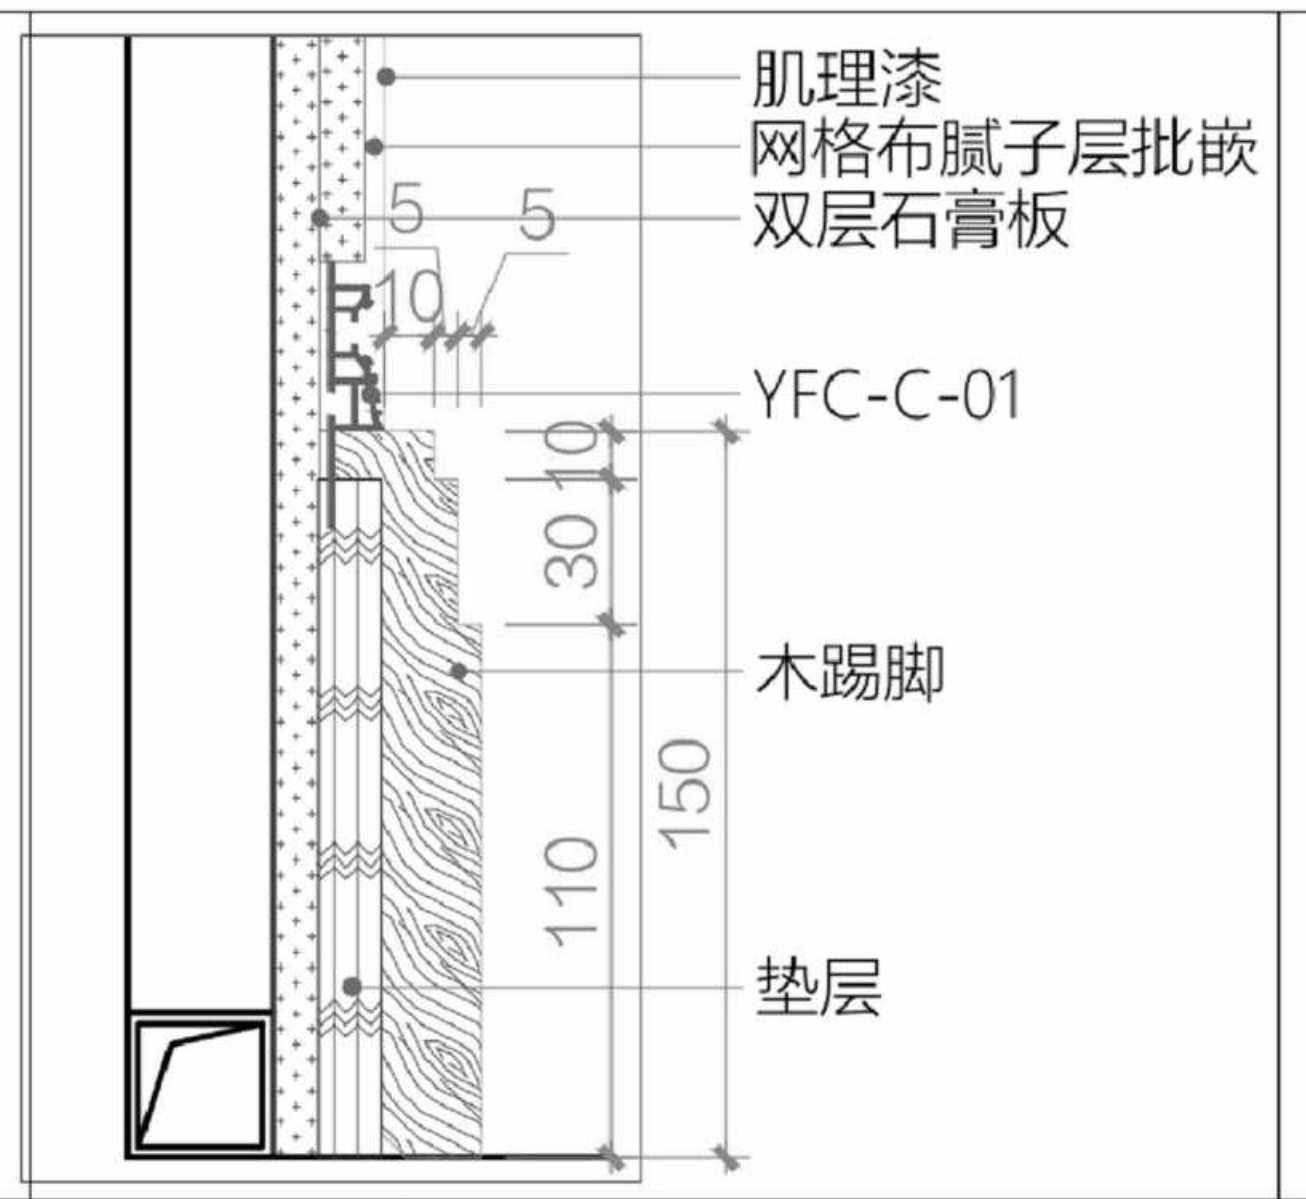
肌理漆
网格布腻子层批嵌
双层石膏板
5
5
10
YFC-C-01
10
30
木踢脚
150
110
垫层

图例E-SB3 踢脚-石膏基找平铝型材

Scale比例 1：1@A2

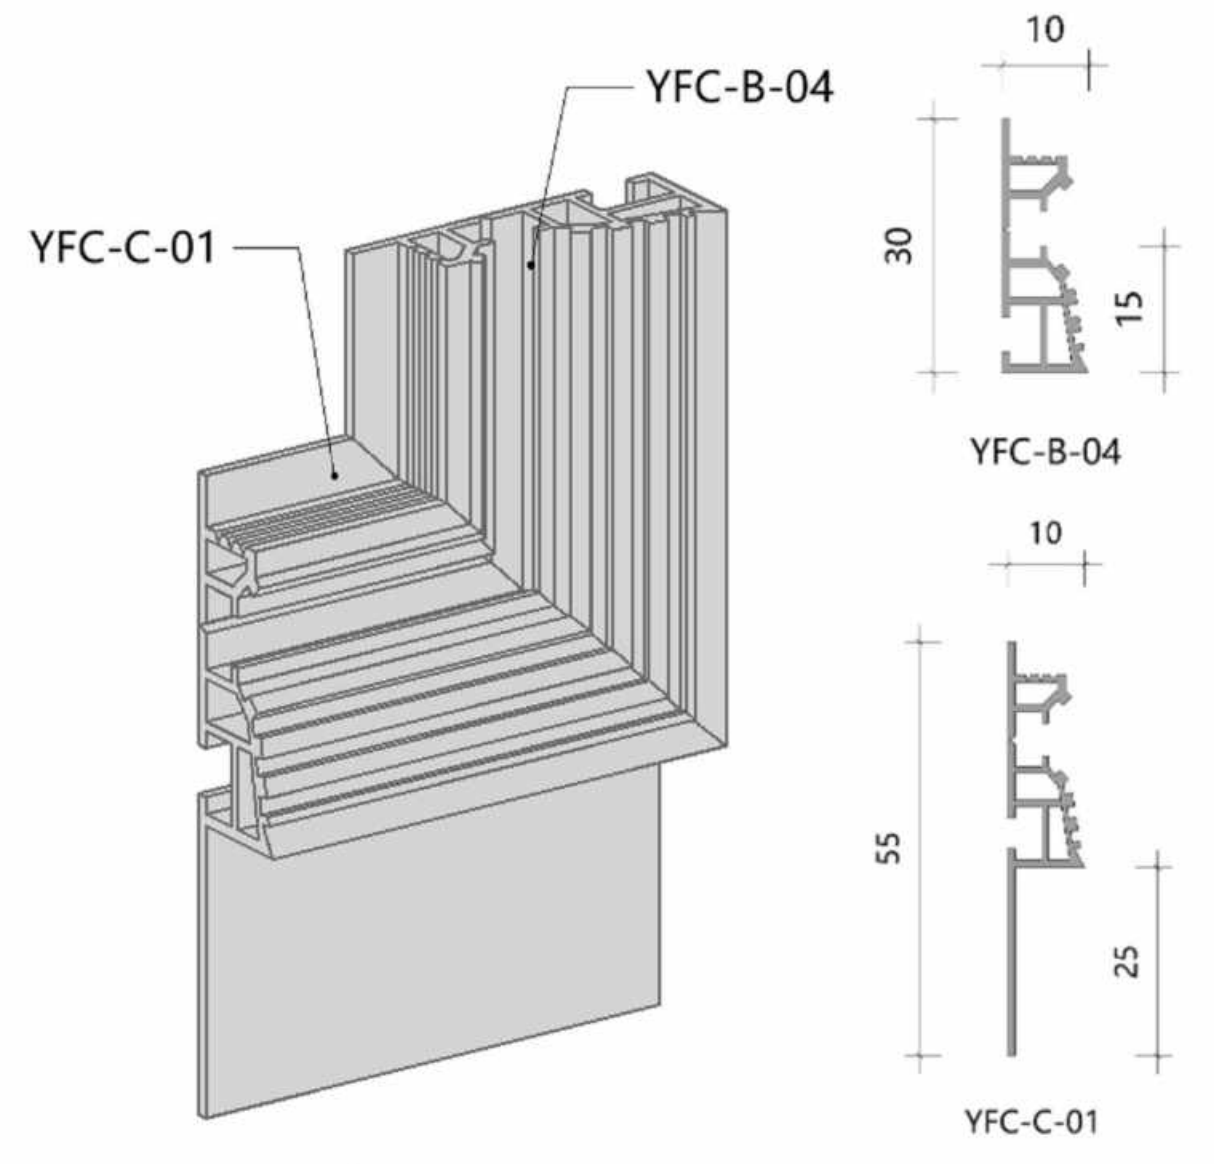
YFC-C-01
YFC-B-04
10
30
15
YFC-B-04
10
55
25
YFC-C-01

3D-06 转角铝型材-拼接跟通

转角数量：5

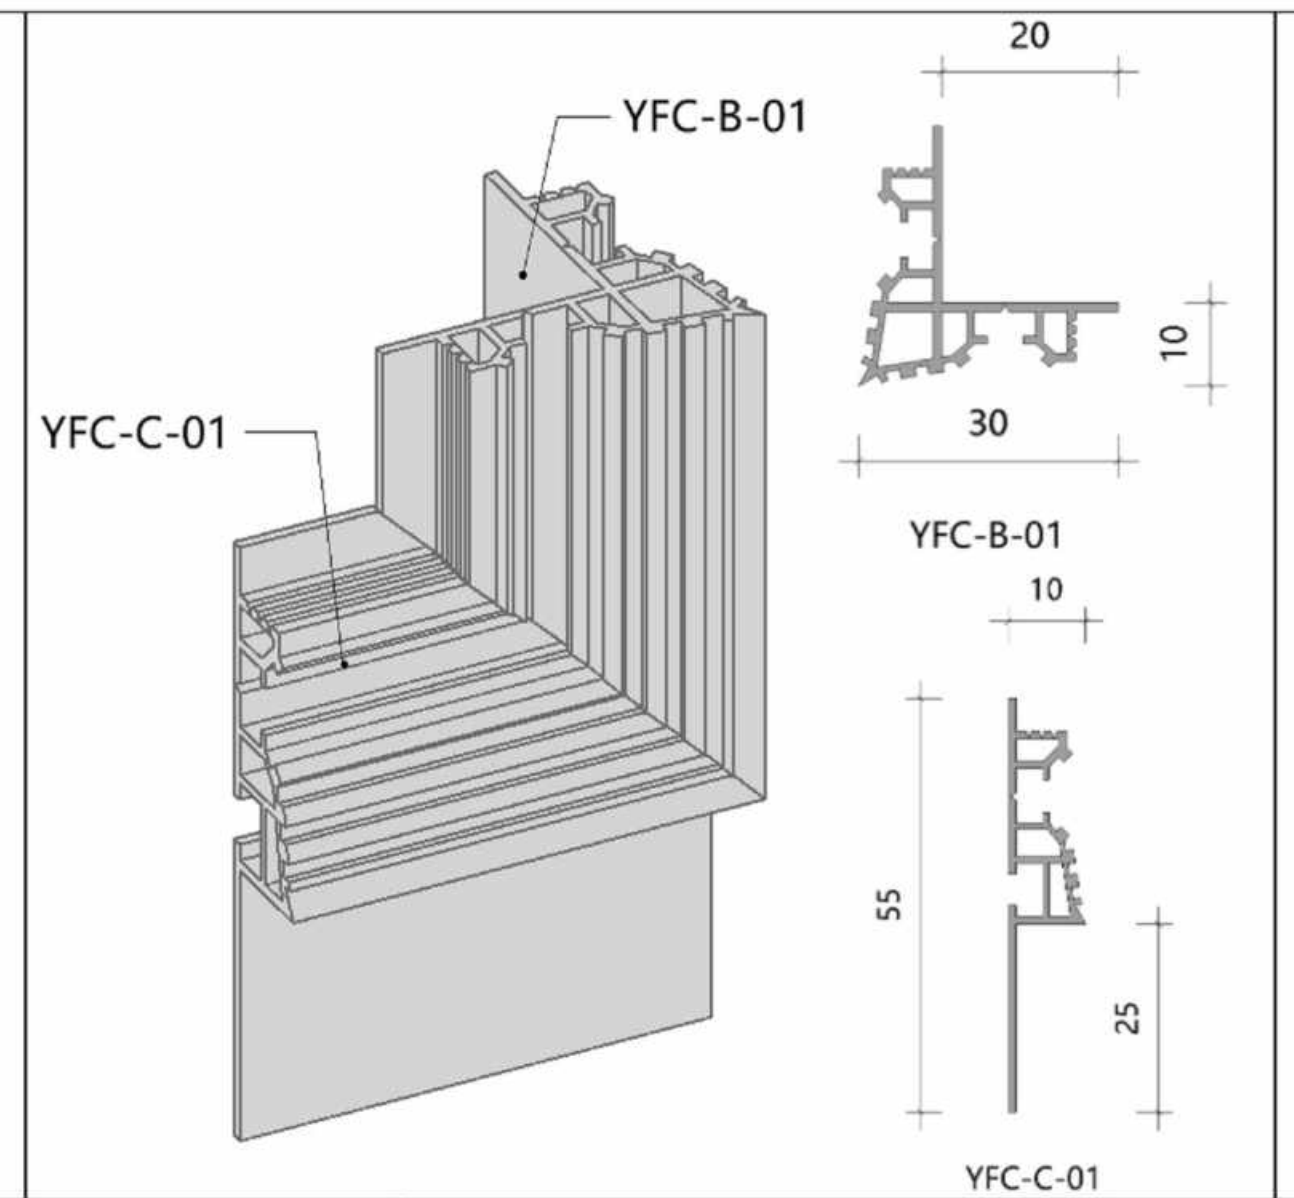
YFC-B-01
YFC-C-01
20
10
30
YFC-B-01
10
55
25
YFC-C-01

3D-07 转角铝型材-拼接跟通

转角数量：1

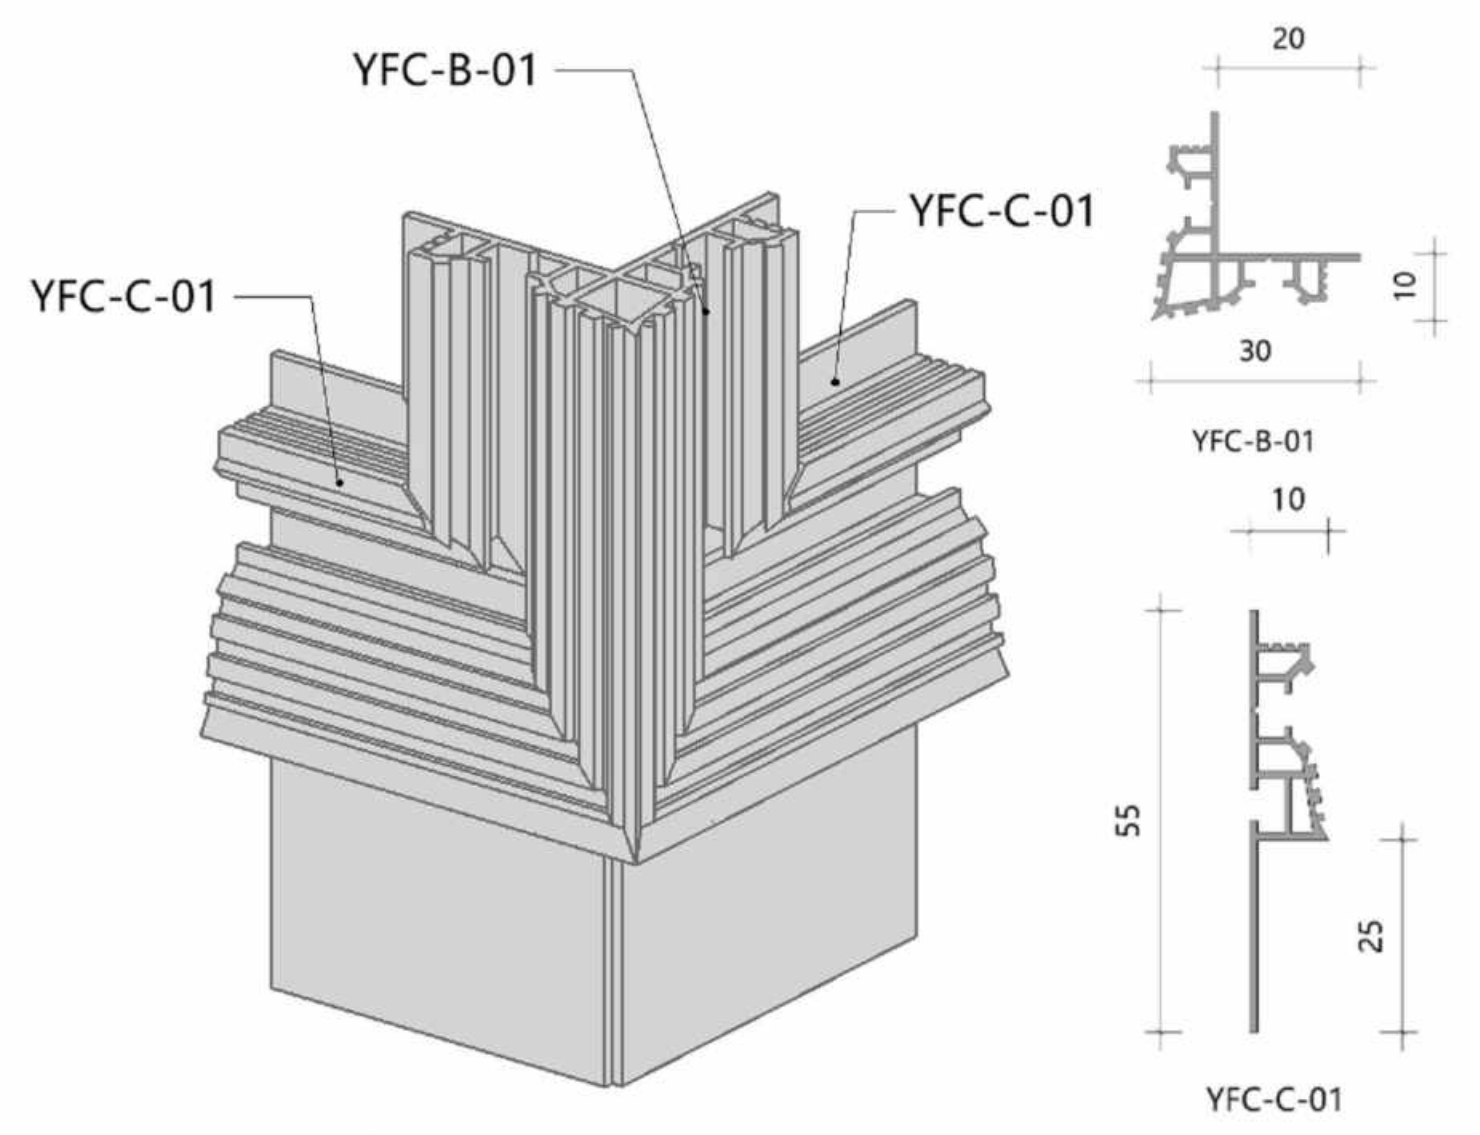
YFC-B-01
YFC-C-01
YFC-C-01
20
10
30
YFC-B-01
10
55
25
YFC-C-01

3D-11 转角铝型材-拼接跟通

转角数量：2

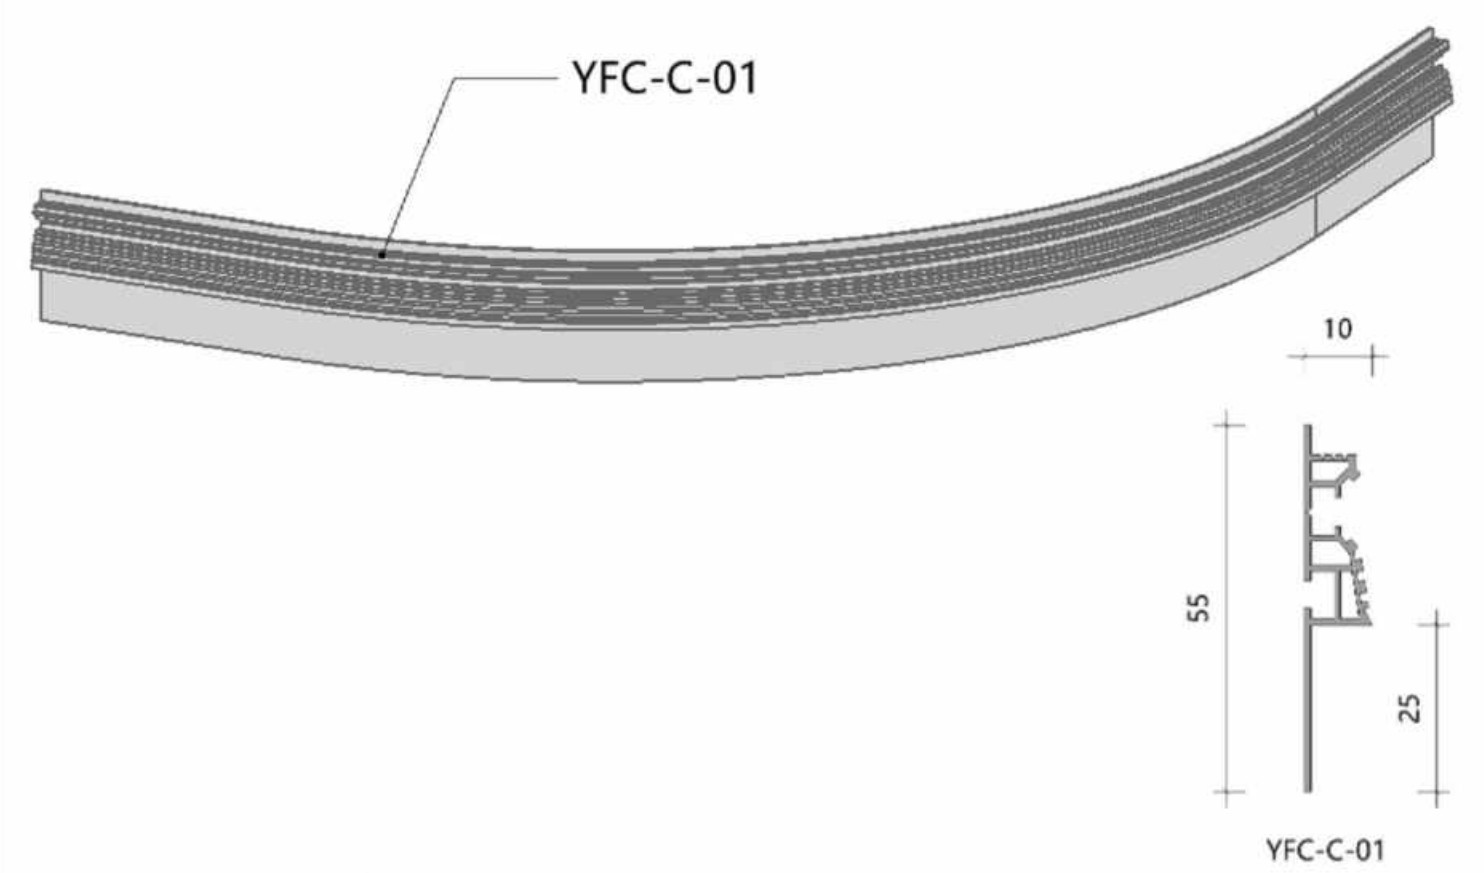
YFC-C-01
10
55
25
YFC-C-01

3D-16 转角铝型材-拼接跟通

转角数量：2

盖章

注释
Notes
1.本图纸如与现场尺寸有误，请施工人员与项目负责人联系。
2.施工前施工人员应认真查阅此图，如有不明确尺寸，按现场测量为准。
3.本图纸必须经甲乙双方认可并签字方可作为施工依据。

日期
Date 03/04/26

修订
Revision
1

项目
Project
潮映华岸府3-801

比例
Scale
餐厅二
墙面及踢脚铝型材

图纸编号
Drawing No.
AP.EL-05

项目编号
Project No.
©2025

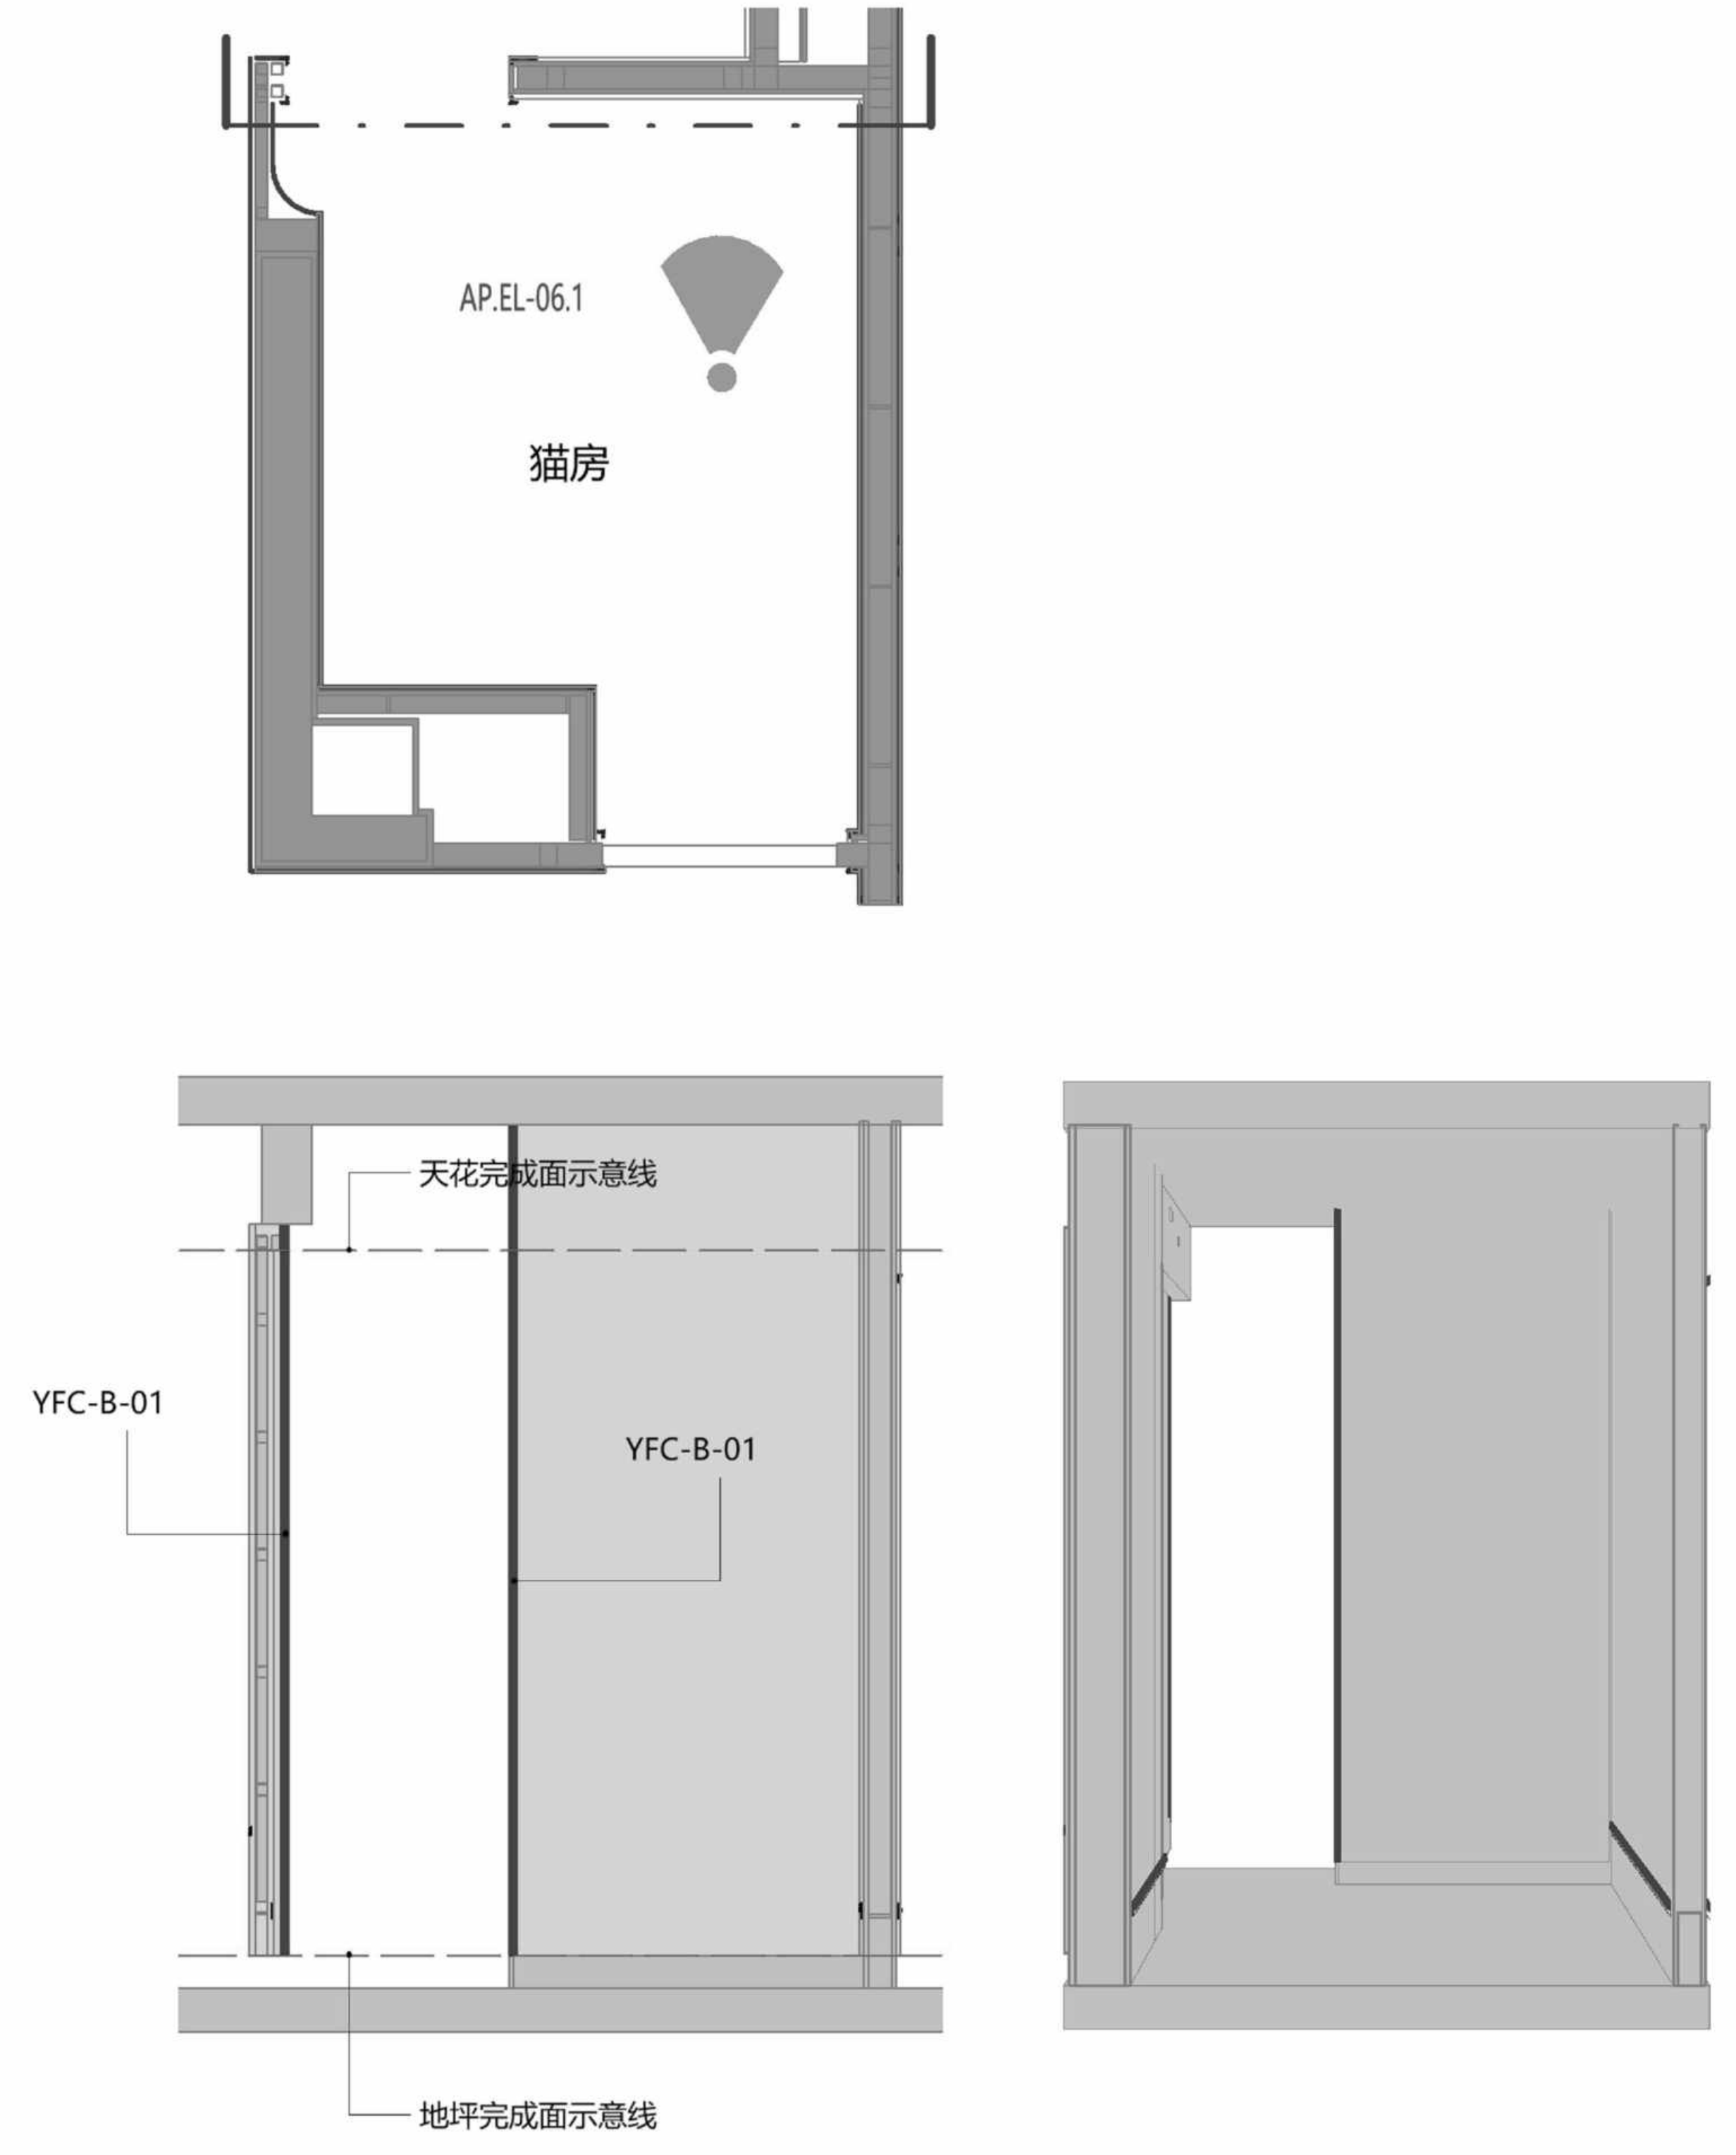
AP.EL-06.1
猫房
天花完成面示意线
YFC-B-01
YFC-B-01
地坪完成面示意线

1	猫房 墙面及踢脚铝型材立面图1
	Scale比例 1：30@A2

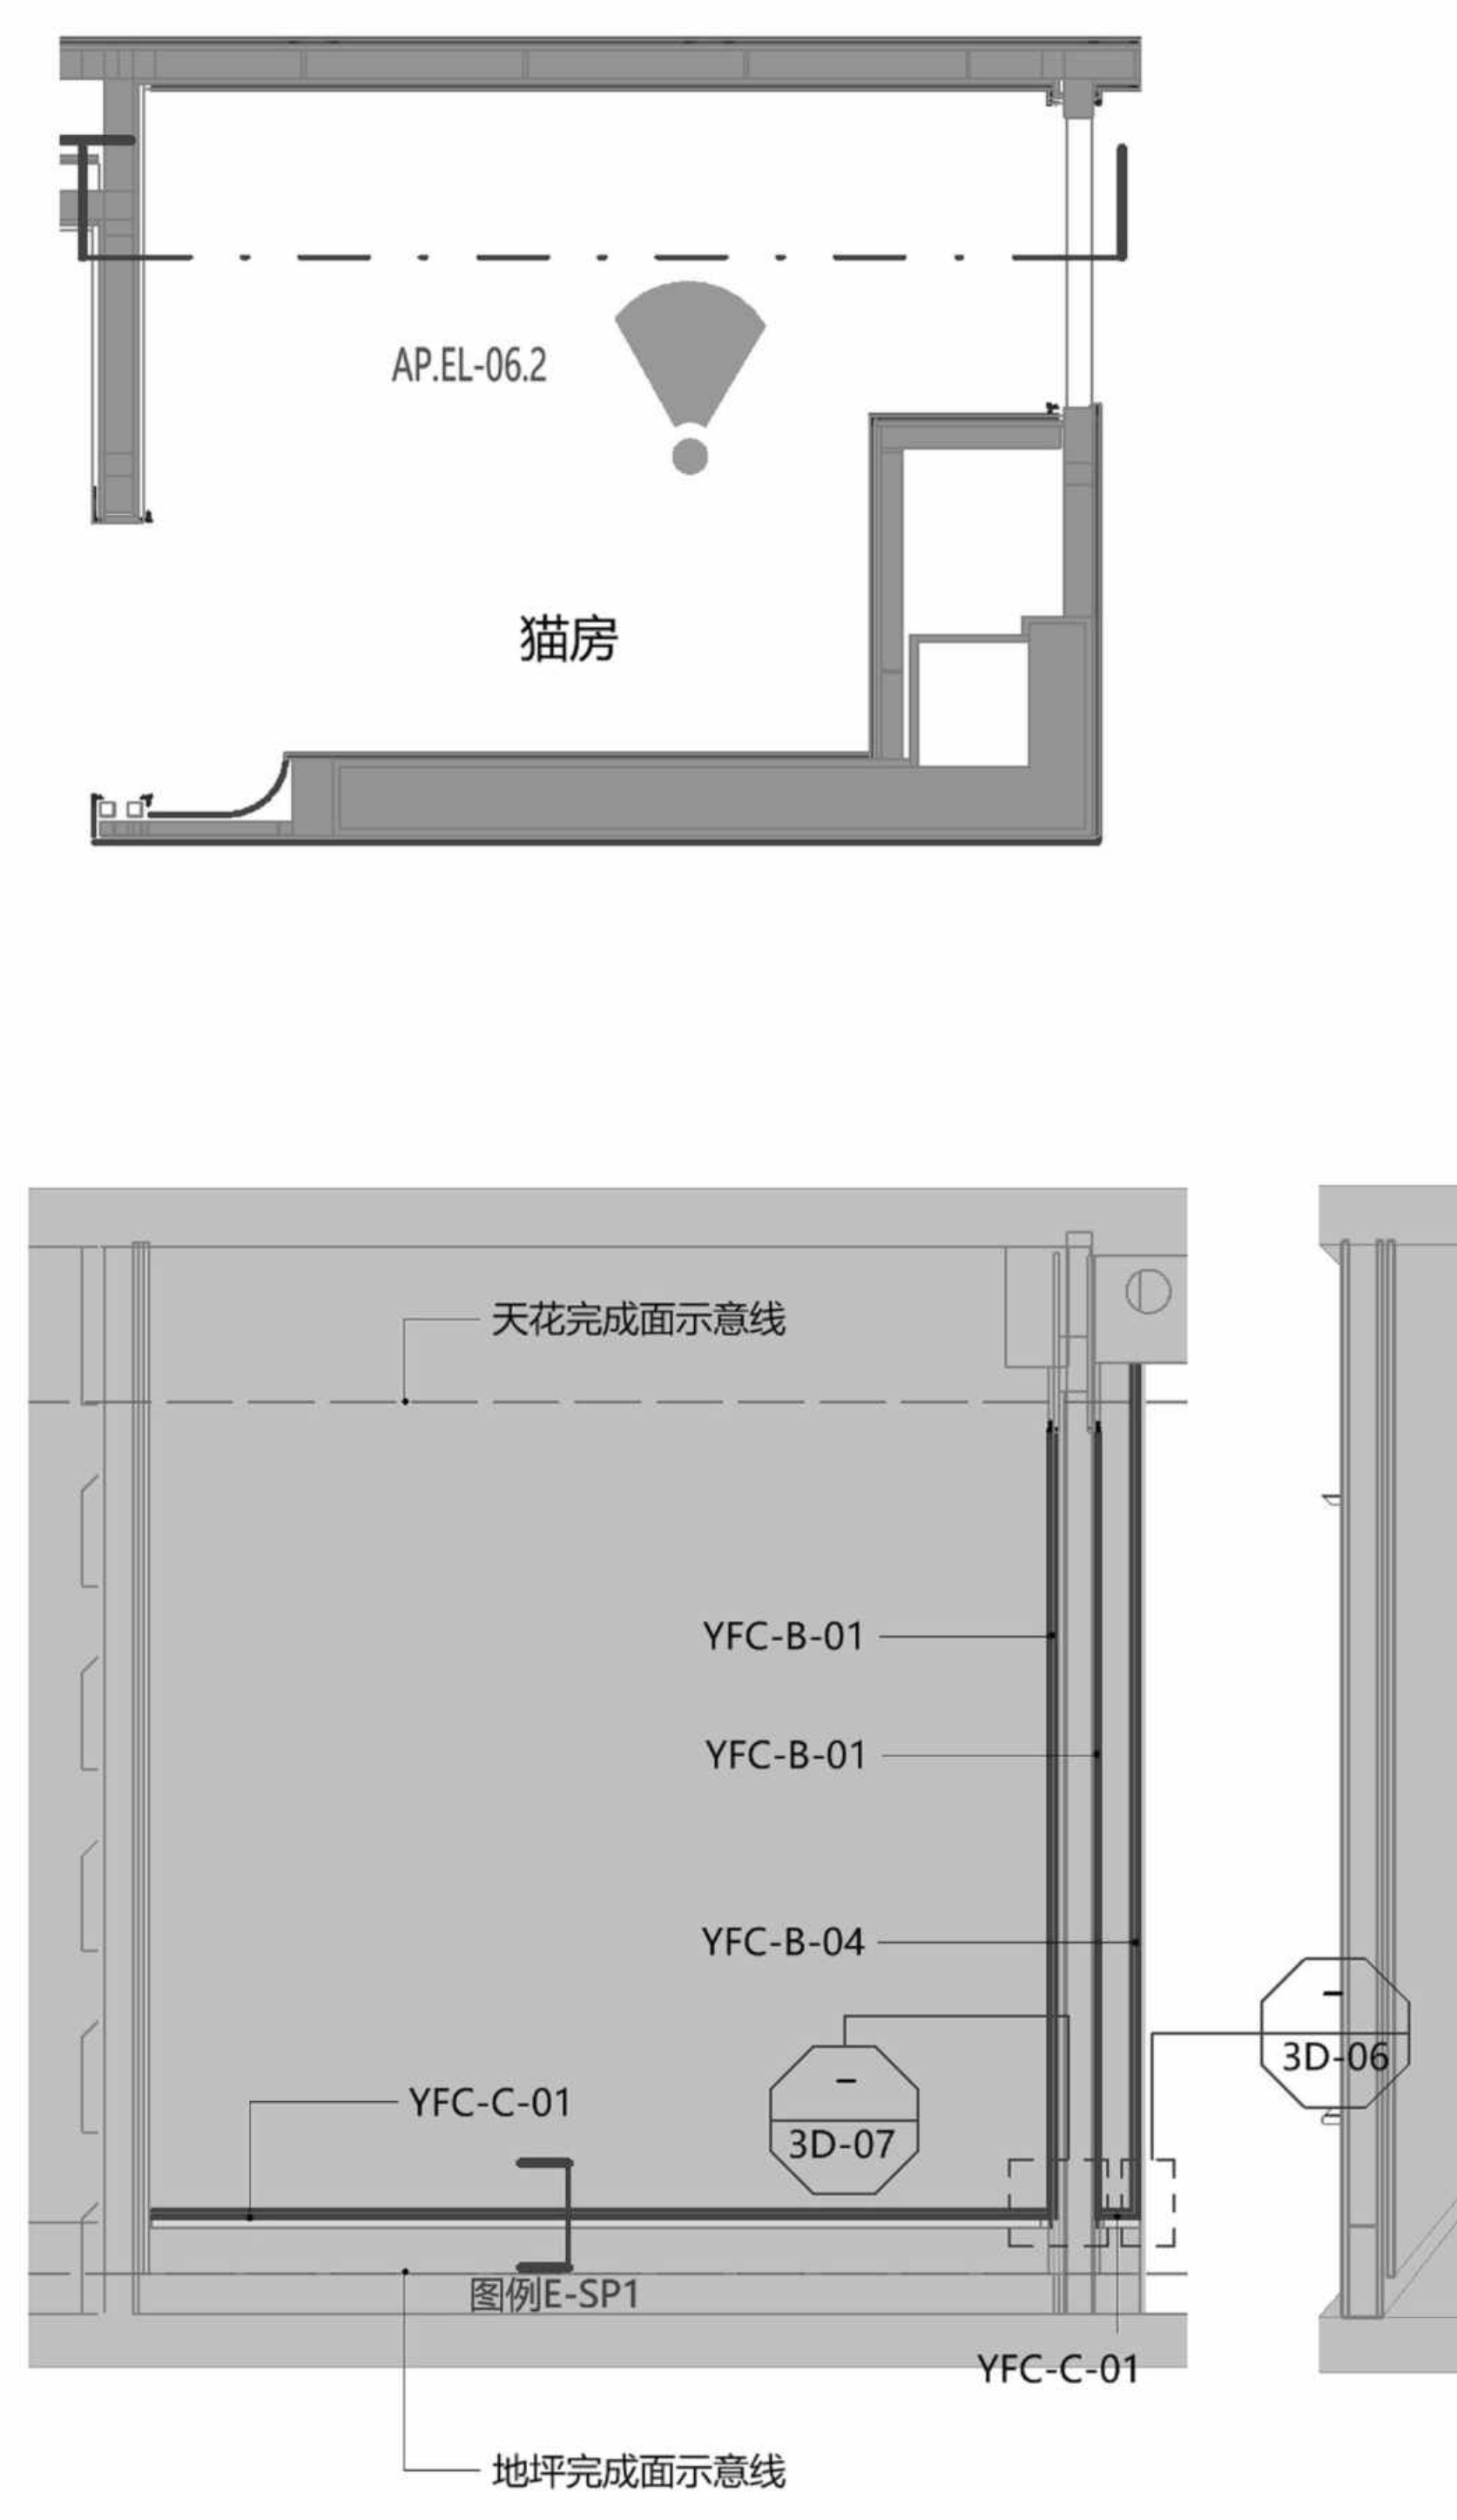
AP.EL-06.2
猫房
天花完成面示意线
YFC-B-01
YFC-B-01
YFC-B-04
YFC-C-01
3D-07
3D-06
图例E-SP1
YFC-C-01
地坪完成面示意线

2	猫房 墙面及踢脚铝型材立面图2
	Scale比例 1：30@A2

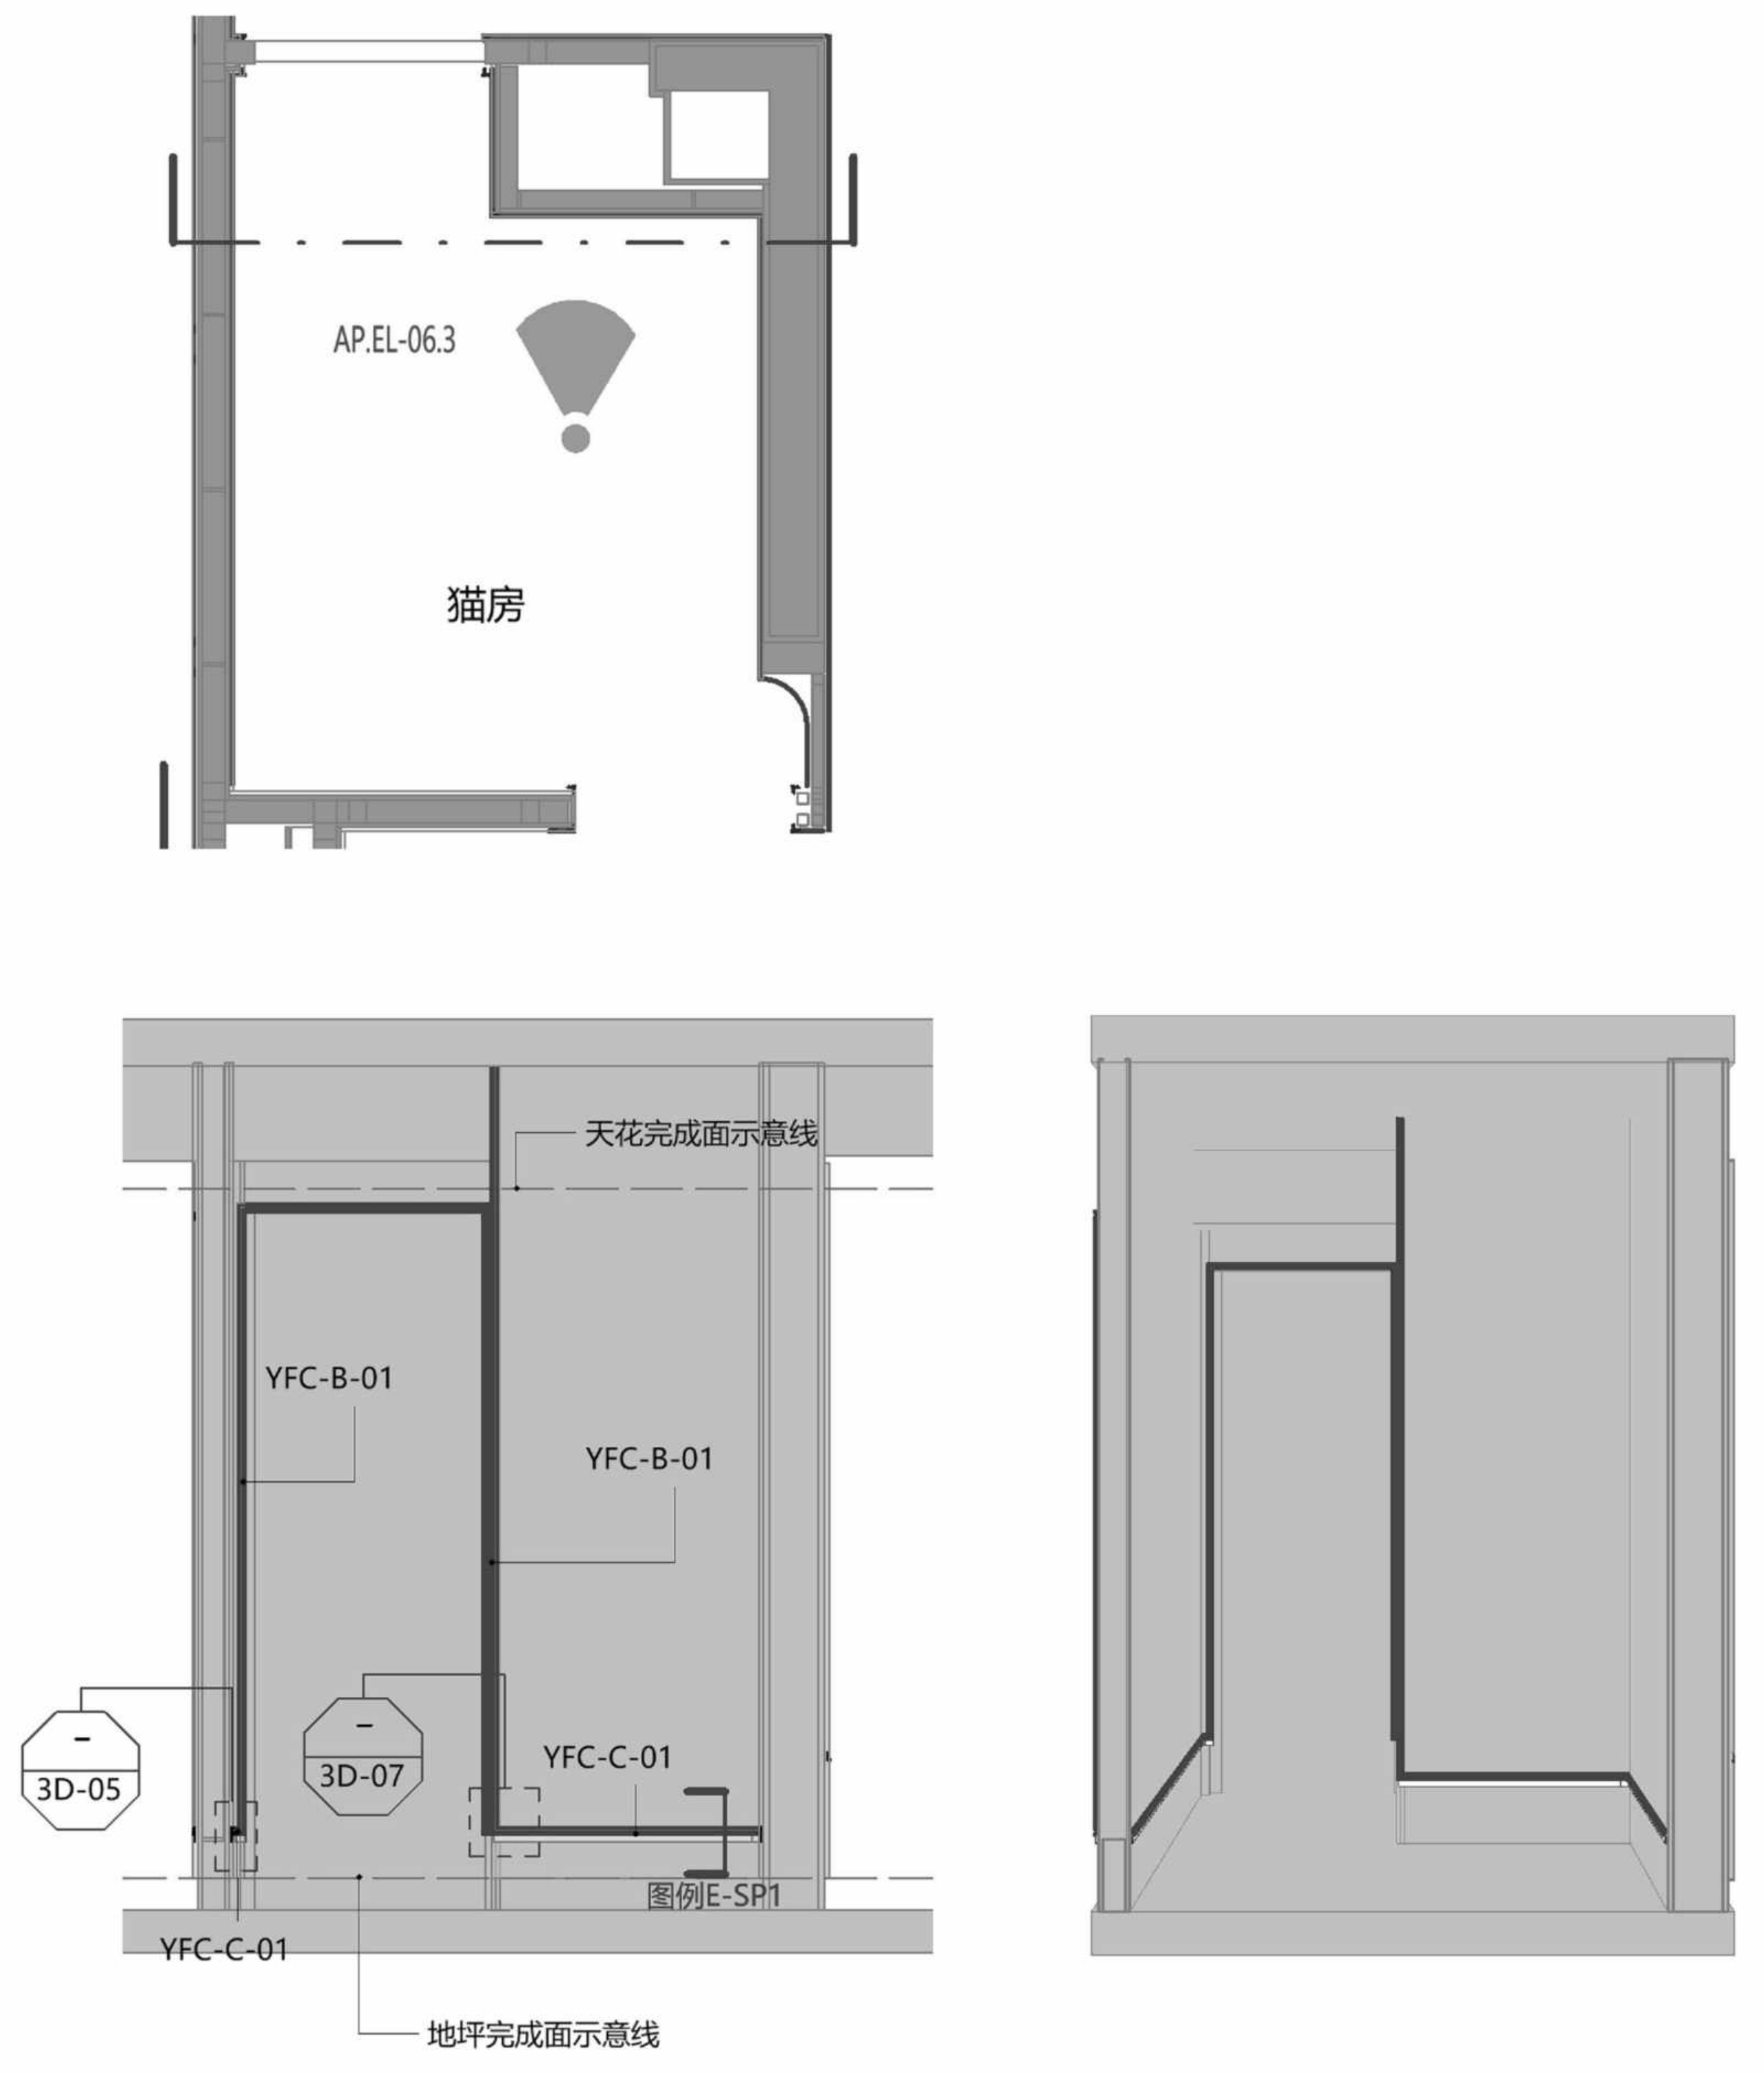
AP.EL-06.3
猫房
天花完成面示意线
YFC-B-01
YFC-B-01
3D-05
3D-07
YFC-C-01
图例E-SP1
YFC-C-01
地坪完成面示意线

3	猫房 墙面及踢脚铝型材立面图3
	Scale比例 1：30@A2

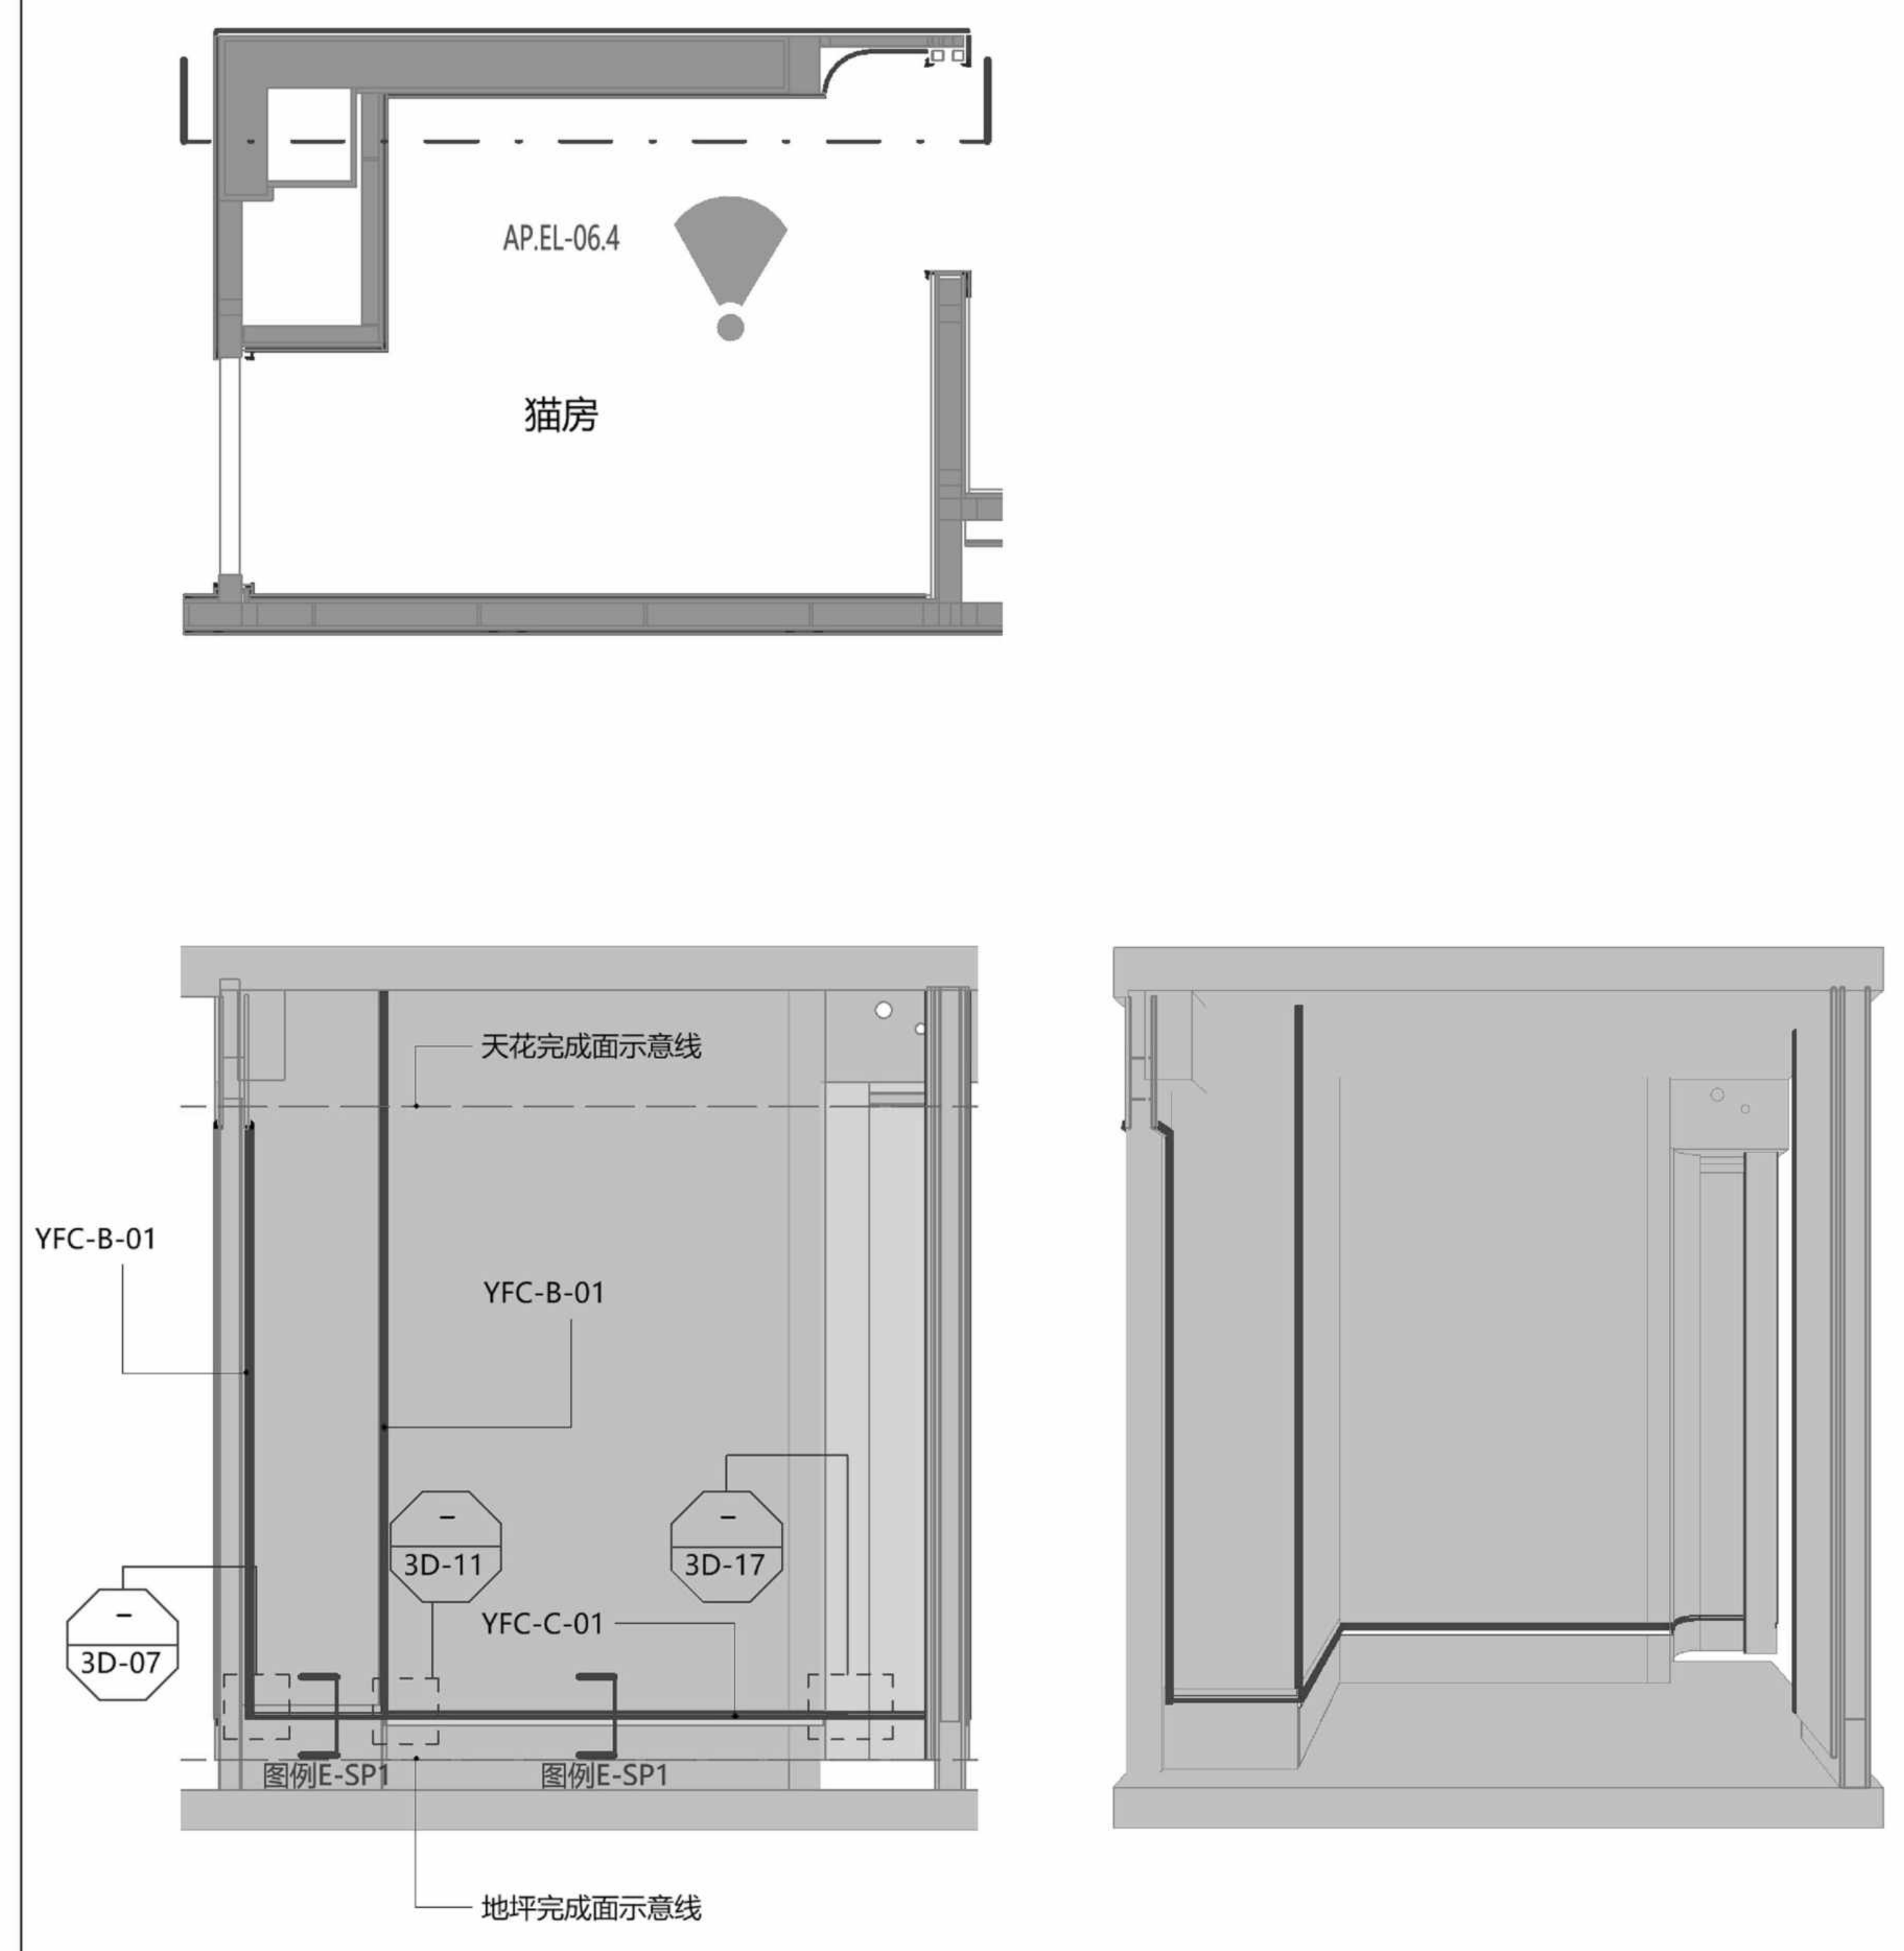
AP.EL-06.4
猫房
天花完成面示意线
YFC-B-01
YFC-B-01
3D-11
3D-17
3D-07
YFC-C-01
图例E-SP1
图例E-SP1
地坪完成面示意线

4	猫房 墙面及踢脚铝型材立面图4
	Scale比例 1：30@A2

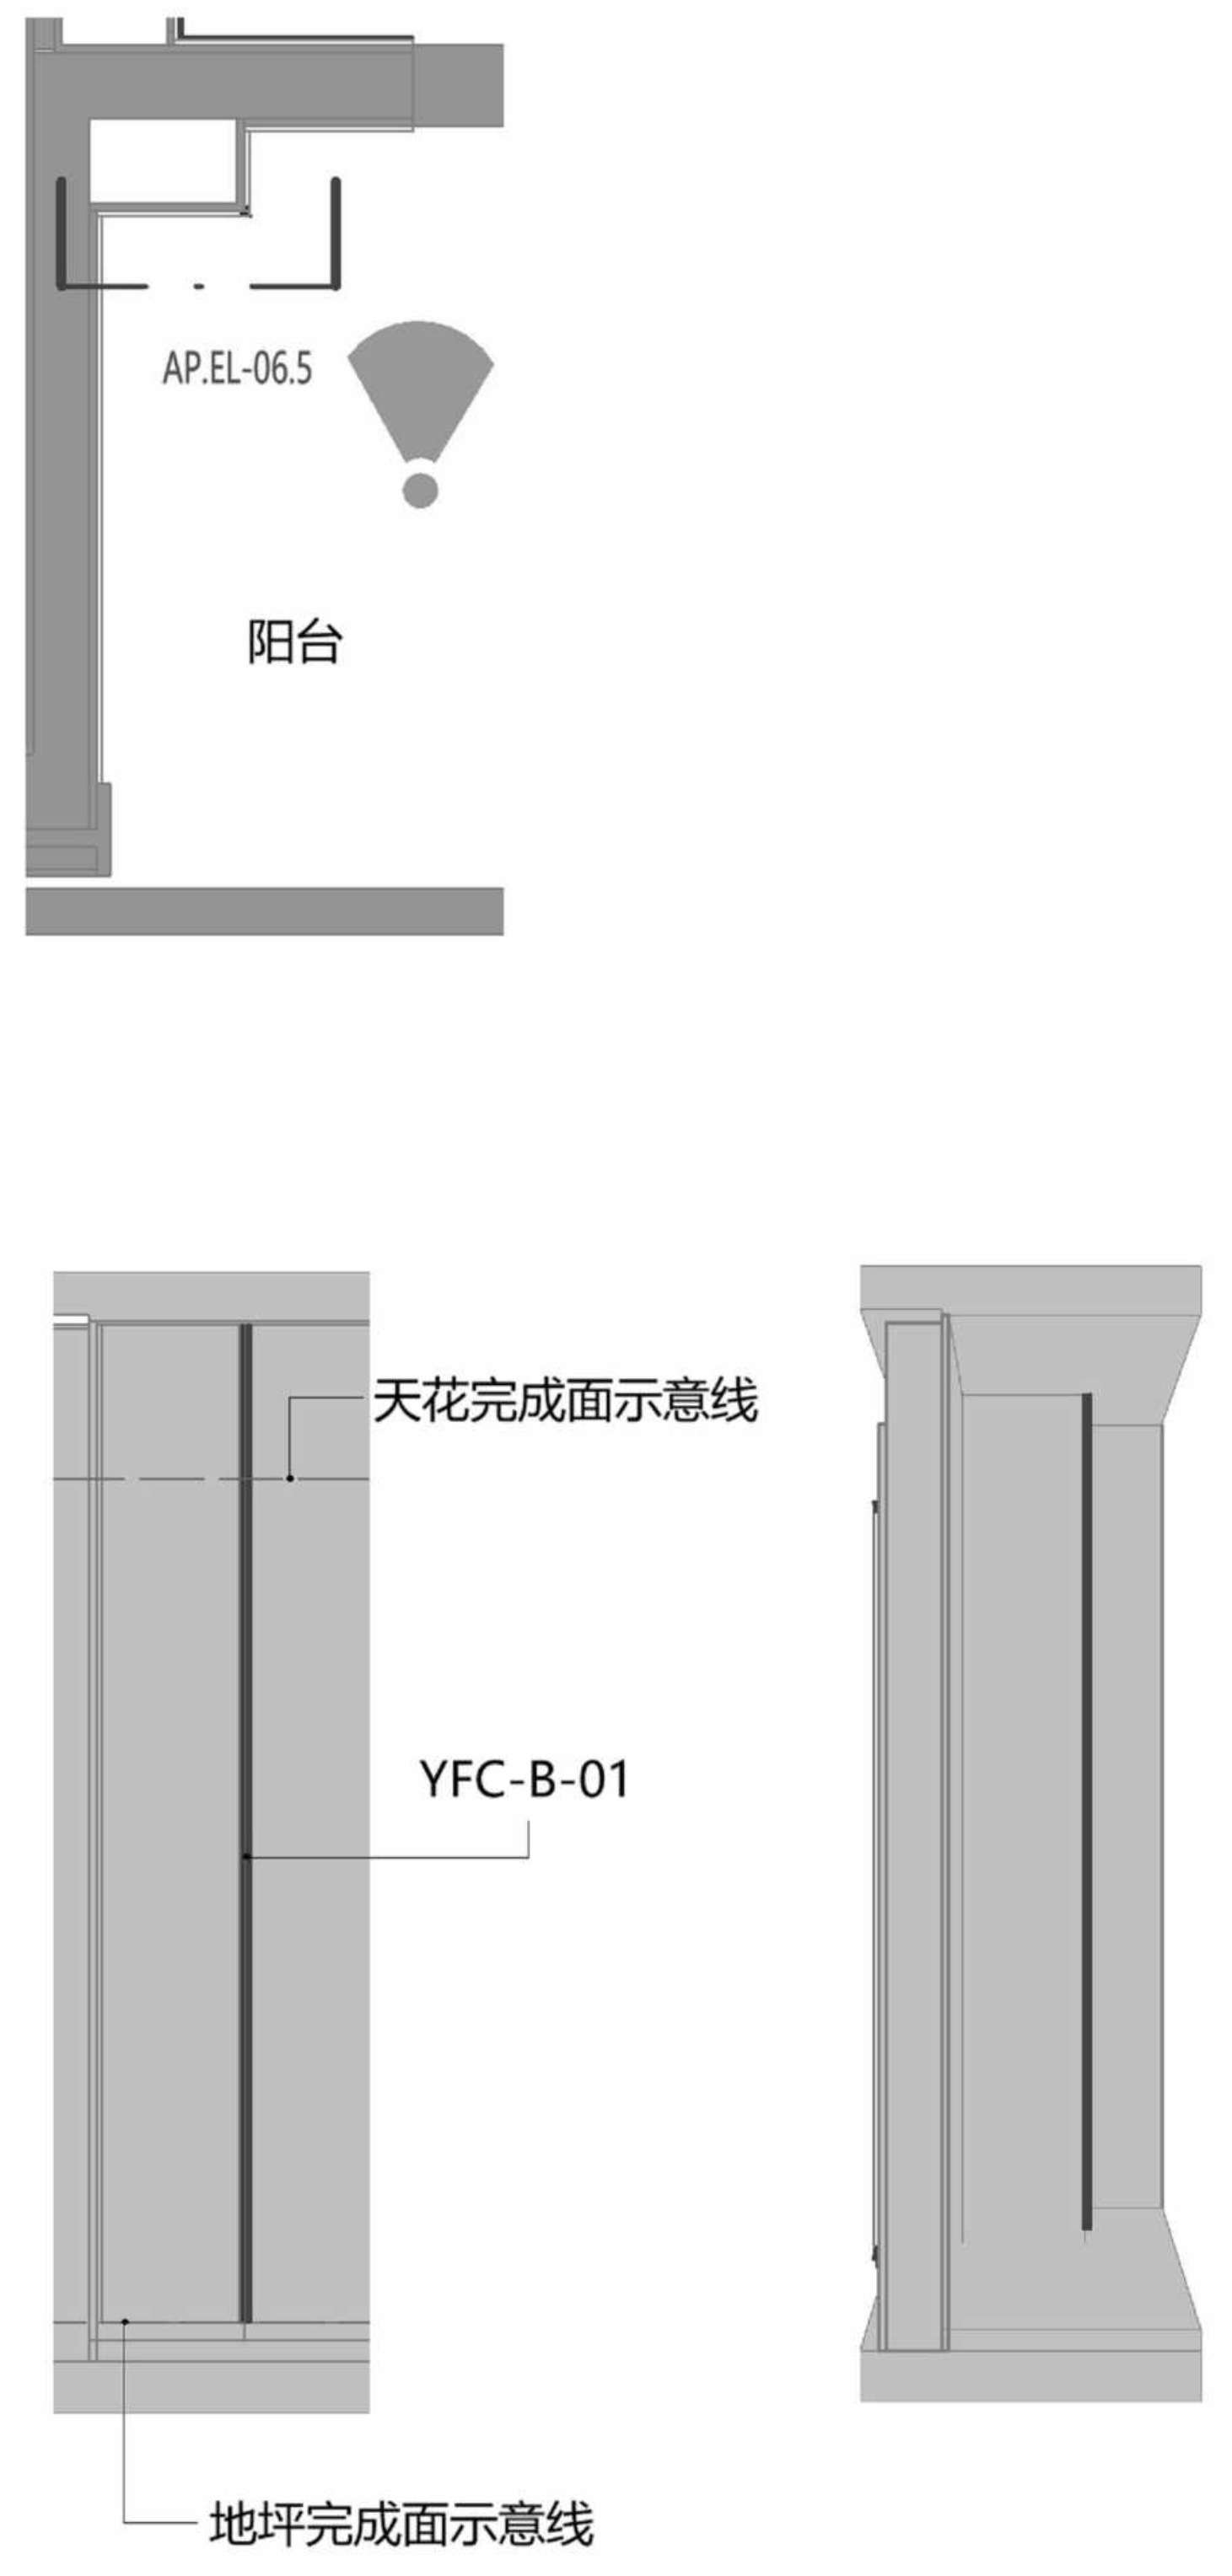
AP.EL-06.5
阳台
天花完成面示意线
YFC-B-01
地坪完成面示意线

5	阳台 墙面及踢脚铝型材立面图
	Scale比例 1：30@A2

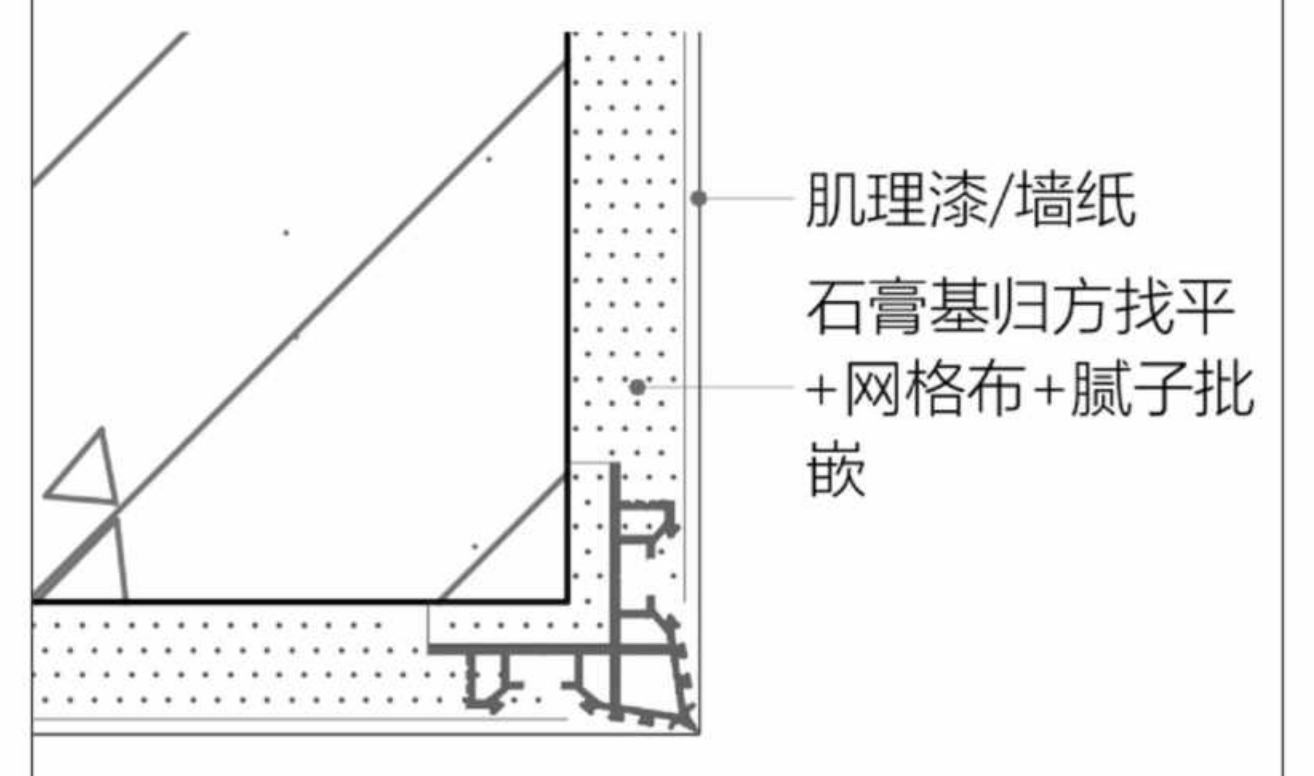
肌理漆/墙纸
石膏基归方找平+网格布+腻子批嵌

图例A-P1	墙面-石膏基找平铝型材
	Scale比例 1：1@A2

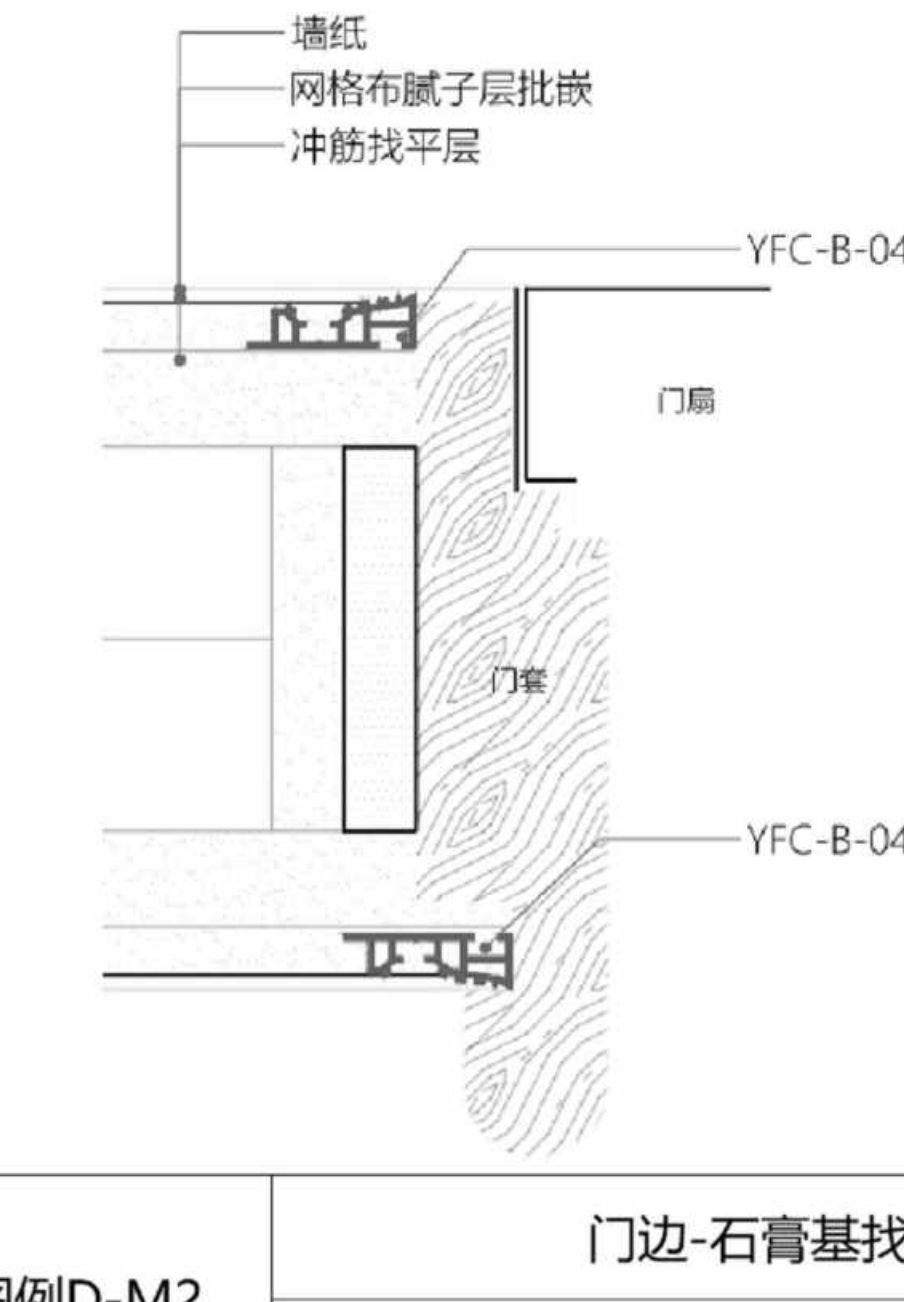
墙纸
网格布腻子层批嵌
冲筋找平层
YFC-B-04
门扇
门套
YFC-B-04

图例D-M2	门边-石膏基找平铝型材
	Scale比例 1：1@A2

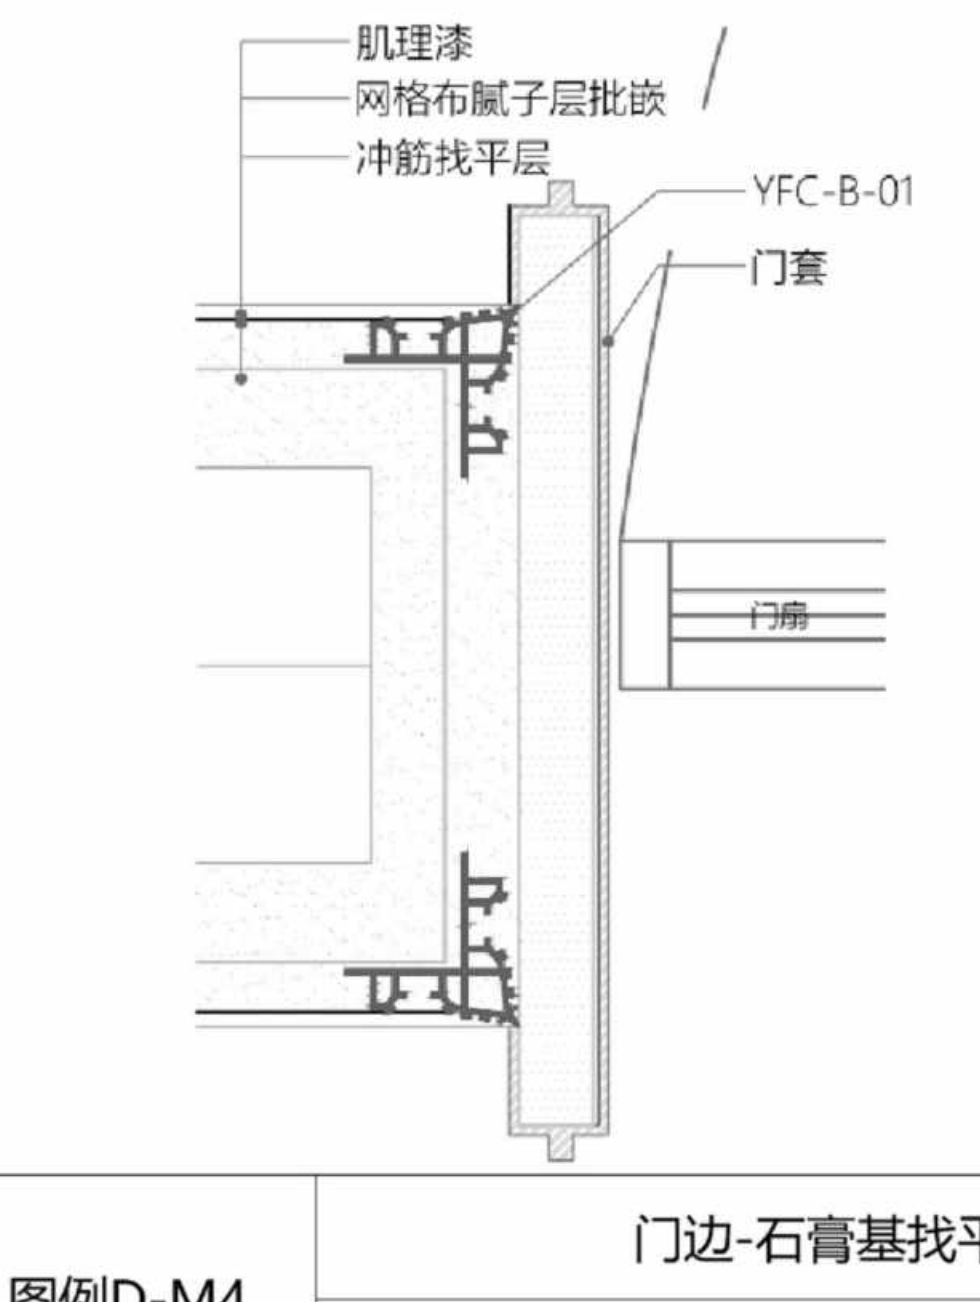
肌理漆
网格布腻子层批嵌
冲筋找平层
YFC-B-01
门套
门扇

图例D-M4	门边-石膏基找平铝型材
	Scale比例 1：1@A2

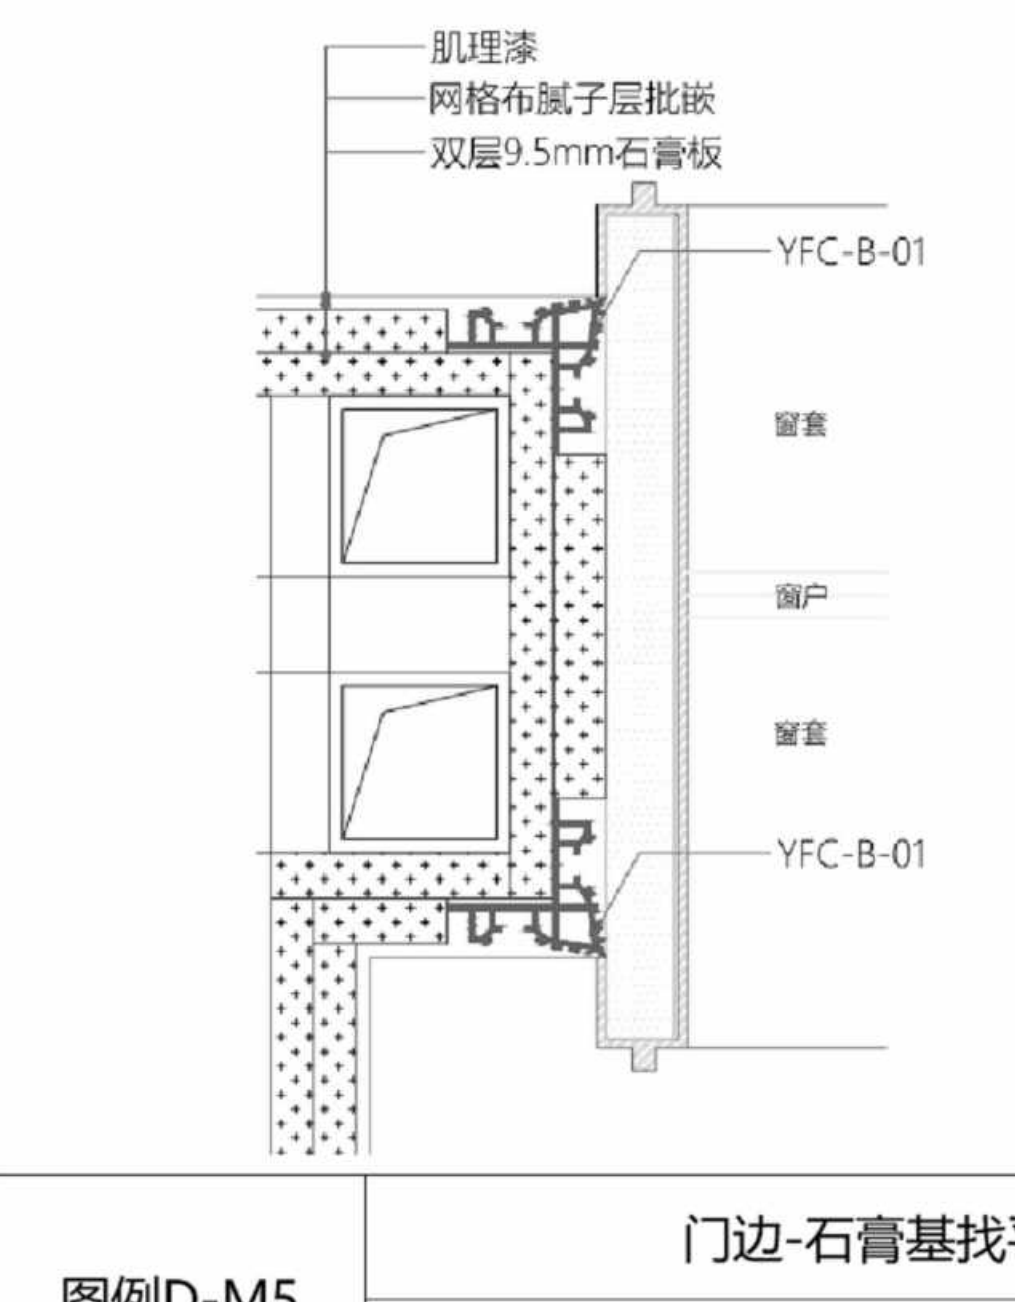
肌理漆
网格布腻子层批嵌
双层9.5mm石膏板
YFC-B-01
窗套
窗户
窗套
YFC-B-01

图例D-M5	门边-石膏基找平铝型材
	Scale比例 1：1@A2

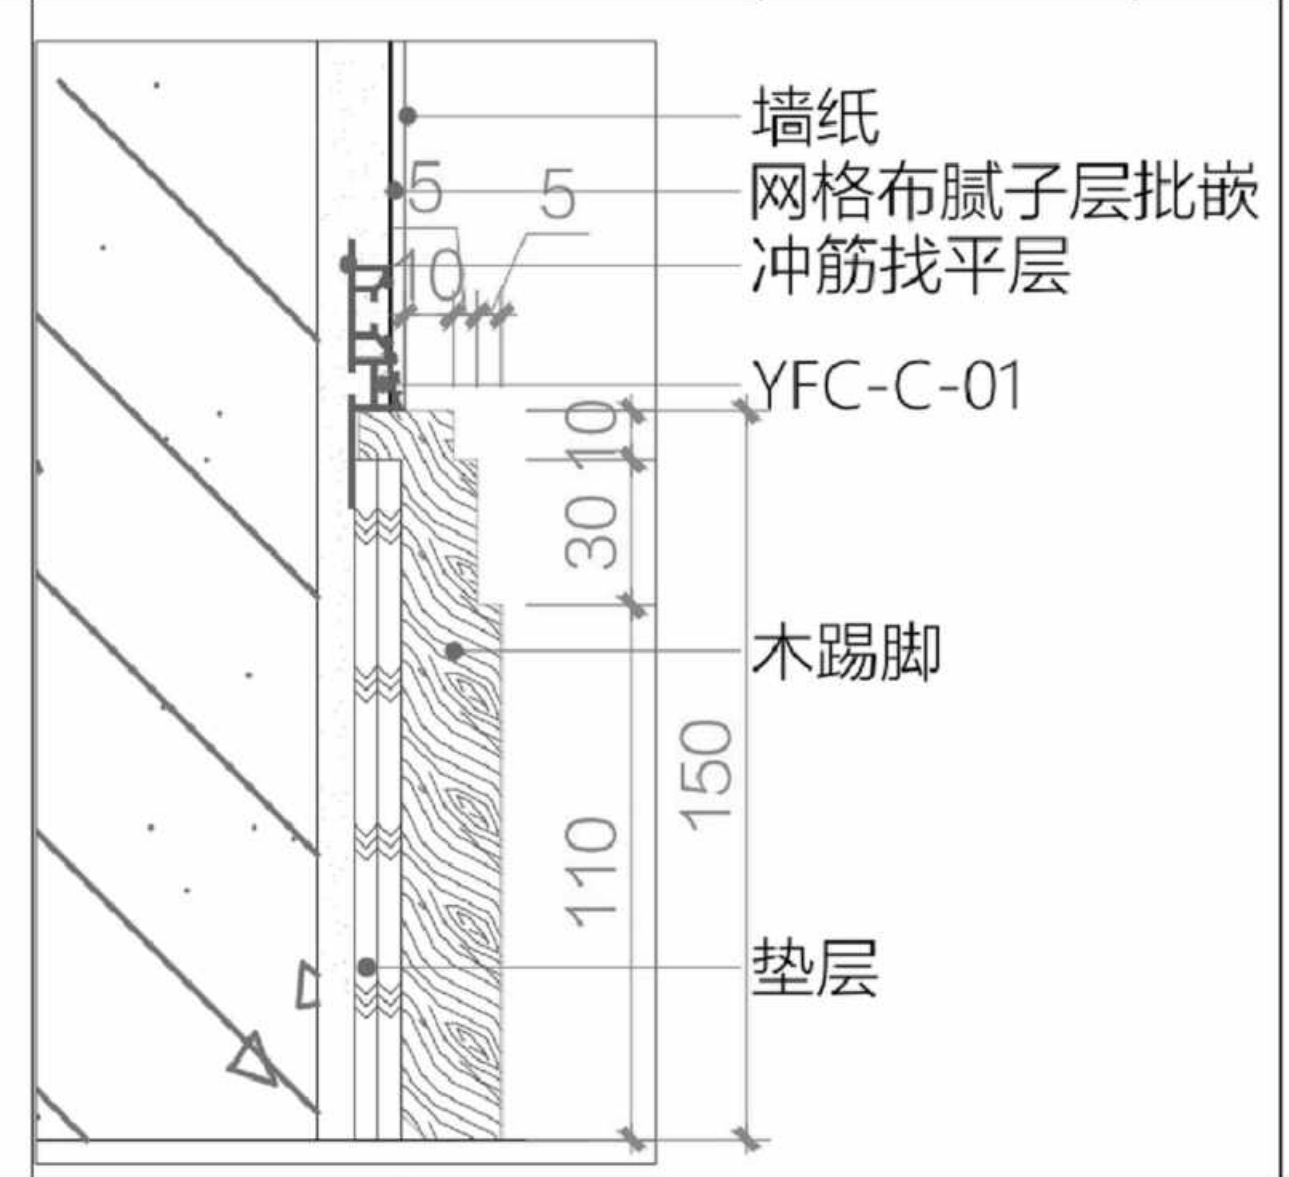
墙纸
网格布腻子层批嵌
冲筋找平层
YFC-C-01
木踢脚
垫层
5
5
10
10
30
150
110

图例E-SP1	踢脚-石膏基找平铝型材
	Scale比例 1：1@A2

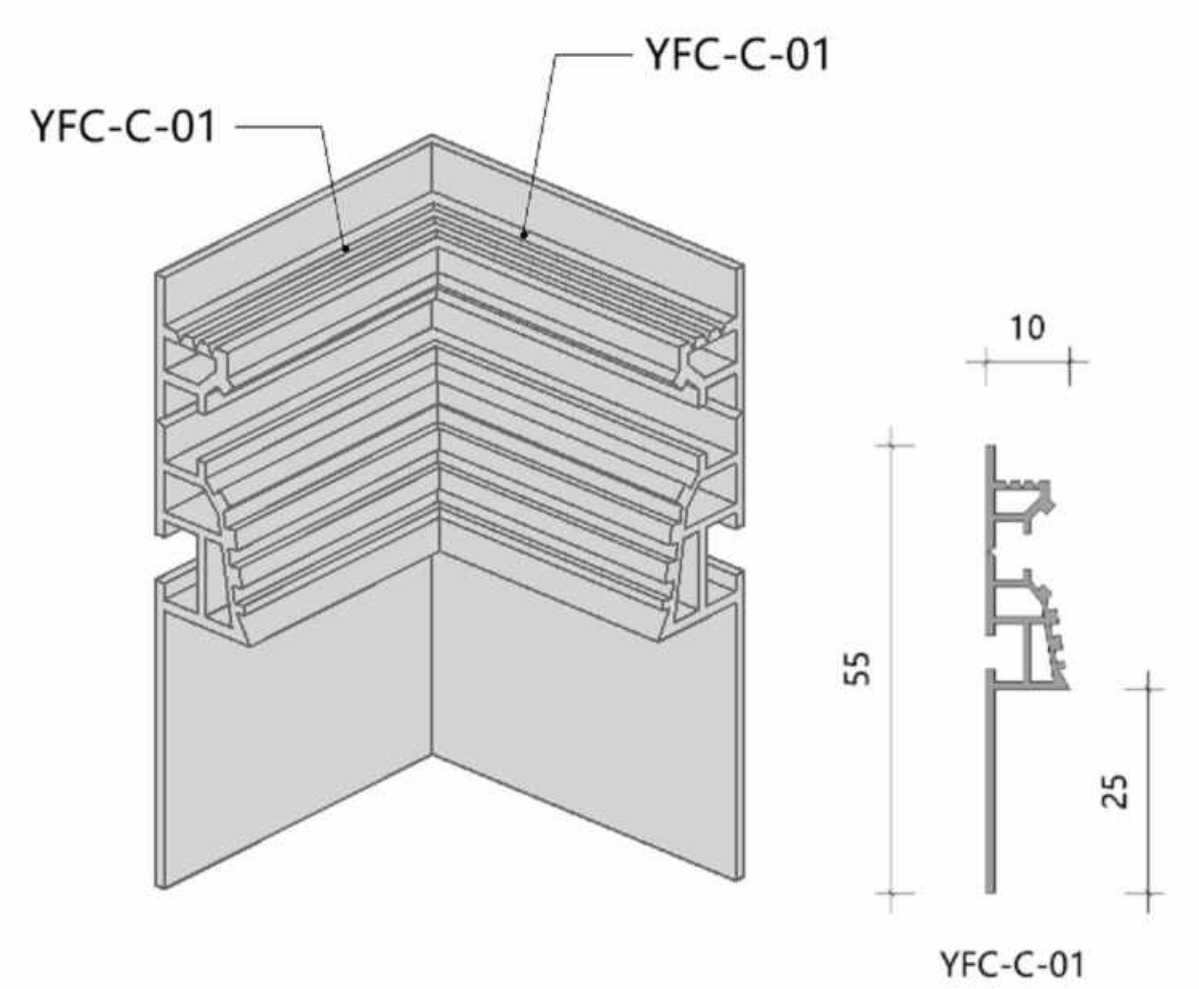
YFC-C-01
YFC-C-01
10
55
25
YFC-C-01

3D-05	转角铝型材-拼接跟通
	转角数量：1

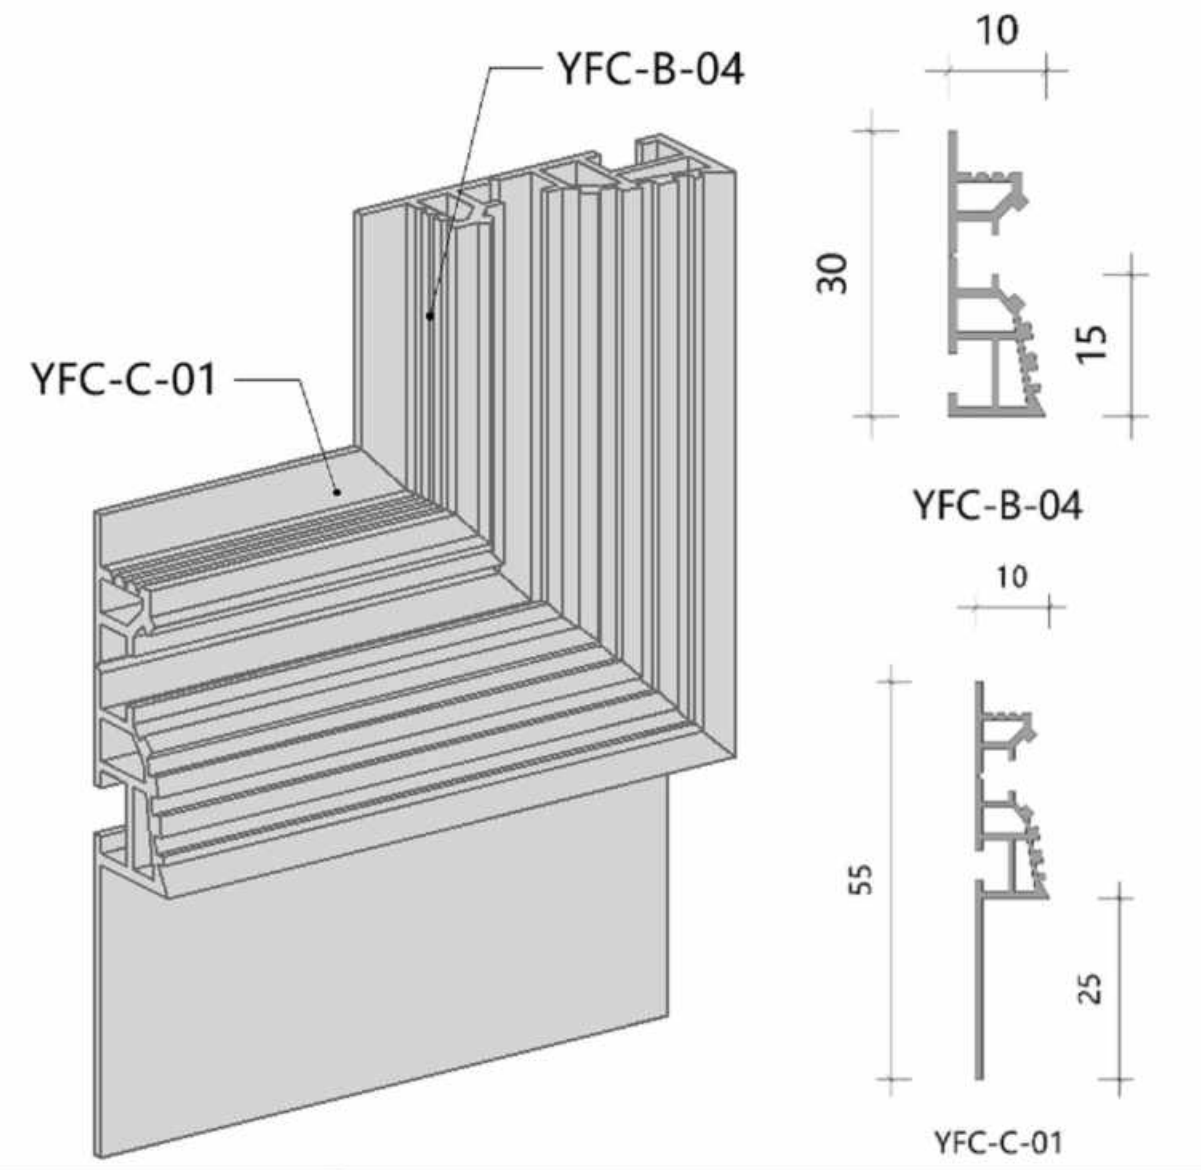
YFC-B-04
YFC-C-01
10
30
15
YFC-B-04
10
55
25
YFC-C-01

3D-06	转角铝型材-拼接跟通
	转角数量：1

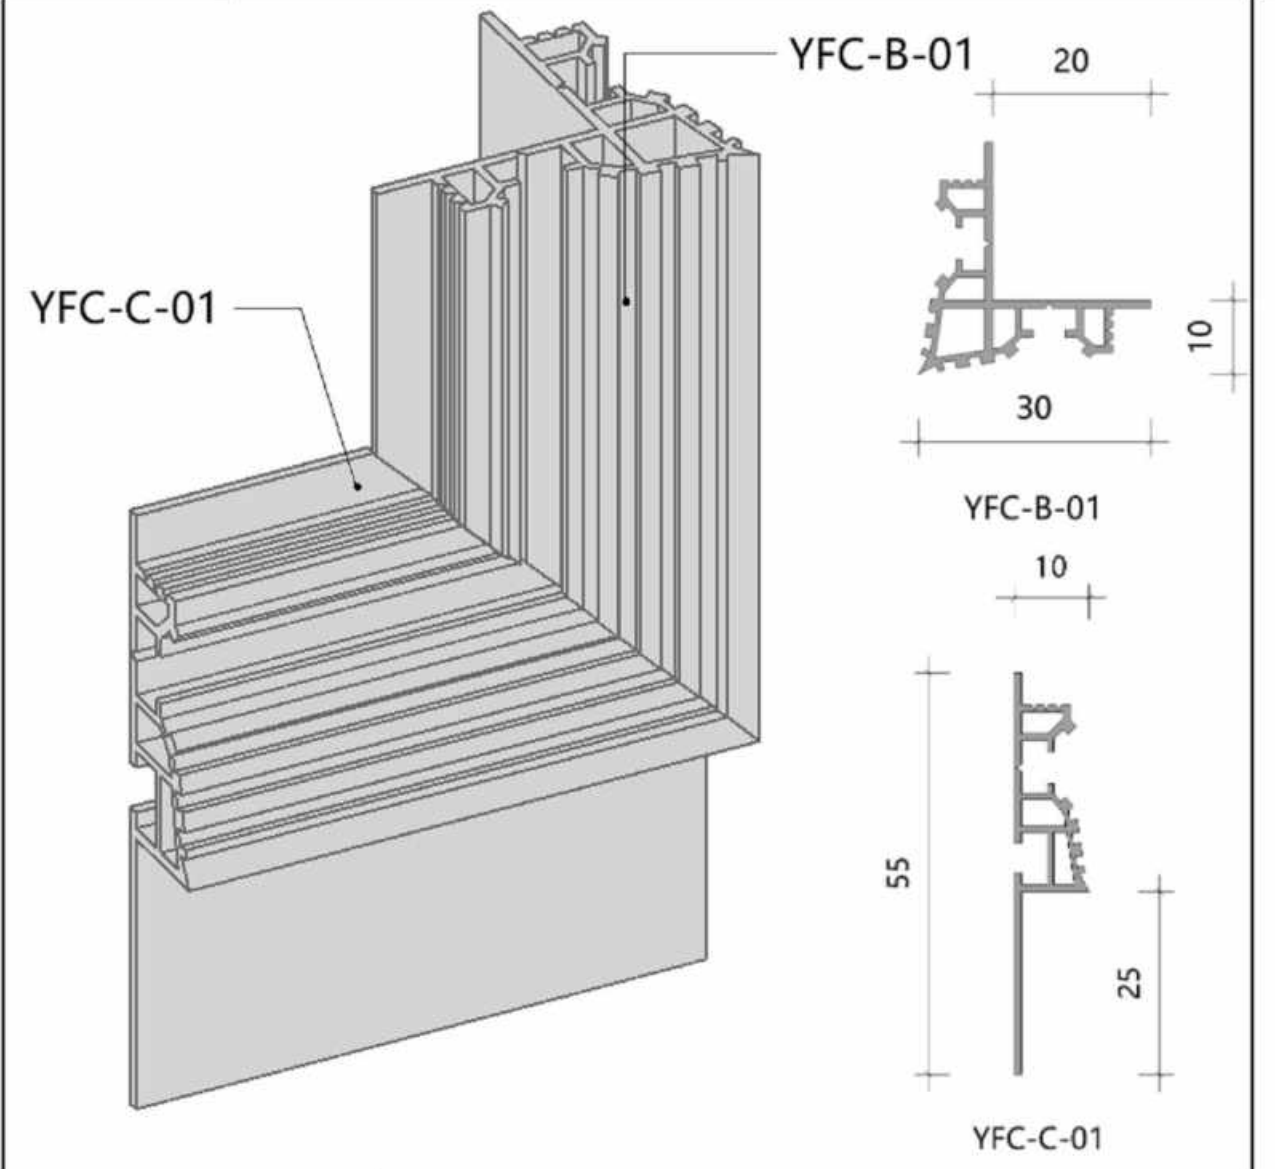
YFC-B-01
YFC-C-01
20
10
30
YFC-B-01
10
55
25
YFC-C-01

3D-07	转角铝型材-拼接跟通
	转角数量：3

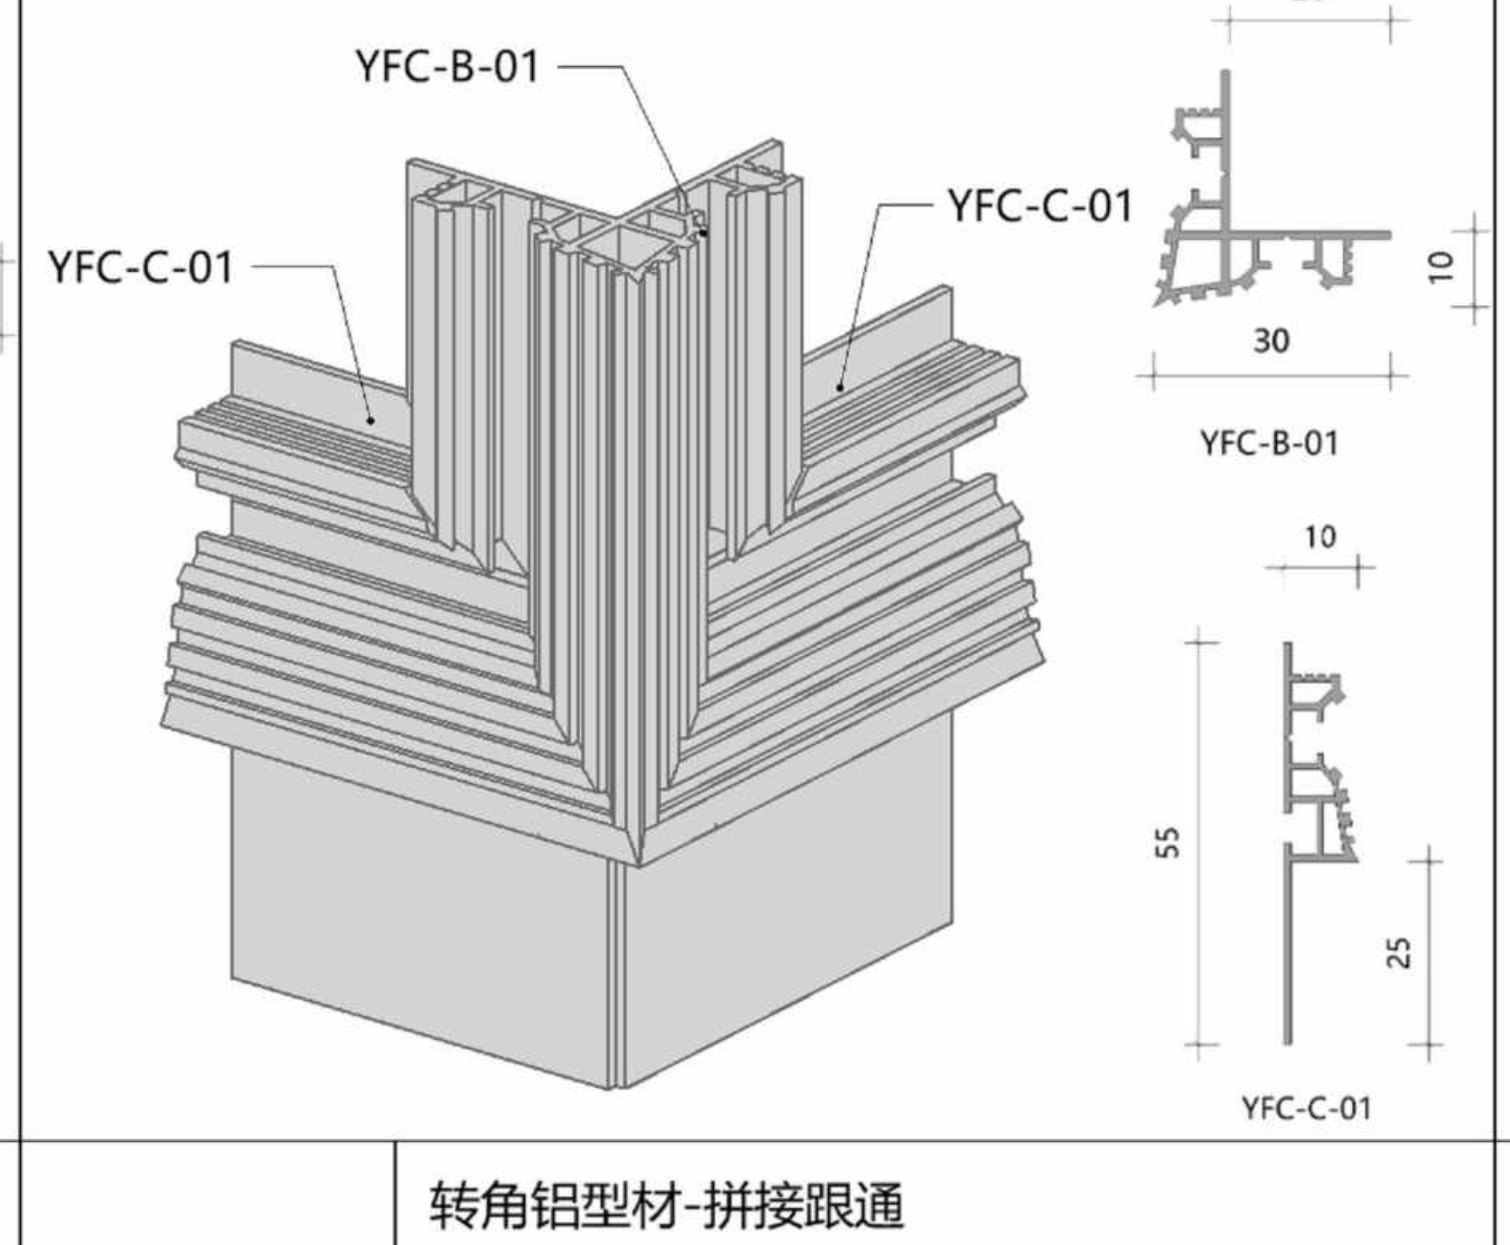
YFC-B-01
YFC-C-01
YFC-C-01
20
10
30
YFC-B-01
10
55
25
YFC-C-01

3D-11	转角铝型材-拼接跟通
	转角数量：1

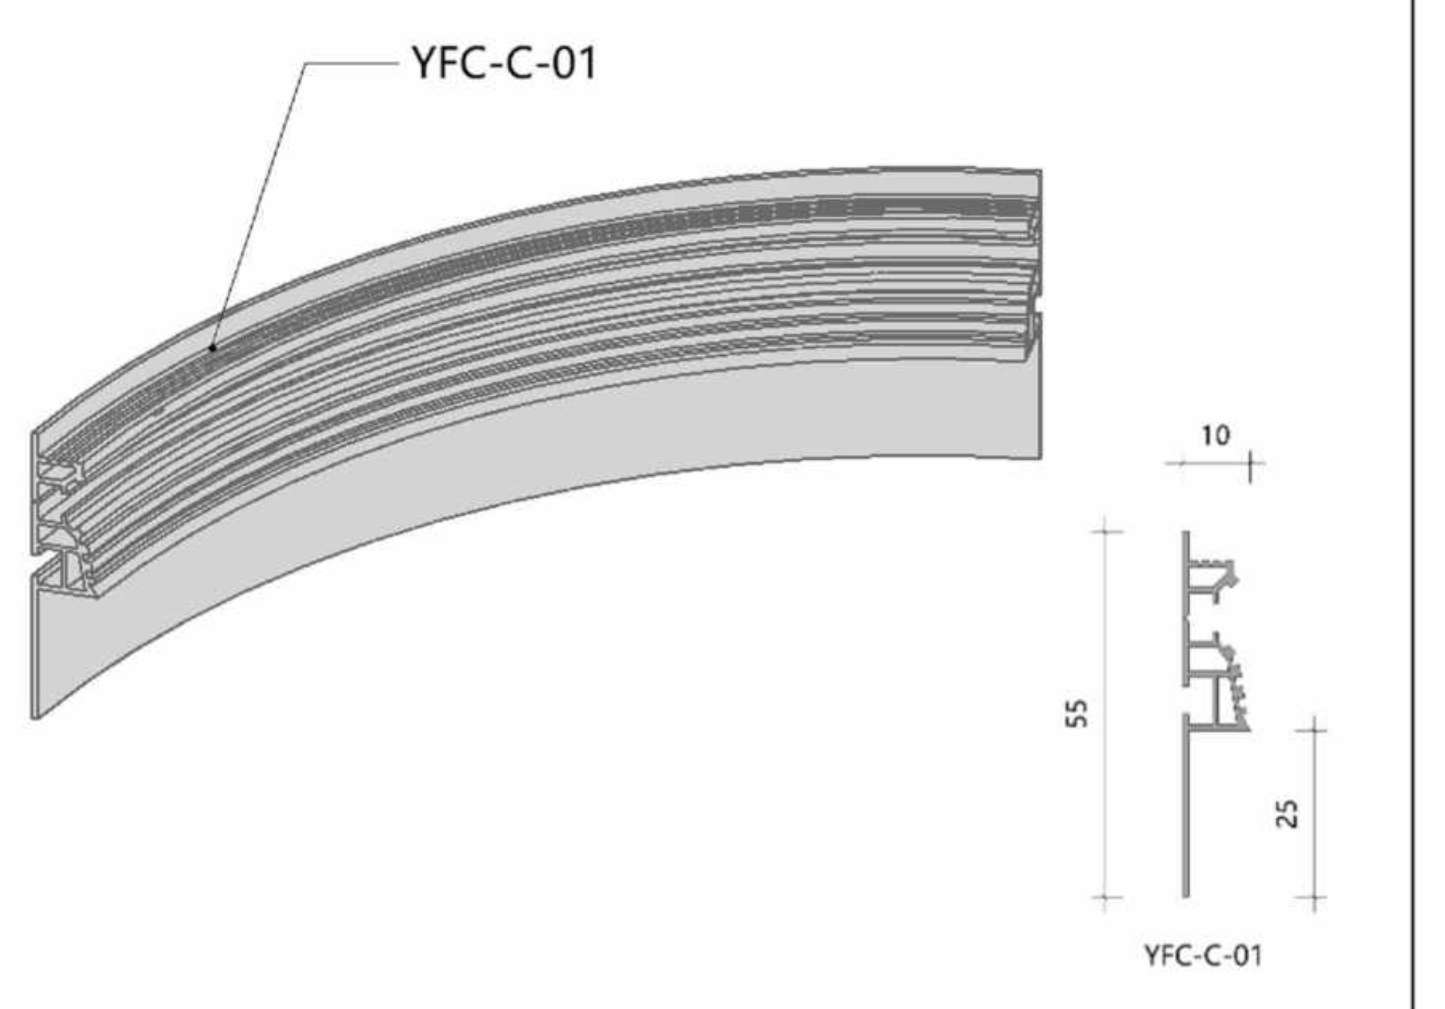
YFC-C-01
10
55
25
YFC-C-01

3D-17	转角铝型材-拼接跟通
	转角数量：1

盖章

注释
Notes
1.本图纸如与现场尺寸有误，请施工人员与项目负责人联系。
2.施工前施工人员应认真查阅此图，如有不明确尺寸，按现场测量为准。
3.本图纸必须经甲乙双方认可并签字方可作为施工依据。

日期
Date 03/04/26

修订
Revision
1

项目
Project
潮映华岸府3-801

比例
Scale
猫房、阳台
墙面及踢脚铝型材

图纸编号
Drawing No.
AP.EL-06

项目编号
Project No.
©2025

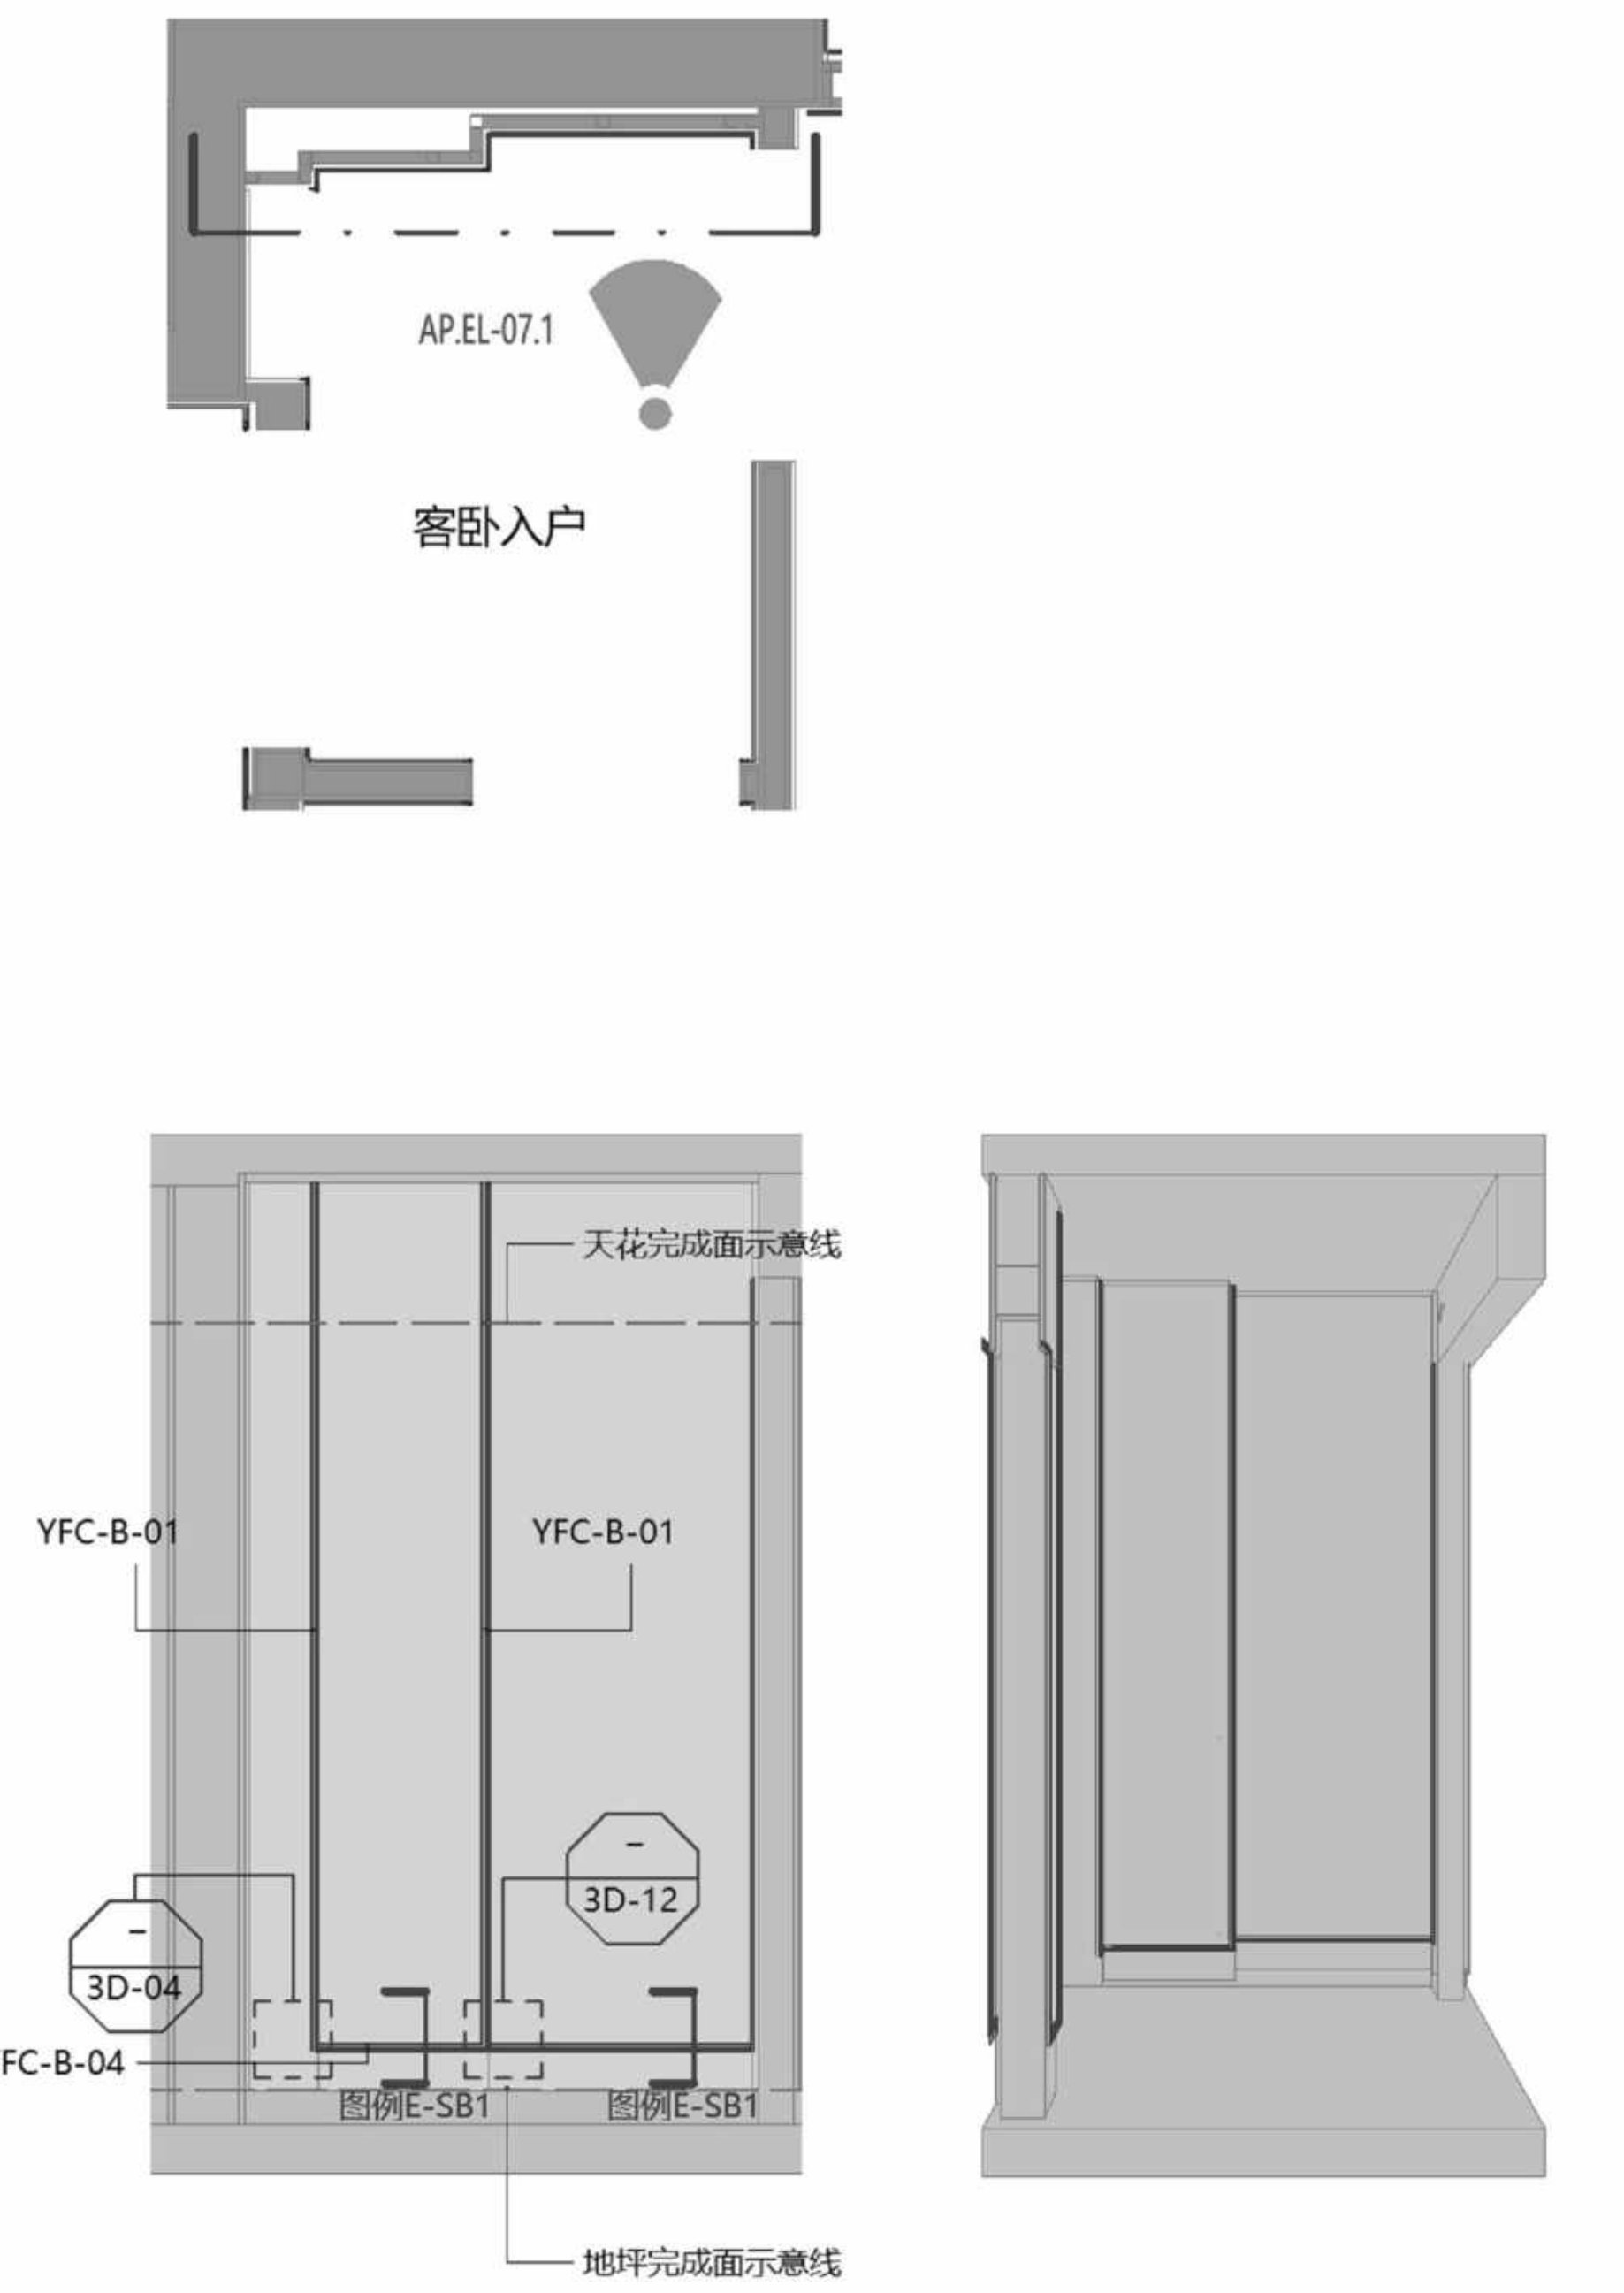
AP.EL-07.1
客卧入户
天花完成面示意线
YFC-B-01
YFC-B-01
–
3D-04
–
3D-12
YFC-B-04
图例E-SB1
图例E-SB1
地坪完成面示意线

1 客卧入户 墙面及踢脚铝型材立面图1

Scale比例 1 : 30@A2

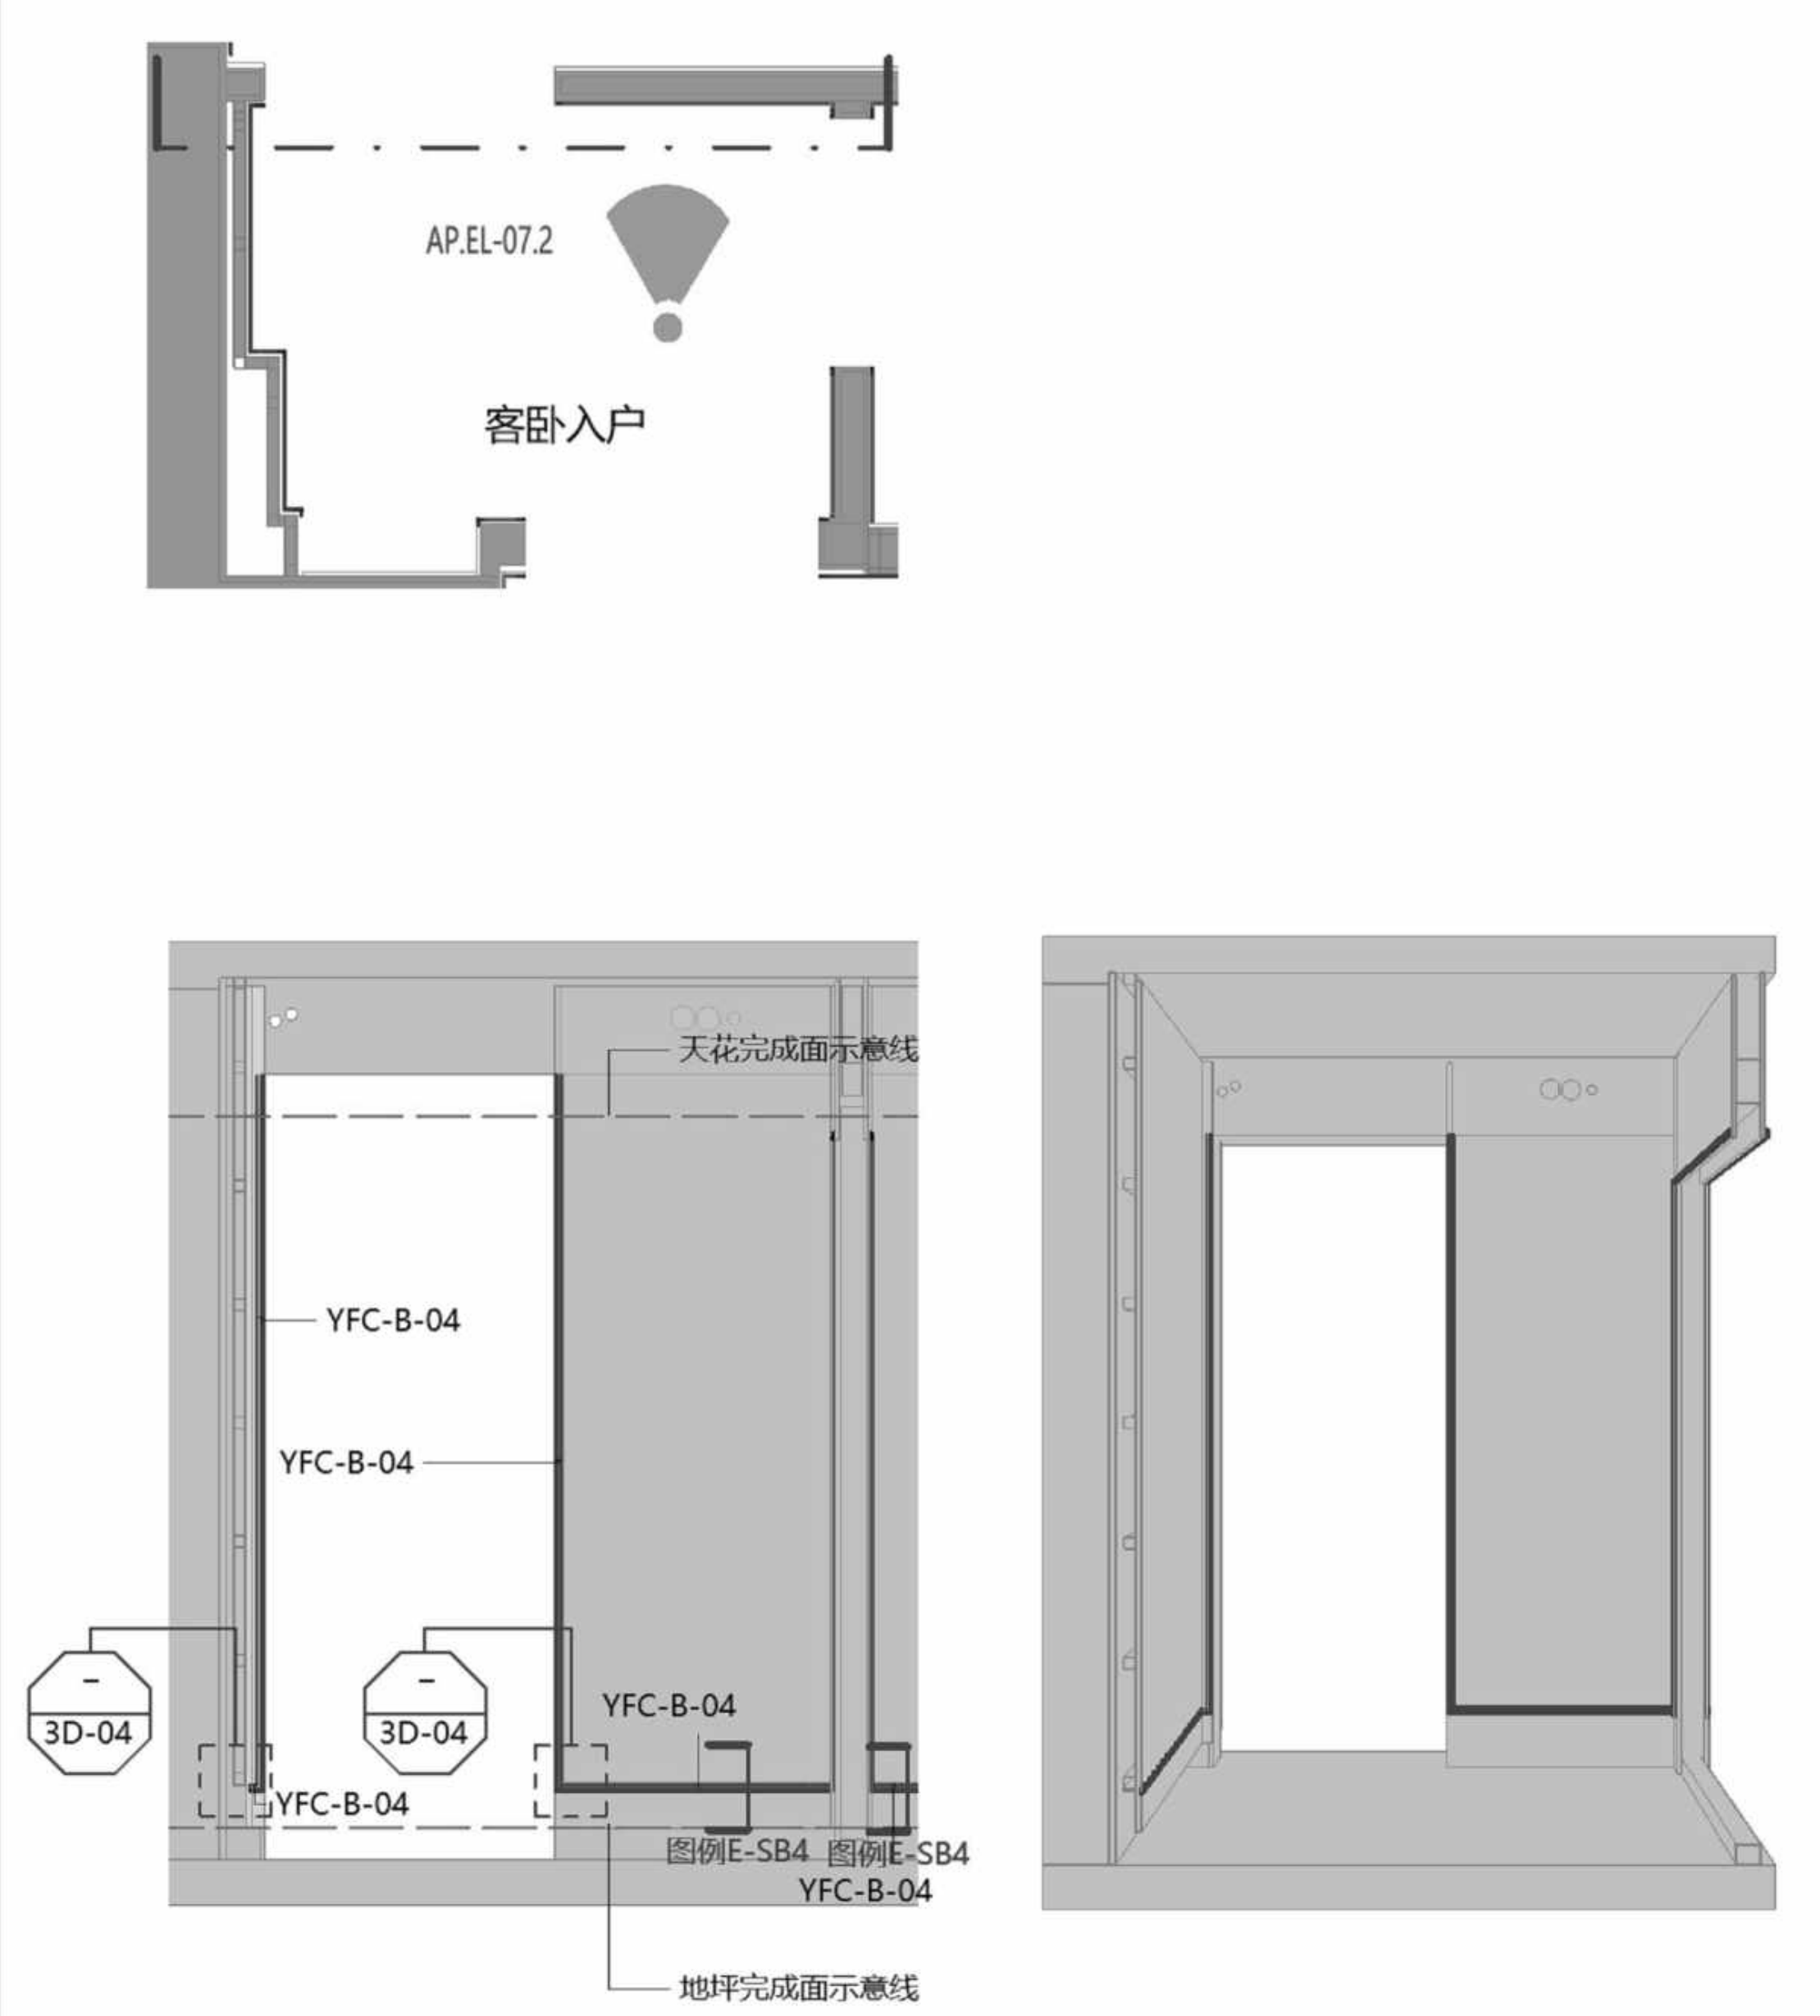
AP.EL-07.2
客卧入户
天花完成面示意线
YFC-B-04
YFC-B-04
–
3D-04
–
3D-04
YFC-B-04
YFC-B-04
图例E-SB4
图例E-SB4
YFC-B-04
地坪完成面示意线

2 客卧入户 墙面及踢脚铝型材立面图2

Scale比例 1 : 30@A2

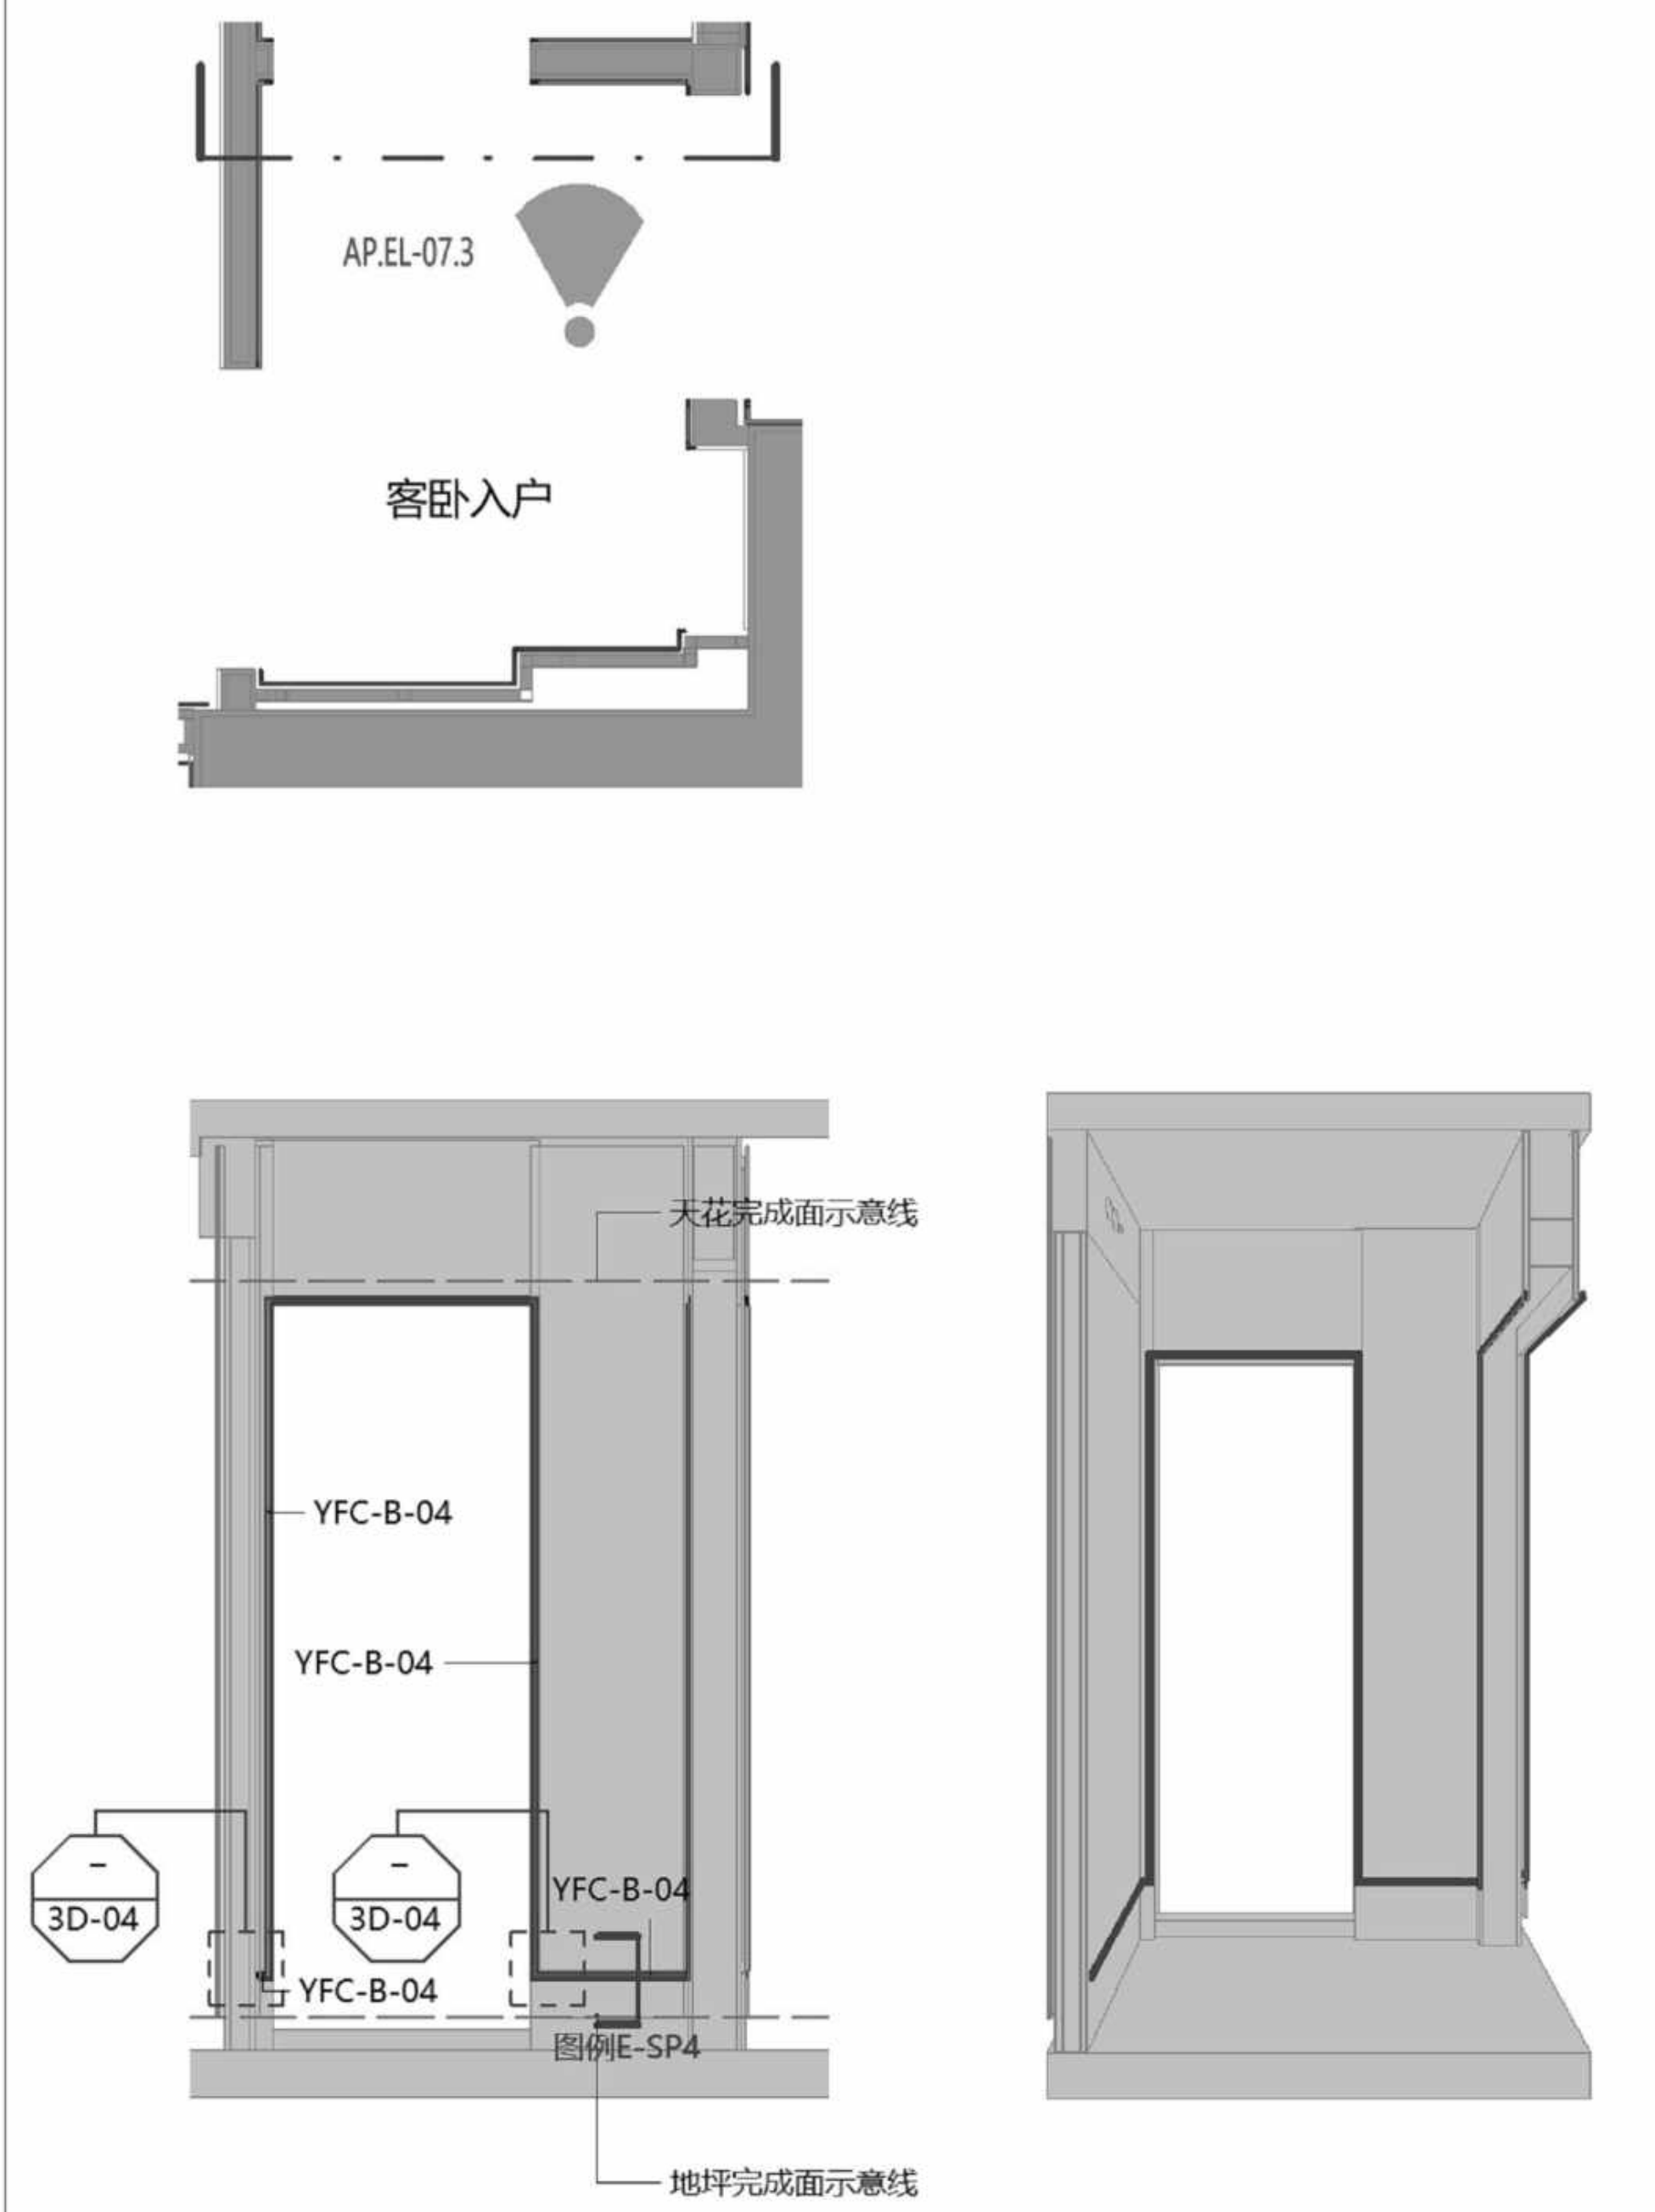
AP.EL-07.3
客卧入户
天花完成面示意线
YFC-B-04
YFC-B-04
–
3D-04
–
3D-04
YFC-B-04
YFC-B-04
图例E-SP4
地坪完成面示意线

3 客卧入户 墙面及踢脚铝型材立面图3

Scale比例 1 : 30@A2

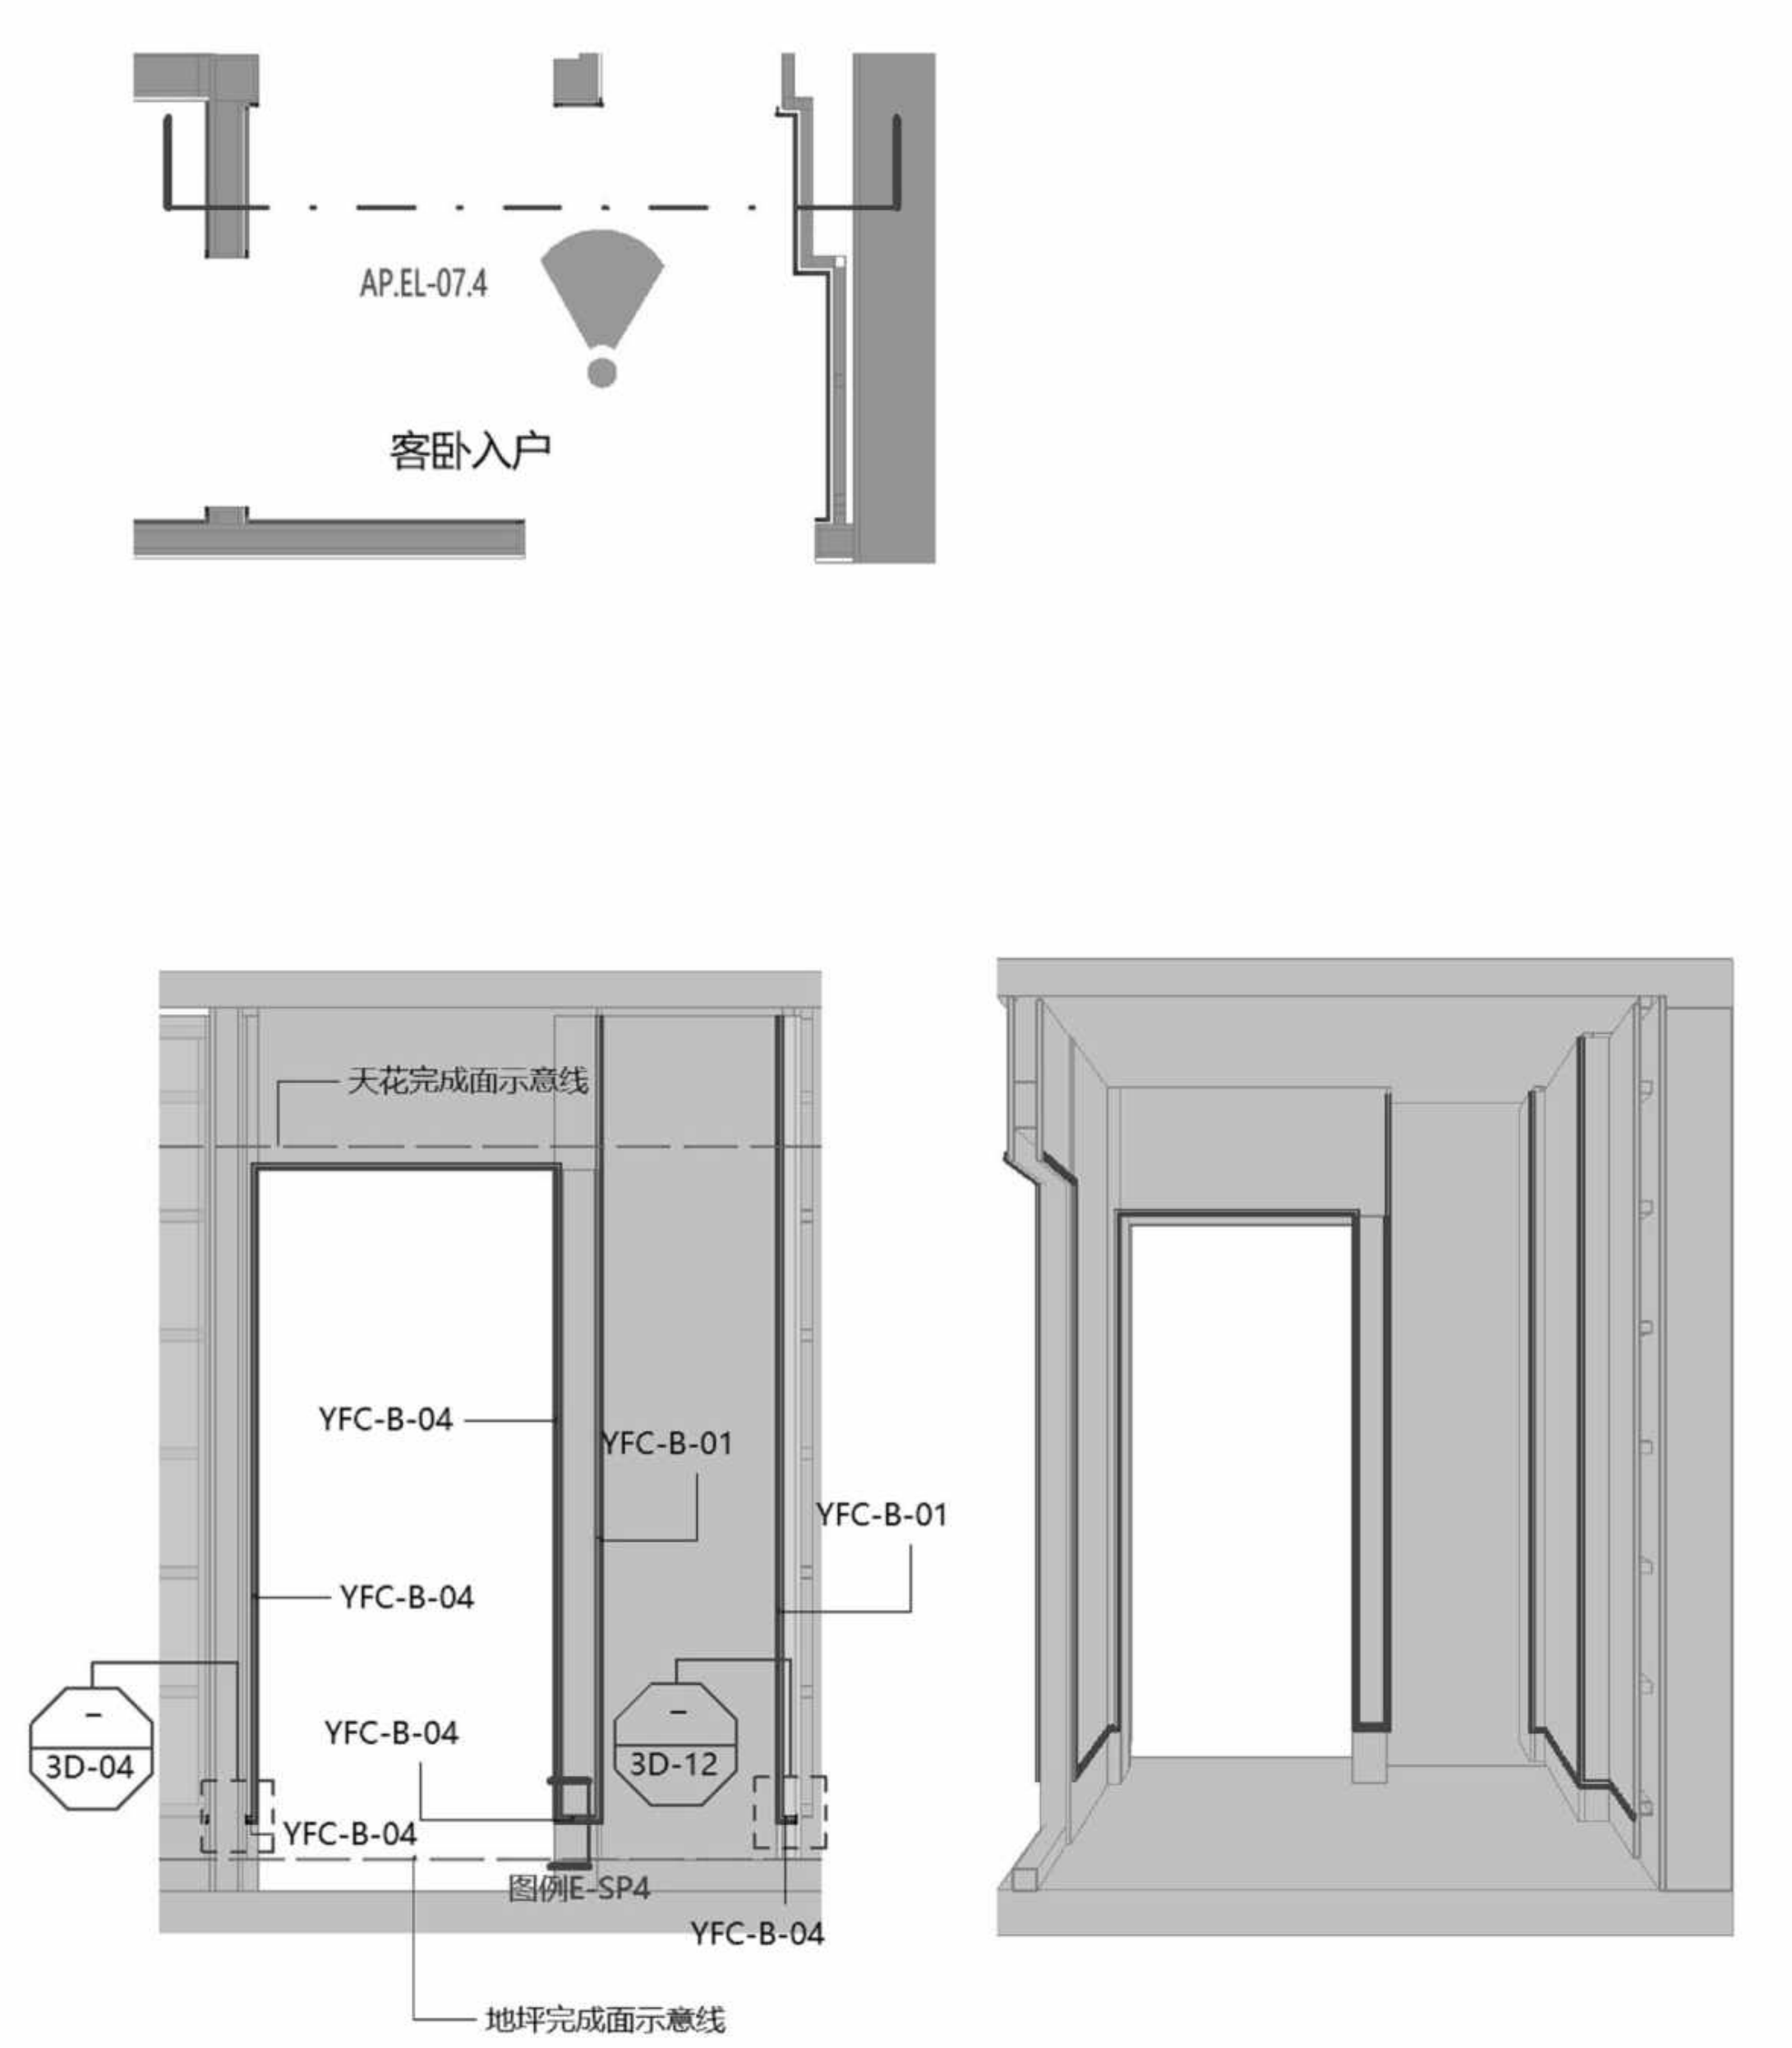
AP.EL-07.4
客卧入户
天花完成面示意线
YFC-B-04
YFC-B-01
YFC-B-01
YFC-B-04
YFC-B-04
–
3D-04
–
3D-12
YFC-B-04
图例E-SP4
YFC-B-04
地坪完成面示意线

4 客卧入户 墙面及踢脚铝型材立面图4

Scale比例 1 : 30@A2

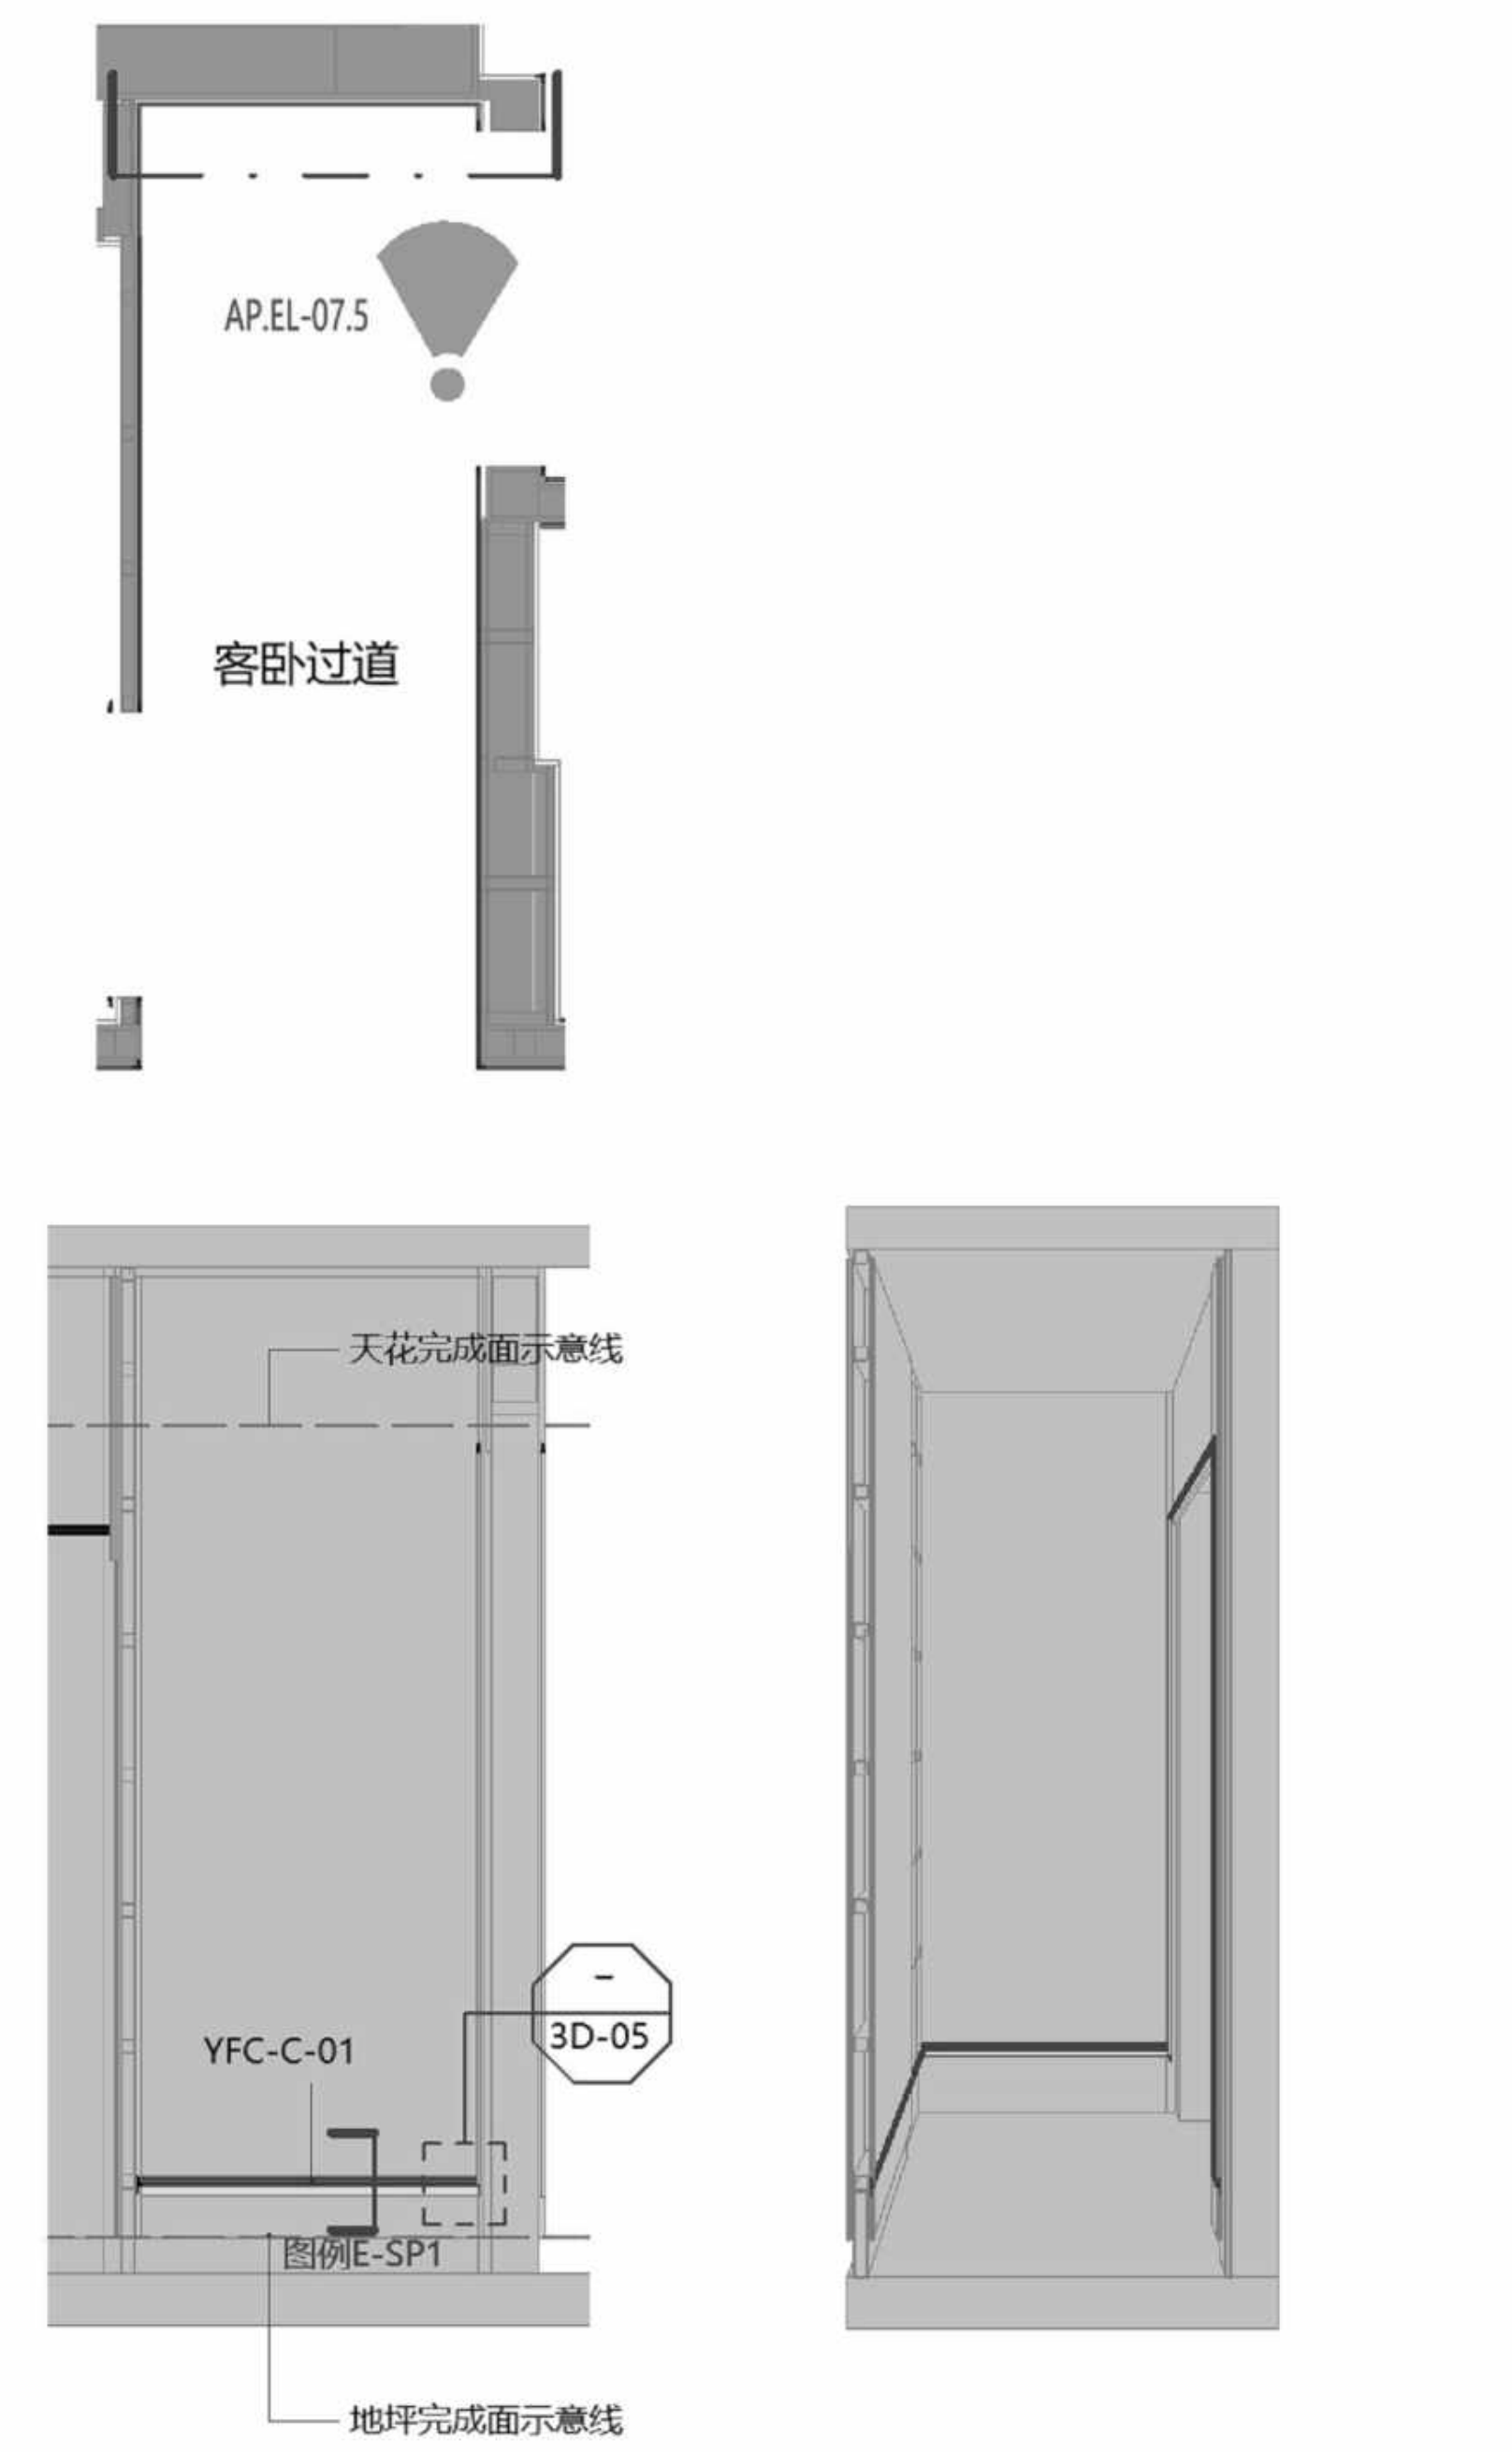
AP.EL-07.5
客卧过道
天花完成面示意线
YFC-C-01
–
3D-05
图例E-SP1
地坪完成面示意线

5 客卧过道 墙面及踢脚铝型材立面图1

Scale比例 1 : 30@A2

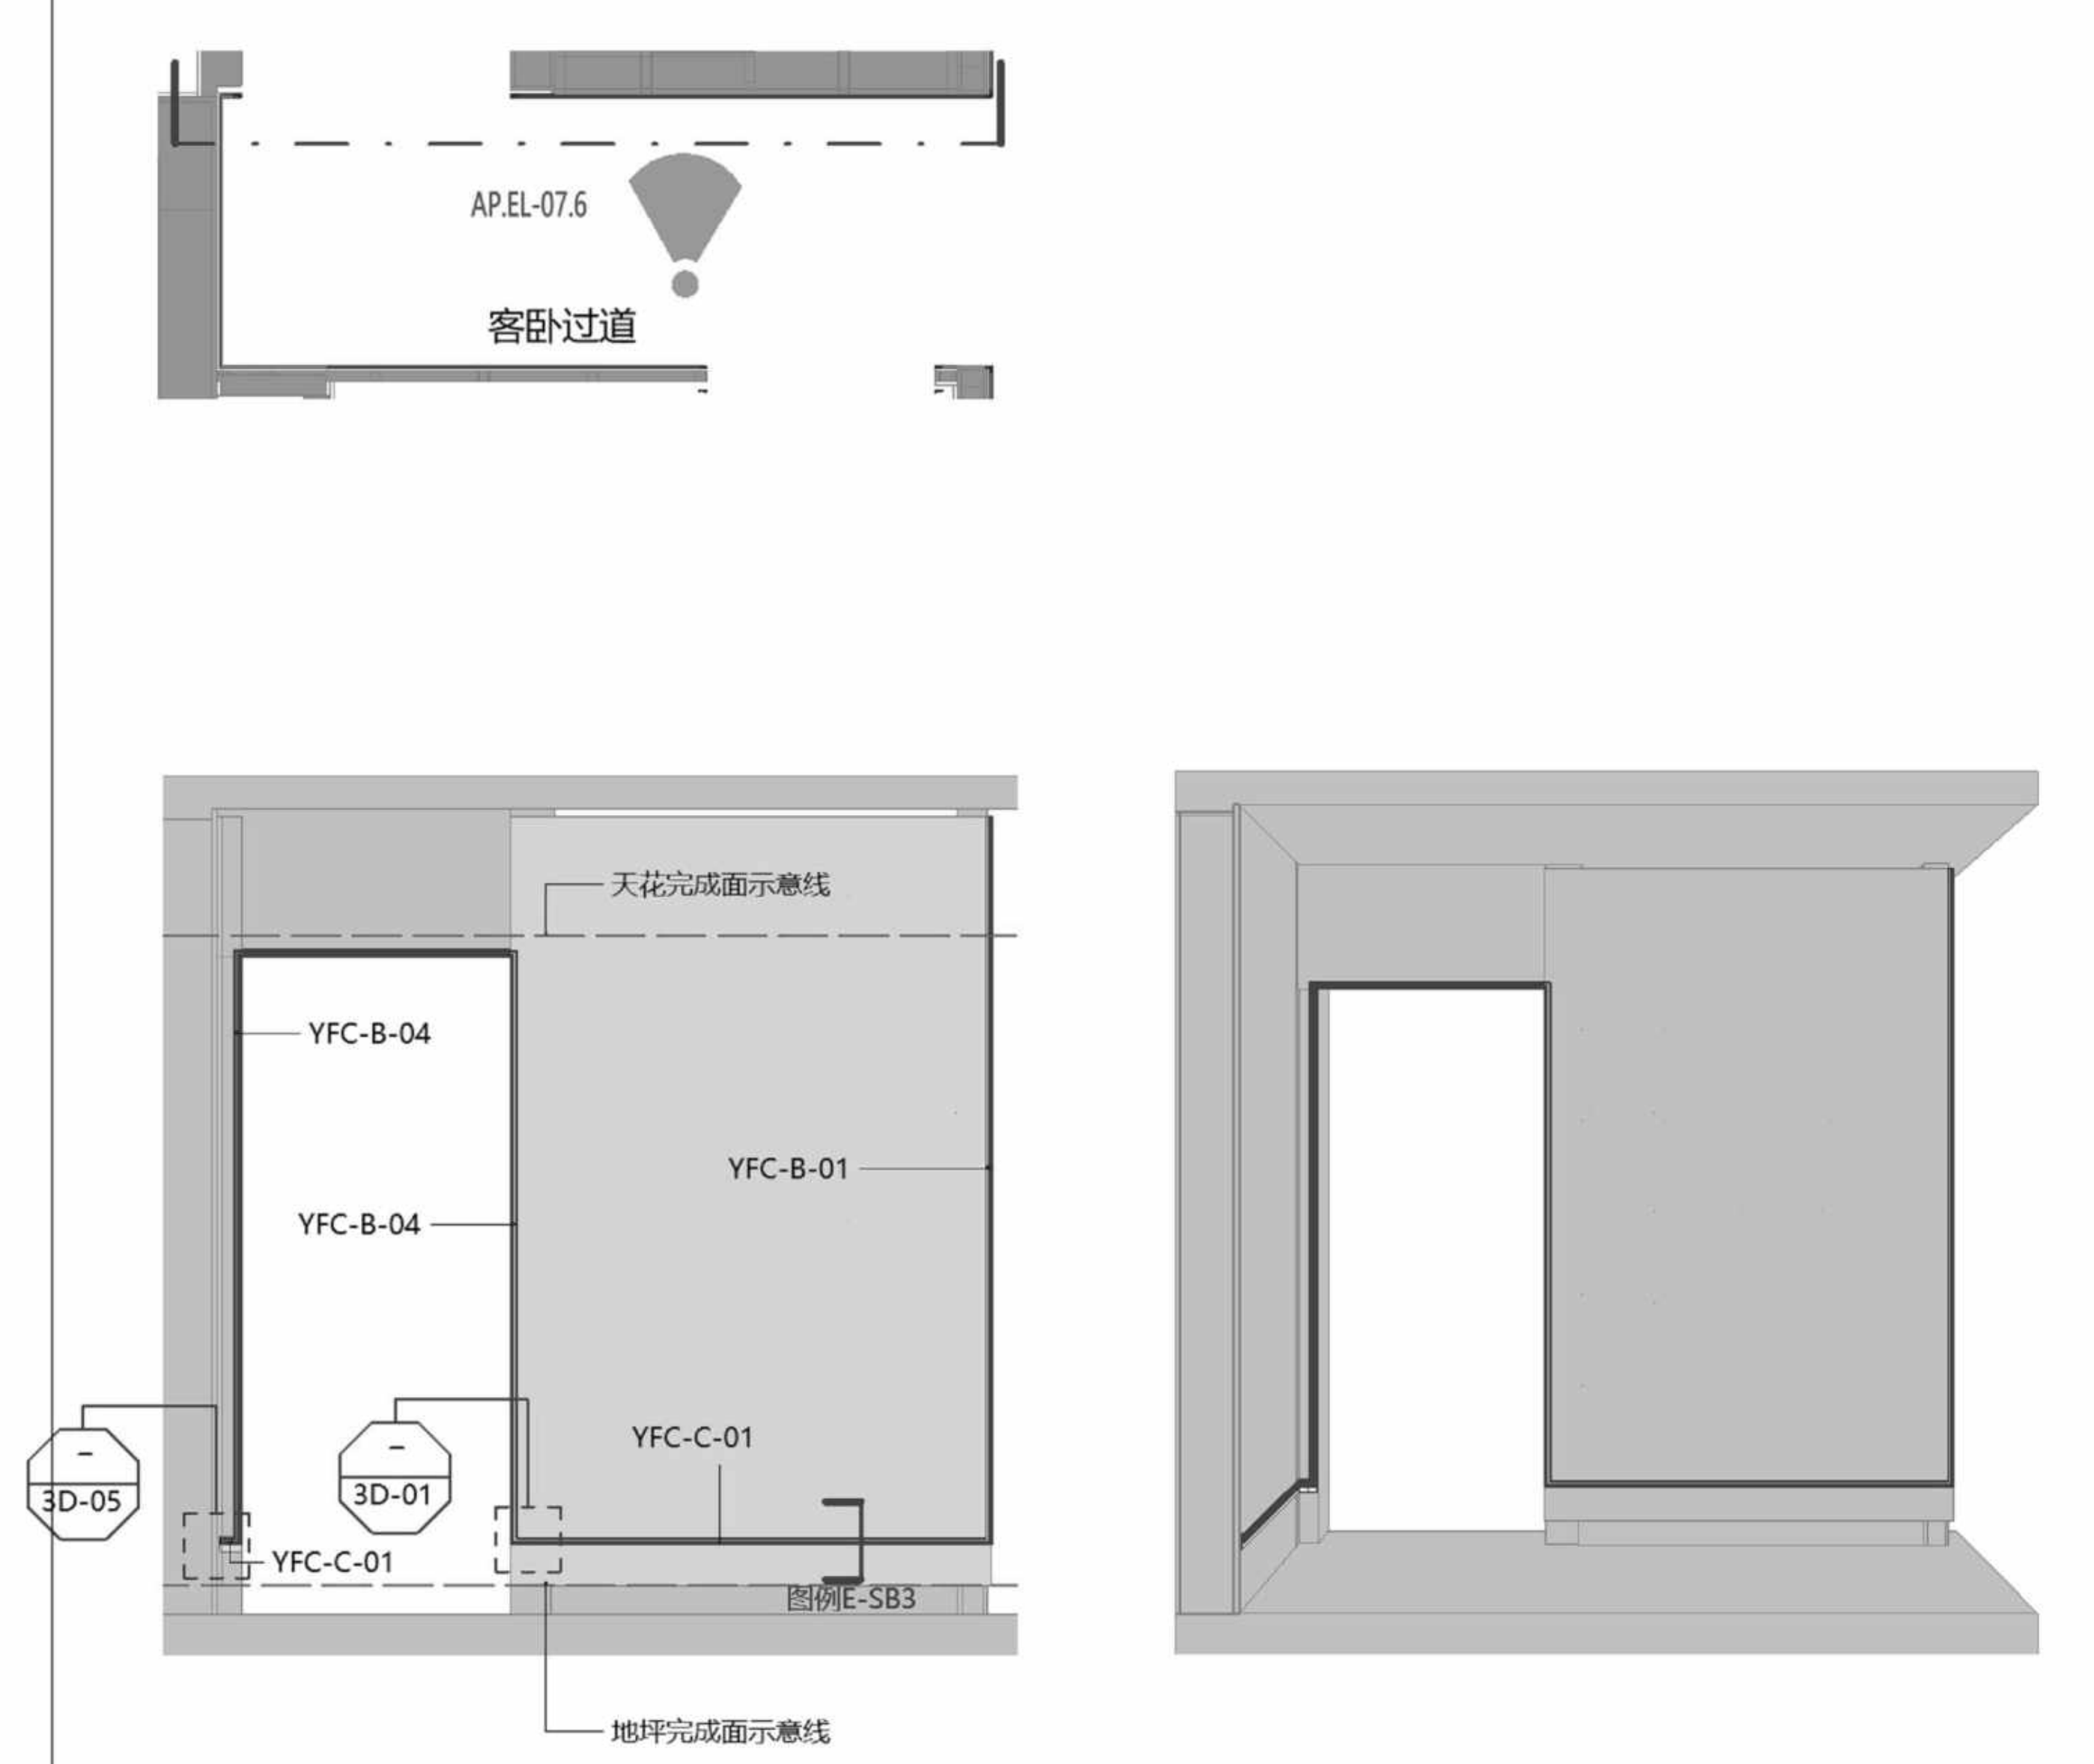
AP.EL-07.6
客卧过道
天花完成面示意线
YFC-B-04
YFC-B-01
YFC-B-04
–
3D-05
–
3D-01
YFC-C-01
YFC-C-01
图例E-SB3
地坪完成面示意线

6 客卧过道 墙面及踢脚铝型材立面图2

Scale比例 1 : 30@A2

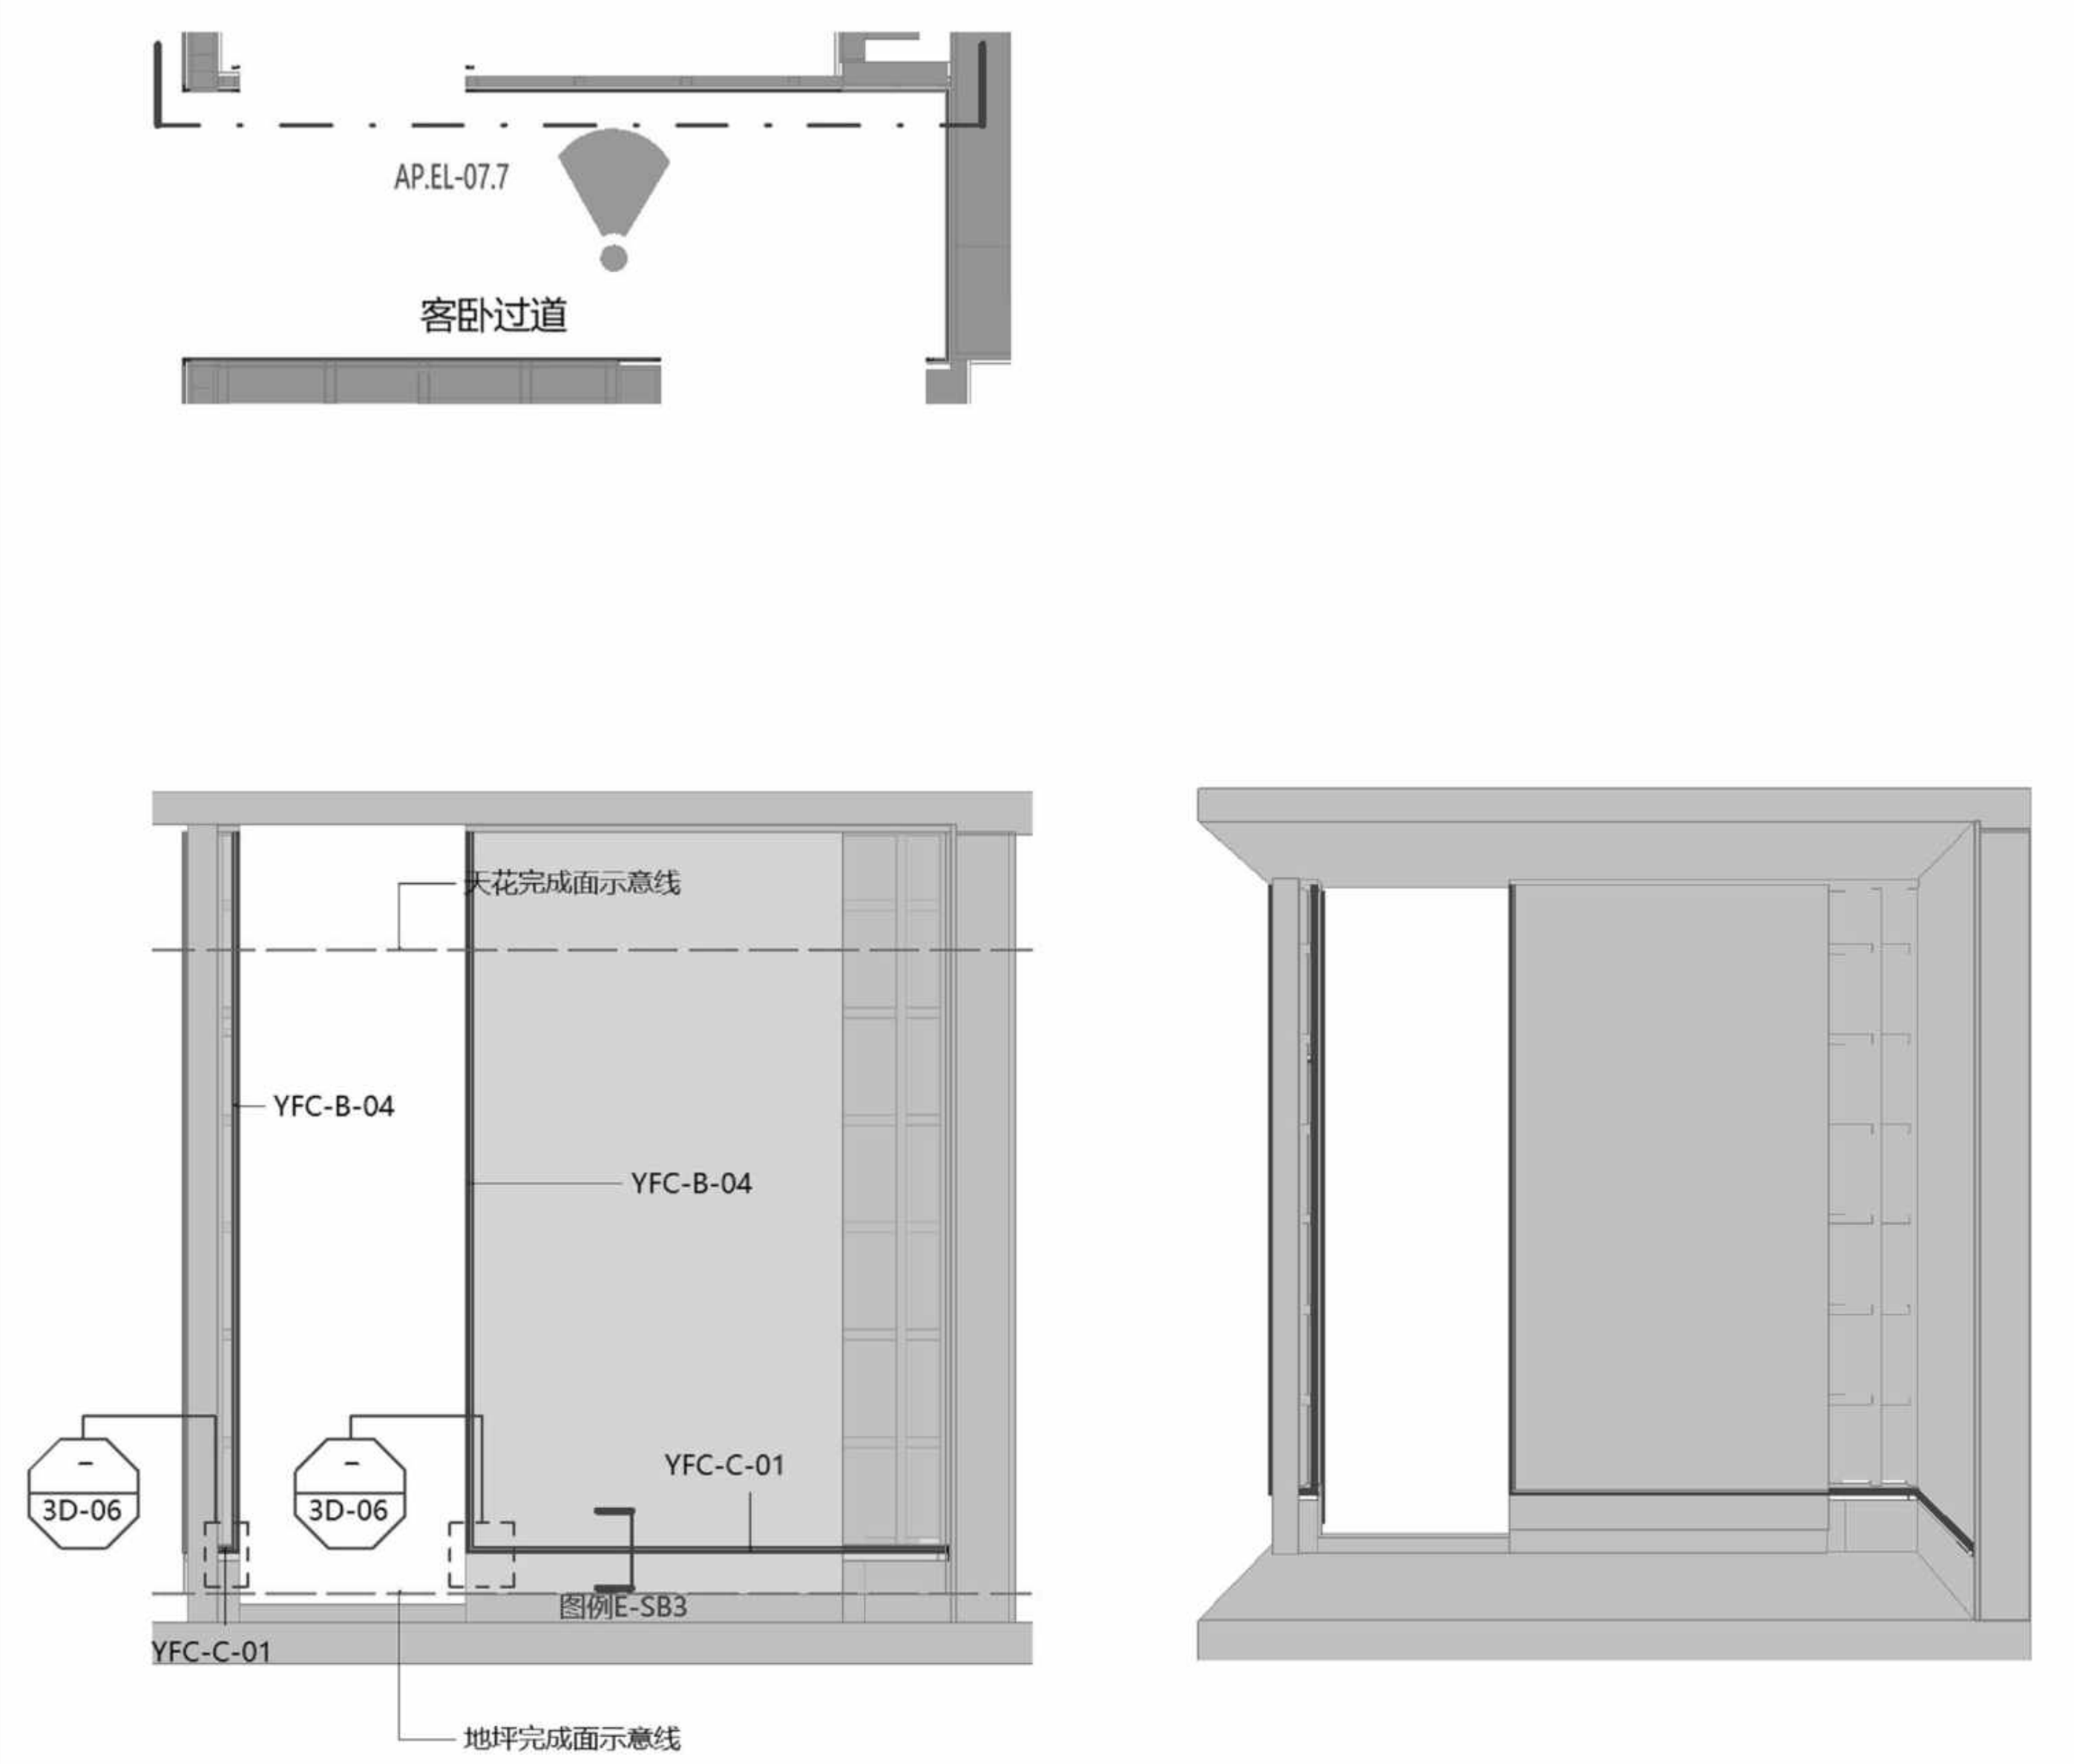
AP.EL-07.7
客卧过道
天花完成面示意线
YFC-B-04
YFC-B-04
–
3D-06
–
3D-06
YFC-C-01
图例E-SB3
YFC-C-01
地坪完成面示意线

7 客卧过道 墙面及踢脚铝型材立面图3

Scale比例 1 : 30@A2

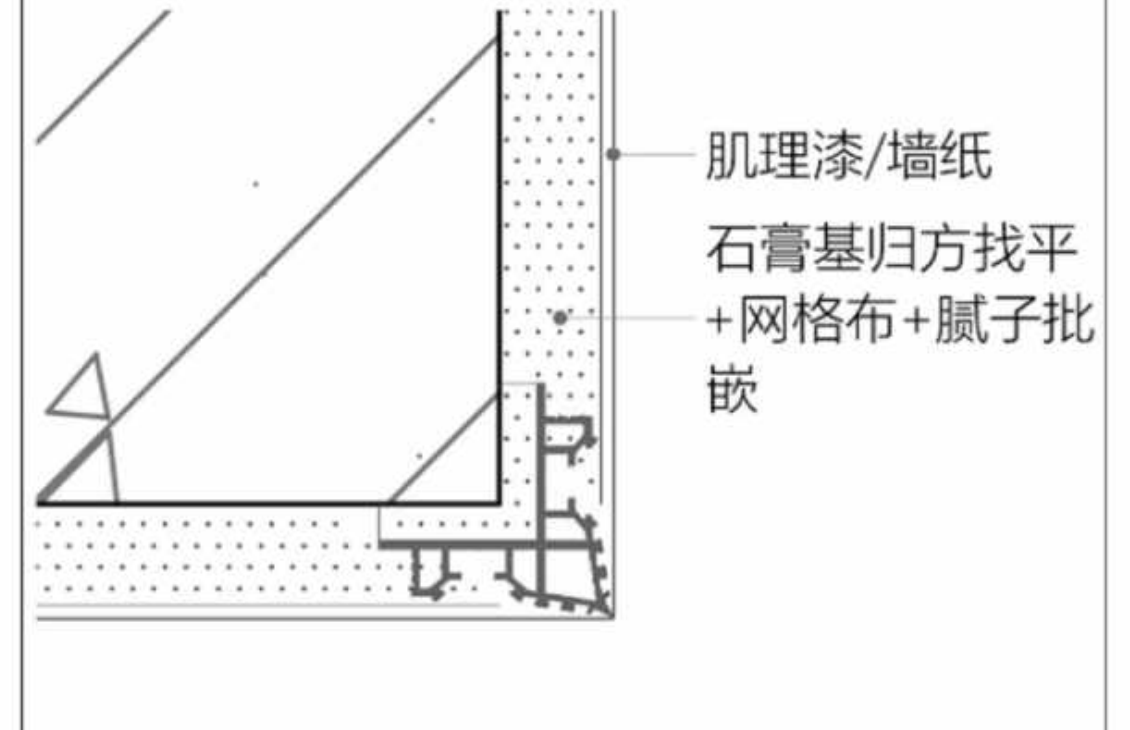
肌理漆/墙纸
石膏基归方找平
+网格布+腻子批
嵌

图例A-P1 墙面-石膏基找平铝型材

Scale比例 1：1@A2

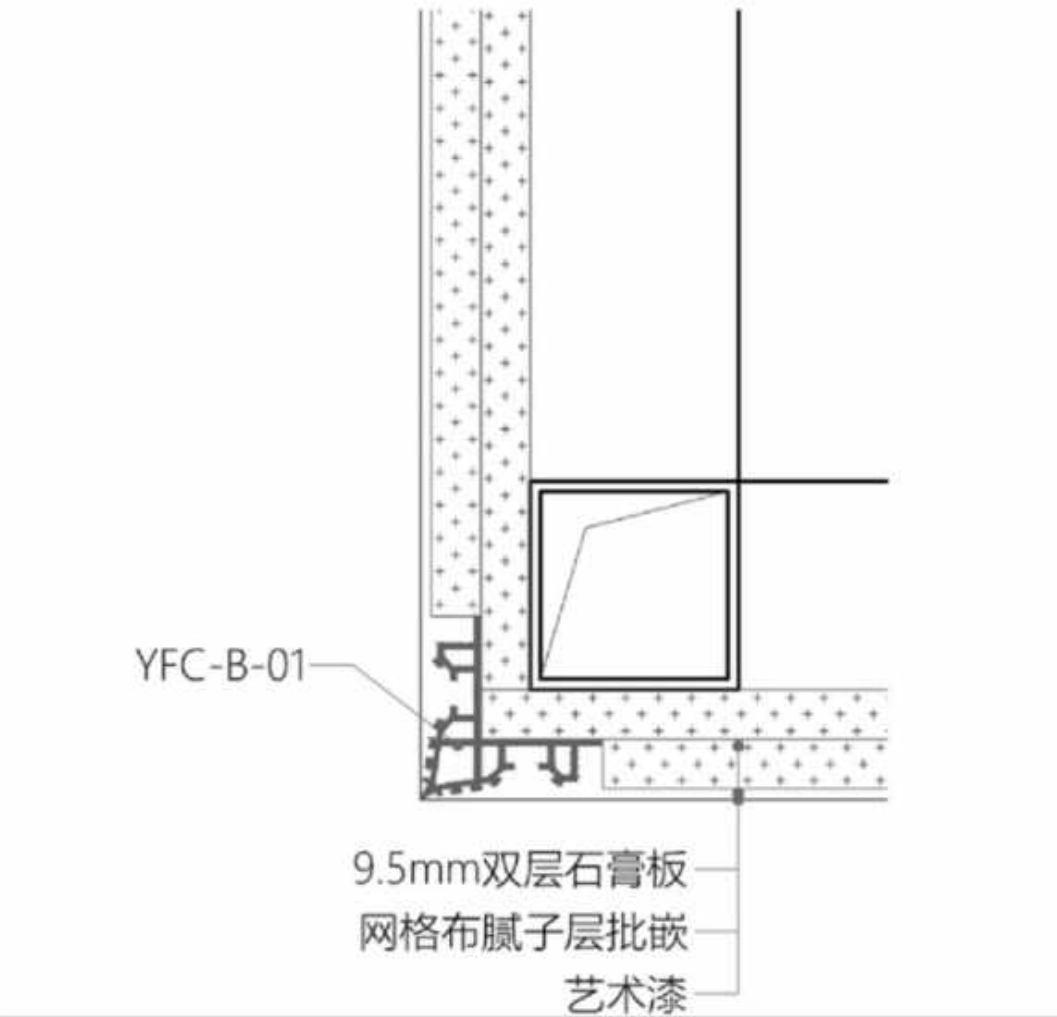
YFC-B-01
9.5mm双层石膏板
网格布腻子层批嵌
艺术漆

图例C-PB1 墙面-石膏基找平铝型材

Scale比例 1：1@A2

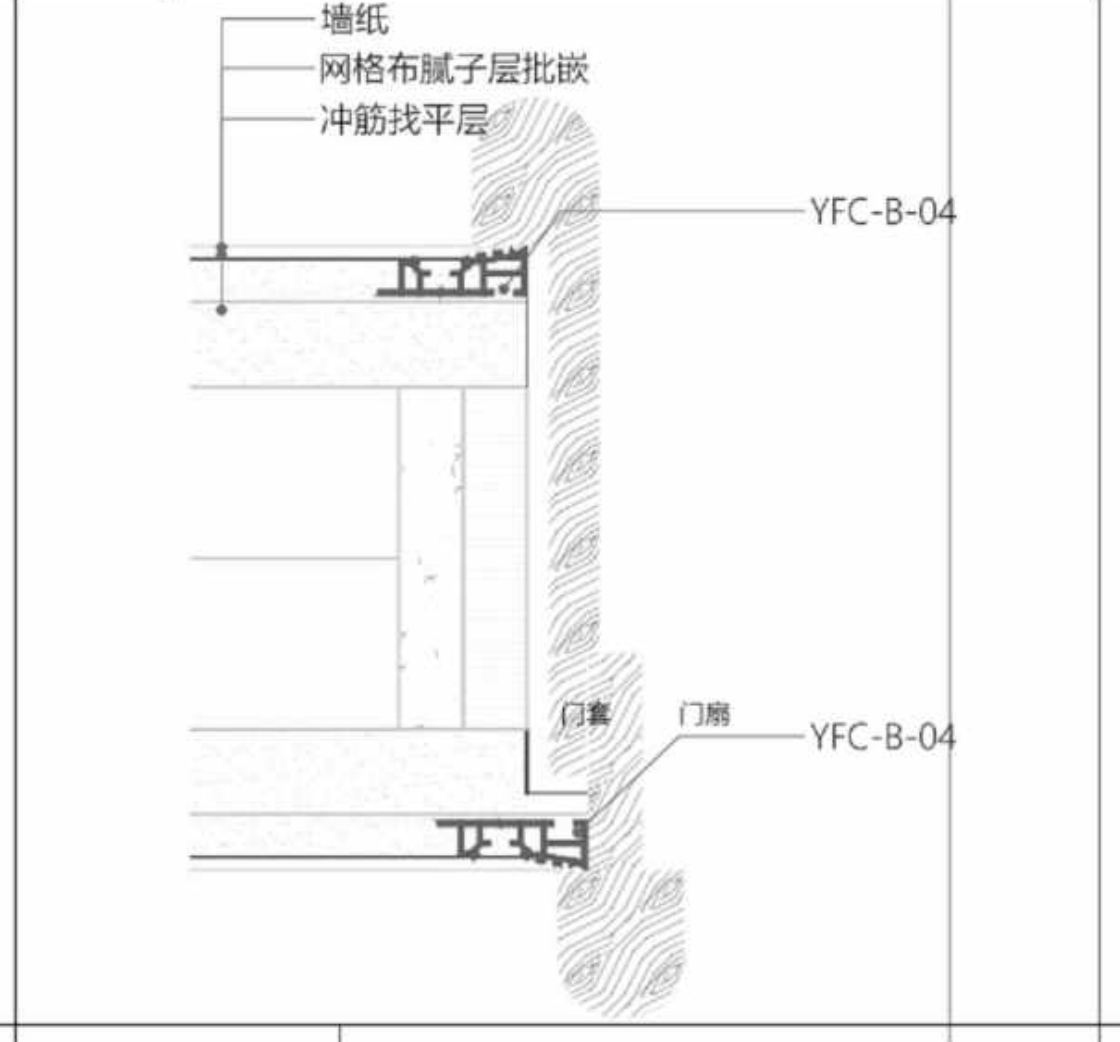
墙纸
网格布腻子层批嵌
冲筋找平层
YFC-B-04
门套
门扇
YFC-B-04

图例D-M1 门边-石膏基找平铝型材

Scale比例 1：1@A2

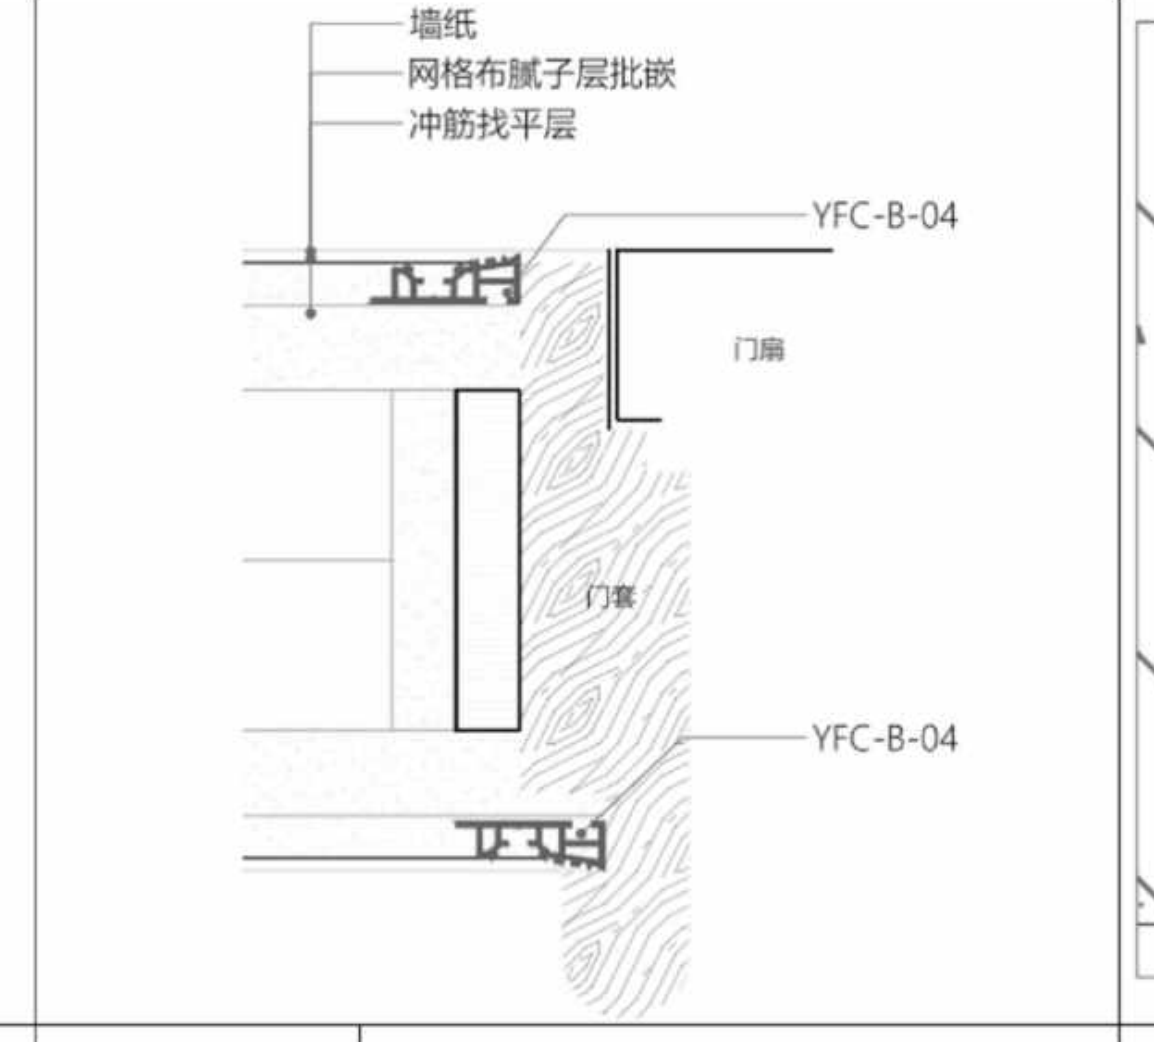
墙纸
网格布腻子层批嵌
冲筋找平层
YFC-B-04
门扇
门套
YFC-B-04

图例D-M2 门边-石膏基找平铝型材

Scale比例 1：1@A2

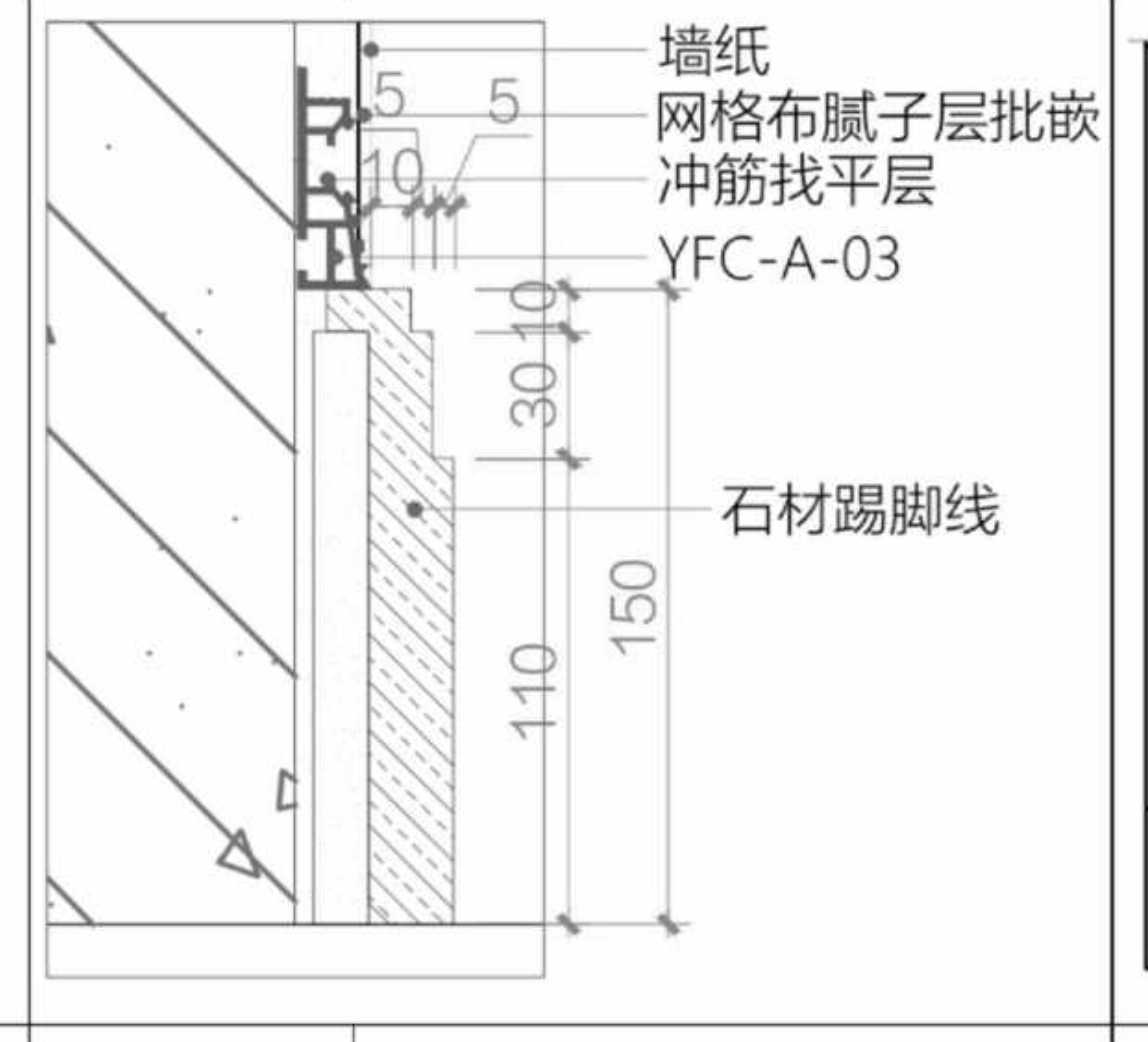
墙纸
网格布腻子层批嵌
冲筋找平层
YFC-A-03
5
5
10
10
30
150
110
石材踢脚线

图例E-SP4 踢脚-石膏基找平铝型材

Scale比例 1：1@A2

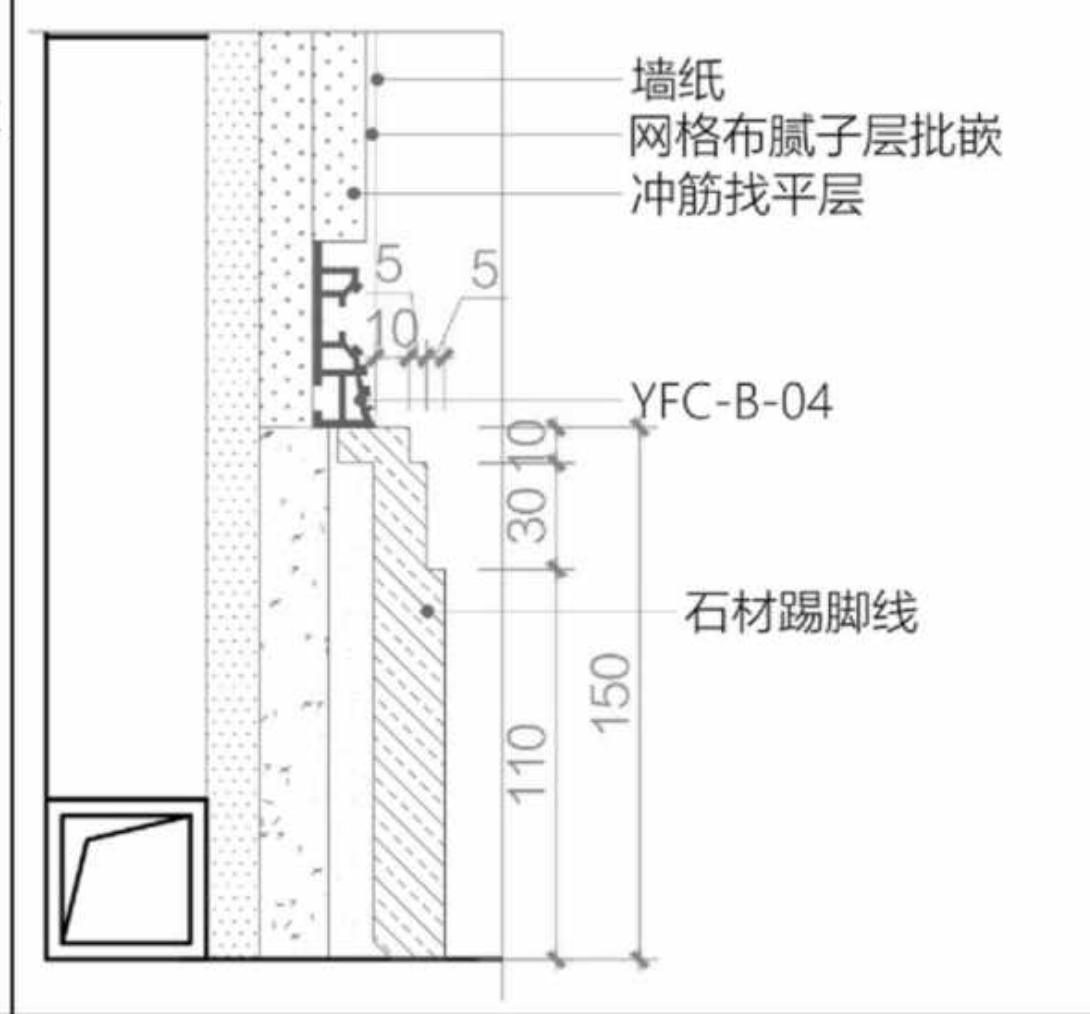
墙纸
网格布腻子层批嵌
冲筋找平层
5
5
10
YFC-B-04
10
30
150
110
石材踢脚线

图例E-SB1 踢脚-石膏基找平铝型材

Scale比例 1：1@A2

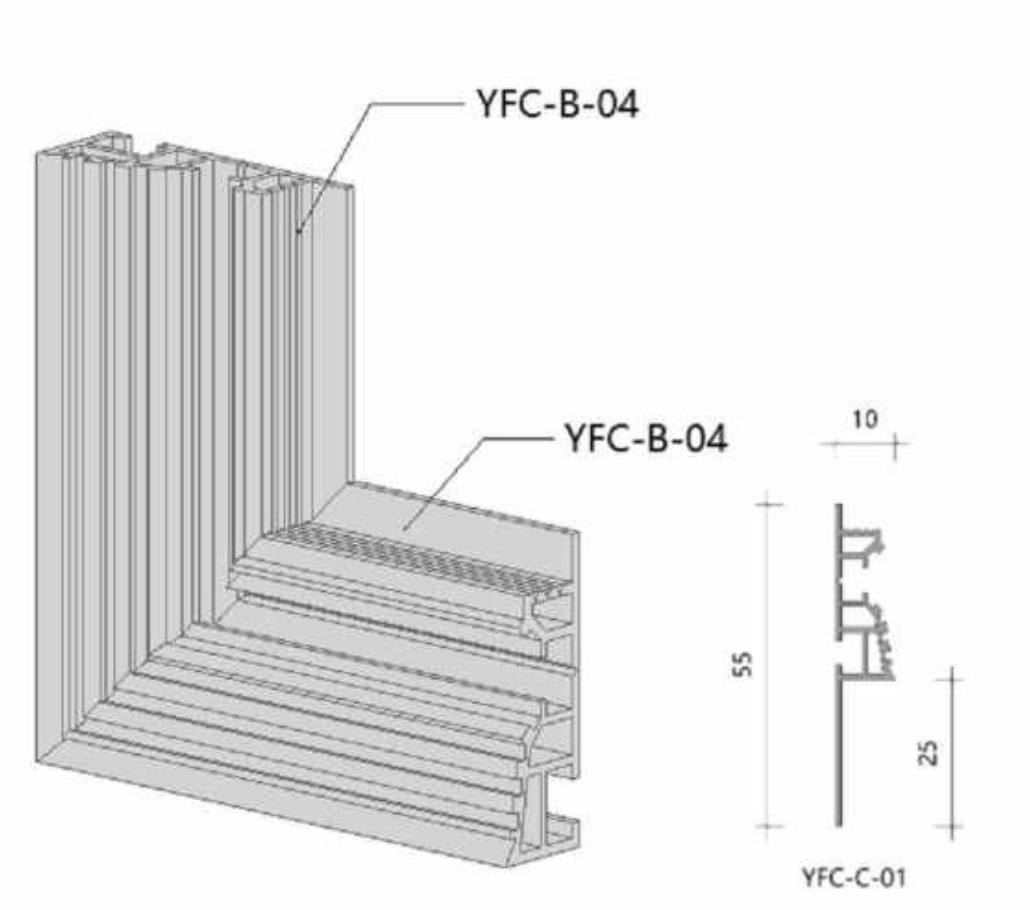
YFC-B-04
YFC-B-04
10
55
25
YFC-C-01

3D-01 转角铝型材-拼接跟通

转角数量：1

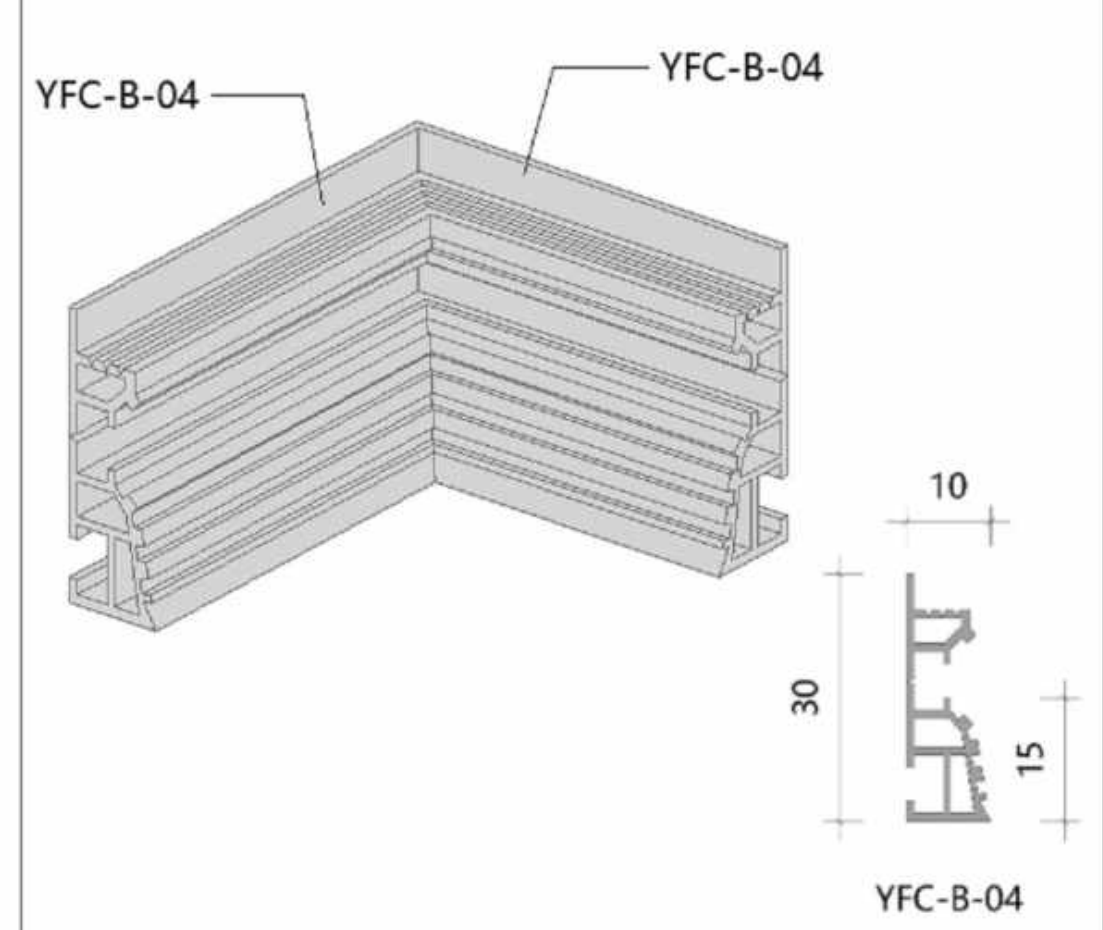
YFC-B-04
YFC-B-04
10
30
15
YFC-B-04

3D-04 转角铝型材-拼接跟通

转角数量：6

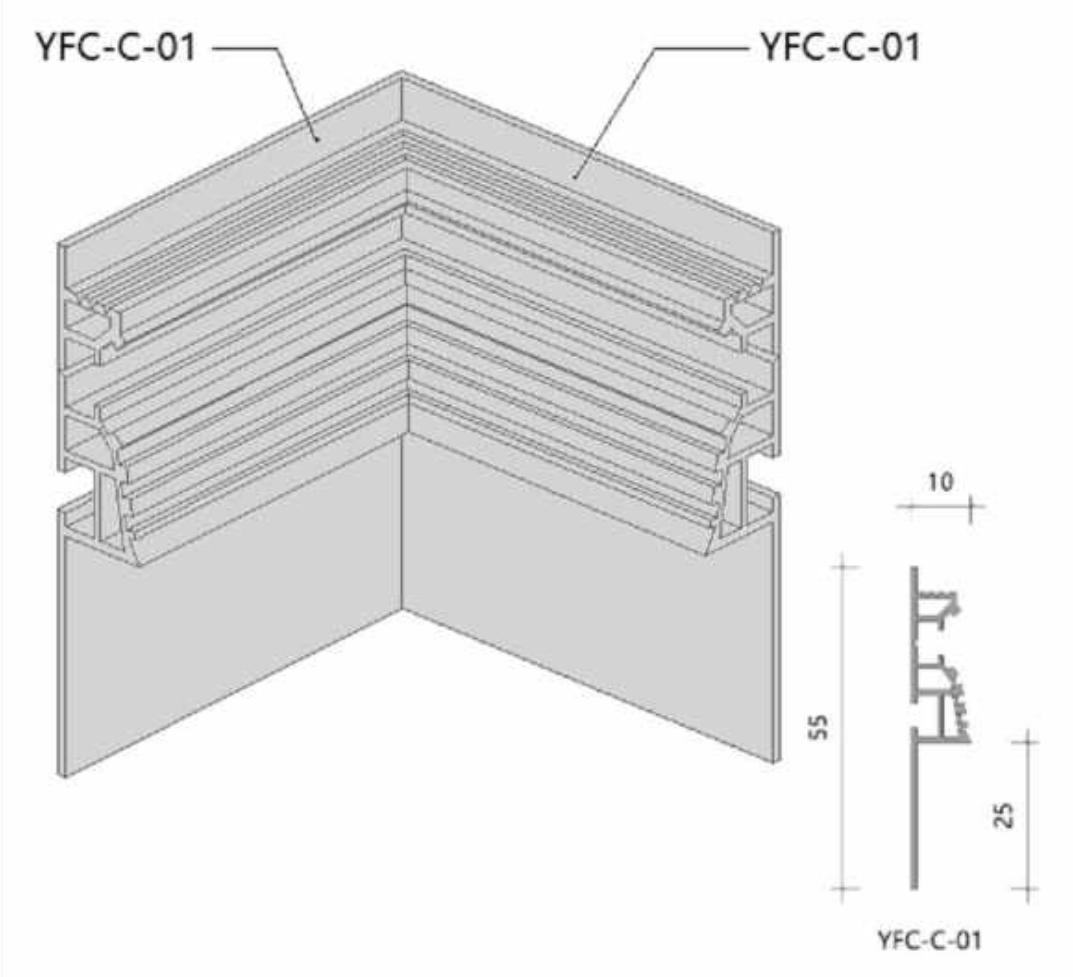
YFC-C-01
YFC-C-01
10
55
25
YFC-C-01

3D-05 转角铝型材-拼接跟通

转角数量：2

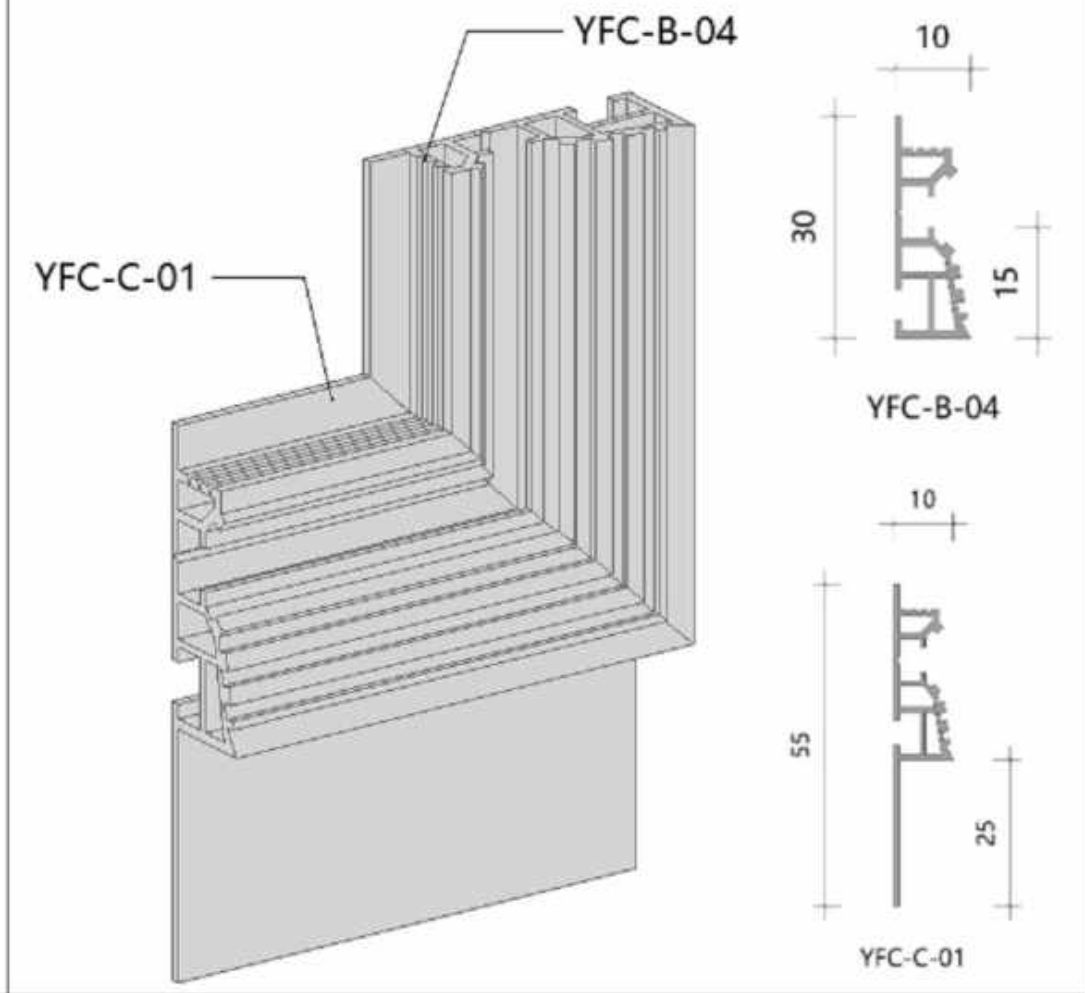
YFC-B-04
YFC-C-01
10
30
15
YFC-B-04
10
55
25
YFC-C-01

3D-6 转角铝型材-拼接跟通

转角数量：2

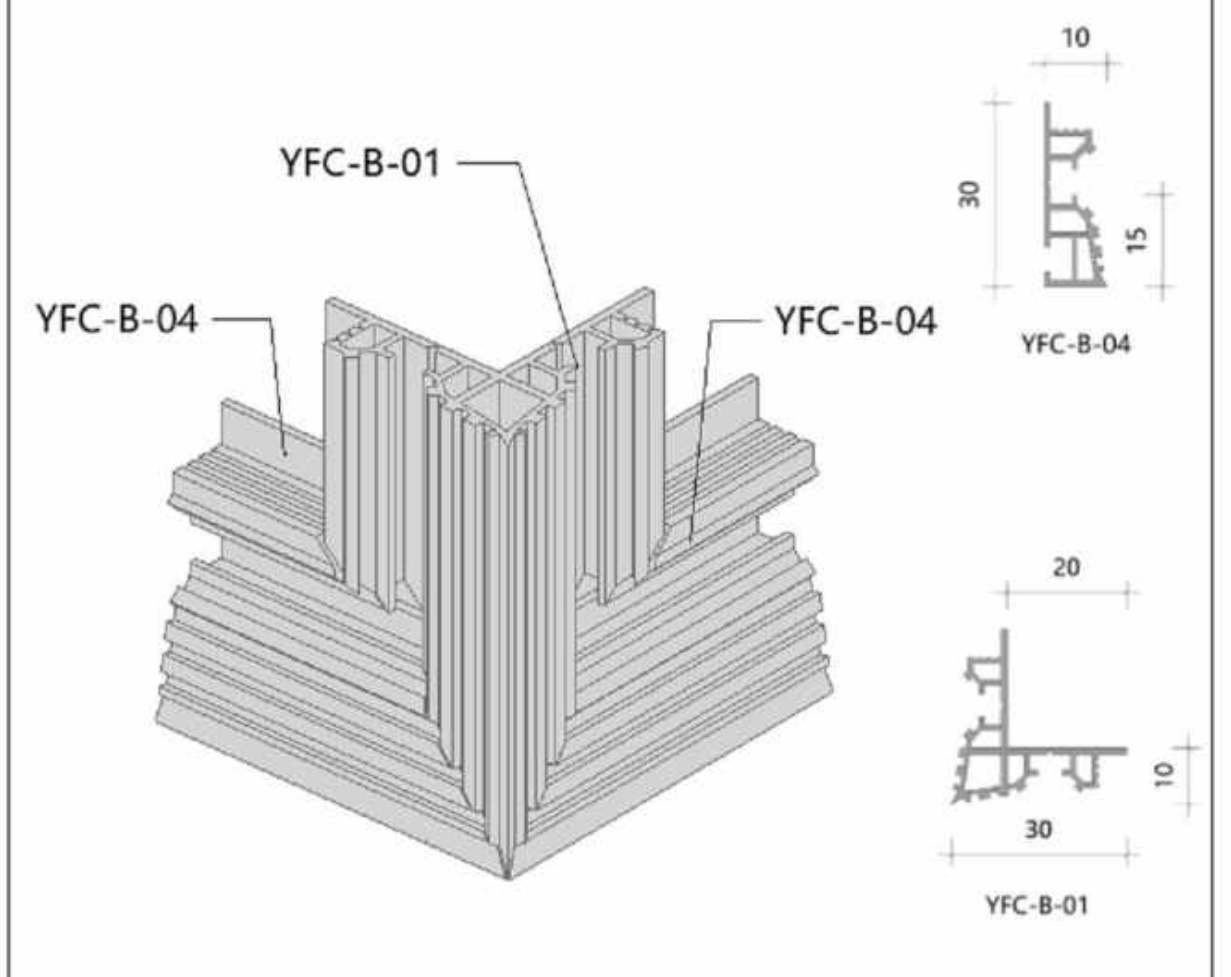
YFC-B-01
YFC-B-04
YFC-B-04
10
30
15
YFC-B-04
20
10
30
YFC-B-01

3D-12 转角铝型材-拼接跟通

转角数量：2

盖章

注释
Notes

1.本图纸如与现场尺寸有误，请施工人员与项目负责人联系。
2.施工前施工人员应认真查阅此图，如有不明确尺寸，按现场测量为准。
3.本图纸必须经甲乙双方认可并签字方可作为施工依据。

日期
Date 03/04/26

修订
Revision

△1

项目
Project
潮映华岸府3-801

比例
Scale
客卧入户、客卧过道
墙面及踢脚铝型材

图纸编号
Drawing No.
AP.EL-07

项目编号
Project No.

©2025

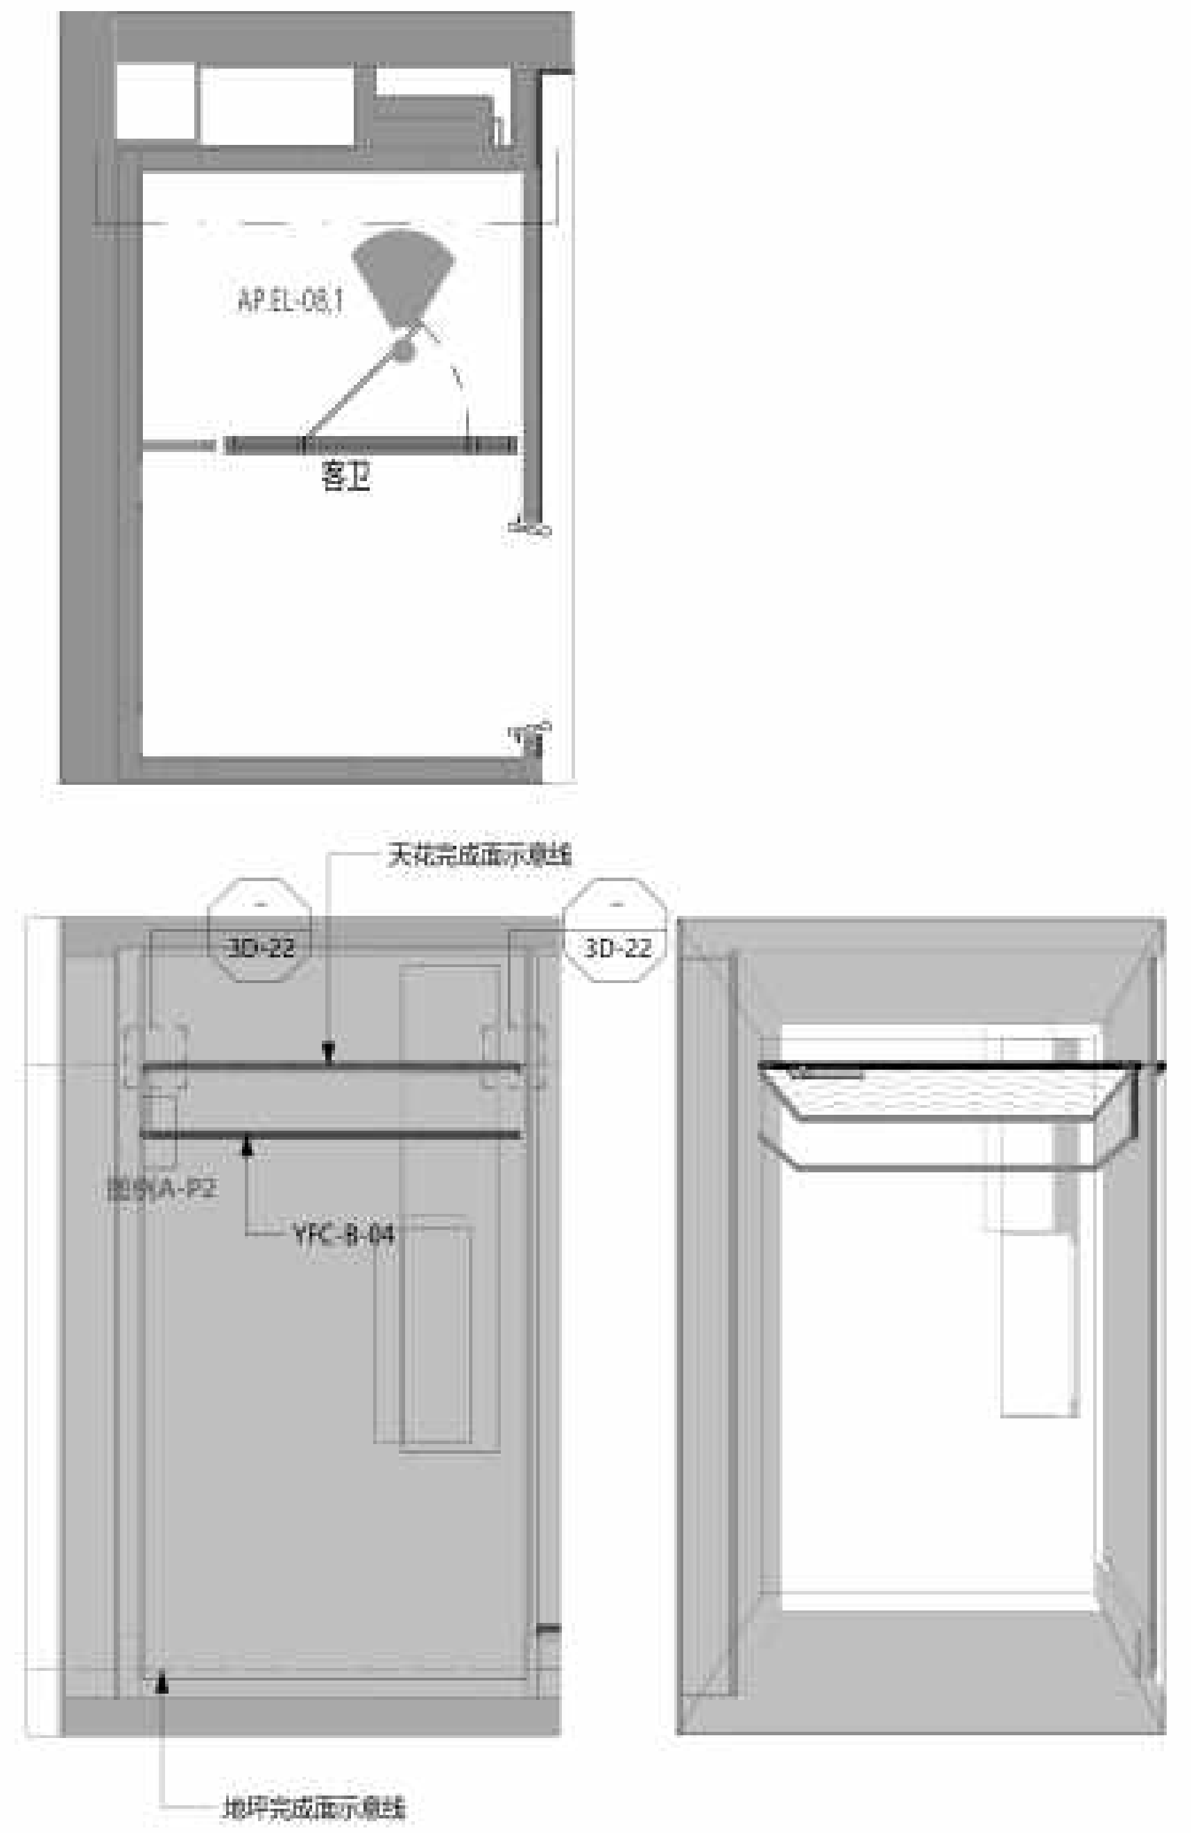
AP.EL-08.1
客卫
天花完成面示意线
3D-22
3D-22
图例A-P2
YFC-B-04
地坪完成面示意线

1

客卫 墙面及踢脚铝型材立面图1

Scale比例 1：30@A2

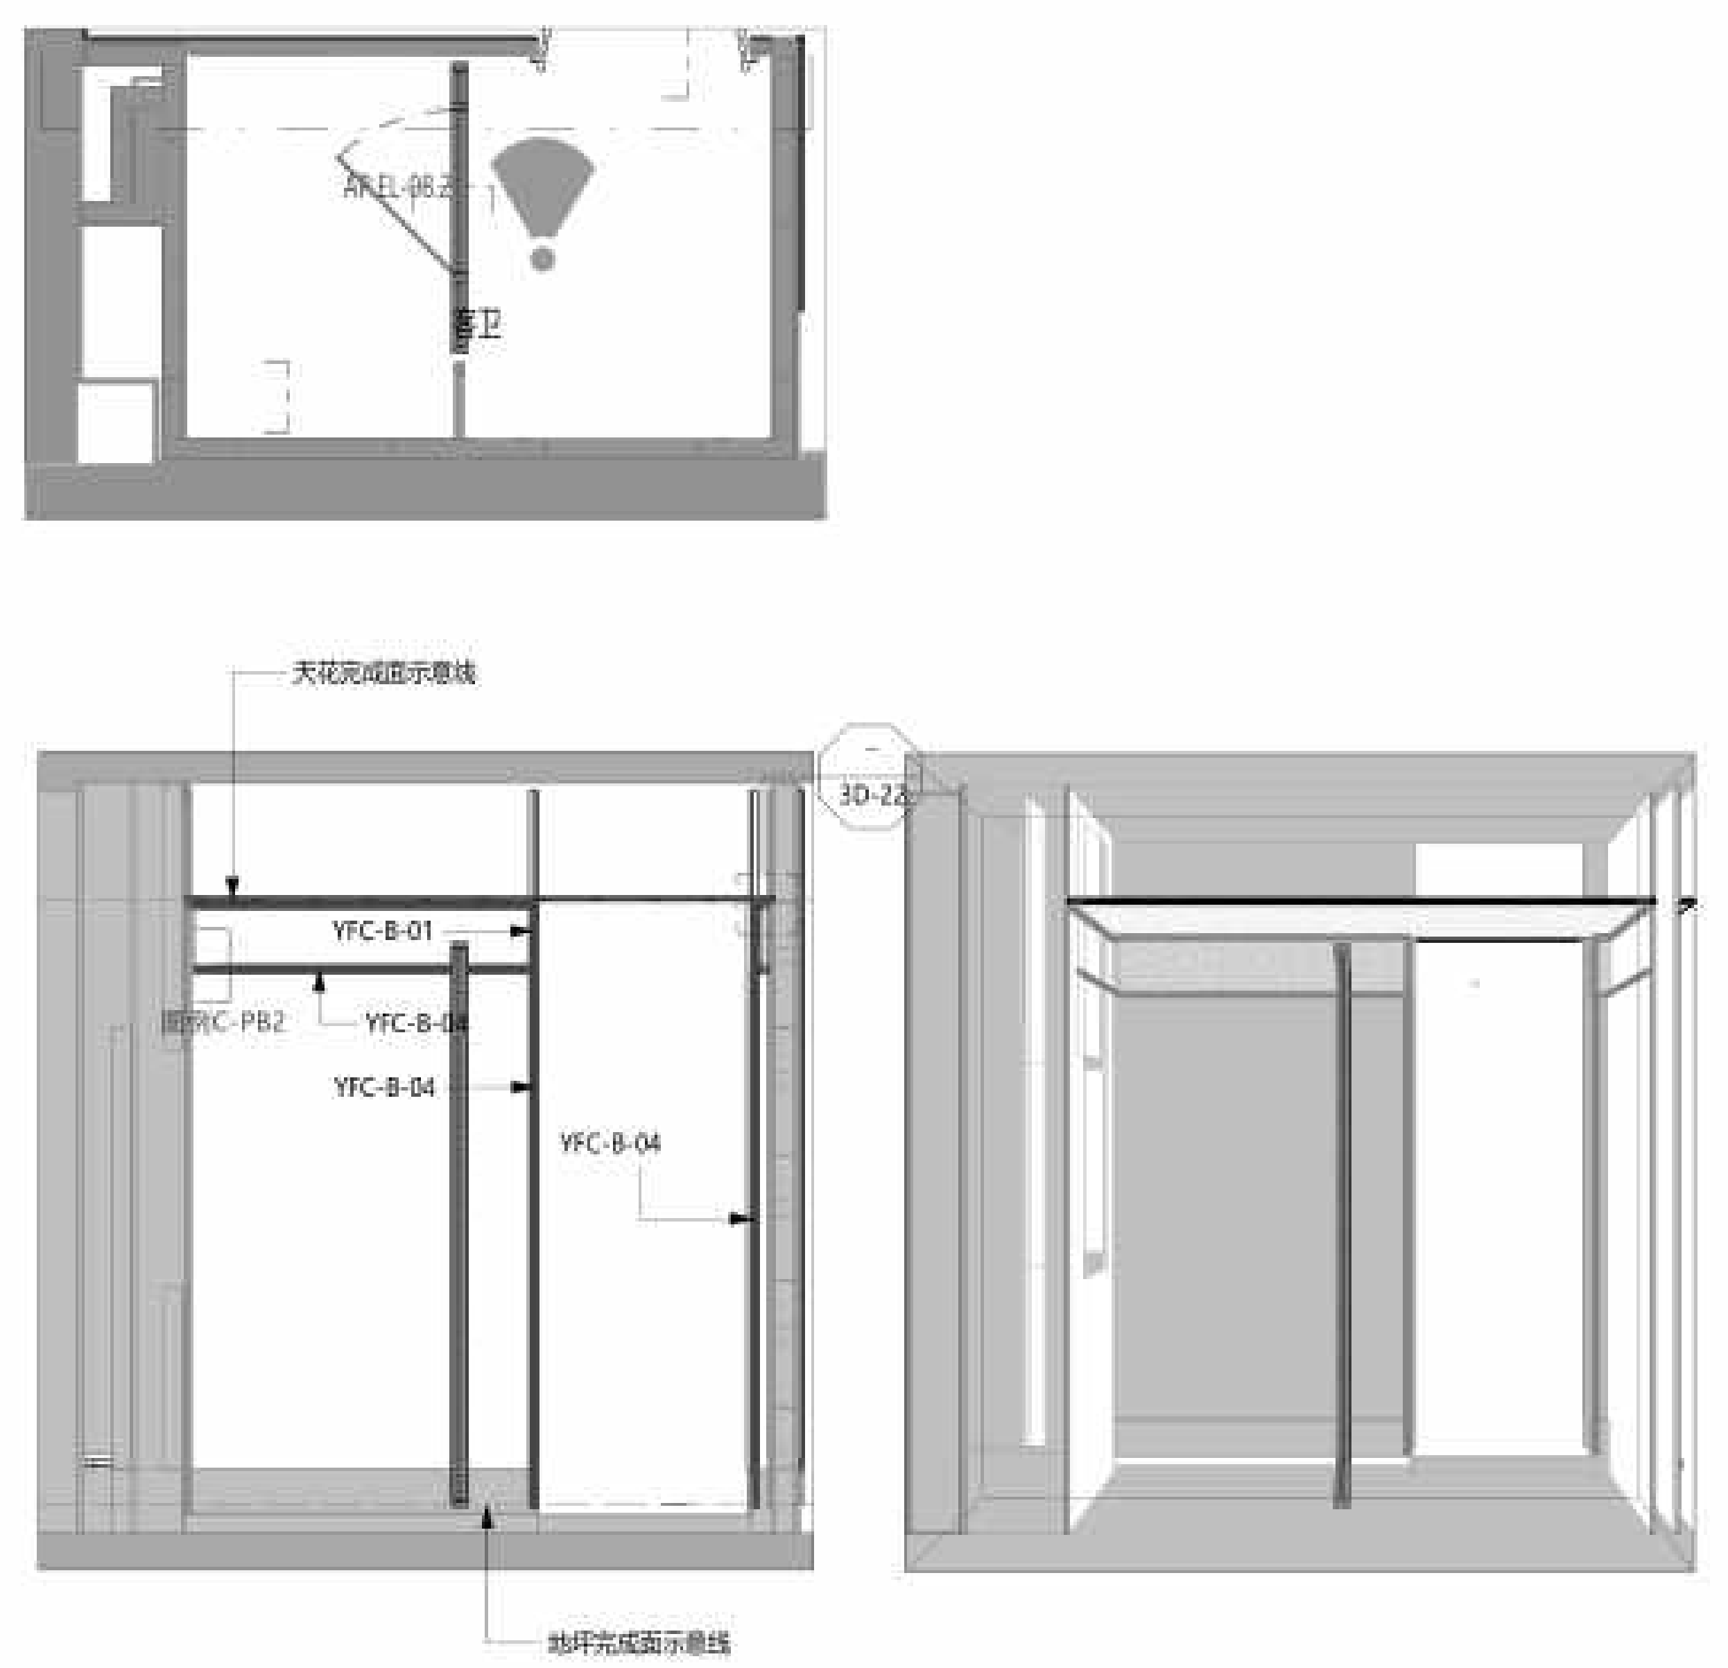
AP.EL-08.2
客卫
天花完成面示意线
3D-22
YFC-B-01
图例C-PB2
YFC-B-04
YFC-B-04
YFC-B-04
地坪完成面示意线

2

客卫 墙面及踢脚铝型材立面图2

Scale比例 1：30@A2

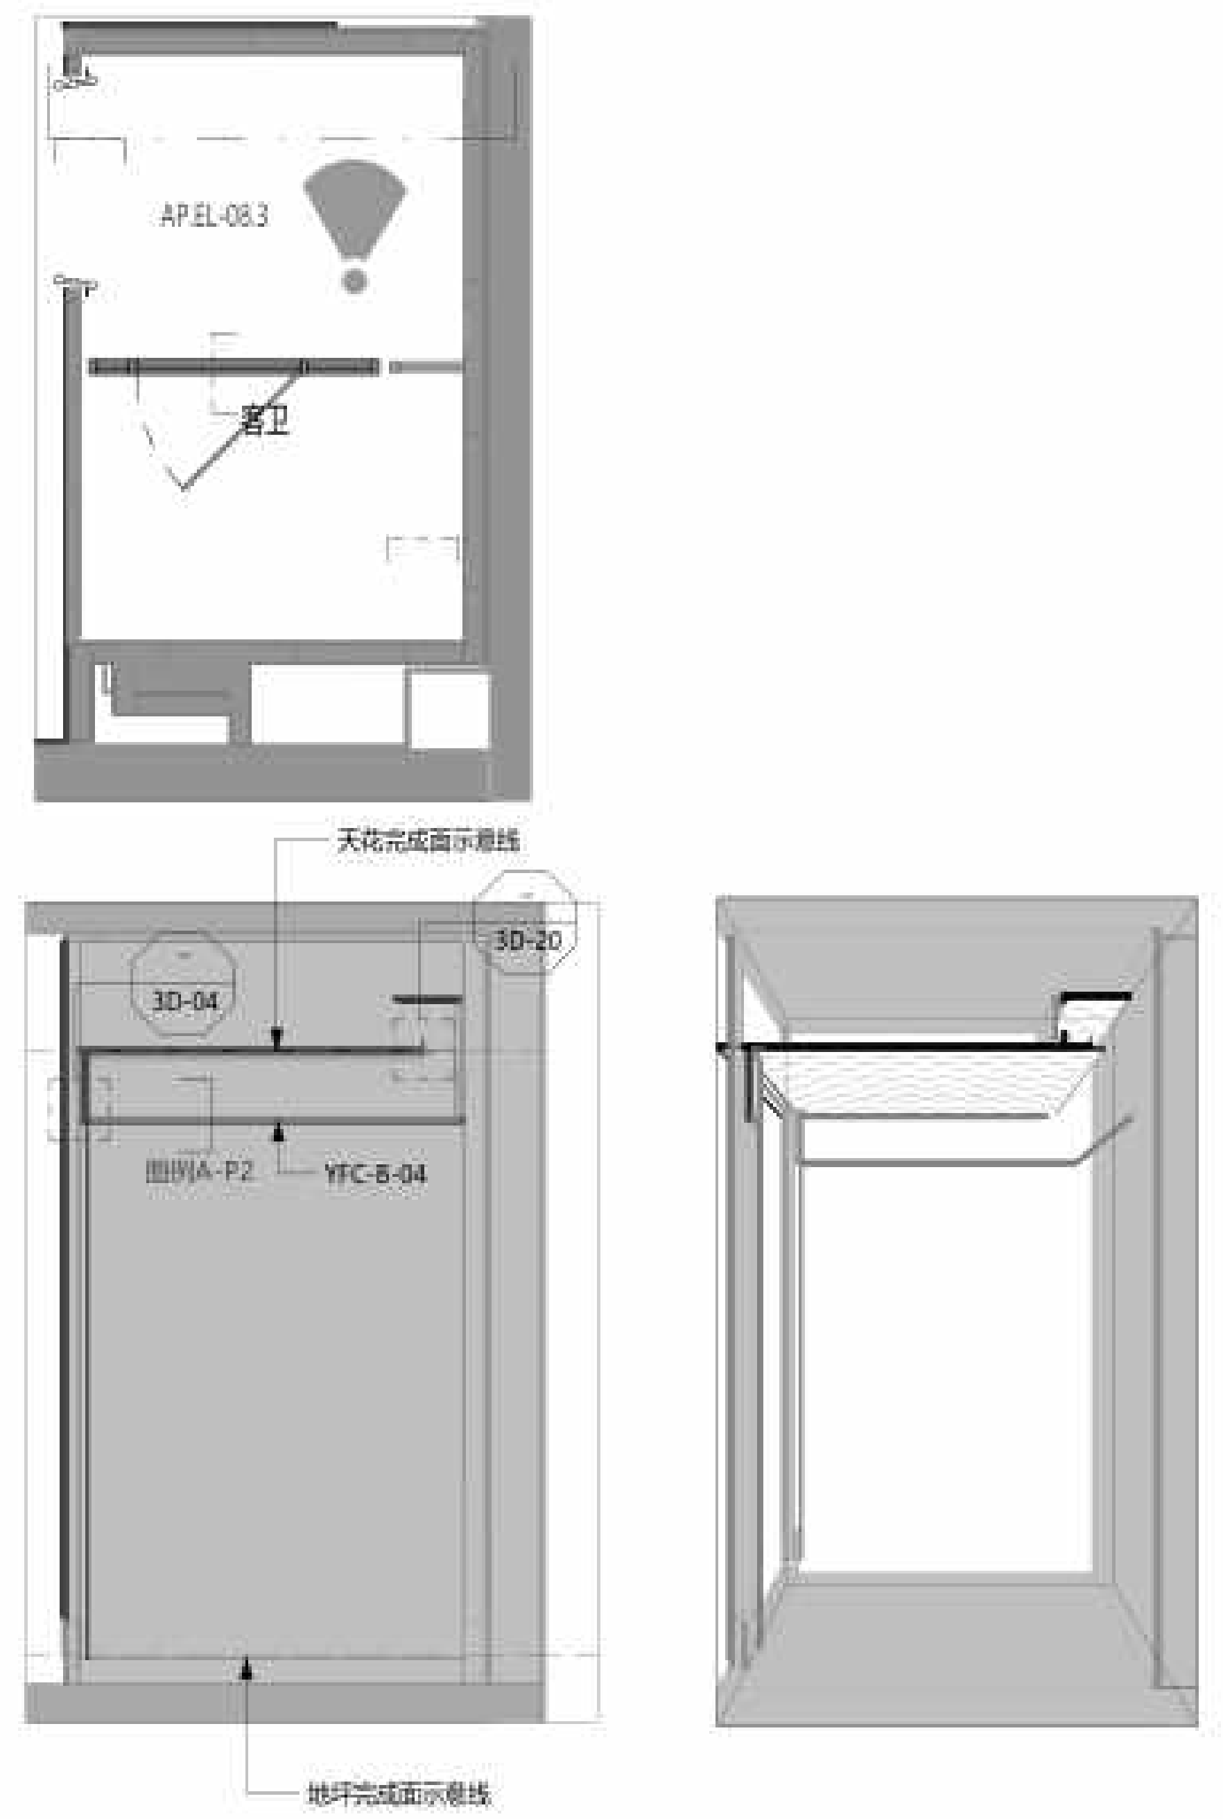
AP.EL-08.3
客卫
天花完成面示意线
3D-04
3D-20
图例A-P2
YFC-B-04
地坪完成面示意线

3

客卫 墙面及踢脚铝型材立面图3

Scale比例 1：30@A2

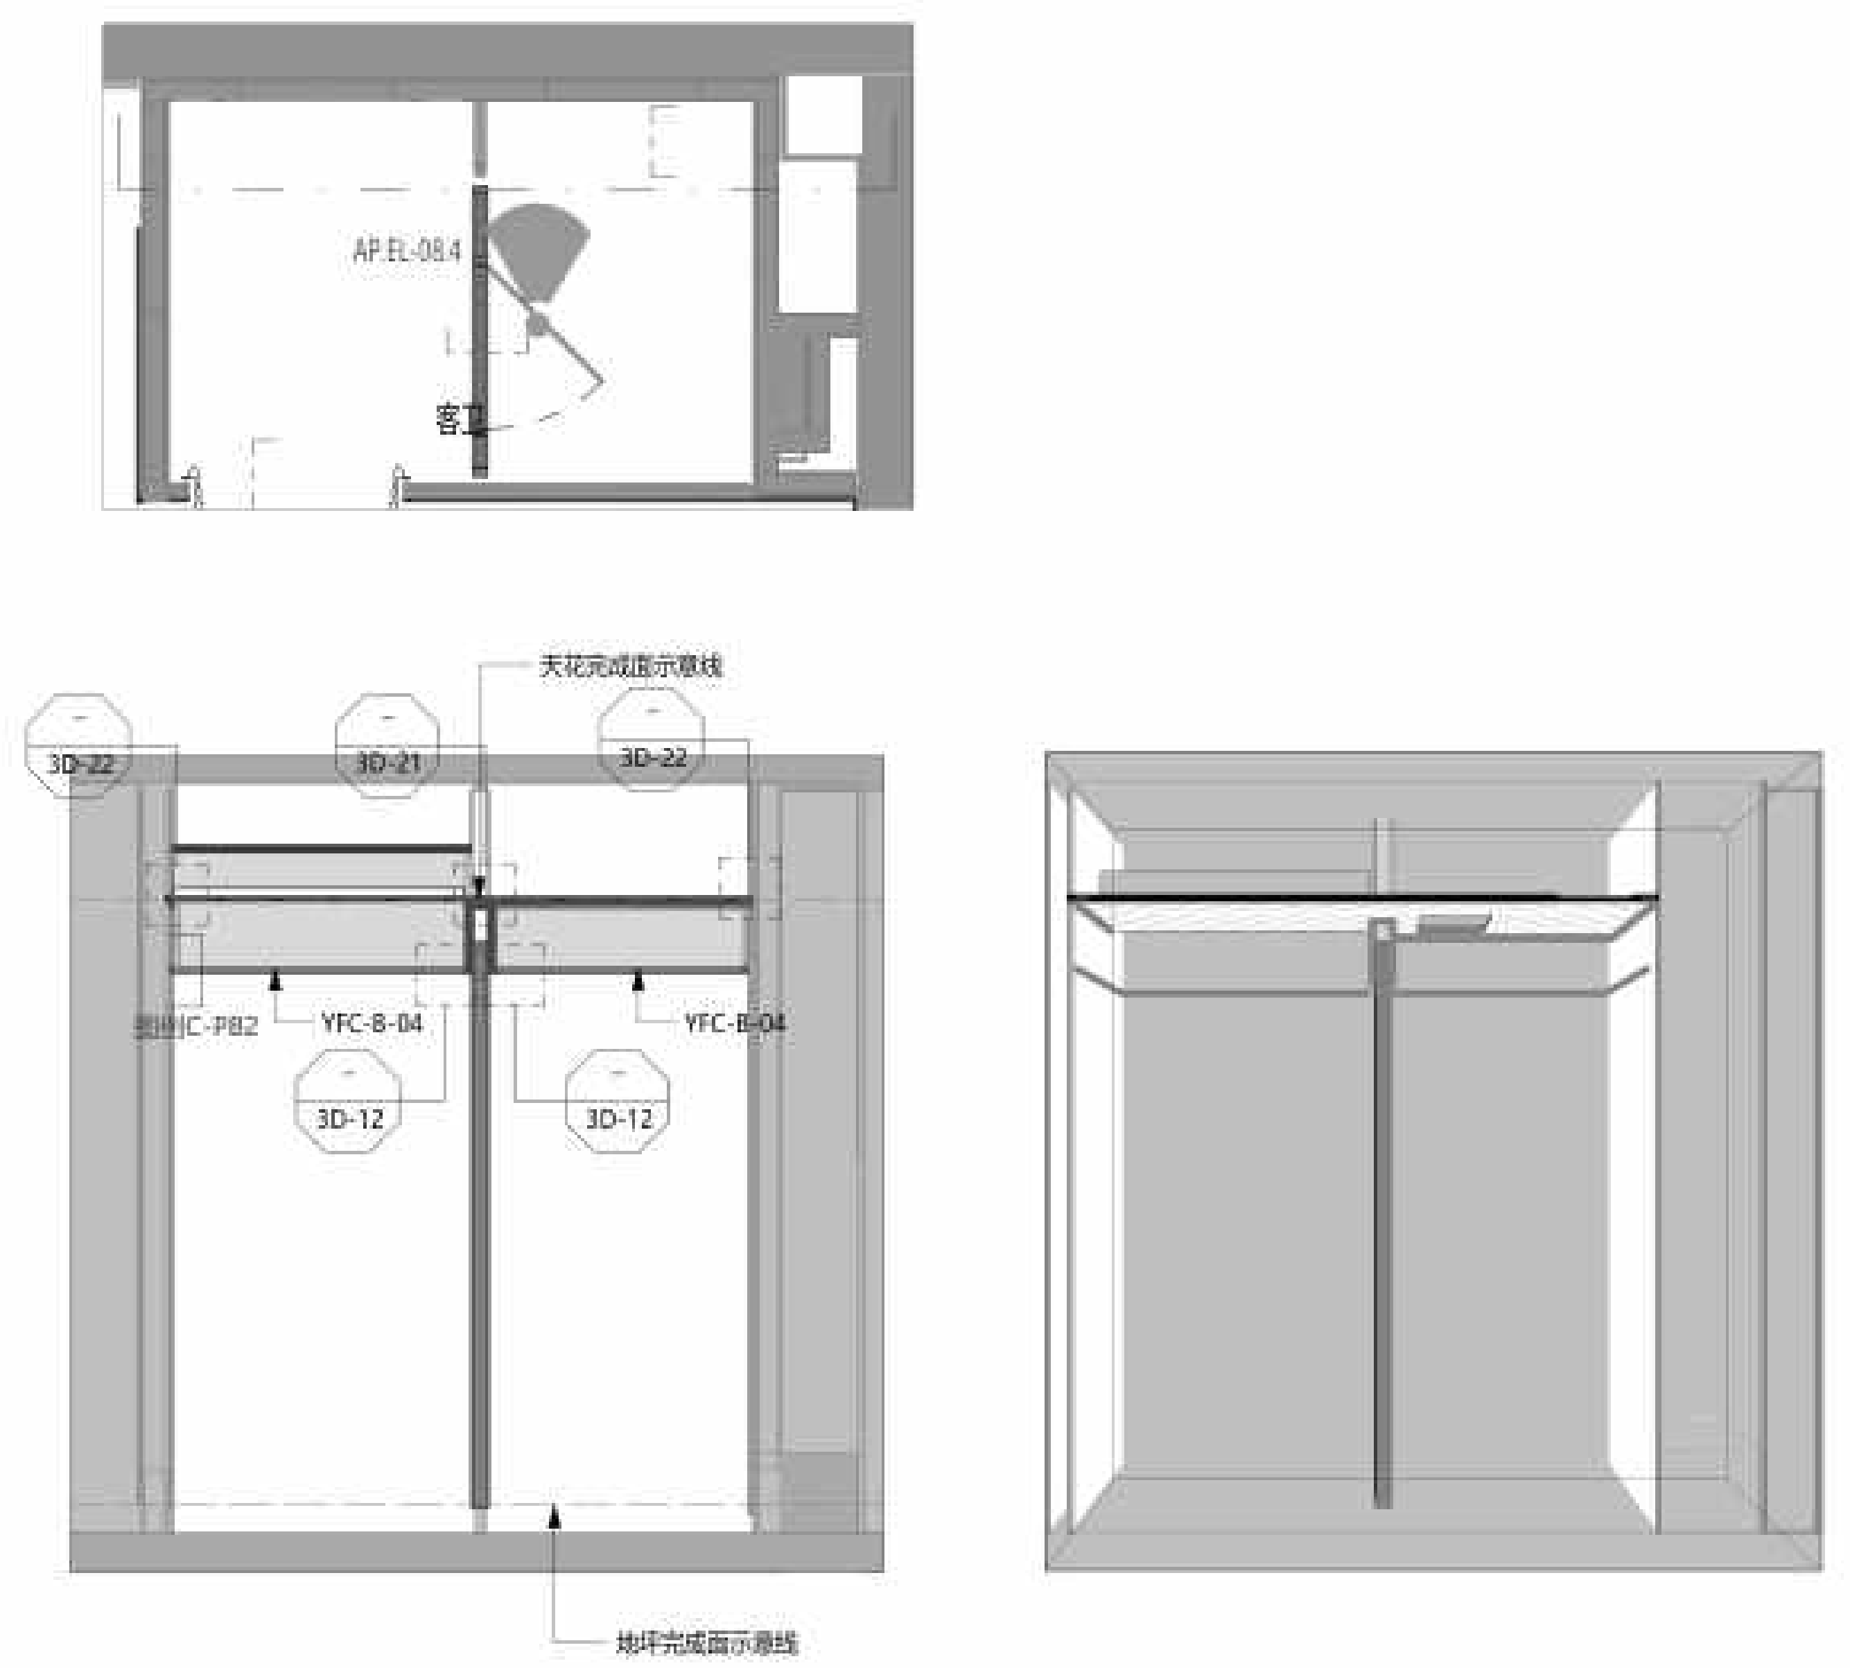
AP.EL-08.4
客卫
天花完成面示意线
3D-22
3D-21
3D-22
图例C-PB2
YFC-B-04
YFC-B-04
3D-12
3D-12
地坪完成面示意线

4

客卫 墙面及踢脚铝型材立面图4

Scale比例 1：30@A2

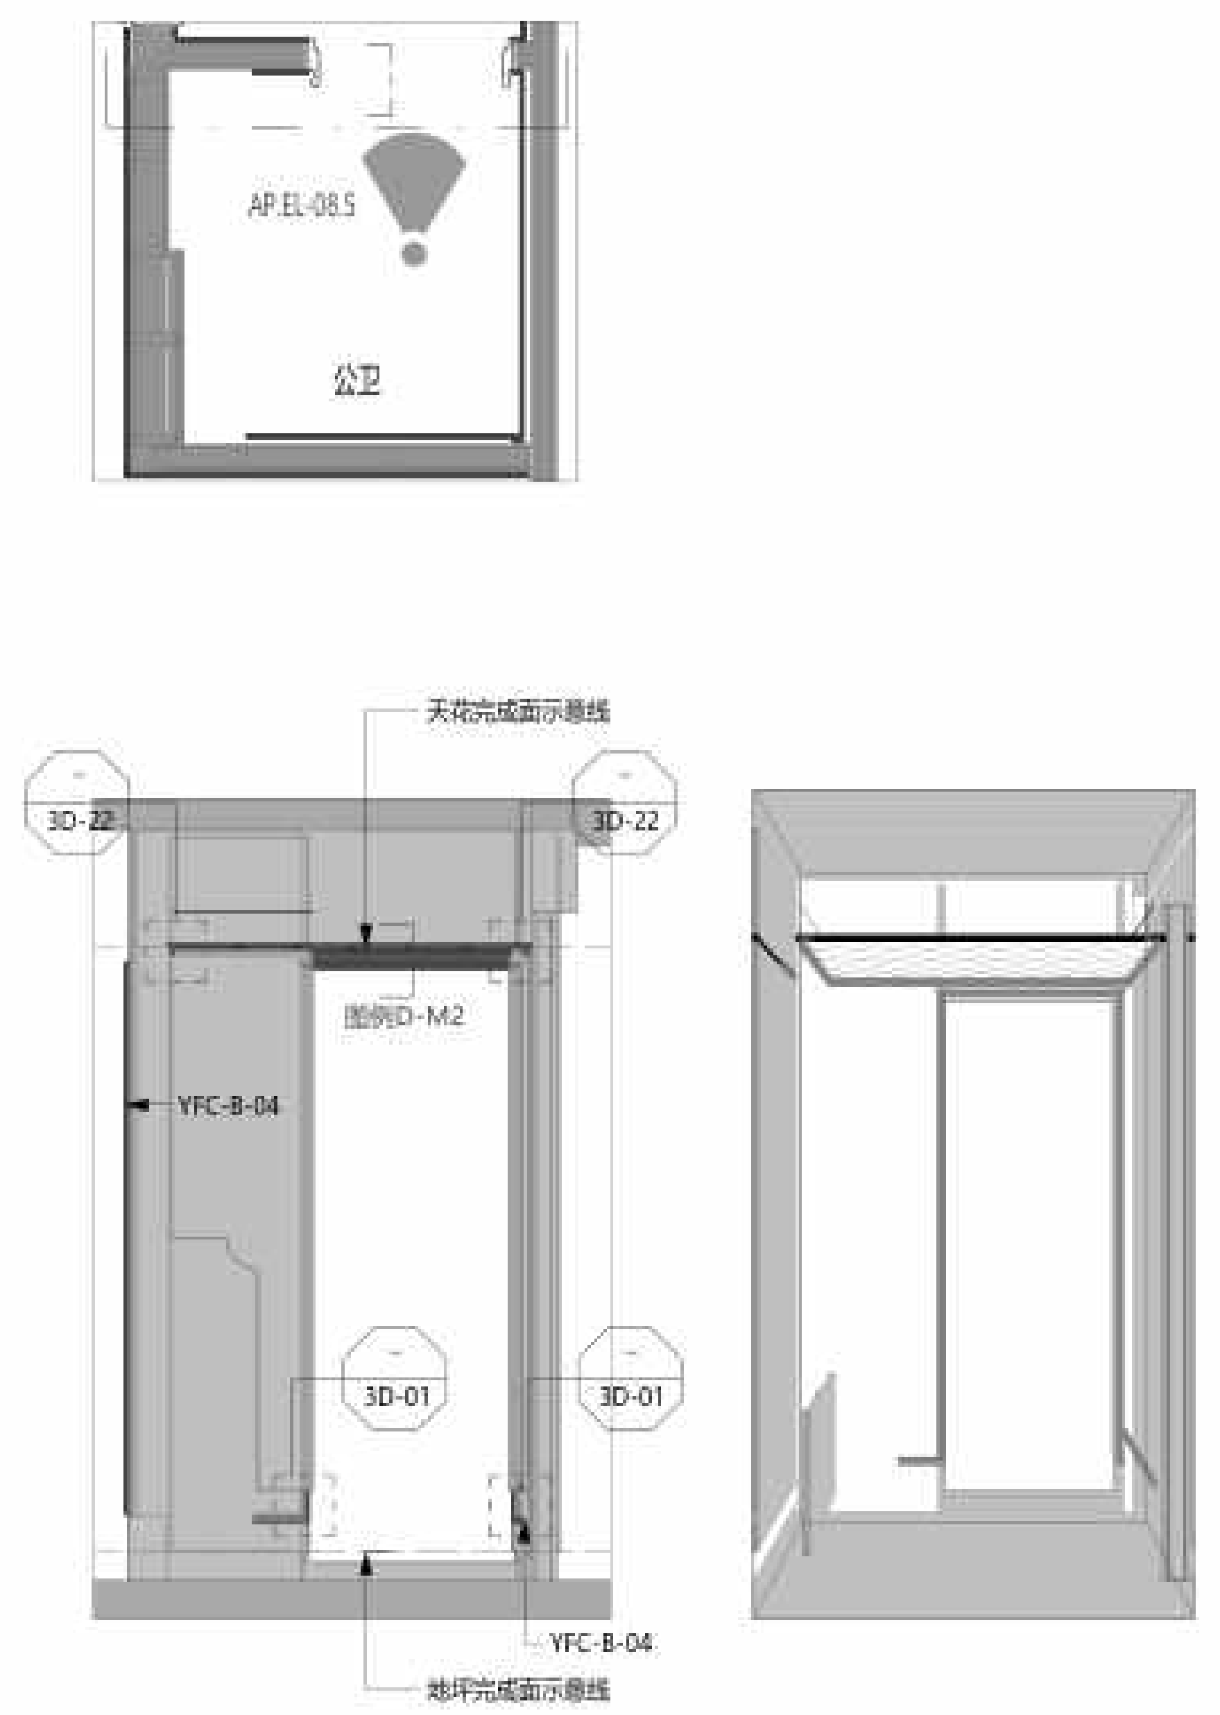
AP.EL-08.5
公卫
天花完成面示意线
3D-22
3D-22
图例D-M2
YFC-B-04
3D-01
3D-01
YFC-B-04
地坪完成面示意线

5

公卫 墙面及踢脚铝型材立面图5

Scale比例 1：30@A2

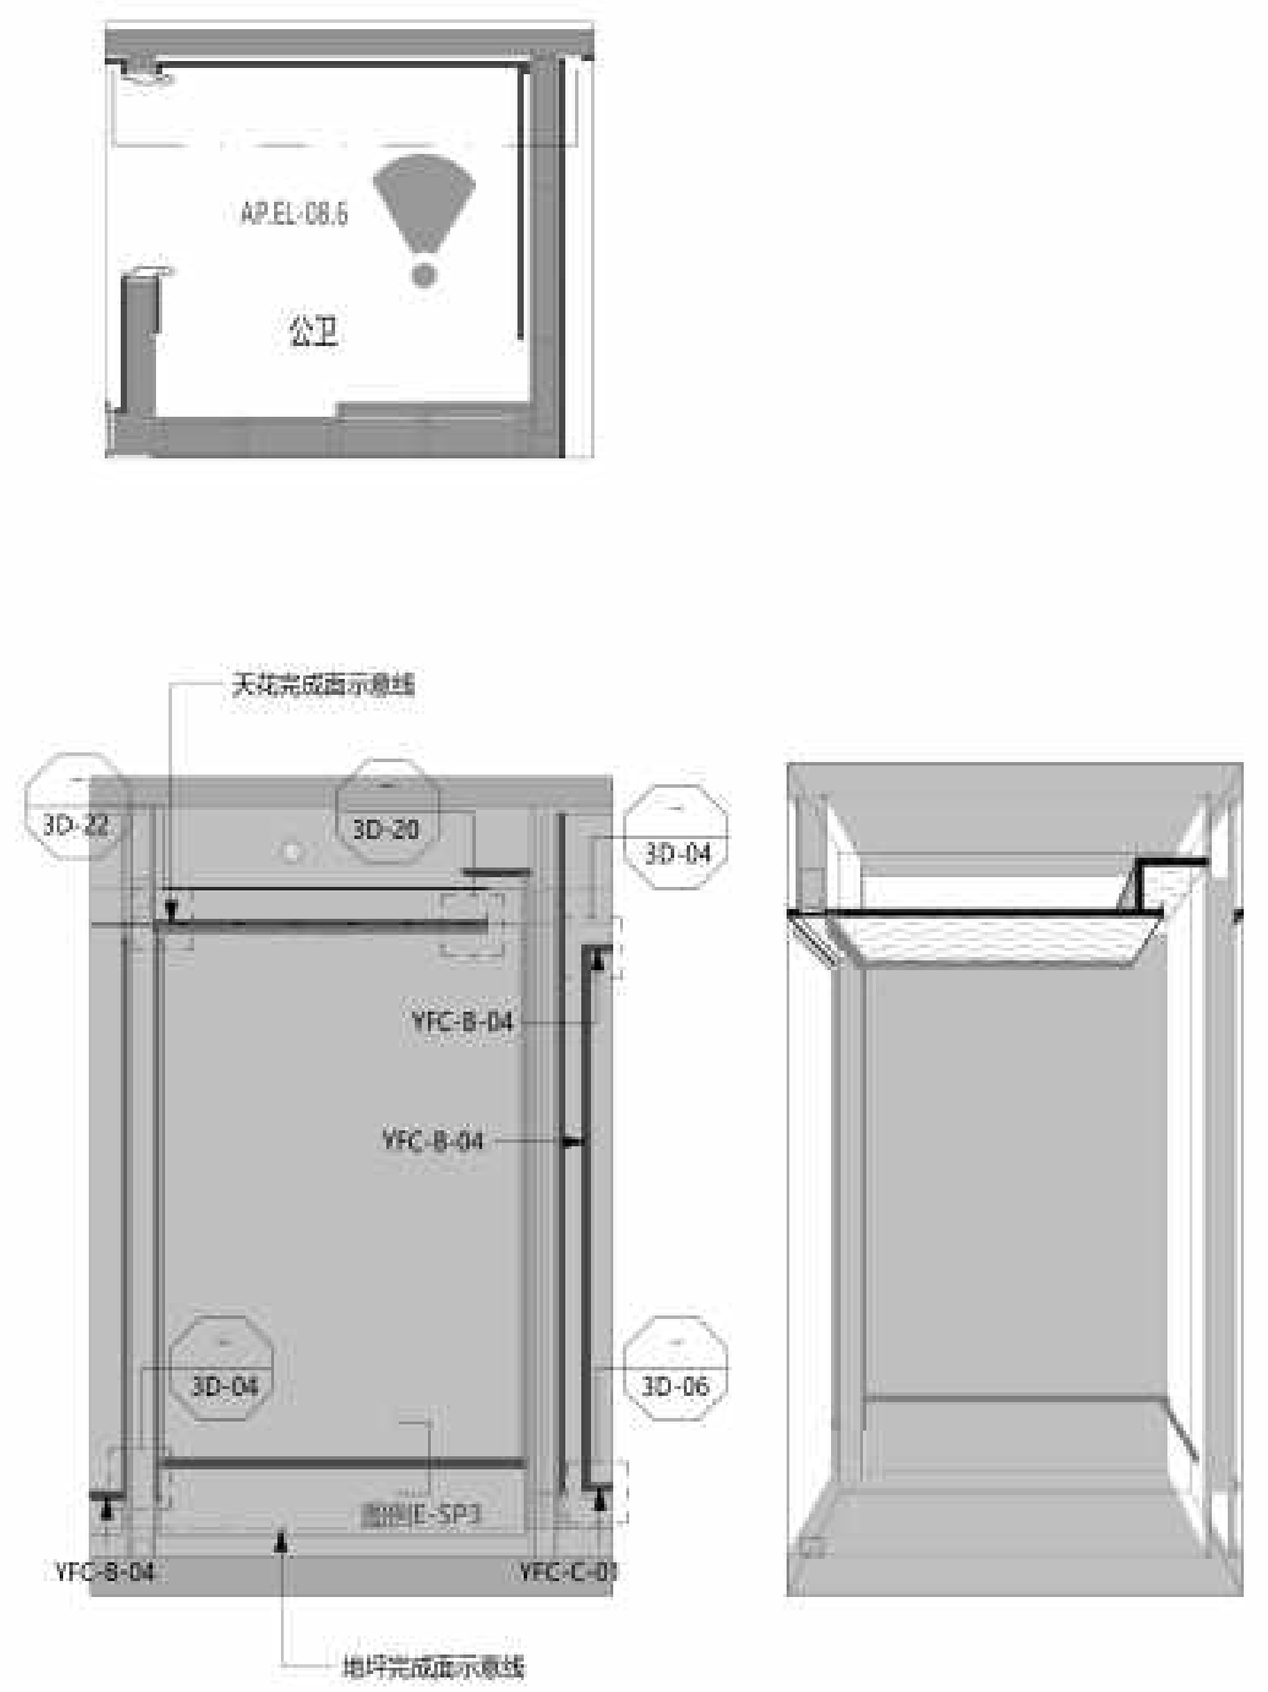
AP.EL-08.6
公卫
天花完成面示意线
3D-22
3D-20
3D-04
YFC-B-04
YFC-B-04
3D-04
3D-06
图例E-SP3
YFC-B-04
YFC-C-01
地坪完成面示意线

6

公卫 墙面及踢脚铝型材立面图6

Scale比例 1：30@A2

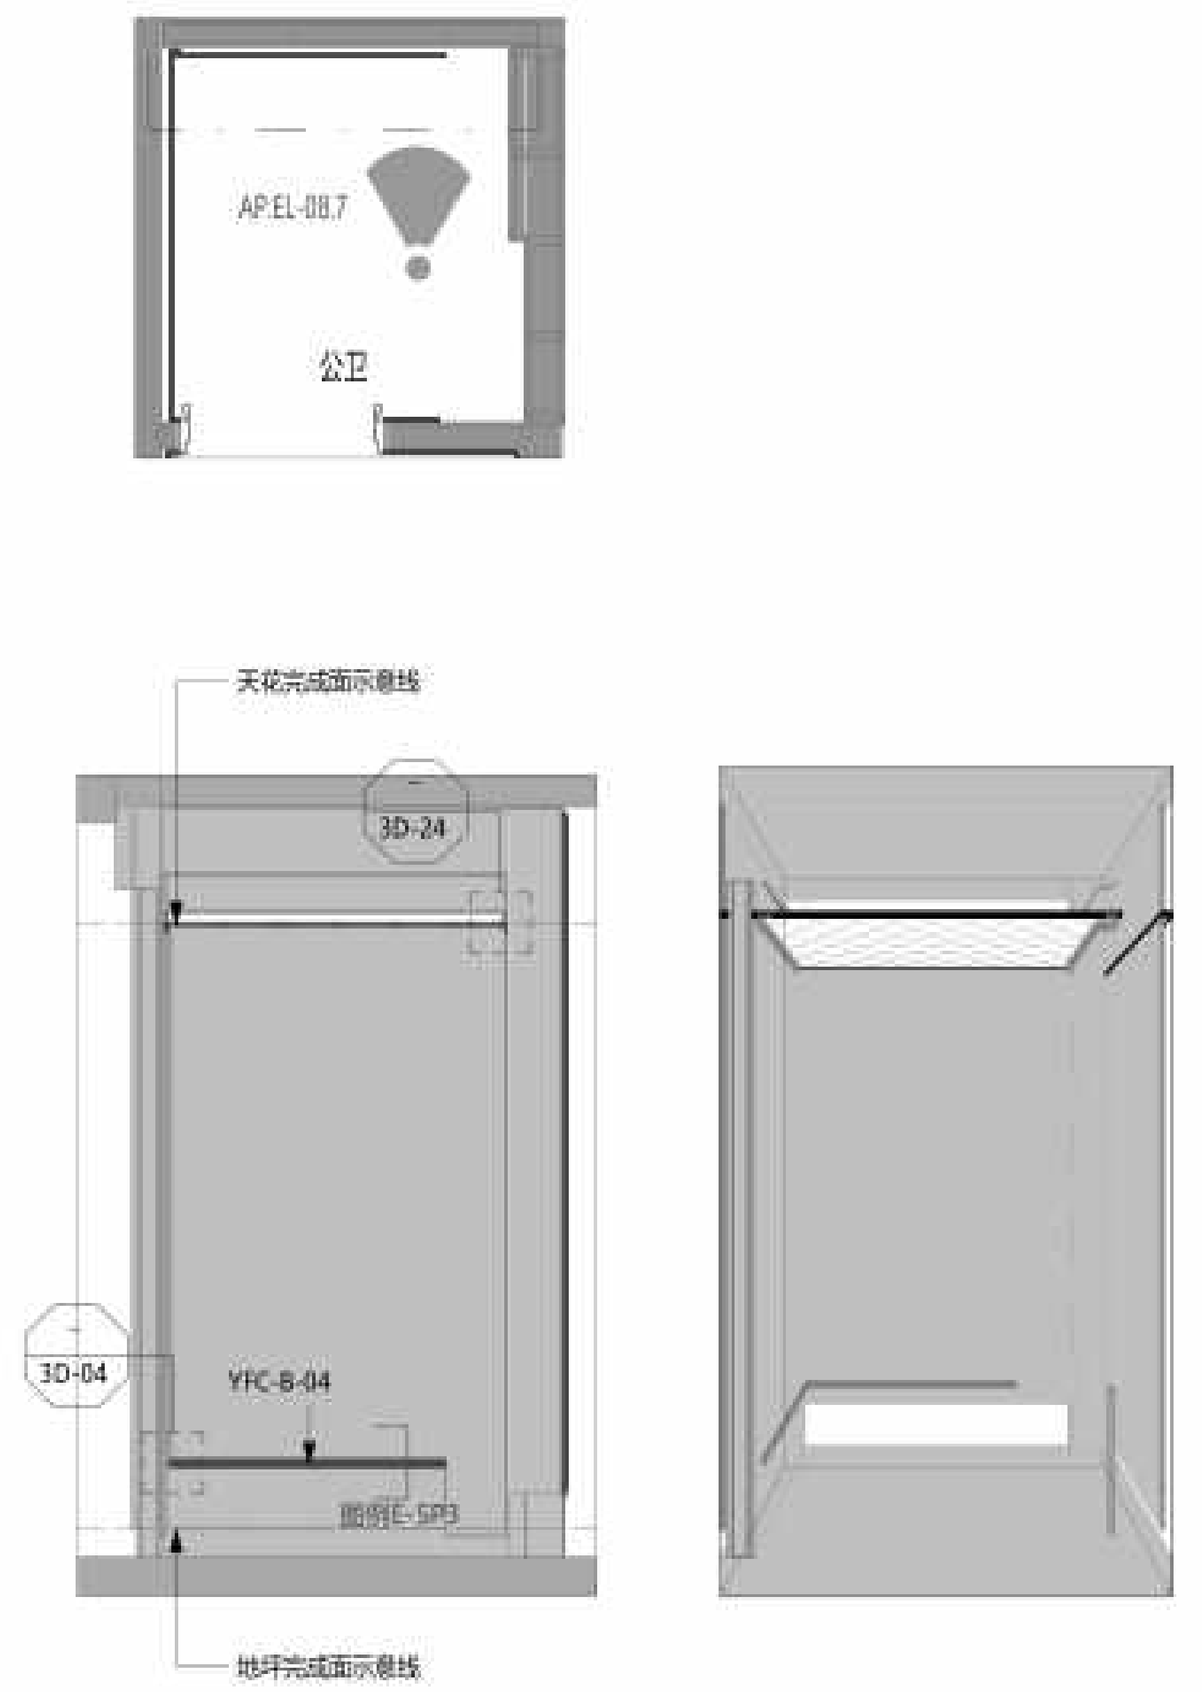
AP.EL-08.7
公卫
天花完成面示意线
3D-24
3D-04
YFC-B-04
图例E-SP3
地坪完成面示意线

7

公卫 墙面及踢脚铝型材立面图7

Scale比例 1：30@A2

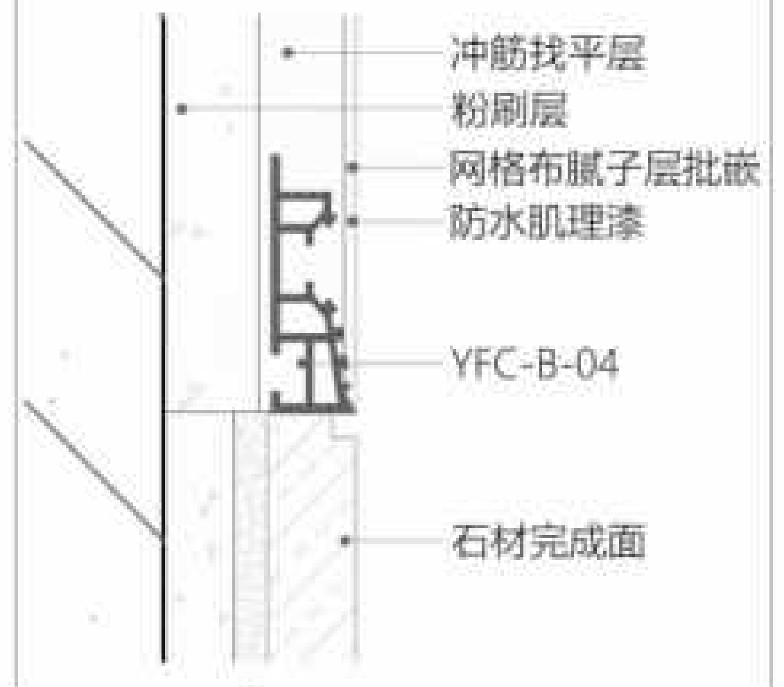
冲筋找平层
粉刷层
网格布腻子层批嵌
防水肌理漆
YFC-B-04
石材完成面

图例A-P2

墙面-石膏基找平铝型材

Scale比例 1：1@A2

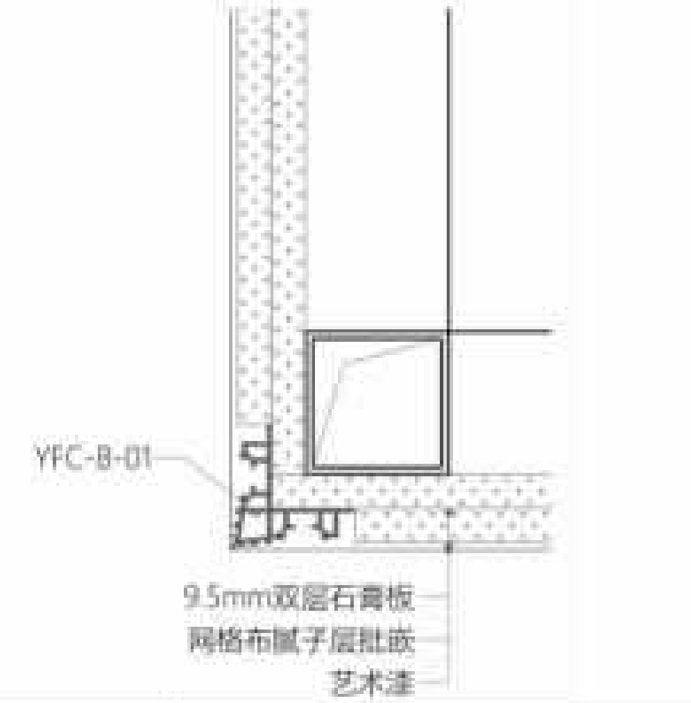
YFC-B-01
9.5mm双层石膏板
网格布腻子层批嵌
艺术漆

图例C-PB1

墙面-石膏基找平铝型材

Scale比例 1：1@A2

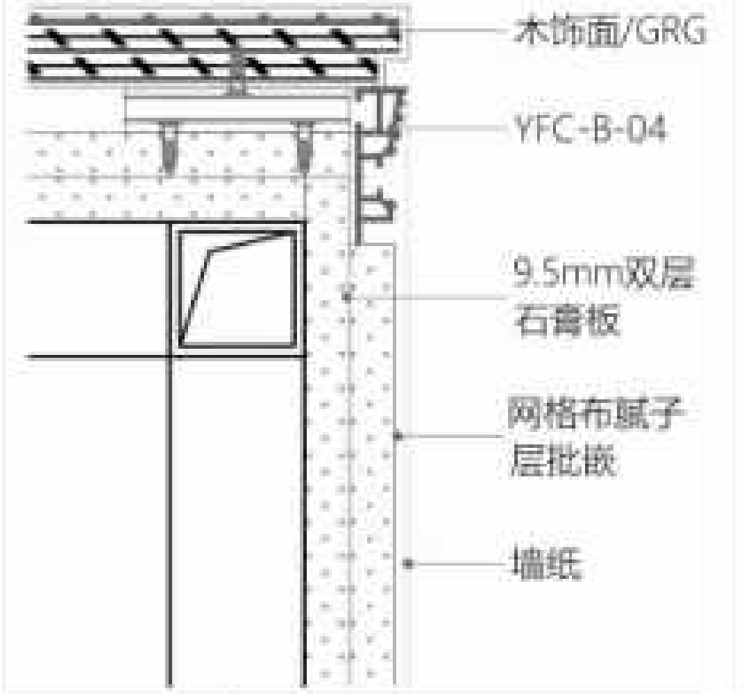
木饰面/GRG
YFC-B-04
9.5mm双层石膏板
网格布腻子层批嵌
墙纸

图例C-PB2

墙面-石膏基找平铝型材

Scale比例 1：1@A2

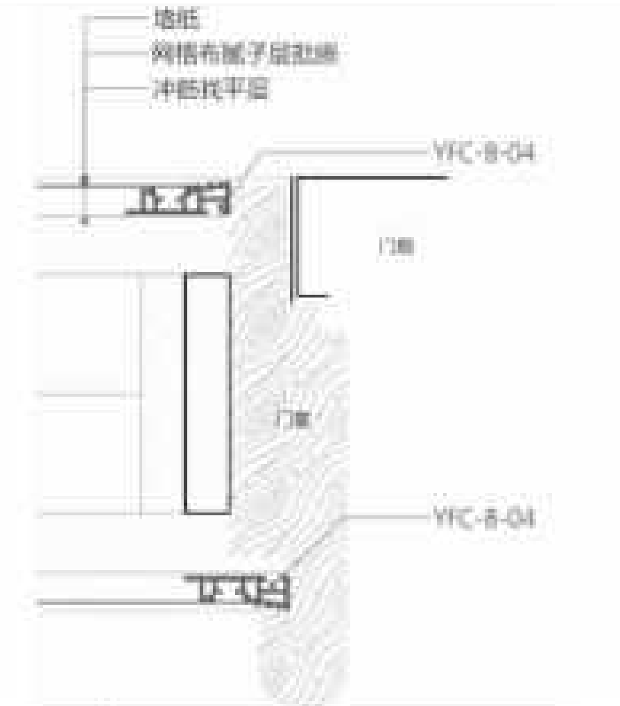
墙纸
网格布腻子层批嵌
冲筋找平层
YFC-B-04
门套
门套
YFC-B-04

图例D-M2

门边-石膏基找平铝型材

Scale比例 1：1@A2

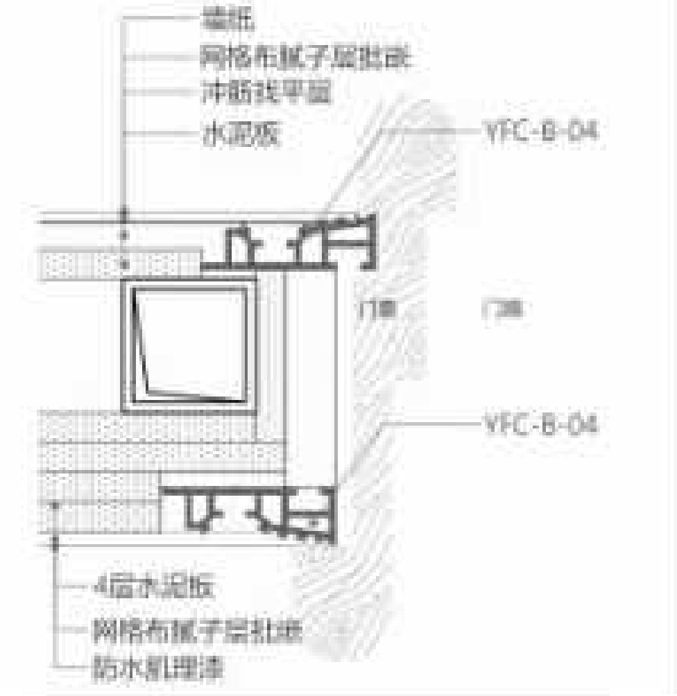
墙纸
网格布腻子层批嵌
冲筋找平层
水泥板
YFC-B-04
门套
门套
YFC-B-04
4层水泥板
网格布腻子层批嵌
防水肌理漆

图例D-M6

门边-石膏基找平铝型材

Scale比例 1：1@A2

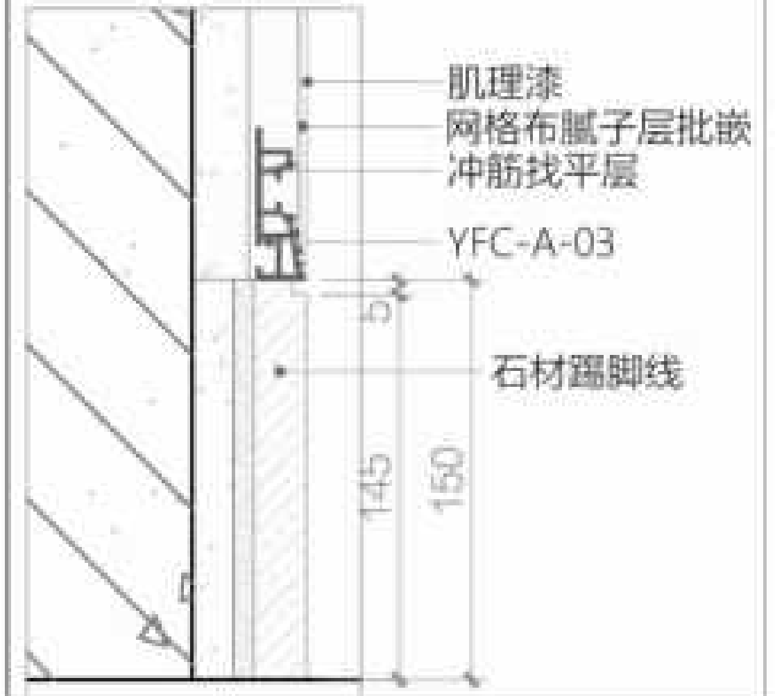
肌理漆
网格布腻子层批嵌
冲筋找平层
YFC-A-03
5
石材踢脚线
145
150

图例E-SP3

踢脚-石膏基找平铝型材

Scale比例 1：1@A2

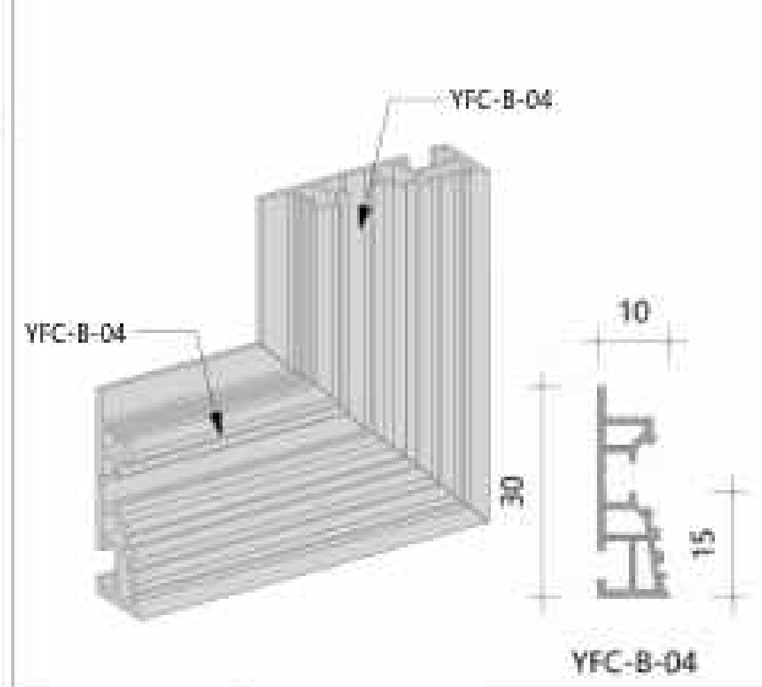
YFC-B-04
YFC-B-04
10
30
15
YFC-B-04

3D-01

转角铝型材-拼接跟通

转角数量：2

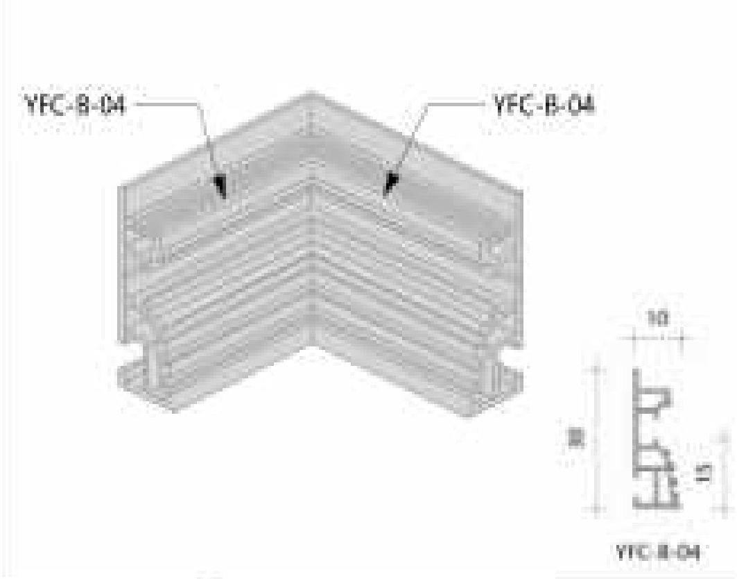
YFC-B-04
YFC-B-04
10
30
15
YFC-B-04

3D-04

转角铝型材-拼接跟通

转角数量：4

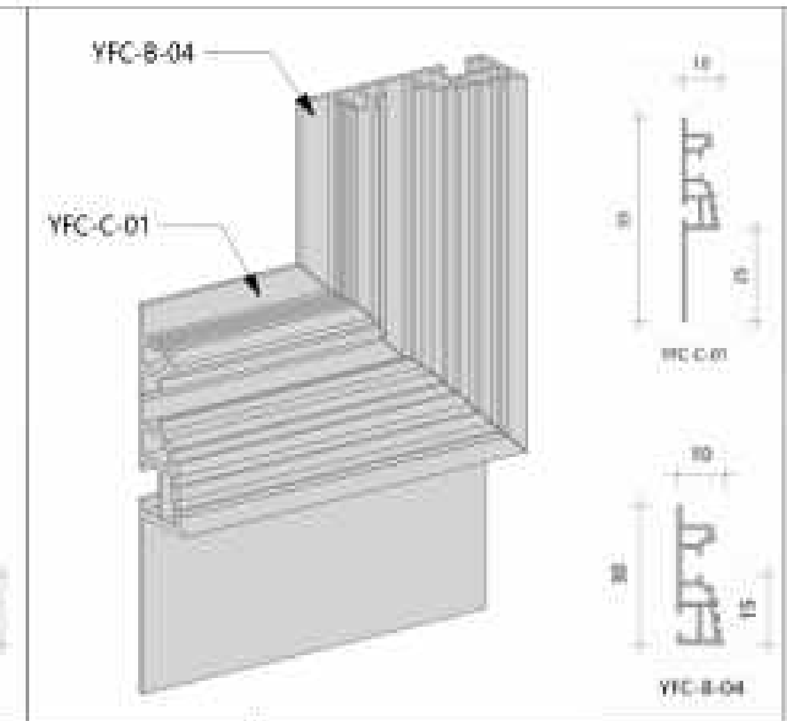
YFC-B-04
YFC-C-01
10
YFC-C-01
10
30
15
YFC-B-04

3D-06

转角铝型材-拼接跟通

转角数量：1

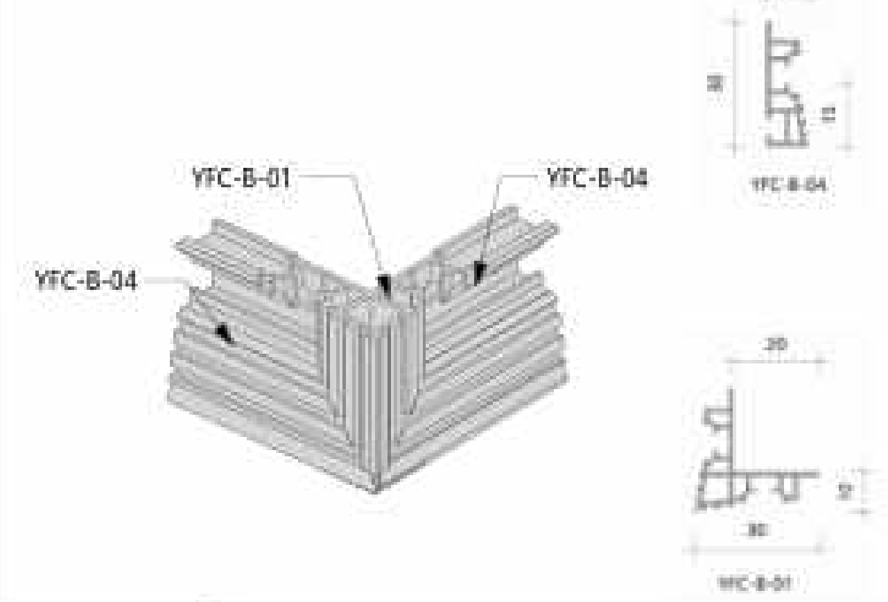
YFC-B-01
YFC-B-04
YFC-B-04
10
30
15
YFC-B-04
20
30
YFC-B-01

3D-12

转角铝型材-拼接跟通

转角数量：2

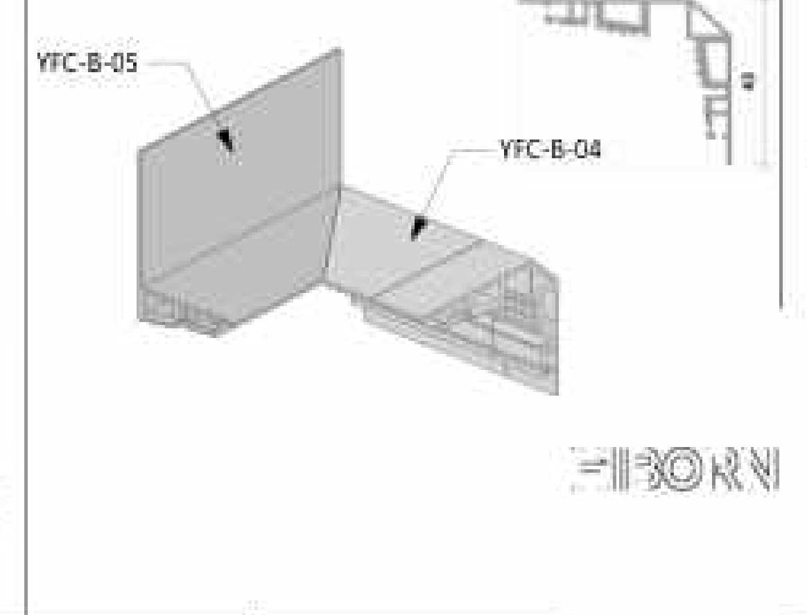
YFC-B-05
YFC-B-04

3D-20

转角铝型材-拼接跟通

转角数量：4

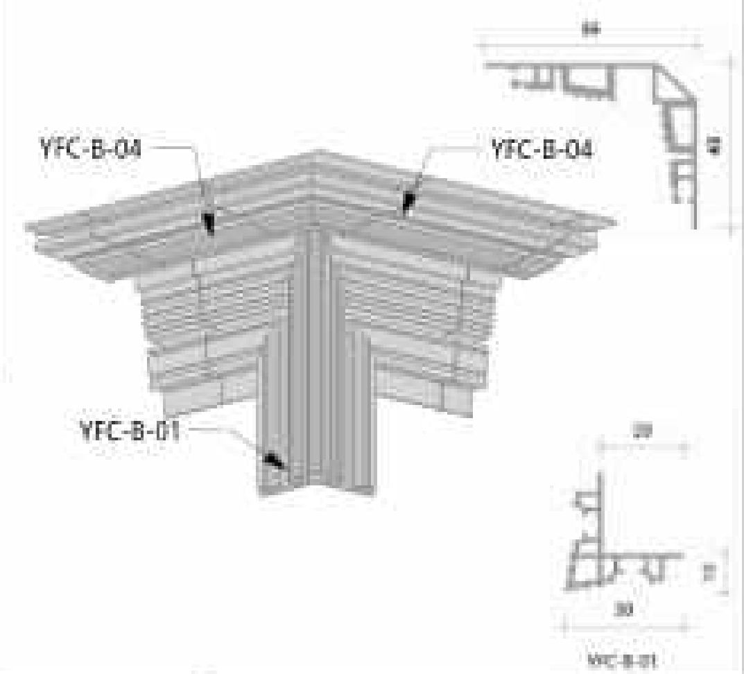
YFC-B-04
YFC-B-04
YFC-B-01
20
30
YFC-B-01

3D-21

转角铝型材-拼接跟通

转角数量：2

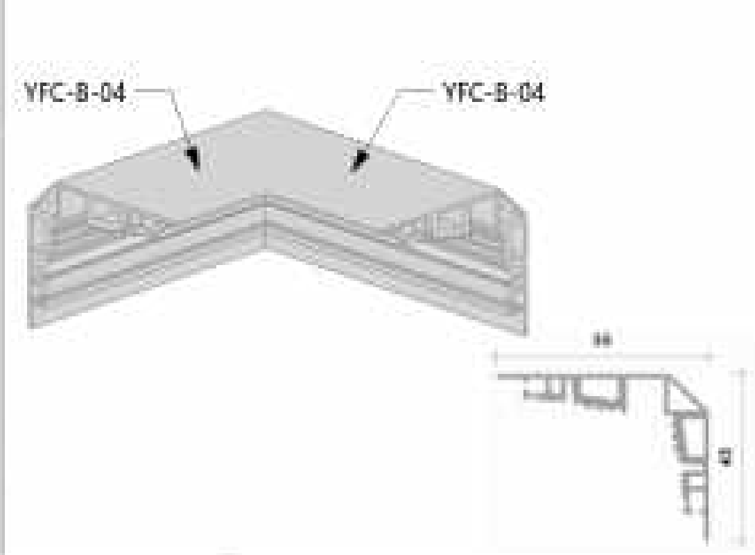
YFC-B-04
YFC-B-04

3D-22

转角铝型材-拼接跟通

转角数量：6

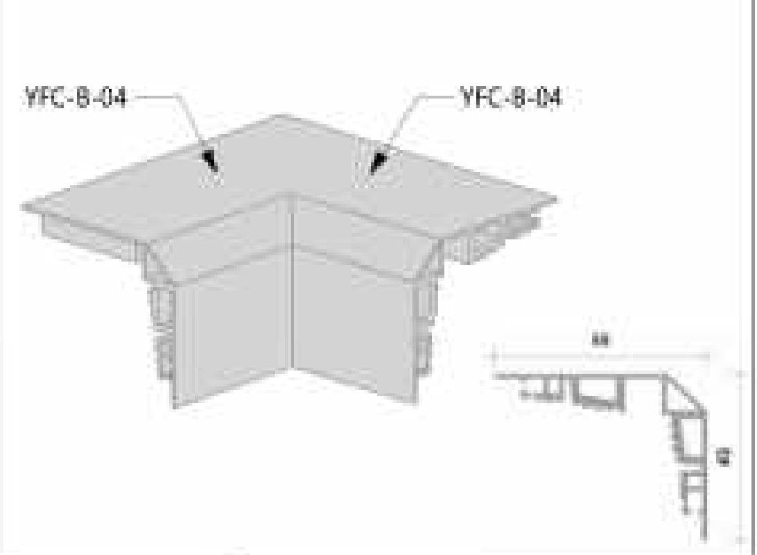
YFC-B-04
YFC-B-04

3D-24

转角铝型材-拼接跟通

转角数量：1

备注

注释
Notes
1.[illegible]
2.[illegible]
3.[illegible]

日期
Date 03/04/26

修订
Revision

项目
Project
潮映华岸府3-801

比例
Scale 1：30@A2

客卫、公卫
墙面及踢脚铝型材

图纸编号
Drawing No.
AP.EL-08

项目编号
Project No.

©2025

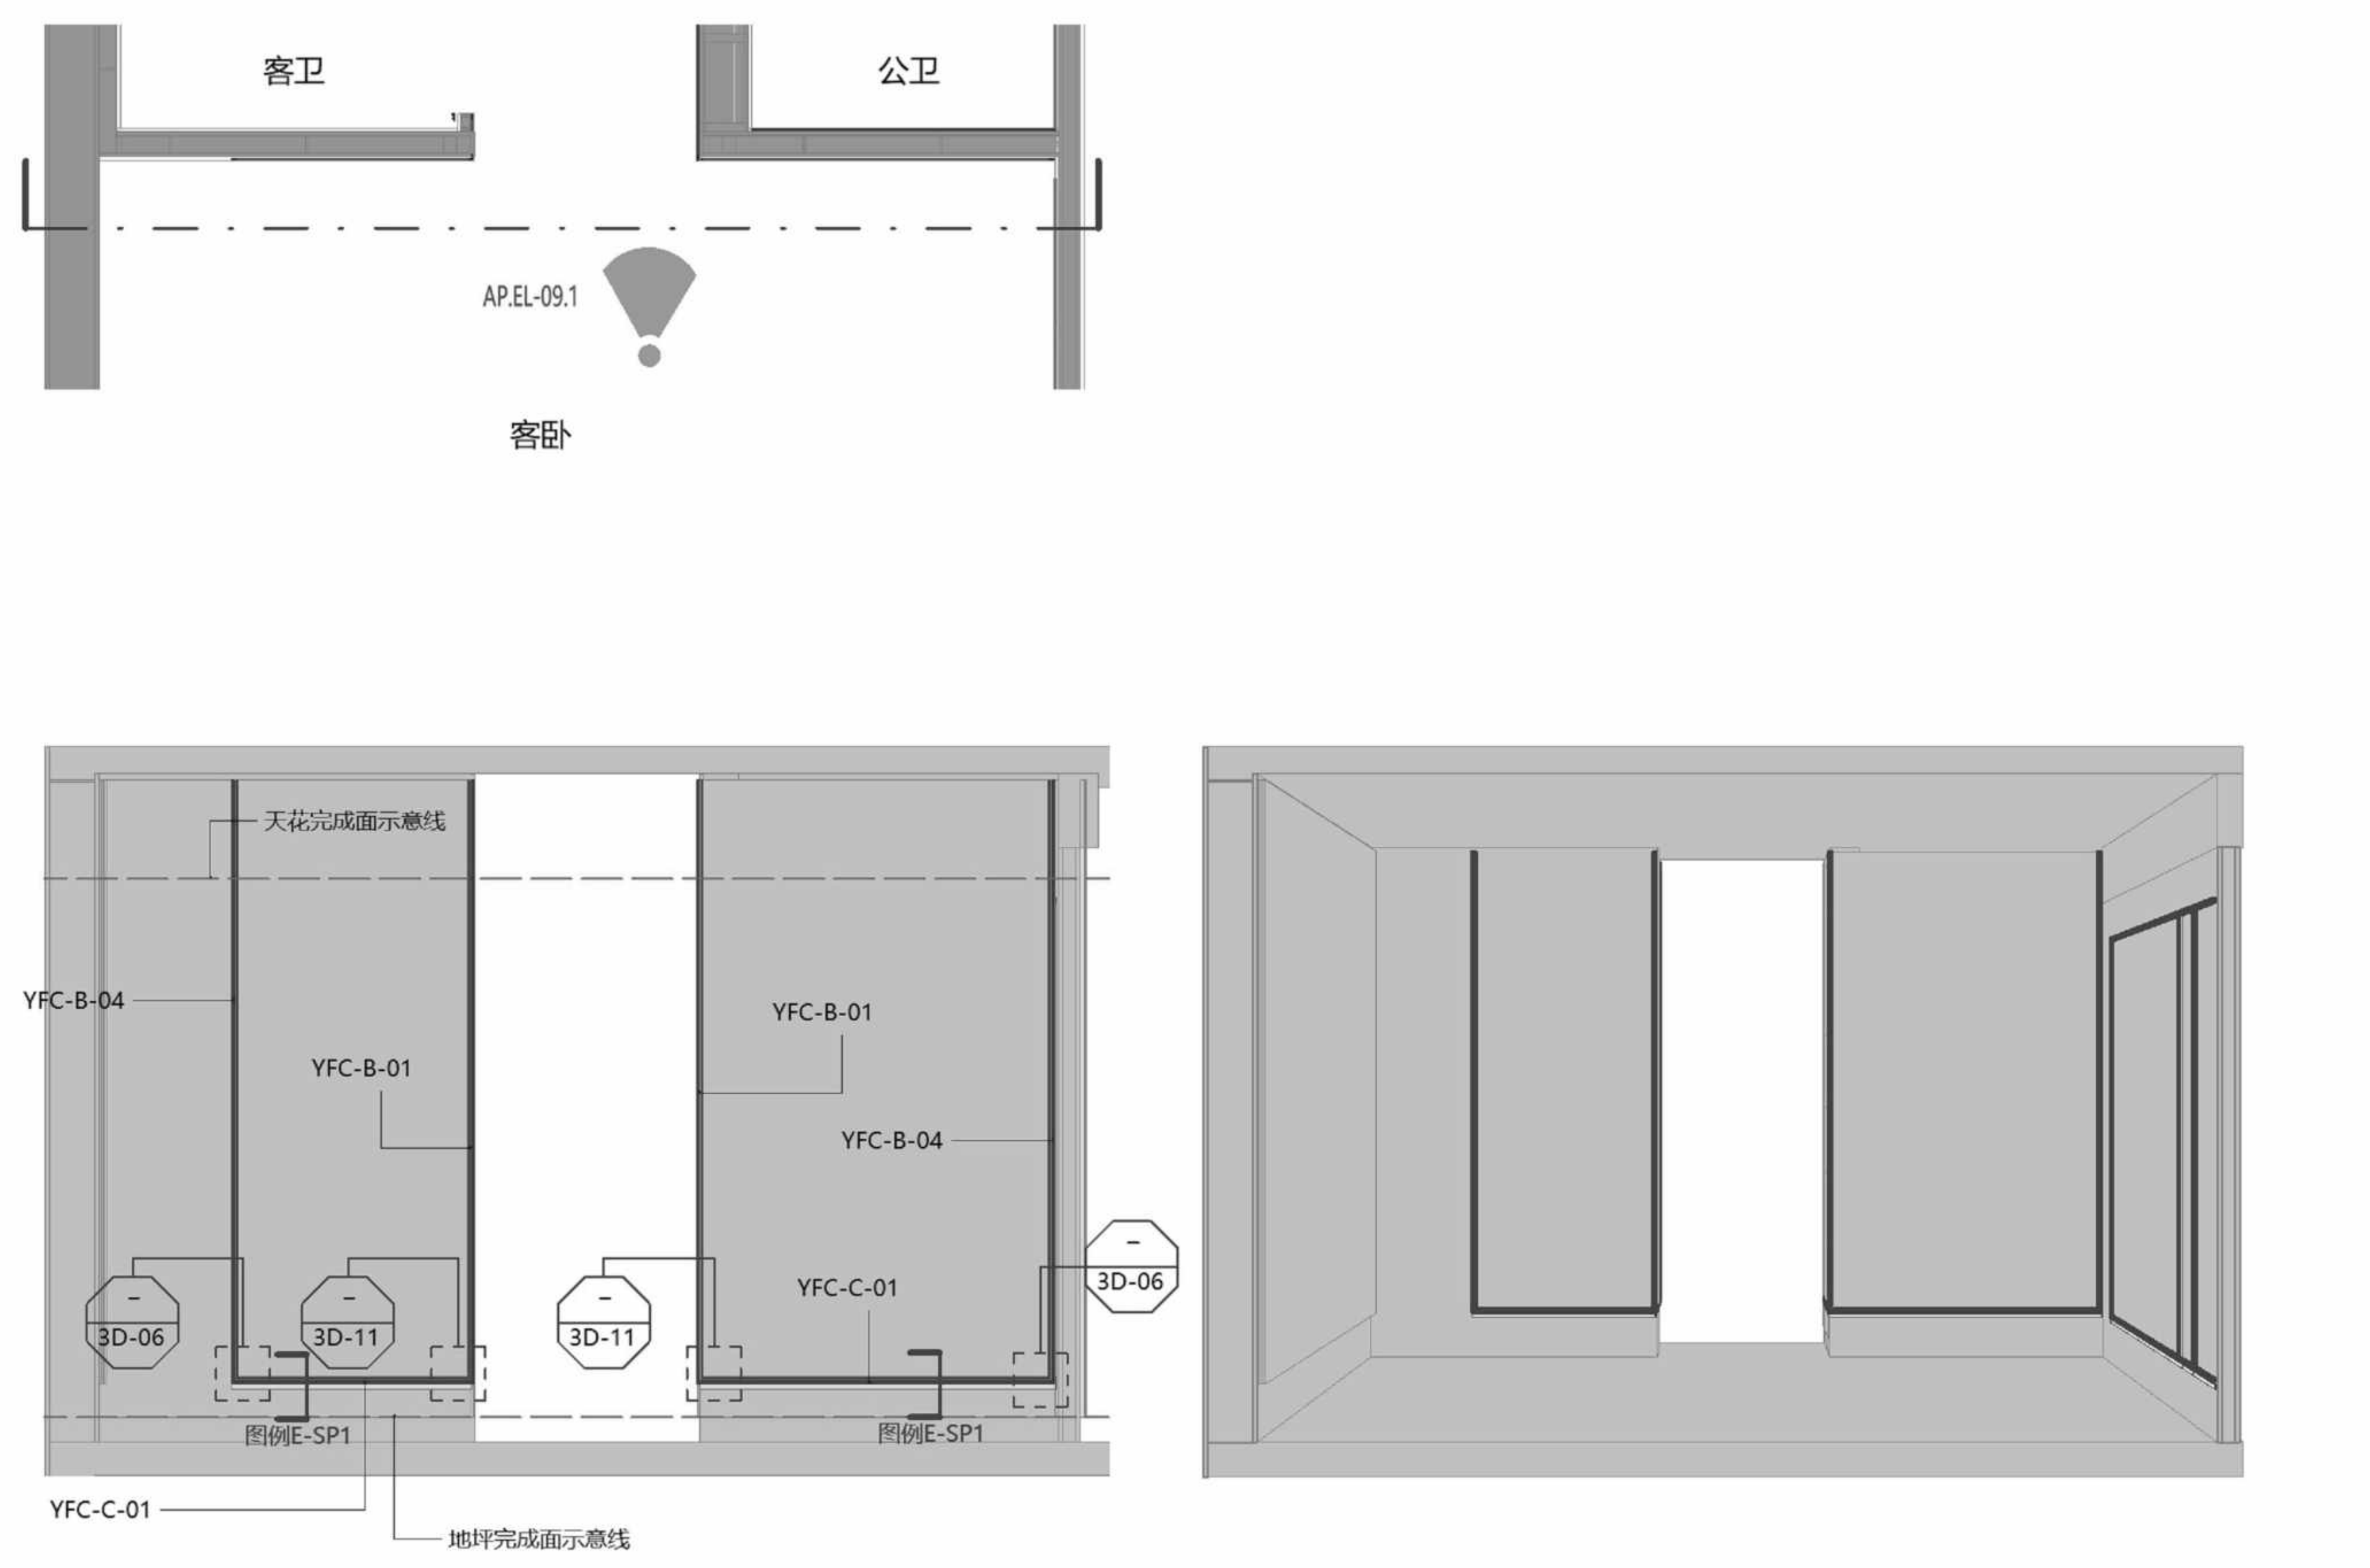
客卫
公卫
AP.EL-09.1
客卧
天花完成面示意线
YFC-B-04
YFC-B-01
YFC-B-01
YFC-B-04
YFC-C-01
3D-06
3D-11
3D-11
3D-06
图例E-SP1
图例E-SP1
YFC-C-01
地坪完成面示意线

1

客卧 墙面及踢脚铝型材立面图1

Scale比例 1：30@A2

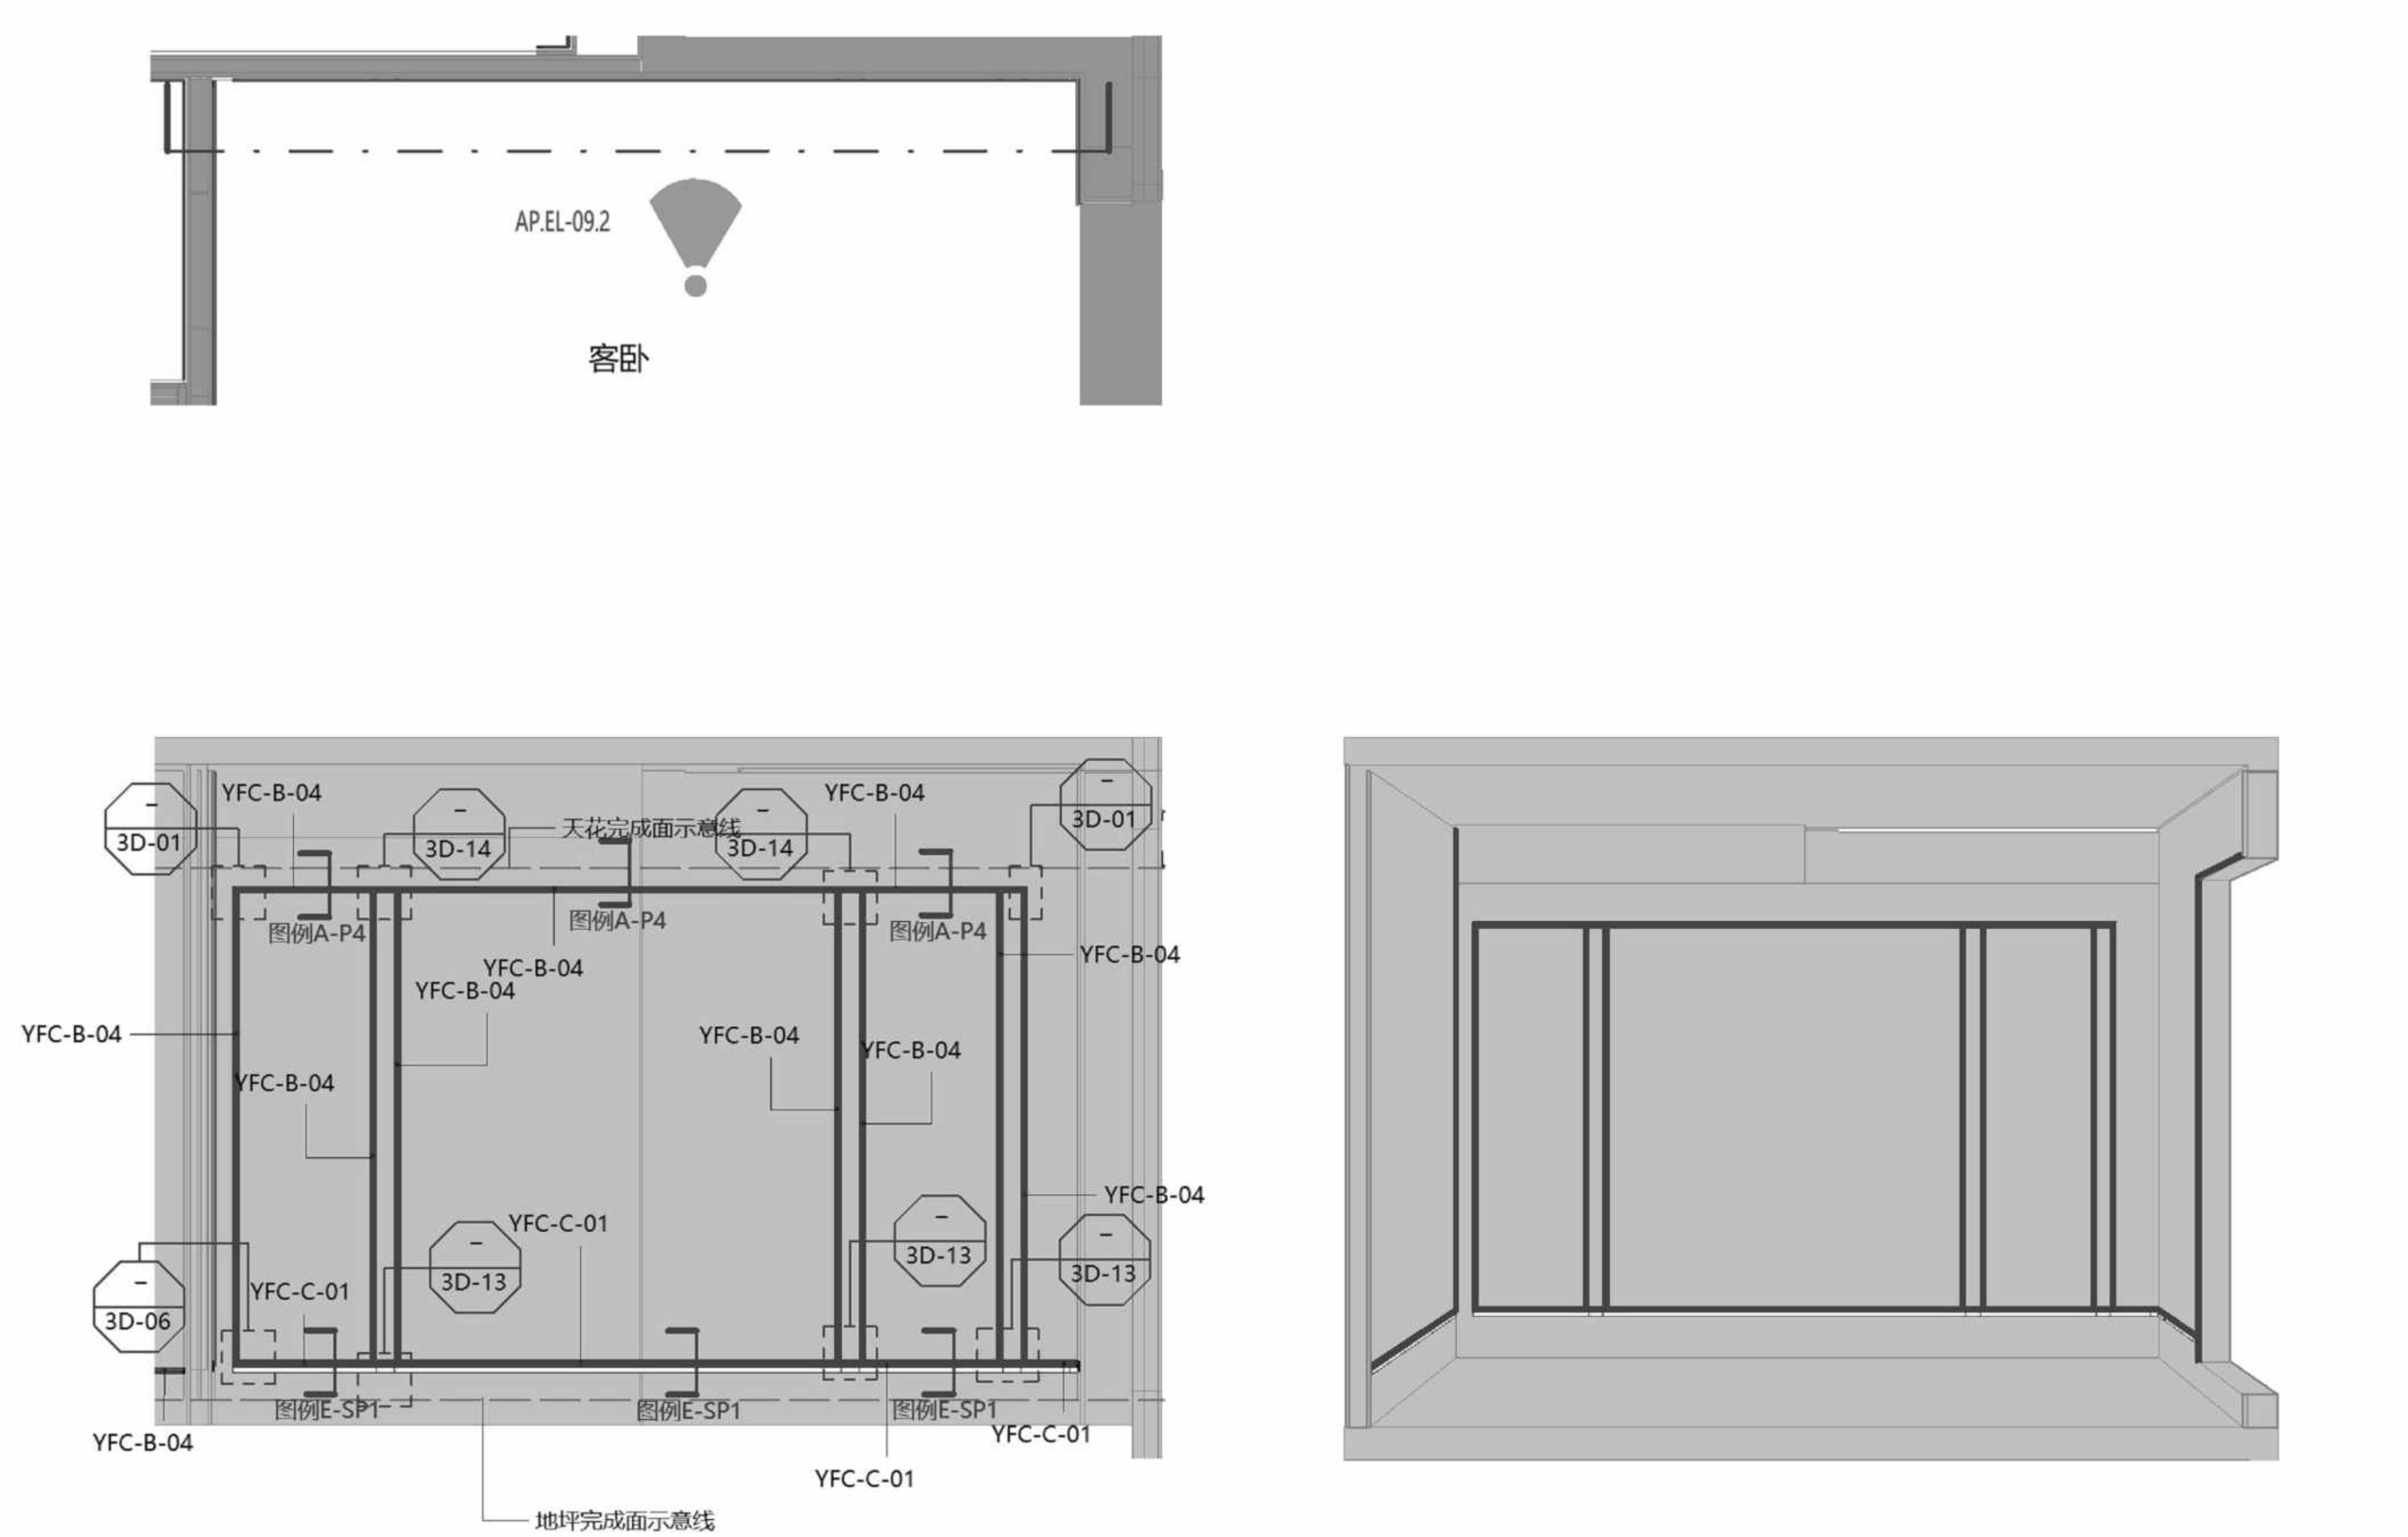
AP.EL-09.2
客卧
3D-01
YFC-B-04
3D-14
天花完成面示意线
3D-14
YFC-B-04
3D-01
图例A-P4
图例A-P4
图例A-P4
YFC-B-04
YFC-B-04
YFC-B-04
YFC-B-04
YFC-B-04
YFC-B-04
YFC-B-04
YFC-B-04
YFC-C-01
YFC-C-01
3D-13
3D-13
3D-13
3D-06
图例E-SP1
图例E-SP1
图例E-SP1
YFC-B-04
YFC-C-01
YFC-C-01
地坪完成面示意线

2

客卧 墙面及踢脚铝型材立面图2

Scale比例 1：30@A2

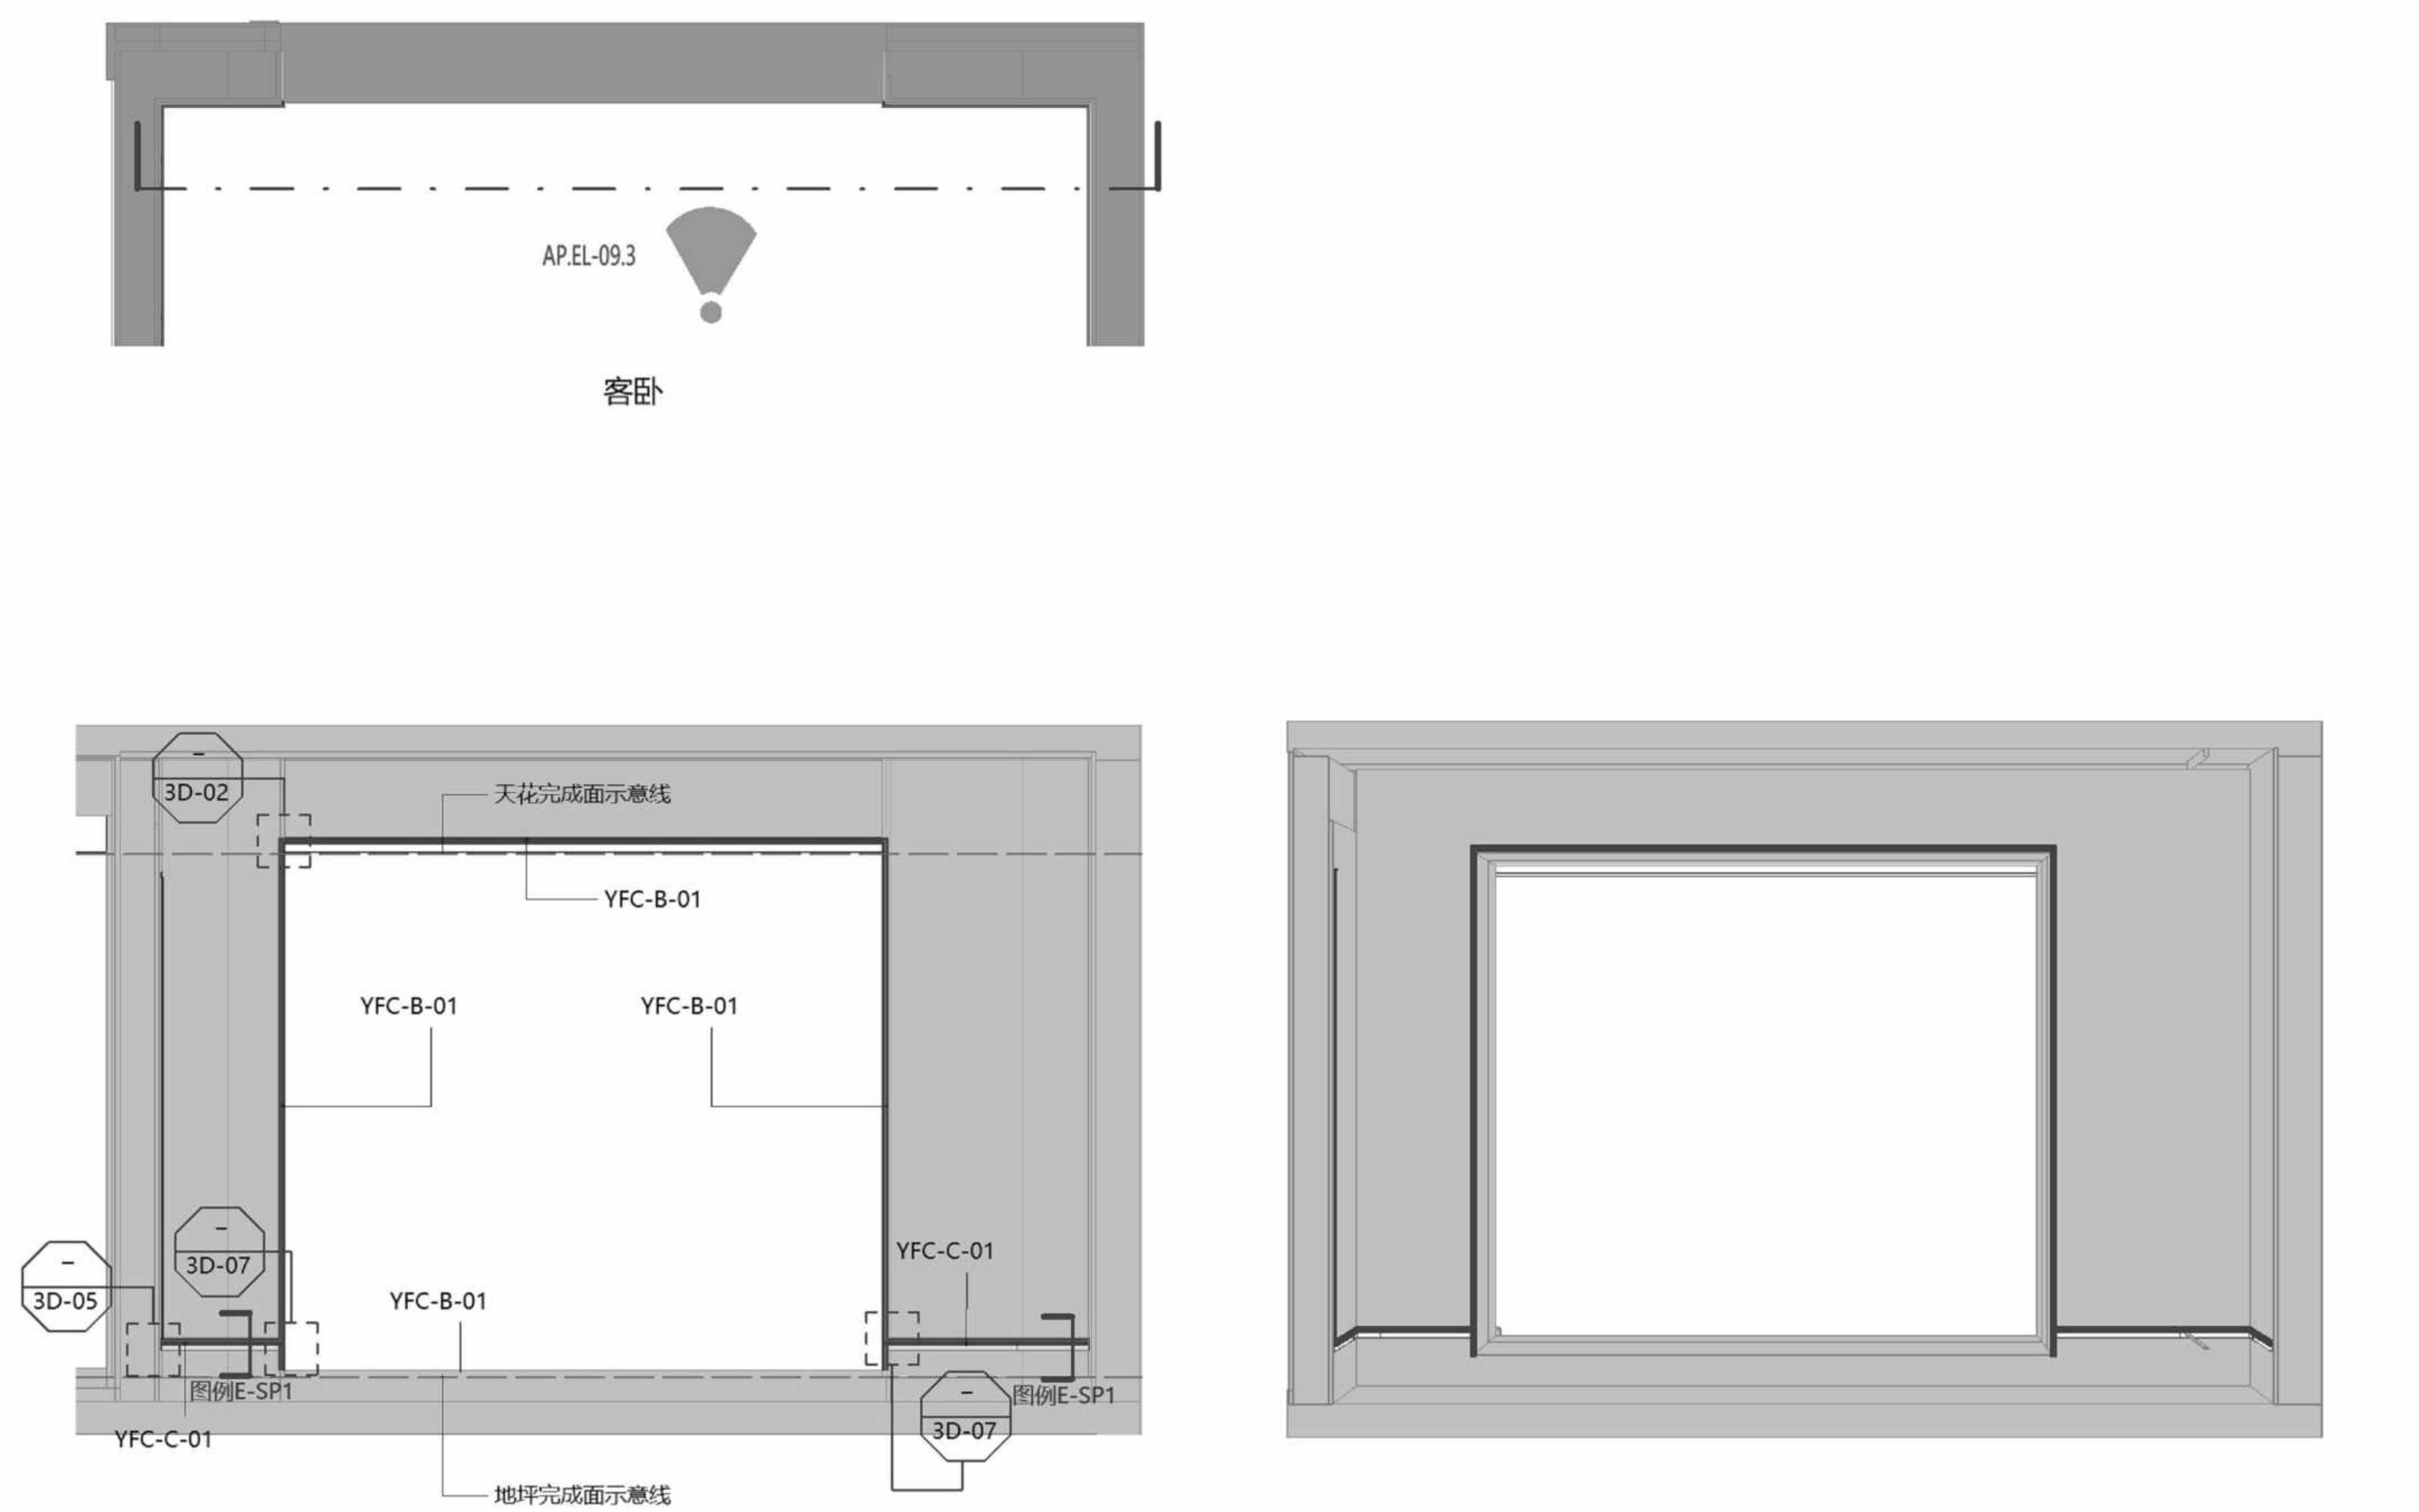
AP.EL-09.3
客卧
3D-02
天花完成面示意线
YFC-B-01
YFC-B-01
YFC-B-01
YFC-B-01
YFC-C-01
3D-05
3D-07
3D-07
图例E-SP1
图例E-SP1
YFC-C-01
地坪完成面示意线

3

客卧 墙面及踢脚铝型材立面图3

Scale比例 1：30@A2

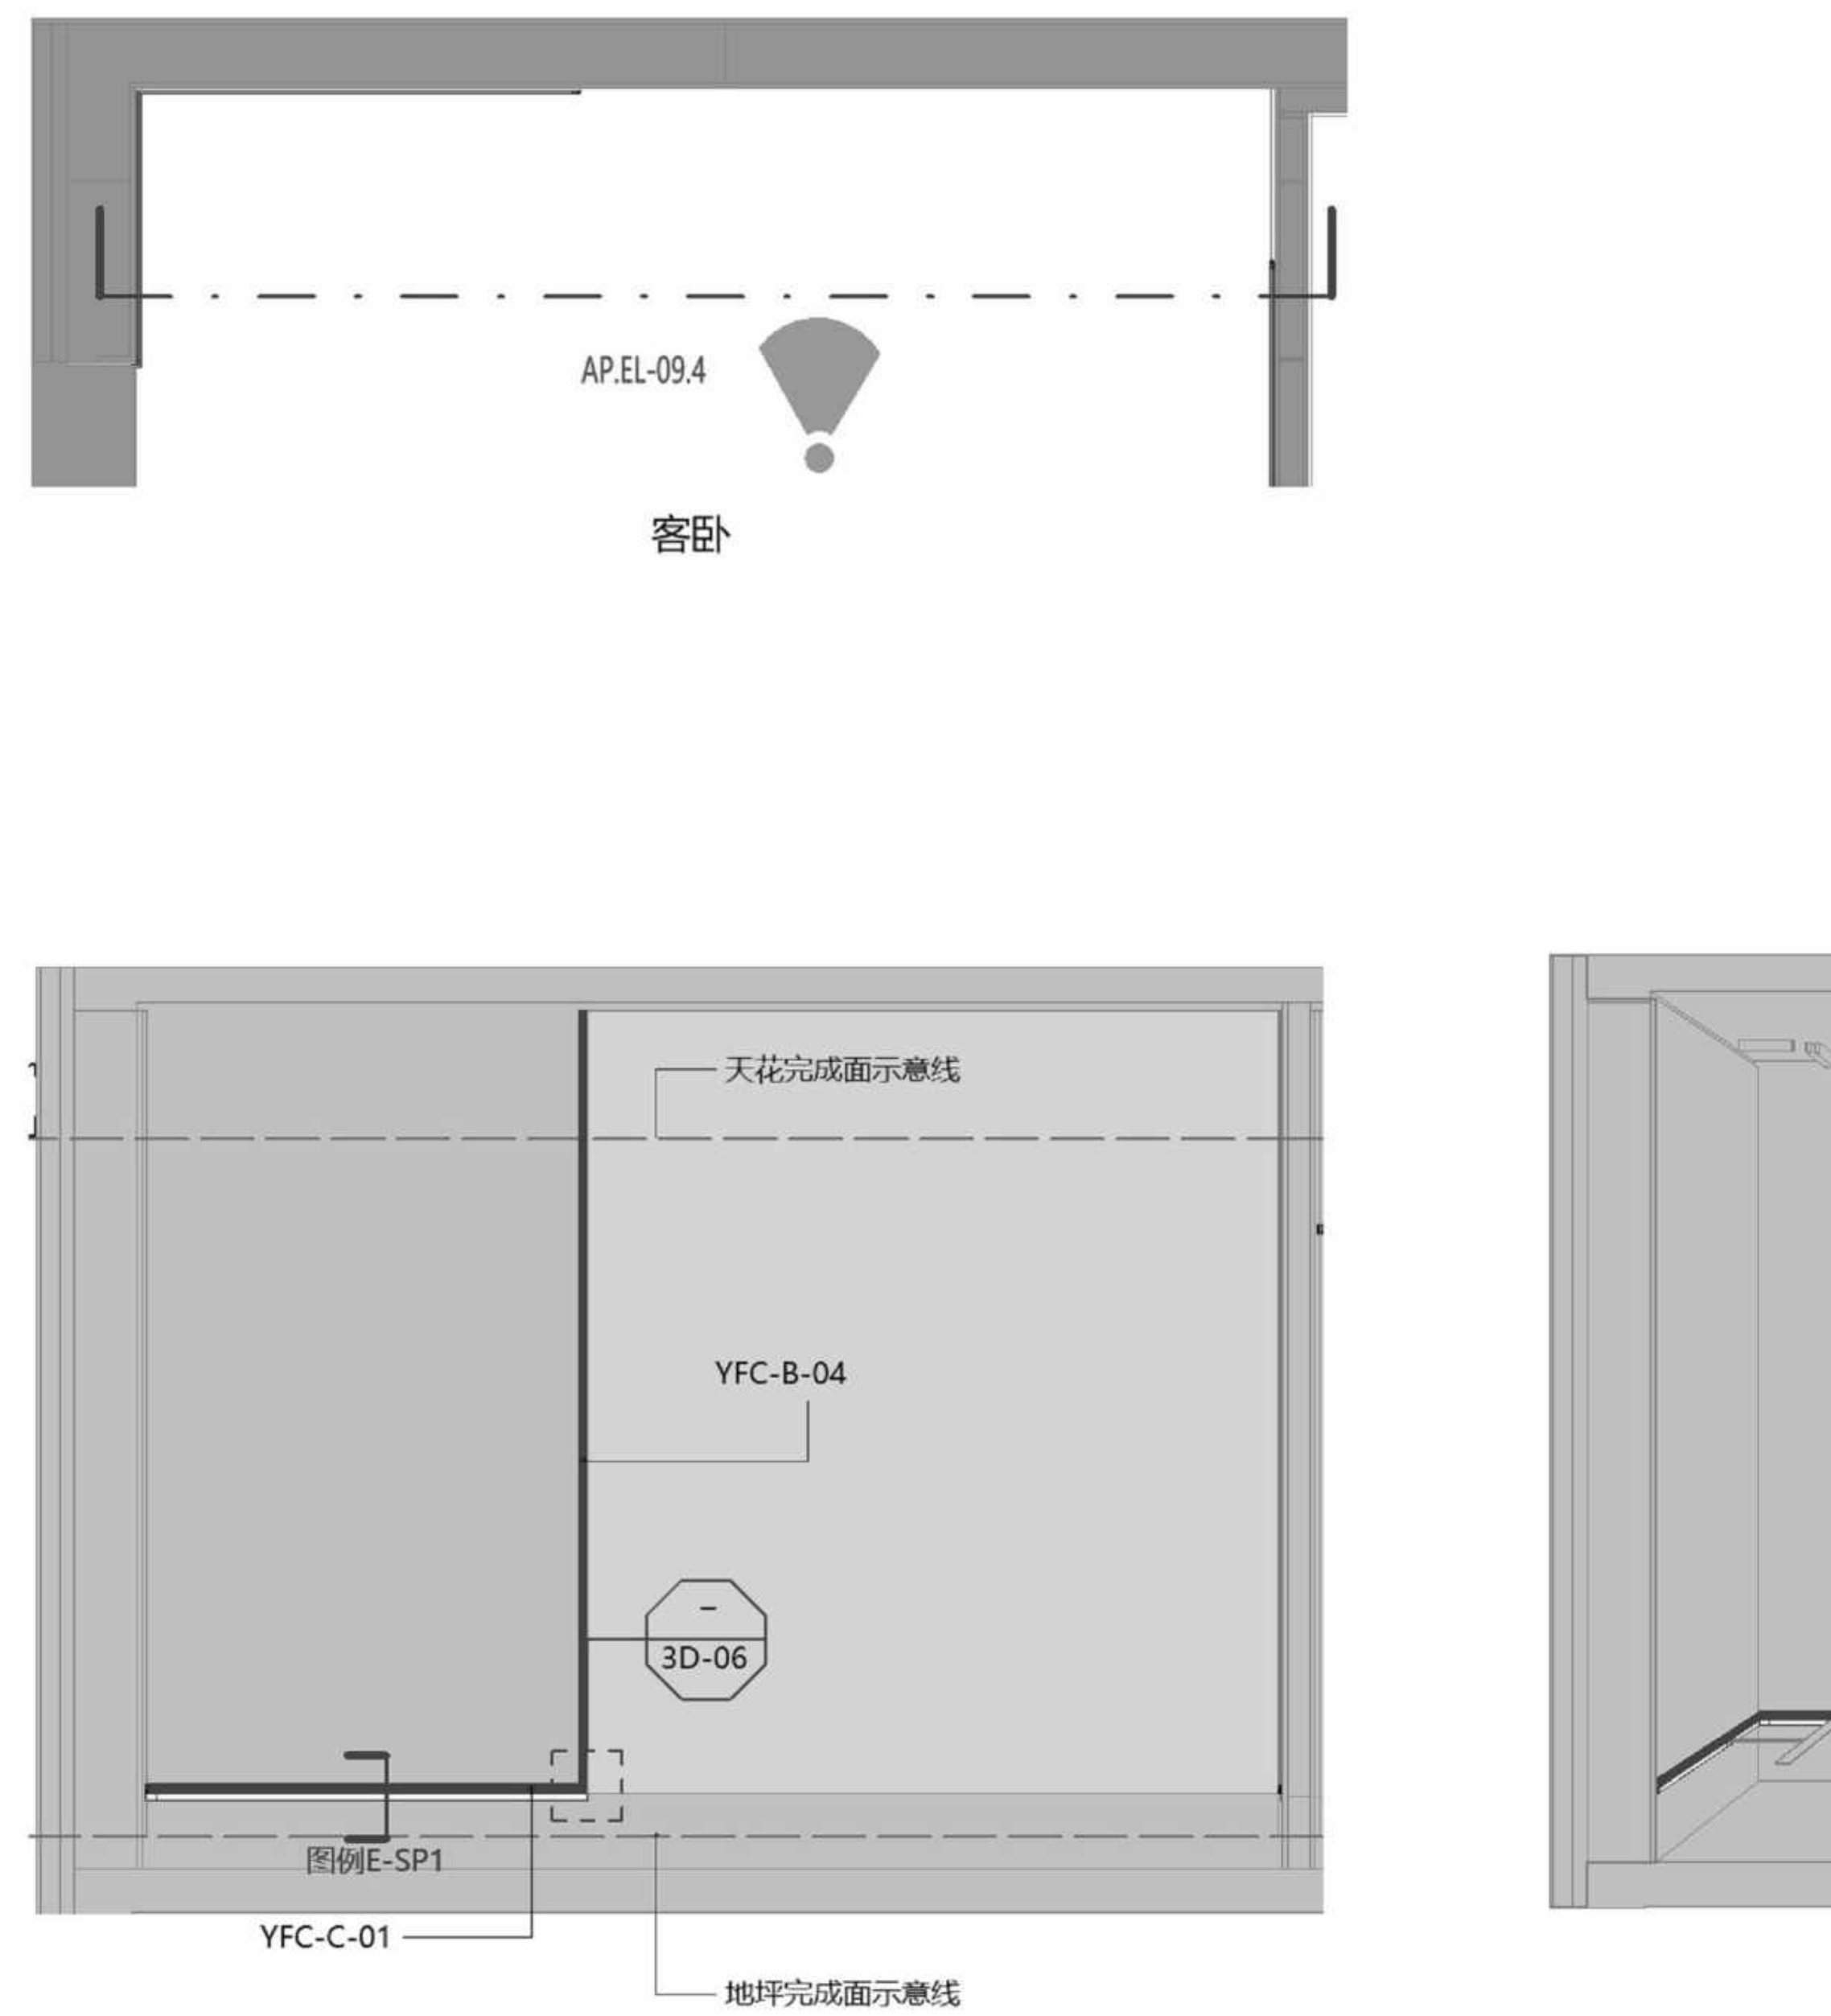
AP.EL-09.4
客卧
天花完成面示意线
YFC-B-04
3D-06
图例E-SP1
YFC-C-01
地坪完成面示意线

4

客卧 墙面及踢脚铝型材立面图4

Scale比例 1：30@A2

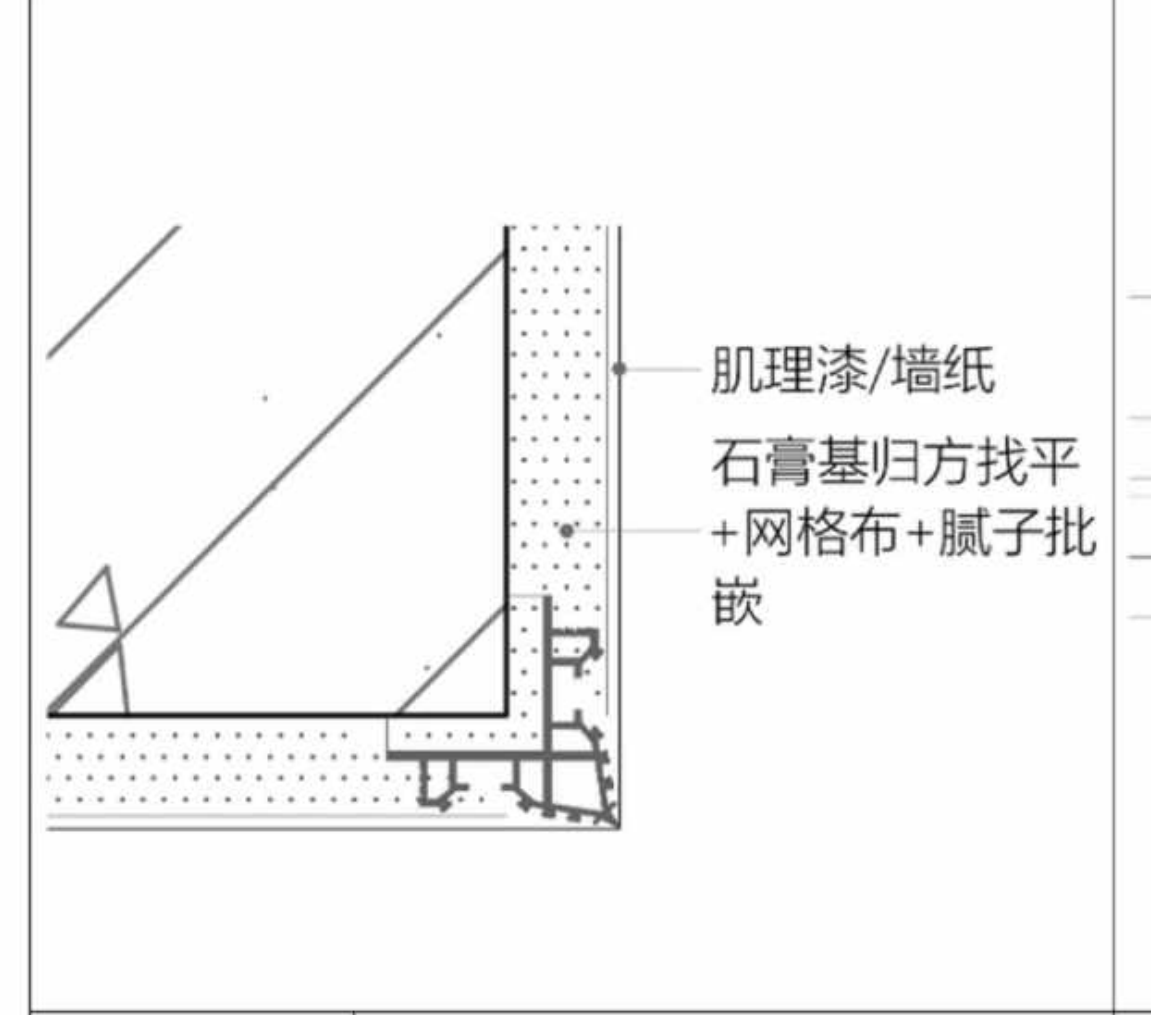
肌理漆/墙纸
石膏基归方找平
+网格布+腻子批嵌

图例A-P1

墙面-石膏基找平铝型材

Scale比例 1：1@A2

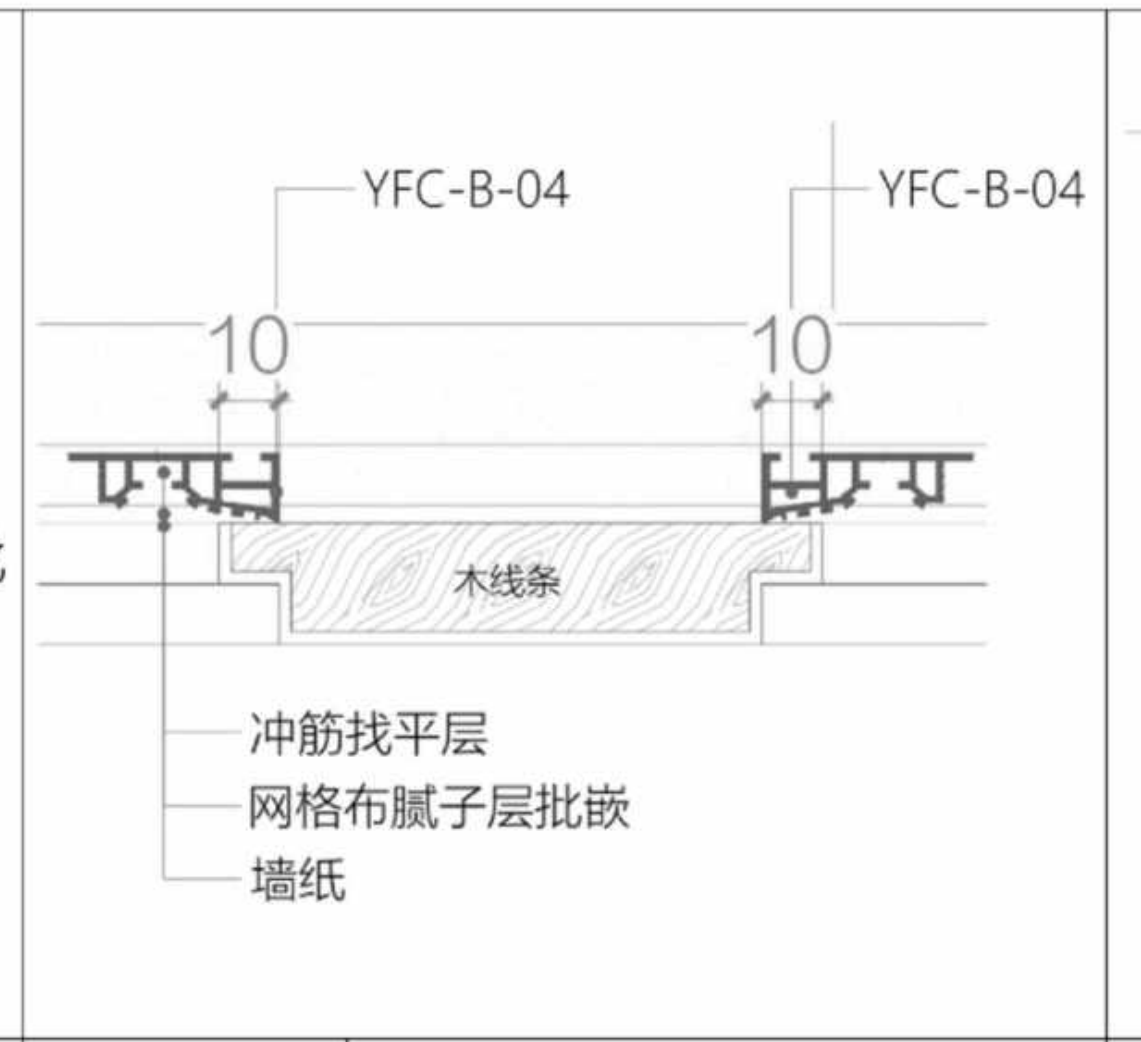
YFC-B-04
YFC-B-04
10
10
木线条
冲筋找平层
网格布腻子层批嵌
墙纸

图例A-P4

墙面-石膏基找平铝型材

Scale比例 1：1@A2

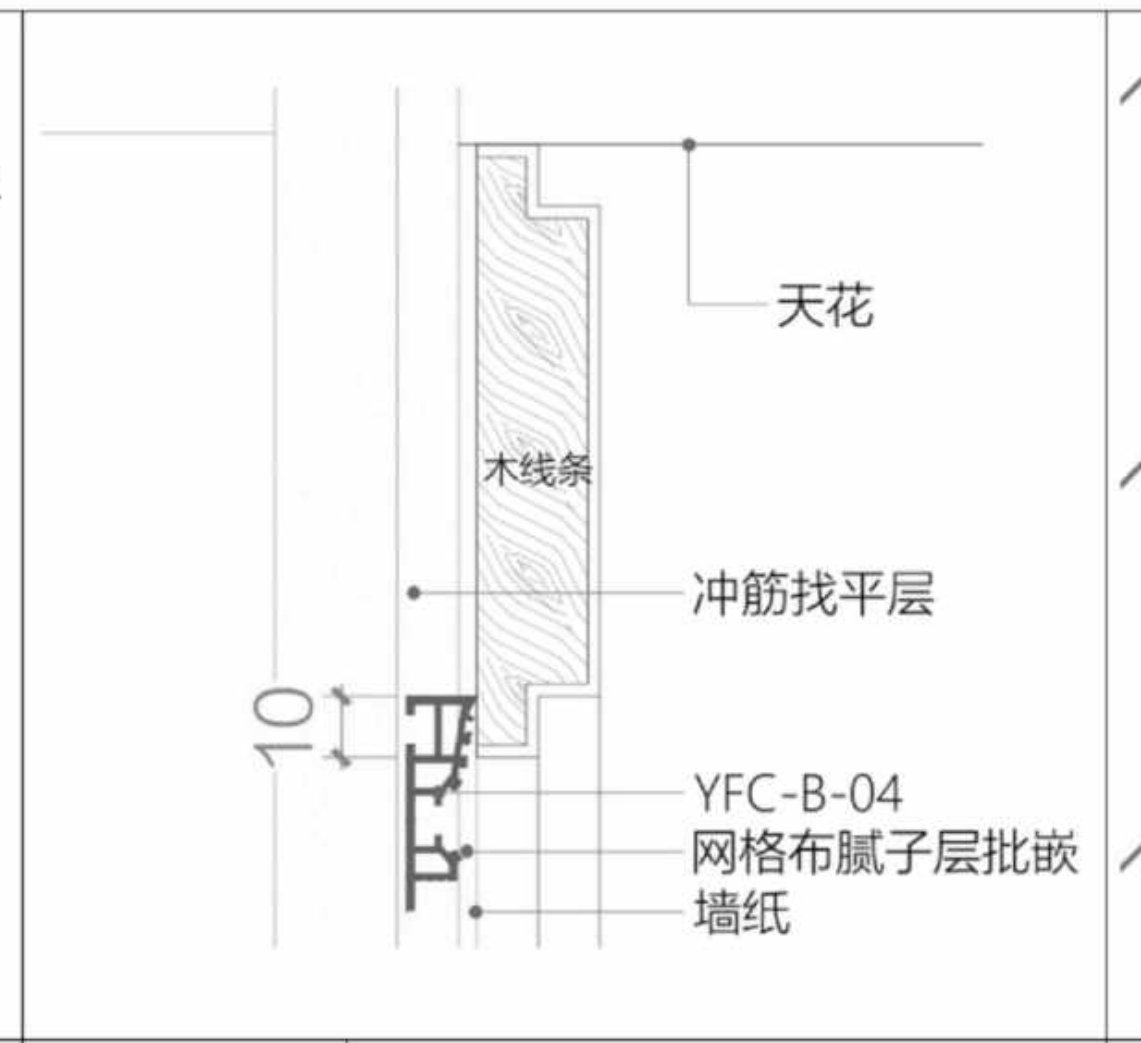
天花
木线条
冲筋找平层
10
YFC-B-04
网格布腻子层批嵌
墙纸

图例A-P5

墙面-石膏基找平铝型材

Scale比例 1：1@A2

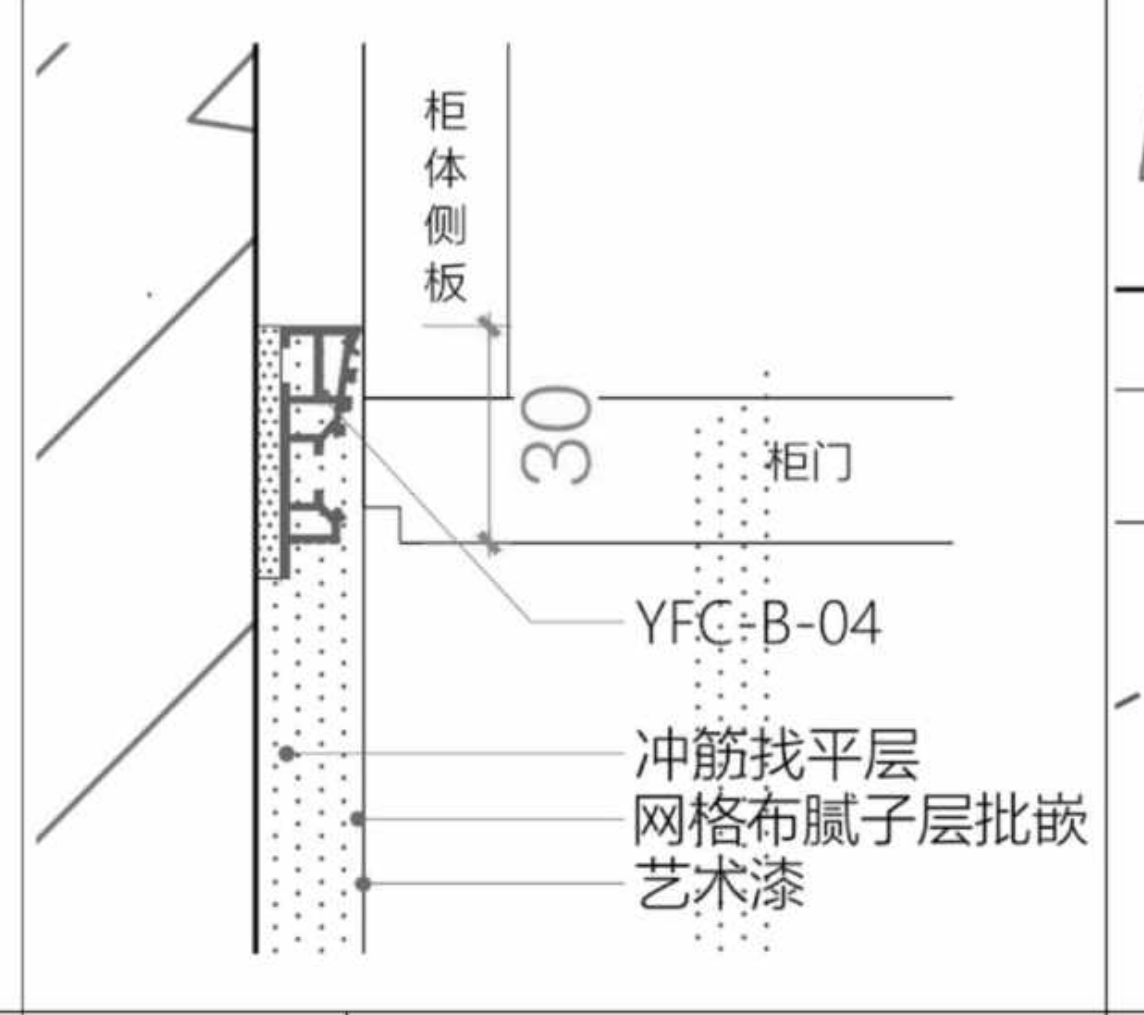
柜体侧板
30
柜门
YFC-B-04
冲筋找平层
网格布腻子层批嵌
艺术漆

图例B-P6

柜边-石膏基找平铝型材

Scale比例 1：1@A2

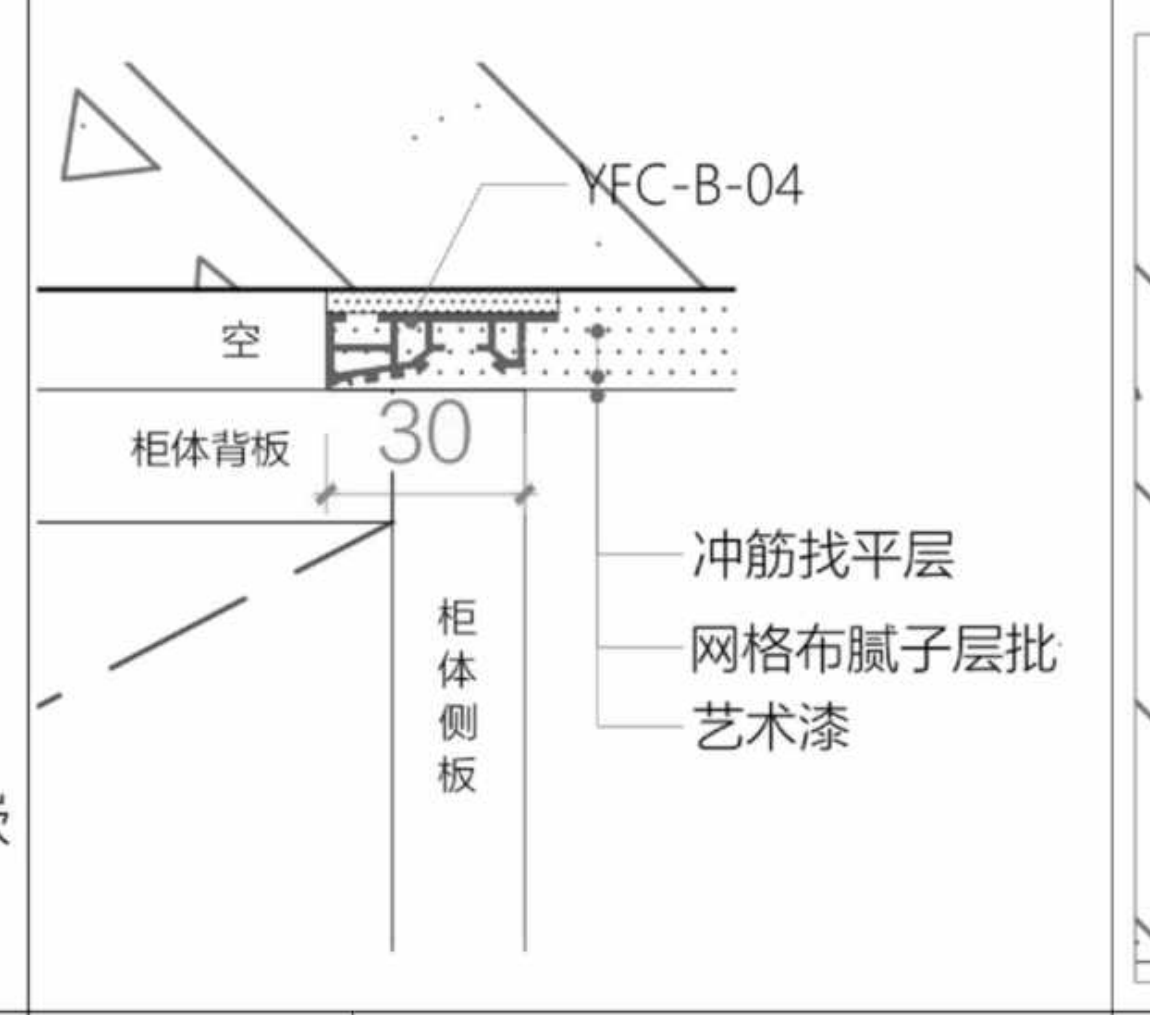
YFC-B-04
空
柜体背板
30
柜体侧板
冲筋找平层
网格布腻子层批
艺术漆

图例A-P7

柜边-石膏基找平铝型材

Scale比例 1：1@A2

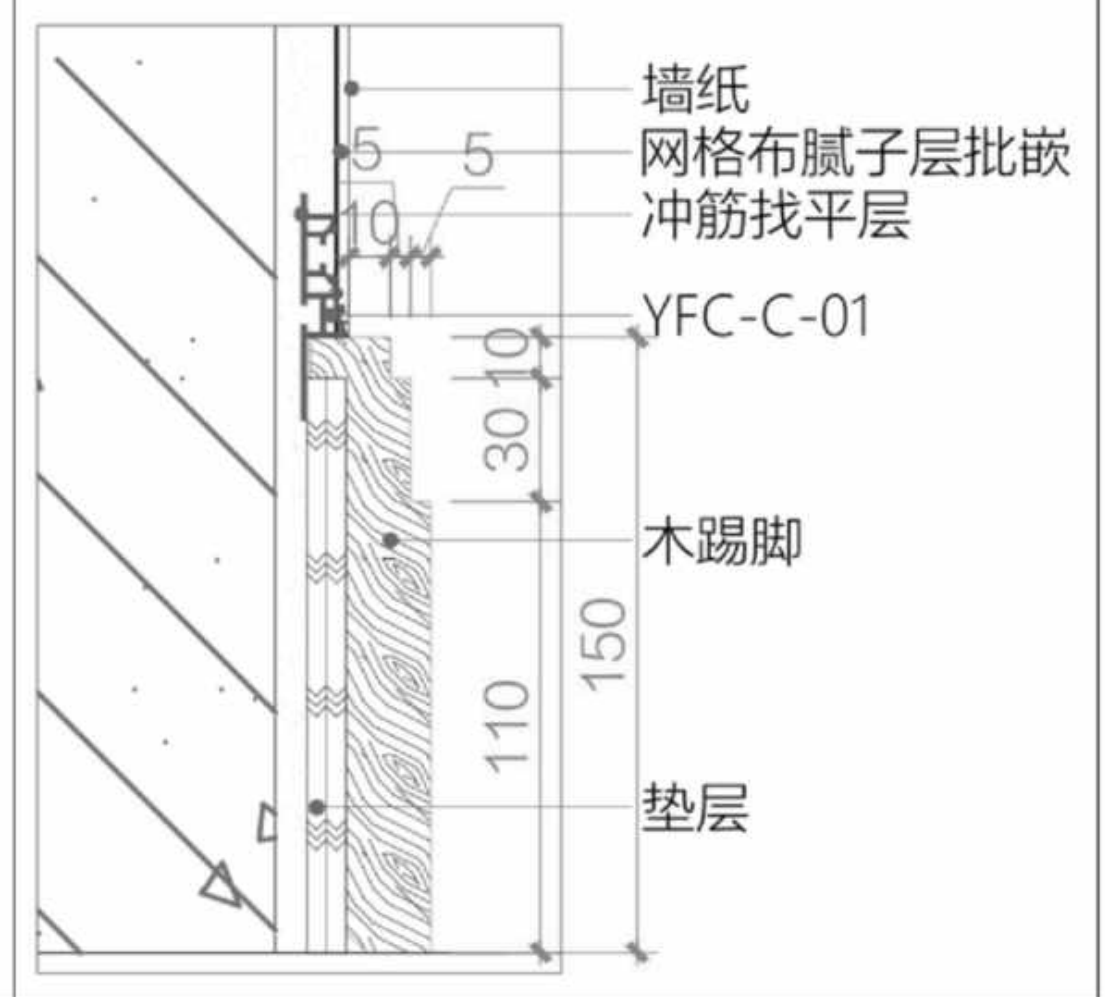
墙纸
网格布腻子层批嵌
冲筋找平层
5
5
10
YFC-C-01
10
30
木踢脚
150
110
垫层

图例E-SP1

踢脚-石膏基找平铝型材

Scale比例 1：1@A2

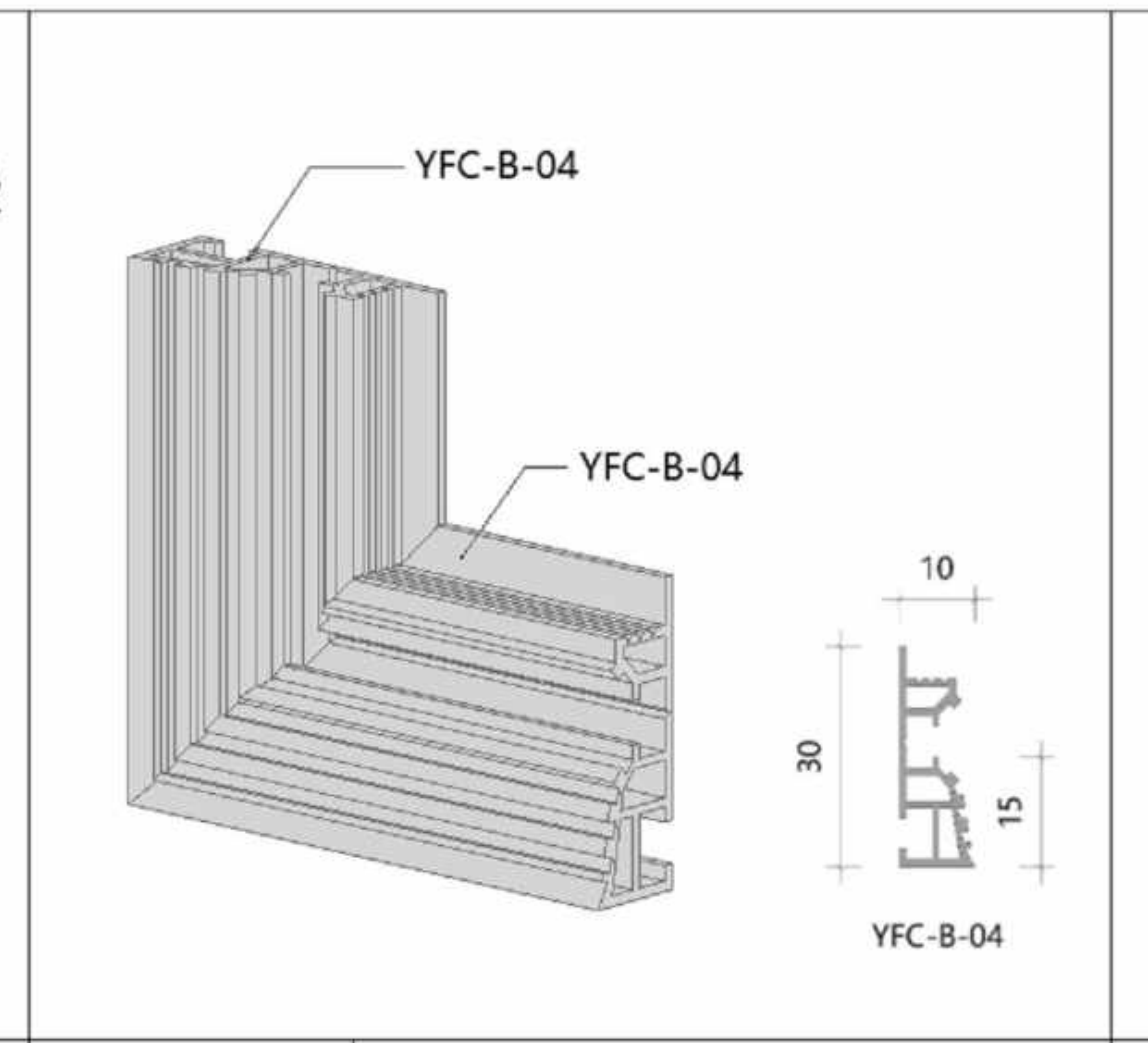
YFC-B-04
YFC-B-04
10
30
15
YFC-B-04

3D-01

转角铝型材-拼接跟通

转角数量：2

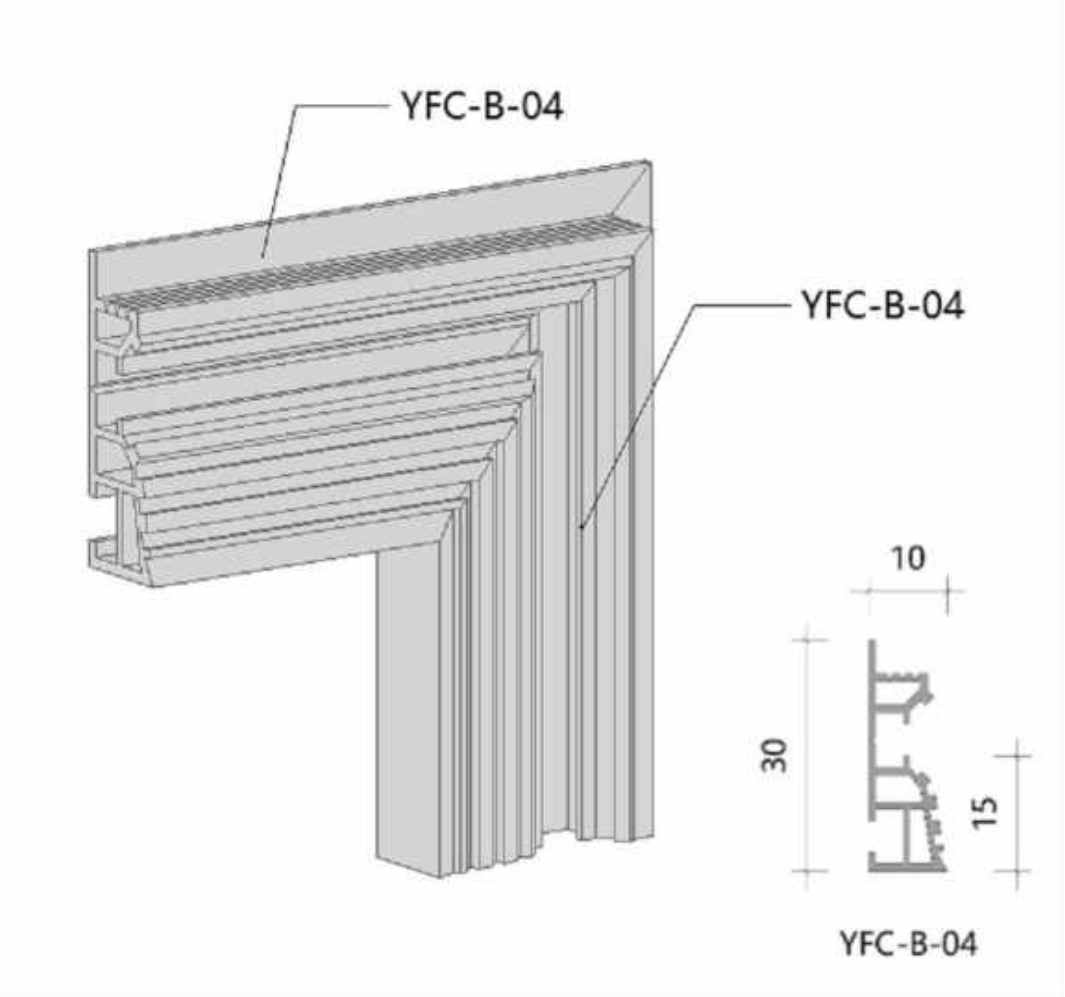
YFC-B-04
YFC-B-04
10
30
15
YFC-B-04

3D-02

转角铝型材-拼接跟通

转角数量：1

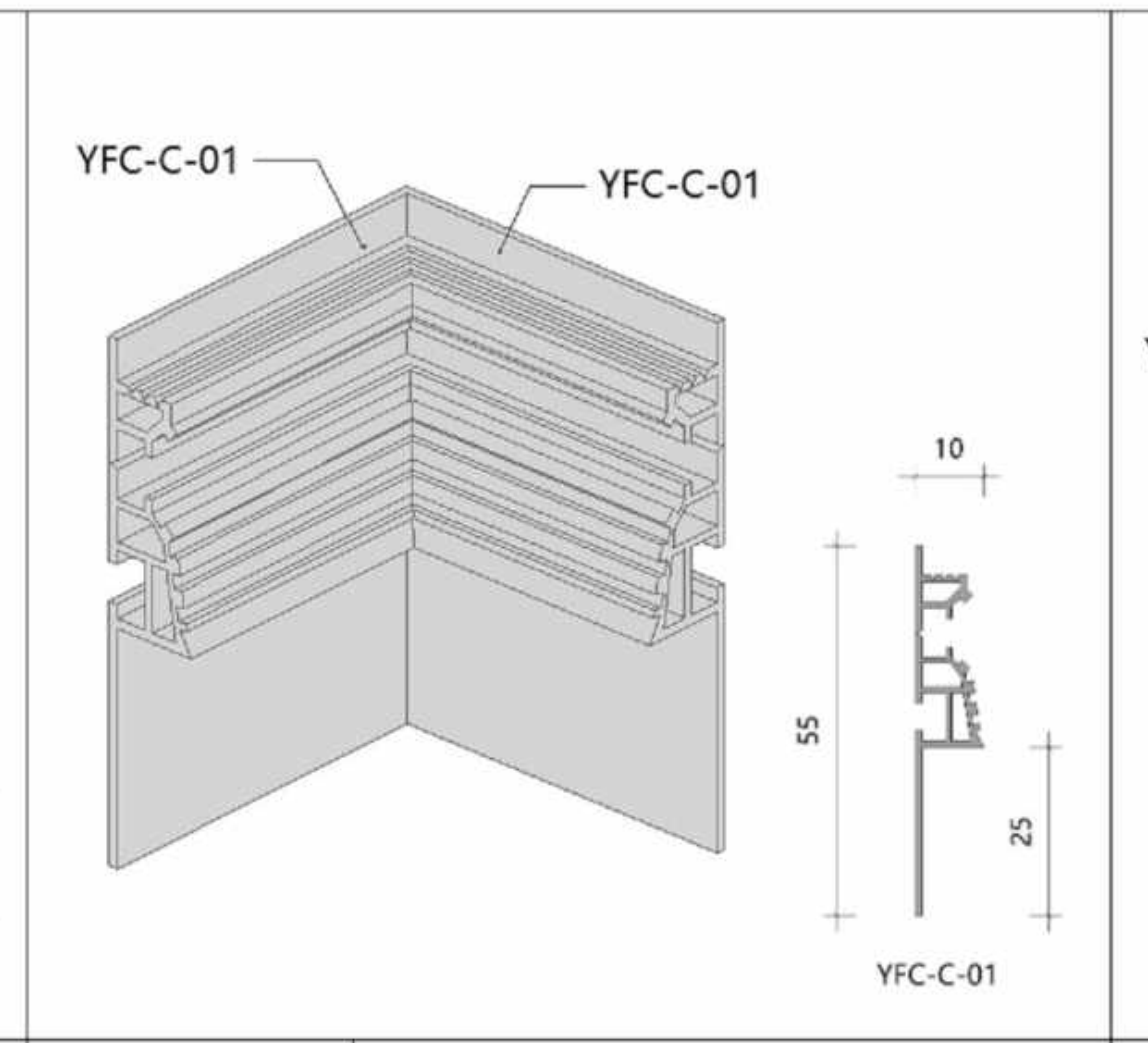
YFC-C-01
YFC-C-01
10
55
25
YFC-C-01

3D-05

转角铝型材-拼接跟通

转角数量：1

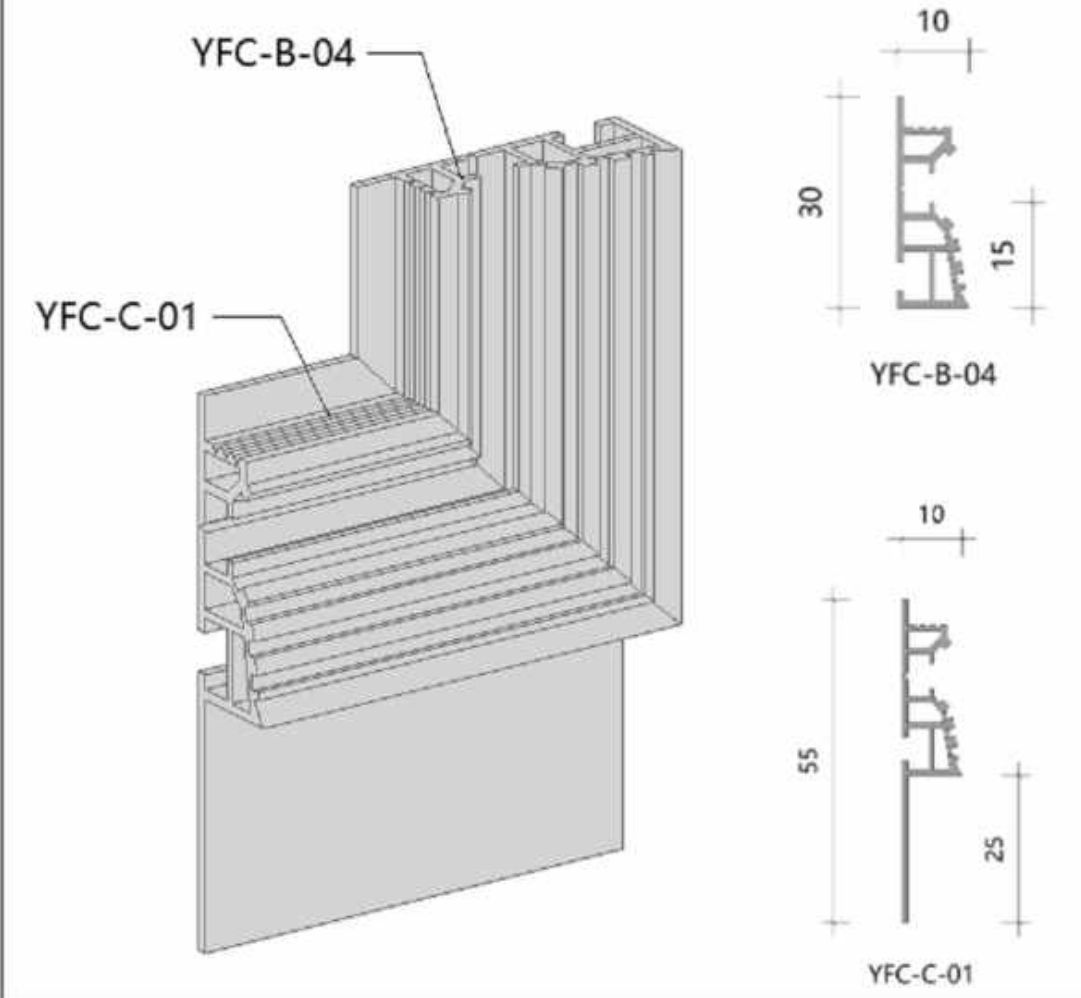
YFC-B-04
YFC-C-01
10
30
15
YFC-B-04
10
55
25
YFC-C-01

3D-06

转角铝型材-拼接跟通

转角数量：4

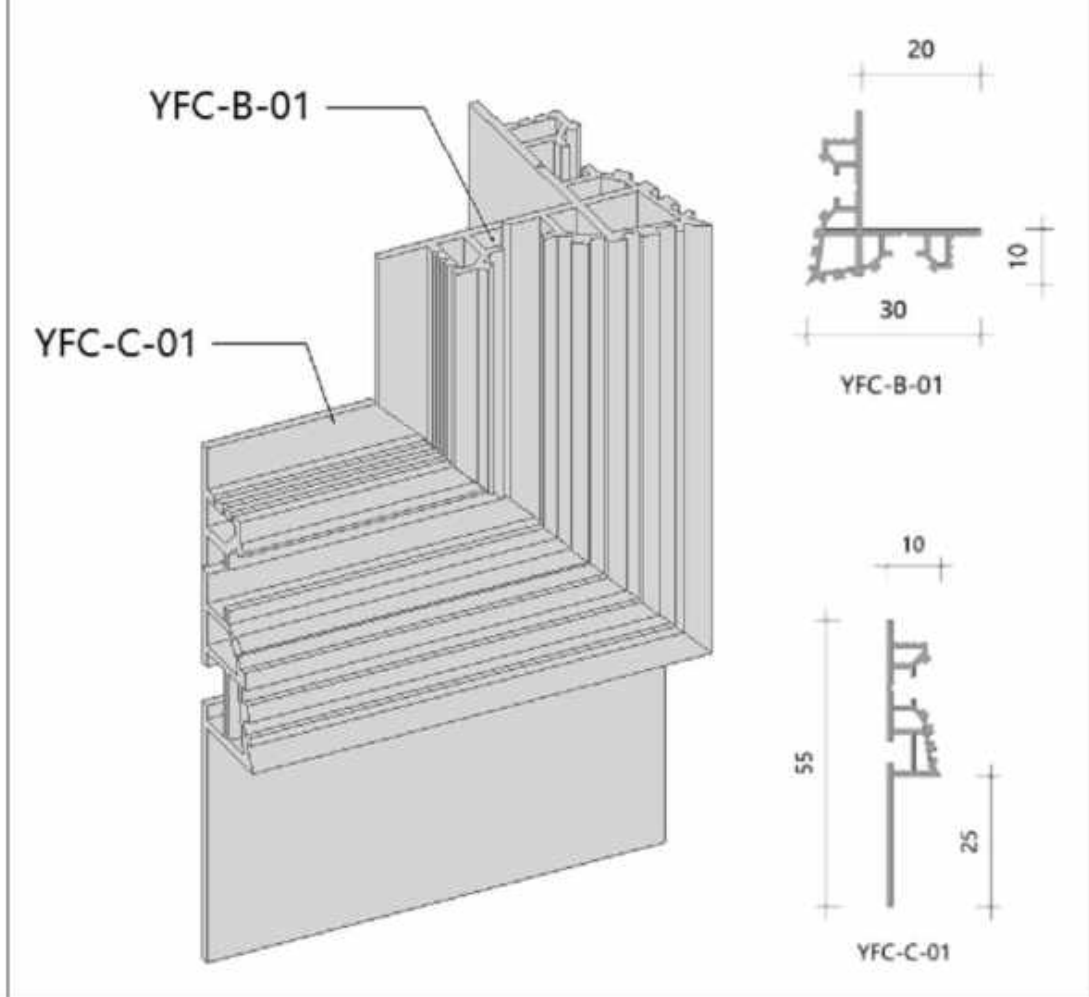
YFC-B-01
YFC-C-01
20
30
10
YFC-B-01
10
55
25
YFC-C-01

3D-07

转角铝型材-拼接跟通

转角数量：2

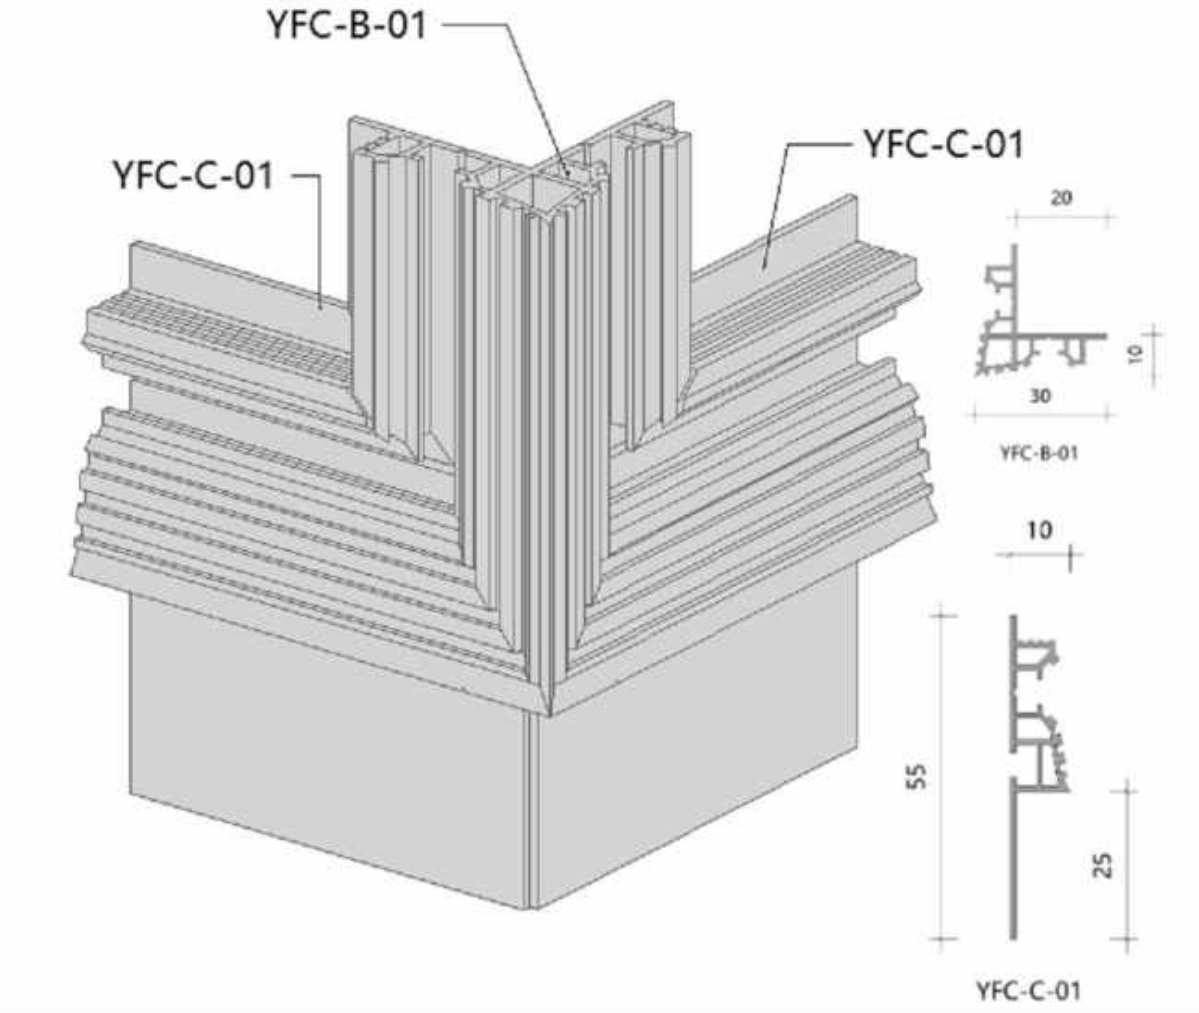
YFC-B-01
YFC-C-01
YFC-C-01
20
30
10
YFC-B-01
10
55
25
YFC-C-01

3D-11

转角铝型材-拼接跟通

转角数量：2

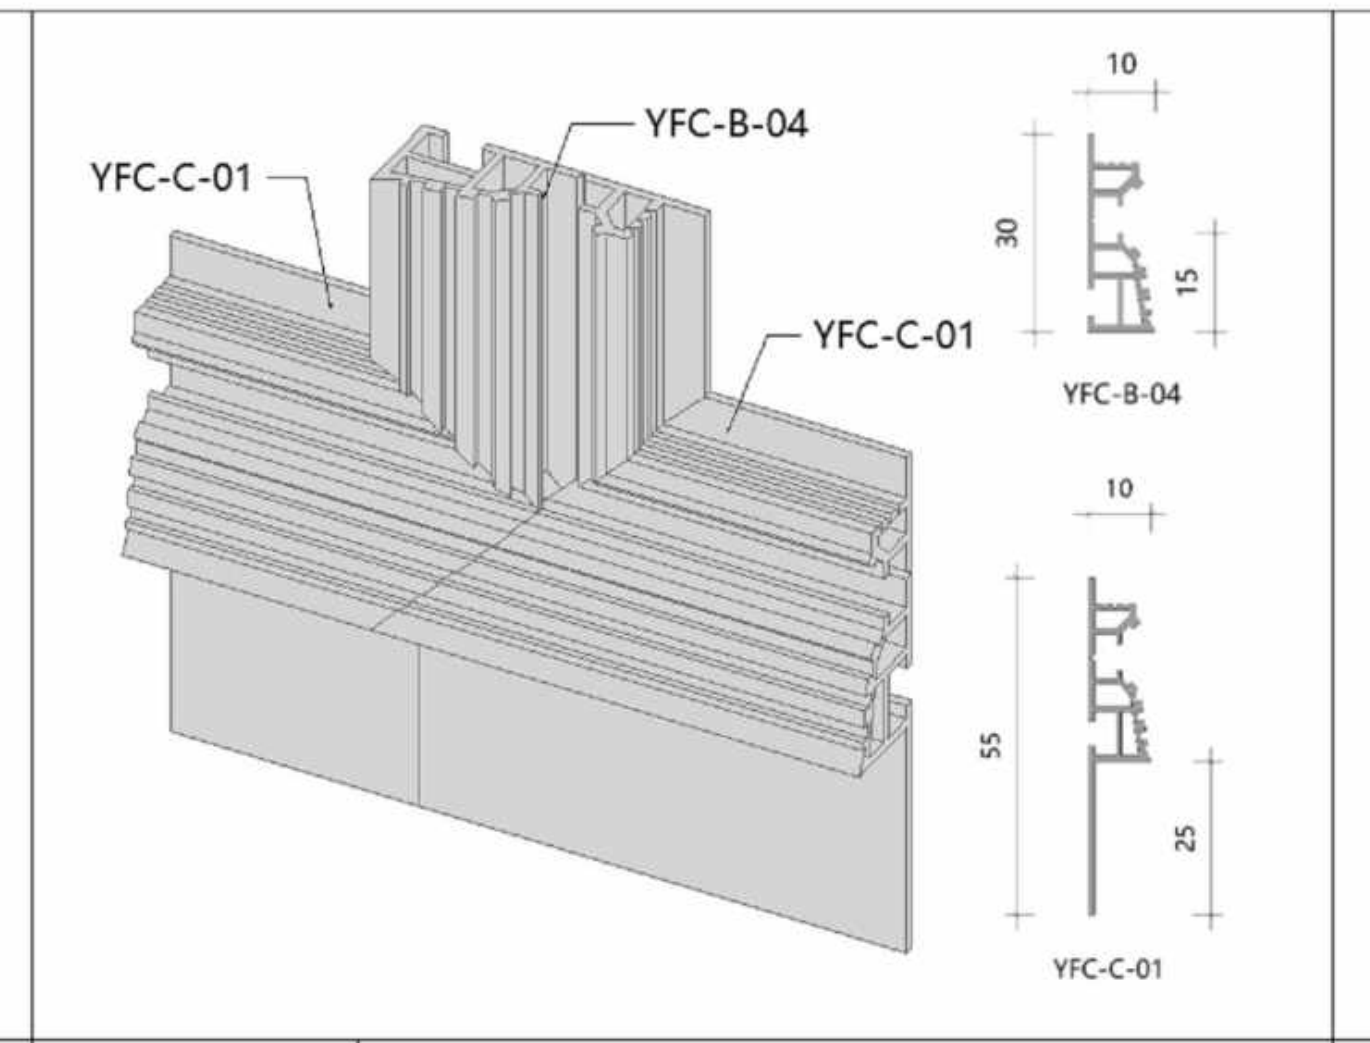
YFC-C-01
YFC-B-04
YFC-C-01
10
30
15
YFC-B-04
10
55
25
YFC-C-01

3D-13

转角铝型材-拼接跟通

转角数量：3

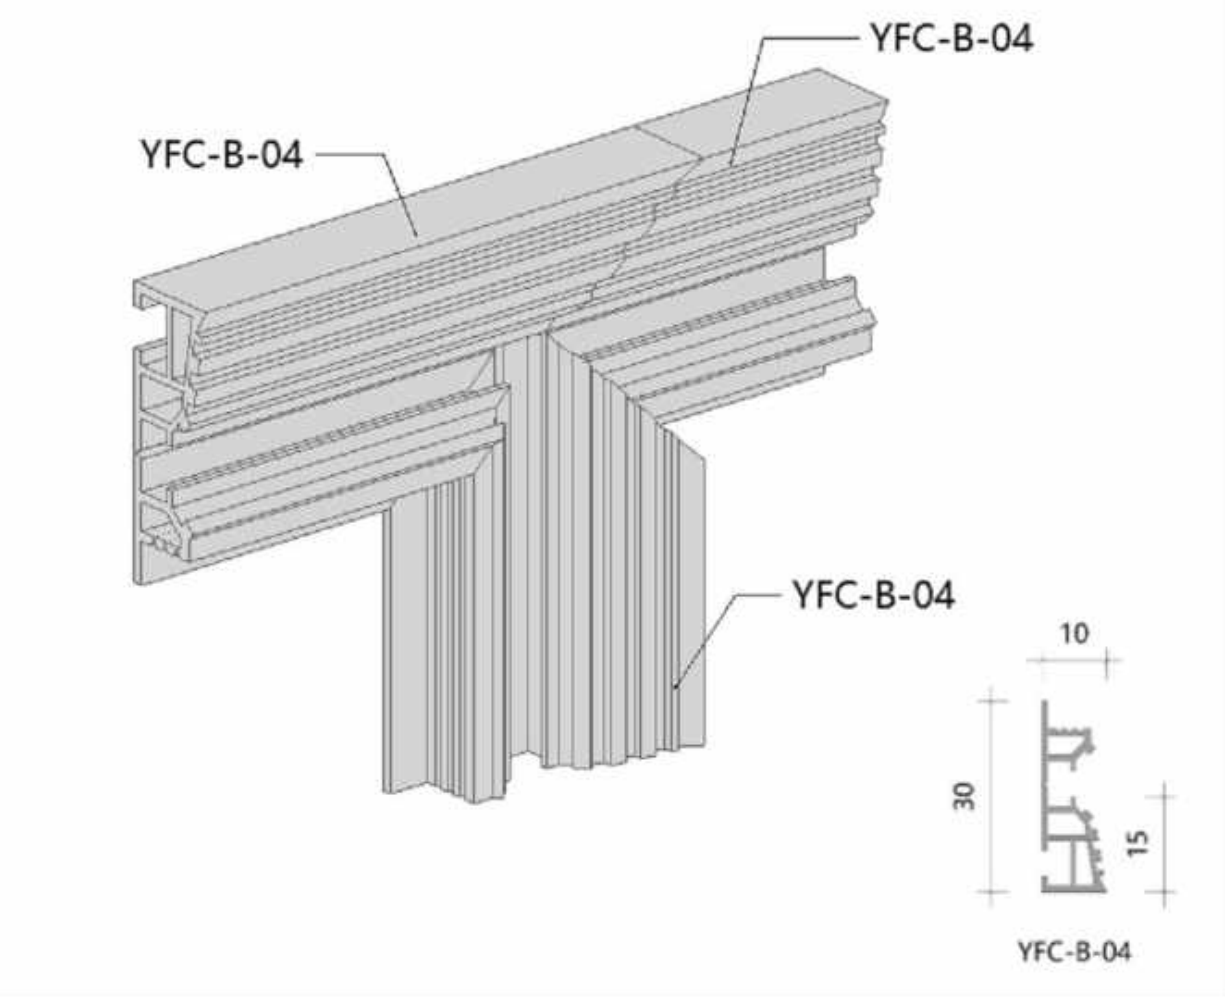
YFC-B-04
YFC-B-04
YFC-B-04
10
30
15
YFC-B-04

3D-14

转角铝型材-拼接跟通

转角数量：2

盖章

注释
Notes
1.本图纸如与现场尺寸有误，请施工人员与项目负责人联系。
2.施工前施工人员应认真查阅此图，如有不明确尺寸，按现场测量为准。
3.本图纸必须经甲乙双方认可并签字方可作为施工依据。

日期
Date 03/04/26

修订
Revision
△1

项目
Project
潮映华岸府3-801

比例
Scale 1：30@A2

客卧
墙面及踢脚铝型材

图纸编号
Drawing No.
AP.EL-09

项目编号
Project No.

©2025

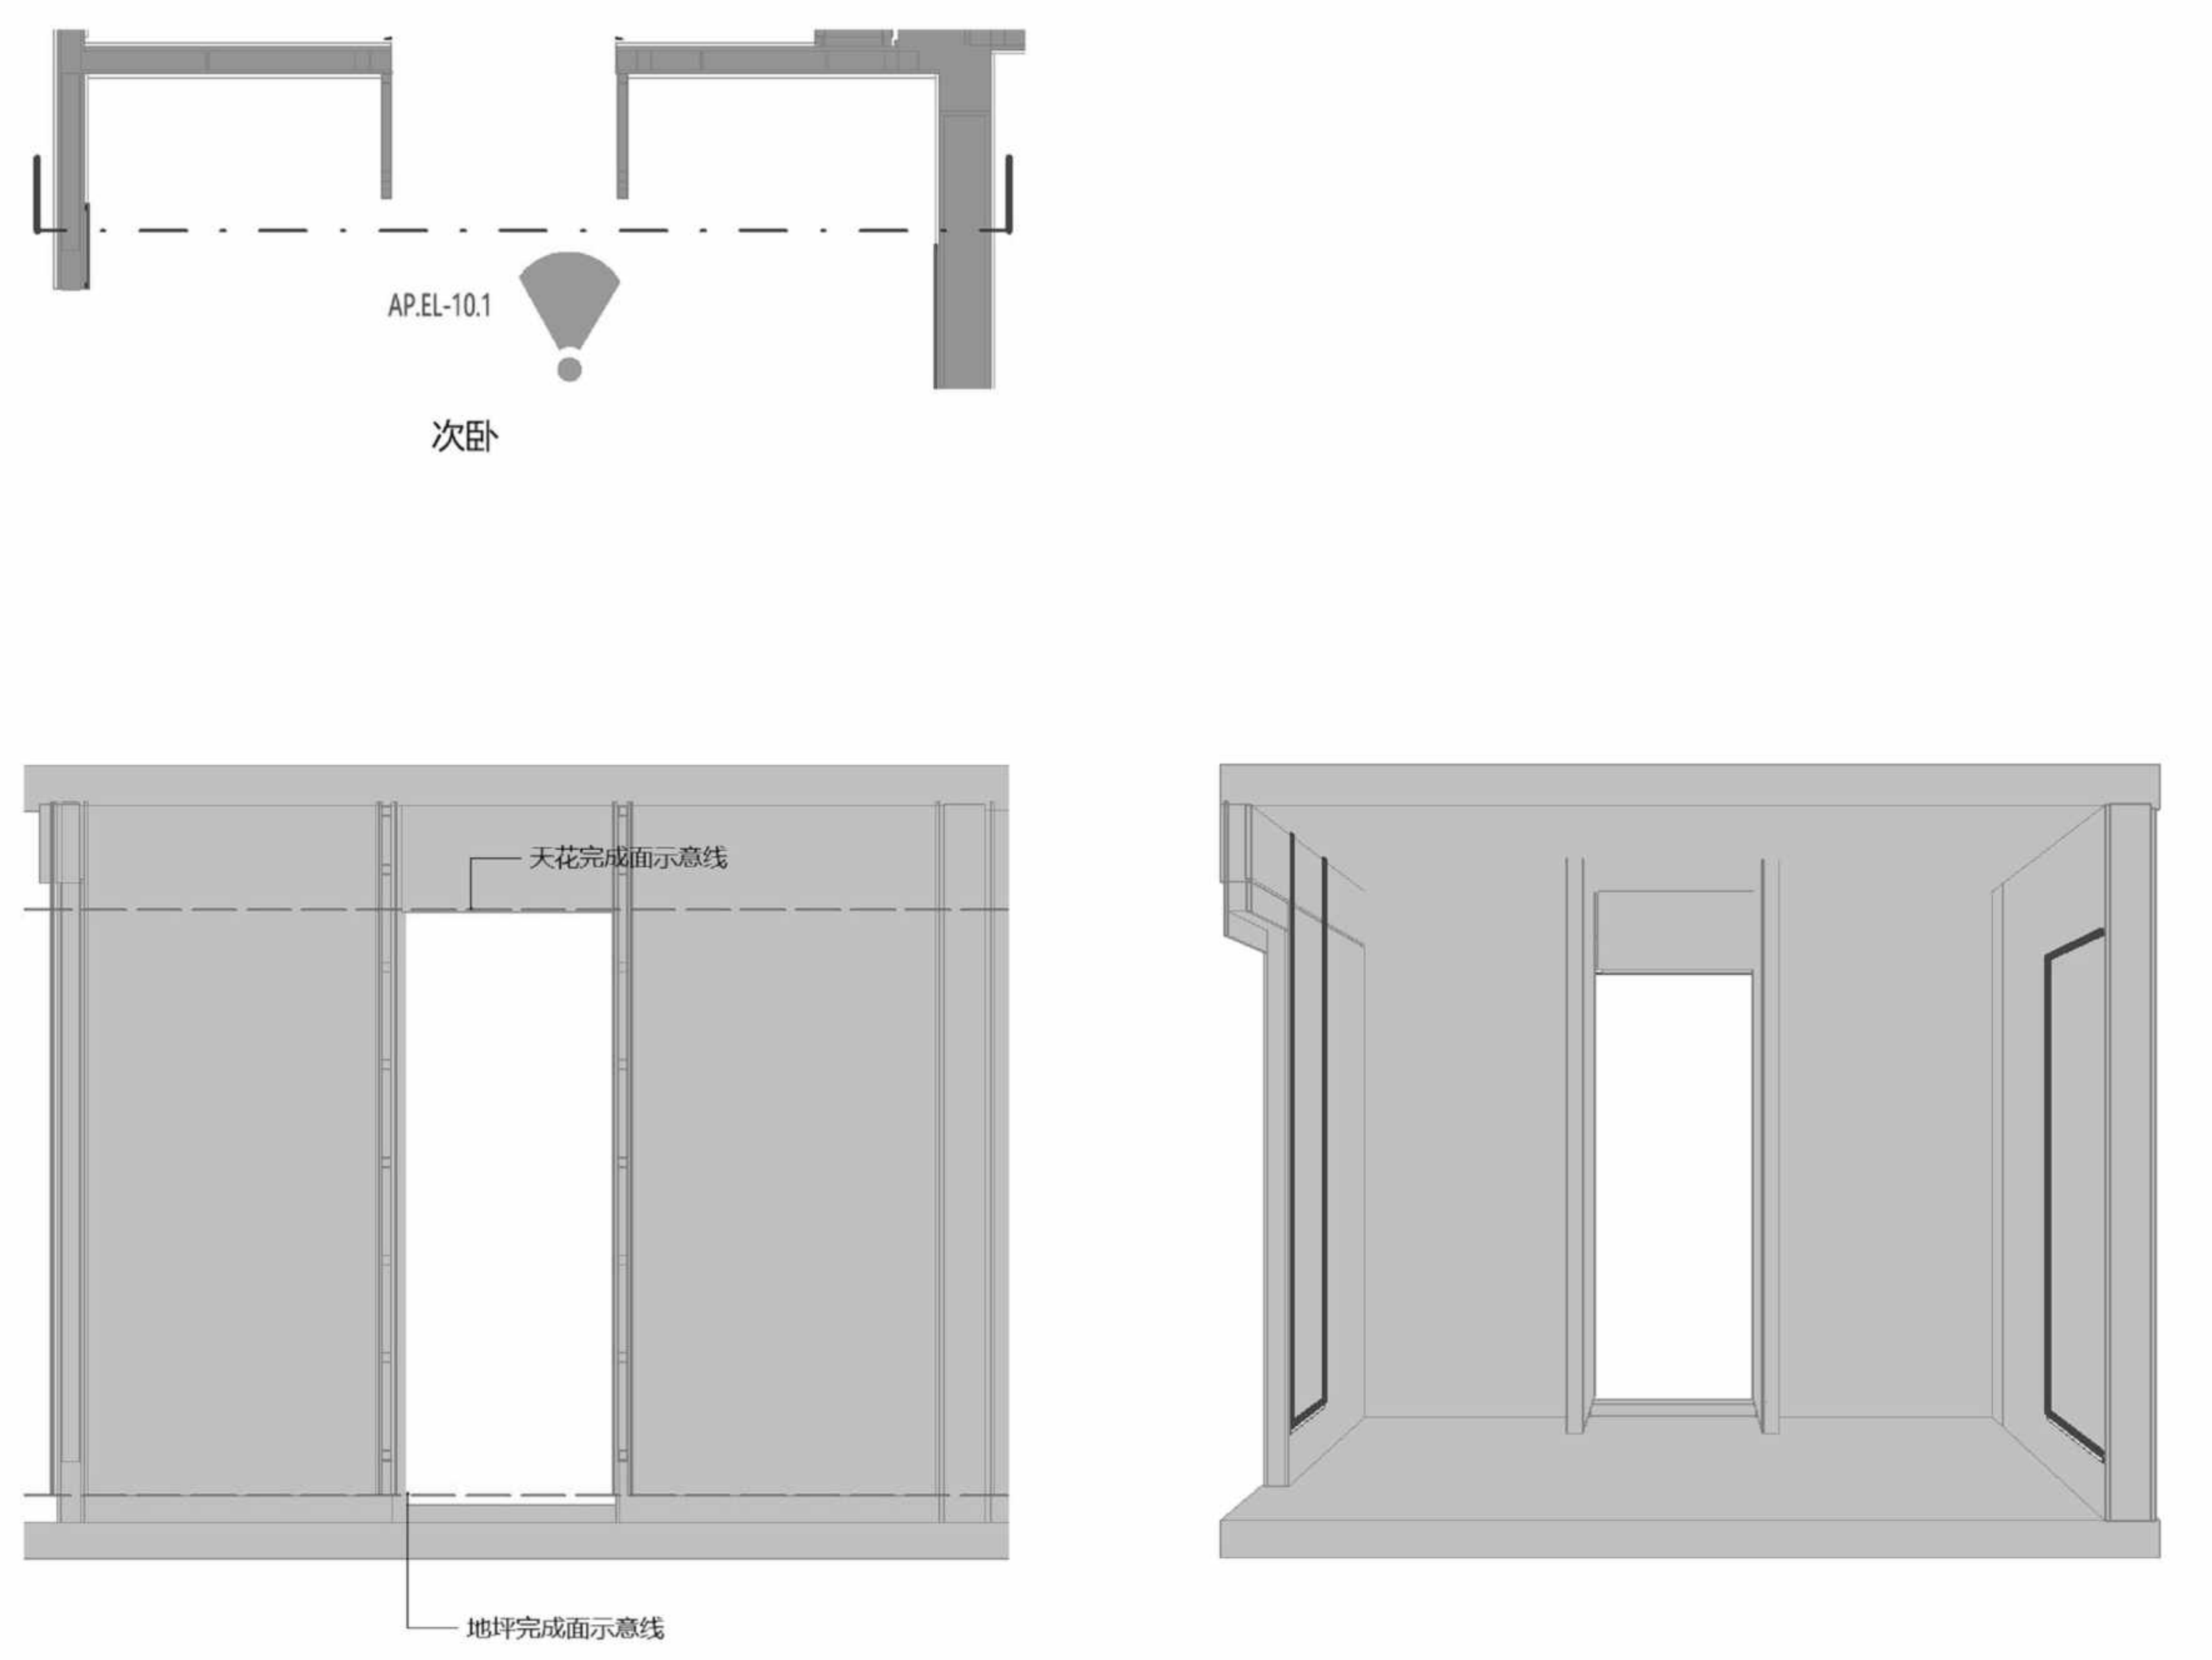
AP.EL-10.1
次卧
天花完成面示意线
地坪完成面示意线

1

次卧 墙面及踢脚铝型材立面图1

Scale比例 1：30@A2

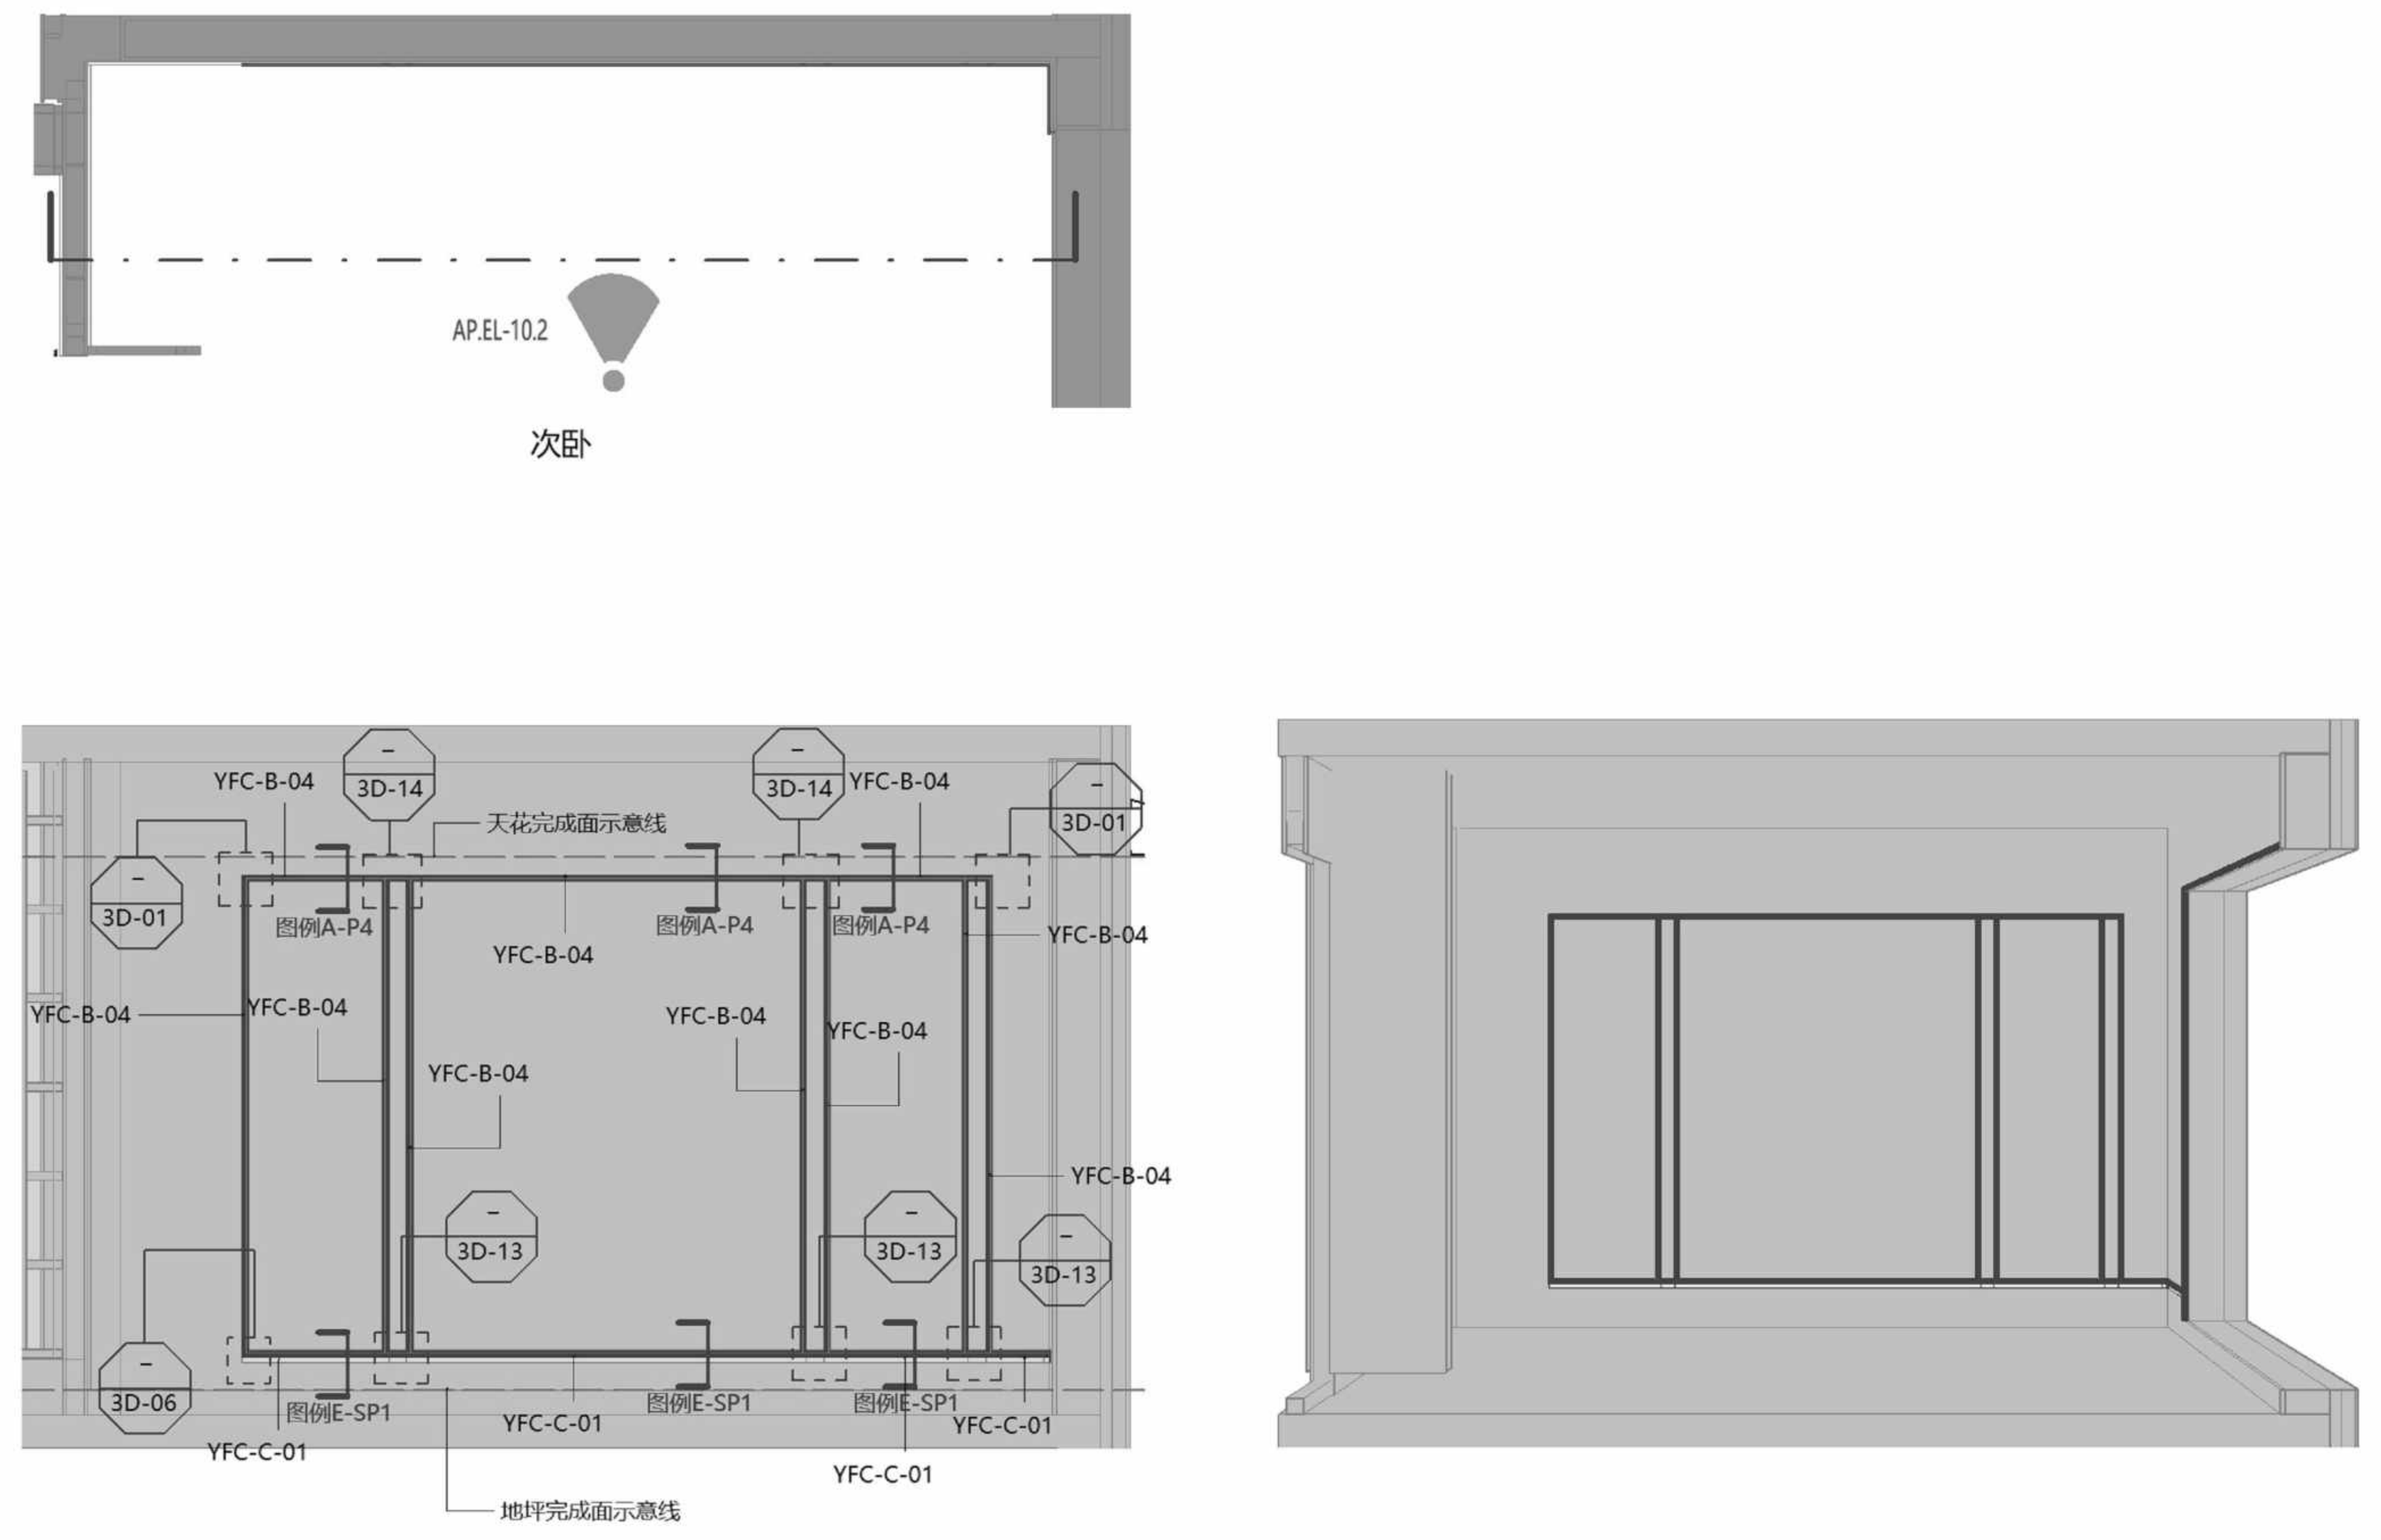
AP.EL-10.2
次卧
YFC-B-04
3D-14
天花完成面示意线
3D-14
YFC-B-04
3D-01
3D-01
图例A-P4
YFC-B-04
图例A-P4
图例A-P4
YFC-B-04
YFC-B-04
YFC-B-04
YFC-B-04
YFC-B-04
YFC-B-04
YFC-B-04
3D-13
3D-13
3D-13
3D-06
图例E-SP1
YFC-C-01
图例E-SP1
图例E-SP1
YFC-C-01
YFC-C-01
YFC-C-01
地坪完成面示意线

2

次卧 墙面及踢脚铝型材立面图2

Scale比例 1：30@A2

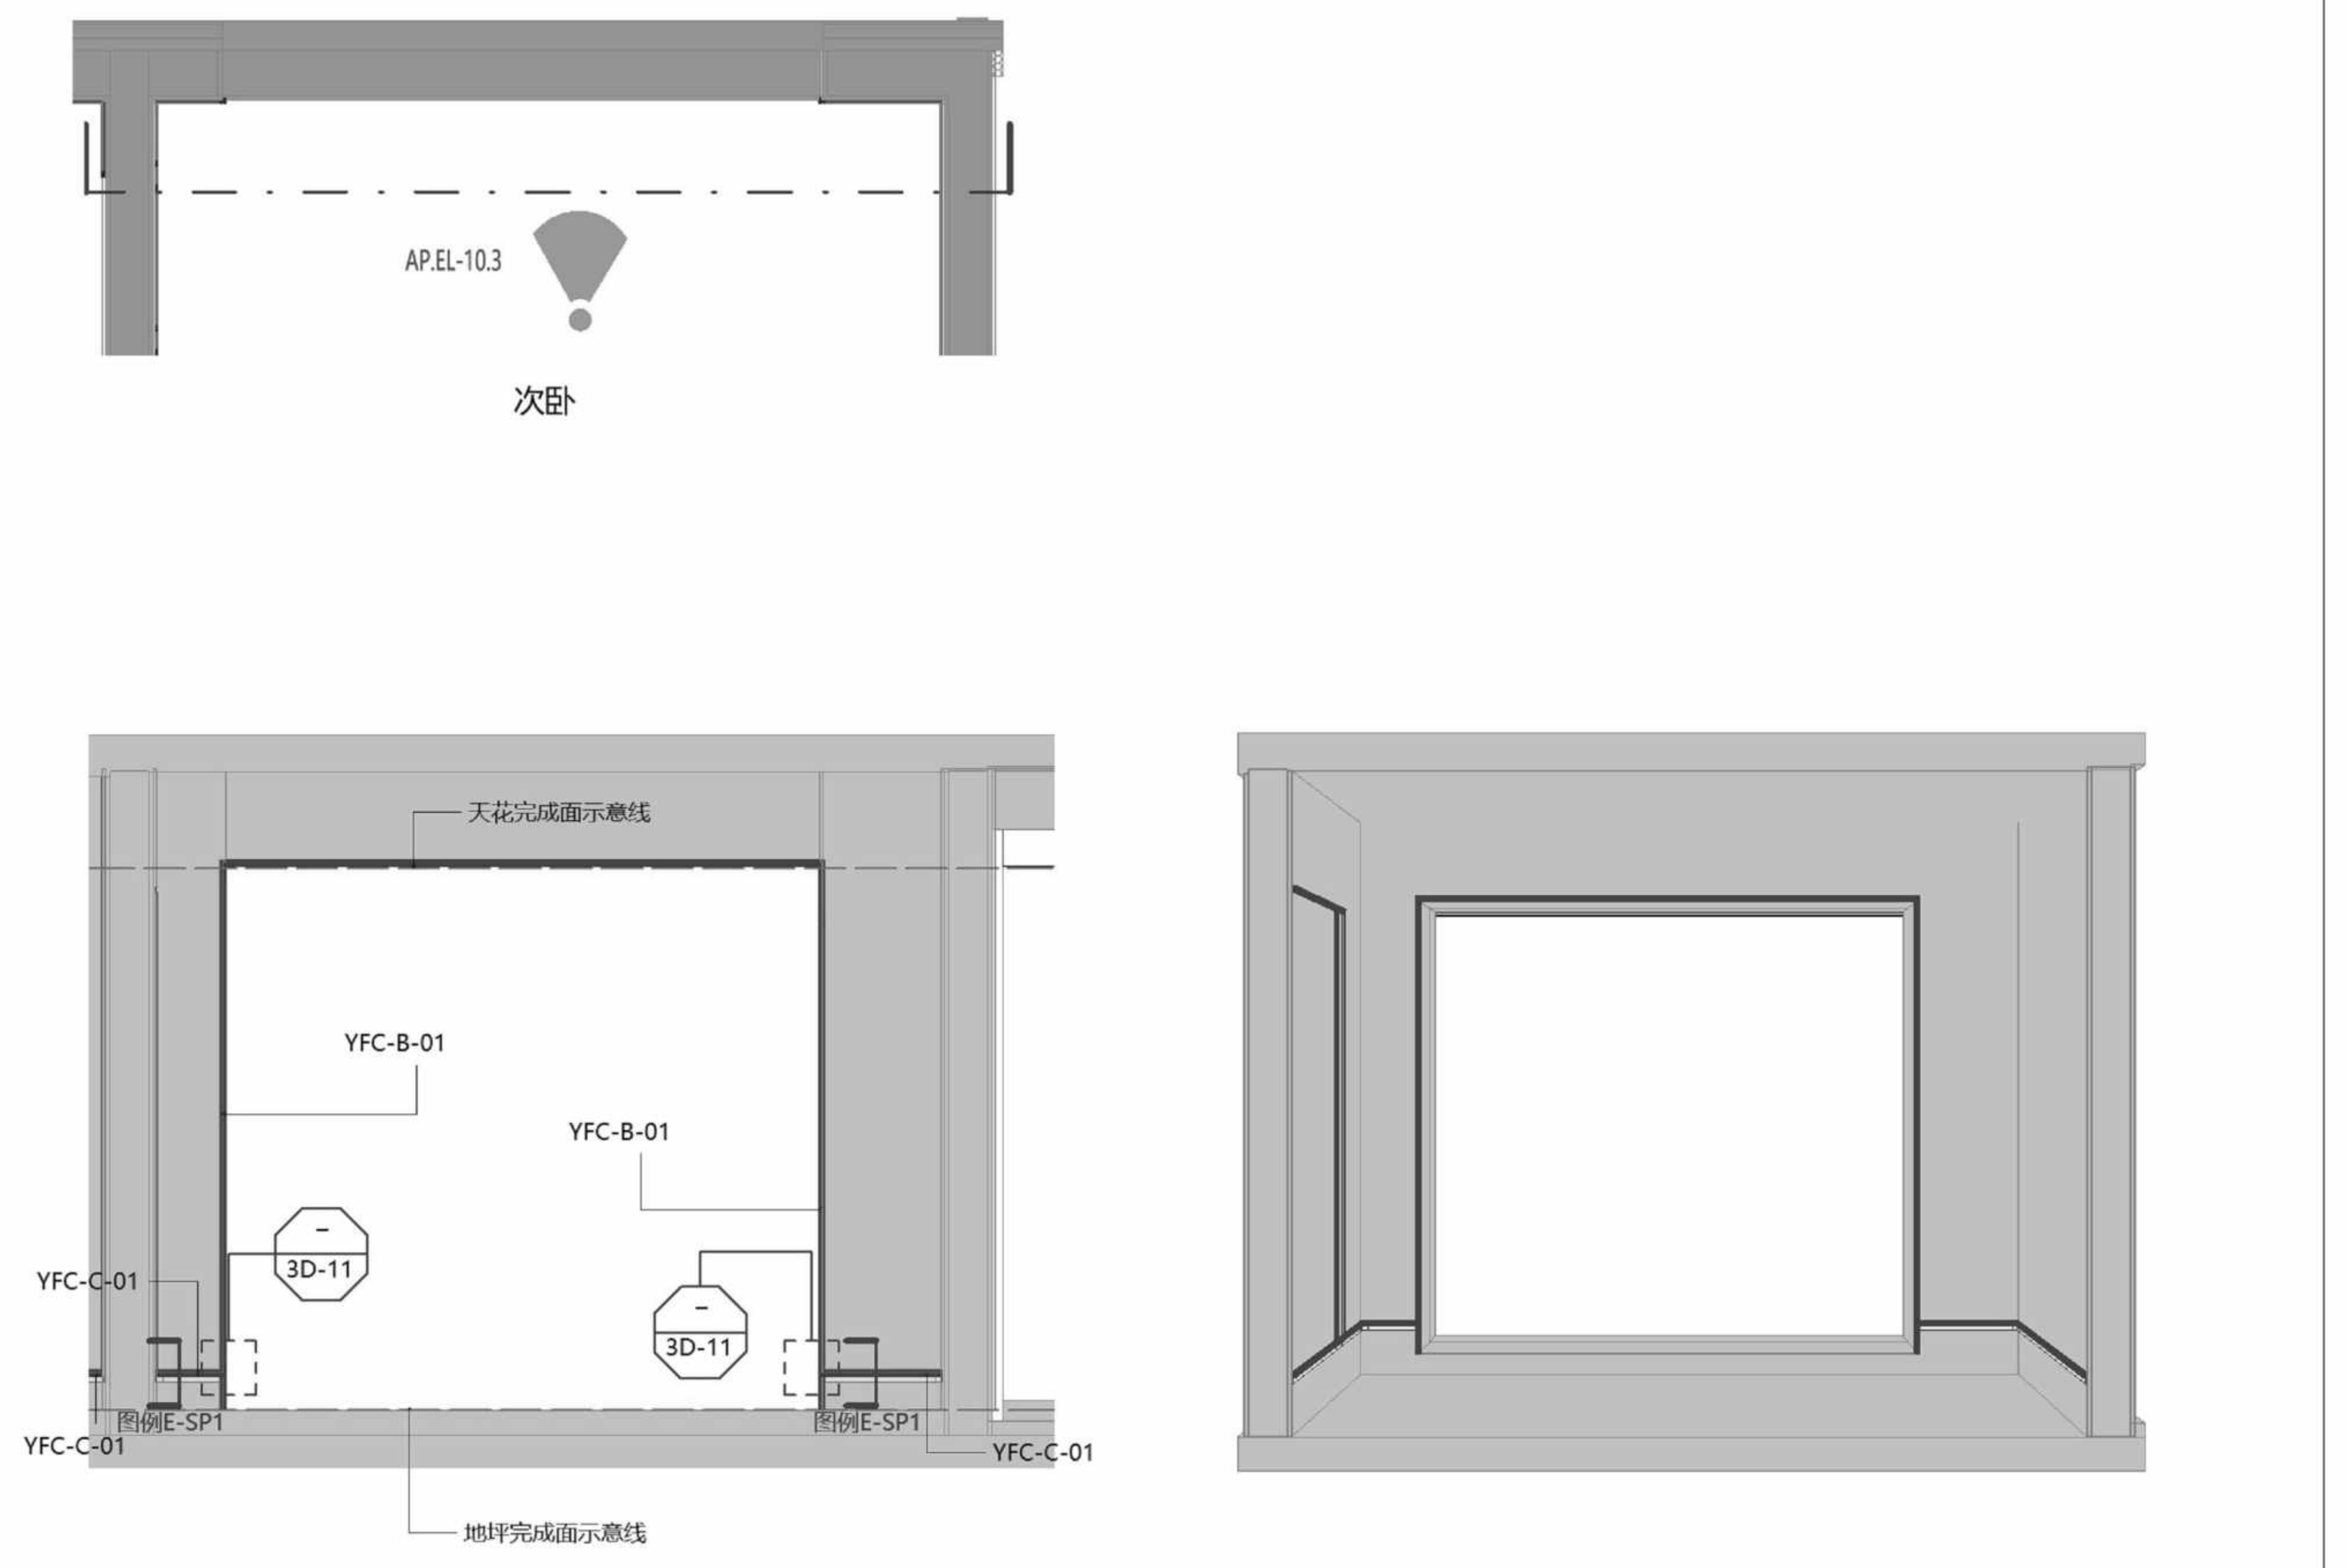
AP.EL-10.3
次卧
天花完成面示意线
YFC-B-01
YFC-B-01
YFC-C-01
3D-11
3D-11
图例E-SP1
图例E-SP1
YFC-C-01
YFC-C-01
地坪完成面示意线

3

次卧 墙面及踢脚铝型材立面图3

Scale比例 1：30@A2

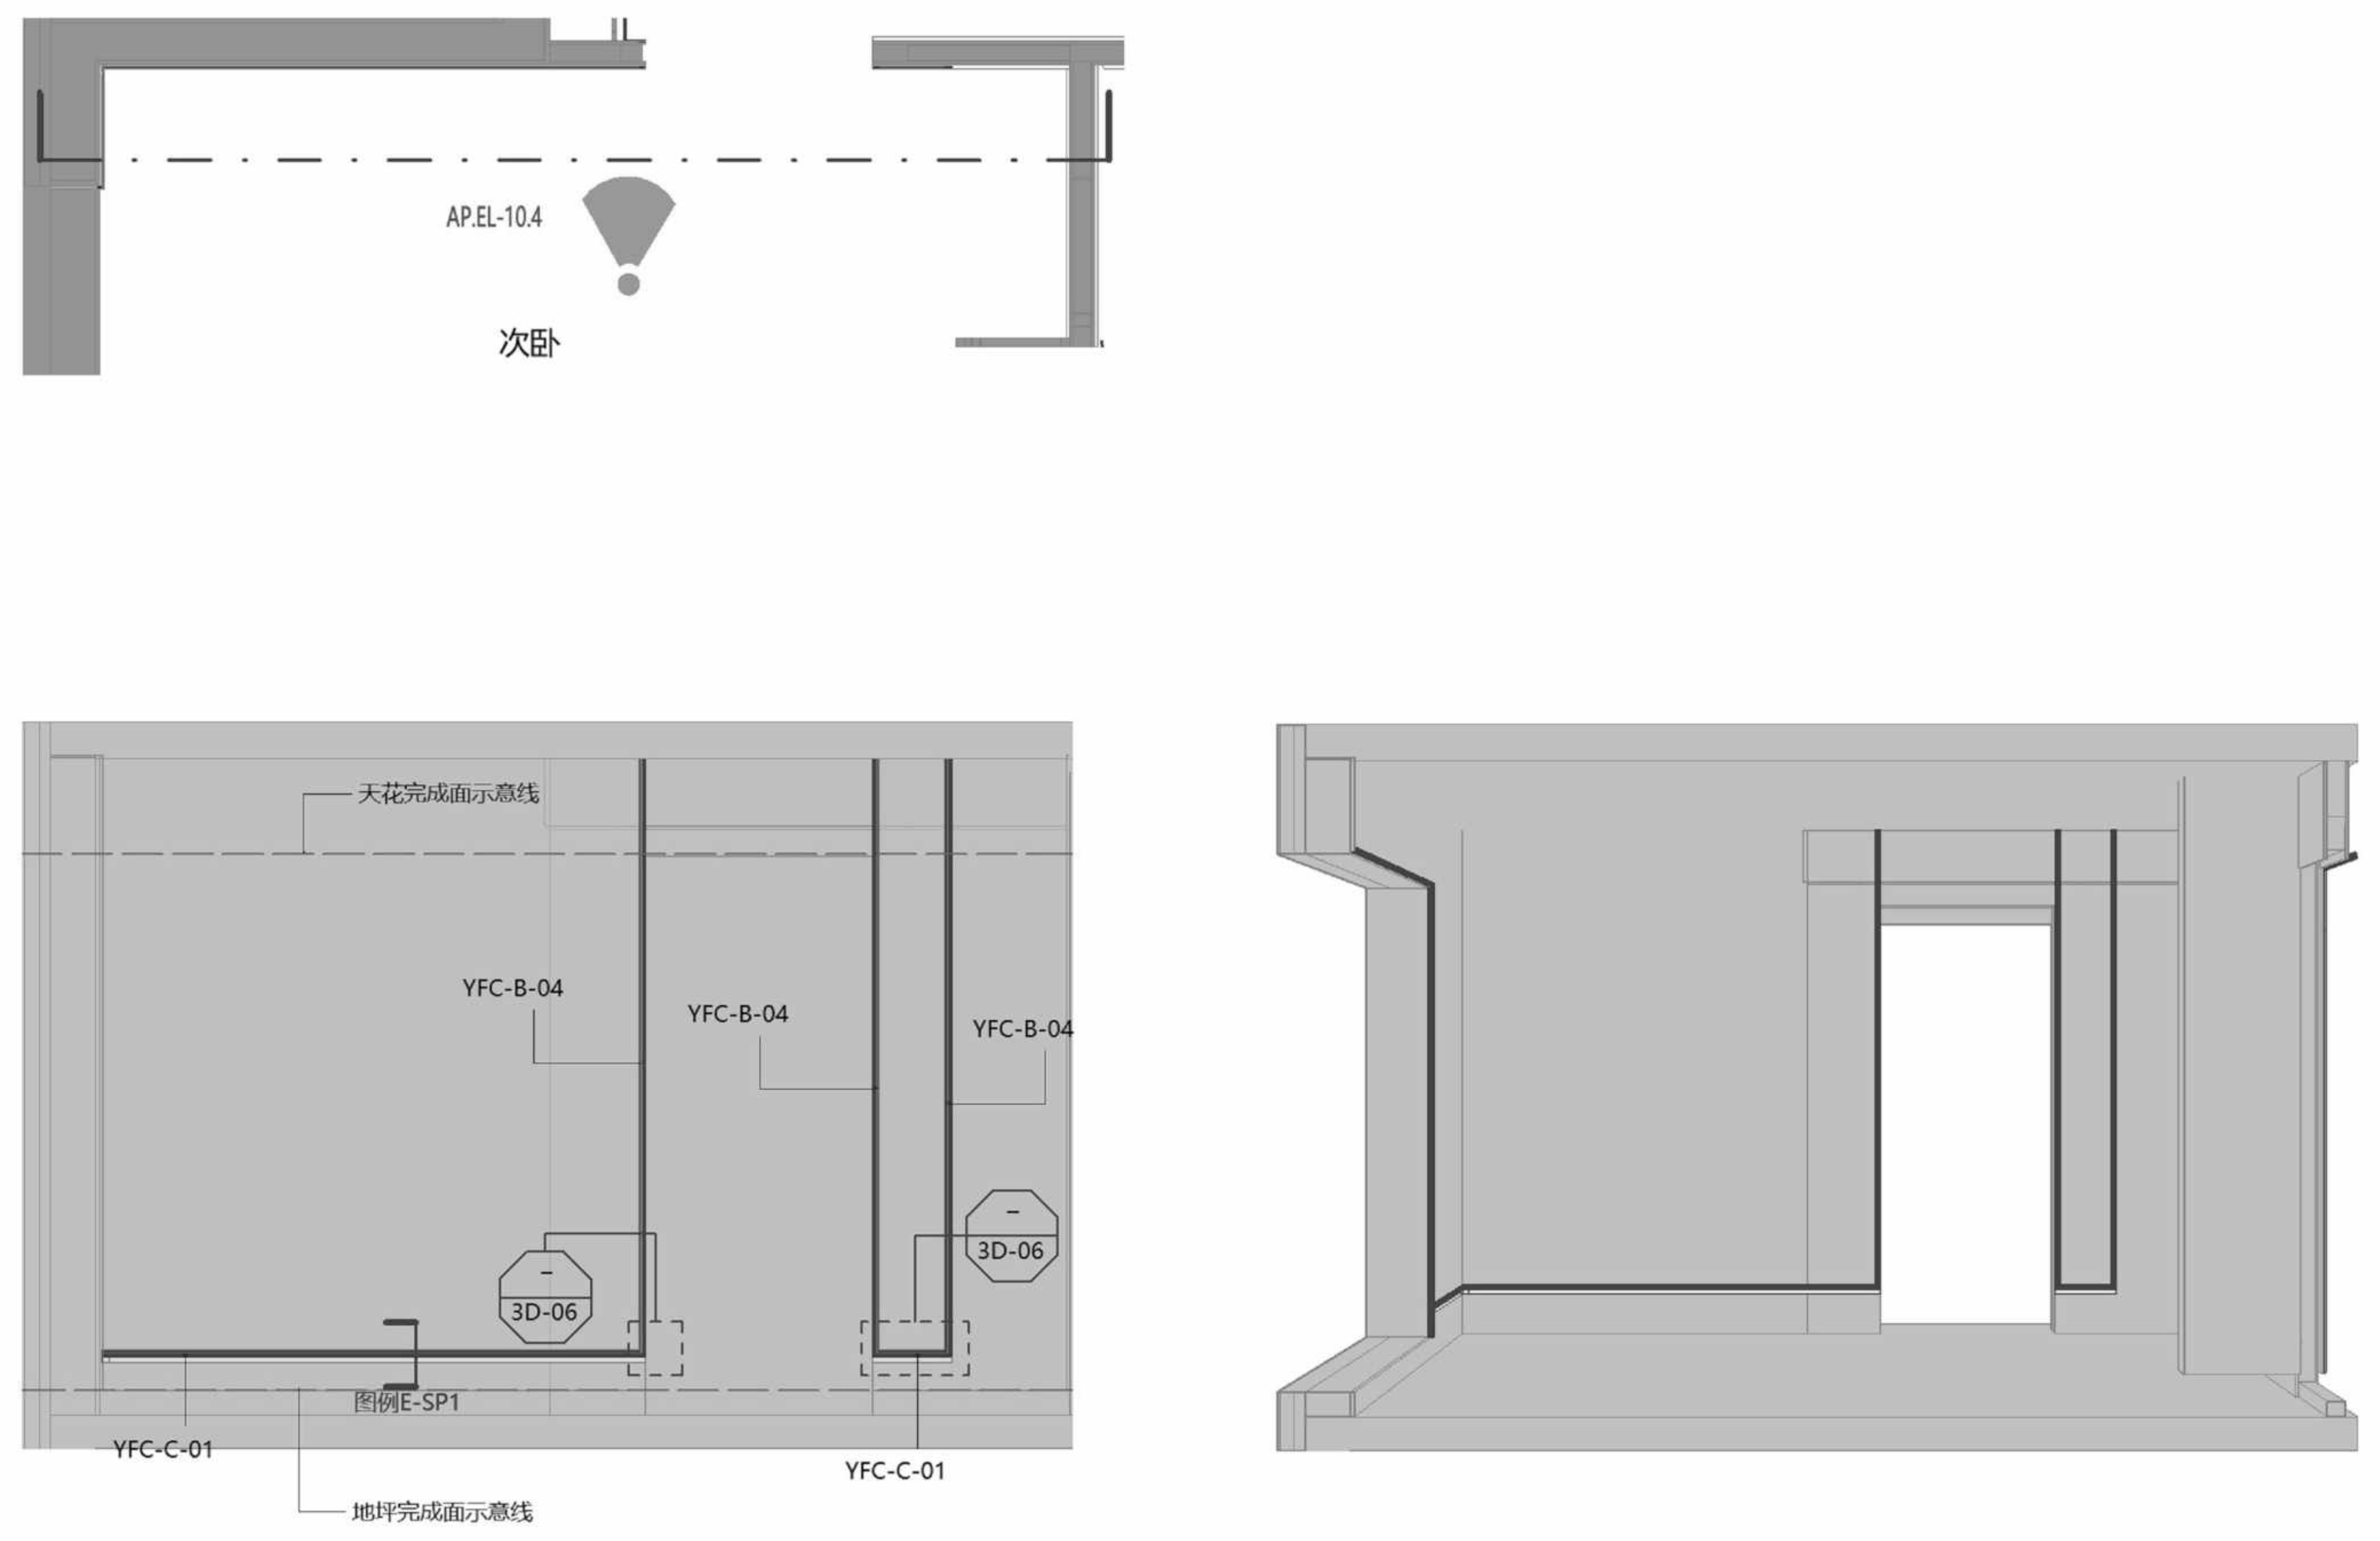
AP.EL-10.4
次卧
天花完成面示意线
YFC-B-04
YFC-B-04
YFC-B-04
3D-06
3D-06
图例E-SP1
YFC-C-01
YFC-C-01
地坪完成面示意线

4

次卧 墙面及踢脚铝型材立面图4

Scale比例 1：30@A2

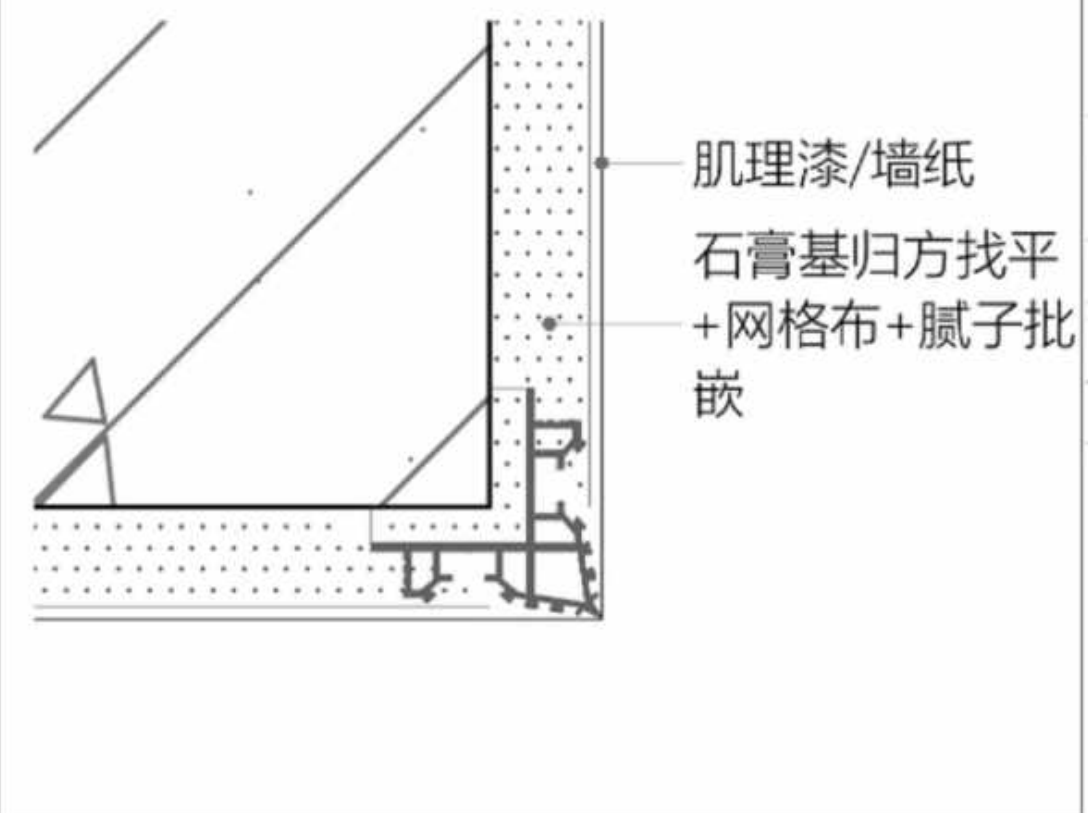
肌理漆/墙纸
石膏基归方找平
+网格布+腻子批嵌

图例A-P1 墙面-石膏基找平铝型材

Scale比例 1：1@A2

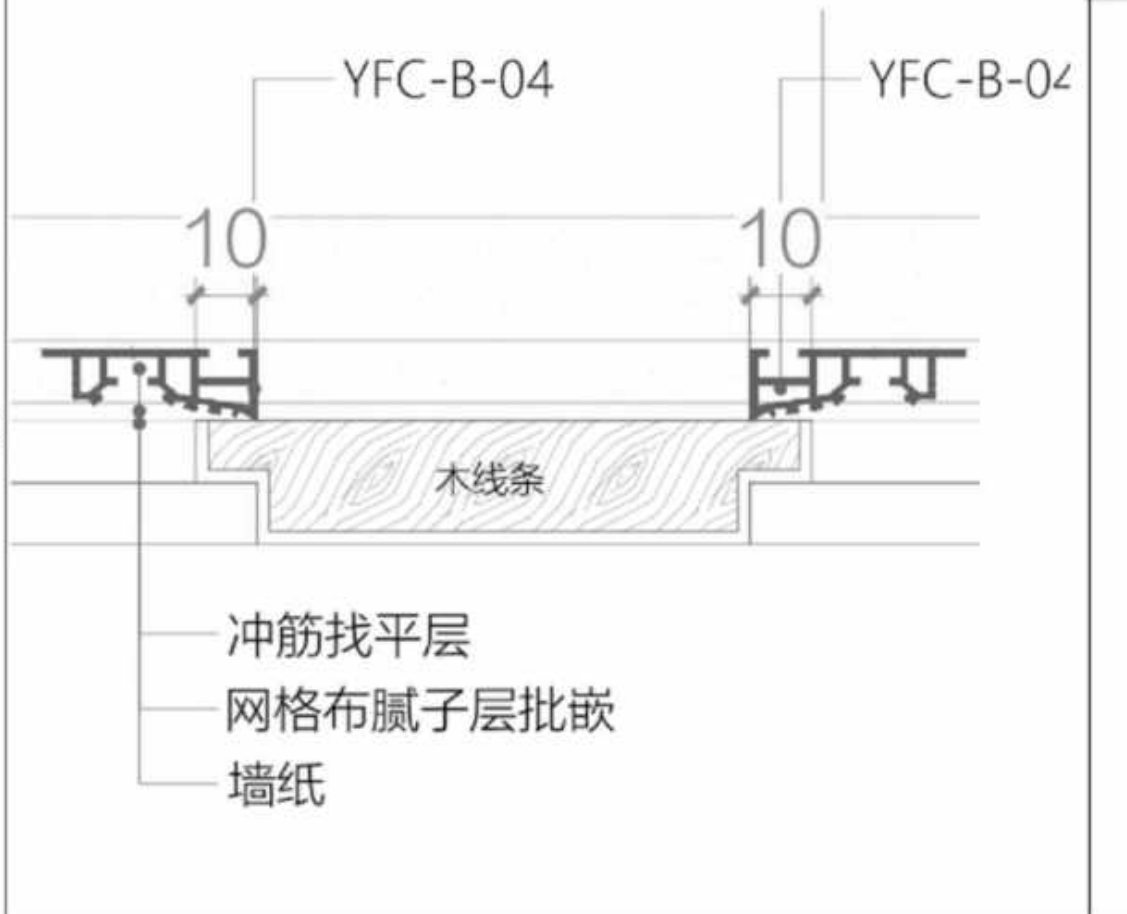
YFC-B-04
YFC-B-04
10
10
木线条
冲筋找平层
网格布腻子层批嵌
墙纸

图例A-P4 墙面-石膏基找平铝型材

Scale比例 1：1@A2

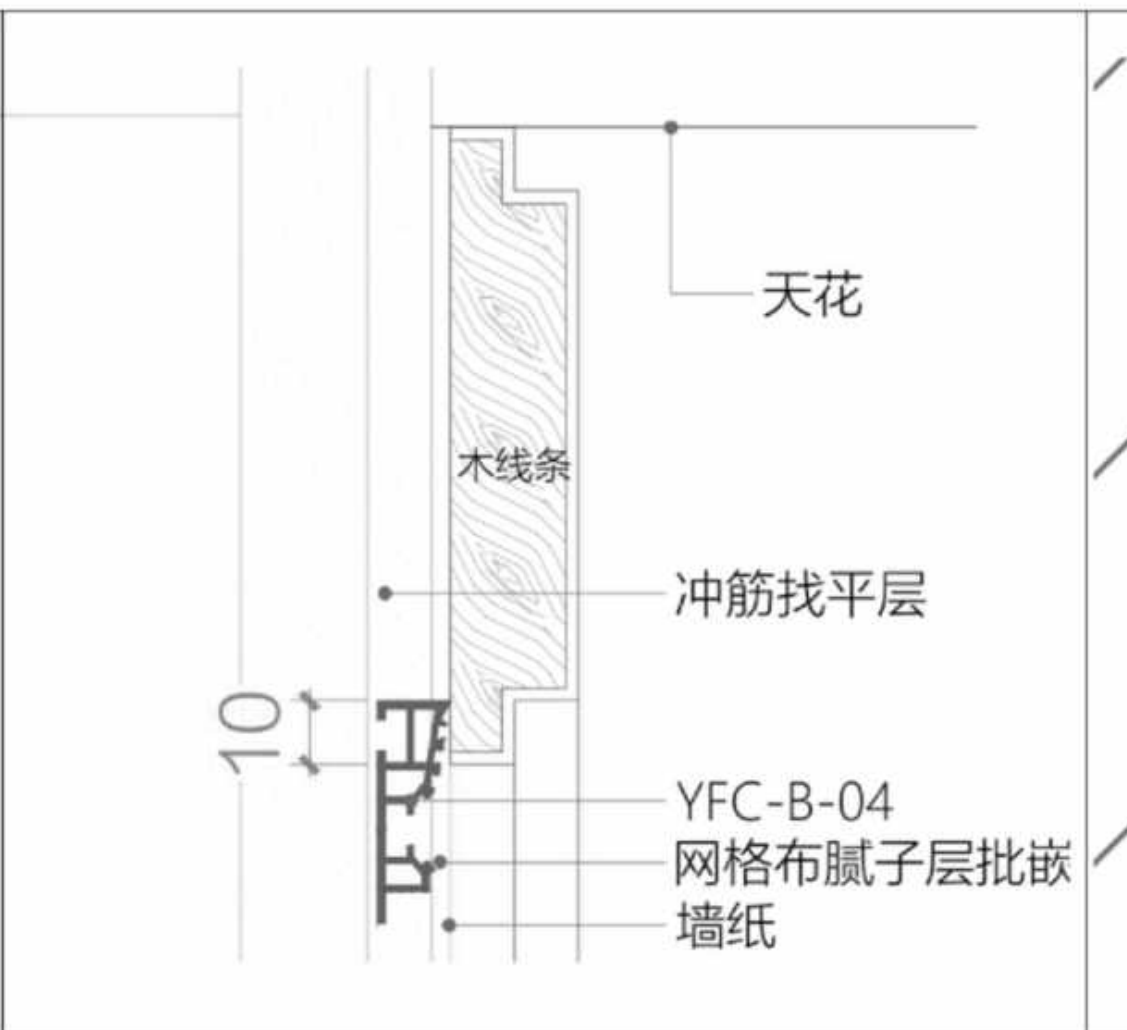
天花
木线条
冲筋找平层
10
YFC-B-04
网格布腻子层批嵌
墙纸

图例A-P5 墙面-石膏基找平铝型材

Scale比例 1：1@A2

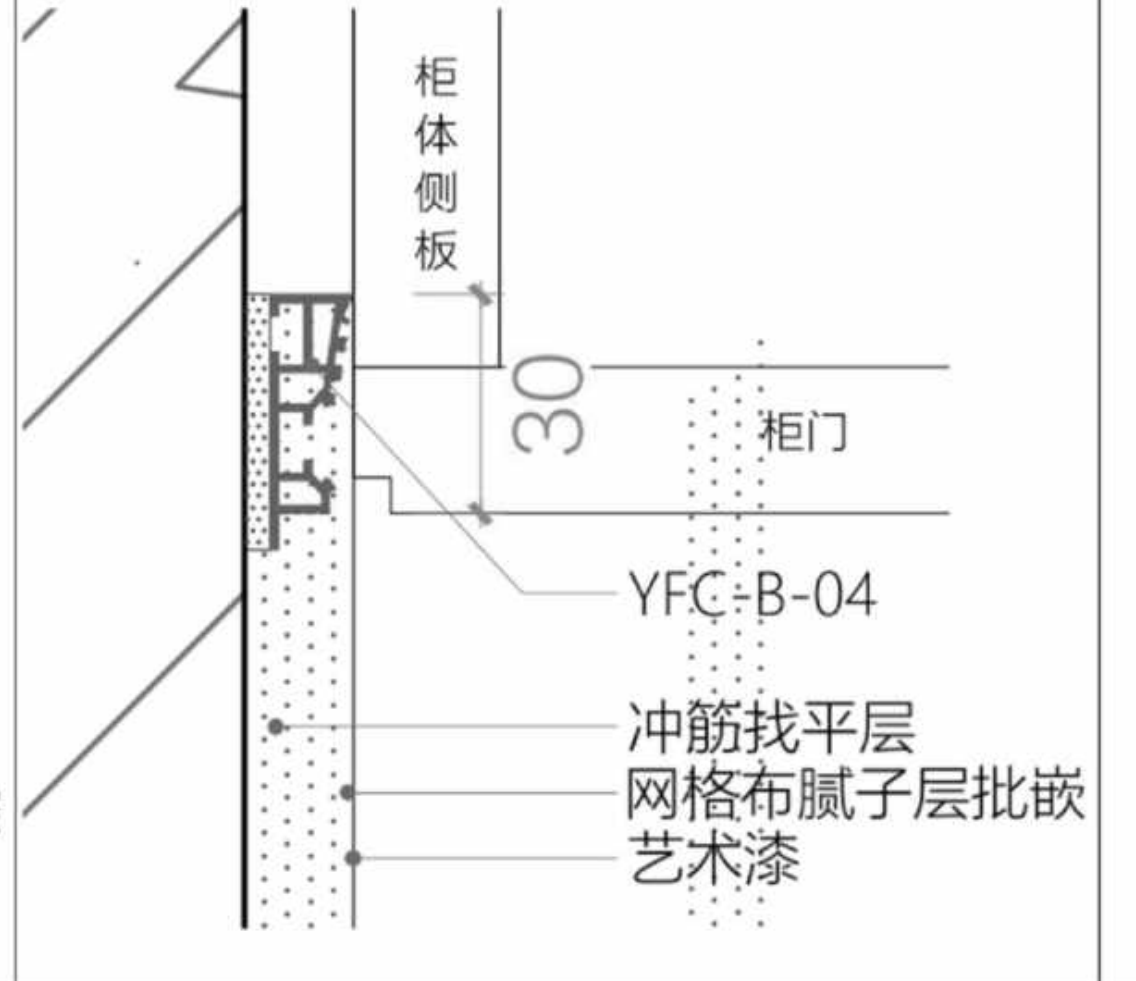
柜体侧板
30
柜门
YFC-B-04
冲筋找平层
网格布腻子层批嵌
艺术漆

图例B-P6 柜边-石膏基找平铝型材

Scale比例 1：1@A2

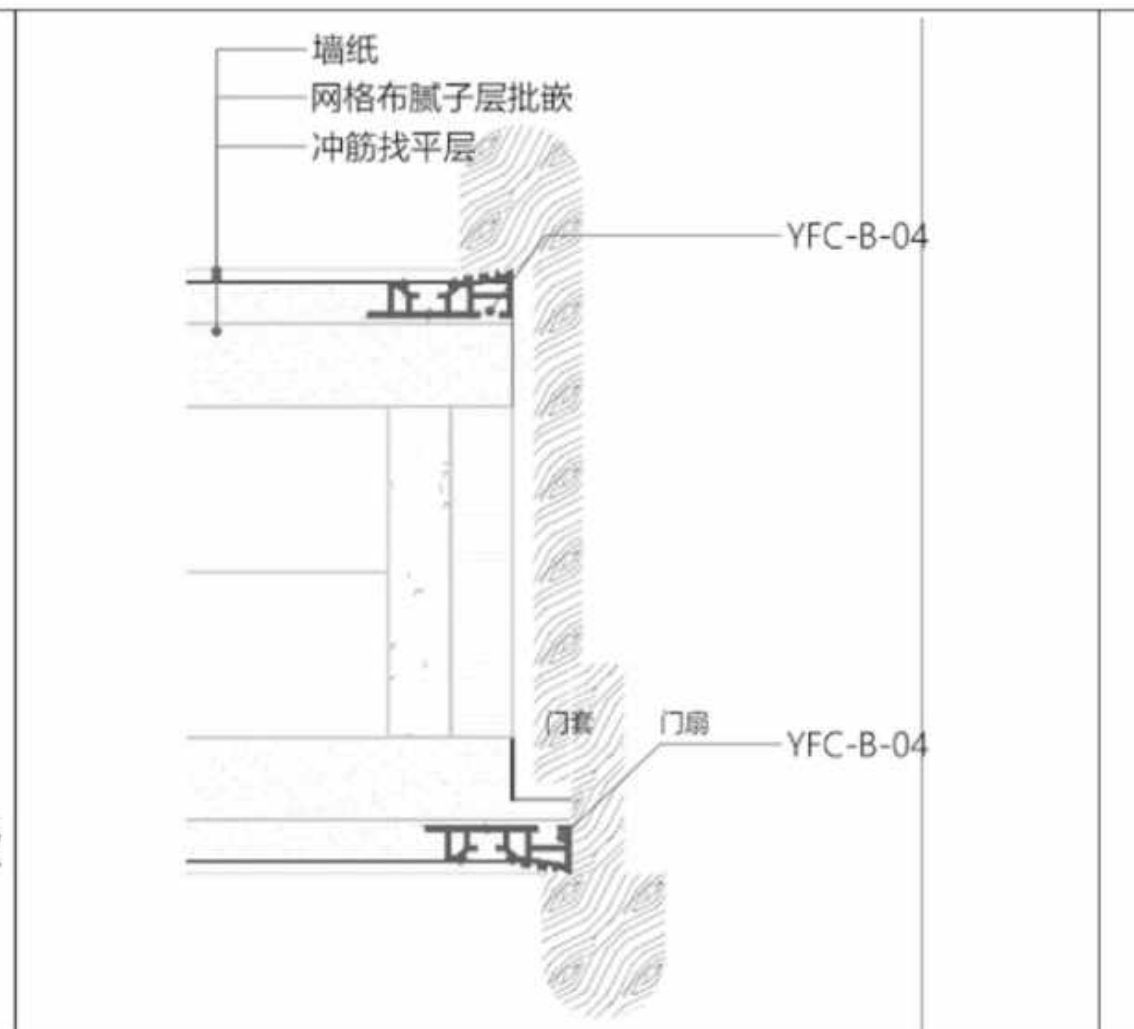
墙纸
网格布腻子层批嵌
冲筋找平层
YFC-B-04
门套
门扇
YFC-B-04

图例D-M1 门边-石膏基找平铝型材

Scale比例 1：1@A2

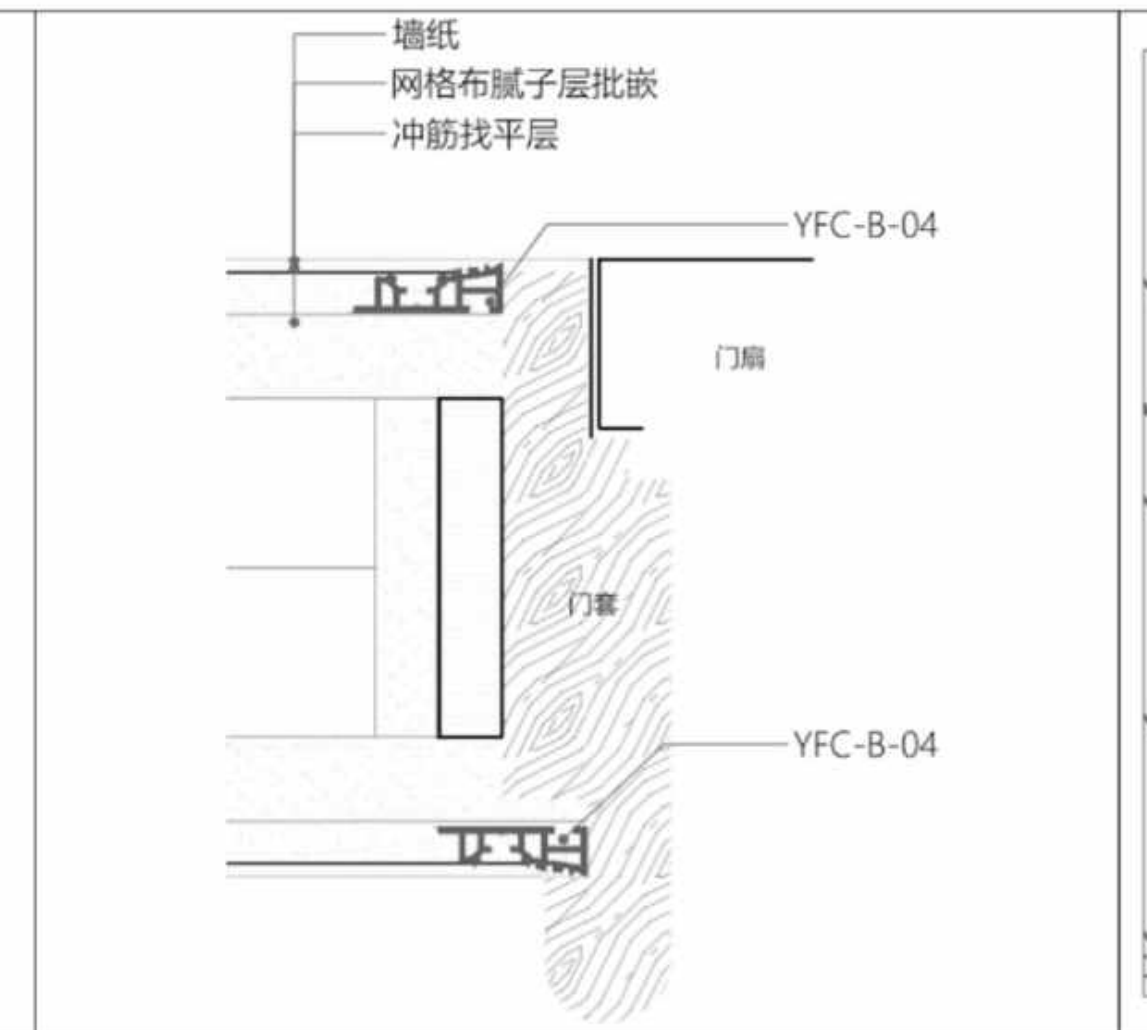
墙纸
网格布腻子层批嵌
冲筋找平层
YFC-B-04
门扇
门套
YFC-B-04

图例D-M2 门边-石膏基找平铝型材

Scale比例 1：1@A2

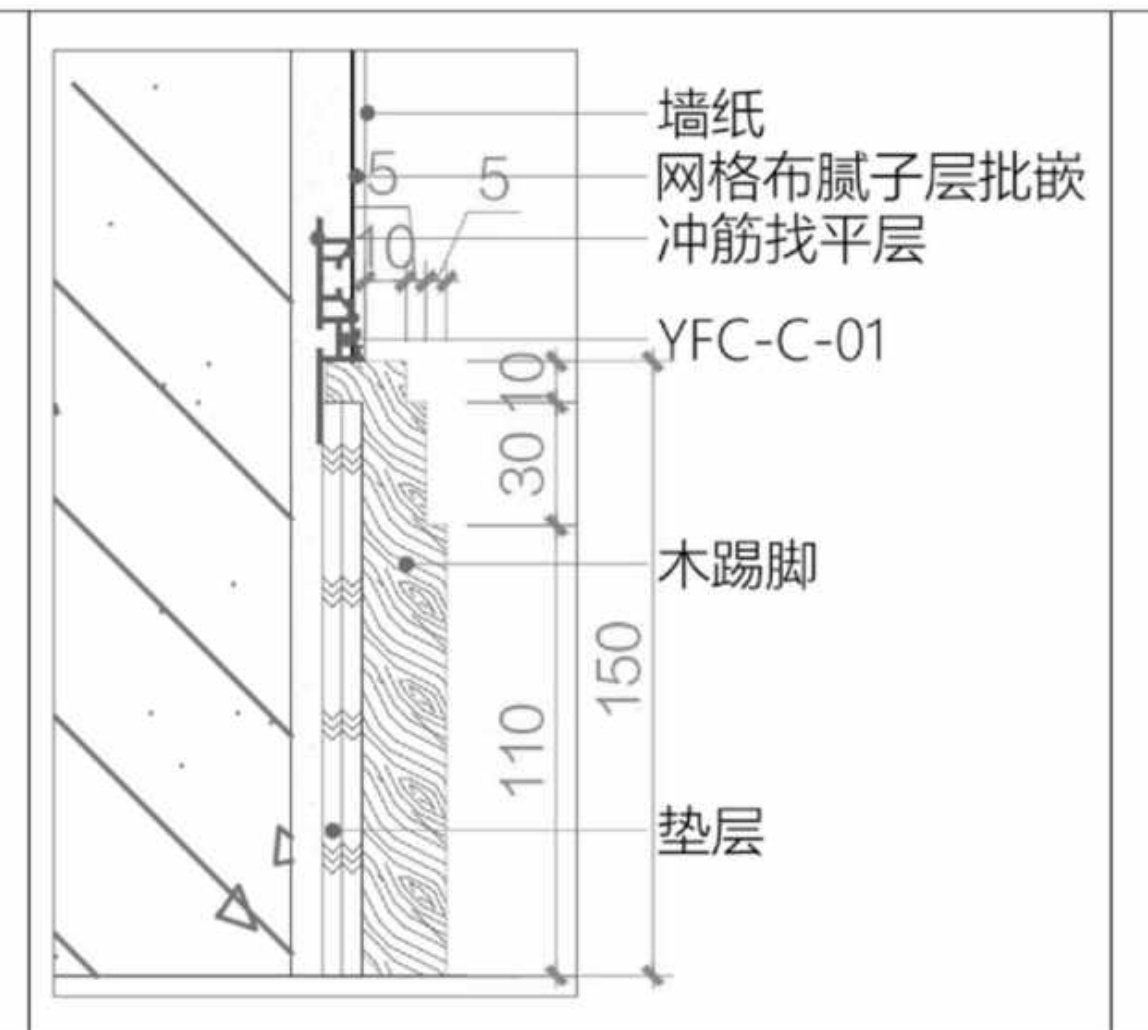
墙纸
网格布腻子层批嵌
冲筋找平层
5
5
10
YFC-C-01
10
30
木踢脚
150
110
垫层

图例E-SP1 踢脚-石膏基找平铝型材

Scale比例 1：1@A2

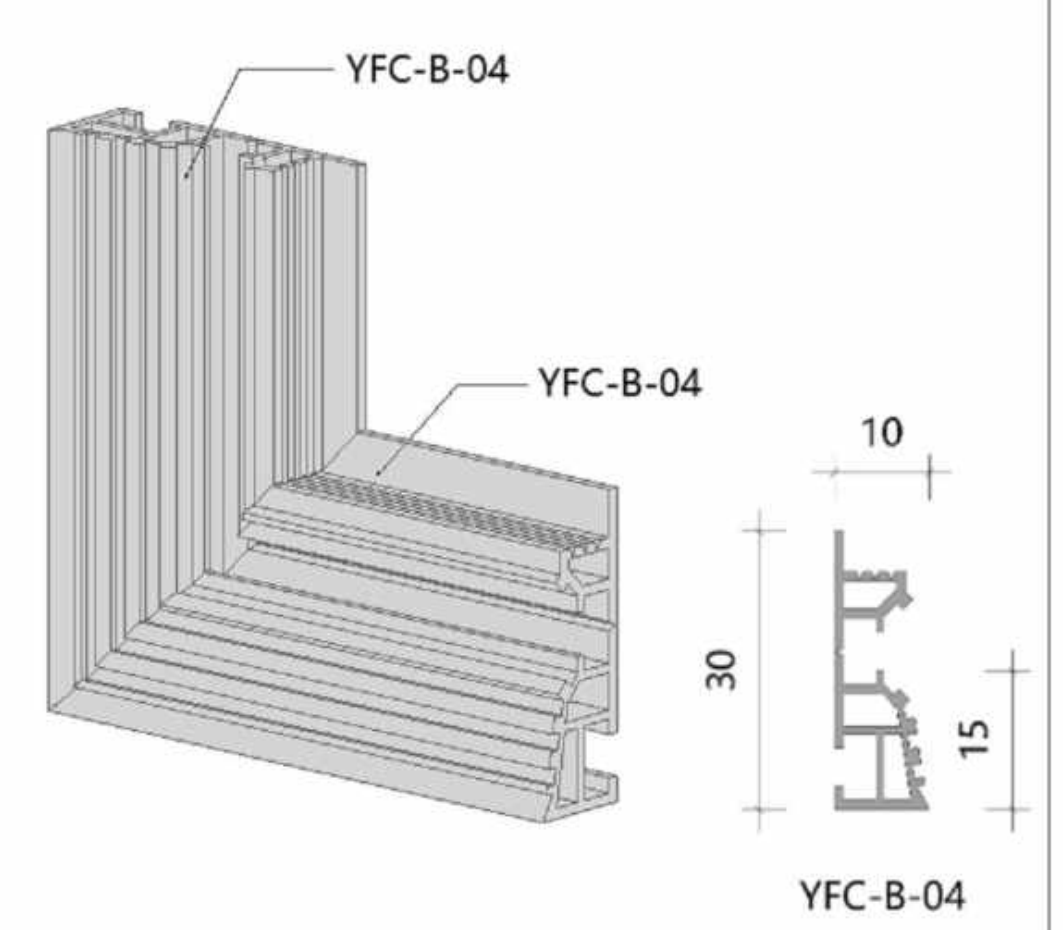
YFC-B-04
YFC-B-04
10
30
15
YFC-B-04

3D-01 转角铝型材-拼接跟通

转角数量：2

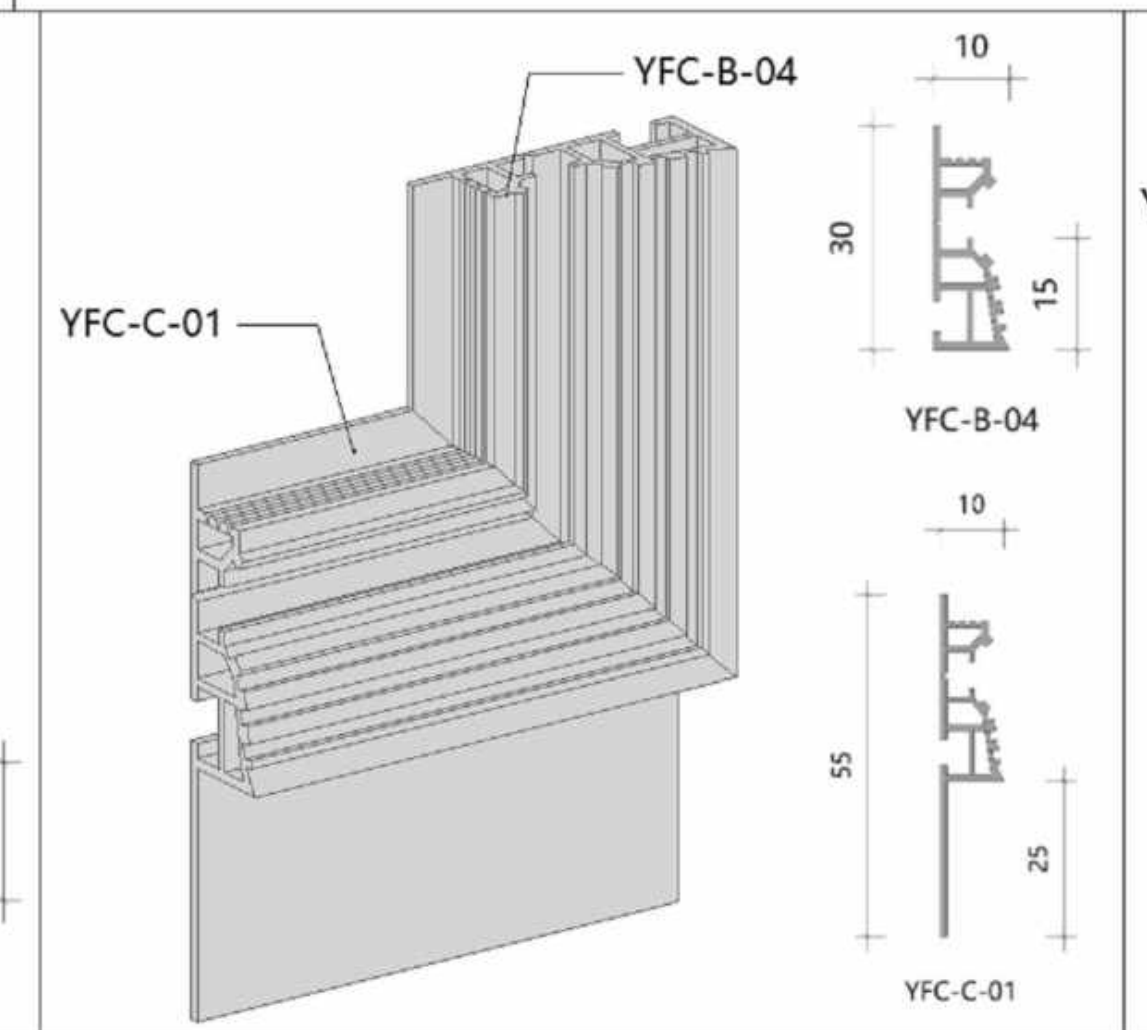
YFC-B-04
YFC-C-01
10
30
15
YFC-B-04
10
55
25
YFC-C-01

3D-06 转角铝型材-拼接跟通

转角数量：3

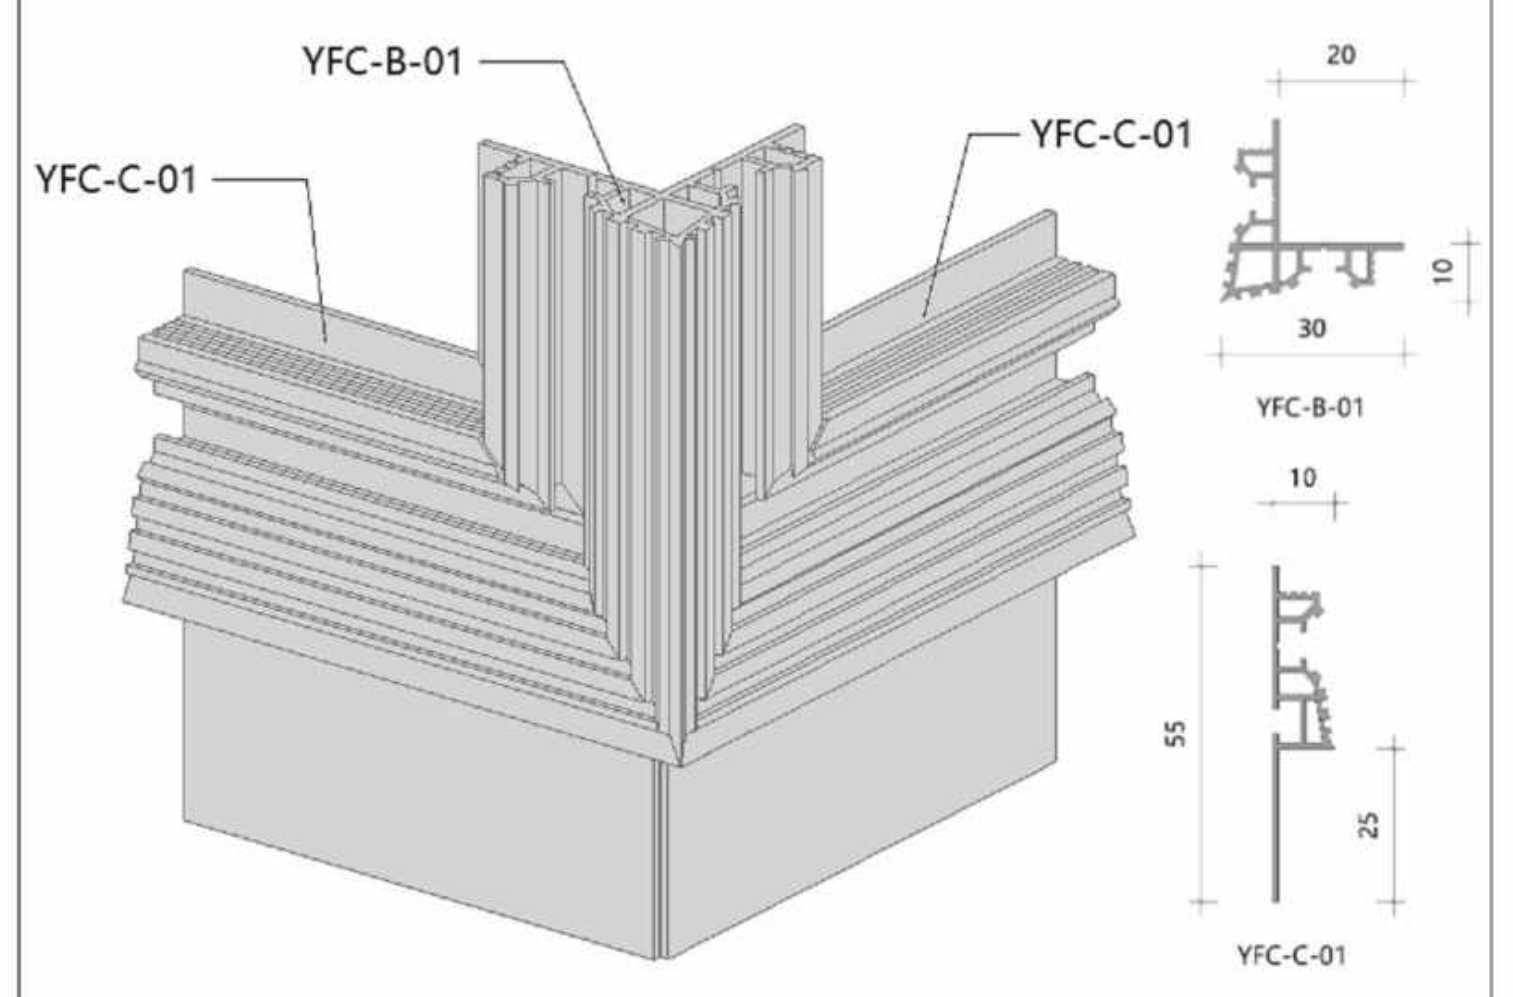
YFC-B-01
YFC-C-01
YFC-C-01
20
30
10
YFC-B-01
10
55
25
YFC-C-01

3D-11 转角铝型材-拼接跟通

转角数量：2

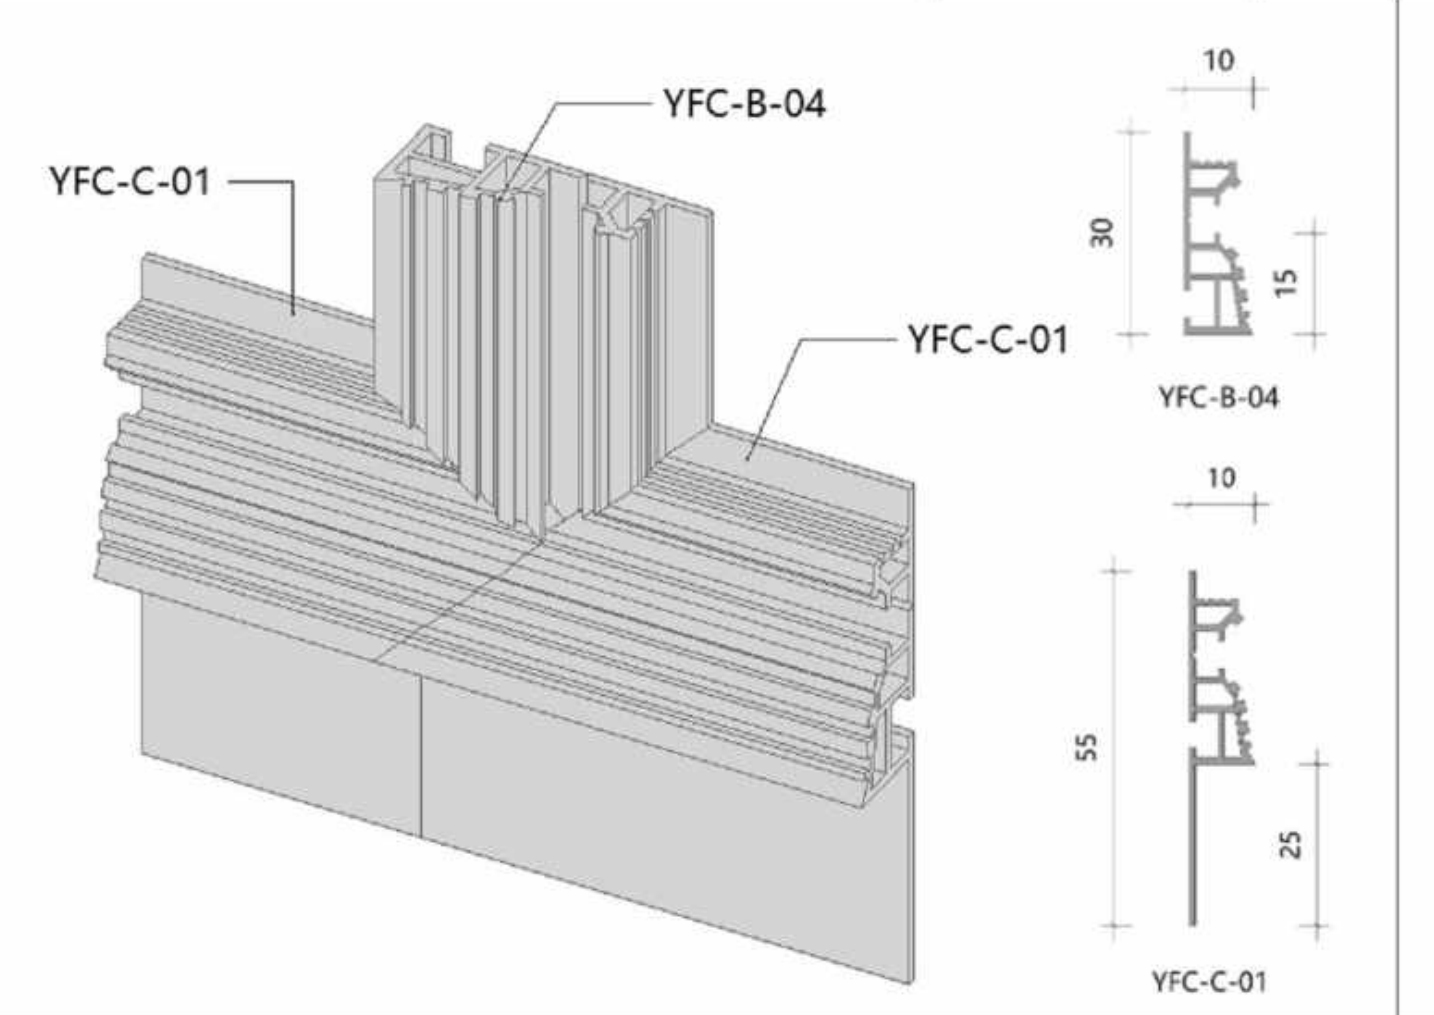
YFC-C-01
YFC-B-04
YFC-C-01
10
30
15
YFC-B-04
10
55
25
YFC-C-01

3D-13 转角铝型材-拼接跟通

转角数量：3

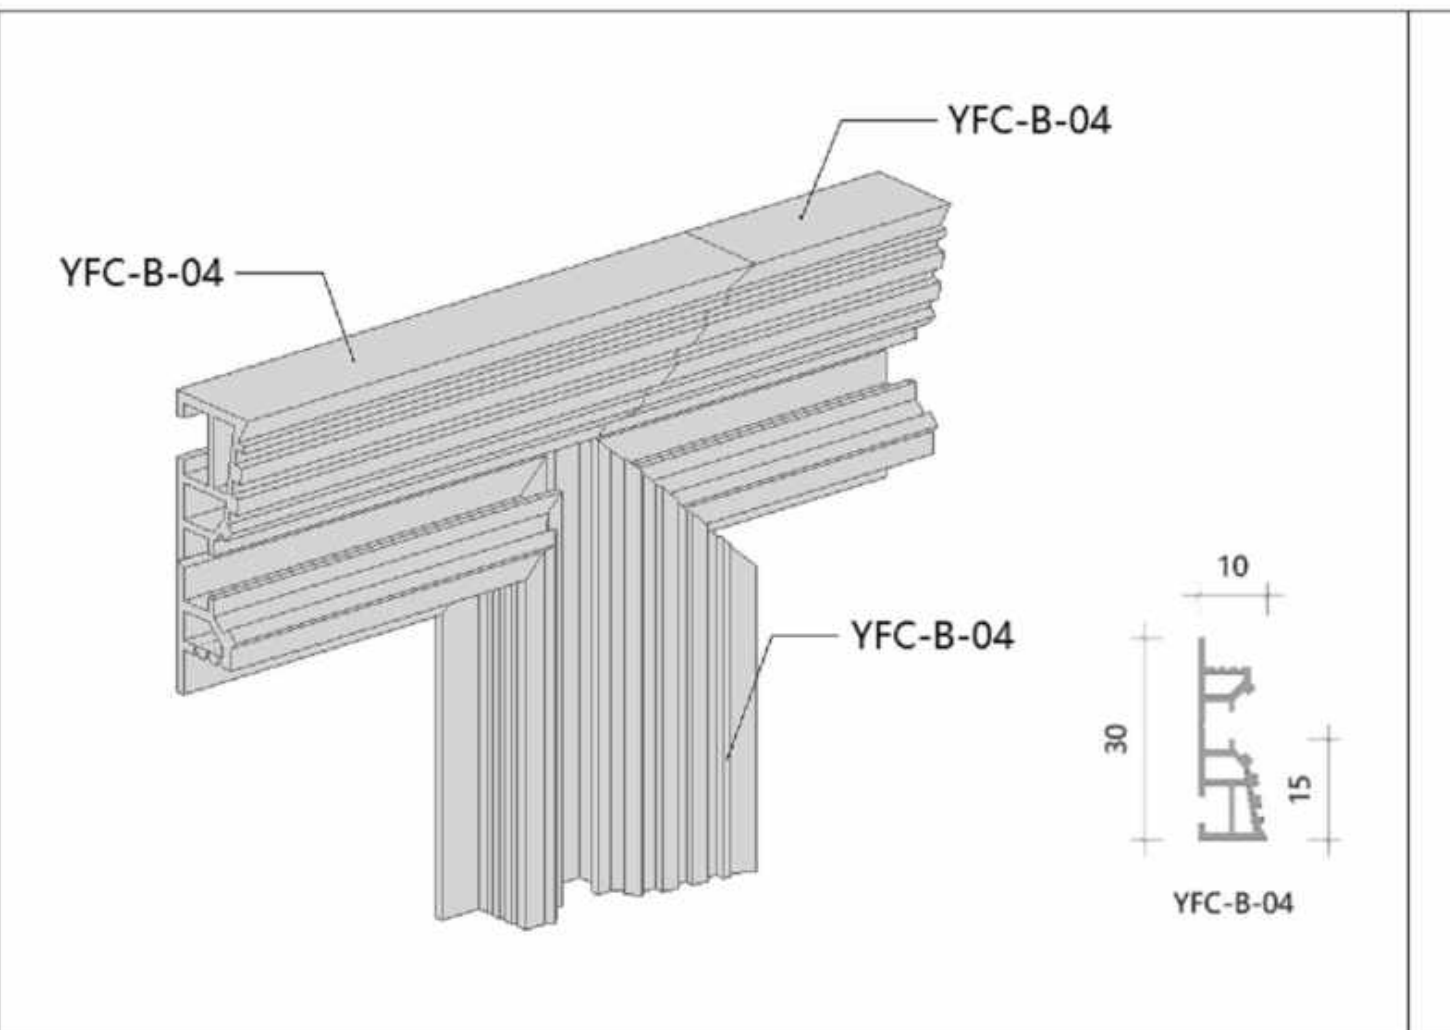
YFC-B-04
YFC-B-04
YFC-B-04
10
30
15
YFC-B-04

3D-14

转角数量：2

盖章

注释
Notes

1.本图纸如与现场尺寸有误，请施工人员与项目负责人联系。
2.施工前施工人员应认真查阅此图，如有不明确尺寸，按现场测量为准。
3.本图纸必须经甲乙双方认可并签字方可作为施工依据。

日期
Date 03/04/26

修订
Revision

△1

项目
Project
潮映华岸府3-801

比例
Scale 1：30@A2

次卧

墙面及踢脚铝型材

图纸编号
Drawing No.
AP.EL-10

项目编号
Project No.

©2025

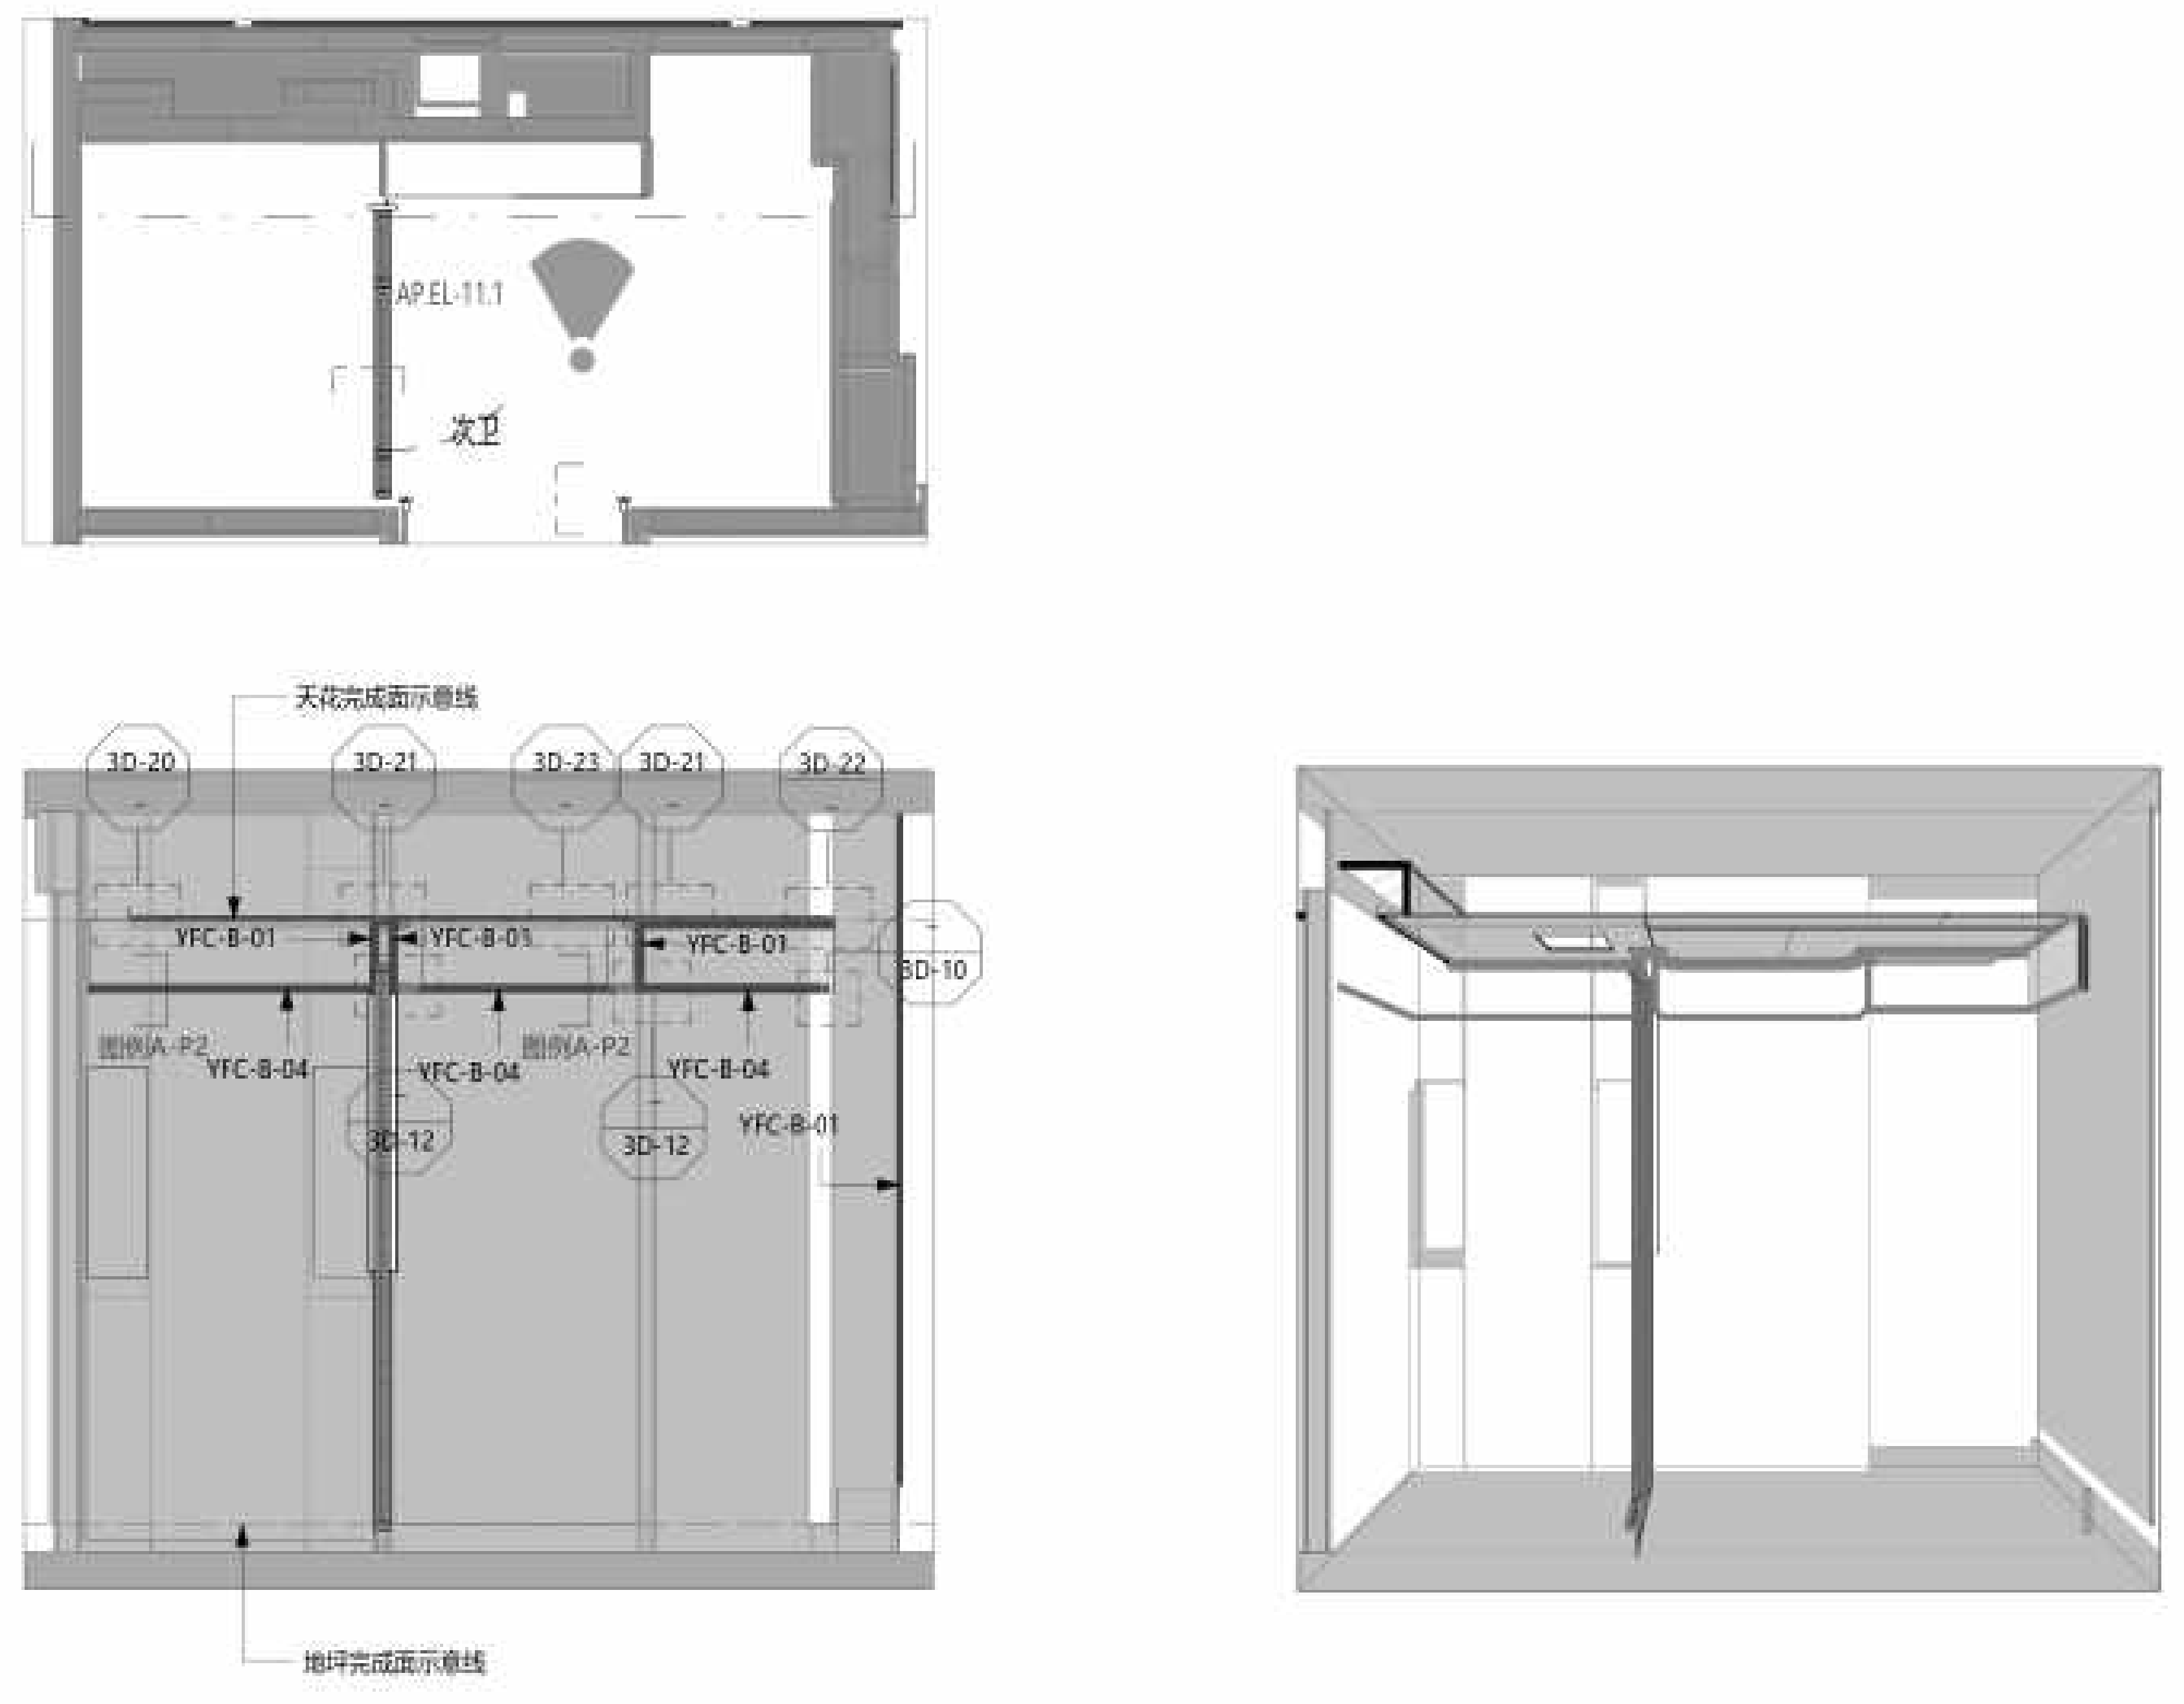
AP.EL-11.1
次卫
天花完成面示意线
3D-20
3D-21
3D-23
3D-21
3D-22
YFC-B-01
YFC-B-01
YFC-B-01
3D-10
图例A-P2
YFC-B-04
YFC-B-04
图例A-P2
YFC-B-04
3D-12
3D-12
YFC-B-01
地坪完成面示意线

1

次卫 墙面及踢脚铝型材立面图1

Scale比例 1 : 30@A2

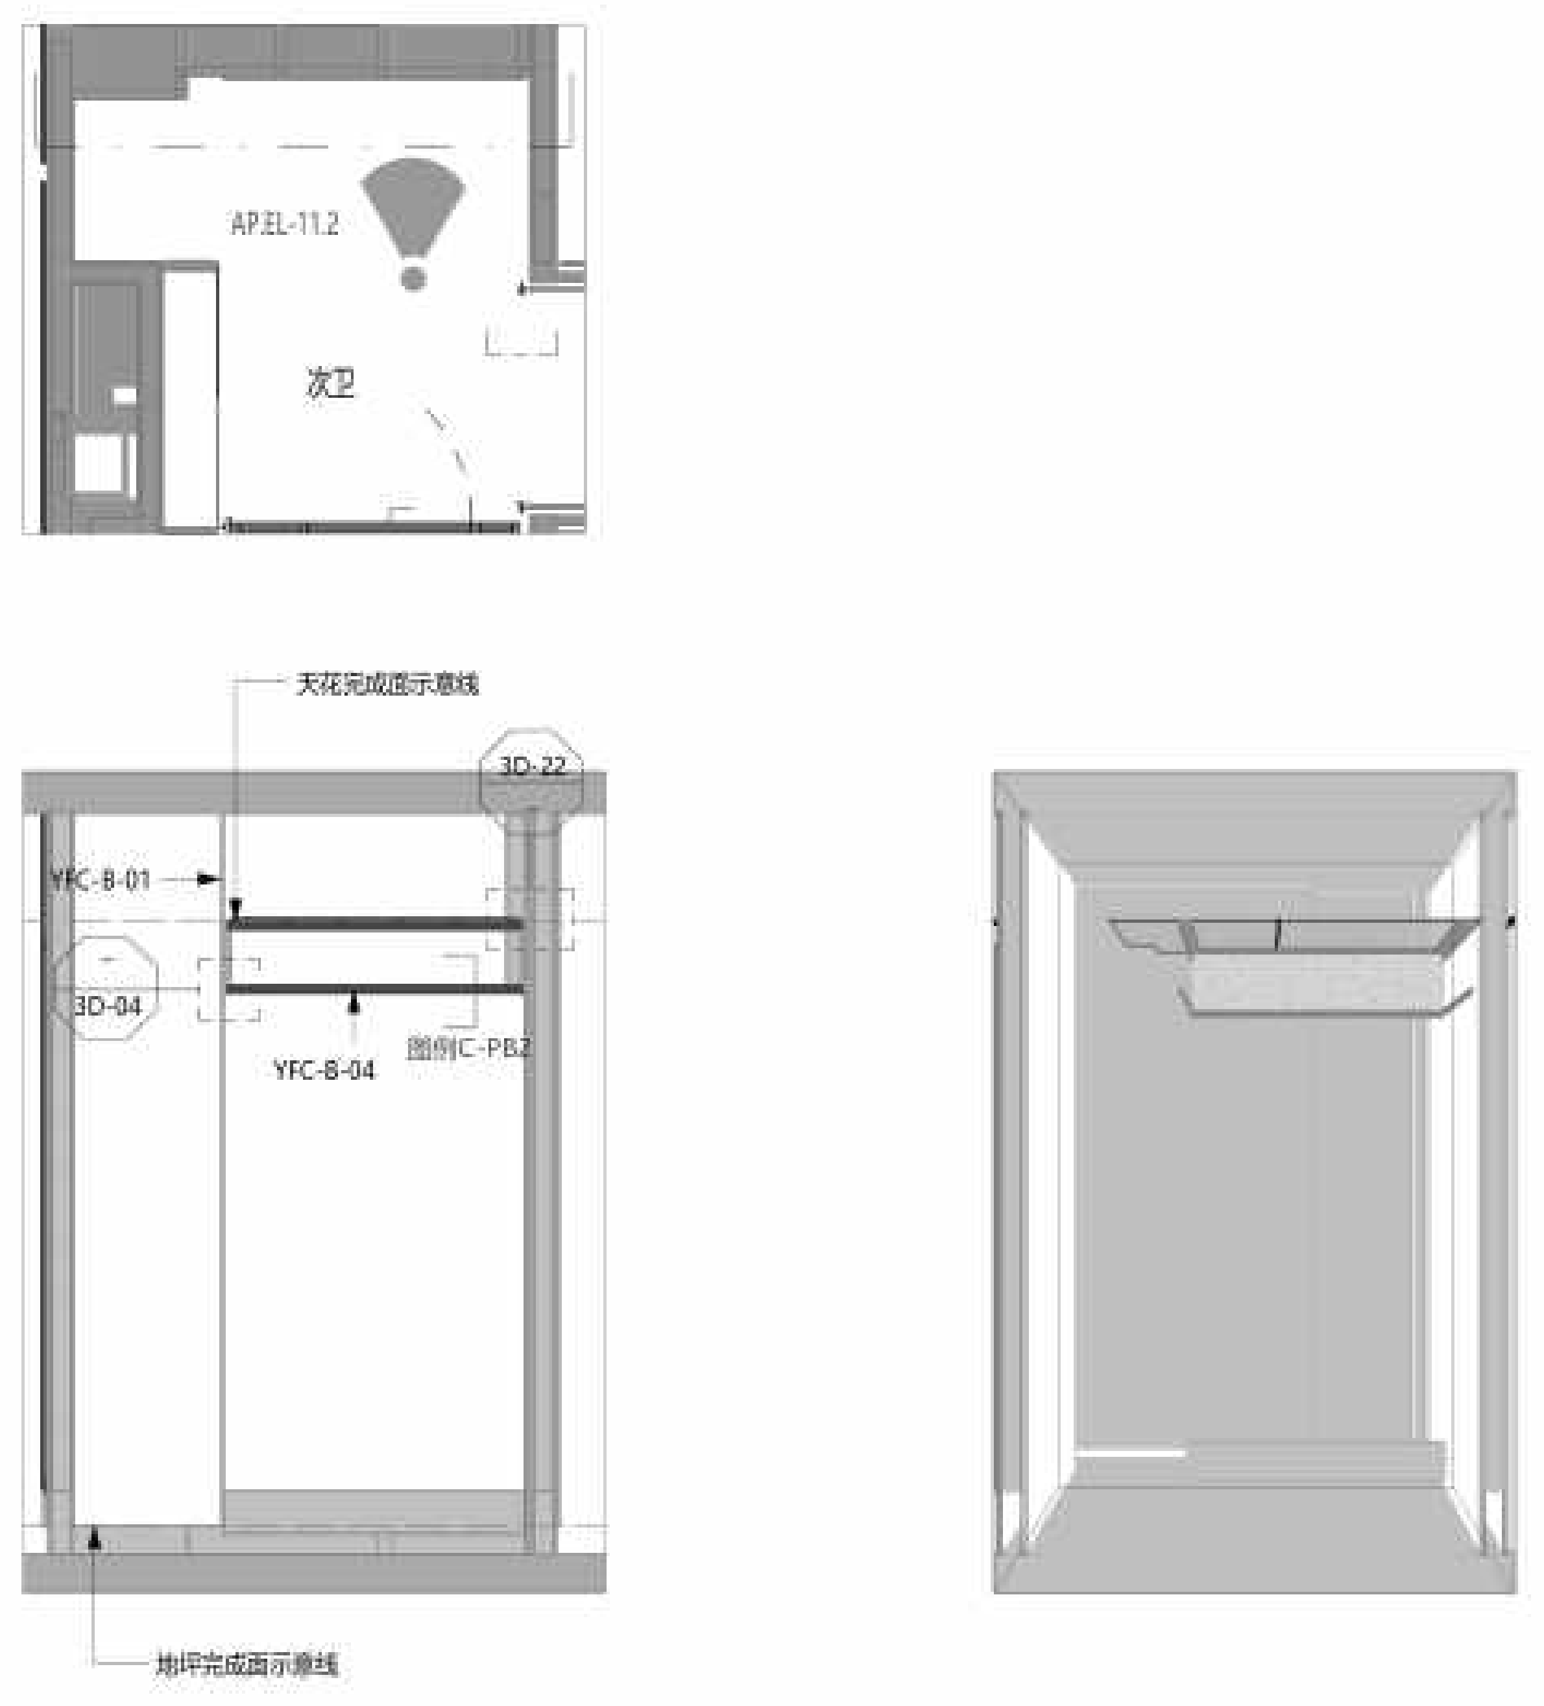
AP.EL-11.2
次卫
天花完成面示意线
3D-22
YFC-B-01
3D-04
YFC-B-04
图例C-PB2
地坪完成面示意线

2

次卫 墙面及踢脚铝型材立面图2

Scale比例 1 : 30@A2

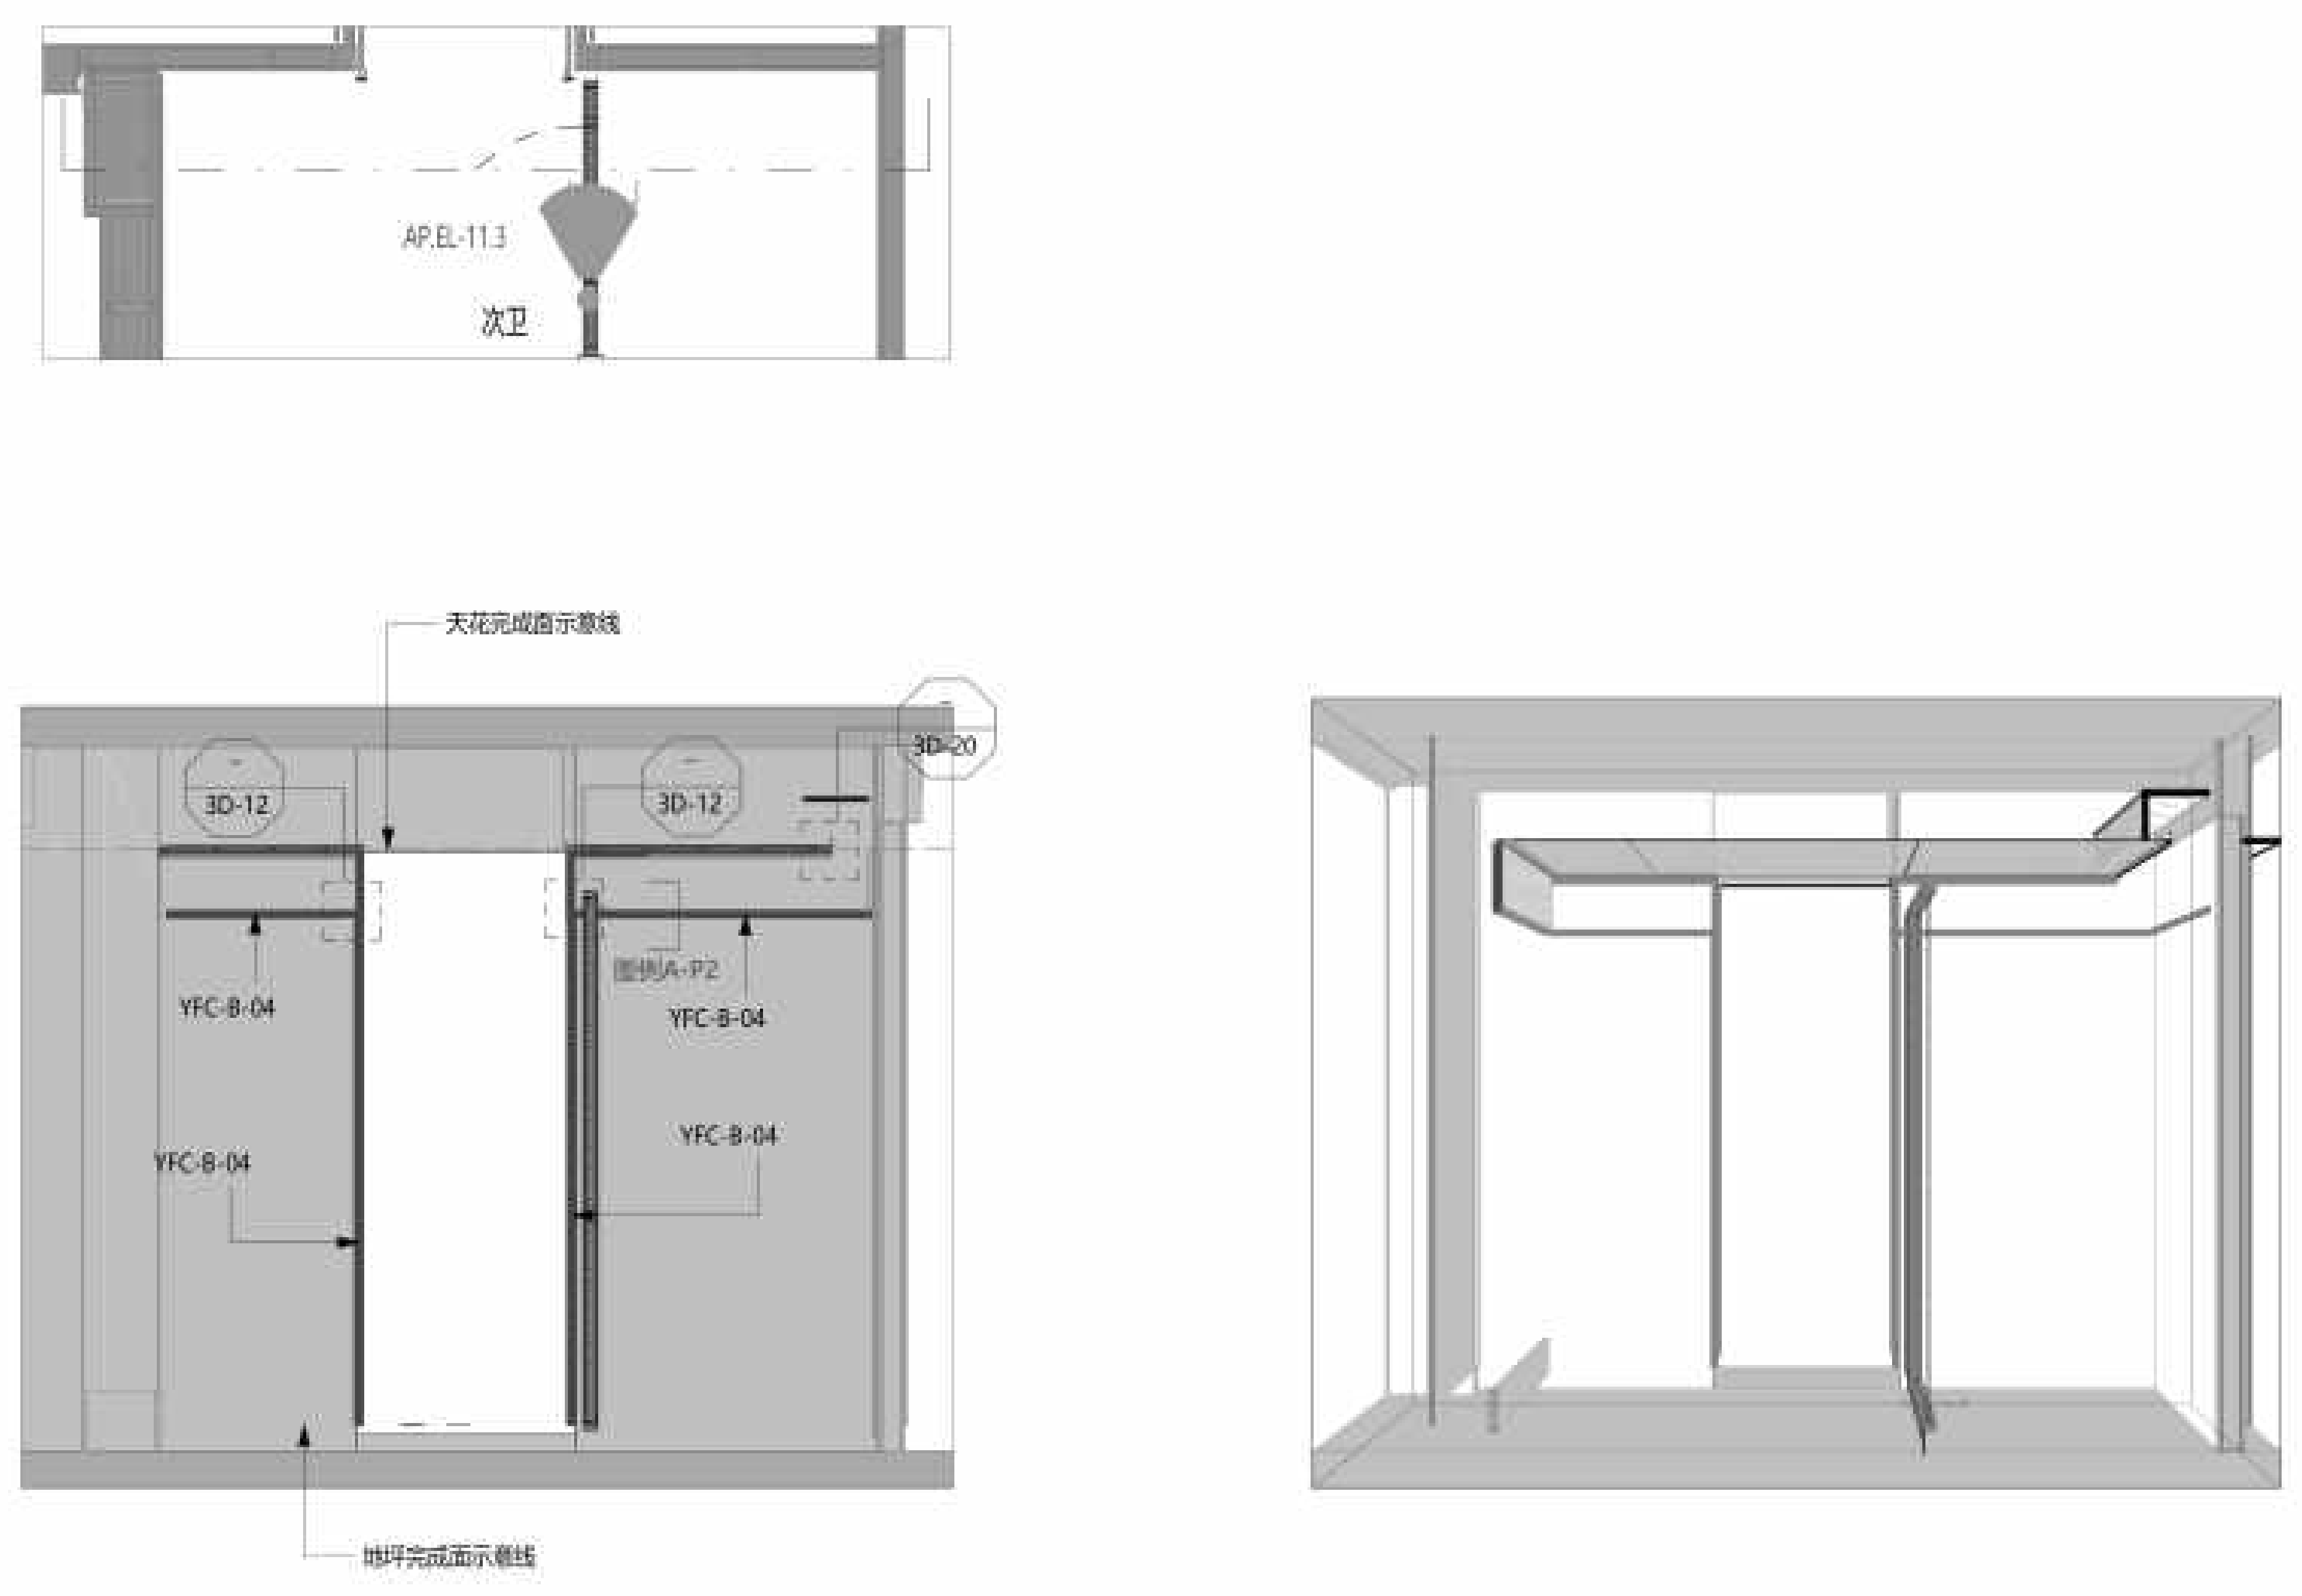
AP.EL-11.3
次卫
天花完成面示意线
3D-12
3D-12
3D-20
YFC-B-04
图例A-P2
YFC-B-04
YFC-B-04
YFC-B-04
地坪完成面示意线

3

次卫 墙面及踢脚铝型材立面图3

Scale比例 1 : 30@A2

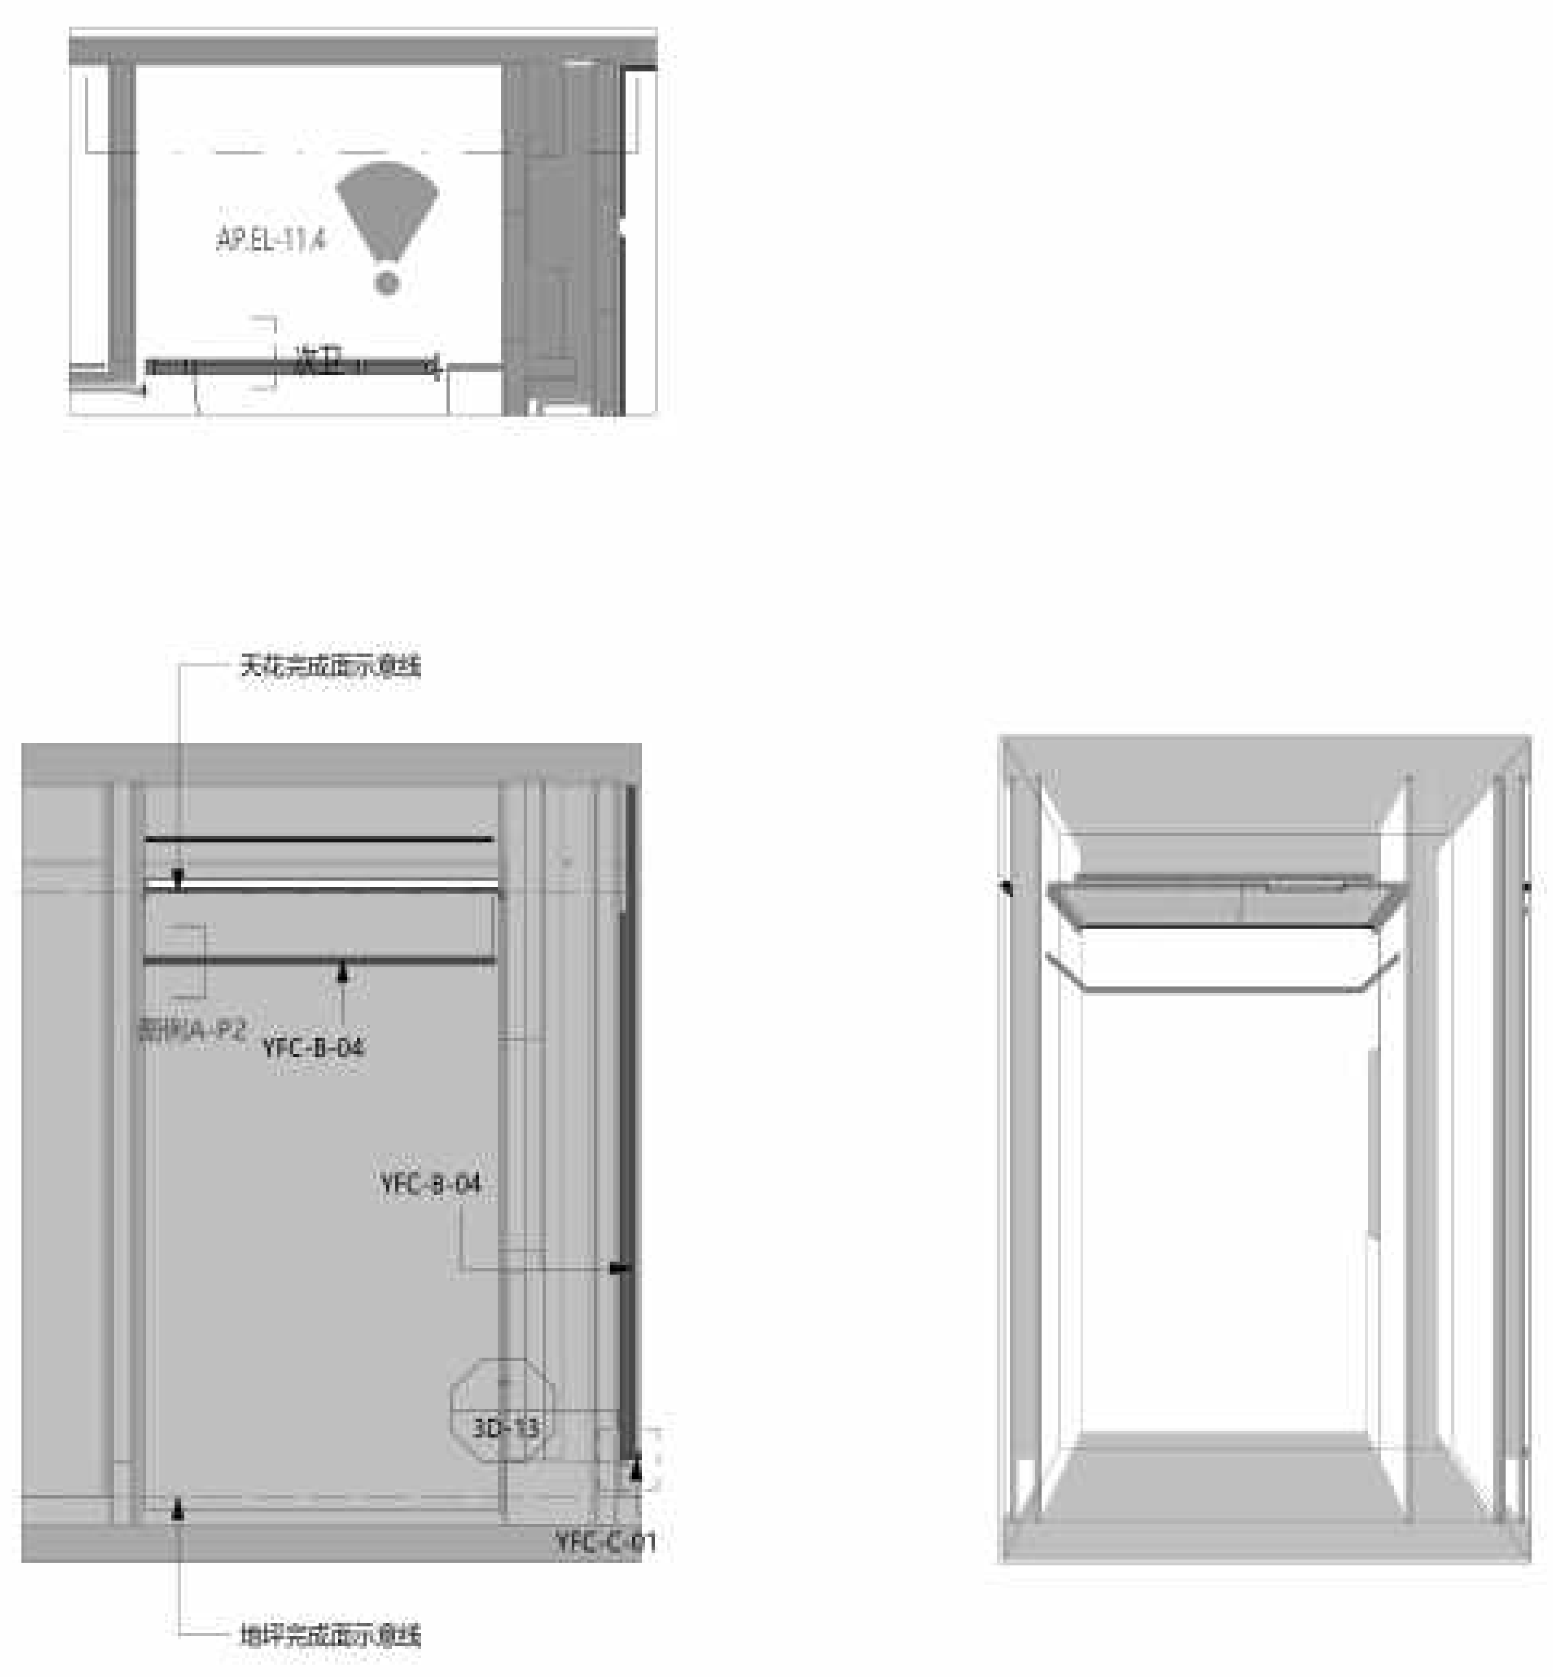
AP.EL-11.4
次卫
天花完成面示意线
图例A-P2
YFC-B-04
YFC-B-04
3D-13
YFC-C-01
地坪完成面示意线

4

次卫 墙面及踢脚铝型材立面图4

Scale比例 1 : 30@A2

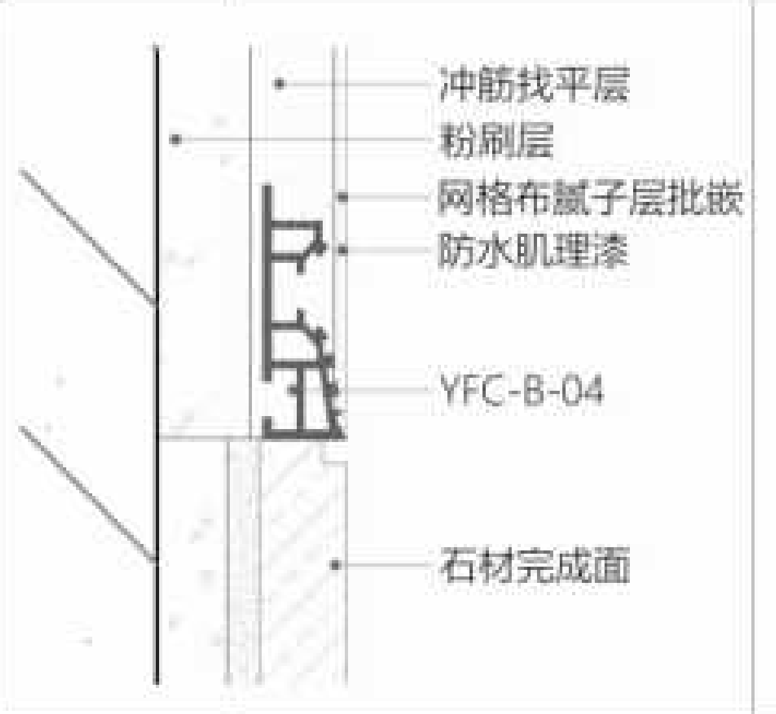
冲筋找平层
粉刷层
网格布腻子层批嵌
防水肌理漆
YFC-B-04
石材完成面

图例A-P2

墙面-石膏基找平铝型材

Scale比例 1 : 1@A2

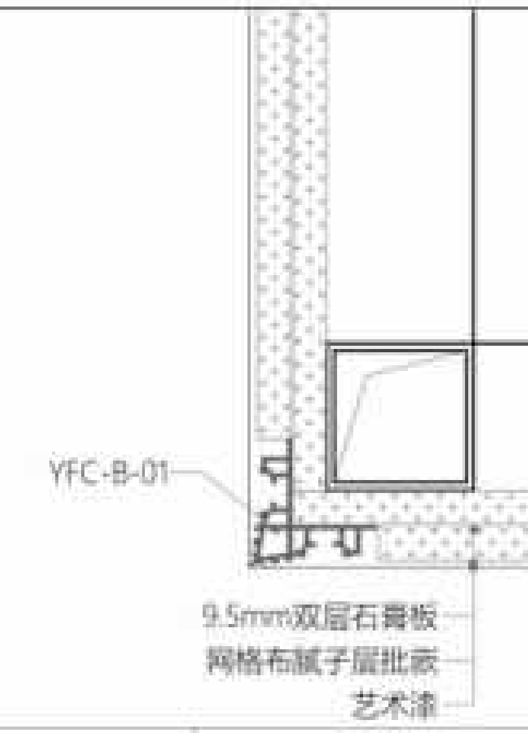
YFC-B-01
9.5mm双层石膏板
网格布腻子层批嵌
艺术漆

图例C-PB1

墙面-石膏基找平铝型材

Scale比例 1 : 1@A2

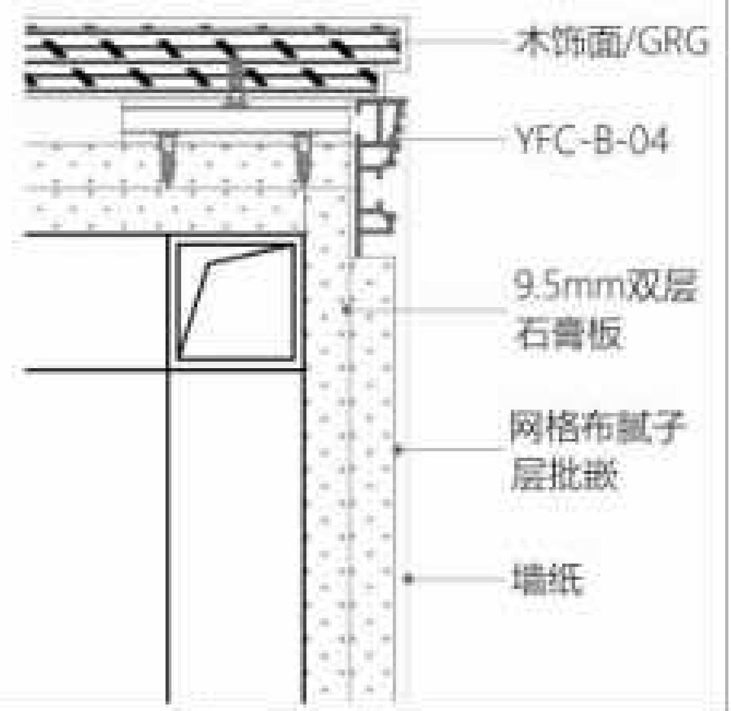
木饰面/GRG
YFC-B-04
9.5mm双层石膏板
网格布腻子层批嵌
墙纸

图例C-PB2

墙面-石膏基找平铝型材

Scale比例 1 : 1@A2

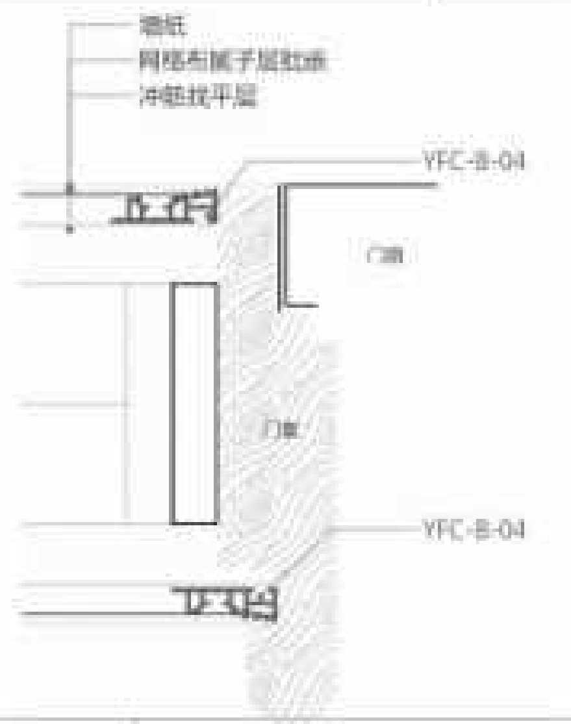
墙纸
网格布腻子层批嵌
冲筋找平层
YFC-B-04
YFC-B-04

图例D-M2

门边-石膏基找平铝型材

Scale比例 1 : 1@A2

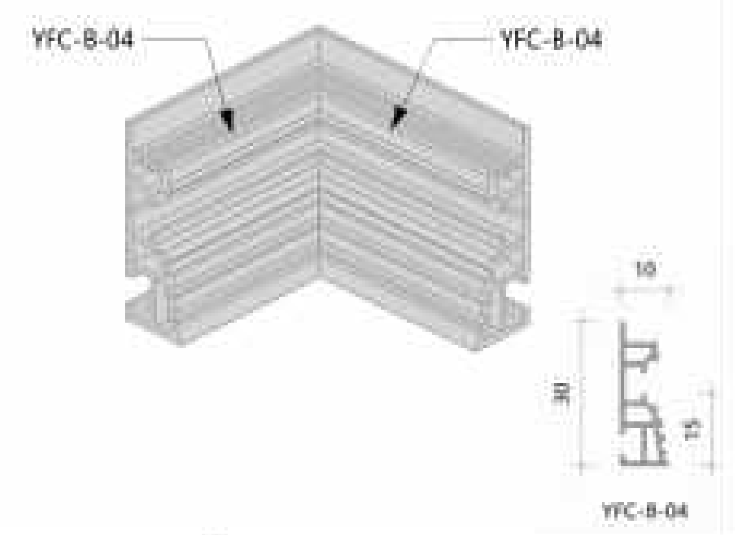
YFC-B-04
YFC-B-04
10
30
15
YFC-B-04

3D-04

转角铝型材-拼接跟通

转角数量：7

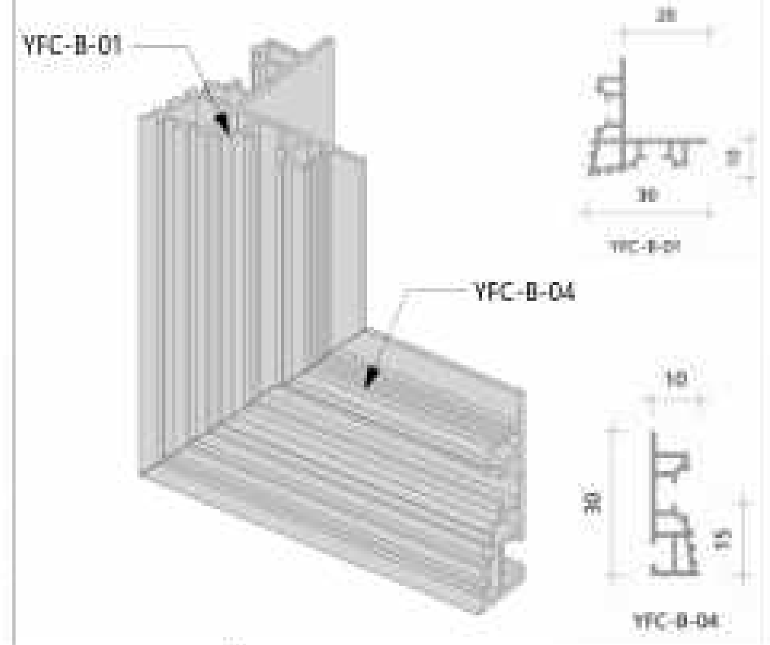
YFC-B-01
YFC-B-04
20
30
17
YFC-B-01
10
30
15
YFC-B-04

3D-10

转角铝型材-拼接跟通

转角数量：1

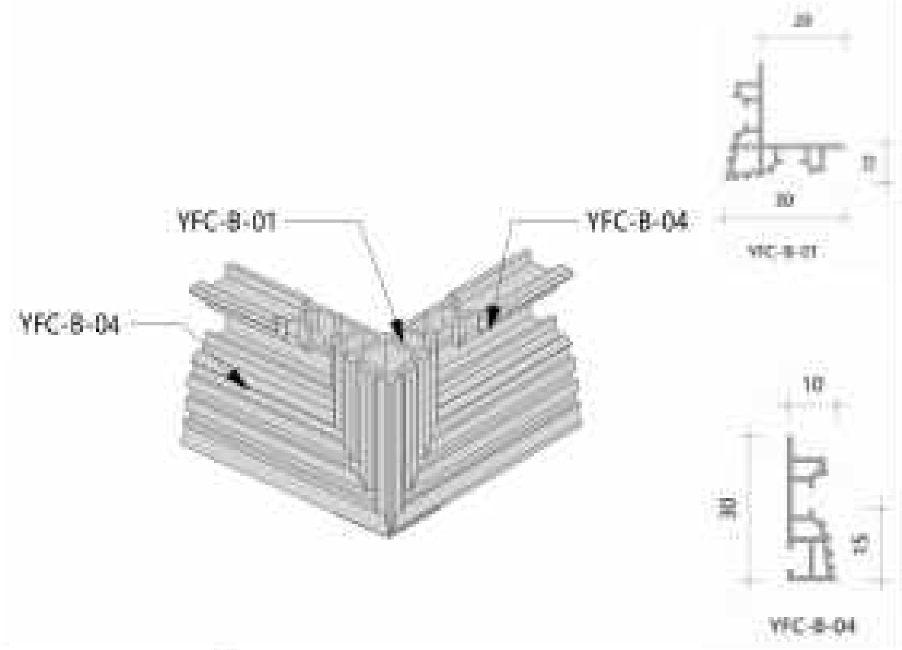
YFC-B-01
YFC-B-04
YFC-B-04
20
30
17
YFC-B-01
10
30
15
YFC-B-04

3D-12

转角铝型材-拼接跟通

转角数量：4

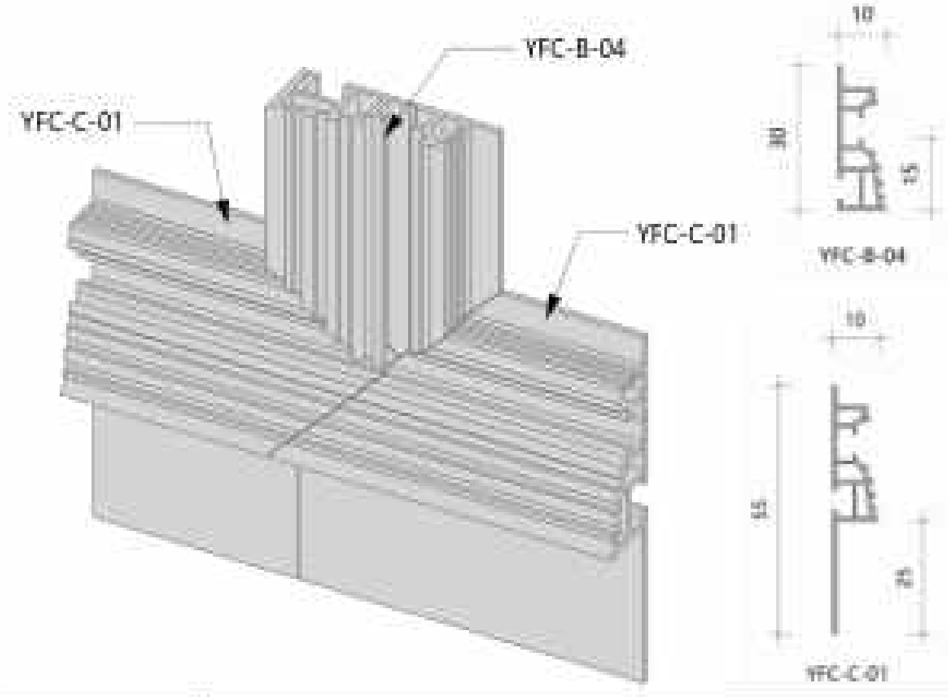
YFC-B-04
YFC-C-01
YFC-C-01
10
30
15
YFC-B-04
10
15
25
YFC-C-01

3D-13

转角铝型材-拼接跟通

转角数量：1

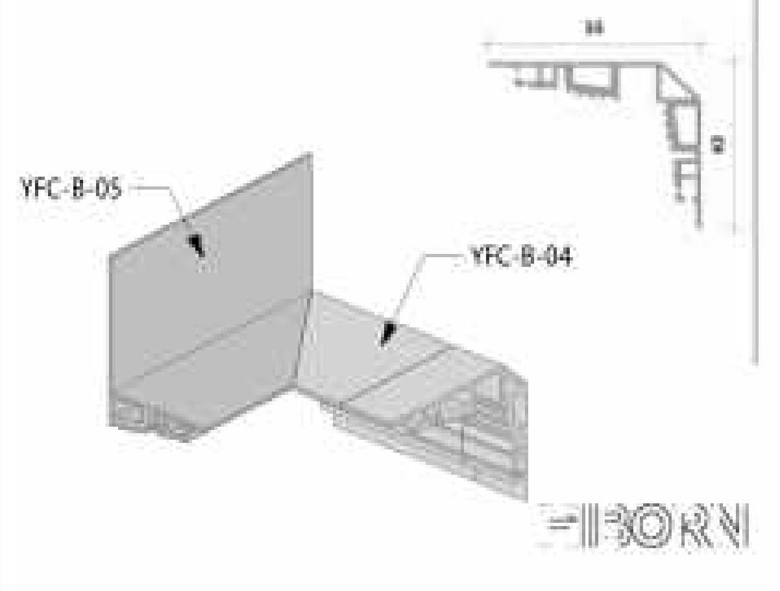
YFC-B-05
YFC-B-04

3D-20

转角铝型材-拼接跟通

转角数量：2

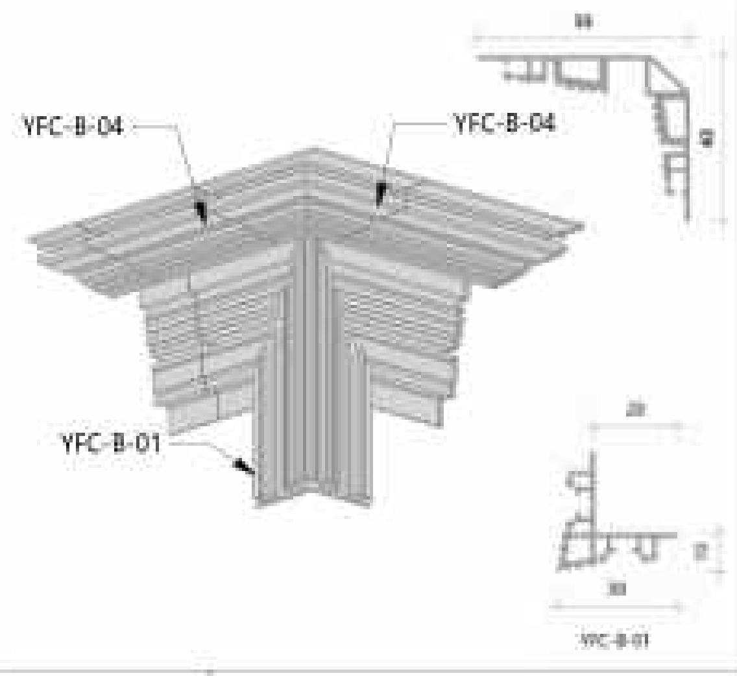
YFC-B-04
YFC-B-04
YFC-B-01
YFC-B-01

3D-21

转角铝型材-拼接跟通

转角数量：3

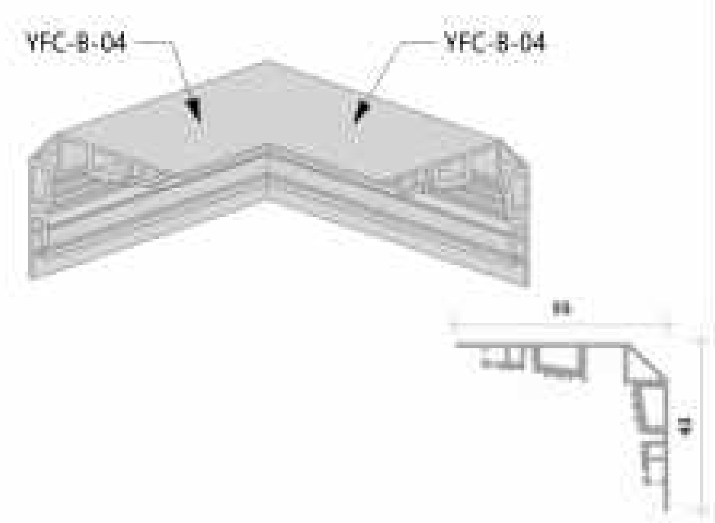
YFC-B-04
YFC-B-04

3D-22

转角铝型材-拼接跟通

转角数量：3

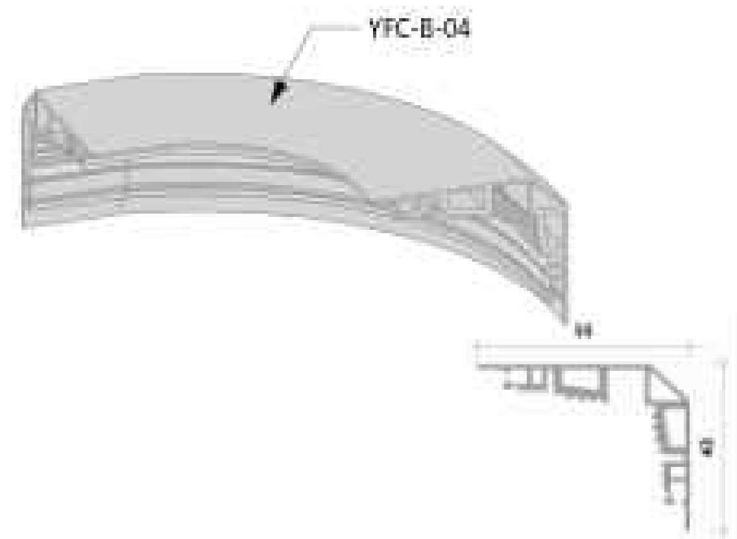

3D-23

转角铝型材-拼接跟通

转角数量：2

盖章

注释
Notes

[illegible]

日期
Date 03/04/26

修订
Revision

项目
Project
潮映华岸府3-801

比例
Scale 1: 30@A2

次卫
墙面及踢脚铝型材

图纸编号
Drawing No.
AP.EL-11

项目编号
Project No.
©2025

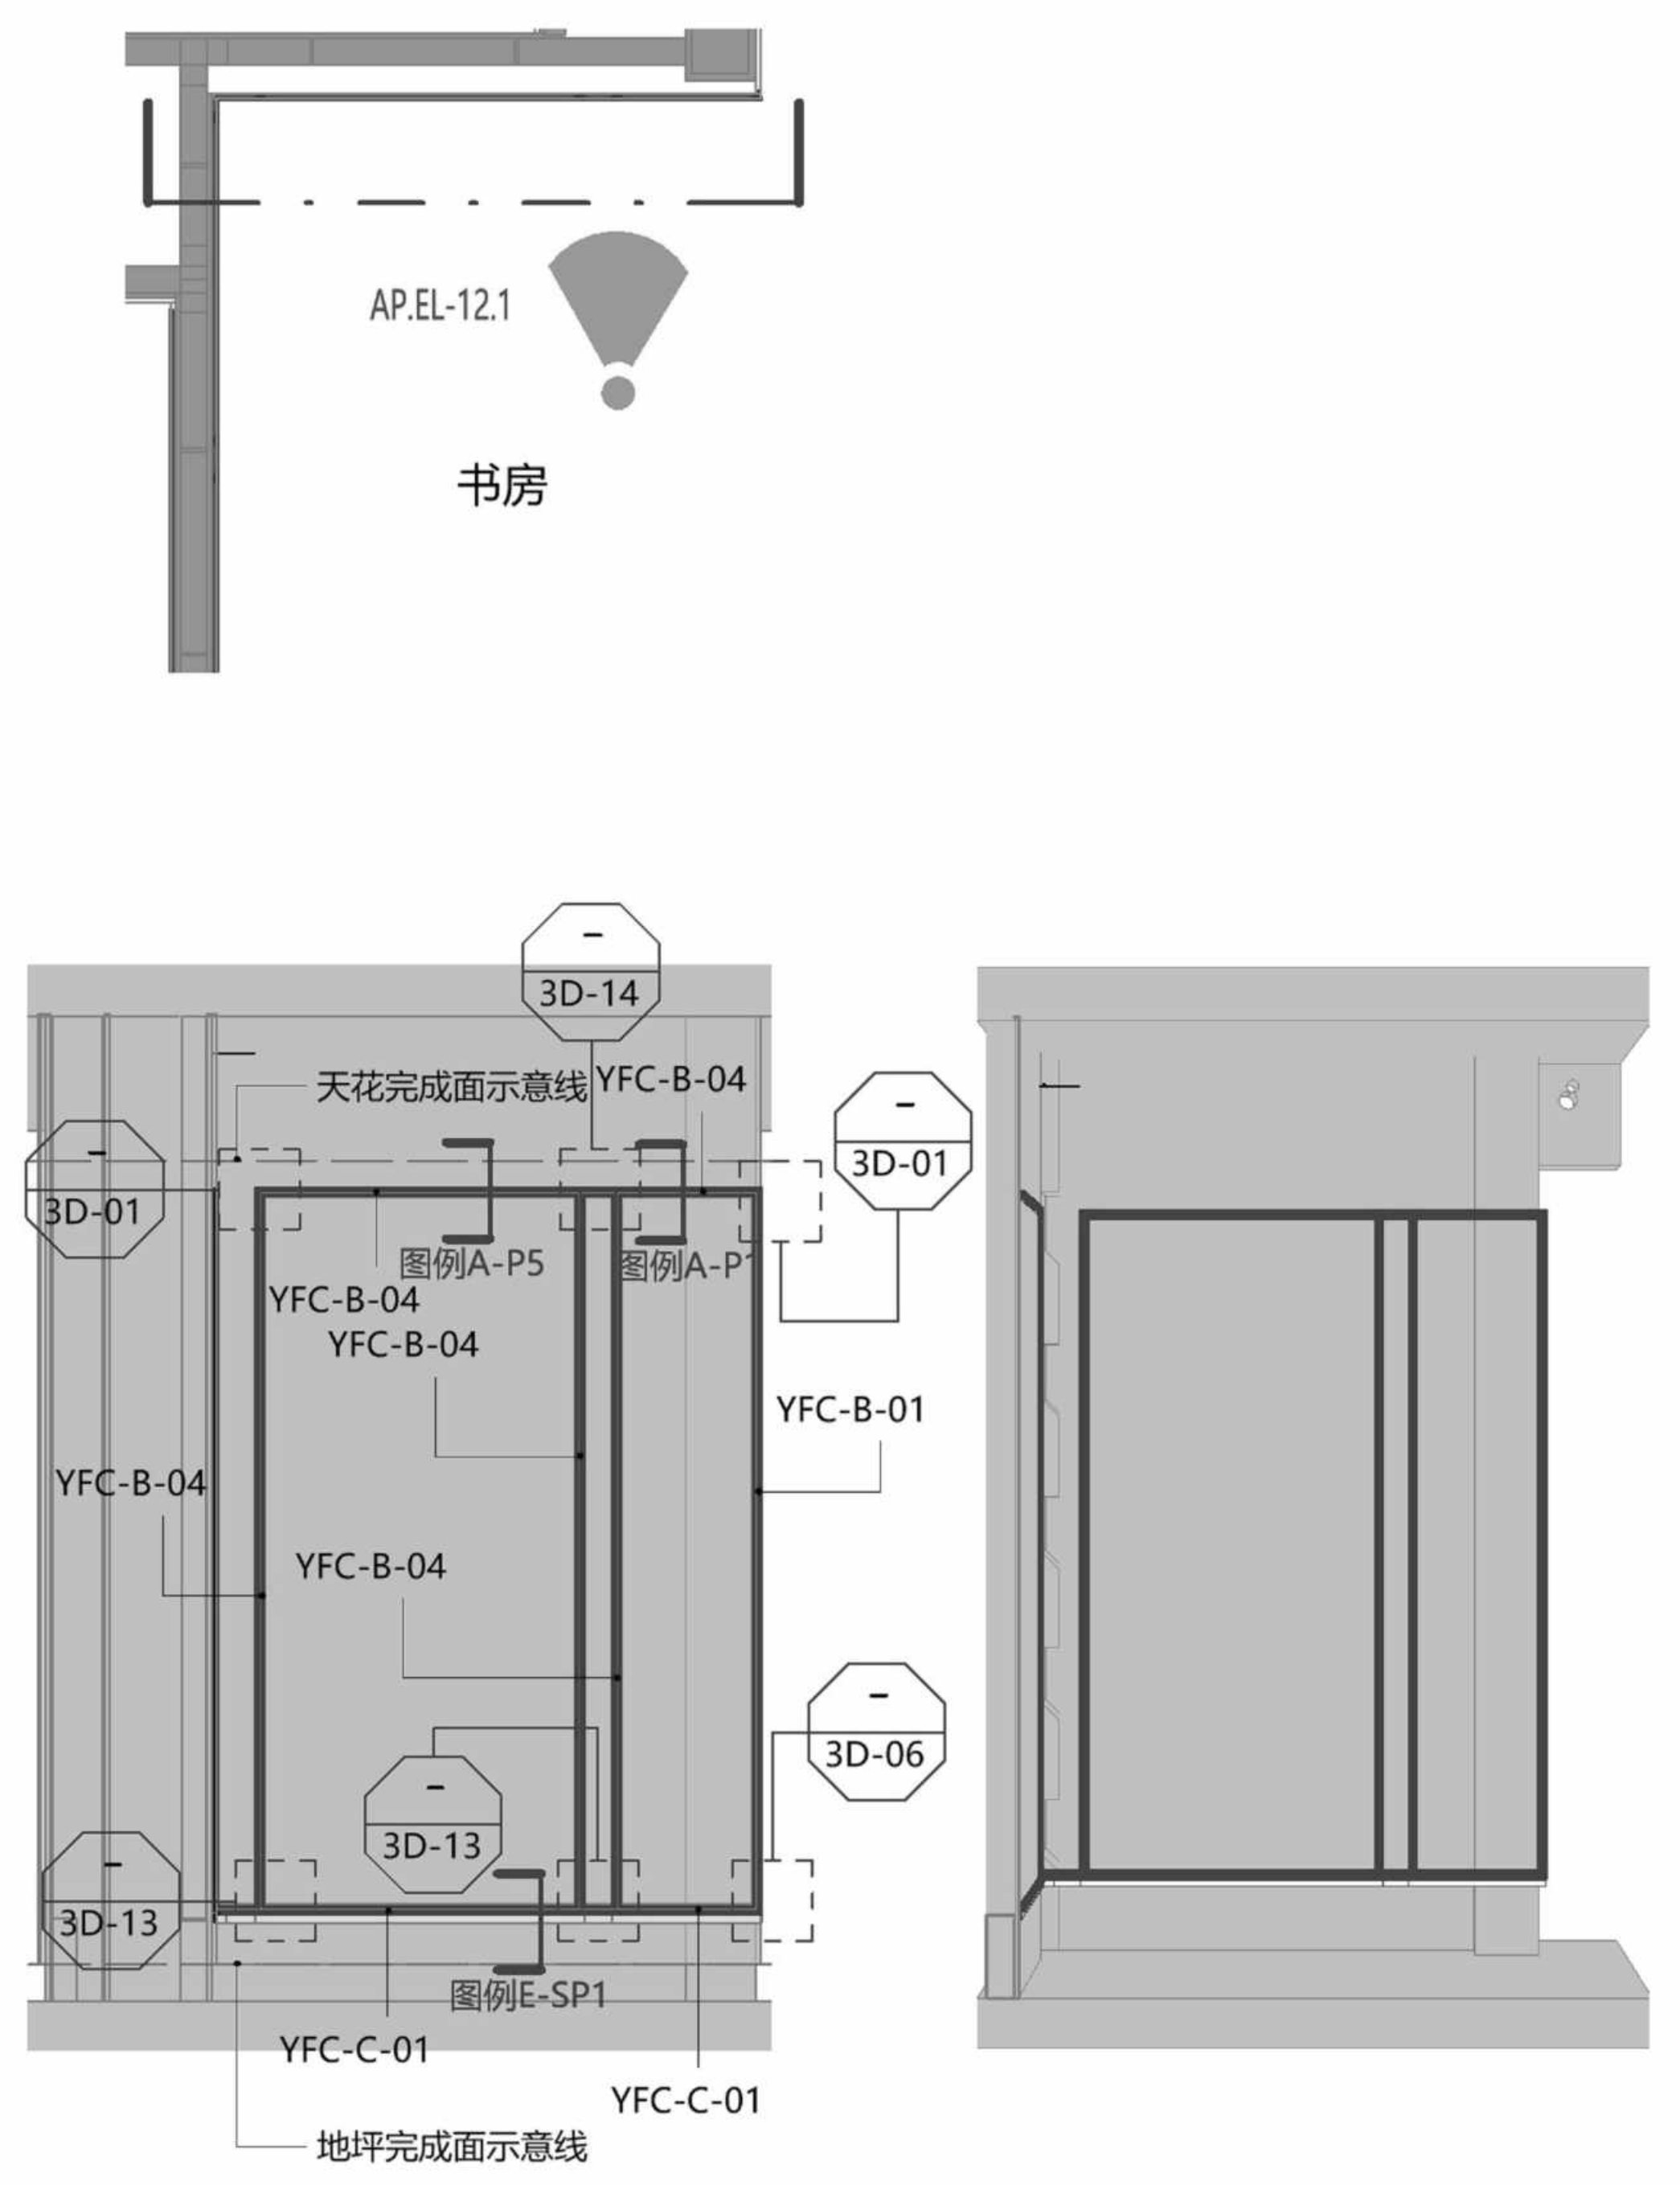
AP.EL-12.1
书房
3D-14
天花完成面示意线
YFC-B-04
3D-01
3D-01
图例A-P5
图例A-P1
YFC-B-04
YFC-B-04
YFC-B-01
YFC-B-04
YFC-B-04
3D-06
3D-13
3D-13
图例E-SP1
YFC-C-01
YFC-C-01
地坪完成面示意线

1

书房 墙面及踢脚铝型材立面图1

Scale比例 1 : 30@A2

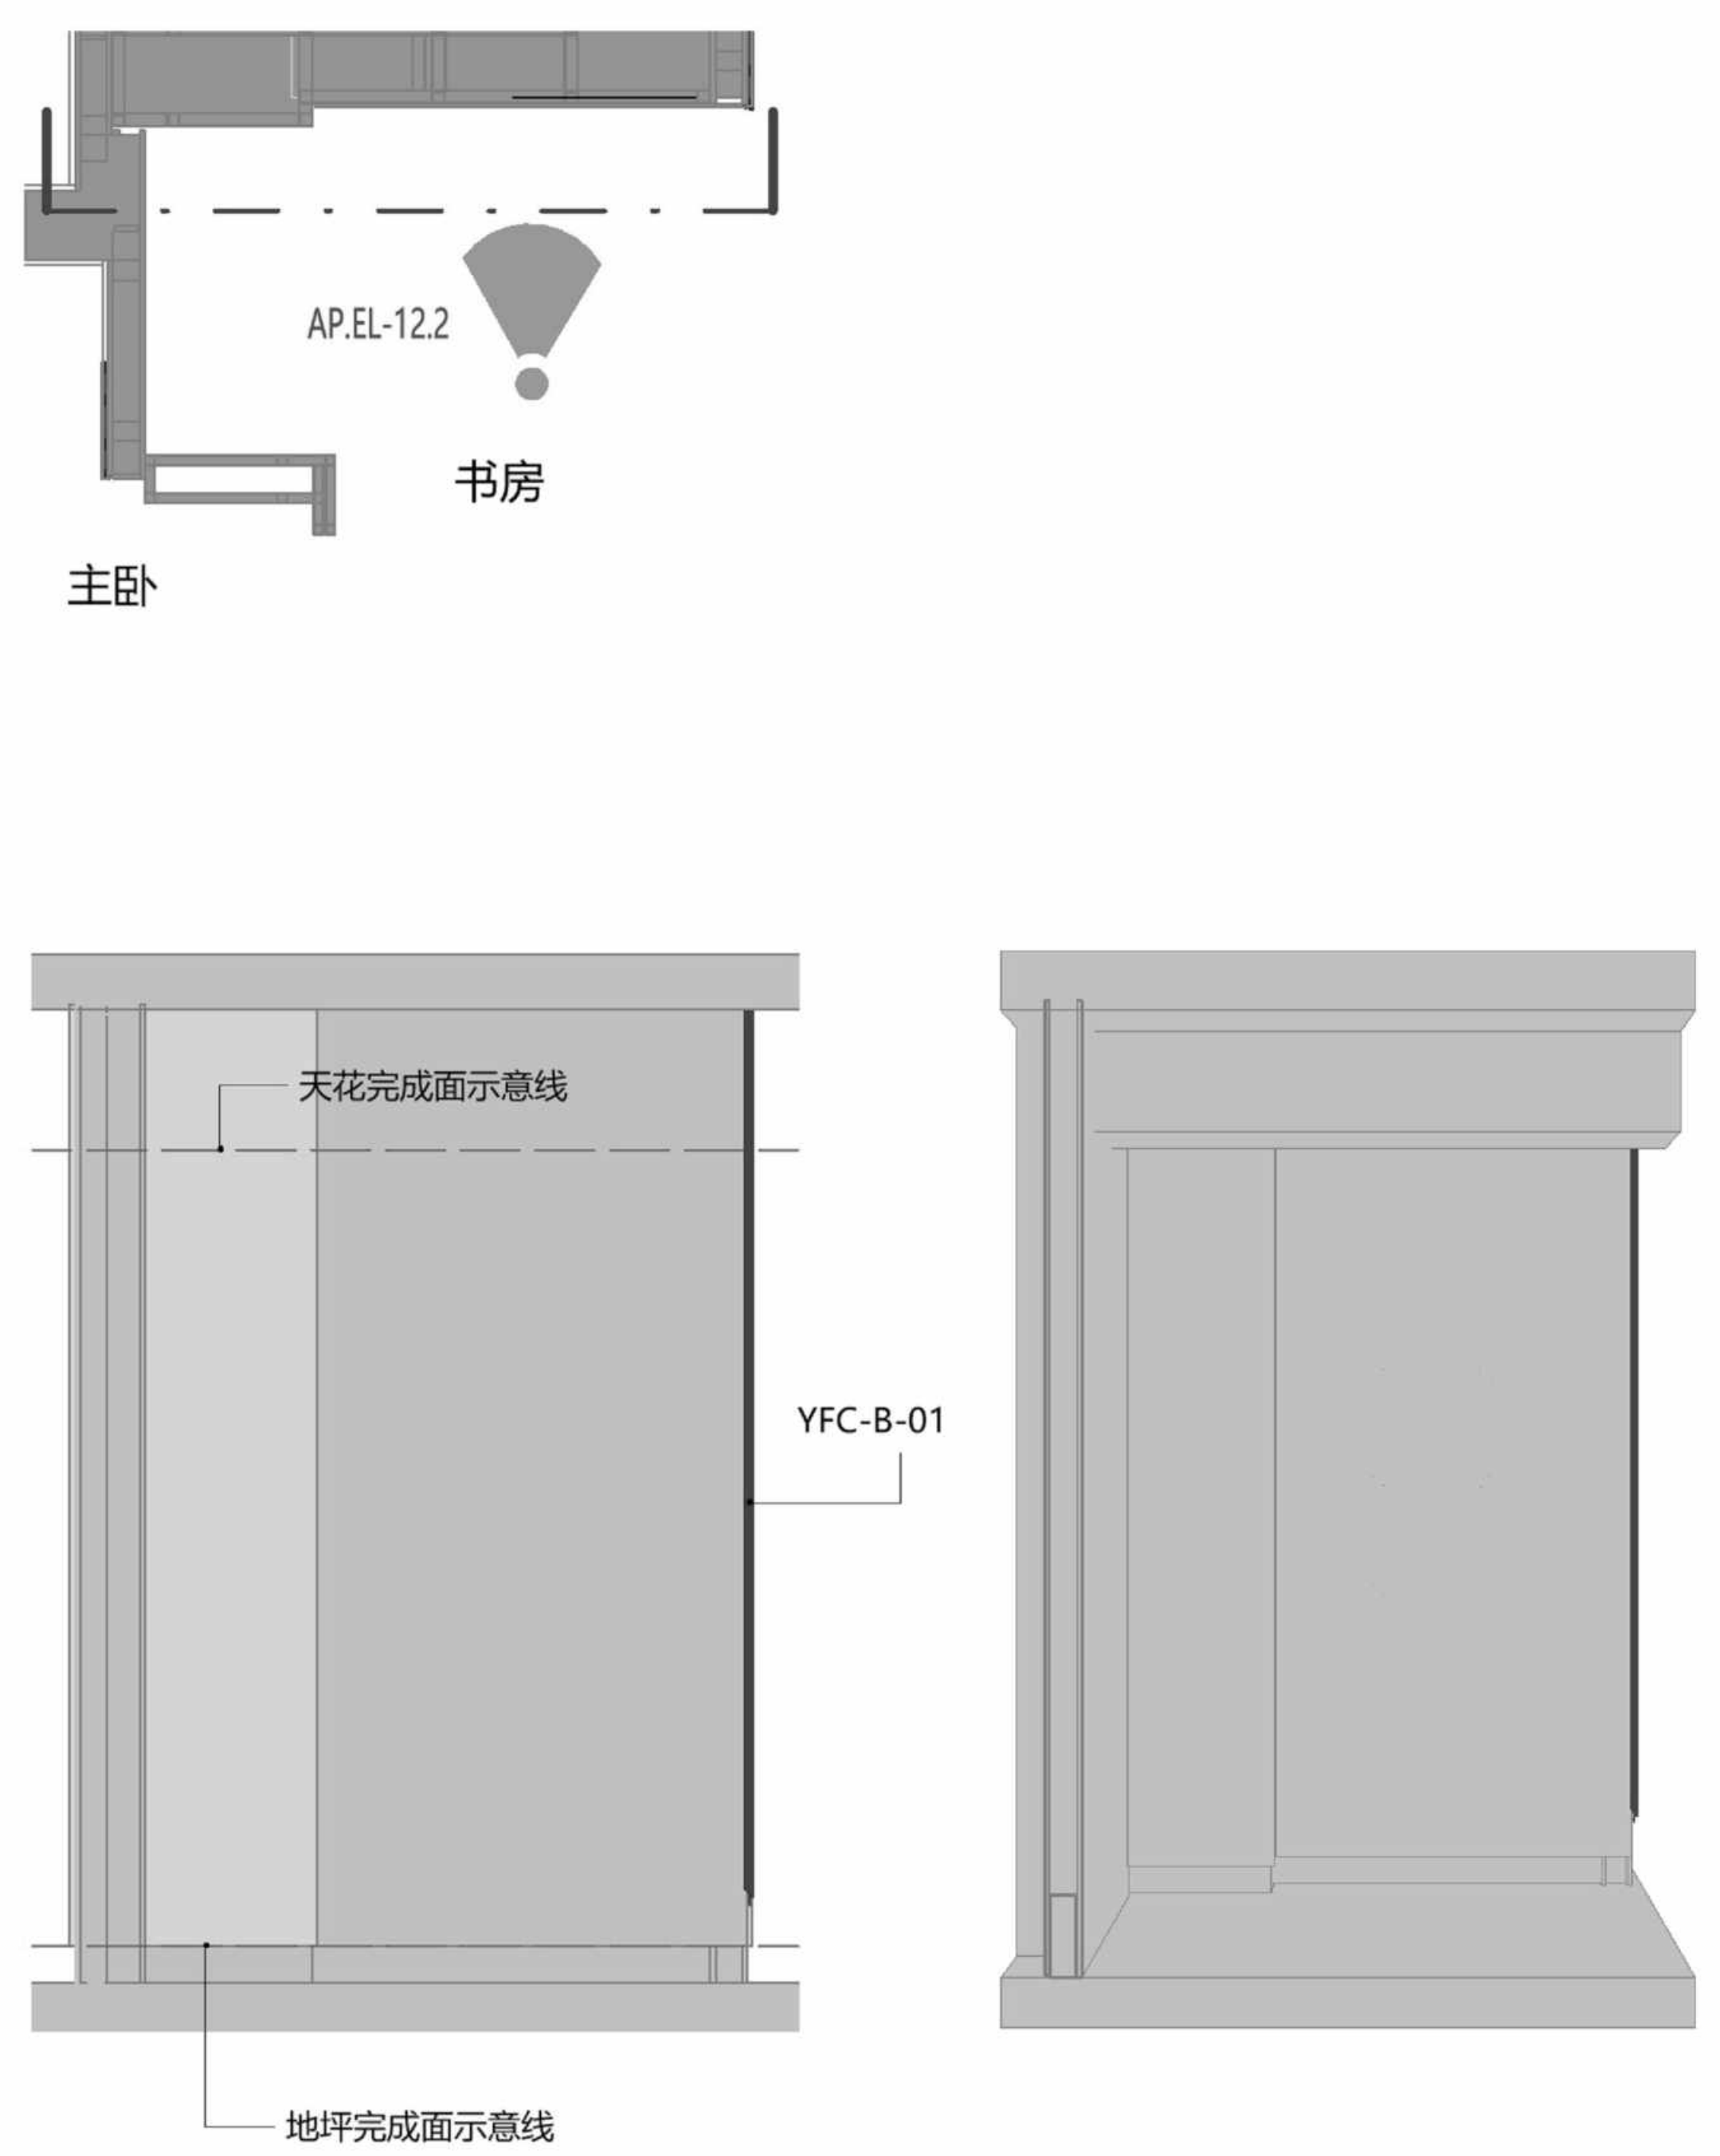
AP.EL-12.2
书房
主卧
天花完成面示意线
YFC-B-01
地坪完成面示意线

2

书房 墙面及踢脚铝型材立面图2

Scale比例 1 : 30@A2

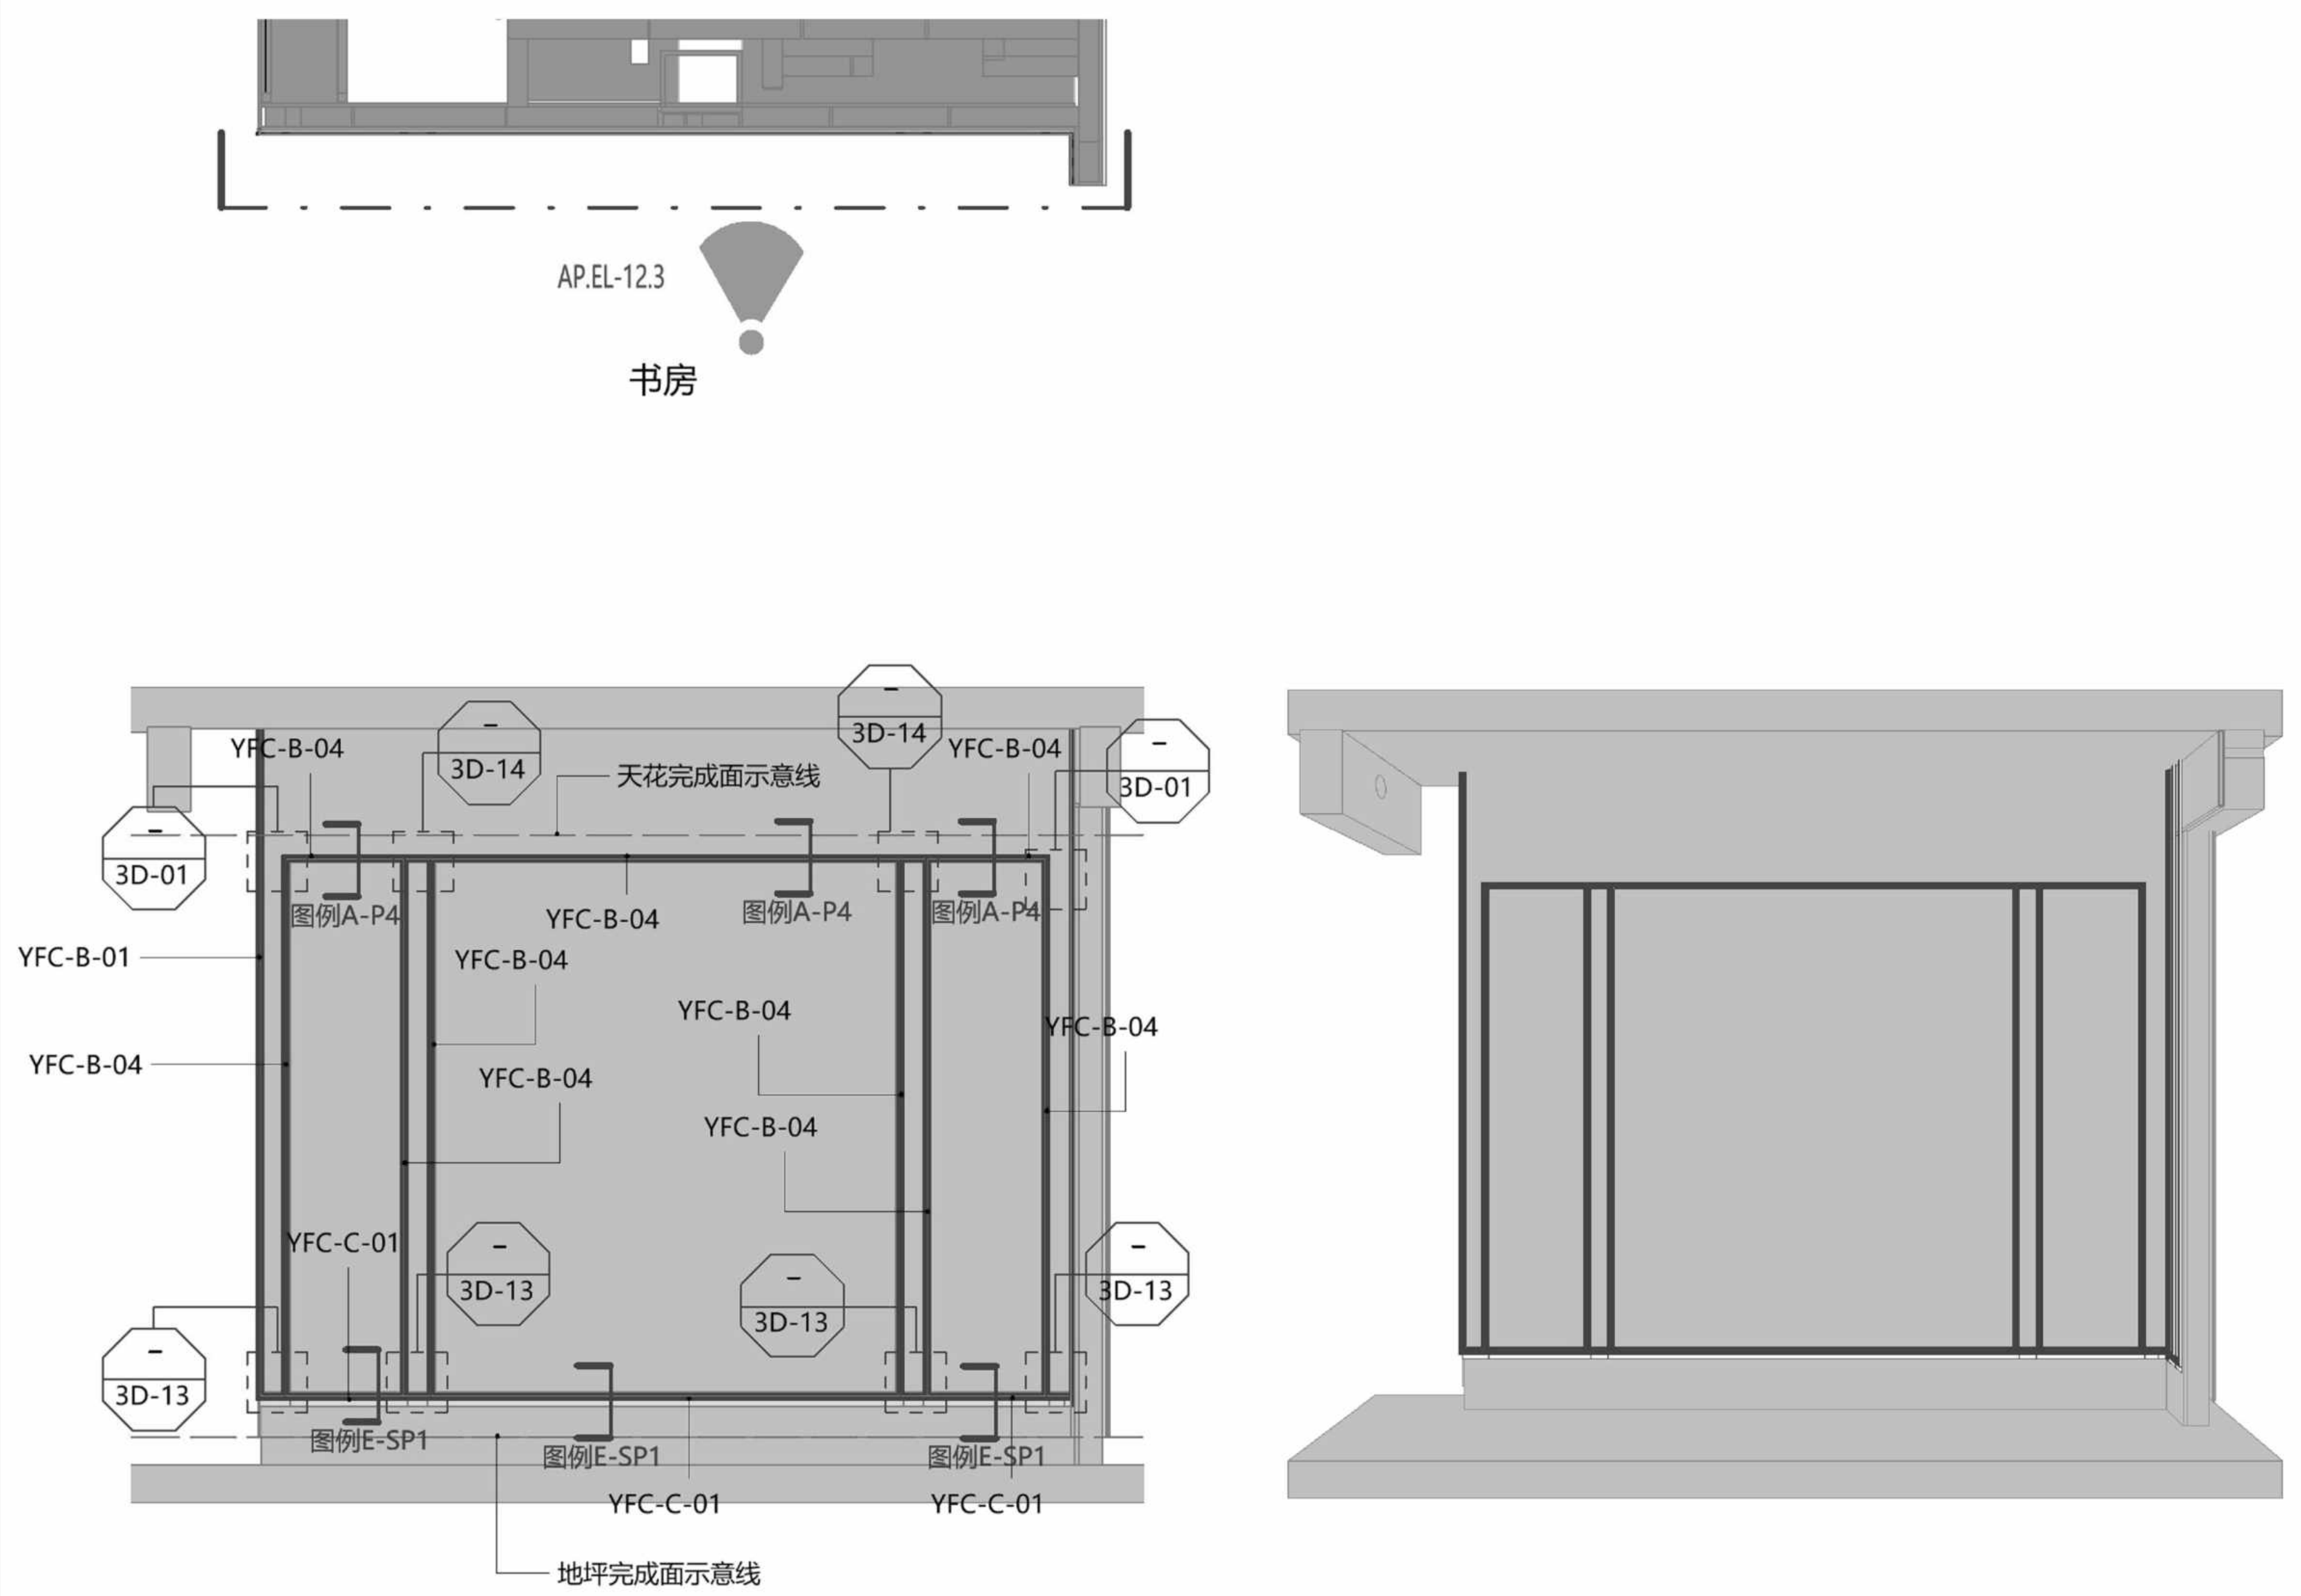
AP.EL-12.3
书房
YFC-B-04
3D-14
天花完成面示意线
3D-14
YFC-B-04
3D-01
3D-01
图例A-P4
图例A-P4
图例A-P4
YFC-B-04
YFC-B-01
YFC-B-04
YFC-B-04
YFC-B-04
YFC-B-04
YFC-B-04
YFC-B-04
YFC-C-01
3D-13
3D-13
3D-13
3D-13
图例E-SP1
图例E-SP1
图例E-SP1
YFC-C-01
YFC-C-01
地坪完成面示意线

3

书房 墙面及踢脚铝型材立面图3

Scale比例 1 : 30@A2

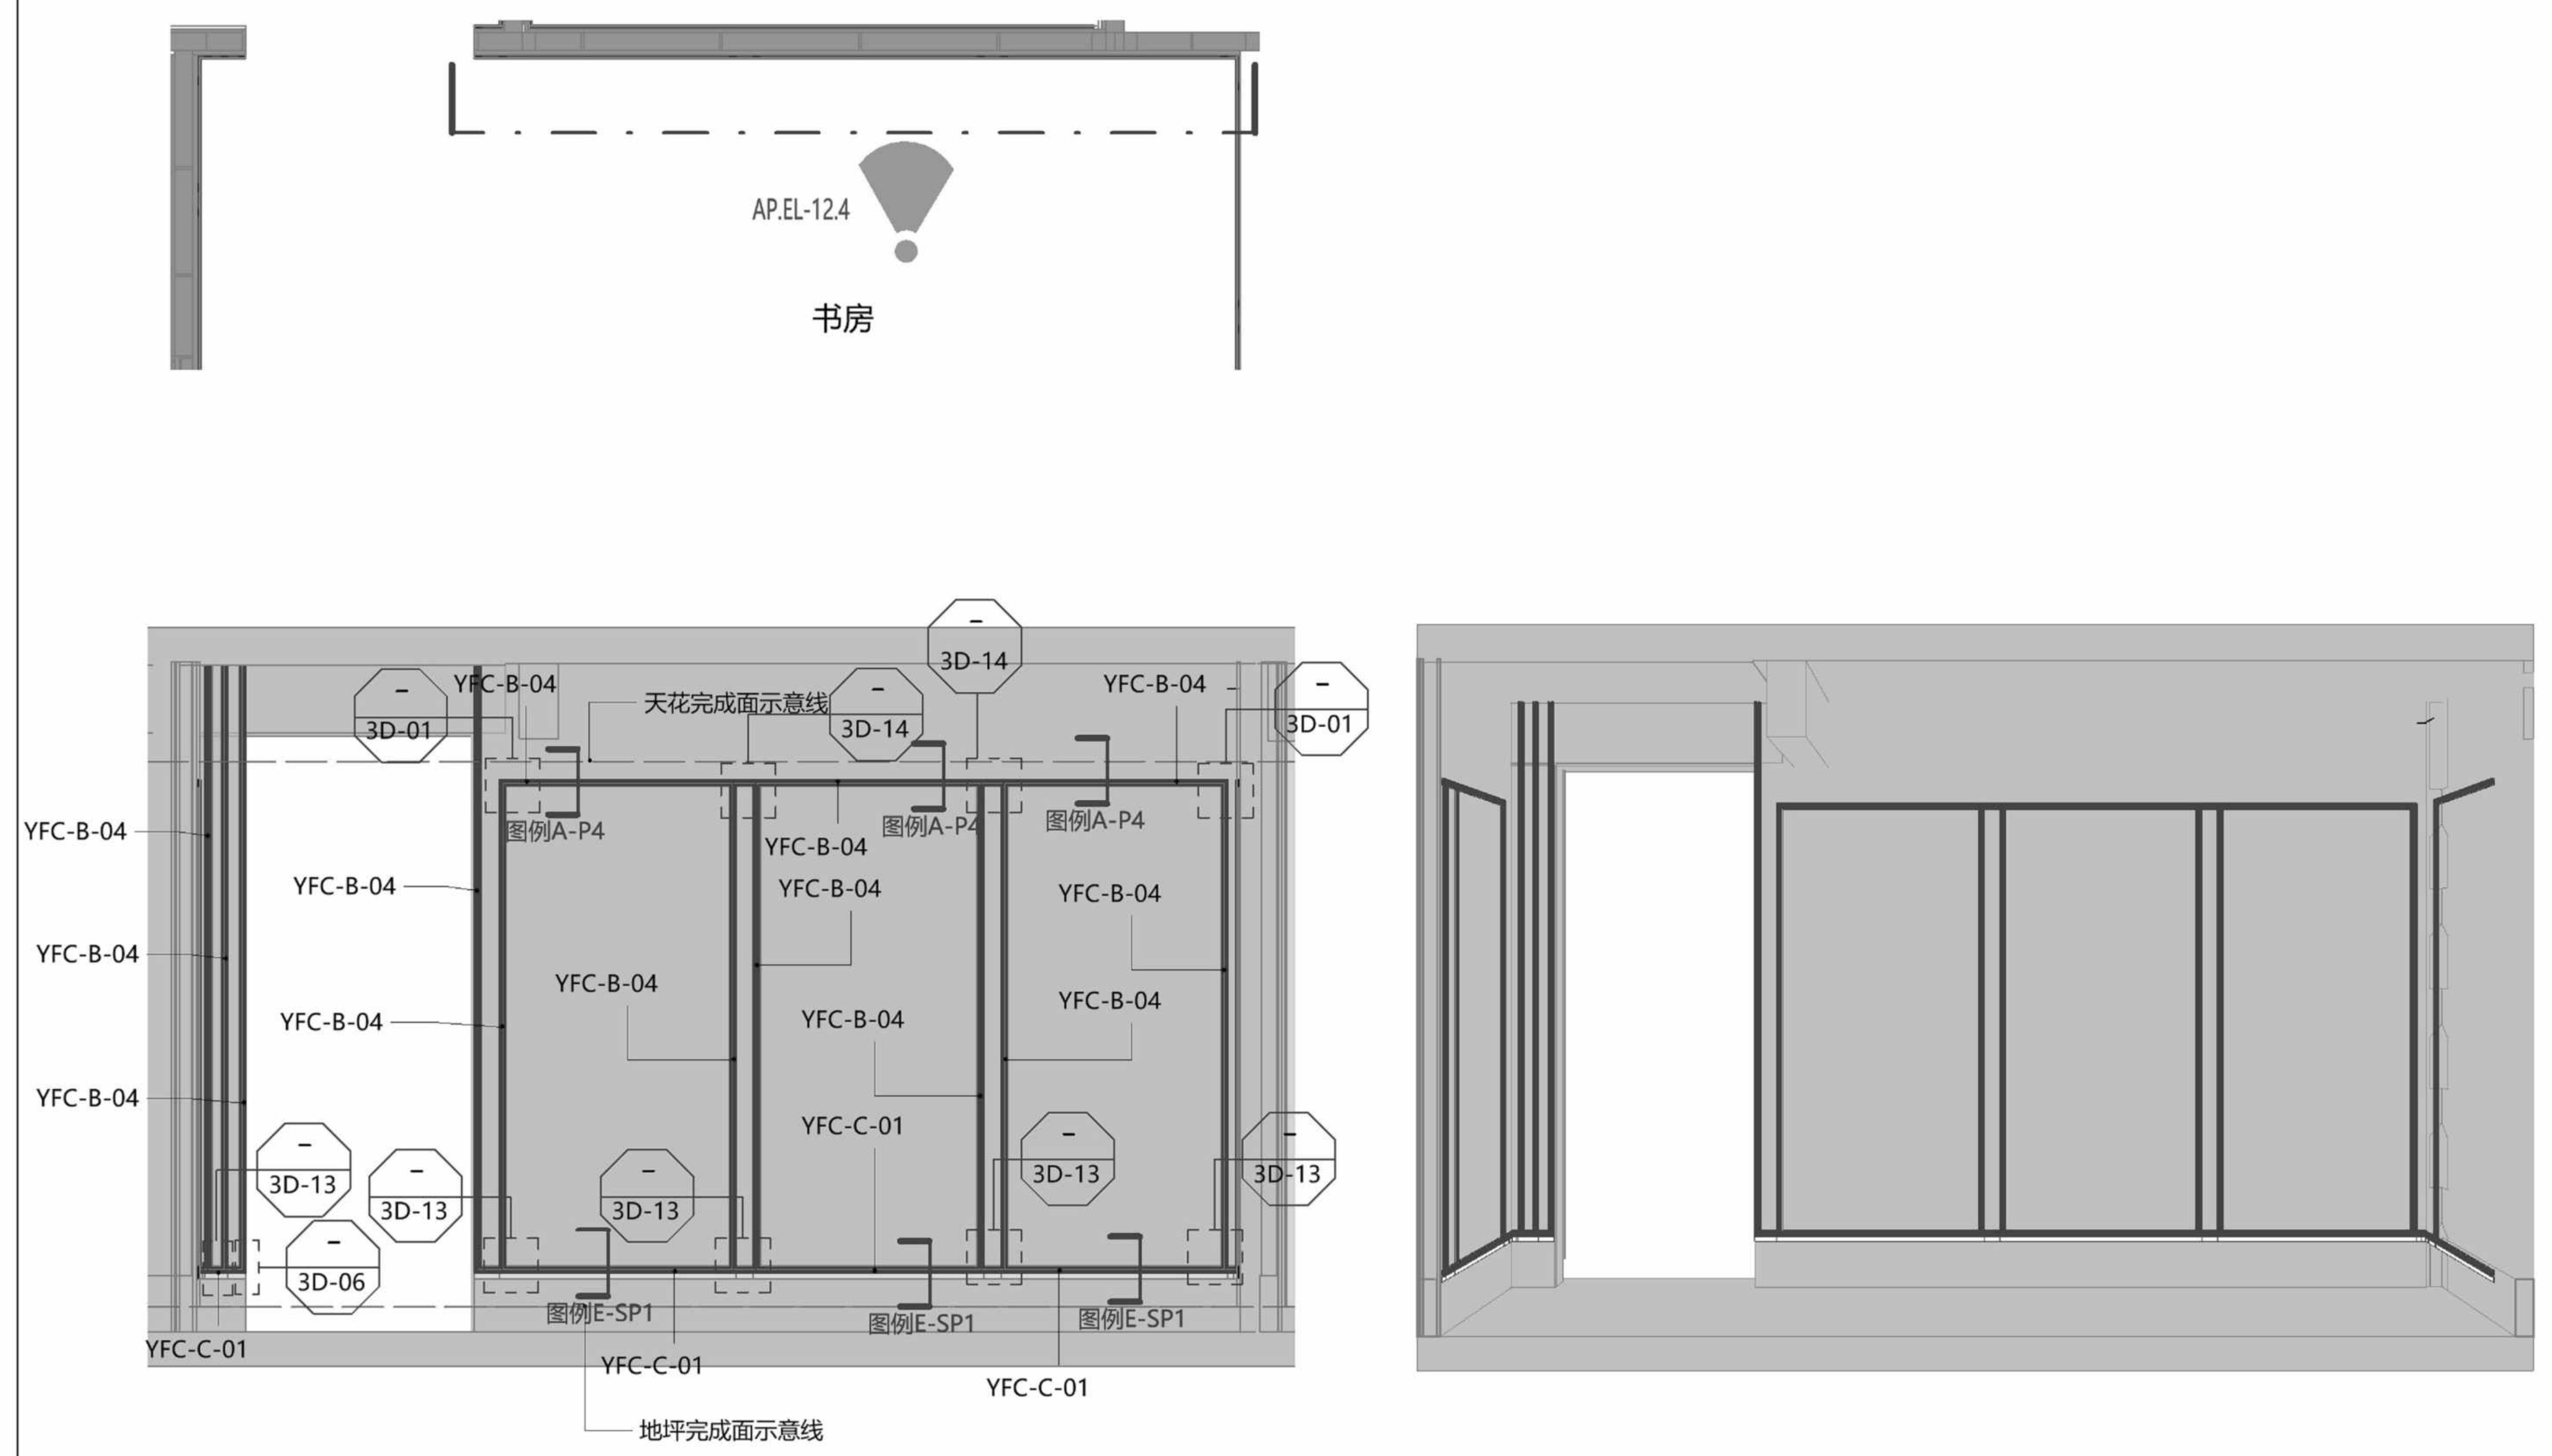
AP.EL-12.4
书房
YFC-B-04
3D-01
天花完成面示意线
3D-14
3D-14
YFC-B-04
3D-01
图例A-P4
图例A-P4
图例A-P4
YFC-B-04
YFC-B-04
YFC-B-04
YFC-B-04
YFC-B-04
YFC-B-04
YFC-B-04
YFC-B-04
YFC-B-04
YFC-C-01
3D-13
3D-13
3D-13
3D-13
3D-13
3D-06
图例E-SP1
图例E-SP1
图例E-SP1
YFC-C-01
YFC-C-01
YFC-C-01
地坪完成面示意线

4

书房 墙面及踢脚铝型材立面图4

Scale比例 1 : 30@A2

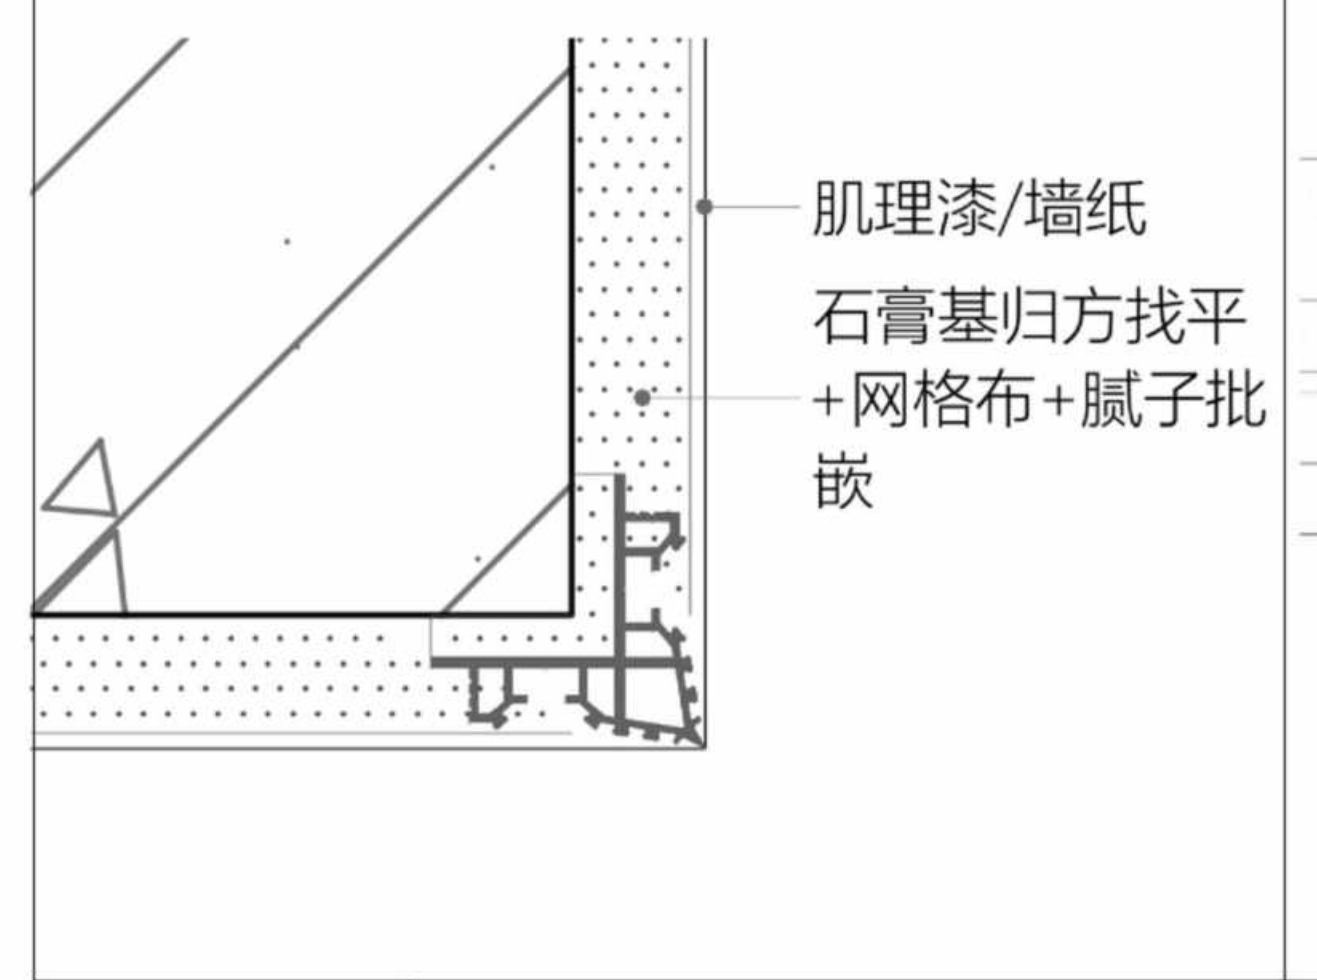
肌理漆/墙纸
石膏基归方找平+网格布+腻子批嵌

图例A-P1

墙面-石膏基找平铝型材

Scale比例 1：1@A2

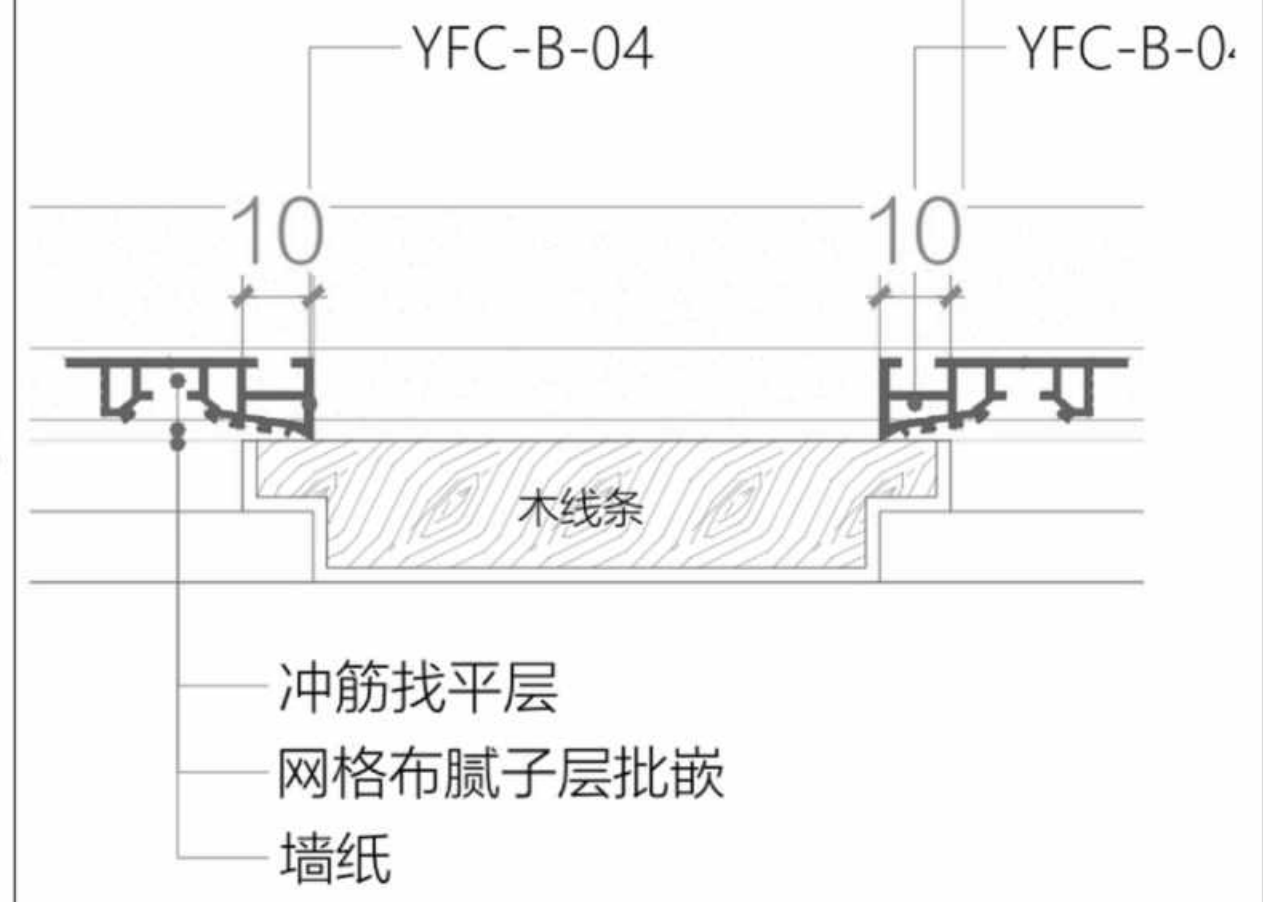
YFC-B-04
YFC-B-0
10
10
木线条
冲筋找平层
网格布腻子层批嵌
墙纸

图例A-P4

墙面-石膏基找平铝型材

Scale比例 1：1@A2

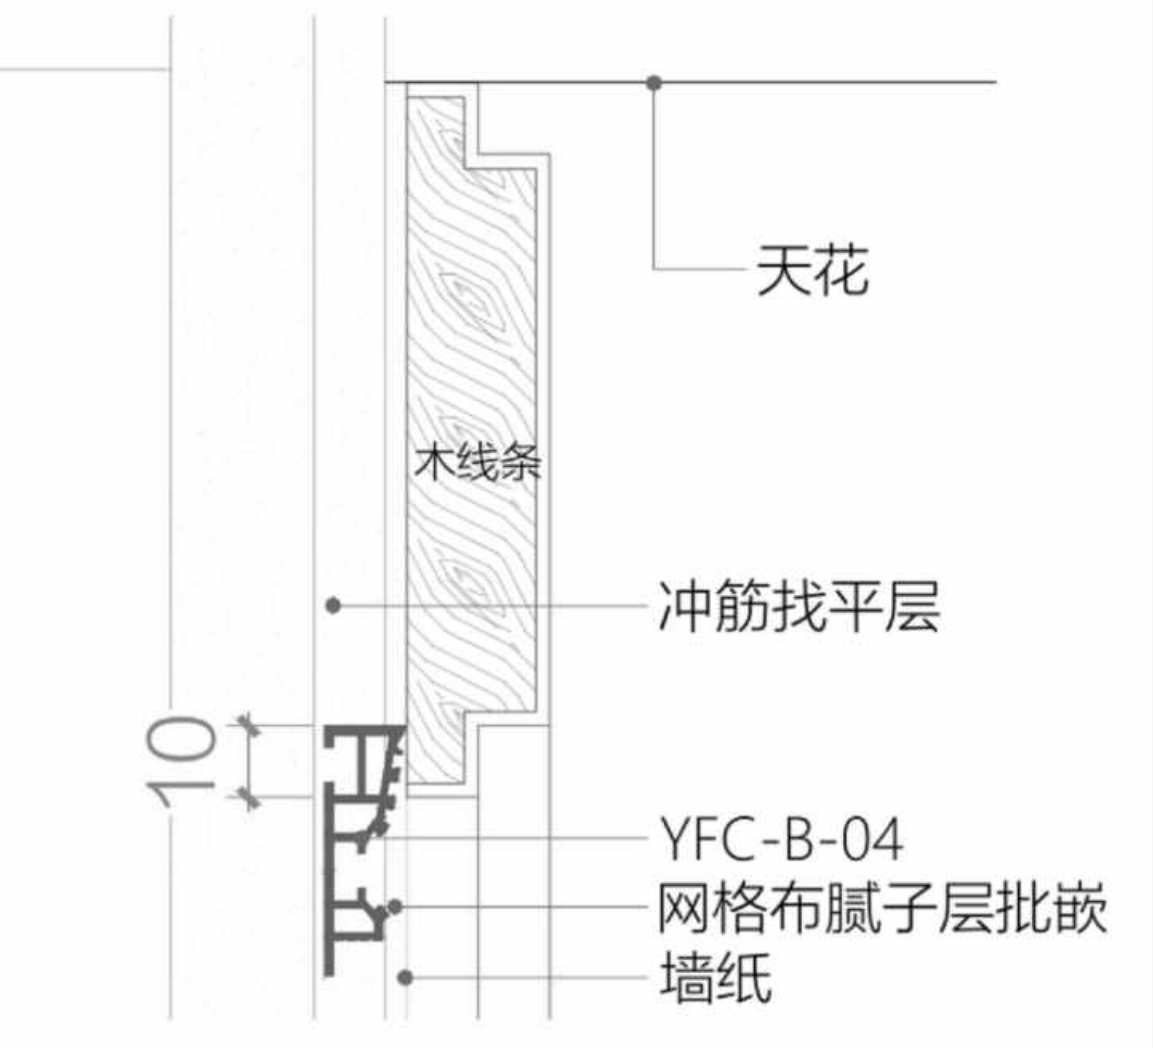
天花
木线条
冲筋找平层
10
YFC-B-04
网格布腻子层批嵌
墙纸

图例A-P5

墙面-石膏基找平铝型材

Scale比例 1：1@A2

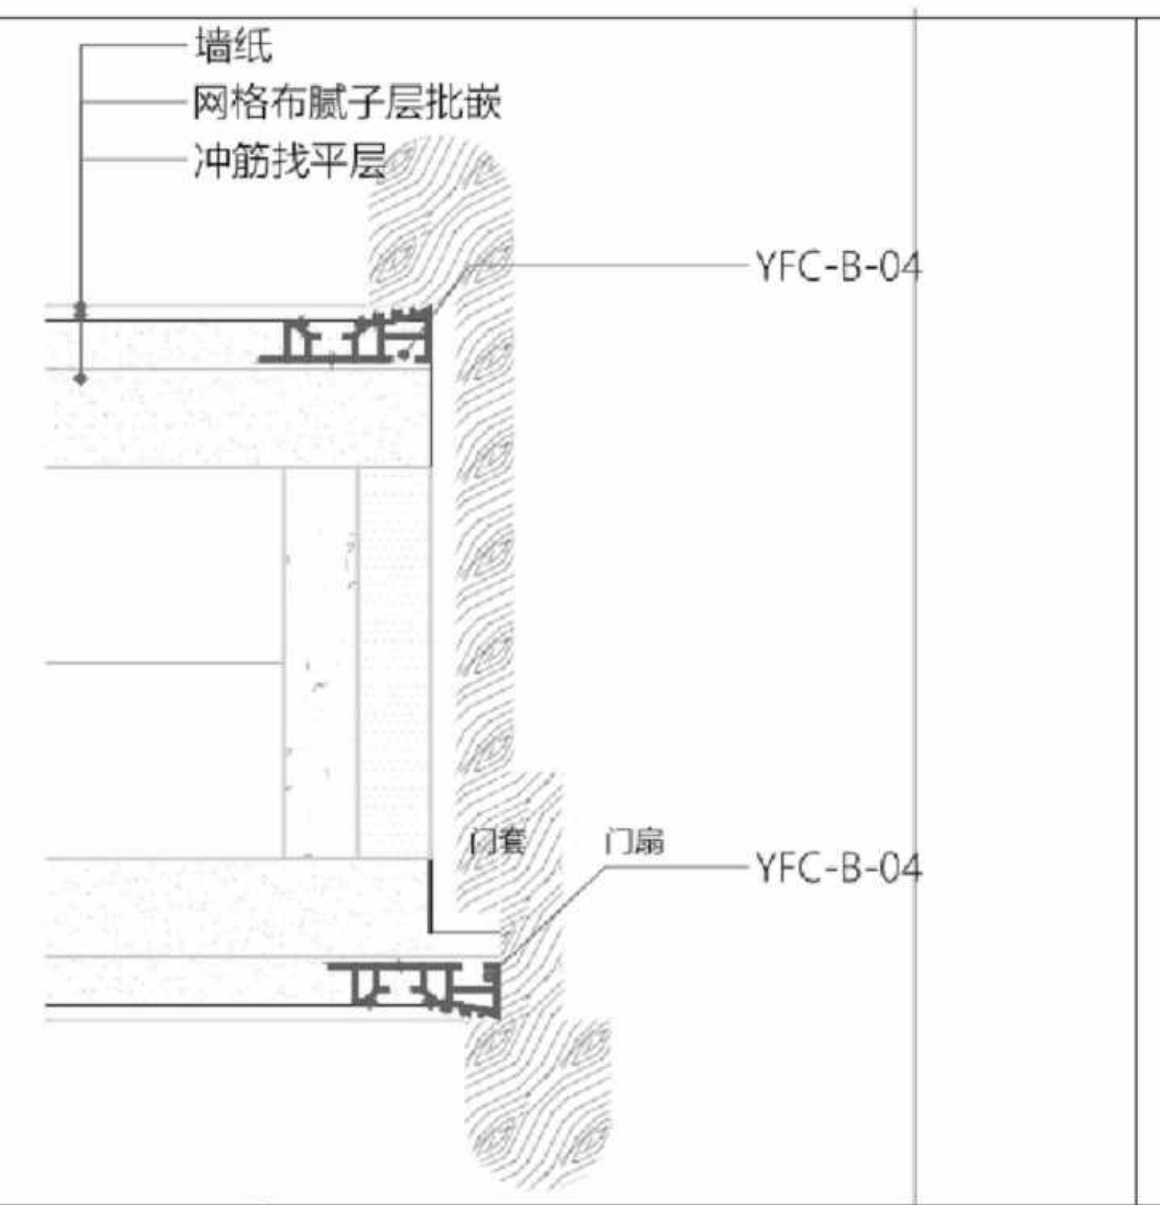
墙纸
网格布腻子层批嵌
冲筋找平层
YFC-B-04
门套
门扇
YFC-B-04

图例D-M1

门边-石膏基找平铝型材

Scale比例 1：1@A2

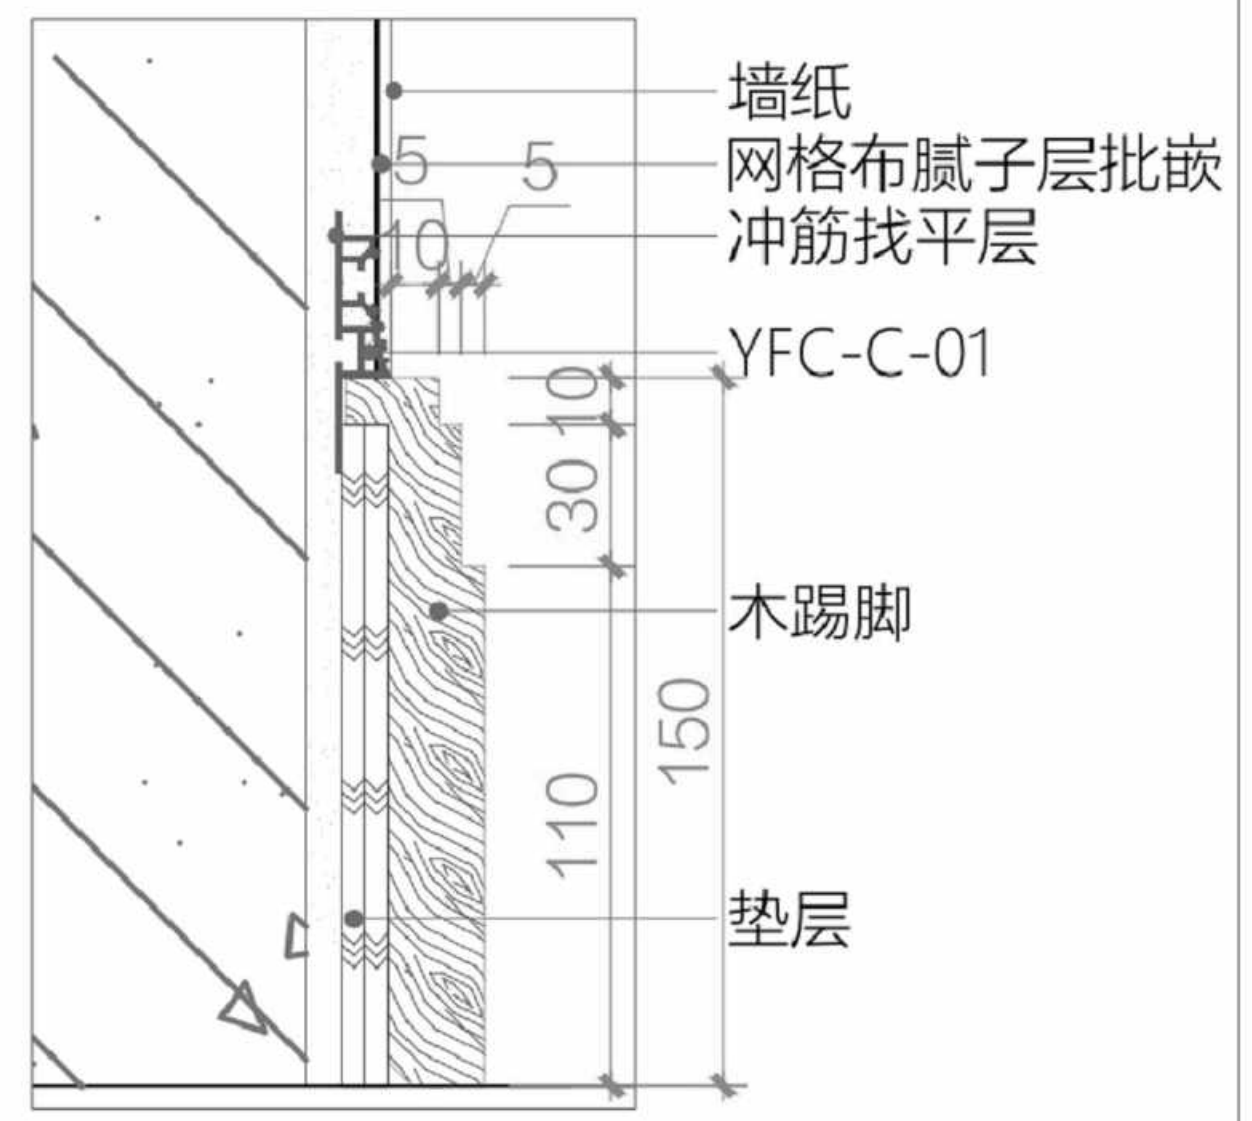
墙纸
网格布腻子层批嵌
冲筋找平层
5
5
10
YFC-C-01
10
30
木踢脚
150
110
垫层

图例E-SP1

踢脚-石膏基找平铝型材

Scale比例 1：1@A2

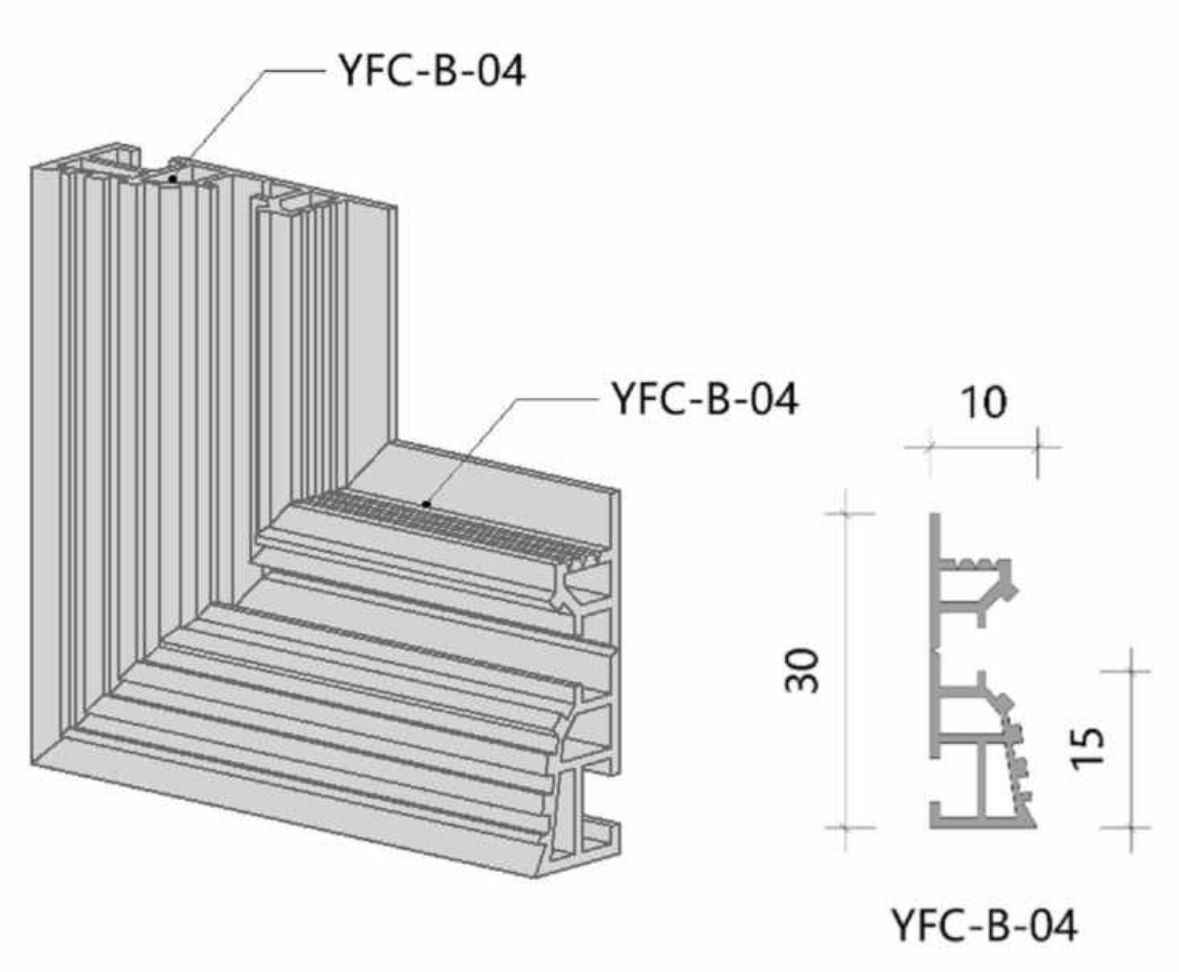
YFC-B-04
YFC-B-04
10
30
15
YFC-B-04

3D-01

转角铝型材-拼接跟通

转角数量：6

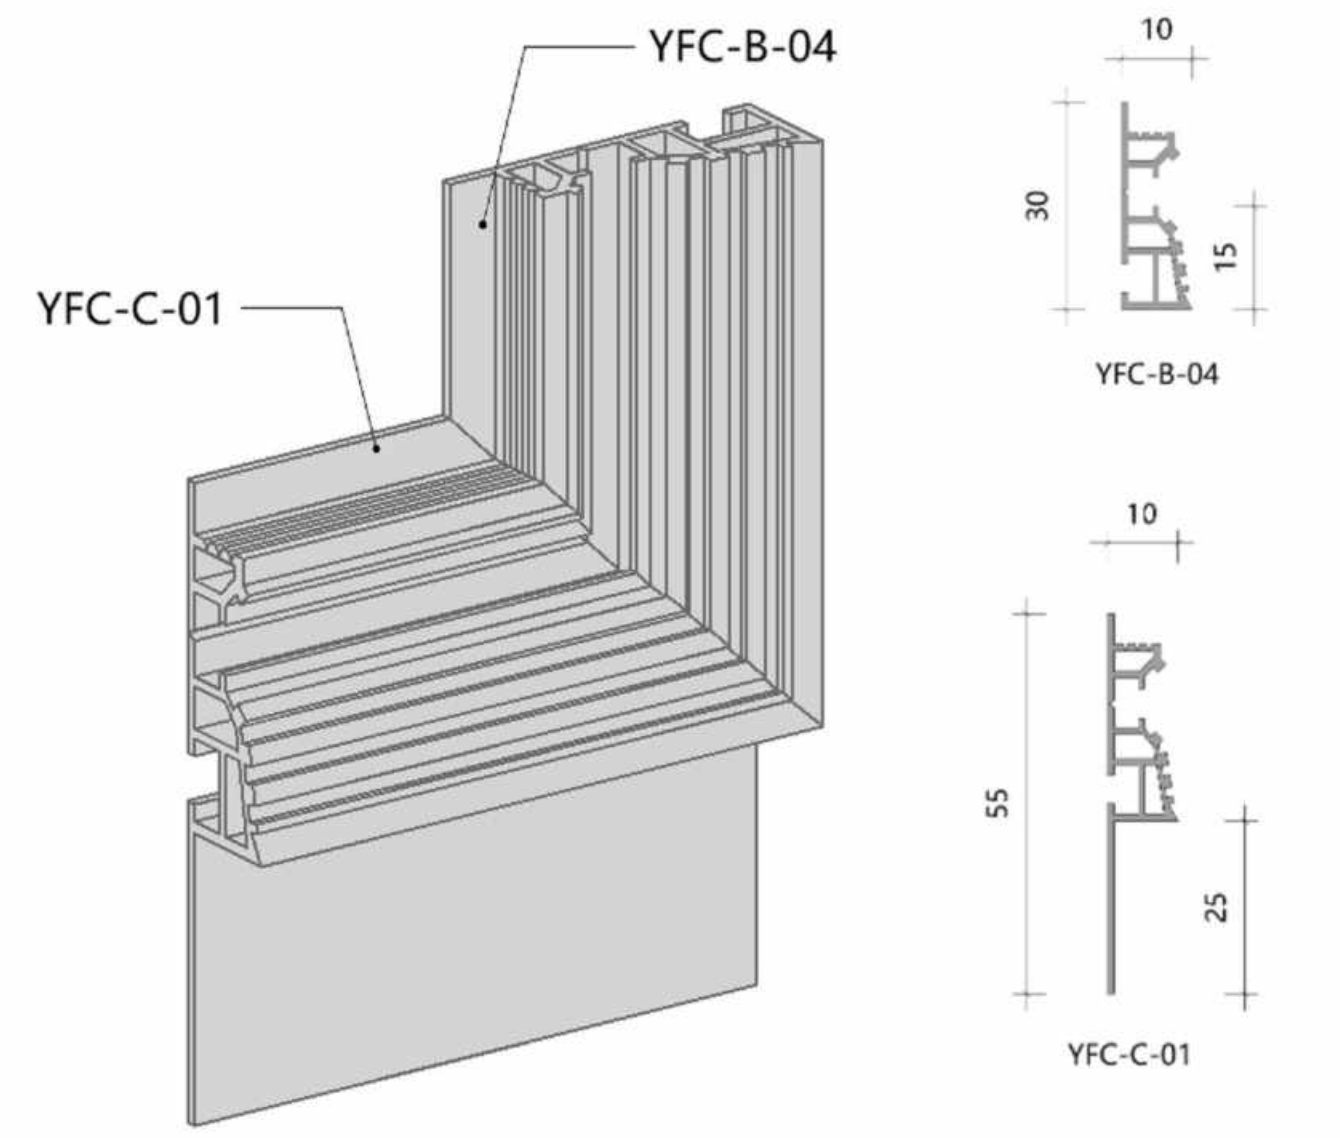
YFC-B-04
YFC-C-01
10
30
15
YFC-B-04
10
55
25
YFC-C-01

3D-06

转角铝型材-拼接跟通

转角数量：2

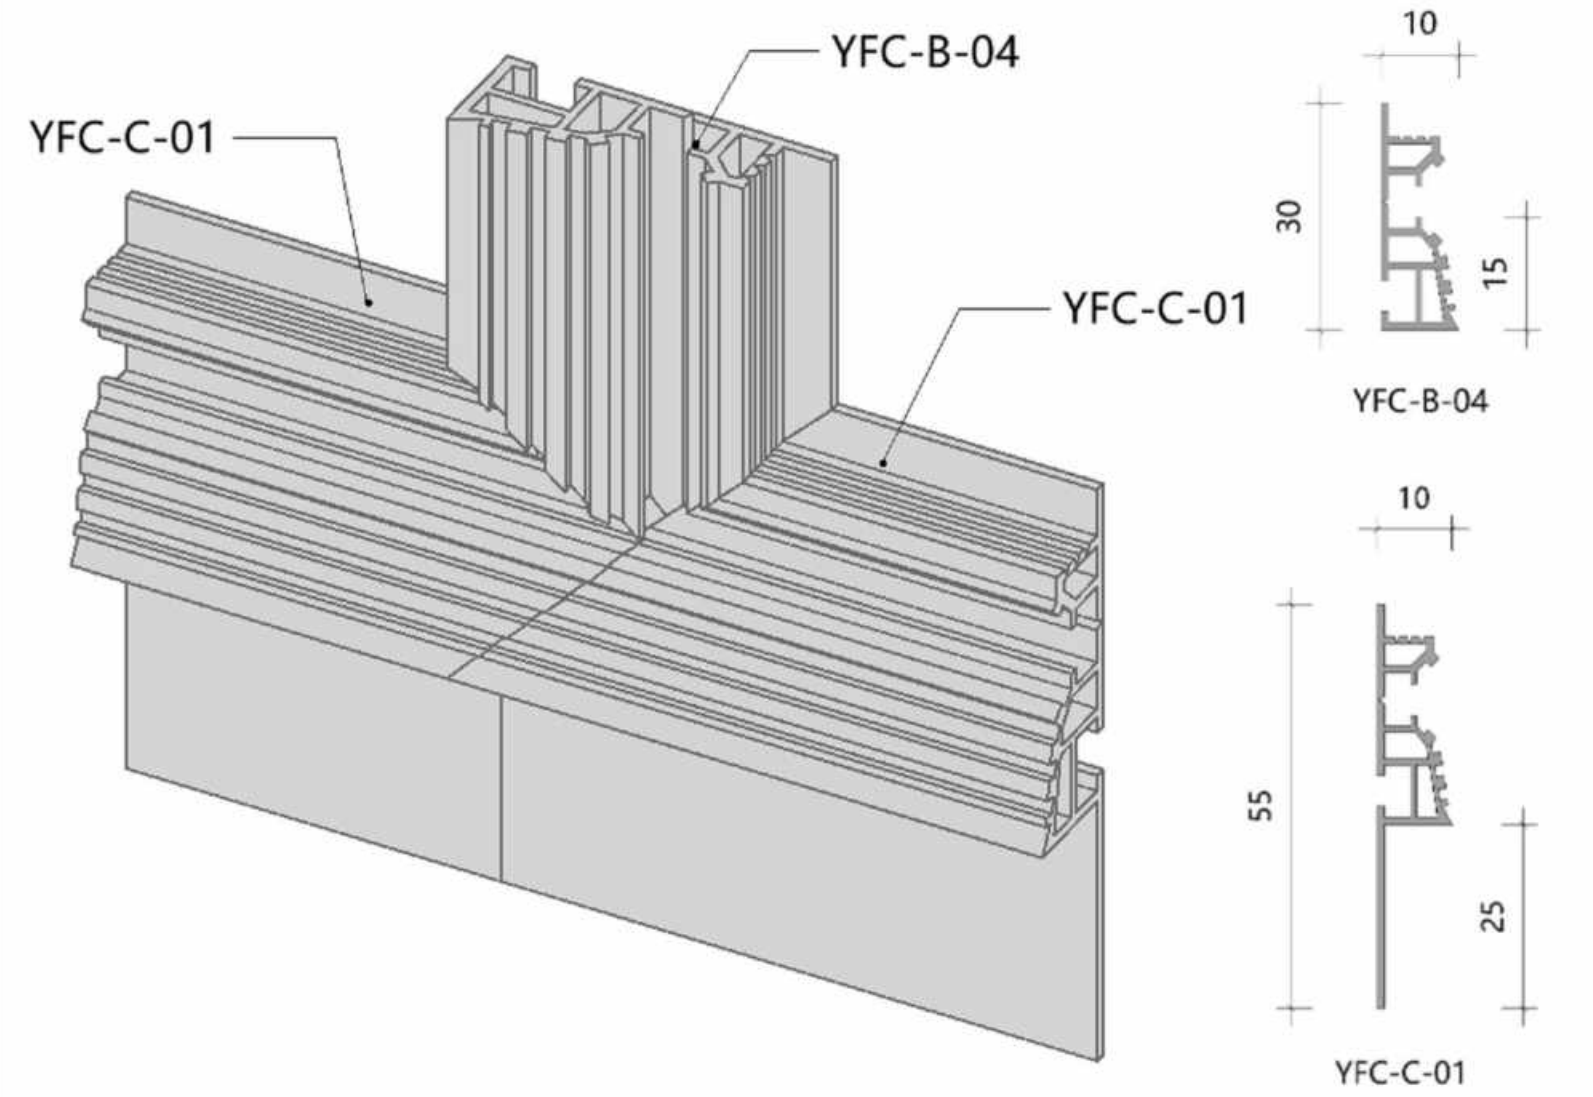
YFC-B-04
YFC-C-01
YFC-C-01
10
30
15
YFC-B-04
10
55
25
YFC-C-01

3D-13

转角铝型材-拼接跟通

转角数量：14

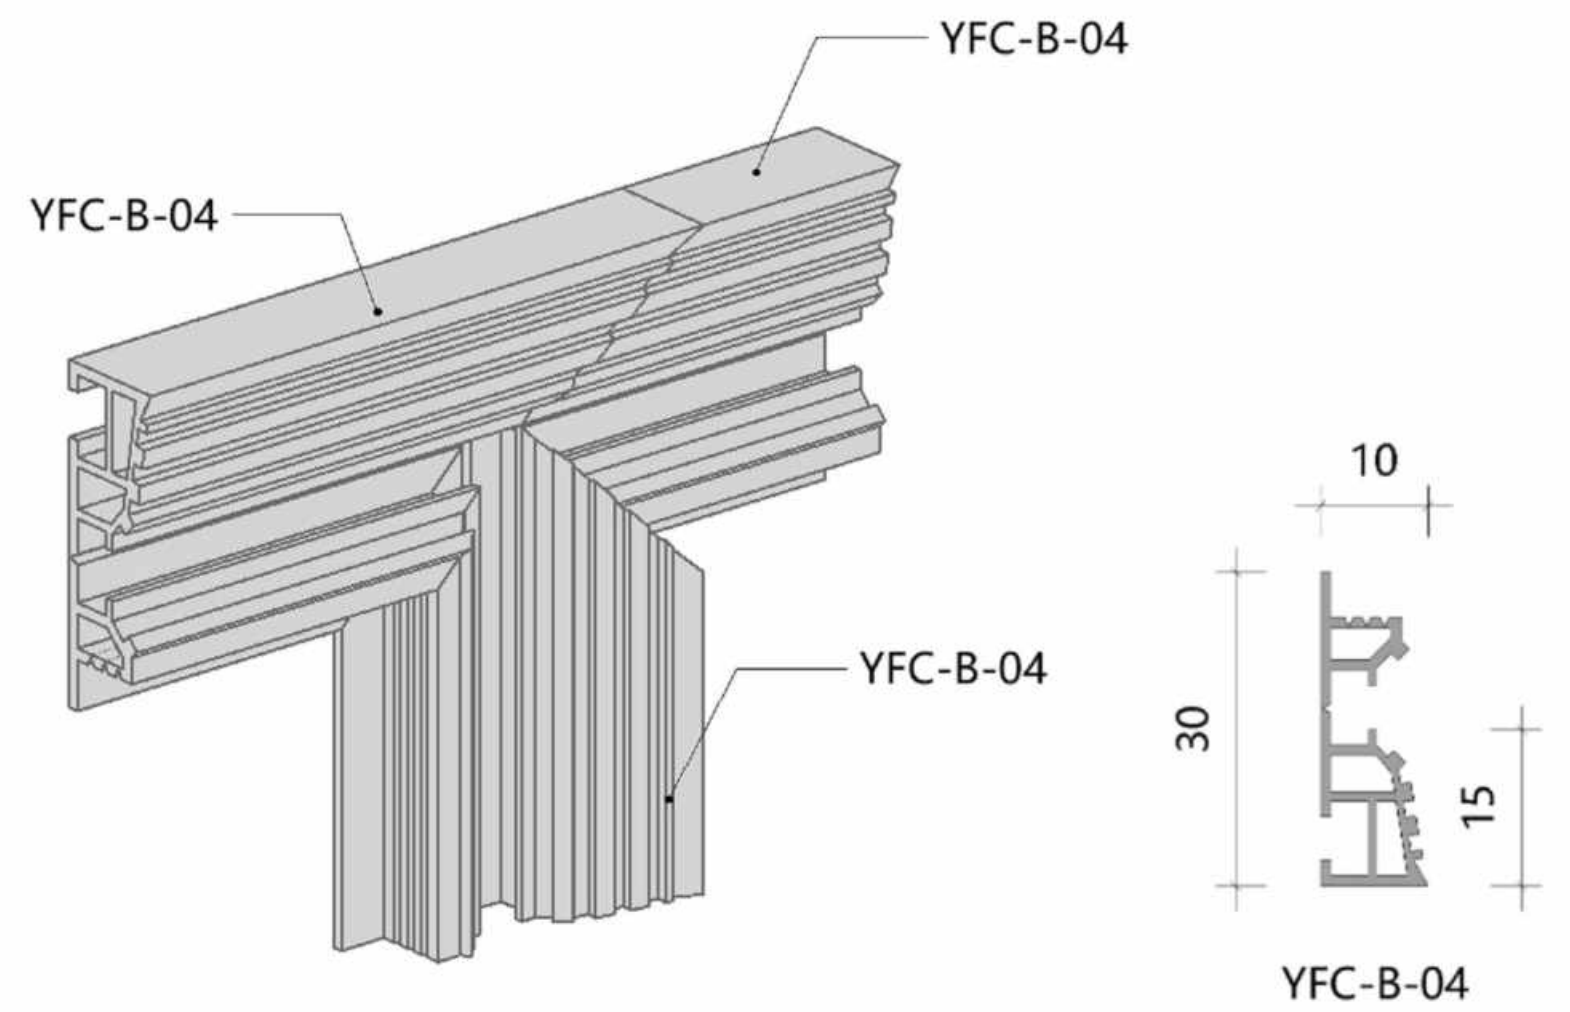
YFC-B-04
YFC-B-04
YFC-B-04
10
30
15
YFC-B-04

3D-14

转角铝型材-拼接跟通

转角数量：5

盖章

注释
Notes

1.本图纸如与现场尺寸有误，请施工人员与项目负责人联系。
2.施工前施工人员应认真查阅此图，如有不明确尺寸，按现场测量为准。
3.本图纸必须经甲乙双方认可并签字方可作为施工依据。

日期
Date 03/04/26

修订
Revision

△1

项目
Project
潮映华岸府3-801

比例
Scale 1：30@A2

书房

墙面及踢脚铝型材

图纸编号
Drawing No.
AP.EL-12

项目编号
Project No.

©2025

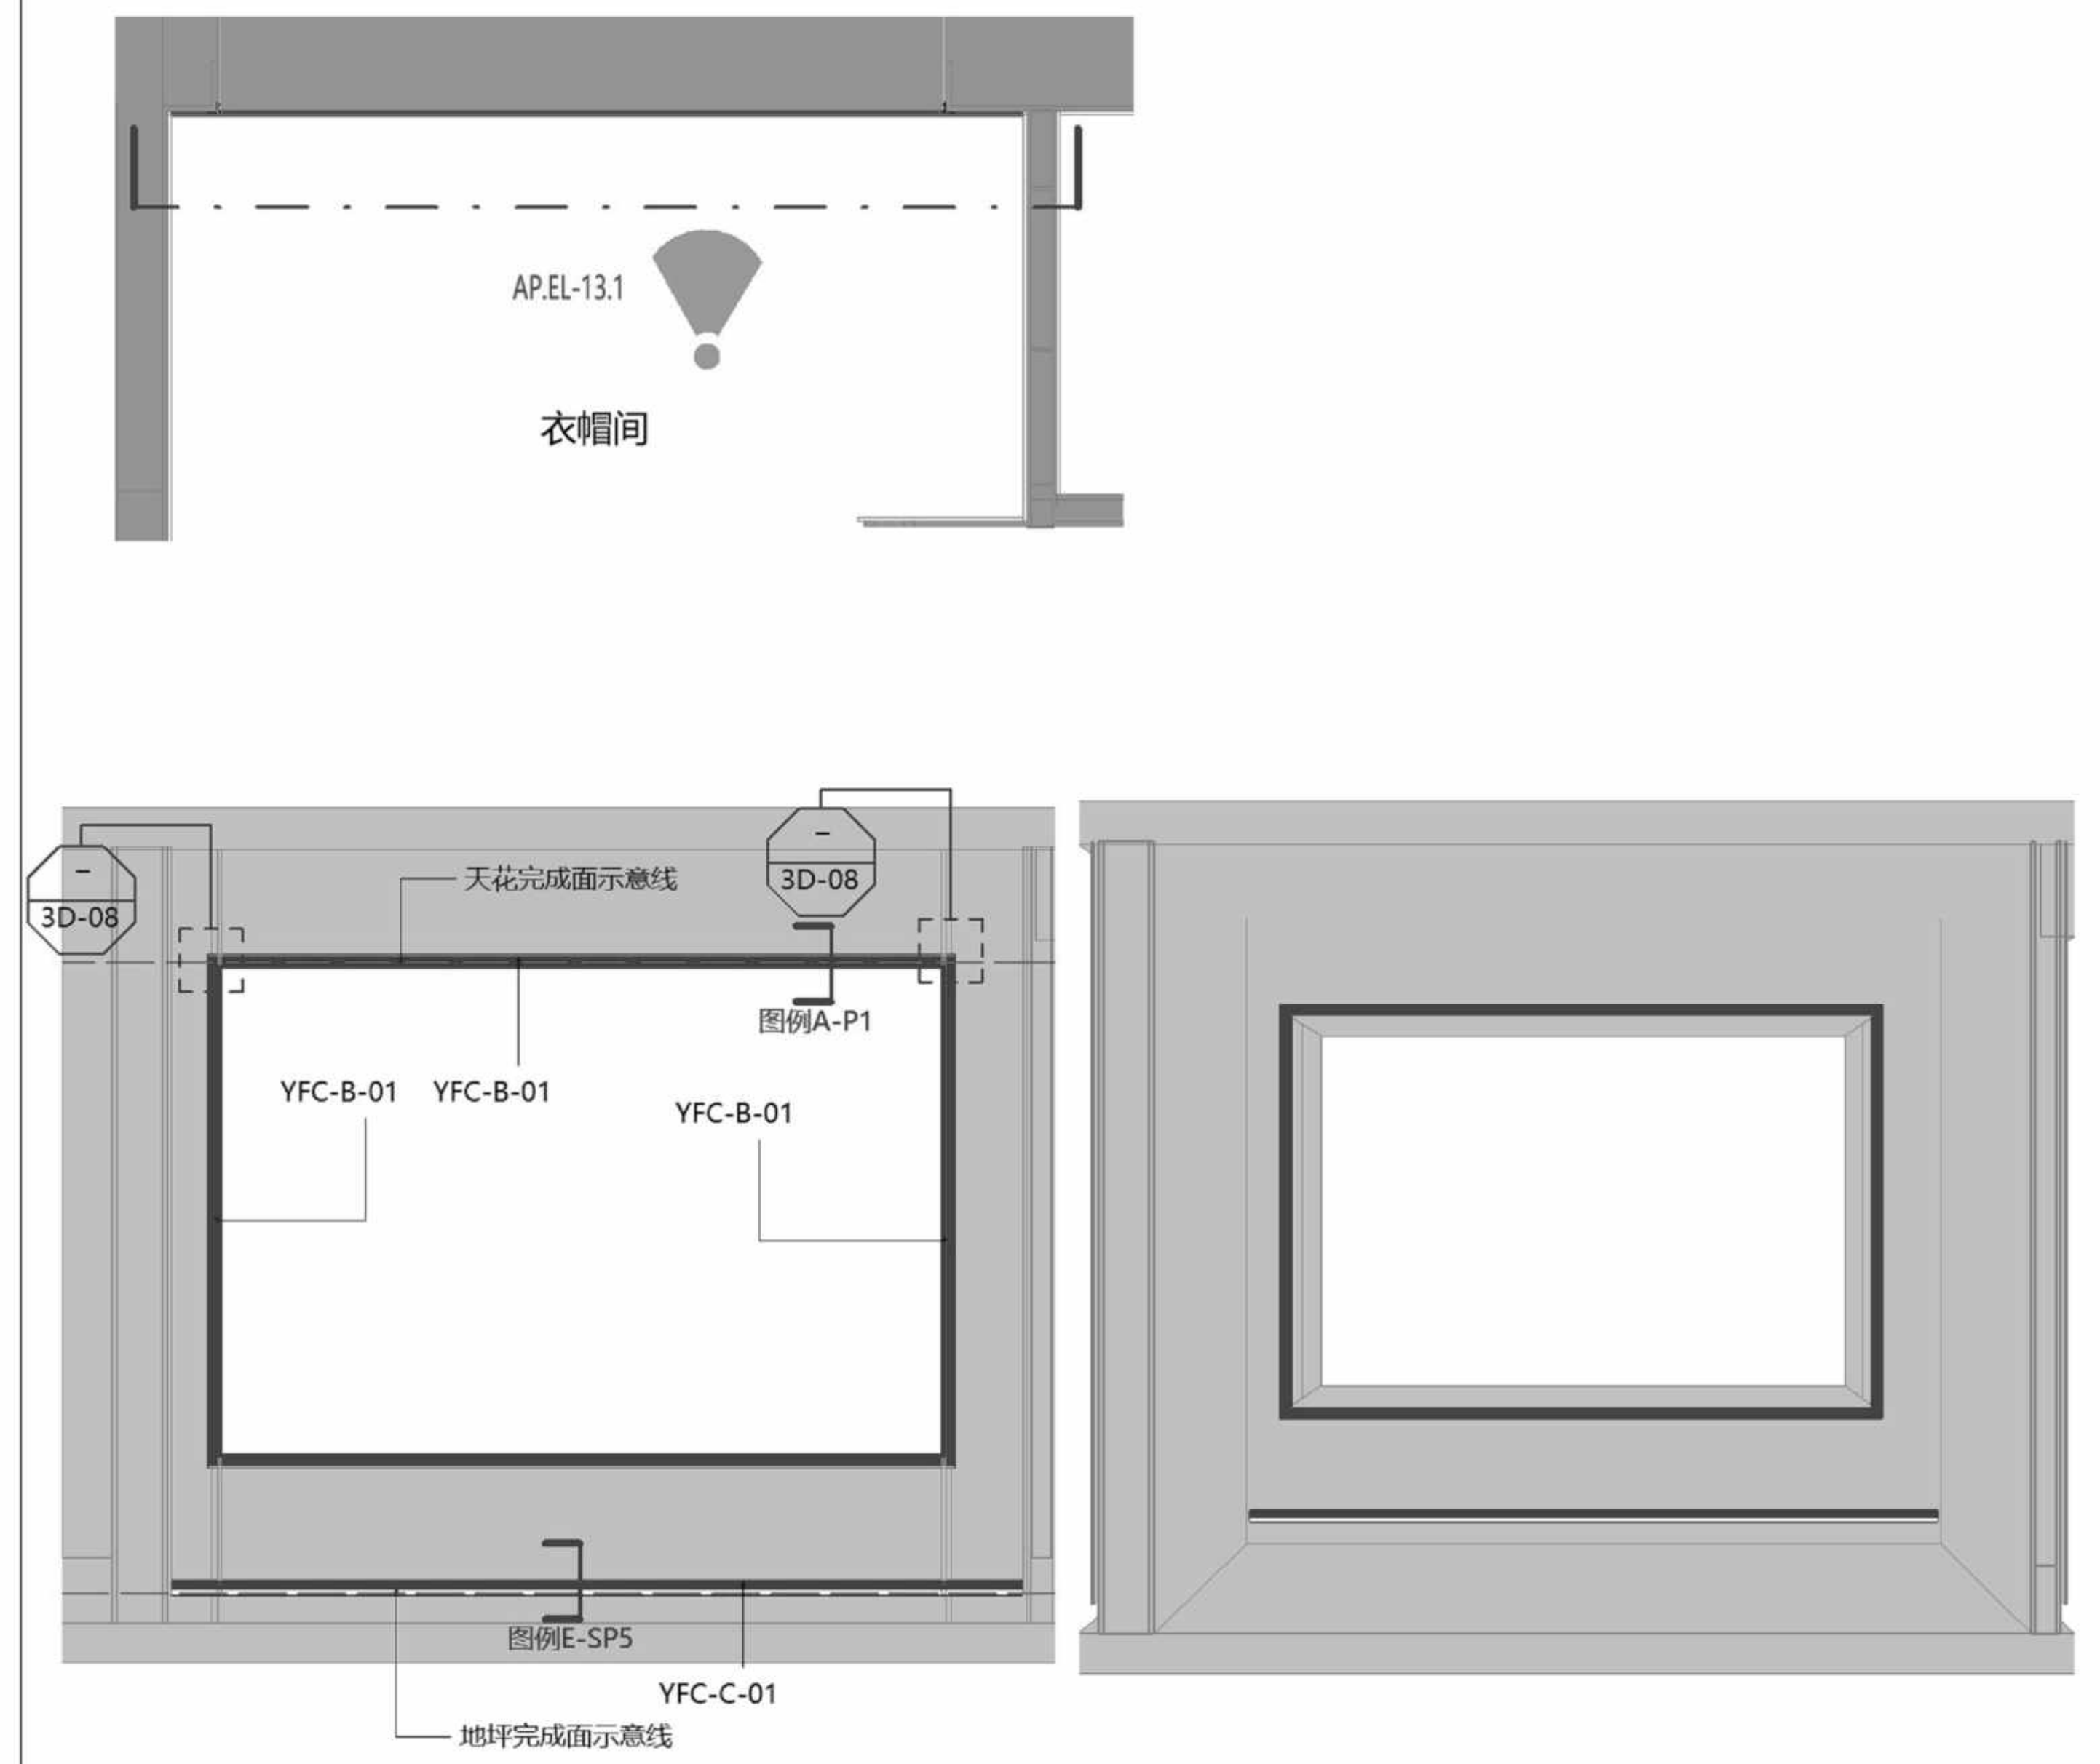
AP.EL-13.1
衣帽间
3D-08
天花完成面示意线
3D-08
图例A-P1
YFC-B-01
YFC-B-01
YFC-B-01
图例E-SP5
YFC-C-01
地坪完成面示意线

1
衣帽间 墙面及踢脚铝型材立面图1
Scale比例 1：30@A2

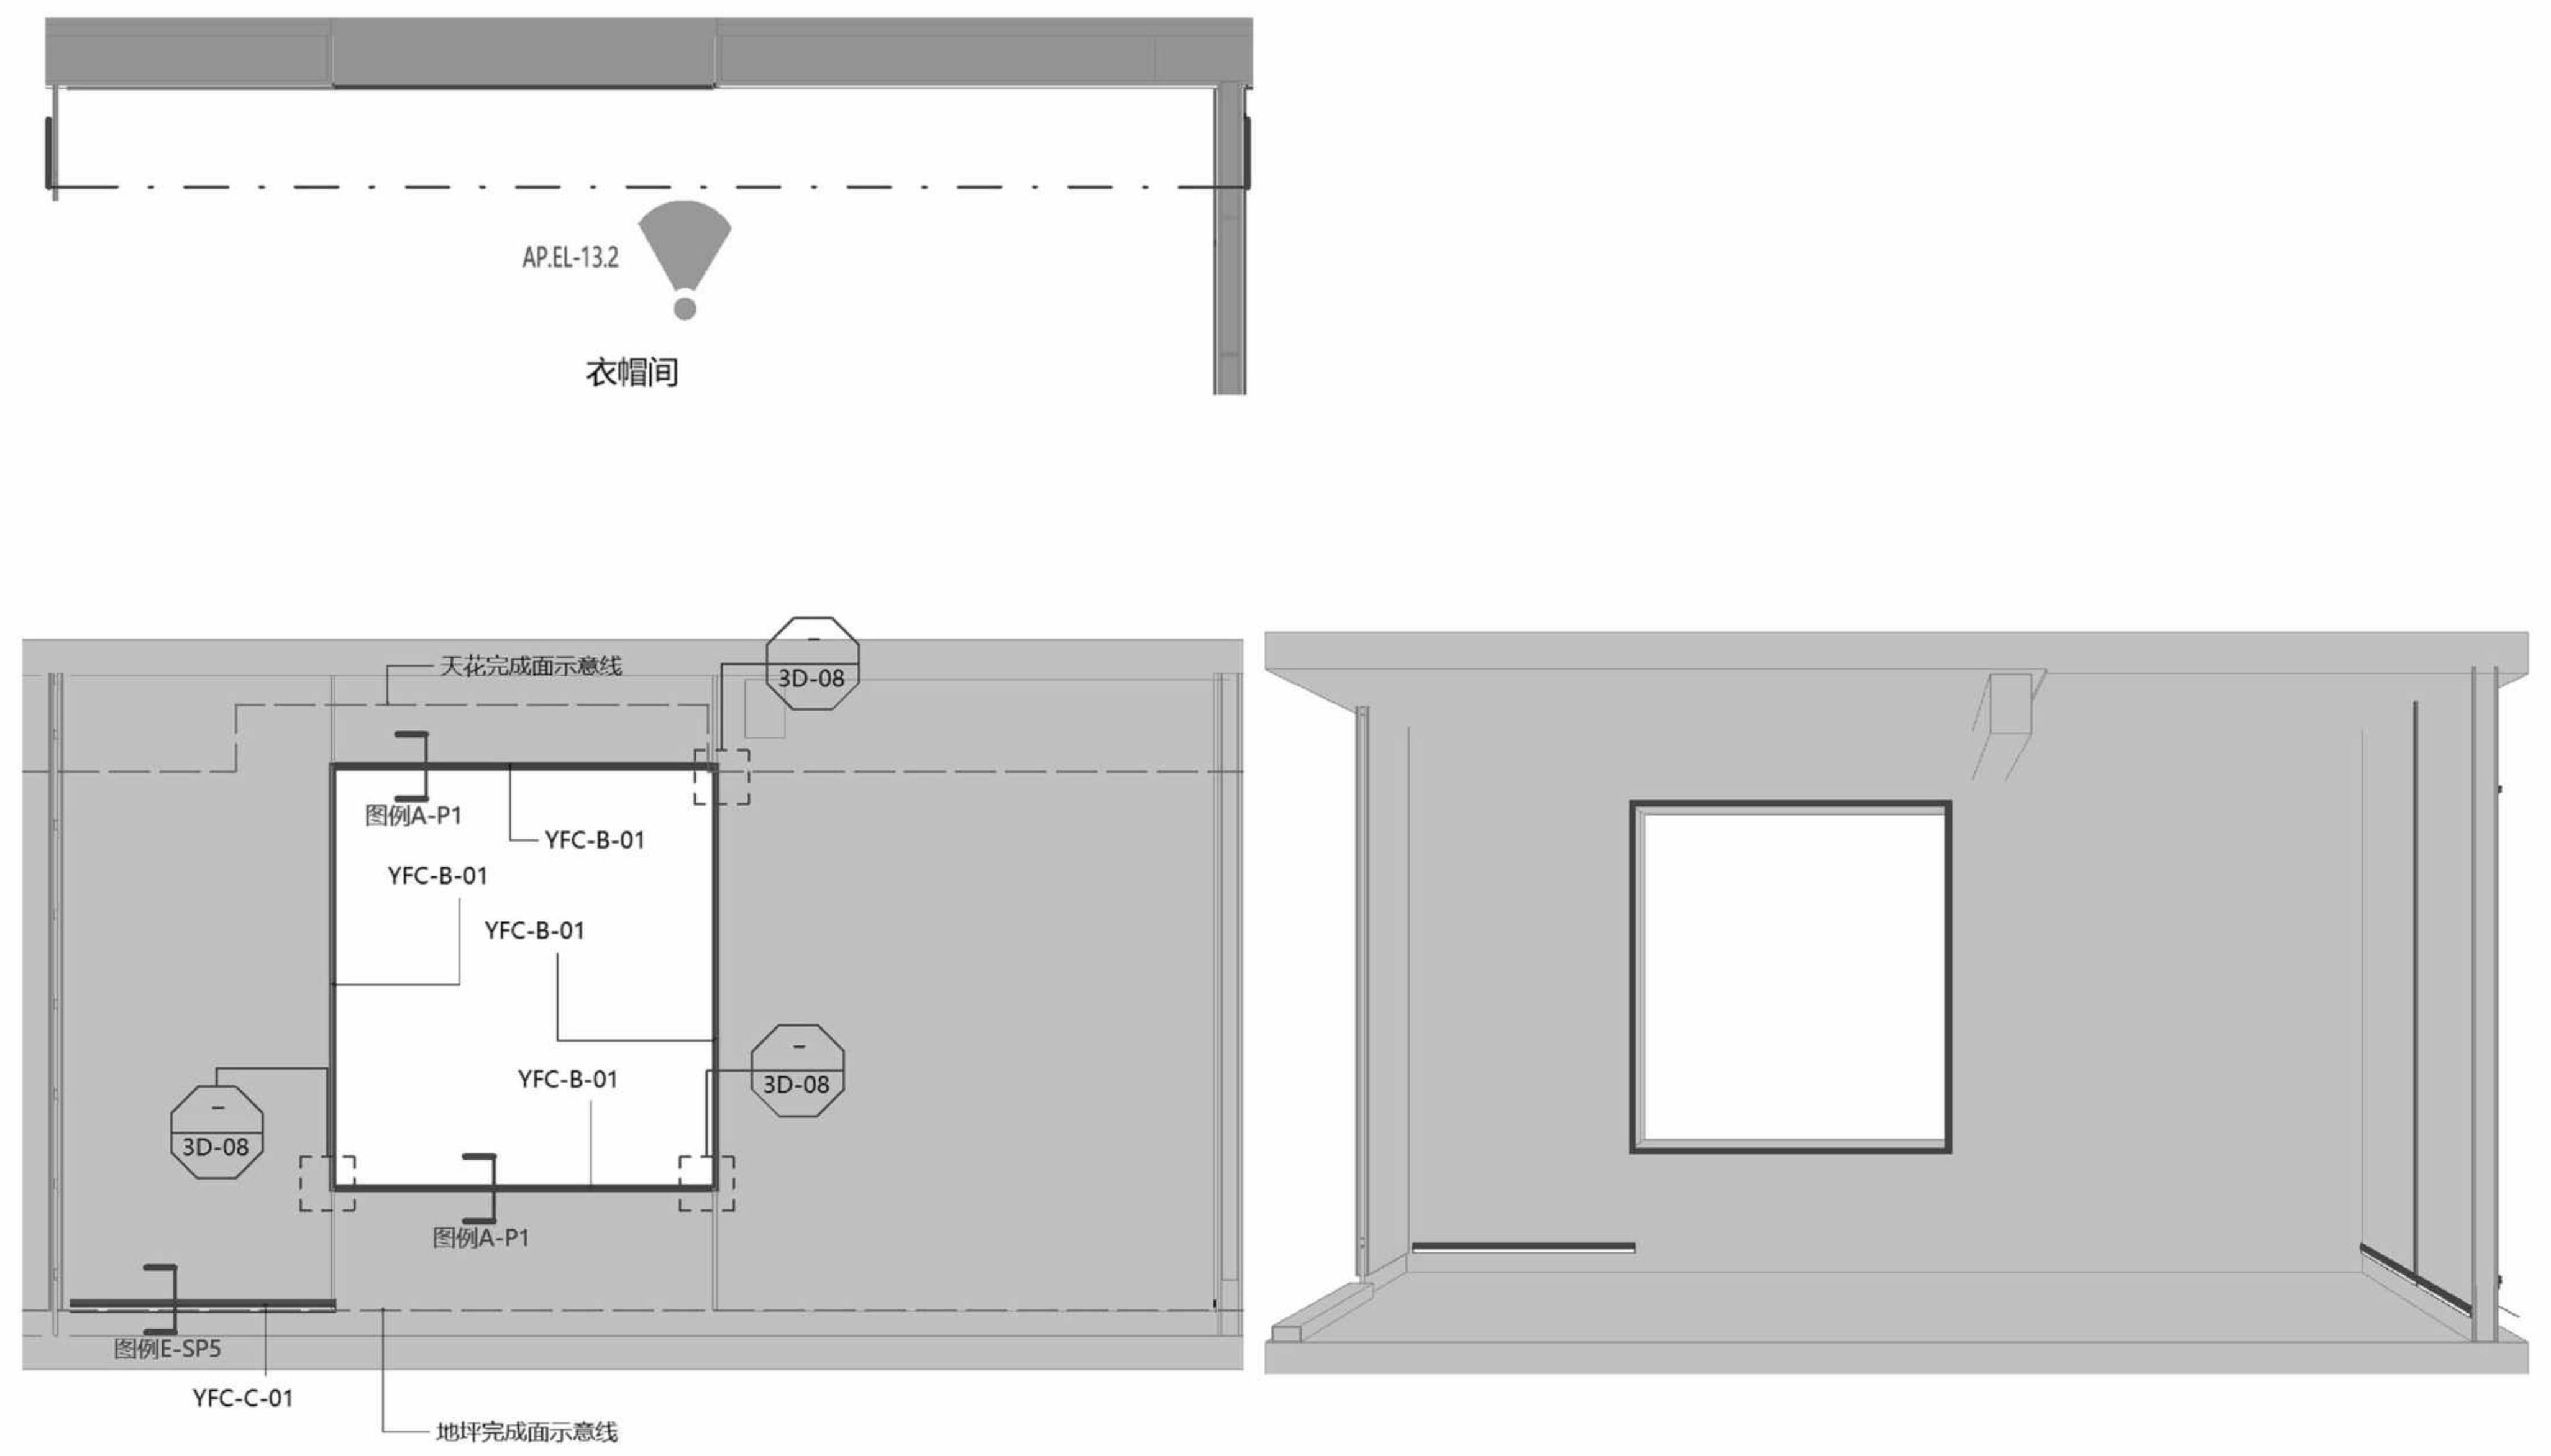
AP.EL-13.2
衣帽间
天花完成面示意线
3D-08
图例A-P1
YFC-B-01
YFC-B-01
YFC-B-01
3D-08
3D-08
YFC-B-01
图例A-P1
图例E-SP5
YFC-C-01
地坪完成面示意线

2
衣帽间 墙面及踢脚铝型材立面图2
Scale比例 1：30@A2

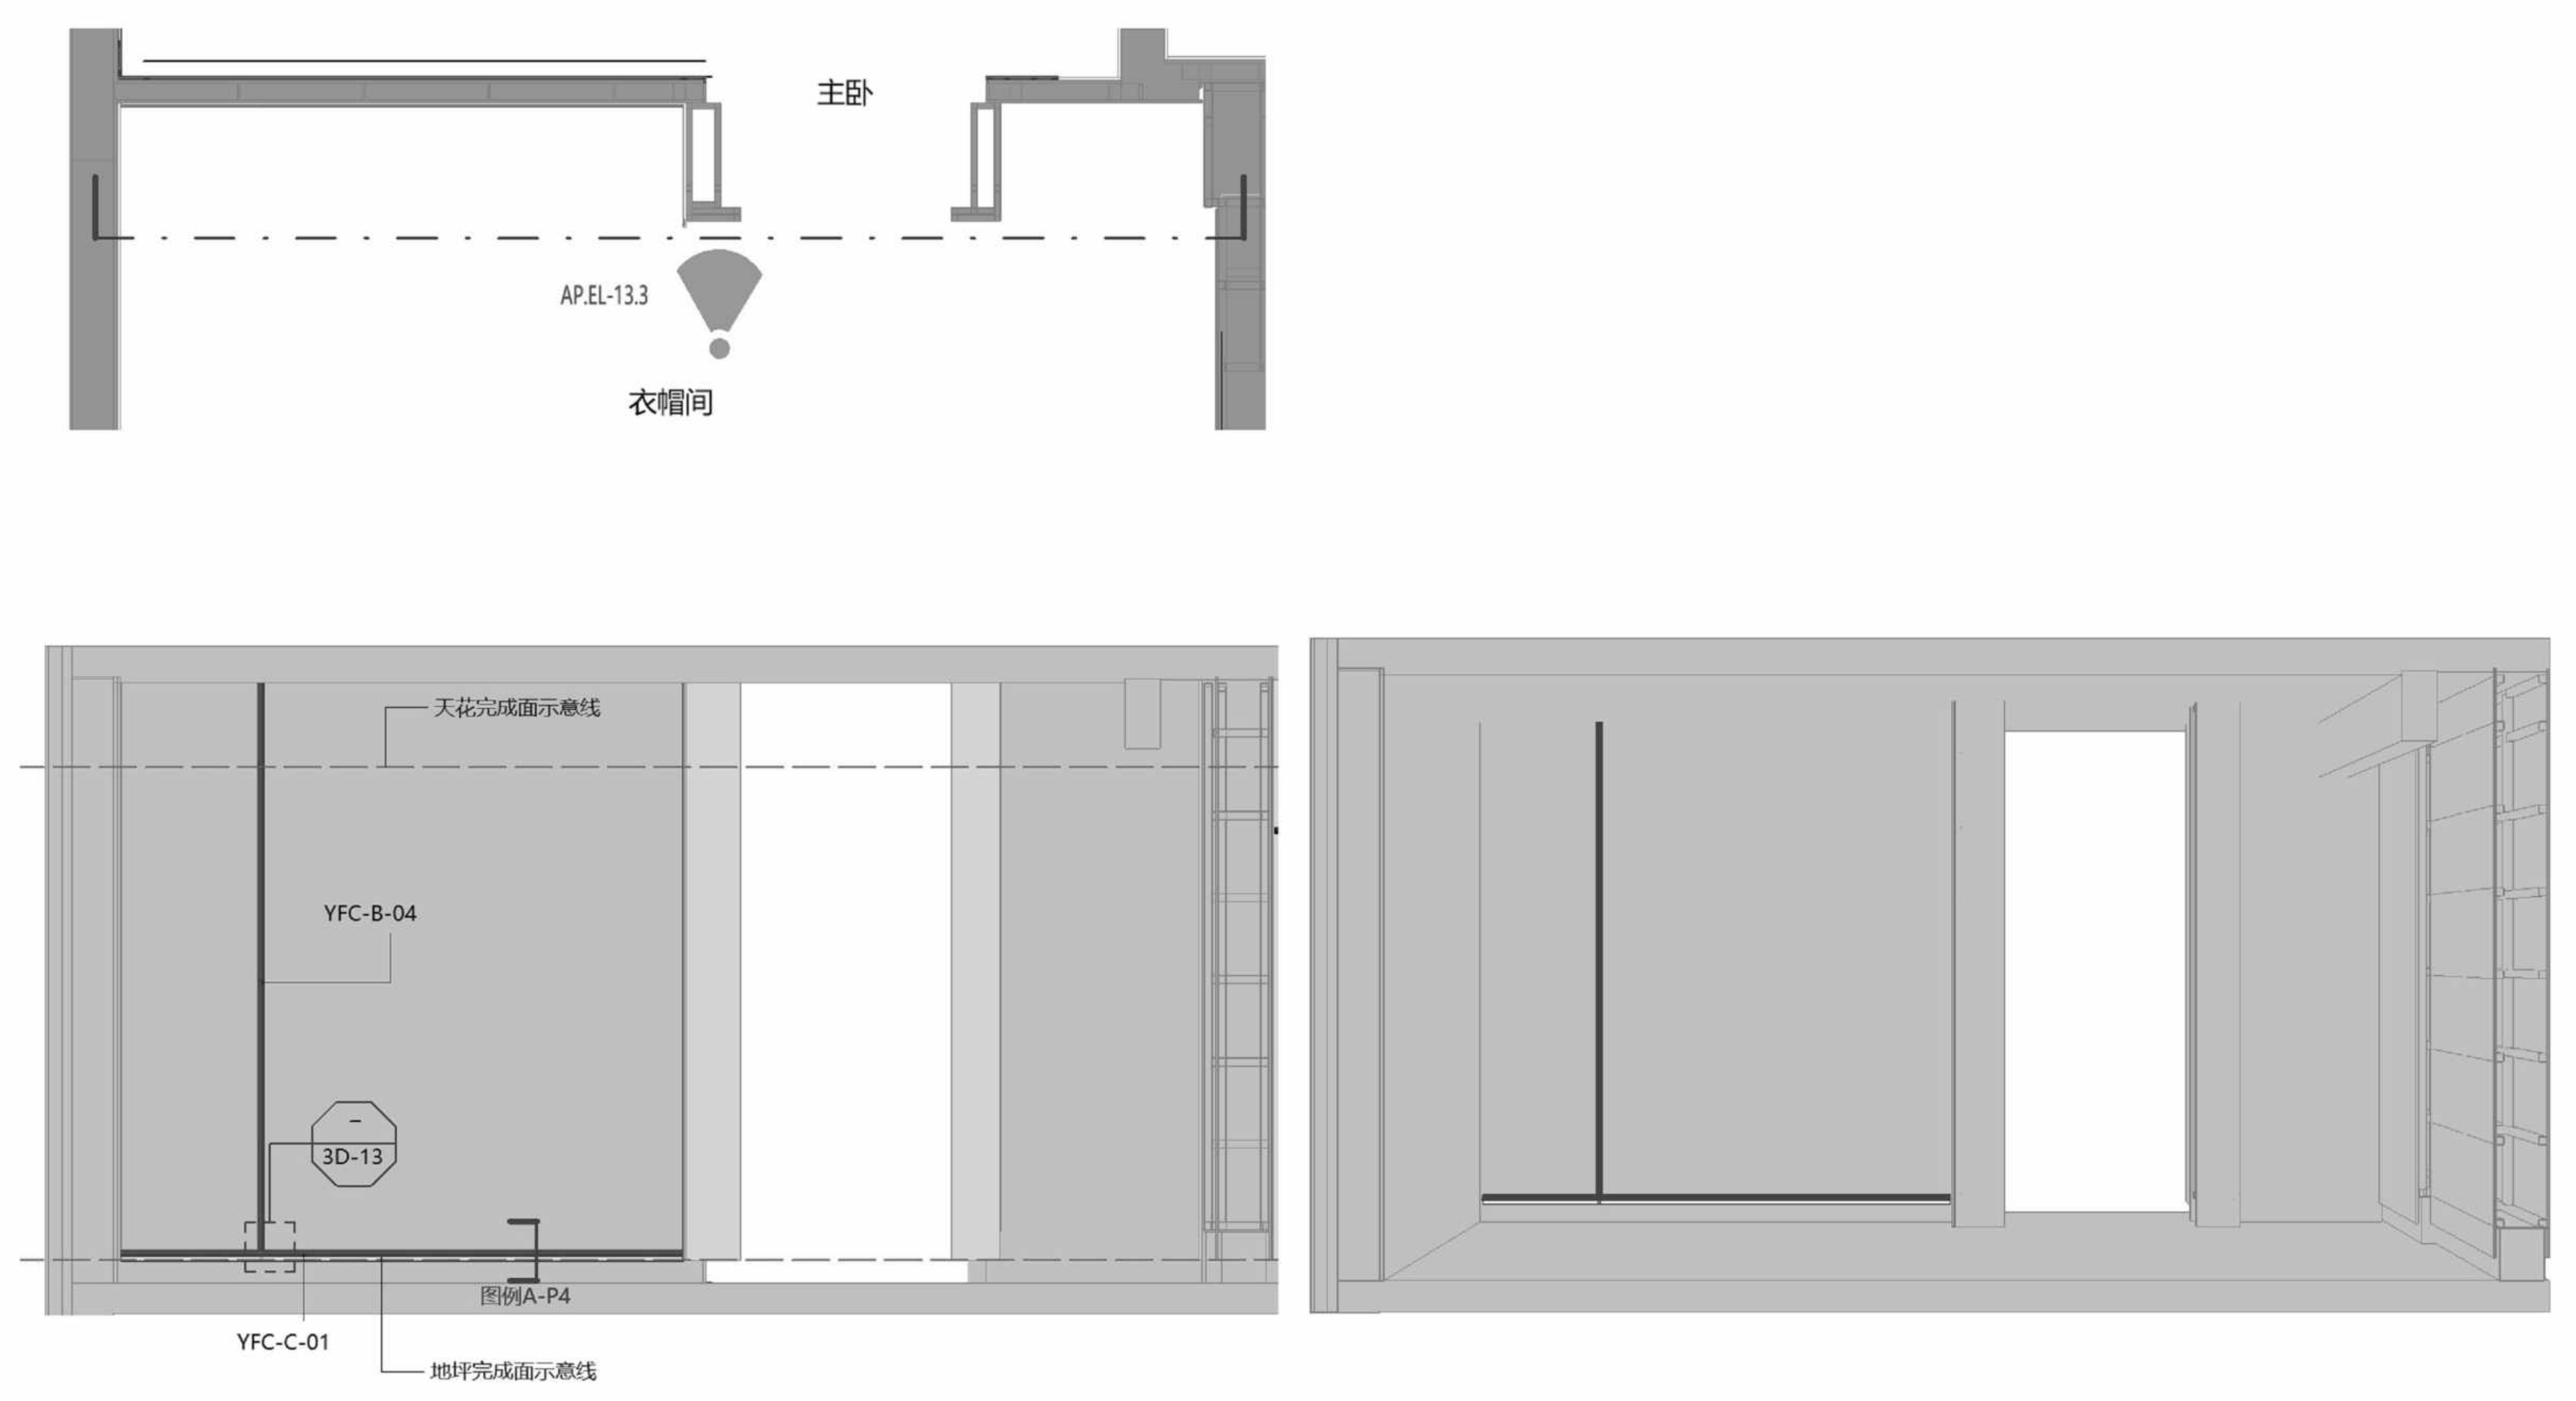
主卧
AP.EL-13.3
衣帽间
天花完成面示意线
YFC-B-04
3D-13
图例A-P4
YFC-C-01
地坪完成面示意线

3
衣帽间 墙面及踢脚铝型材立面图3
Scale比例 1：30@A2

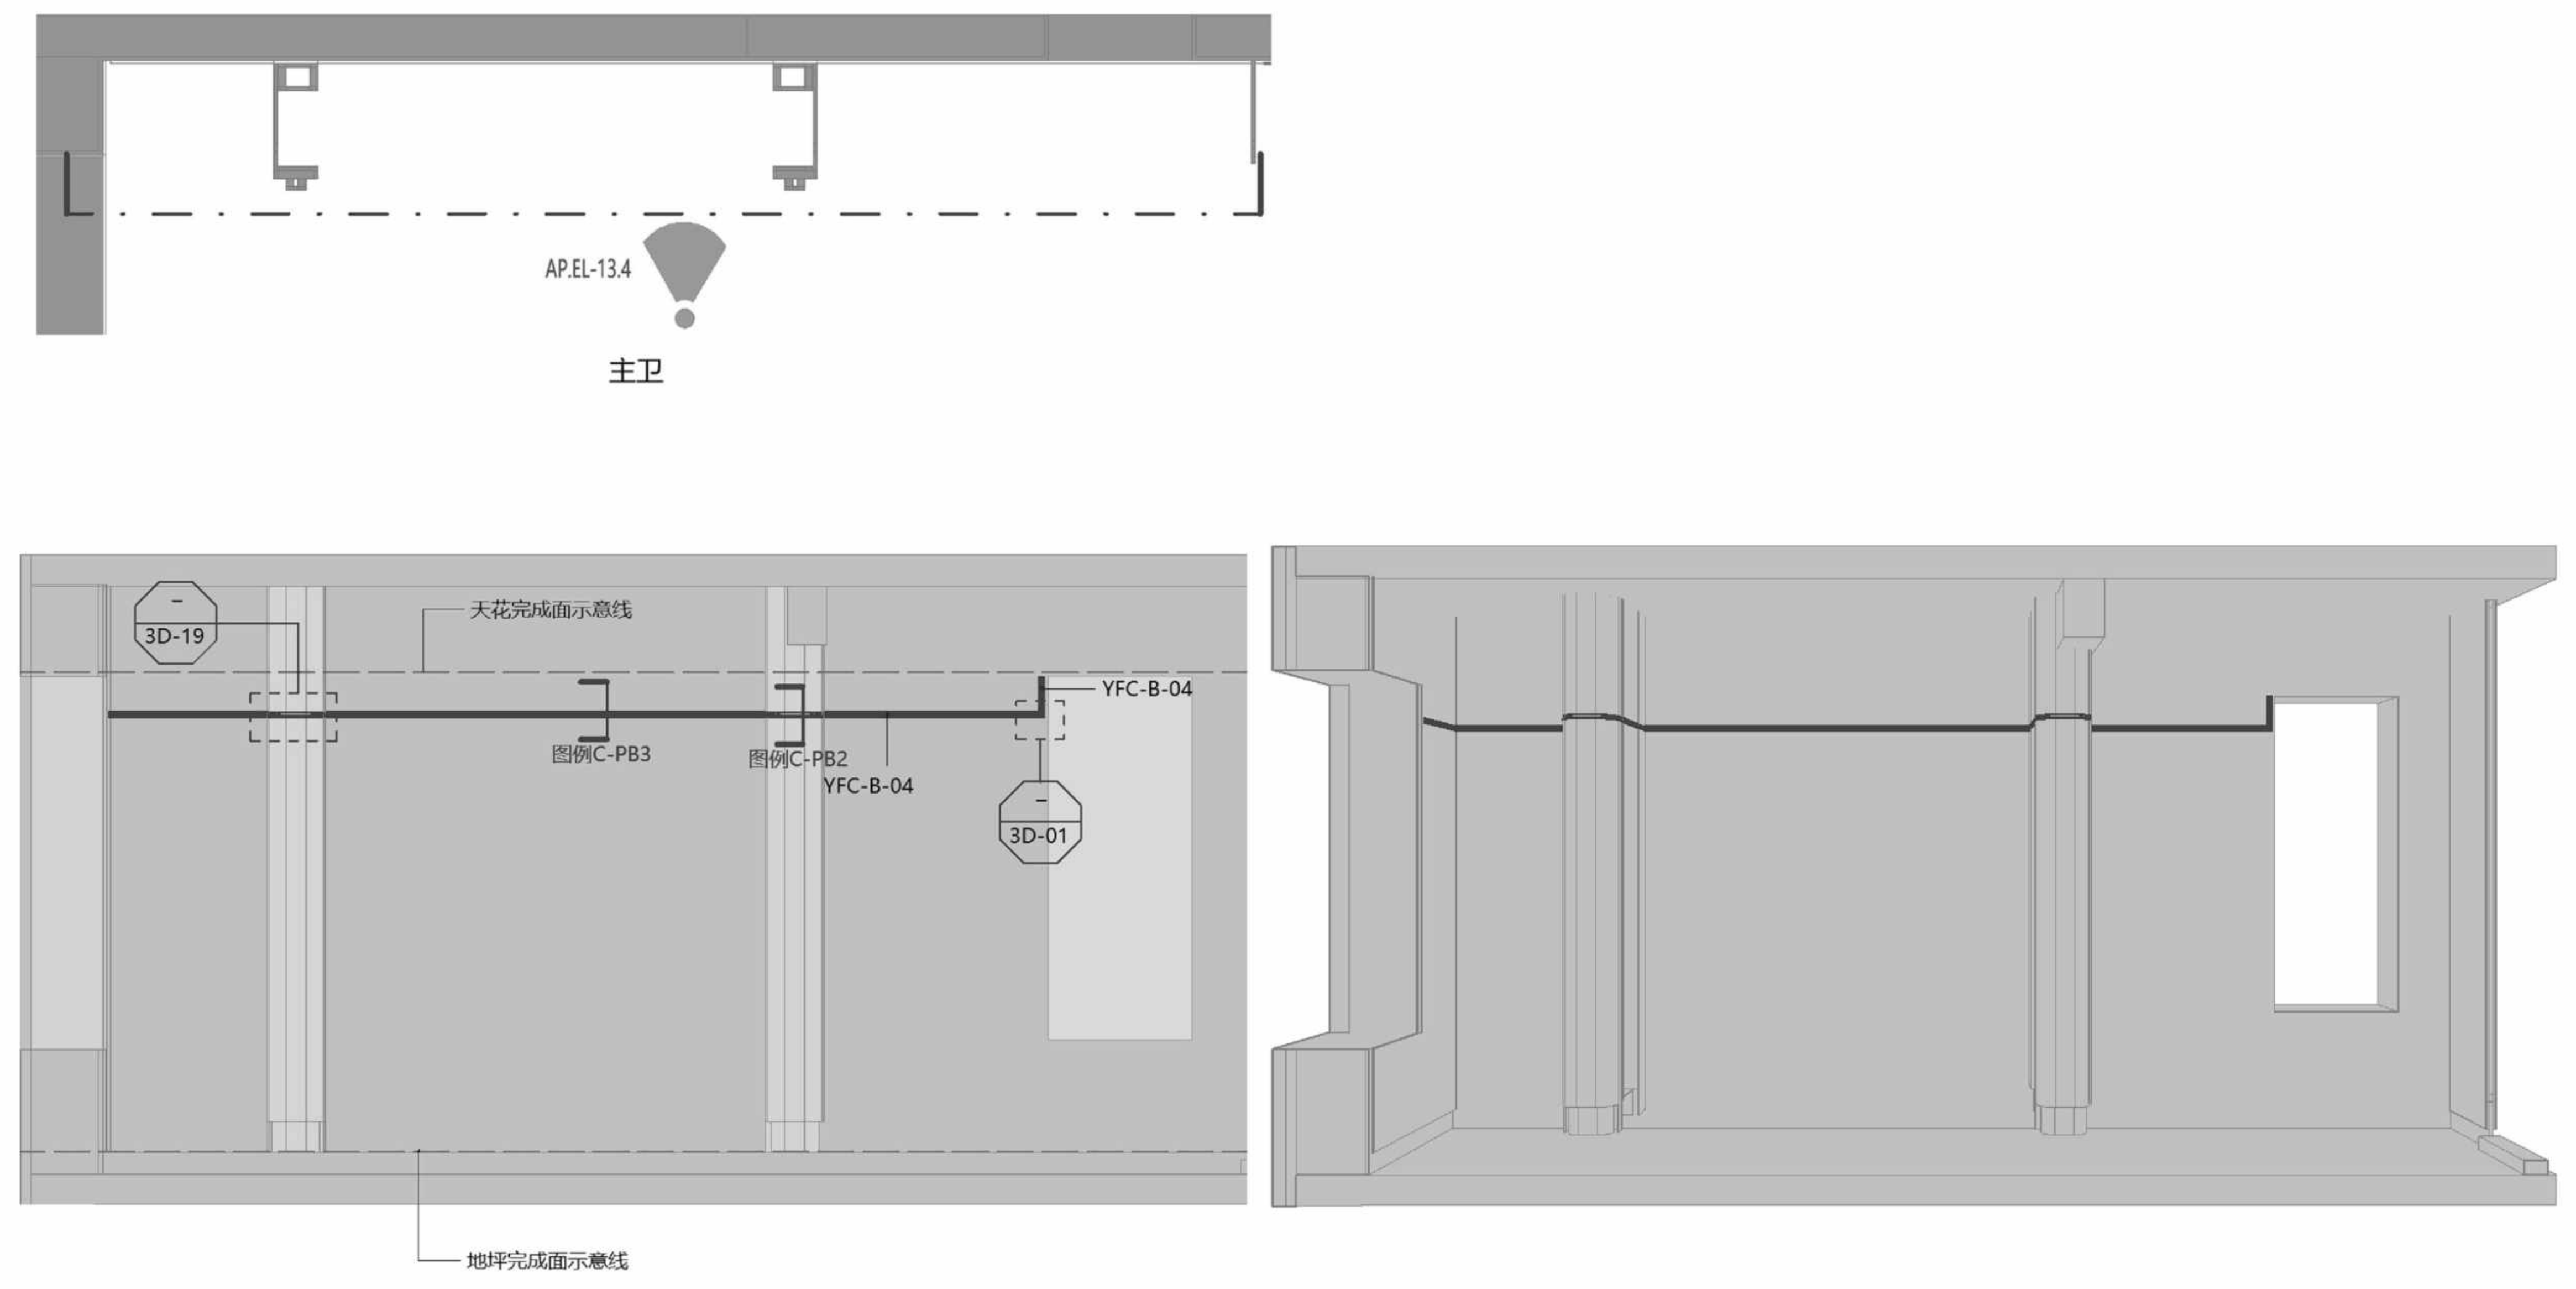
AP.EL-13.4
主卫
3D-19
天花完成面示意线
YFC-B-04
图例C-PB3
图例C-PB2
YFC-B-04
3D-01
地坪完成面示意线

4
主卫 墙面及踢脚铝型材立面图
Scale比例 1：30@A2

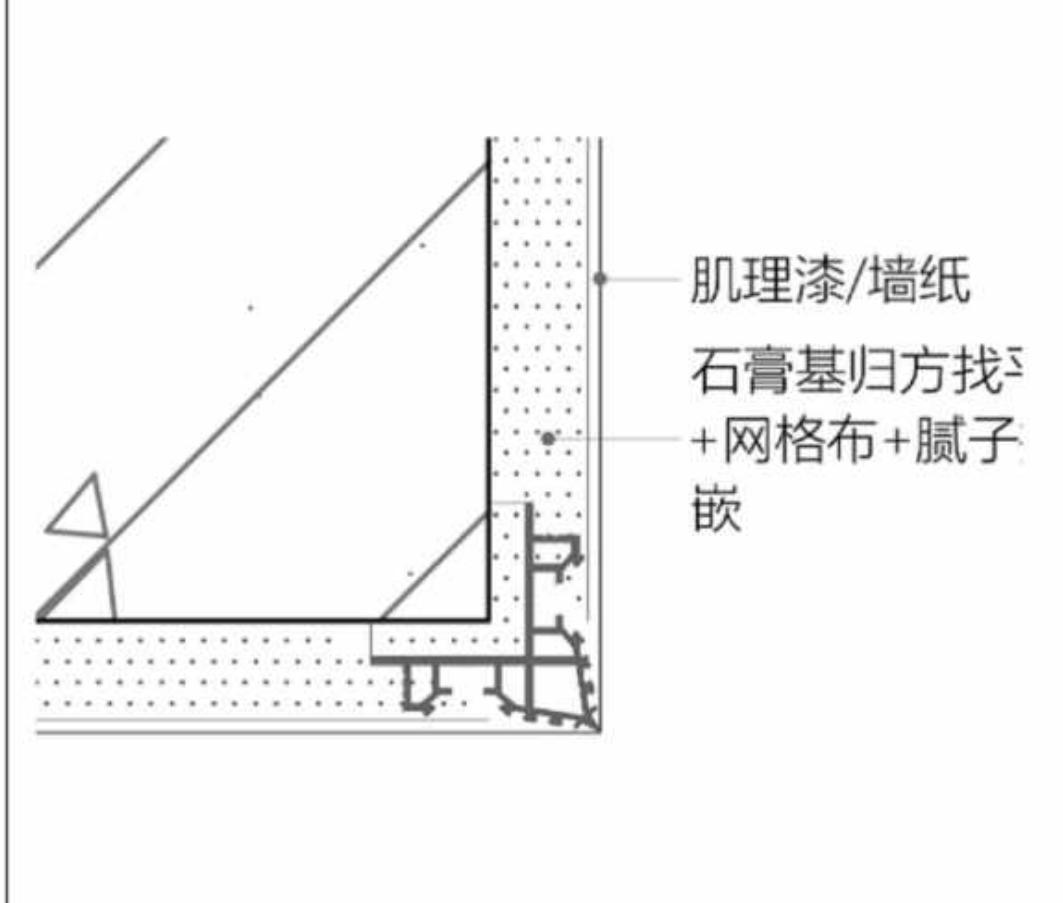
肌理漆/墙纸
石膏基归方找
+网格布+腻子
嵌

图例A-P1
墙面-石膏基找平铝型材
Scale比例 1：1@A2

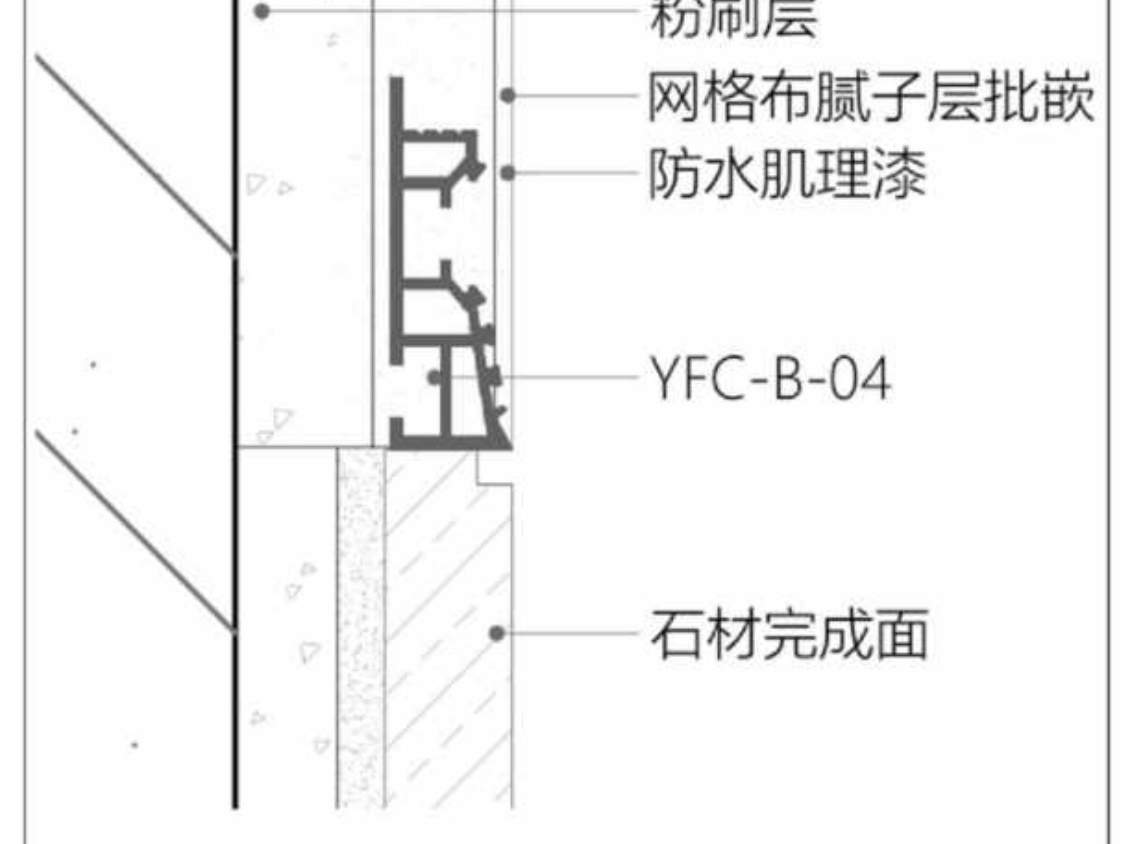
冲筋找平层
粉刷层
网格布腻子层批嵌
防水肌理漆
YFC-B-04
石材完成面

图例A-P2
墙面-石膏基找平铝型材
Scale比例 1：1@A2

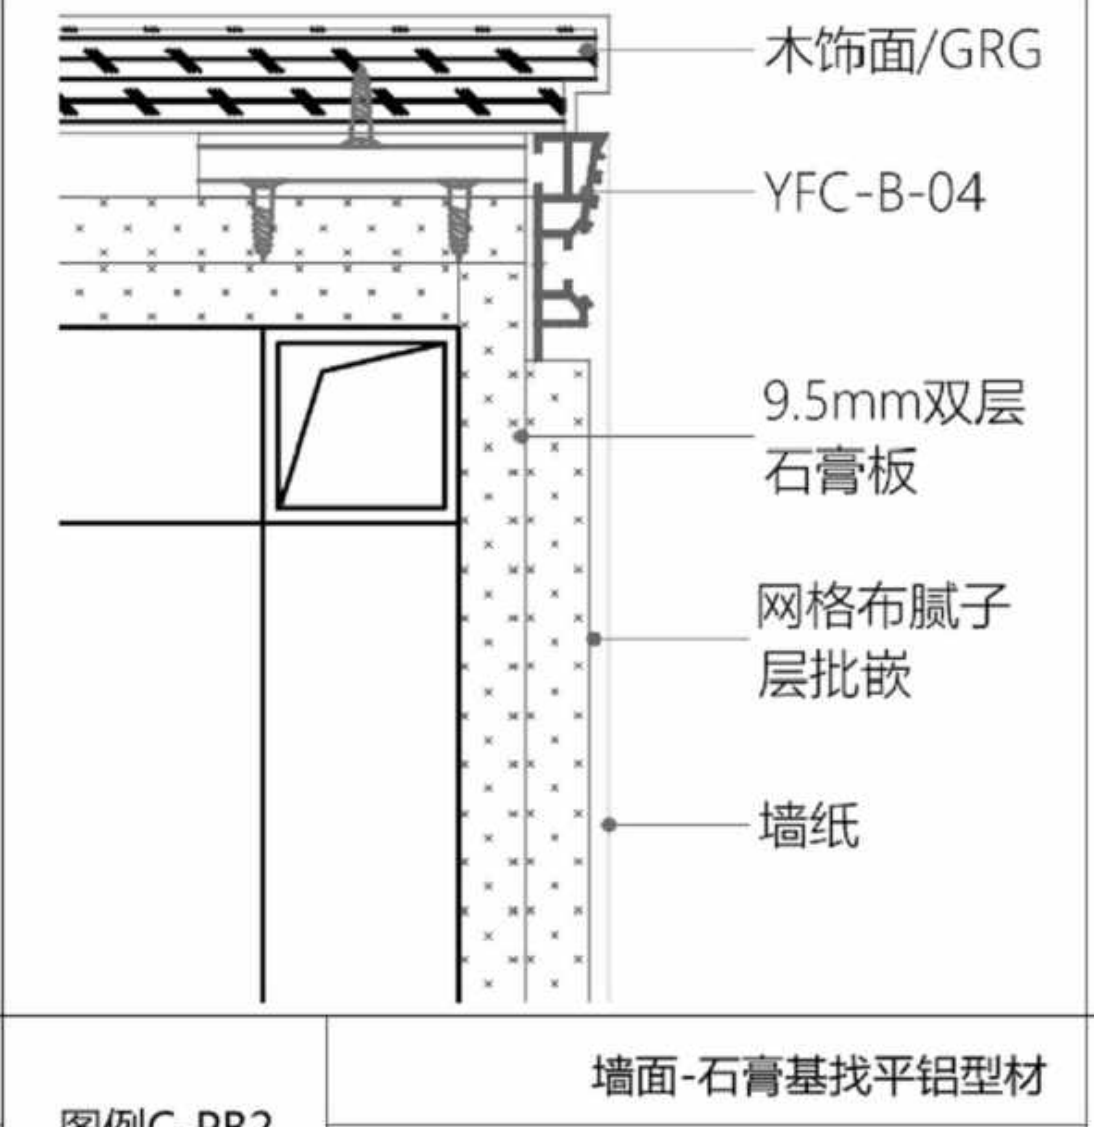
木饰面/GRG
YFC-B-04
9.5mm双层
石膏板
网格布腻子
层批嵌
墙纸

图例C-PB2
墙面-石膏基找平铝型材
Scale比例 1：1@A2

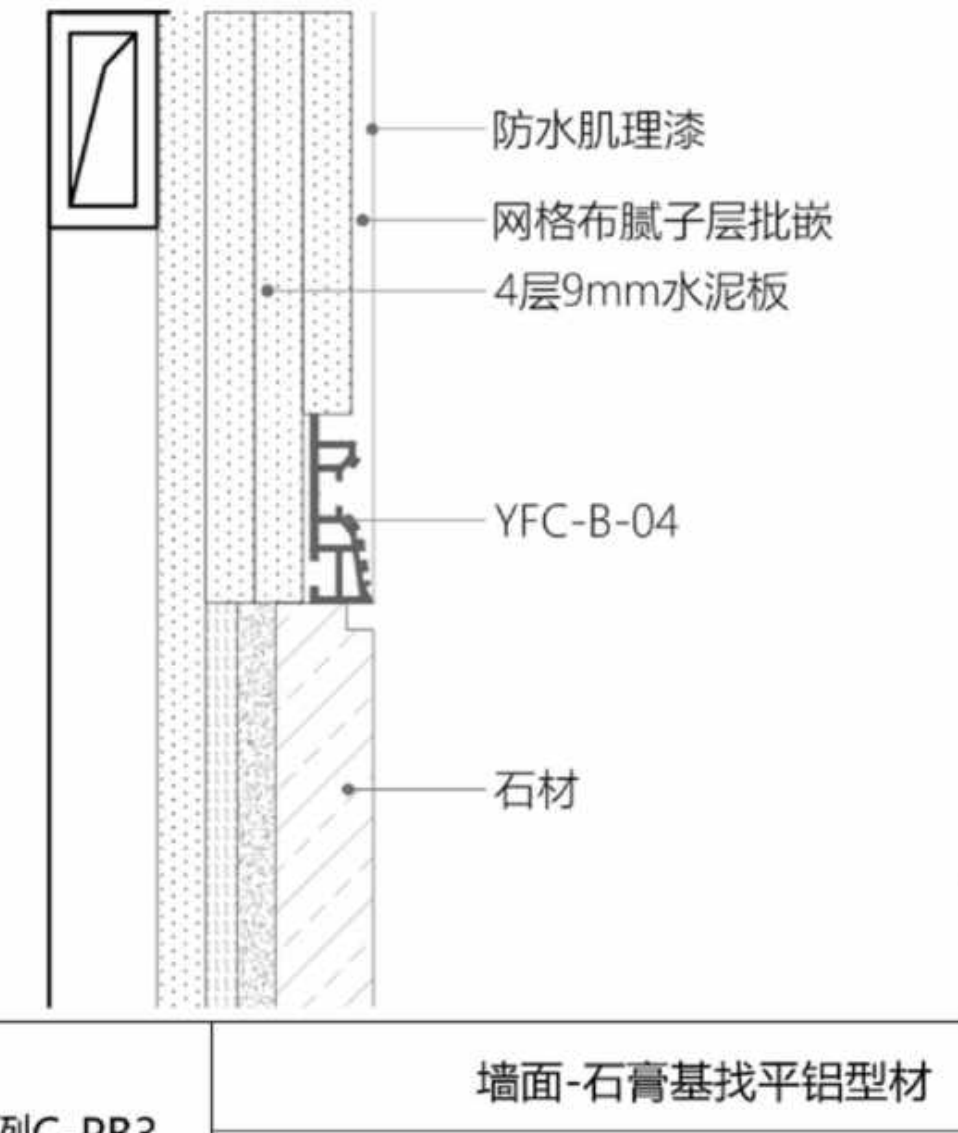
防水肌理漆
网格布腻子层批嵌
4层9mm水泥板
YFC-B-04
石材

图例C-PB3
墙面-石膏基找平铝型材
Scale比例 1：1@A2

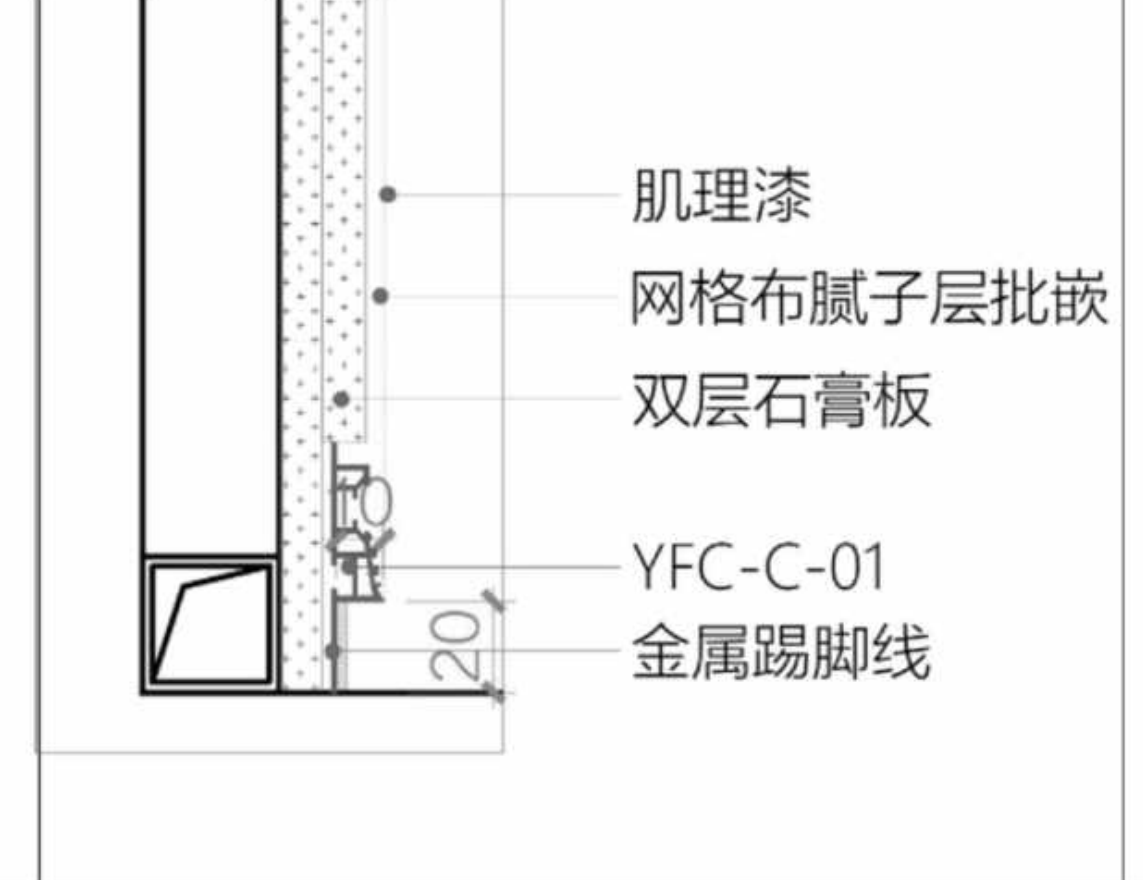
肌理漆
网格布腻子层批嵌
双层石膏板
YFC-C-01
20
金属踢脚线

图例E-SB2
踢脚-石膏基找平铝型材
Scale比例 1：1@A2

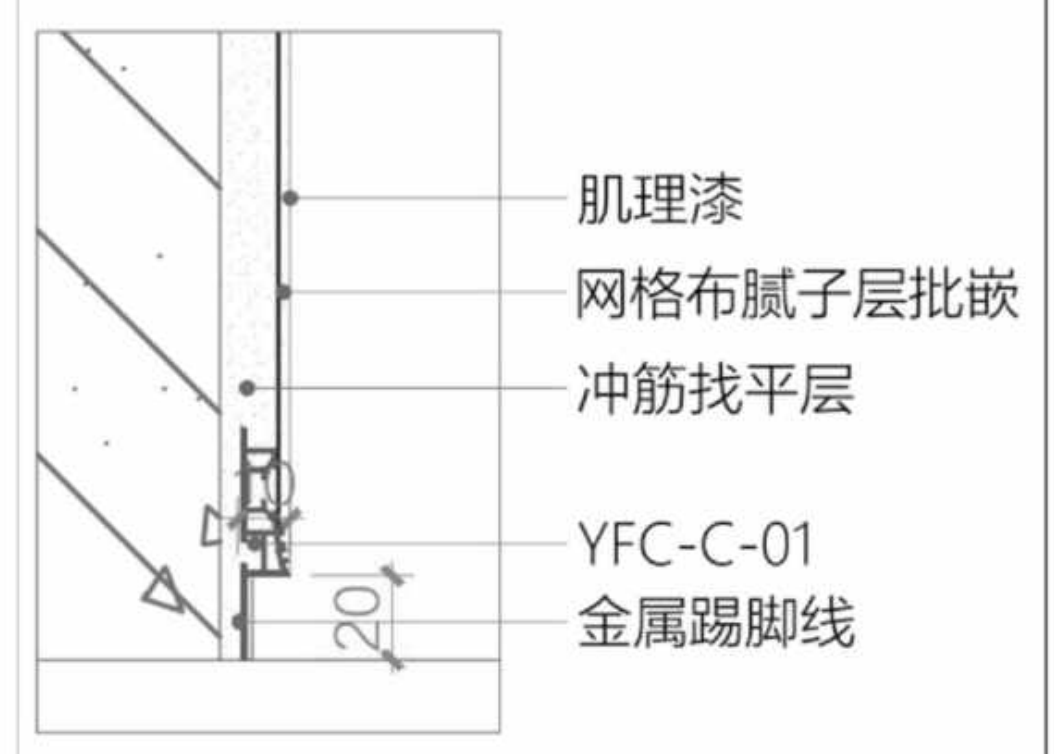
肌理漆
网格布腻子层批嵌
冲筋找平层
YFC-C-01
20
金属踢脚线

图例E-SB6
踢脚-石膏基找平铝型材
Scale比例 1：1@A2

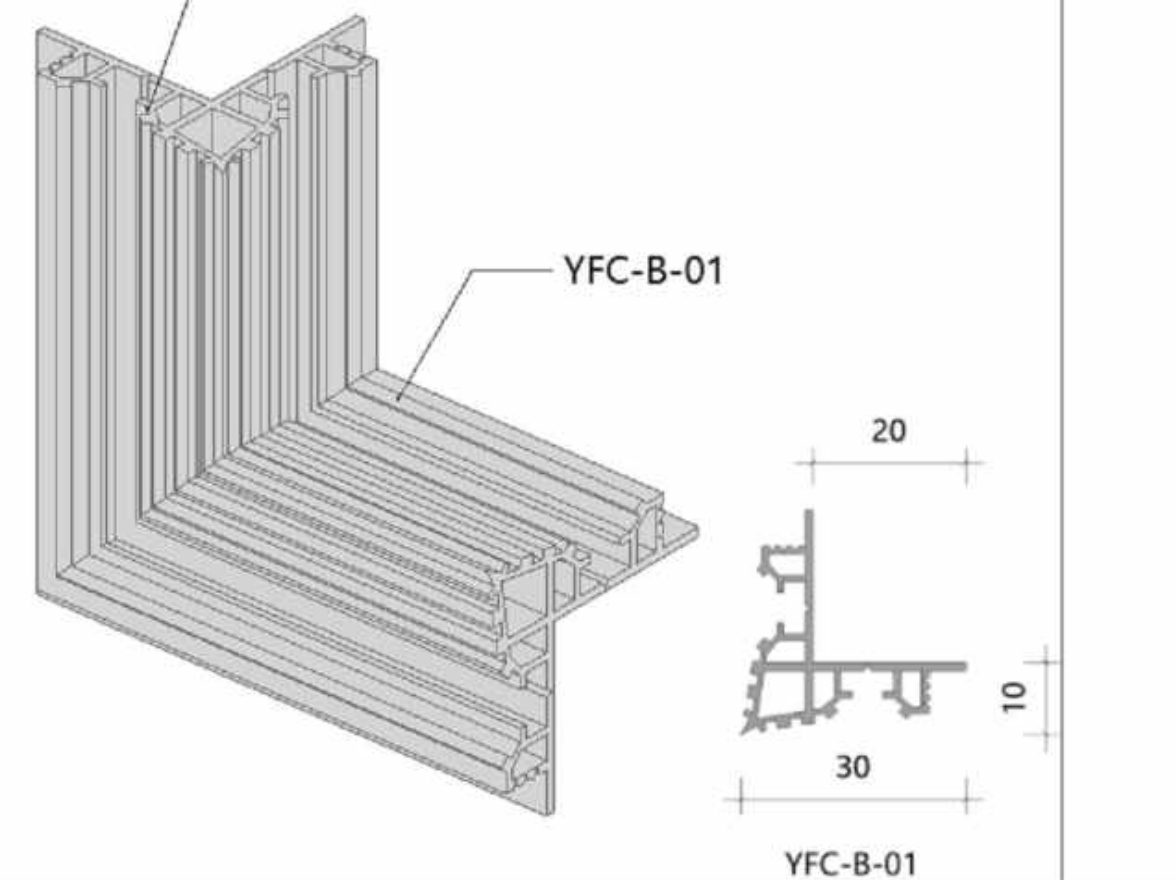
YFC-B-01
YFC-B-01
20
10
30
YFC-B-01

3D-08
转角铝型材-拼接跟通
转角数量：5

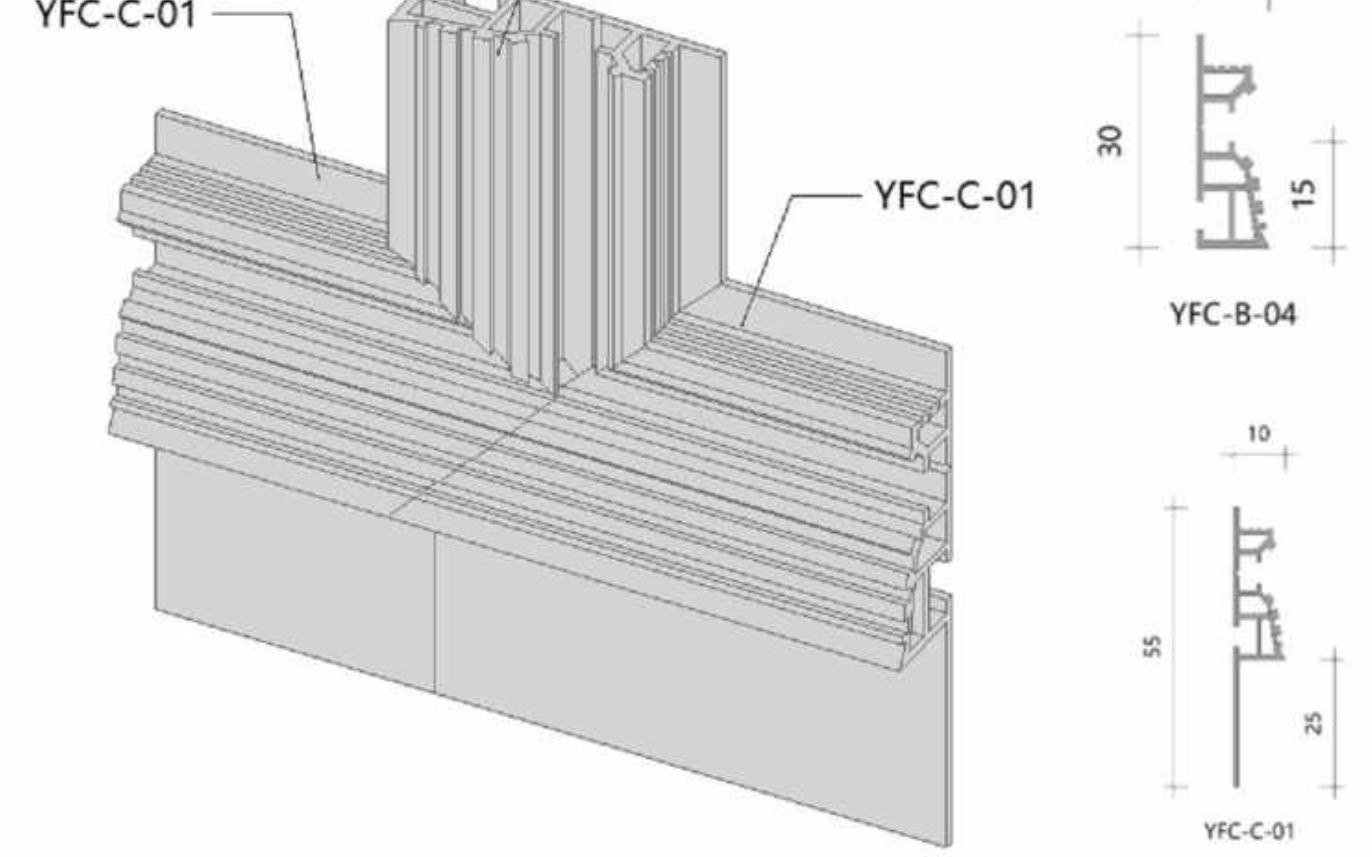
YFC-B-04
YFC-C-01
YFC-C-01
10
30
15
YFC-B-04
10
55
25
YFC-C-01

3D-13
转角铝型材-拼接跟通
转角数量：1

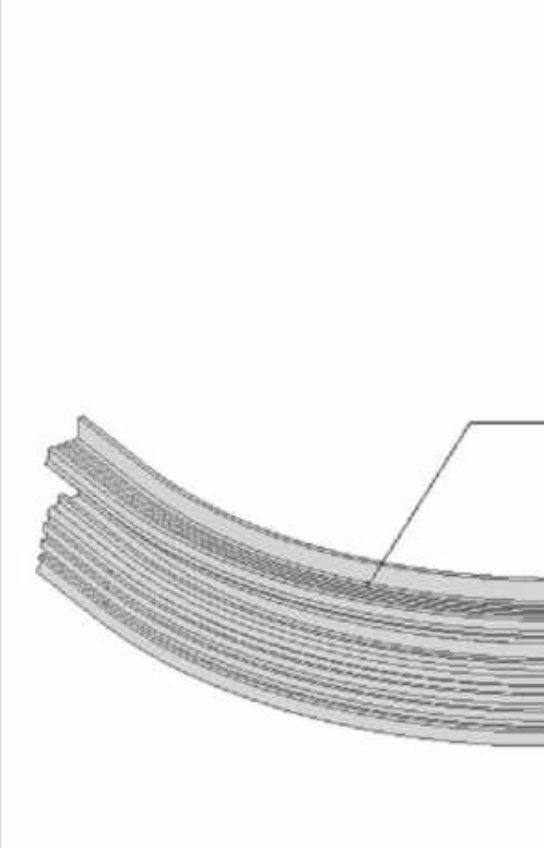
YFC-B-04
10
30
15
YFC-B-04

3D-19
转角铝型材-拼接跟通
转角数量：2

盖章

注释
Notes
1.本图纸如与现场尺寸有误，请施工人员与项目负责人联系。
2.施工前施工人员应认真查阅此图，如有不明确尺寸，按现场测量为准。
3.本图纸必须经甲乙双方认可并签字方可作为施工依据。

日期
Date 03/04/26

修订
Revision
△1

项目
Project
潮映华岸府3-801

比例
Scale 1：30@A2

衣帽间、主卫
墙面及踢脚铝型材

图纸编号
Drawing No.
AP.EL-13

项目编号
Project No.
©2025

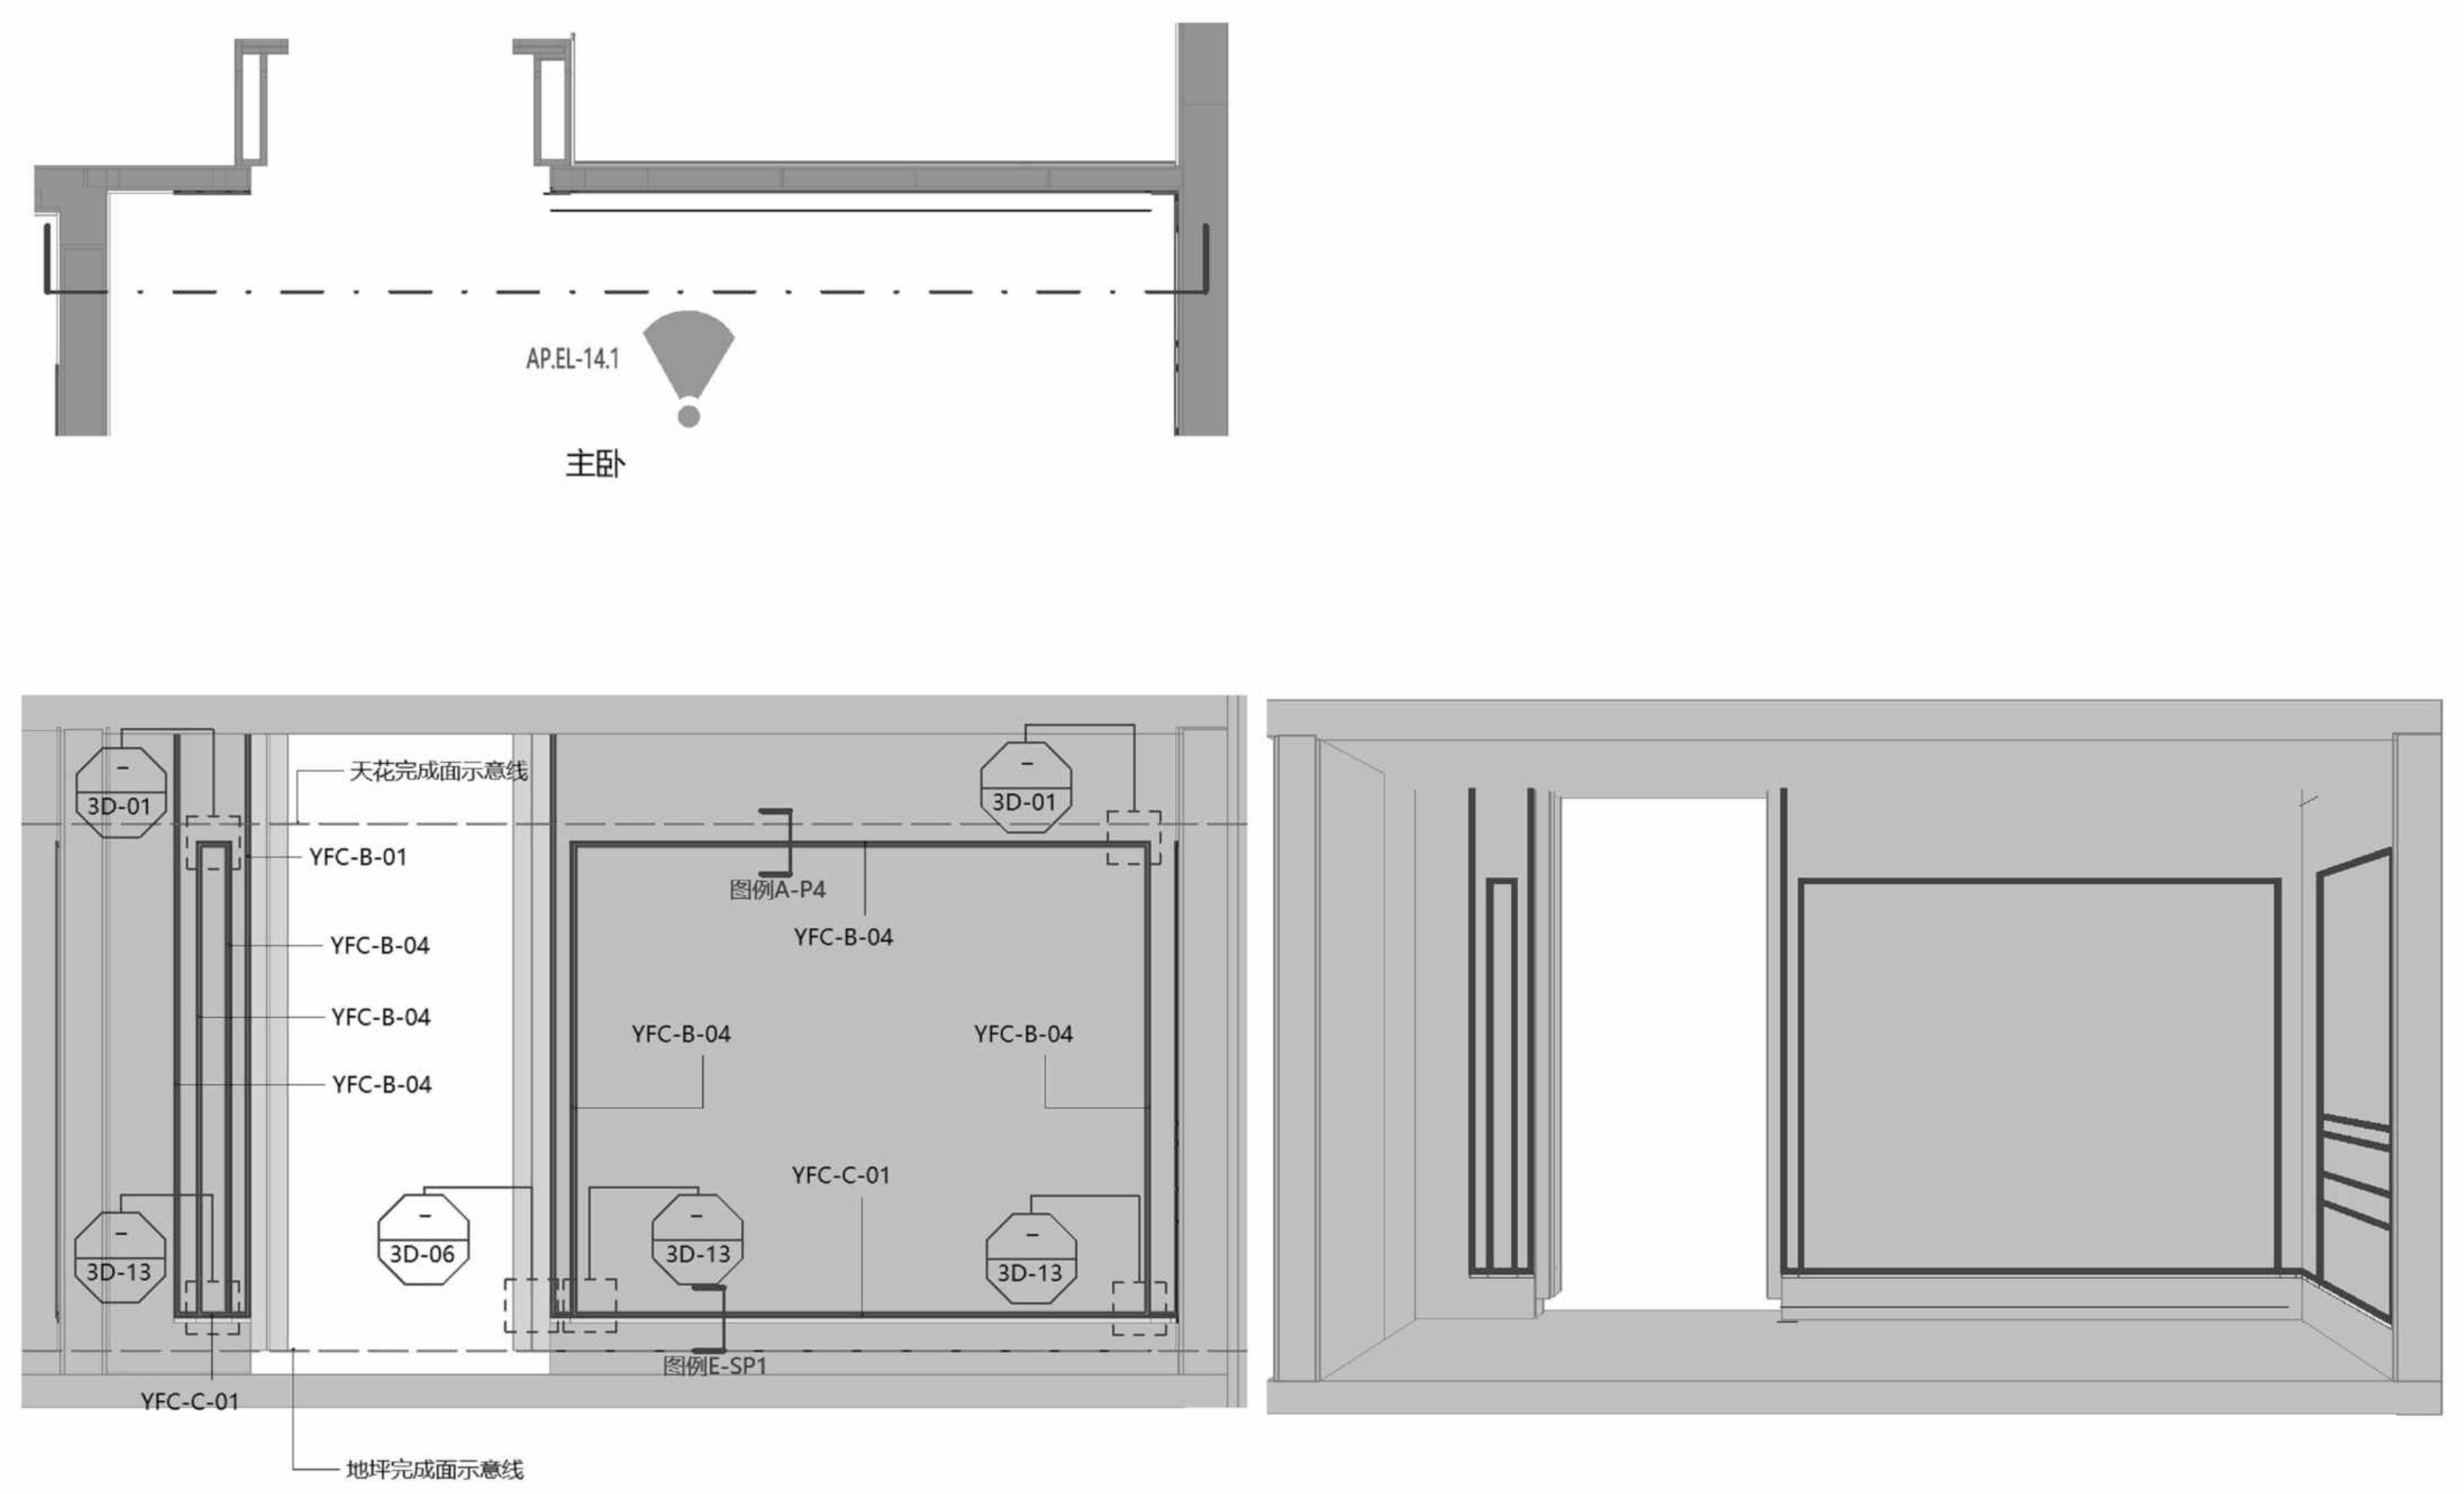

AP.EL-14.1
主卧
3D-01
天花完成面示意线
YFC-B-01
YFC-B-04
YFC-B-04
YFC-B-04
3D-01
图例A-P4
YFC-B-04
YFC-B-04
YFC-B-04
YFC-C-01
3D-13
3D-06
3D-13
3D-13
图例E-SP1
YFC-C-01
地坪完成面示意线

1 主卧 墙面及踢脚铝型材立面图1

Scale比例 1：30@A2

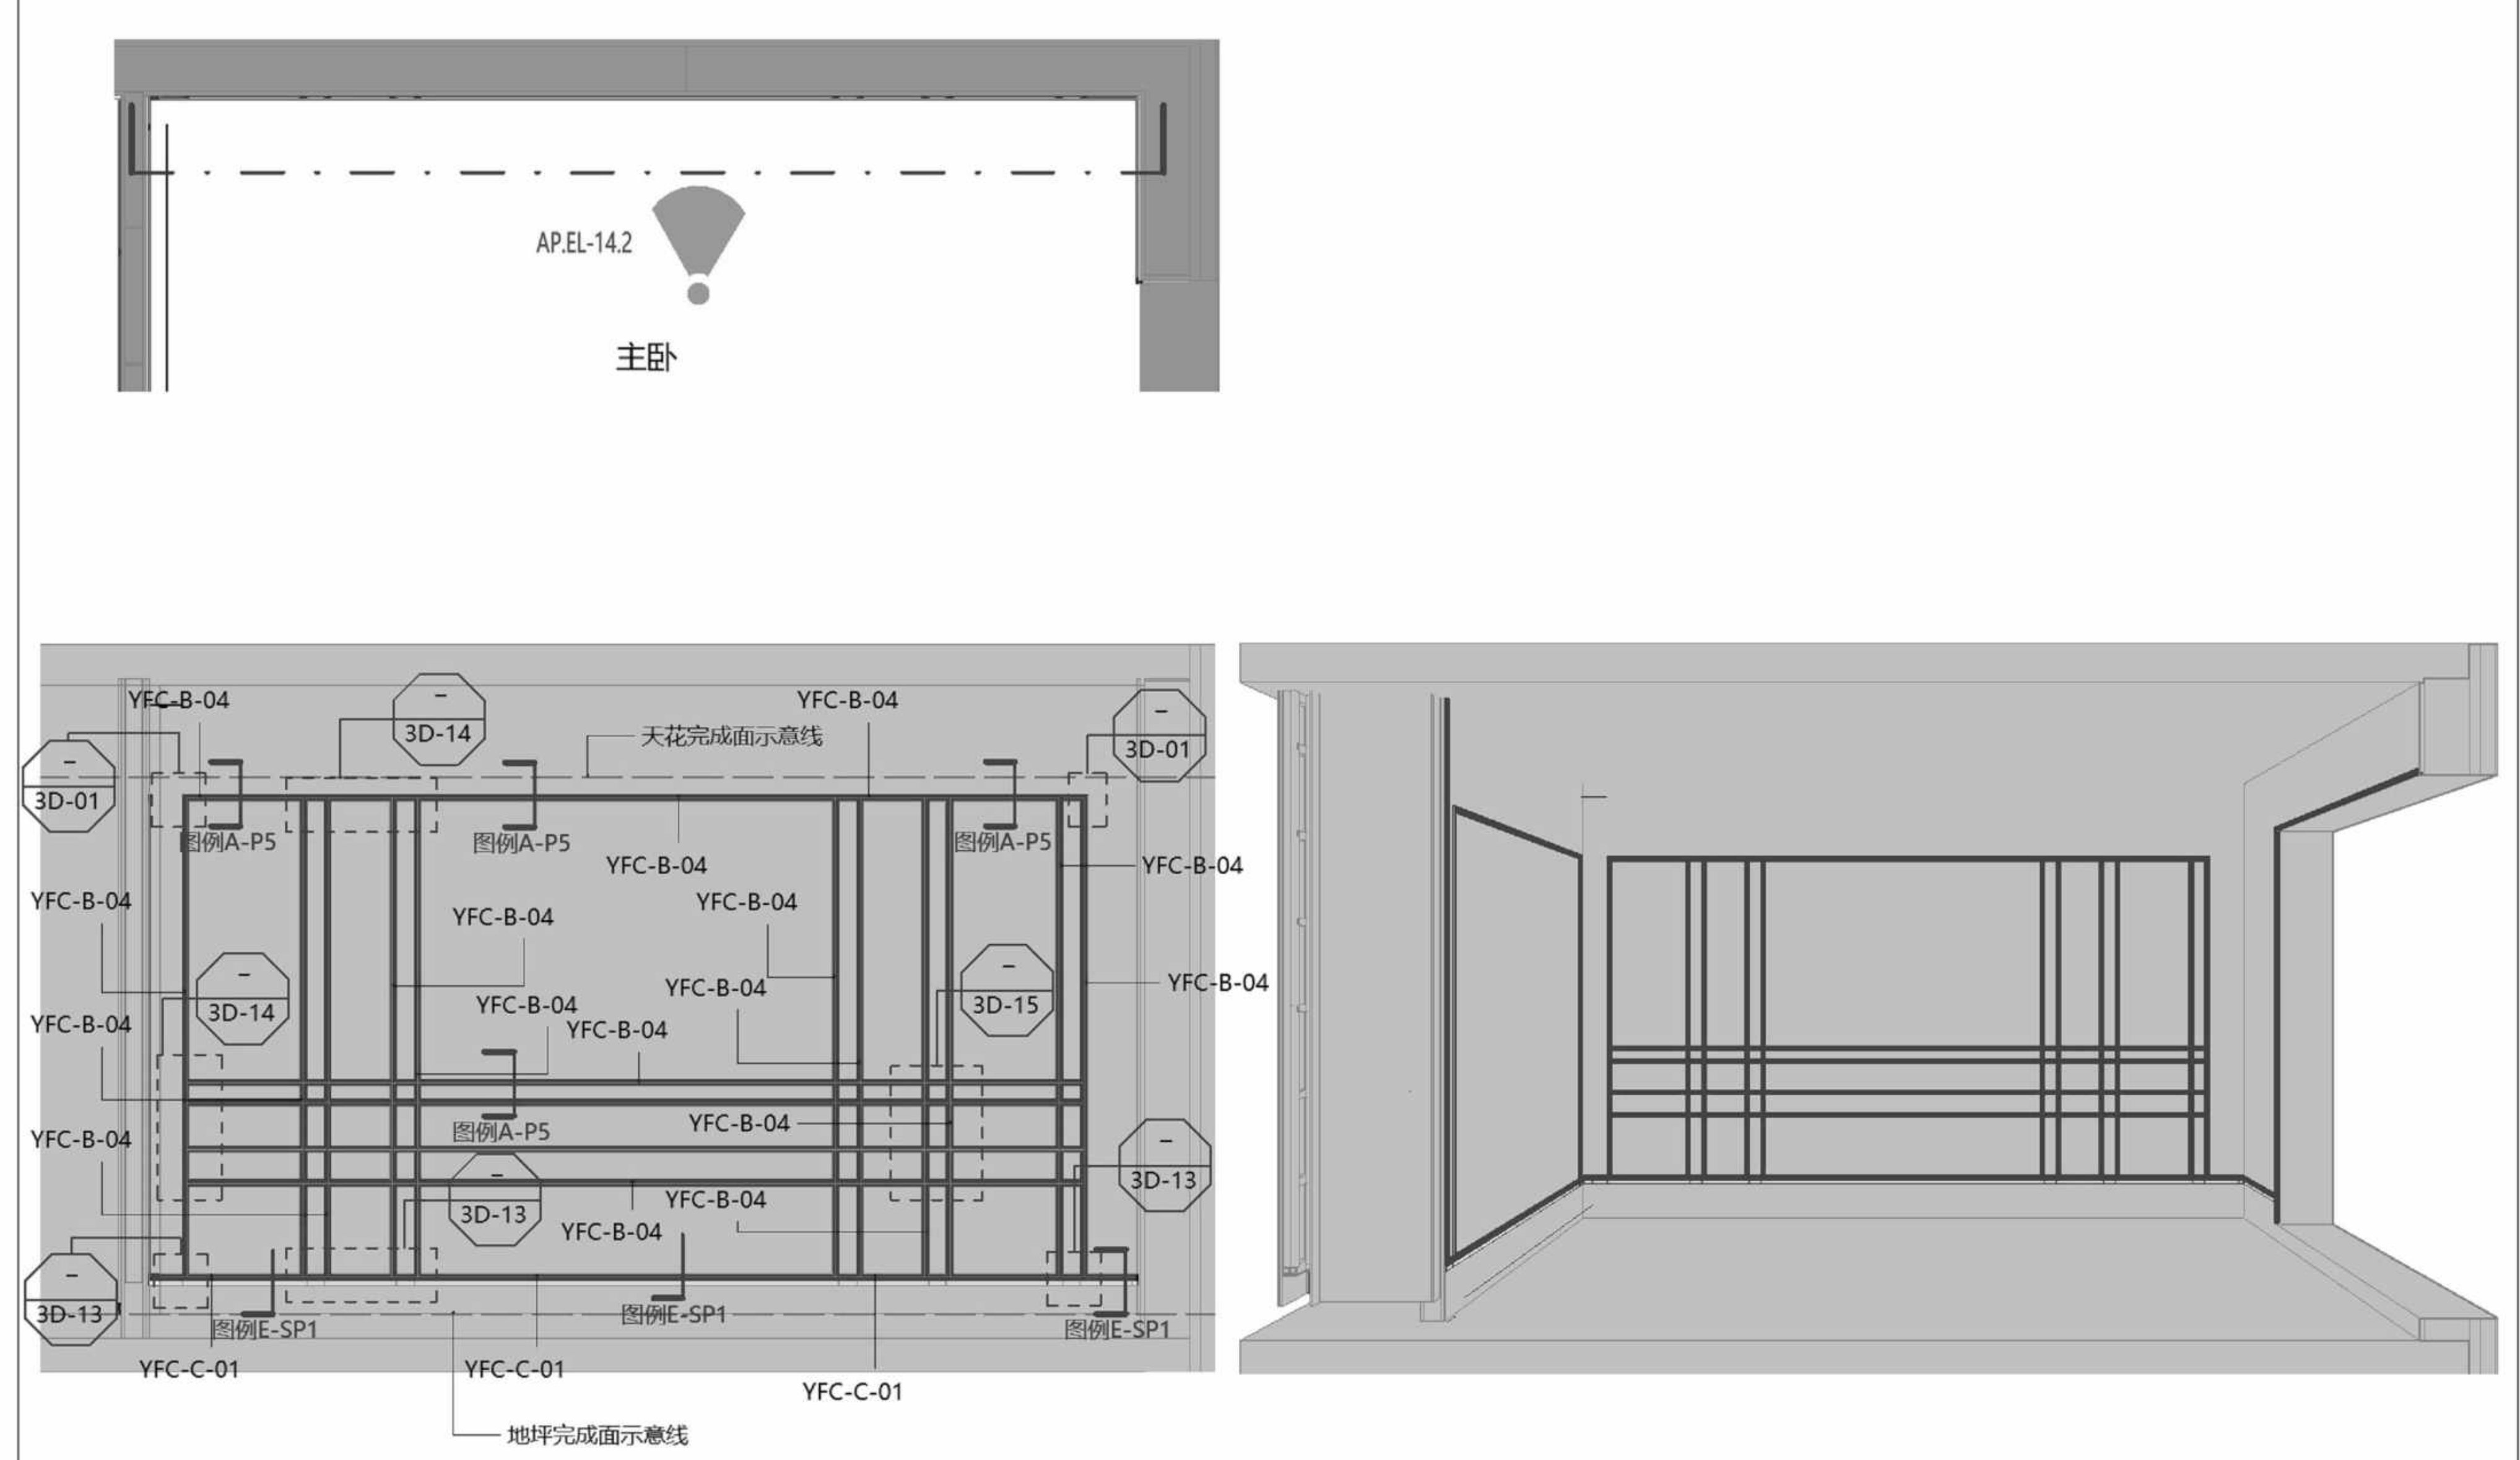

AP.EL-14.2
主卧
YFC-B-04
3D-14
YFC-B-04
天花完成面示意线
3D-01
3D-01
图例A-P5
图例A-P5
图例A-P5
YFC-B-04
YFC-B-04
YFC-B-04
YFC-B-04
YFC-B-04
3D-14
3D-15
YFC-B-04
YFC-B-04
YFC-B-04
YFC-B-04
YFC-B-04
图例A-P5
YFC-B-04
3D-13
3D-13
YFC-B-04
YFC-B-04
3D-13
图例E-SP1
图例E-SP1
图例E-SP1
YFC-C-01
YFC-C-01
YFC-C-01
地坪完成面示意线

2 主卧 墙面及踢脚铝型材立面图2

Scale比例 1：30@A2

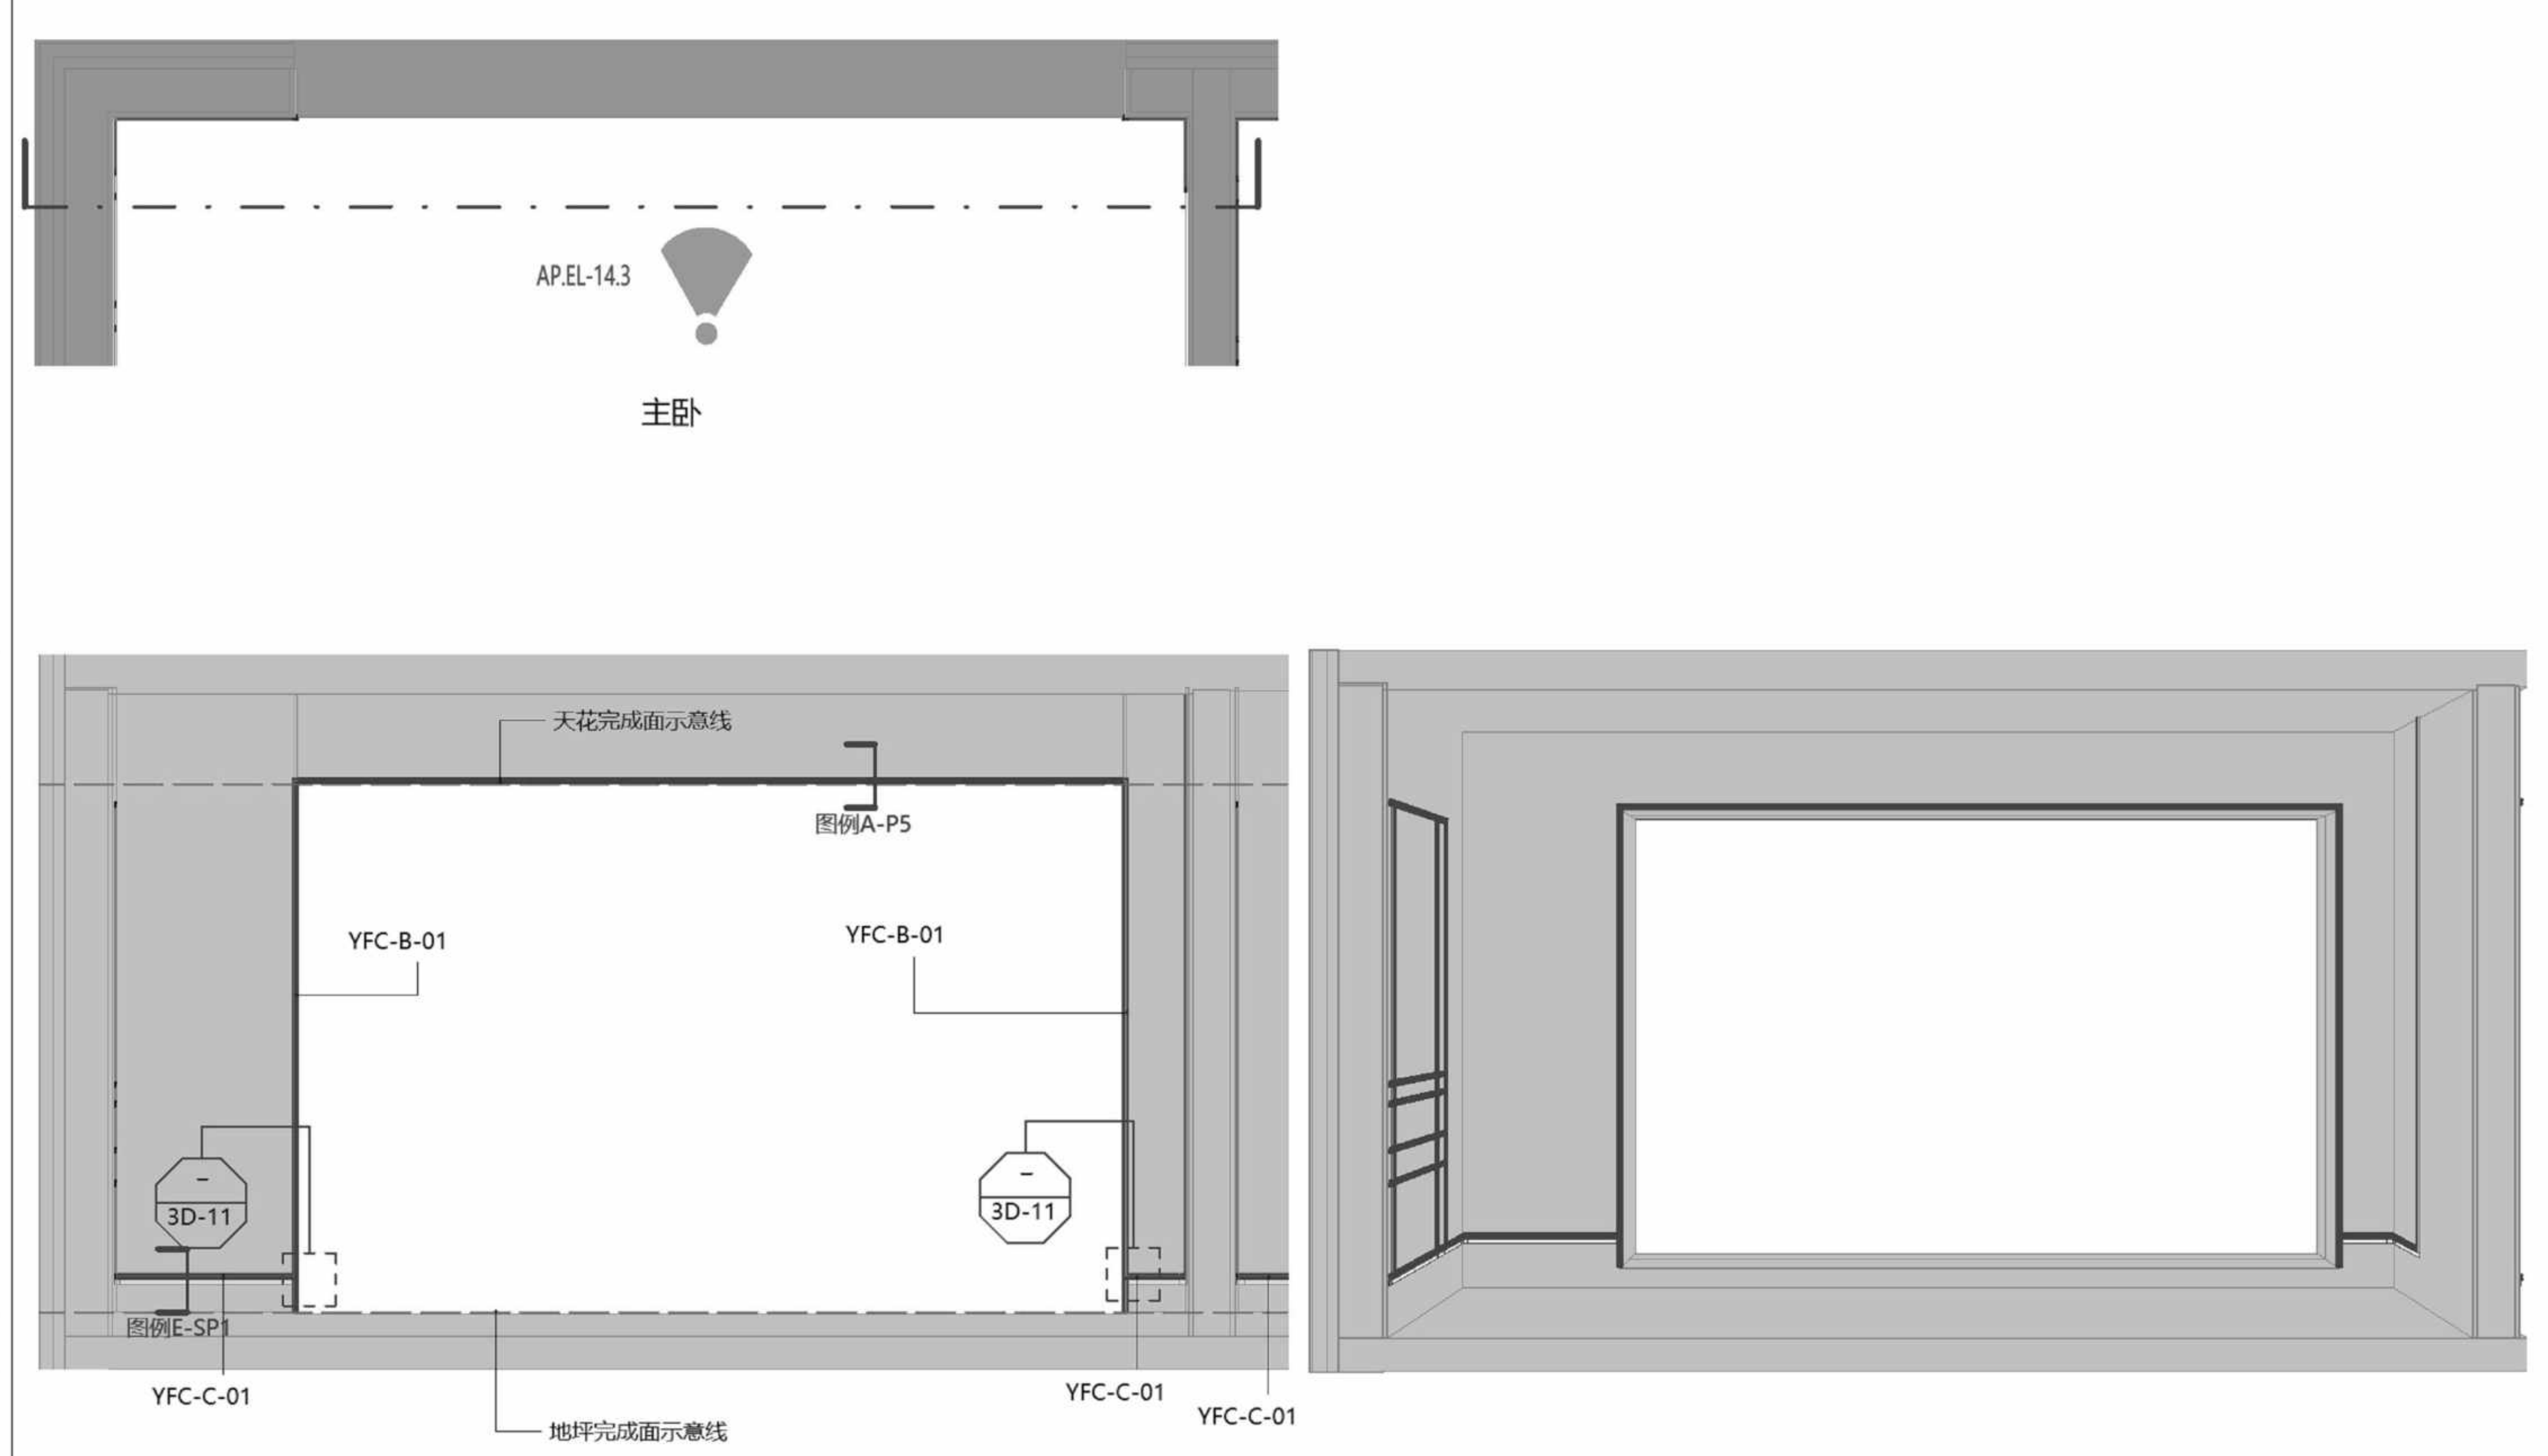

AP.EL-14.3
主卧
天花完成面示意线
图例A-P5
YFC-B-01
YFC-B-01
3D-11
3D-11
图例E-SP1
YFC-C-01
YFC-C-01
YFC-C-01
地坪完成面示意线

3 主卧 墙面及踢脚铝型材立面图3

Scale比例 1：30@A2

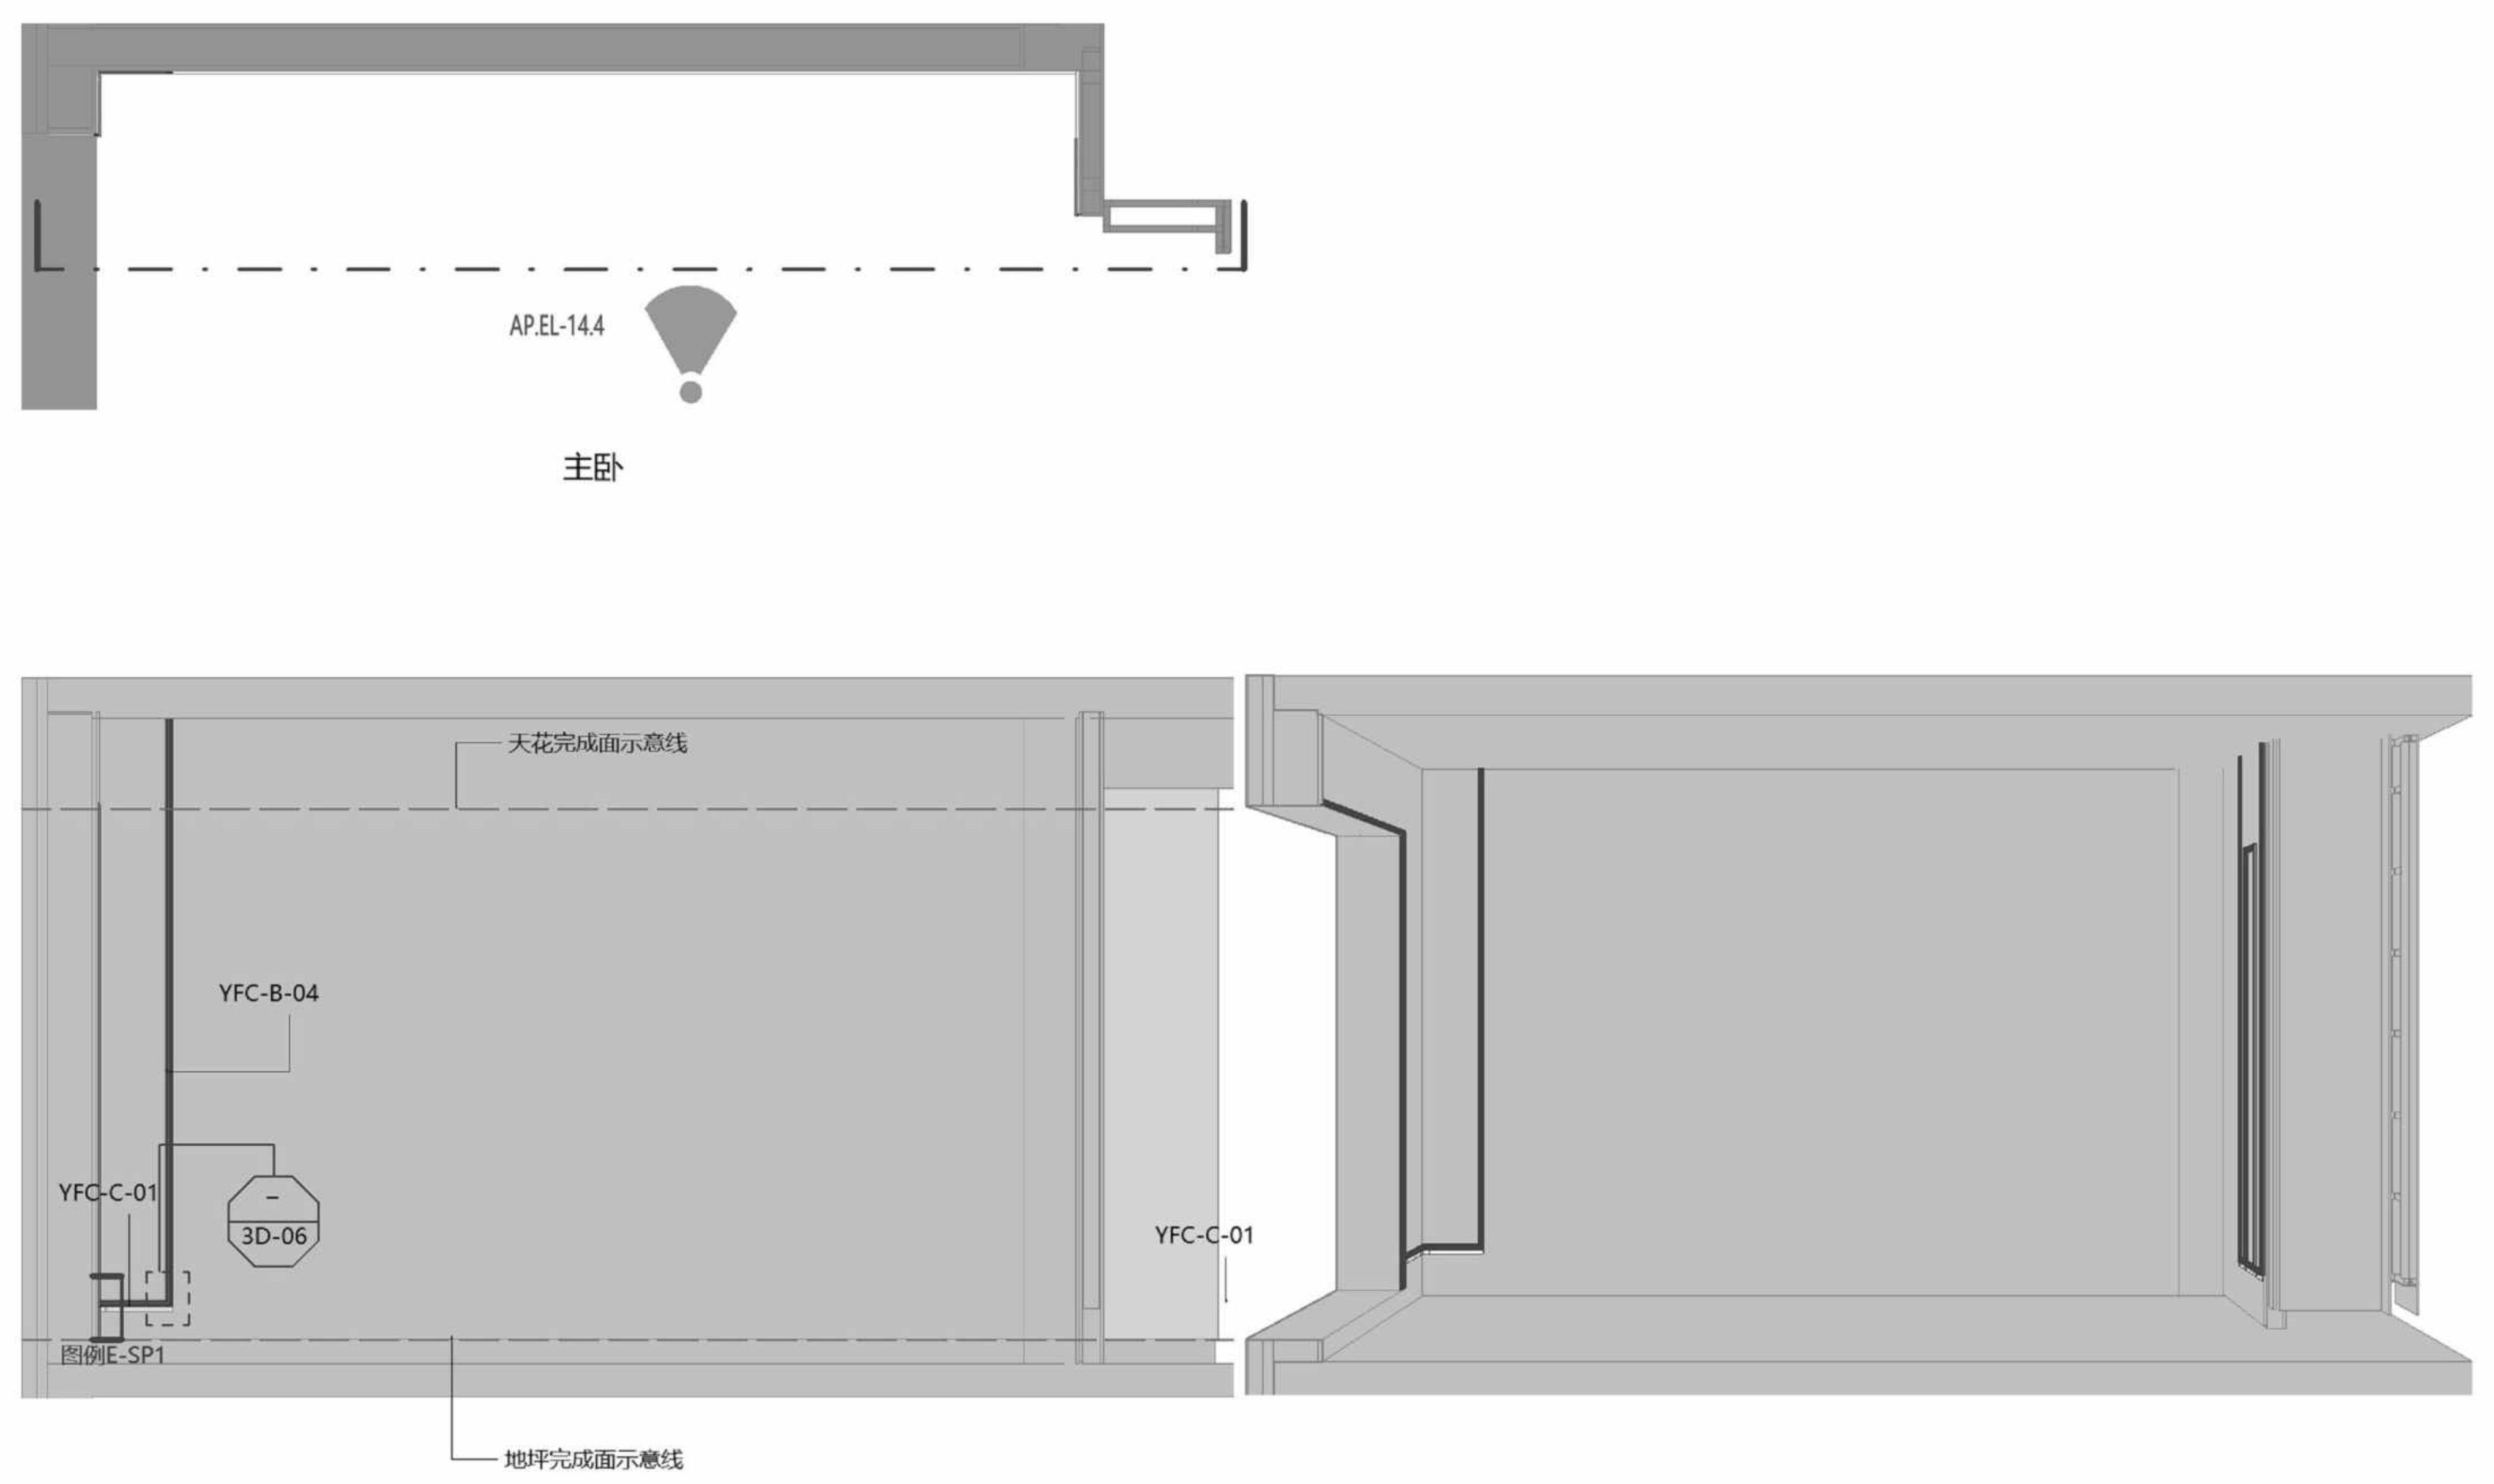

AP.EL-14.4
主卧
天花完成面示意线
YFC-B-04
YFC-C-01
3D-06
图例E-SP1
YFC-C-01
地坪完成面示意线

4 主卧 墙面及踢脚铝型材立面图4

Scale比例 1：30@A2

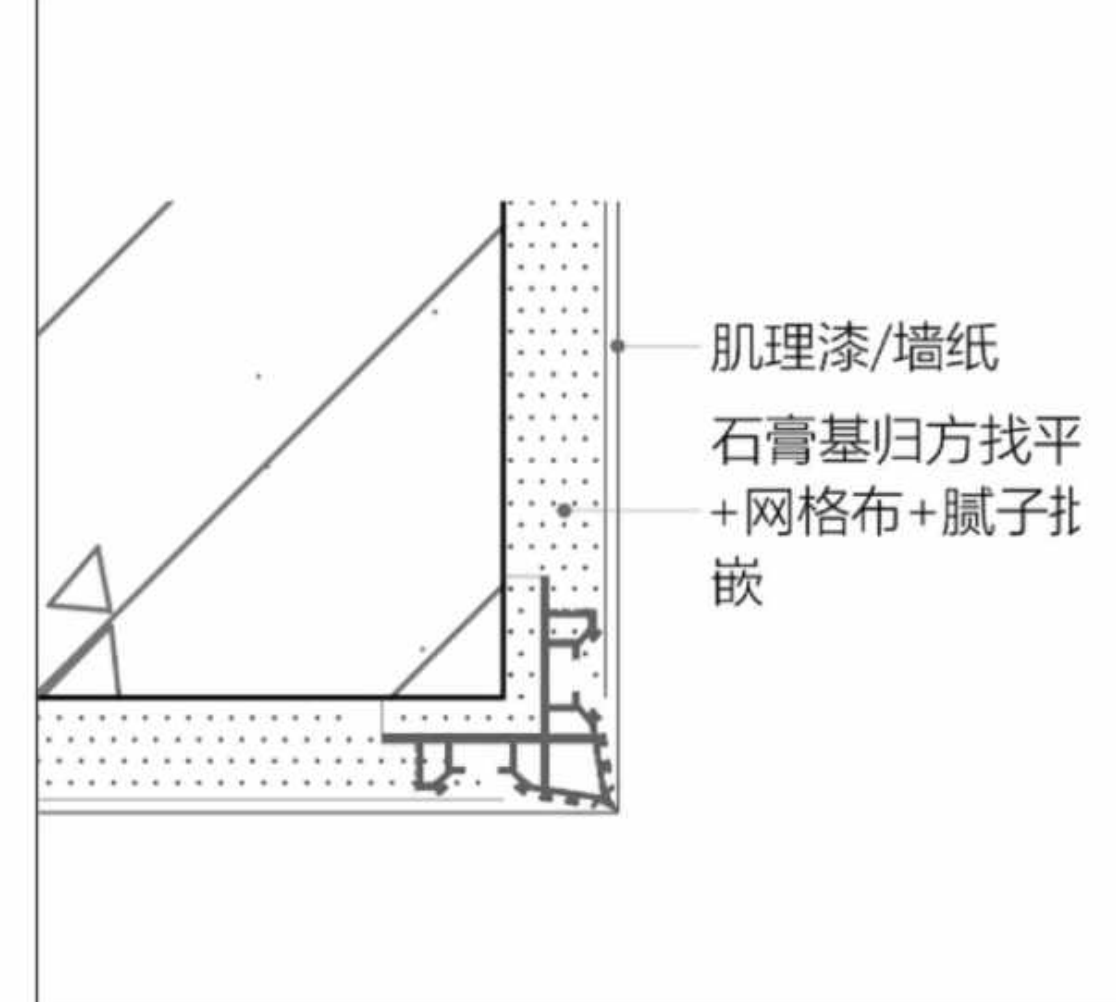

肌理漆/墙纸
石膏基归方找平
+网格布+腻子批
嵌

图例A-P1 墙面-石膏基找平铝型材

Scale比例 1：1@A2

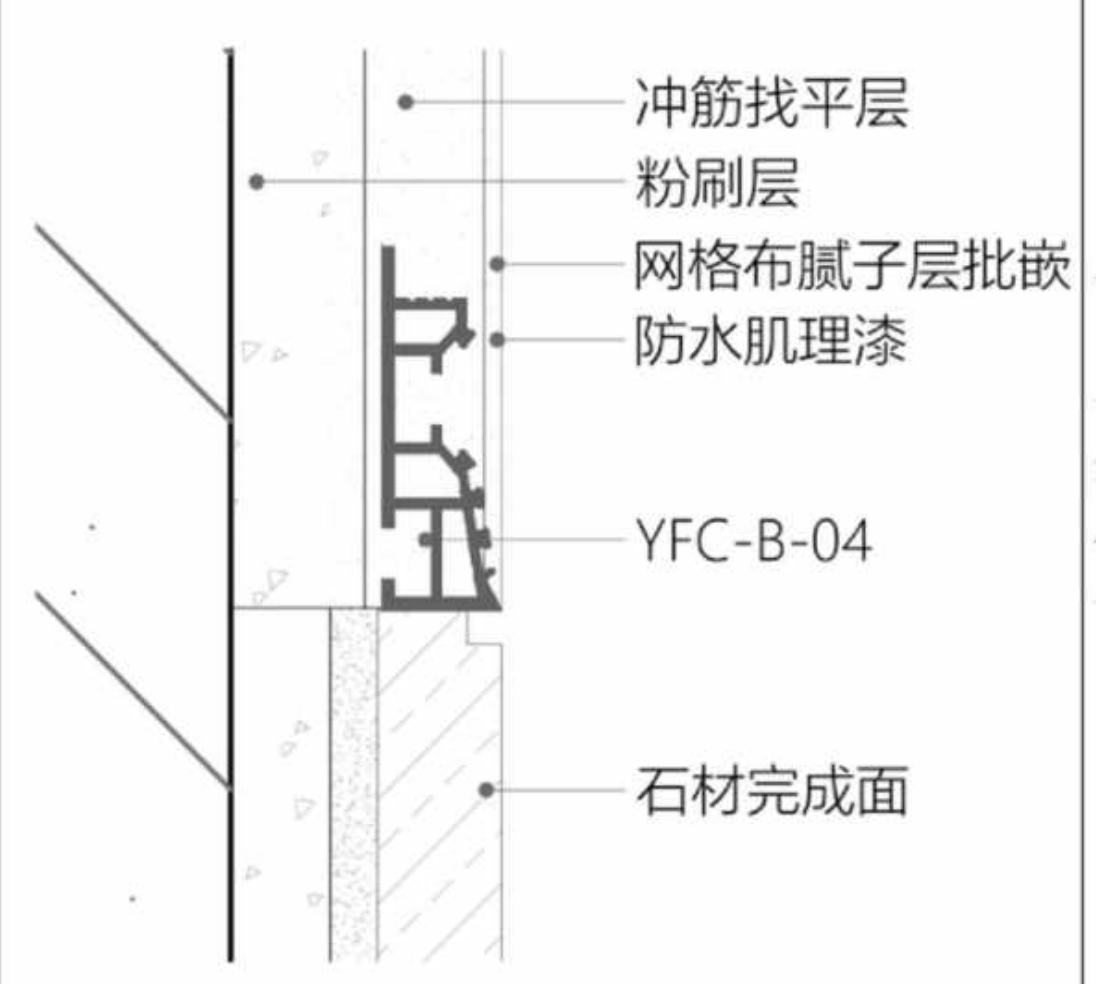

冲筋找平层
粉刷层
网格布腻子层批嵌
防水肌理漆
YFC-B-04
石材完成面

图例A-P2 墙面-石膏基找平铝型材

Scale比例 1：1@A2

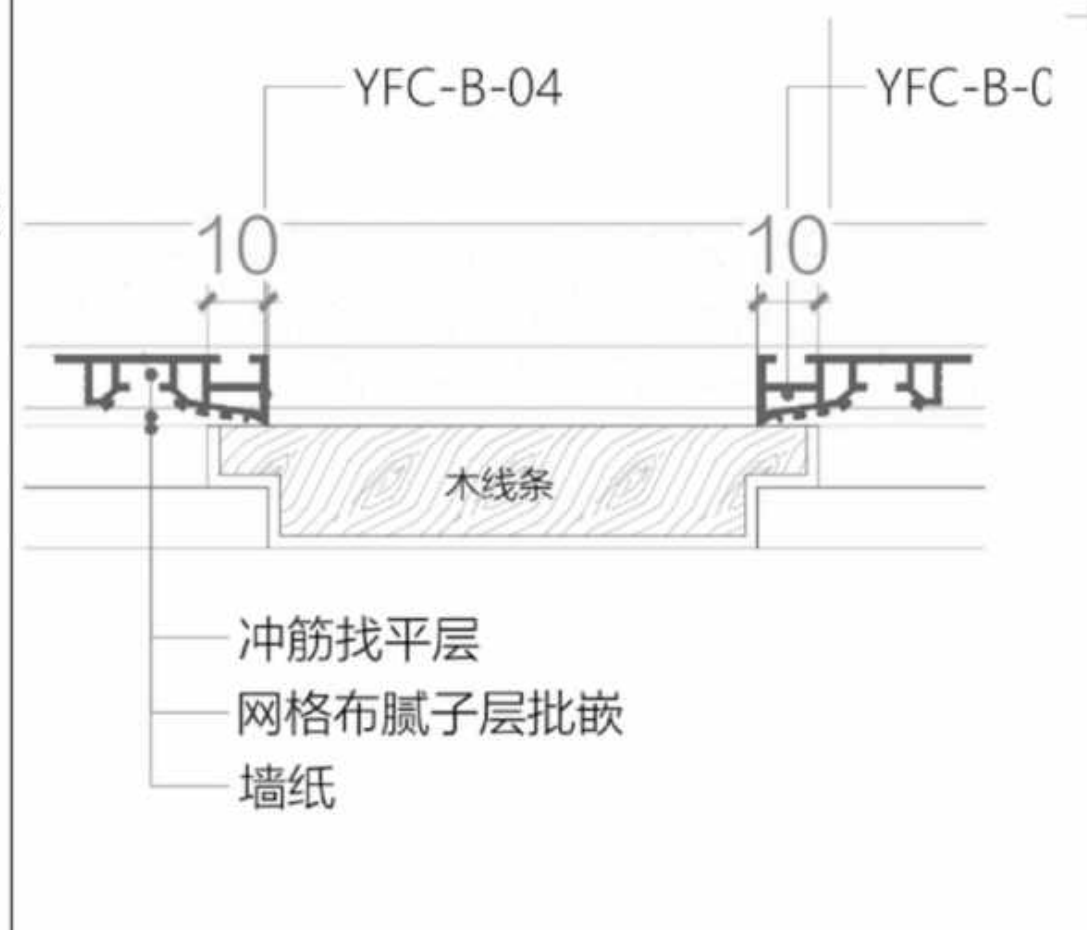

YFC-B-04
YFC-B-C
10
10
木线条
冲筋找平层
网格布腻子层批嵌
墙纸

图例A-P4 墙面-石膏基找平铝型材

Scale比例 1：1@A2

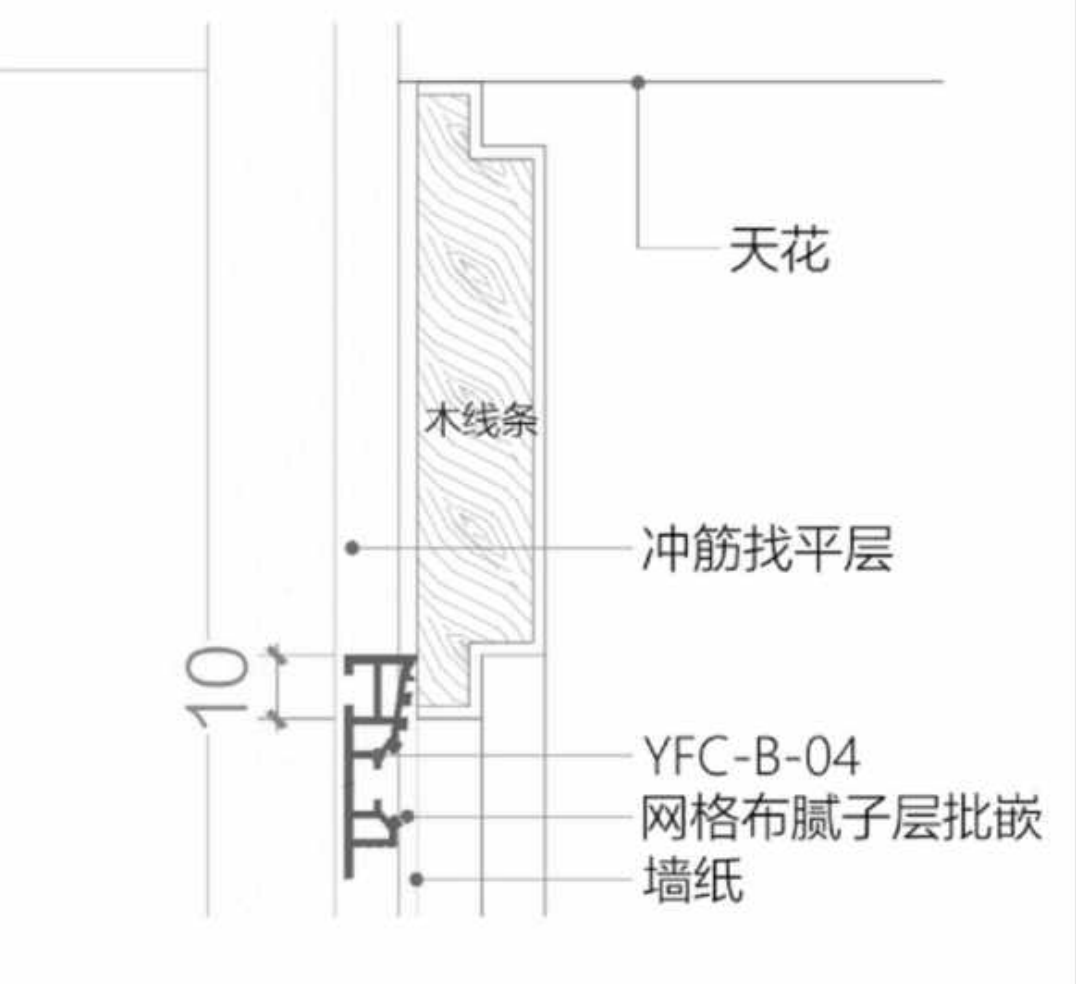

天花
木线条
冲筋找平层
10
YFC-B-04
网格布腻子层批嵌
墙纸

图例A-P5 墙面-石膏基找平铝型材

Scale比例 1：1@A2

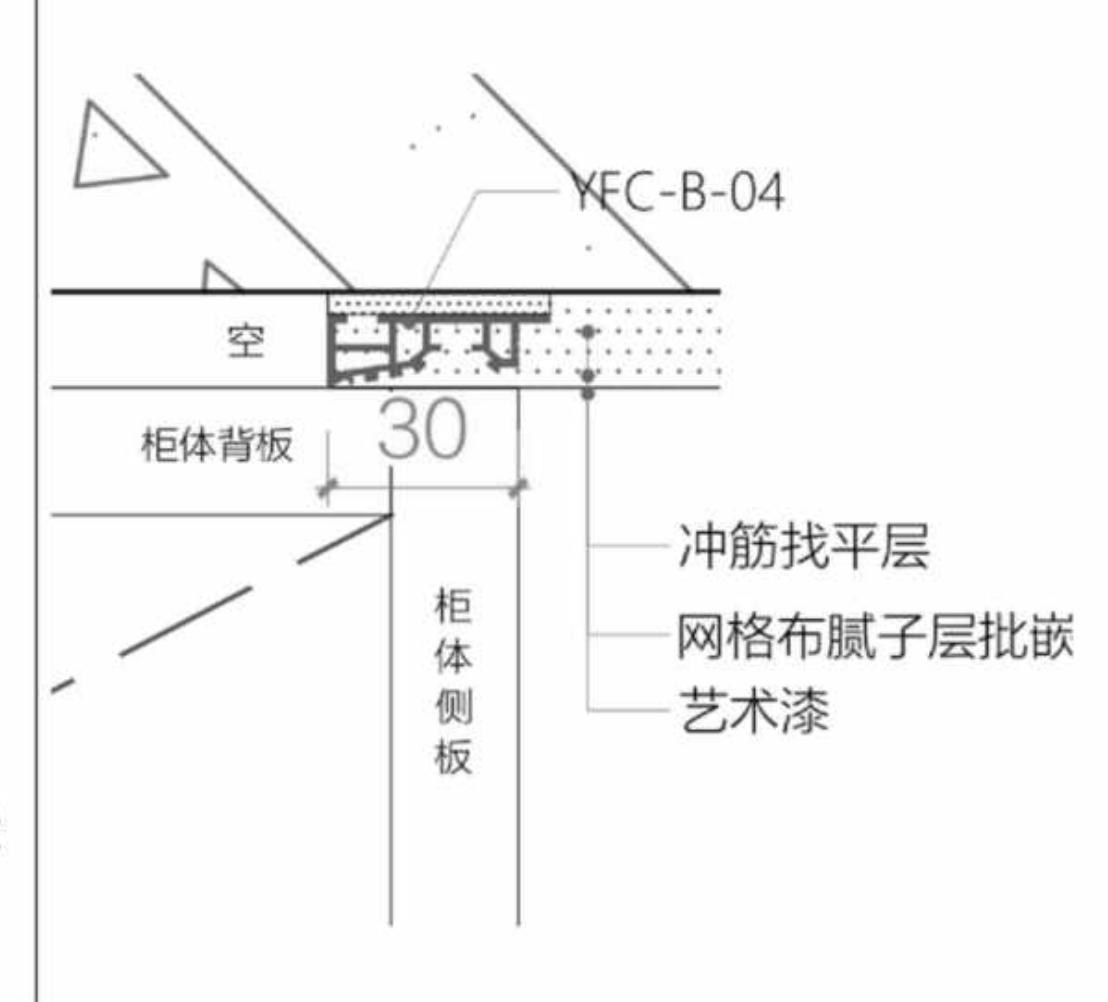

YFC-B-04
空
柜体背板
30
柜体侧板
冲筋找平层
网格布腻子层批嵌
艺术漆

图例B-P7 柜边-石膏基找平铝型材

Scale比例 1：1@A2

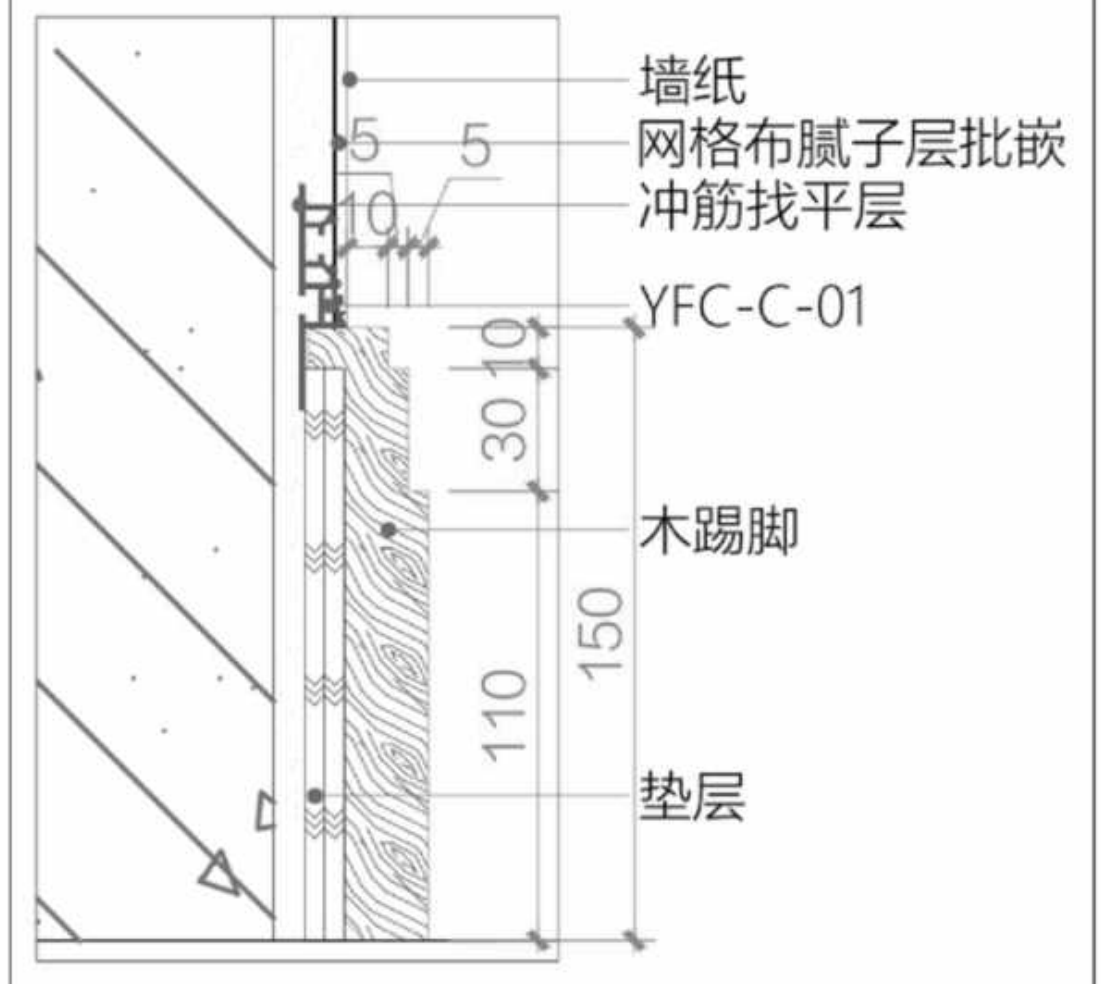

墙纸
网格布腻子层批嵌
冲筋找平层
5
5
10
YFC-C-01
10
30
木踢脚
150
110
垫层

图例E-SP1 踢脚-石膏基找平铝型材

Scale比例 1：1@A2

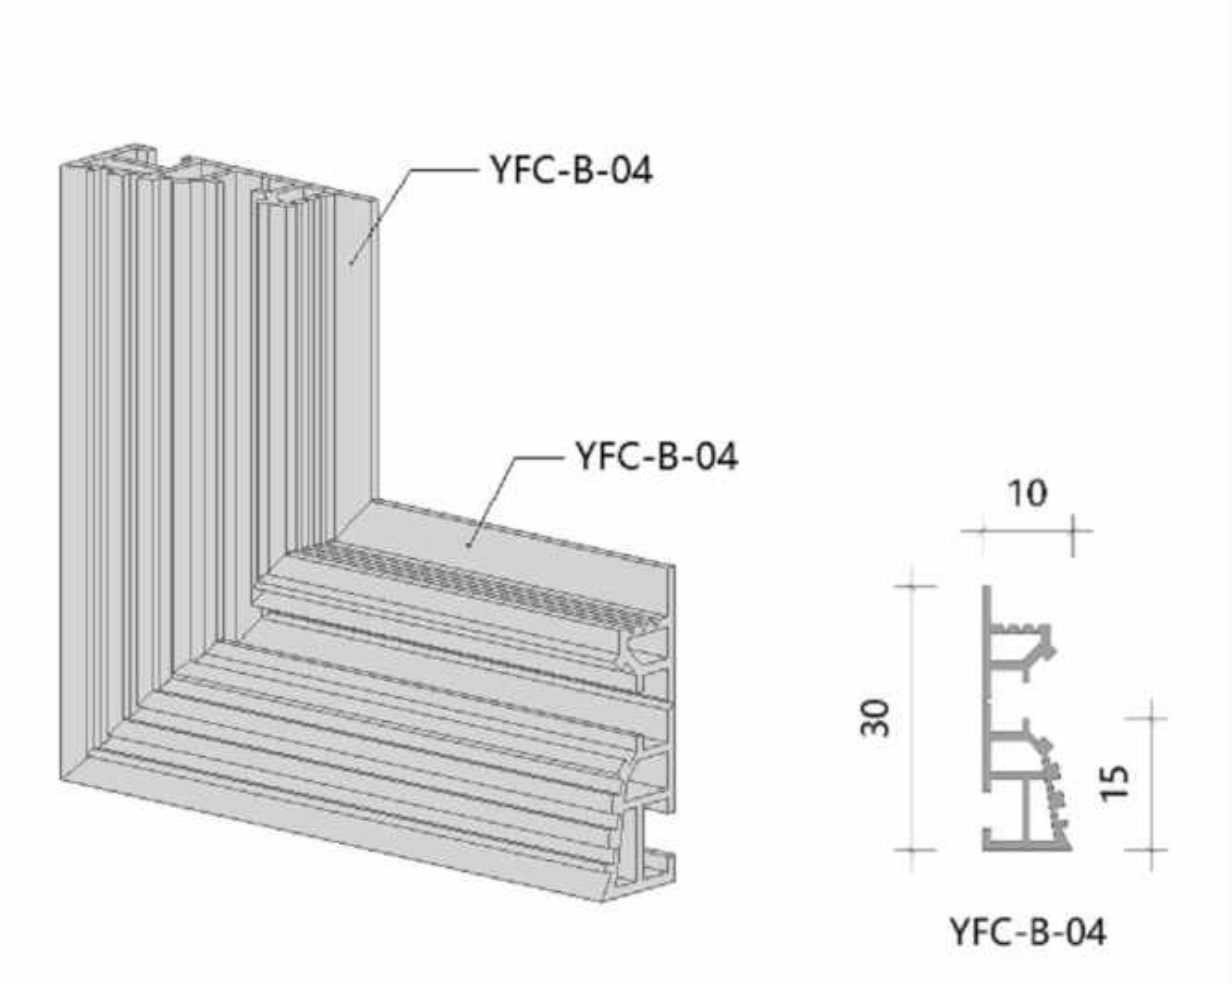

YFC-B-04
YFC-B-04
10
30
15
YFC-B-04

3D-01 转角铝型材-拼接跟通

转角数量：4

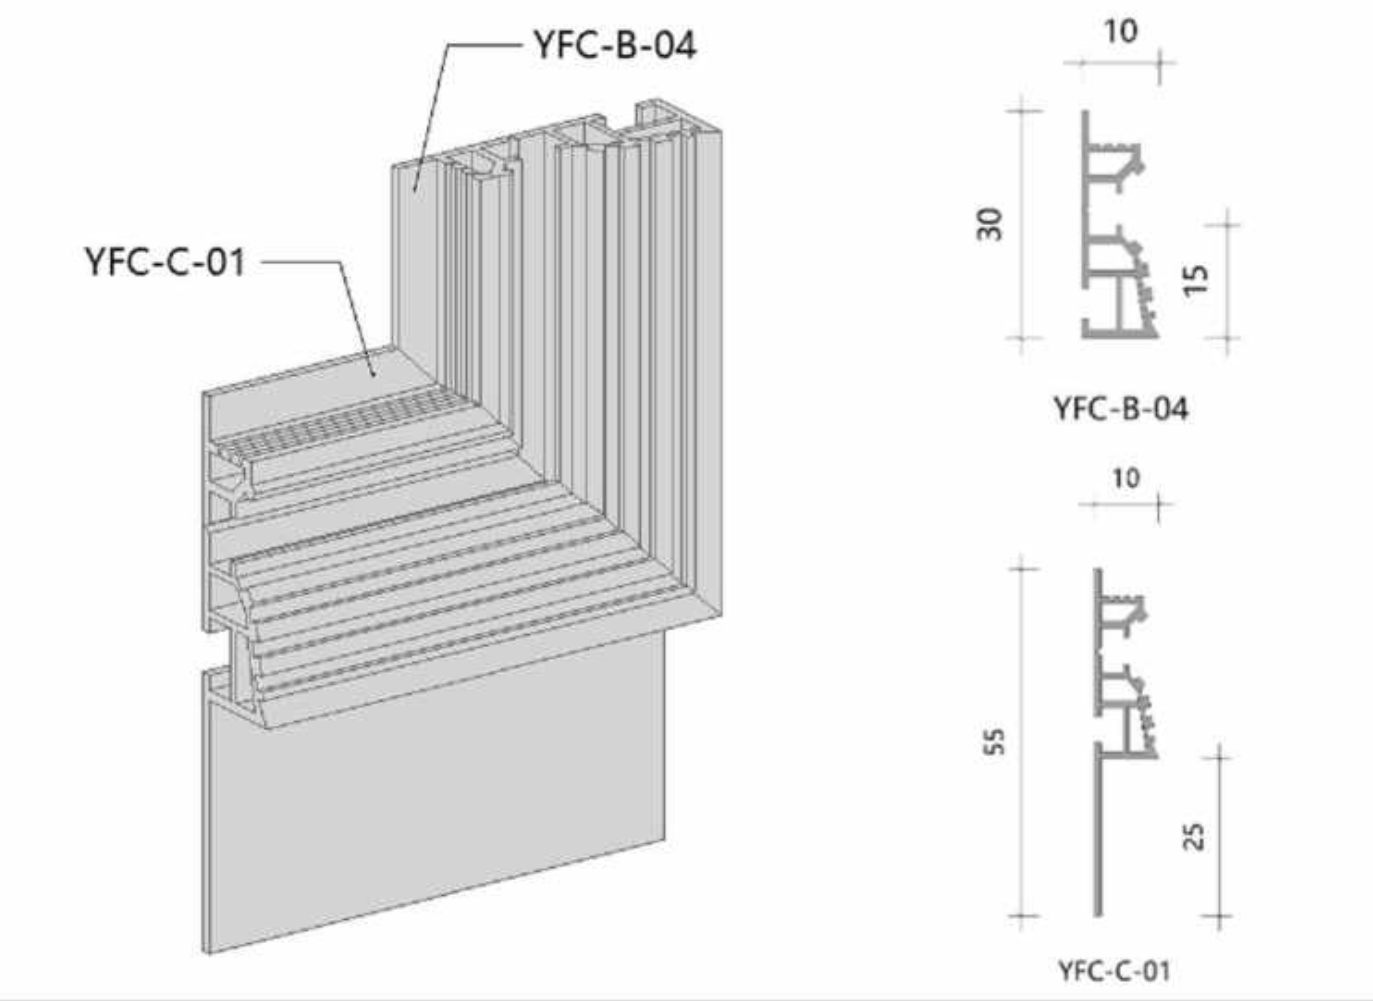

YFC-B-04
YFC-C-01
10
30
15
YFC-B-04
10
55
25
YFC-C-01

3D-06 转角铝型材-拼接跟通

转角数量：2

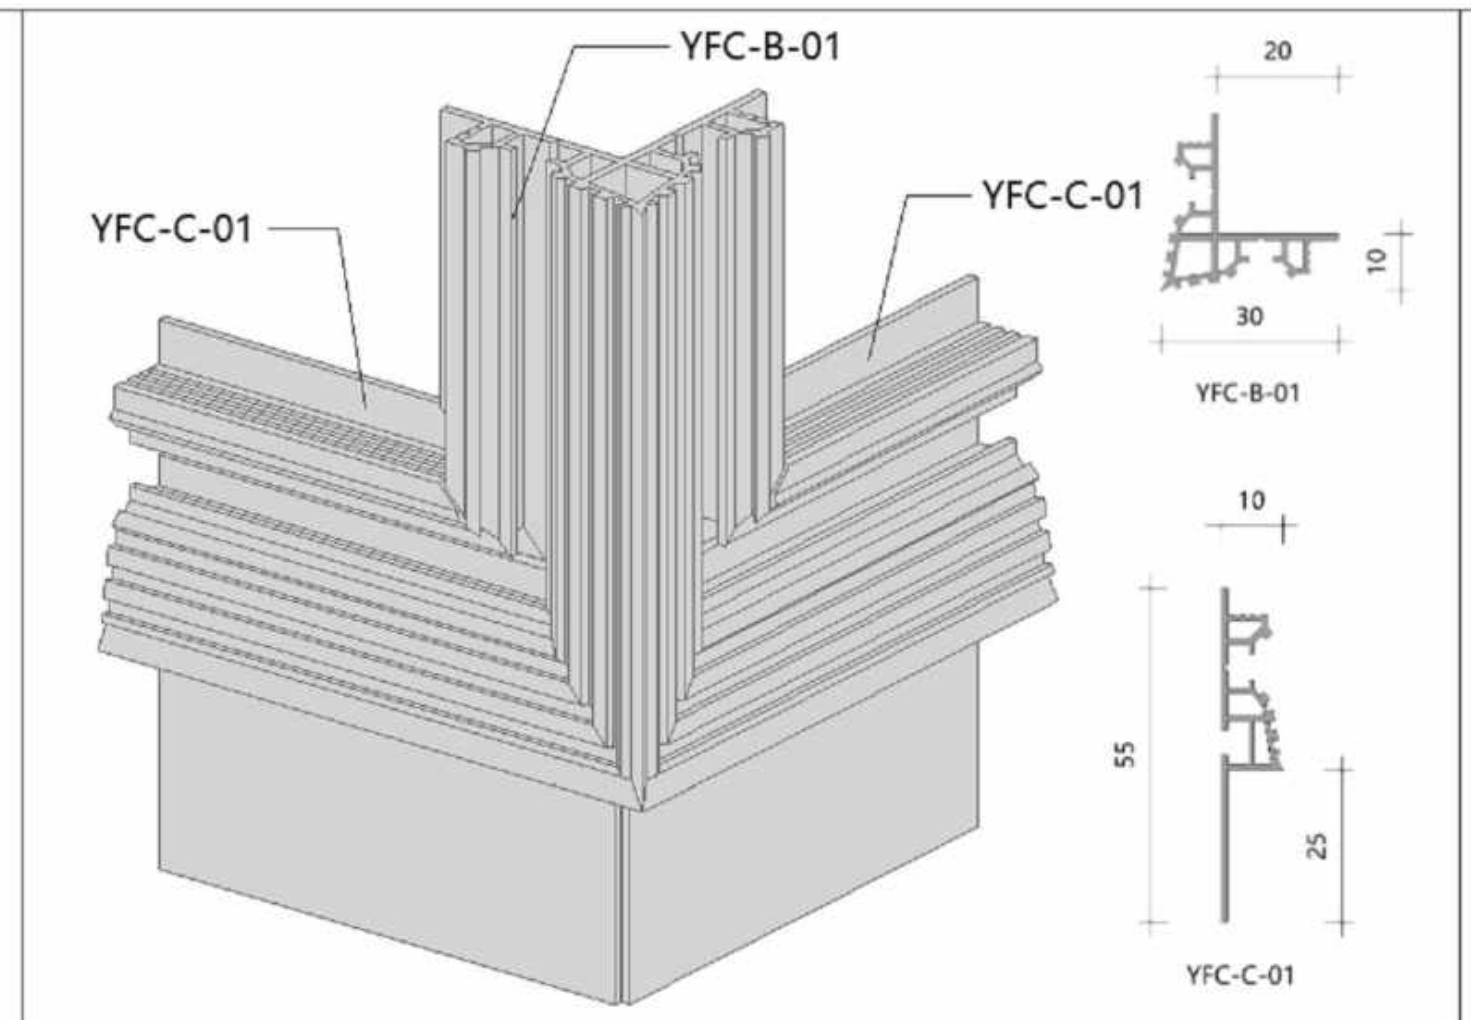

YFC-B-01
YFC-C-01
YFC-C-01
20
30
10
YFC-B-01
10
55
25
YFC-C-01

3D-11 转角铝型材-拼接跟通

转角数量：2

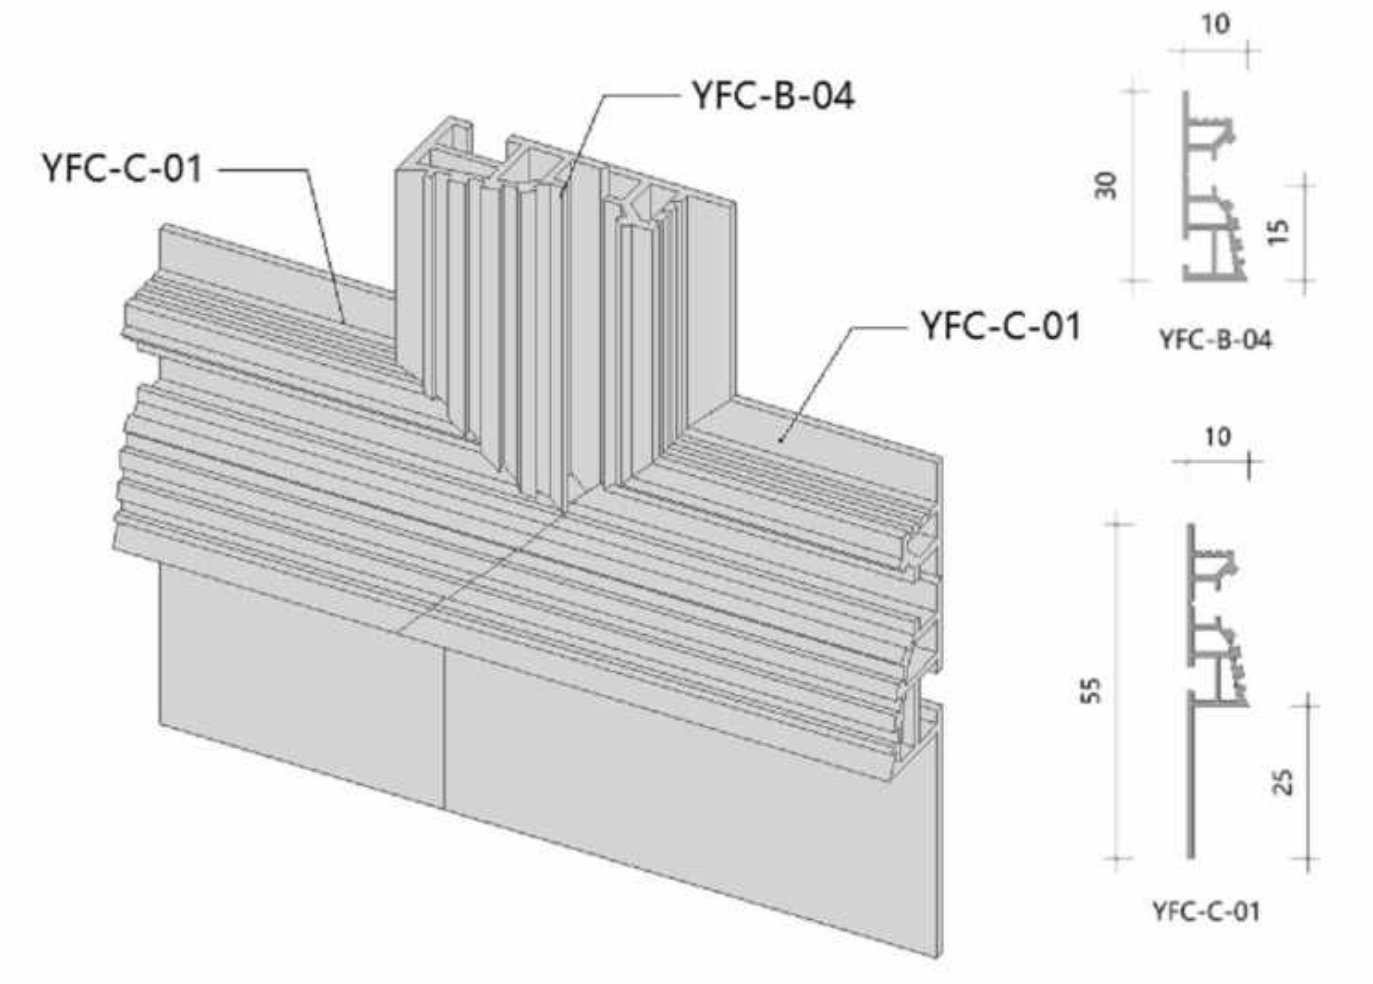

YFC-C-01
YFC-B-04
YFC-C-01
10
30
15
YFC-B-04
10
55
25
YFC-C-01

3D-13 转角铝型材-拼接跟通

转角数量：11

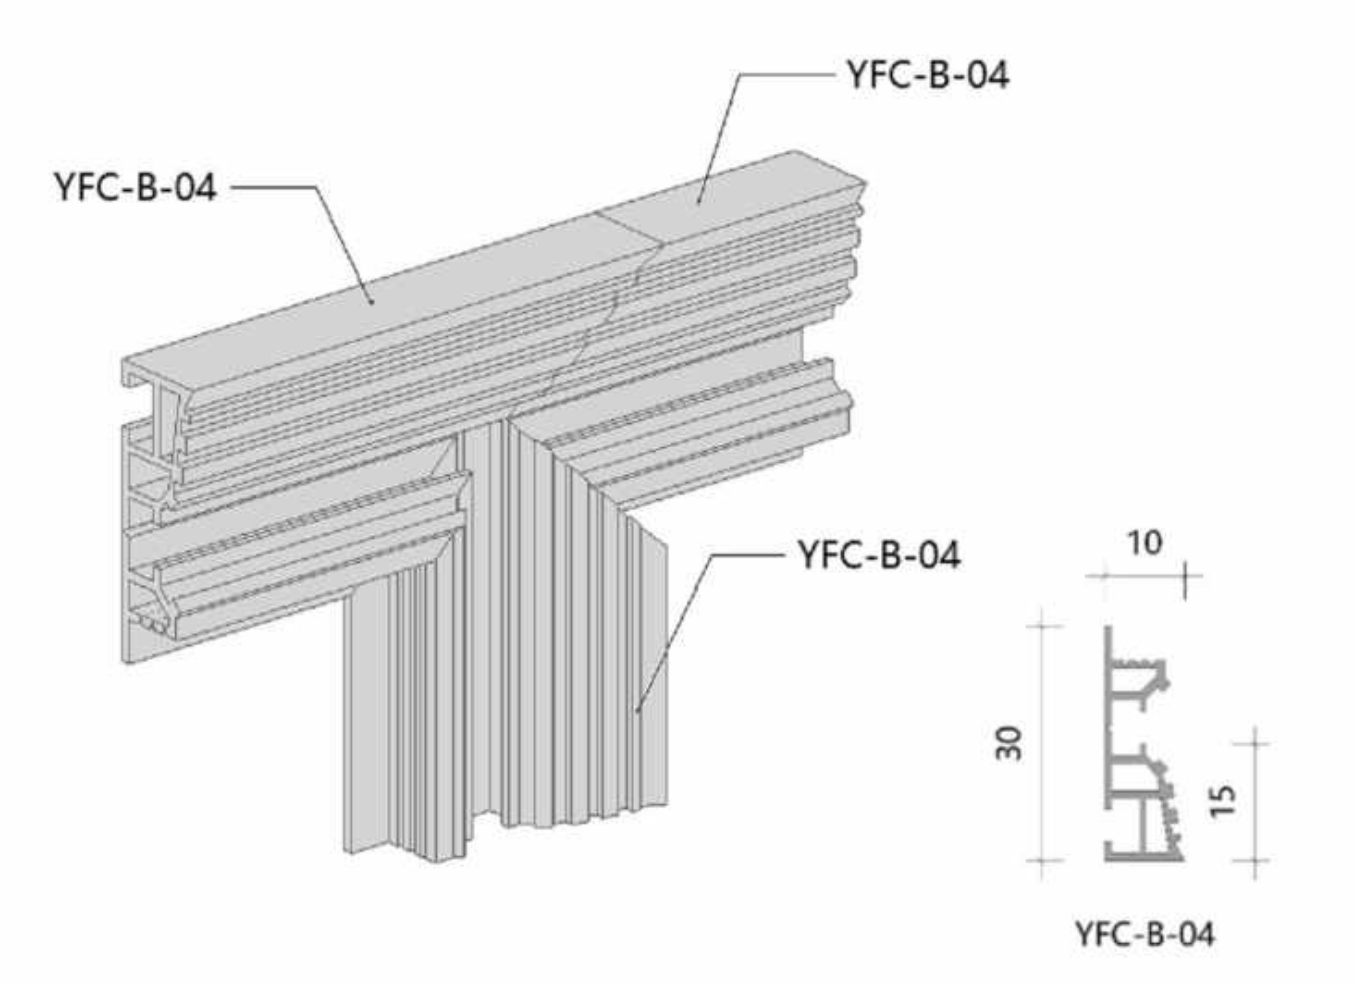

YFC-B-04
YFC-B-04
YFC-B-04
10
30
15
YFC-B-04

3D-14 转角铝型材-拼接跟通

转角数量：12

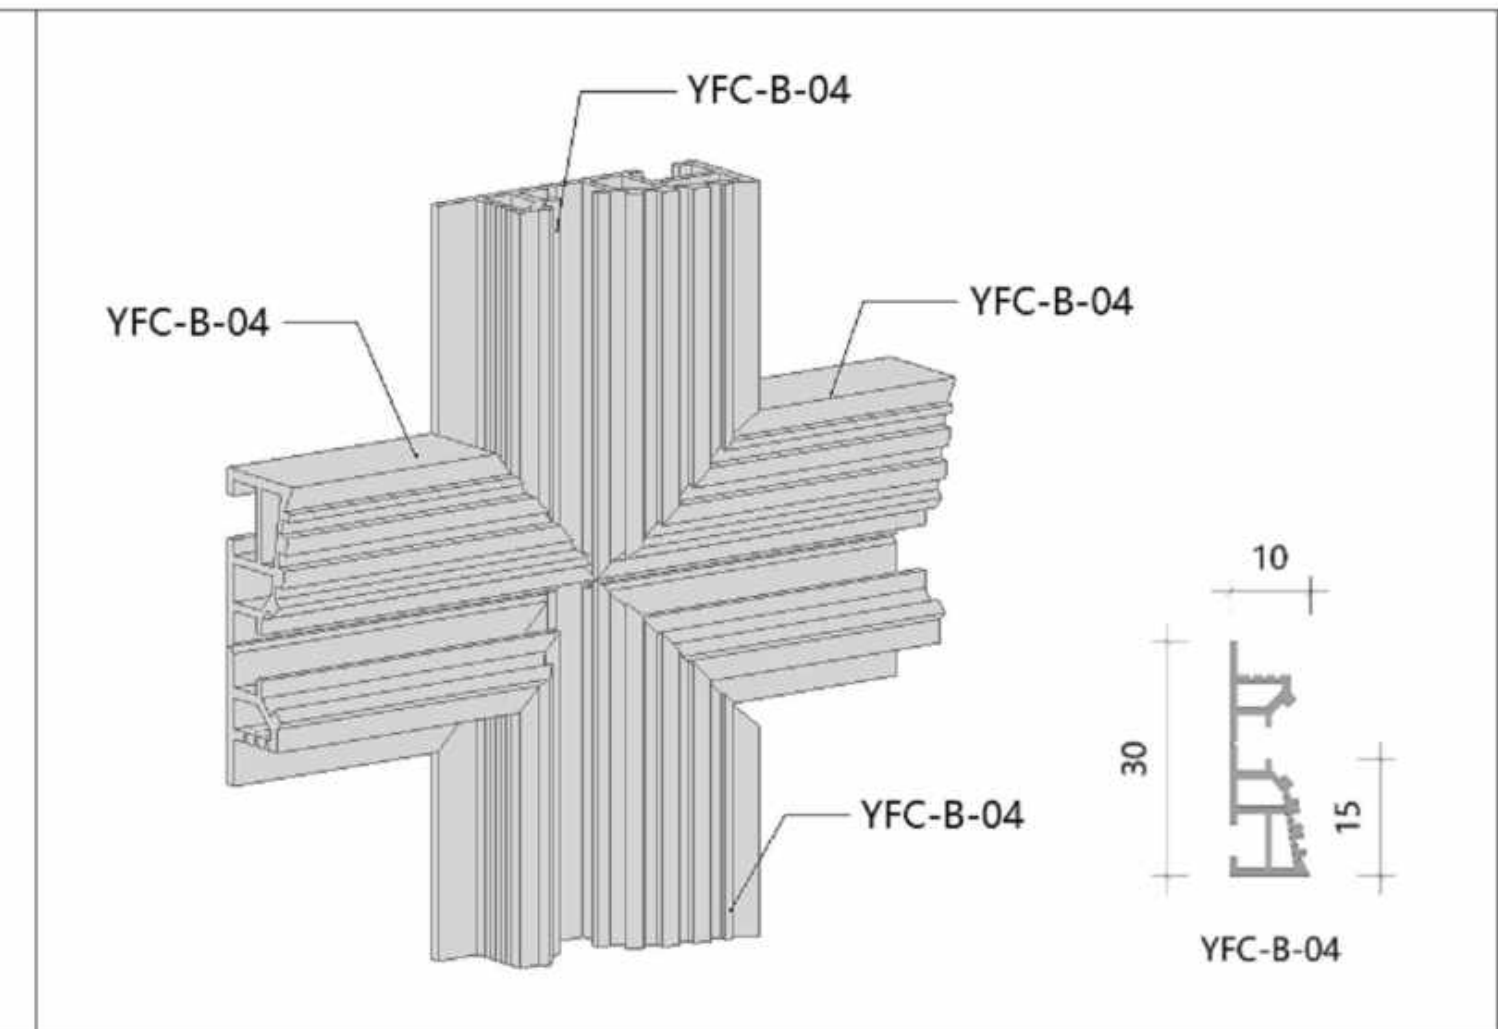

YFC-B-04
YFC-B-04
YFC-B-04
YFC-B-04
10
30
15
YFC-B-04

3D-15 转角铝型材-拼接跟通

转角数量：32

盖章

注释
Notes

1.本图纸如与现场尺寸有误，请施工人员与项目负责人联系。
2.施工前施工人员应认真查阅此图，如有不明确尺寸，按现场测量为准。
3.本图纸必须经甲乙双方认可并签字方可作为施工依据。

日期
Date 03/04/26

修订
Revision

1

项目
Project
潮映华岸府3-801

比例
Scale 1：30@A2

主卧

墙面及踢脚铝型材

图纸编号
Drawing No.
AP.EL-14

项目编号
Project No.

©2025