


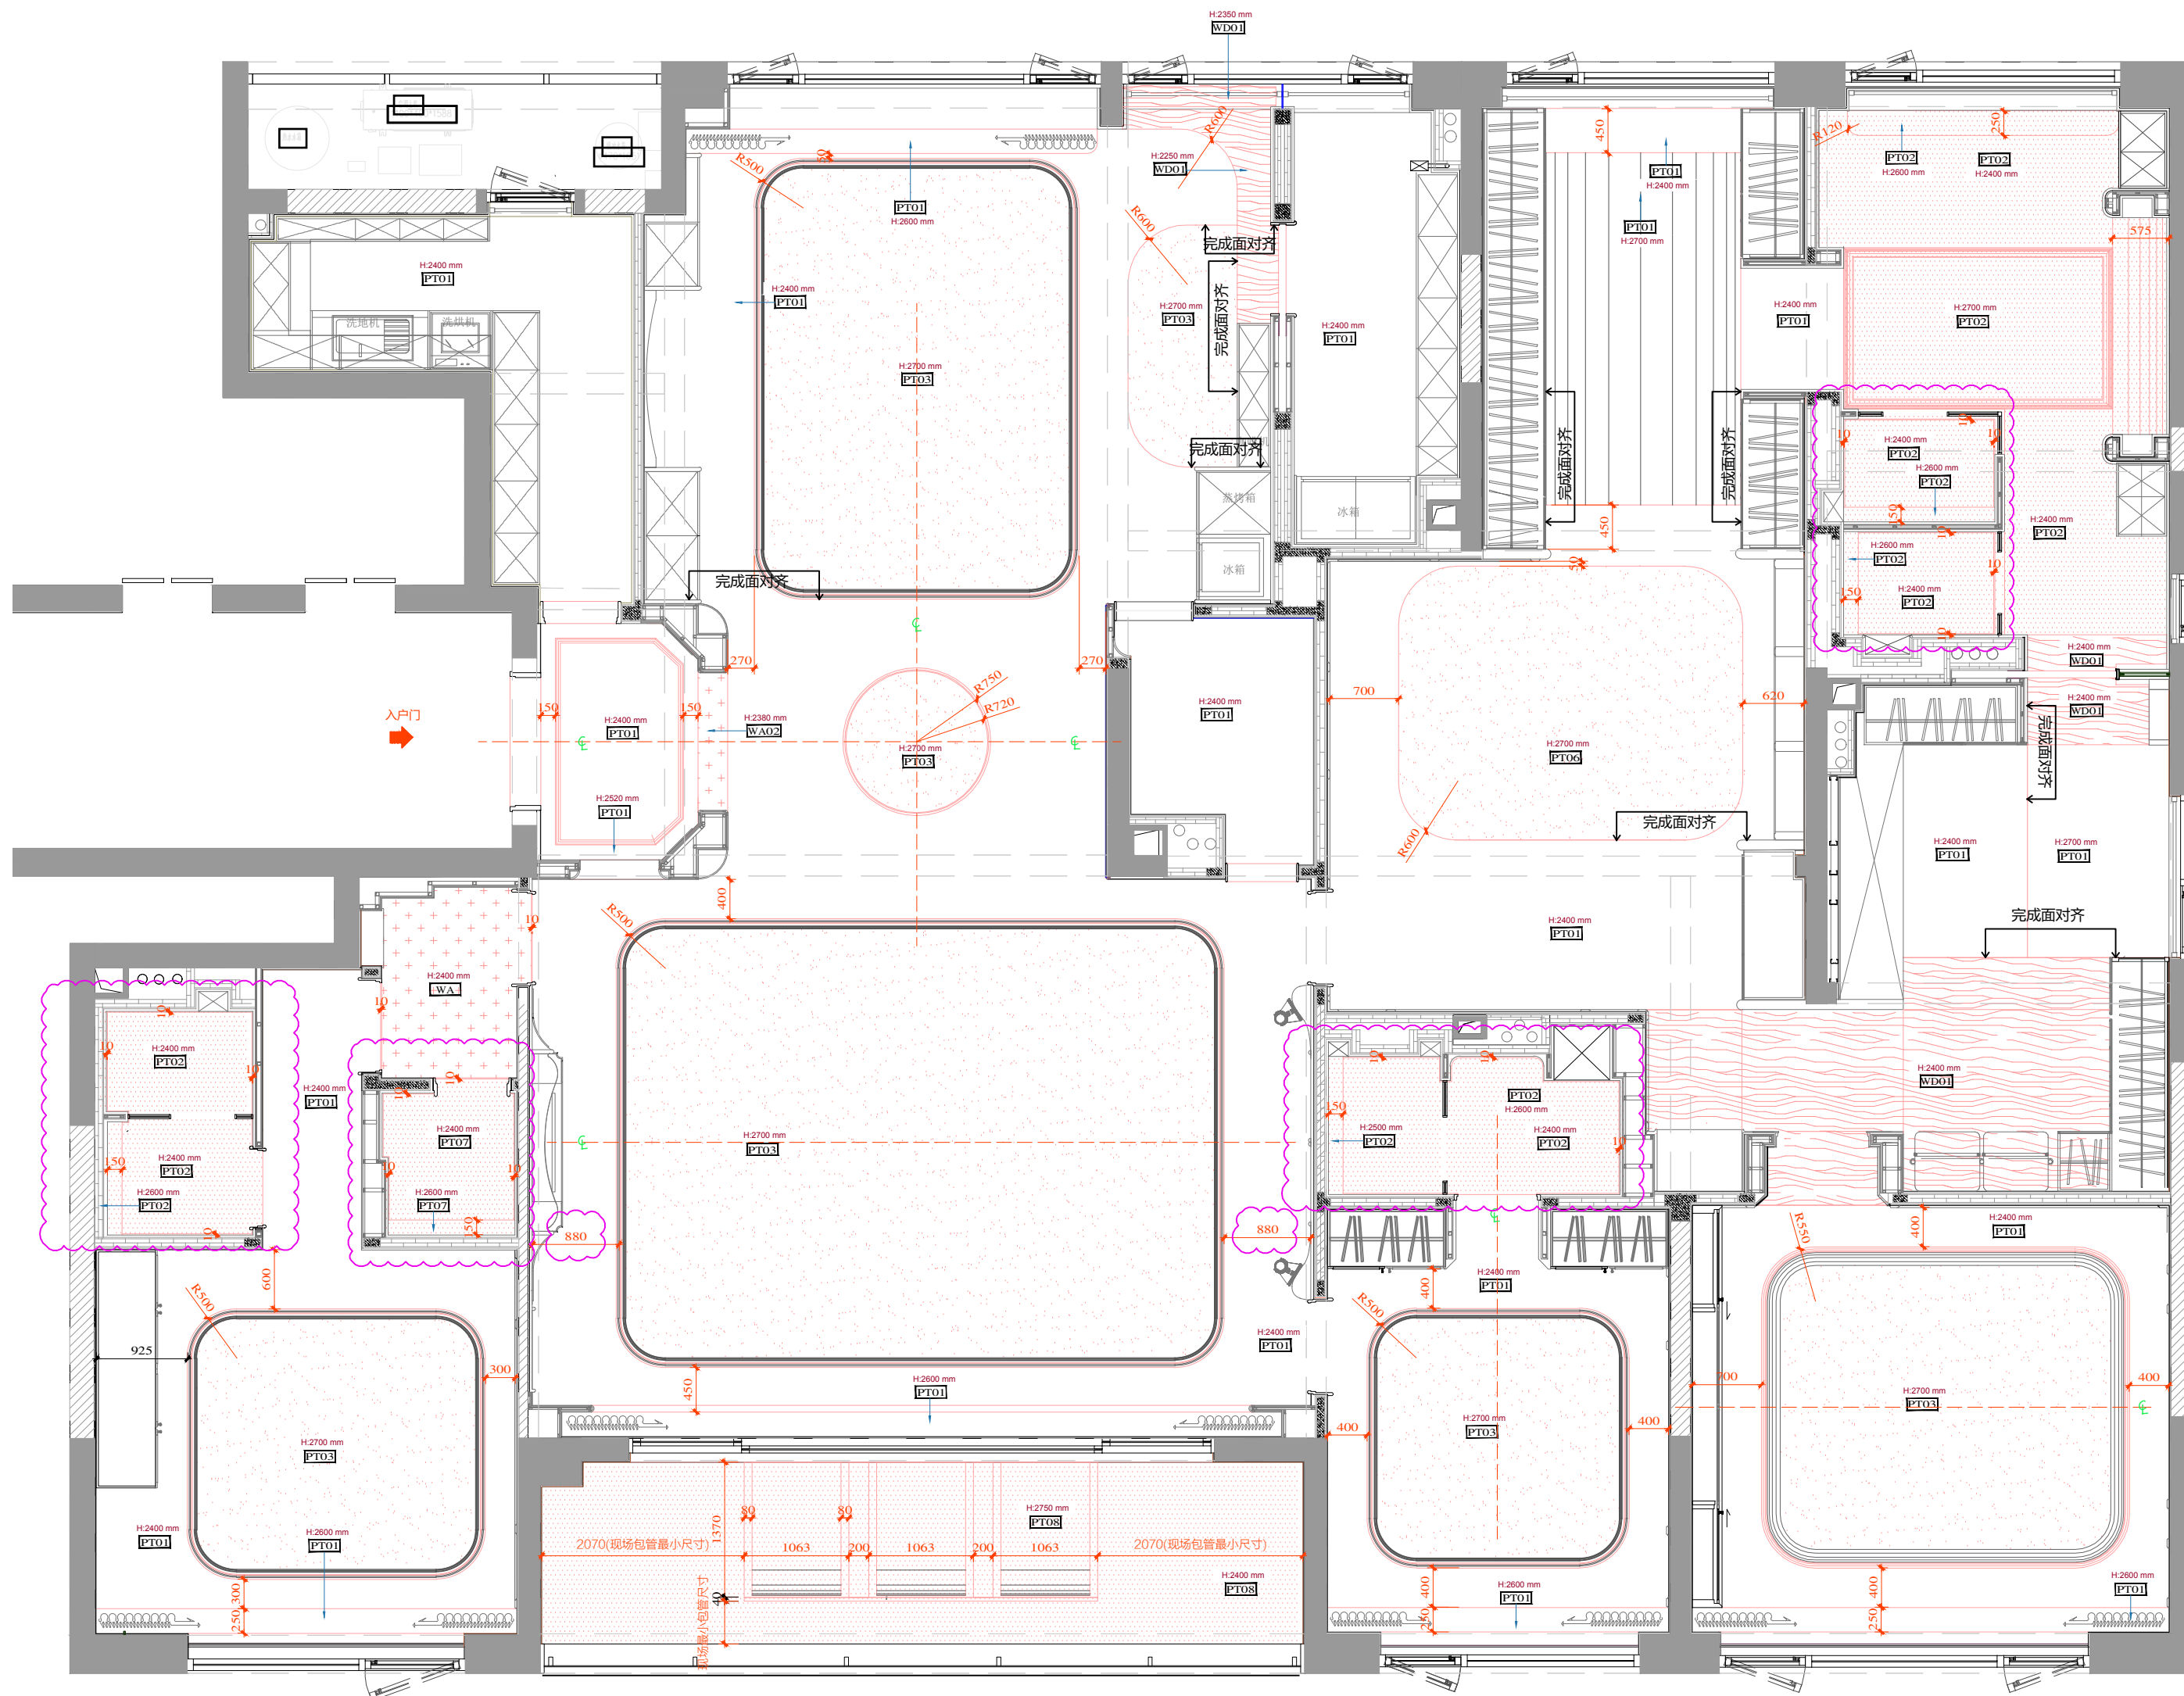

2026.5.6变更: 次卫灯槽位置调整。
2026.6.2变更: 卫生间天花增加10*10凹槽,客厅吊顶宽度由750改为880。

天花完成面尺寸图

Scale比例 1:60@A2

注释
Notes

1. 本图纸尺寸如与现场尺寸有误, 请施工人员与项目负责人联系。
2. 施工前施工人员应认真查阅此图, 如有不明确尺寸, 按现场测量为准。
3. 本图纸必须经甲乙双方认可并签字方可作为施工依据。

LEGEND A

编号	图例示意	说明
①		乳胶漆
②		防水乳胶漆
③		肌理漆
④		墙纸
⑤		木饰面

正式施工图
26-06-02

日期
Date 2026.3.27修订
Revisions项目
Project


杭州 华岸府

Scale
比例 1:60 @A2Drawing No.
图纸编号

CL.PL-02

Project No.
项目编号

© 2025

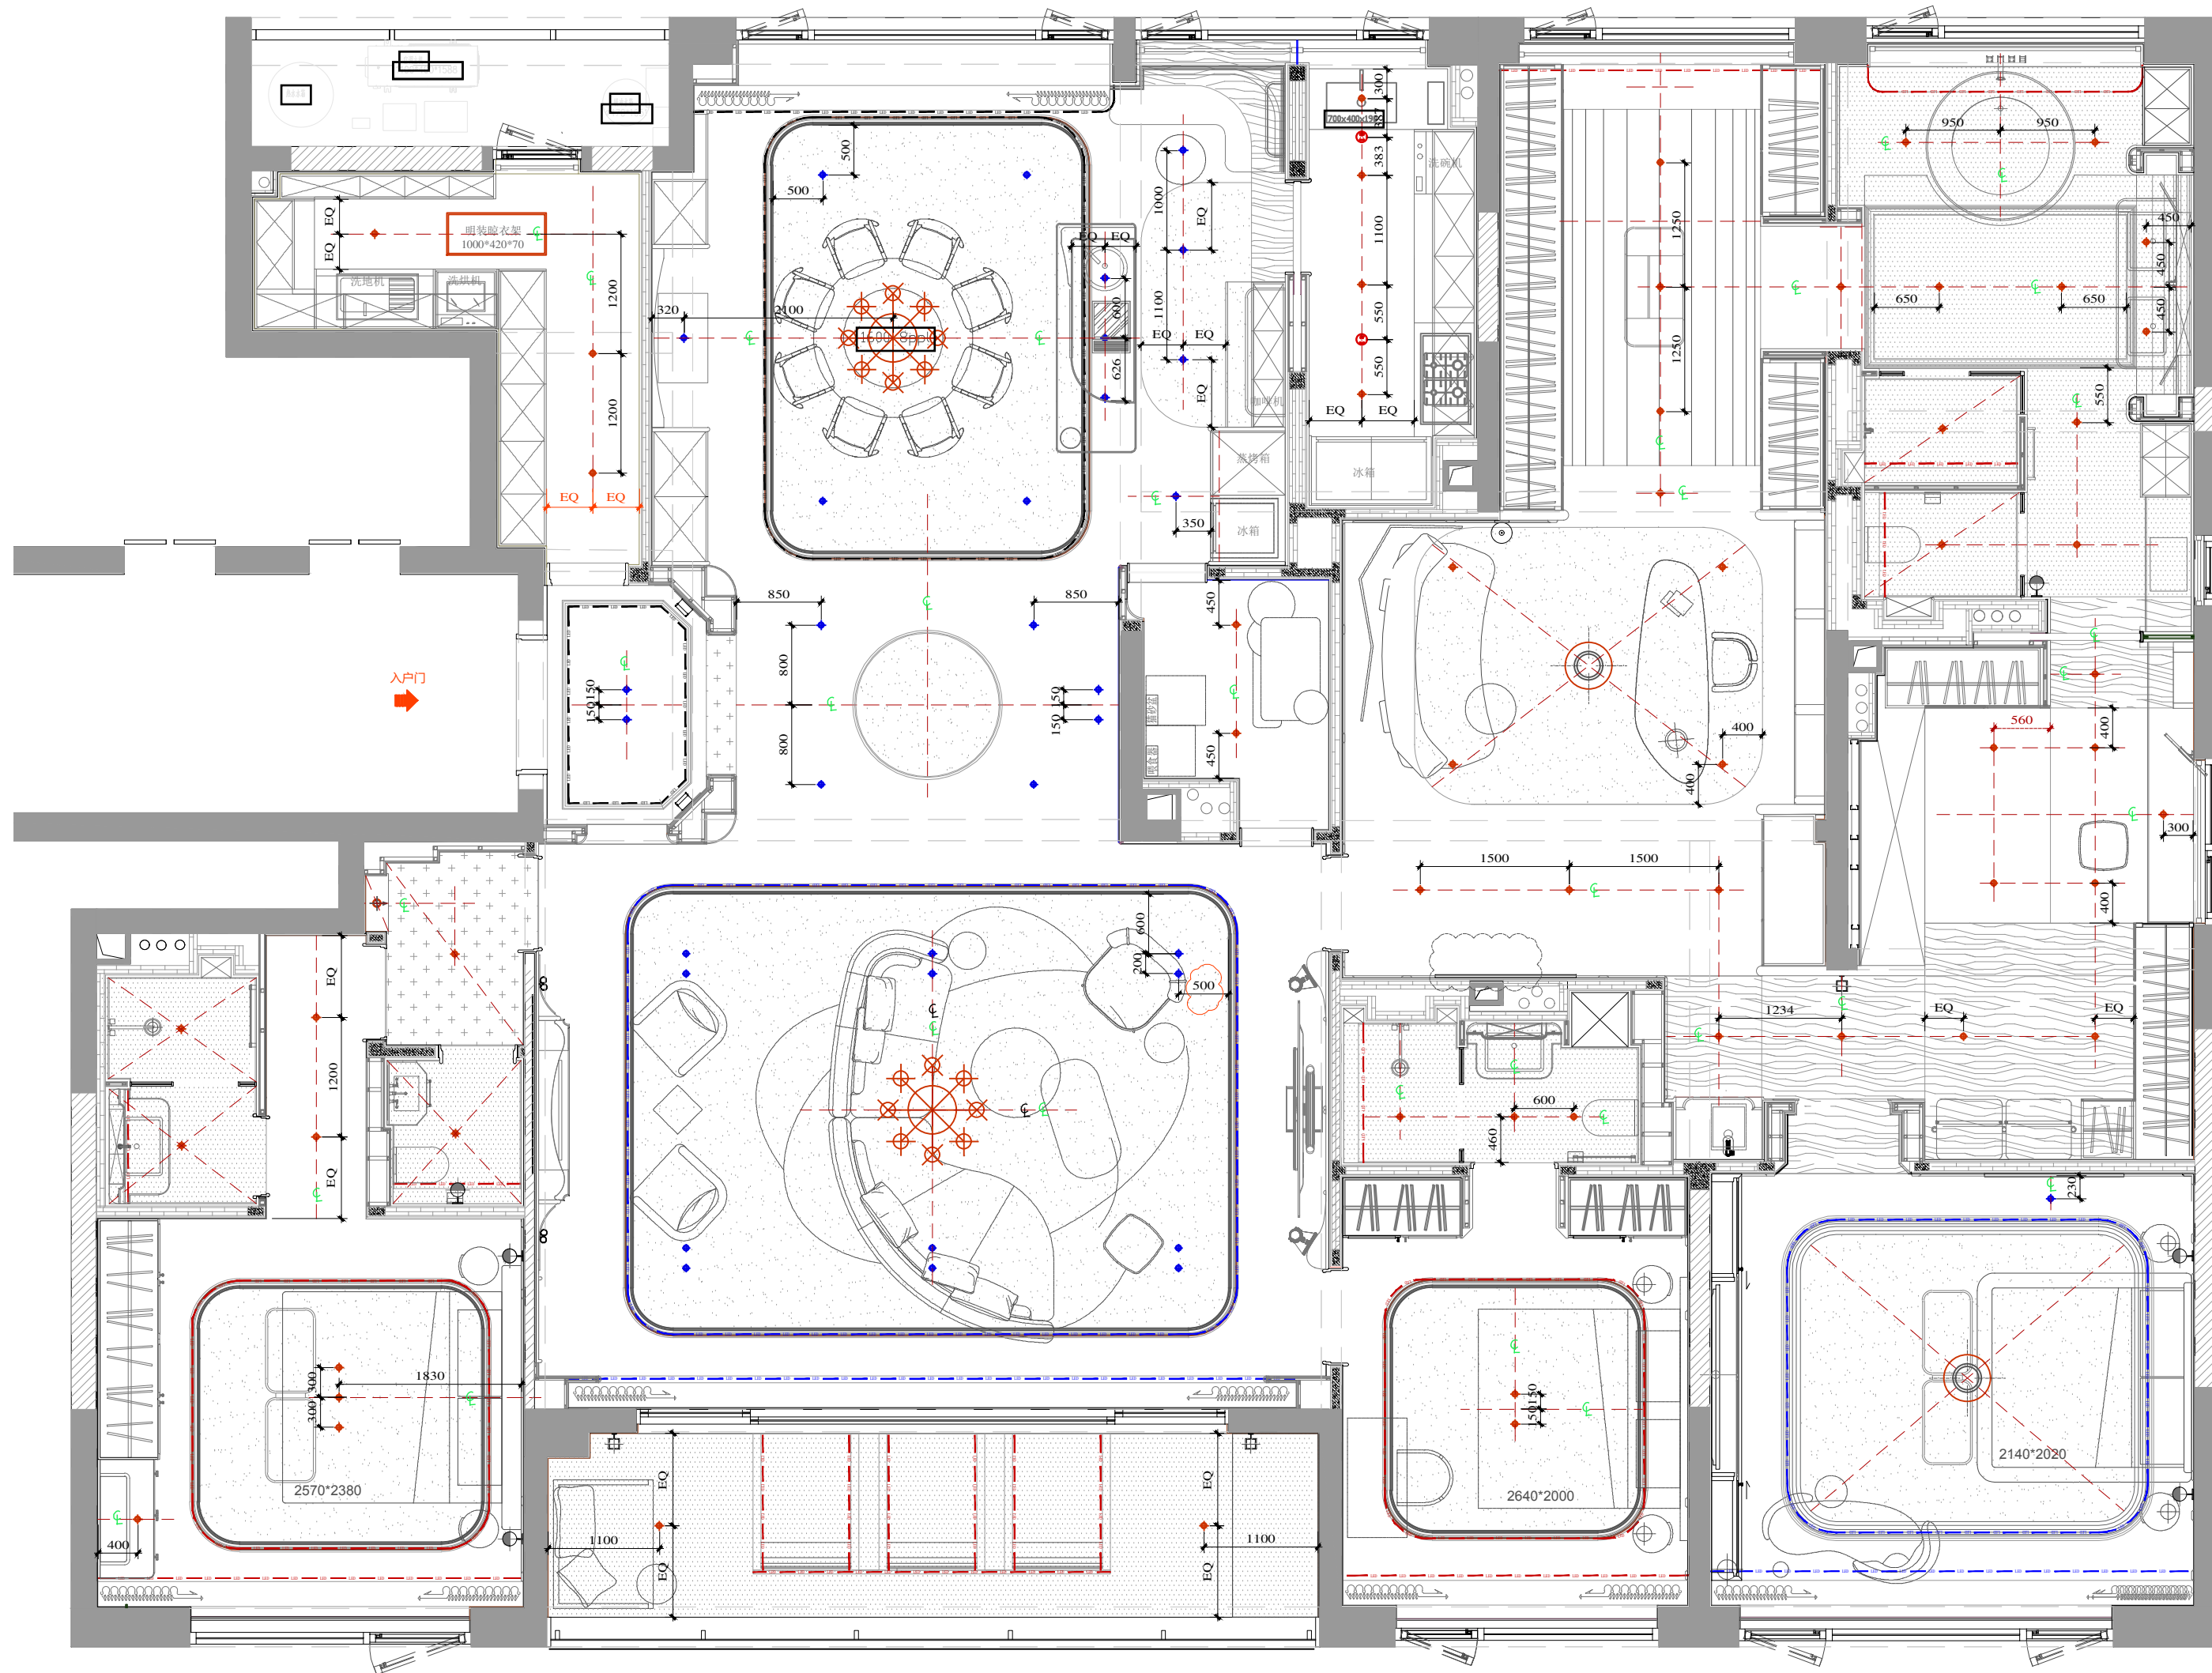

2026.4.21变更: 取消书房过道一个灯。
2026.5.6变更: 家政间天花灯位置调整,增加晾衣架。

天花灯具布置图

Scale比例 1:60@A2

注释
Notes

1. 本图纸尺寸如与现场尺寸有误差, 请施工人员与项目负责人联系。
2. 施工前施工人员应认真查阅此图, 如有不明确尺寸, 按现场测量为准。
3. 本图纸必须经甲乙双方认可并签字方可作为施工依据。

灯具编号	参数	开孔尺寸(宽x高)
Q2.75	恒压双色温群控	角度24 开孔75
Q3.75	恒压双色温群控	角度36 开孔75
LS3.50	恒压双色温群控	角度36 开孔50
K1.55	开闭	15° 3500K 55开孔
K2.75	开闭	24° 3500K 55开孔
K3.75	开闭	36° 3500K 75开孔

正式施工图
26-06-02

日期
Date 2026.4.3

修订
Revisions



项目
Project

杭州 华岸府

Scale
比例 1:60 @A2


杭州 华岸府

Drawing No.
图纸编号

CL.PL-03.1

Project No.
项目编号

© 2025

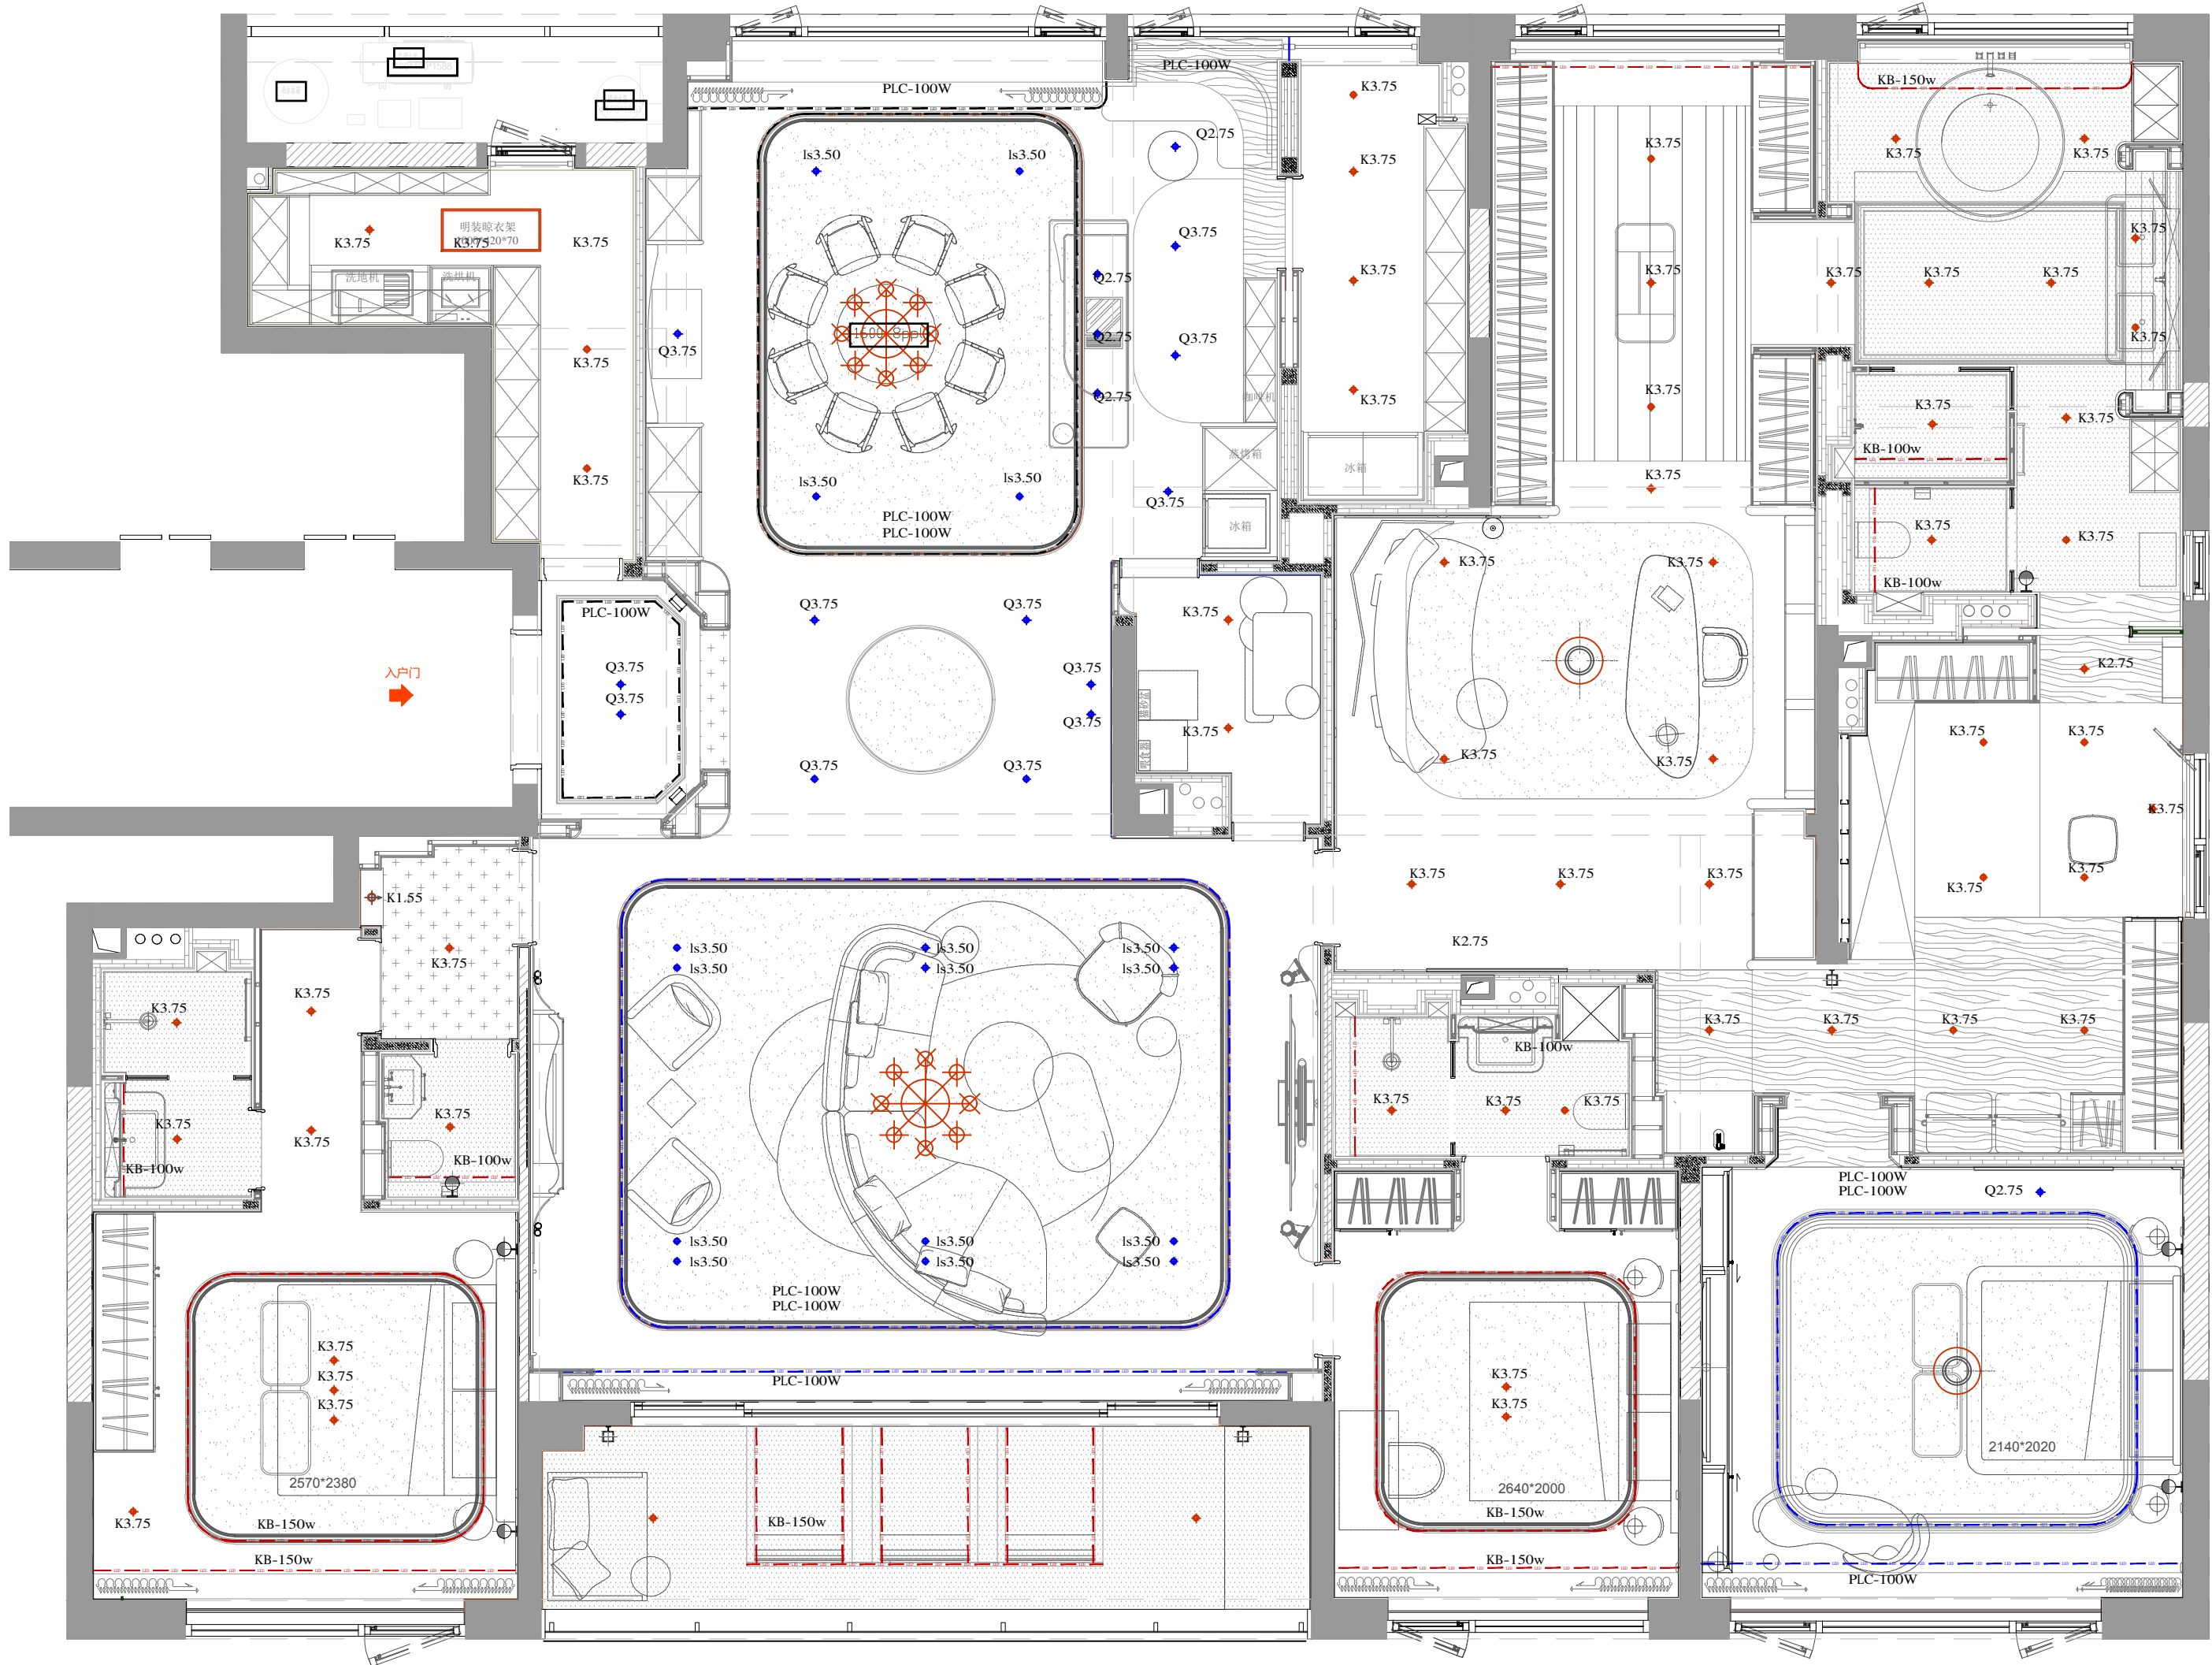

灯具编号	参数	开孔尺寸(宽x高)
Q2.75	恒压双色温群控	角度24 开孔75
Q3.75	恒压双色温群控	角度36 开孔75
LS3.50	恒压双色温群控	角度36 开孔50
K1.55	开闭	15° 3500K 55开孔
K2.75	开闭	24° 3500K 55开孔
K3.75	开闭	36° 3500K 75开孔

正式施工图
26-06-02

日期
Date 2026.4.3

修订
Revisions



项目
Project

杭州 华岸府

Scale
比例 1:60 @A2

杭州 华岸府

Drawing No.
图纸编号

CL.PL-03.1

Project No.
项目编号

© 2025


天花灯具编号图

Scale比例 1:60@A2

注释

Notes

1. 本图纸尺寸如与现场尺寸有误差，请施工人员与项目负责人联系。
2. 施工前施工人员应认真查阅此图，如有不明确尺寸，按现场测量为准。
3. 本图纸必须经甲乙双方认可并签字方可作为施工依据。

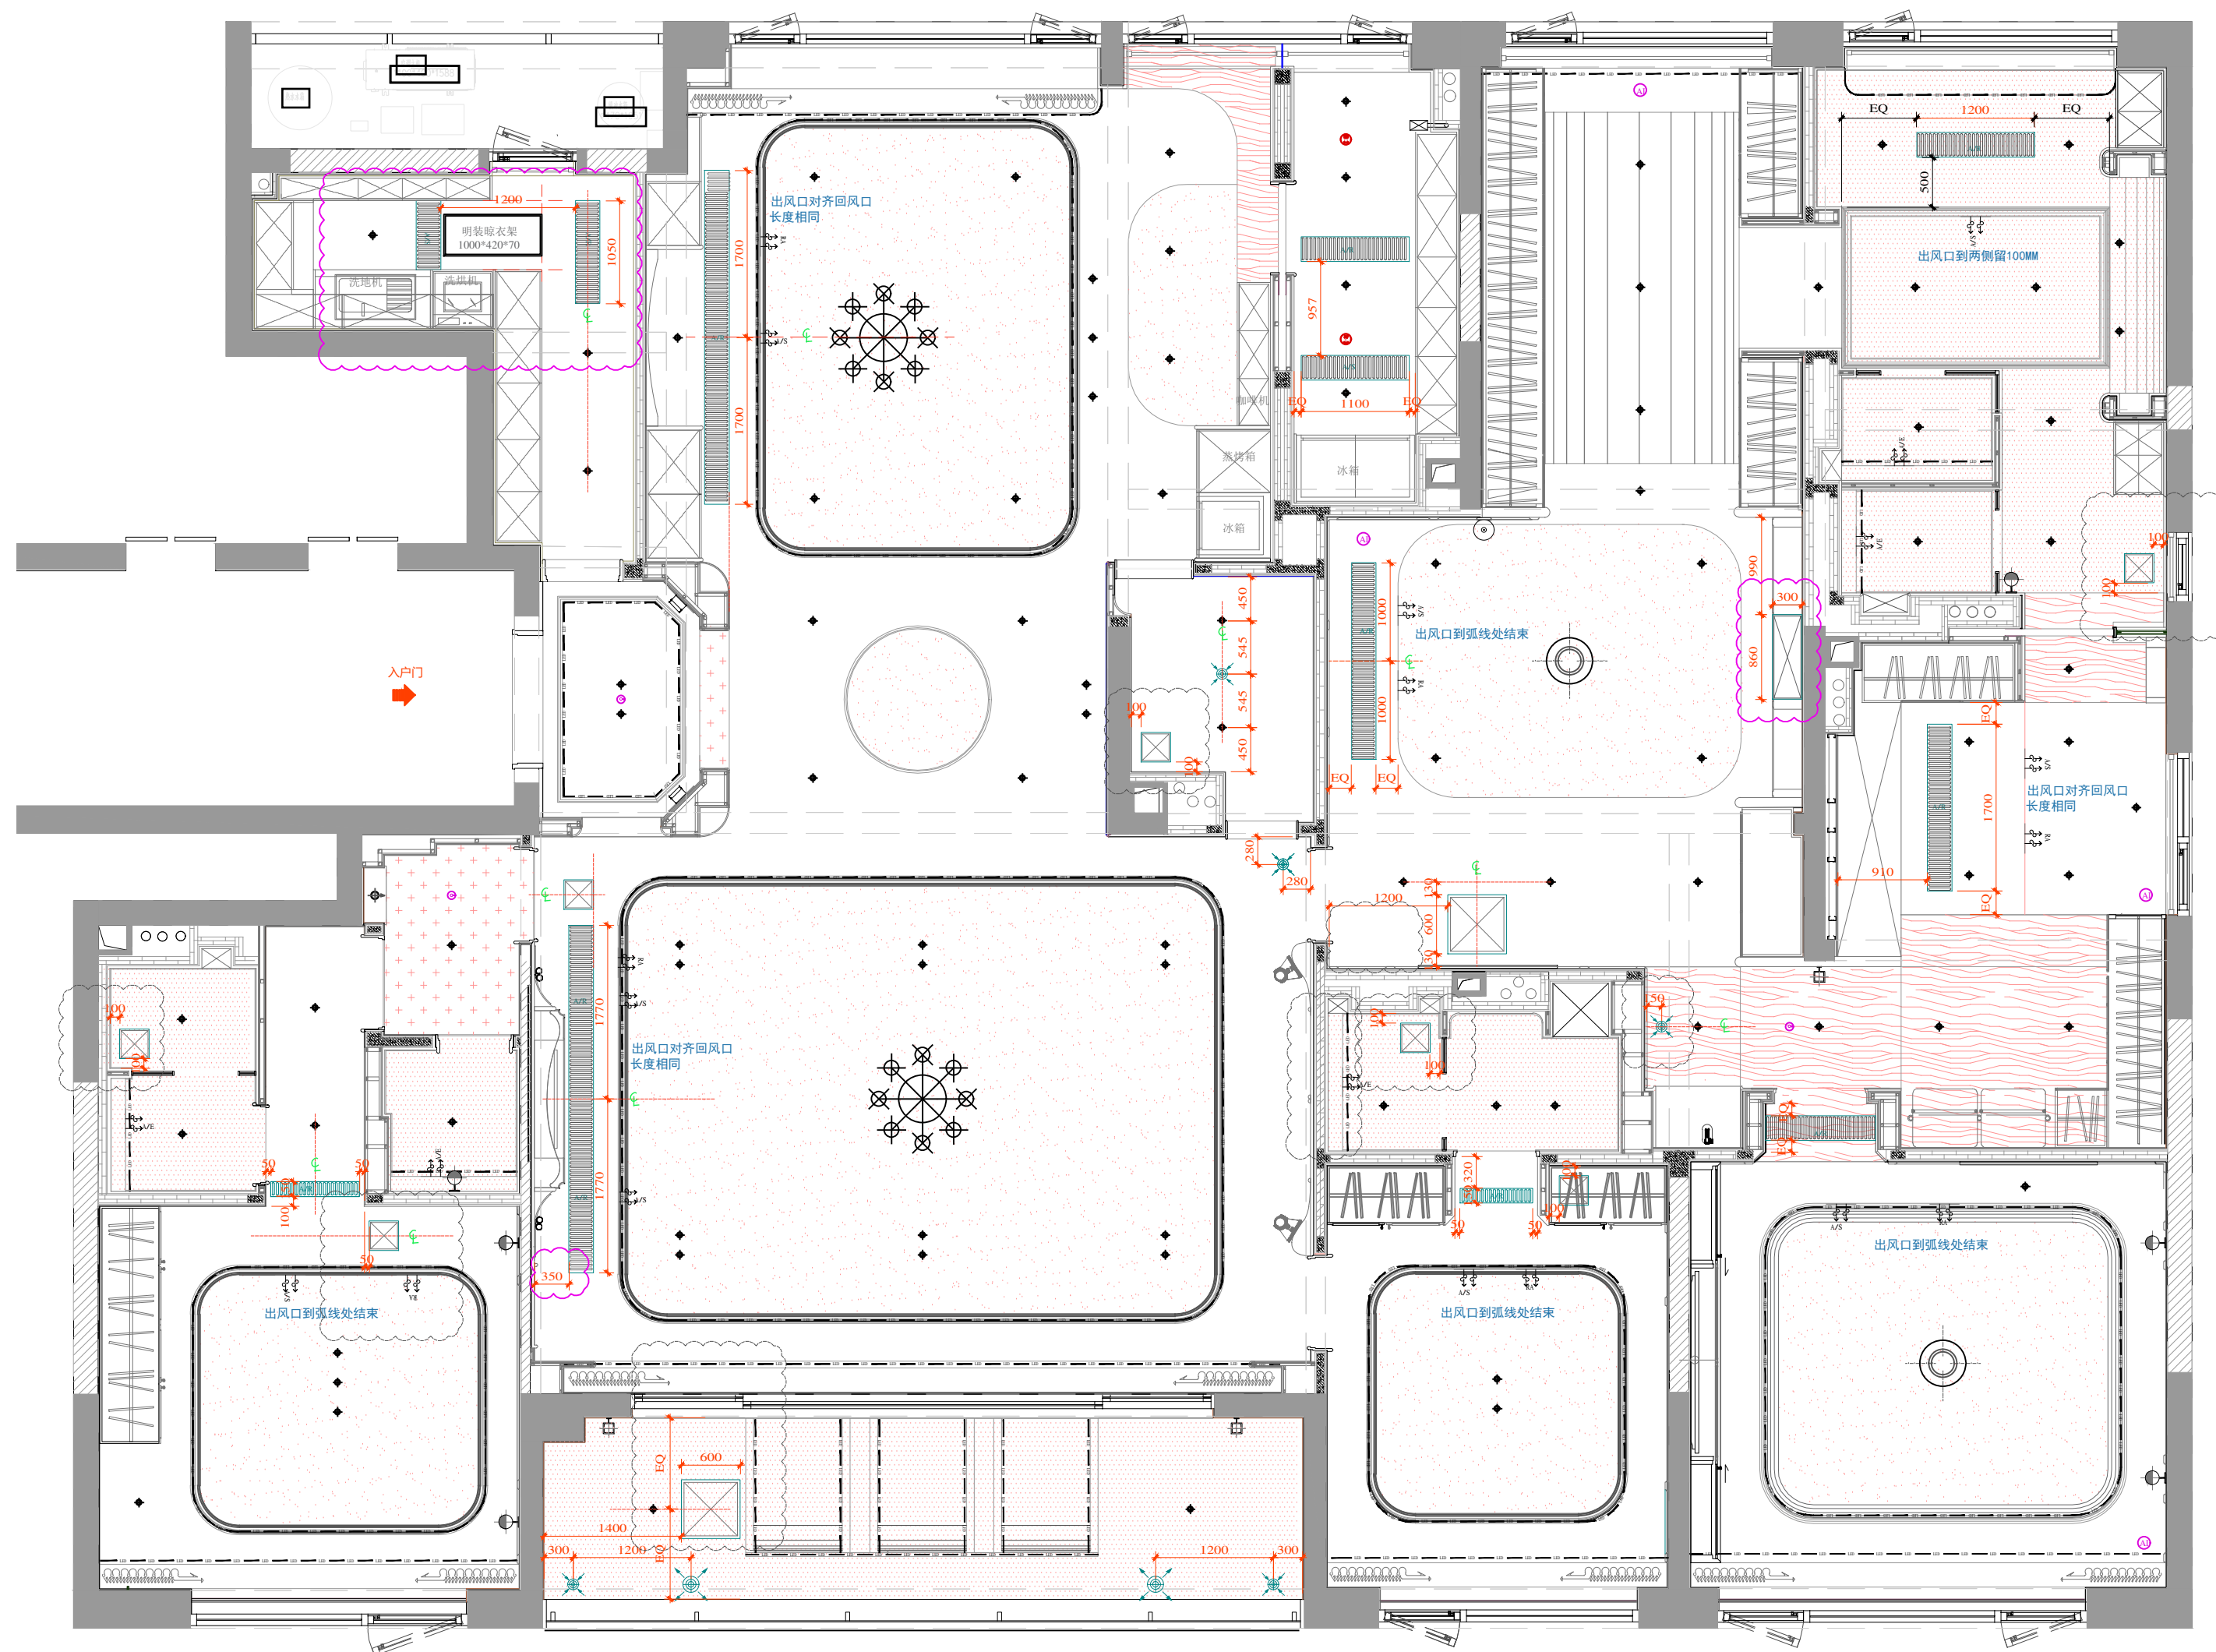

2026.4.21变更：增加排风和新风检修口定位。
2026.5.6变更：风口和检修口位置根据现场情况调整。
2026.5.18变更：家政间明确晾衣架位置，书房增加水阀检修口。

M-机电点位	
图 例	名 称
	百叶风口（无特殊标注宽度为250mm）
	检修口（无特殊标注边长为300mm）
	新风回风口
	新风出风口

正式施工图
26-06-02

日期 Date	2026.4.3
------------	----------

修订
Revisions

 1

2026.4.21

项目
Project

杭州 华岸府

Scale 1:60 @A2
比例

Drawing No.
图纸编号

CL.PL-3.3

Project No.
项目编号


© 2025

天花风口及检修口平面图

Scale比例 1:60@A2

注释	Notes
----	-------

1. 本图纸尺寸如与现场尺寸有误, 请施工人员与项目负责人联系。
2. 施工前施工人员应认真查阅此图, 如有不明确尺寸, 按现场测量为准。
3. 本图纸必须经甲乙双方认可并签字方可作为施工依据。

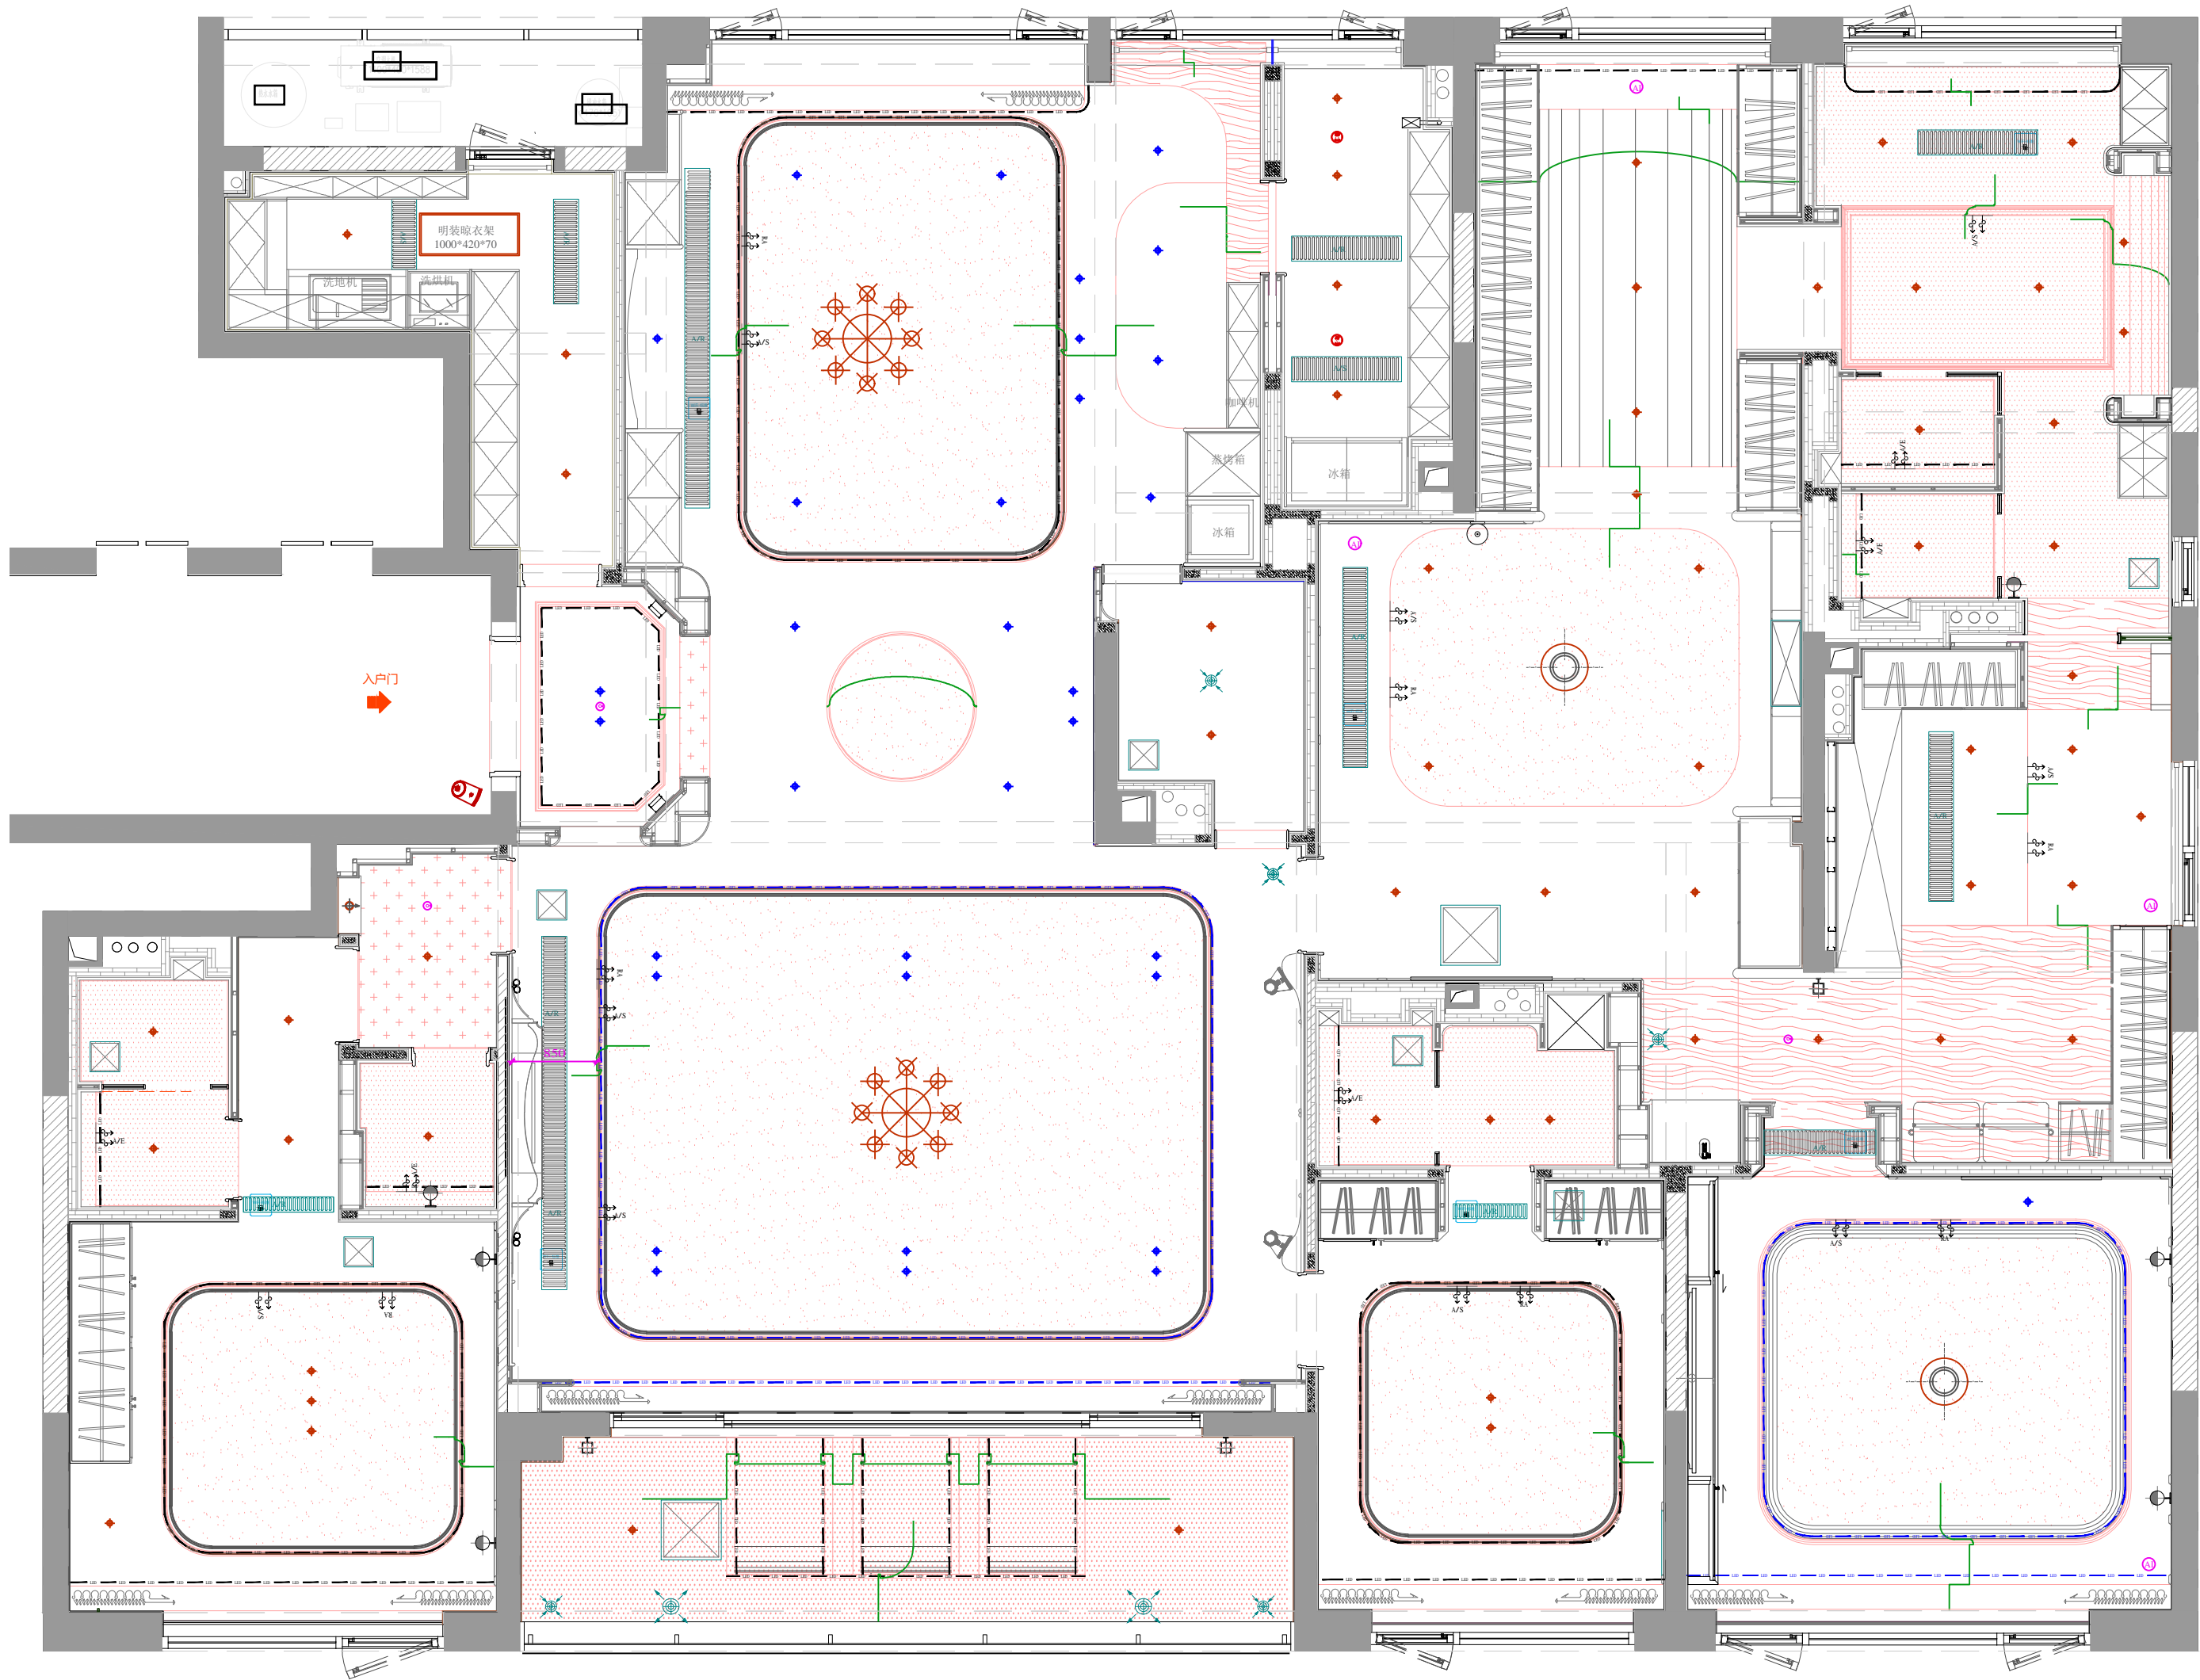

ELIBORN

M-机电点位		
图 例	名 称	备 注
	QW全屋WiFi子路由	放置空调风口内
	QW麦乐克红外传感器	深86底盒
	qw伯恩传感器	86底盒
	三系1键智能开关	86底盒
	三系2键智能开关	86底盒
	三系3键智能开关面板	86底盒
	三系智能面板	86底盒
	海雀AI摄像头	吸顶安装
	家用可燃气体探测器	吸顶安装
	独立式光电感烟火灾探测器	吸顶安装

M-机电点位	
图 例	名 称
	百叶风口（无特殊标注宽度为250mm）
	检修口（无特殊标注边长为300mm）
	新风回风口
	新风出风口

正式施工图
26-06-02

日期
Date 2026.1.8

修订
Revisions



项目
Project

杭州 华岸府

Scale 比例 1:60 @A2

Drawing No.
图纸编号

CL.PL-4

Project No.
项目编号

© 2025

综合天花平面图

Scale比例 1:60@A2

注释

Notes

1. 本图纸尺寸如与现场尺寸有误差，请施工方与项目负责人联系。
2. 施工前施工方应认真查阅此图，如有不明确尺寸，按现场测量为准。
3. 本图纸必须经甲乙双方认可并签字方可作为施工依据。