DRAWINGS LIST 图纸目录

PROJECT 项目名称：杭州华岸府

DQG.NO 图号	TITLE 内容	SCALE 比例	DATE/日期	REV.修订
CL.PL-01	天花完成面材质及标高平面图	1 : 60@A2	2026.6.11	
CL.PL-02	天花完成面尺寸图	1 : 60@A2	2026.6.11	
CL.PL-03.1	天花灯具布置图	1 : 60@A2	2026.6.11	
CL.PL-03.2	天花灯具编号图	1 : 60@A2	2026.6.11	
CL.PL-03.3	天花风口及检修口平面图	1 : 60@A2	2026.6.11	
CL.PL-4	综合天花平面图	1 : 60@A2	2026.6.11	
CL.PL-04.1	边龙+吊点平面图	1 : 60@A2	2026.6.11	
CL.PL-04.2	吊点索引图	1 : 60@A2	2026.6.11	
CL.PL-04.2.1	①玄关、家政间吊点尺寸图	1 : 25@A2	2026.6.11	
CL.PL-04.2.2	②餐厅、中厨、猫房吊点尺寸图	1 : 25@A2	2026.6.11	
CL.PL-04.2.3	③书房、衣帽间吊点尺寸图	1 : 25@A2	2026.6.11	
CL.PL-04.2.4	④主卫吊点尺寸图	1 : 25@A2	2026.6.11	
CL.PL-04.2.5	⑤衣帽间吊点尺寸图	1 : 25@A2	2026.6.11	
CL.PL-04.2.6	⑥主卧吊点尺寸图	1 : 25@A2	2026.6.11	
CL.PL-04.2.7	⑦次卧、次卫吊点尺寸图	1 : 25@A2	2026.6.11	

DQG.NO 图号	TITLE 内容	SCALE 比例	DATE/日期	REV.修订
CL.PL-04.2.8	⑧客厅、阳台吊点尺寸图	1 : 25@A2	2026.6.11	
CL.PL-04.2.9	⑨客卧、客卫、阳台吊点尺寸图	1 : 25@A2	2026.6.11	
CL.PL-04.3	主龙骨平面图	1 : 60@A2	2026.6.11	
CL.PL-04.4	副龙骨平面图	1 : 60@A2	2026.6.11	
CL.PL-05.1	第一层石膏板平面图	1 : 60@A2	2026.6.11	
CL.PL-05.2	天花铝型材分析图	1 : 60@A2	2026.6.11	
CL.PL-05.3	天花GRG分析图	1 : 60@A2	2026.6.11	
CL.PL-05.4	第二层石膏板平面图	1 : 60@A2	2026.6.11	
CL.PL-02	天花剖面索引图	1 : 60@A2	2026.6.11	
CL.DT-01	天花节点图	1 : 5@A2	2026.6.11	
CL.DT-02	天花节点图	1 : 5@A2	2026.6.11	
CL.DT-03	天花节点图	1 : 5@A2	2026.6.11	
CL.DT-04	天花节点图	1 : 5@A2	2026.6.11	
CL.DT-05	天花节点图	1 : 5@A2	2026.6.11	
CL.DT-06	天花节点图	1 : 5@A2	2026.6.11	

盖章

注释
Notes

1.本图纸如与现场尺寸有误，请施工人员与项目负责人联系。
2.施工前施工人员应认真查阅此图，如有不明确尺寸，按现场测量为准。
3.本图纸必须经甲乙双方认可并签字方可作为施工依据。

日期
Date 03/04/26

修订
Revision

1

项目
Project
潮映华岸府3-801

比例
Scale

图纸目录

图纸编号
Drawing No.
CL.目录

项目编号
Project No.

©2025

云线批注处：主卧衣帽间木饰面吊顶范围调整，局部标高调整；书房新增检修口

云线批注处： 阳台处局部标高调整;玄关穹顶范围调整

图例A
LEGEND A

材质	图例	说明
防水乳胶漆		PT-08 暖黄色防水乳胶漆
		PT-07 红色防水乳胶漆
		PT-02 米白色防水乳胶漆
肌理漆		PT-01 米白色肌理漆
		PT-06 薄荷色肌理漆
		PT-03 暖黄色肌理漆
墙纸		WA-13 墙布12
		WA-02 墙布1
木饰面		WD-01 橡木饰面

说明：木饰面以厂家为准。

盖章

注释
Notes

1.本图纸如与现场尺寸有误，请施工人员与项目负责人联系。
2.施工前施工人员应认真查阅此图，如有不明确尺寸，按现场测量为准。
3.本图纸必须经甲乙双方认可并签字方可作为施工依据。

日期
Date 03/24/26

修订
Revision

1

项目
Project
潮映华岸府3-801

比例
Scale 1:60@A2

天花完成面材质及标高平面图

图纸编号
Drawing No.
CL.PL-01

项目编号
Project No.

©2025

图例A
LEGEND A

材质	图例	说明
防水乳胶漆		PT-08 暖黄色防水乳胶漆
		PT-07 红色防水乳胶漆
		PT-02 米白色防水乳胶漆
肌理漆		PT-01 米白色肌理漆
		PT-06 薄荷色肌理漆
		PT-03 暖黄色肌理漆
墙纸		WA-13 墙布12
		WA-02 墙布1
木饰面		WD-01 橡木饰面

说明：木饰面以厂家为准。

盖章

注释
Notes

1.本图纸如与现场尺寸有误，请施工人员与项目负责人联系。
2.施工前施工人员应认真查阅此图，如有不明确尺寸，按现场测量为准。
3.本图纸必须经甲乙双方认可并签字方可作为施工依据。

日期
Date 03/24/26

修订
Revision

1

项目
Project

潮映华岸府3-801

比例
Scale

天花剖面索引图

图纸编号
Drawing No.

CL.PL-02

项目编号
Project No.

©2025

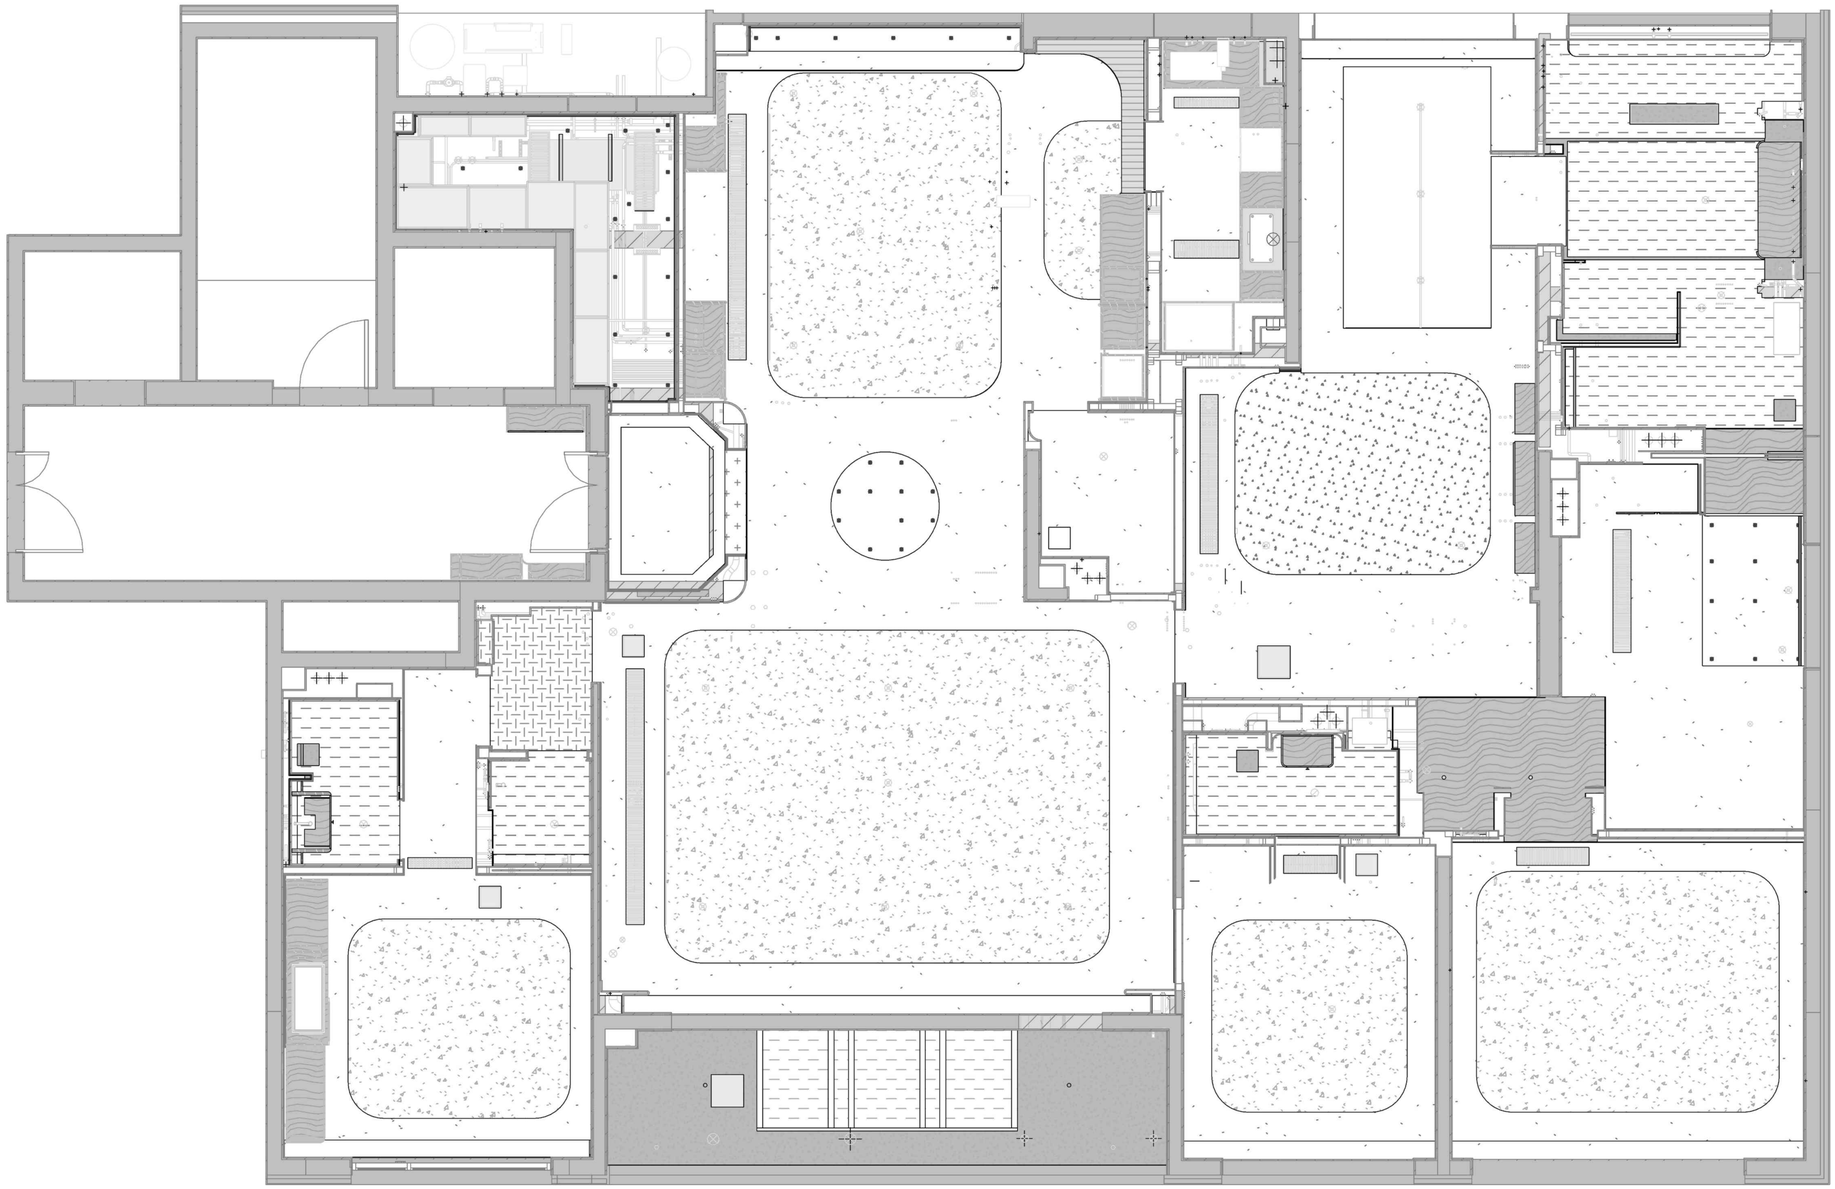

注意：
原则1：规格-丝杆离墙≤300mm，丝杆间距≤800mm。
原则2：主龙间距≤800mm，接口采用双铆钉固定。
原则3：副龙间距≤300mm，接口采用双铆钉固定。
原则4：弹性尺寸，若受管路影响可依现场情况调节；但必须符合原则1的要求。

图例A
LEGEND A

编号	图例	说明
1		边龙骨
2		主龙骨-常规龙骨
3		主龙骨-卡式龙骨
4		副龙骨
5		吊点
6		L型防裂板
7		L型转角防裂板
8		起铺点标识
9		第一层石膏板分缝
10		第二层石膏板分缝
11		室内梁
12		检修口
13		空调检修口
14		晾衣架角钢
15		加固区域，具体以灯具厂商的说明为准

盖章

注释
Notes

1.本图纸如与现场尺寸有误，请施工人员与项目负责人联系。
2.施工前施工人员应认真查阅此图，如有不明确尺寸，按现场测量为准。
3.本图纸必须经甲乙双方认可并签字方可作为施工依据。

日期
Date 03/24/26

修订
Revision

1

项目
Project
潮映华岸府3-801

比例
Scale 1:60@A2

边龙+吊点平面图

图纸编号
Drawing No.
CL.PL-04.1

项目编号
Project No.

©2025

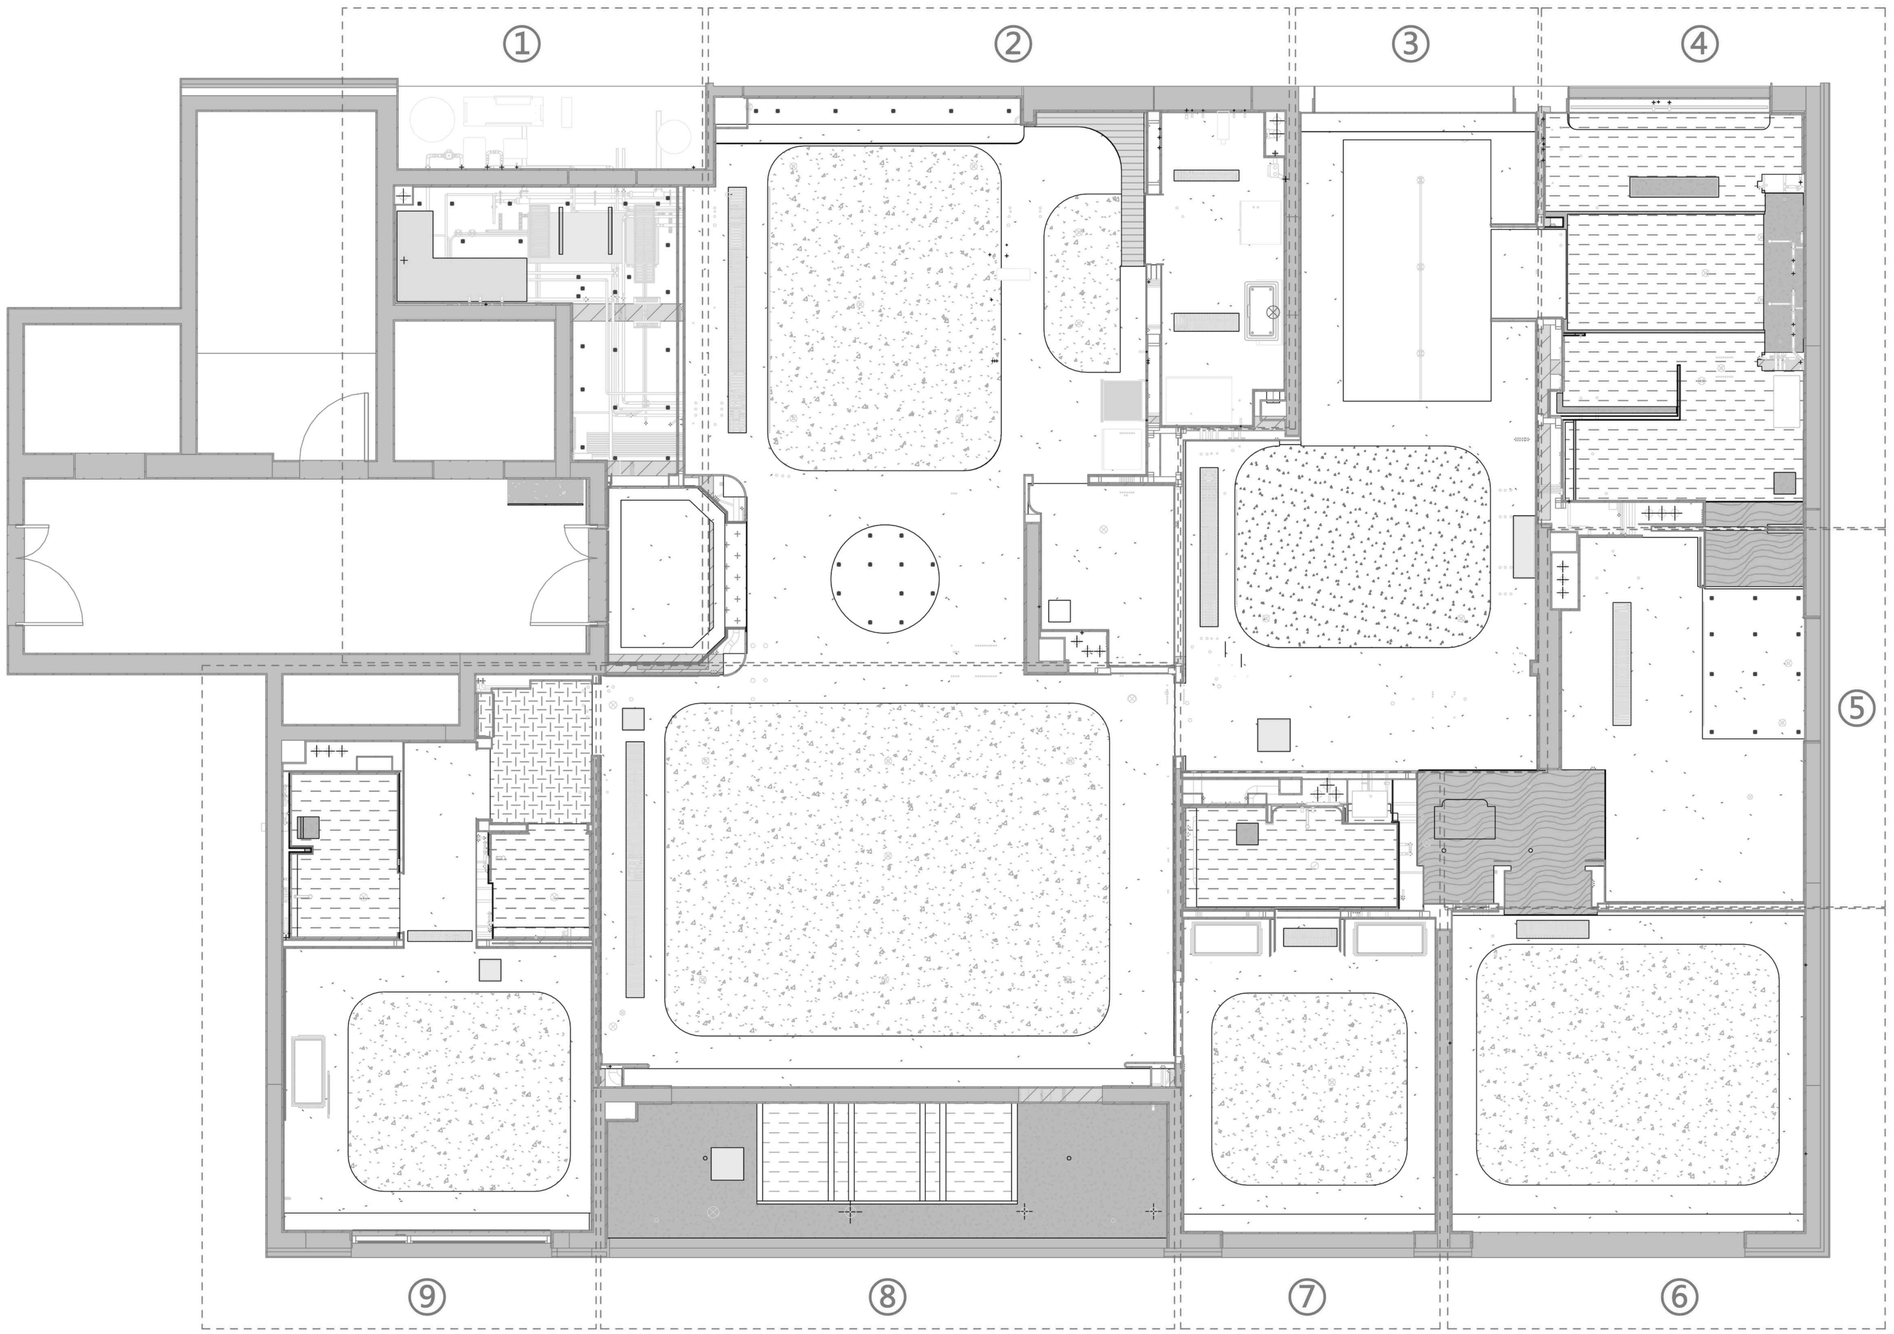

注意：
原则1：规格-丝杆离墙≤300mm，丝杆间距≤800mm。
原则2：主龙间距≤800mm，接口采用双铆钉固定。
原则3：副龙间距≤300mm，接口采用双铆钉固定。
原则4：弹性尺寸，若受管路影响可依现场情况调节；但必须符合原则1的要求。

图例A
LEGEND A

编号	图例	说明
1		边龙骨
2		主龙骨-常规龙骨
3		主龙骨-卡式龙骨
4		副龙骨
5		吊点
6		L型防裂板
7		L型转角防裂板
8		起铺点标识
9		第一层石膏板分缝
10		第二层石膏板分缝
11		室内梁
12		检修口
13		空调检修口
14		晾衣架角钢
15		加固区域，具体以灯具厂商的说明为准

盖章

注释
Notes

1.本图纸如与现场尺寸有误，请施工人员与项目负责人联系。
2.施工前施工人员应认真查阅此图，如有不明确尺寸，按现场测量为准。
3.本图纸必须经甲乙双方认可并签字方可作为施工依据。

日期
Date 03/24/26

修订
Revision

1

项目
Project
潮映华岸府3-801

比例
Scale 1:60@A2

吊点索引图

图纸编号
Drawing No.
CL.PL-04.2

项目编号
Project No.

©2025

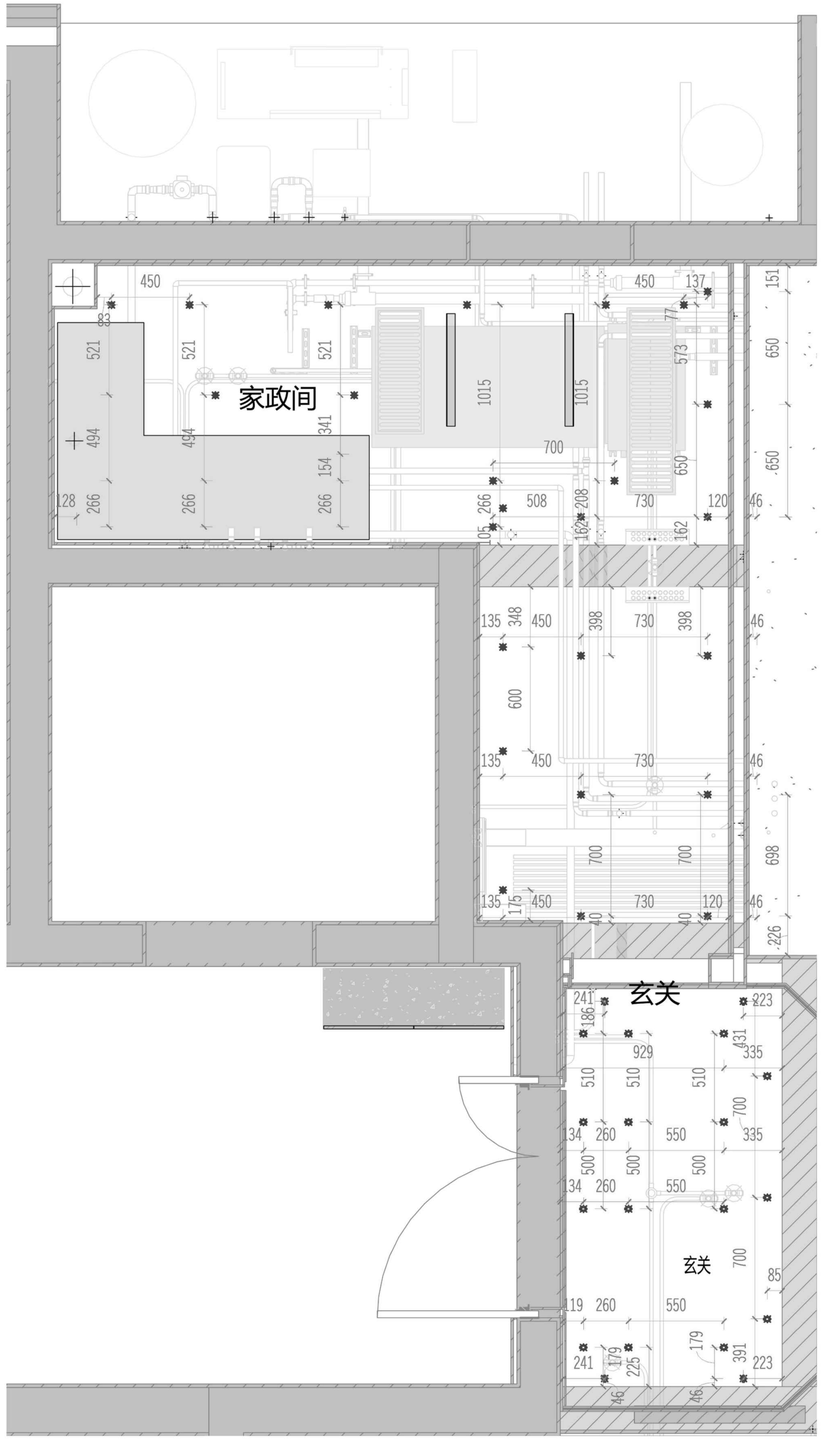

说明：
未标注点间距为800mm。

盖章

注释
Notes

1.本图纸如与现场尺寸有误，请施工人员与项目负责人联系。
2.施工前施工人员应认真查阅此图，如有不明确尺寸，按现场测量为准。
3.本图纸必须经甲乙双方认可并签字方可作为施工依据。

日期
Date 03/24/26

修订
Revision

1

项目
Project
潮映华岸府3-801

比例
Scale 1:25@A2

①玄关、家政间吊点尺寸图

图纸编号
Drawing No.
CL.PL-04.2.1

项目编号
Project No.

©2025

说明：
未标注点间距为800mm。

盖章

注释
Notes

1.本图纸如与现场尺寸有误，请施工人员与项目负责人联系。
2.施工前施工人员应认真查阅此图，如有不明确尺寸，按现场测量为准。
3.本图纸必须经甲乙双方认可并签字方可作为施工依据。

日期
Date 03/24/26

修订
Revision

1

项目
Project
潮映华岸府3-801

比例
Scale 1:25@A2

②餐厅、中厨、猫房吊点尺寸图

图纸编号
Drawing No.
CL.PL-04.2.2

项目编号
Project No.

©2025

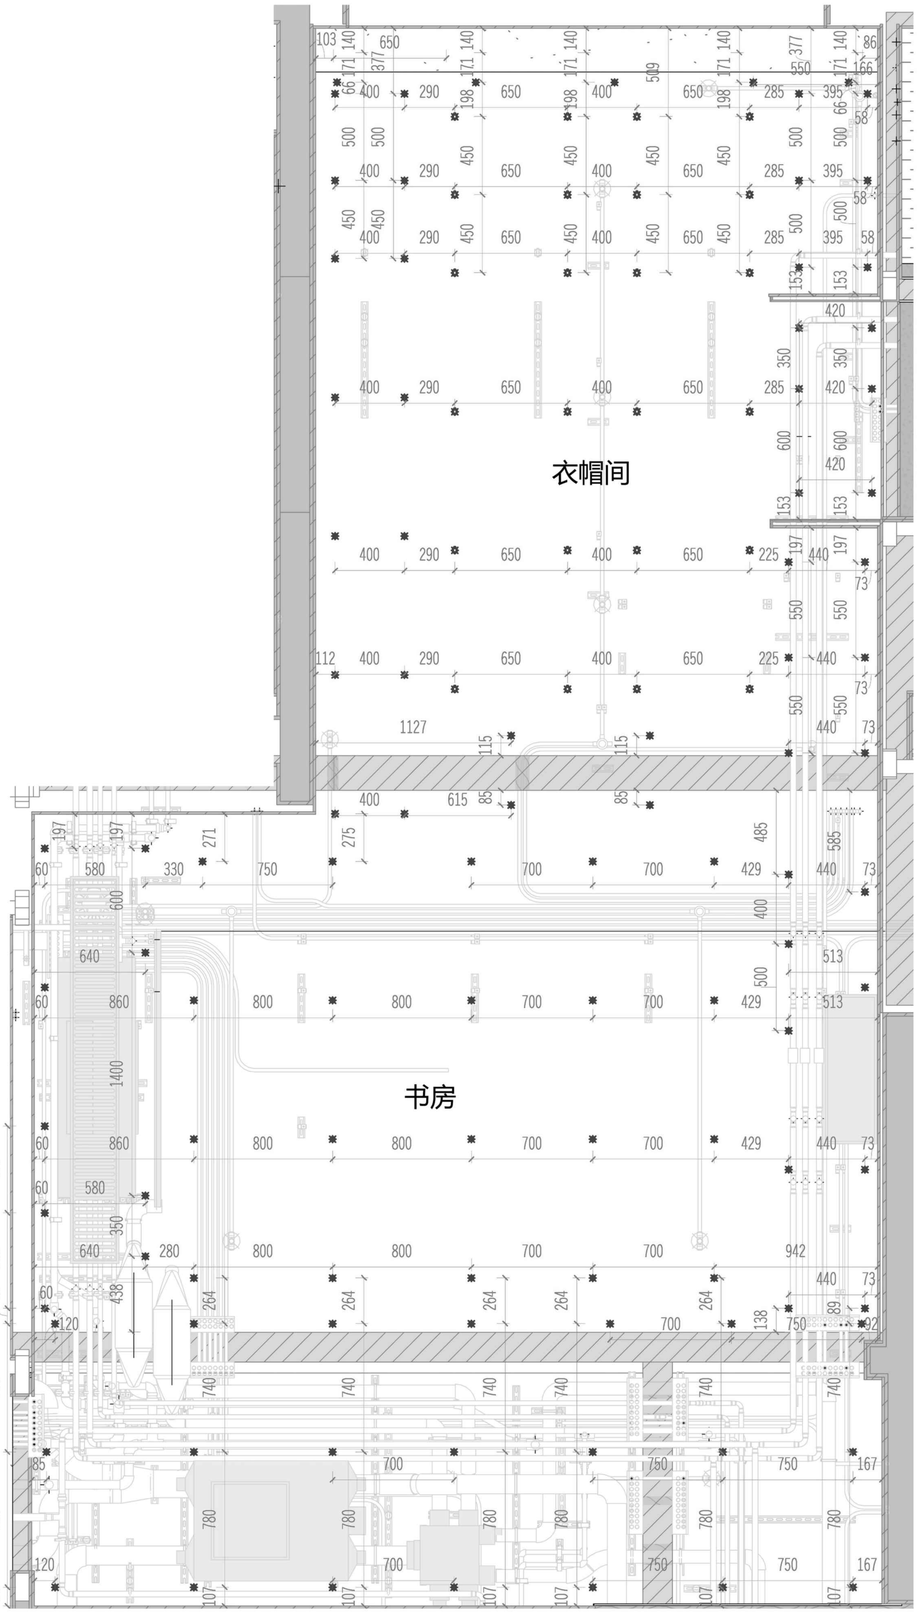

说明：
未标注点间距为800mm。

盖章

注释
Notes

1.本图纸如与现场尺寸有误，请施工人员与项目负责人联系。
2.施工前施工人员应认真查阅此图，如有不明确尺寸，按现场测量为准。
3.本图纸必须经甲乙双方认可并签字方可作为施工依据。

日期
Date 03/24/26

修订
Revision

1

项目
Project
潮映华岸府3-801

比例
Scale 1:25@A2

③书房、衣帽间吊点尺寸图

图纸编号
Drawing No.
CL.PL-04.2.3

项目编号
Project No.

©2025

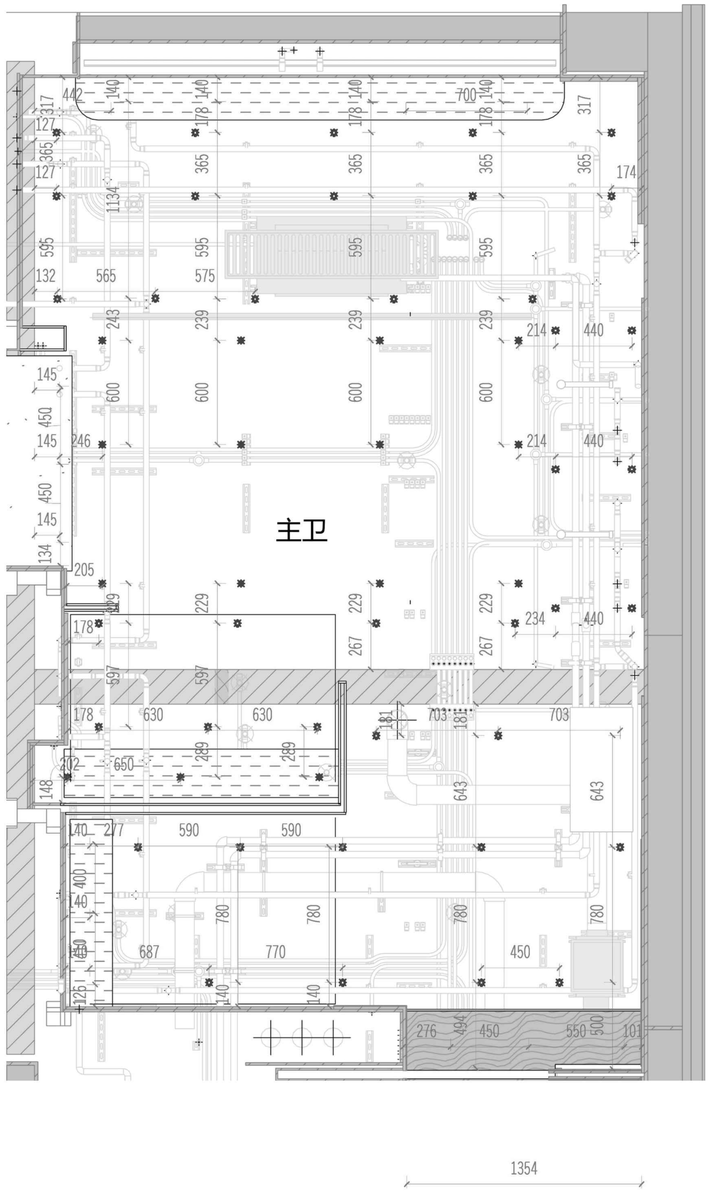

说明：
未标注点间距为800mm。

盖章

注释
Notes

1.本图纸如与现场尺寸有误，请施工人员与项目负责人联系。
2.施工前施工人员应认真查阅此图，如有不明确尺寸，按现场测量为准。
3.本图纸必须经甲乙双方认可并签字方可作为施工依据。

日期
Date 03/24/26

修订
Revision

1

项目
Project
潮映华岸府3-801

比例
Scale 1:25@A2

④主卫吊点尺寸图

图纸编号
Drawing No.
CL.PL-04.2.4

项目编号
Project No.

©2025

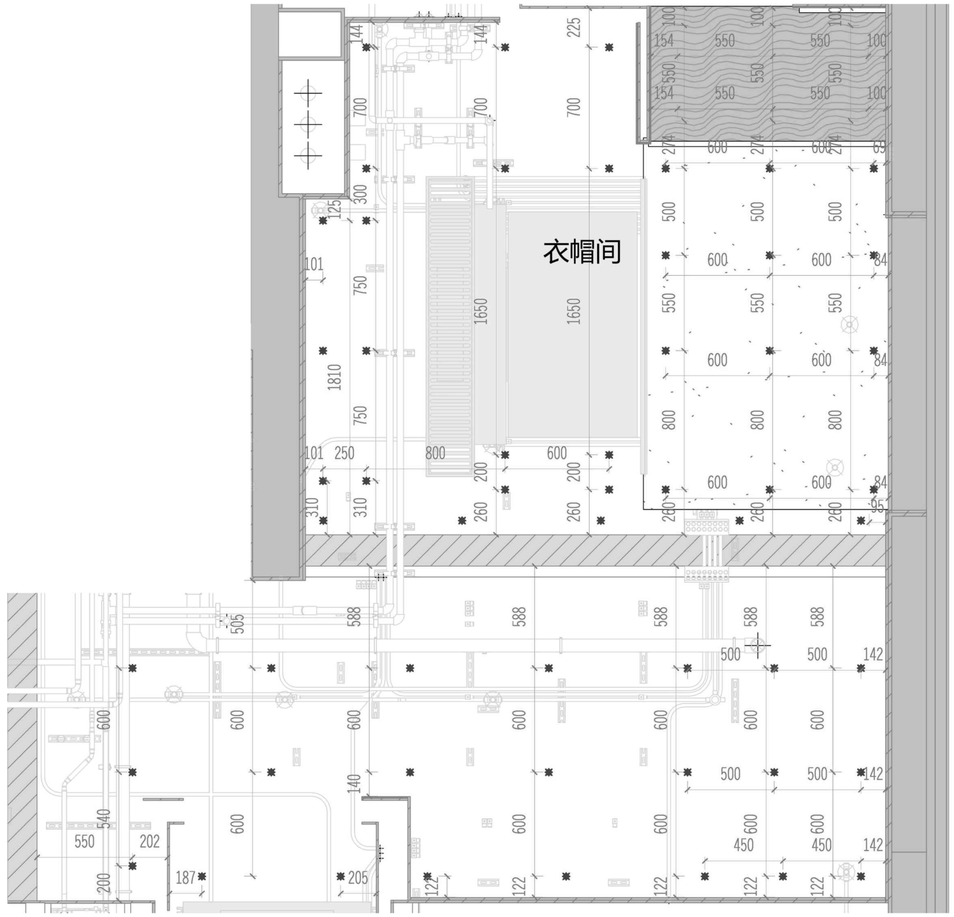

说明：
未标注点间距为800mm。

盖章

注释
Notes

1.本图纸如与现场尺寸有误，请施工人员与项目负责人联系。
2.施工前施工人员应认真查阅此图，如有不明确尺寸，按现场测量为准。
3.本图纸必须经甲乙双方认可并签字方可作为施工依据。

日期
Date 03/24/26

修订
Revision

1

项目
Project
潮映华岸府3-801

比例
Scale 1:25@A2

⑤衣帽间吊点尺寸图

图纸编号
Drawing No.
CL.PL-04.2.5

项目编号
Project No.

©2025

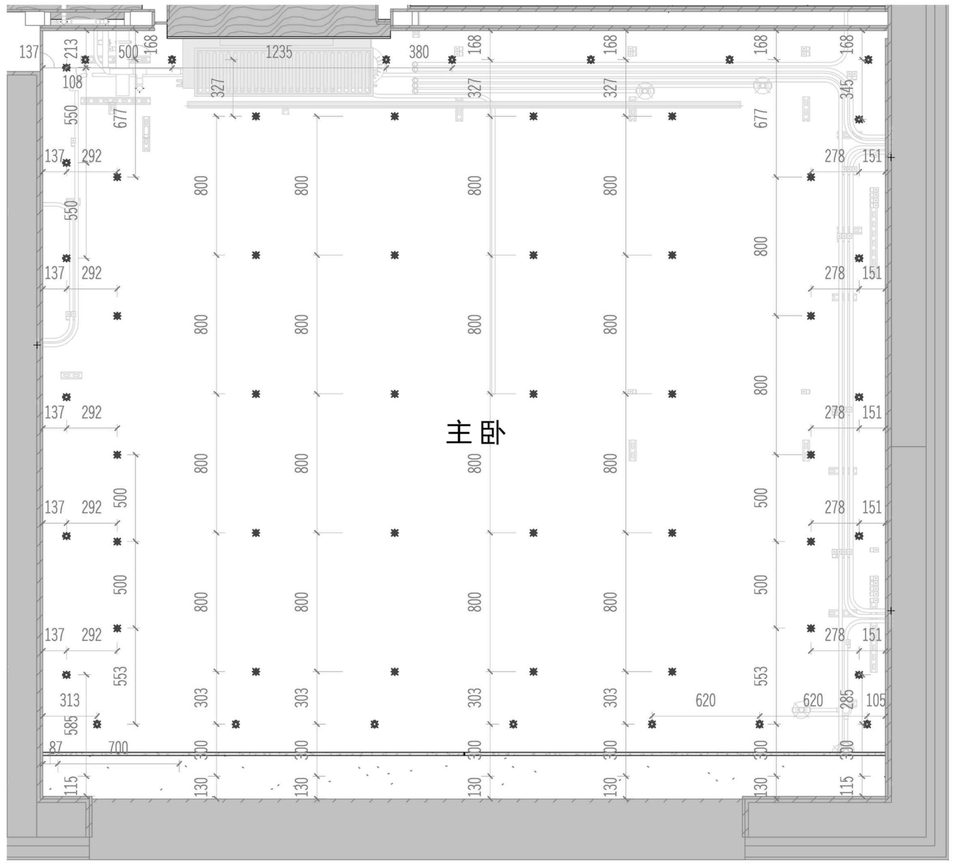

说明：
未标注点间距为800mm。

盖章

注释
Notes

1.本图纸如与现场尺寸有误，请施工人员与项目负责人联系。
2.施工前施工人员应认真查阅此图，如有不明确尺寸，按现场测量为准。
3.本图纸必须经甲乙双方认可并签字方可作为施工依据。

日期
Date 03/24/26

修订
Revision

1

项目
Project
潮映华岸府3-801

比例
Scale 1:25@A2

⑥主卧吊点尺寸图

图纸编号
Drawing No.
CL.PL-04.2.6

项目编号
Project No.

©2025

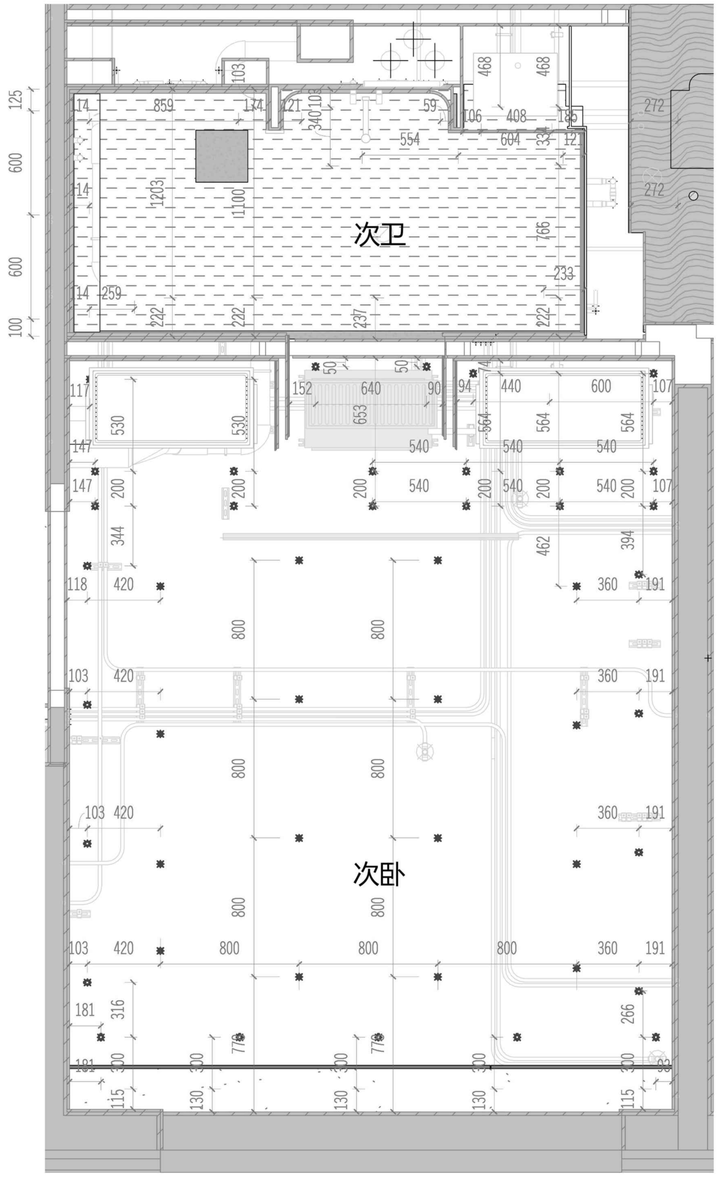

说明：
未标注点间距为800mm。

盖章

注释
Notes

1.本图纸如与现场尺寸有误，请施工人员与项目负责人联系。
2.施工前施工人员应认真查阅此图，如有不明确尺寸，按现场测量为准。
3.本图纸必须经甲乙双方认可并签字方可作为施工依据。

日期
Date 03/24/26

修订
Revision

1

项目
Project

潮映华岸府3-801

比例
Scale 1:25@A2

⑦次卧、次卫吊点尺寸图

图纸编号
Drawing No.

CL.PL-04.2.7

项目编号
Project No.

©2025

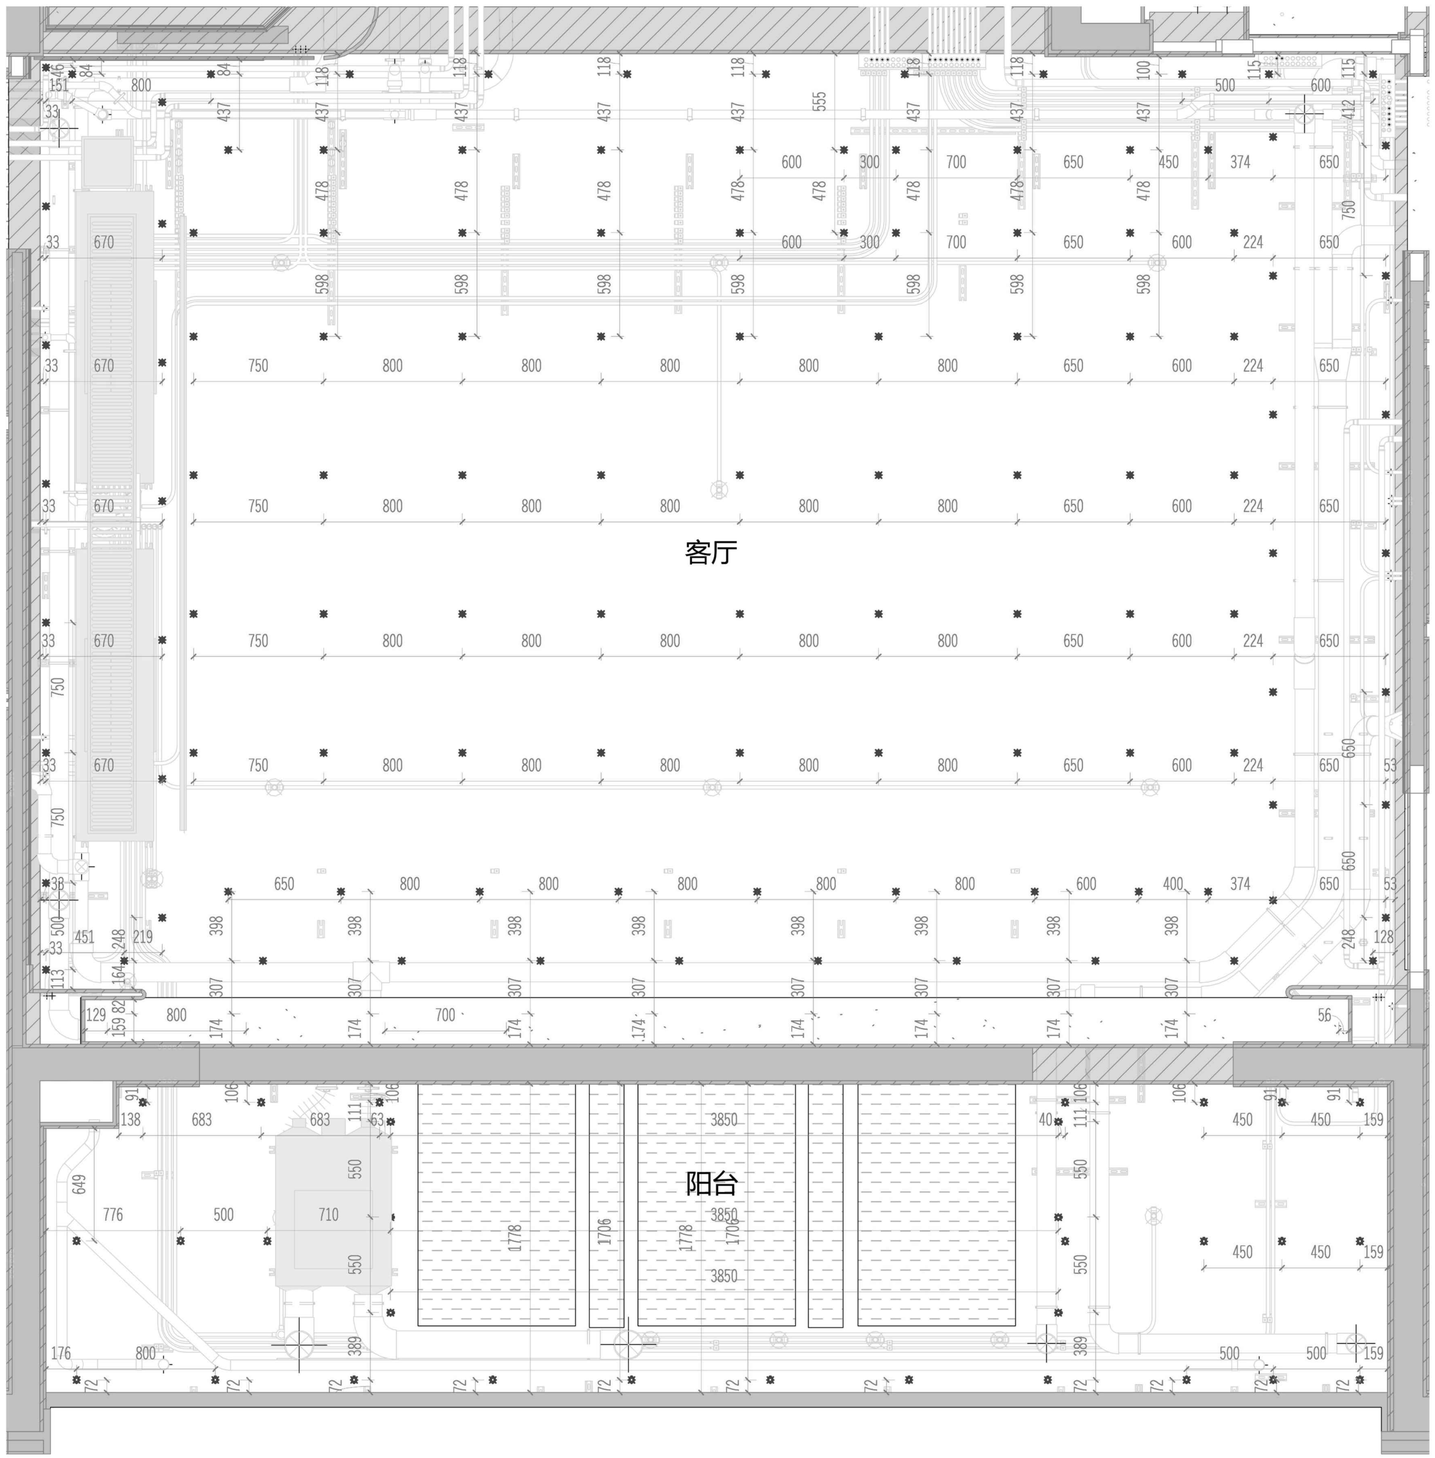

说明：
未标注点间距为800mm。

盖章

注释
Notes

1.本图纸如与现场尺寸有误，请施工人员与项目负责人联系。
2.施工前施工人员应认真查阅此图，如有不明确尺寸，按现场测量为准。
3.本图纸必须经甲乙双方认可并签字方可作为施工依据。

日期
Date 03/24/26

修订
Revision

1

项目
Project

潮映华岸府3-801

比例
Scale 1:25@A2

⑧客厅、阳台吊点尺寸图

图纸编号
Drawing No.

CL.PL-04.2.8

项目编号
Project No.

©2025

说明：
未标注点间距为800mm。

盖章

注释
Notes

1.本图纸如与现场尺寸有误，请施工人员与项目负责人联系。
2.施工前施工人员应认真查阅此图，如有不明确尺寸，按现场测量为准。
3.本图纸必须经甲乙双方认可并签字方可作为施工依据。

日期
Date 03/24/26

修订
Revision

1

项目
Project
潮映华岸府3-801

比例
Scale 1:25@A2

⑨客卧、客卫、公卫吊点尺寸图

图纸编号
Drawing No.
CL.PL-04.2.9

项目编号
Project No.

©2025

注意：
原则1：规格-丝杆离墙≤300mm，丝杆间距≤800mm。
原则2：主龙间距≤800mm，接口采用双铆钉固定。
原则3：副龙间距≤300mm，接口采用双铆钉固定。
原则4：弹性尺寸，若受管路影响可依现场情况调节；但必须符合原则1的要求。

图例A
LEGEND A

编号	图例	说明
1		边龙骨
2		主龙骨-常规龙骨
3		主龙骨-卡式龙骨
4		副龙骨
5		吊点
6		L型防裂板
7		L型转角防裂板
8		起铺点标识
9		第一层石膏板分缝
10		第二层石膏板分缝
11		室内梁
12		检修口
13		空调检修口
14		晾衣架角钢
15		加固区域，具体以灯具厂商的说明为准

盖章

注释
Notes

1.本图纸如与现场尺寸有误，请施工人员与项目负责人联系。
2.施工前施工人员应认真查阅此图，如有不明确尺寸，按现场测量为准。
3.本图纸必须经甲乙双方认可并签字方可作为施工依据。

日期
Date 03/24/26

修订
Revision

1

项目
Project
潮映华岸府3-801

比例
Scale 1:60@A2

主龙骨平面图

图纸编号
Drawing No.
CL.PL-04.3

项目编号
Project No.

©2025

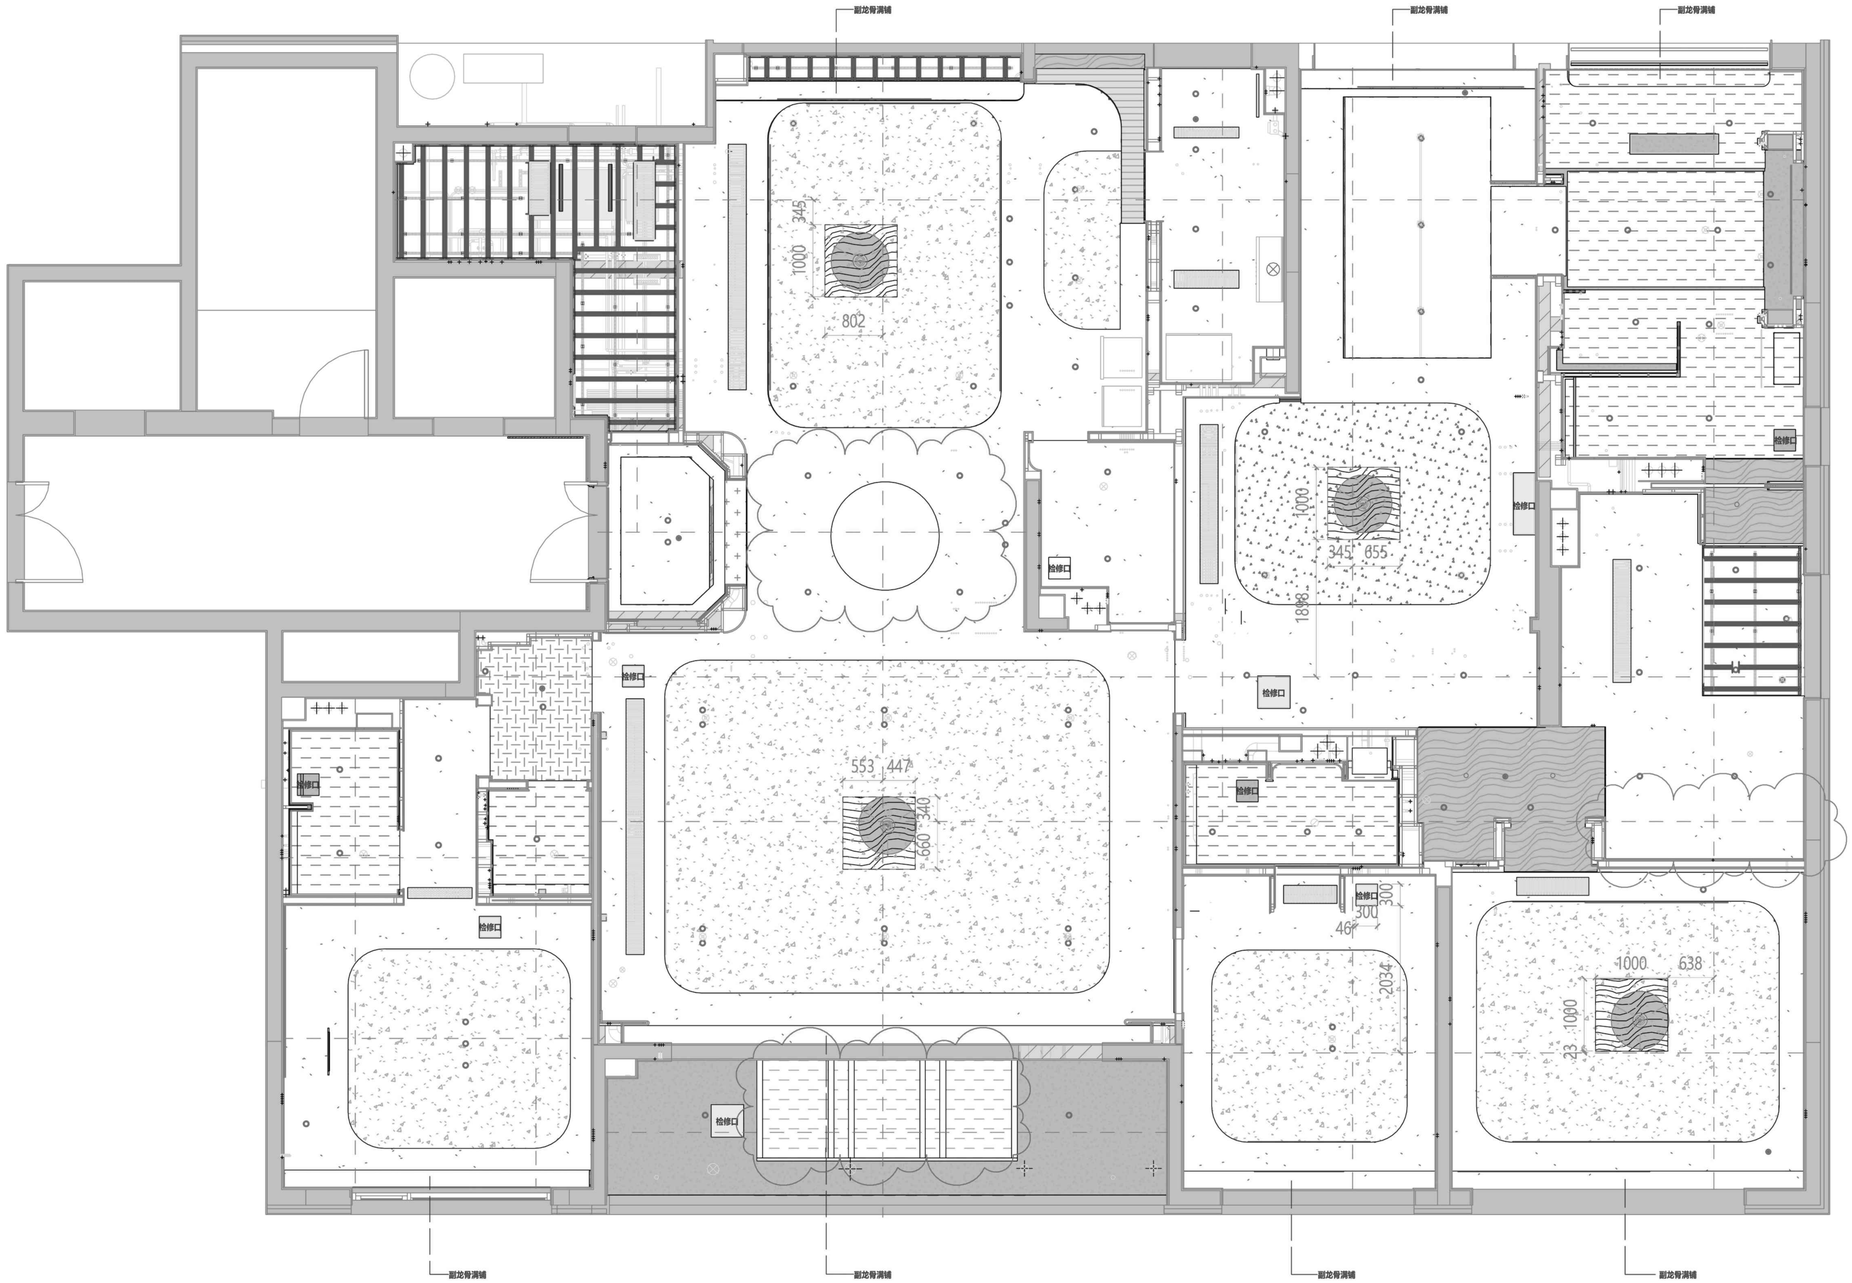
副龙骨调铺
副龙骨调铺
副龙骨调铺
检修口
检修口
检修口

云线批注处：主卧衣帽间木饰面和石膏板吊顶范围调整。

第一层石膏板平面图

Scale比例 1:60@A2

FIBORN

注意：
原则1：规格-丝杆离墙≤300mm，丝杆间距≤800mm。
原则2：主龙间距≤800mm，接口采用双铆钉固定。
原则3：副龙间距≤300mm，接口采用双铆钉固定。
原则4：弹性尺寸，若受管路影响可依现场情况调节；但必须符合原则1的要求。

图例A
LEGEND A

编号	图例	说明
1		边龙骨
2		主龙骨-常规龙骨
3		主龙骨-卡式龙骨
4		副龙骨
5		吊点
6		L型防裂板
7		L型转角防裂板
8		起铺点标识
9		第一层石膏板分缝
10		第二层石膏板分缝
11		室内梁
12		检修口
13		空调检修口
14		晾衣架角钢
15		加固区域，具体以灯具厂商的说明为准

盖章

注释
Notes

1.本图纸如与现场尺寸有误，请施工人员与项目负责人联系。
2.施工前施工人员应认真查阅此图，如有不明确尺寸，按现场测量为准。
3.本图纸必须经甲乙双方认可并签字方可作为施工依据。

日期
Date 03/24/26

修订
Revision

1

项目
Project

潮映华岸府3-801

比例
Scale 1:60@A2

第一层石膏板平面图

图纸编号
Drawing No.

CL.PL-05.1

项目编号
Project No.

©2025

云线批注处：主卧衣帽间和主卫铝型材调整

编号	大样	截面
CL1 平面图例	9.5mm厚纸面石膏板 铝型材YFC-B-01	5 25 25 5 YFC-B-01
CL2 平面图例	铝型材YFC-B-05 34 50	40 10 14 20 YFC-B-05
CL3 平面图例	10 9.5mm厚纸面石膏板 铝型材YFC-B-04	30 10 8 YFC-B-04
CL4 平面图例	铝型材SK-A102 9.5mm厚纸面石膏板	12 15 10 15 SK-A102
CL5 平面图例	9.5mm厚防潮石膏板 铝型材SK-A501	13 12 11 7 SK-A501
CL6 平面图例	铝型材YFC-D-02 50 34 9.5mm厚防潮石膏板	10 11 27 7 10 26 7 6 YFC-D-02

CL1

位置编号	铝型材	铝型材长度(mm)
	YFC-B-01	1393 mm
	YFC-B-01	1393 mm
	YFC-B-01	1393 mm
	YFC-B-01	1393 mm
	YFC-B-01	1393 mm
	YFC-B-01	1393 mm
CL1-1	YFC-B-01	4152 mm
CL1-2	YFC-B-01	3744 mm
CL1-3	YFC-B-01	455 mm
CL1-4	YFC-B-01	455 mm
CL1-5	YFC-B-01	1270 mm
CL1-6	YFC-B-01	1944 mm
CL1-7	YFC-B-01	3233 mm
CL1-8	YFC-B-01	1944 mm
CL1-9	YFC-B-01	2565 mm
CL1-10	YFC-B-01	2319 mm
CL1-11	YFC-B-01	1590 mm
CL1-12	YFC-B-01	2319 mm
CL1-13	YFC-B-01	1590 mm
CL1-14	YFC-B-01	4855 mm
CL1-15	YFC-B-01	3448 mm
CL1-22	YFC-B-01	4220 mm
CL1-23	YFC-B-01	7279 mm
总计		55740 mm

CL2

位置编号	铝型材	铝型材长度(mm)
CL2-1	YFC-B-05	1518 mm
CL2-2	YFC-B-05	1054 mm
CL2-3	YFC-B-05	1375 mm
CL2-4	YFC-B-05	1325 mm
CL2-5	YFC-B-05	1143 mm
总计		6415 mm

CL3

位置编号	铝型材	铝型材长度(mm)
CL3-1	YFC-B-04	2470 mm
CL3-2	YFC-B-04	1361 mm
CL3-3	YFC-B-04	1245 mm
CL3-4	YFC-B-04	1652 mm
CL3-5	YFC-B-04	1288 mm
总计		8016 mm

CL4

位置编号	铝型材	铝型材长度(mm)
CL4-1	SK-A102	810 mm
CL4-2	SK-A102	980 mm
CL4-3	SK-A102	995 mm
总计		2785 mm

CL5

位置编号	铝型材	铝型材长度(mm)
	SK-A501	3605
	SK-A501	1403
	SK-A501	1403
	SK-A501	1403
	SK-A501	1403
	SK-A501	1403
	SK-A501	1403
	SK-A501	1403
	SK-A501	1403
	SK-A501	1403
CL5		17635
总计		

位置编号	铝型材	铝型材长度(mm)
CL6-1	YFC-D-02	4566
CL6-2	YFC-D-02	1092
CL6-3	YFC-D-02	1288
CL6-4	YFC-D-02	1902
CL6-5	YFC-D-02	4390
CL6-6	YFC-D-02	1388
总计		14626

铝型材用量(图纸尺寸，须以现场核实为准)

位置编号	铝型材	数量
CL1	YFC-B-01	55740mm≈22支（3000/支）
CL2	YFC-B-05	6415mm≈5支（3000/支）
CL3	YFC-B-04	8016mm≈5支（3000/支）
CL4	SK-A102	2785mm≈3支（3000/支）
CL5	SK-A501	12023mm≈7支（3000/支）
CL6	YFC-D-02	14626mm≈6支（3000/支）

小计	YFC-B-01	23支（3000/支）
	YFC-B-05	5支（3000/支）
	YFC-B-04	5支（3000/支）
	SK-A102	3支（3000/支）
	SK-A501	7支（3000/支）
	YFC-D-02	6支（3000/支）

图例A
LEGEND A

颜色	图例
	YFC-B-01
	YFC-B-05
	YFC-B-04
	SK-A102
	SK-A501
	YFC-D-02

日期
Date 03/24/26

修订
Revision 1

项目
Project
潮映华府府3-801

Scale 比例 1:5@A2

天花铝型材分析图

Drawing No. 图纸编号
CL.PL-05.2

Project No. 项目编号 ©2026

1 天花铝型材分析图

Scale比例 1 : 60@A2

2 天花铝型材节点图

Scale比例 1:5@A2

注释
Notes
1.本图纸如与现场尺寸有误，请施工人员与项目负责人联系。
2.施工前施工人员应认真查阅此图，如有不明确尺寸，按现场测量为准。
3.本图纸必须结甲乙双方认可并签字方可作为施工依据。

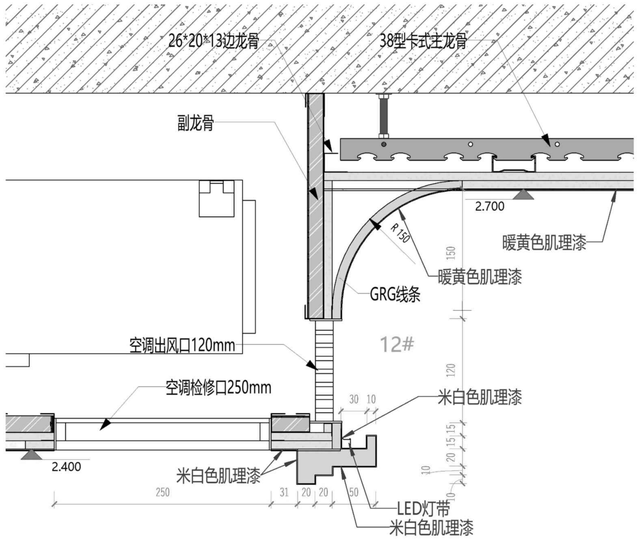

1 CL.DT-06 DT-20

scale: 1:5

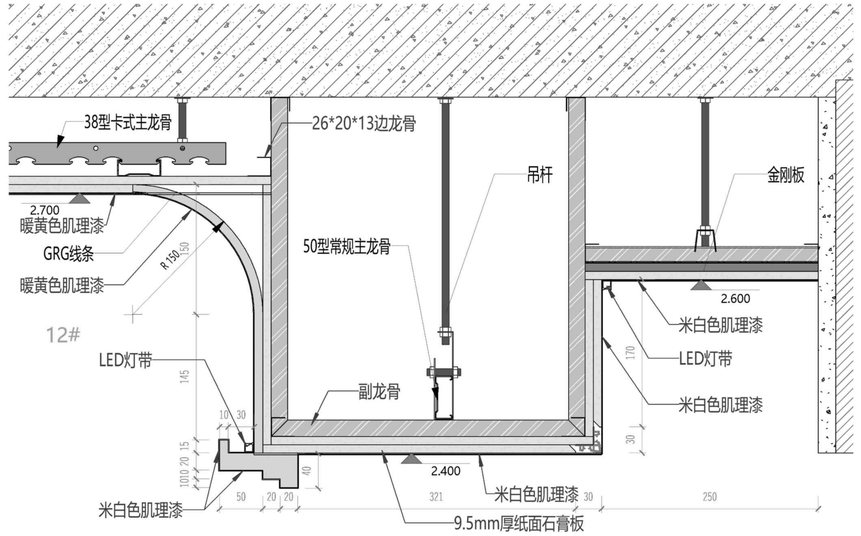

2 CL.DT-06 DT-21

scale: 1:5

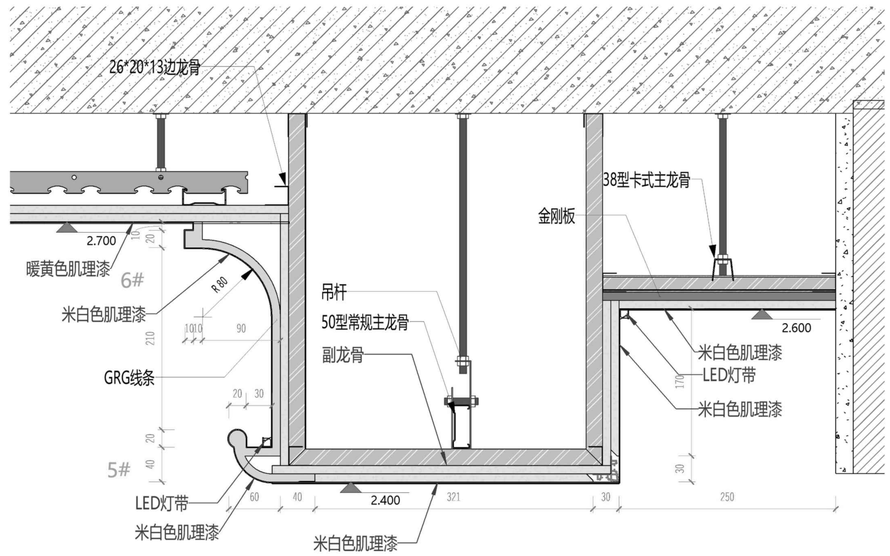

3 CL.DT-06 DT-22

scale: 1:5

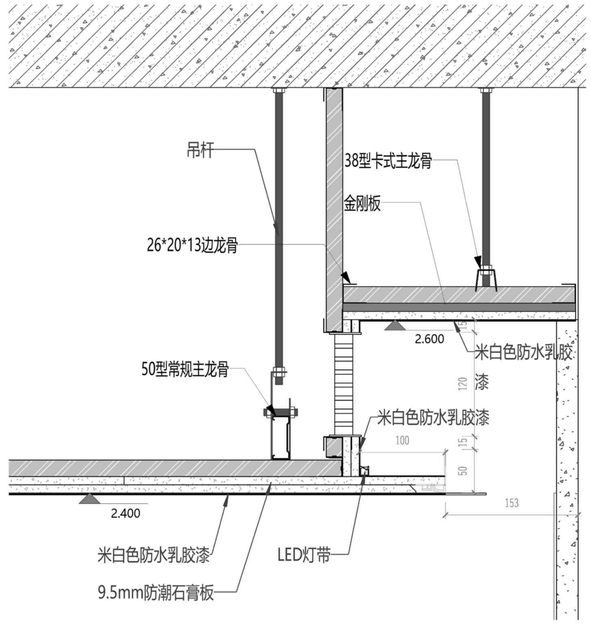

4 CL.DT-06 DT-23

scale: 1:5

FIBORN

盖章

注释
Notes

1.本图纸如与现场尺寸有误，请施工人员与项目负责人联系。
2.施工前施工人员应认真查阅此图，如有不明确尺寸，按现场测量为准。
3.本图纸必须经甲乙双方认可并签字方可作为施工依据。

日期
Date 03/24/26

修订
Revision

1

项目
Project

潮映华岸府3-801

比例
Scale 1:5@A2

天花节点图

图纸编号
Drawing No.

CL.DT-06

项目编号
Project No.

©2025

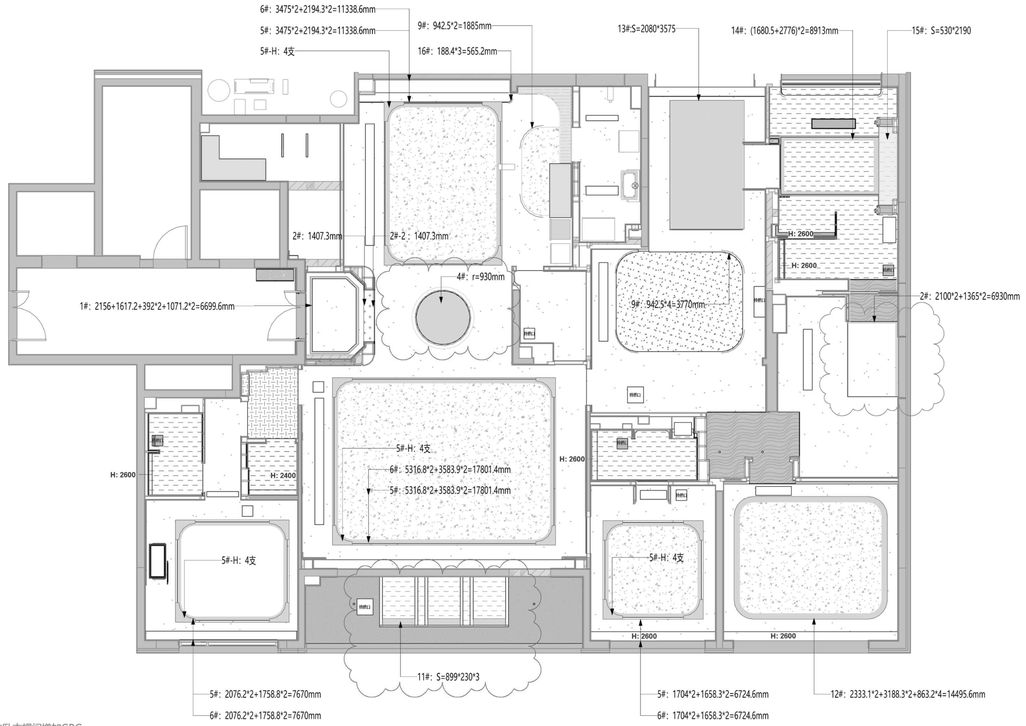

云线批注处：主卧-衣帽间增加GRG

云线批注处：阳台GRG，玄关穹顶处GRG大样调整

编号	大样	截面	长度
1#	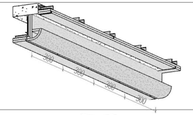		6699.6mm
2#	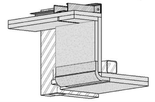		8337.3mm
2#-2			1407.3mm
4#	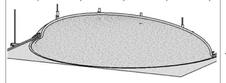		r=930mm
5#	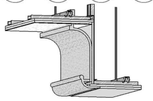		43534.6mm
5#-H	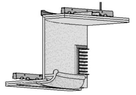		12支
6#	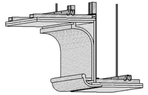		43534.6mm

编号	大样	截面	长度
9#	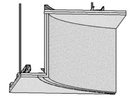	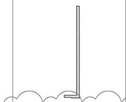	5655mm
11#	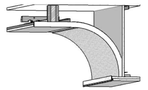	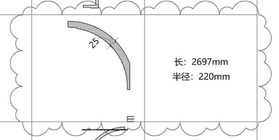	长：2697mm 半径：220mm
12#	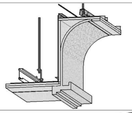	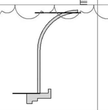	14495.6mm
13#	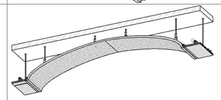		长：2080mm 宽：3575mm
14#	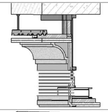		8913mm
15#	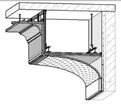		长：530mm 宽：2190mm
16#	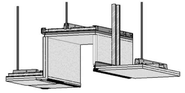		565.2mm

1	GRG平面图	2	GRG节点图
	Scale比例 1：60@A2		Scale比例 1:5@A2

注释
Notes
1.本图纸如与现场尺寸有误，请施工人员与项目负责人联系。
2.施工前施工人员应认真查阅此图，如有不明确尺寸，按现场测量为准。
3.本图纸必须经甲乙双方认可并签字方可作为施工依据。

日期
Date 03/24/26

修订
Revision 1

项目
Project
潮映华府府3-801

Scale
比例 1:5@A2

天花GRG分析图

Drawing No.
图纸编号
CL-PL-05.3

Project No.
项目编号 ©2026

云线批注处：主卧衣帽间木饰面和石膏板吊顶范围调整。

注意：
原则1：规格-丝杆离墙≤300mm，丝杆间距≤800mm。
原则2：主龙间距≤800mm，接口采用双铆钉固定。
原则3：副龙间距≤300mm，接口采用双铆钉固定。
原则4：弹性尺寸，若受管路影响可依现场情况调节；但必须符合原则1的要求。

图例A
LEGEND A

编号	图例	说明
1		边龙骨
2		主龙骨-常规龙骨
3		主龙骨-卡式龙骨
4		副龙骨
5		吊点
6		L型防裂板
7		L型转角防裂板
8		起铺点标识
9		第一层石膏板分缝
10		第二层石膏板分缝
11		室内梁
12		检修口
13		空调检修口
14		晾衣架角钢
15		加固区域，具体以灯具厂商的说明为准

盖章

注释
Notes

1.本图纸如与现场尺寸有误，请施工人员与项目负责人联系。
2.施工前施工人员应认真查阅此图，如有不明确尺寸，按现场测量为准。
3.本图纸必须经甲乙双方认可并签字方可作为施工依据。

日期
Date 03/24/26

修订
Revision

1

项目
Project
潮映华岸府3-801

比例
Scale 1:60@A2

第二层石膏板平面图

图纸编号
Drawing No.
CL.PL-05.4

项目编号
Project No.

©2025

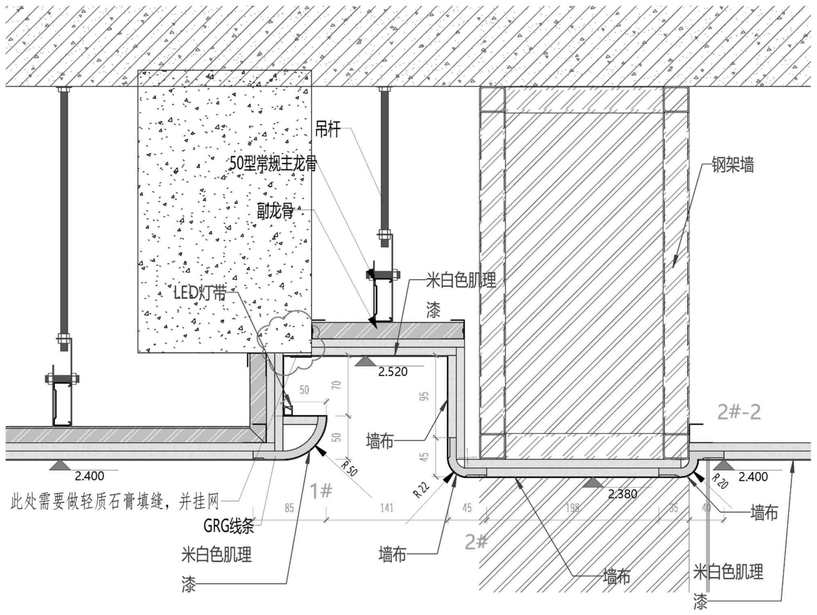

1 DT-01
CL.DT-01
scale: 1 : 5

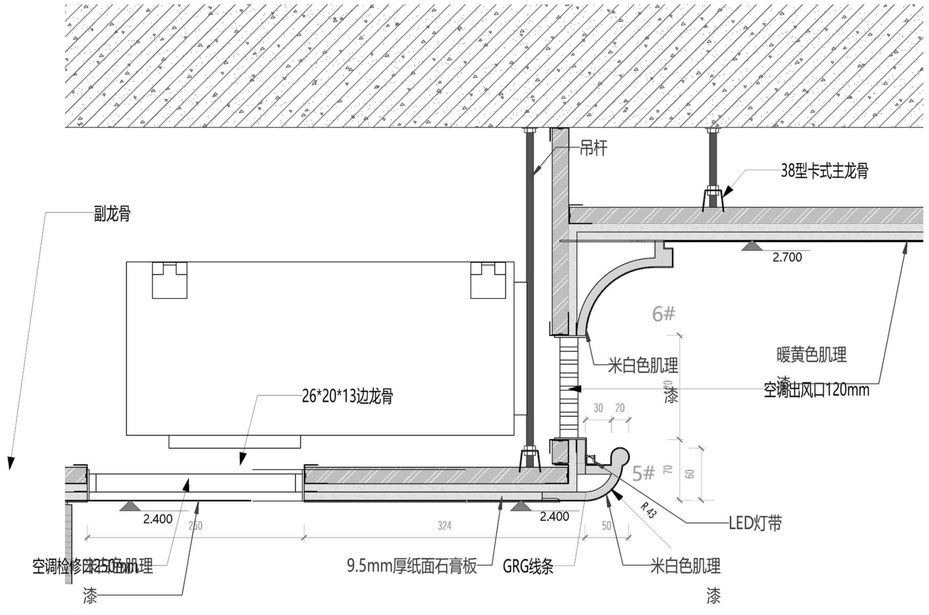

2 DT-02
CL.DT-01
scale: 1 : 5

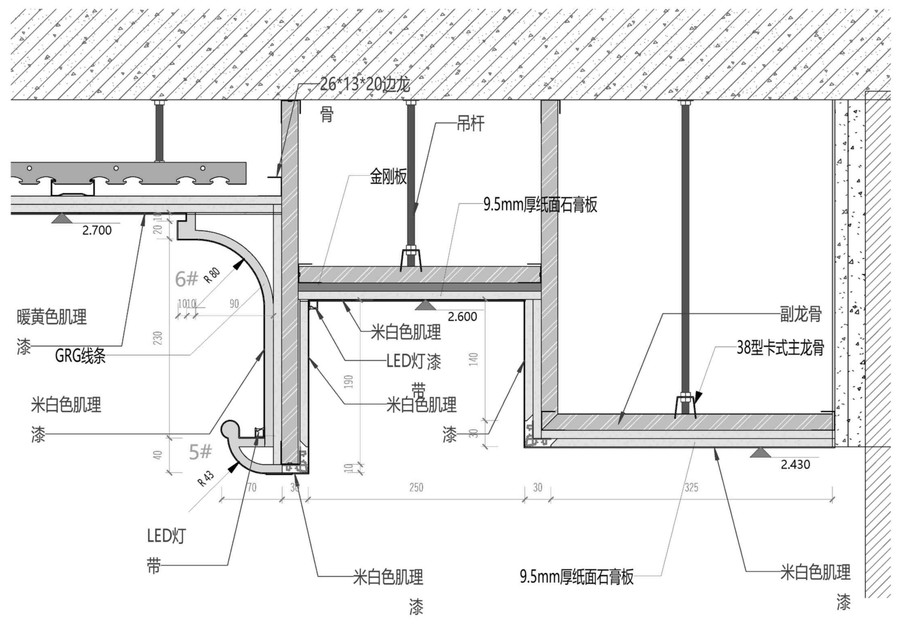

3 DT-03
CL.DT-01
scale: 1 : 5

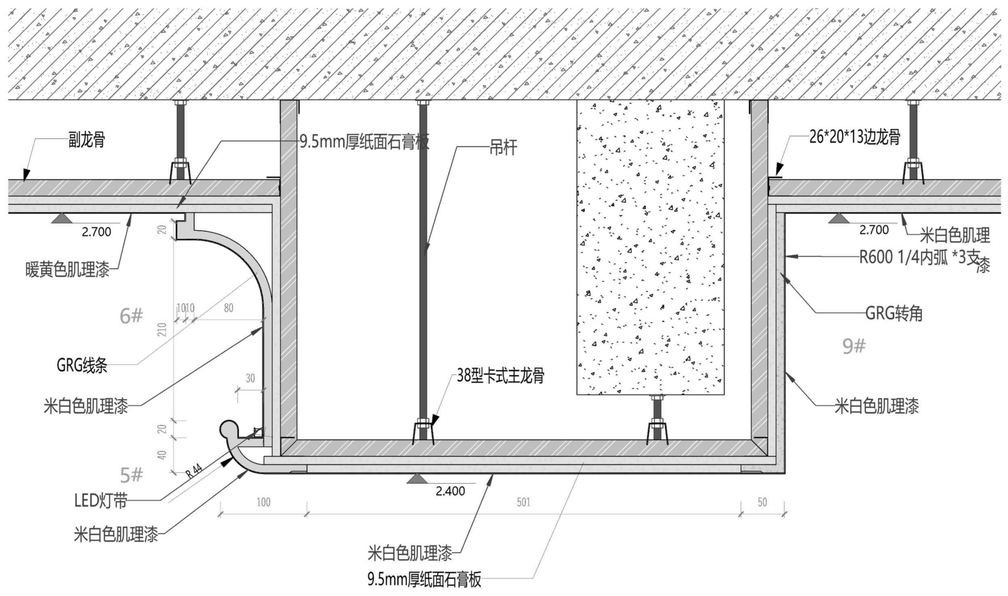

4 DT-04
CL.DT-01
scale: 1 : 5

盖章

注释
Notes

1.本图纸如与现场尺寸有误，请施工人员与项目负责人联系。
2.施工前施工人员应认真查阅此图，如有不明确尺寸，按现场测量为准。
3.本图纸必须经甲乙双方认可并签字方可作为施工依据。

日期
Date 03/24/26

修订
Revision

1

项目
Project
潮映华岸府3-801

比例
Scale 1:5@A2

天花节点图

图纸编号
Drawing No.
CL.DT-01

项目编号
Project No.

©2025

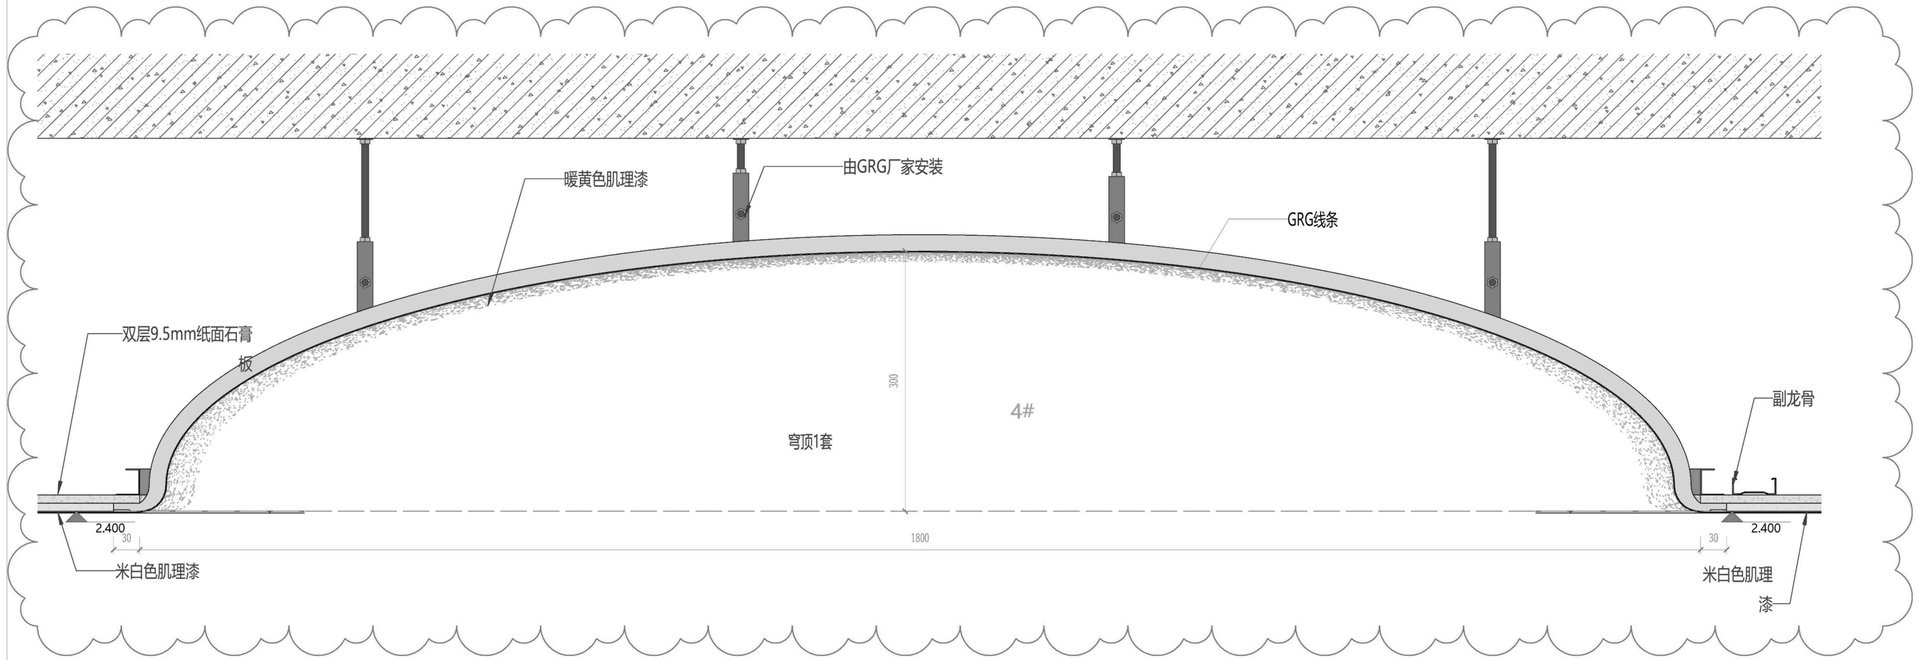

1 DT-05
CL.DT-02
scale: 1:5

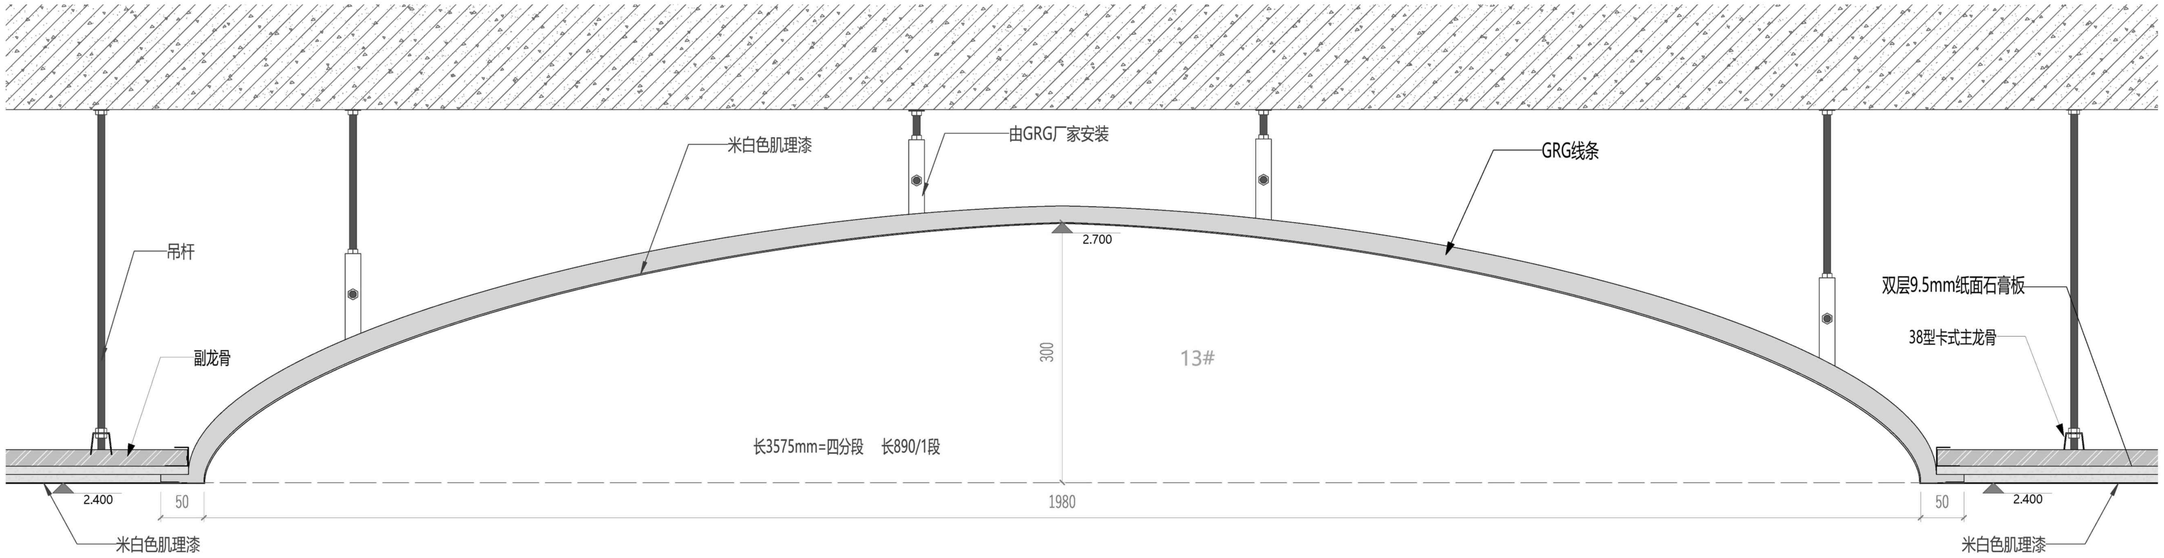

2 DT-11
CL.DT-02
scale: 1:5

云线批注处：玄关处穹顶GRG调整

天花节点图

Scale比例 1:5@A2

FIBORN

盖章

注释
Notes

1.本图纸如与现场尺寸有误，请施工人员与项目负责人联系。
2.施工前施工人员应认真查阅此图，如有不明确尺寸，按现场测量为准。
3.本图纸必须经甲乙双方认可并签字方可作为施工依据。

日期
Date 03/24/26

修订
Revision

1

项目
Project
潮映华岸府3-801

比例
Scale 1:5@A2

天花节点图

图纸编号
Drawing No.
CL.DT-02

项目编号
Project No.

©2025

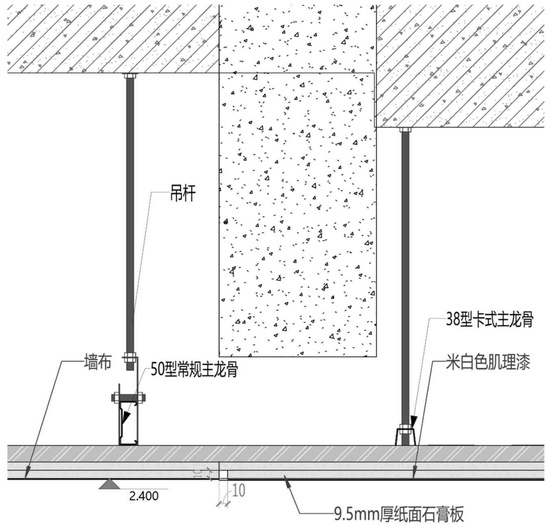

1 CL.DT-03 DT-06

scale: 1:5

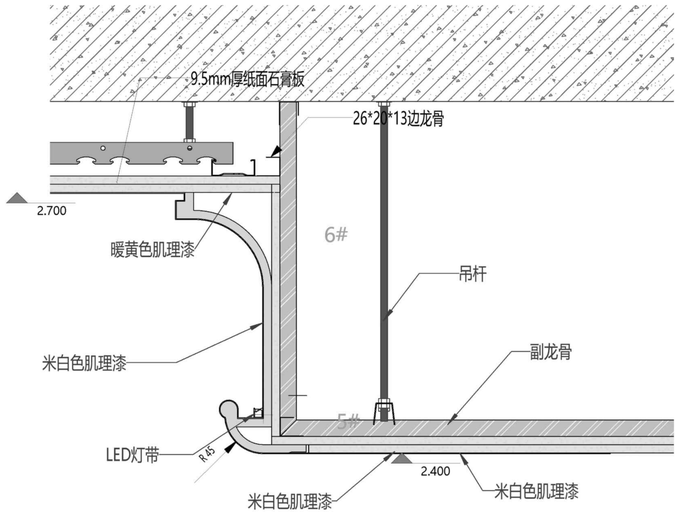

2 CL.DT-03 DT-07

scale: 1:5

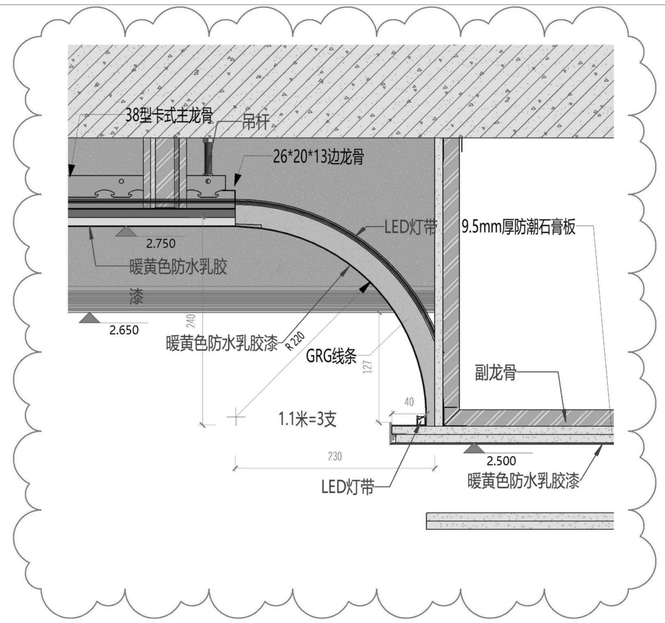

3 CL.DT-03 DT-08

scale: 1:5

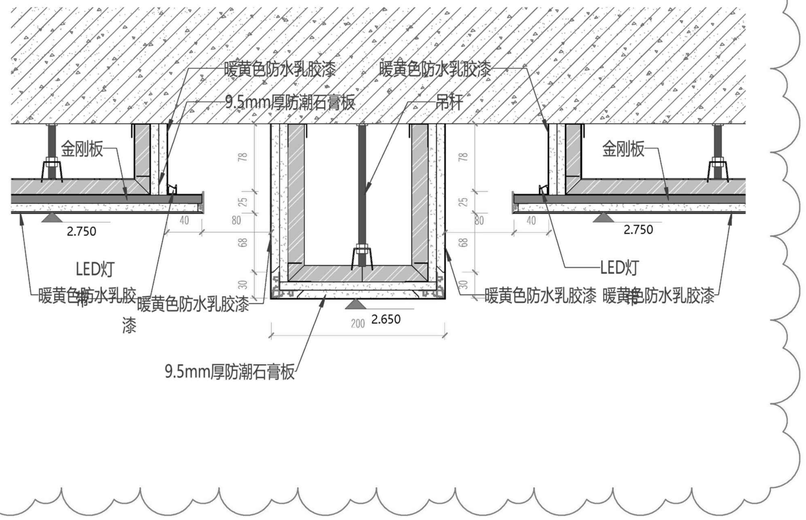

4 CL.DT-03 DT-09

scale: 1:5

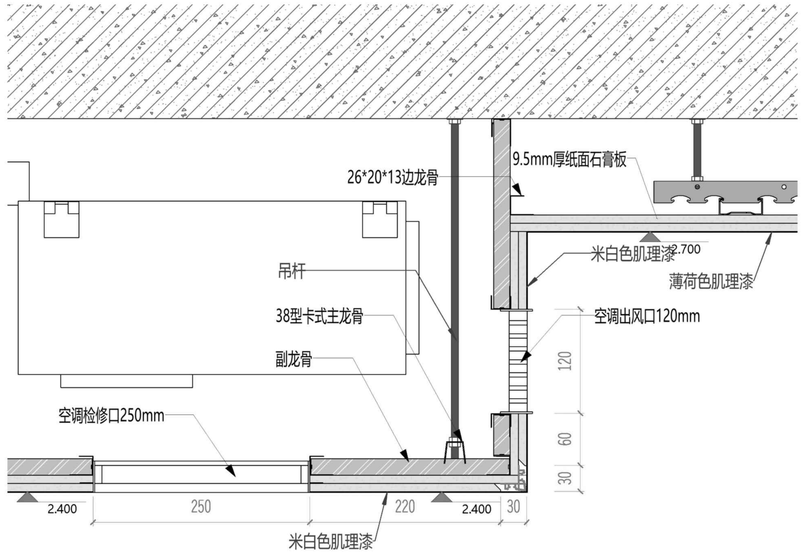

5 CL.DT-03 DT-10

scale: 1:5

云线批注处：阳台处龙骨跟随石膏板标高进行调整；GRG进行调整

天花节点图

Scale比例 1:5@A2

EIBORN

盖章

注释
Notes

1.本图纸如与现场尺寸有误，请施工人员与项目负责人联系。
2.施工前施工人员应认真查阅此图，如有不明确尺寸，按现场测量为准。
3.本图纸必须经甲乙双方认可并签字方可作为施工依据。

日期
Date 03/24/26

修订
Revision

1

项目
Project

潮映华岸府3-801

比例
Scale 1:5@A2

天花节点图

图纸编号
Drawing No.

CL.DT-03

项目编号
Project No.

©2025

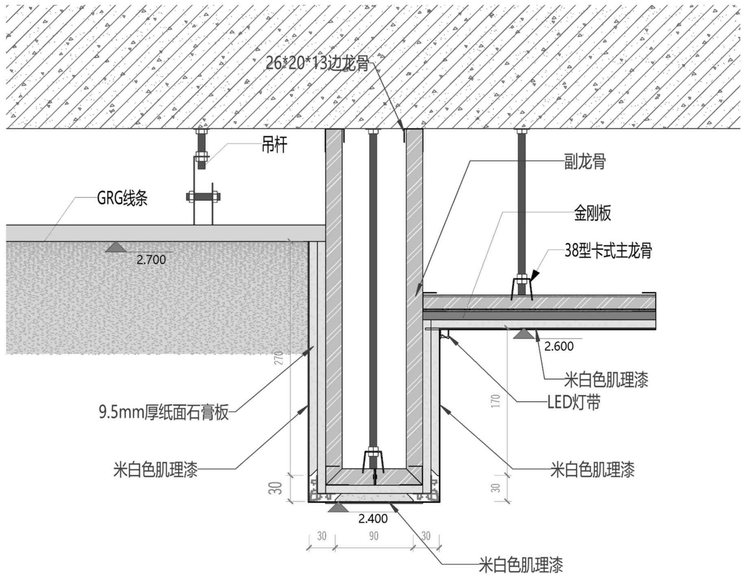

1 CL.DT-04 DT-12

scale: 1:5

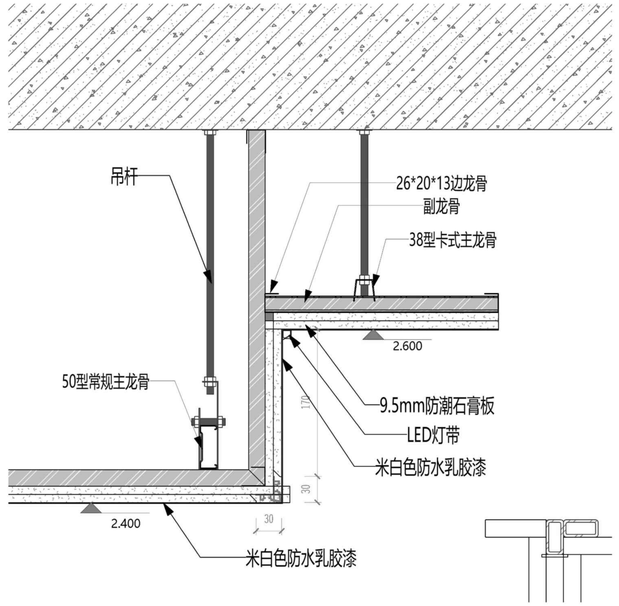

2 CL.DT-04 DT-13

scale: 1:5

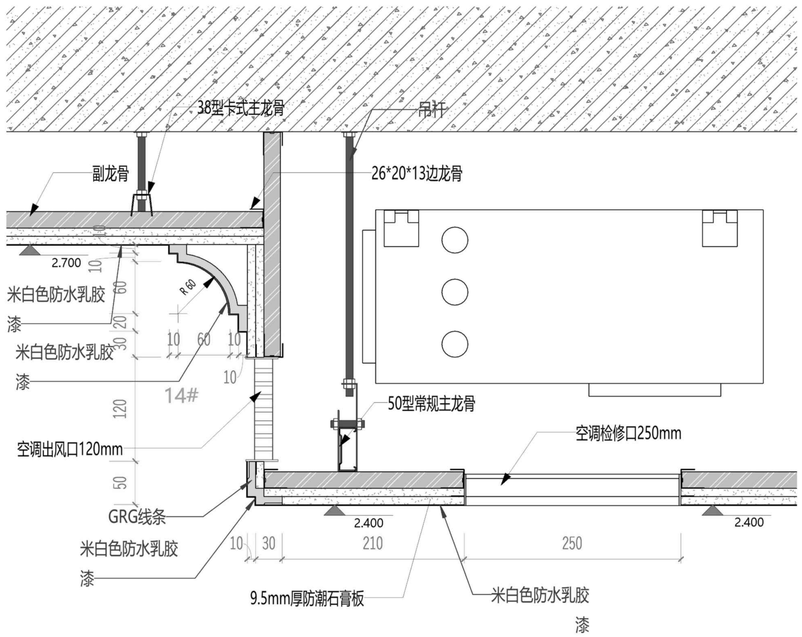

3 CL.DT-04 DT-14

scale: 1:5

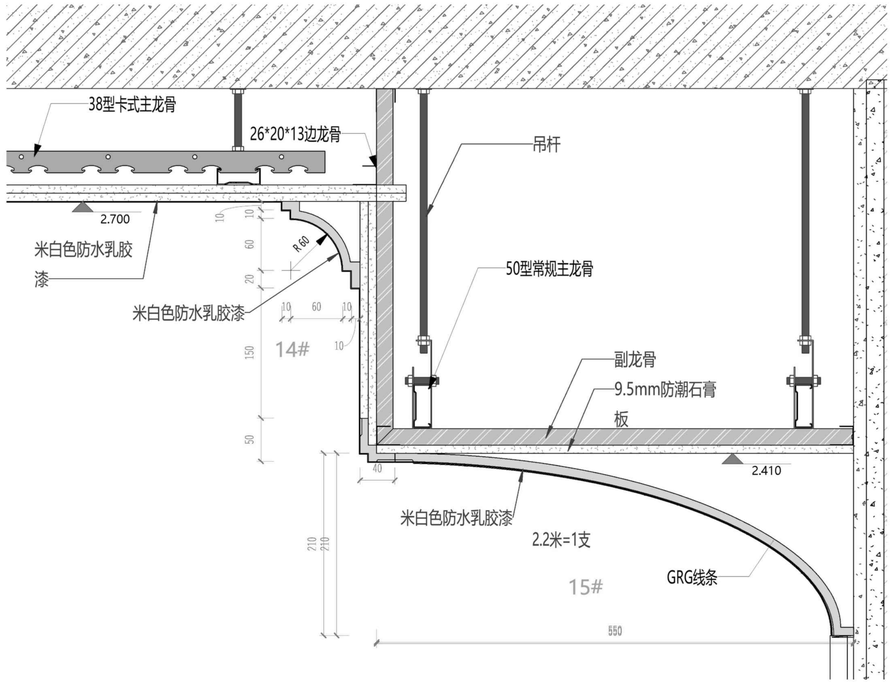

4 CL.DT-04 DT-15

scale: 1:5

天花节点图

Scale比例 1:5@A2

盖章

注释
Notes

1.本图纸如与现场尺寸有误，请施工人员与项目负责人联系。
2.施工前施工人员应认真查阅此图，如有不明确尺寸，按现场测量为准。
3.本图纸必须经甲乙双方认可并签字方可作为施工依据。

日期
Date 03/24/26

修订
Revision

1

项目
Project

潮映华岸府3-801

比例
Scale 1:5@A2

天花节点图

图纸编号
Drawing No.

CL.DT-04

项目编号
Project No.

©2025

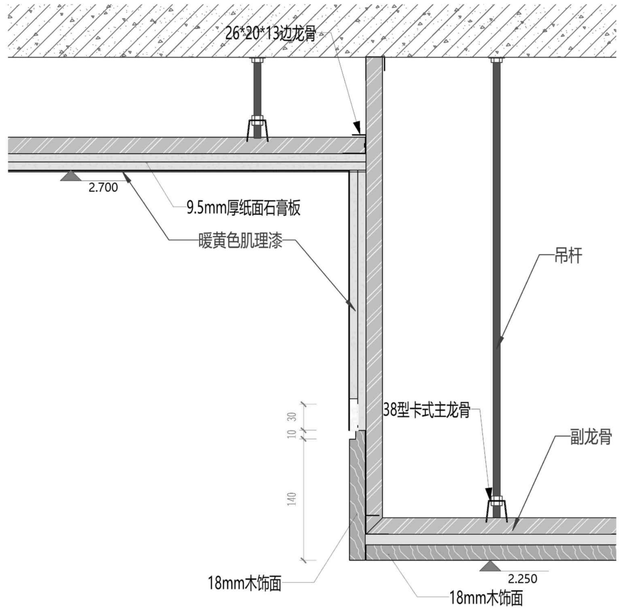

1 DT-16
CL.DT-05
scale: 1 : 5

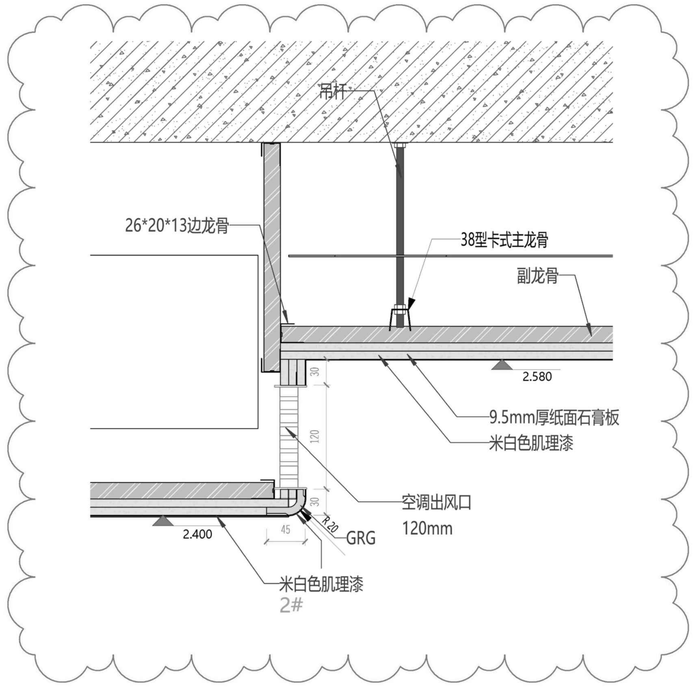

2 DT-17
CL.DT-05
scale: 1 : 5

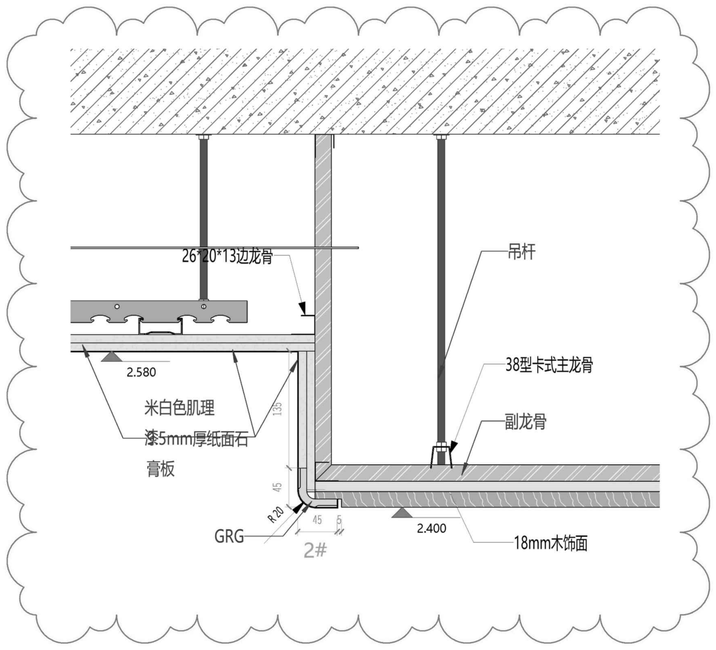

3 DT-18
CL.DT-05
scale: 1 : 5

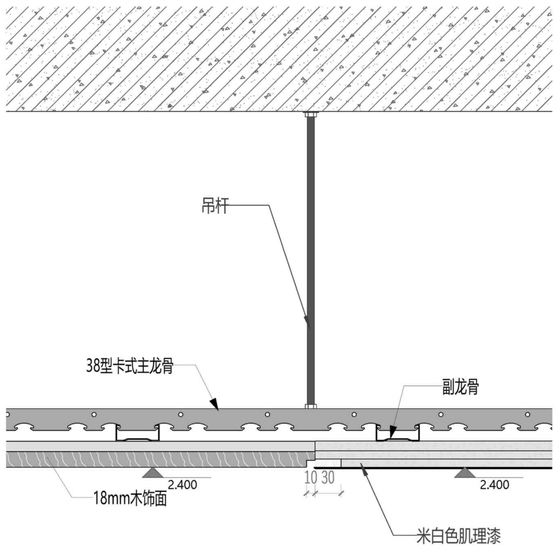

4 DT-19
CL.DT-05
scale: 1 : 5

云线批注处：主卧衣帽间高区龙骨跟随石膏板进行调整；铝型材调整为GRG

天花节点图

Scale比例 1:5@A2

盖章

注释
Notes

1.本图纸如与现场尺寸有误，请施工人员与项目负责人联系。
2.施工前施工人员应认真查阅此图，如有不明确尺寸，按现场测量为准。
3.本图纸必须经甲乙双方认可并签字方可作为施工依据。

日期
Date 03/24/26

修订
Revision

1

项目
Project

潮映华岸府3-801

比例
Scale 1:5@A2

天花节点图

图纸编号
Drawing No.

CL.DT-05

项目编号
Project No.

©2025