


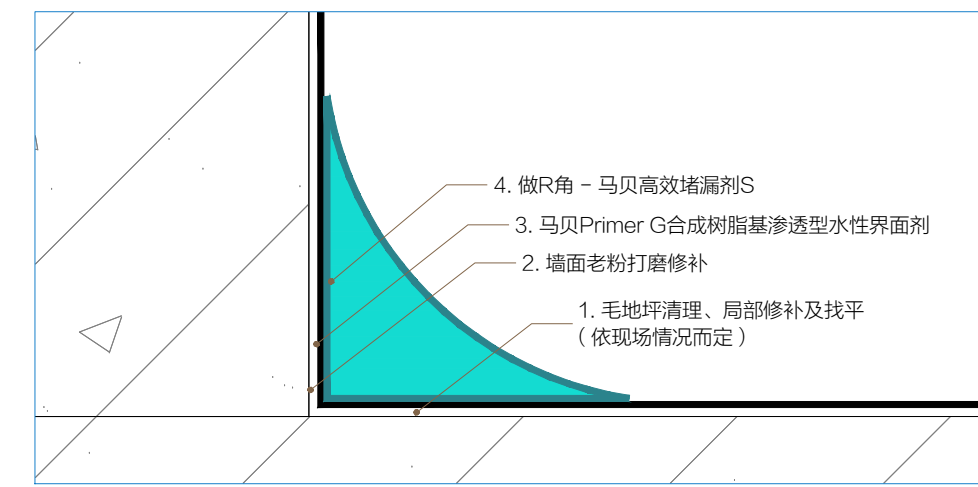
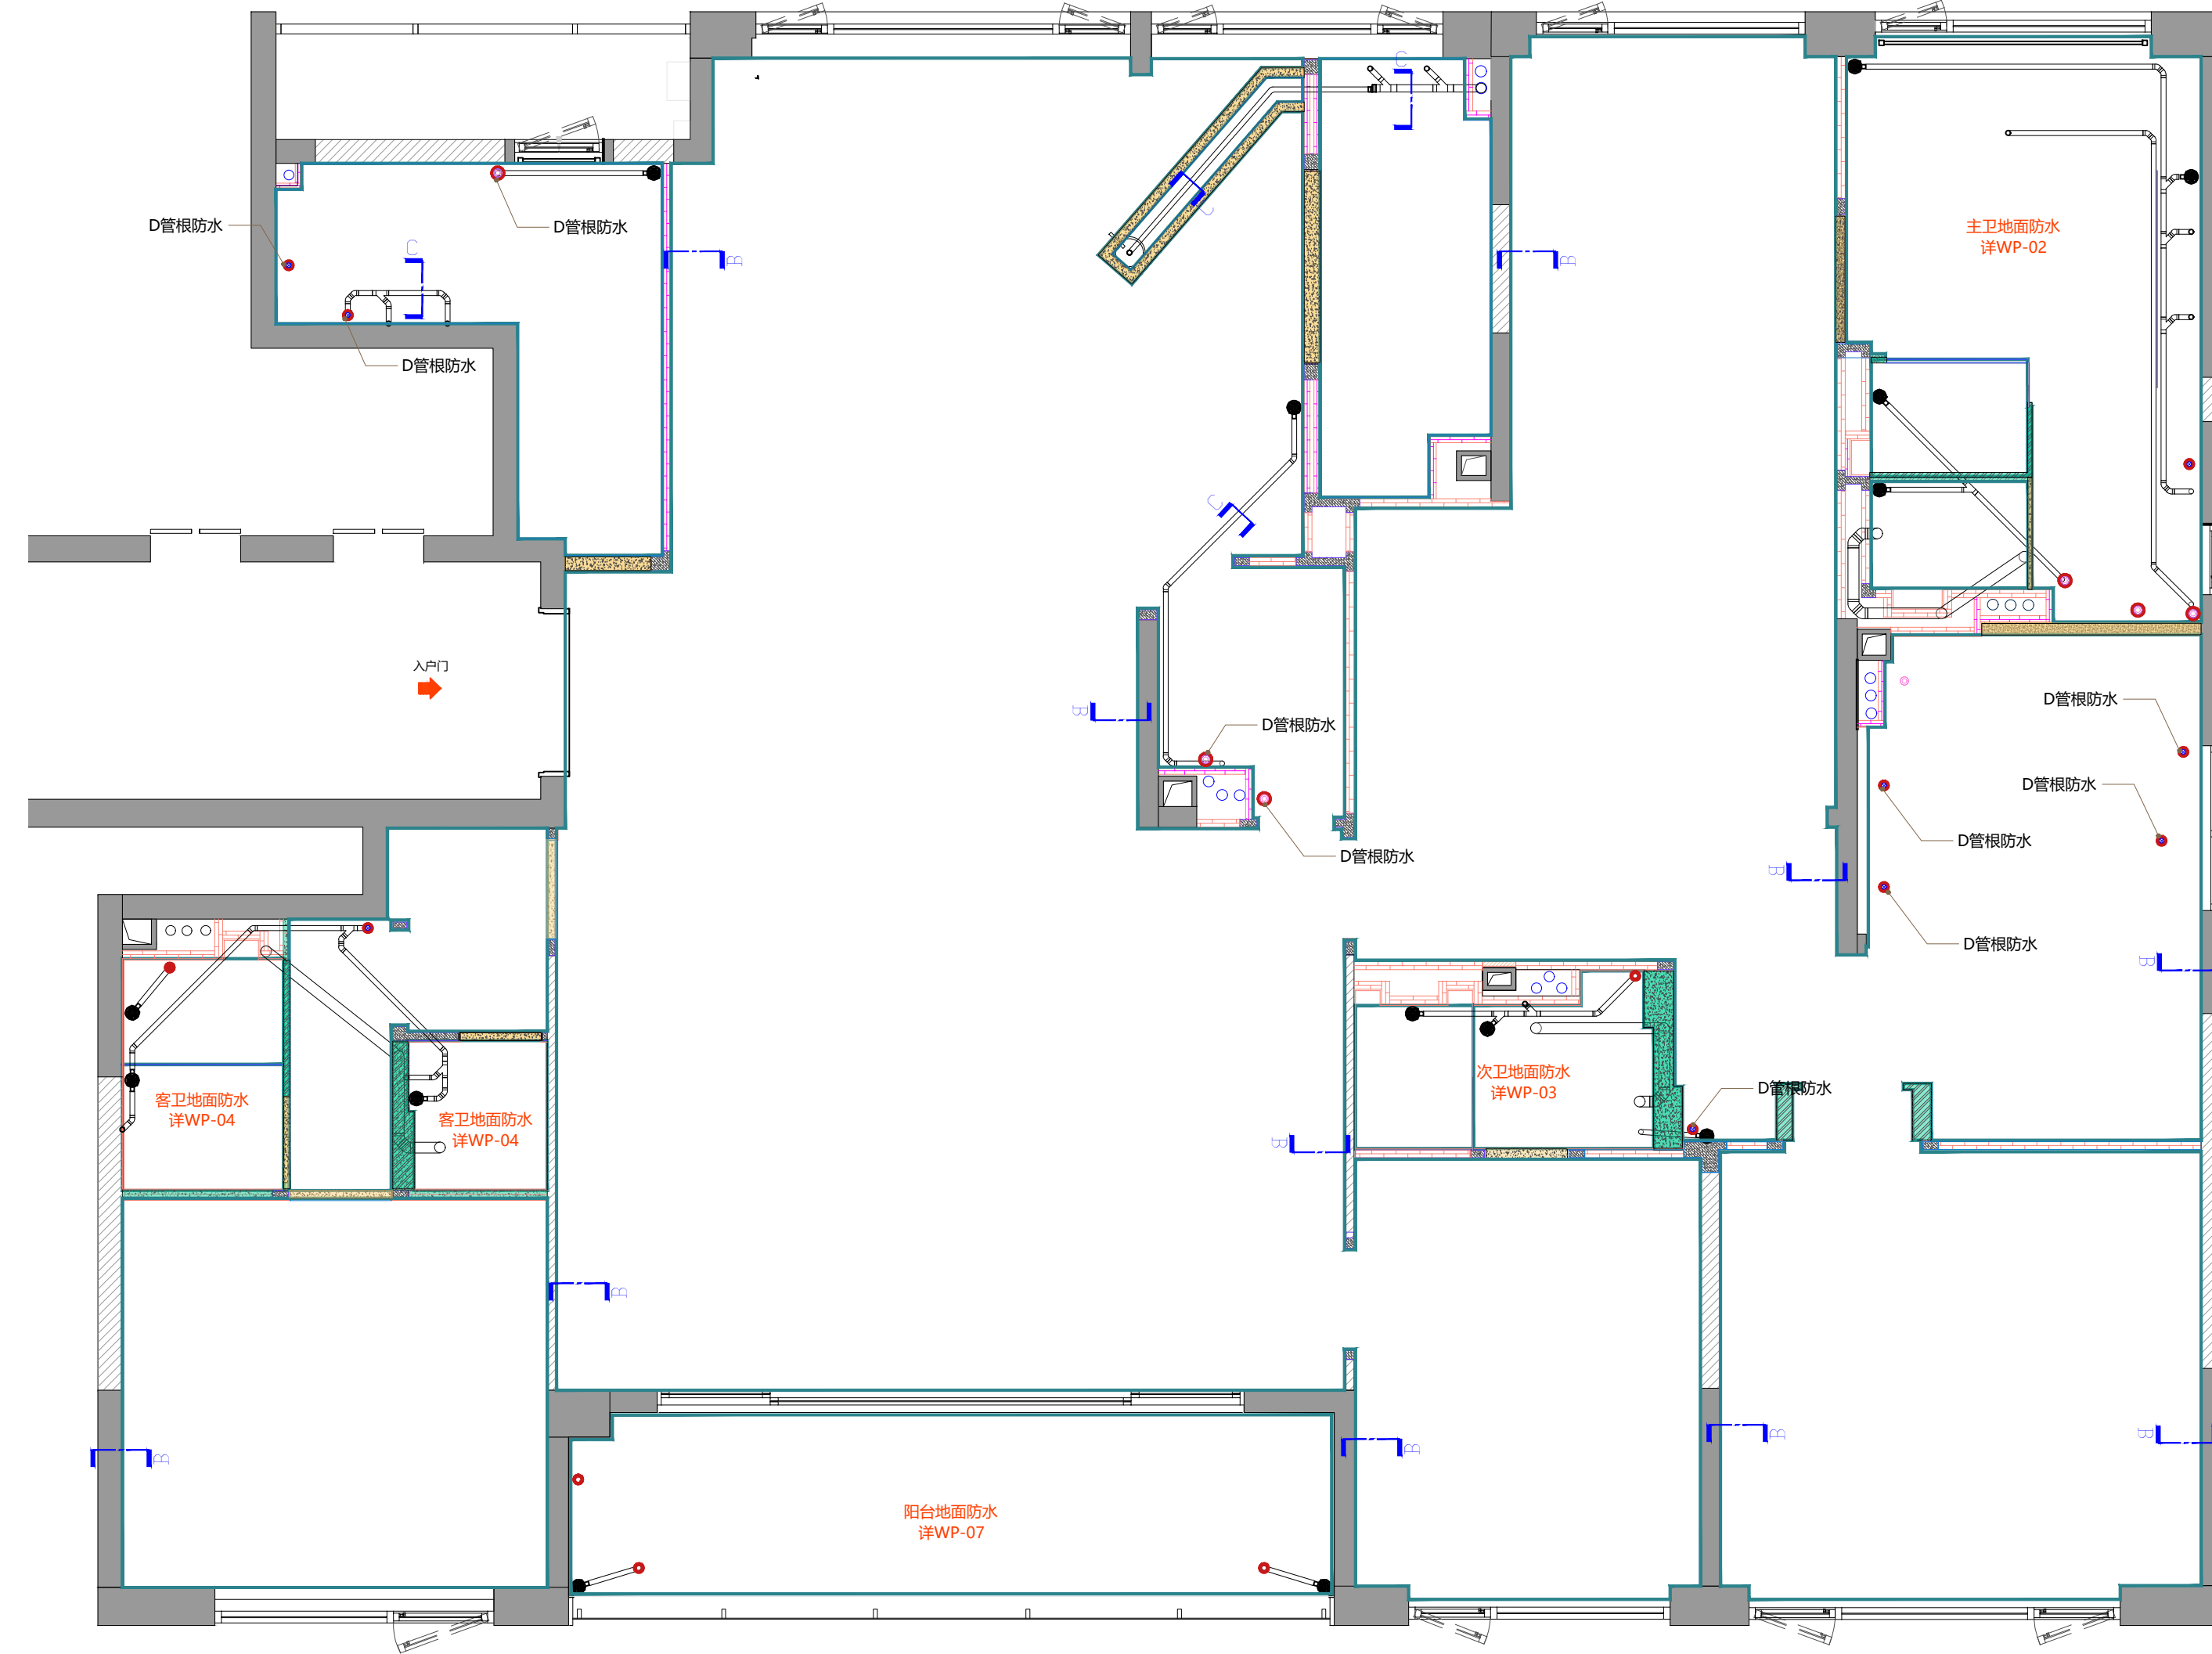
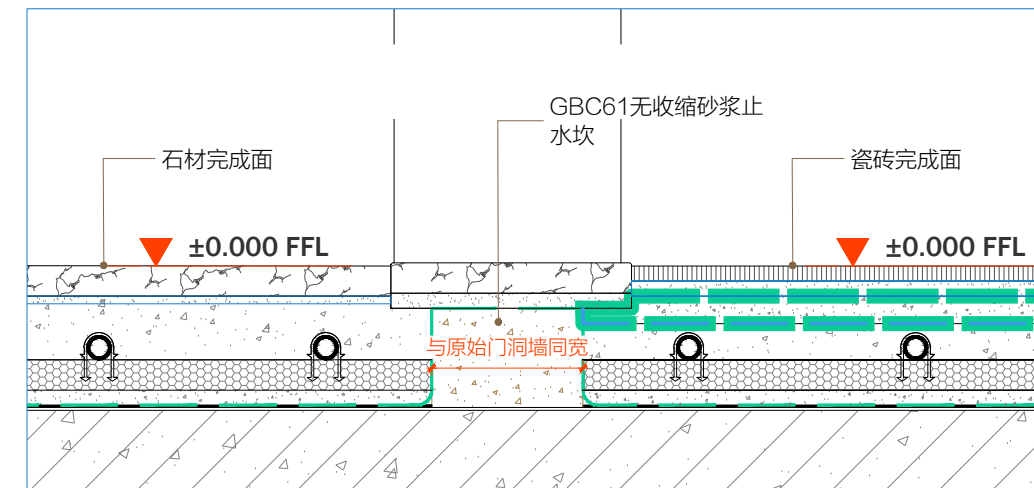
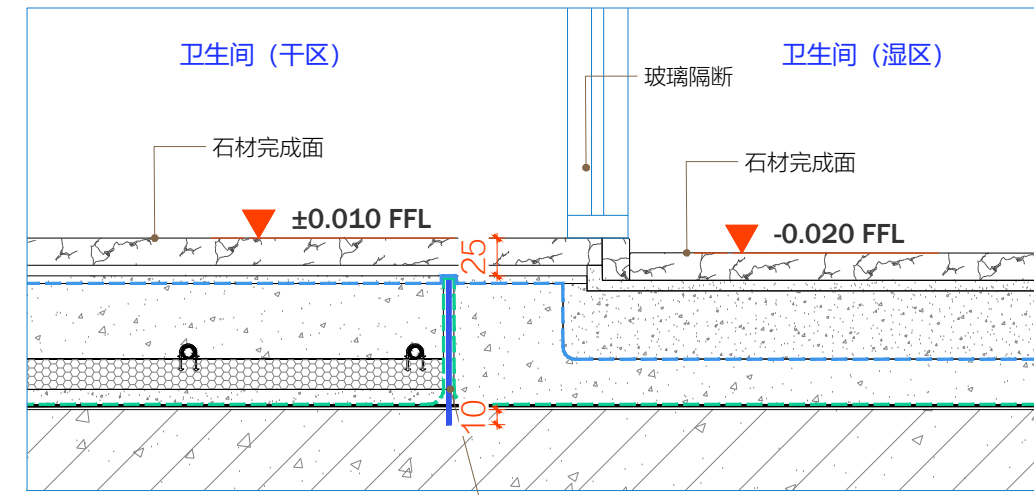
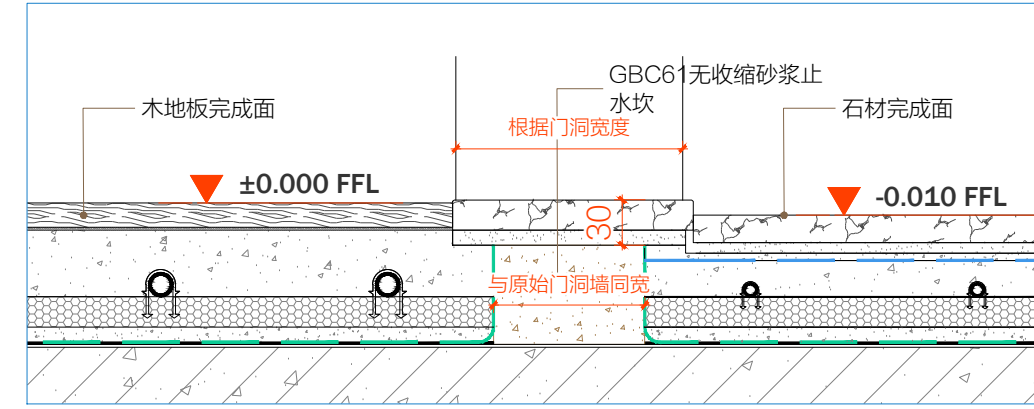
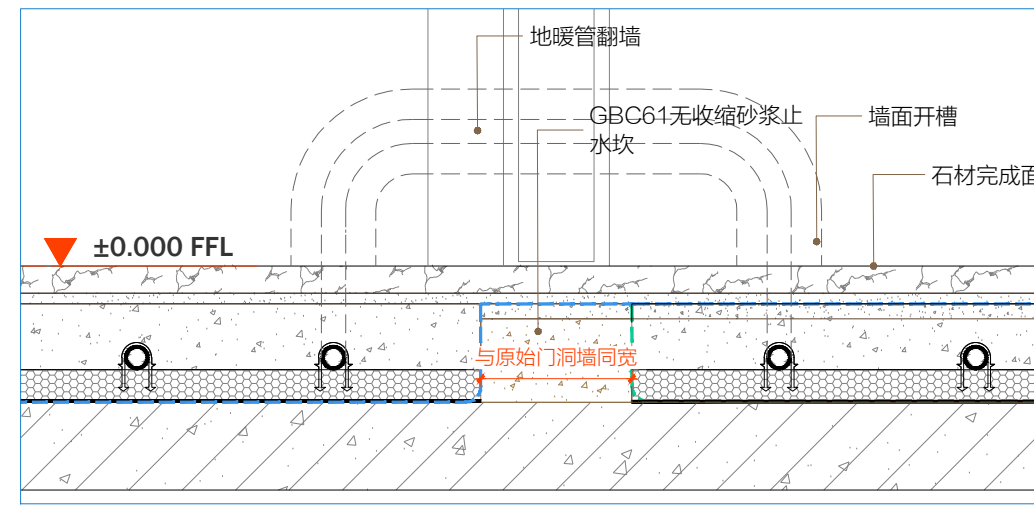
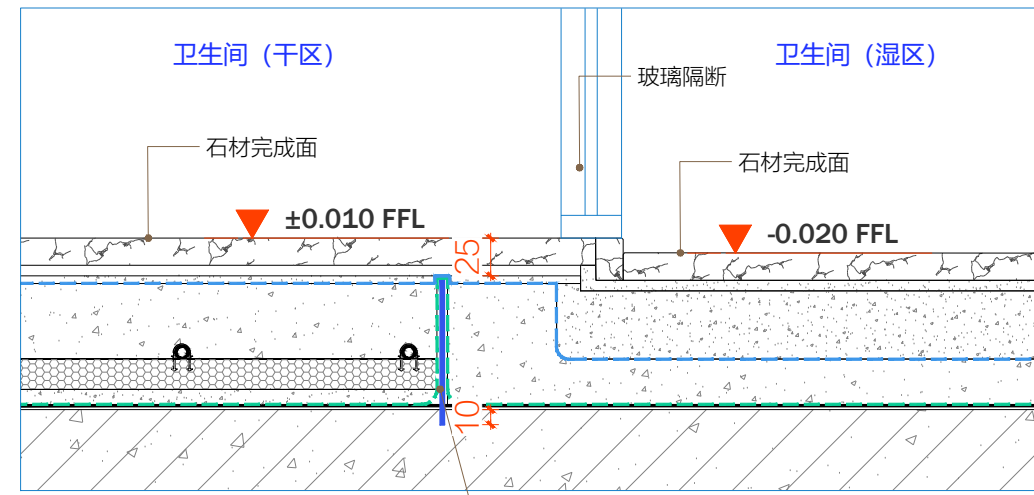
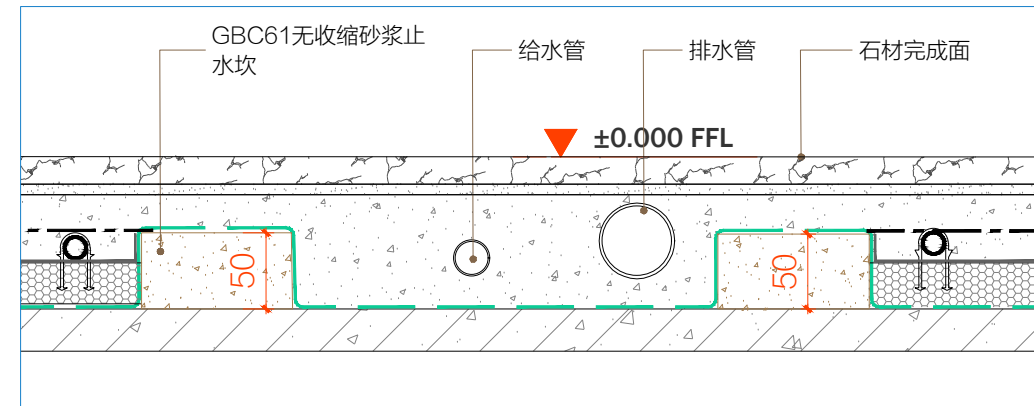


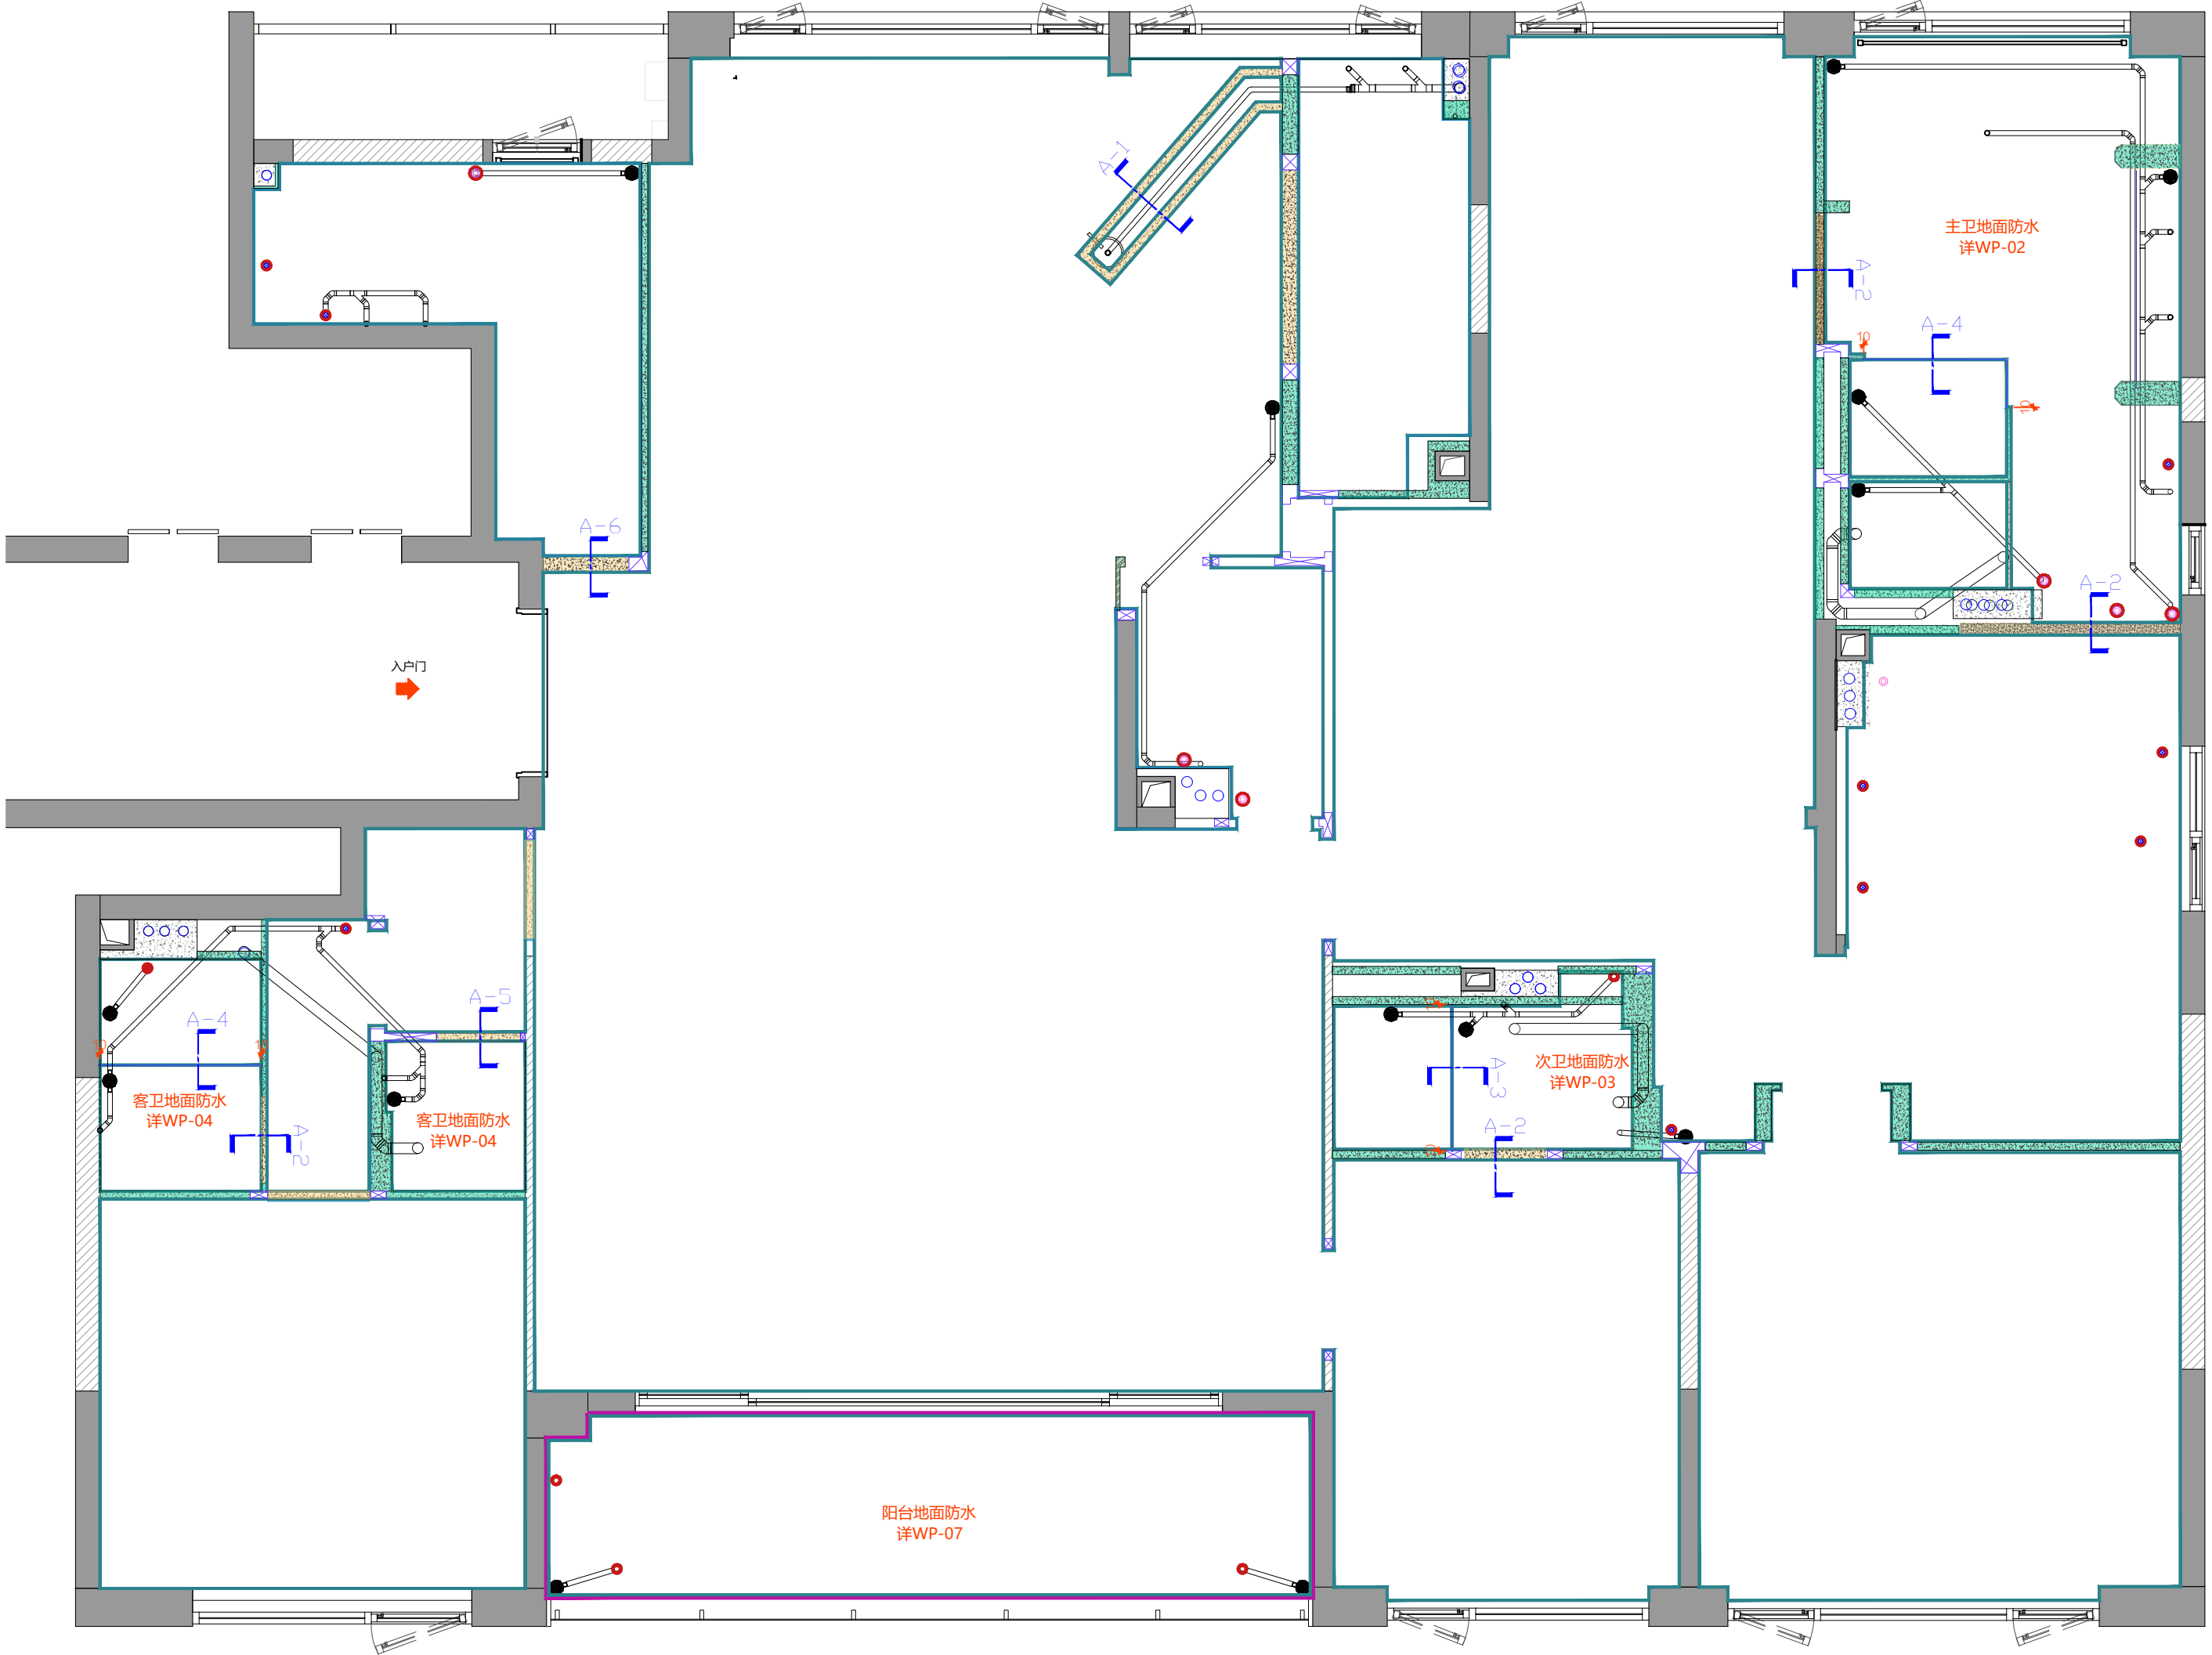


B 墙根防水节点图
Scale比例 1:2 @A2

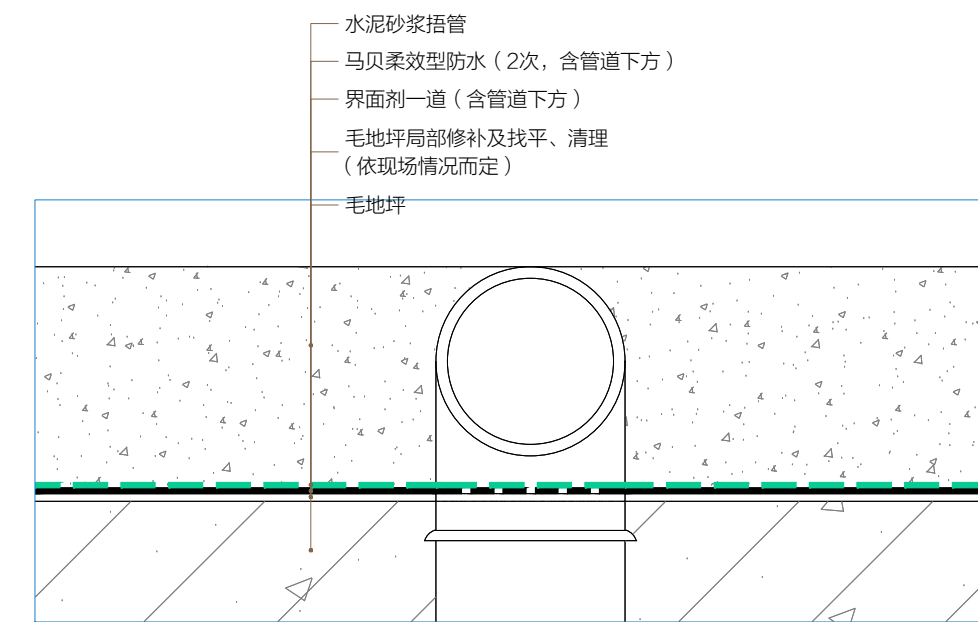

C 地面管道 堵管防水节点图
Scale比例 1:2 @A2

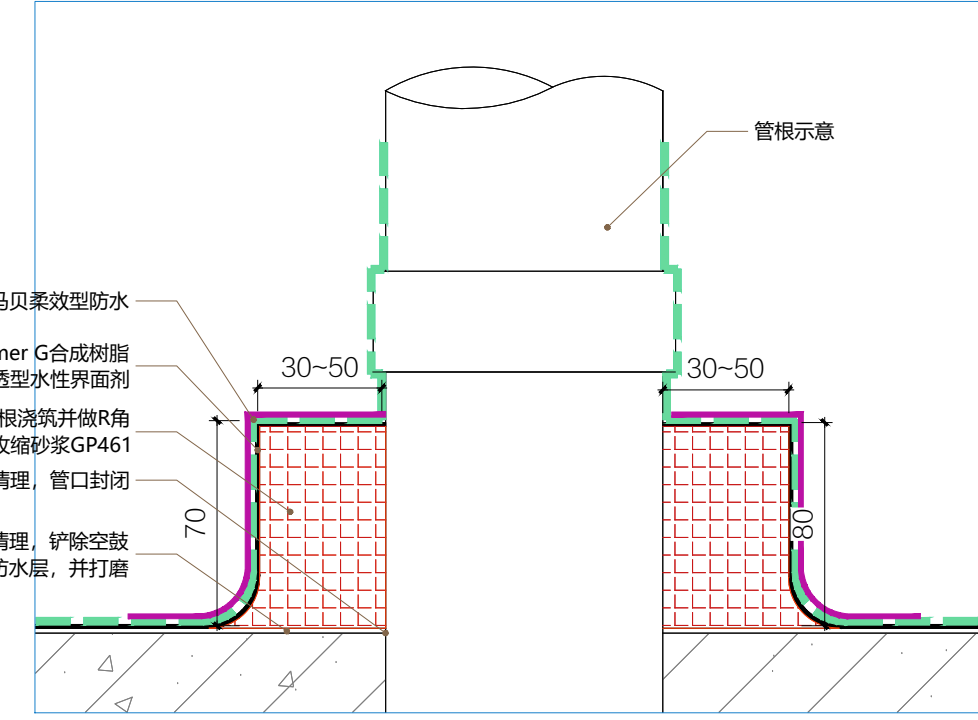

D 管根防水平面图
Scale比例 1:3 @A2

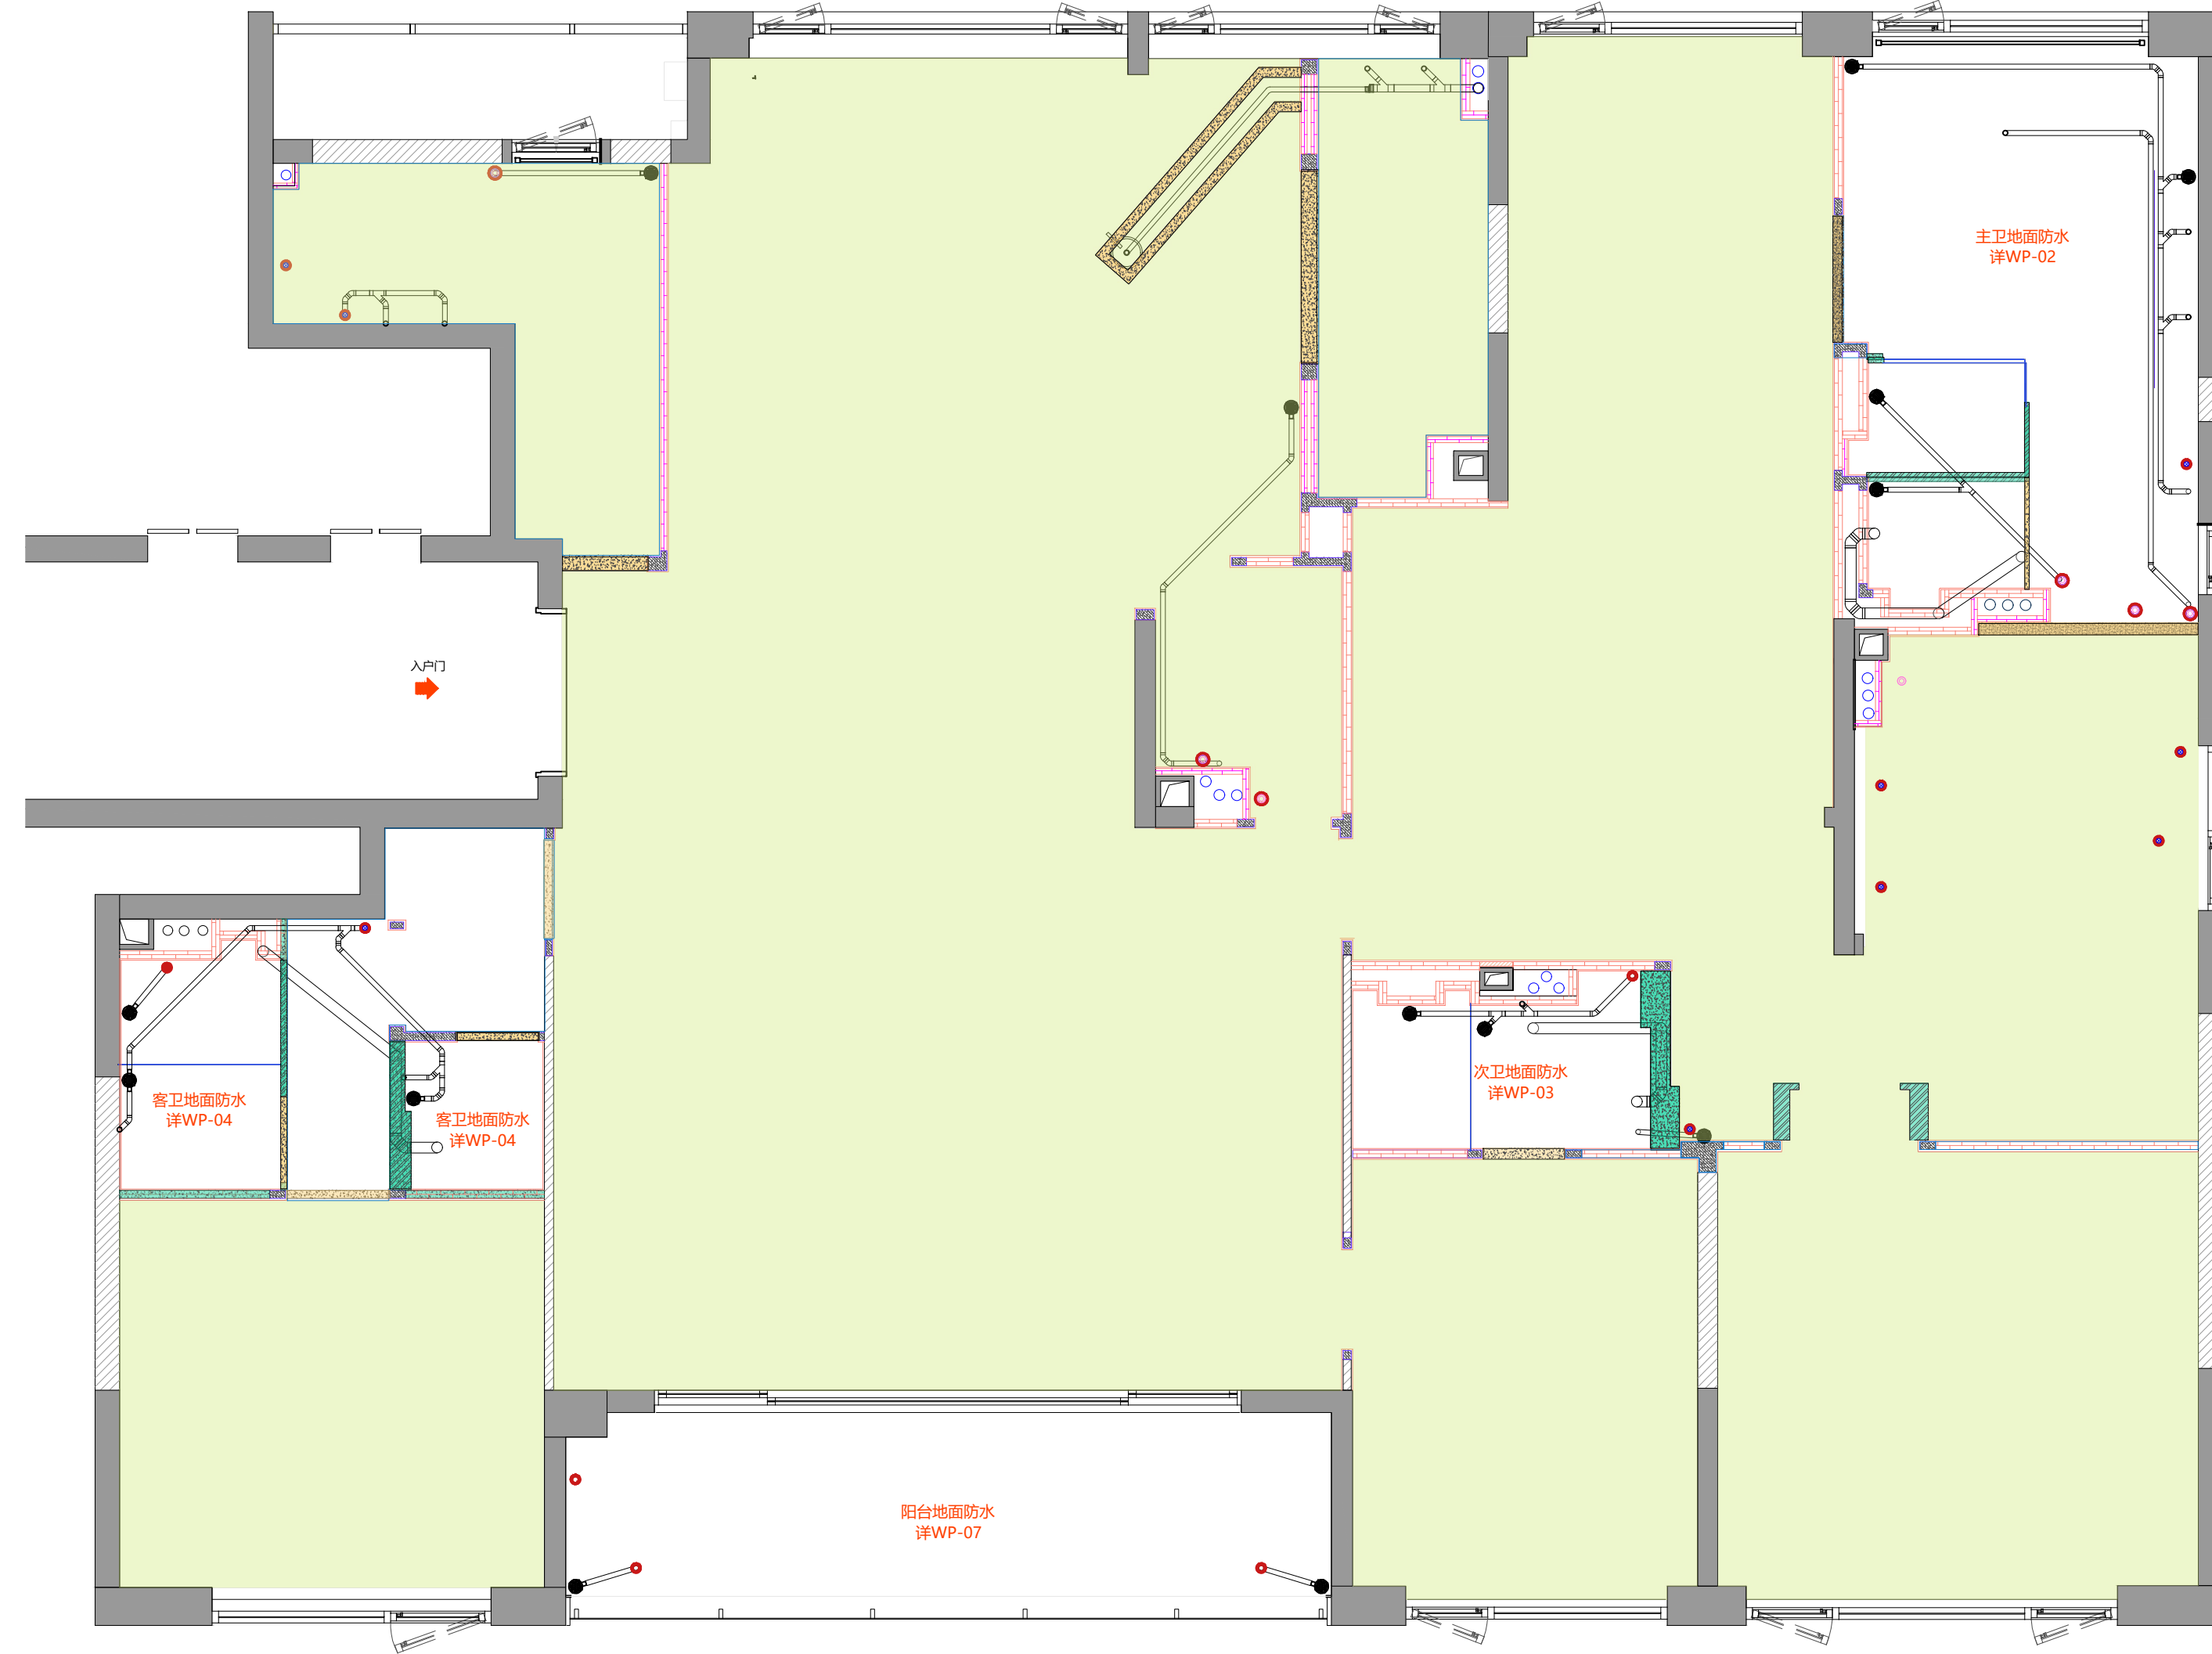

墙根/管根/堵管平面图
Scale比例 1:60 @A2

地面防水平面图
Scale比例 1:60 @A2

1

2

3

WUJIA

LEGEND 图例

	混凝土止水坎		地面: 防水 2遍/次墙面上翻200mm 产品: 马贝麦效型防水
	3mm厚不锈钢止水坎		
	墙根防水		
	管根防水		

注意事项:

- 地面防水层涂刷前, 地面基层需做修补、找平及清理。
 - 防水层厚度需有1.2mm。
- 更多资讯参考悦享《大平层全屋地面防水制程分析》

盖章:

正式施工图
2026-04-23

日期
Date 2026.04.09

修订
Revisions

注释
Notes

项目
Project

比例
As Shown @A2

Scale

Drawing No.

项目编号



Project No.

项目编号


比例

As Shown @A2


© 2025

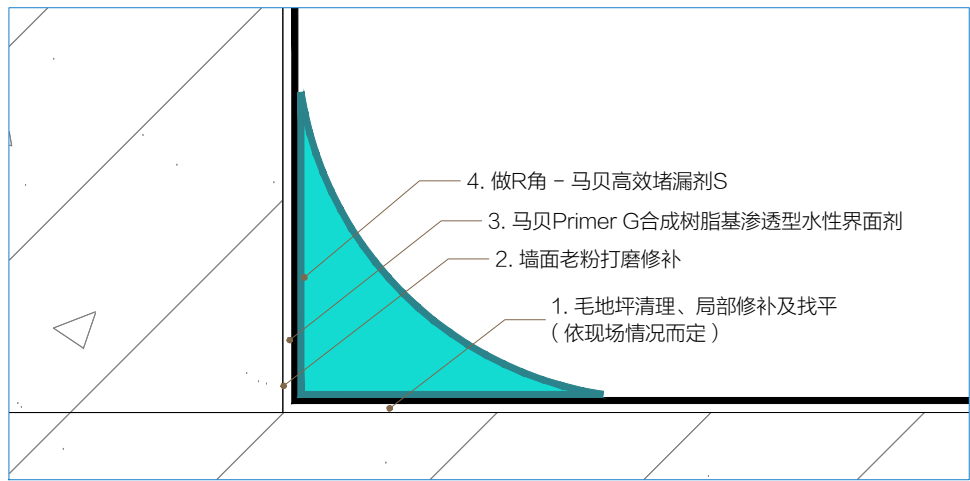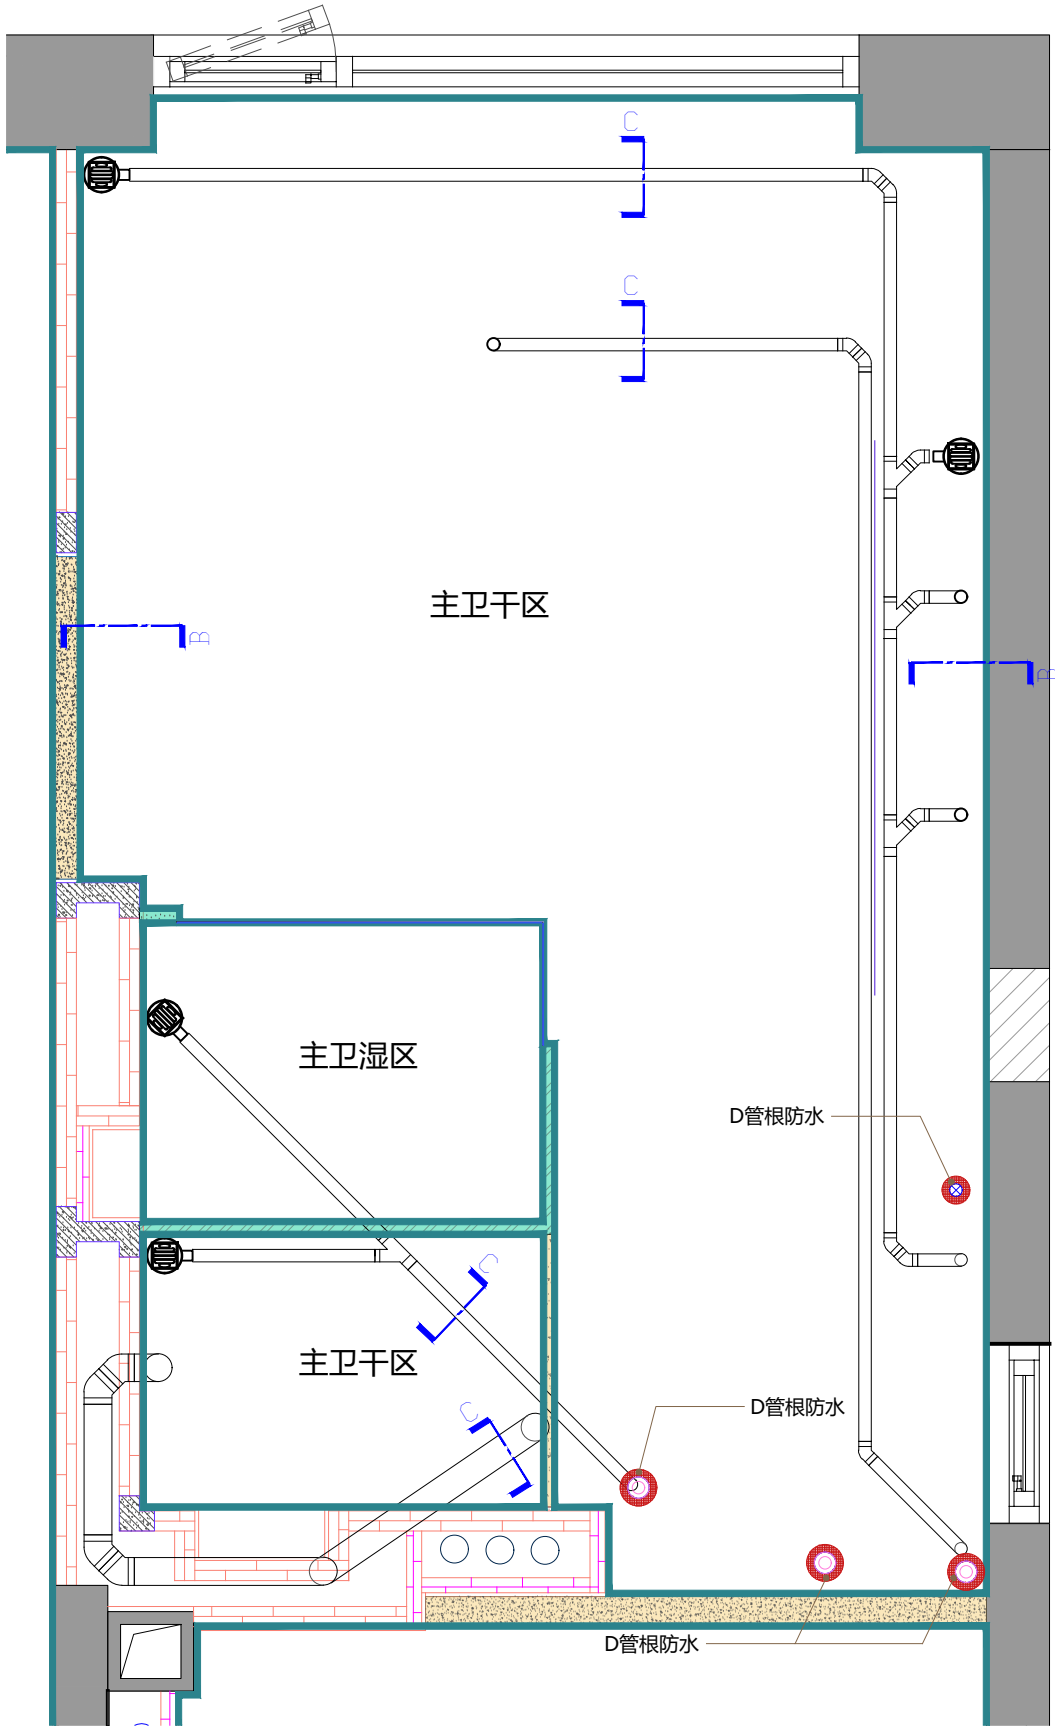



B 墙根防水节点图
Scale比例 1:2 @A2

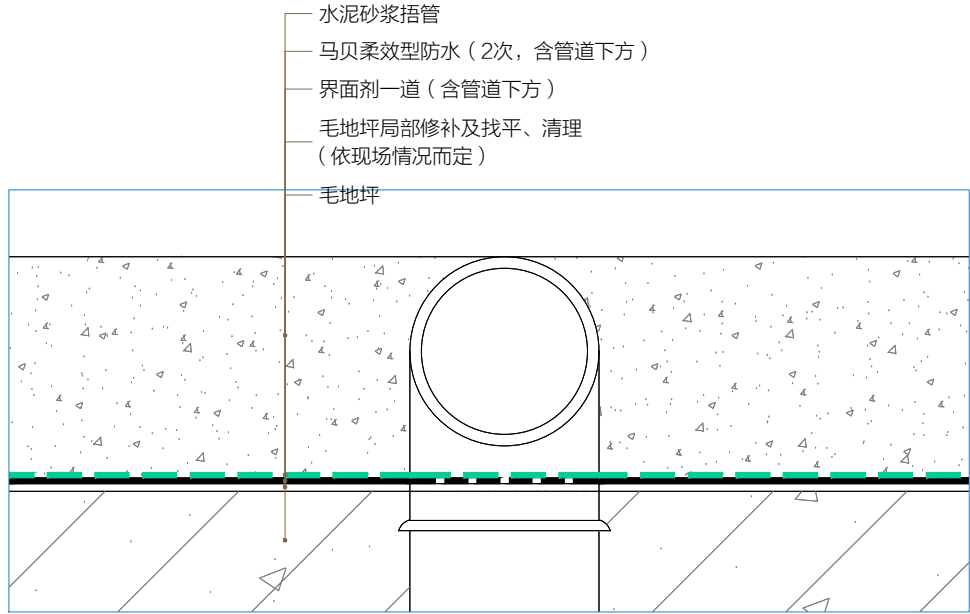

C 地面管道 捂管防水节点图
Scale比例 1:2 @A2

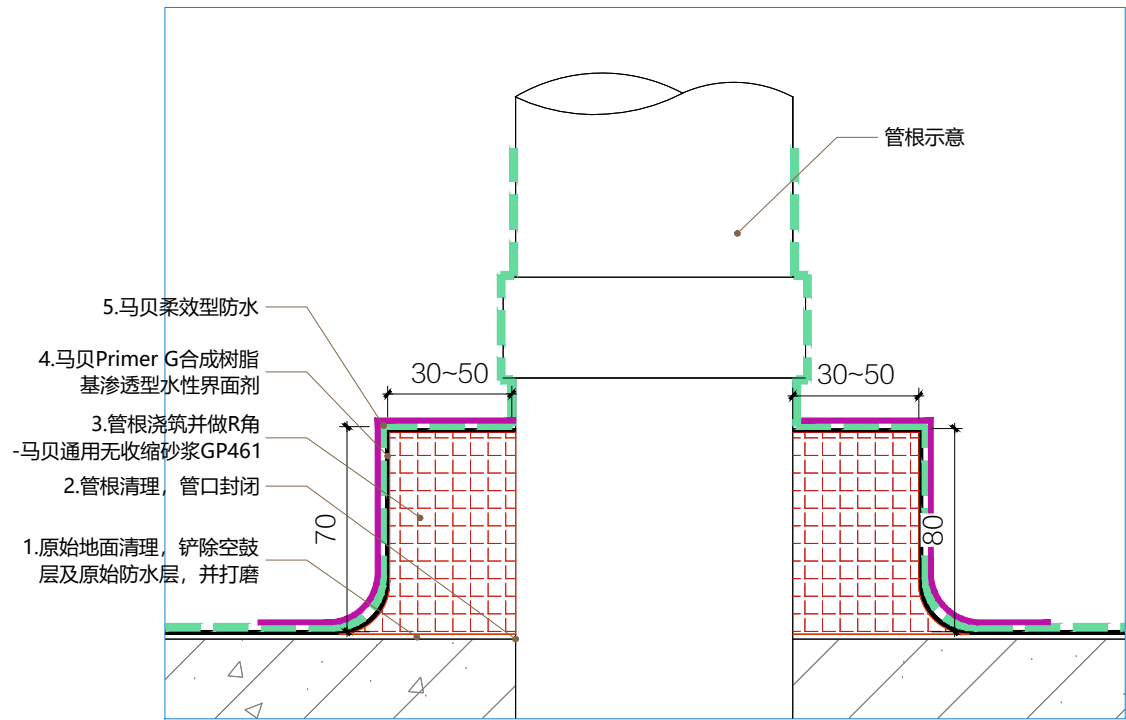

D 管根防水平面图
Scale比例 1:3 @A2

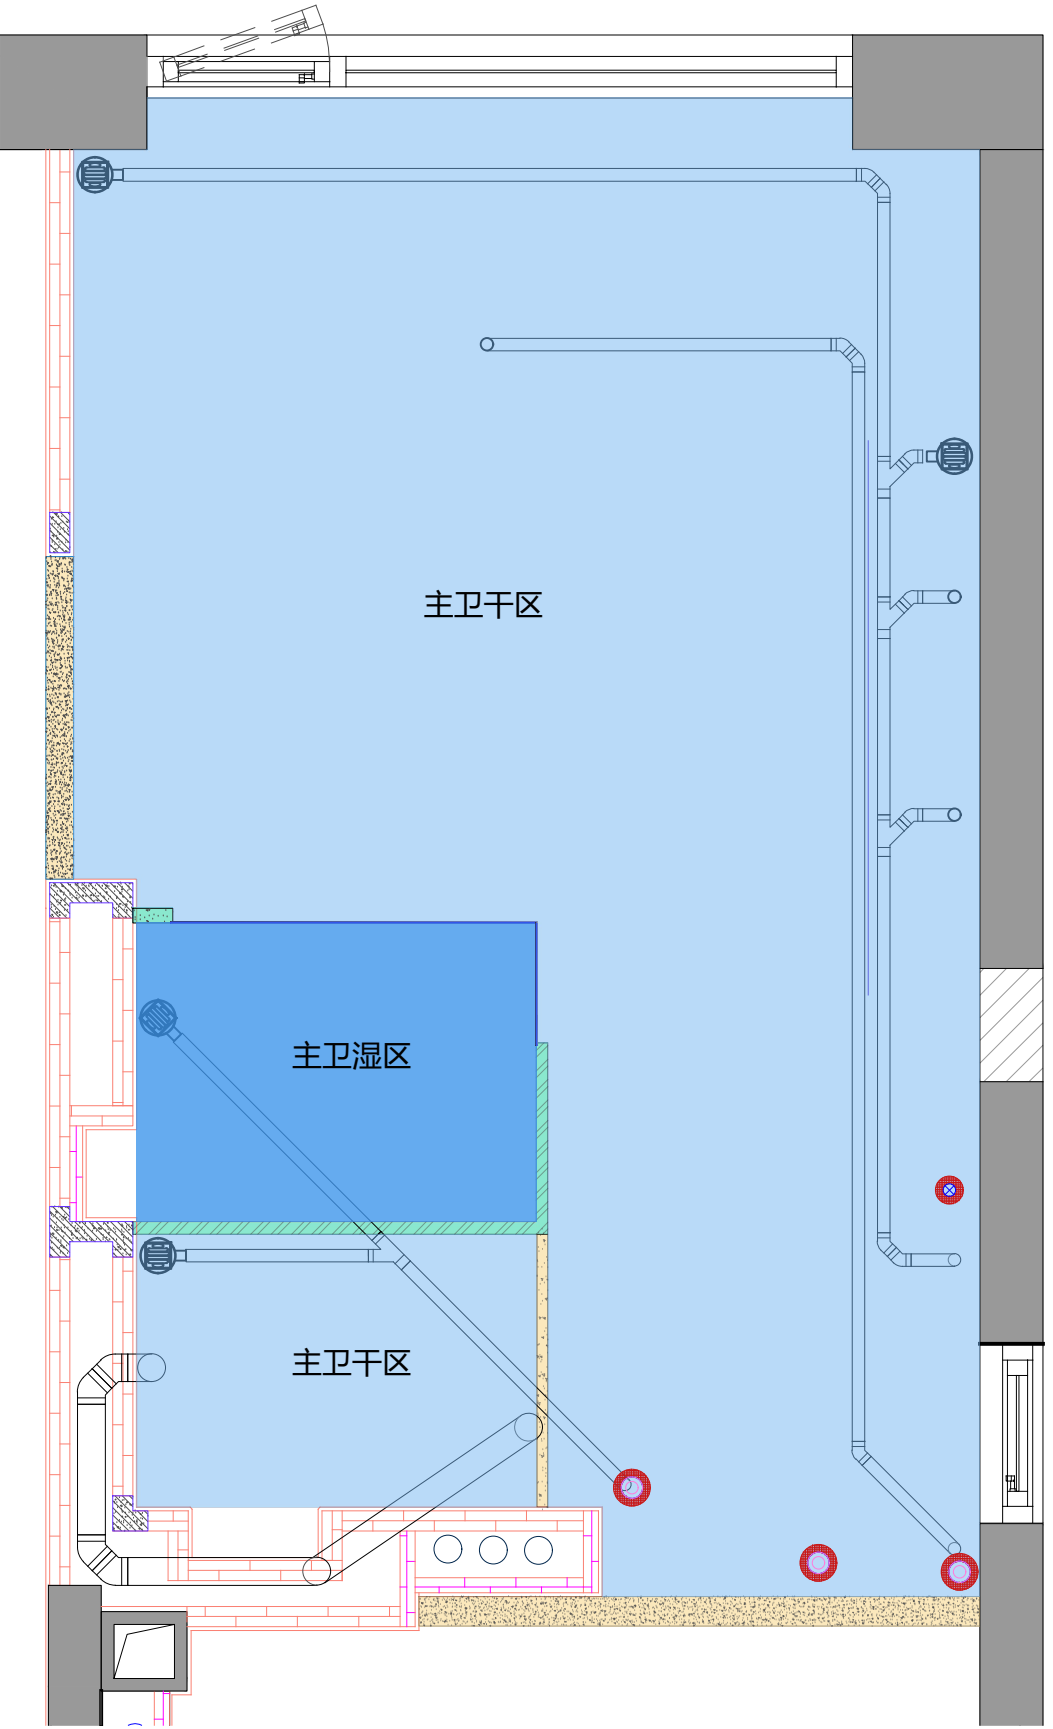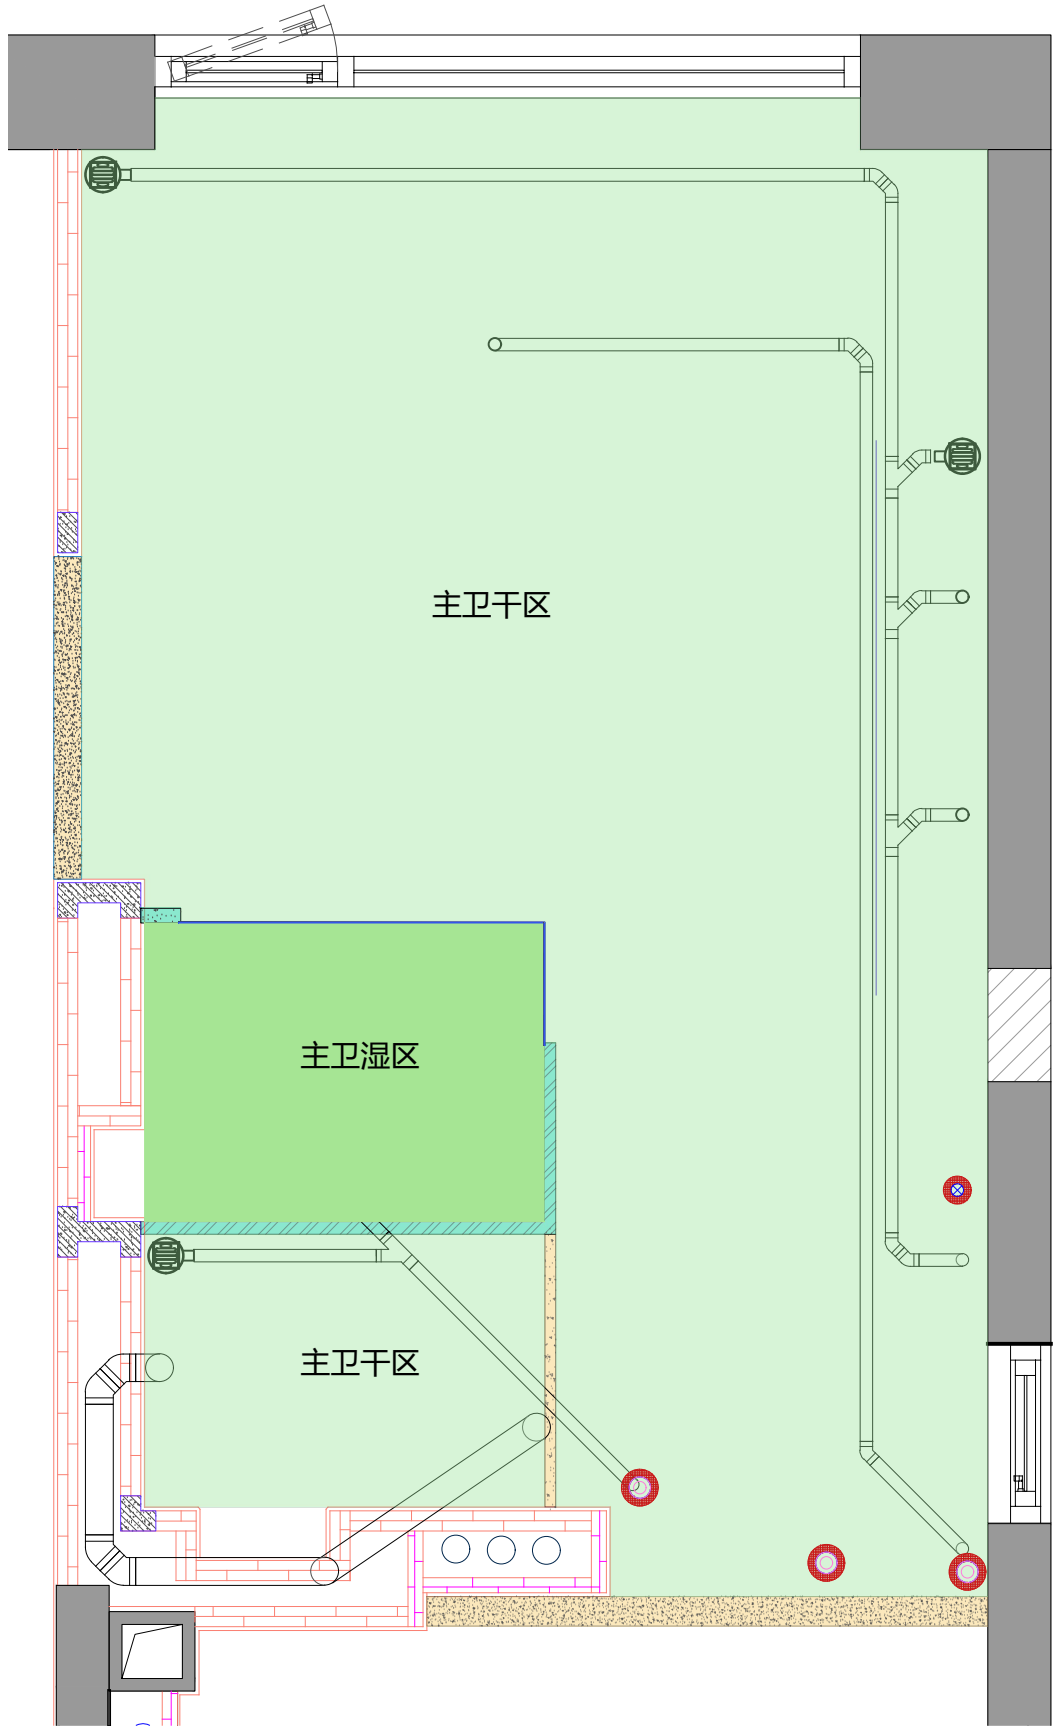

1

主卫--墙根/管根防水平面图

Scale比例 1:30 @A2

2

主卫--第一次地面防水平面图

Scale比例 1:30 @A2

3

主卫--第二次地面防水平面图

Scale比例 1:30 @A2

FORN

LEGEND 图例

	混凝土止水坎		卫生间干区地面： 第一次防水 (2遍/次,墙面上翻300mm) 产品：马贝柔效型防水
	3mm厚不锈钢止水坎		卫生间湿区地面： 第一次防水 (2遍/次,墙面上翻300mm) 产品：马贝柔效型防水
	墙根防水		卫生间干区地面 (地面找平后)： 第二次防水 (2遍/次,墙面上翻300mm) 产品：马贝柔效型防水 卫生间干区墙面 (地面找平后)： 高度2000mm 产品：马贝高级通用型防水
	管根防水		卫生间湿区地面 (地面找平后)： 第二次防水 (2遍/次,墙面上翻300mm) 产品：马贝柔效型防水 卫生间湿区墙面 (地面找平后)： 高度至原始顶面 产品：马贝高级通用型防水

注意事项：
1. 地面防水层涂刷前，地面基层需做修补、找平及清理。
2. 湿区地面加强防水及蓄水试验。
蓄水试验**须大于48小时**，淋浴房蓄水试验先做。
3. 防水层厚度需有1.2mm。
更多资讯参考悦孚《卫生间地面防水制程分析》

盖章：

正式施工图
2026-04-23

日期
Date 2026.04.09

修订
Revisions

1

注释
Notes

1. 本图纸尺寸如与现场尺寸有误，请施工人员与项目负责人联系。
2. 施工前施工人员应认真查阅此图，如有不明确尺寸，按现场测量为准。
3. 本图纸必须经甲乙双方认可并签字方可作为施工依据。

项目
Project

Scale
比例

As Shown @A2





Drawing No.
图纸编号

WP-02

Project No.
项目编号

© 2025

主卫地面防水图

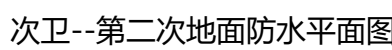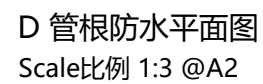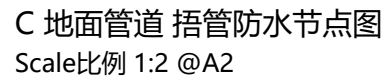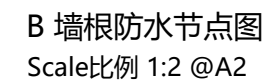Project No. © 2025

1

客卫--墙根/管根防水平面图
Scale比例 1:20 @A2

客卫干区

客卫湿区

D管根防水

客卫干区

客卫湿区

D管根防水

B 墙根防水节点图
Scale比例 1:2 @A2

1. 毛地坪清理、局部修补及找平
(依现场情况而定)

2. 墙面老粉打磨修补

3. 马贝Primer G合成树脂基渗透型水性界面剂

4. 做R角 - 马贝高效堵漏剂S

C 地面管道 挡管防水节点图
Scale比例 1:2 @A2

水泥砂浆挡管

马贝柔效型防水 (2次, 含管道下方)

界面剂一道 (含管道下方)

毛地坪局部修补及找平、清理
(依现场情况而定)

毛地坪

D 管根防水平面图
Scale比例 1:3 @A2

1.原始地面清理, 铲除空鼓
层及原始防水层, 并打磨

2.管根清理, 管口封闭

3.管根浇筑并做R角
-马贝通用无收缩砂浆GP461

4.马贝Primer G合成树脂
基渗透型水性界面剂

5.马贝柔效型防水

管根示意

2

客卫--第一次地面防水平面图
Scale比例 1:20 @A2

客卫干区

客卫湿区

3

客卫--第二次地面防水平面图
Scale比例 1:20 @A2

客卫干区

客卫湿区

LEGEND 图例

	混凝土止水坎		卫生间干区地面: 第一次防水 (2遍/次,墙面上翻300mm) 产品: 马贝柔效型防水
	3mm厚不锈钢止水坎		卫生间湿区地面: 第一次防水 (2遍/次,墙面上翻300mm) 产品: 马贝柔效型防水
	墙根防水		卫生间干区地面 (地面找平后): 第二次防水 (2遍/次,墙面上翻300mm) 产品: 马贝柔效型防水 卫生间干区墙面 (地面找平后): 高度2000mm 产品: 马贝高级通用型防水
	管根防水		卫生间湿区地面 (地面找平后): 第二次防水 (2遍/次,墙面上翻300mm) 产品: 马贝柔效型防水 卫生间湿区墙面 (地面找平后): 高度至原始顶面 产品: 马贝高级通用型防水

注意事项:

1. 地面防水层涂刷前, 地面基层需做修补、找平及清理。

2. 湿区地面加强防水及蓄水试验。
蓄水试验须大于48小时, 淋浴房蓄水试验先做。

3. 防水层厚度需有1.2mm。

更多资讯参考悦孚《卫生间地面防水制程分析》

盖章:

正式施工图
2026-04-23

日期
Date

2026.04.09

修订
Revisions

1

注释
Notes

1. 本图纸尺寸如与现场尺寸有误差,
请施工人员与项目负责人联系。

2. 施工前施工人员应认真查阅此
图, 如有不明确尺寸, 按现场测量
为准。

3. 本图纸必须经甲乙双方认可并
签字方可作为施工依据。

项目
Project

Scale
比例

As Shown @A2



公卫地面防水图

Drawing No.
图纸编号


WP-04

Project No.
项目编号


© 2025

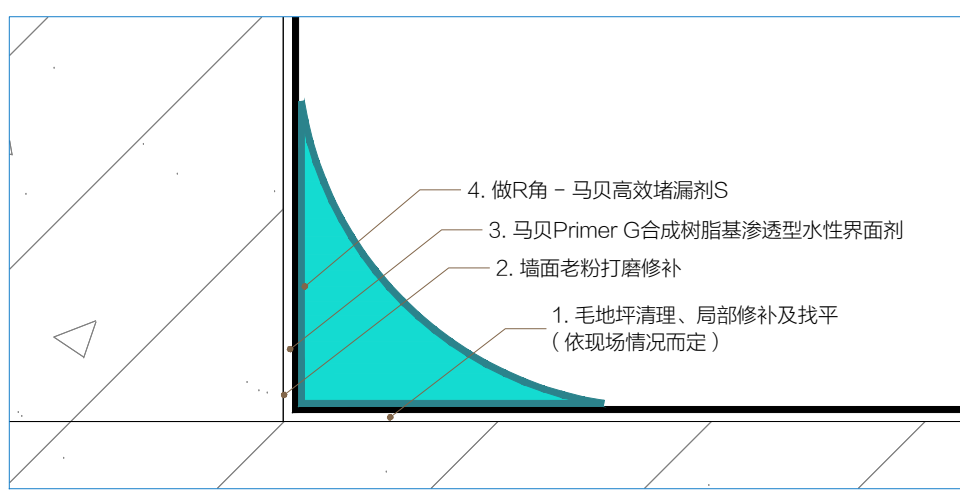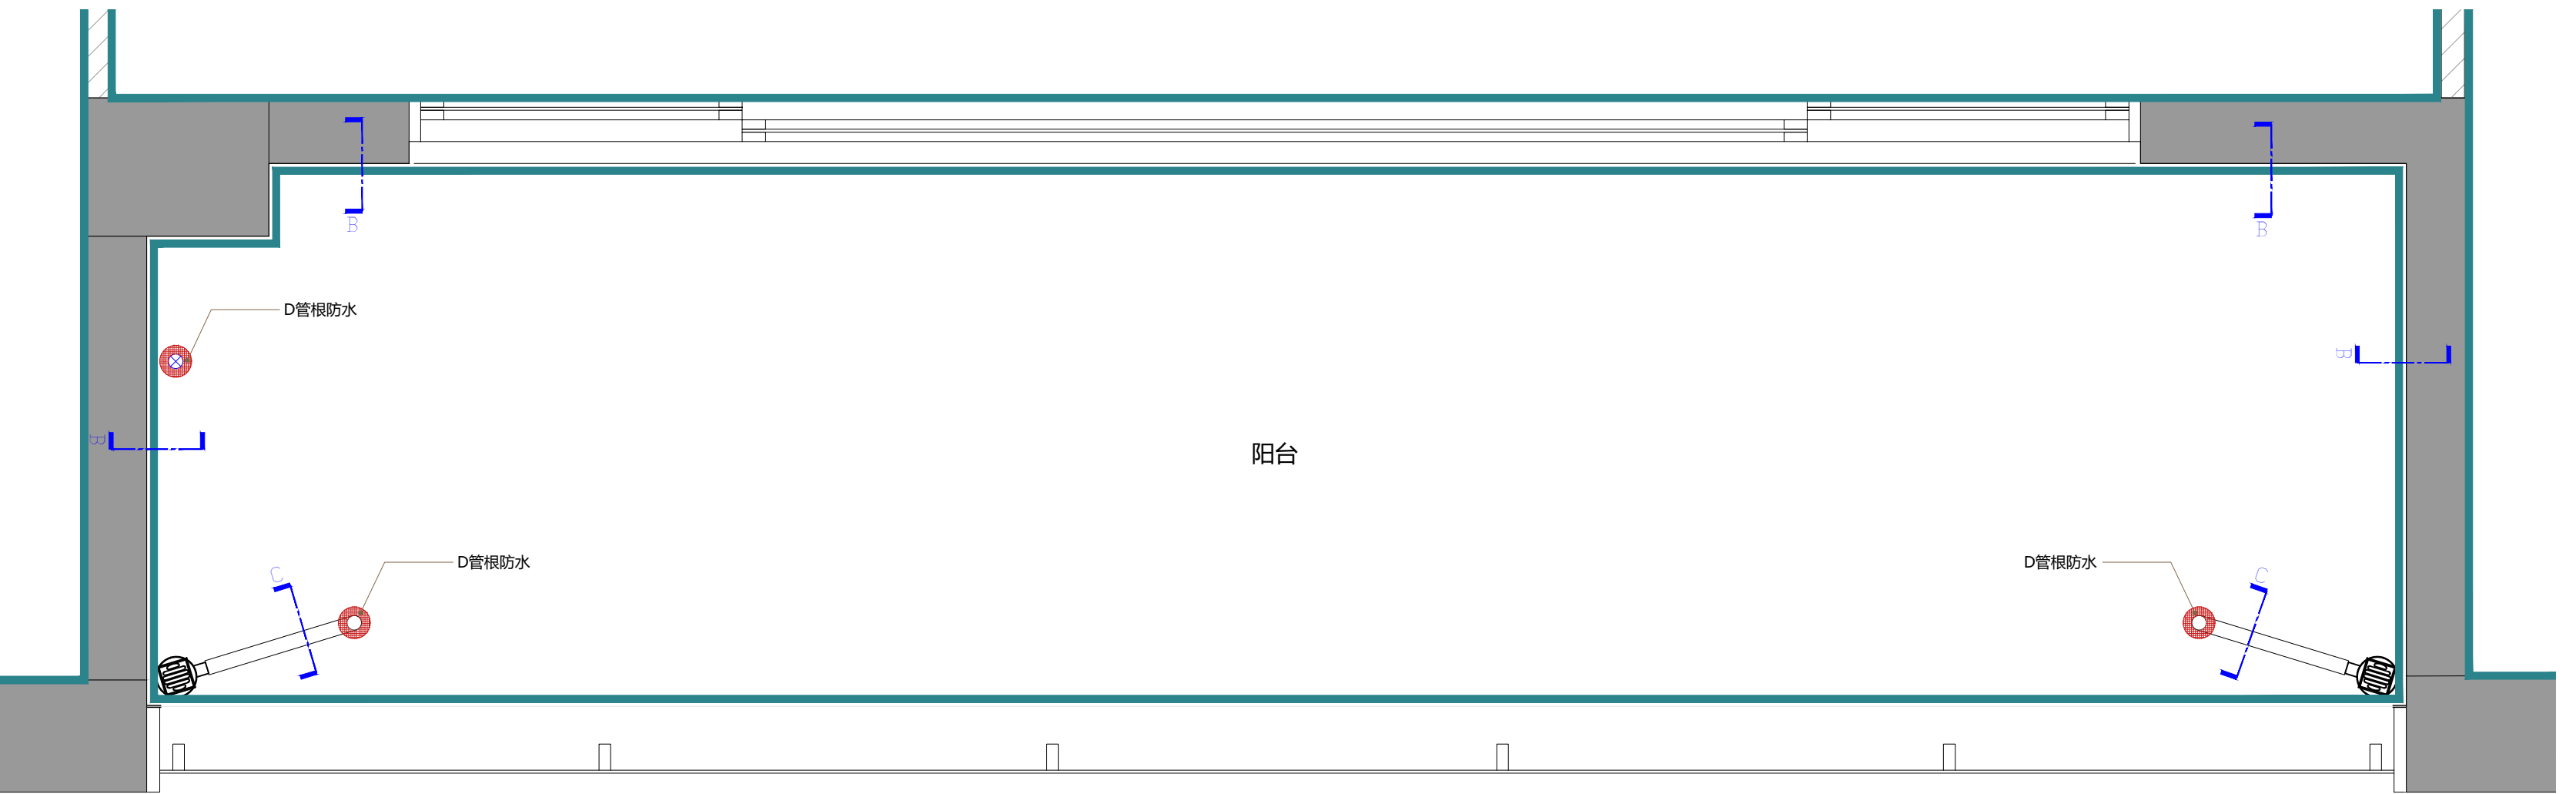

B 墙根防水节点图
Scale比例 1:2 @A2

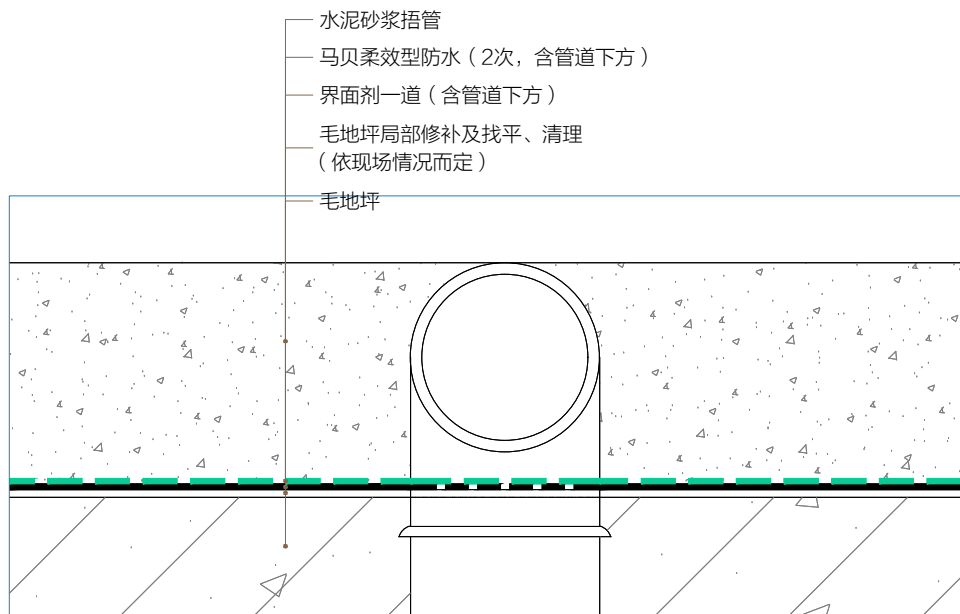

C 地面管道 插管防水节点图
Scale比例 1:2 @A2

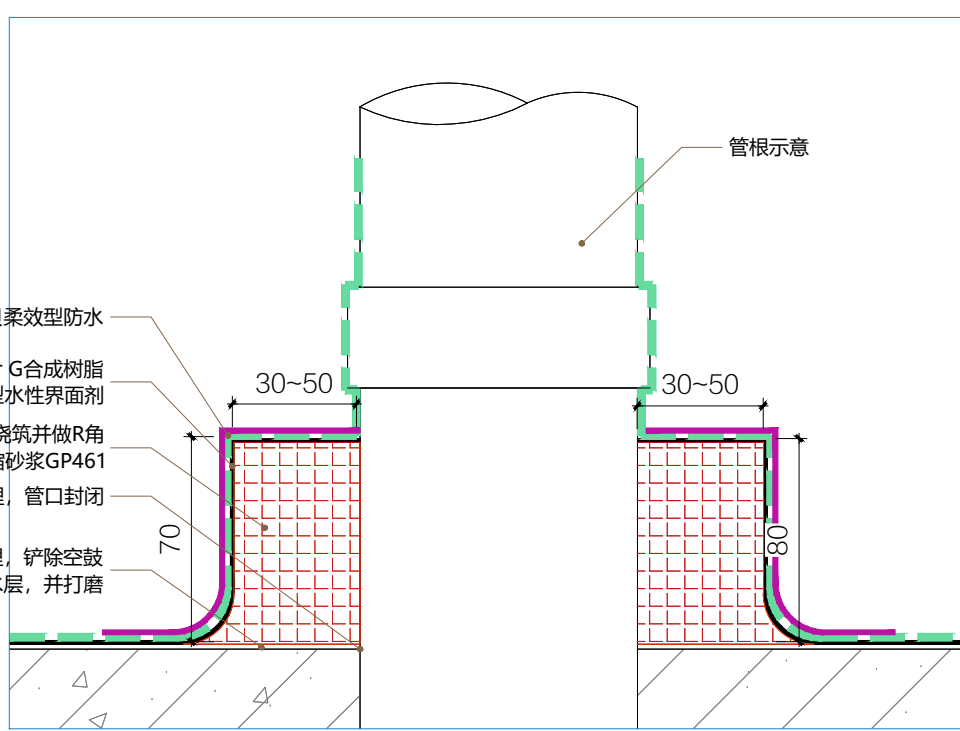

D 管根防水平面图
Scale比例 1:3 @A2


阳台--墙根/管根防水平面图

Scale比例 1:20 @A2




阳台--第一次地面防水平面图

Scale比例 1:20 @A2

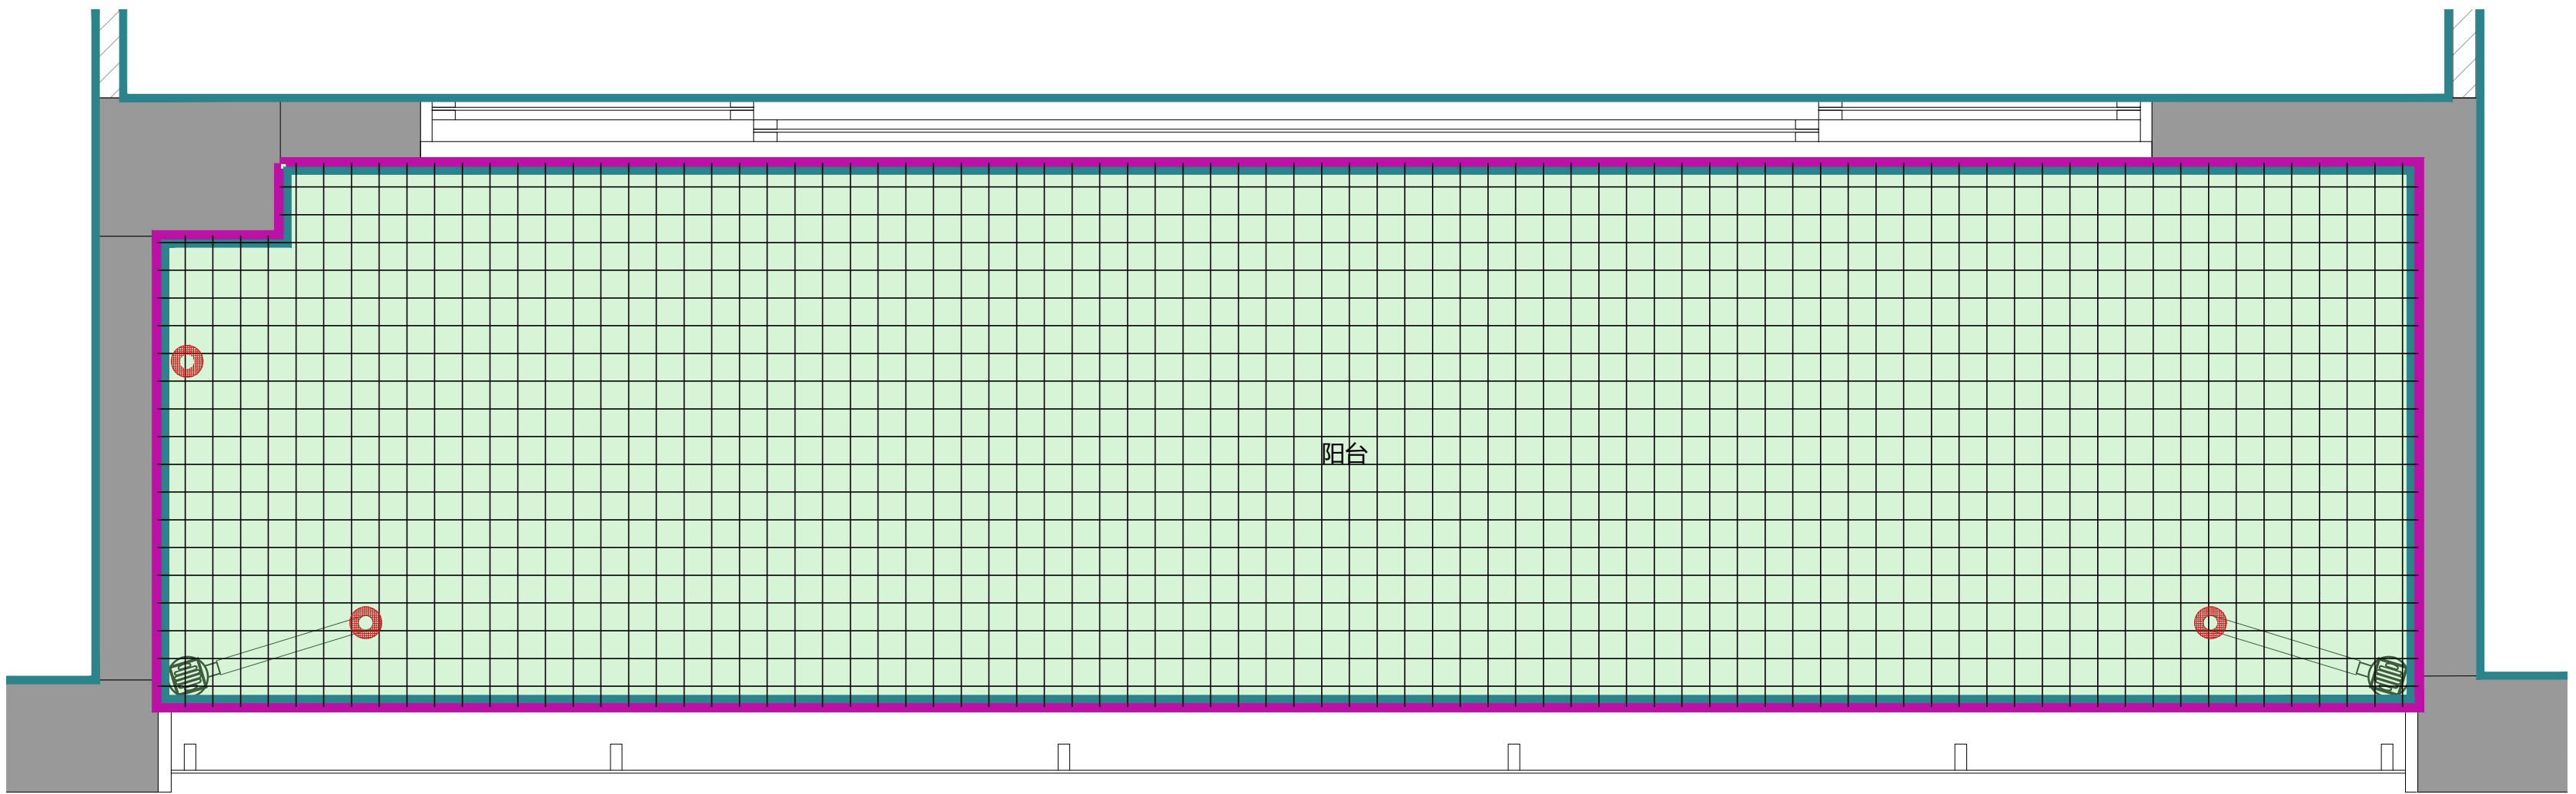

阳台--阴角贴玻纤网+第2次墙根/管根+铺高抗裂玻纤网平面图

Scale比例 1:20 @A2

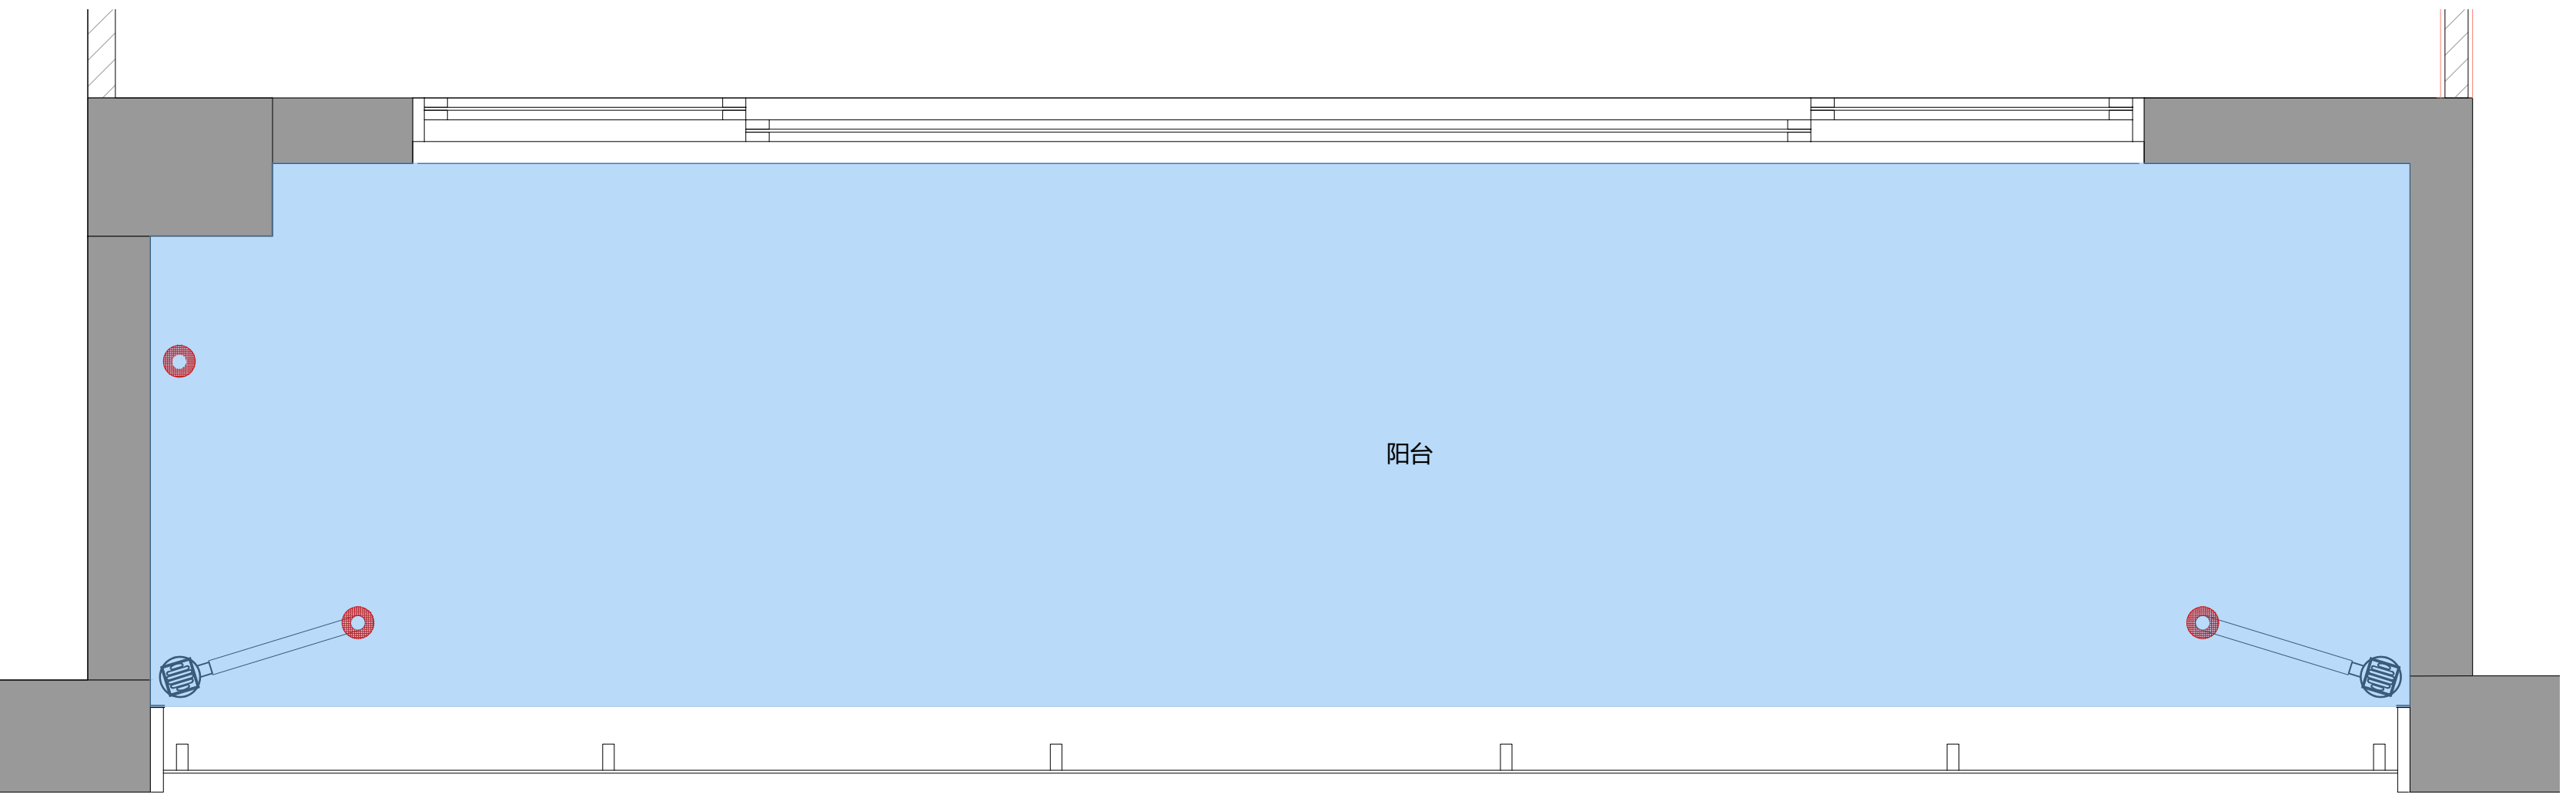

阳台--地面第二次防水平面图

Scale比例 1:20 @A2

1

PHON

LEGEND 图例

	混凝土止水坎		卫生间干区地面：第一次防水 (2遍/次,墙面上翻300mm) 产品：马贝柔效型防水
	3mm厚不锈钢止水坎		卫生间湿区地面：第一次防水 (2遍/次,墙面上翻300mm) 产品：马贝柔效型防水
	墙根防水		卫生间干区地面 (地面找平后)：第二次防水 (2遍/次,墙面上翻300mm) 产品：马贝柔效型防水 卫生间干区墙面 (地面找平后)：高度2000mm 产品：马贝高效通用型防水
	管根防水		卫生间湿区地面 (地面找平后)：第二次防水 (2遍/次,墙面上翻300mm) 产品：马贝柔效型防水 卫生间湿区墙面 (地面找平后)：高度至原始顶面 产品：马贝高效通用型防水

注意事项：
1. 地面防水层涂刷前，地面基层需做修补、找平及清理。
2. 湿区地面加强防水及蓄水试验。
蓄水试验须大于48小时，淋浴房蓄水试验先做。
3. 防水层厚度需有1.2mm。
更多信息参考悦享《卫生间地面防水制程分析》

盖章：

正式施工图
2026-04-23

日期 Date	2026.04.09
Revisions	
Revisions	
Revisions	
Revisions	

日期 Date	2026.04.09
Revisions	
Revisions	
Revisions	
Revisions	

日期 Date	2026.04.09
Revisions	
Revisions	
Revisions	
Revisions	

Project
Scale
比例
As Shown @A2
Drawing No.
WP-05
Project No.
© 2025