


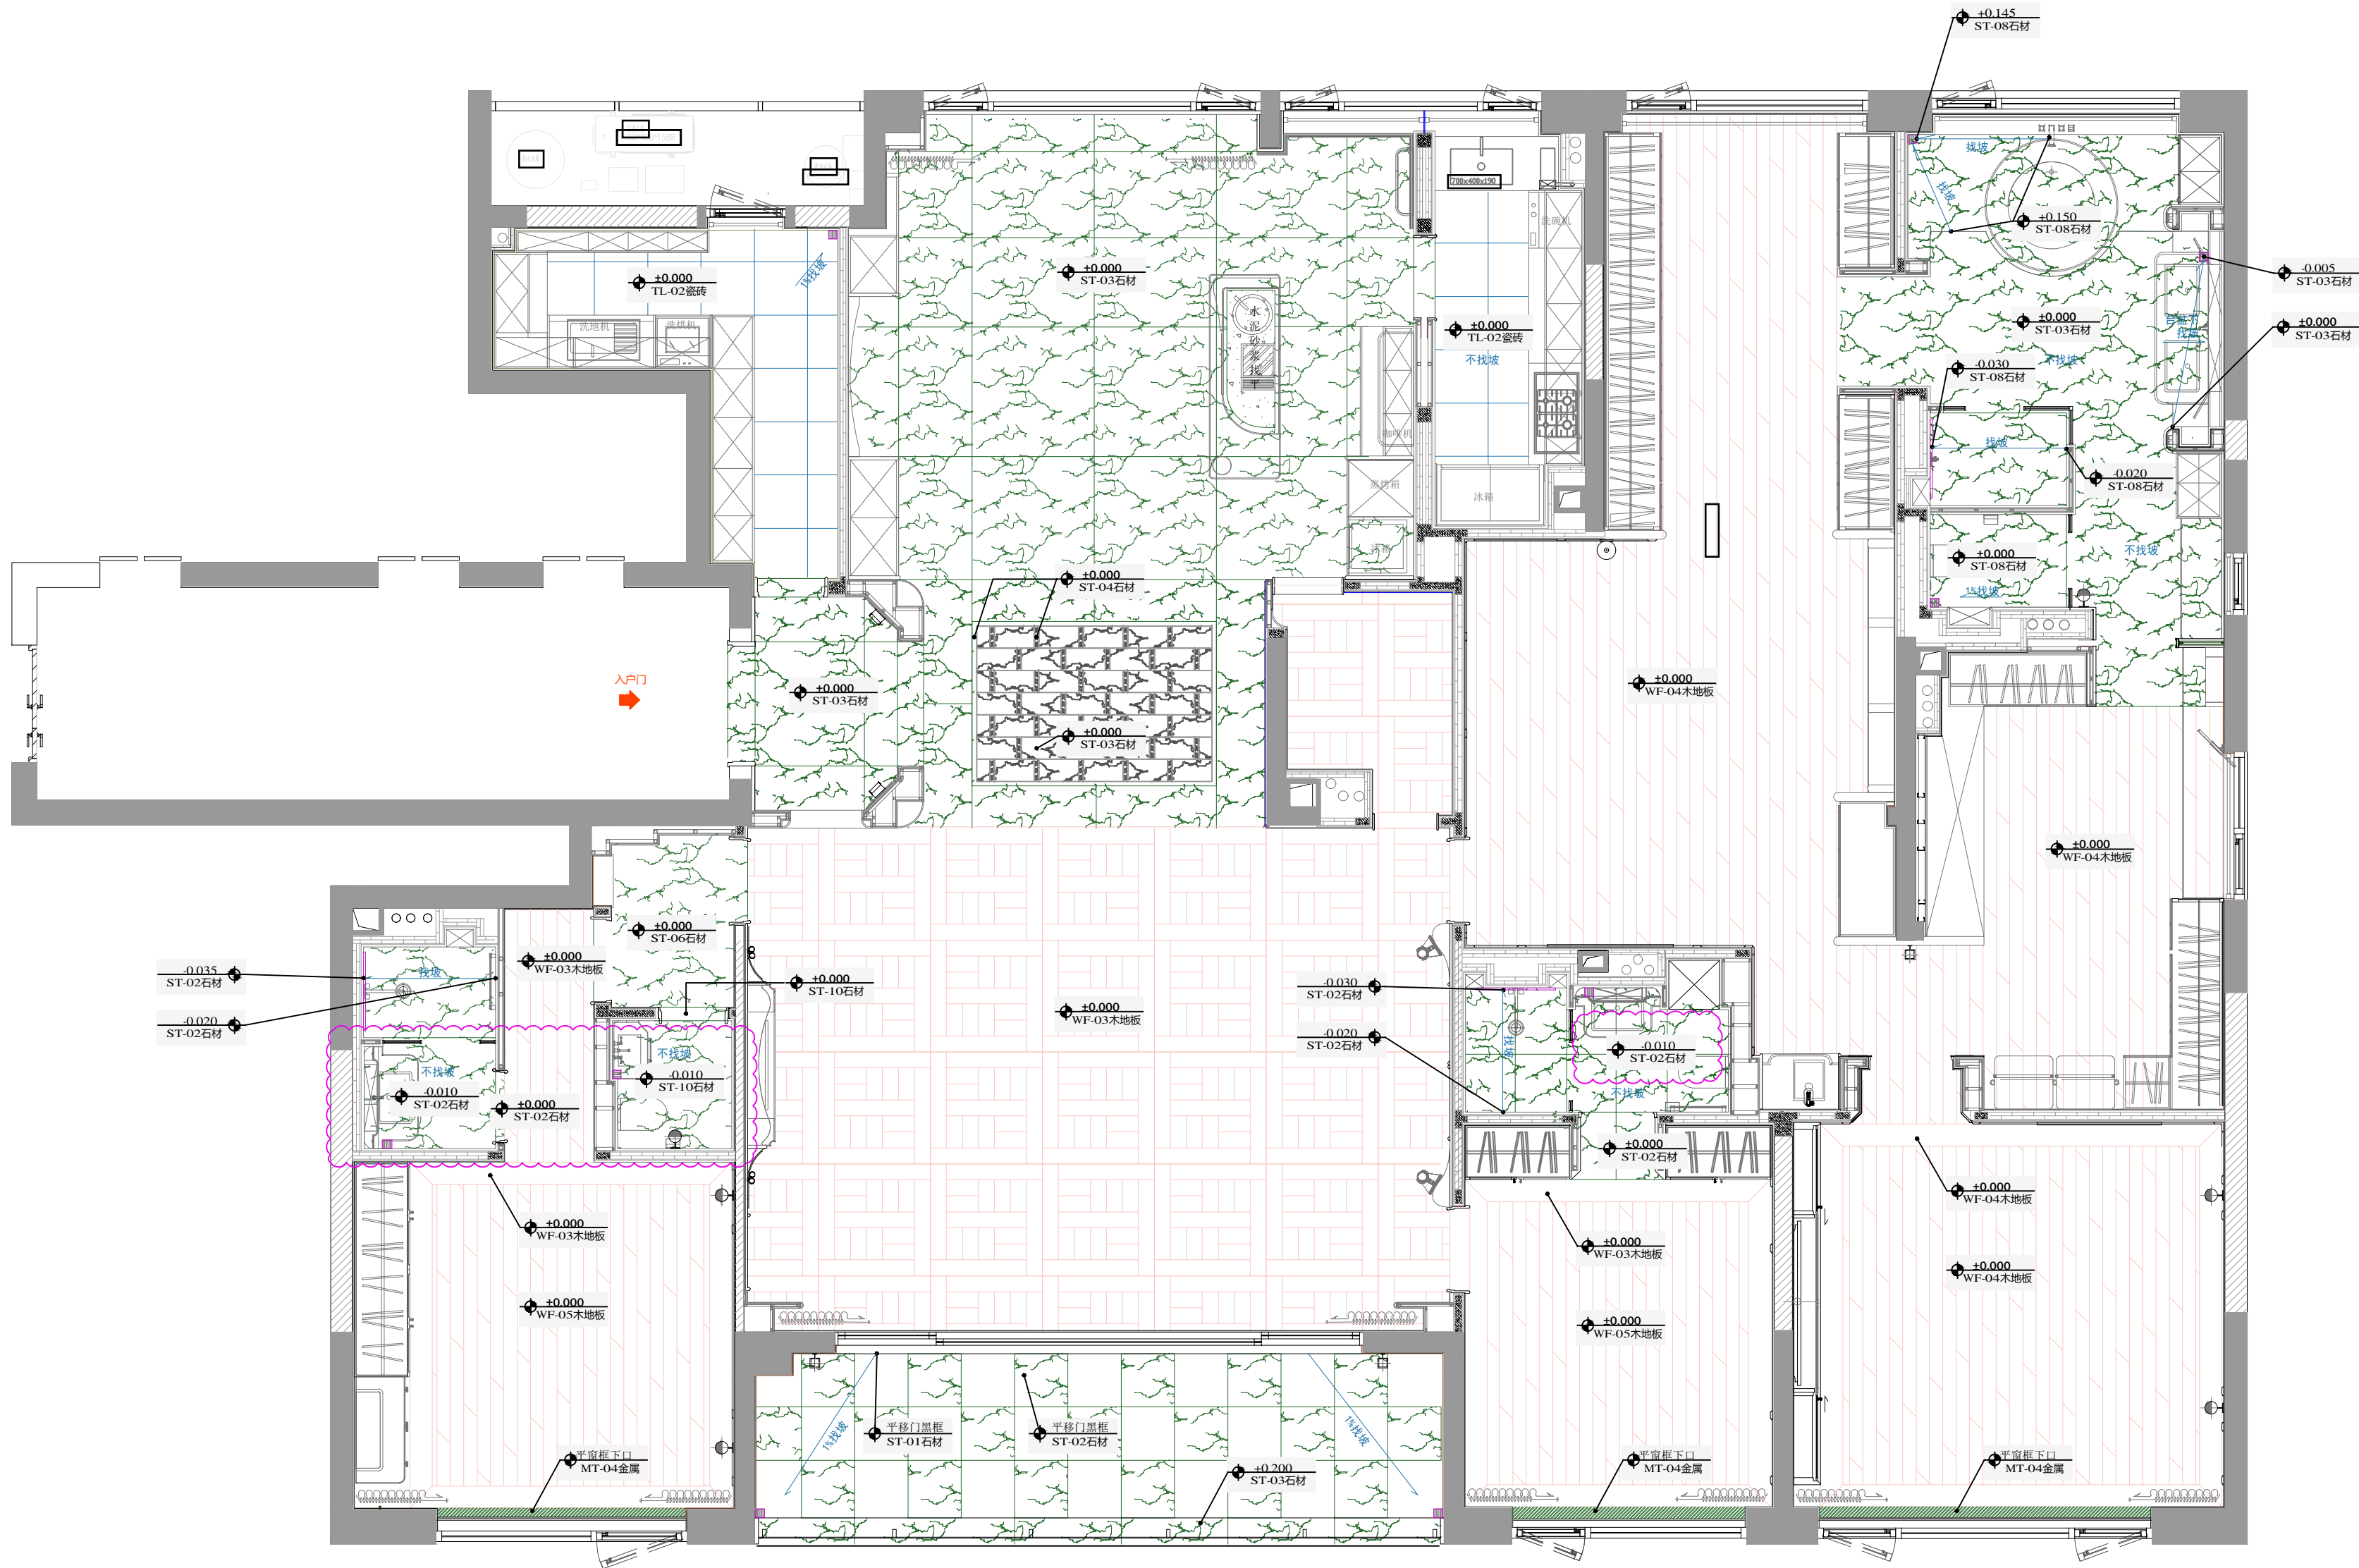

LEGEND A

图例示意	说明
	石材
	岩板/瓷砖
	木地板
	木地板

正式施工图
26-05-20

日期
Date 2026.4.3

修订
Revisions
 2026.4.30

项目
Project

杭州 华岸府

Scale
比例

Drawing No.
图纸编号

FL.PL-01

Project No.
项目编号

© 2025

2026.4.30变更：卫生间地坪标高调整。



最终面材铺贴样式以专业厂家图纸为准

地坪完成面材质及标高平面图



注释
Notes

- 本图纸尺寸如与现场尺寸有误差，请施工方与项目负责人联系。
- 施工前施工方应认真查阅此图，如有不明尺寸，按现场测量为准。
- 本图纸必须经甲乙双方认可并签字方可作为施工依据。



Scale比例 1:60@A2

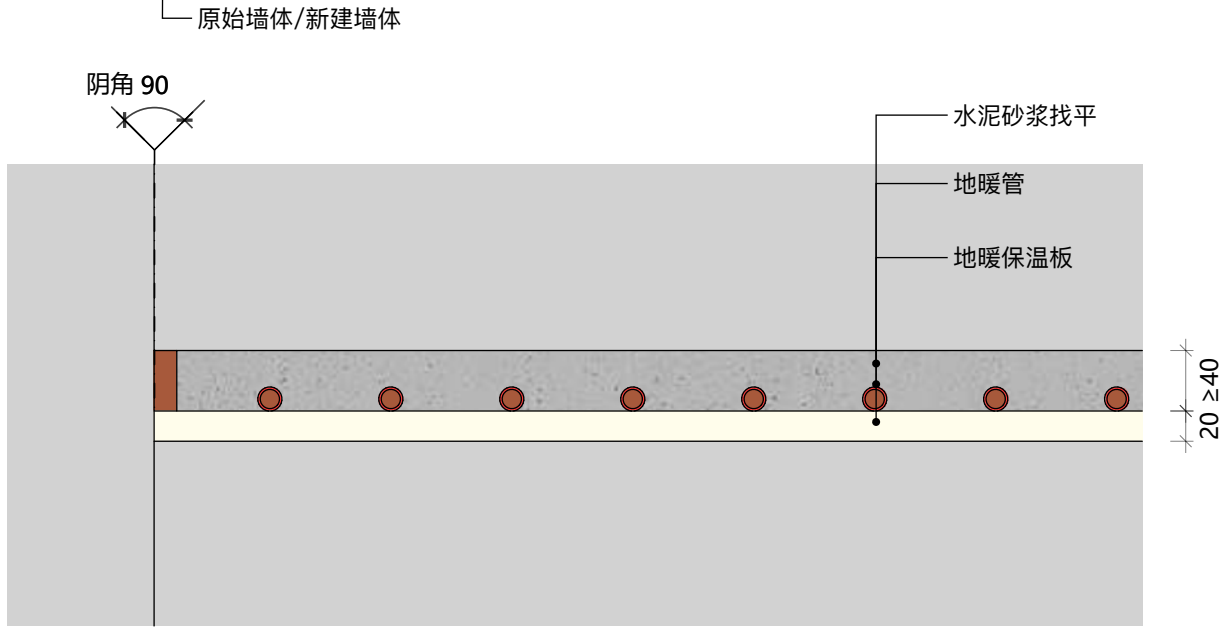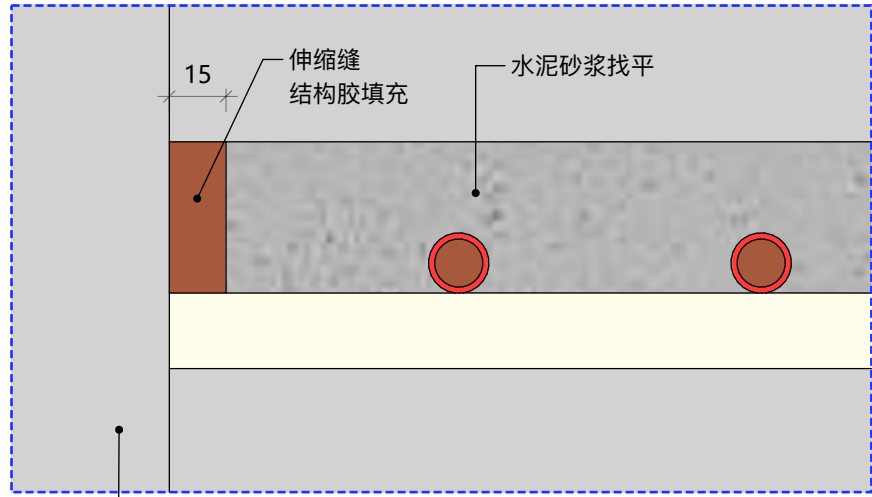


靠墙阴角处必须设置伸缩缝

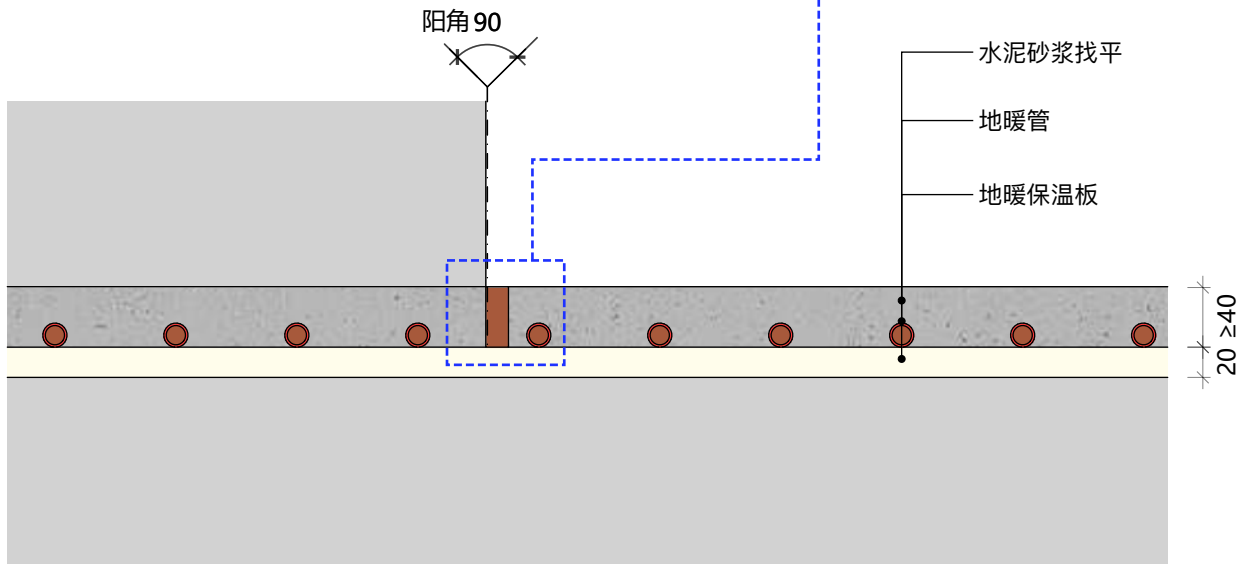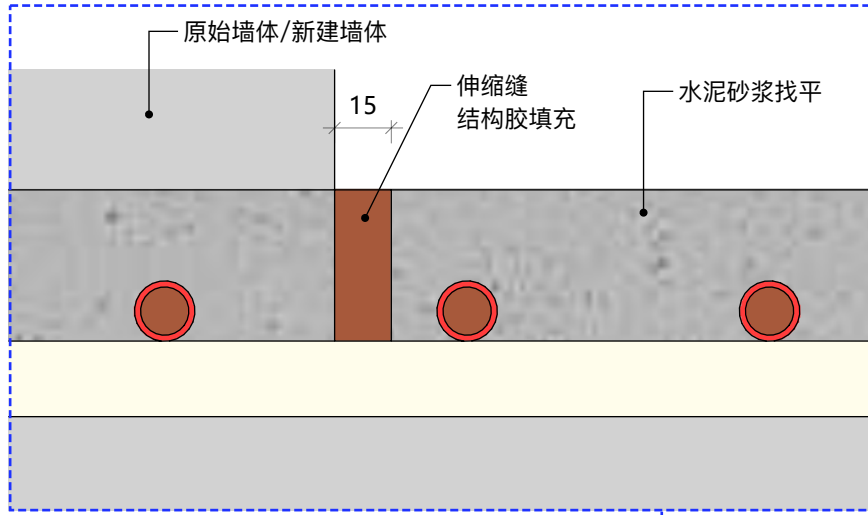


伸缩缝要以墙的阳角为基准，垂直及水平向延伸

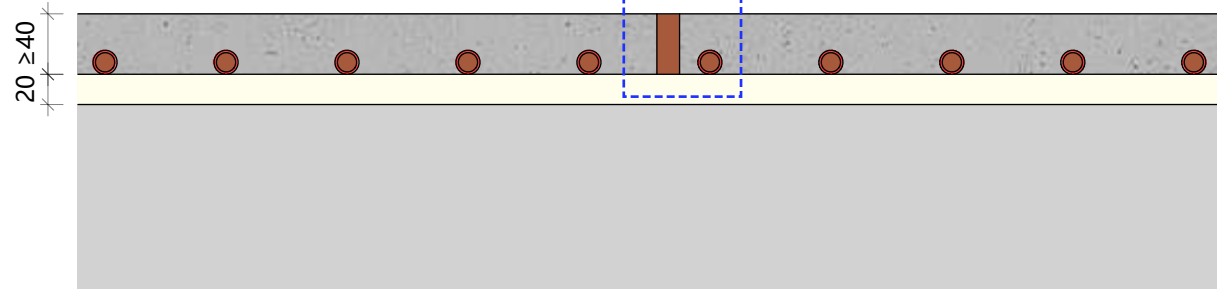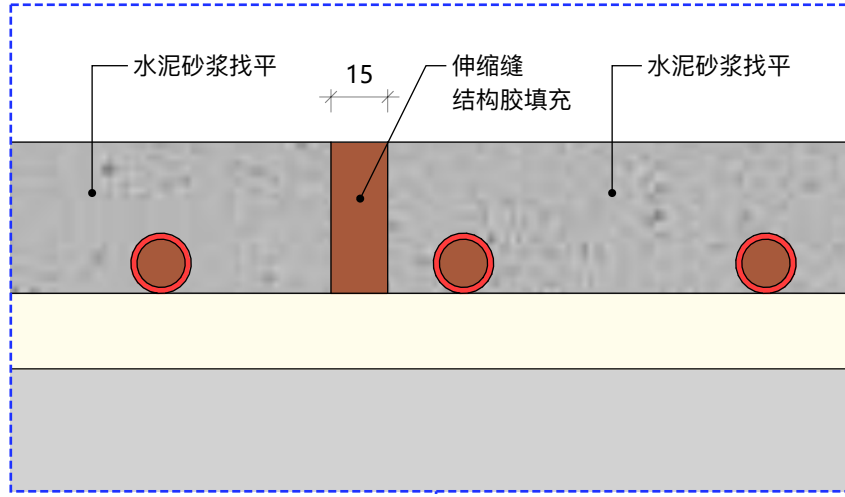


墙角为基准，中间部位等分不大于6米
如遇到地暖管道，请注意避让

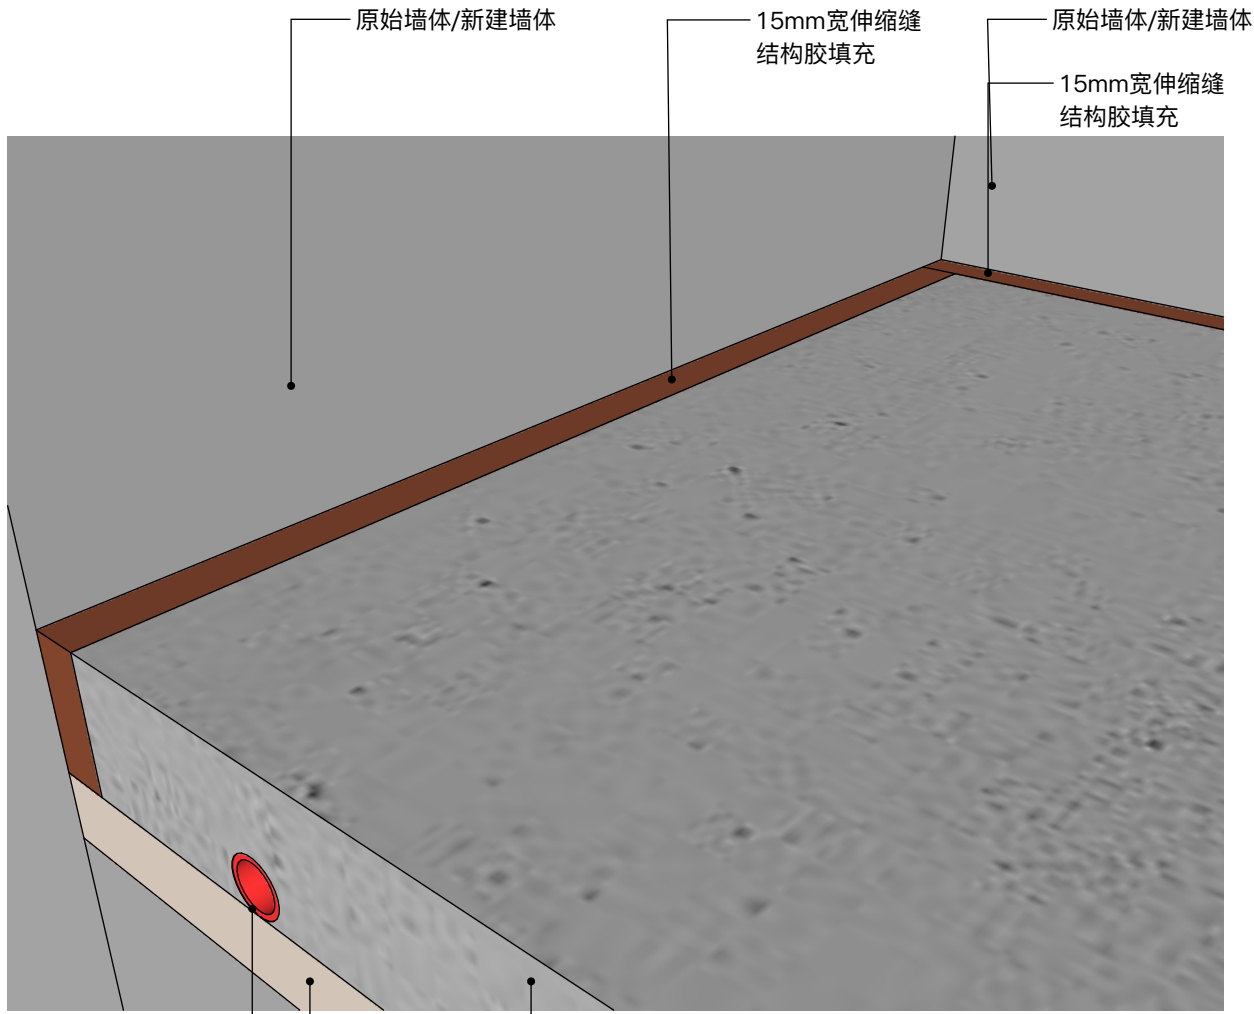

阴角伸缩缝剖面3D示意图

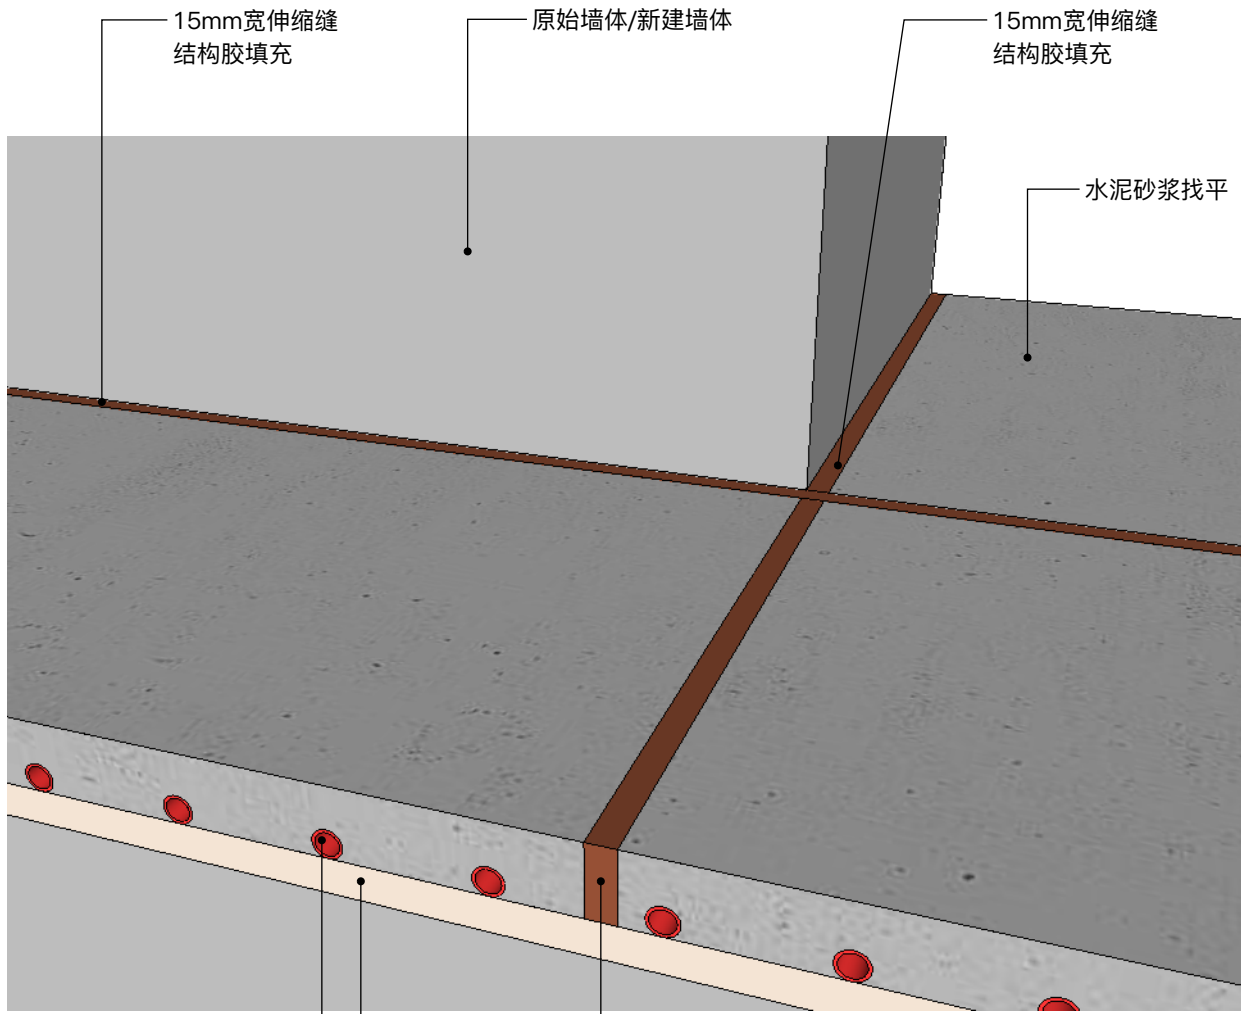

阳角伸缩缝剖面3D示意图

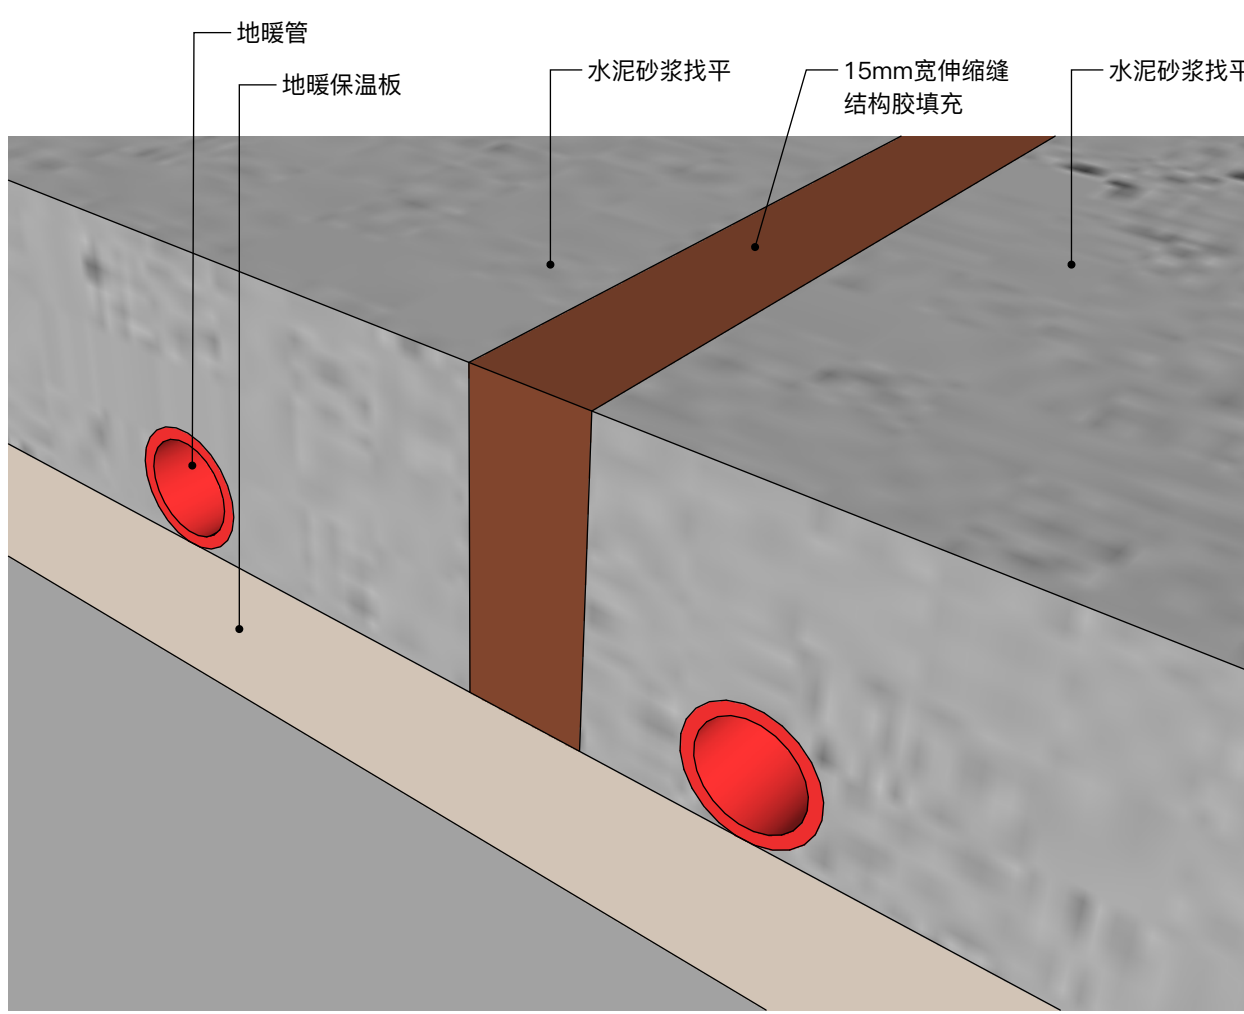

伸缩缝剖面3D示意图

三和

PM
PROJECT MANAGEMENT

机电
MEP ENGINEER

整饰
FIXTURE ENGINEER

照明
LIGHTING ENGINEER

五金
HARDWARE ENGINEER

石材
STONE ENGINEER

日期
Date 2024.11.21

修订
Revisions

注释

Notes

1. 本图纸尺寸如与现场尺寸有误差，请施工人员与项目负责人联系。
2. 施工前施工人员应认真查阅此图，如有不明确尺寸，按现场测量为准。
3. 本图纸必须经甲乙双方认可并签字方可作为施工依据。

正式施工图
26-05-20

比例
Scale as Shown @A2

水泥砂浆找平层-伸缩缝剖面图

图纸编号
Drawing No.

FL-02

项目编号
Project No. @2024

1

水泥砂浆找平层--阴角伸缩缝剖面图

2

水泥砂浆找平层--阳角伸缩缝剖面图

3

水泥砂浆找平层--伸缩缝剖面图

FL-02

Scale: 1:5 @A2

FL-02

Scale: 1:5 @A2

FL-02

Scale: 1:5 @A2

LEGEND A

图例示意	说明
	伸缩缝，宽度10mm，结构胶填充
	水泥砂浆找平

施工原则：

- 靠墙都要有伸缩缝。
- 伸缩缝要以墙的阳角为基准，垂直及水平向延伸。
- 墙角为基准，中间部分等分不大于6米。

正式施工图
26-05-20

日期
Date 2026.5.9

修订
Revisions



项目
Project

杭州 华岸府


Scale
比例

Drawing No.
图纸编号

FL.PL-05

Project No.
项目编号

© 2025

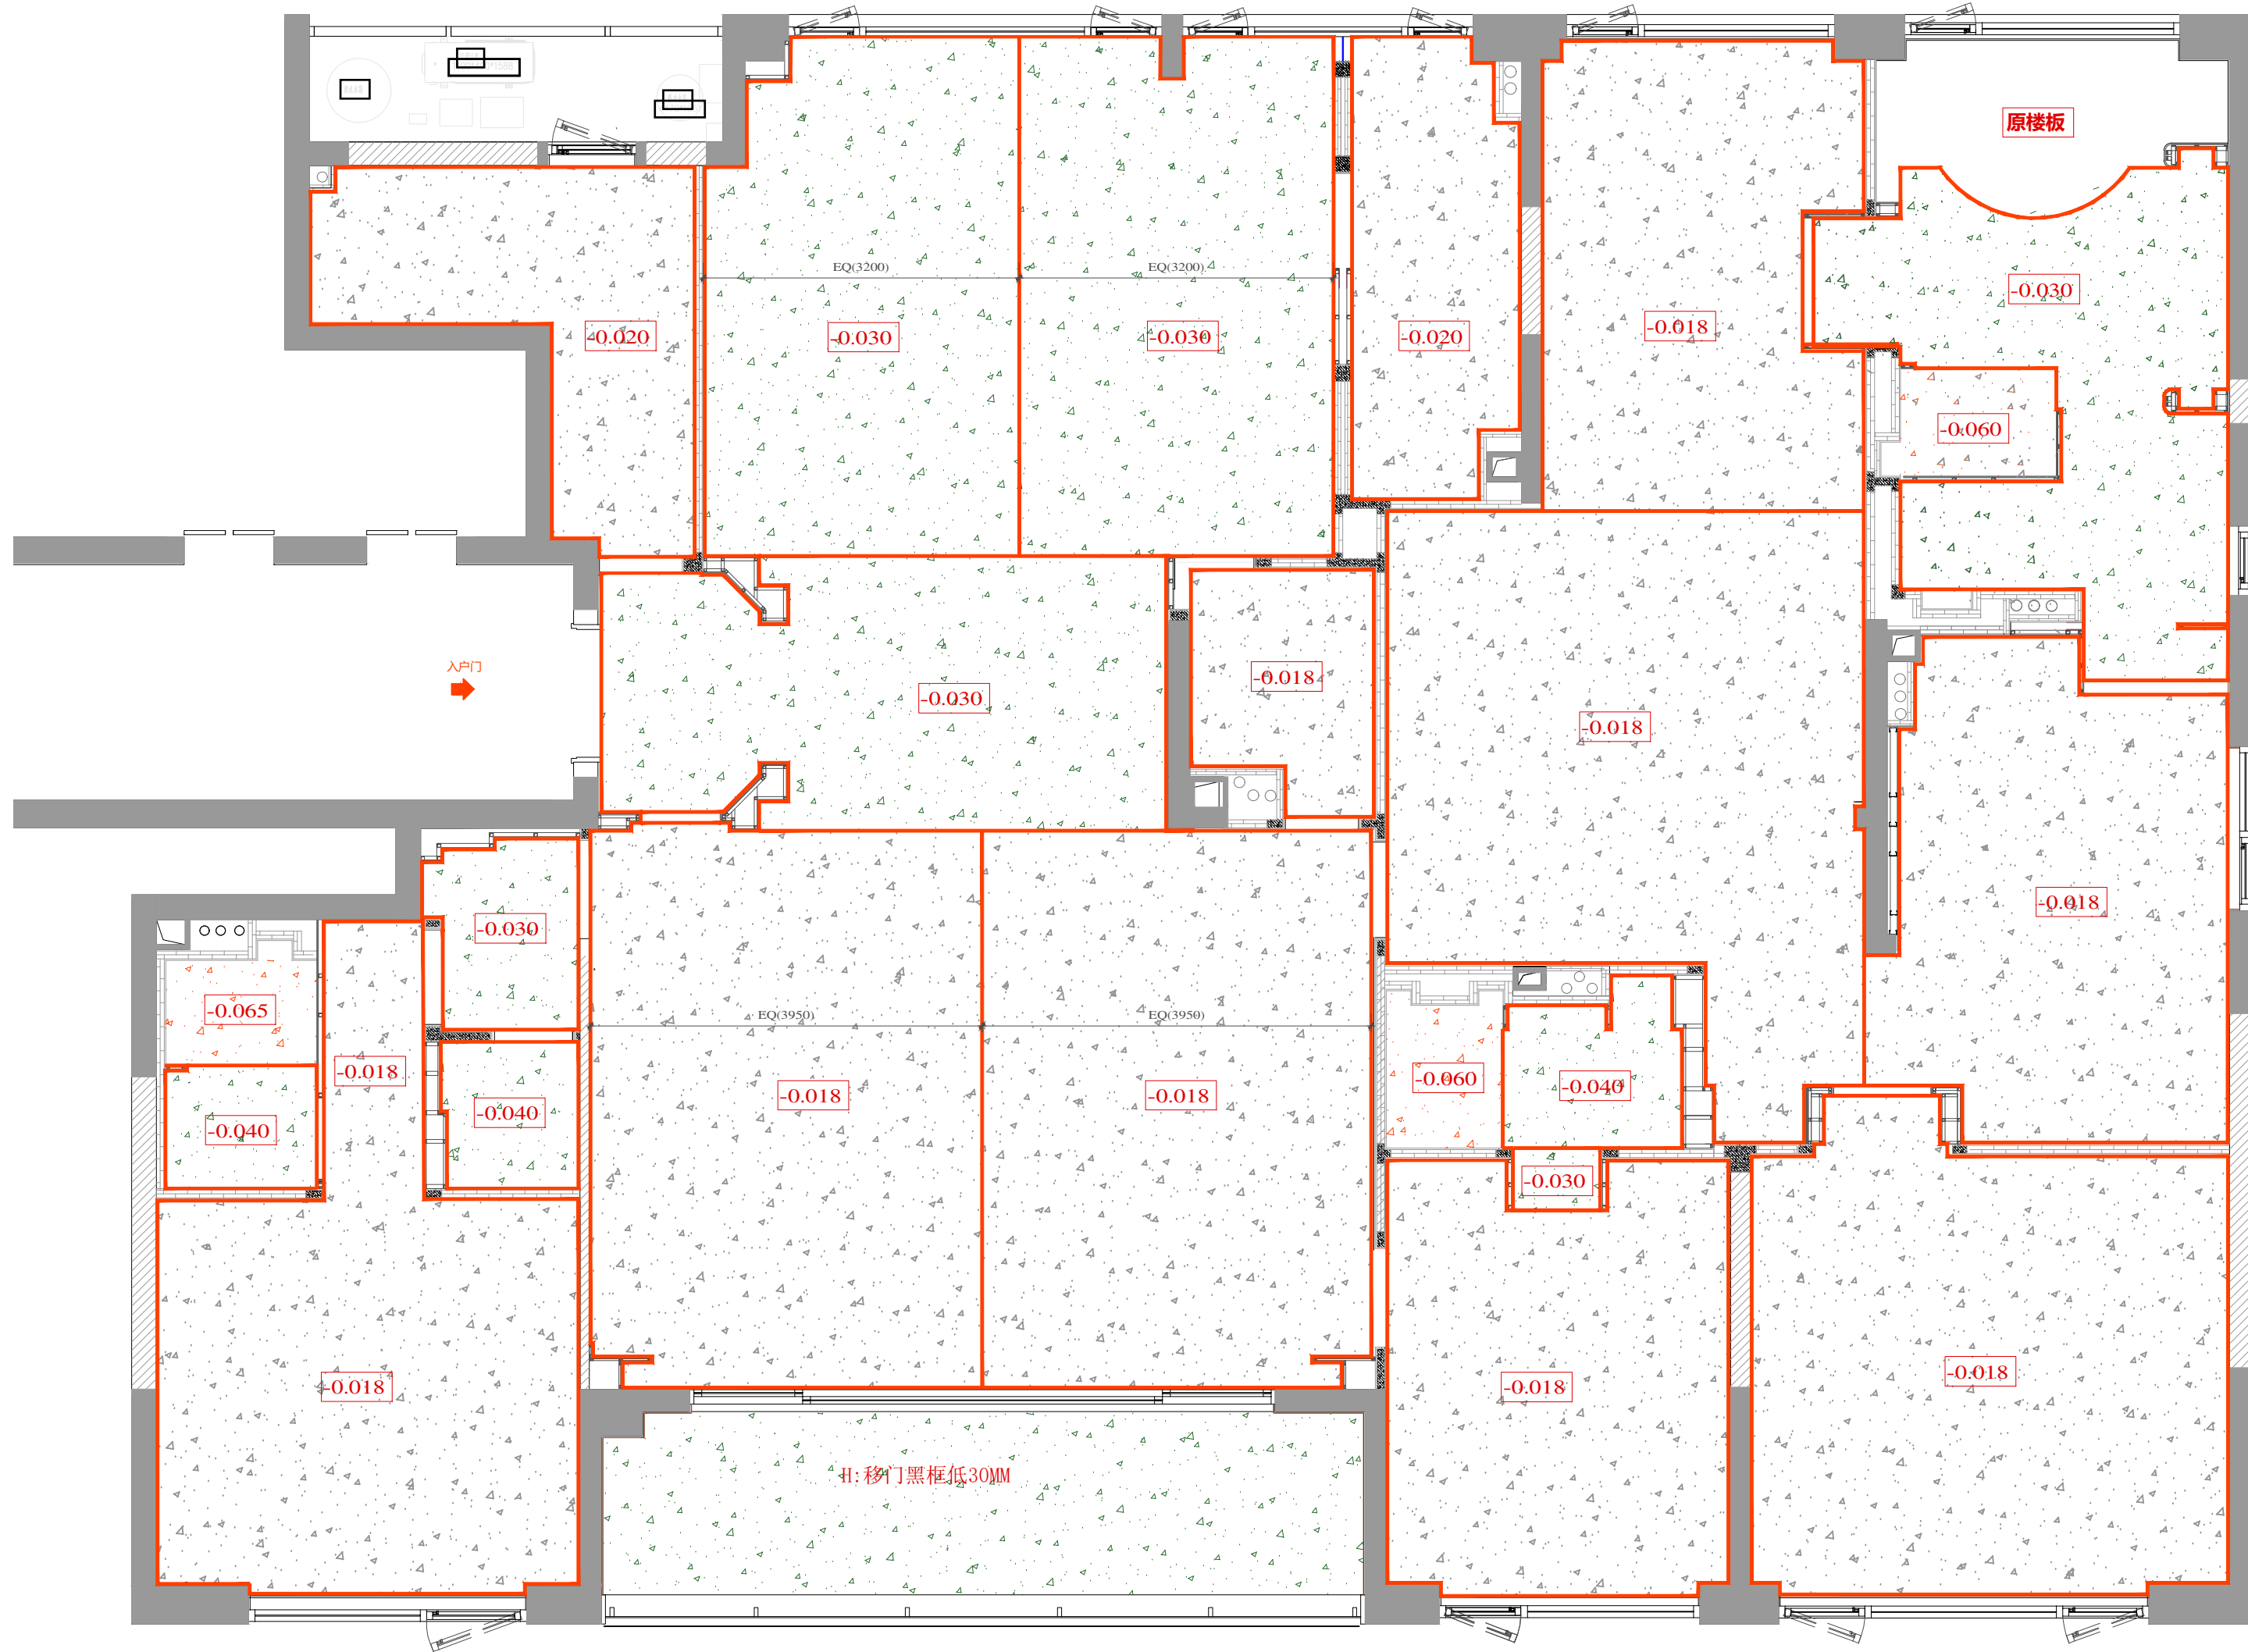

水泥砂浆找平标高及伸缩缝平面图


Scale比例 1:60@A2

注释

Notes

- 本图纸尺寸如与现场尺寸有误，请施工人员与项目负责人联系。
- 施工前施工人员应认真查阅此图，如有不明尺寸，按现场测量为准。
- 本图纸必须经甲乙双方认可并签字方可作为施工依据。

最终面材铺贴样式以专业厂家图纸为准

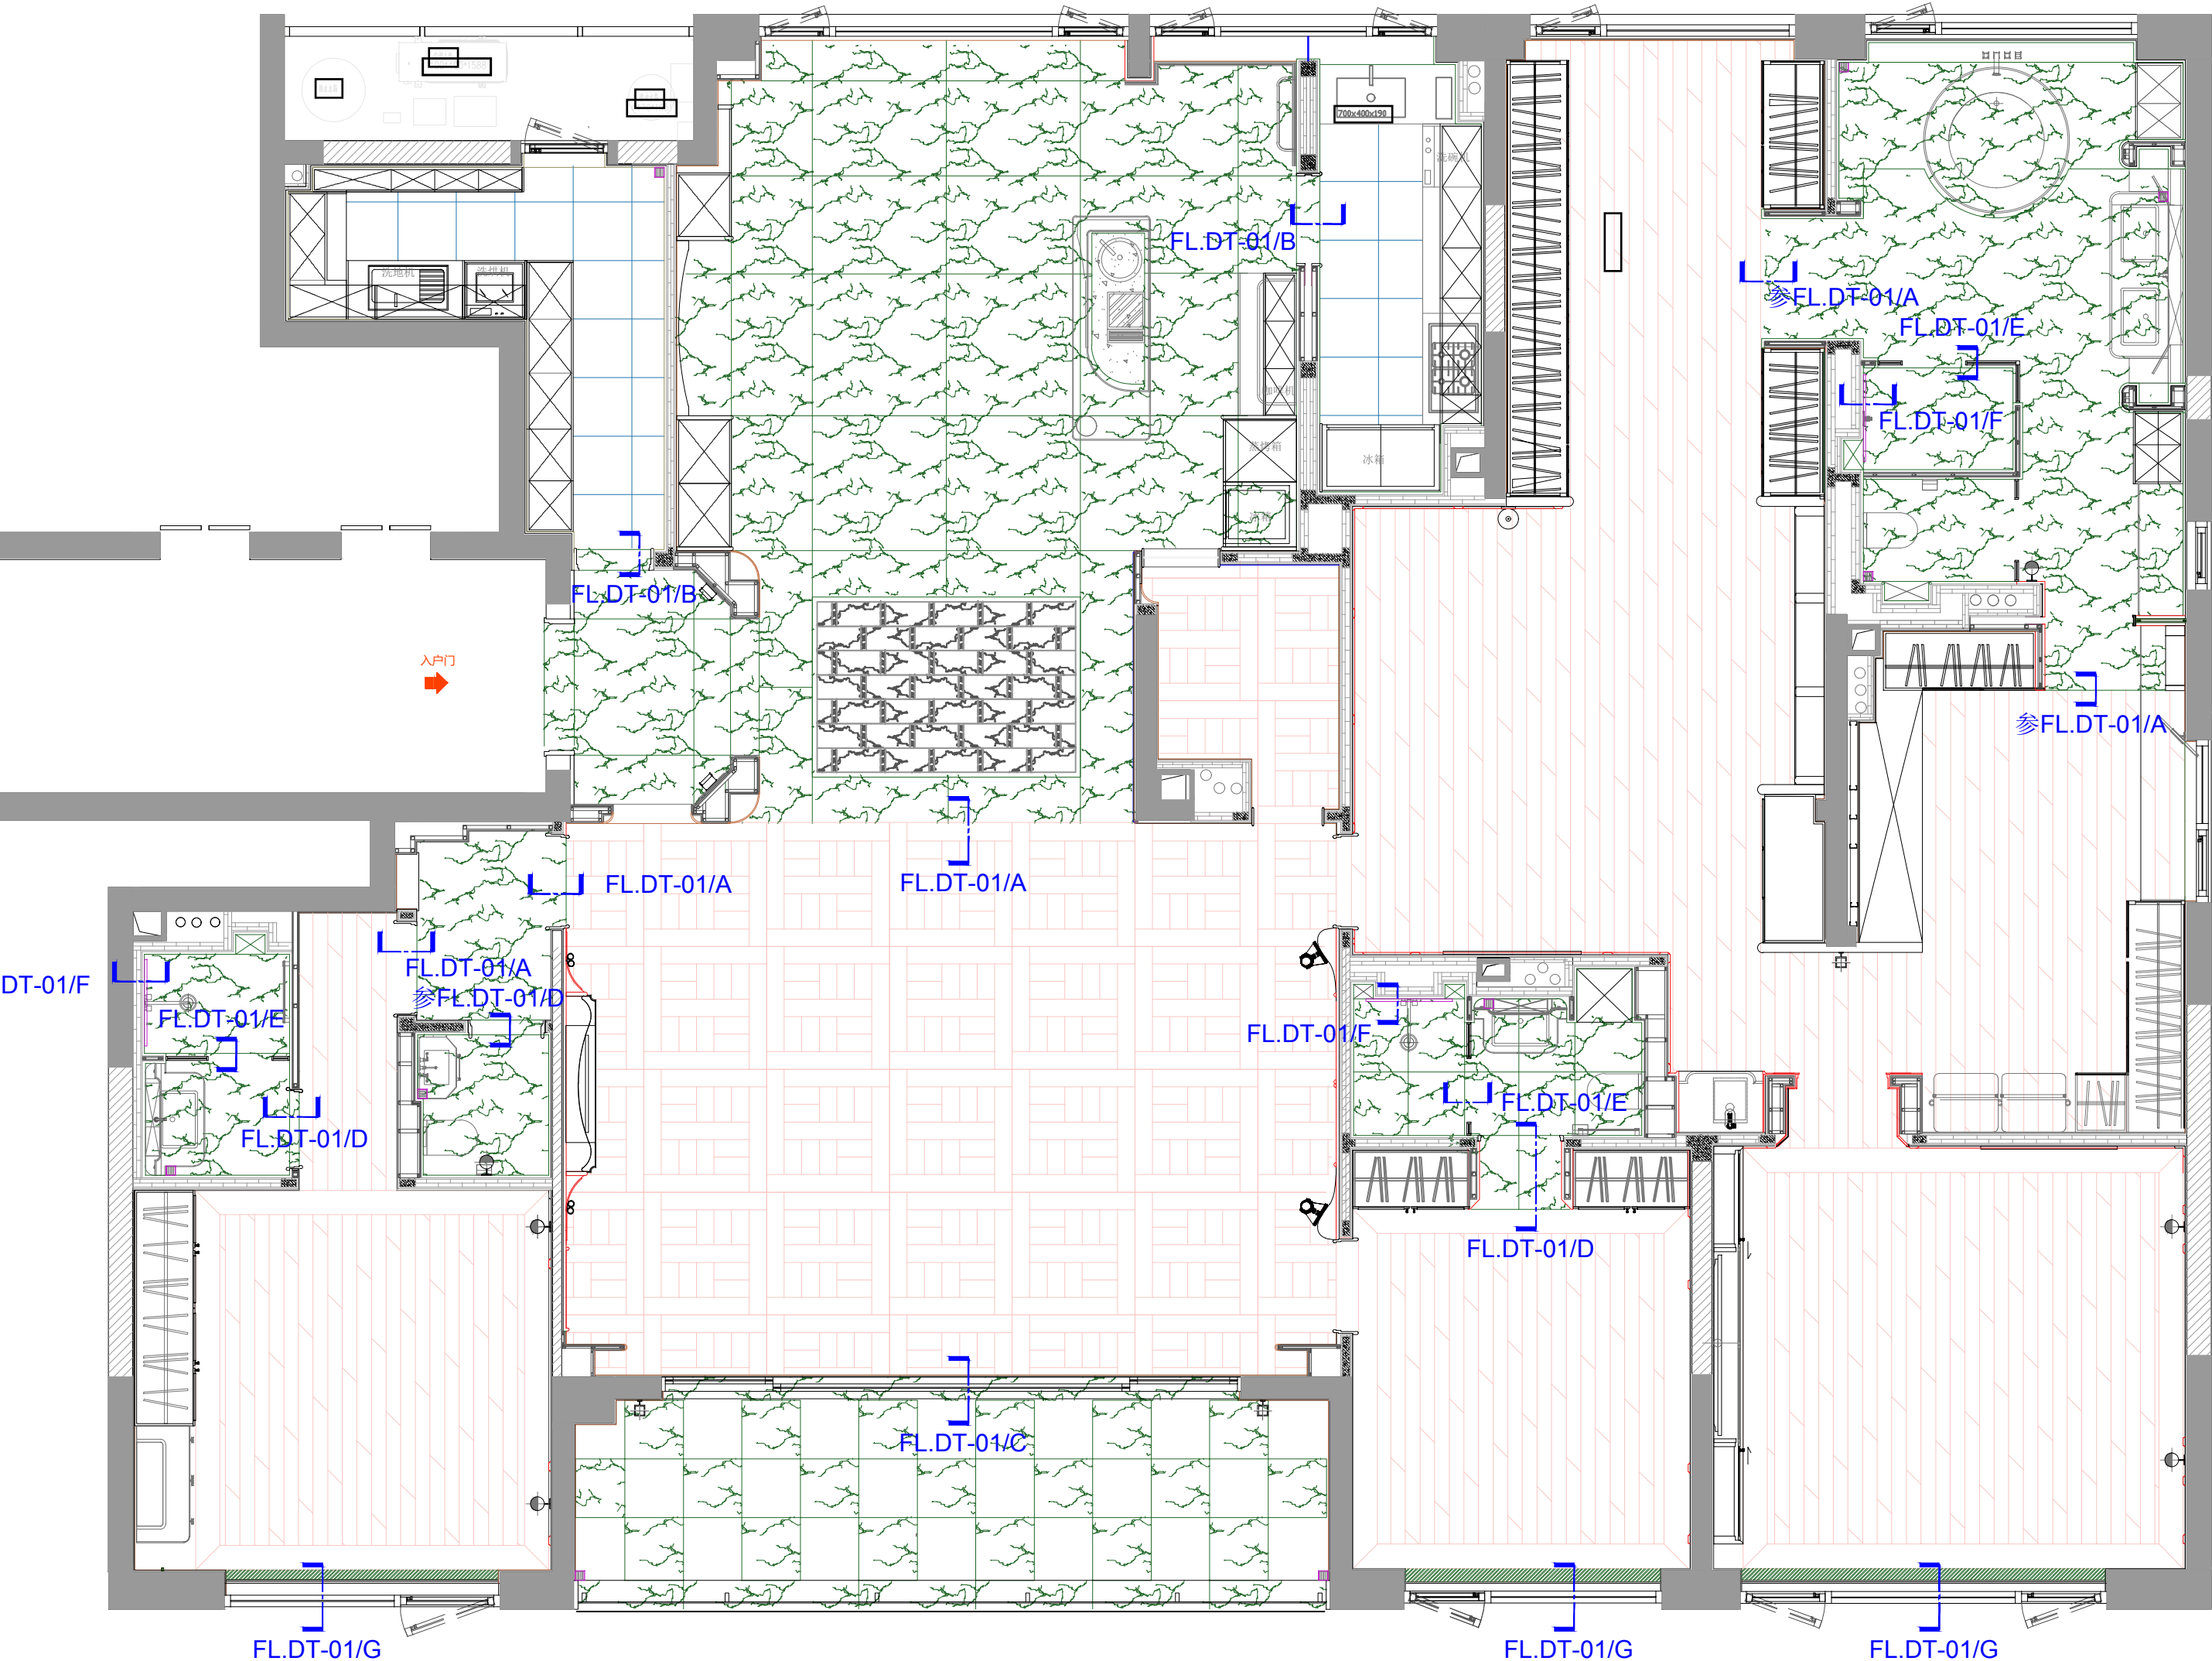

ELIBORN

LEGEND A	
图例示意	说明
	石材
	岩板/瓷砖
	木地板
	木地板

正式施工图
26-05-20

日期
Date 2026.5.9

修订
Revisions



项目
Project

杭州 华岸府

Scale
比例

Drawing No.
图纸编号

FL.DT-02

Project No.
项目编号

© 2025


地坪剖面索引图

Scale比例 1:60@A2


注释
Notes

1. 本图纸尺寸如与现场尺寸有误差，请施工方与项目负责人联系。
2. 施工前施工方应认真查阅此图，如有不明尺寸，按现场测量为准。
3. 本图纸必须经甲乙双方认可并签字方可作为施工依据。


无特殊说明的材质拼接均为密拼。

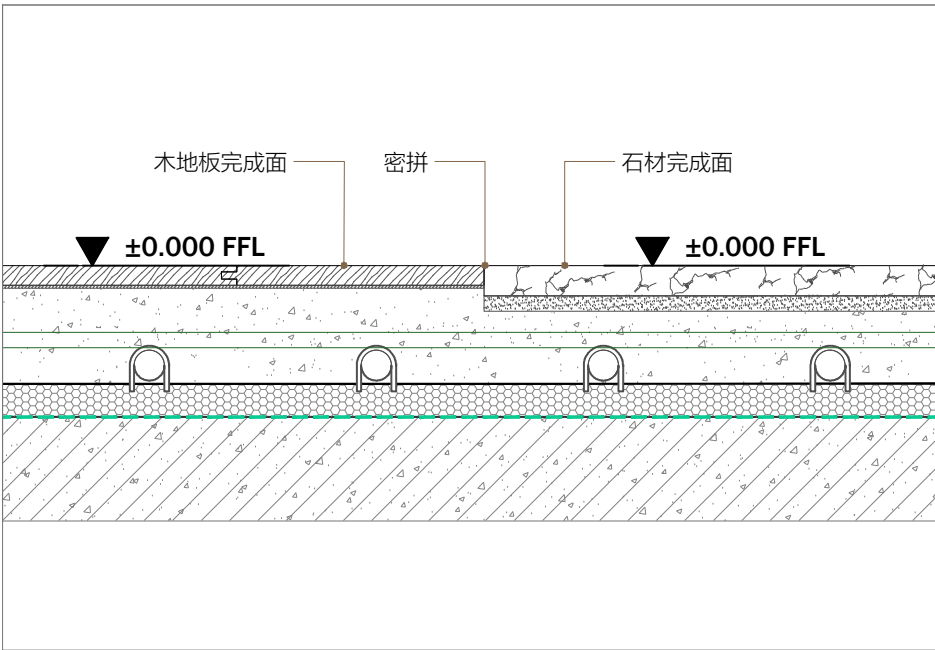


A 石材和木地板收口大样
Scale比例 1:5 @A2

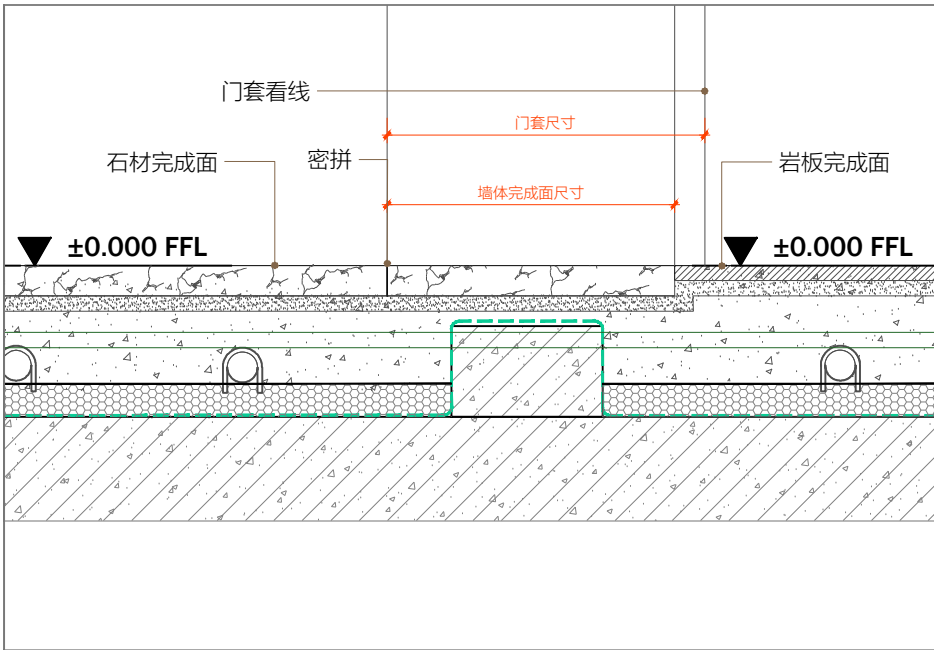


B 石材和岩板收口大样
Scale比例 1:5 @A2

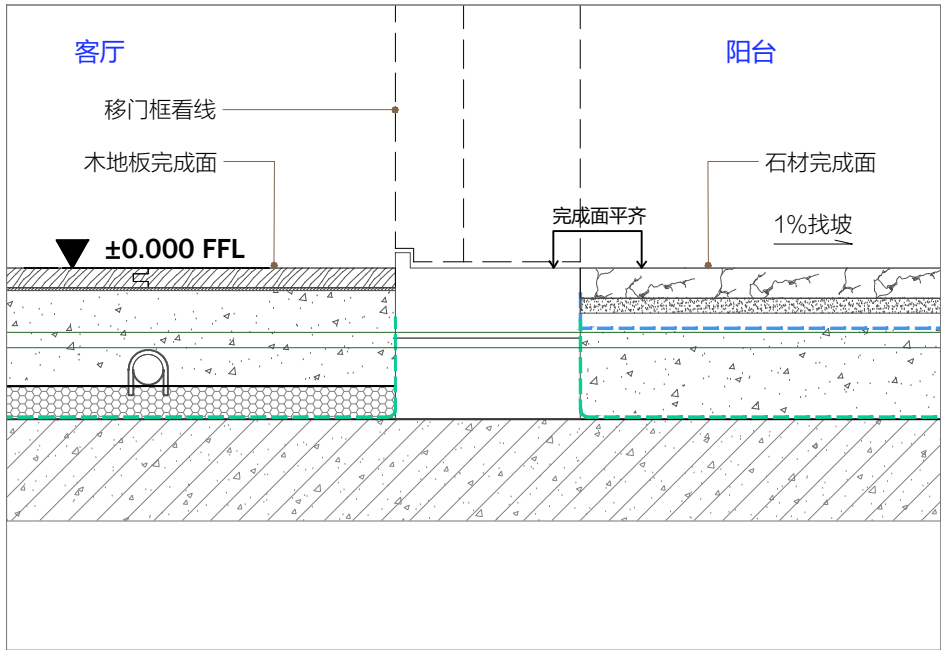


C 阳台门槛大样
Scale比例 1:5 @A2

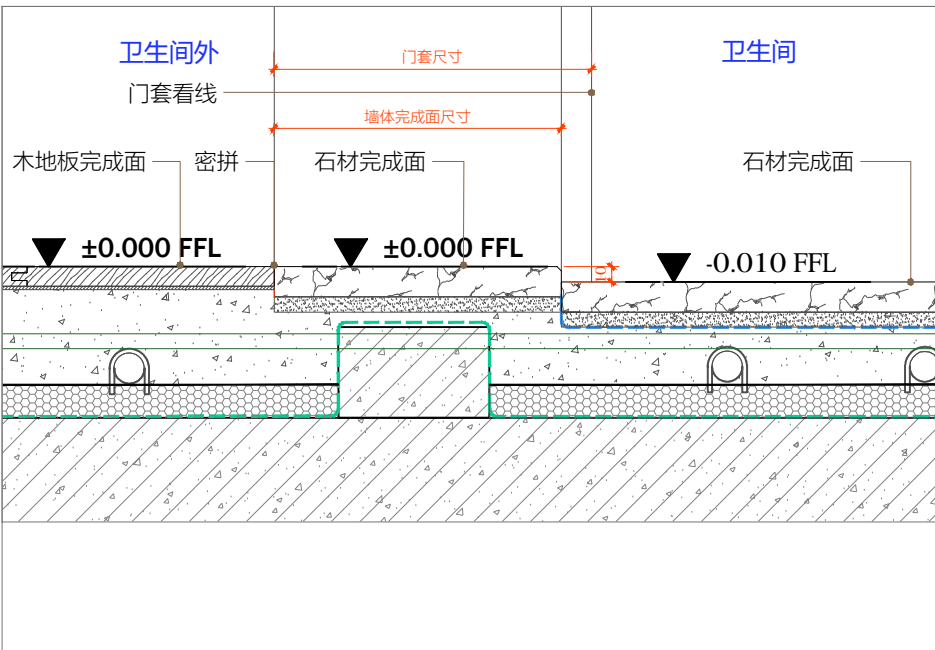


D 卫生间门槛大样
Scale比例 1:5 @A2

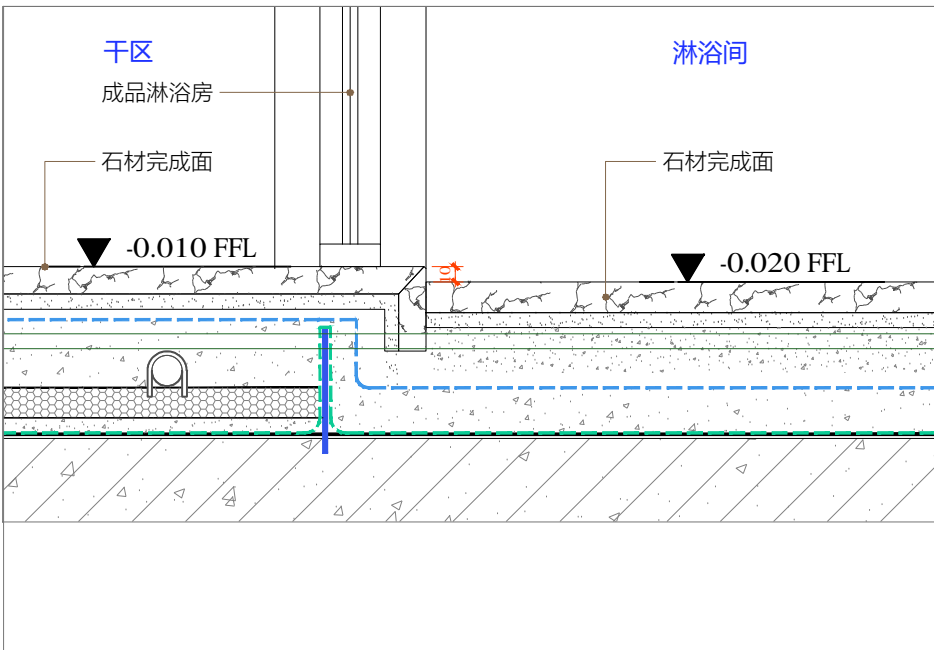

E 淋浴间大样
Scale比例 1:5 @A2

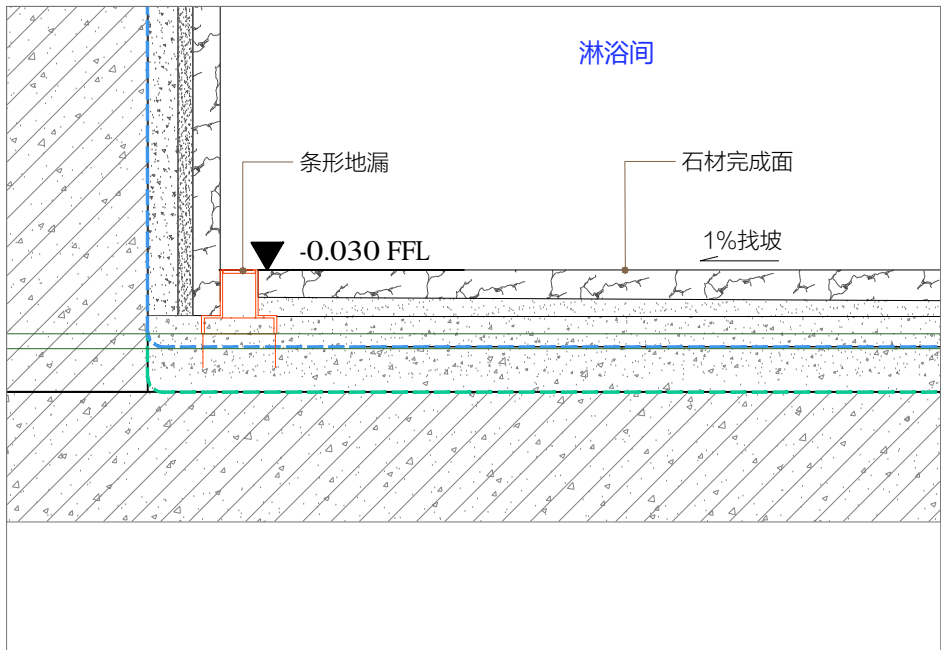

F 淋浴间地漏大样
Scale比例 1:5 @A2

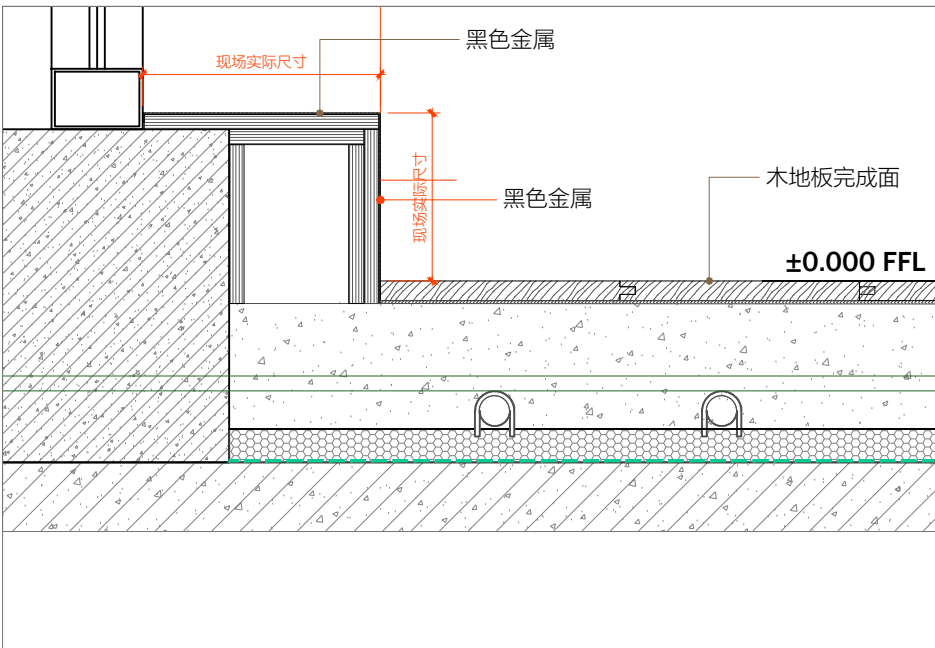

G 落地窗台大样
Scale比例 1:5 @A2

FLBORN

LEGEND A

正式施工图
26-05-20

日期
Date 2026.5.9

修订
Revisions



项目
Project

杭州 华岸府

Scale
比例

Drawing No.
图纸编号

FL.DT-01

Project No.
项目编号

© 2025

地坪节点图

Scale比例 1:5@A2

注释

Notes

1. 本图尺寸如与现场尺寸有误，请施工人员与项目负责人联系。
2. 施工前施工人员应认真查阅此图，如有不明确尺寸，按现场测量为准。
3. 本图纸必须经甲乙双方认可并签字方可作为施工依据。