


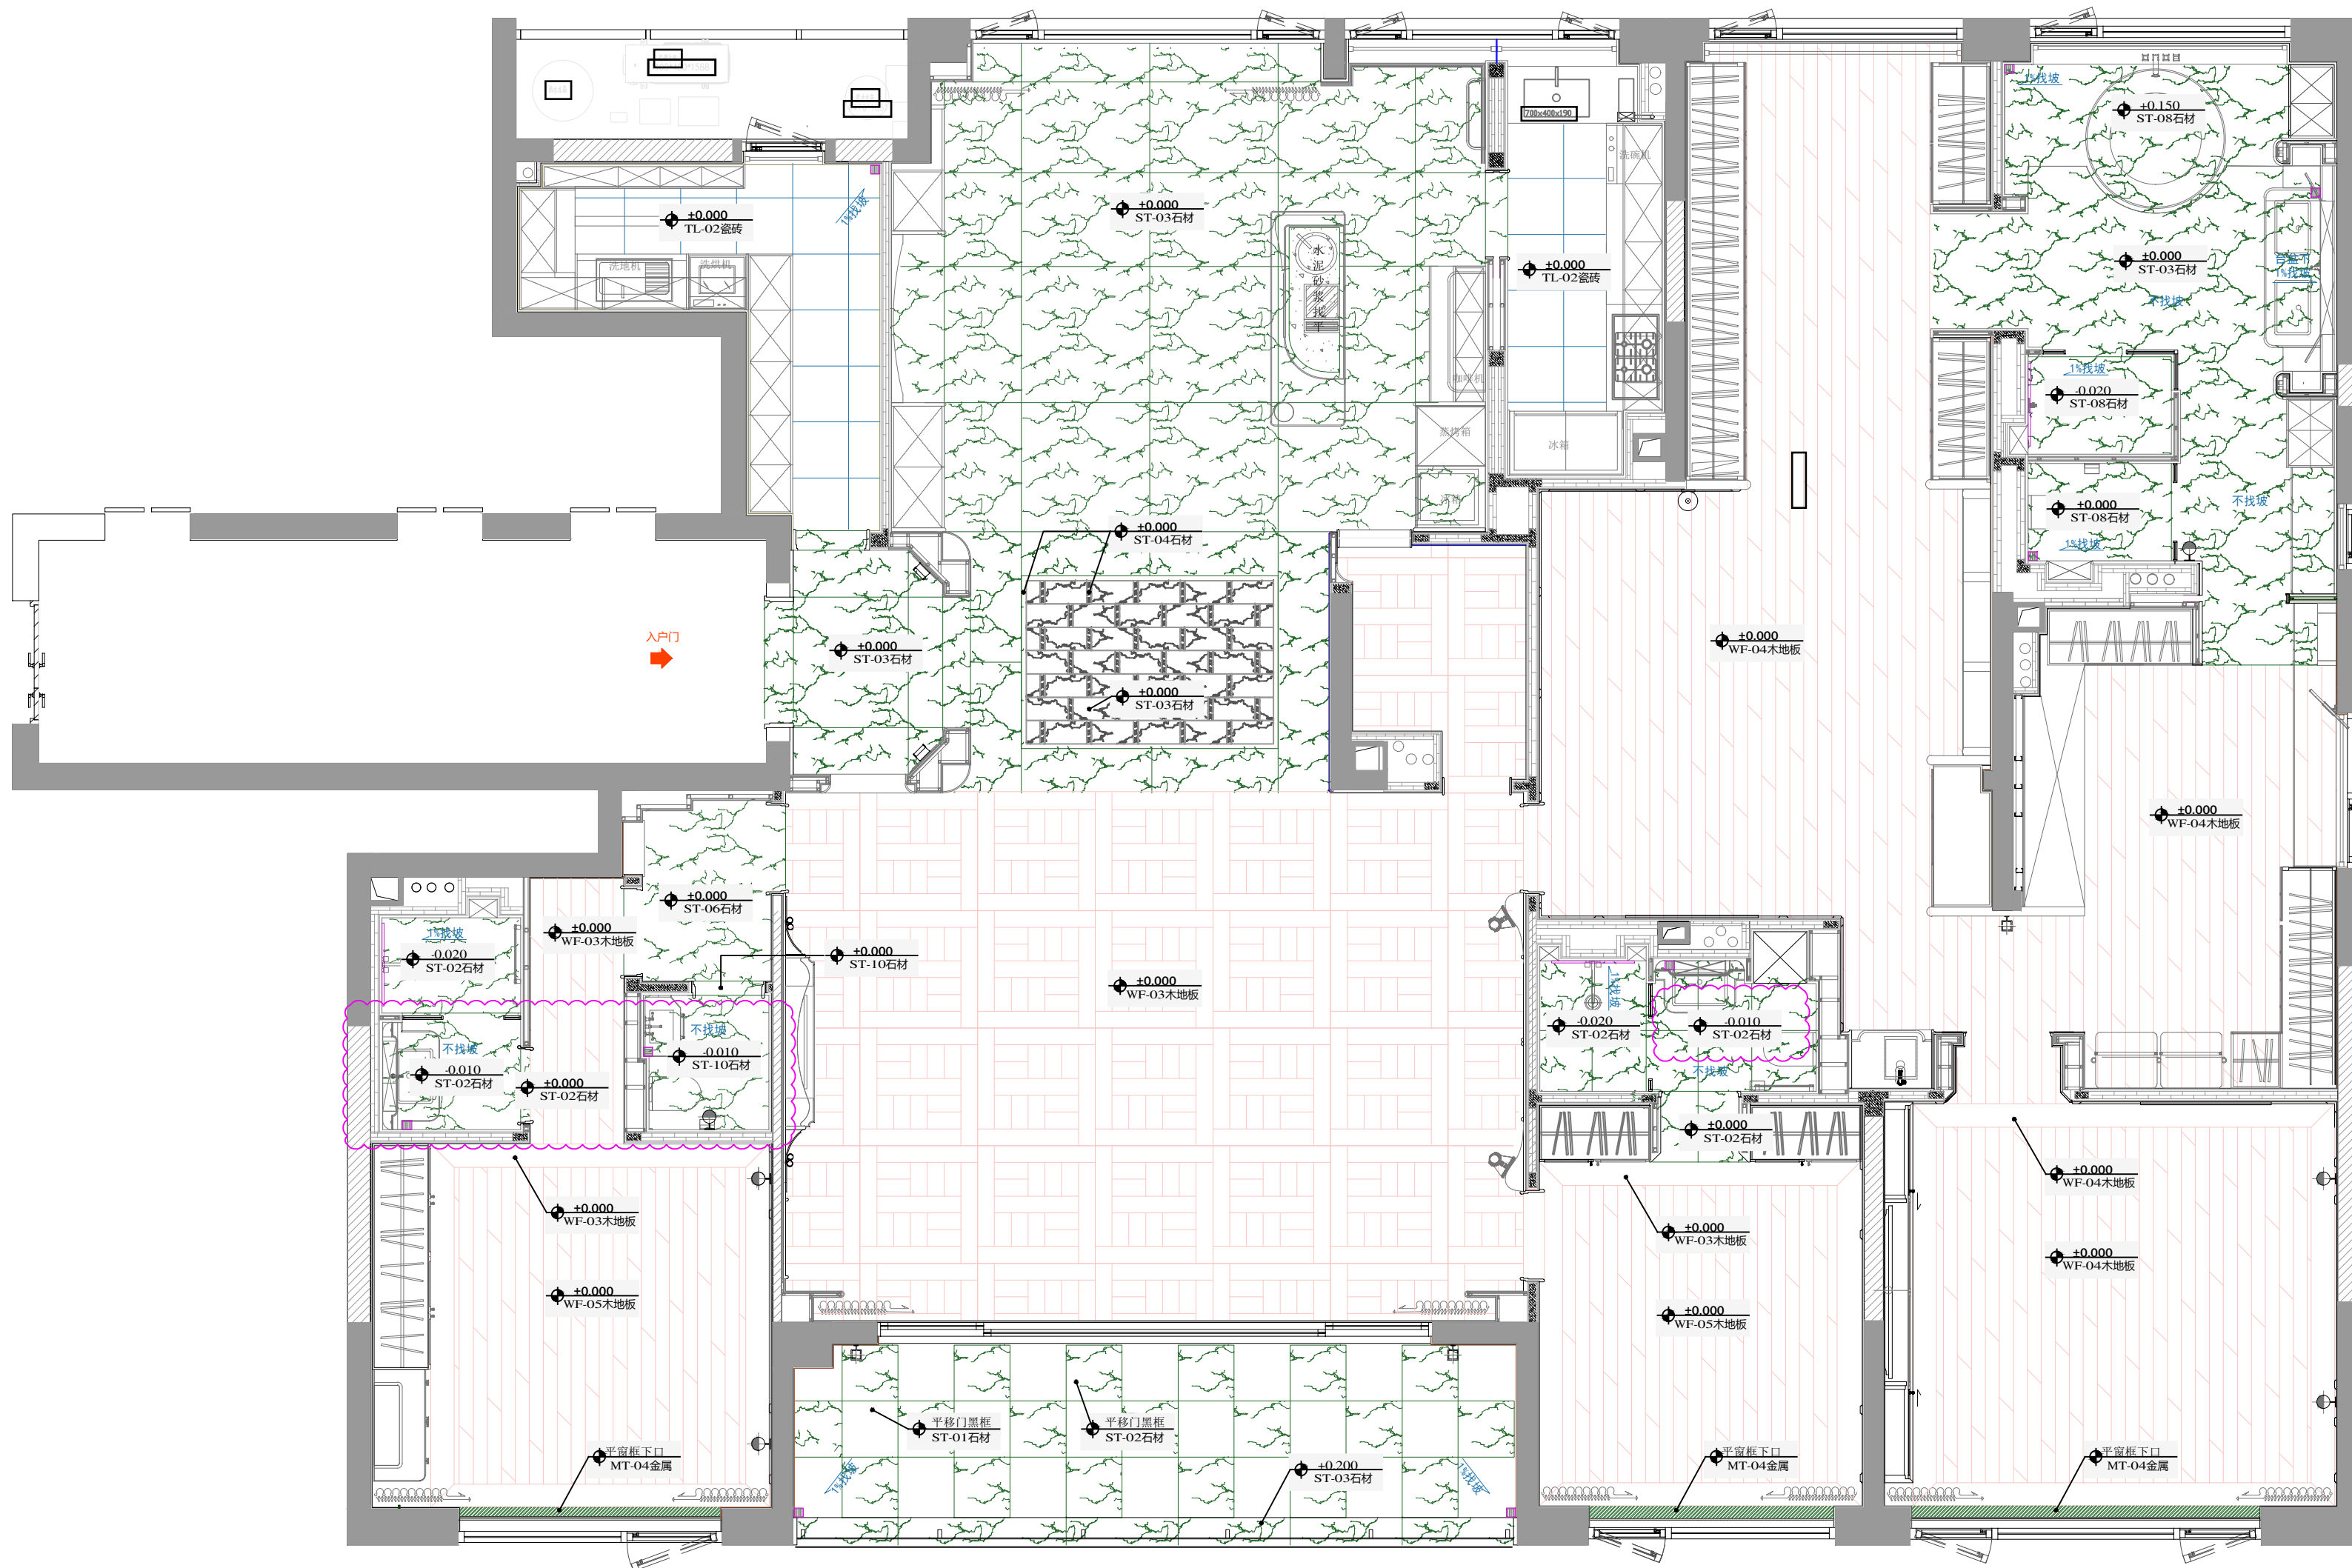

2026.4.30变更：卫生间地坪标高调整。

最终面材铺贴样式以专业厂家图纸为准

图例示意	说明
	石材
	岩板\瓷砖
	木地板
	木地板

日期
Date 2026.4.3

修订
Revisions

	2026.4.30
---	-----------

项目
Project

Scale
比例

Drawing No.
图纸编号

FL.PL-01


Project No. © 2025
项目编号

地坪完成面材质及标高平面图

注释
Notes

1. 本图纸尺寸如与现场尺寸有误, 请施工人员与项目负责人联系。
2. 施工前施工人员应认真查阅此图, 如有不明确尺寸, 按现场测量为准。
3. 本图纸必须经甲乙双方认可并签字方可作为施工依据。

Scale比例 1:60@A2

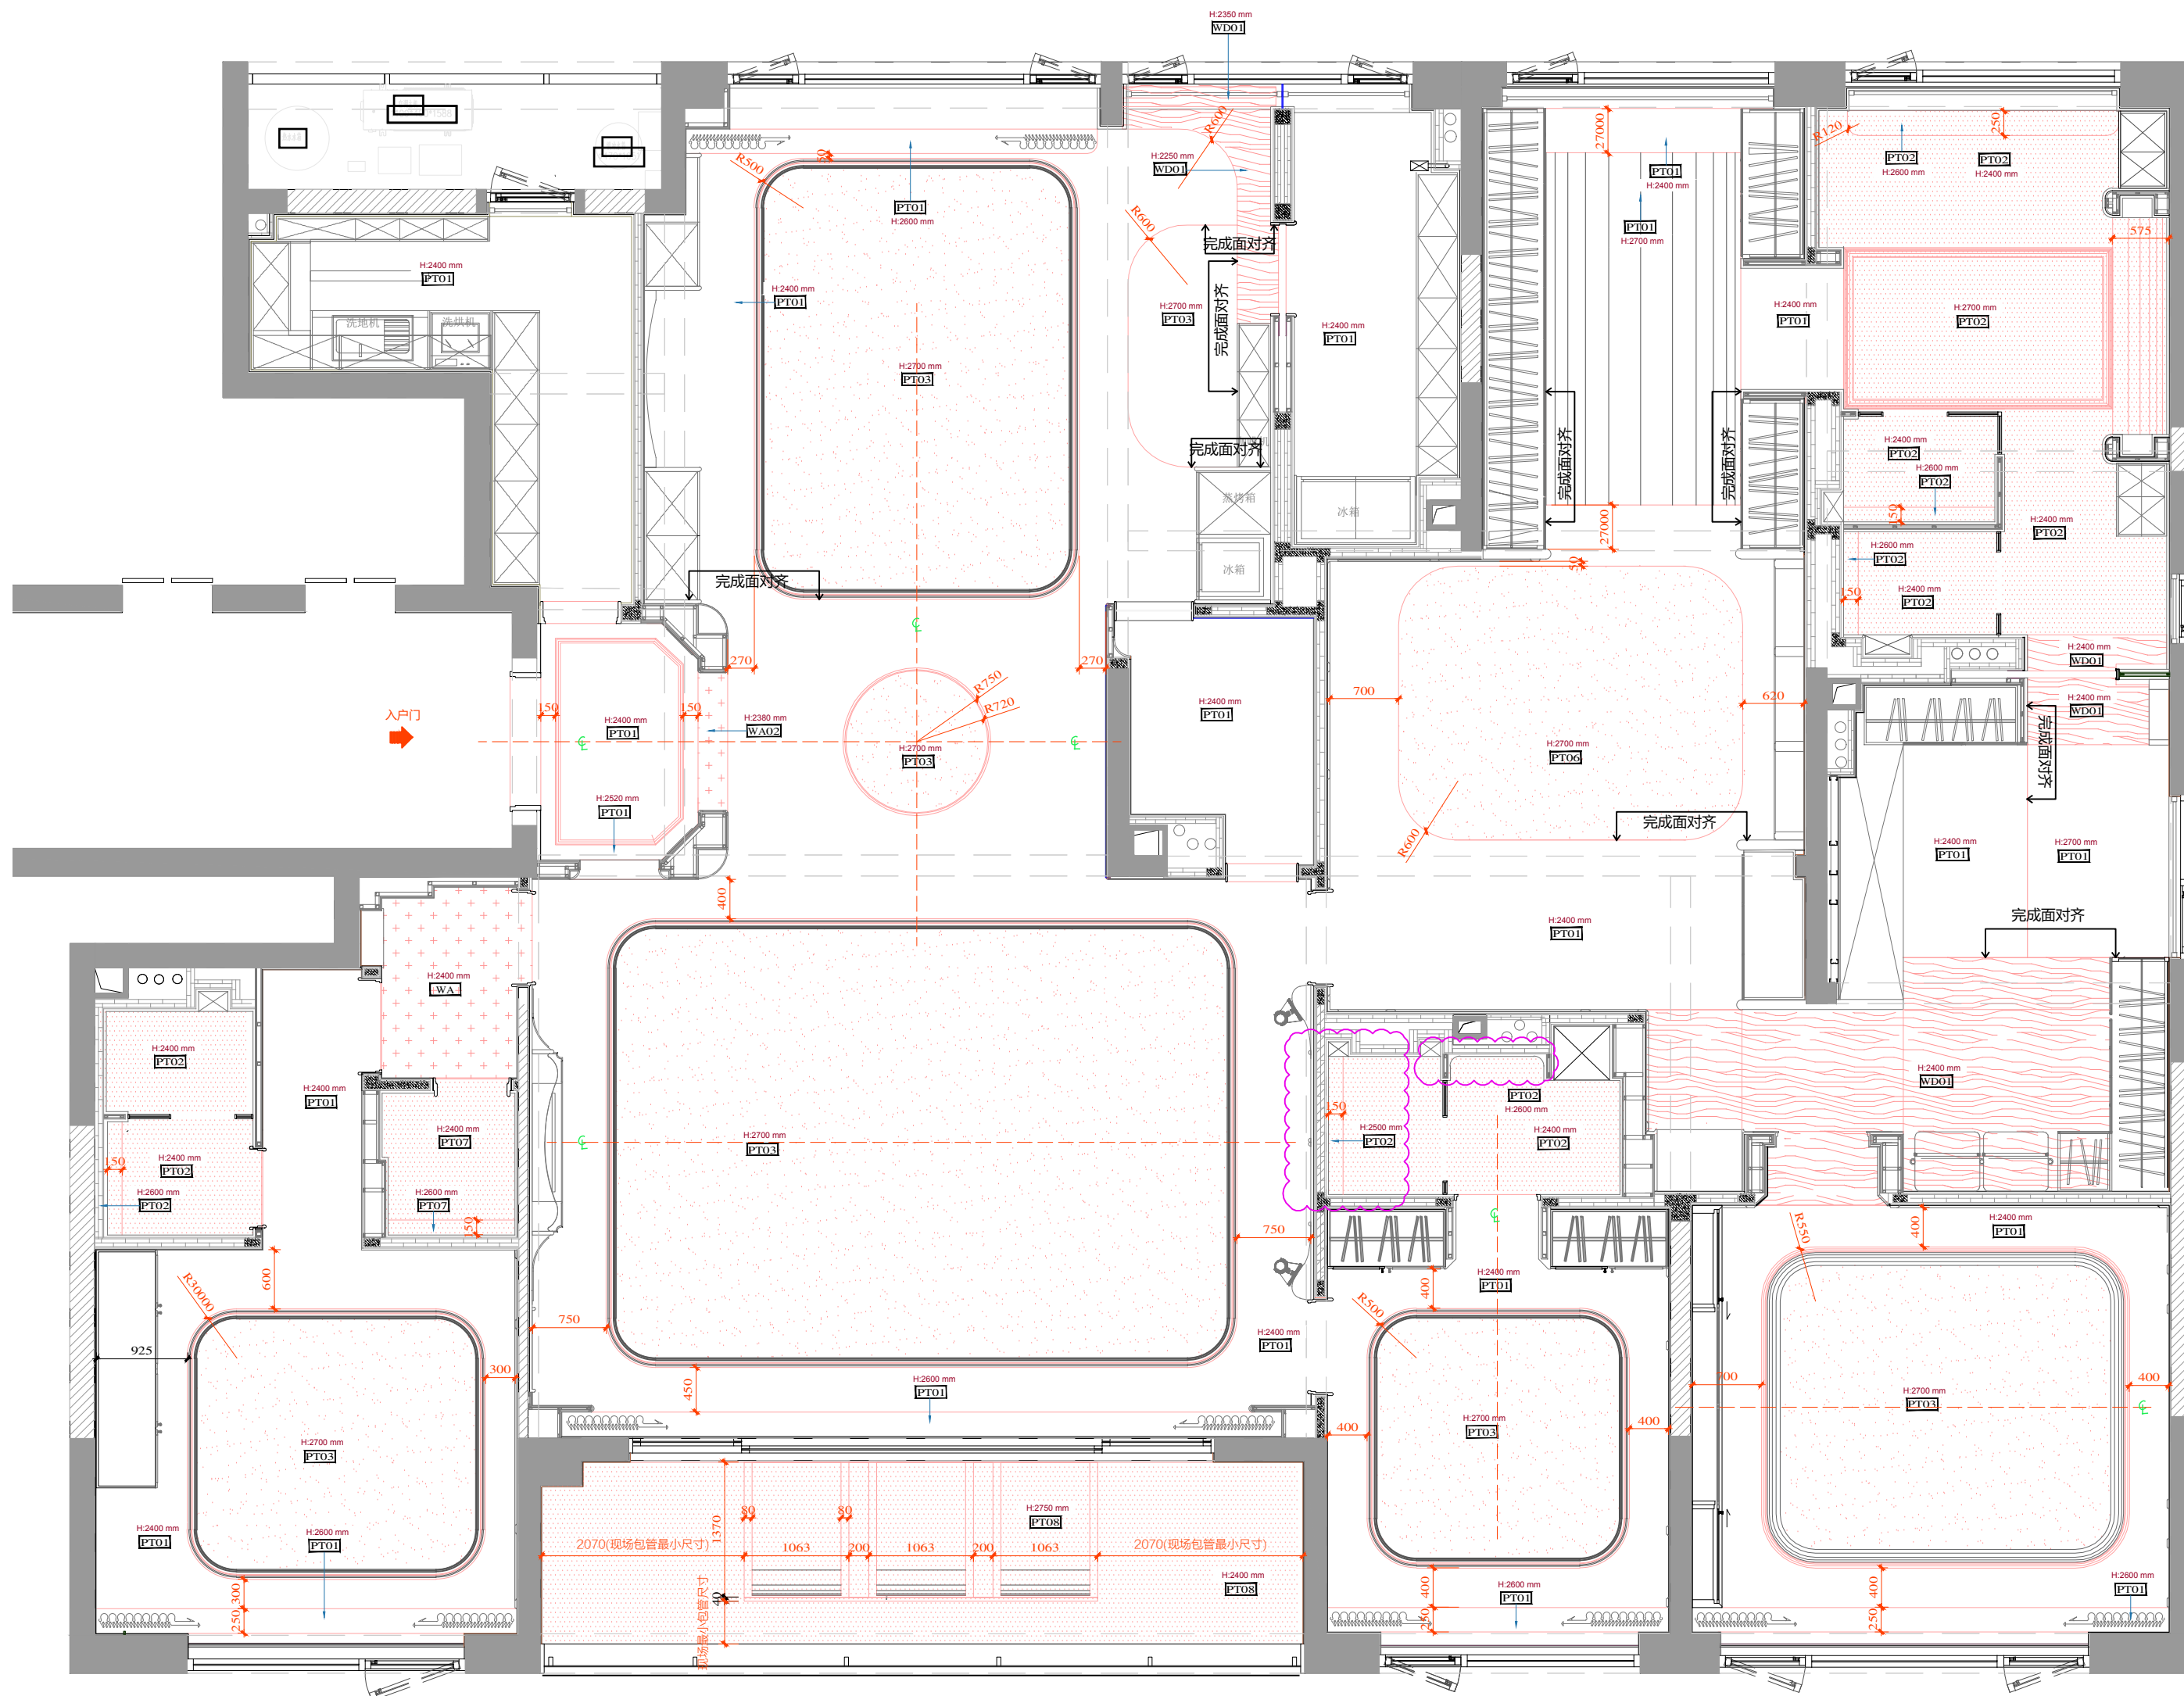

2026.5.6变更：次卫灯槽位置调整。

天花完成面尺寸图

Scale比例 1:60@A2

注释
Notes

1. 本图尺寸如与现场尺寸有误差，请施工人员与项目负责人联系。
2. 施工前施工人员应认真查阅此图，如有不明确尺寸，按现场测量为准。
3. 本图必须经甲乙双方认可并签字方可作为施工依据。

日期
Date 2026.3.27

修订
Revisions



项目
Project

杭州 华岸府


Scale
比例 1:60 @A2

Drawing No.
图纸编号


CL.PL-02

Project No.
项目编号

© 2025

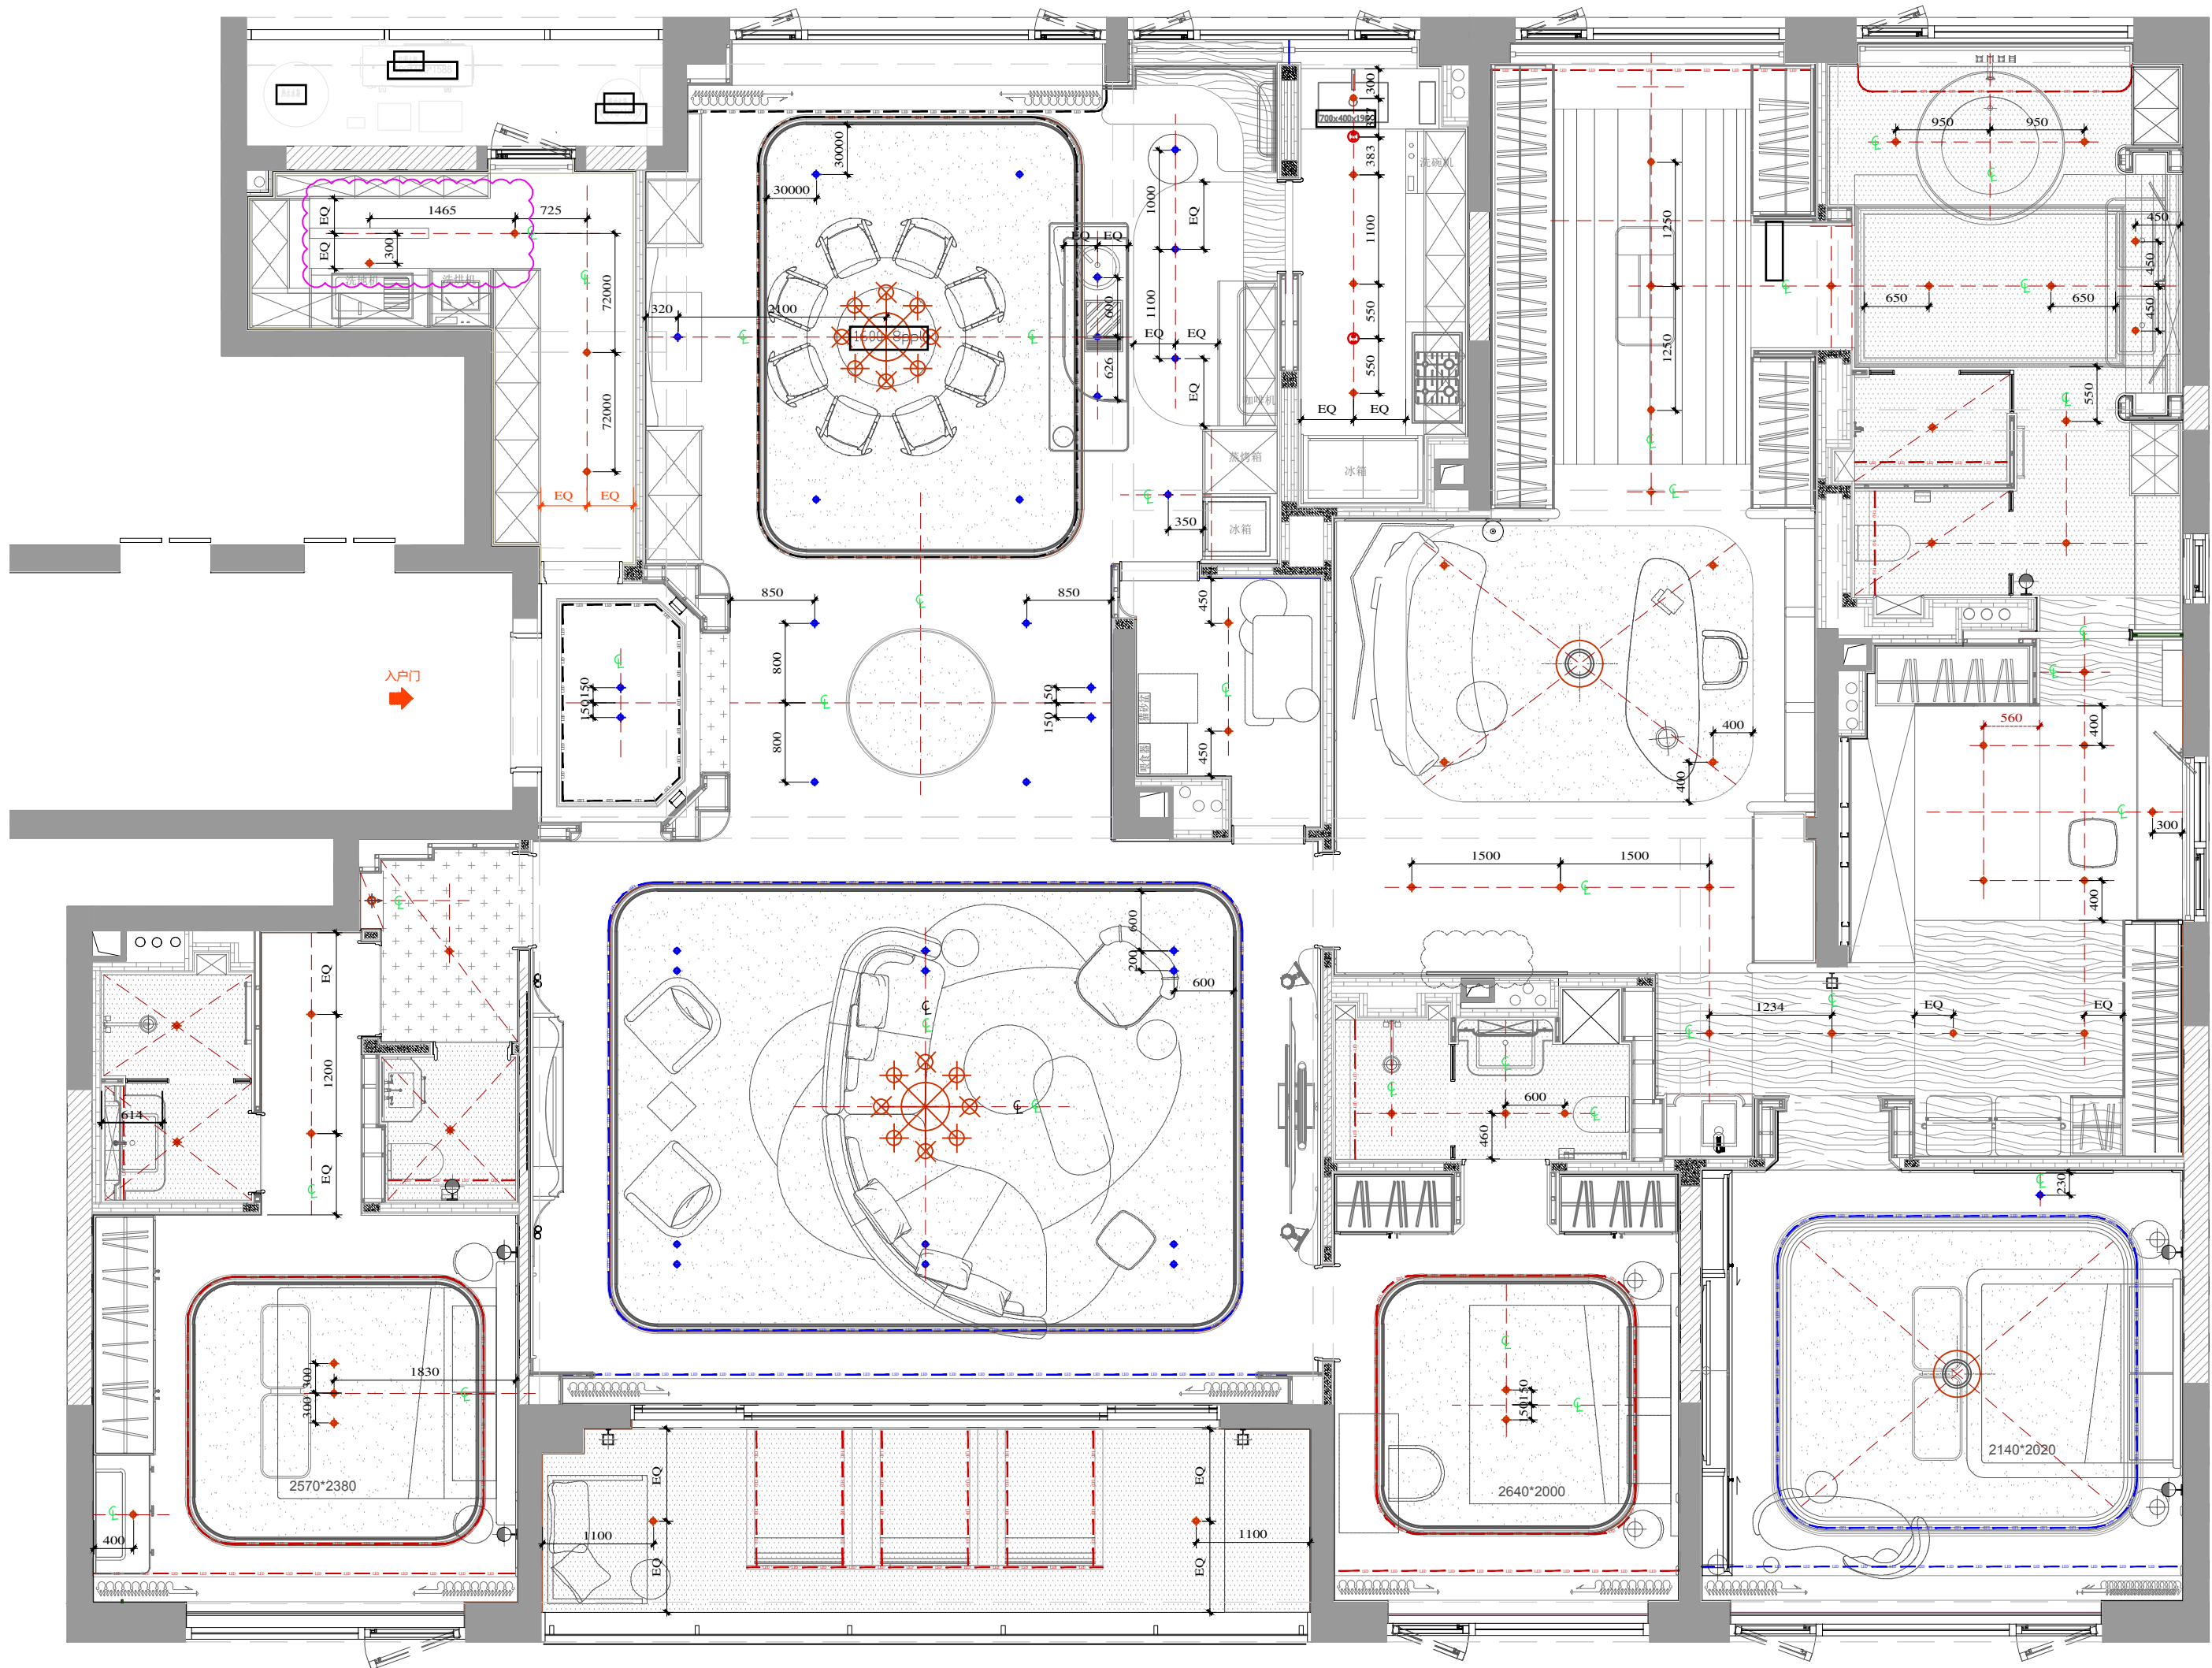

Project No. 项目编号 © 2025

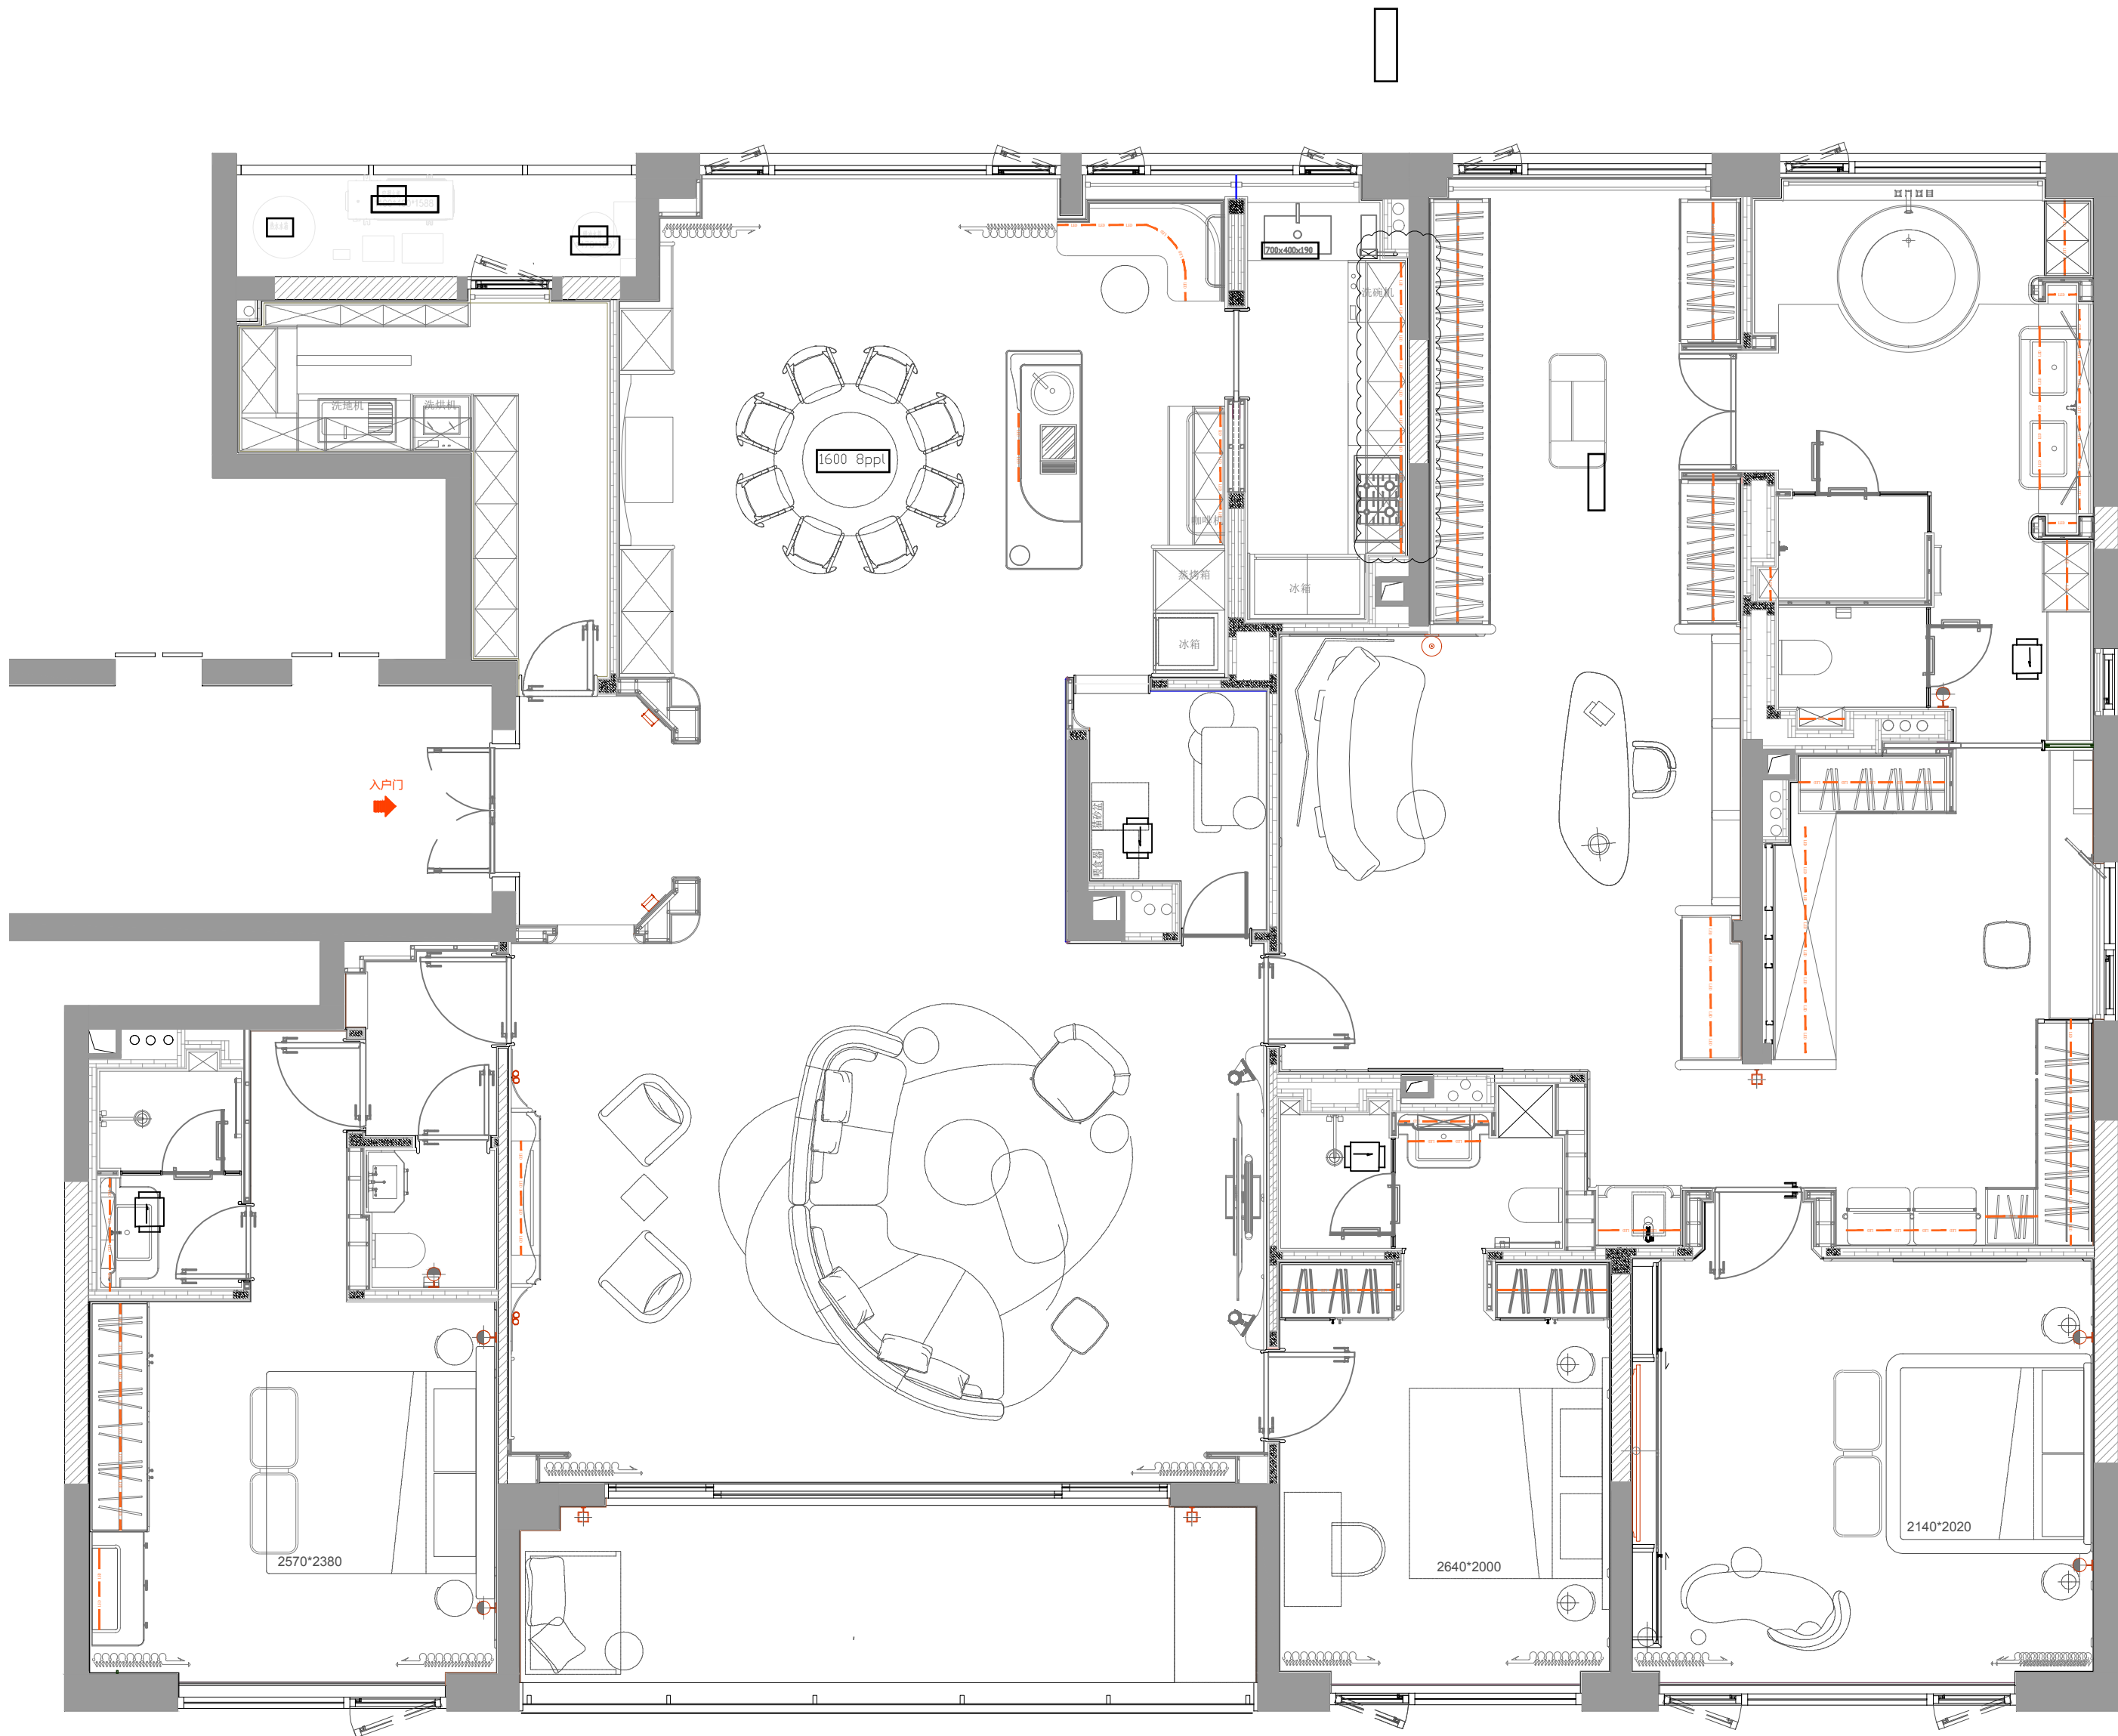

墙地面灯具布置图

Scale比例 1:60@A2

注释
Notes

1. 本图尺寸如与现场尺寸有误，请施工人员与项目负责人联系。
2. 施工前施工人员应认真查阅此图，如有不明尺寸，按现场测量为准。
3. 本图纸必须经甲乙双方认可并签字方可作为施工依据。

日期
Date 2026.4.3

修订
Revisions



项目
Project

杭州 华岸府

Scale
比例 1:60 @A2


杭州 华岸府

Drawing No.
图纸编号

CL.PL-03.2

Project No.
项目编号

© 2025

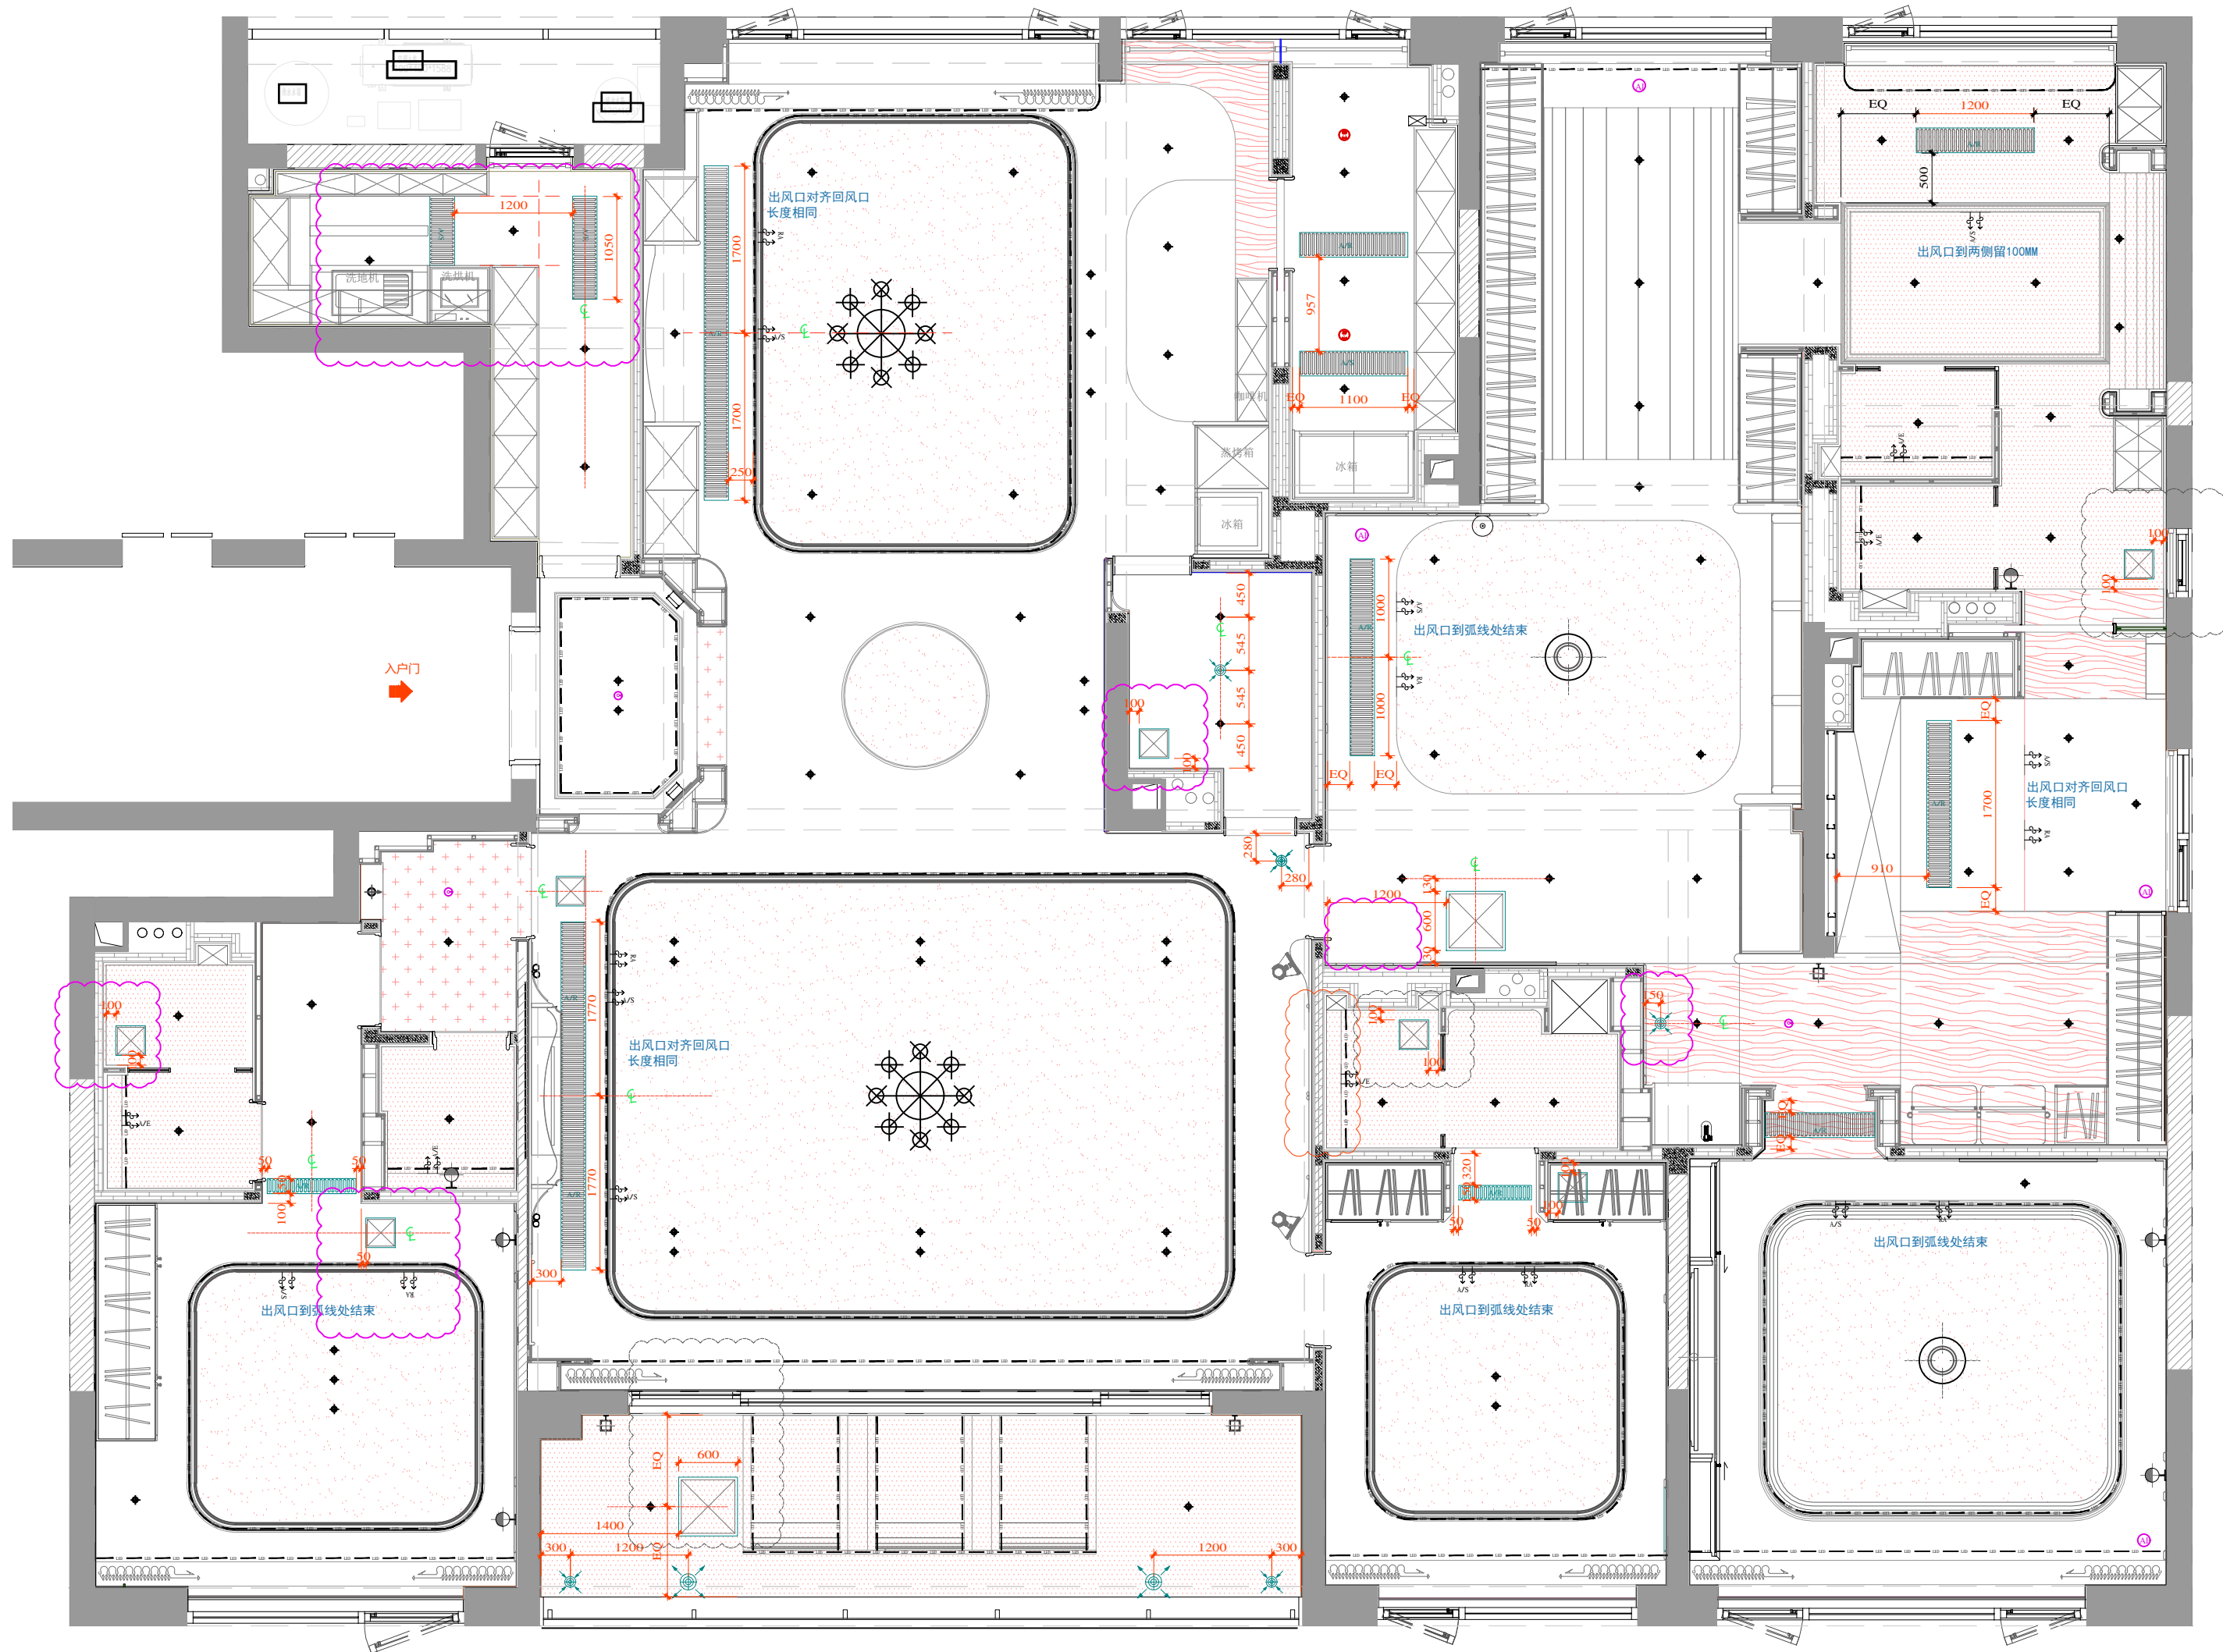

2026.4.21变更: 增加排风和新风检修口定位。
2026.5.6变更: 风口和检修口位置根据现场情况调整。

天花风口及检修口平面图

天花风口及检修口平面图

Scale比例 1:60 @A2

注释
Notes

1. 本图纸尺寸如与现场尺寸有误, 请施工人员与项目负责人联系。
2. 施工前施工人员应认真查阅此图, 如有不明确尺寸, 按现场测量为准。
3. 本图纸必须经甲乙双方认可并签字方可作为施工依据。

M-机电点位	
图 例	名 称
	百叶风口 (无特殊标注宽度为250mm)
	检修口 (无特殊标注边长为300mm)
	新风回风口
	新风出风口

日期
Date 2026.4.3修订
Revisions
 2026.4.21项目
Project


杭州 华岸府

Scale
比例 1:60 @A2Drawing No.
图纸编号

CL.PL-3.3

Project No.
项目编号

© 2025

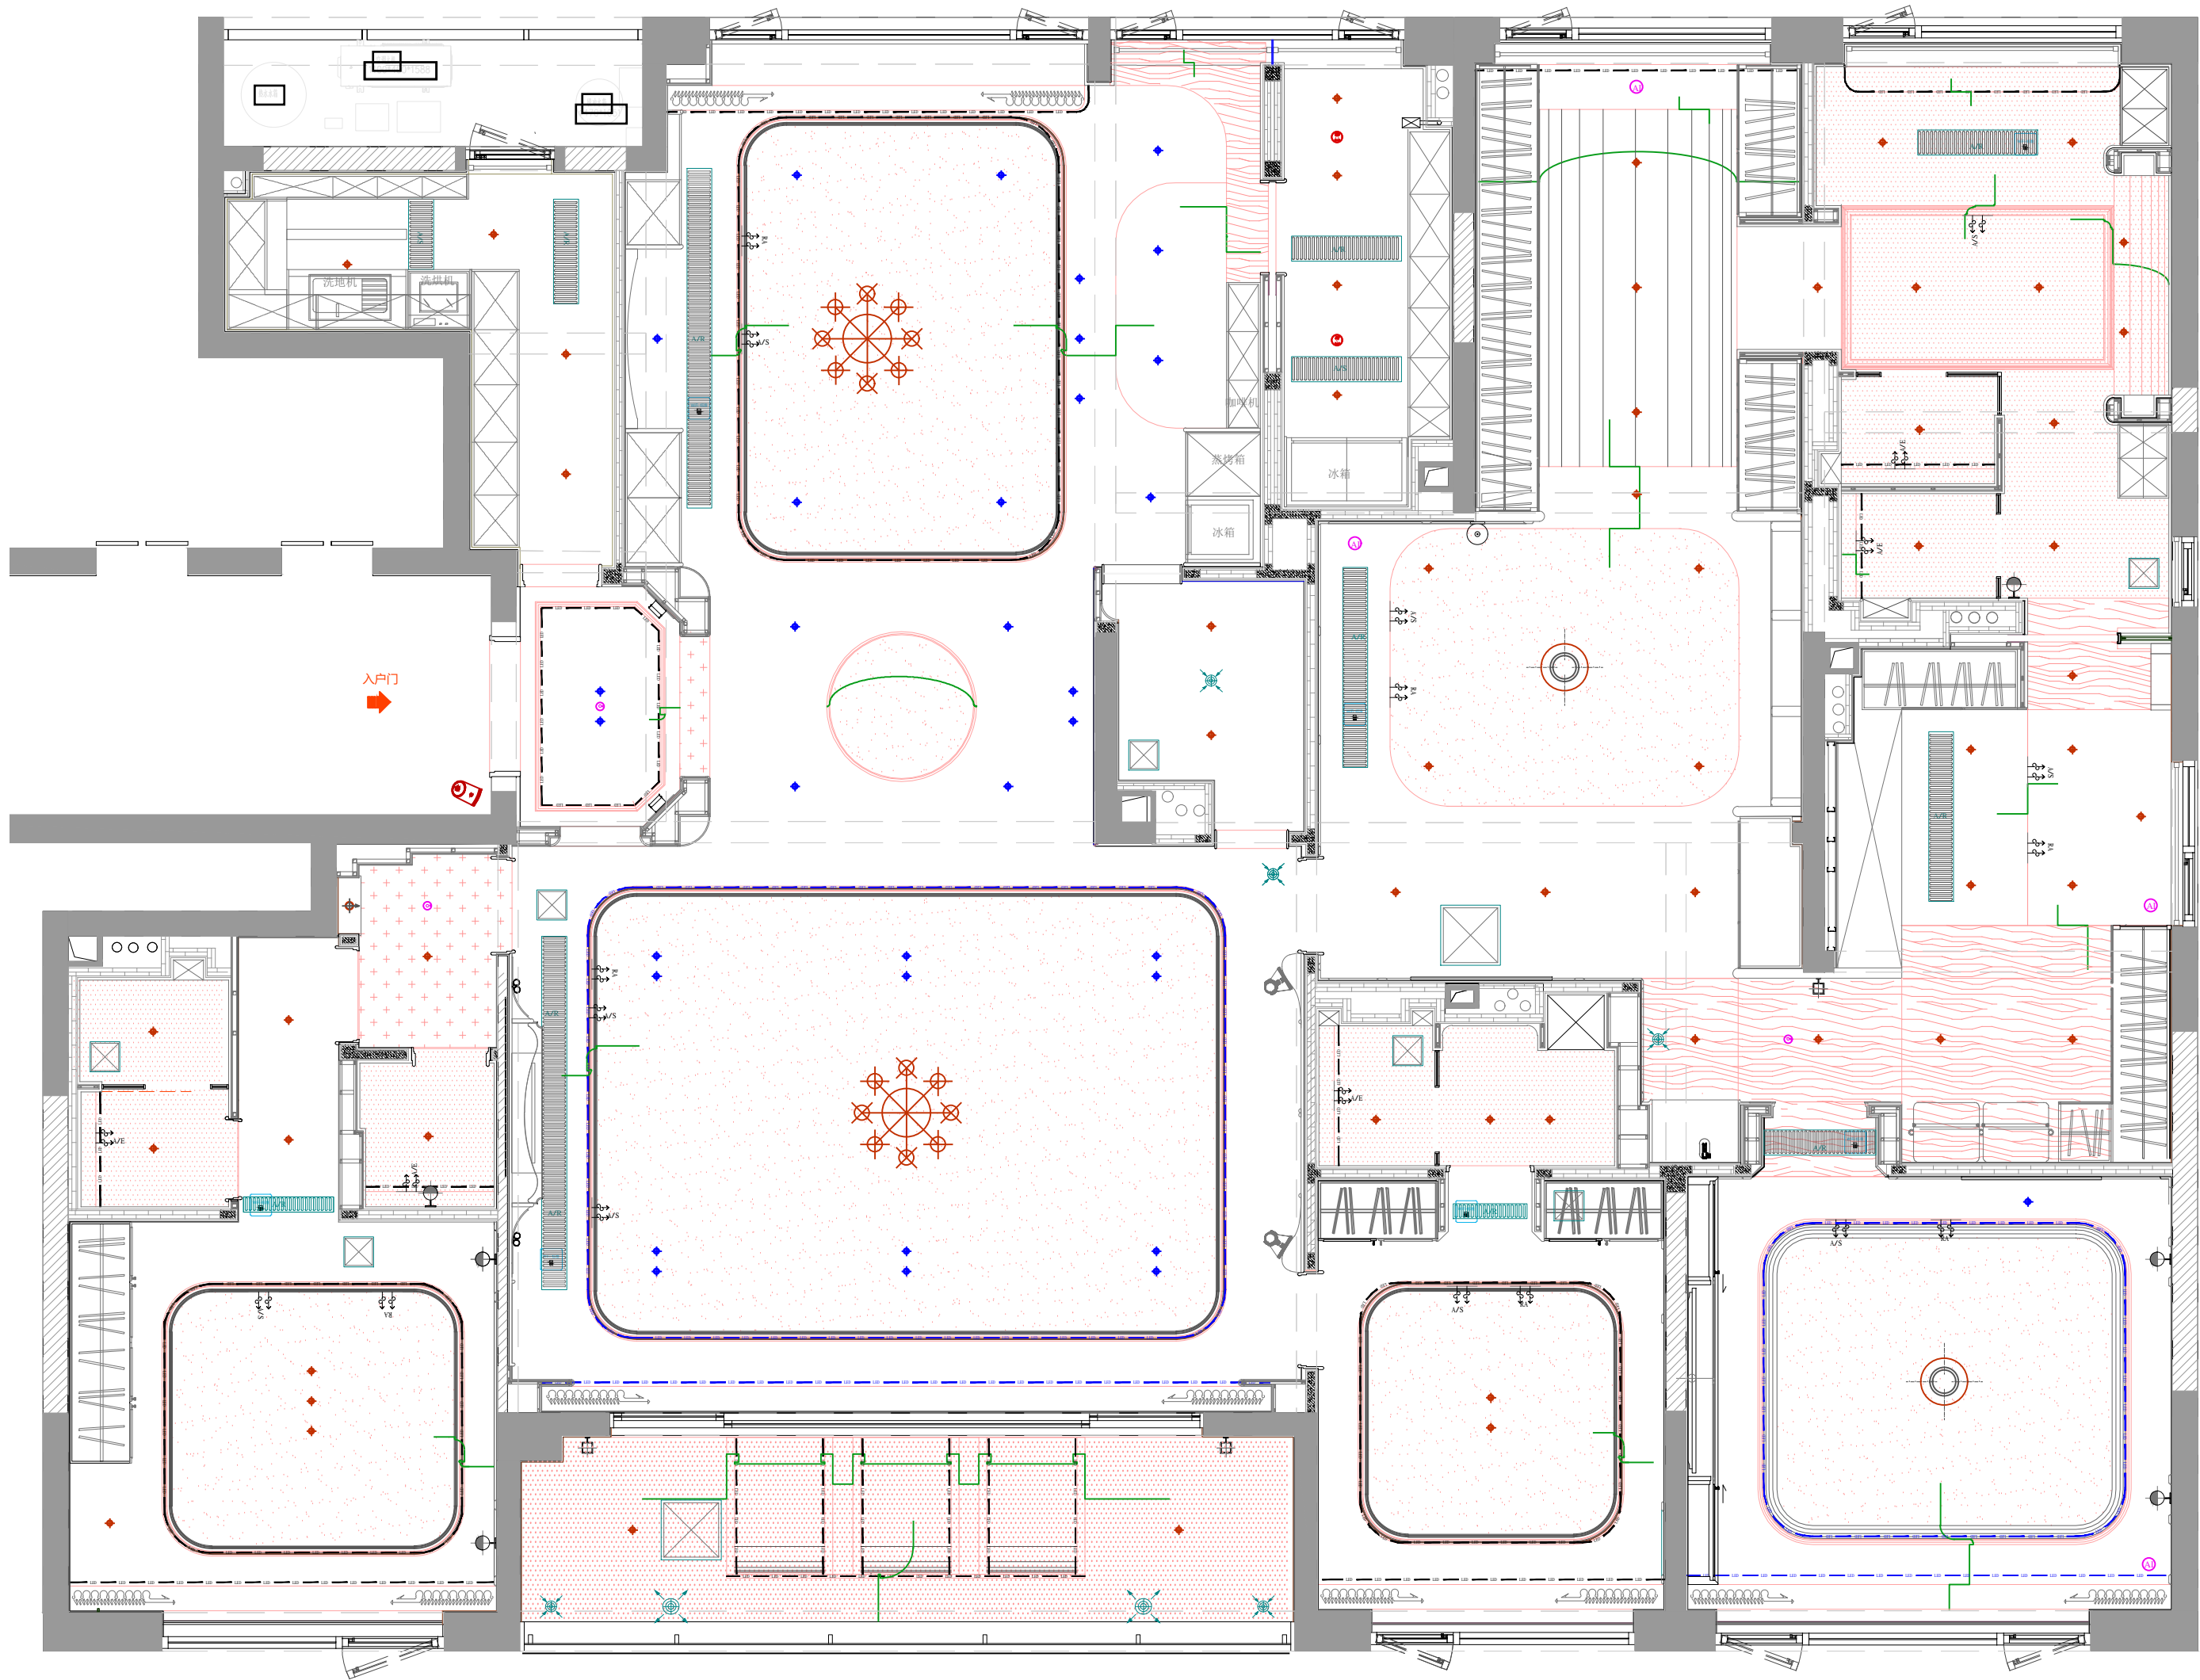

ELIBORN

M-机电点位		
图 例	名 称	备 注
	QW全屋WiFi子路由	放置空调风口内
	QW麦克体红外传感器	深86底盒
	qw伯恩传感器	86底盒
	三系1键智能开关	86底盒
	三系2键智能开关	86底盒
	三系3键智能开关面板	86底盒
	三系智能面板	86底盒
	海雀AI摄像头	吸顶安装
	家用可燃气体探测器	吸顶安装
	独立式光电感烟火灾探测器	吸顶安装

M-机电点位	
图 例	名 称
	百叶风口 (无特殊标注宽度为250mm)
	检修口 (无特殊标注边长为300mm)
	新风回风口
	新风出风口

日期
Date 2026.1.8

修订
Revisions

项目
Project

杭州 华岸府

Scale 1:60 @A2
比例

Drawing No.
图纸编号
CL.PL-4



Project No.
项目编号
© 2025

综合天花平面图

Scale比例 1:60@A2

注释
Notes

1. 本图纸尺寸如与现场尺寸有误差, 请施工人员与项目负责人联系。
2. 施工前施工人员应认真查阅此图, 如有不明确尺寸, 按现场测量为准。
3. 本图纸必须经甲乙双方认可并签字方可作为施工依据。

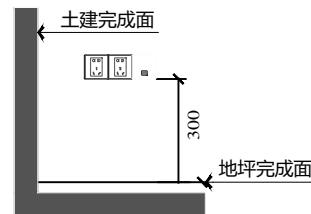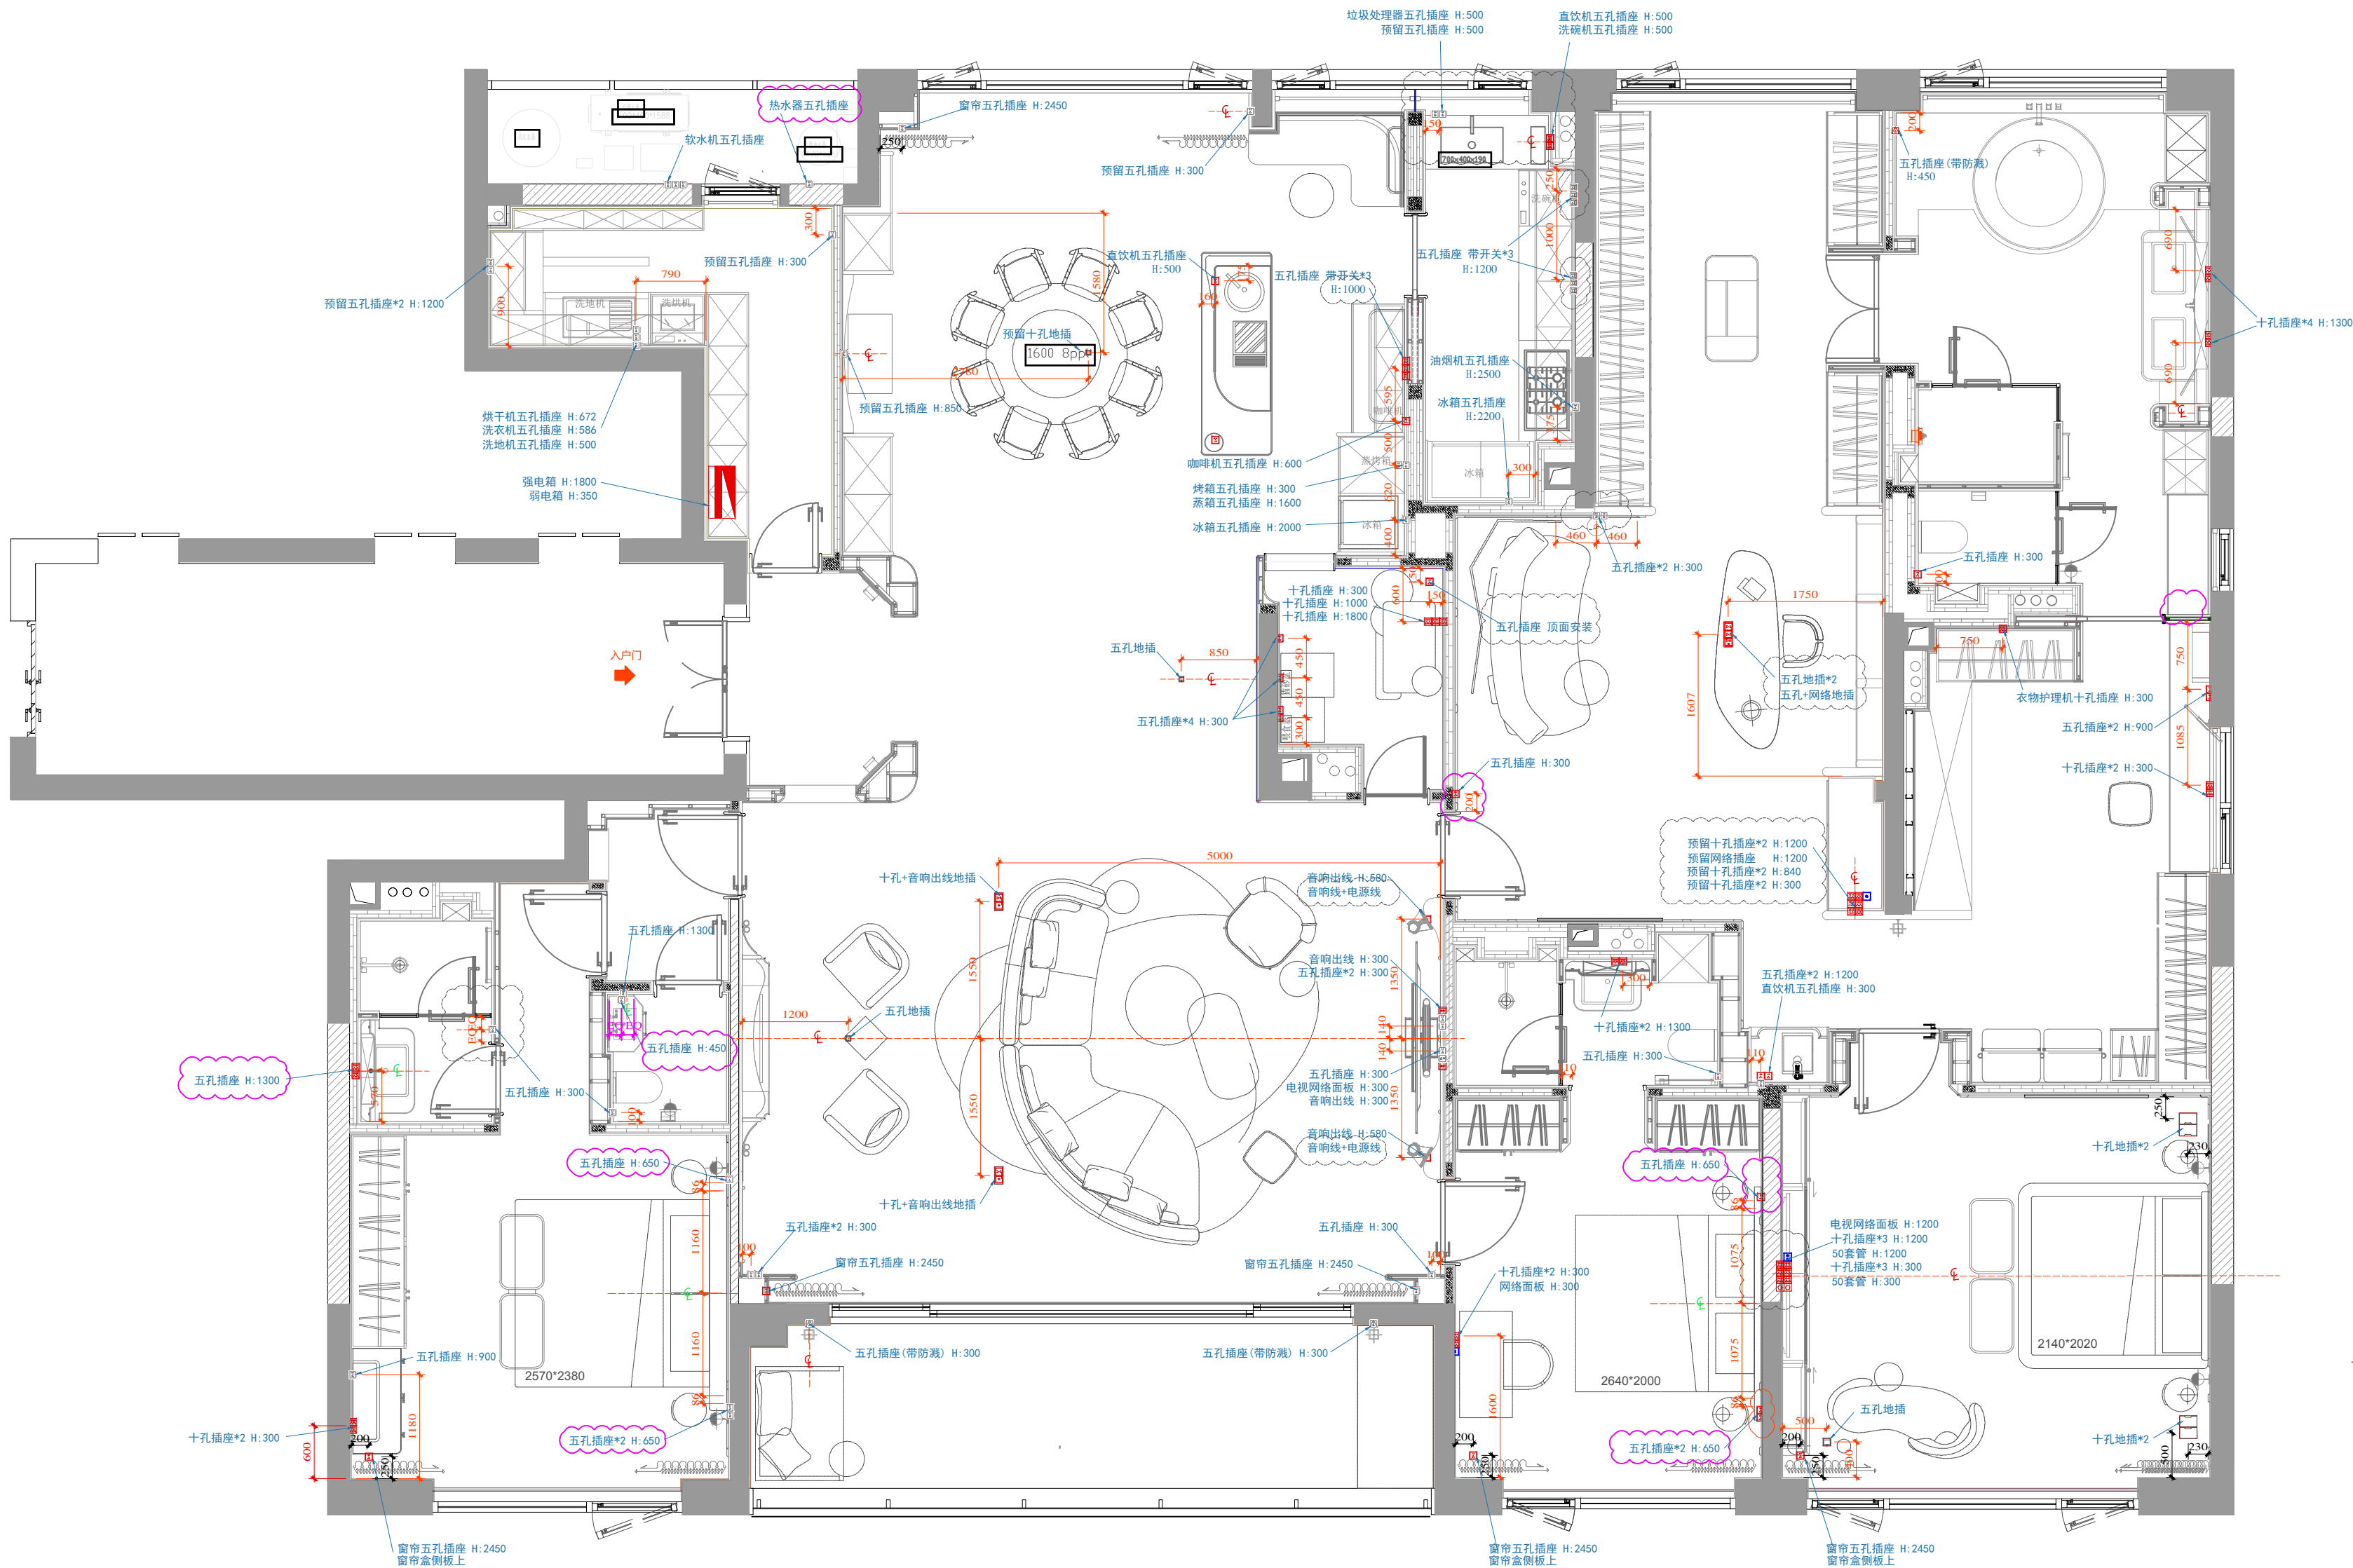

- 注意事项:
- 插座水平间距按土建成面算起,高度按地坪完成面算起。
 - 除图纸标注的高度外,其他均按表格高度安装。
 - 特殊插座需根据机电设备复核确认。
 - 厨房插座点位仅供参考,实际由橱柜公司深化提供。
 - 空调/热水器根据业主所购设备及现场实际情况预留所需电源。
 - 根据实际需要,预留监控、无线所需电源、网络。
 - 弱电电箱位置根据现场实际情况,施工人员与设计确定后方可实施。

M-机电点位	
图例	名称
	墙面二、三级插座(H=300mm)
	墙面二、三级插座带开关(H=300mm)
	墙面带USB、二、三级插座(H=300mm)
	二、三级防溅插座(H=300mm)
	地面二、三级插座
	网络插座
	网络+电视插座
	无线AP
	音响出线
	预留电源线头
	天花电源出线
	墙面电源出线
	地面电源出线
	强电控制箱(H=1800mm)
	弱电控制箱(H=350mm)
	监控摄像头
	门禁(H=1500)

日期
Date 2026.3.31

修订
Revisions

项目
Project

杭州 华岸府

Scale 比例 1:60 @A2

Drawing No.
图纸编号

EP.PL-02.1

Project No.
项目编号

© 2025

2026.4.27变更: 客卧、次卧床头插座开关面板位置调整。客卫镜柜插座高度调整。书房入口开关、插座位置调整。主卫窗边插座取消。

注: 地插需要根据最终地坪排版图微调位置。

强弱电点位分析图

注释
Notes

- 本图纸尺寸如与现场尺寸有误差, 请施工人员与项目负责人联系。
- 施工前施工人员应认真查阅此图, 如有不明确尺寸, 按现场测量为准。
- 本图纸必须经甲乙双方认可并签字方可作为施工依据。

Scale比例 1:60 @A2

注意事项:

- 1.插座水平间距按土建完成面算起,高度按地坪完成面算起。
- 2.除图纸标注的高度外,其他均按表格高度安装。
- 3.特殊插座需根据机电设备复核确定。
- 4.厨房插座点位仅供参考,实际由橱柜公司深化提供。
- 5.空调/热水器根据业主所购设备及现场实际情况预留电源电源。
- 6.根据实际需要,预留监控、无线所需电源、网络。
- 7.强电配电箱位置根据现场实际情况,施工方与设计师确定后方可实施。

M-机电点位	
图 例	名 称
	墙面二、三级插座(H=300mm)
	墙面二、三级插座带开关(H=300mm)
	墙面带USB、二、三级插座(H=300mm)
	二、三级防溅插座(H=300mm)
	地面二、三级插座
	网络插座
	网络+电视插座
	无线AP
	音响出线
	预留电源线头
	天花电源出线
	墙面电源出线
	地面电源出线
	强电控制箱(H=1800mm)
	弱电控制箱(H=350mm)
	监控摄像头
	门禁 (H=1500)


Revisions



Project

Scale 1:60 @A2
比例Drawing No.
 图纸编号Project No.
项目编号

© 2025

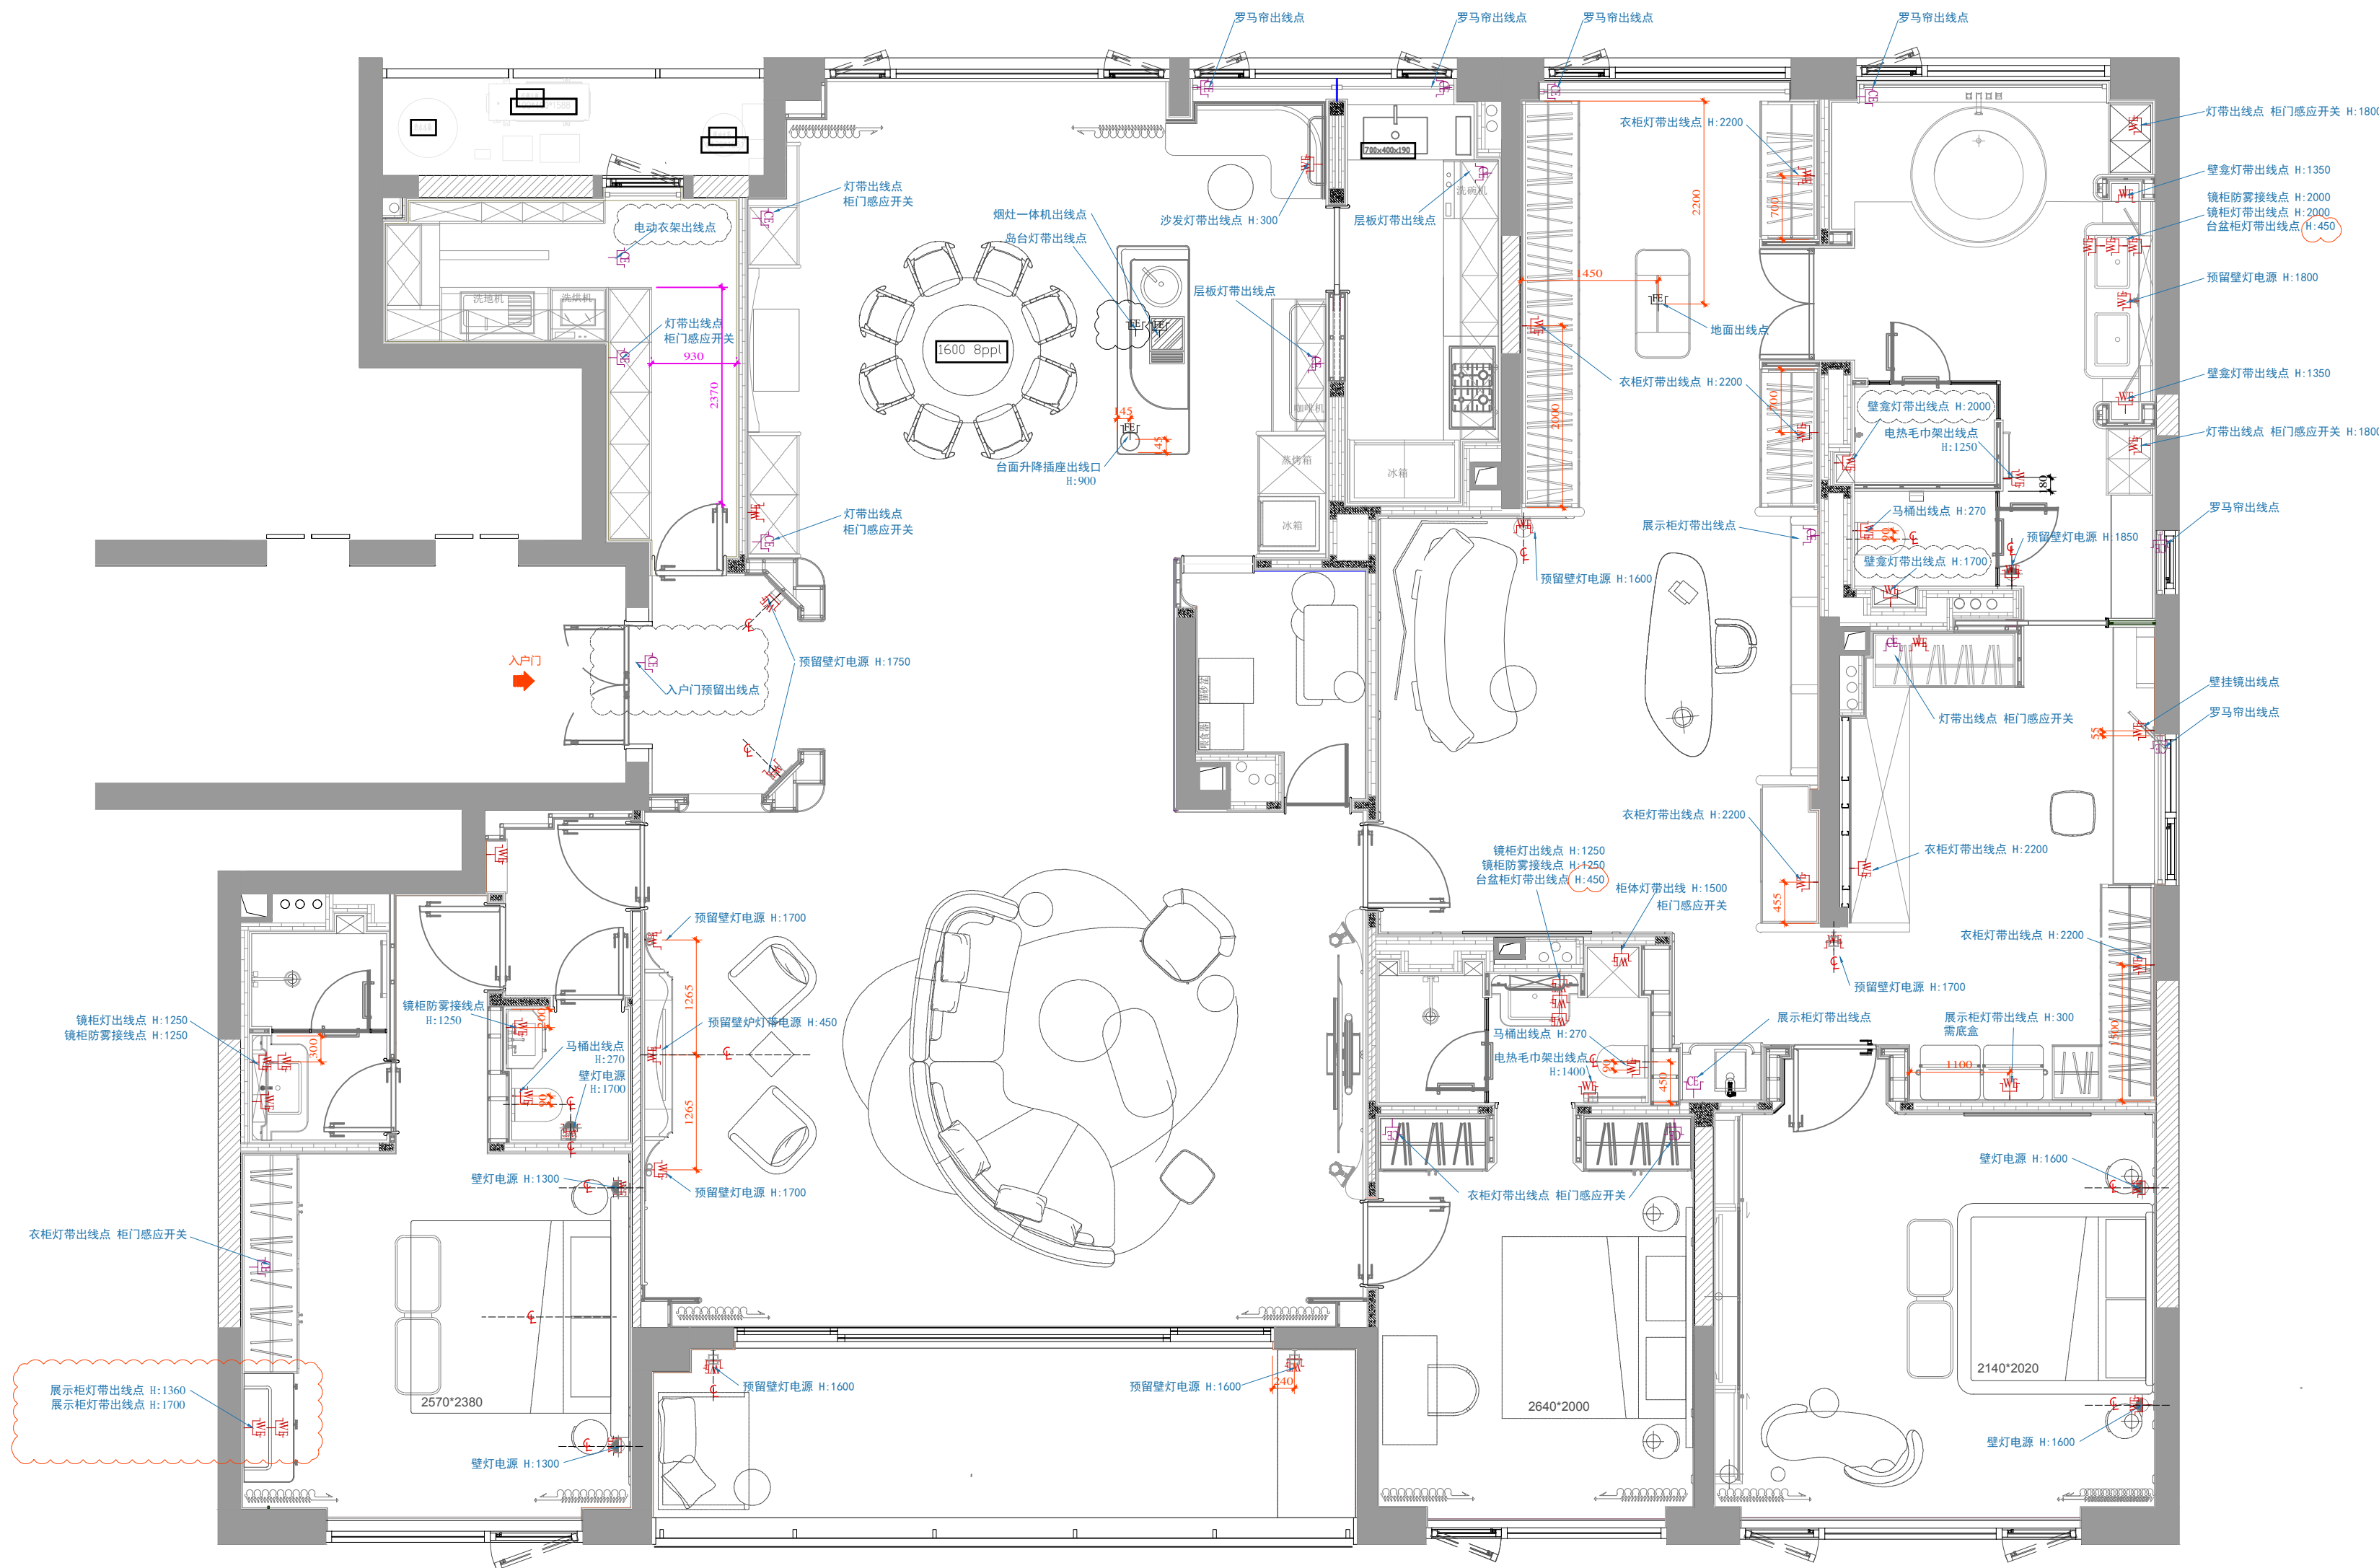



2026.4.23变更：客卧展示柜灯带出线点高度调整，主卫、次卫台盆柜出线点高度调整。

天花墙面出线点位布置图

Scale比例 1:60 @A2

注释
Notes

1. 本图纸尺寸如与现场尺寸有误, 请施工人员与项目负责人联系。
2. 施工前施工人员应认真查阅此图, 如有不明确尺寸, 按现场测量为准。
3. 本图纸必须经甲乙双方认可并签字方可作为施工依据。

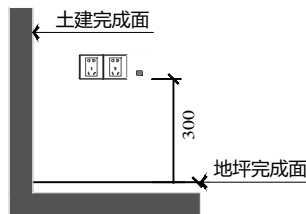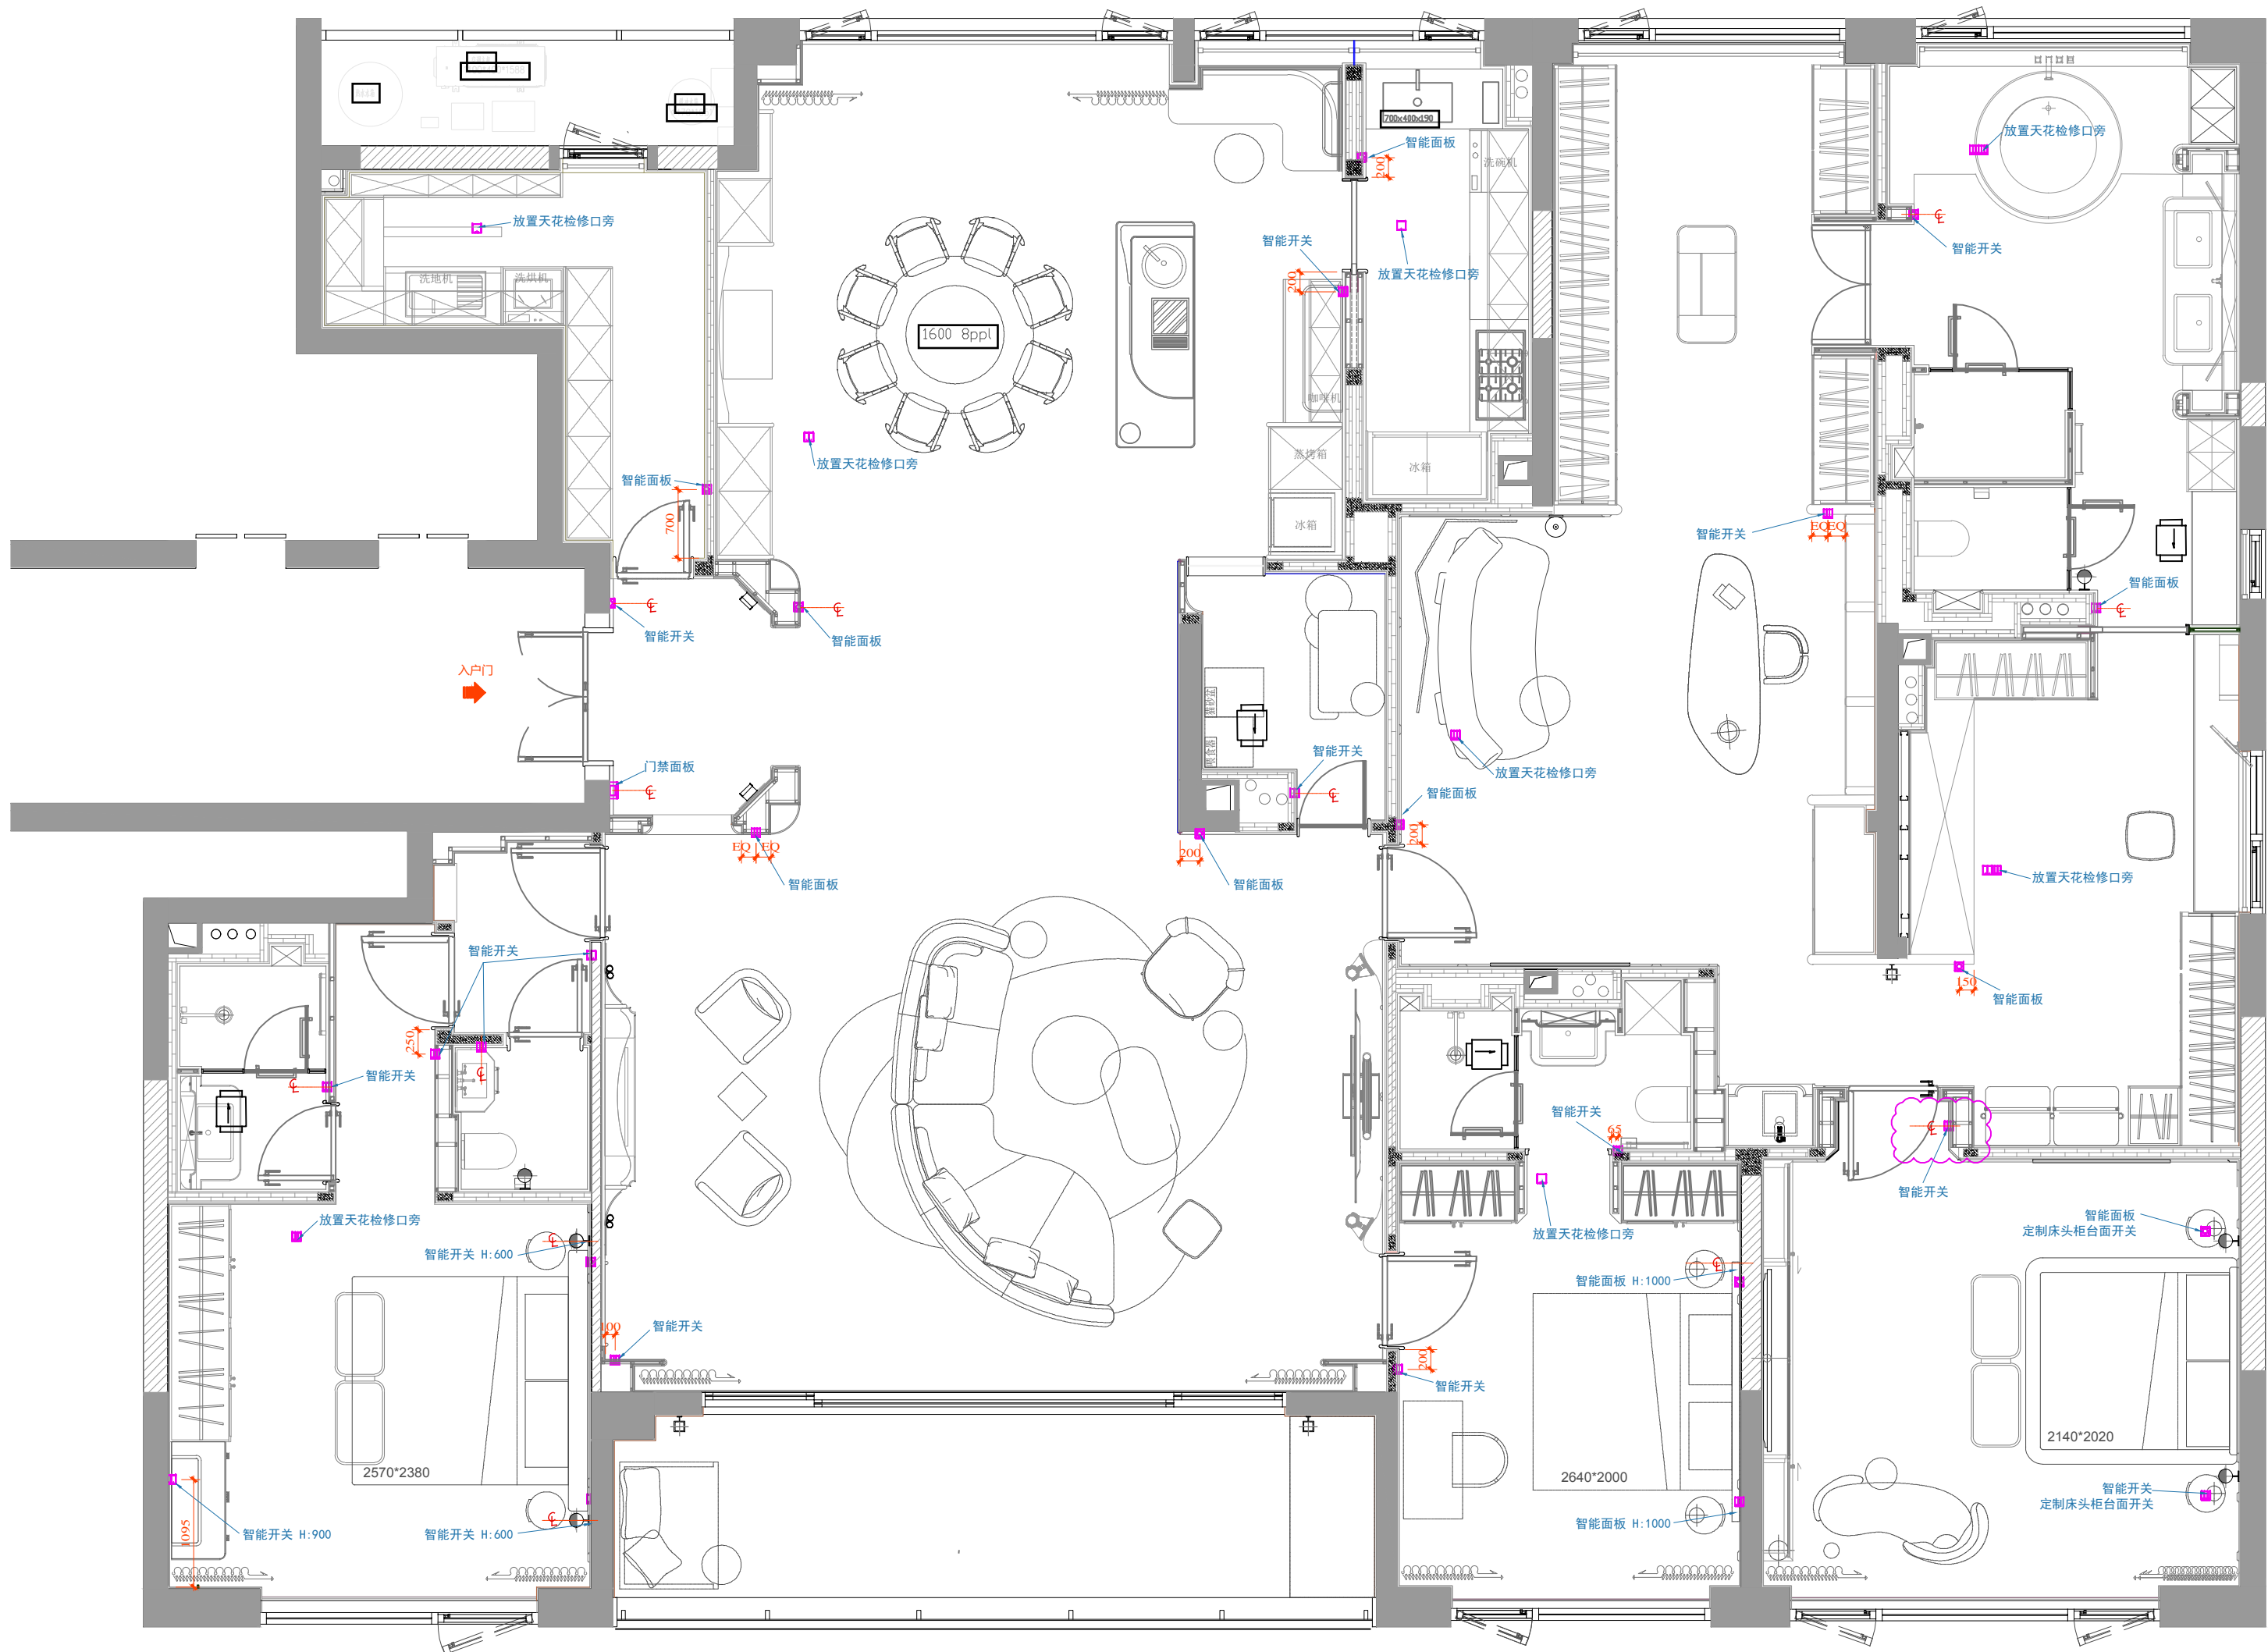

注意事项:
1.插座水平间距按土建完成面算起,高度按地坪完成面算起。
2.除图纸标注的高度外,其他均按表格高度安装。
3.特殊插座需根据机电设备复核确认。
4.厨房插座点位仅供参考,实际由橱柜公司深化提供。
5.空调/热水器根据业主所购设备及现场实际情况预留所需电源。
6.根据实际需要,预留监控、无线所需电源、网络。
7.弱电箱位置根据现场实际情况,施工人员与设计确定后方可实施。

M-机电点位		
图例	名称	备注
	QW全屋WiFi子路由	放置空调风口内
	QW麦乐壳红外传感器	深86底盒
	qw白恩传感器	86底盒
	三系1键智能开关	86底盒
	三系2键智能开关	86底盒
	三系3键智能开关面板	86底盒
	三系智能面板	86底盒
	海雀AI摄像头	吸顶安装
	家用可燃气体探测器	吸顶安装
	独立式光电感烟火灾探测器	吸顶安装

日期
Date 2026.2.6

修订
Revisions



项目
Project

杭州 华岸府

Scale 比例 1:60 @A2

Drawing No.
图纸编号

EP.PL-03.1

Project No.
项目编号

© 2025

开关及面板点位分析图

Scale比例 1:60 @A2

注释

Notes

1. 本图纸尺寸如与现场尺寸有误, 请施工人员与项目负责人联系。
2. 施工前施工人员应认真查阅此图, 如有不明确尺寸, 按现场测量为准。
3. 本图纸必须经甲乙双方认可并签字方可作为施工依据。