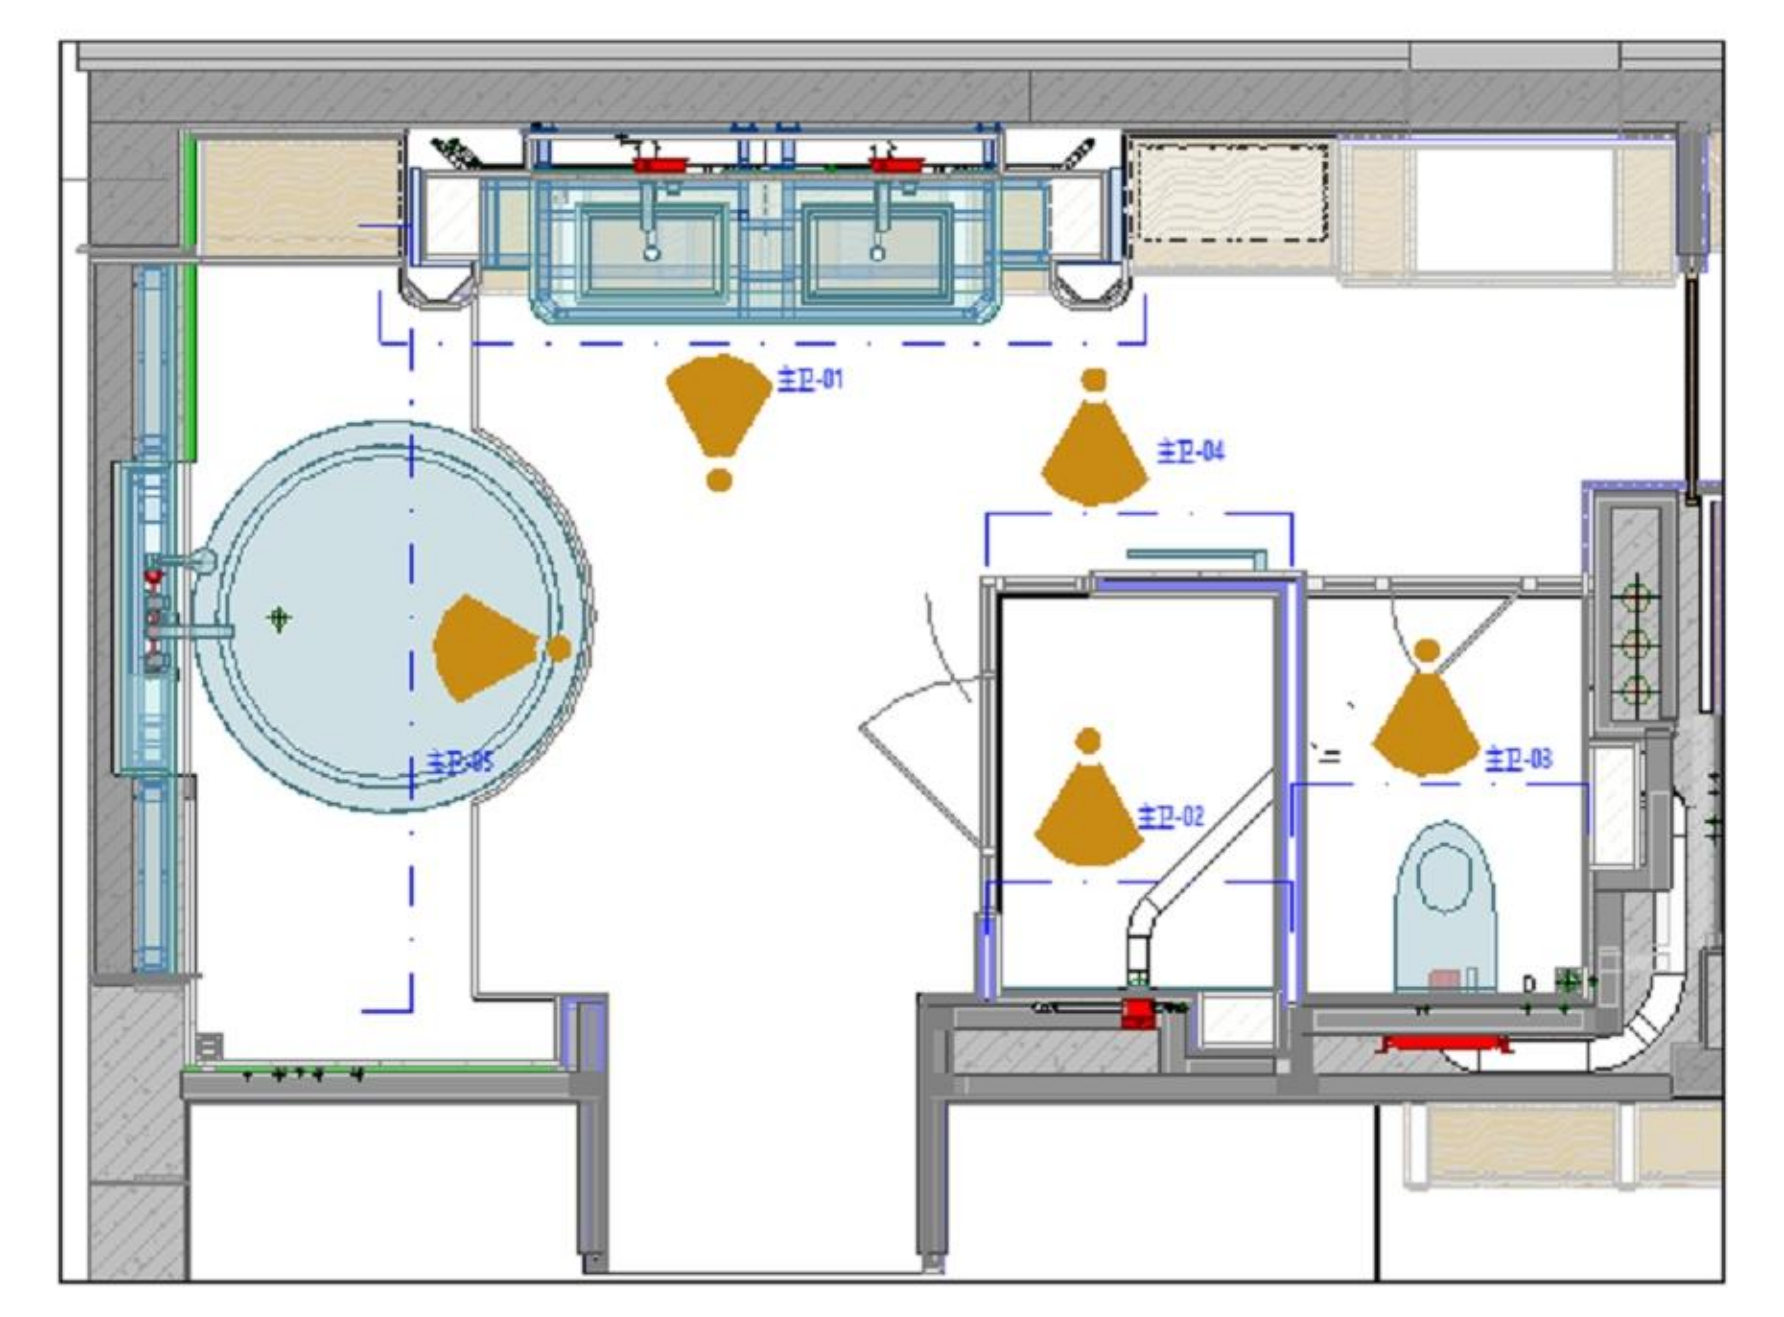
主卫-01
主卫-02
主卫-03
主卫-04
主卫-05

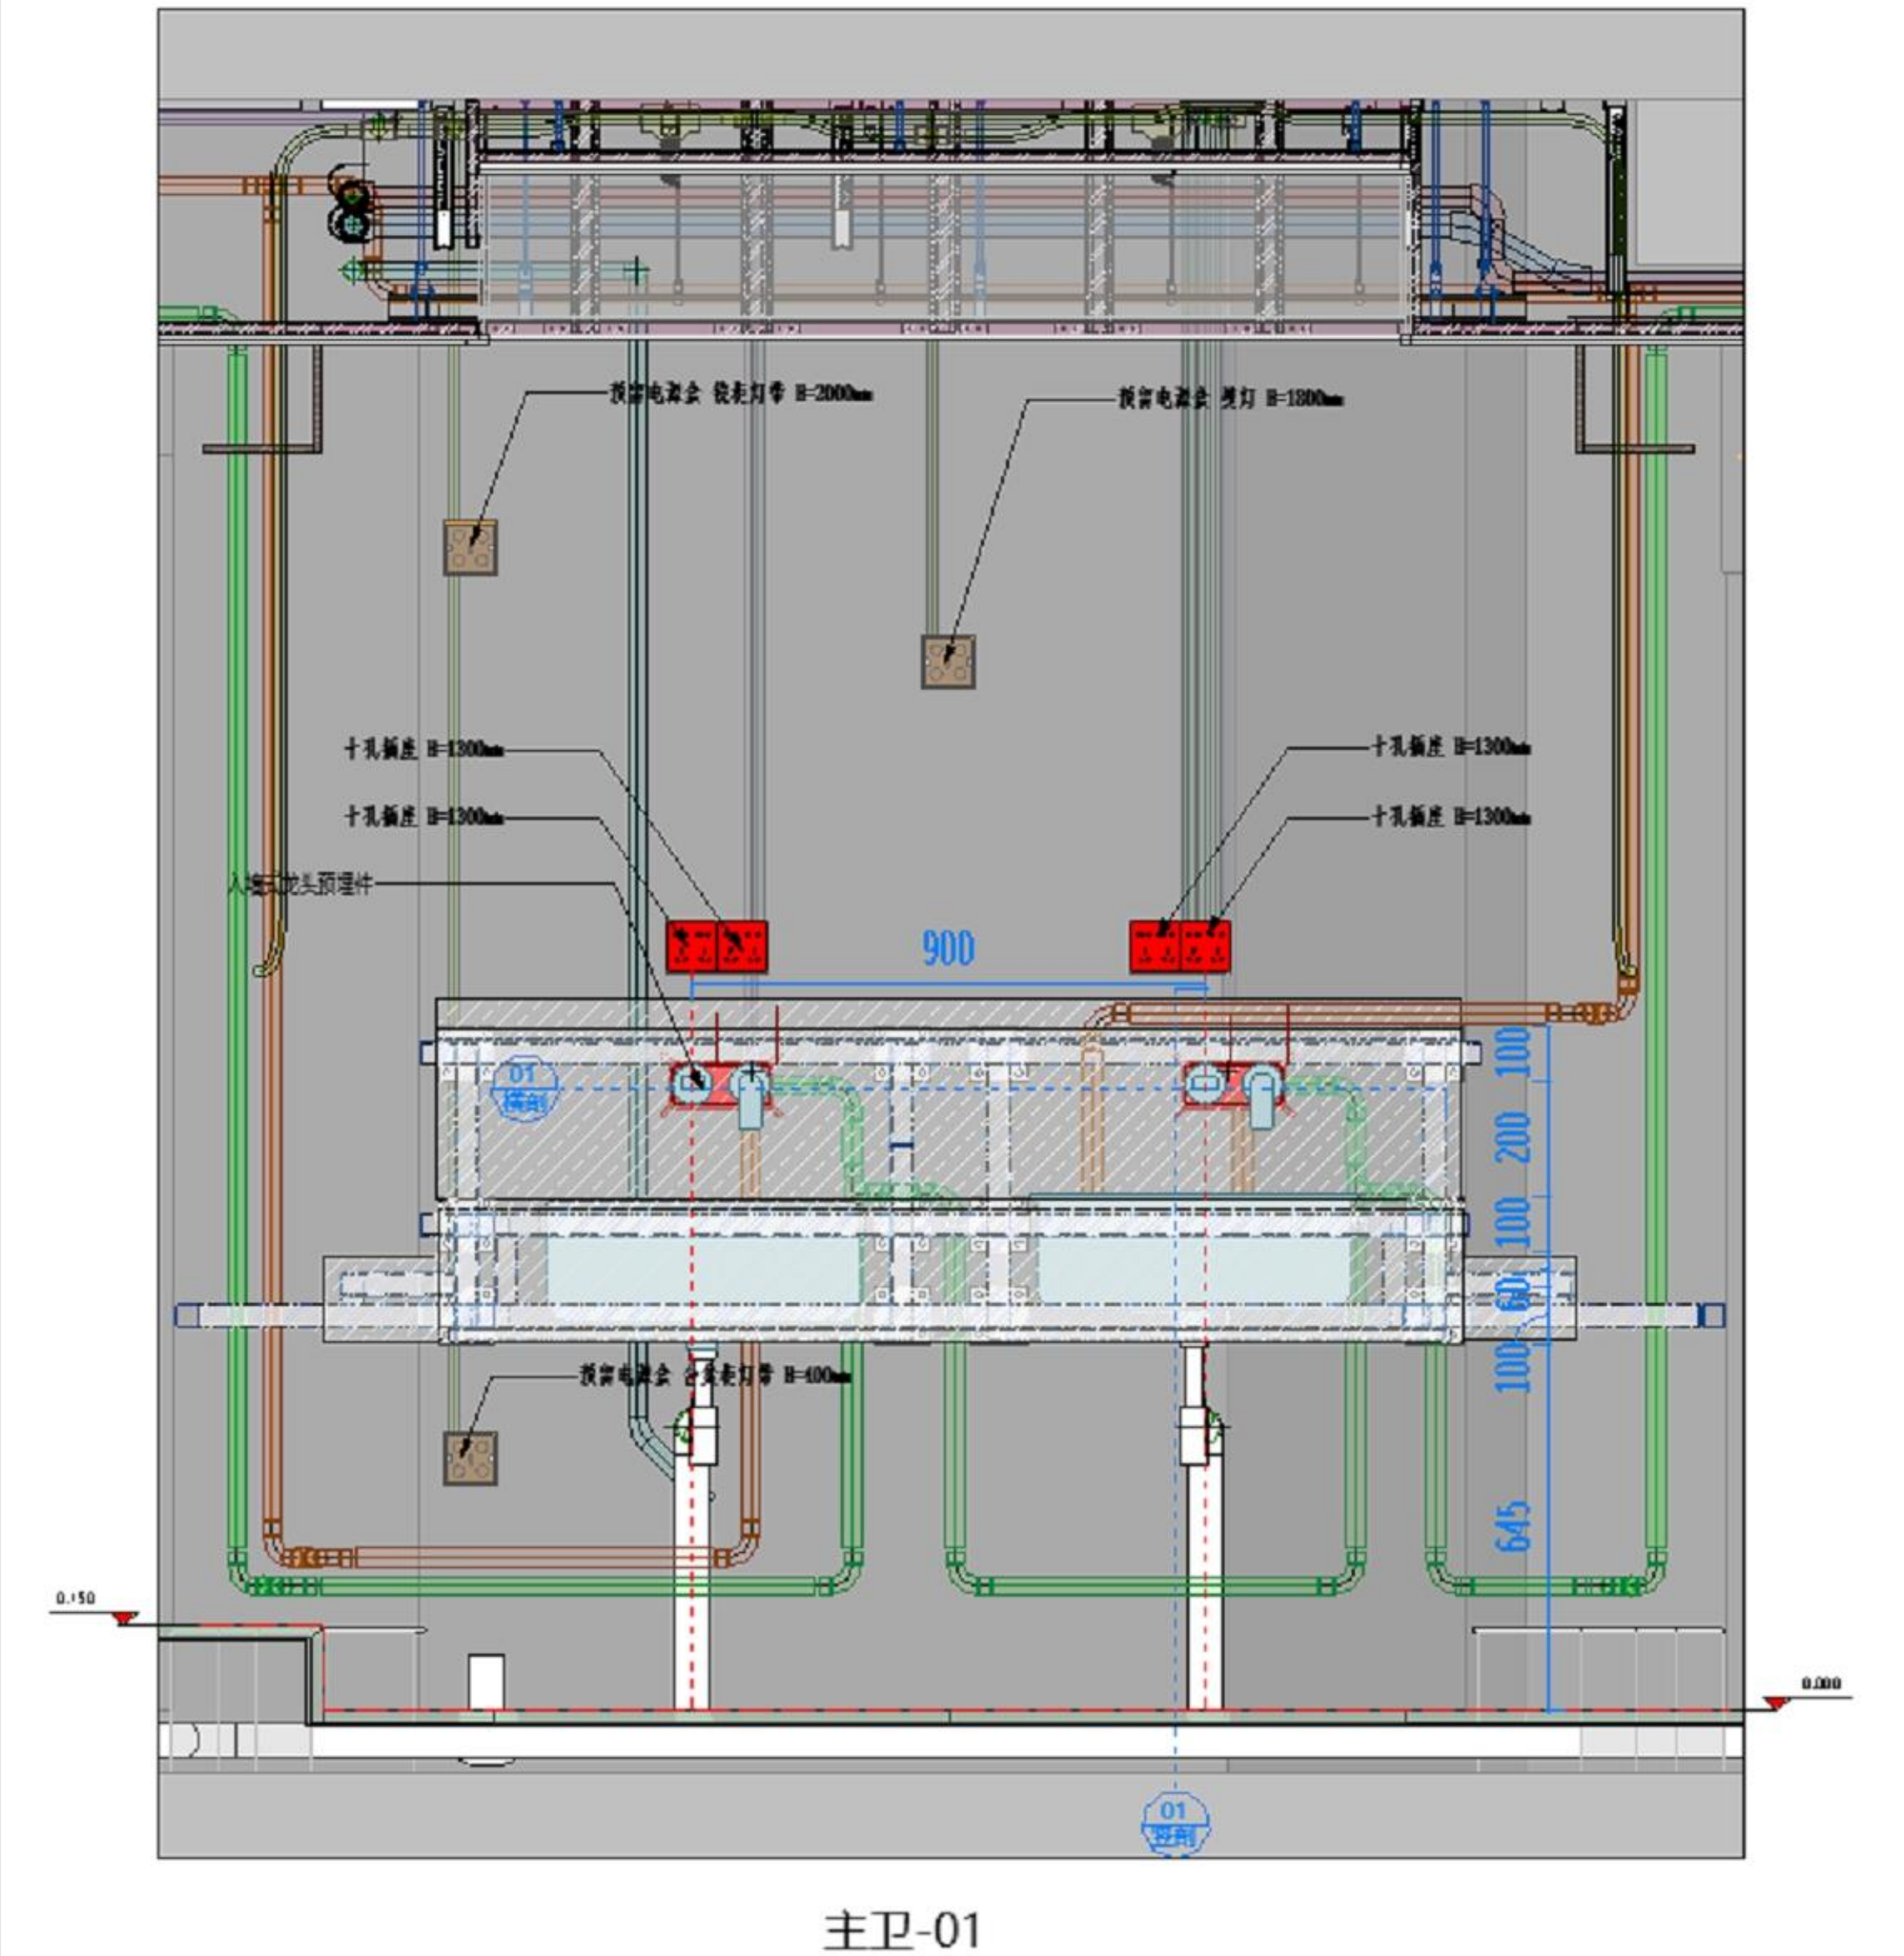
900
100
200
100
100
645
01

主卫-01

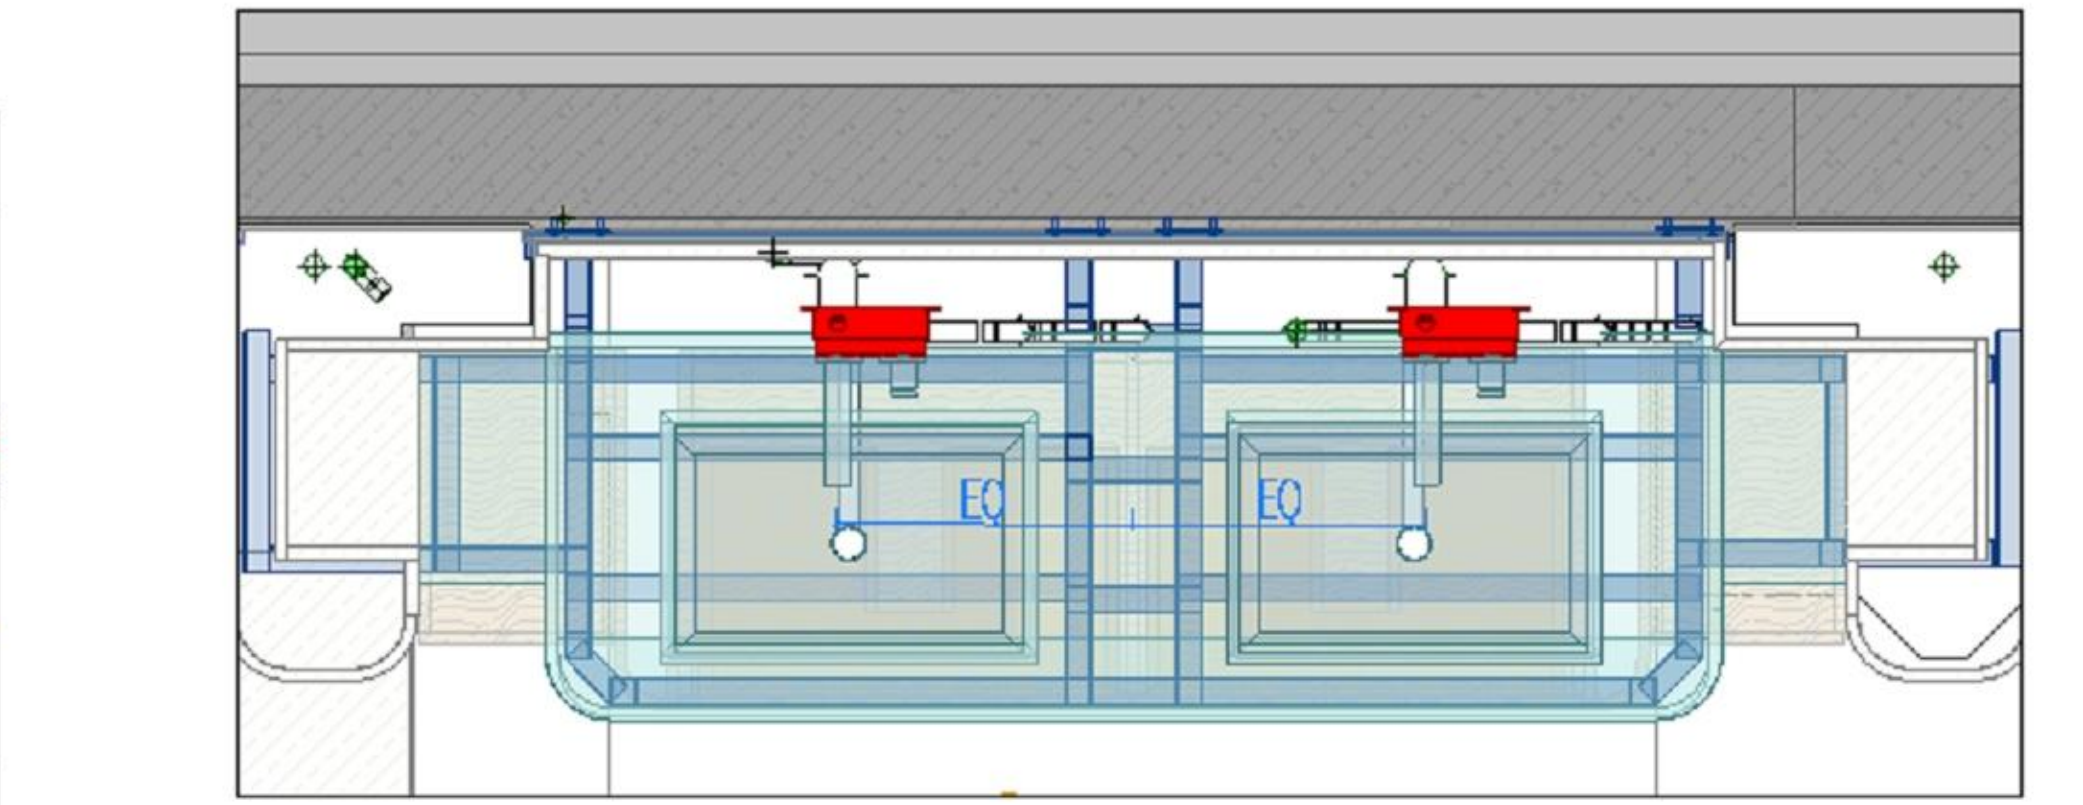

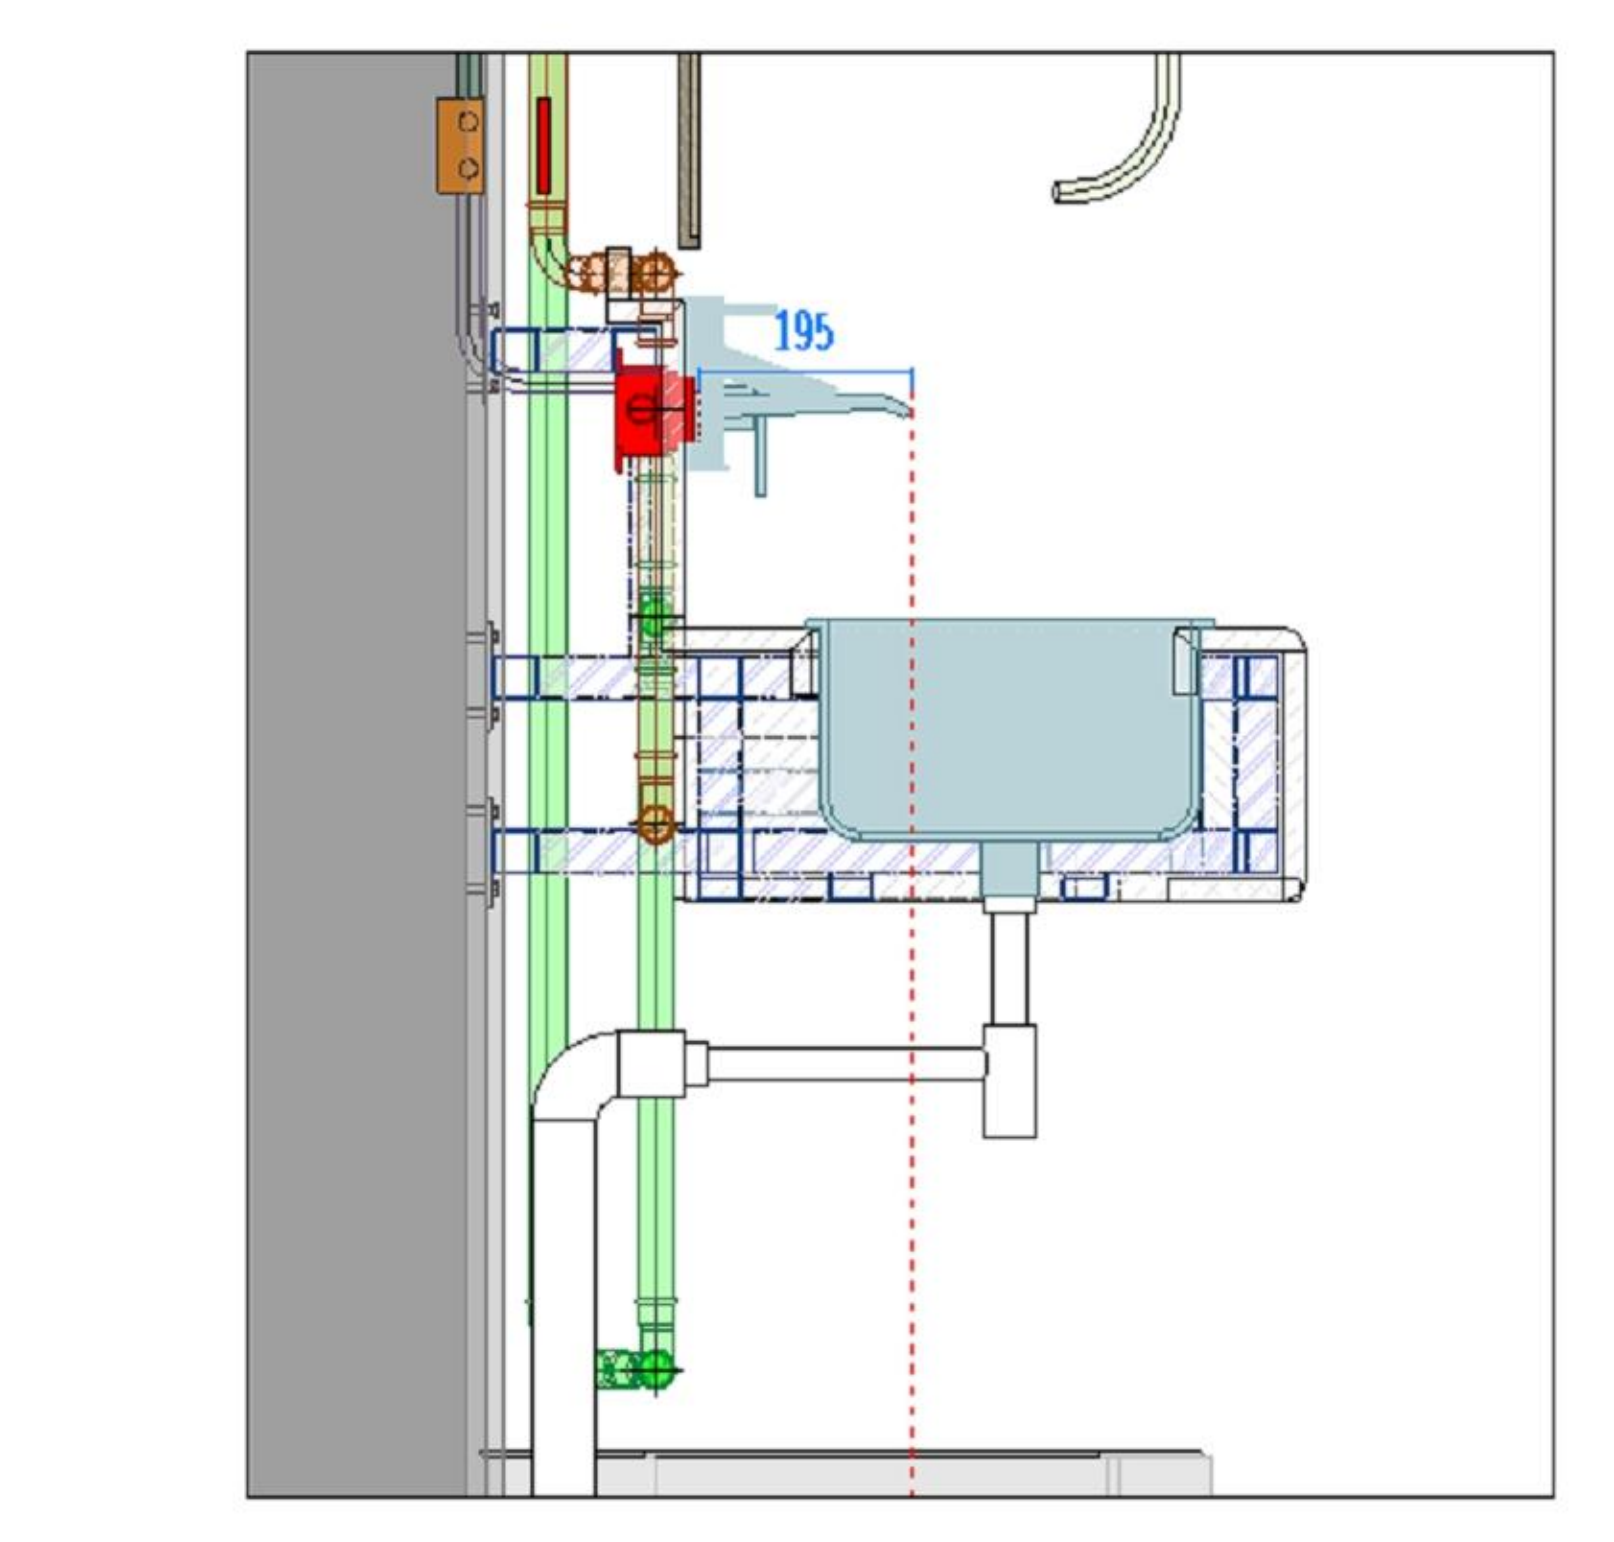

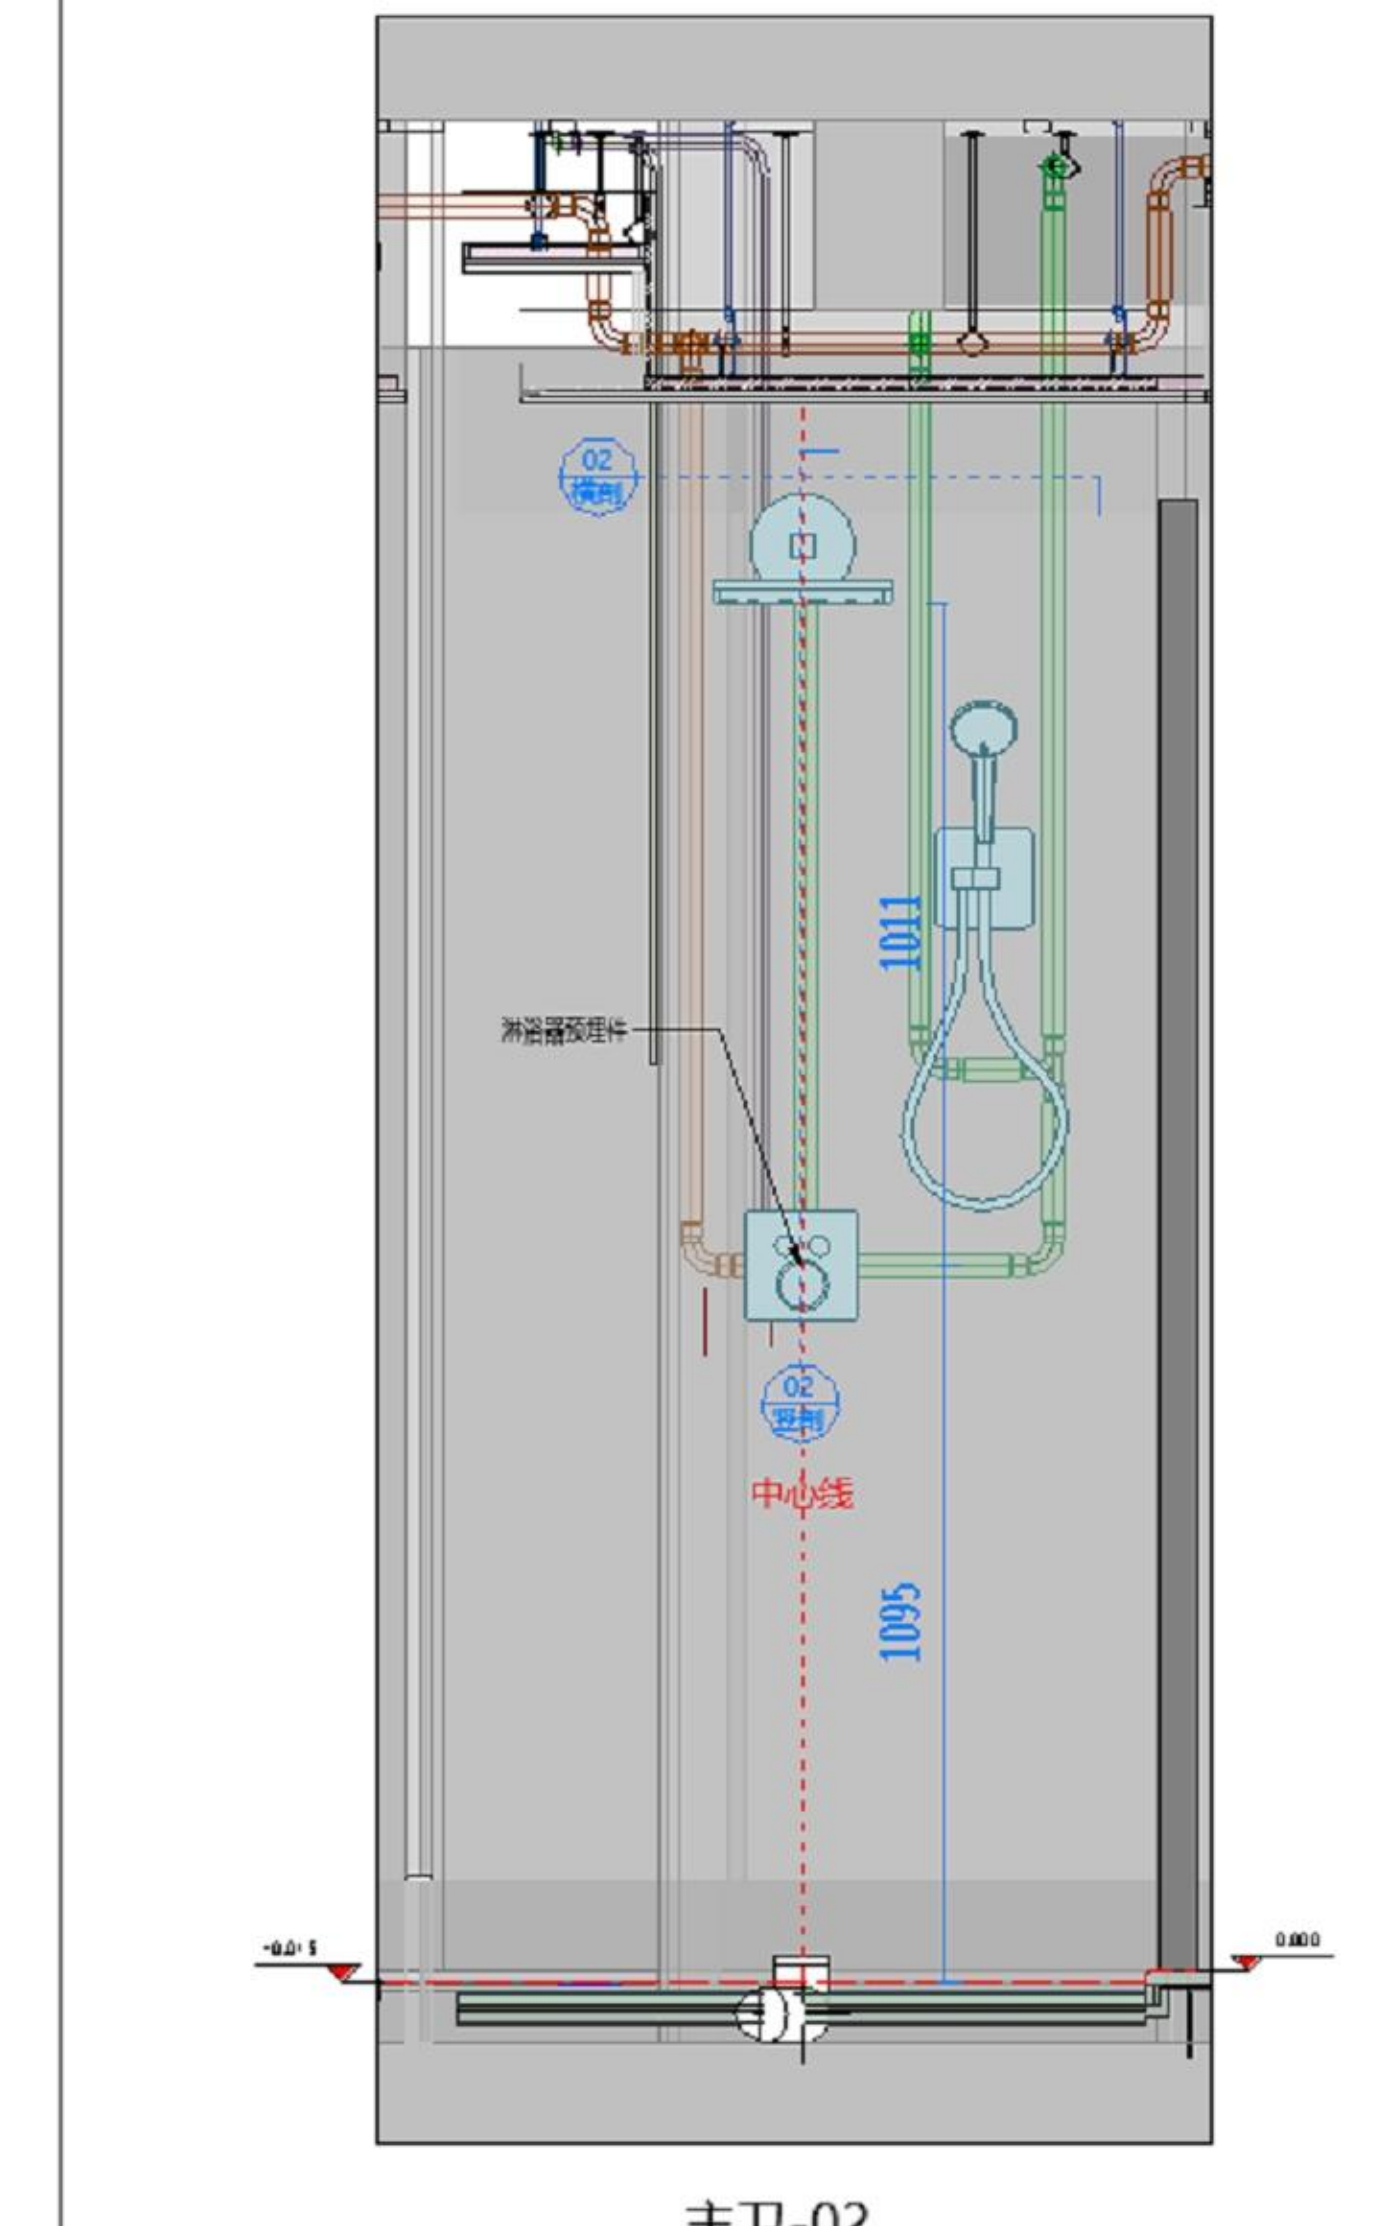
02
1011
1095
中心线

主卫-02

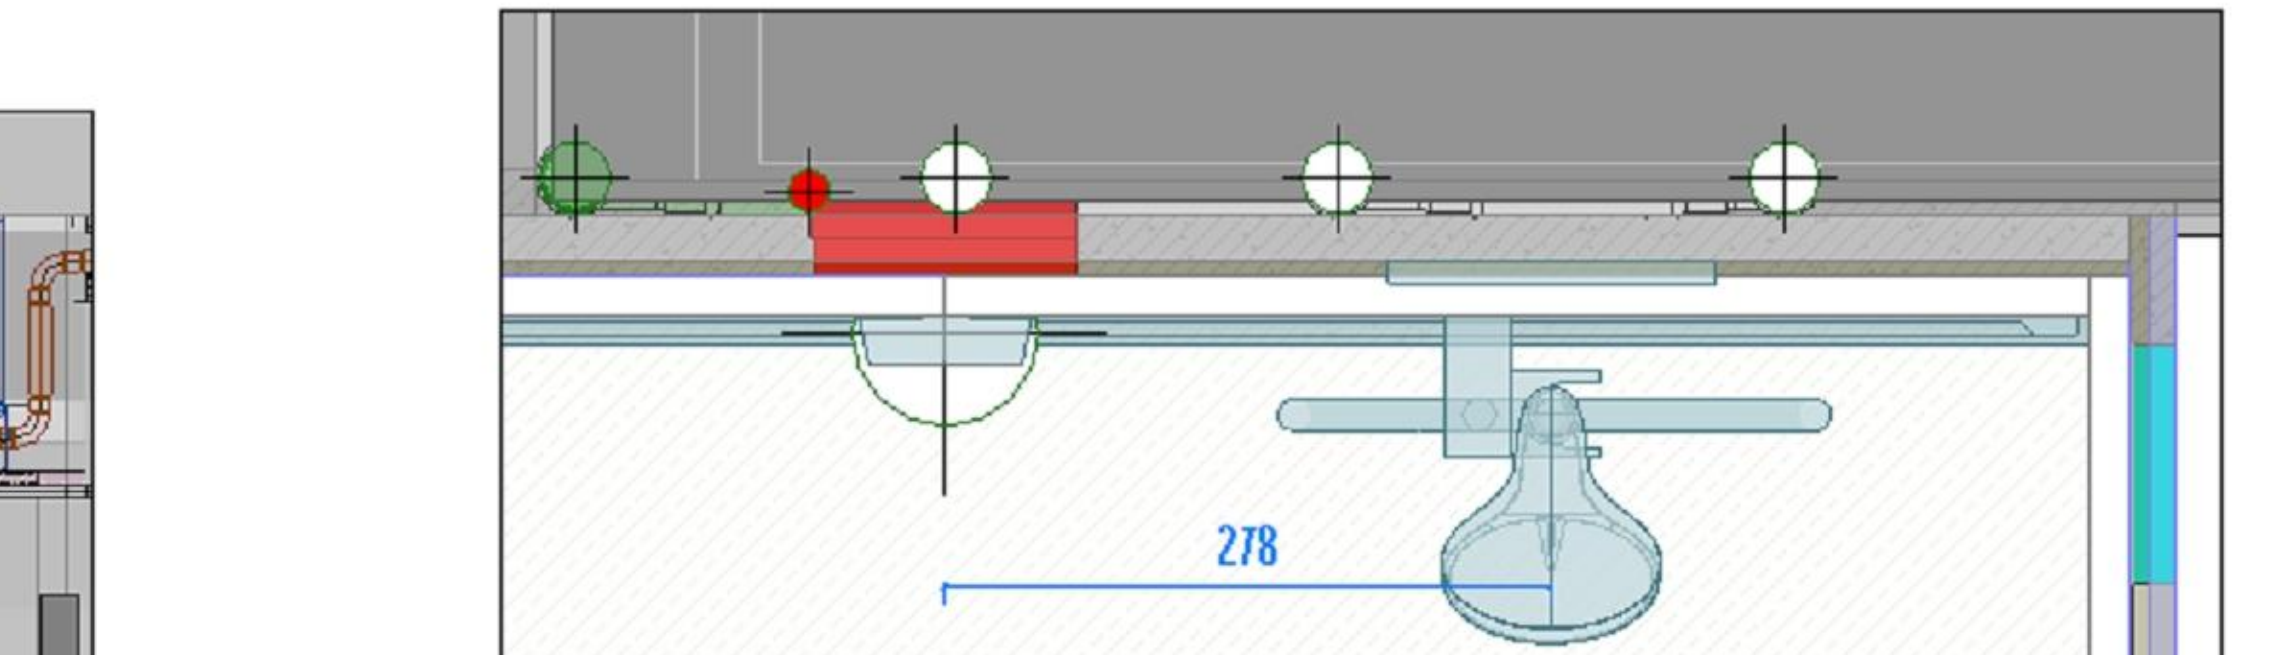

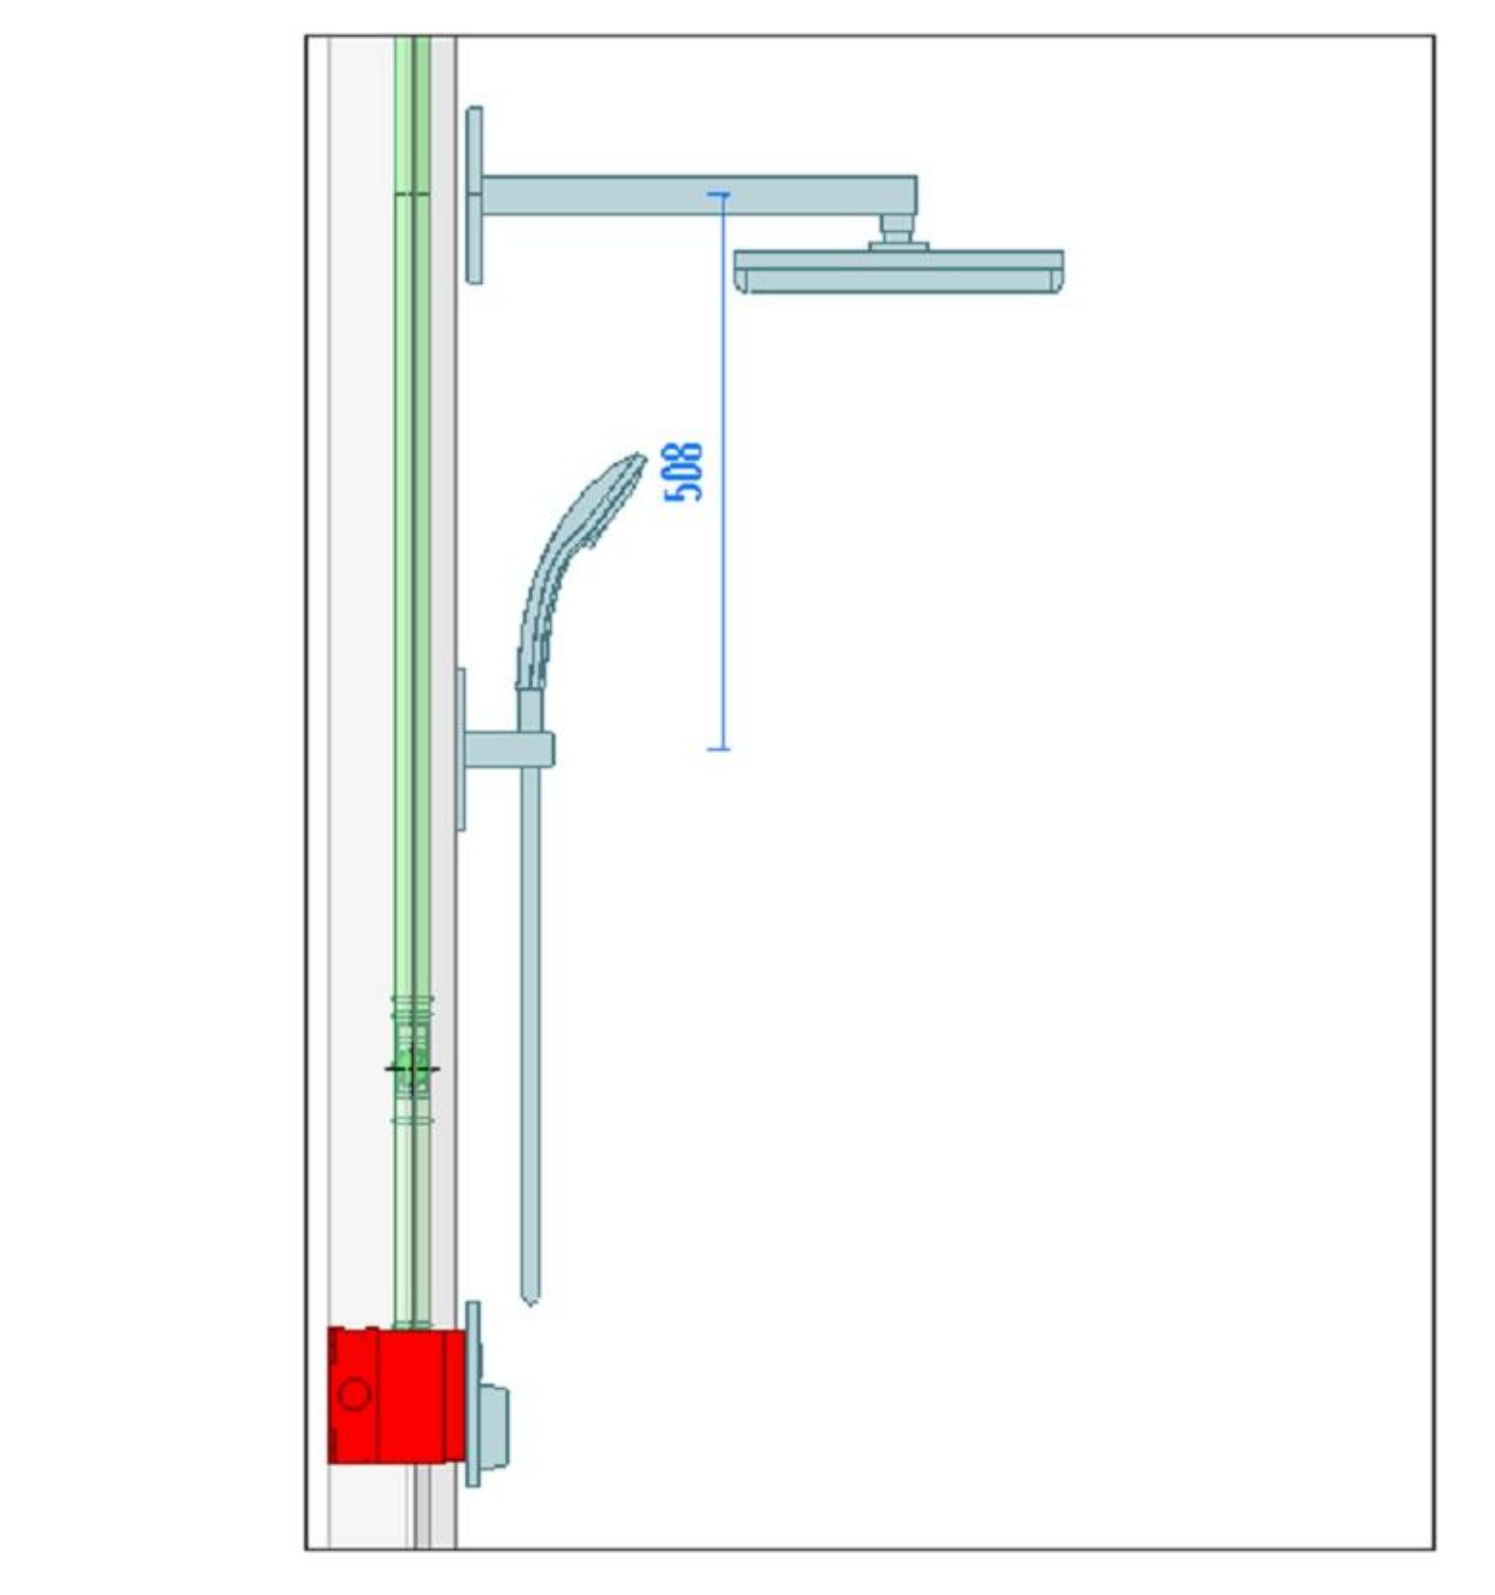

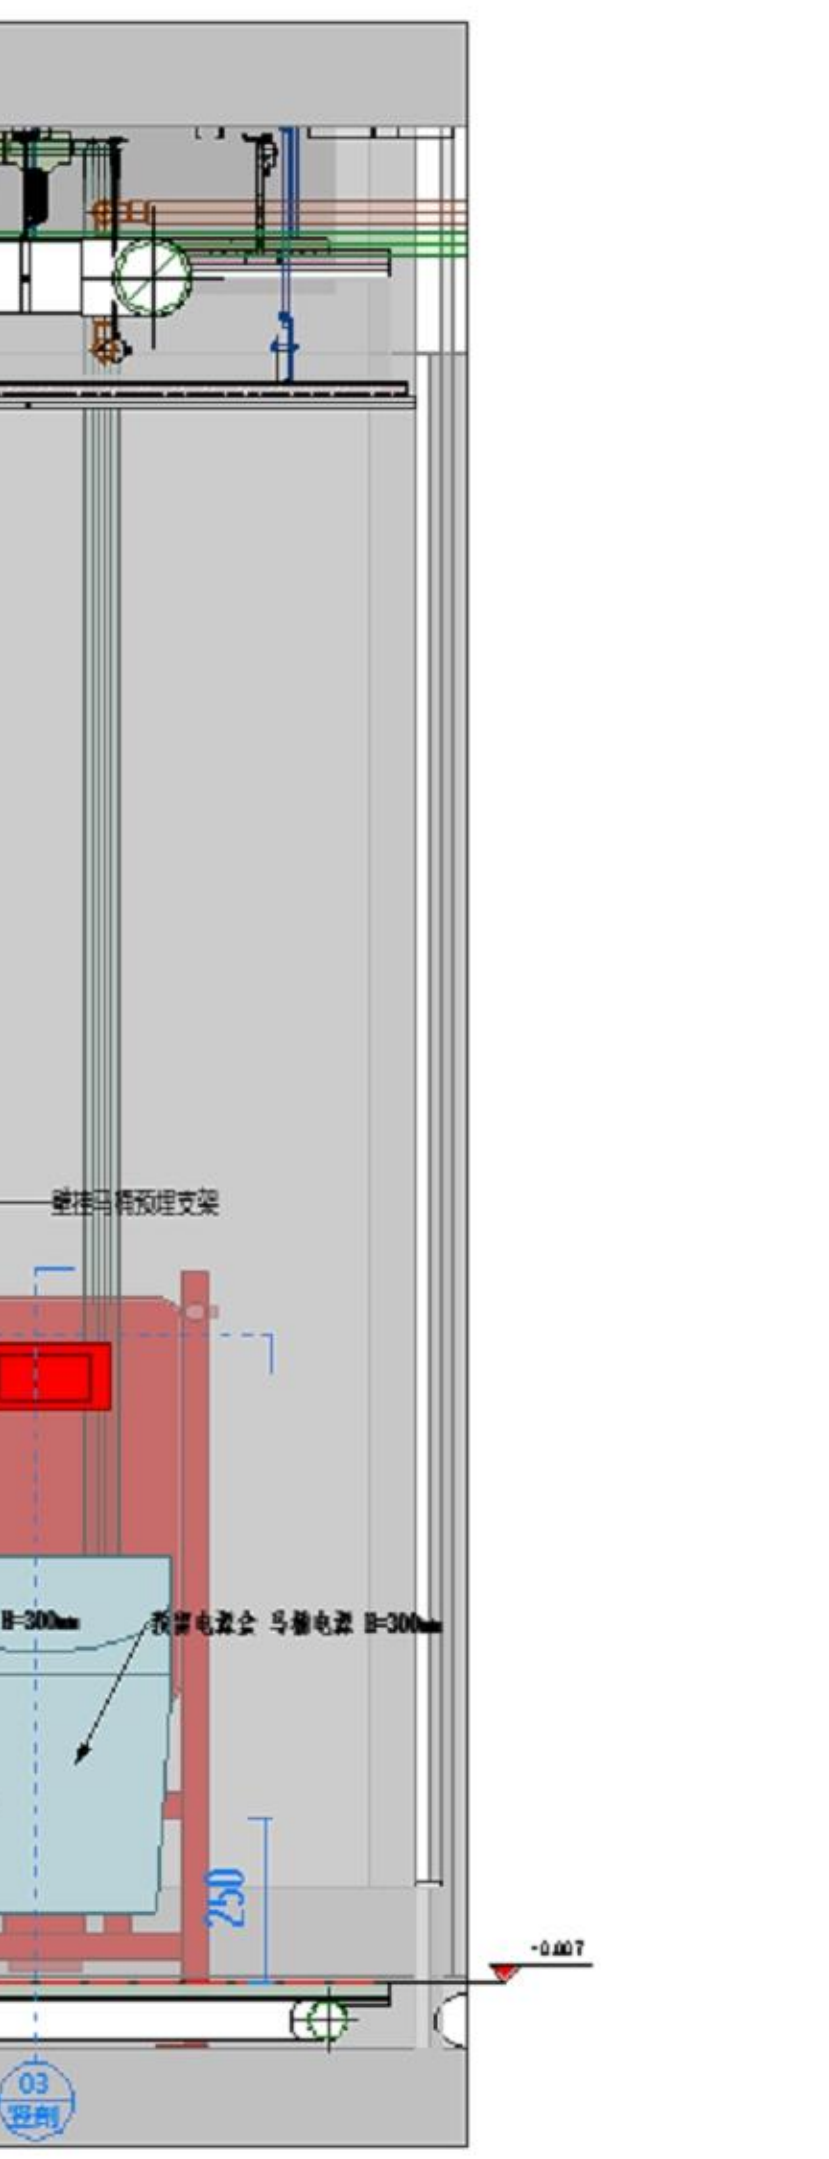

主卫-03

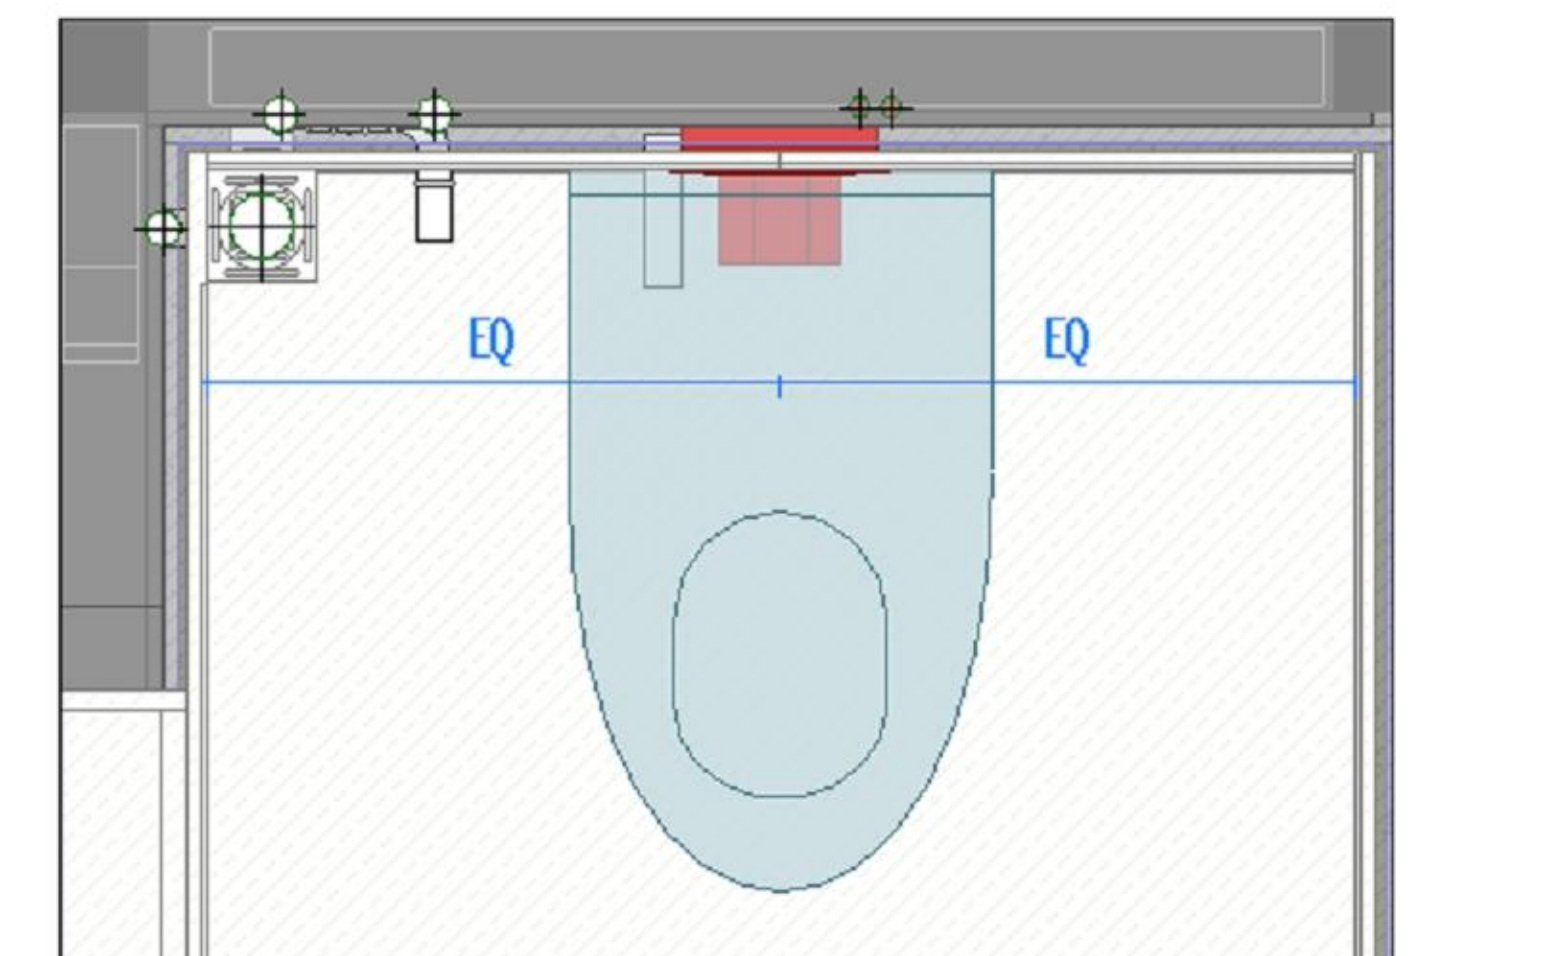

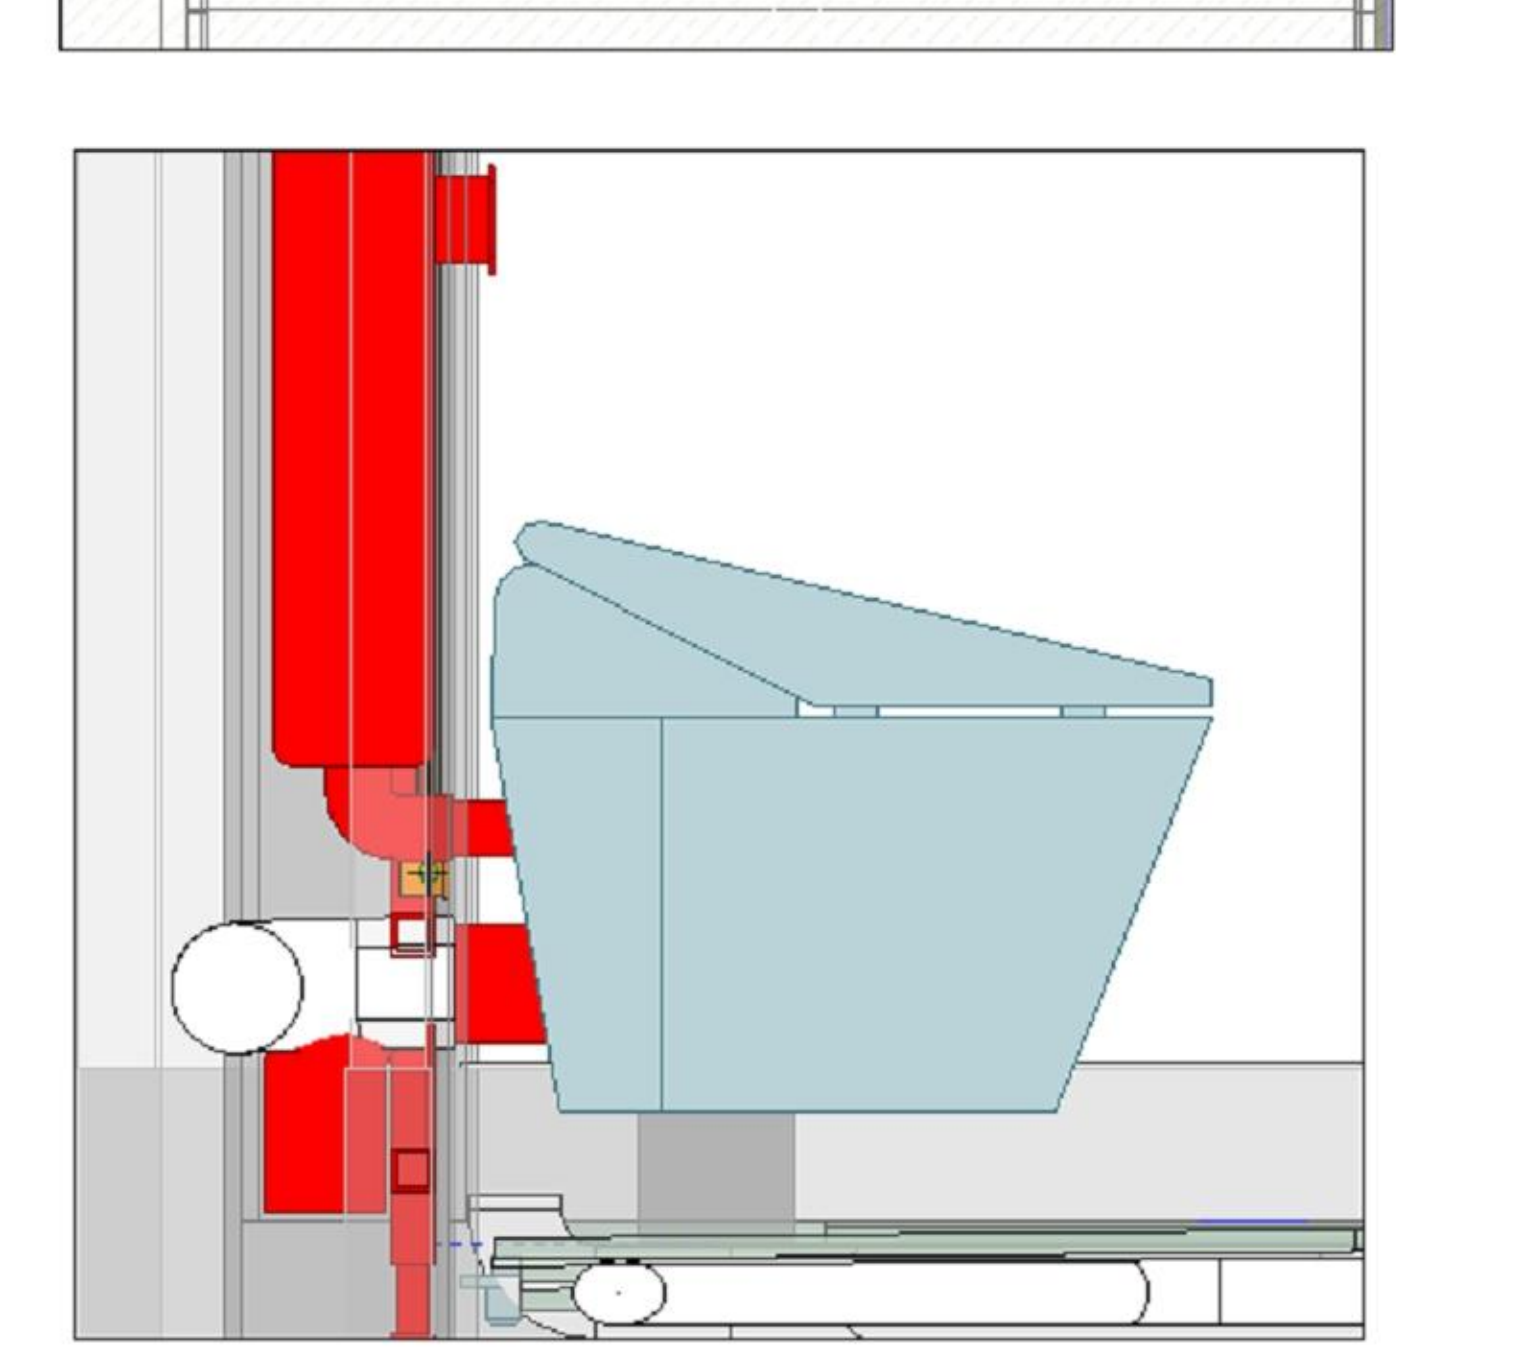

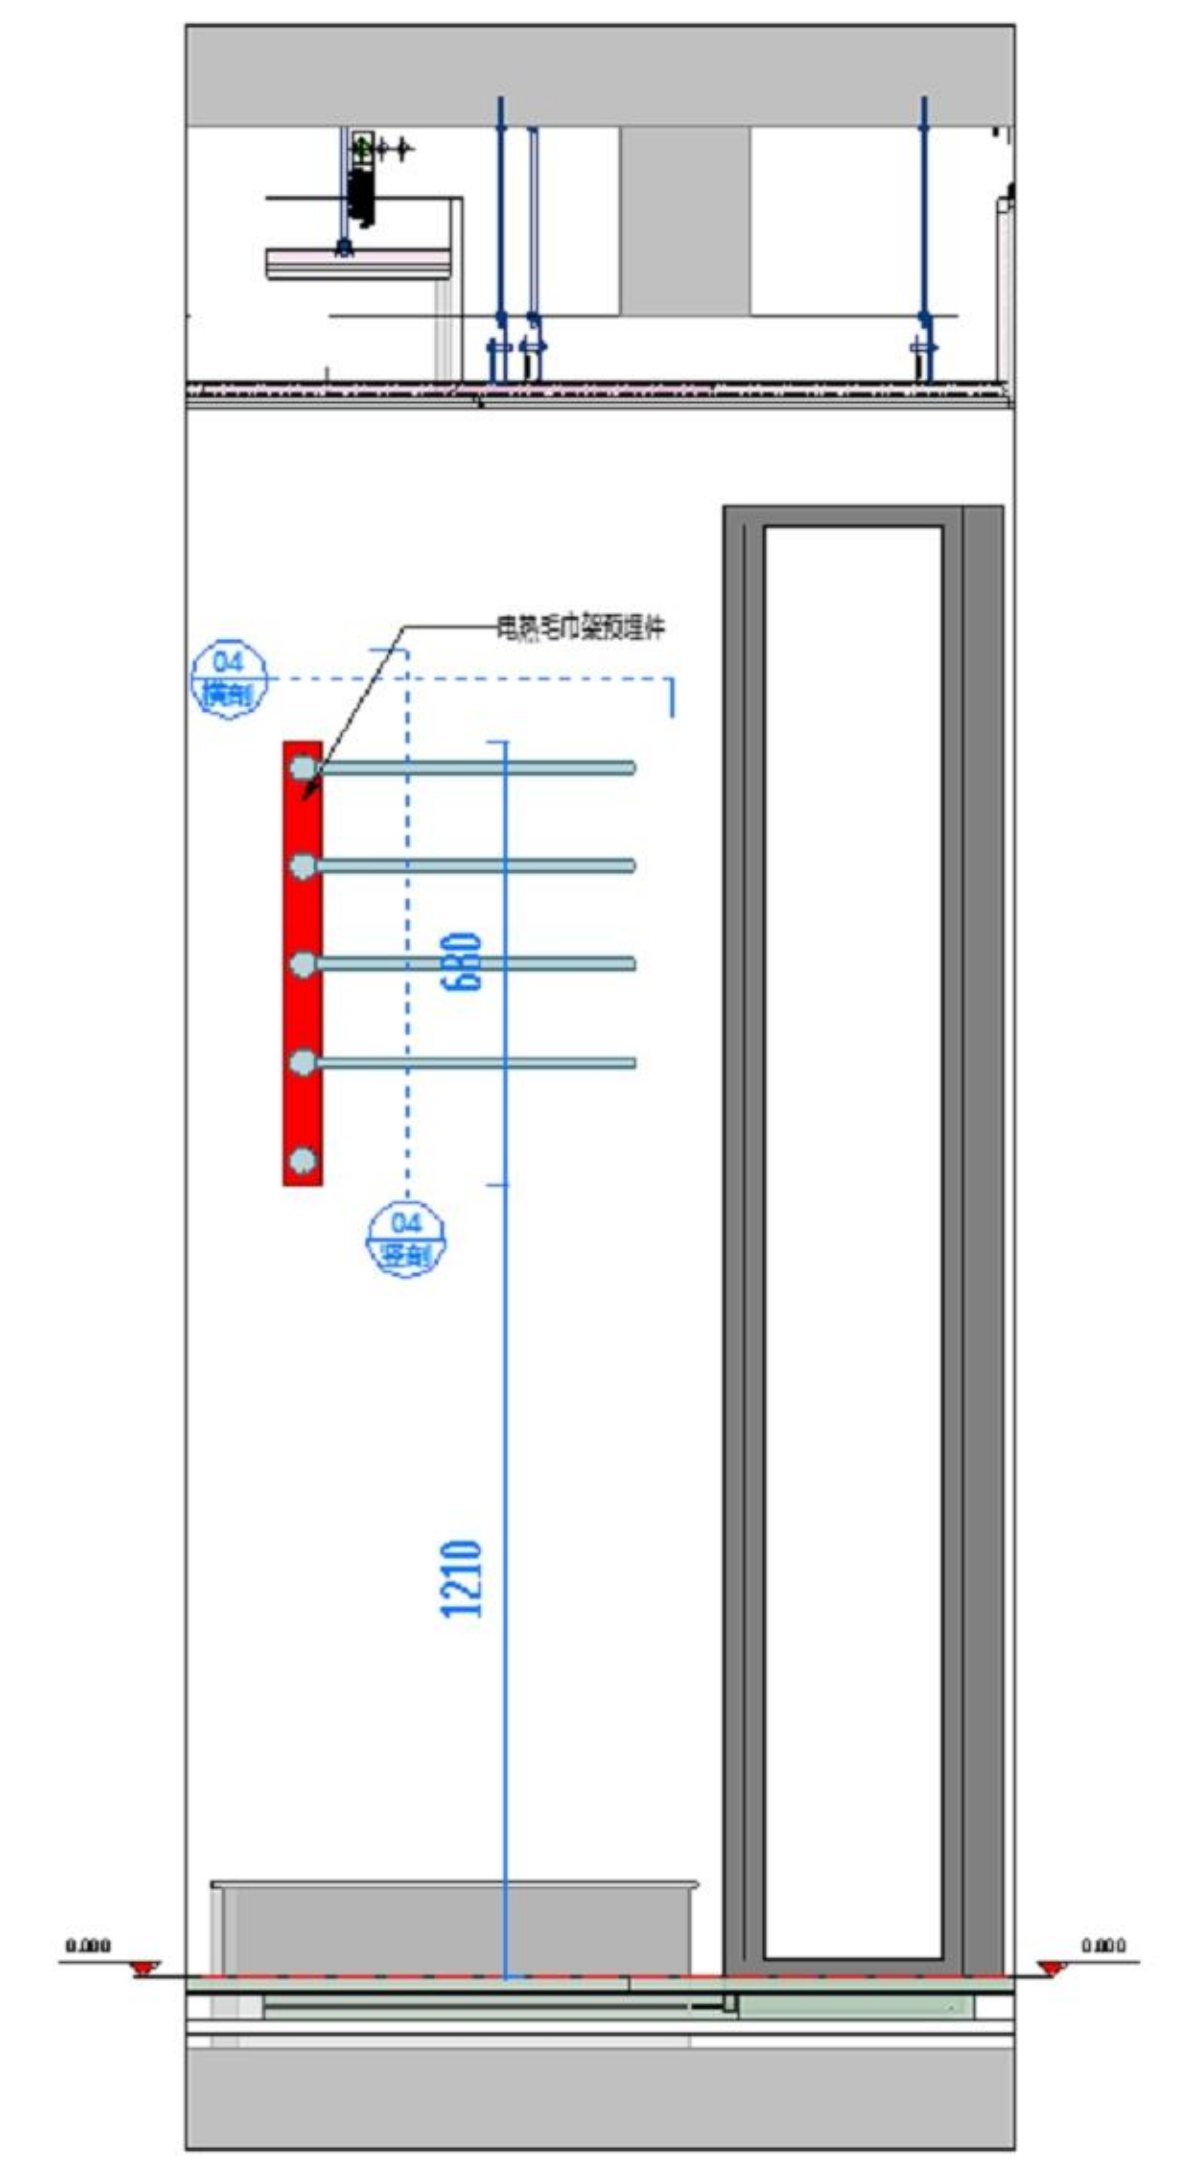

主卫-04

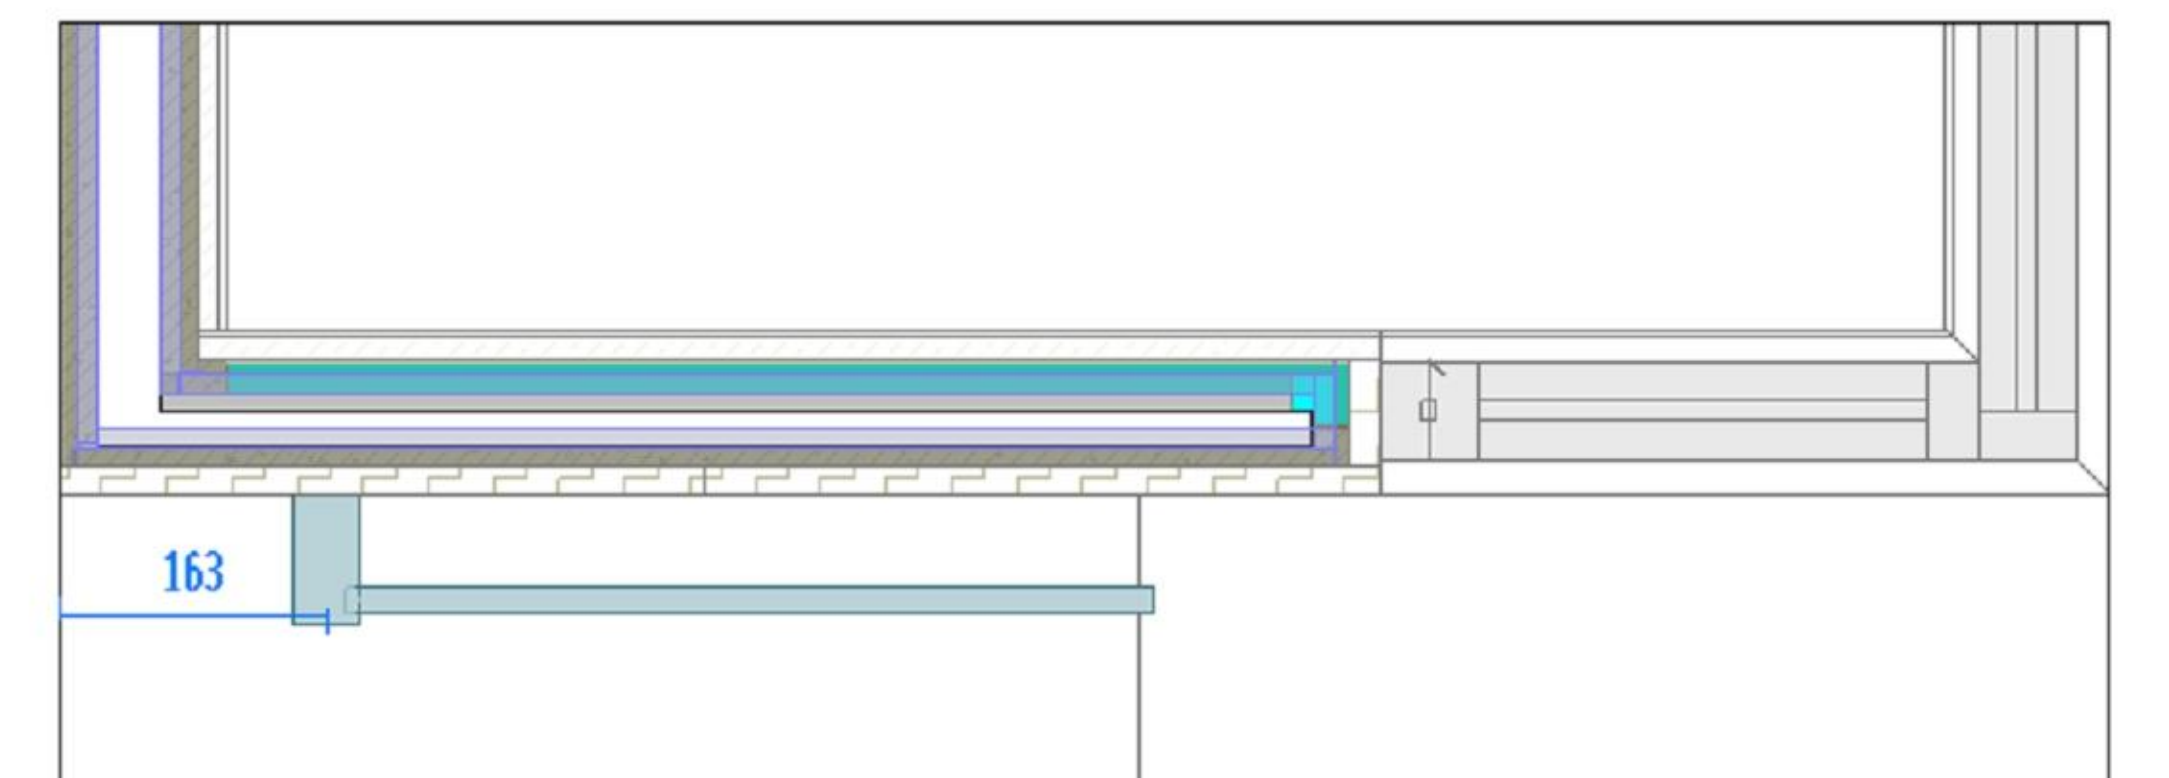

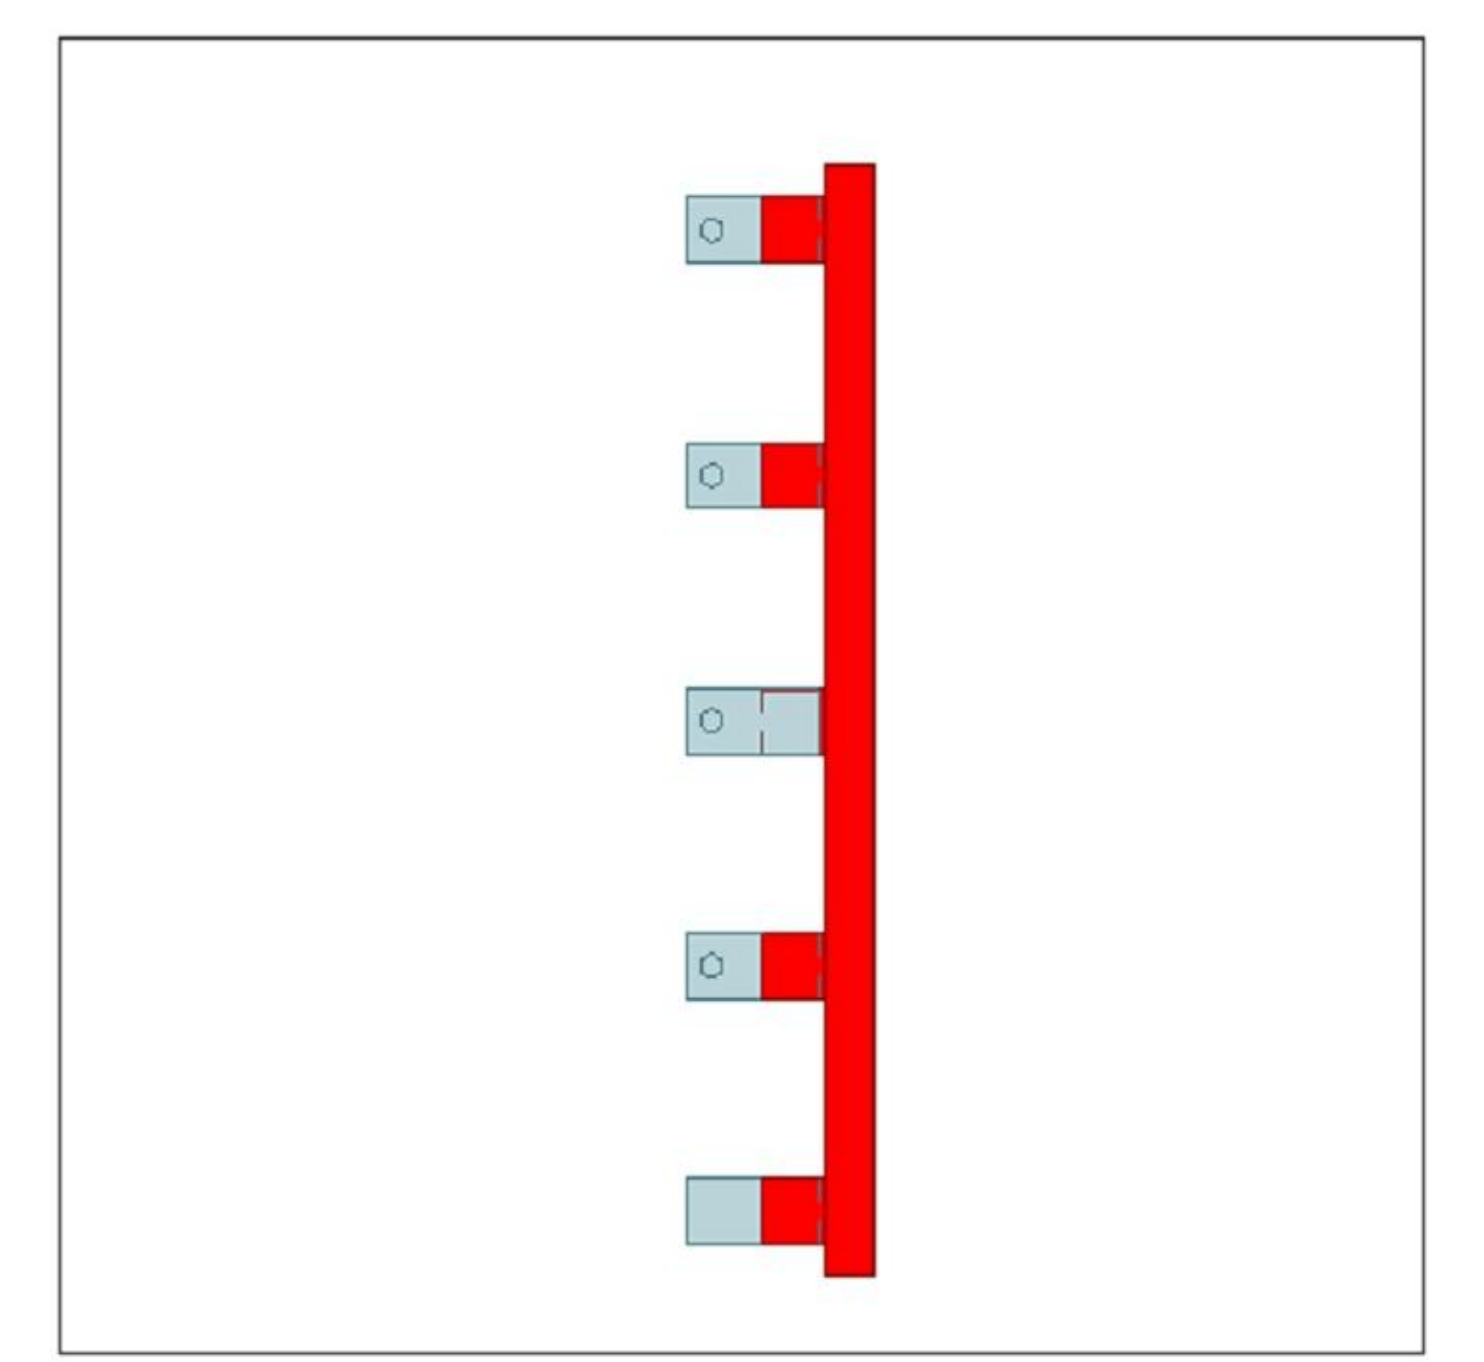

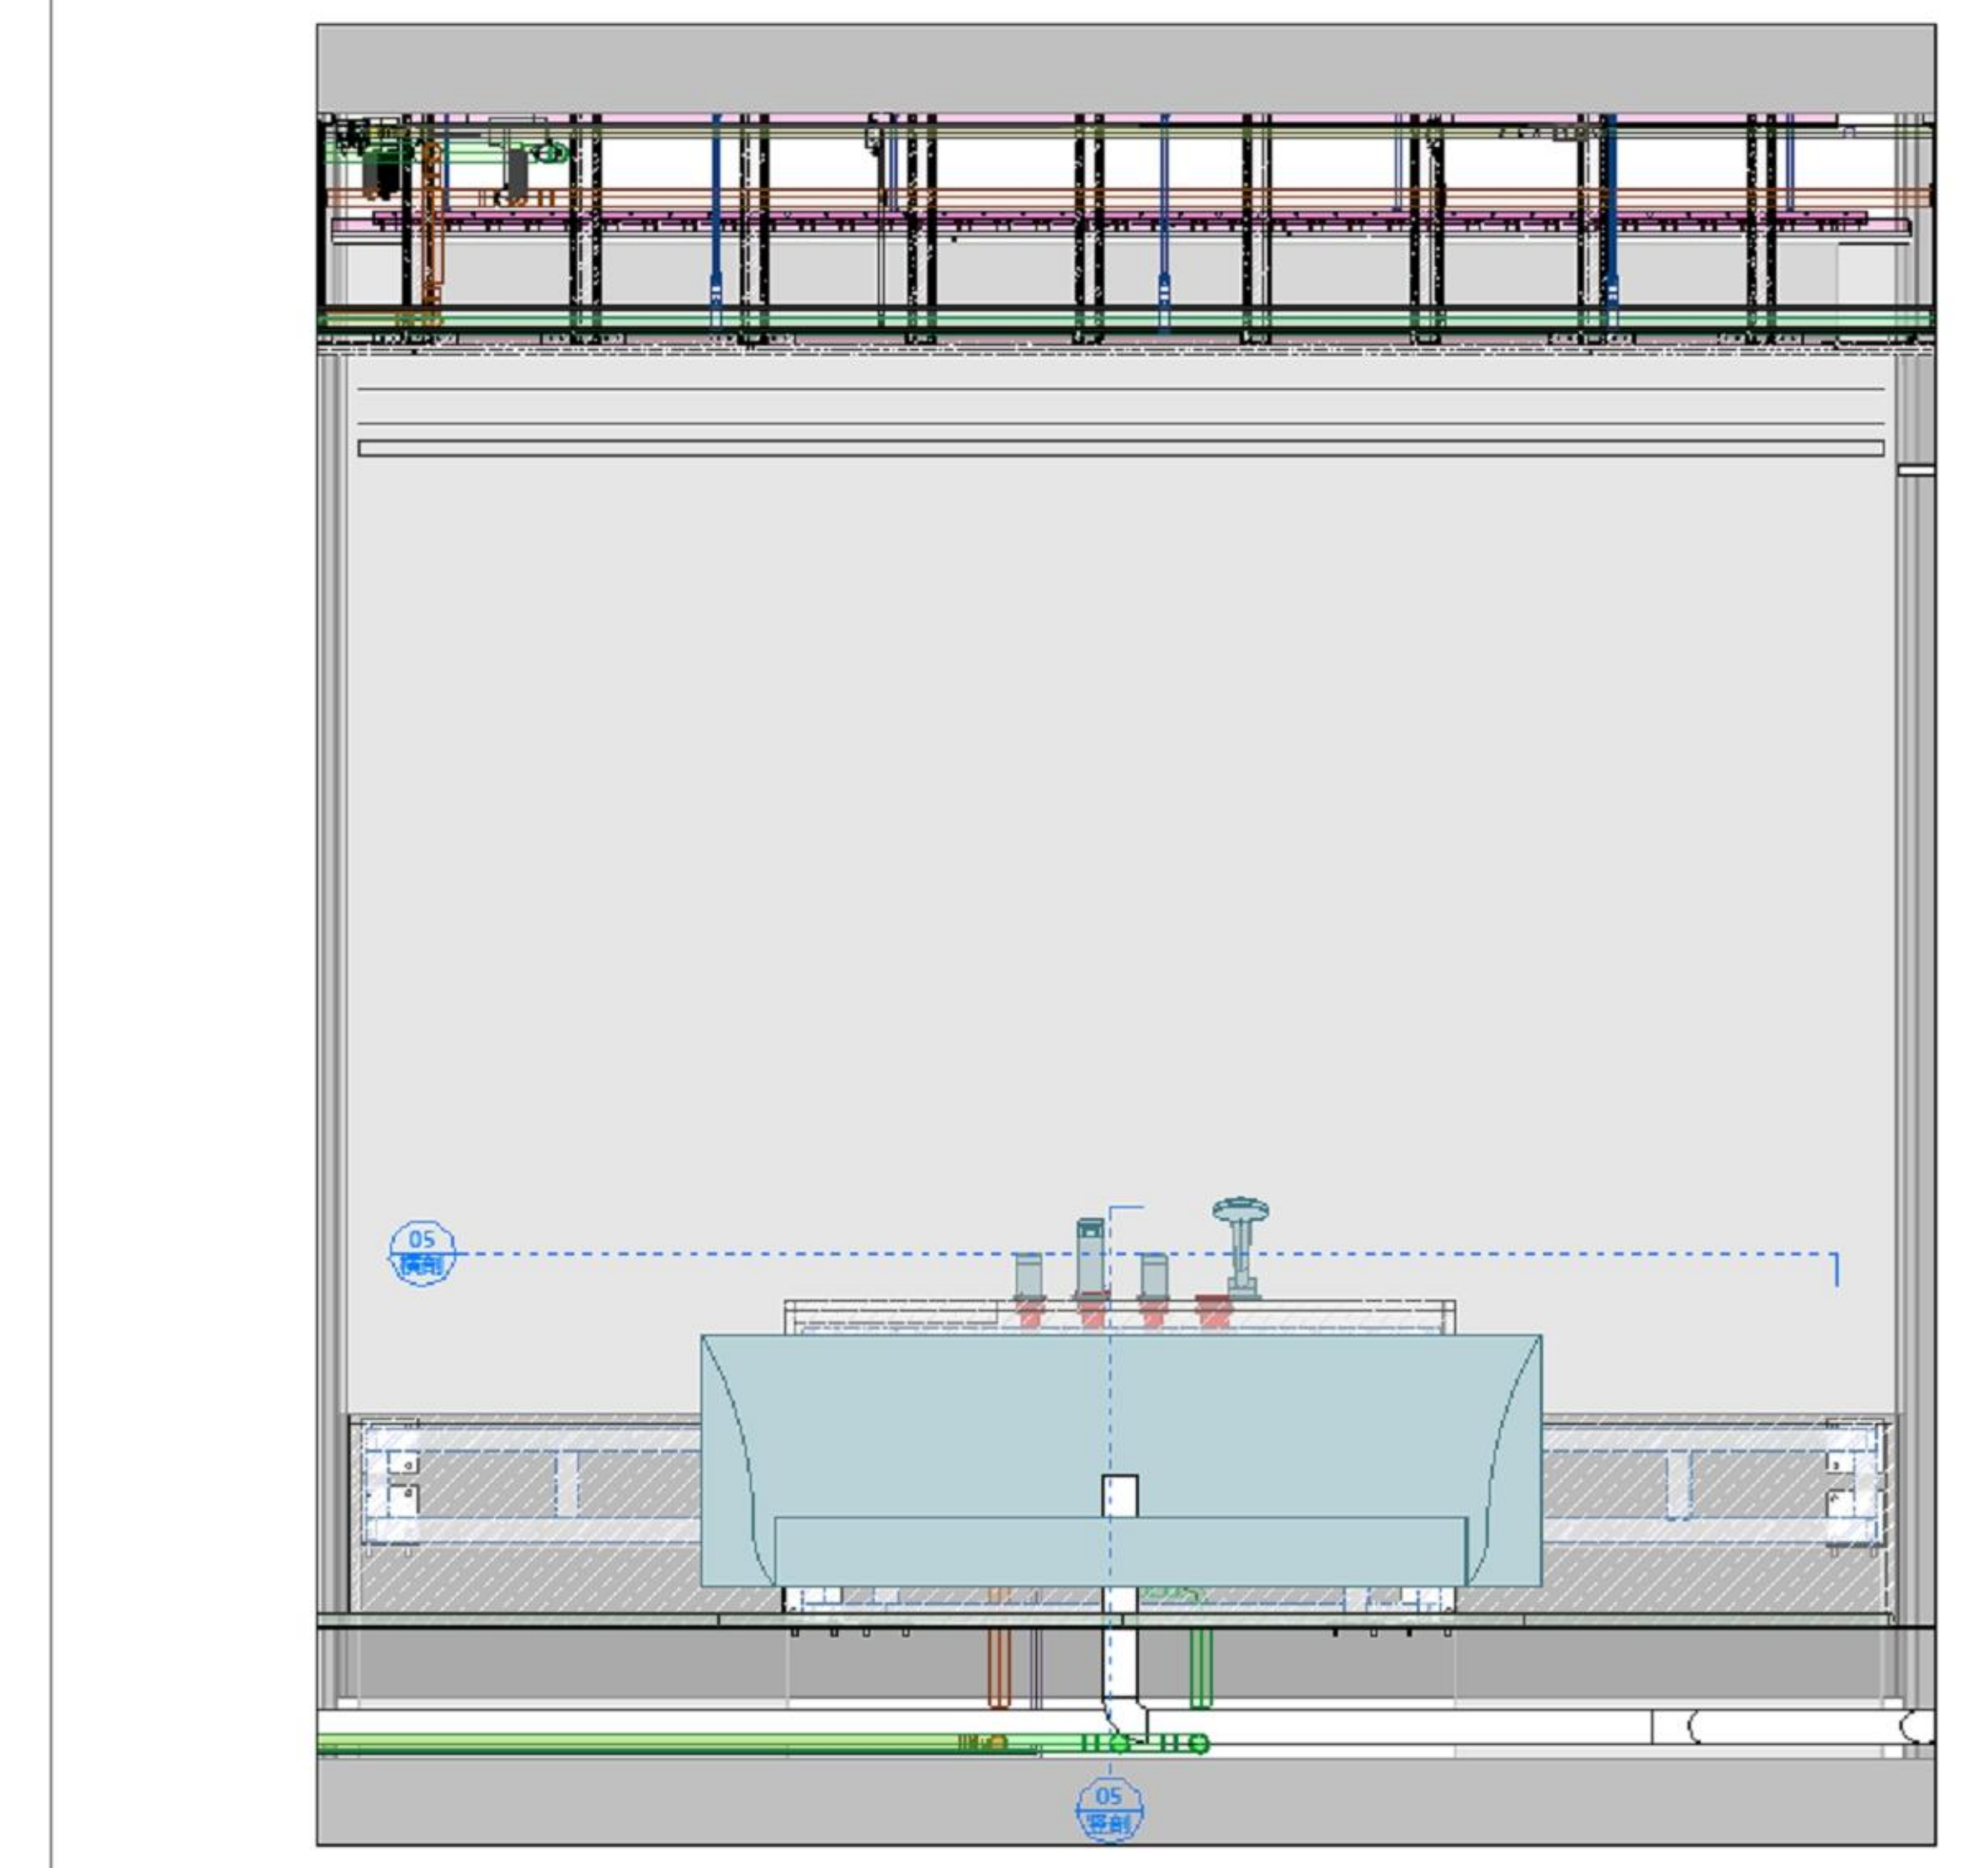

主卫-05

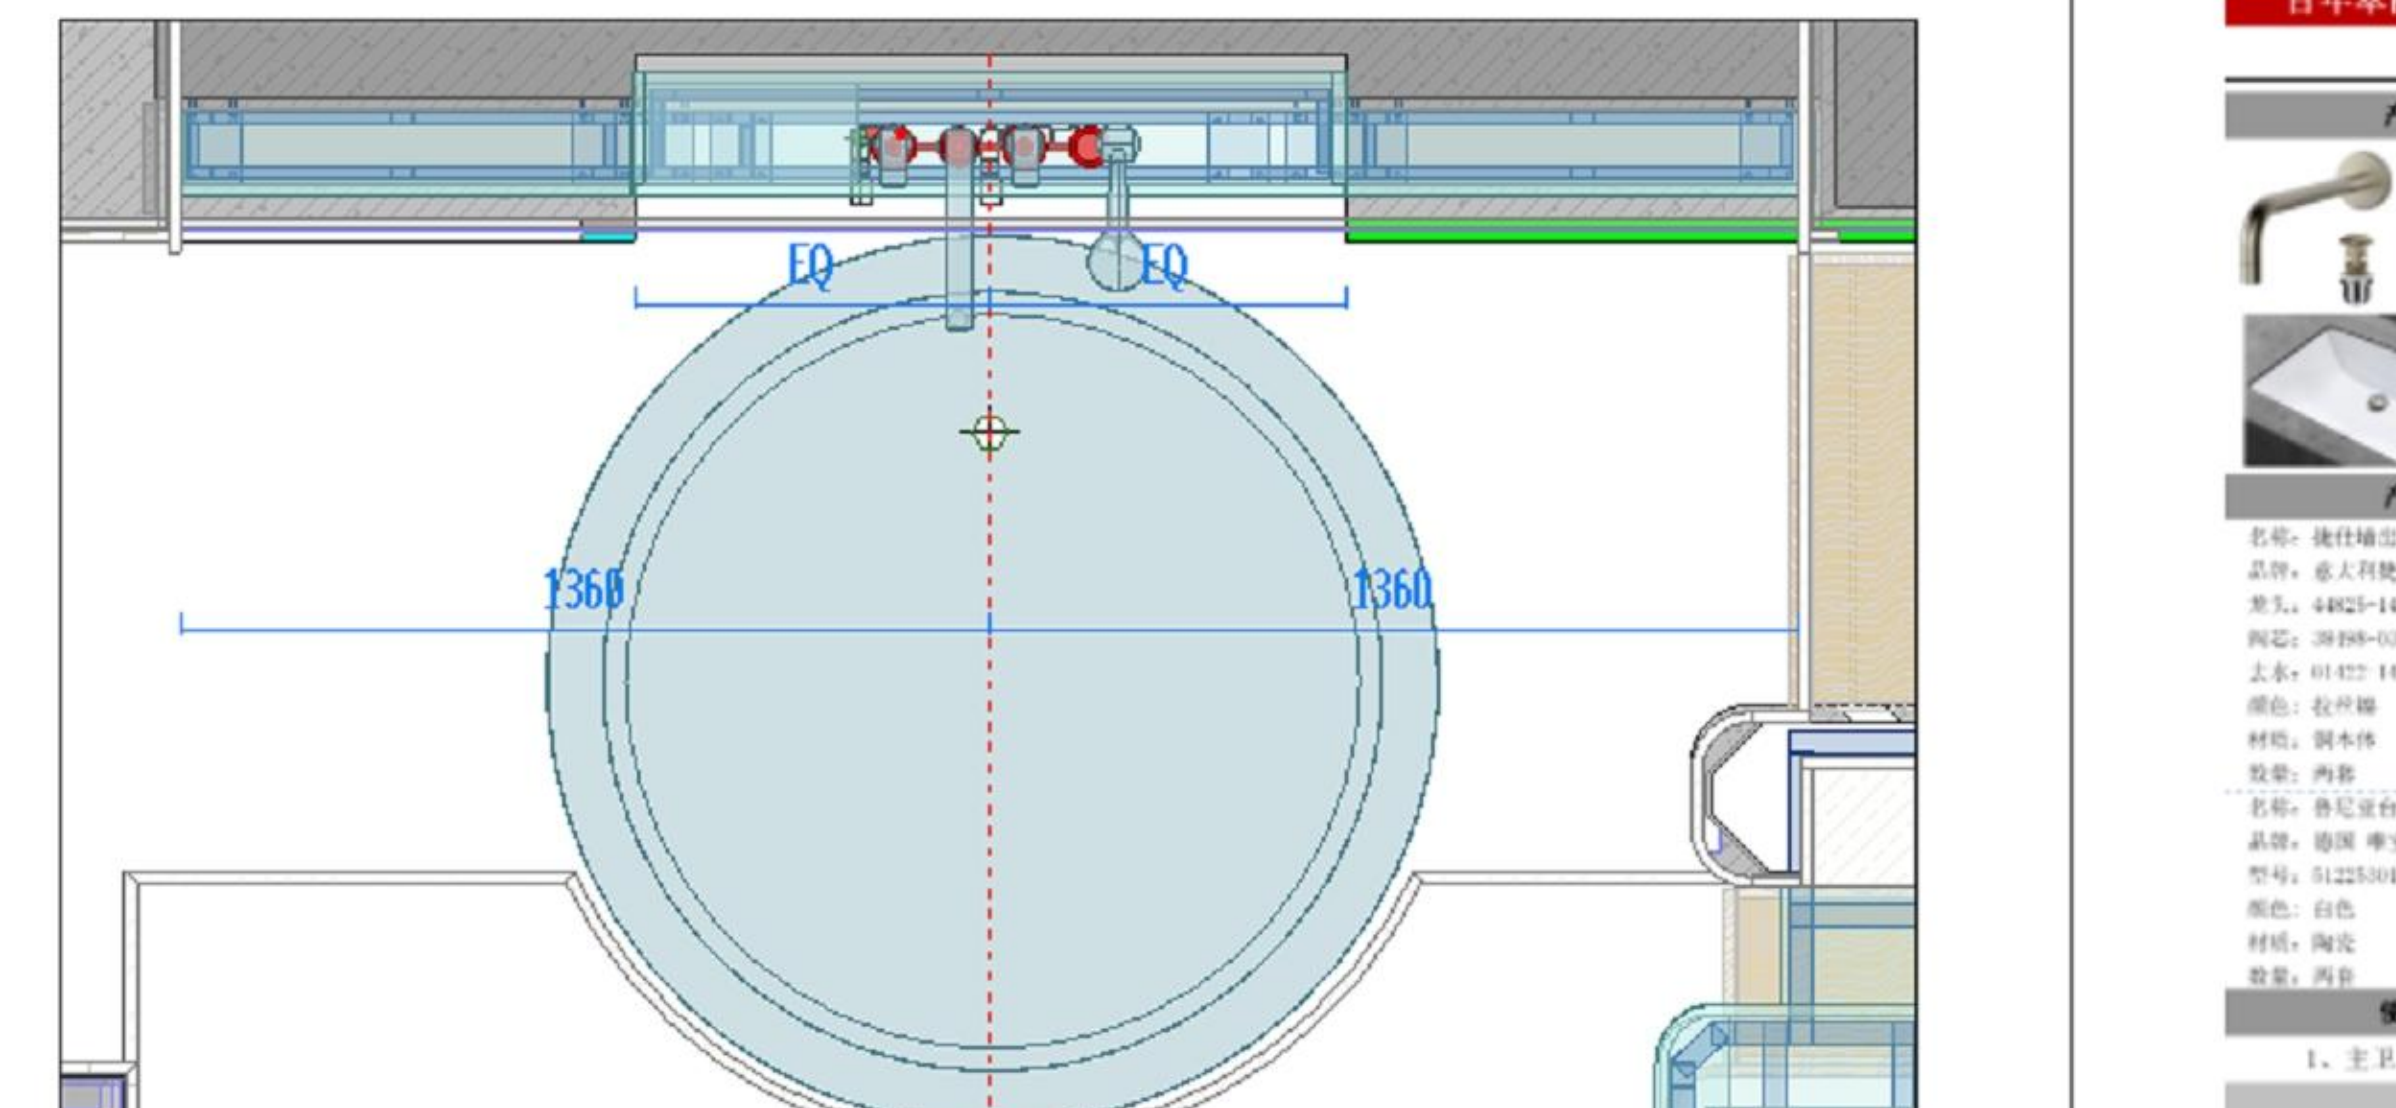
EQ
EQ
1360
1360

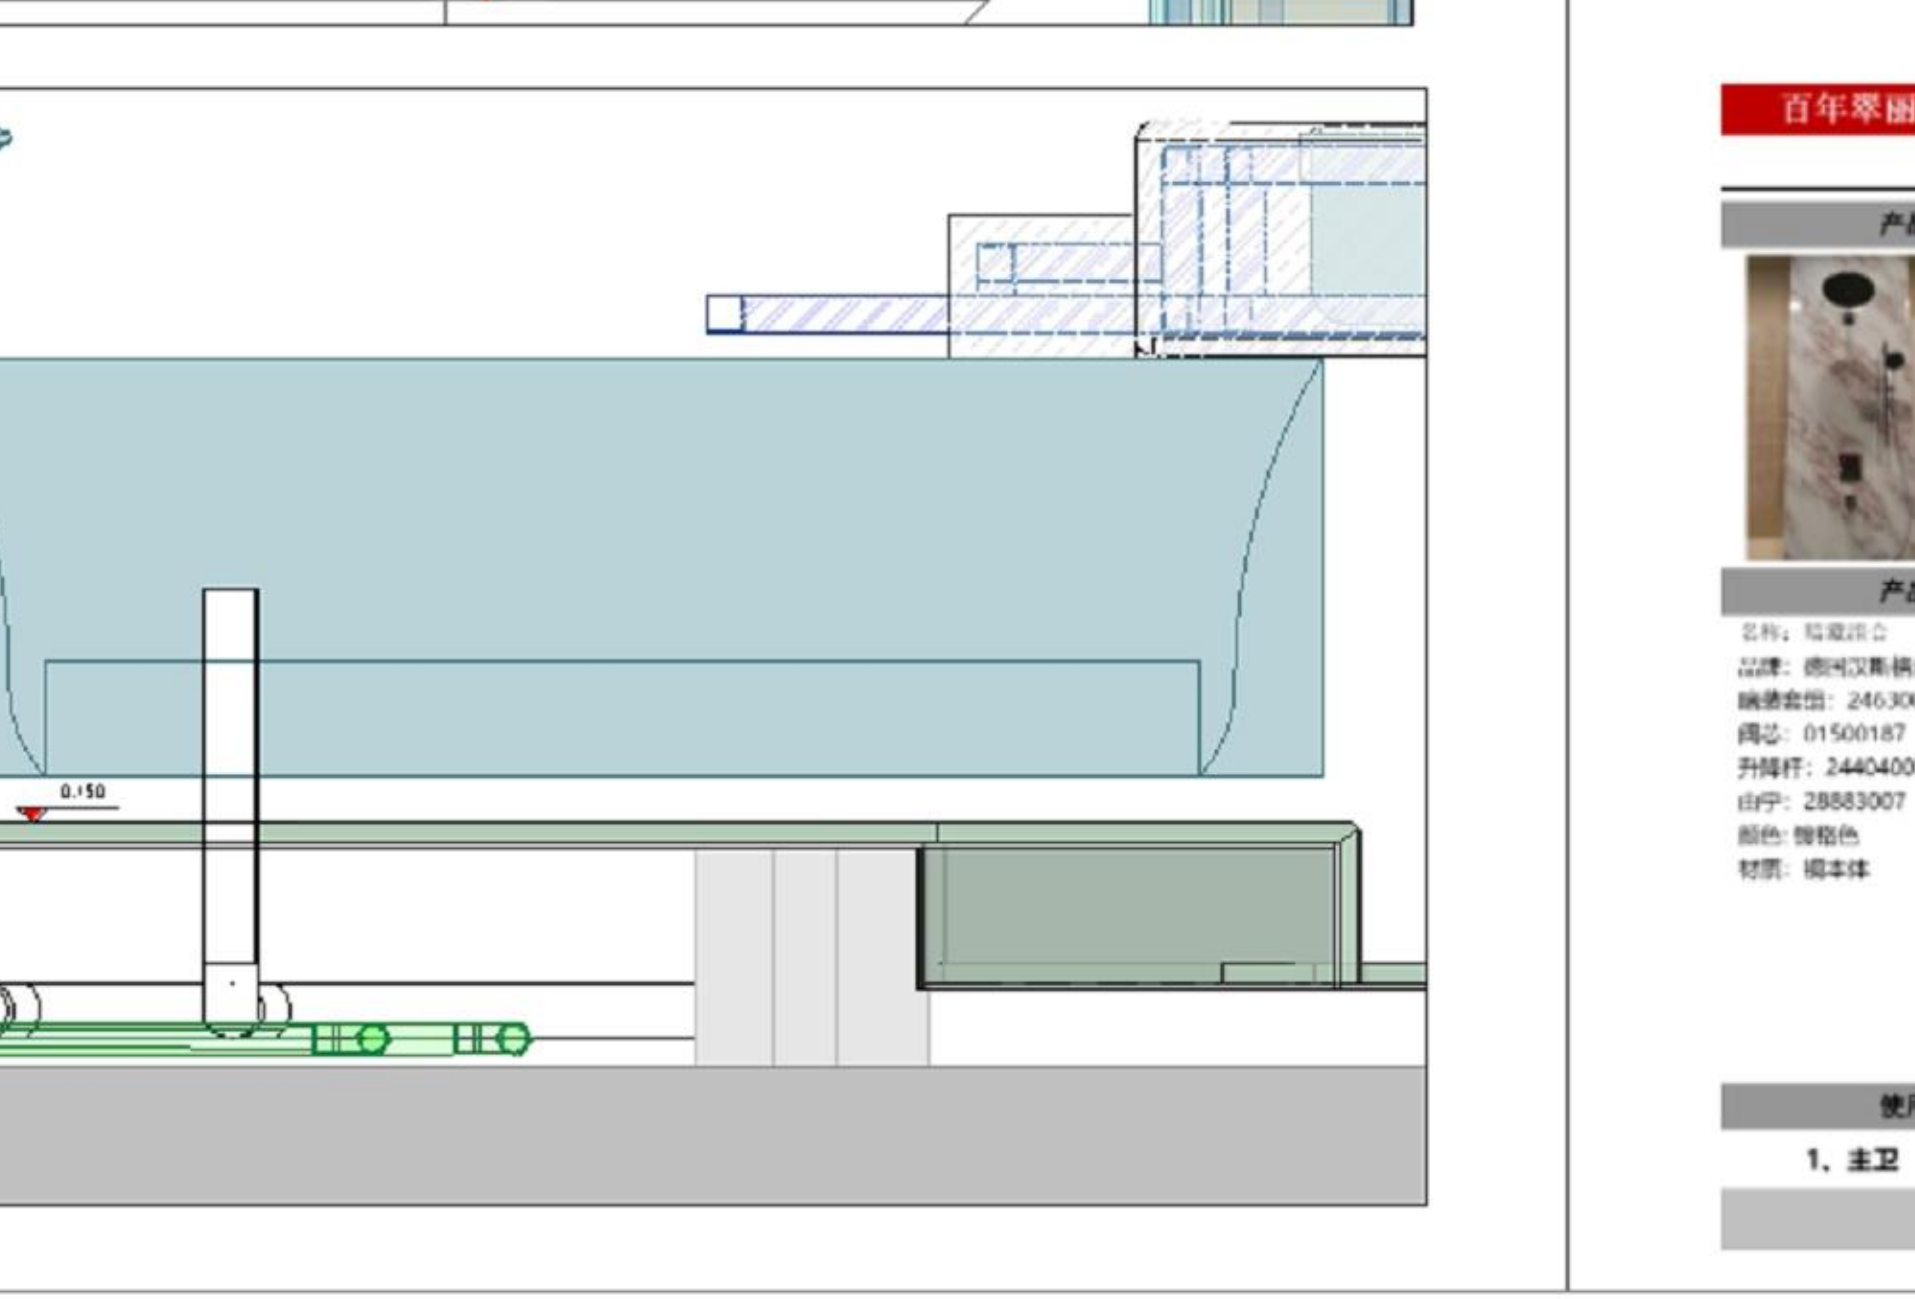

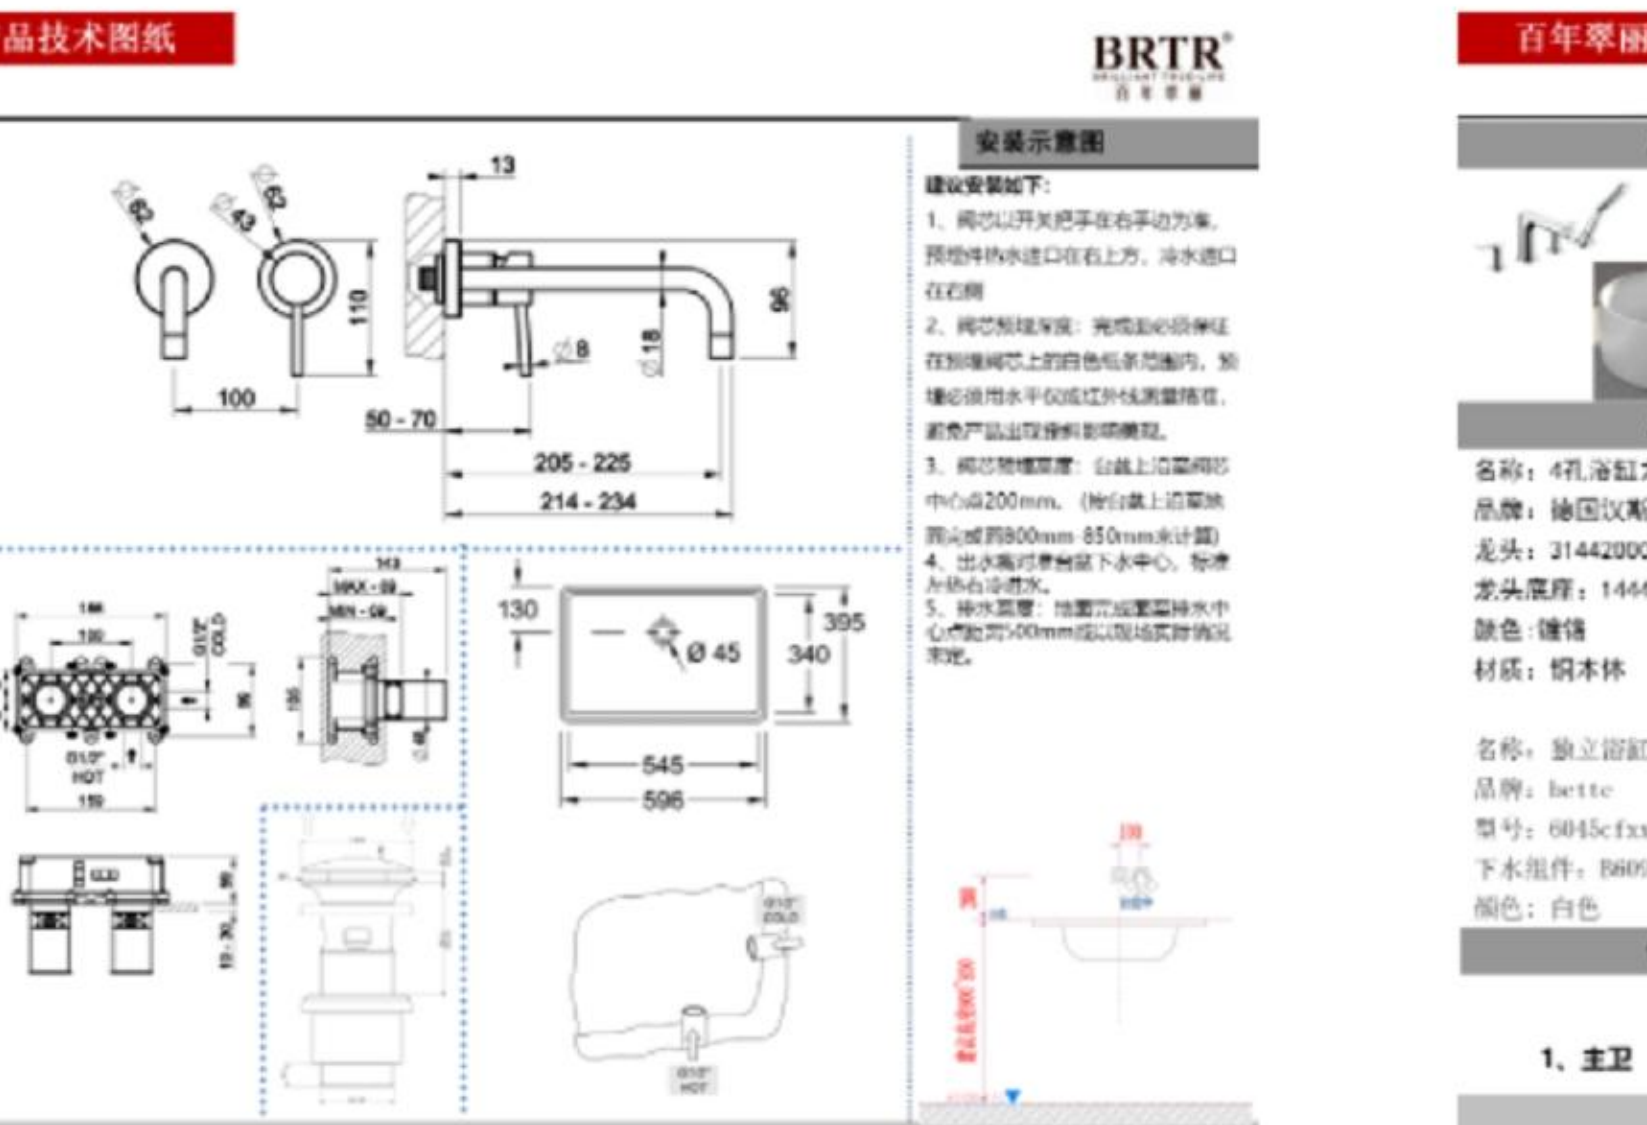

百年翠丽卫浴产品技术图纸

BRTR

产品图示

产品型号

使用区域

1、主卫

安装示意图

100
50-70
205-225
214-234
130
Ø 45
395
340
545
596

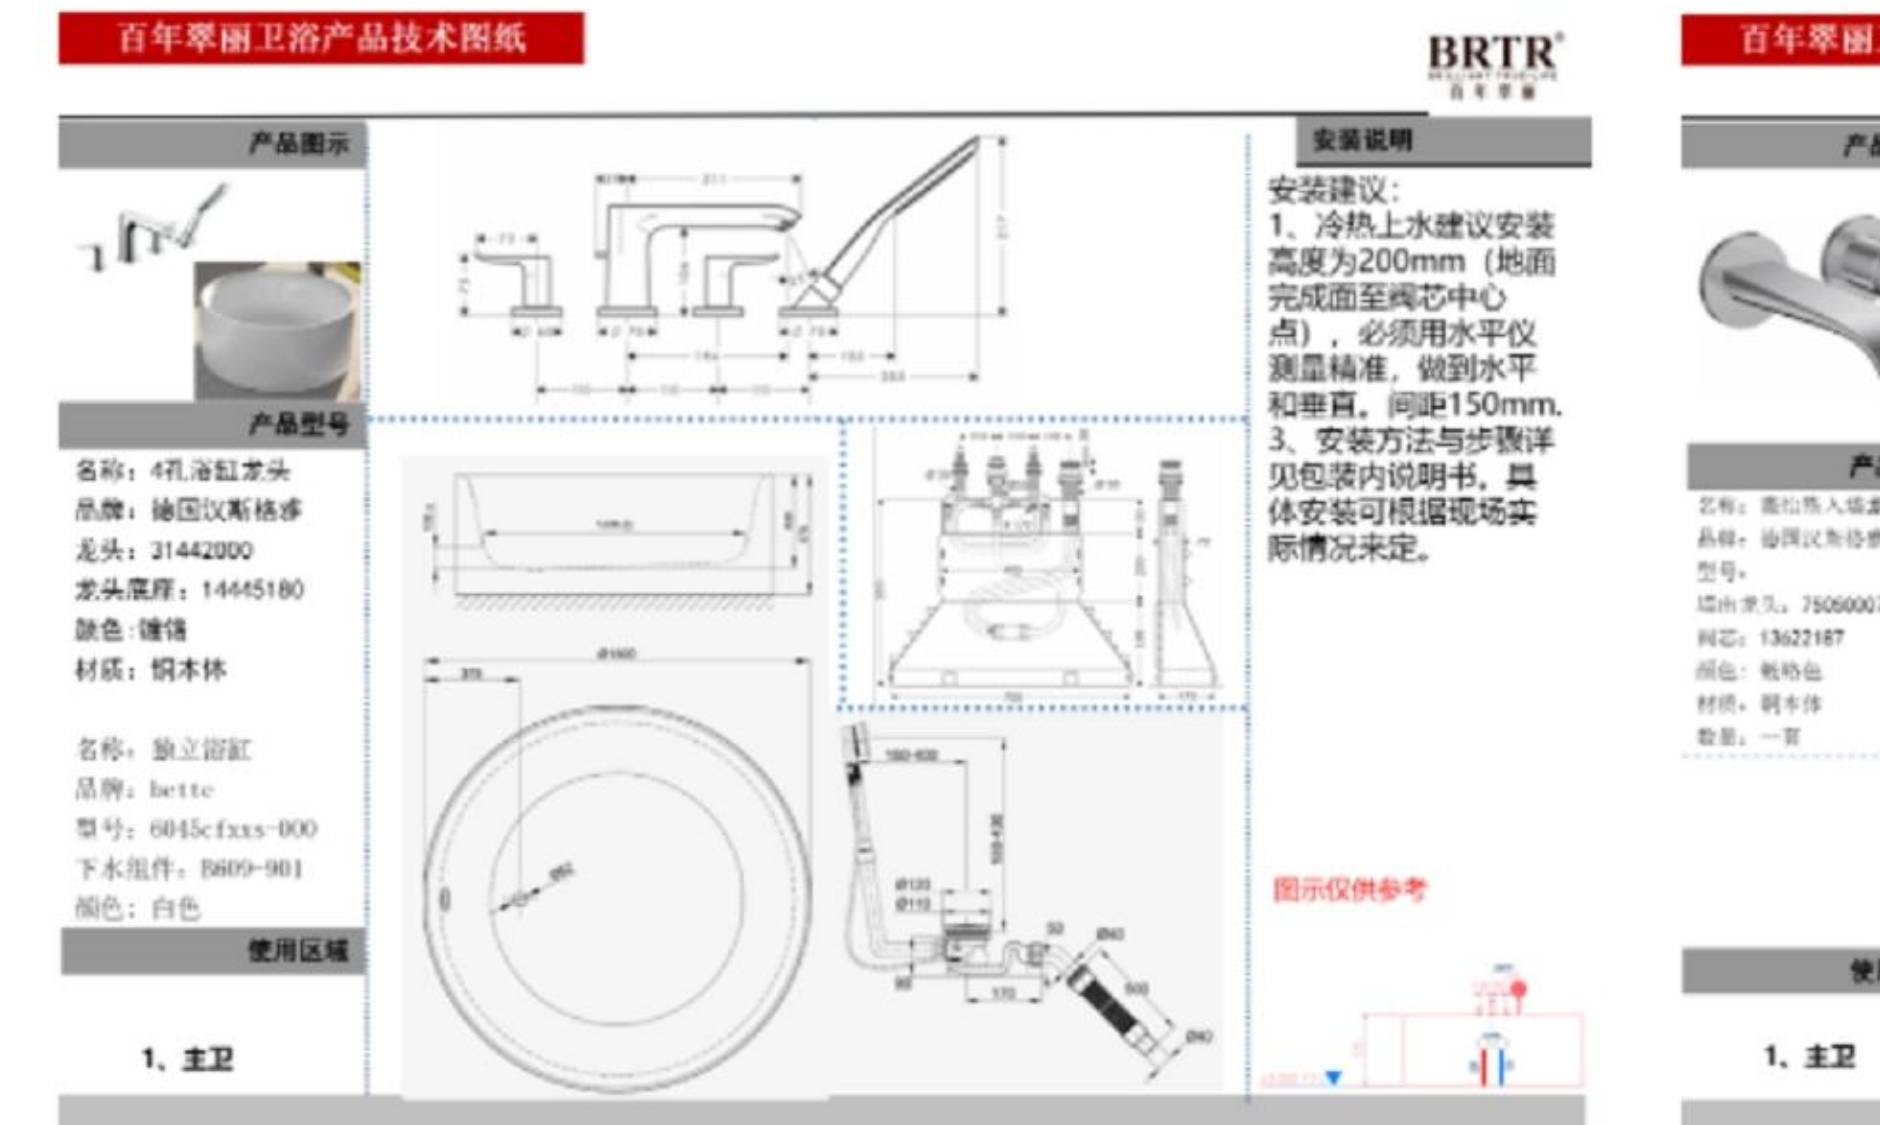

百年翠丽卫浴产品技术图纸

BRTR

产品图示

产品型号

名称：4孔浴缸龙头
品牌：德国汉斯格雅
龙头：31442000
龙头底座：14445180
颜色：镀铬
材质：铜本体

名称：独立浴缸
品牌：bette
型号：6045cfxxs-000
下水组件：B609-901
颜色：白色

使用区域

1、主卫

安装说明

安装建议：
1、冷热上水建议安装高度为200mm（地面完成面至阀芯中心点），必须用水平仪测量精准，做到水平和垂直，间距150mm。
3、安装方法与步骤详见包装内说明书，具体安装可根据现场实际情况来定。

图示仅供参考

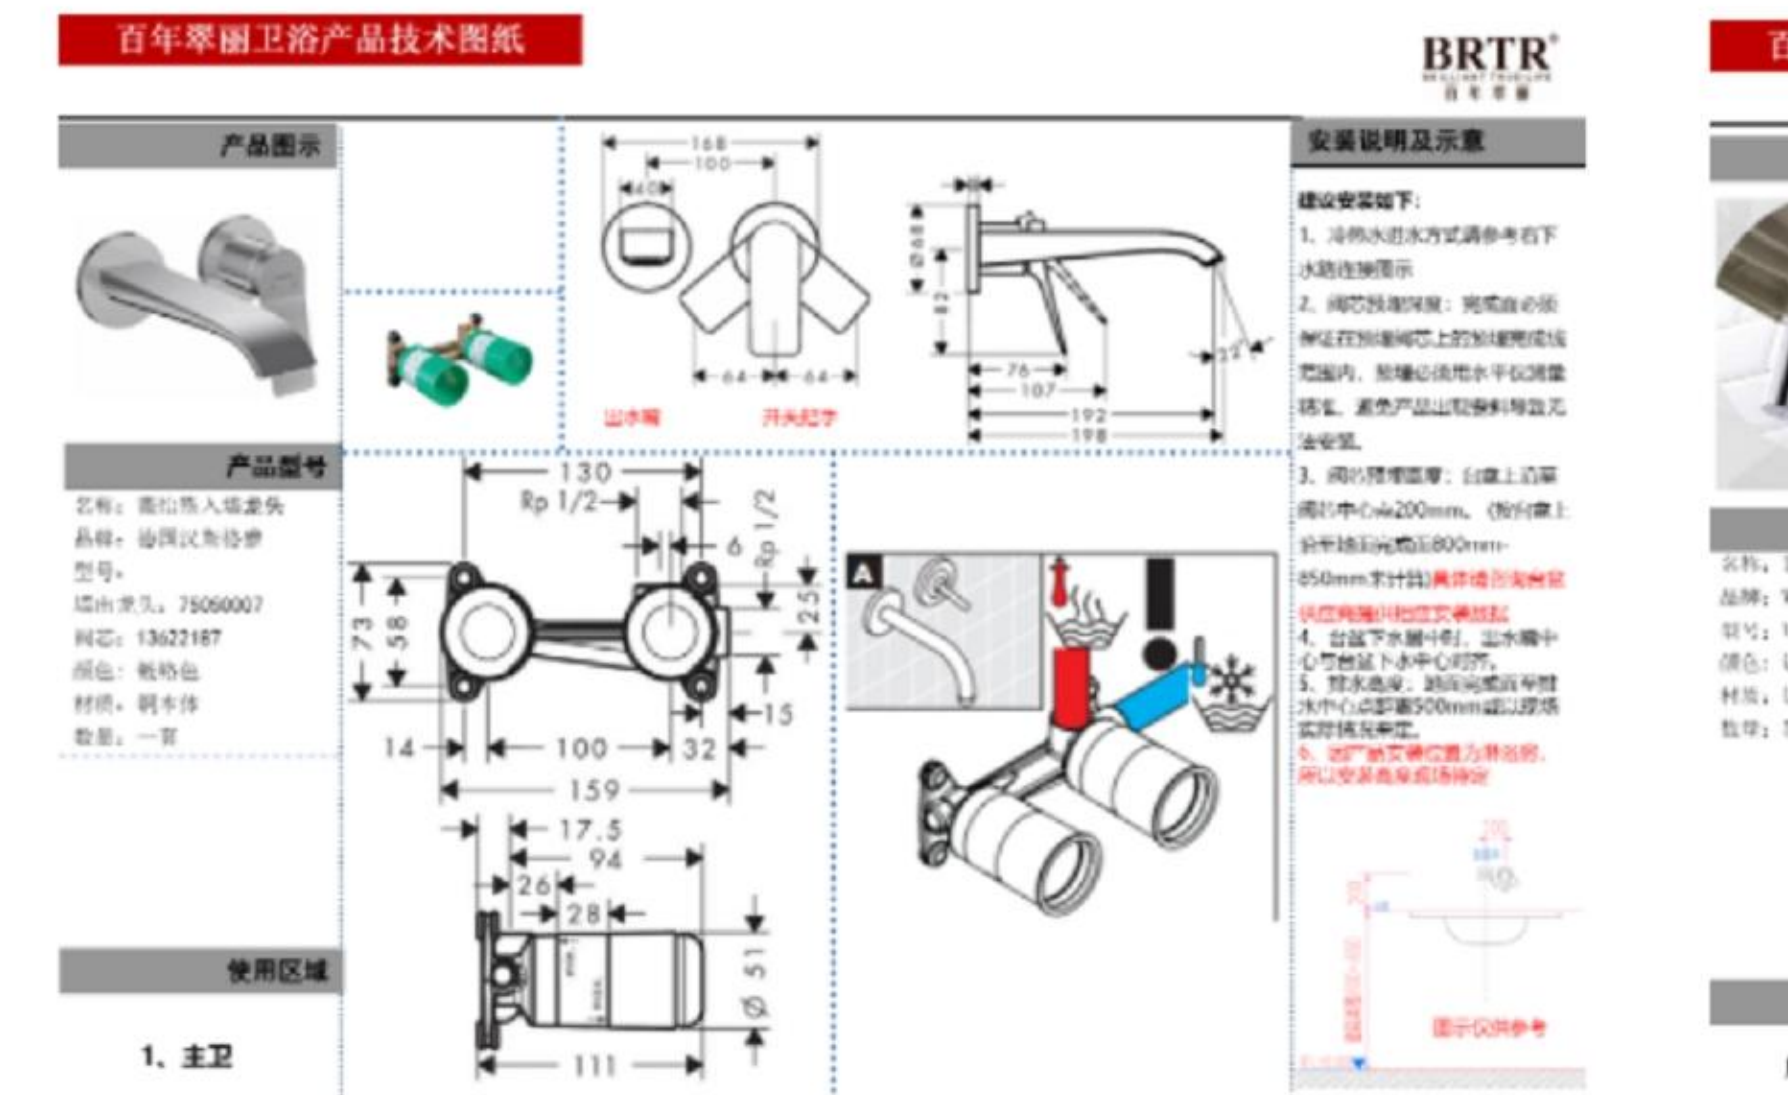

百年翠丽卫浴产品技术图纸

BRTR

产品图示

产品型号

使用区域

1、主卫

130
Rp 1/2
73
58
14
100
159
17.5
94
26
28
111

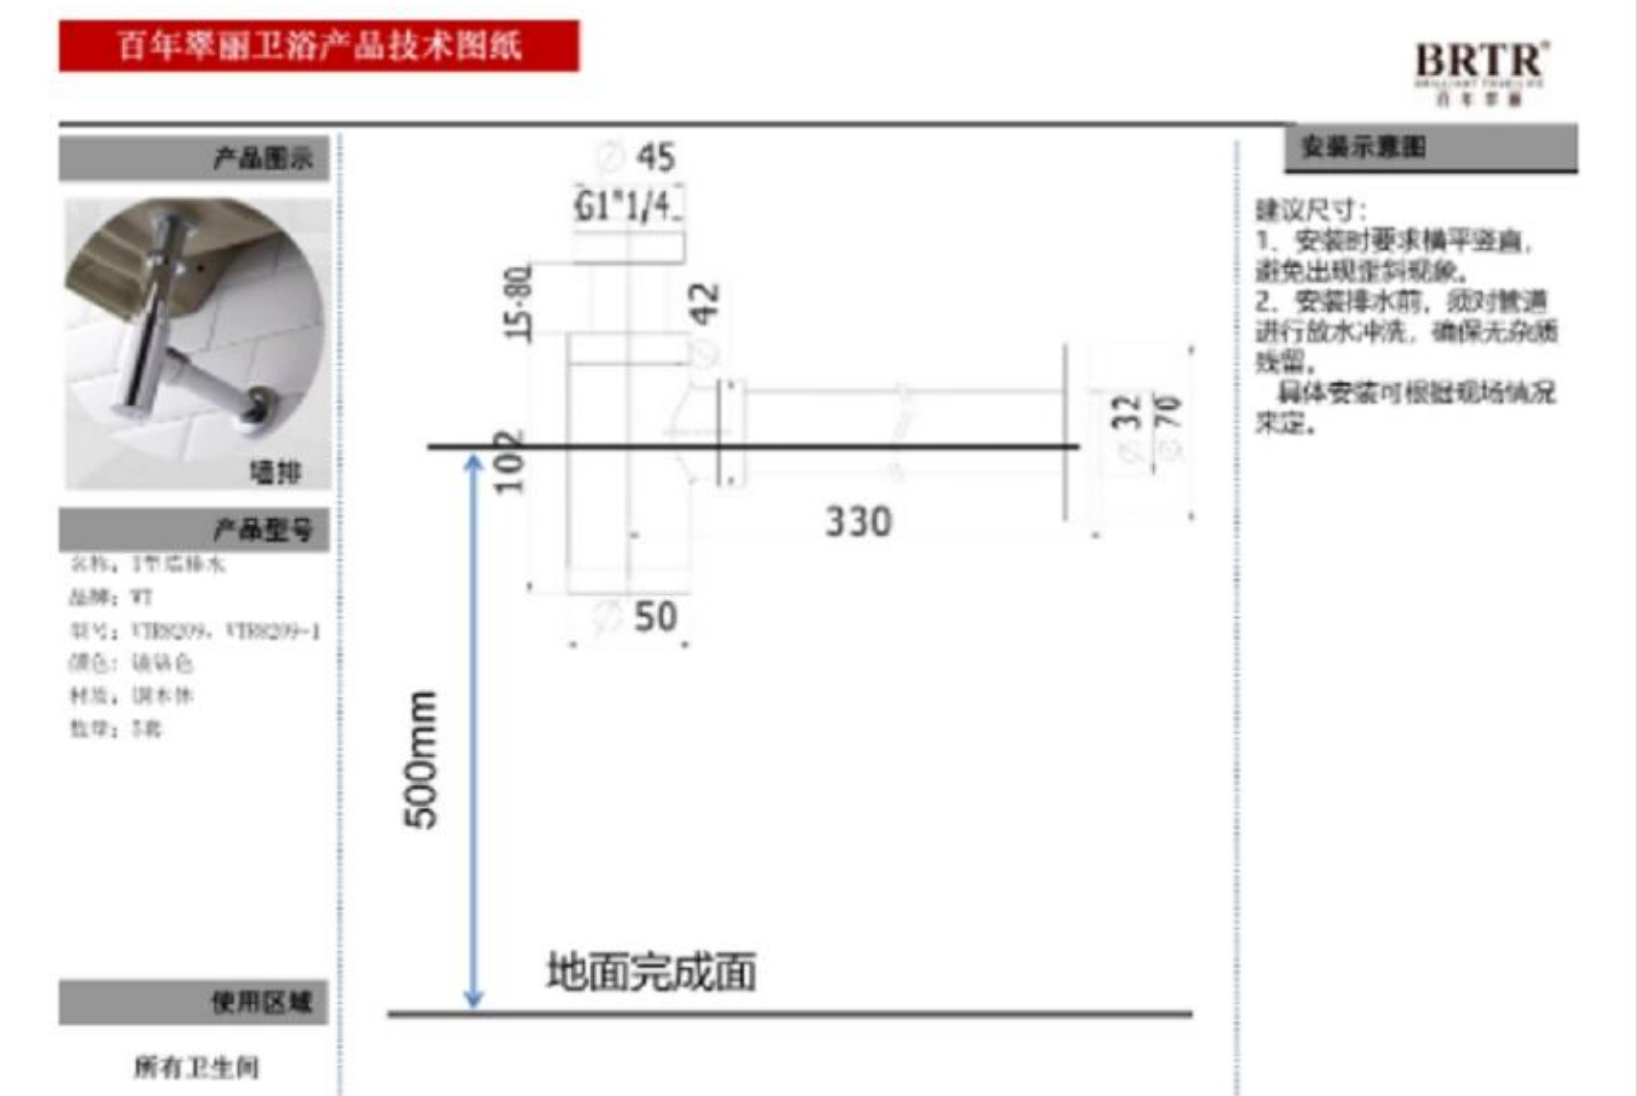

百年翠丽卫浴产品技术图纸

BRTR

产品图示

产品型号

所有卫生间

安装示意图

建议尺寸：
1、安装时要求横平竖直，避免出现歪斜现象。
2、安装排水前，须对管道进行放水冲洗，确保无杂质残留。
具体安装可根据现场情况来定。

45
G1"1/4
42
15-80
100
330
50
32
70
500mm
地面完成面

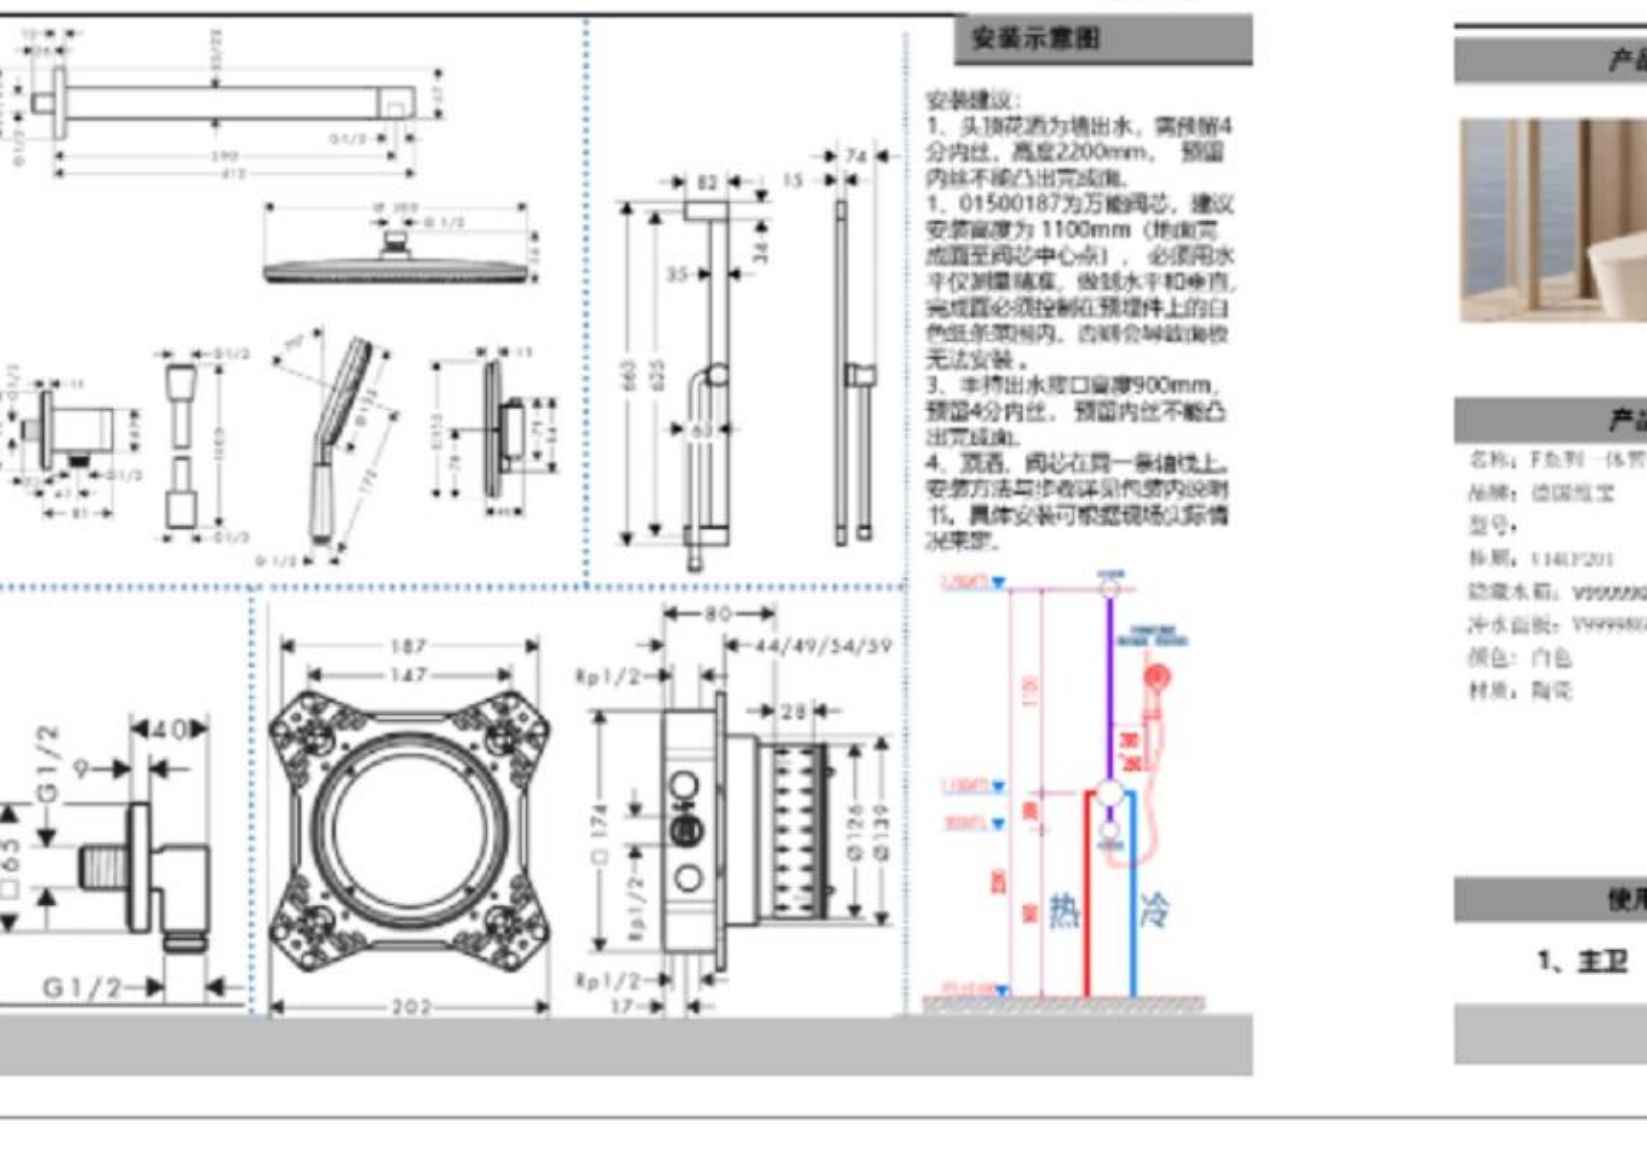

百年翠丽卫浴产品技术图纸

BRTR

产品图示

产品型号

名称：恒温淋浴
品牌：德国汉斯格雅
编号：24630007
阀芯：01500187
升降杆：24404007
台阶：28883007
颜色：镀铬色
材质：铜本体

使用区域

1、主卫

安装示意图

G1/2
40
63
187
147
202
80
44/49/54/59
28
Rp1/2
174
热
冷

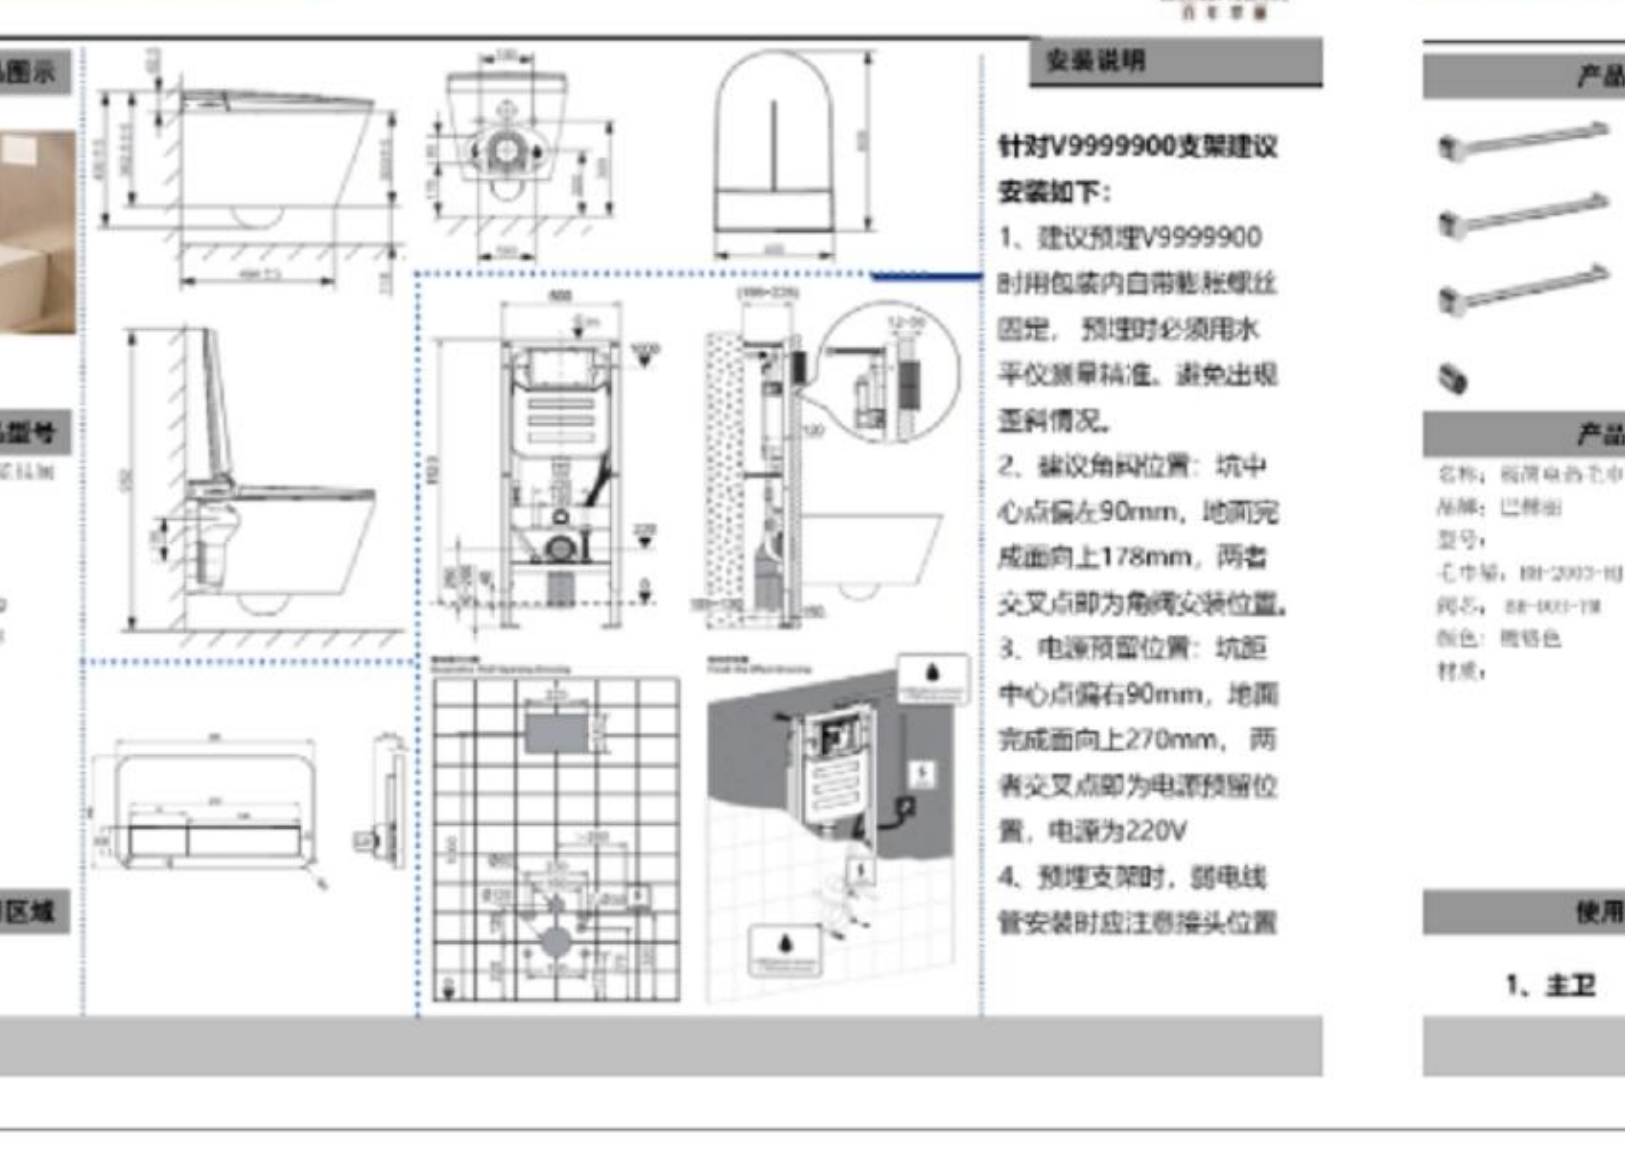

百年翠丽卫浴产品技术图纸

BRTR

产品图示

产品型号

使用区域

1、主卫

安装说明

针对V9999900支架建议安装如下：
1、建议预埋V9999900时用包装内自带膨胀螺丝固定，预埋时必须用水平仪测量精准，避免出现歪斜情况。
2、建议角阀位置：坑中心点偏左90mm，地面完成面向上178mm，两者交叉点即为角阀安装位置。
3、电源预留位置：坑距中心点偏右90mm，地面完成面向上270mm，两者交叉点即为电源预留位置，电源为220V
4、预埋支架时，弱电线管安装时应注意接头位置

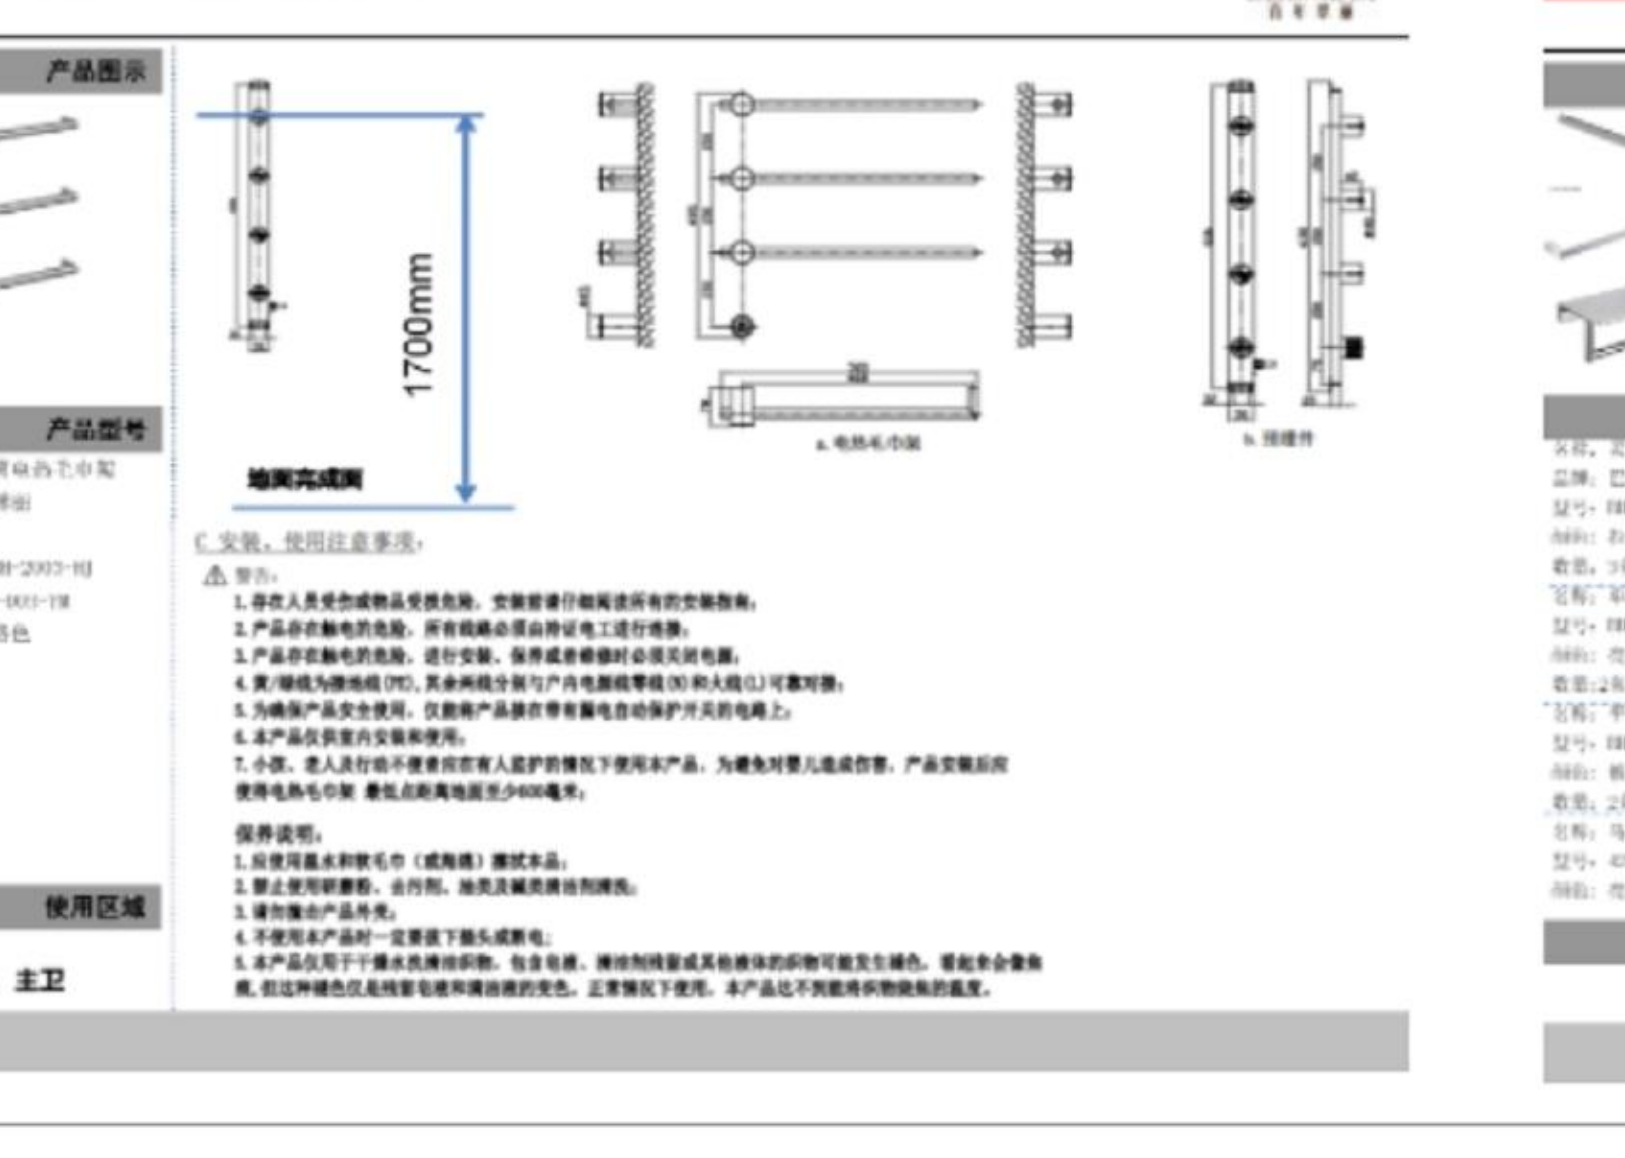

百年翠丽卫浴产品技术图纸

BRTR

产品图示

产品型号

使用区域

1、主卫

1700mm
地面完成面

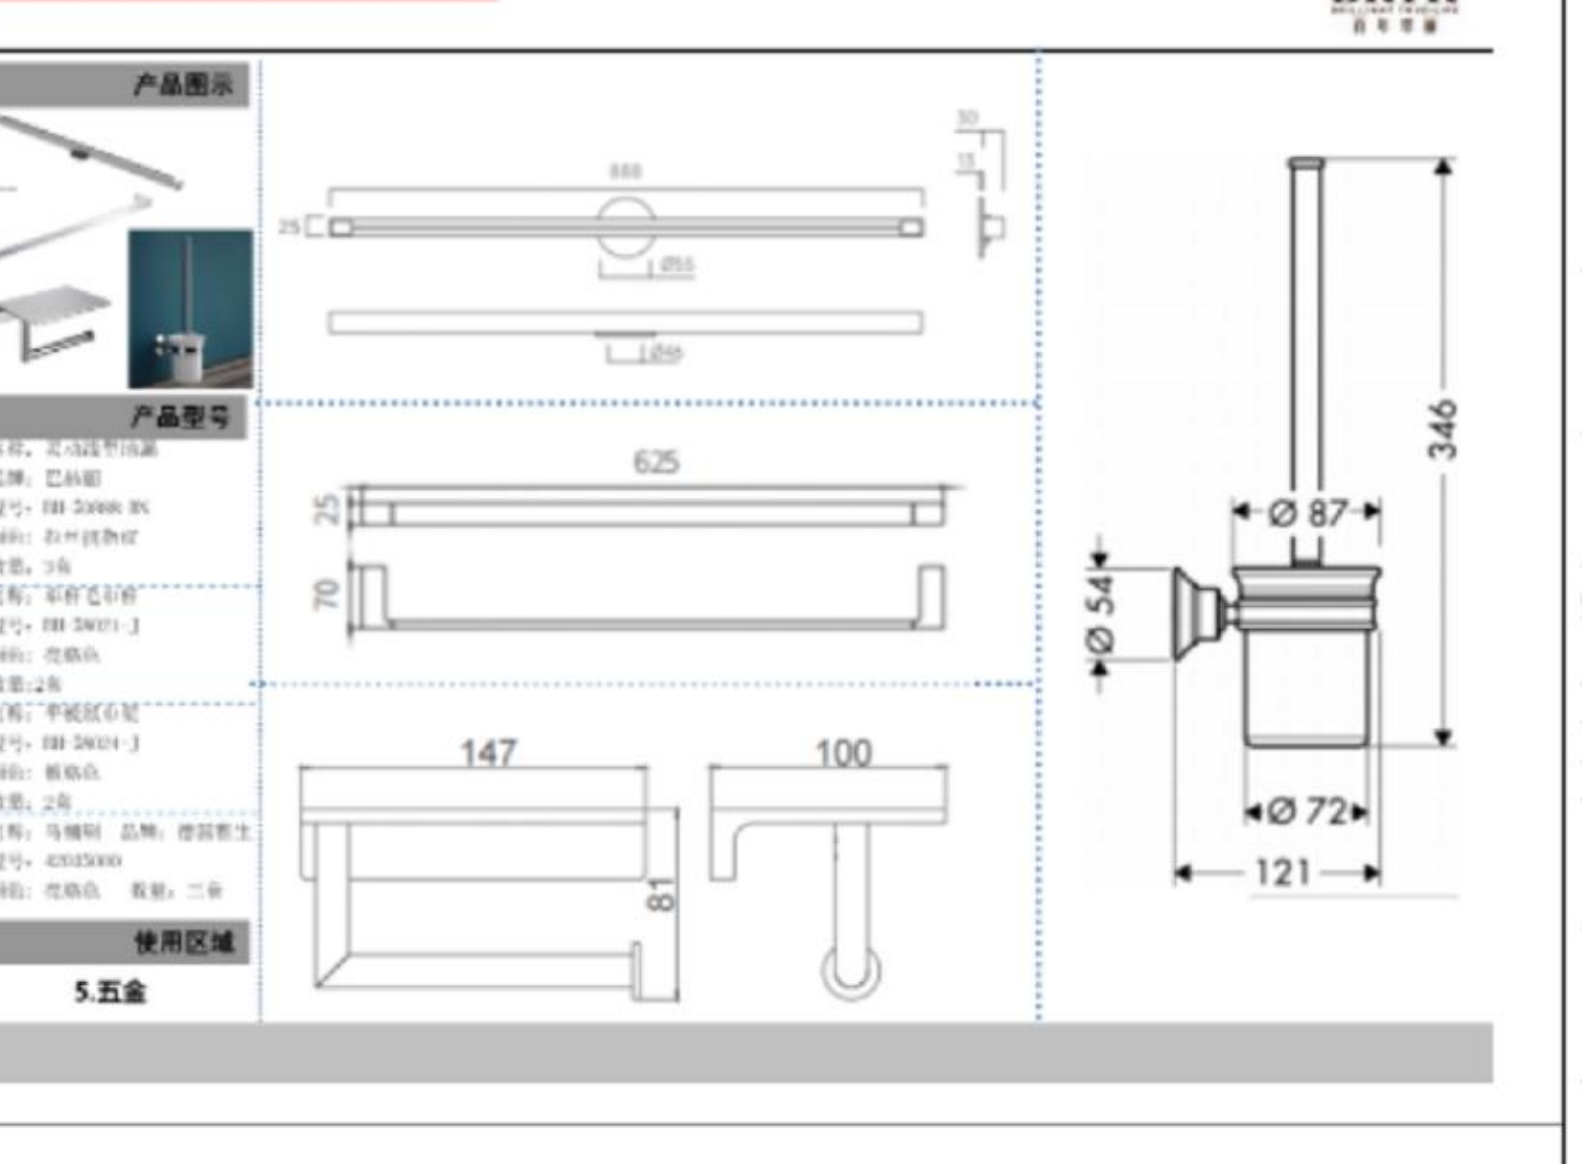

百年翠丽卫浴产品技术图纸

BRTR

产品图示

产品型号

使用区域

5.五金

625
147
100
25
70
346
Ø 87
Ø 54
Ø 72
121

LEGEND图例

编号	图例	说明
1	🟥	强电
2	▬	弱电
3	🟩	给水
4	▬	排水
5	▬	排水(原有)
6	🟥	冷媒进管
7	▬	冷媒出管
8	▬	冷凝水管
9	▬	等电位接地线
10	▬	原结构
11	▬	墙面抹灰≈15mm
12	▭	灰缝≈15mm
13	▬	地面找平层≈15mm
14	▬	墙面砖粘结层≈7mm
15	▬	防水背衬板≈12mm
16	▭	[illegible]≈18mm
17	▭	[illegible]≈18mm
18	▭	[illegible]大理石≈18mm
19	▭	[illegible]大理石≈18mm

签章

注释
Notes

日期
Date
06/06/26

修订
Revision

项目
Project
潮映华岸府3-801

比例
Scale
主卫洁具分析图

图纸编号
Drawing No.
ST-17

项目编号
Project No.
#2025

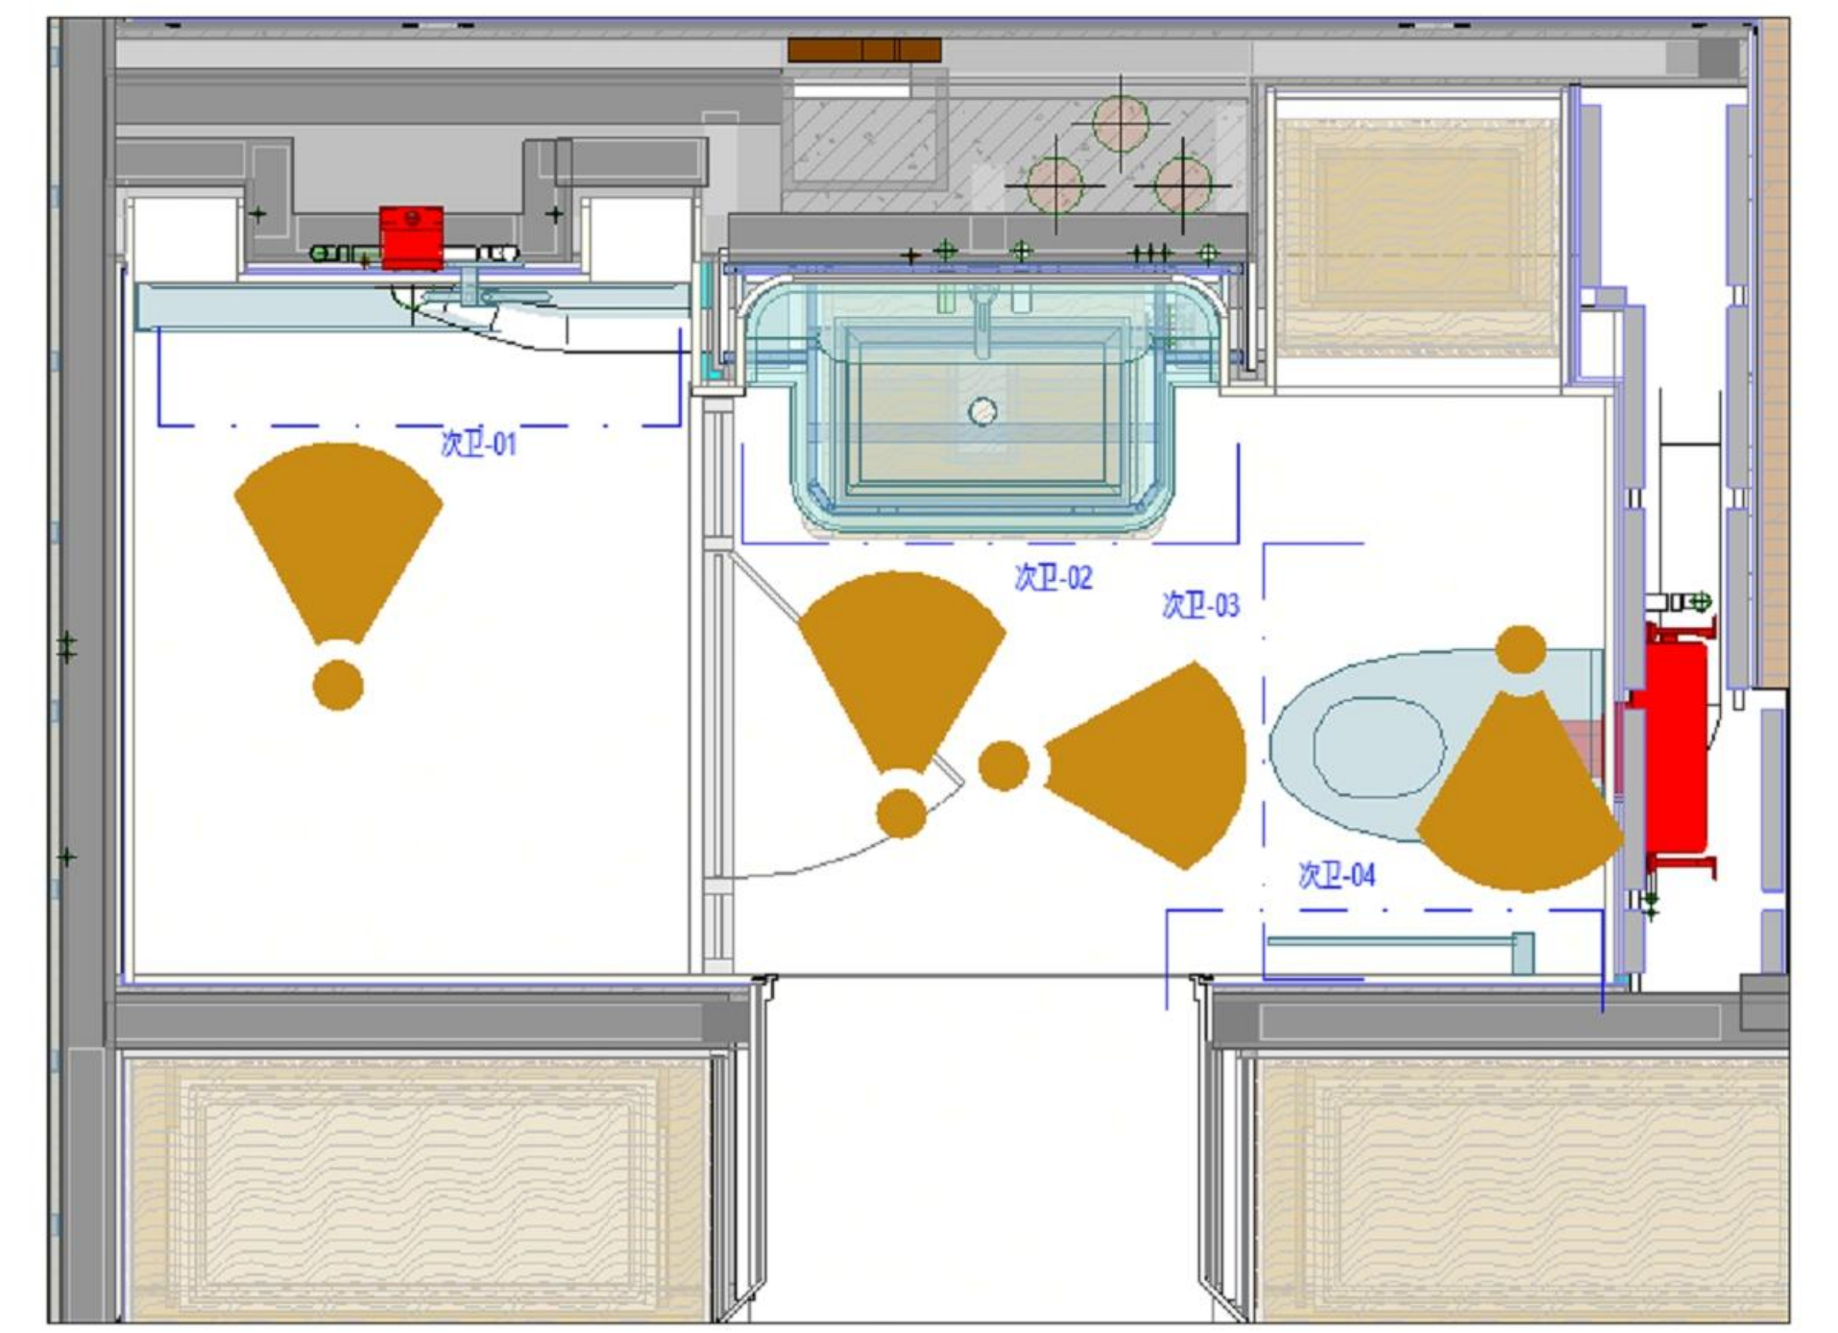
次卫-01
次卫-02
次卫-03
次卫-04

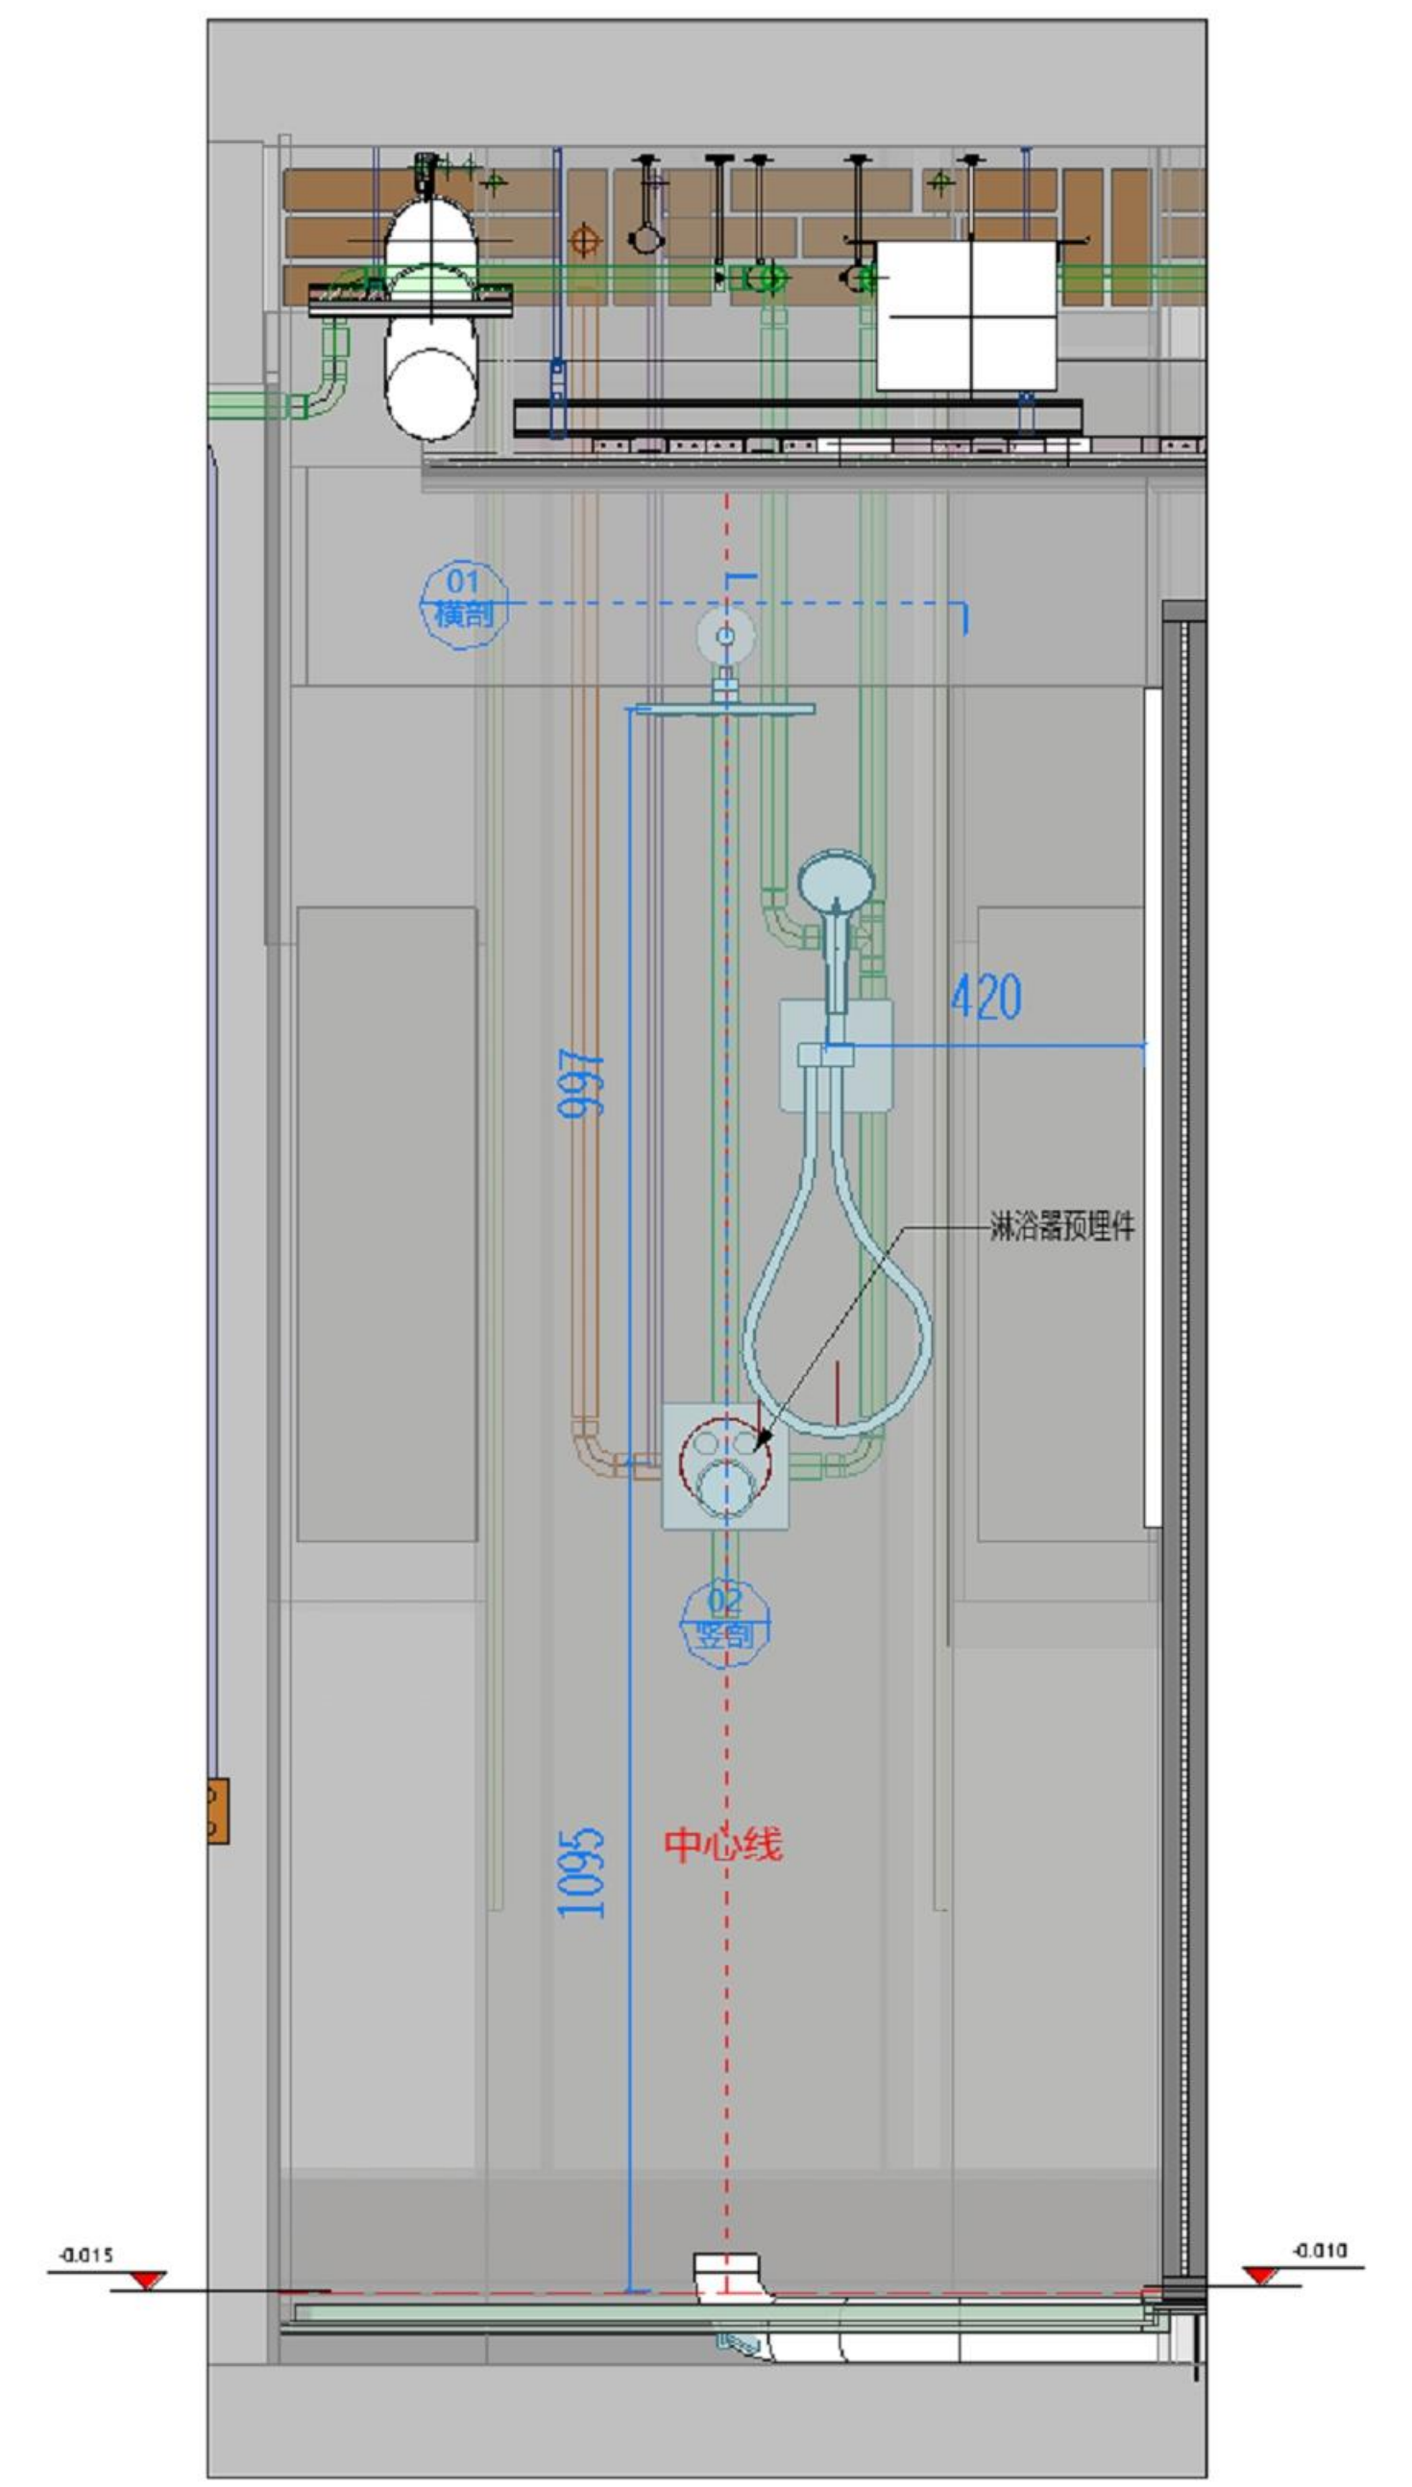
01
横剖
420
997
淋浴器预埋件
02
竖剖
1095
中心线
-0.015
-0.010

次卫-01

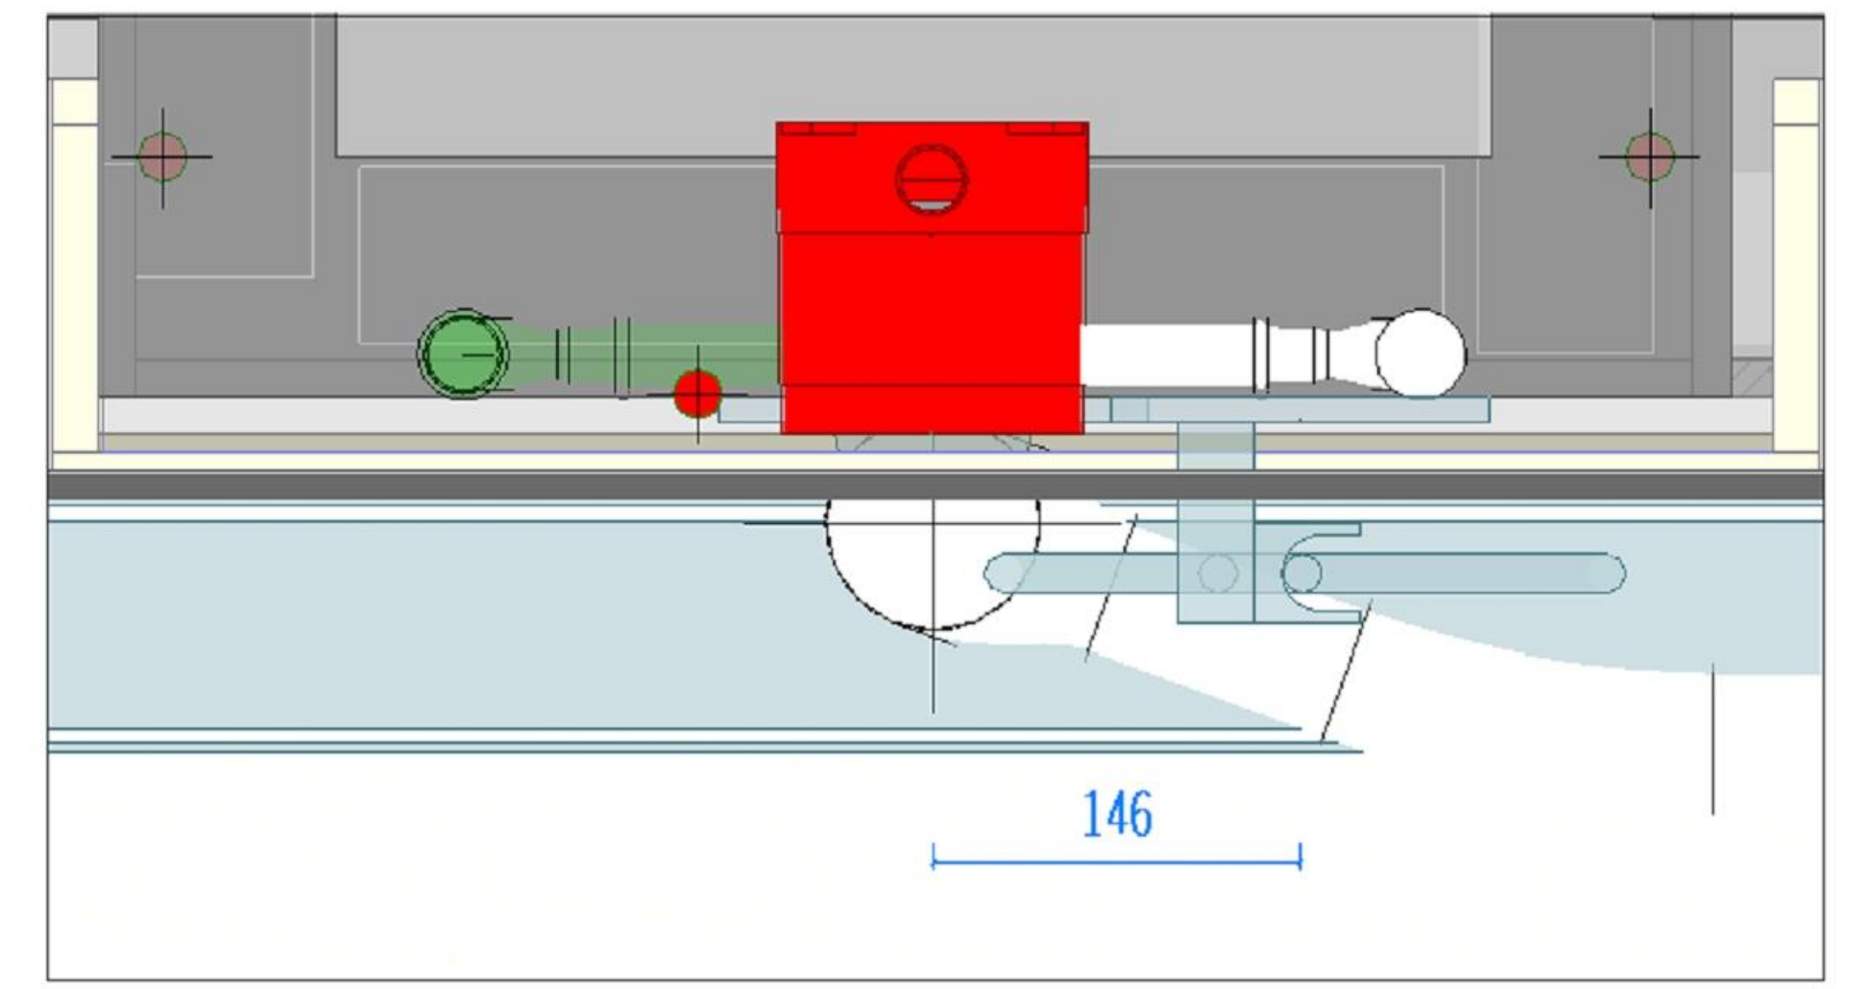

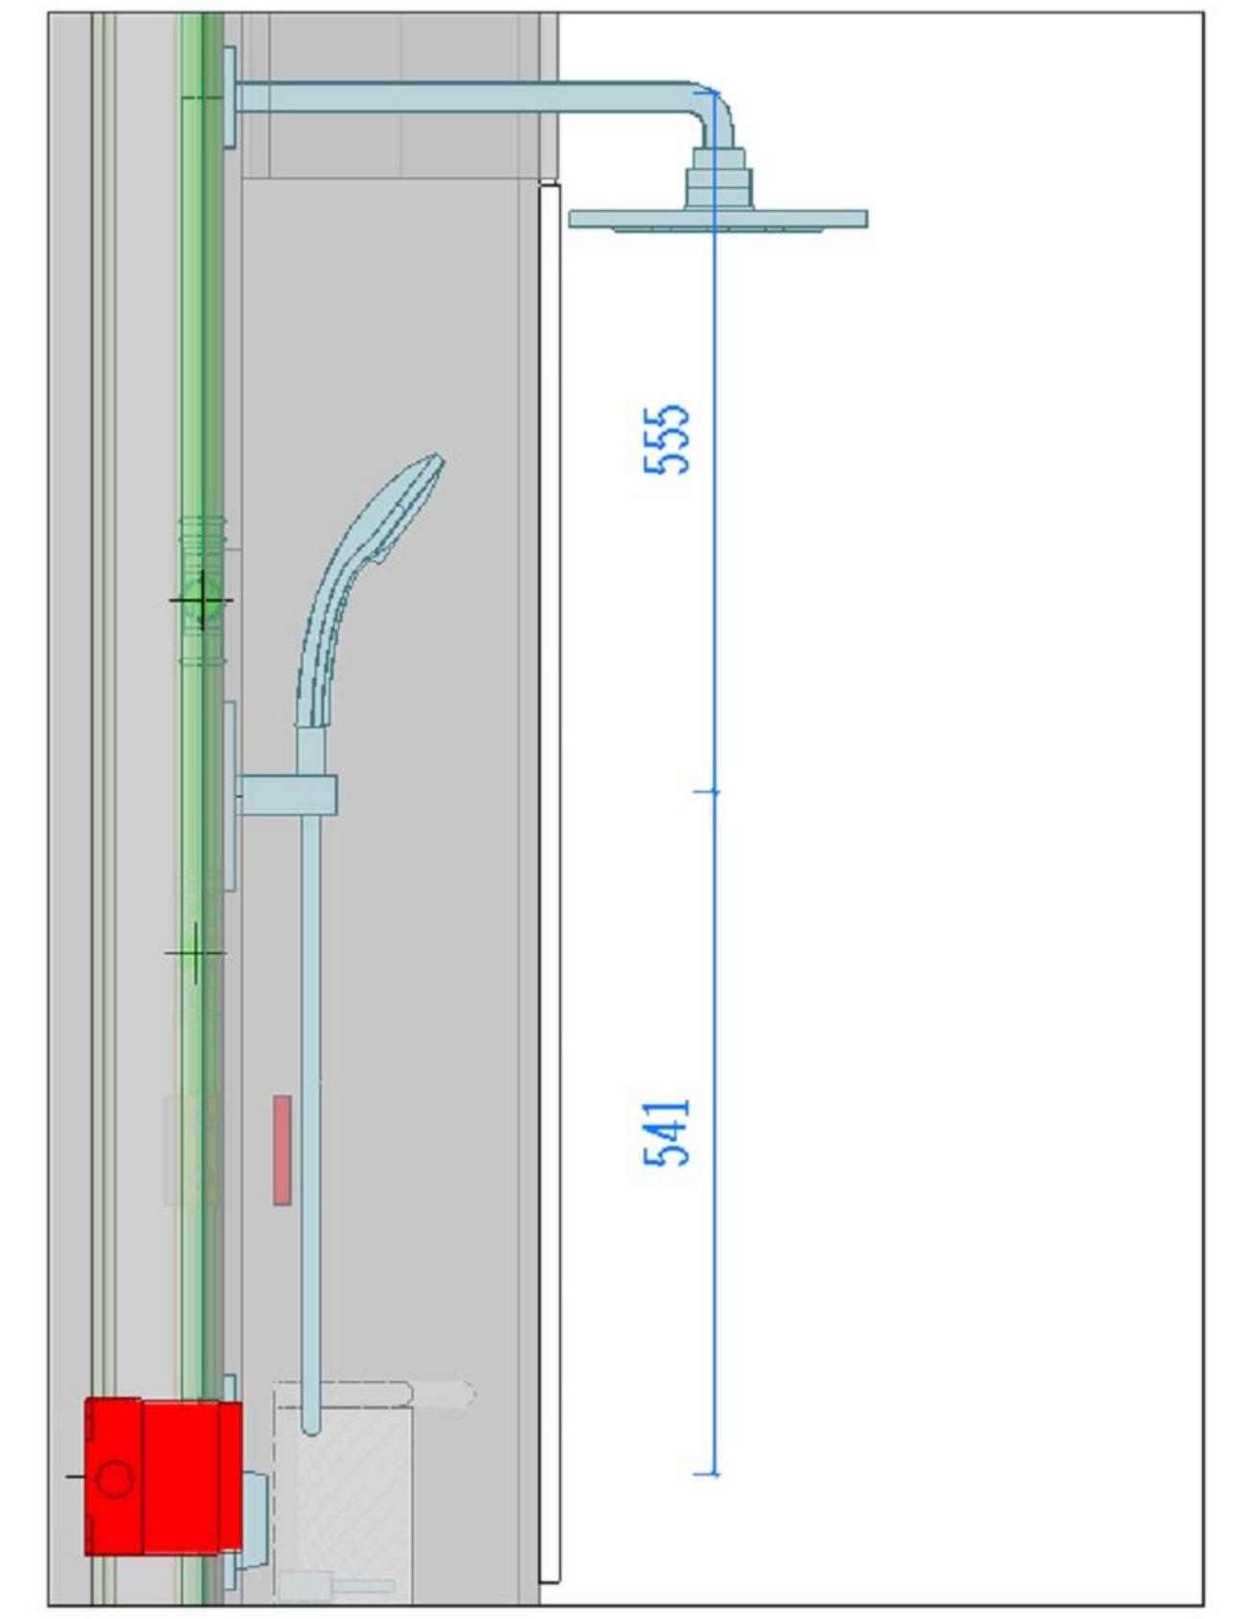

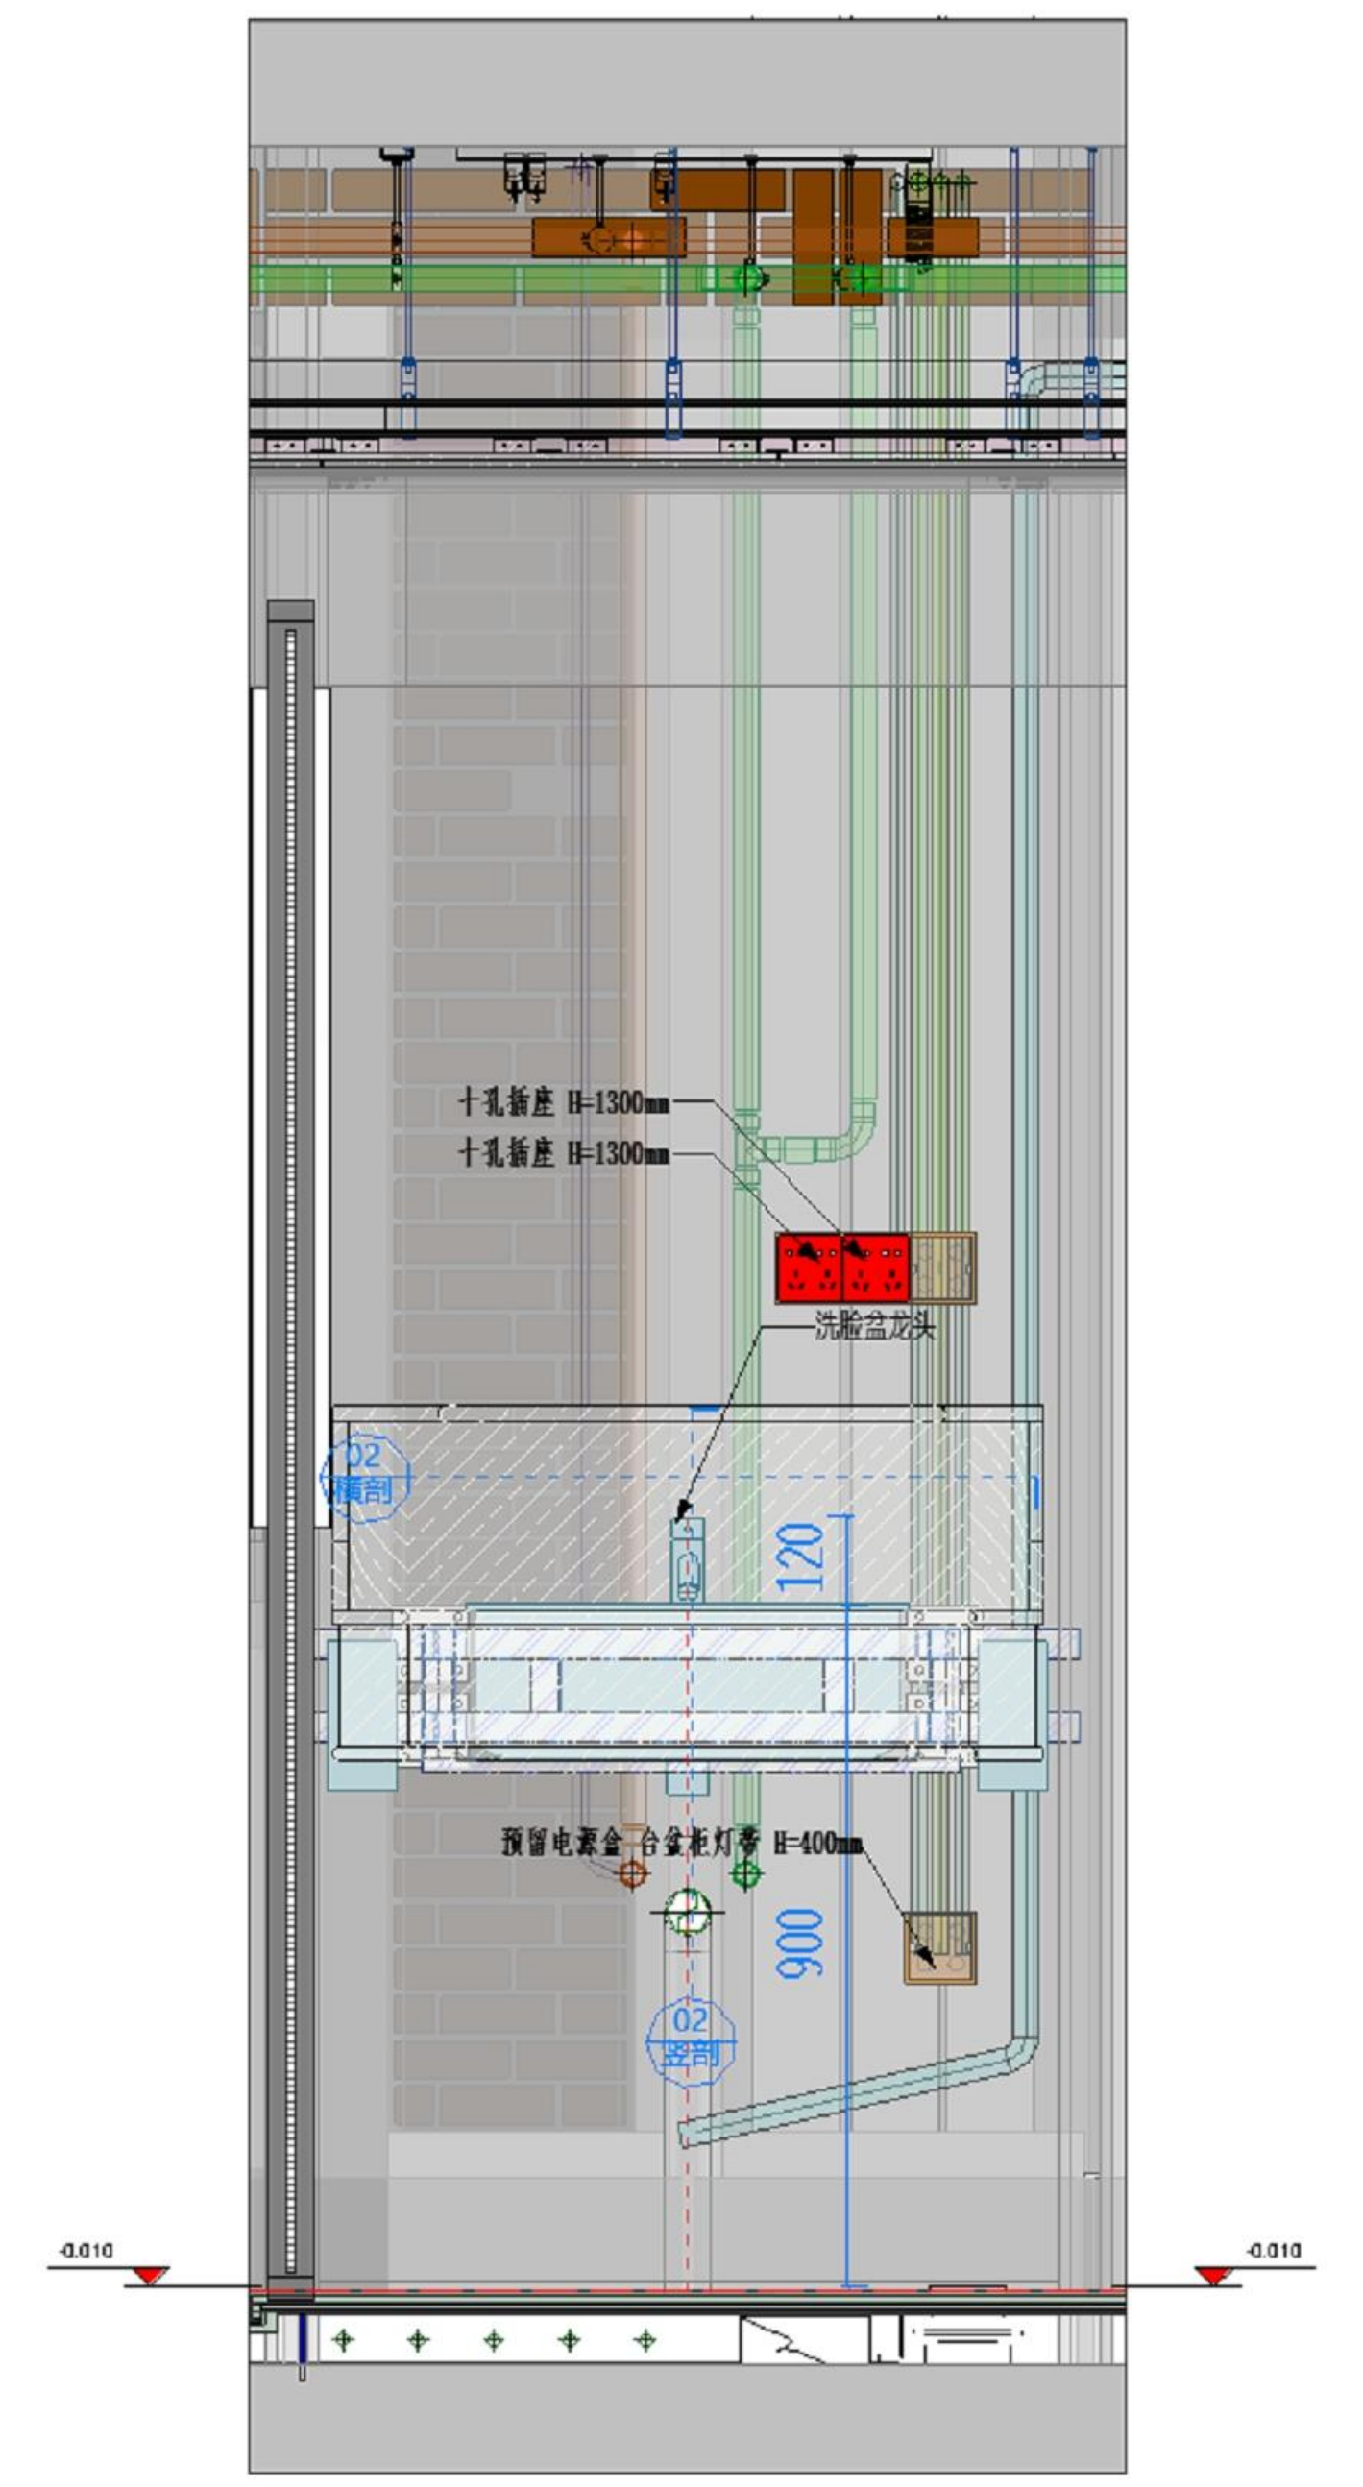
十孔插座 H=1300mm
十孔插座 H=1300mm
洗脸盆龙头
02
横剖
120
预留电源盒 台盆灯带 H=400mm
900
02
竖剖
-0.010
-0.010

次卫-02

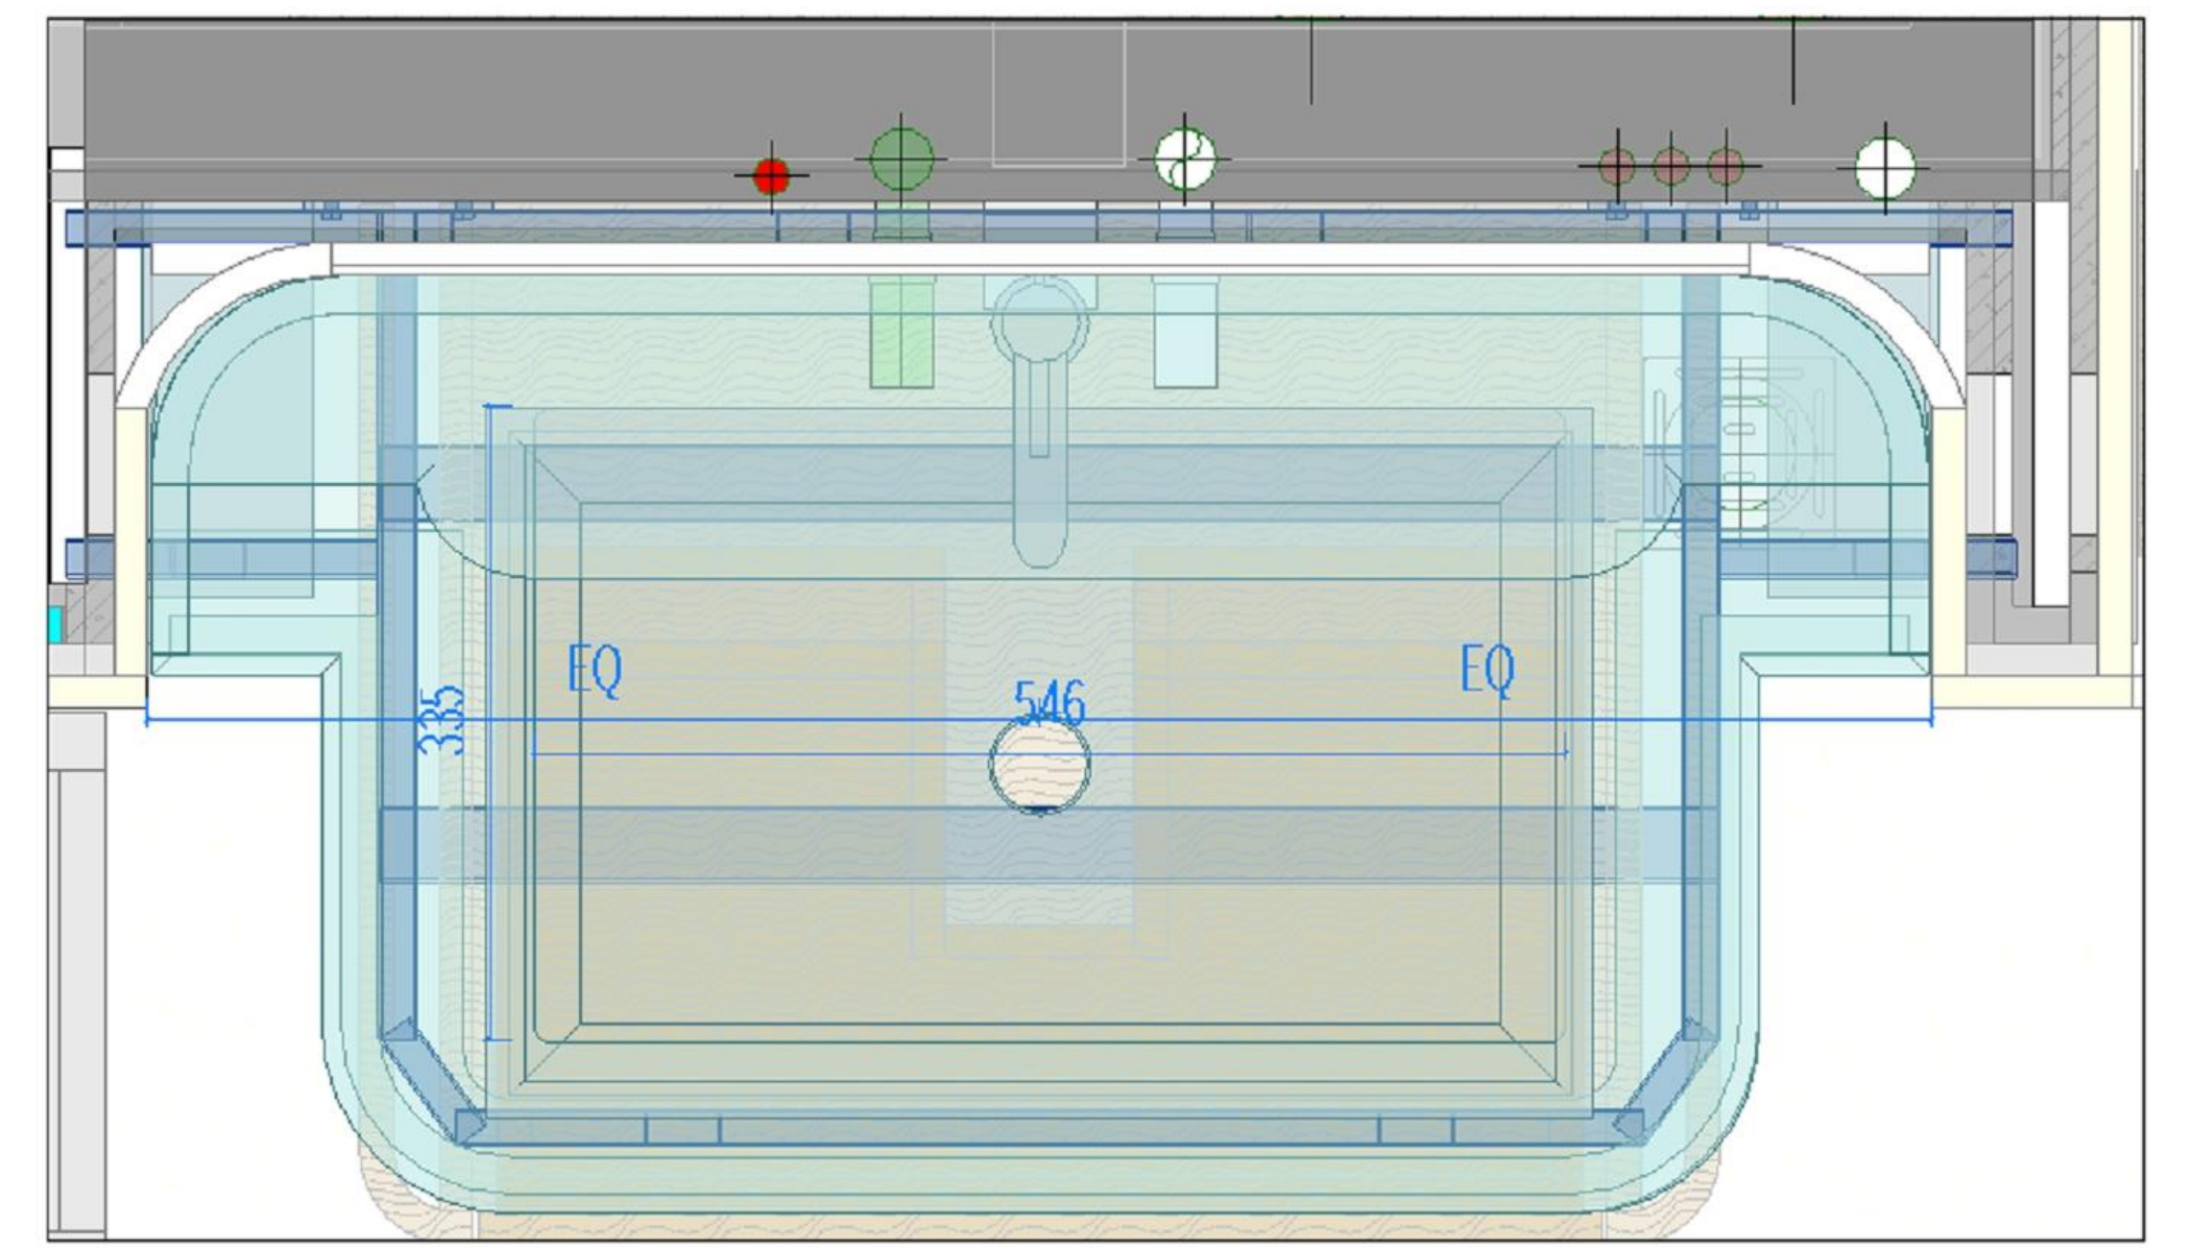
335
EQ
546
EQ

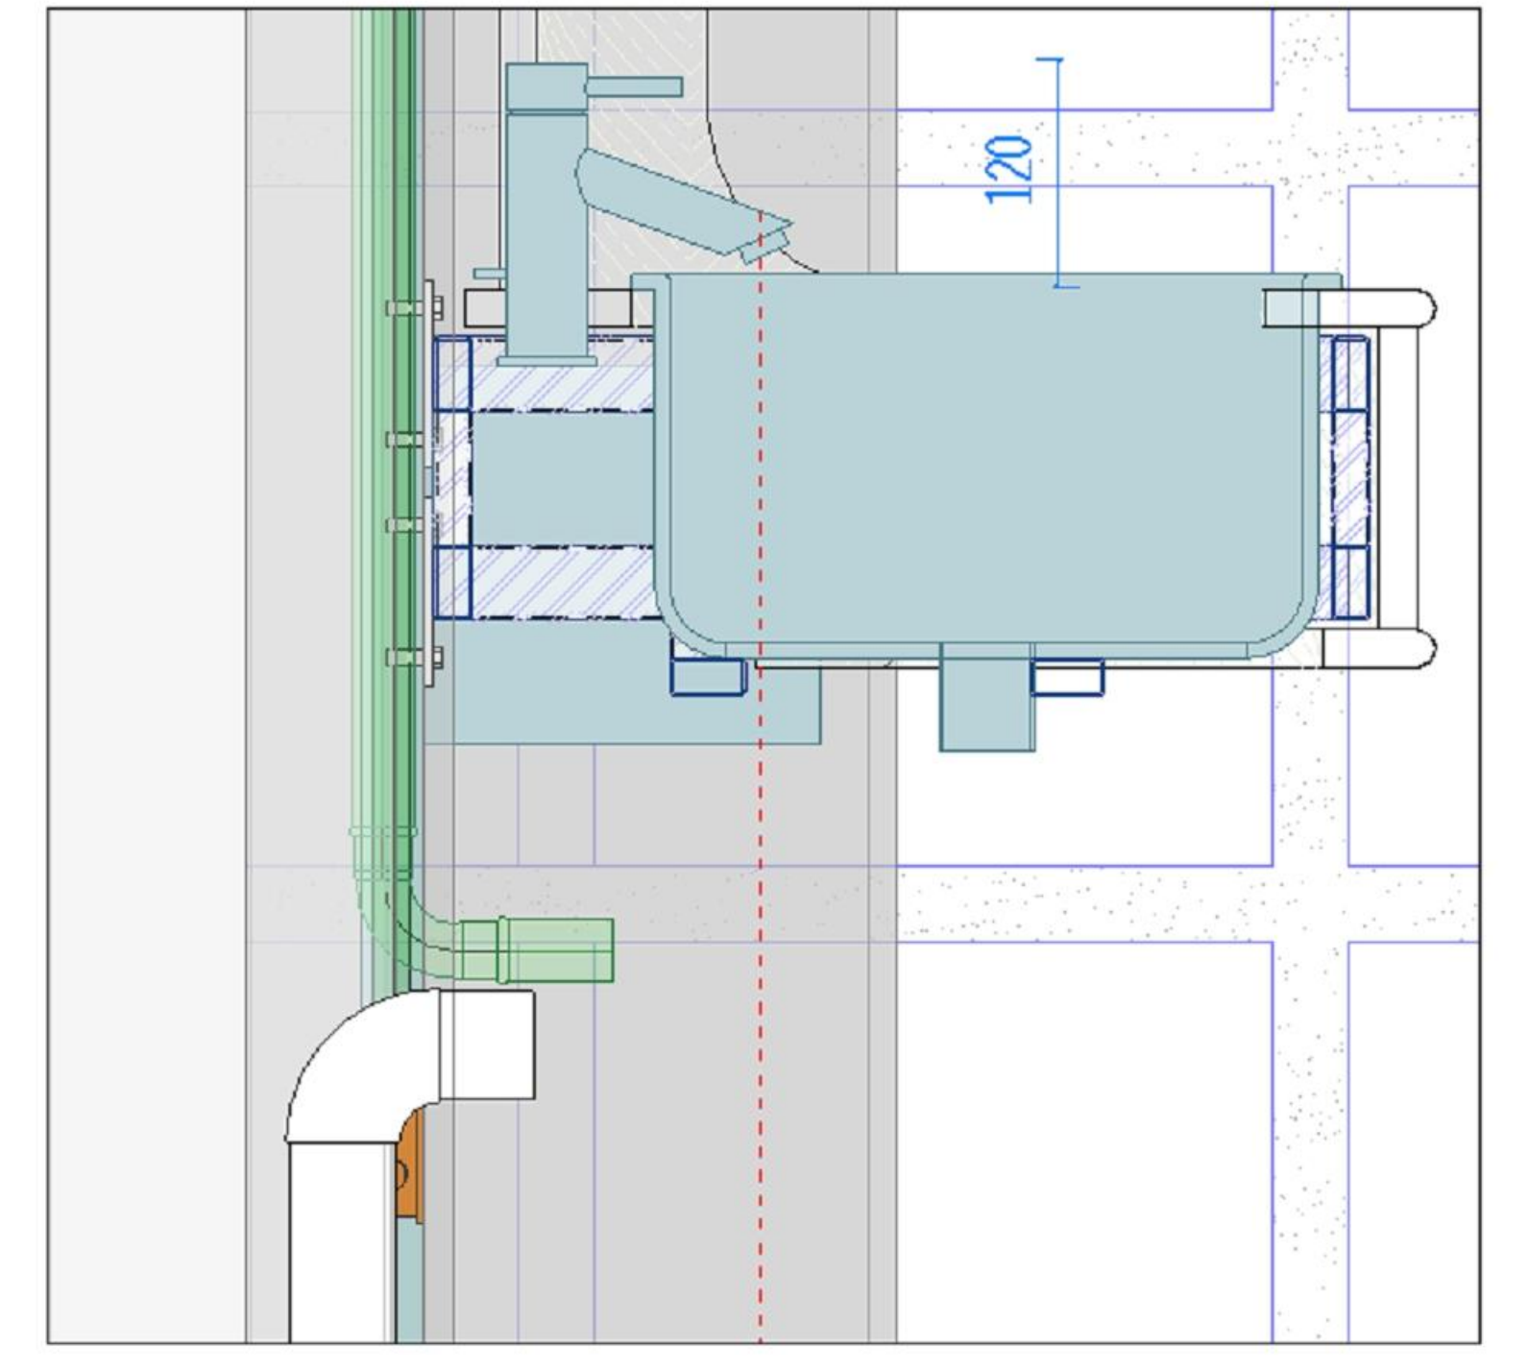

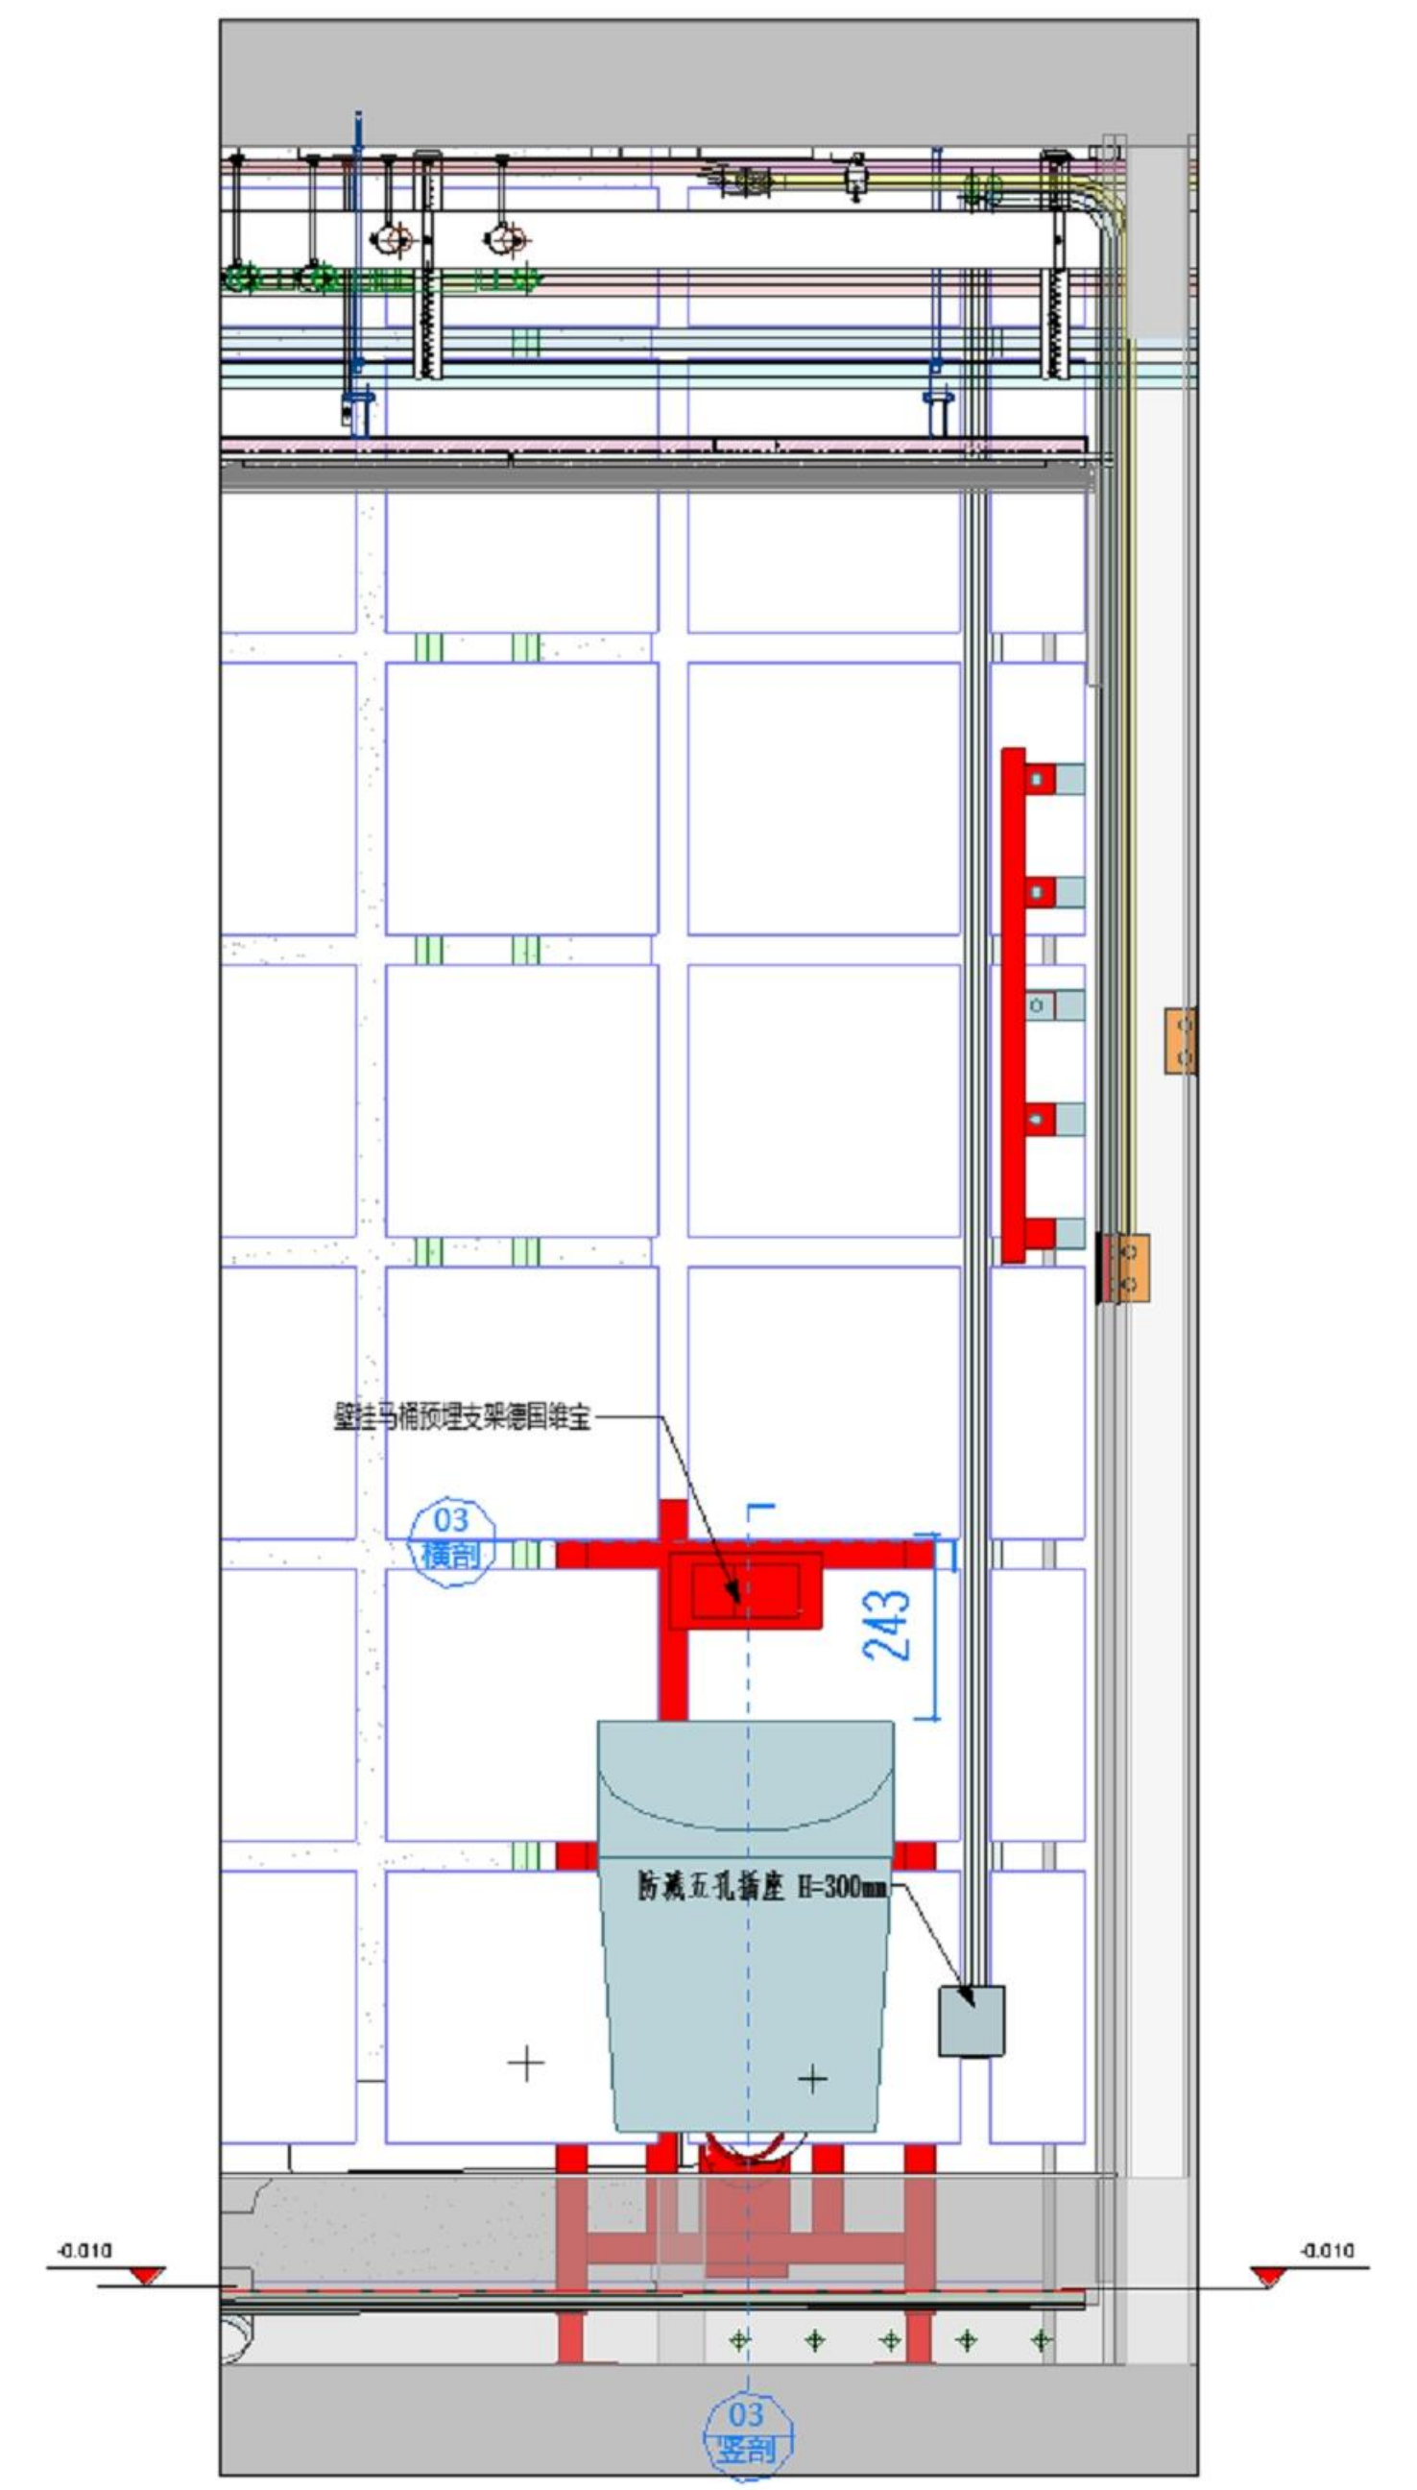
壁挂马桶预埋支架德国维宝
03
横剖
243
防溅五孔插座 H=300mm
-0.010
-0.010
03
竖剖

次卫-03

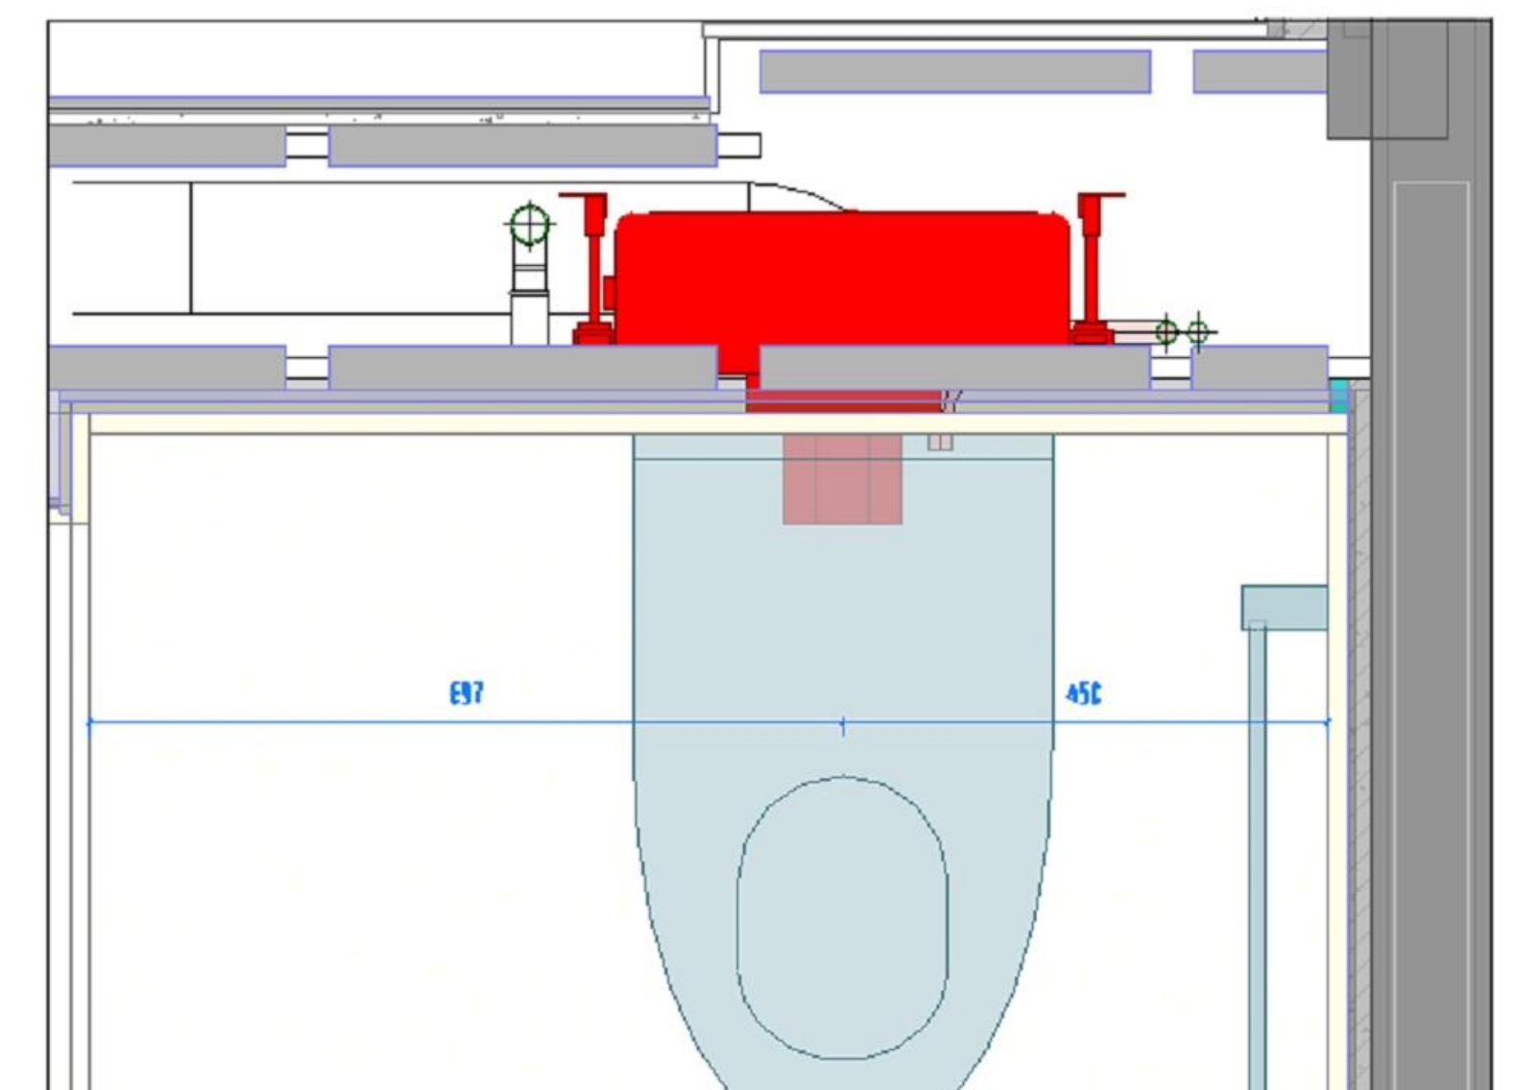

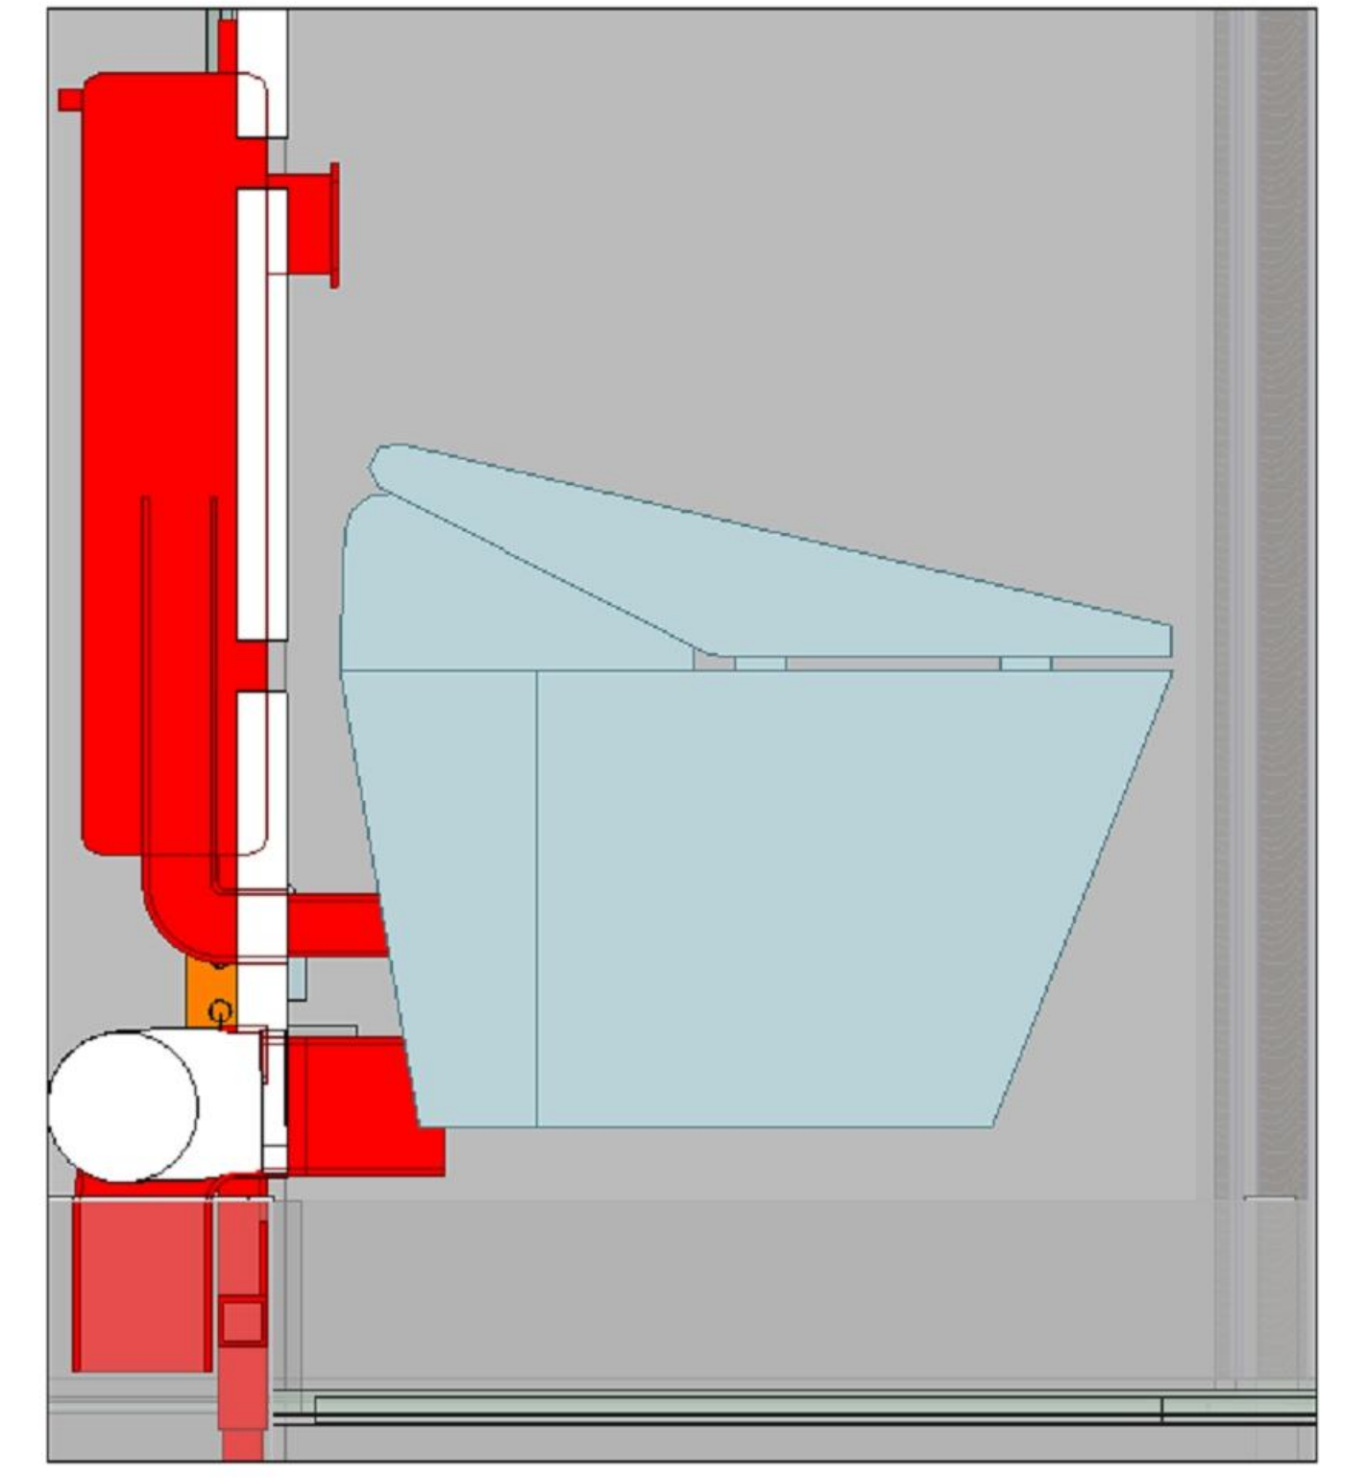

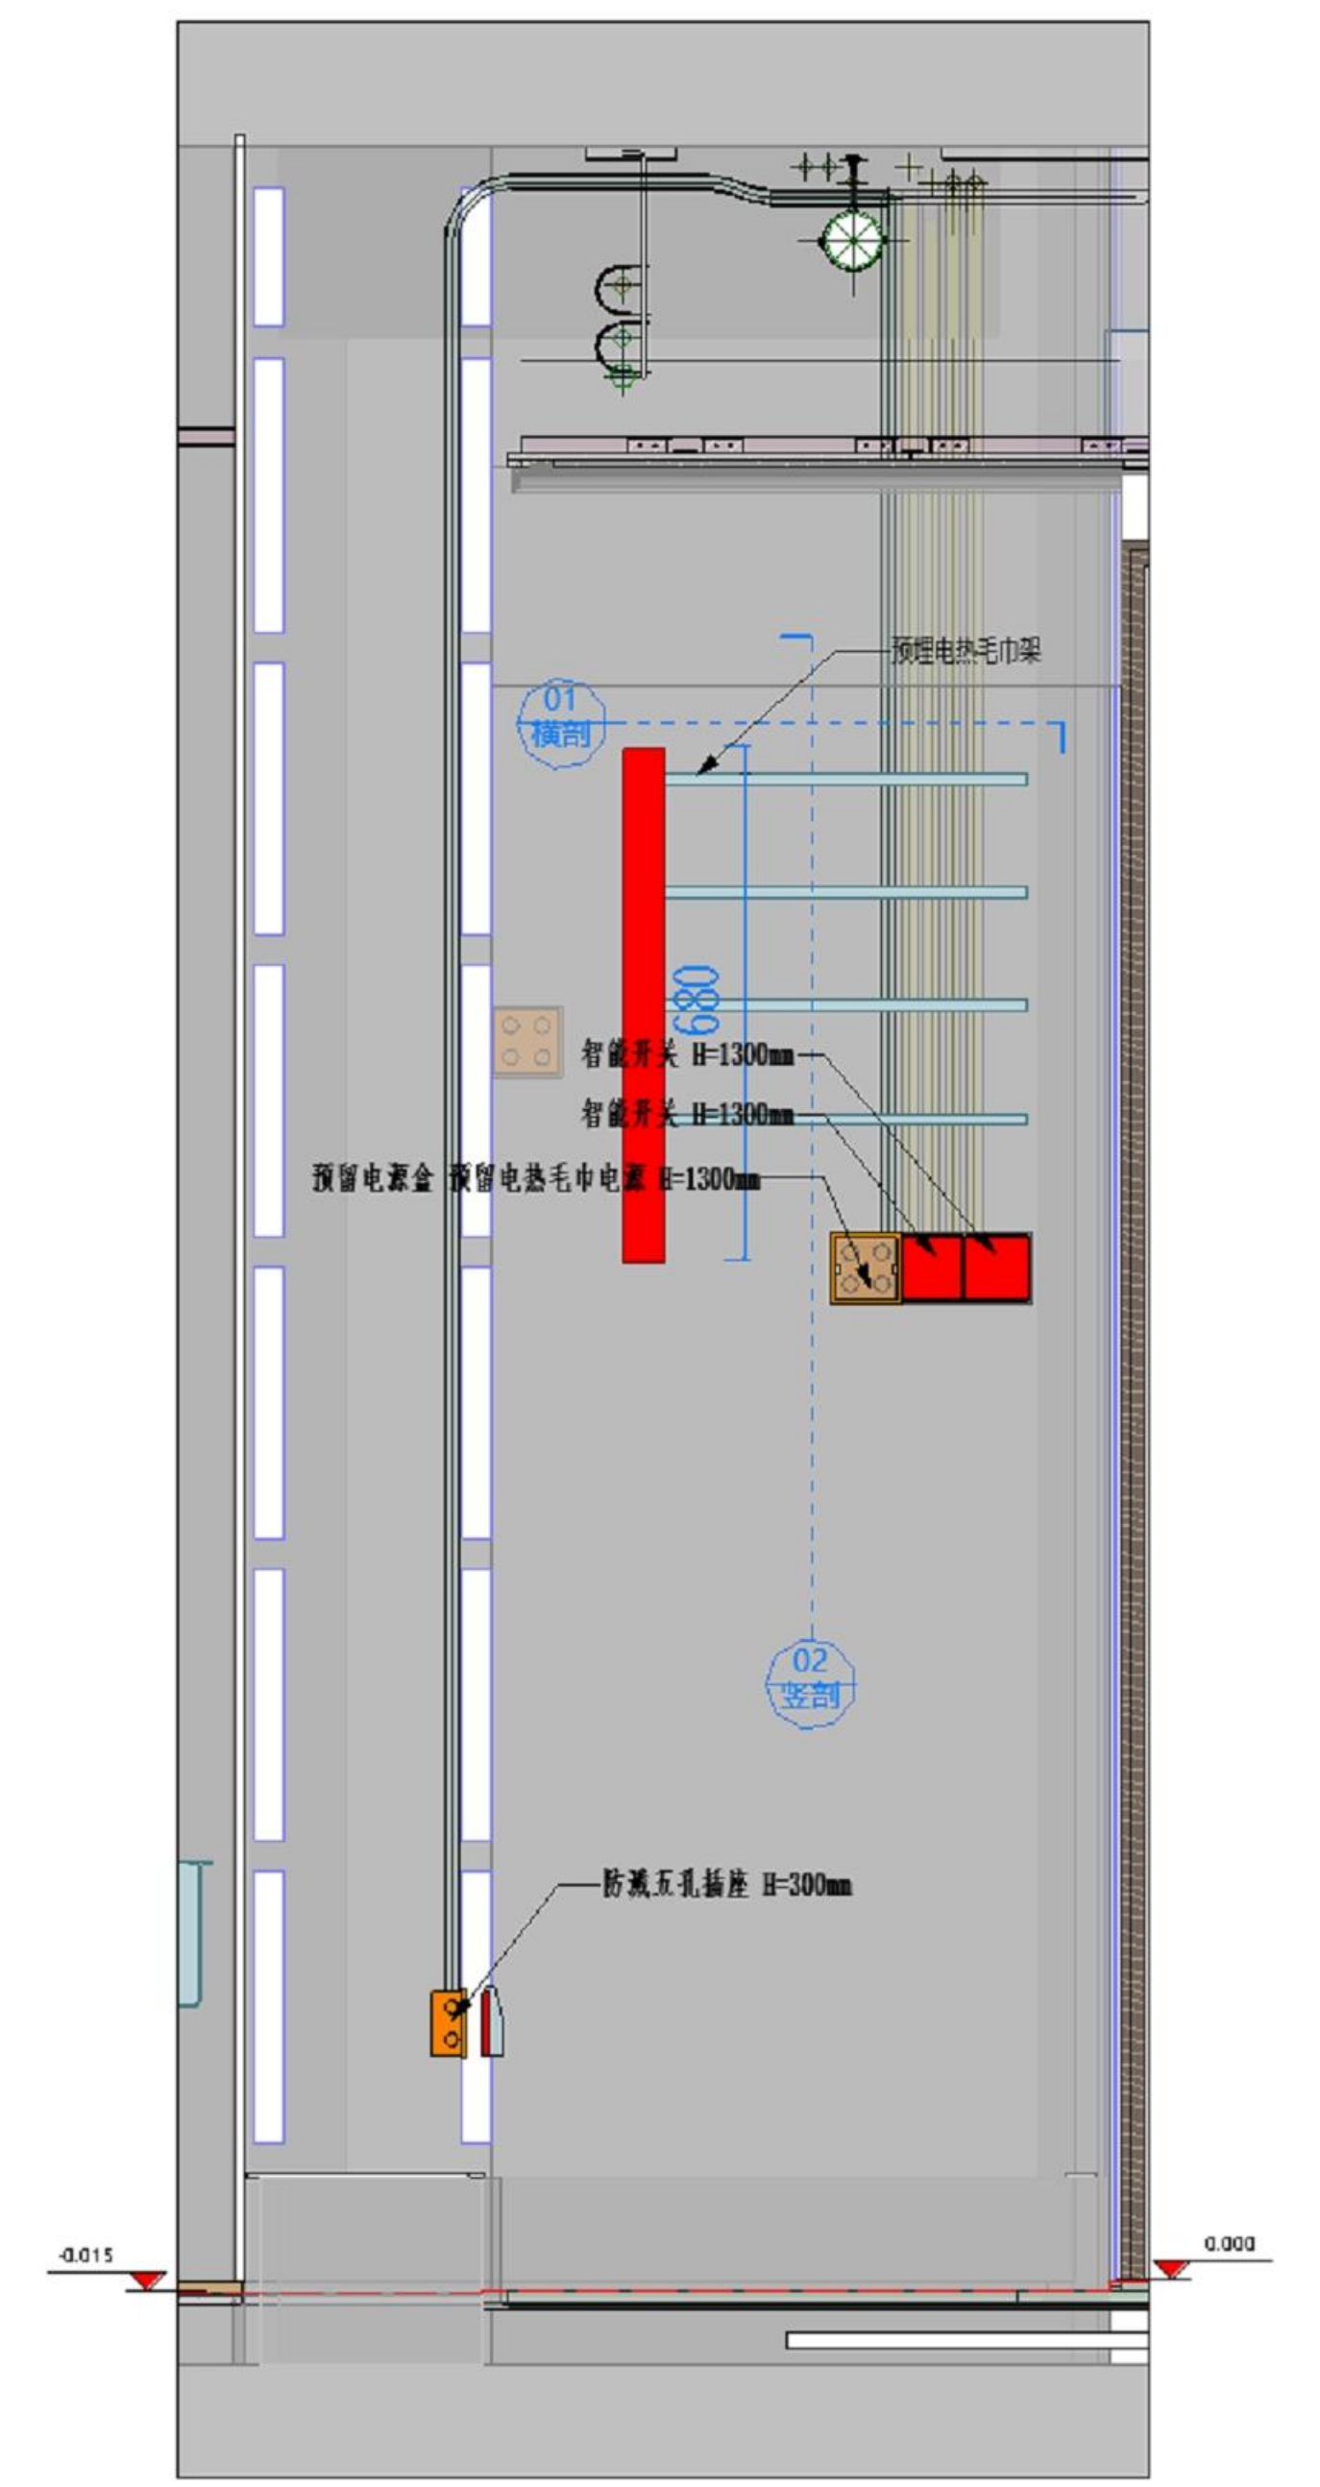
预埋电热毛巾架
01
横剖
680
智能开关 H=1300mm
智能开关 H=1300mm
预留电源盒 预留电热毛巾电源 H=1300mm
02
竖剖
防溅五孔插座 H=300mm
-0.011
0.000

次卫-04

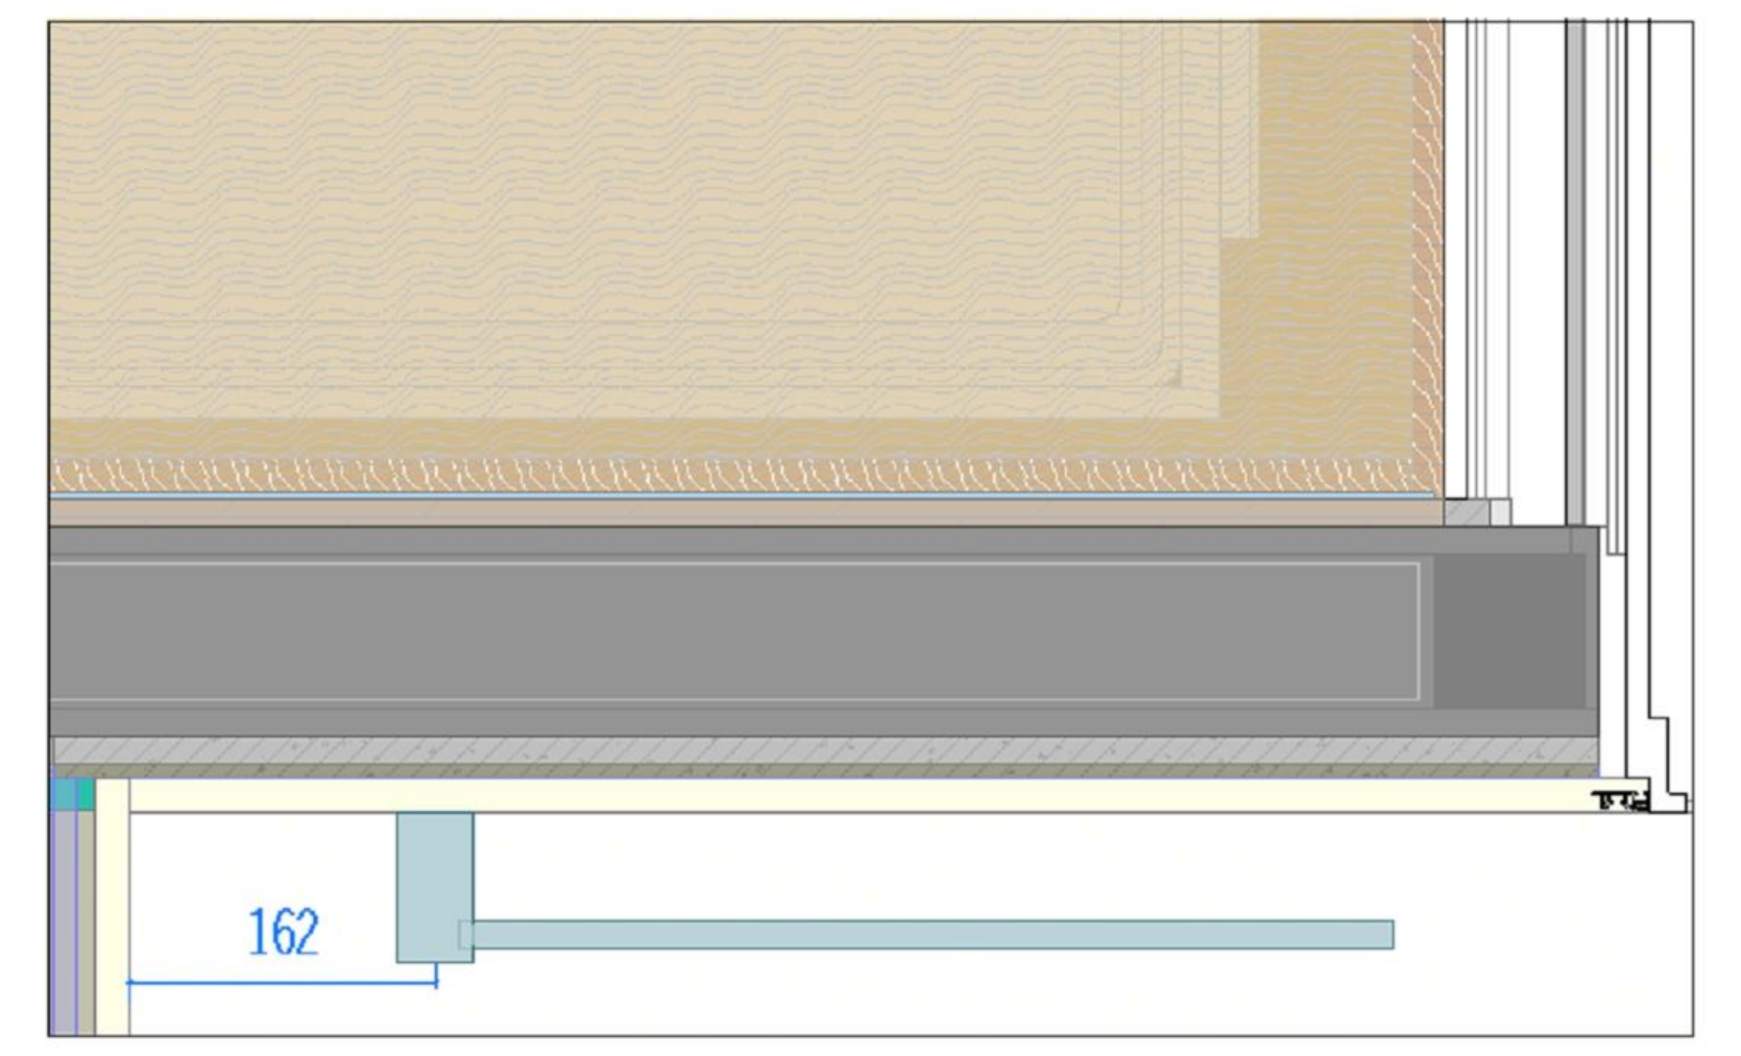

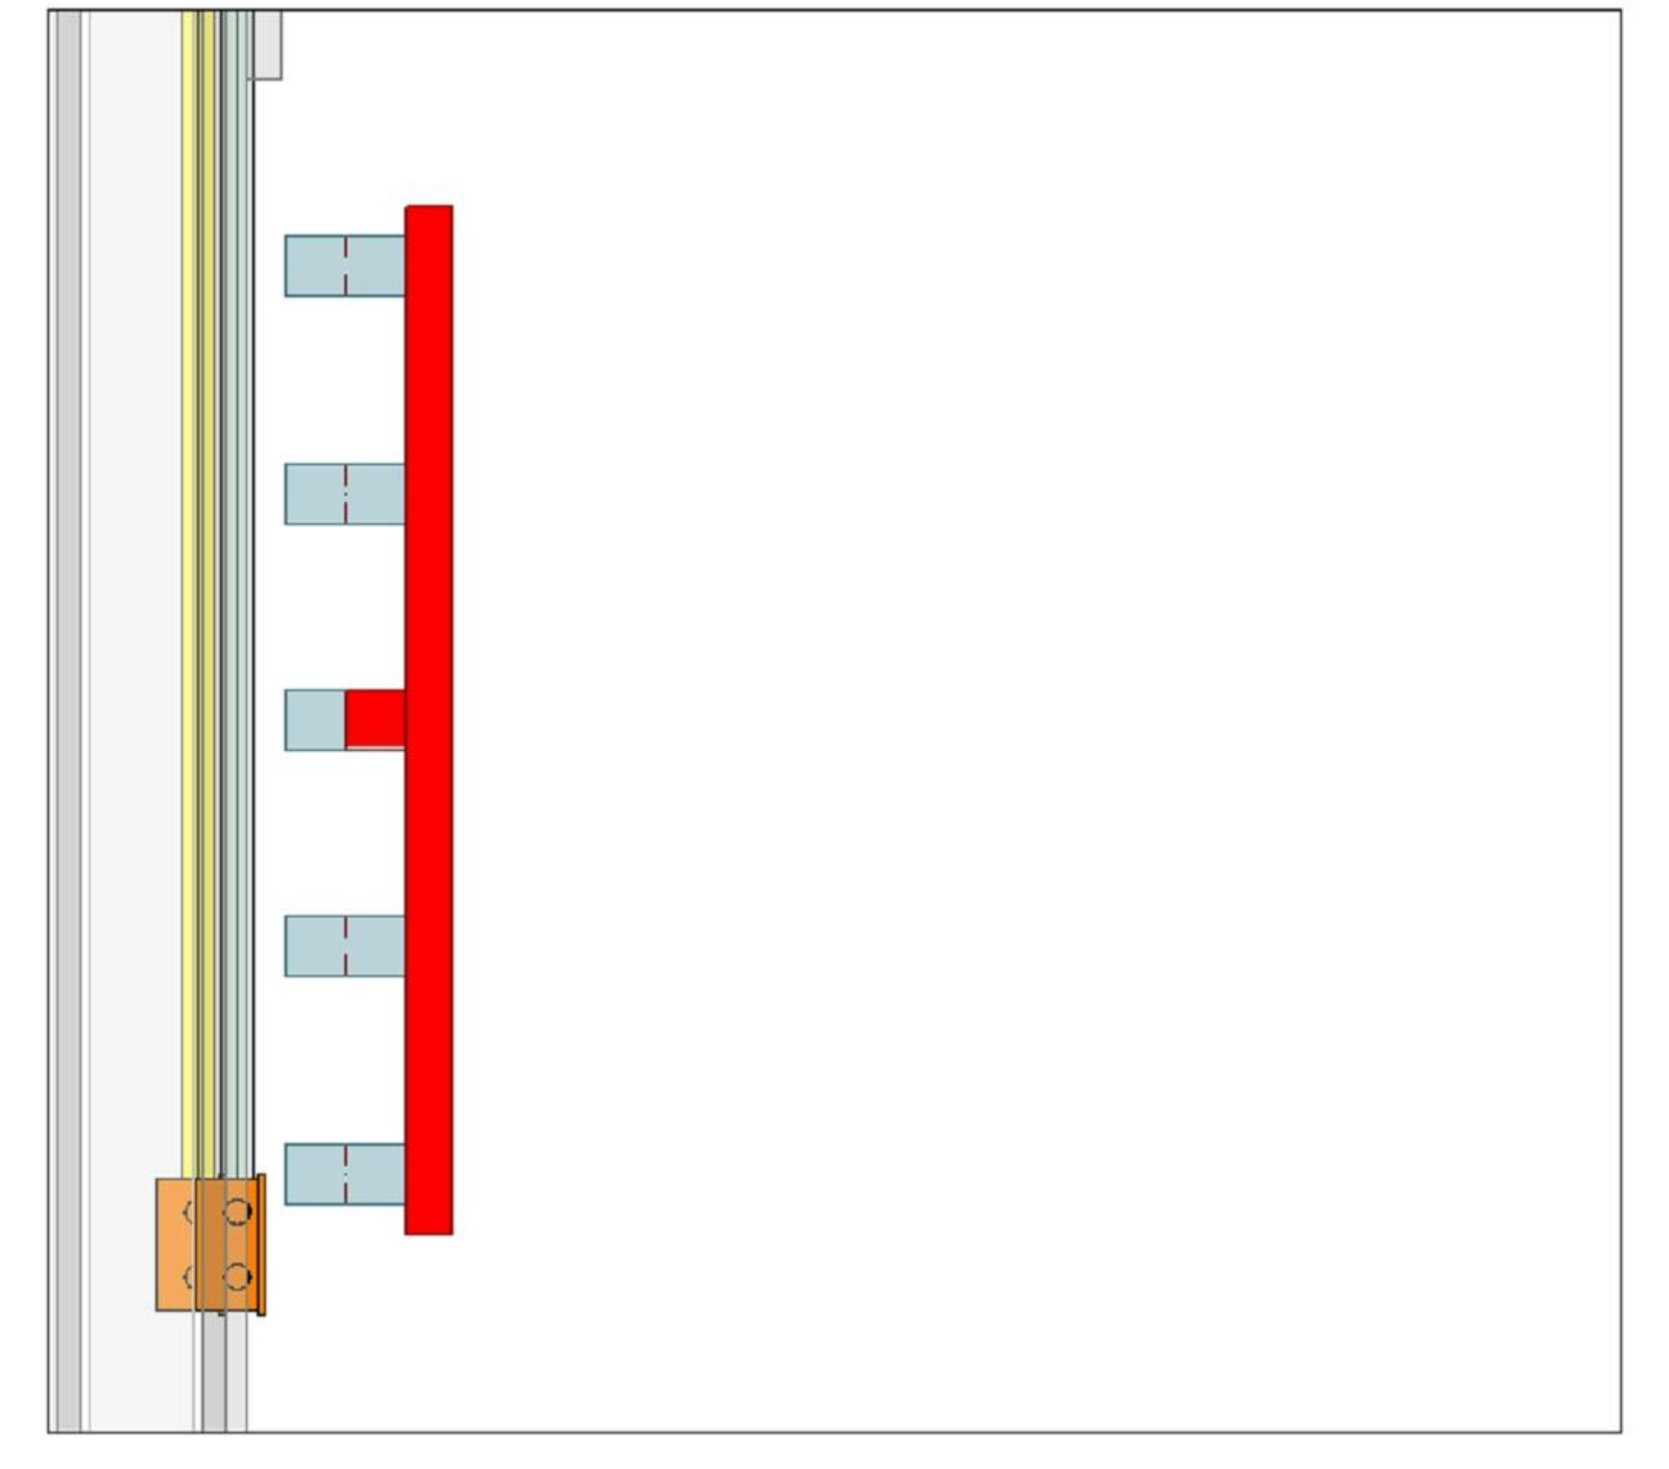

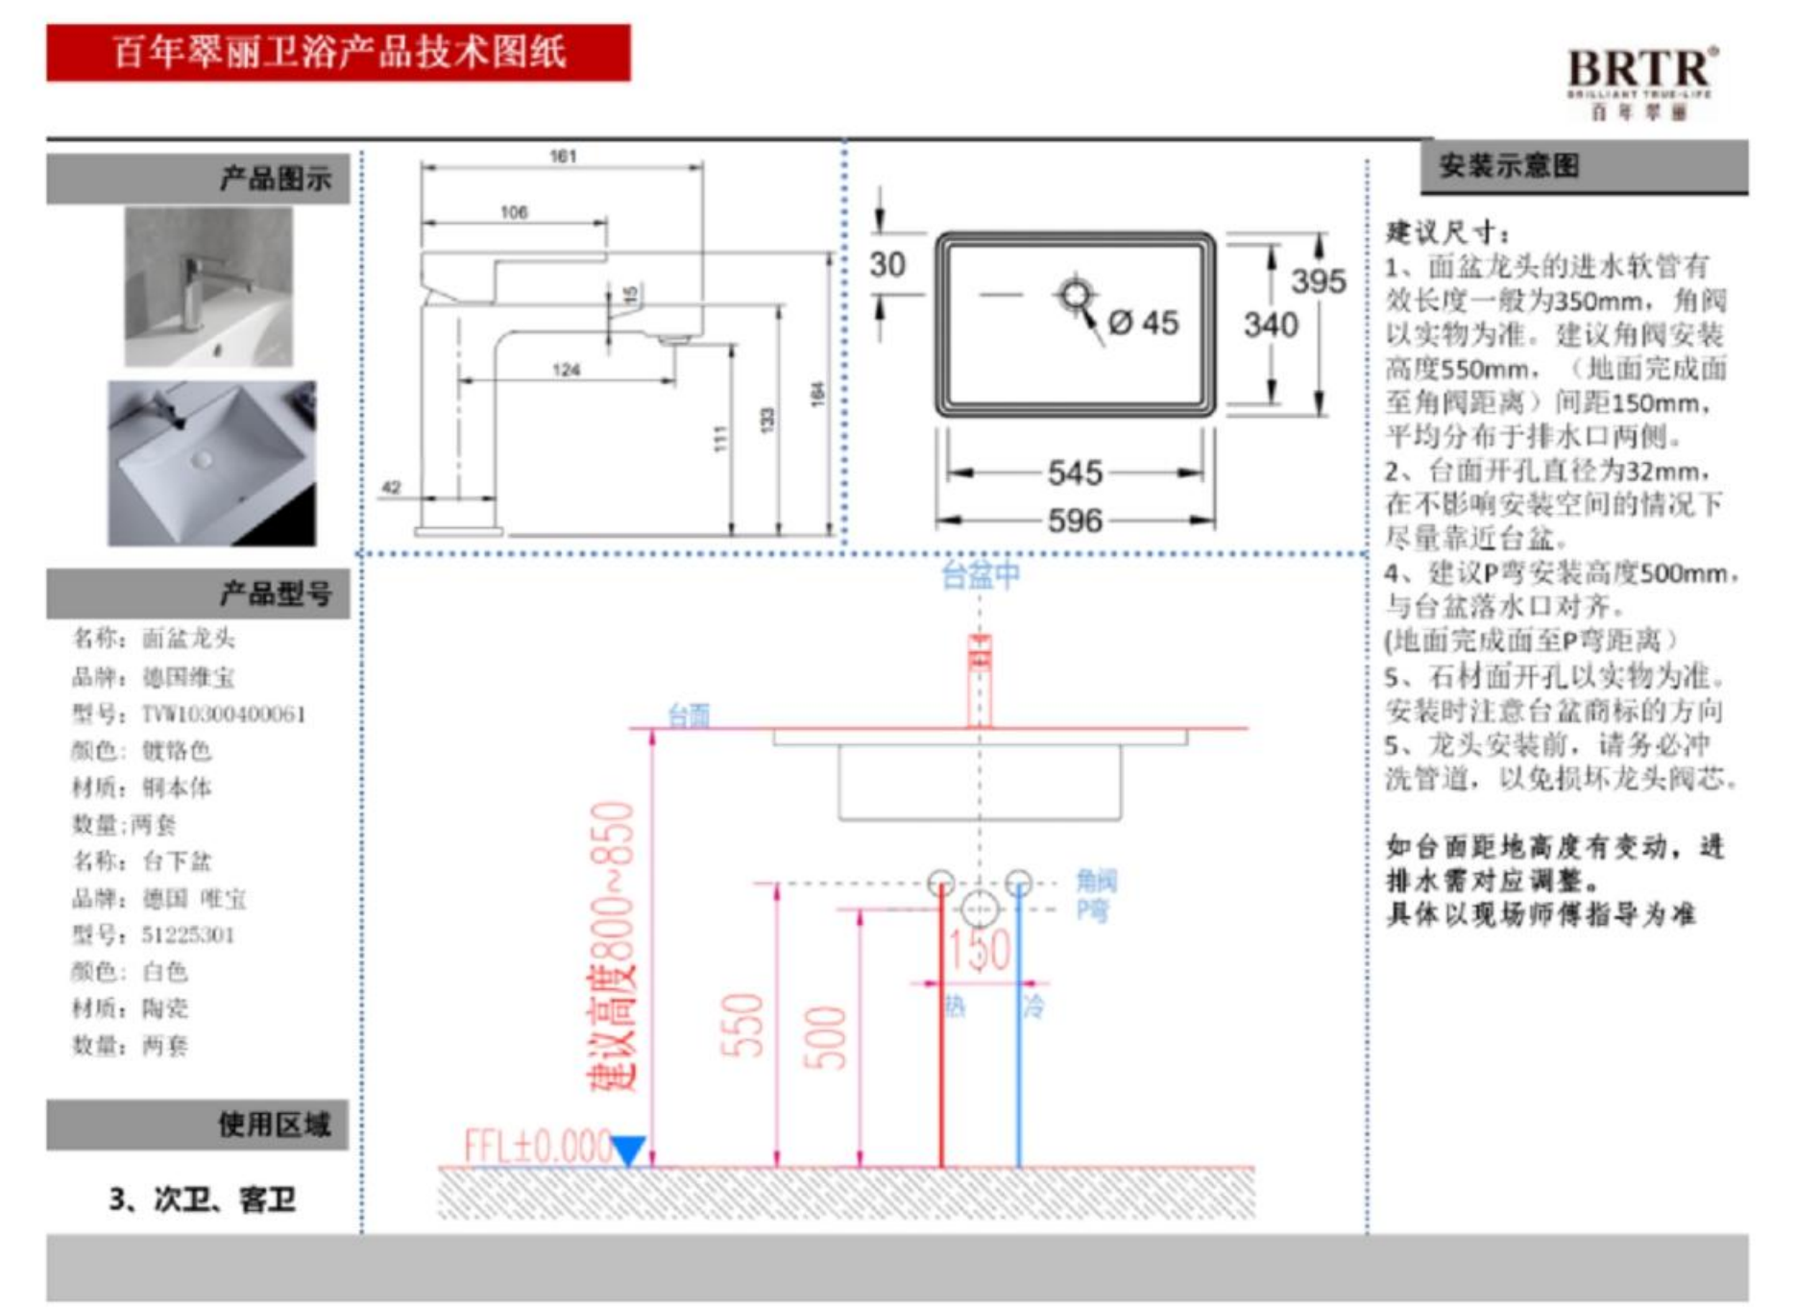

百年翠丽卫浴产品技术图纸

BRTR

产品图示

产品型号

名称：面盆龙头
品牌：德国维宝
型号：TVW10300400061
颜色：镀铬色
材质：铜本体
数量：两套
名称：台下盆
品牌：德国 唯宝
型号：51225301
颜色：白色
材质：陶瓷
数量：两套

使用区域

3、次卫、客卫

安装示意图

建议尺寸：
1、面盆龙头的进水软管有效长度一般为350mm，角阀以实物为准。建议角阀安装高度550mm，（地面完成面至角阀距离）间距150mm，平均分布于排水口两侧。
2、台面开孔直径为32mm，在不影响安装空间的情况下尽量靠近台盆。
4、建议P弯安装高度500mm，与台盆落水口对齐。
(地面完成面至P弯距离）
5、石材面开孔以实物为准。安装时注意台盆商标的方向
5、龙头安装前，请务必冲洗管道，以免损坏龙头阀芯。

如台面距地高度有变动，进排水需对应调整。
具体以现场师傅指导为准

161
106
15
124
42
111
133
164
30
Ø 45
395
340
545
596
台盆中
台面
角阀
P弯
150
热
冷
建议高度800~850
550
500
FFL±0.000

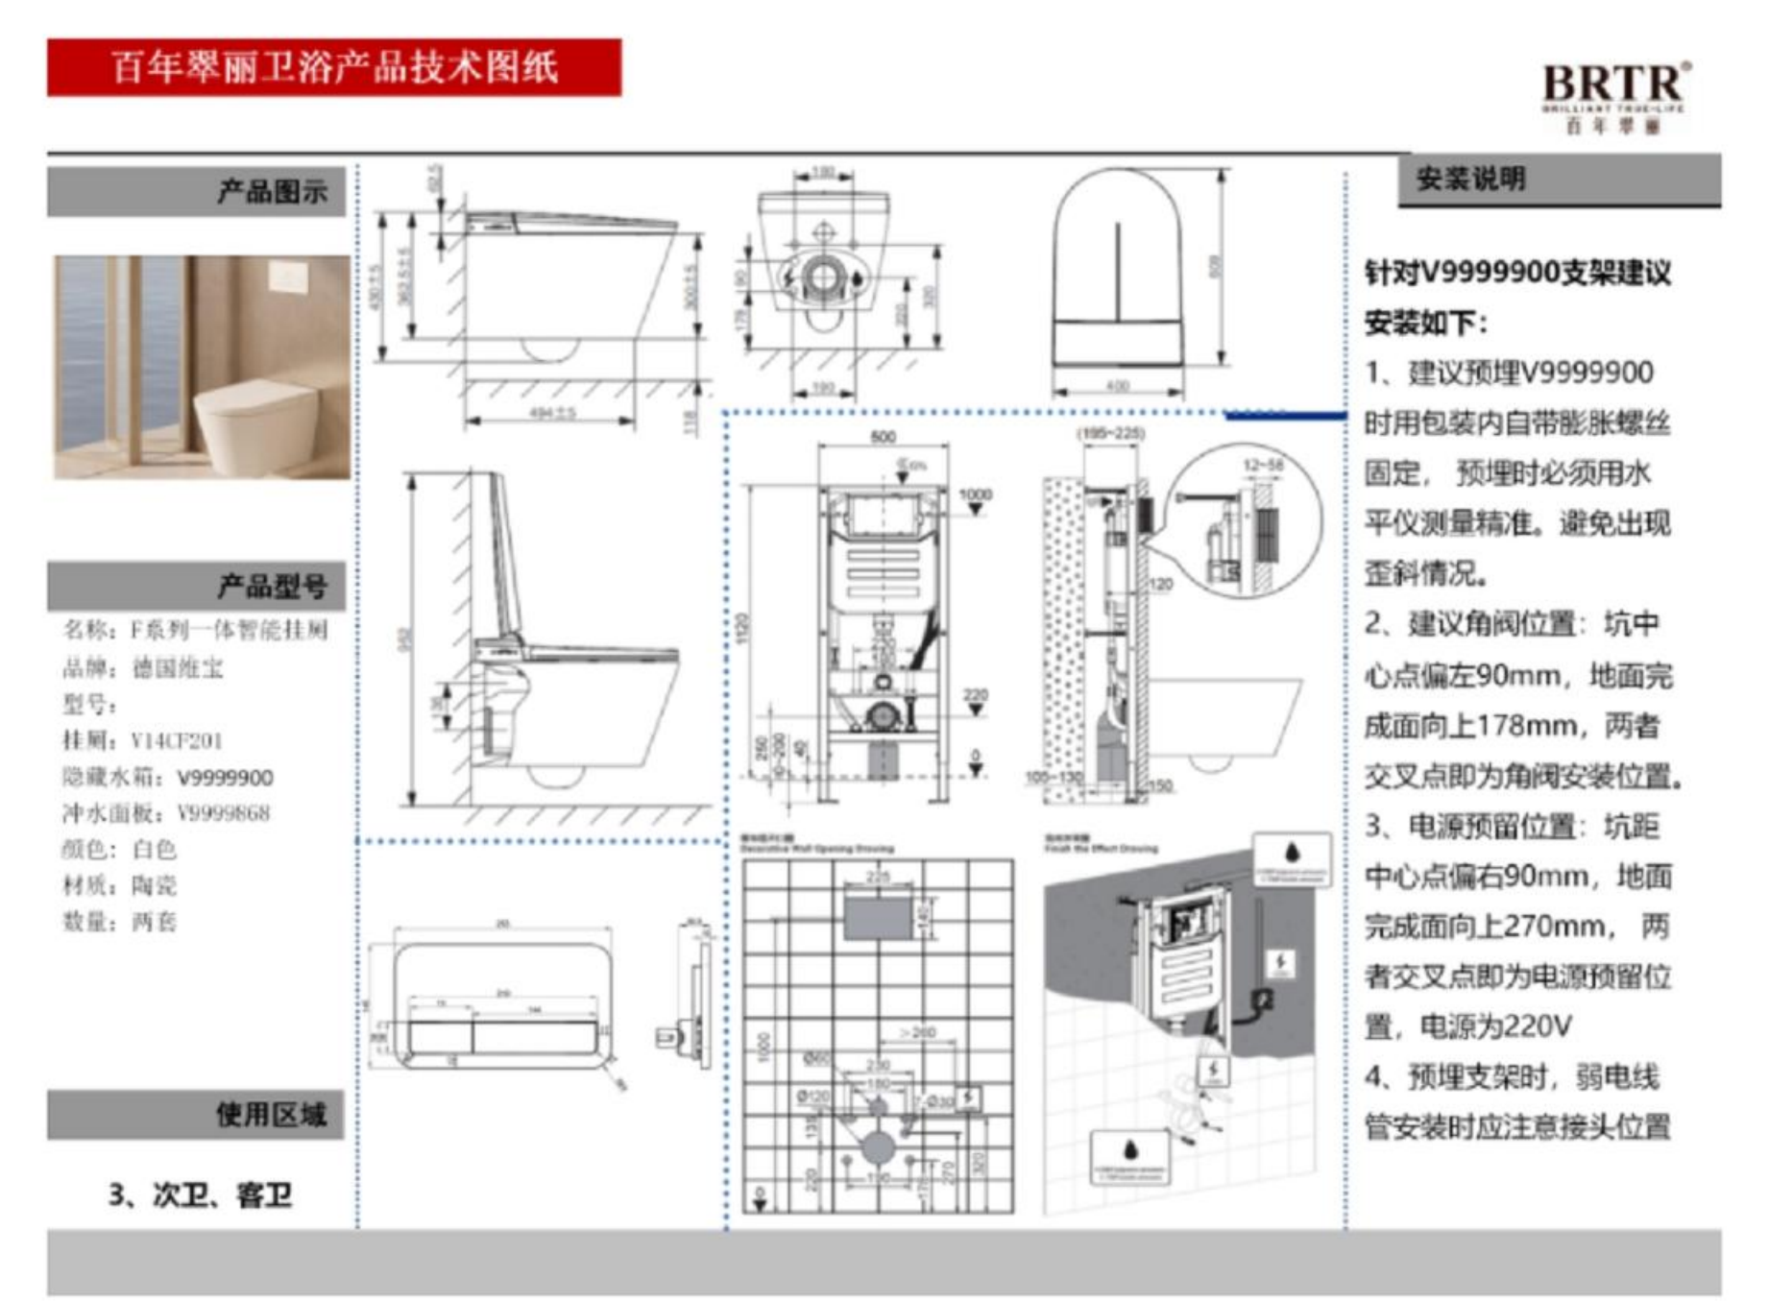

百年翠丽卫浴产品技术图纸

BRTR

产品图示

产品型号

名称：F系列一体智能挂厕
品牌：德国维宝
型号：
挂厕：V14CF201
隐藏水箱：V9999900
冲水面板：V9999868
颜色：白色
材质：陶瓷
数量：两套

使用区域

3、次卫、客卫

安装说明

针对V9999900支架建议安装如下：

1、建议预埋V9999900时用包装内自带膨胀螺丝固定，预埋时必须用水平仪测量精准。避免出现歪斜情况。
2、建议角阀位置：坑中心点偏左90mm，地面完成面向上178mm，两者交叉点即为角阀安装位置。
3、电源预留位置：坑距中心点偏右90mm，地面完成面向上270mm，两者交叉点即为电源预留位置，电源为220V
4、预埋支架时，弱电线管安装时应注意接头位置

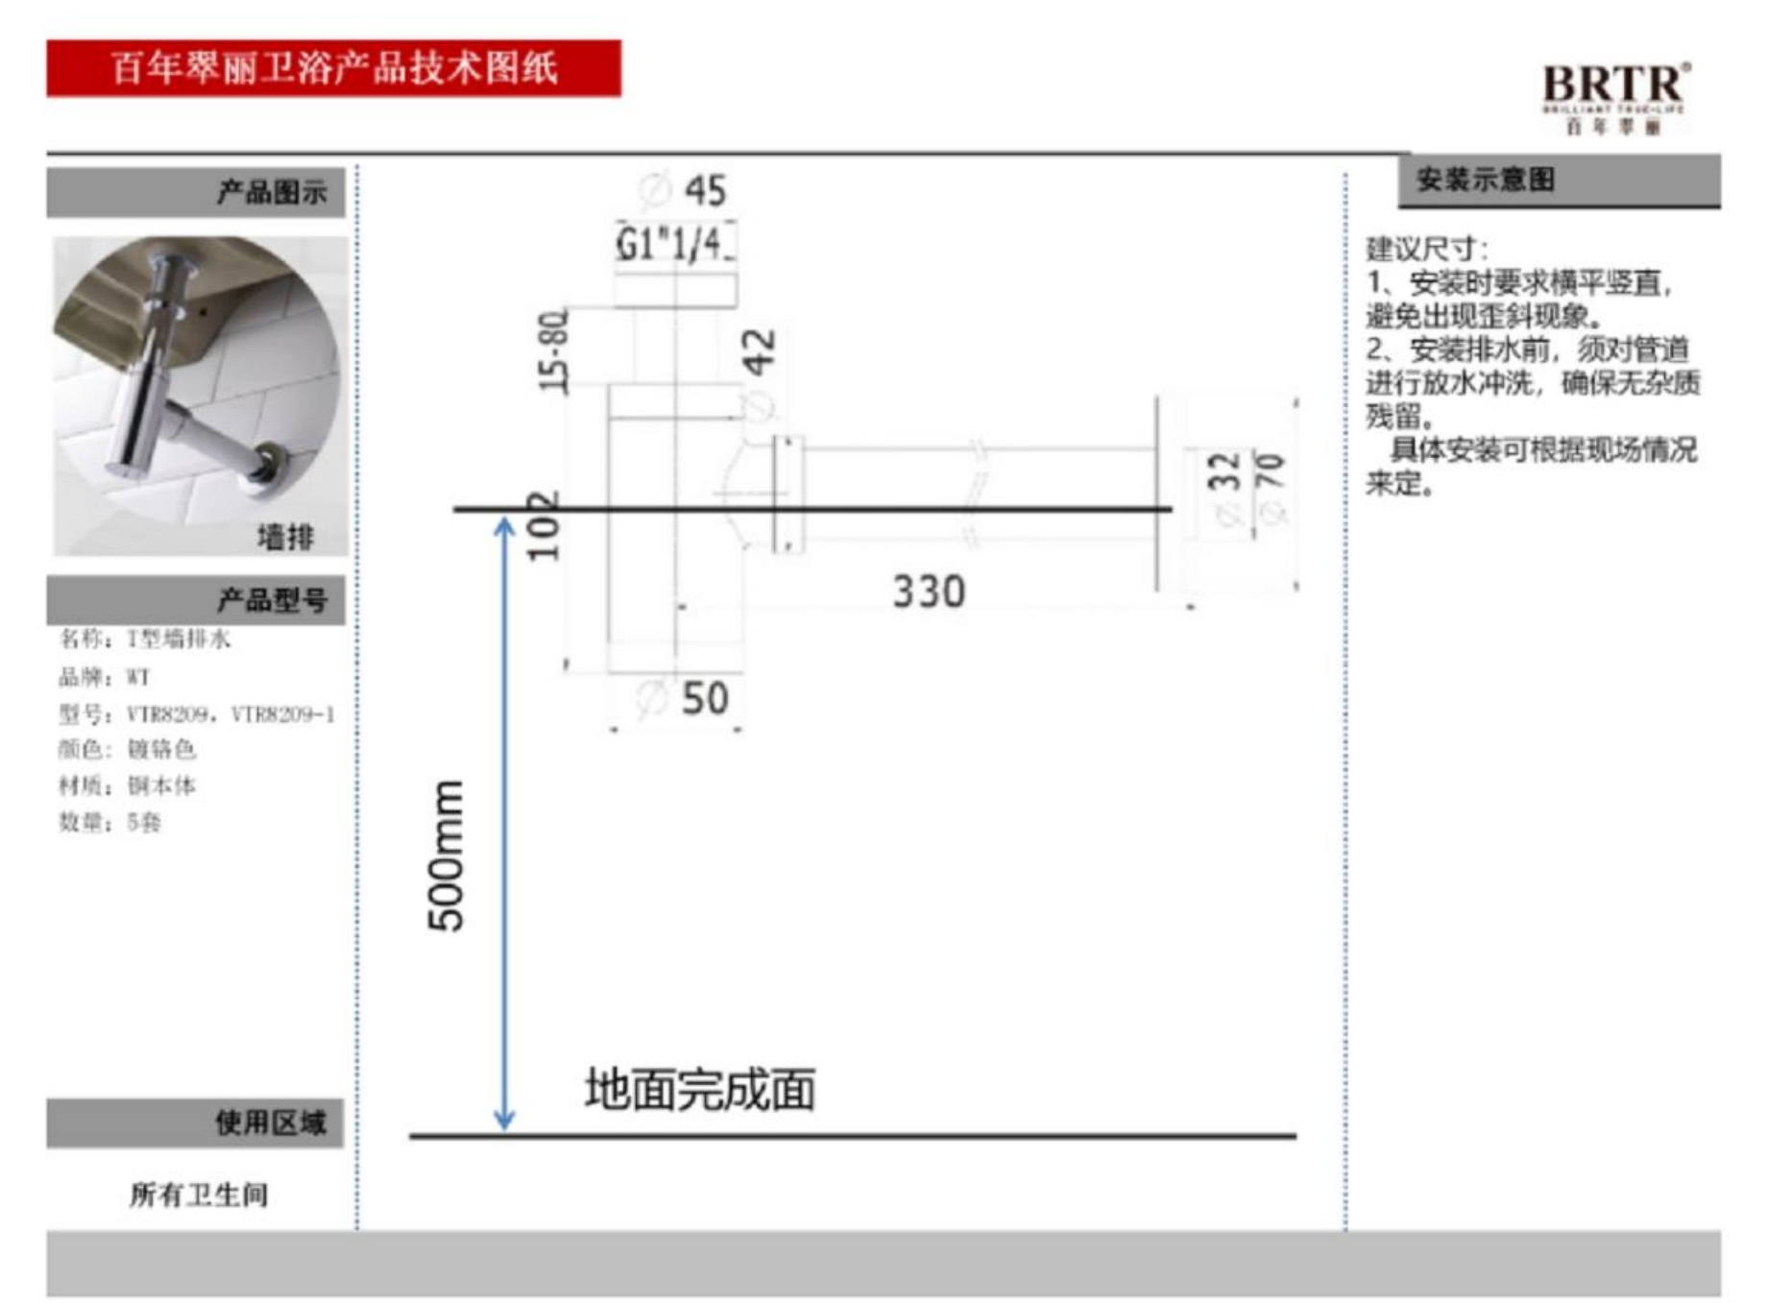

百年翠丽卫浴产品技术图纸

BRTR

产品图示

墙排

产品型号

名称：T型墙排水
品牌：WT
型号：VTR8209，VTR8209-1
颜色：镀铬色
材质：铜本体
数量：5套

使用区域

所有卫生间

安装示意图

建议尺寸：
1、安装时要求横平竖直，避免出现歪斜现象。
2、安装排水前，须对管道进行放水冲洗，确保无杂质残留。
具体安装可根据现场情况来定。

Ø 45
G1"1/4
15-80
42
102
330
Ø 32
Ø 70
Ø 50
500mm
地面完成面

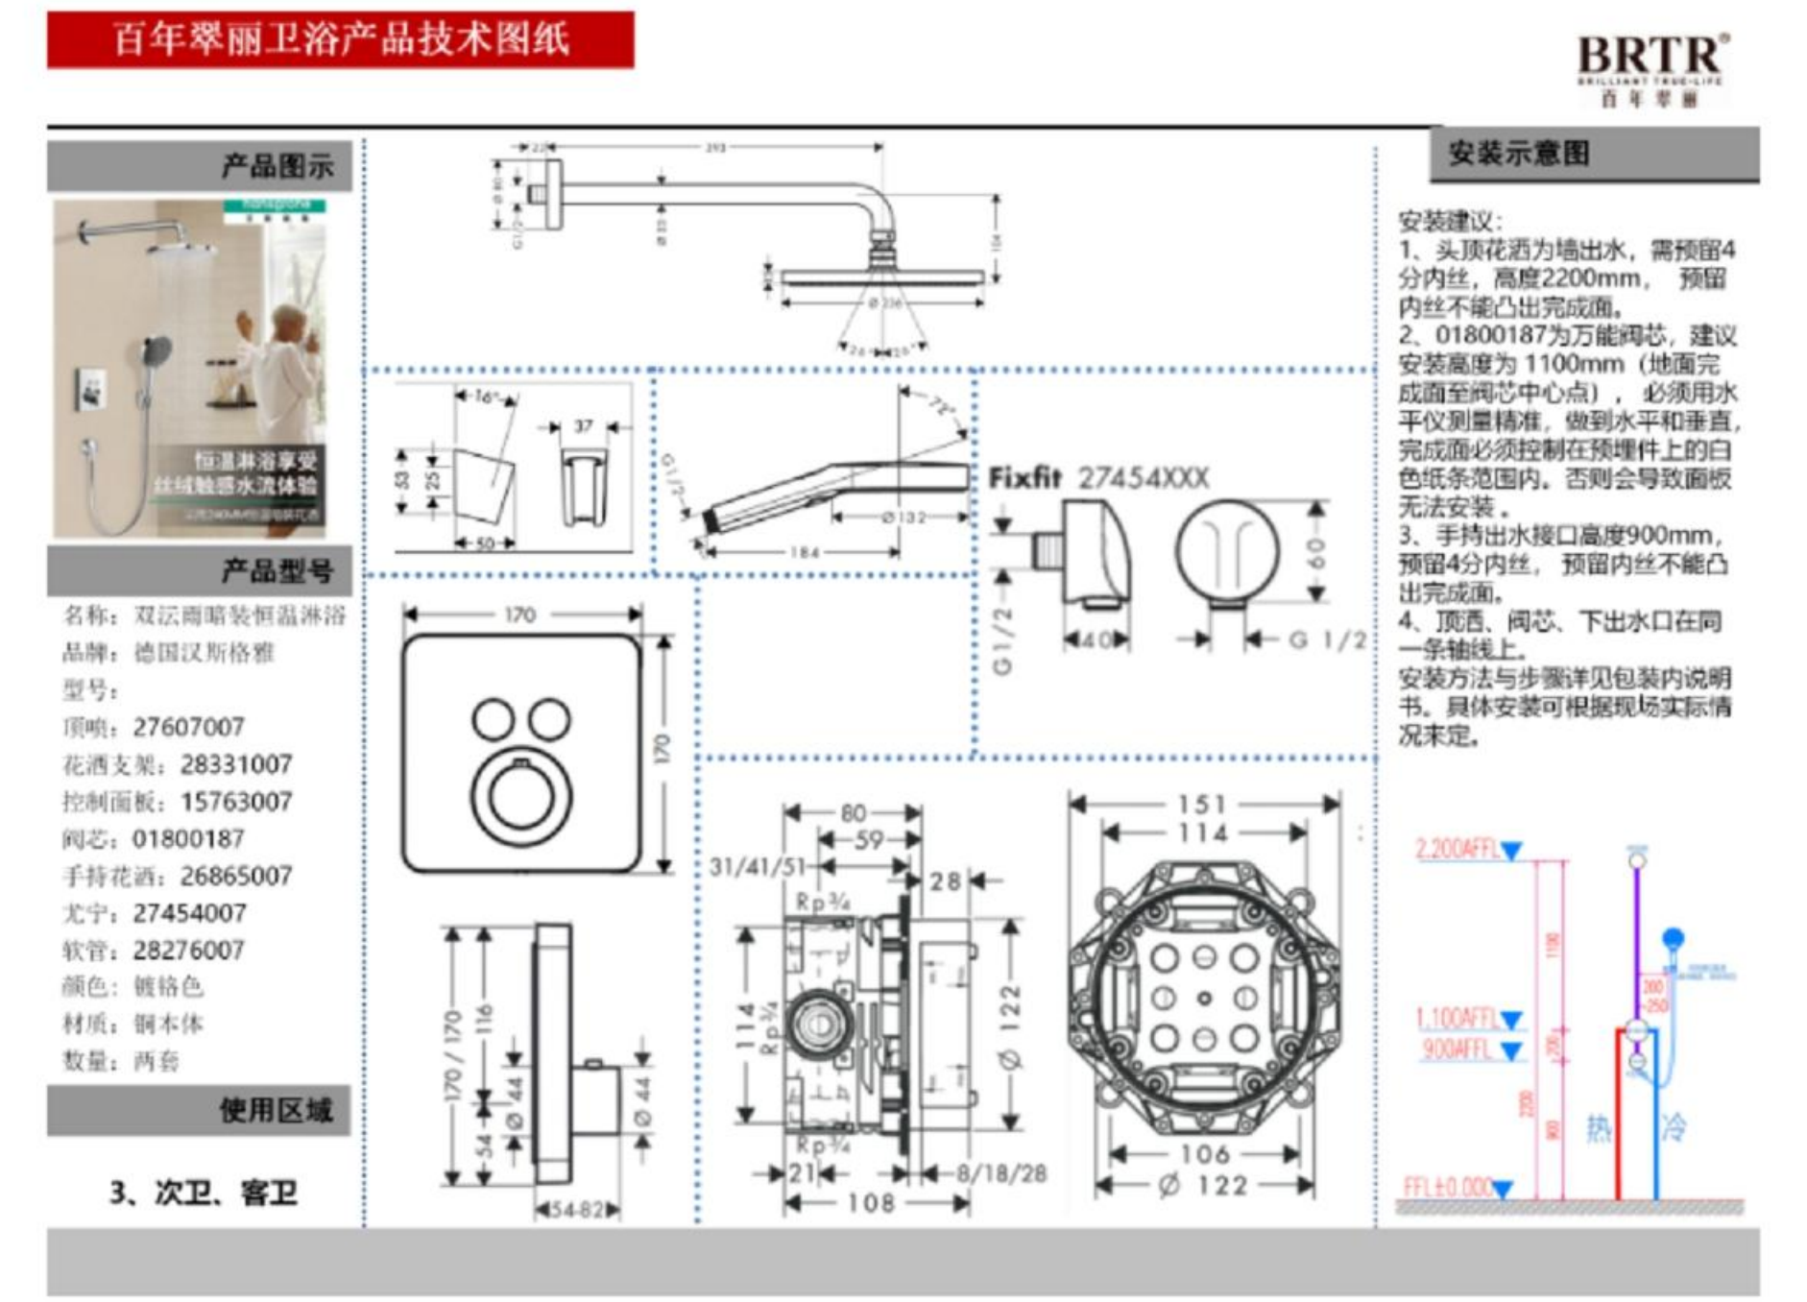

百年翠丽卫浴产品技术图纸

BRTR

产品图示

产品型号

名称：双江雨暗装恒温淋浴
品牌：德国汉斯格雅
型号：
顶喷：27607007
花洒支架：28331007
控制面板：15763007
阀芯：01800187
手持花洒：26865007
尤宁：27454007
软管：28276007
颜色：镀铬色
材质：铜本体
数量：两套

使用区域

3、次卫、客卫

安装示意图

安装建议：
1、头顶花洒为墙出水，需预留4分内丝，高度2200mm，预留内丝不能凸出完成面。
2、01800187为万能阀芯，建议安装高度为 1100mm（地面完成面至阀芯中心点），必须用水平仪测量精准，做到水平和垂直，完成面必须控制在预埋件上的白色纸条范围内。否则会导致面板无法安装。
3、手持出水接口高度900mm，预留4分内丝，预留内丝不能凸出完成面。
4、顶洒、阀芯、下出水口在同一条轴线上。
安装方法与步骤详见包装内说明书。具体安装可根据现场实际情况来定。

恒温淋浴享受
丝绒触感水流体验
Fixfit 27454XXX
170
170
80
59
31/41/51
28
151
114
106
Ø 122
108
21
8/18/28
54-82
G 1/2
40
60
2,200AFFL
1,100AFFL
900AFFL
FFL±0.000
热
冷

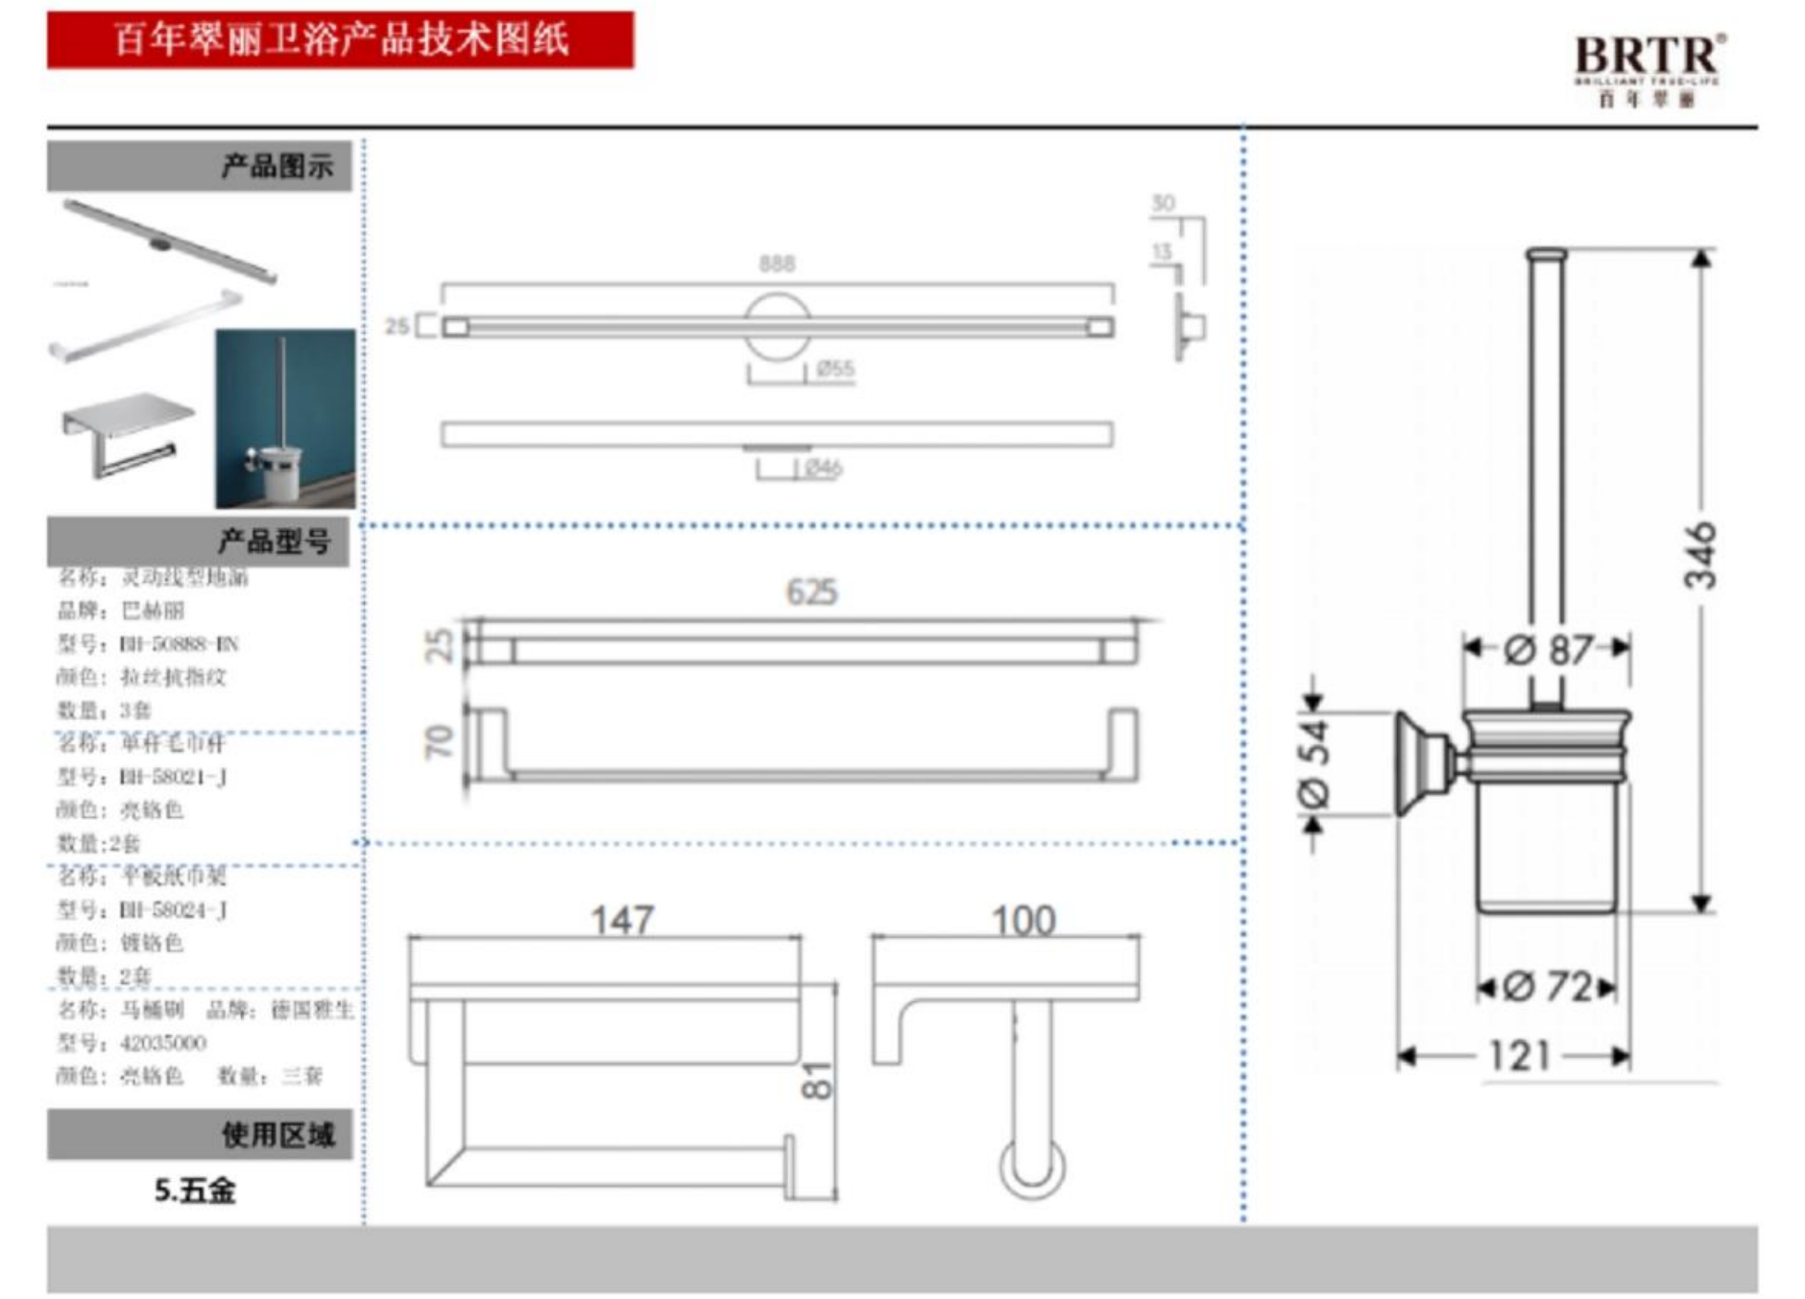

百年翠丽卫浴产品技术图纸

BRTR

产品图示

产品型号

名称：灵动线型地漏
品牌：巴赫丽
型号：BH-50888-BN
颜色：拉丝抗指纹
数量：3套
名称：单杆毛巾杆
型号：BH-58021-J
颜色：亮铬色
数量：2套
名称：平板纸巾架
型号：BH-58024-J
颜色：镀铬色
数量：2套
名称：马桶刷 品牌：德国雅生
型号：42035000
颜色：亮铬色 数量：三套

使用区域

5.五金

888
25
30
13
Ø55
Ø46
625
25
70
147
100
81
346
Ø 87
Ø 54
Ø 72
121

LEGEND图例

编号	图例	说明
1	🟥	强电
2	🟪	弱电
3	🟩	给水
4	🟦	排水
5	▭	排水(原有)
6	🟥	冷媒进管
7	🟦	冷媒出管
8	🟦	冷凝水管
9	▬	等电位接地线
10	▬	原始墙
11	▬	墙面抹灰≈15mm
12	▭	灰缝≈15mm
13	▭	归方找平层≈15mm
14	▬	墙面粘接剂≈7mm
15	▬	防水背衬板≈12mm
16	▭	直纹白玉石材≈18mm
17	▭	枫丹白露石材≈18mm
18	▭	黑白根大理石≈18mm
19	▭	伊朗绿大理石≈18mm

盖章

注释
Notes
1.本图纸如与现场尺寸有误，请施工人员与项目负责人联系。
2.施工前施工人员应认真查阅此图，如有不明确尺寸，按现场测量为准。
3.本图纸必须经甲乙双方认可并签字方可作为施工依据。

日期
Date 06/06/26

修订
Revision

△1

项目
Project
潮映华岸府3-801

比例
Scale

次卫洁具分析图

图纸编号
Drawing No.
ST-18

项目编号
Project No.

©2025

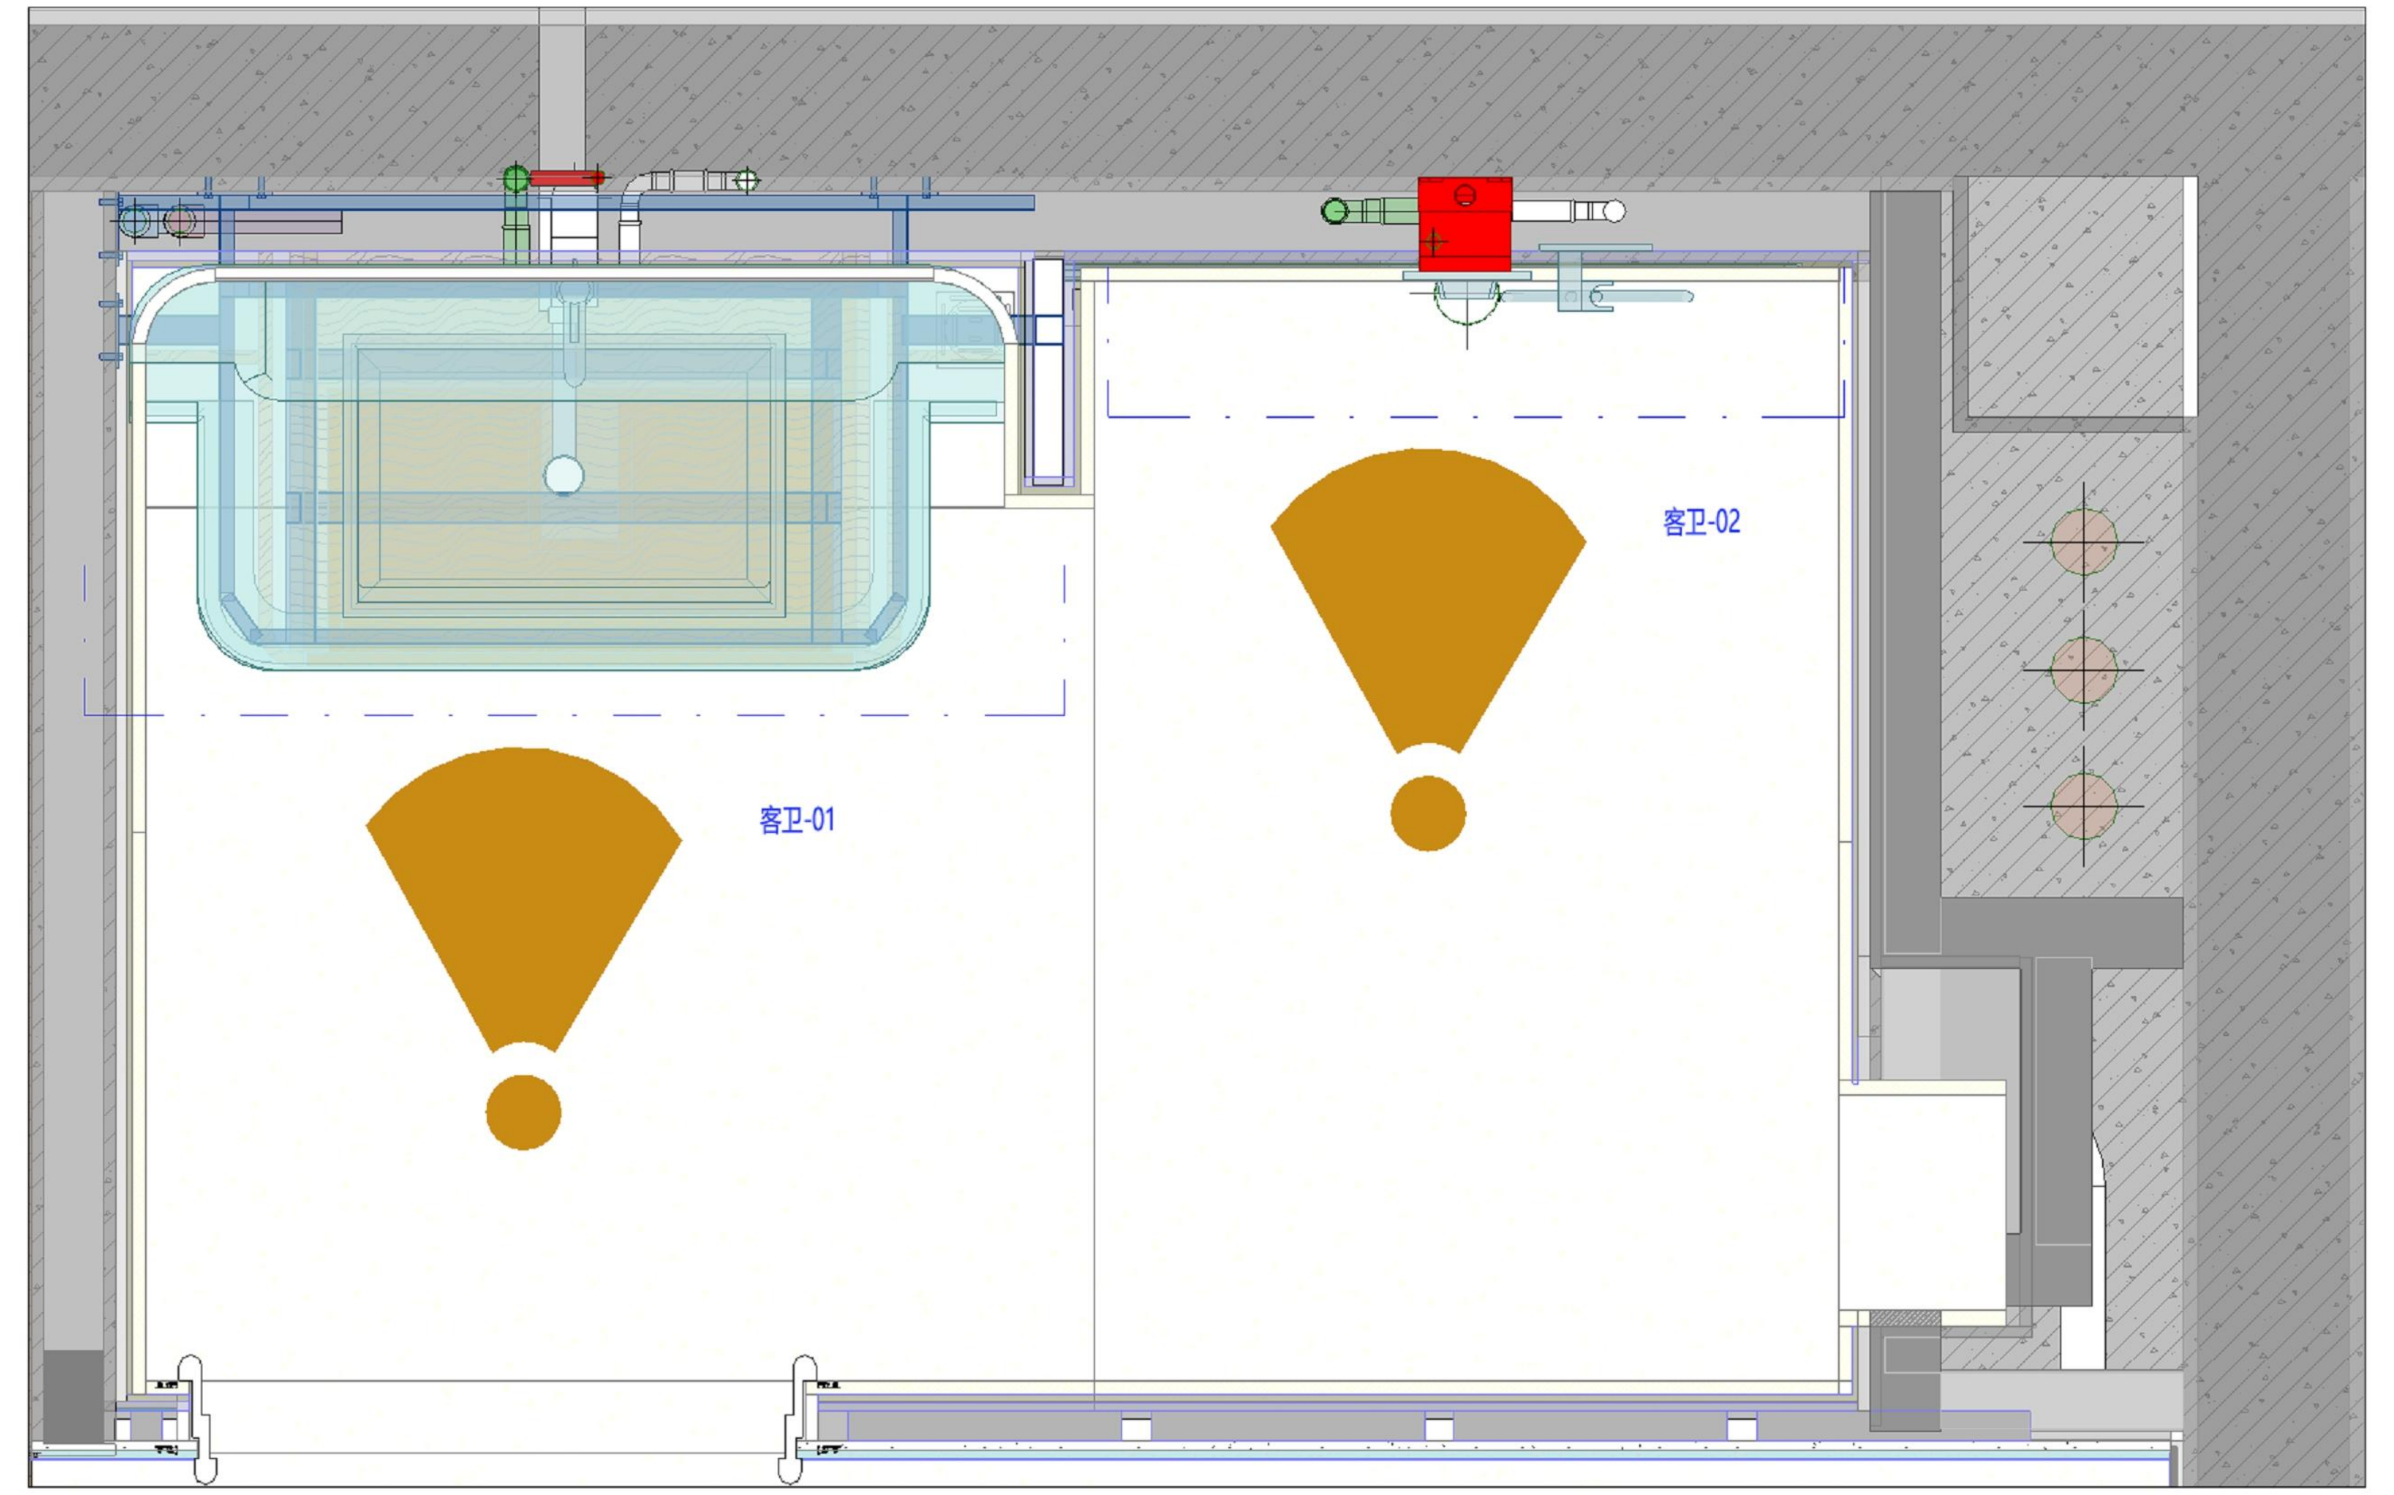

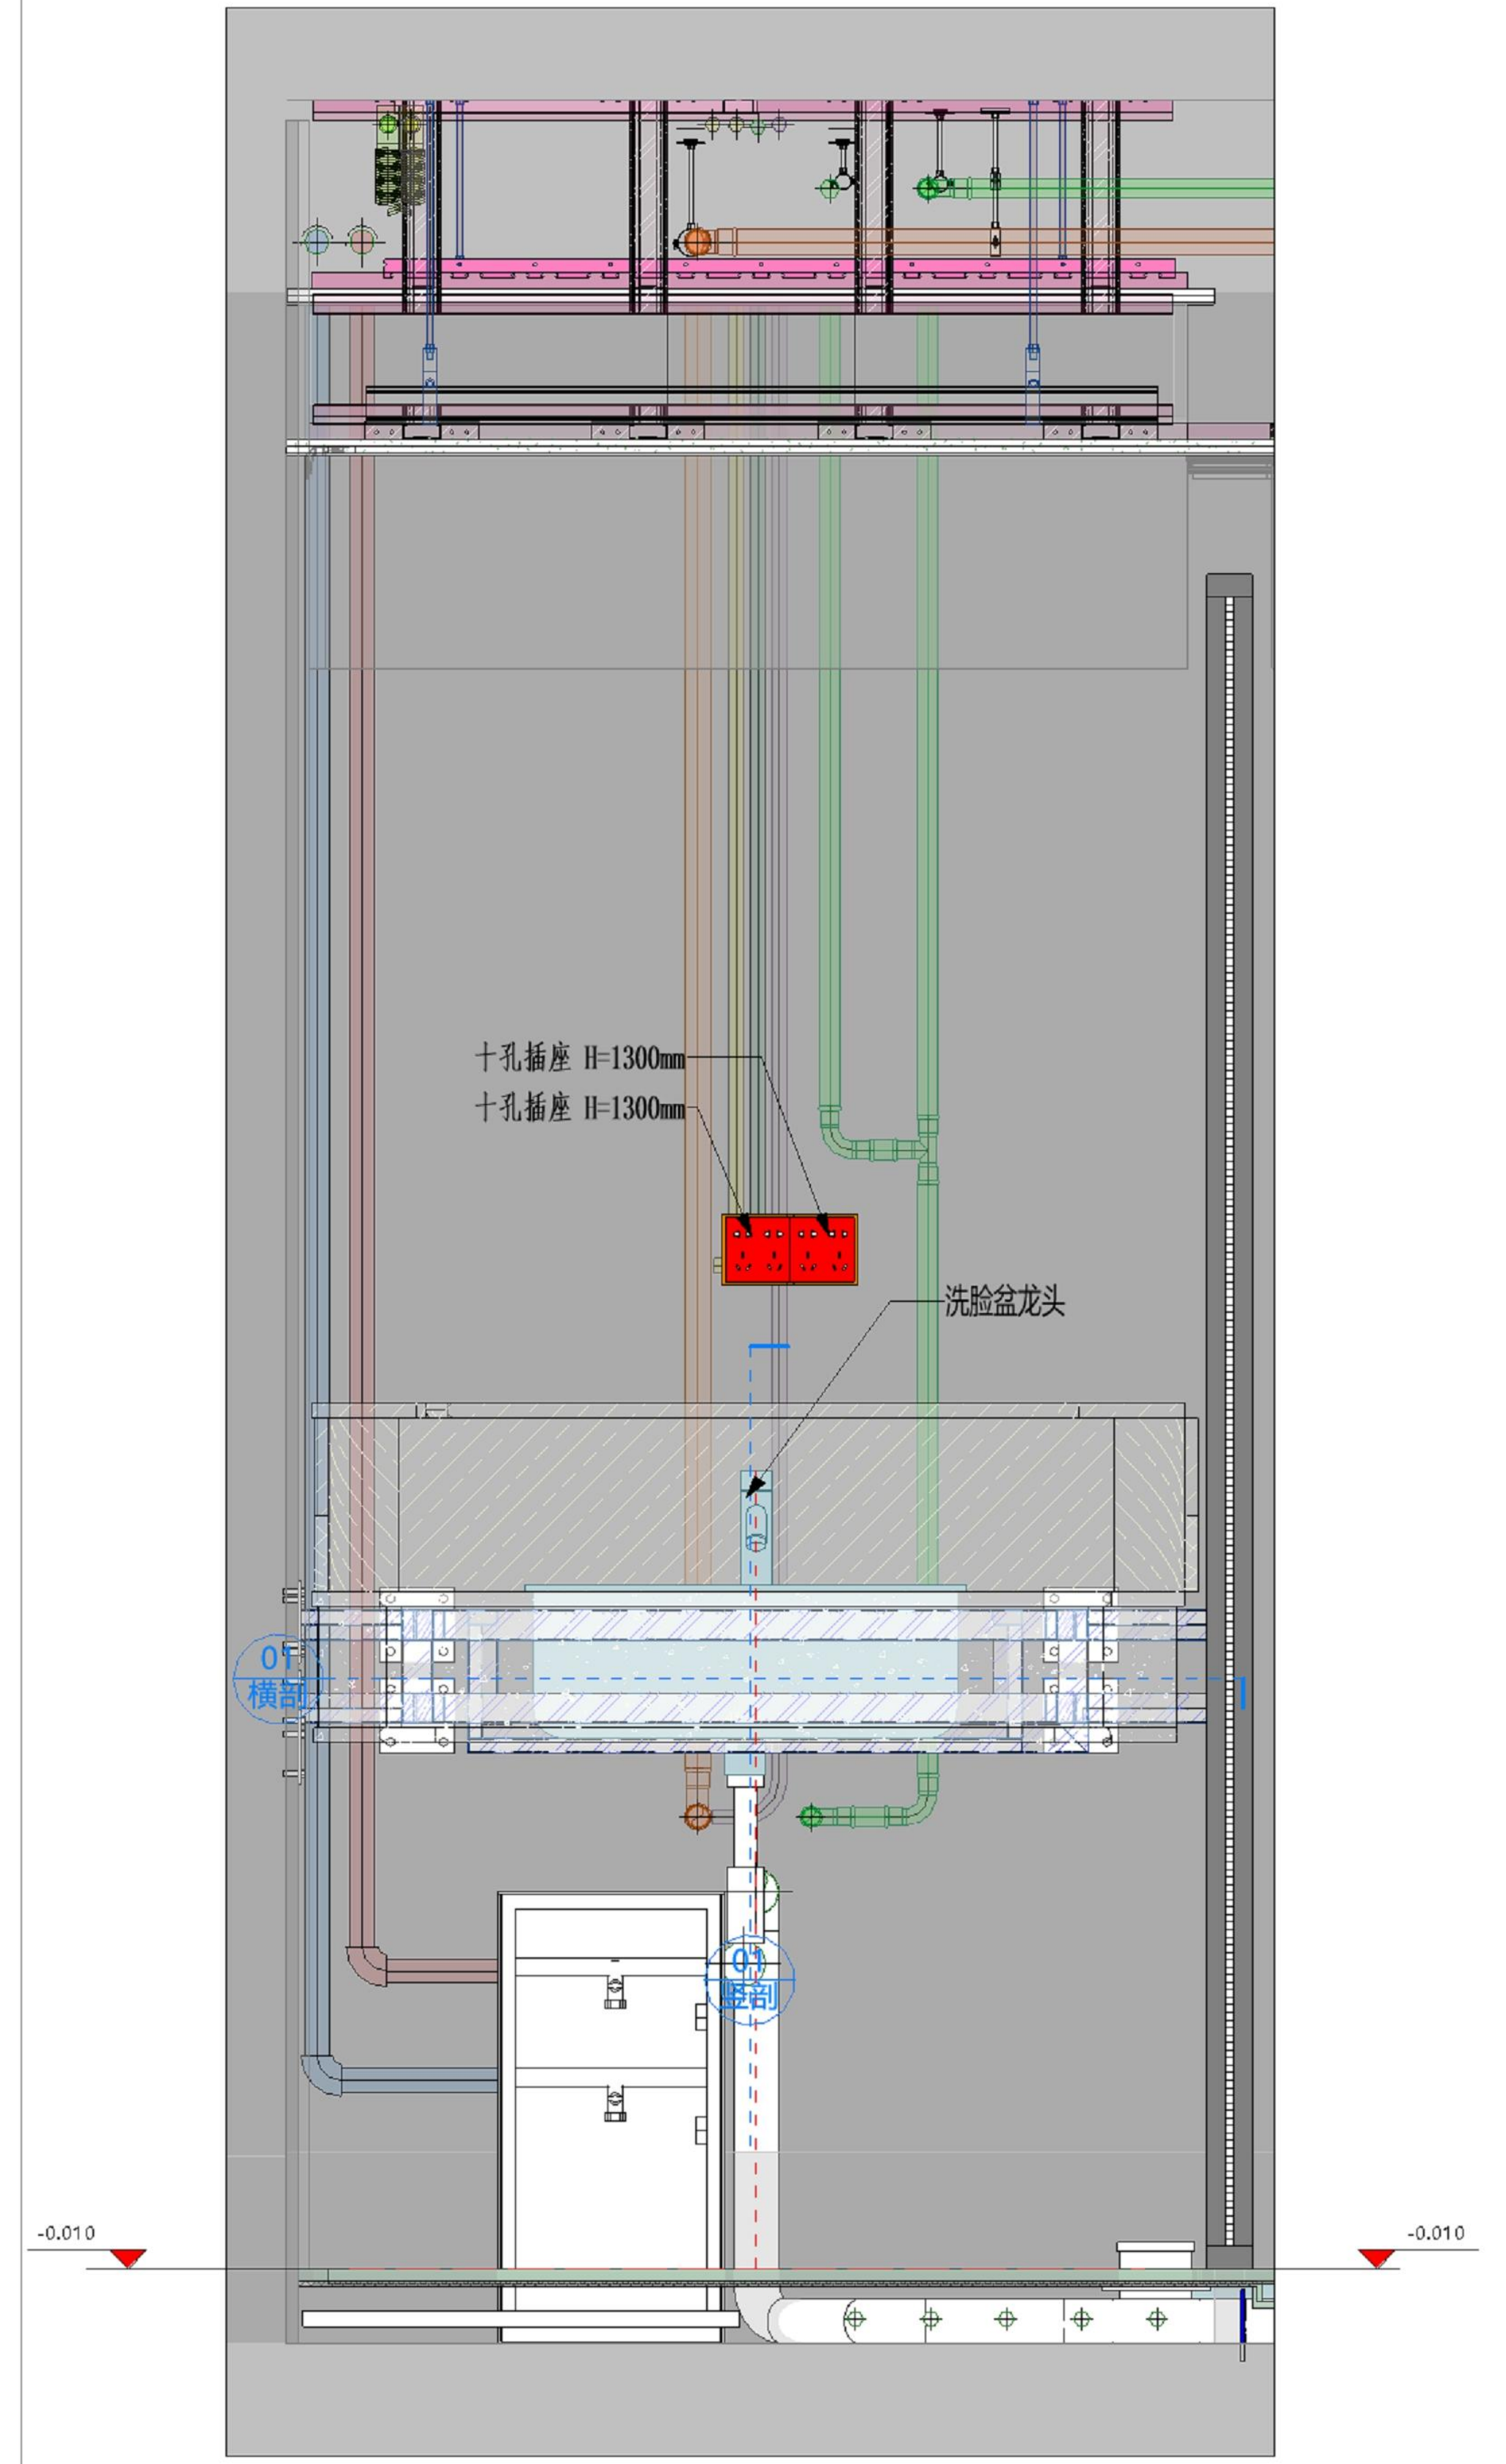
十孔插座 H=1300mm
十孔插座 H=1300mm
洗脸盆龙头
01 横剖
01 竖剖
-0.010
-0.010

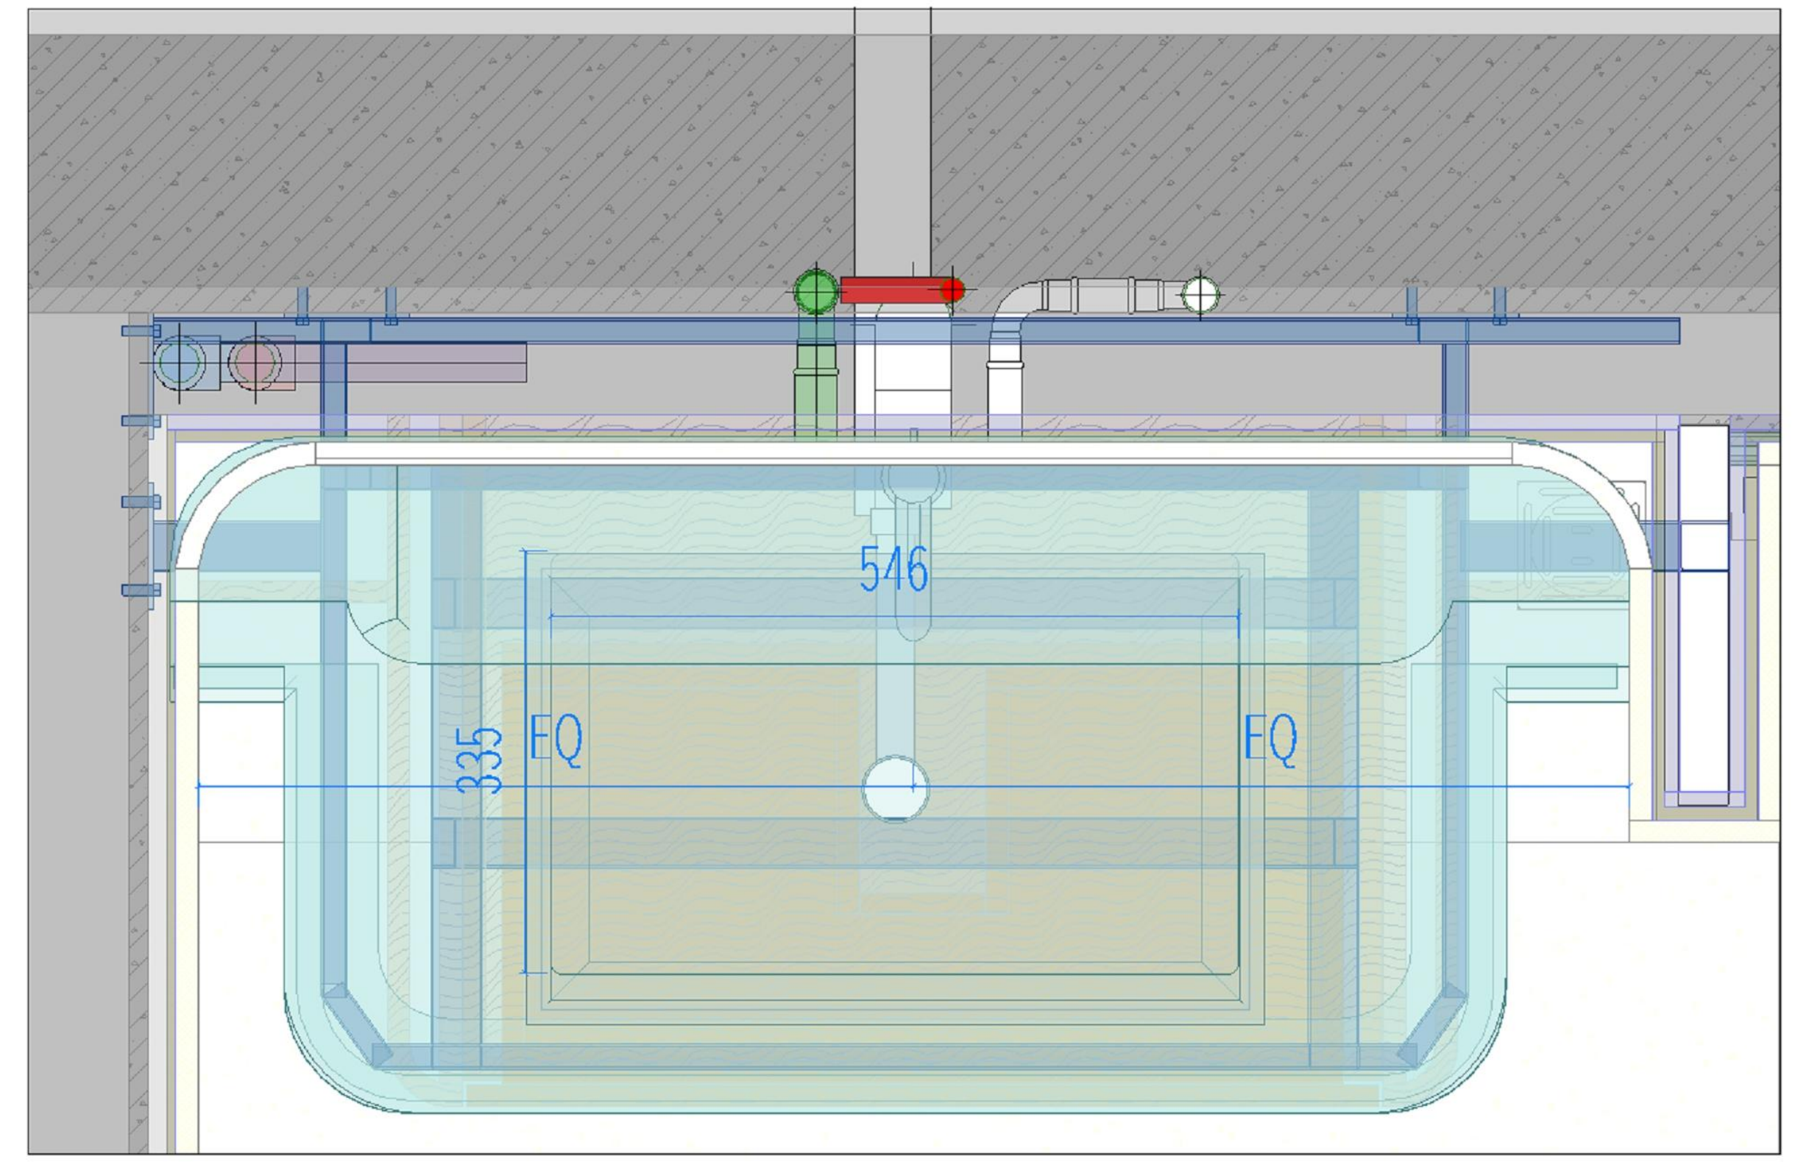
546
335
FQ
FQ

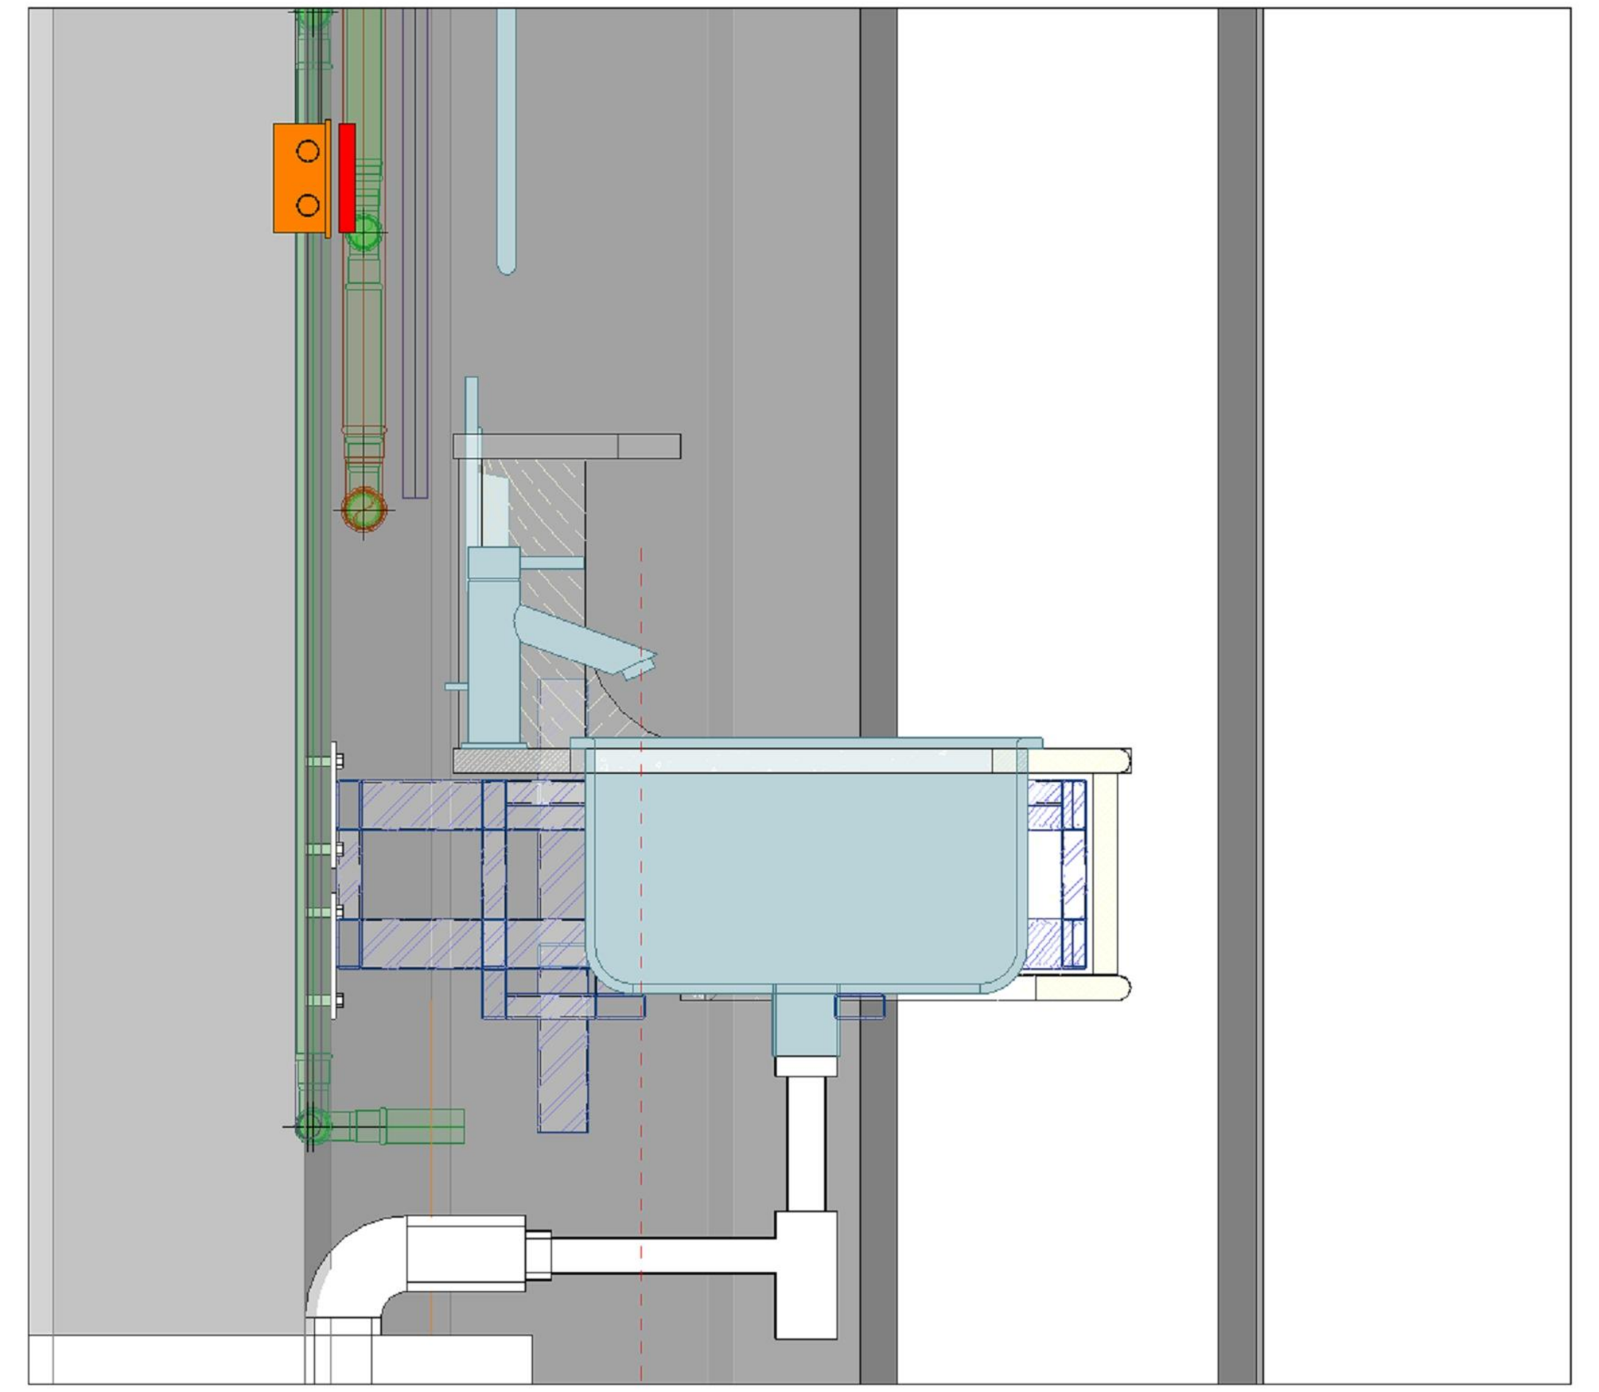

客卫-01

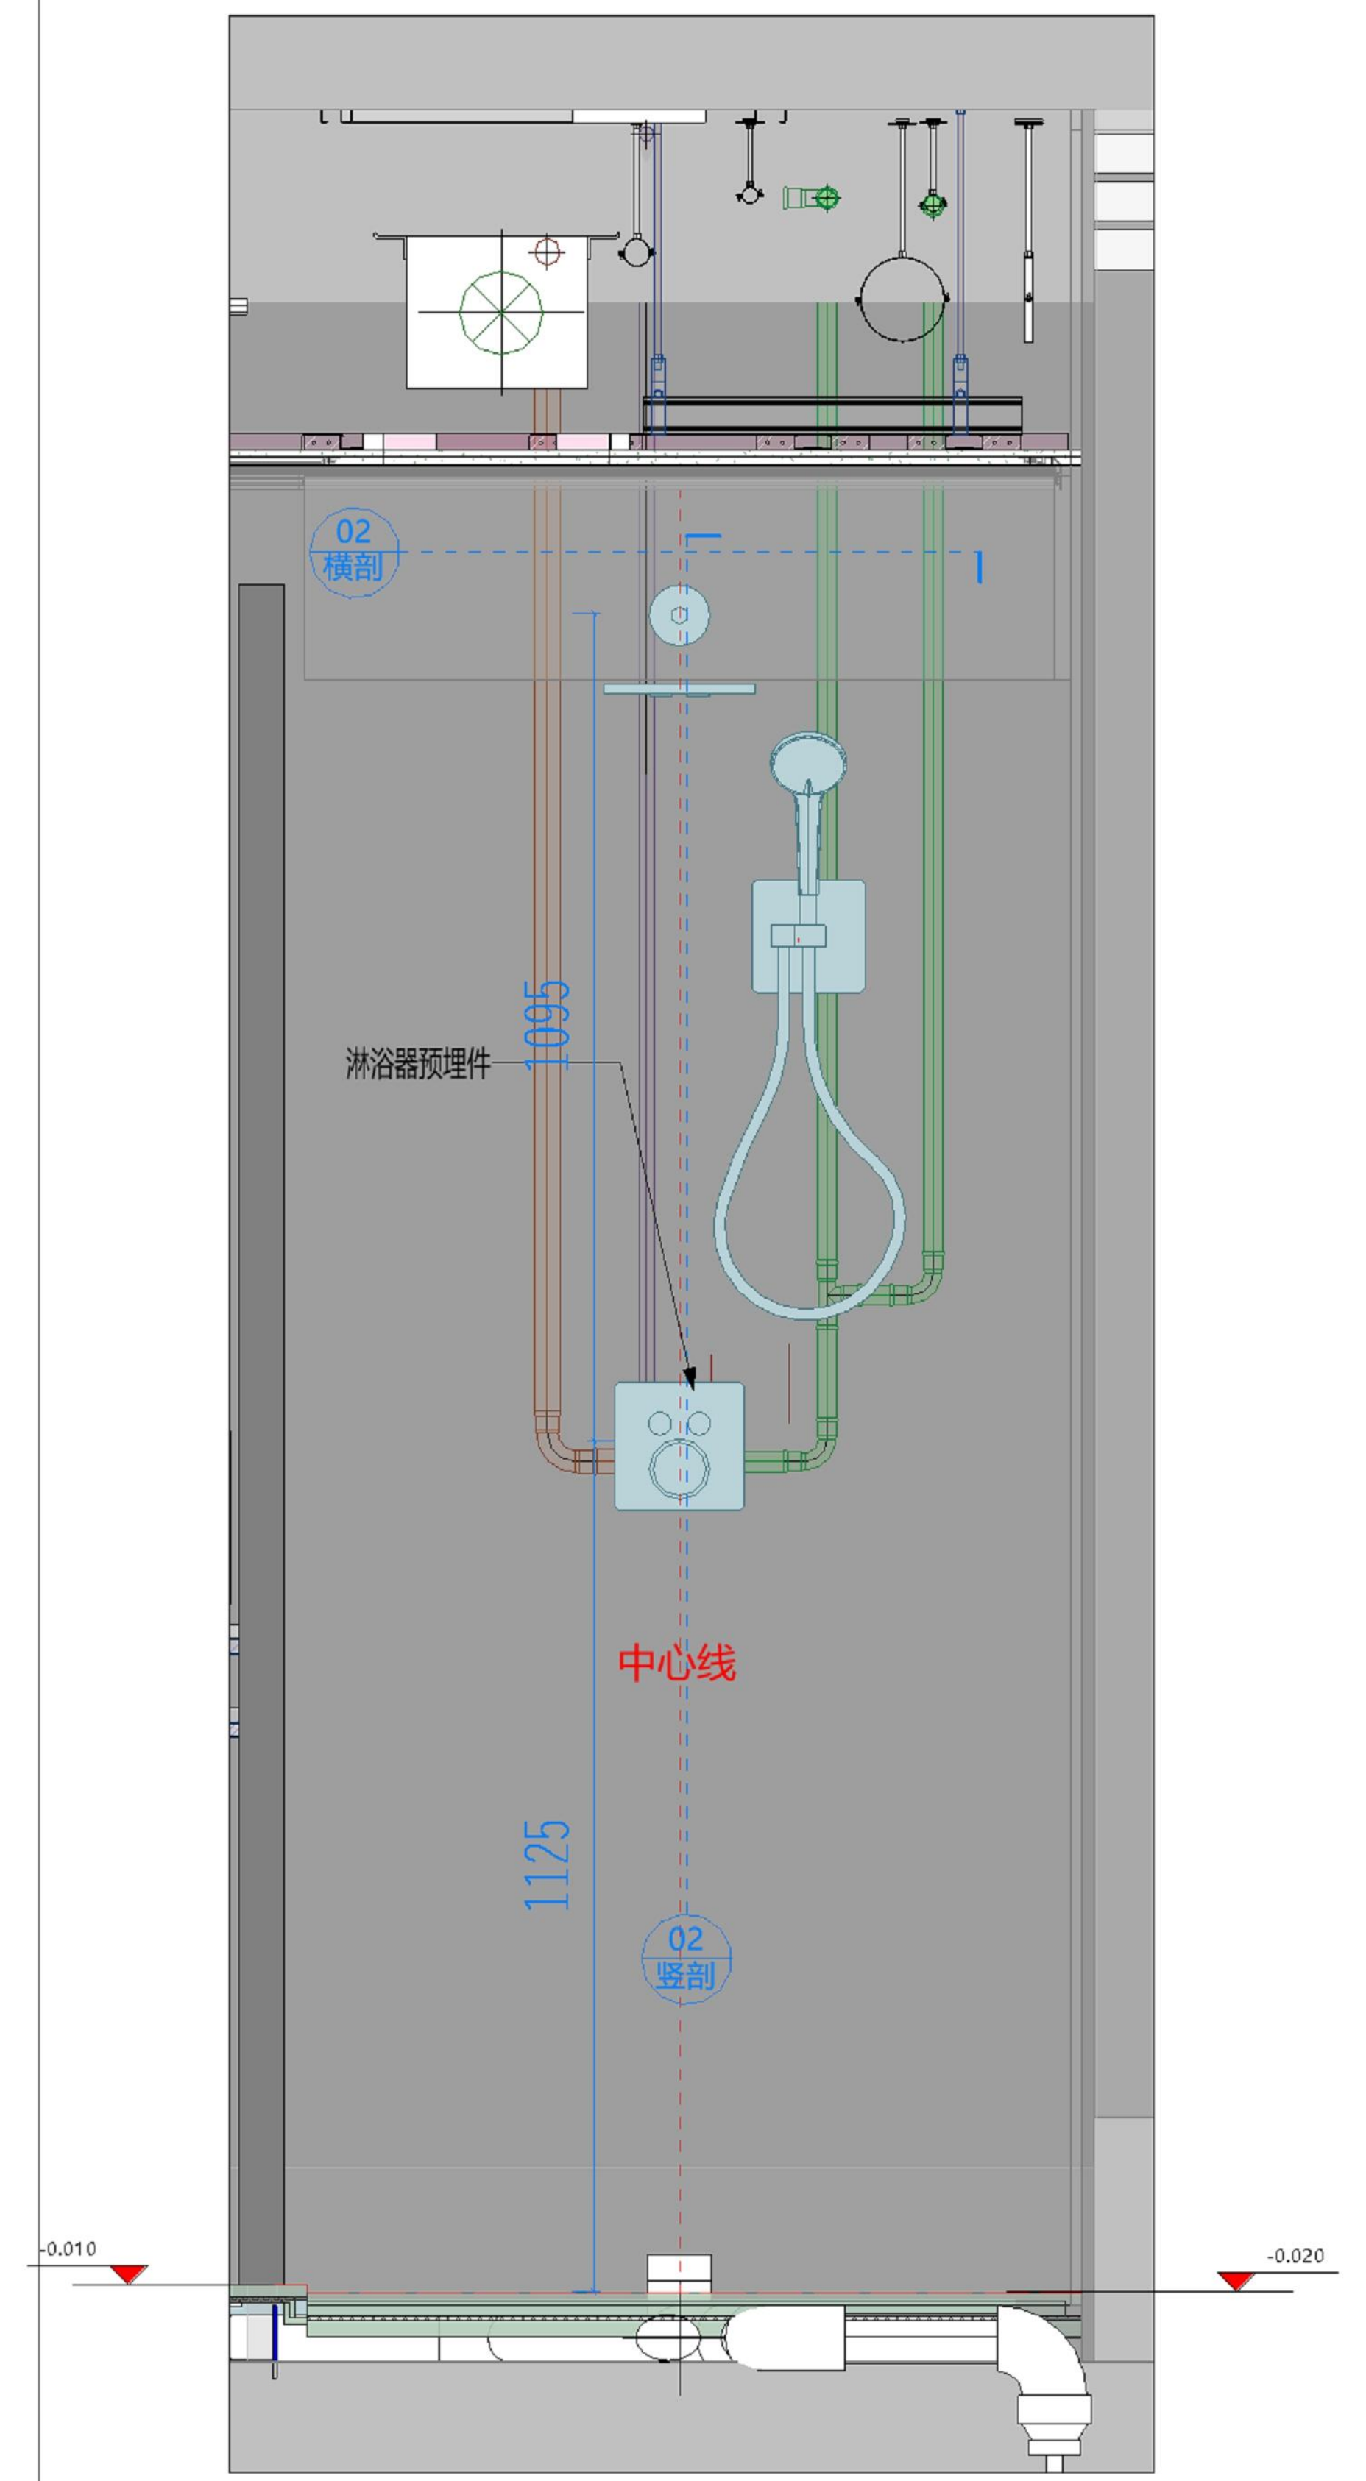
02 横剖
1095
淋浴器预埋件
中心线
1125
02 竖剖
-0.010
-0.020

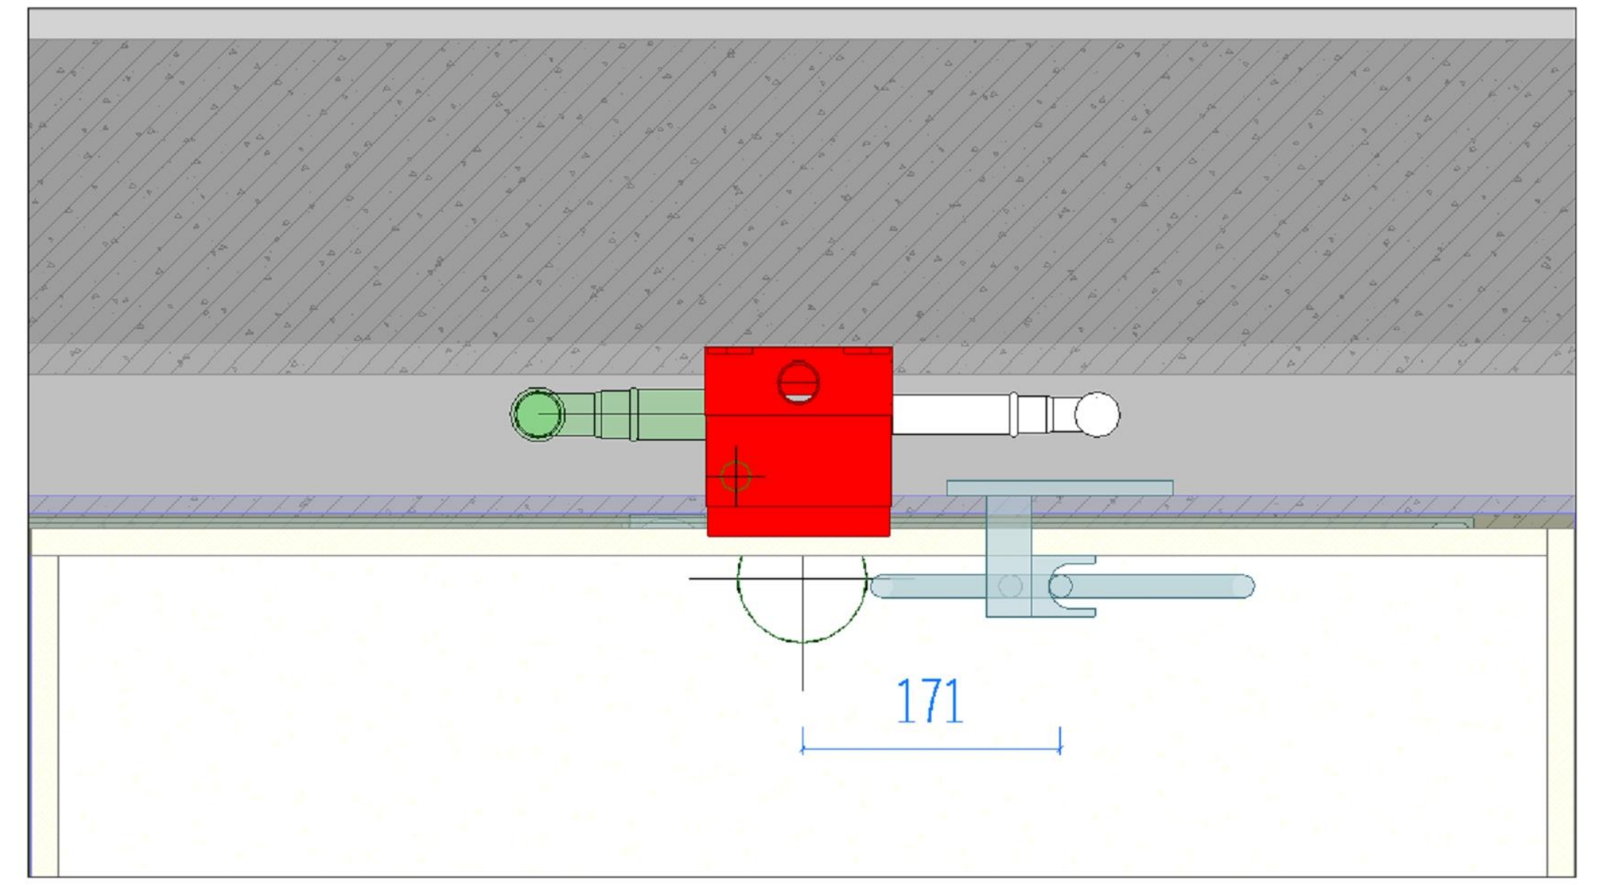

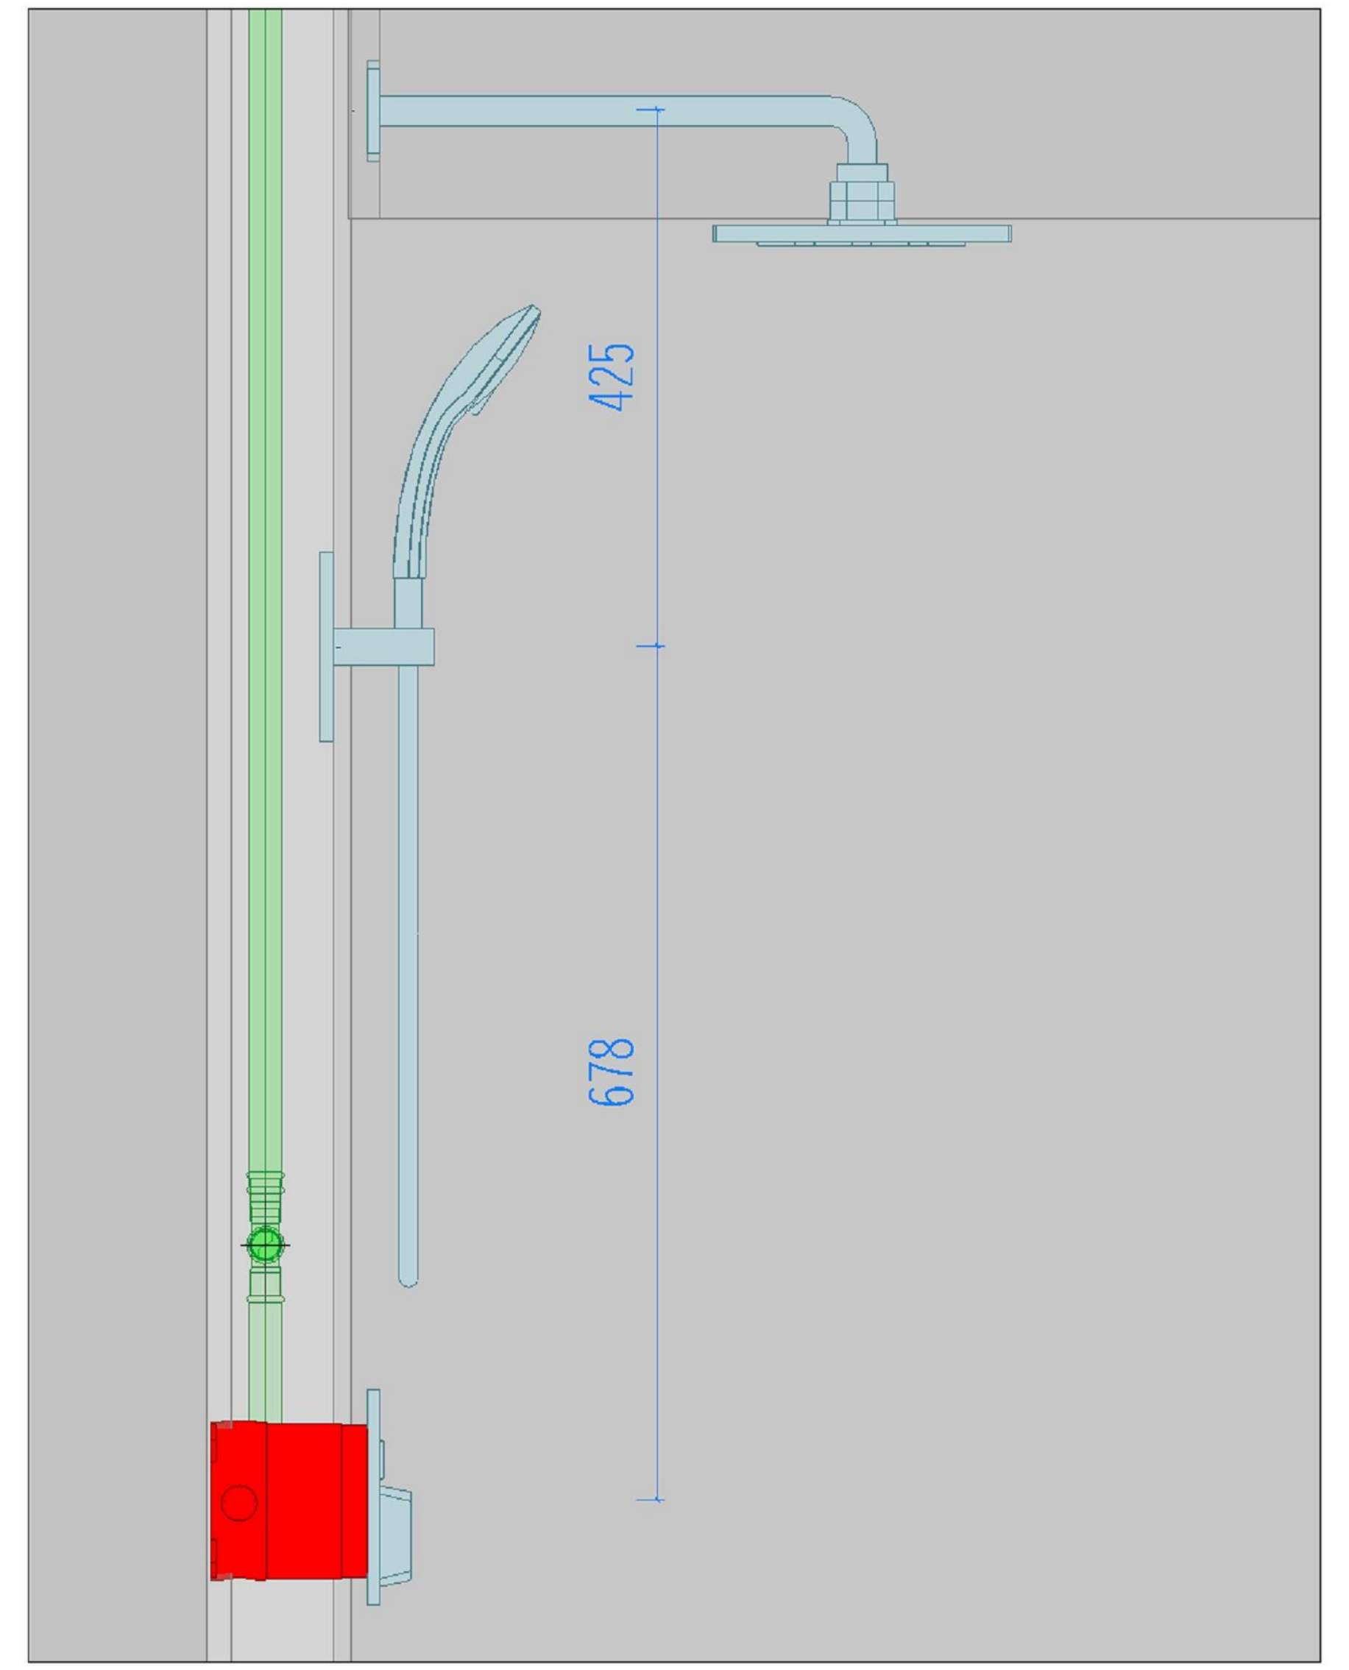

客卫-02

百年翠丽卫浴产品技术图纸

BRTR® BRILLIANT TRUE-LIFE 百年翠丽

产品图示

产品型号

名称：面盆龙头
品牌：德国维宝
型号：TVW10300400061
颜色：镀铬色
材质：铜本体
数量：两套
名称：台下盆
品牌：德国 唯宝
型号：51225301
颜色：白色
材质：陶瓷
数量：两套

使用区域

3、次卫、客卫

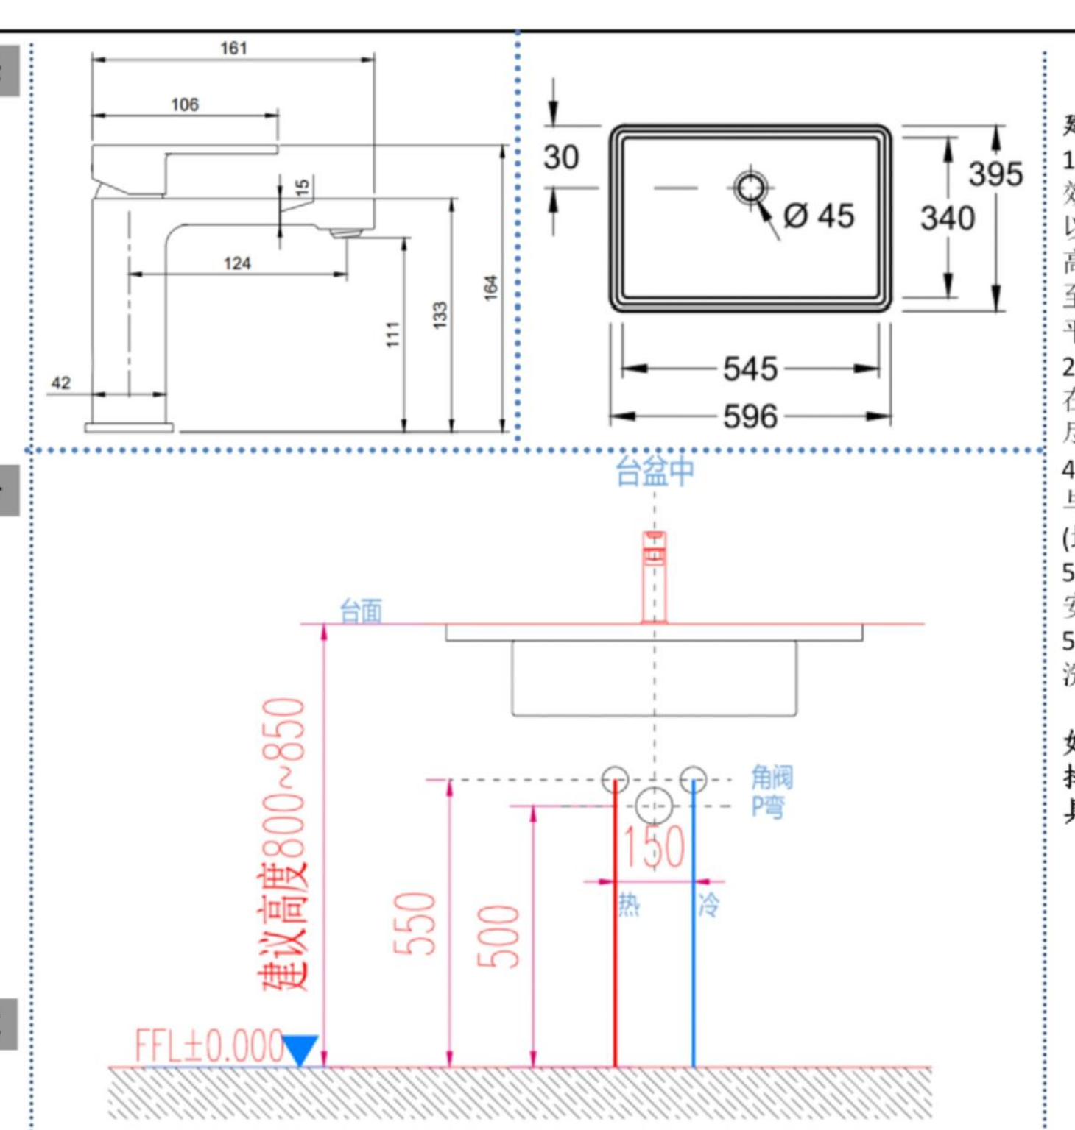
161
106
15
124
42
111
133
164
30
Ø 45
395
340
545
596
台盆中
台面
建议高度800~850
550
500
150
角阀
P弯
热
冷
FFL±0.000

安装示意图

建议尺寸：
1、面盆龙头的进水软管有效长度一般为350mm，角阀以实物为准。建议角阀安装高度550mm，（地面完成面至角阀距离）间距150mm，平均分布于排水口两侧。
2、台面开孔直径为32mm，在不影响安装空间的情况下尽量靠近台盆。
4、建议P弯安装高度500mm，与台盆落水口对齐。
(地面完成面至P弯距离)
5、石材面开孔以实物为准。安装时注意台盆商标的方向
5、龙头安装前，请务必冲洗管道，以免损坏龙头阀芯。

如台面距地高度有变动，进排水需对应调整。
具体以现场师傅指导为准

百年翠丽卫浴产品技术图纸

BRTR® BRILLIANT TRUE-LIFE 百年翠丽

产品图示

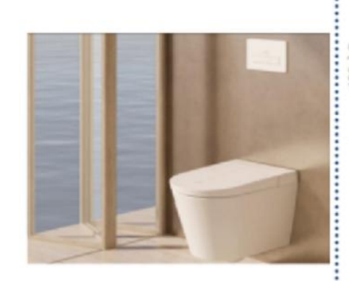

产品型号

名称：F系列一体智能挂厕
品牌：德国维宝
型号：
挂厕：V14CF201
隐藏水箱：V9999900
冲水面板：V9999868
颜色：白色
材质：陶瓷
数量：两套

使用区域

3、次卫、客卫

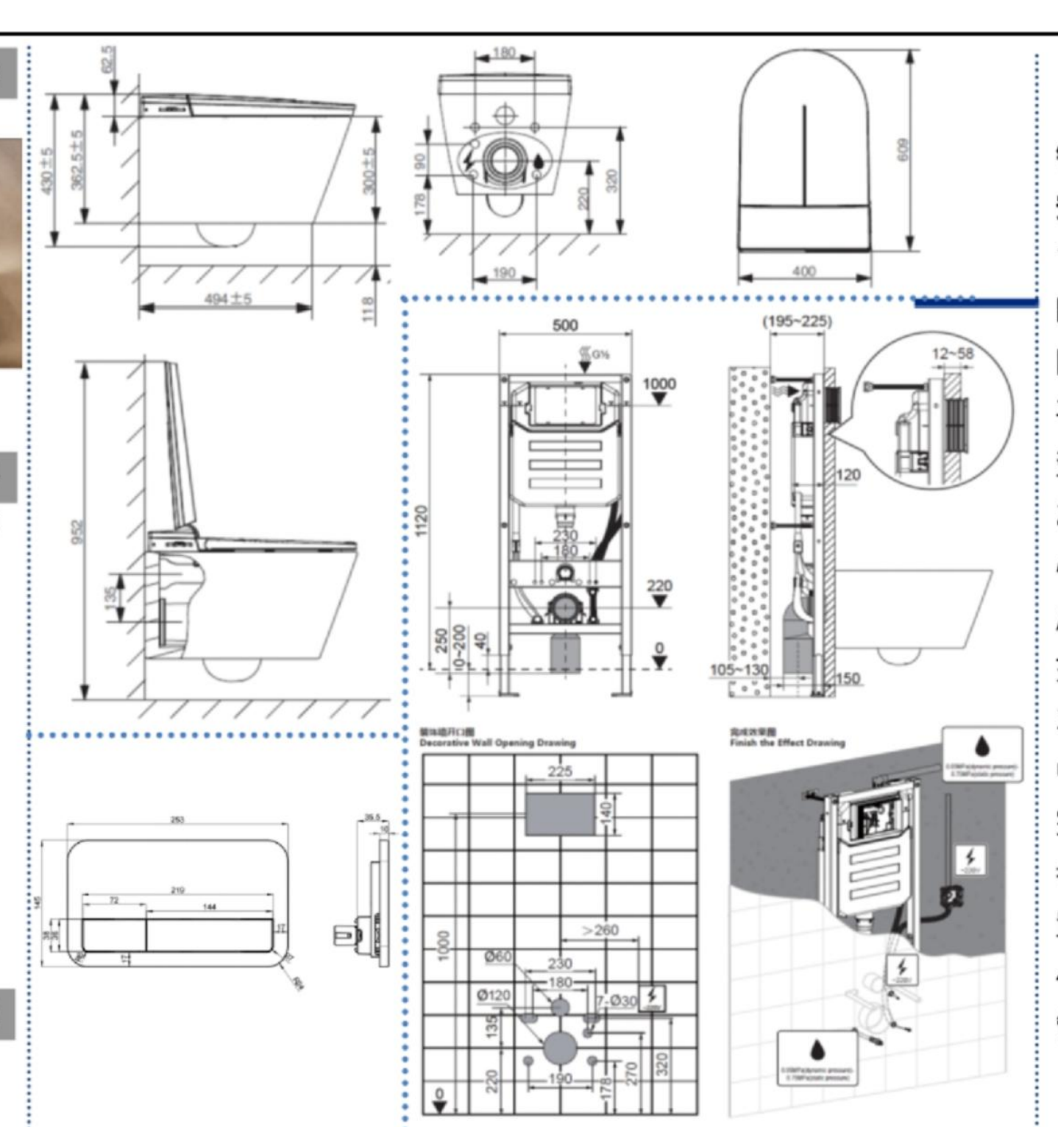

安装说明

针对V9999900支架建议安装如下：

1、建议预埋V9999900时用包装内自带膨胀螺丝固定，预埋时必须用水平仪测量精准。避免出现歪斜情况。
2、建议角阀位置：坑中心点偏左90mm，地面完成面向上178mm，两者交叉点即为角阀安装位置。
3、电源预留位置：坑距中心点偏右90mm，地面完成面向上270mm，两者交叉点即为电源预留位置，电源为220V
4、预埋支架时，弱电线管安装时应注意接头位置

百年翠丽卫浴产品技术图纸

BRTR® BRILLIANT TRUE-LIFE 百年翠丽

产品图示

恒温淋浴享受
丝绒触感水流体验

产品型号

名称：双沄雨暗装恒温淋浴
品牌：德国汉斯格雅
型号：
顶喷：27607007
花洒支架：28331007
控制面板：15763007
阀芯：01800187
手持花洒：26865007
尤宁：27454007
软管：28276007
颜色：镀铬色
材质：铜本体
数量：两套

使用区域

3、次卫、客卫

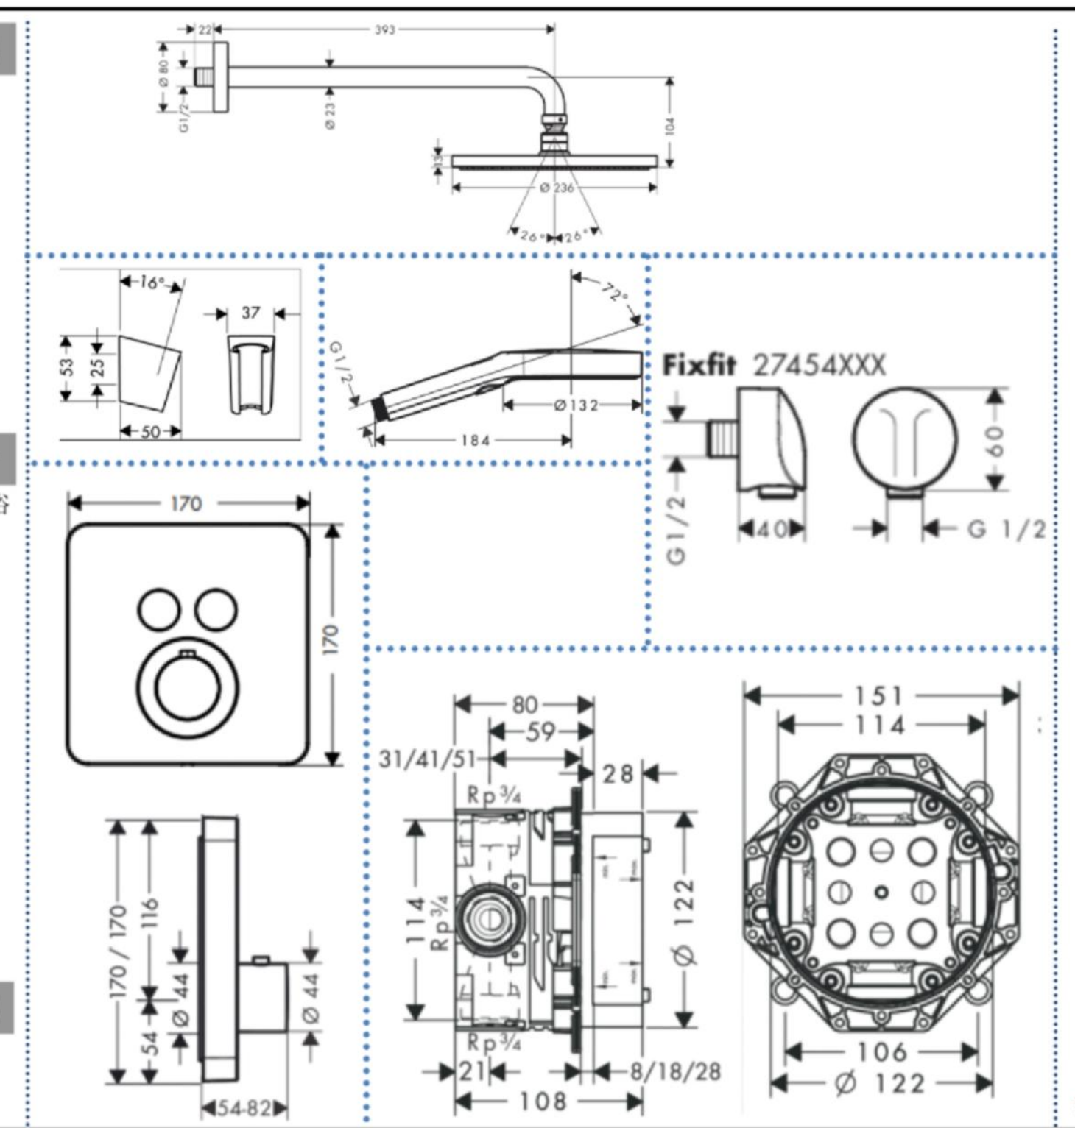
Fixfit 27454XXX
170
31/41/51
80
59
28
114
Rp¾
122
151
114
106
Ø 122
108
8/18/28
G 1/2
2.200AFFL
1.100AFFL
900AFFL
热
冷
FFL±0.000

安装示意图

安装建议：
1、头顶花洒为墙出水，需预留4分内丝，高度2200mm，预留内丝不能凸出完成面。
2、01800187为万能阀芯，建议安装高度为1100mm（地面完成面至阀芯中心点），必须用水平仪测量精准，做到水平和垂直，完成面必须控制在预埋件上的白色纸条范围内。否则会导致面板无法安装。
3、手持出水接口高度900mm，预留4分内丝，预留内丝不能凸出完成面。
4、顶洒、阀芯、下出水口在同一条轴线上。
安装方法与步骤详见包装内说明书。具体安装可根据现场实际情况来定。

百年翠丽卫浴产品技术图纸

BRTR® BRILLIANT TRUE-LIFE 百年翠丽

产品图示

产品型号

名称：T型墙排水
品牌：WT
型号：VTR8209，VTR8209-1
颜色：镀铬色
材质：铜本体
数量：5套

使用区域

所有卫生间

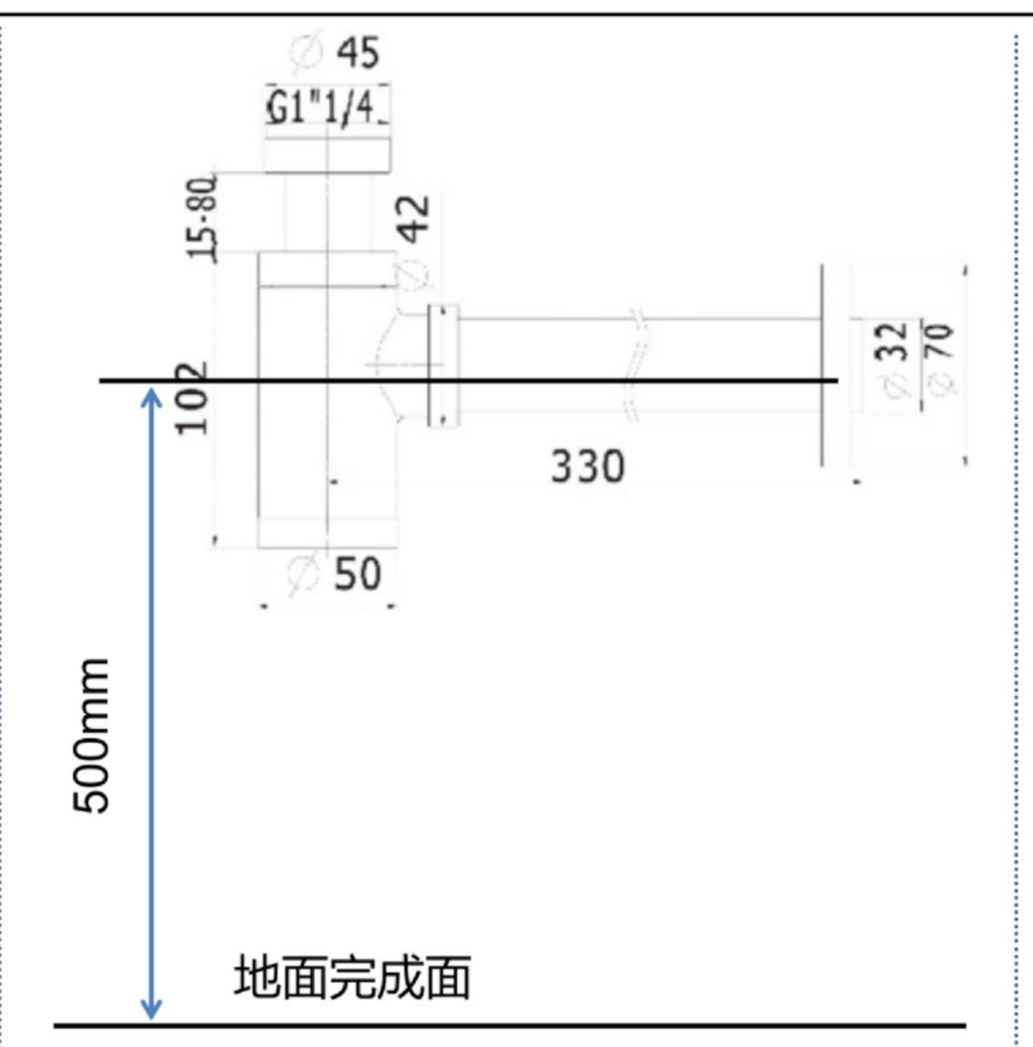
Ø 45
G1"1/4
15-80
42
102
330
32
70
50
500mm
地面完成面

安装示意图

建议尺寸：
1、安装时要求横平竖直，避免出现歪斜现象。
2、安装排水前，须对管道进行放水冲洗，确保无杂质残留。
具体安装可根据现场情况来定。

EIBORN

LEGEND图例

编号	图例	说明
1	🟥	强电
2	🟪	弱电
3	🟩	给水
4	🟦	排水
5	▭	排水(原有)
6	🟥	冷媒进管
7	🟦	冷媒出管
8	🟦	冷凝水管
9	▭	等电位接地线
10	▭	原始墙
11	▭	墙面抹灰≈15mm
12	▭	灰缝≈15mm
13	▭	归方找平层≈15mm
14	▭	墙面粘接剂≈7mm
15	▭	防水背衬板≈12mm
16	▭	直纹白玉石材≈18mm
17	▭	枫丹白露石材≈18mm
18	▭	黑白根大理石≈18mm
19	▭	伊朗绿大理石≈18mm

盖章

注释
Notes
1.本图纸如与现场尺寸有误，请施工人员与项目负责人联系。
2.施工前施工人员应认真查阅此图，如有不明确尺寸，按现场测量为准。
3.本图纸必须经甲乙双方认可并签字方可作为施工依据。

日期
Date 06/06/26

修订
Revision
△1

项目
Project
潮映华岸府3-801

比例
Scale

客卫洁具分析图

图纸编号
Drawing No.
ST-19

项目编号
Project No.

©2025

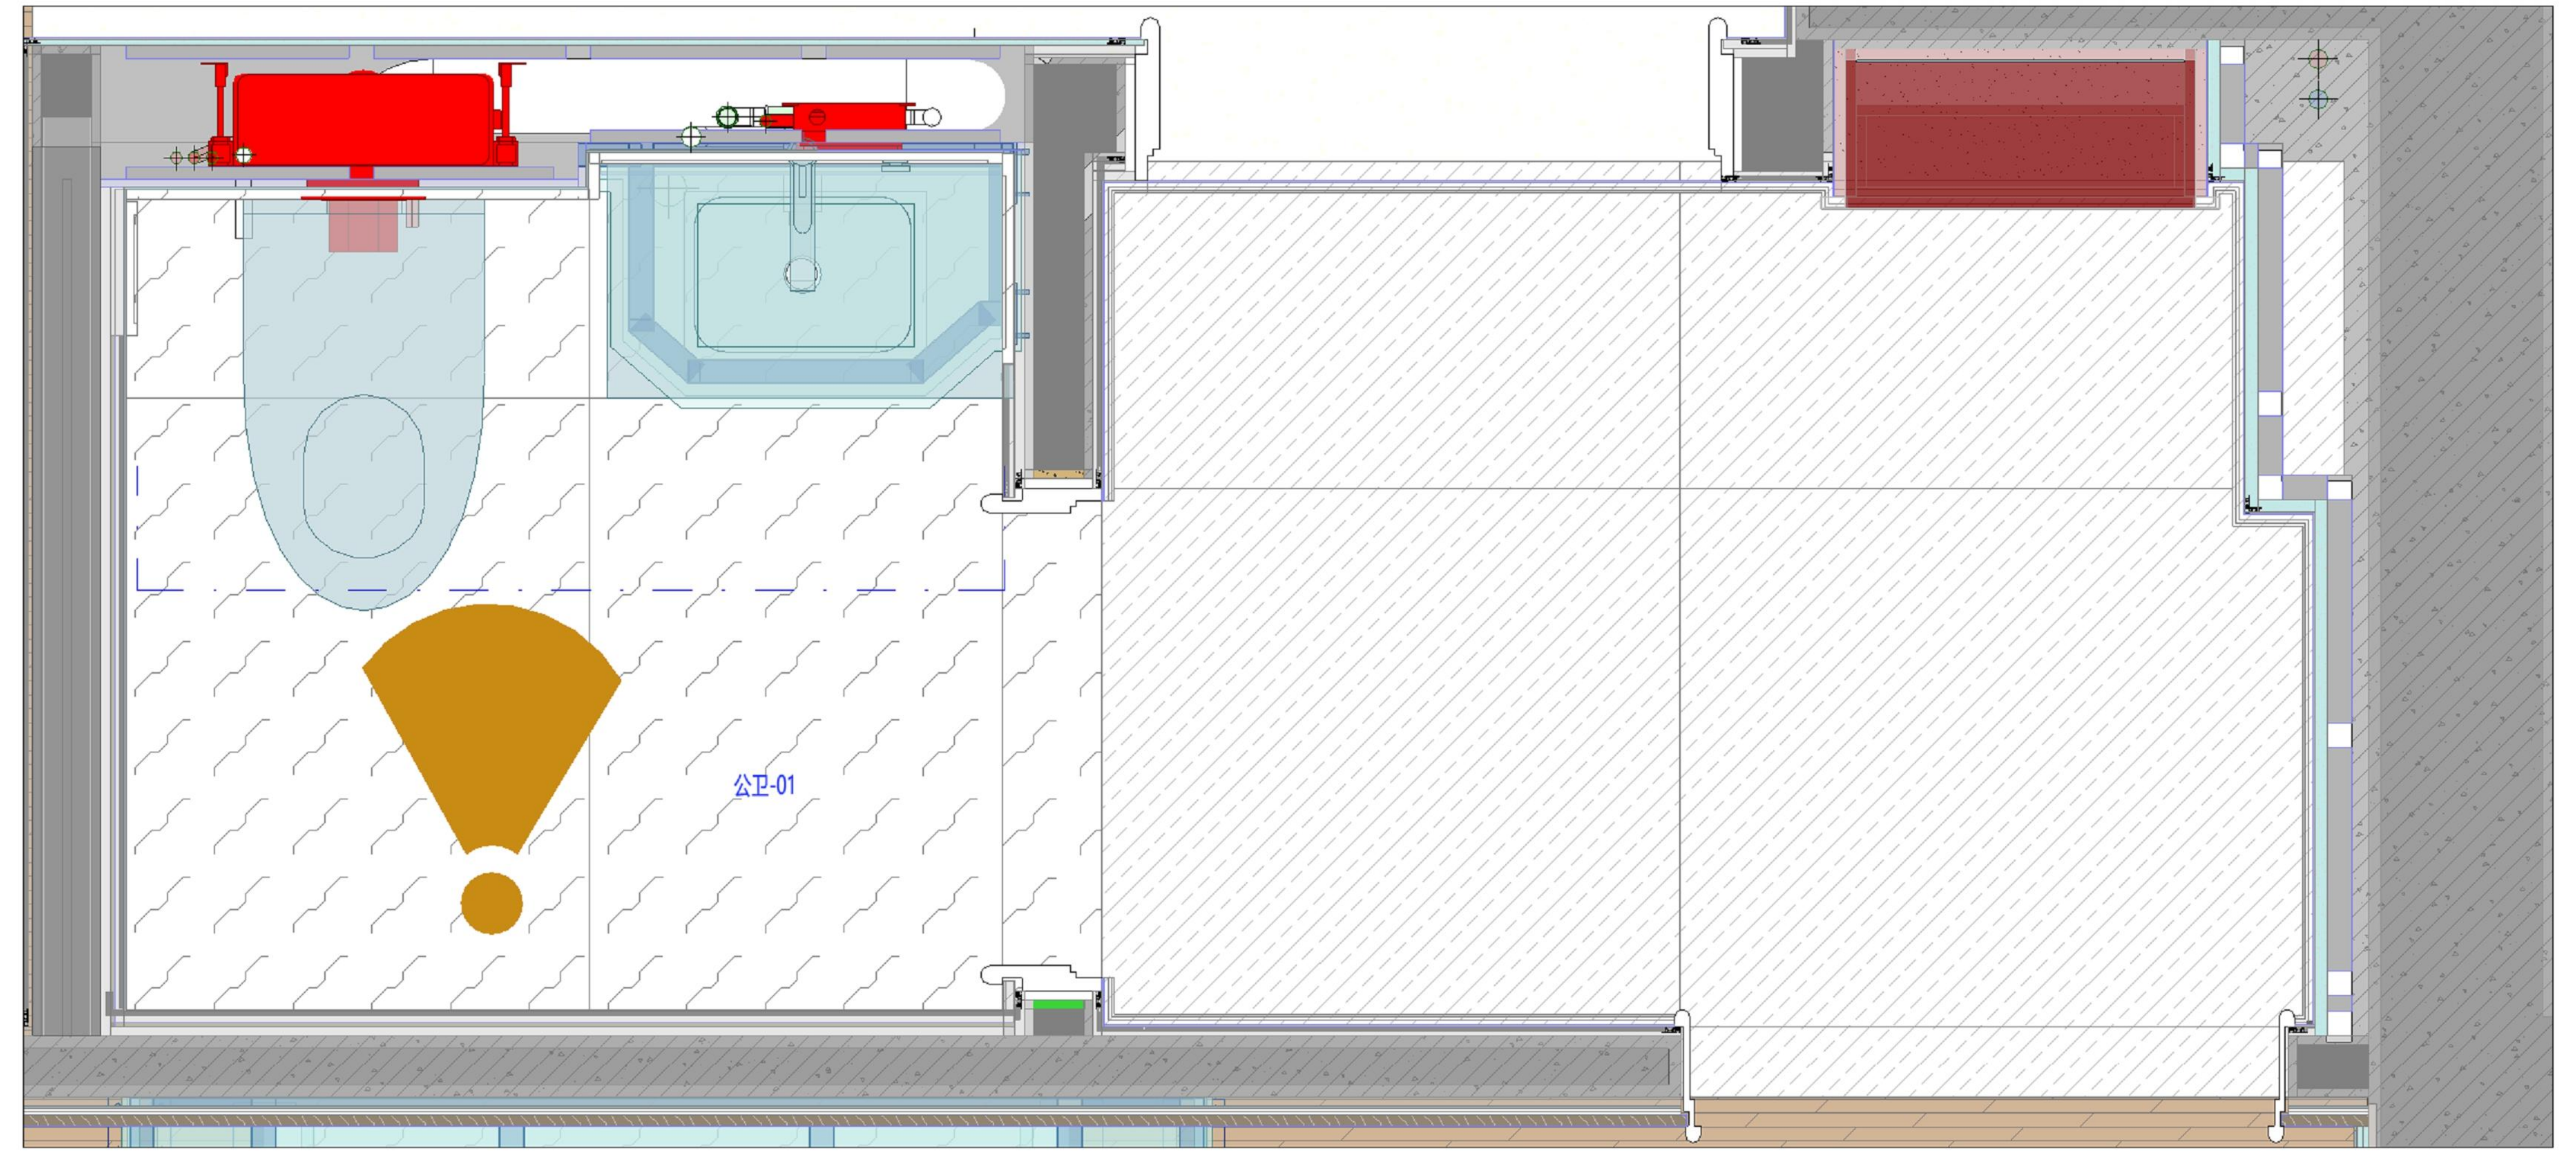

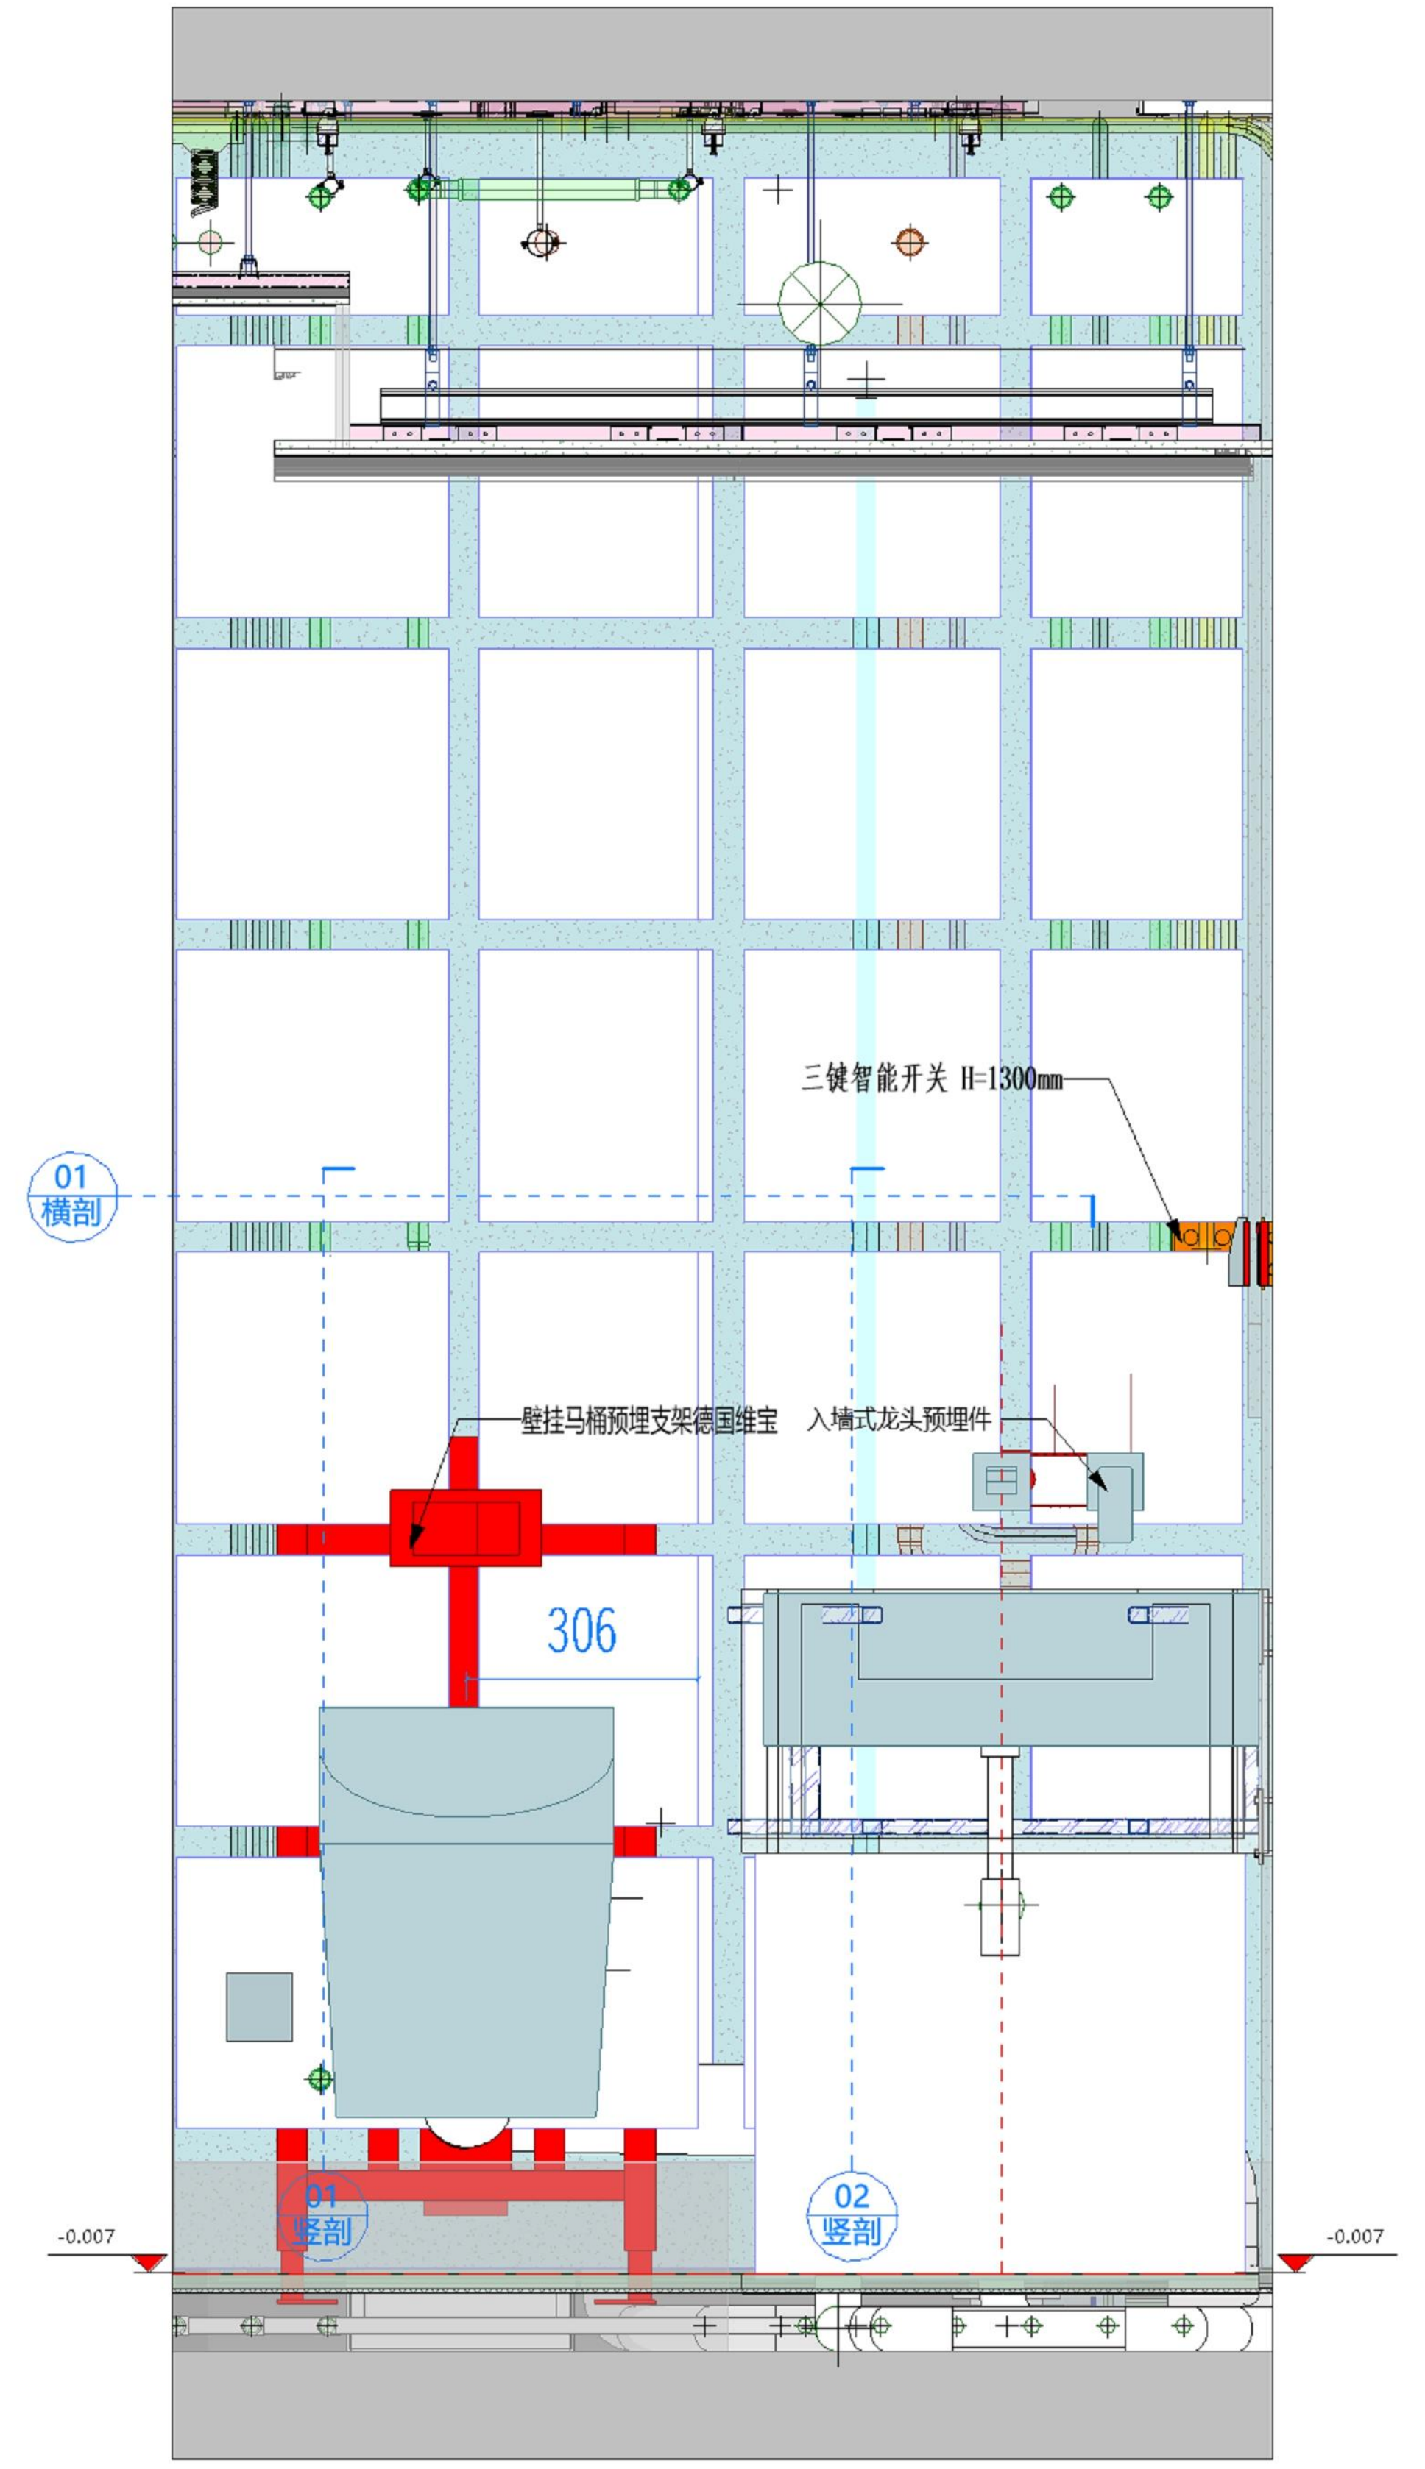
三键智能开关 H=1300mm
01
横剖
壁挂马桶预埋支架德国维宝
入墙式龙头预埋件
306
01
竖剖
02
竖剖
-0.007
-0.007

公卫-01

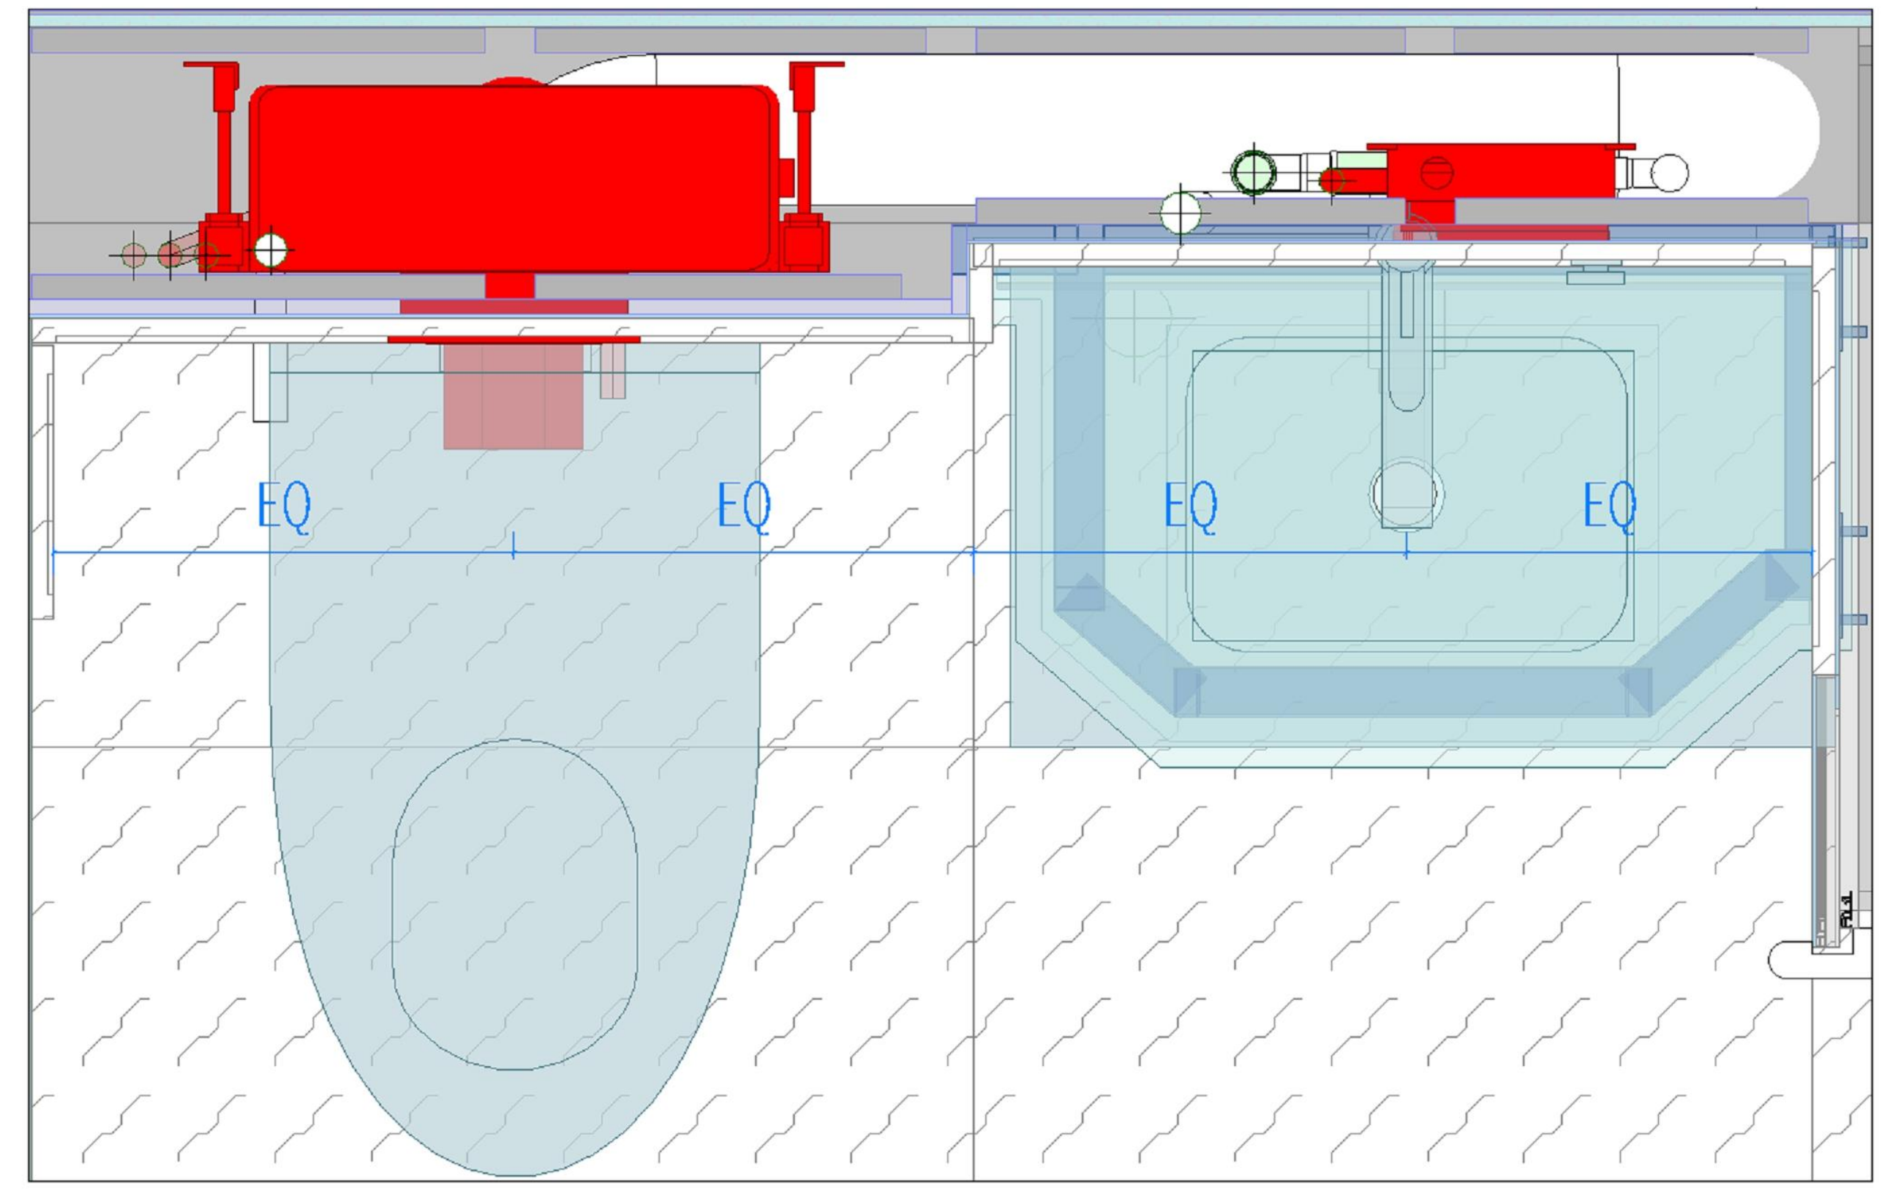

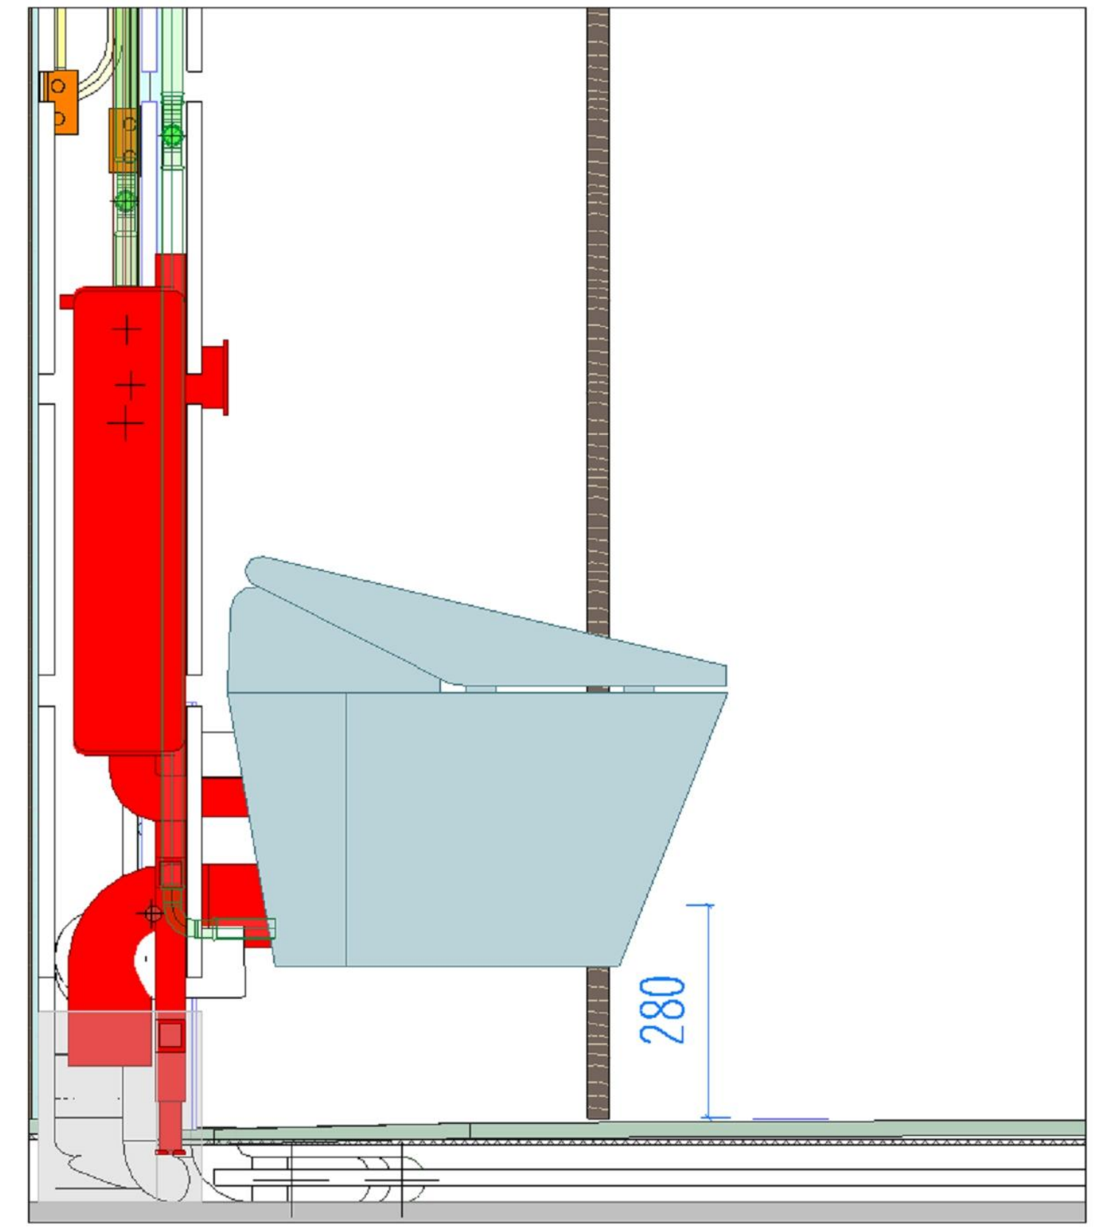

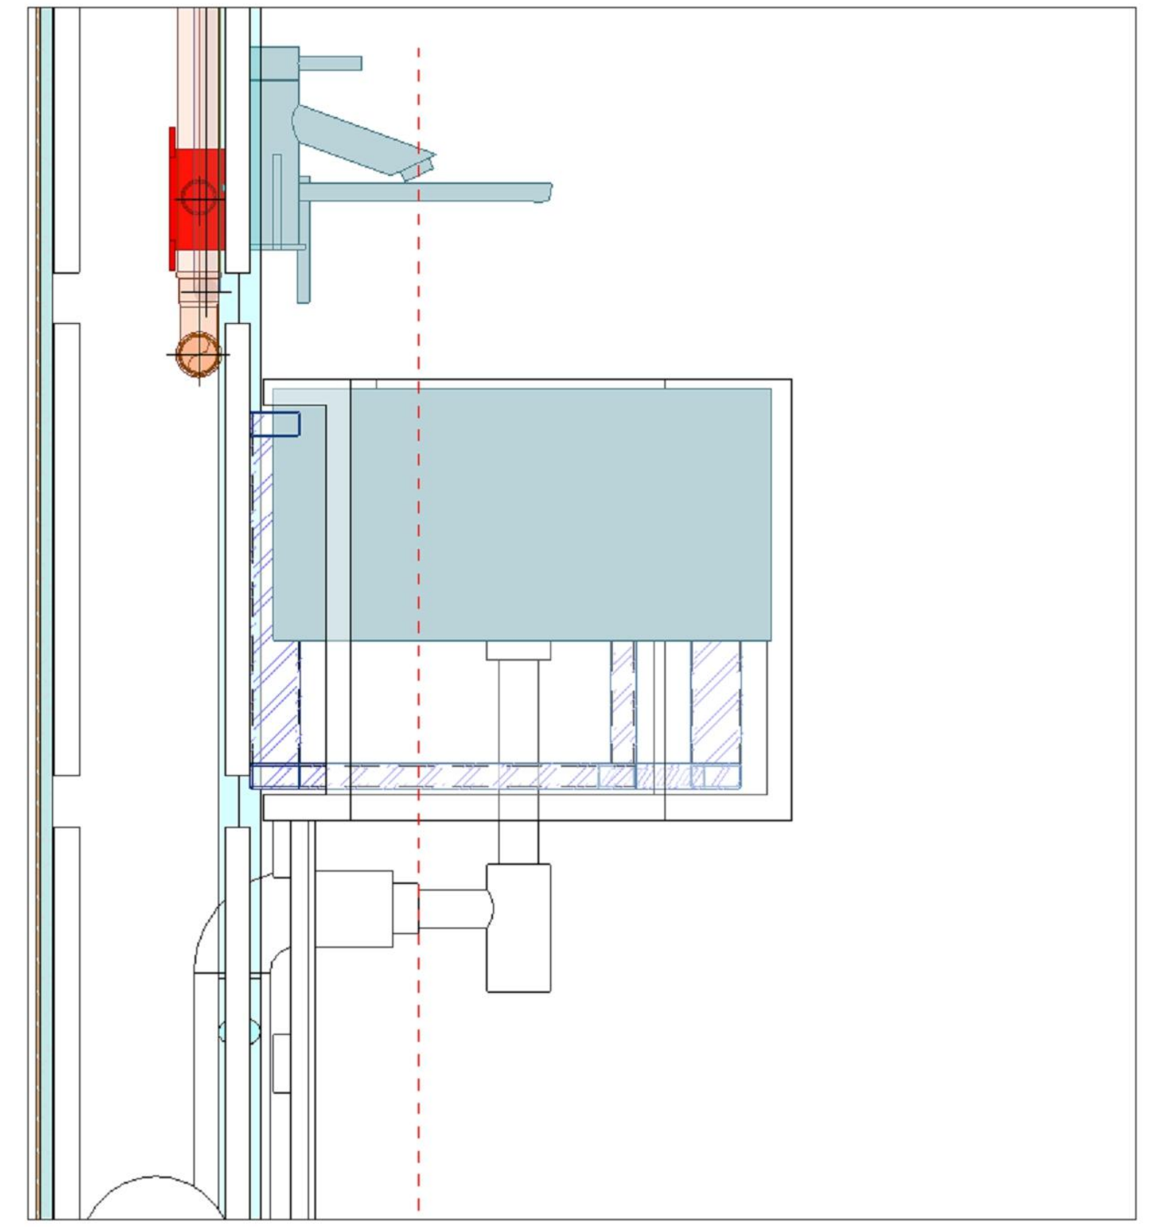

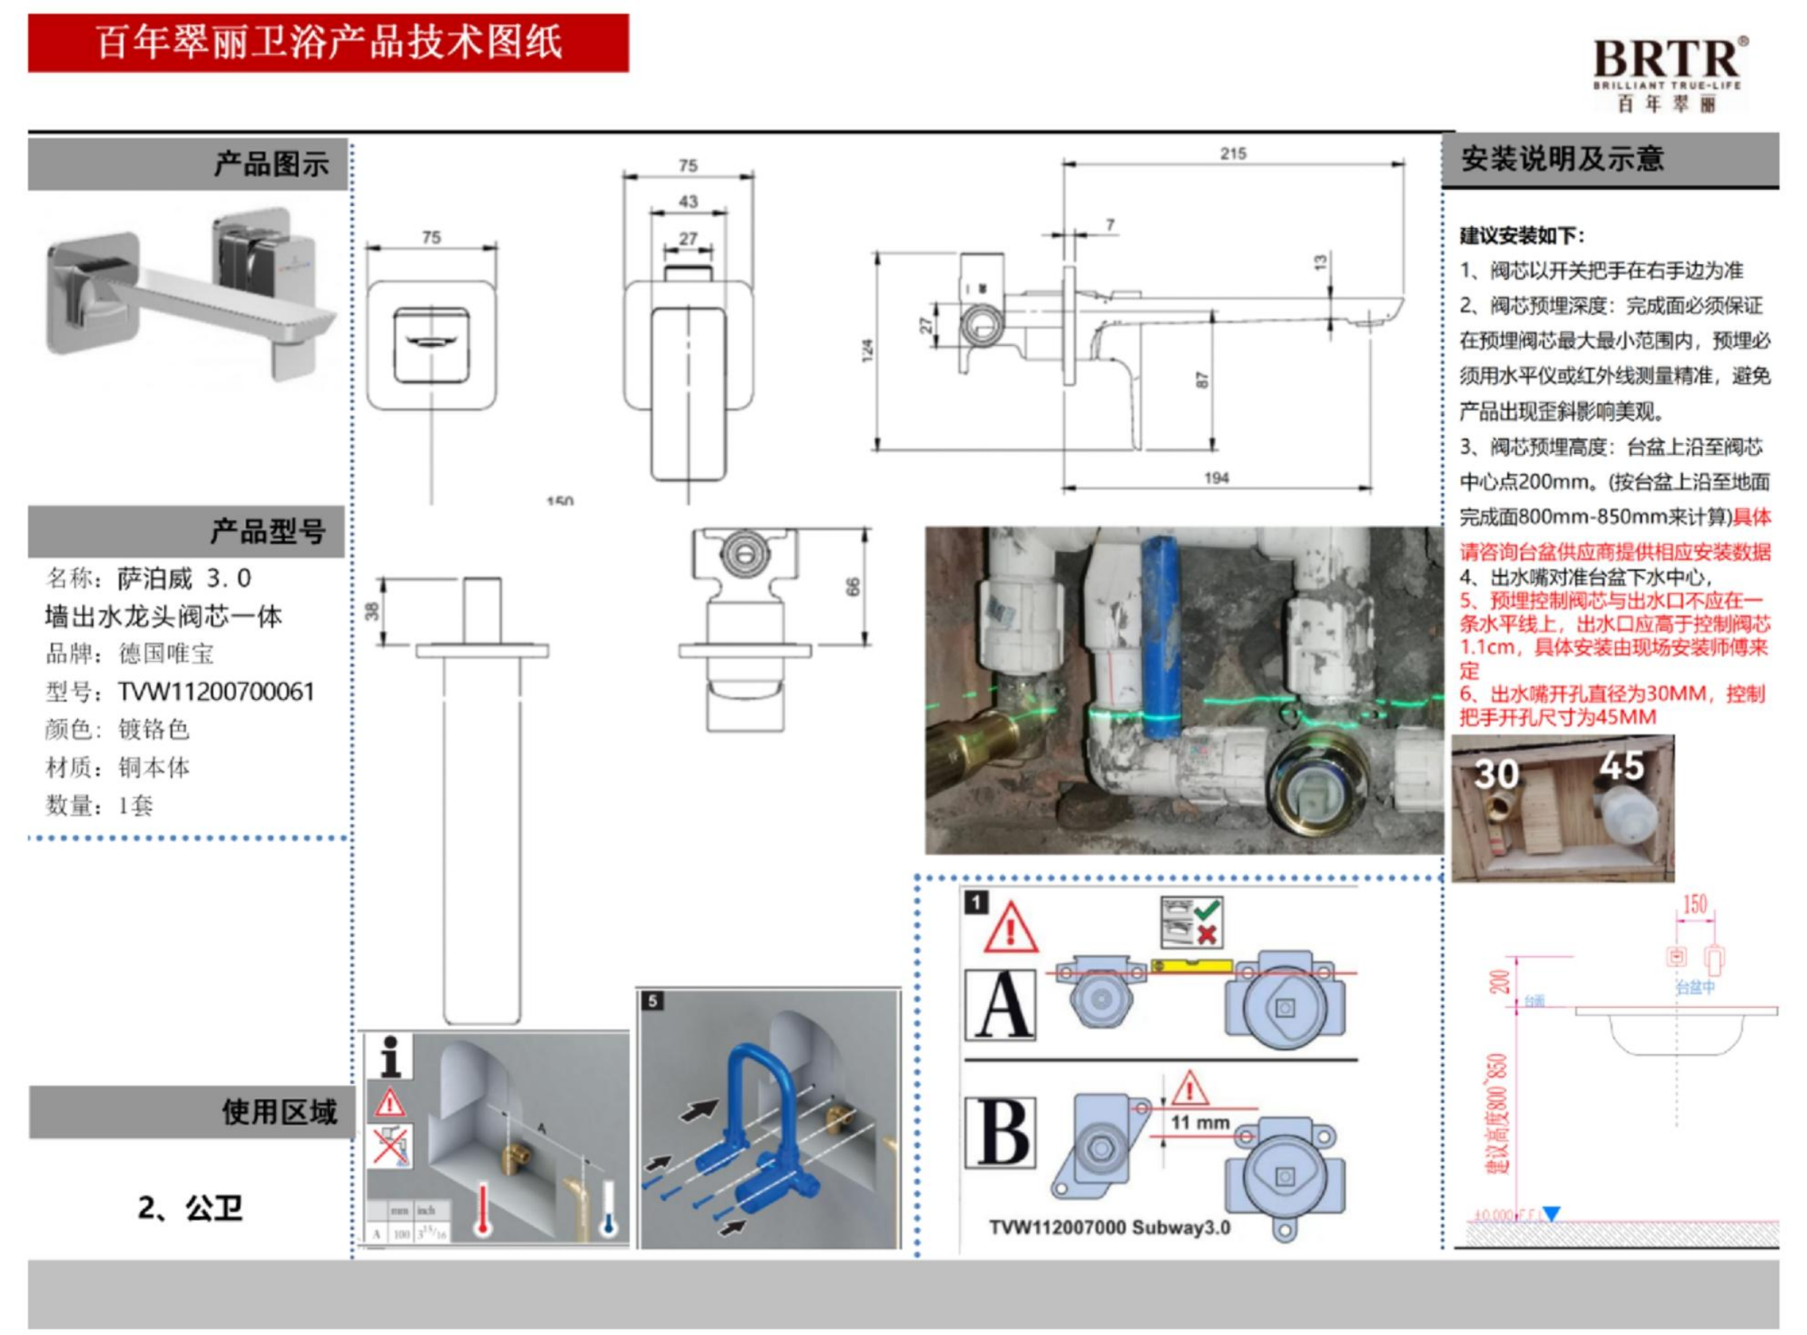

百年翠丽卫浴产品技术图纸

BRTR
BRILLIANT TRUE-LIFE
百年翠丽

产品图示

产品型号

名称：萨泊威 3.0
墙出水龙头阀芯一体
品牌：德国唯宝
型号：TVW11200700061
颜色：镀铬色
材质：铜本体
数量：1套

使用区域

2、公卫

安装说明及示意

建议安装如下：
1、阀芯以开关把手在右手边为准
2、阀芯预埋深度：完成面必须保证在预埋阀芯最大最小范围内，预埋必须用水平仪或红外线测量精准，避免产品出现歪斜影响美观。
3、阀芯预埋高度：台盆上沿至阀芯中心点200mm。(按台盆上沿至地面完成面800mm-850mm来计算)具体请咨询台盆供应商提供相应安装数据
4、出水嘴对准台盆下水中心。
5、预埋控制阀芯与出水口不应在一条水平线上，出水口应高于控制阀芯1.1cm，具体安装由现场安装师傅来定
6、出水嘴开孔直径为30MM，控制把手开孔尺寸为45MM

75
75
43
27
215
7
13
124
27
87
194
38
66
30
45
A
B
11 mm
TVW112007000 Subway3.0
150
200
建议高度800~850

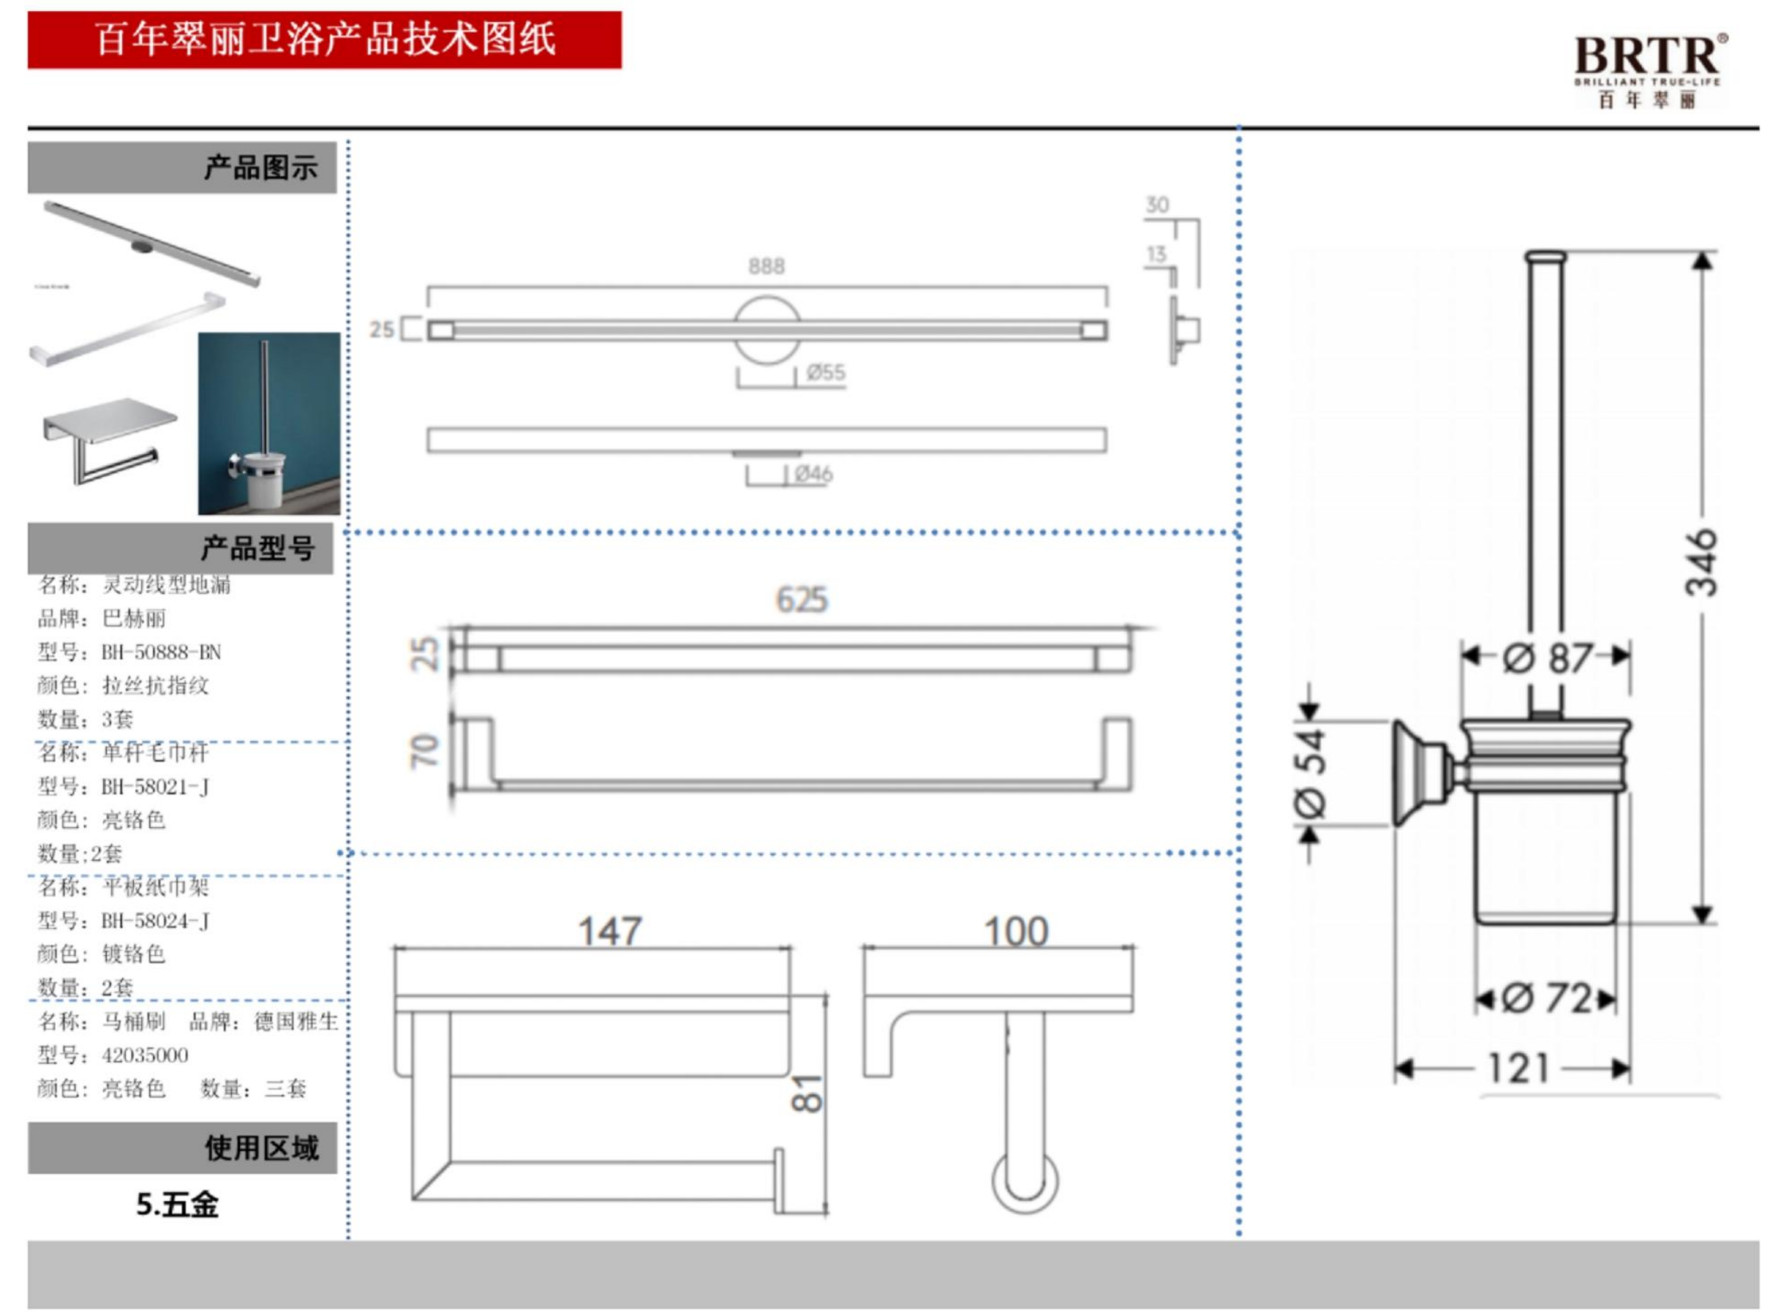

百年翠丽卫浴产品技术图纸

BRTR
BRILLIANT TRUE-LIFE
百年翠丽

产品图示

产品型号

名称：灵动线型地漏
品牌：巴赫丽
型号：BH-50888-BN
颜色：拉丝抗指纹
数量：3套

名称：单杆毛巾杆
型号：BH-58021-J
颜色：亮铬色
数量:2套

名称：平板纸巾架
型号：BH-58024-J
颜色：镀铬色
数量：2套

名称：马桶刷　品牌：德国雅生
型号：42035000
颜色：亮铬色　数量：三套

使用区域

5.五金

888
30
13
25
Ø55
Ø46
625
25
70
147
100
81
346
Ø 87
Ø 54
Ø 72
121

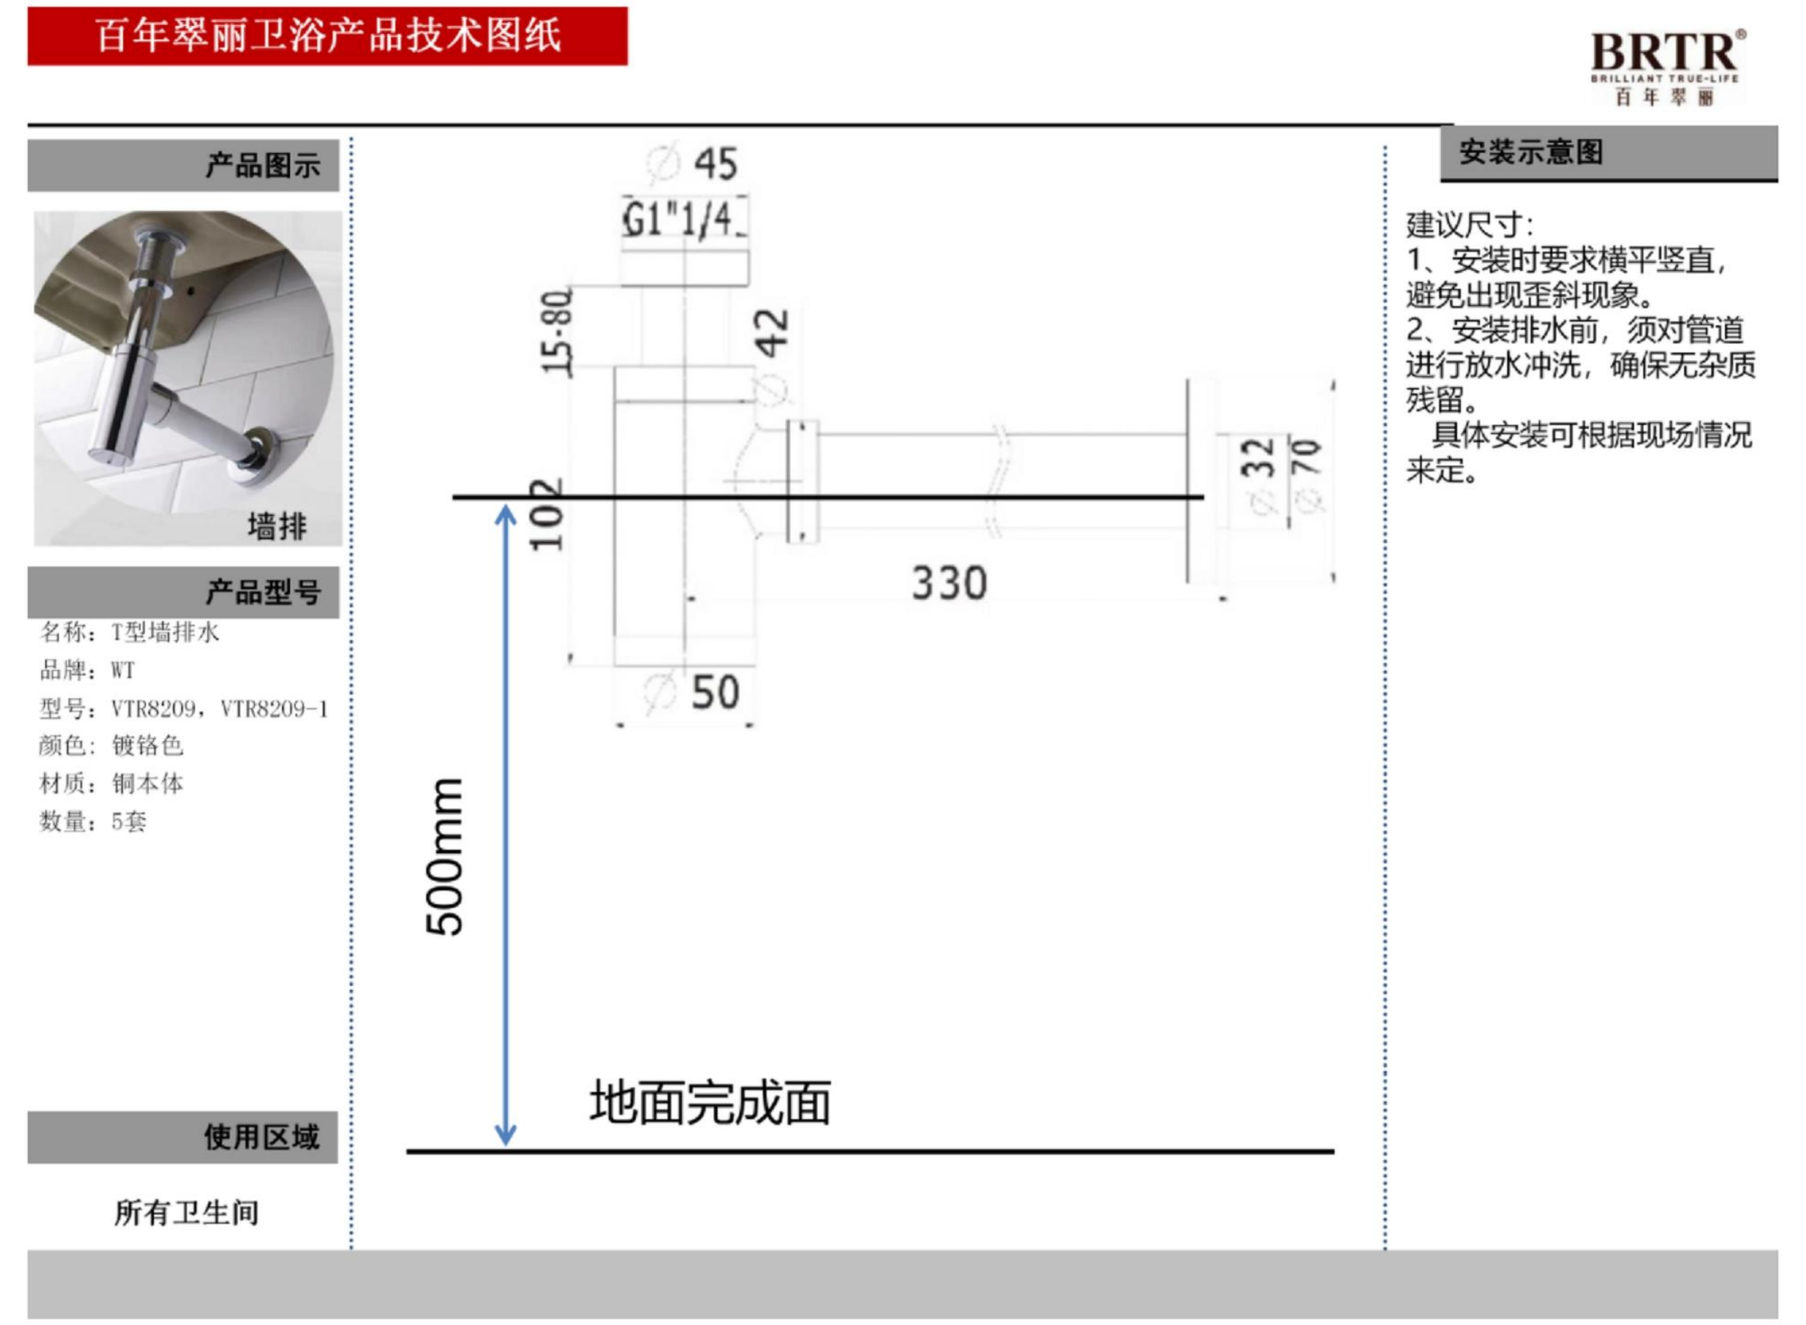

百年翠丽卫浴产品技术图纸

BRTR
BRILLIANT TRUE-LIFE
百年翠丽

产品图示

墙排

产品型号

名称：T型墙排水
品牌：WT
型号：VTR8209，VTR8209-1
颜色：镀铬色
材质：铜本体
数量：5套

使用区域

所有卫生间

安装示意图

建议尺寸：
1、安装时要求横平竖直，避免出现歪斜现象。
2、安装排水前，须对管道进行放水冲洗，确保无杂质残留。
具体安装可根据现场情况来定。

Ø 45
G1"1/4
15-80
42
102
330
Ø 32
Ø 70
Ø 50
500mm
地面完成面

LEGEND图例

编号	图例	说明
1	🟥	强电
2	🟪	弱电
3	🟩	给水
4	🟦	排水
5	▬	排水(原有)
6	🟥	冷媒进管
7	🟦	冷媒出管
8	🟦	冷凝水管
9	▬	等电位接地线
10	▬	原始墙
11	▬	墙面抹灰≈15mm
12	▭	灰缝≈15mm
13	▬	归方找平层≈15mm
14	▬	墙面粘接剂≈7mm
15	▬	防水背衬板≈12mm
16	▭	直纹白玉石材≈18mm
17	▭	枫丹白露石材≈18mm
18	▭	黑白根大理石≈18mm
19	▭	伊朗绿大理石≈18mm

盖章

注释
Notes
1.本图纸如与现场尺寸有误，请施工人员与项目负责人联系。
2.施工前施工人员应认真查阅此图，如有不明确尺寸，按现场测量为准。
3.本图纸必须经甲乙双方认可并签字方可作为施工依据。

日期
Date　06/06/26

修订
Revision
1

项目
Project
潮映华岸府3-801

比例
Scale

公卫洁具分析图

图纸编号
Drawing No.
ST-20

项目编号
Project No.
©2025