杭州潮映华岸府项目

机电深化施工图

出图日期：2026年3月24日

DRAWINGS LIST 图纸目录

PROJECT 项目名称：杭州潮映华岸府3-801

DQG.NO 图号	TITLE 内容	SCALE 比例	DATE/日期	REV.修订
MEP-01	封面	1 : 55@A2	2026.4.1	
MEP-02	目录	1 : 55@A2	2026.4.1	
MEP-03	综合天花图	1 : 55@A2	2026.4.1	
MEP-04	管综布置图	1 : 55@A2	2026.4.1	
MEP-05	管路过梁图	1 : 55@A2	2026.4.1	
MEP-06A	设备支吊架布置图A	1 : 55@A2	2026.4.1	
MEP-06B	设备支吊架布置图B	1 : 55@A2	2026.4.1	
MEP-07	检修口与风口布置图	1 : 55@A2	2026.4.1	
MEP-08	空调布置图	1 : 55@A2	2026.4.1	
MEP-09	新风布置图	1 : 55@A2	2026.4.1	
MEP-10A	水电支吊架布置图A	1 : 55@A2	2026.4.1	
MEP-10B	水电支吊架布置图B	1 : 55@A2	2026.4.1	
MEP-11	灯具定位图	1 : 55@A2	2026.4.1	
MEP-12	点位布置图	1 : 55@A2	2026.4.1	
MEP-13	桥架布置图	1 : 55@A2	2026.4.1	
MEP-14	电路布置图	1 : 55@A2	2026.4.1	

DQG.NO 图号	TITLE 内容	SCALE 比例	DATE/日期	REV.修订
MEP-15	电气系统图	1 : 55@A2	2026.4.1	
MEP-16	给水布置图	1 : 55@A2	2026.4.1	
MEP-17	排水布置图	1 : 55@A2	2026.4.1	
MEP-17A	主卫排水布置图	1 : 50@A2	2026.4.1	
MEP-17B	客卫排水布置图	1 : 50@A2	2026.4.1	
MEP-17C	次卫排水布置图	1 : 25@A2	2026.4.1	
MEP-17D	中西厨排水布置图	1 : 50@A2	2026.4.1	
MEP-17E	家政间排水布置图	1 : 25@A2	2026.4.1	
MEP-18	水电立面索引图	1 : 55@A2	2026.4.1	
MEP-19	主卫	1 : 30@A2	2026.4.1	
MEP-20	次卫	1 : 30@A2	2026.4.1	
MEP-21	公卫	1 : 30@A2	2026.4.1	
MEP-22	客卫	1 : 30@A2	2026.4.1	
MEP-23	家政间	1 : 30@A2	2026.4.1	
MEP-24	中厨	1 : 30@A2	2026.4.1	
MEP-25	西厨	1 : 30@A2	2026.4.1	

注释
Notes
1.本图纸如与现场尺寸有误，请施工人员与项目负责人联系。
2.施工前施工人员应认真查阅此图，如有不明确尺寸，按现场测量为准。
3.本图纸必须经甲乙双方认可并签字方可作为施工依据。

日期
Date 01/20/26

修订
Revision

项目
Project
潮映华岸府3-801

Scale
比例
目录

Drawing No.
图纸编号
MEP-02

Project No.
项目编号

©2025

天花图立面梁窗帘

直接做在自上 看图例说明

直接做在上 看图例说明

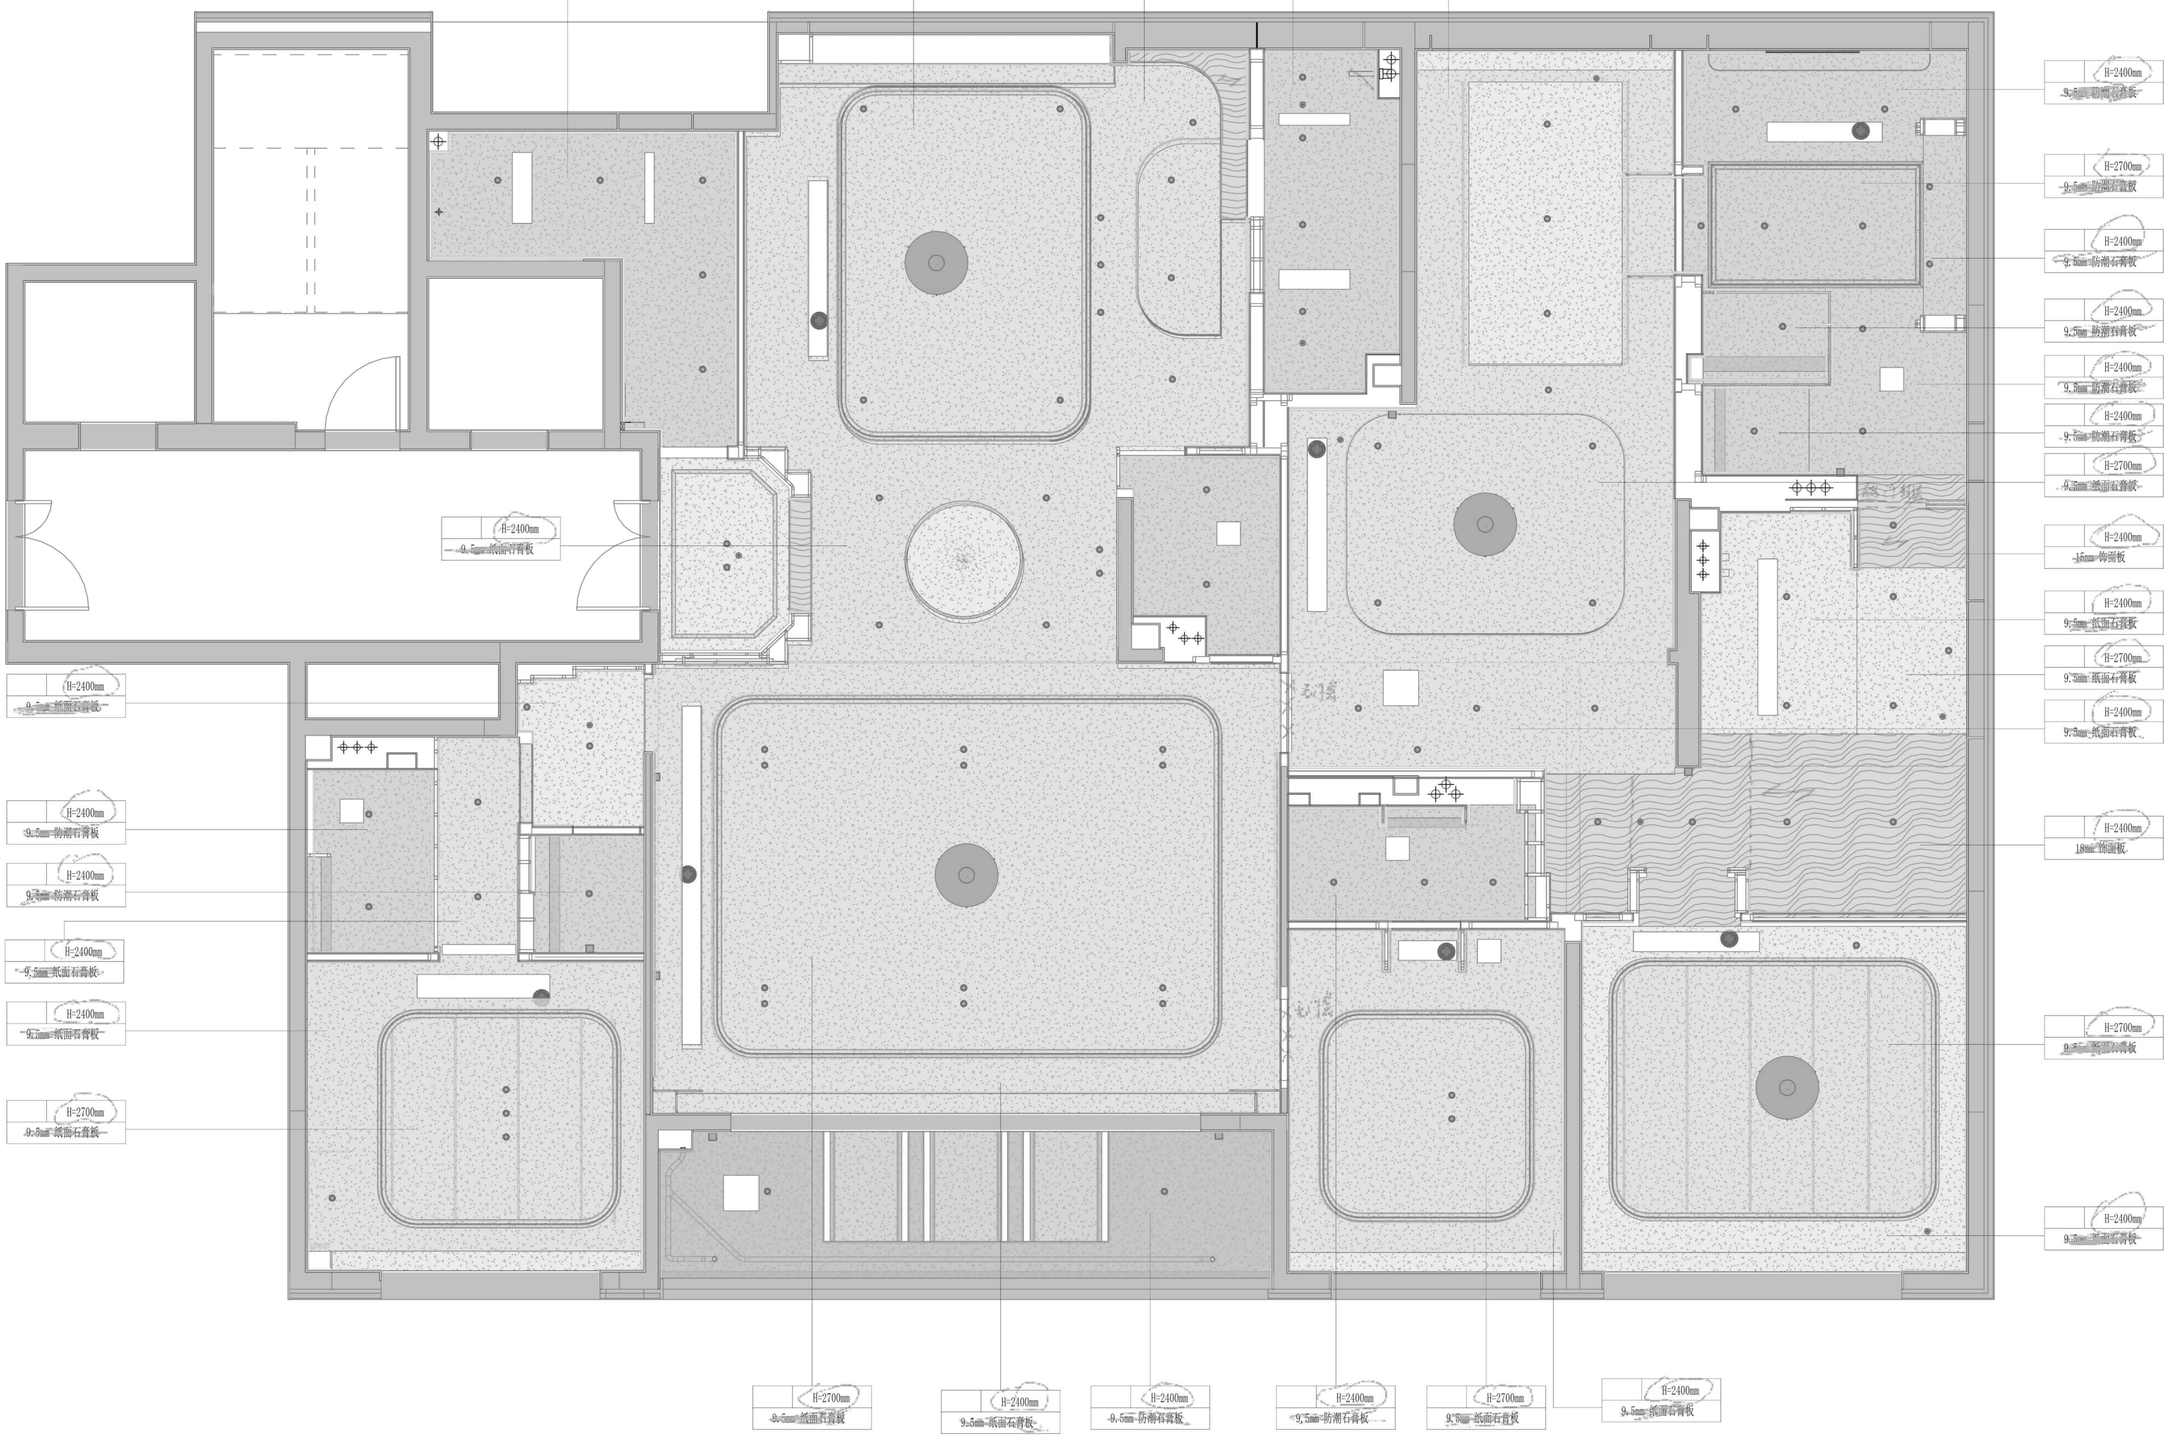

1

综合天花图

Scale比例 1:55@A2

EIBORN

LEGEND图例

编号	图例	说明
1		9.5mm纸面石膏板
2		9.5mm防潮石膏板

图例无显示饰面材料石膏板型号请显示在饰面石膏板下面图号

补充图例：PT-01 PT-02 PT-03 PT-06 PT-07 WA-02 WA-13 WO-01 灯具图例对应编号出风口回风口按需设，监控等末端点位

盖章

注释
Notes

1.本图纸如与现场尺寸有误，请施工人员与项目负责人联系。
2.施工前施工人员应认真查阅此图，如有不明确尺寸，按现场测量为准。
3.本图纸必须经甲乙双方认可并签字方可作为施工依据。

日期
Date 01/24/26

修订
Revision

1

项目
Project

潮映华岸府3-801

比例
Scale 1:55@A2

综合天花图

图纸编号
Drawing No.

MEP-03

项目编号
Project No.

©2025

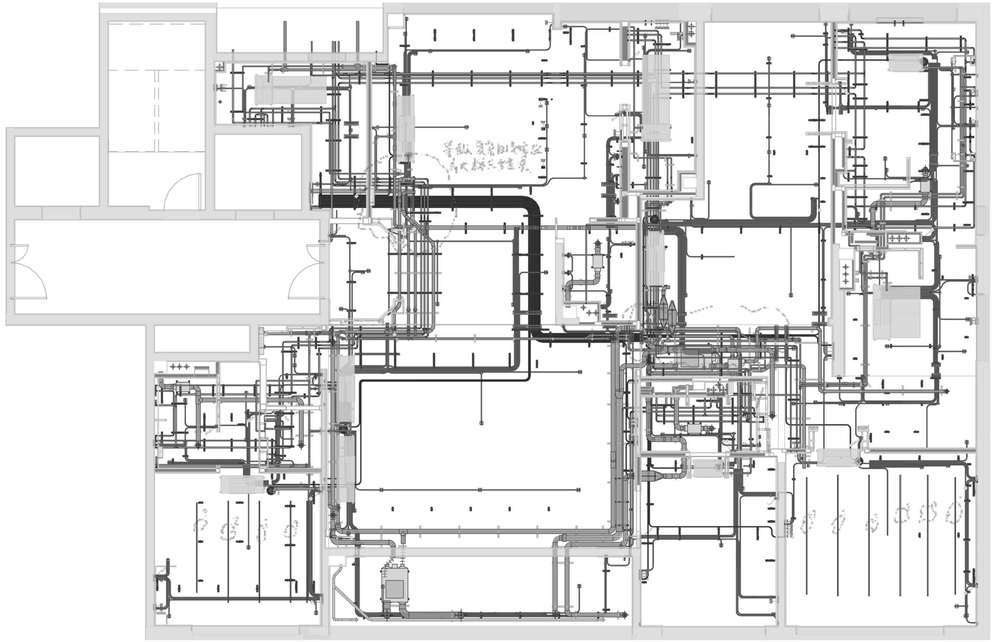

1

管综-01

管综布置平面图

Scale比例 1 : 55@A2

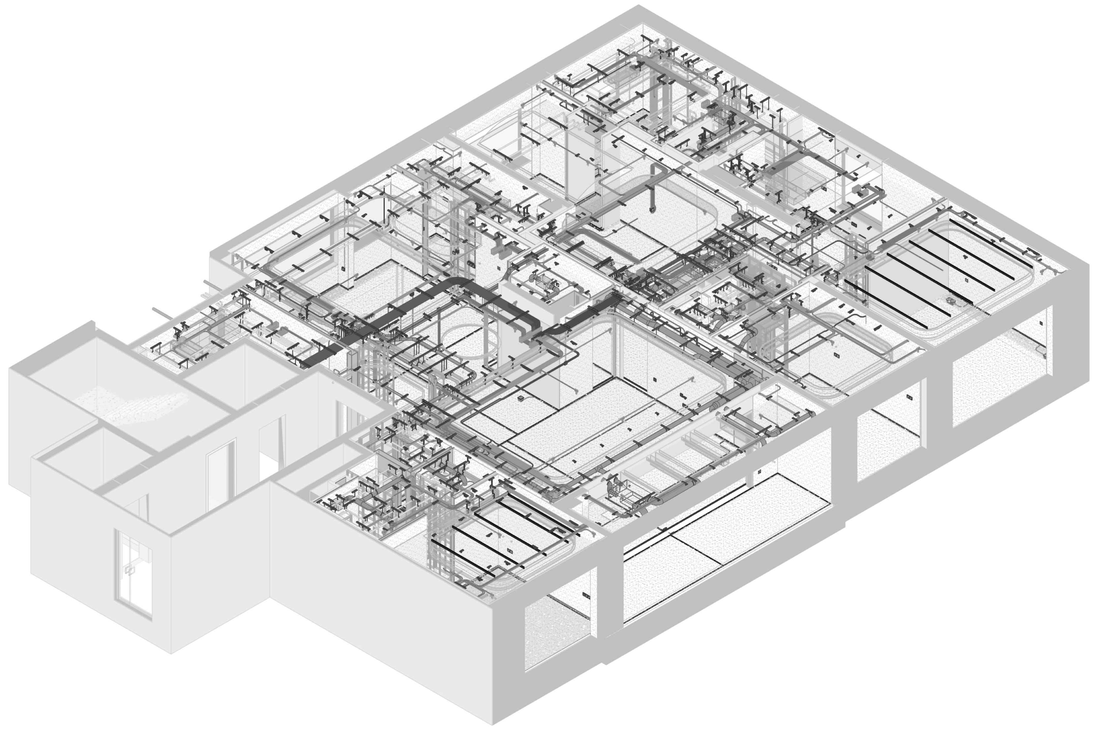

2

管综-02

管综布置三维图

Scale比例 1:55@A2

注释
Notes
1.本图纸如与现场尺寸有误，请施工人员与项目负责人联系。
2.施工前施工人员应认真查阅此图，如有不明确尺寸，按现场测量为准。
3.本图纸必须经甲乙双方认可并签字方可作为施工依据。

LEGEND图例

编号	图例	说明
1		强电
2		弱电
3		给水
4		排水
5		排水(原有)
6		空调
7		新风
8		室内梁
9		桥架
10		水电支吊系统
11		设备支吊系统

线管过梁器节点

日期
Date 01/20/26

修订
Revision

项目
Project

潮映华府府3-801

Scale
比例 1:55@A2

管综布置图

Drawing No.
图纸编号

MEP-04

Project No.
项目编号 ©2026

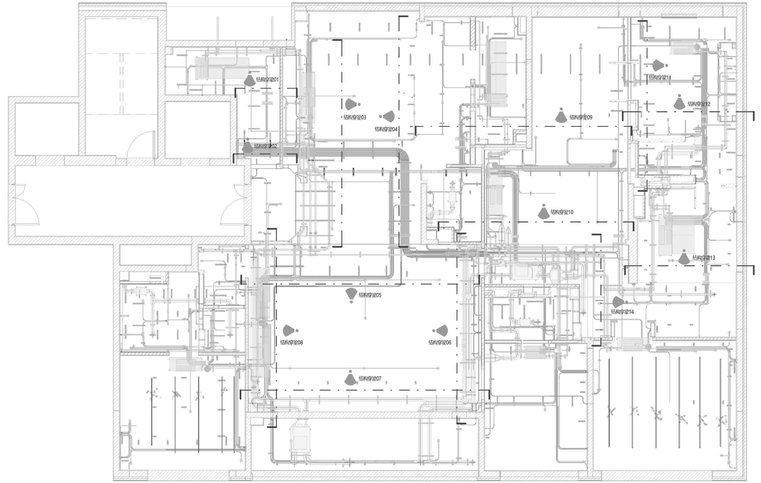

管路过梁01

管路过梁02

管路过梁03

管路过梁04

管路过梁05

管路过梁06

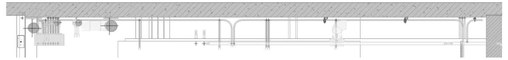

管路过梁07

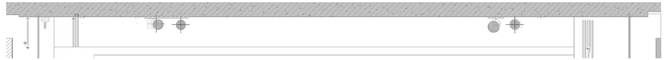

管路过梁08

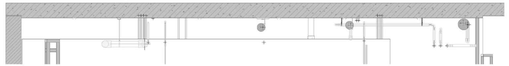

管路过梁09

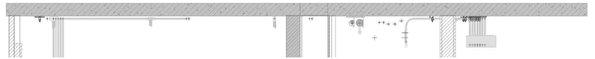

管路过梁10

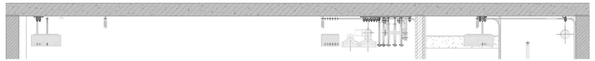

管路过梁11

管路过梁12

管路过梁13

管路过梁14

LEGEND图例

编号	图例	说明
1		烟气
2		消防
3		给水
4		排水
5		雨水(屋面)
6		空调
7		新风
8		室内区
9		预留
10		冷机出供系统
11		冷机出回系统

日期 Date 01/09/26

修订 Revision

项目 Project
湖映华府府3-B01

Scale 比例 1:20@A2

管路过梁图

Drawing No. 图纸编号 MEP-05

Project No. 项目编号 e-2026

1	结构梁梁索引图	2	管路过梁大样图
结构梁-01	Scale比例 1：55@A2	结构梁-02	Scale比例 1:20@A2

注释 Notes
1.本图纸如与图纸尺寸有误，请施工人员与总院负责人联系。
2.施工前施工人员认真查验现场，如有不明确尺寸，按照实际测量为准。
3.本图纸以结构中间区部分以可供参考不可作为施工依据。

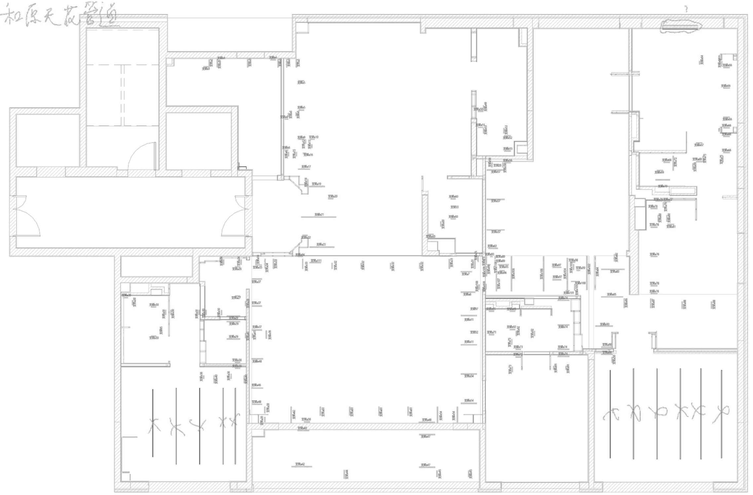

1		2	
支吊架-04	设备支吊架布置平面图 Scale比例 1 : 55@A2	支吊架-05	

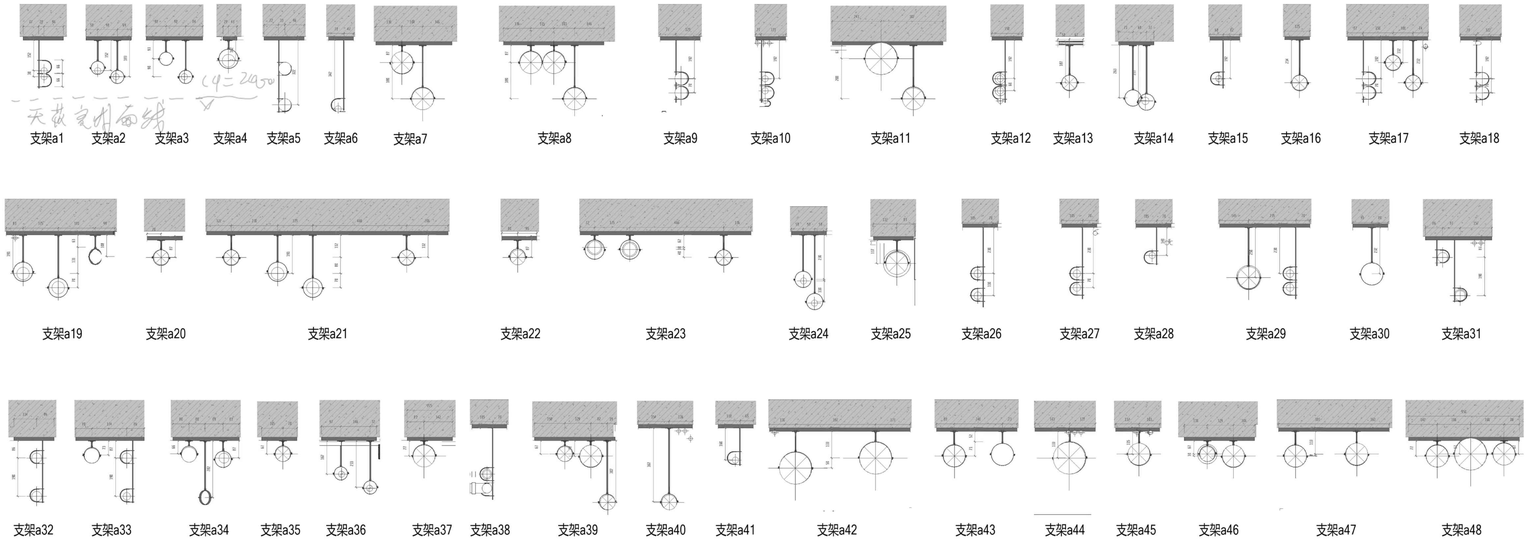

设备支吊架大样图C

Scale比例 1:8@A2

Notes
1.本图纸如与图纸尺寸有误，请施工人员与总院负责人联系。
2.施工前施工人员认真熟悉此图，如有不明确尽早，到现场调解为宜。
3.本图纸以设备中式支吊架为施工依据。

Date	01/09/26
Revision	
Project	国映华府府3-B01
Scale	1:8@A2
Drawing No.	MEP-06A
Project No.	e3026

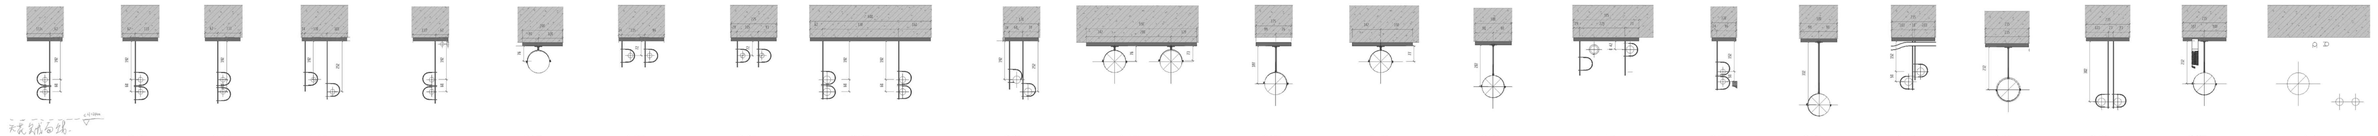

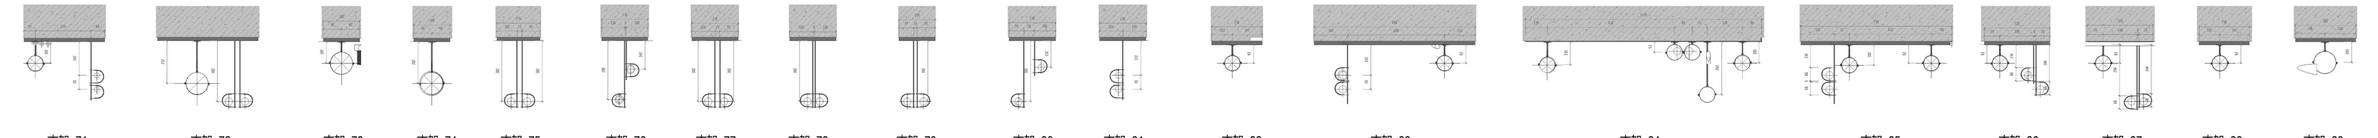

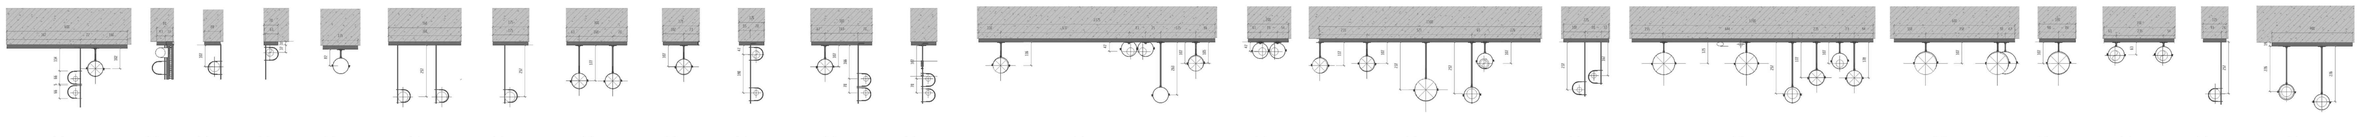

1		设备支吊架大样图D	
支吊架-06		Scale比例 1:8@A2	

注释 Notes
1.本图纸如与图纸尺寸存标注，请施工人员与总图负责人联系。
2.施工前施工人员应认真阅读此图，如有不明确处下计，按图纸明确为准。
3.本图纸此设备吊架仅提供以可供参考不可作为施工依据。

悦孚 Yue Fu China

上海服务中心
徐汇区湖南路20弄14号

日期 Date 01/09/26
修订 Revision
项目 Project
国铁华翠路3-801
Scale 比例 1:8@A2
设备支吊架布置图B
Drawing No. 图纸编号 MEP-068
Project No. 项目编号 #3025

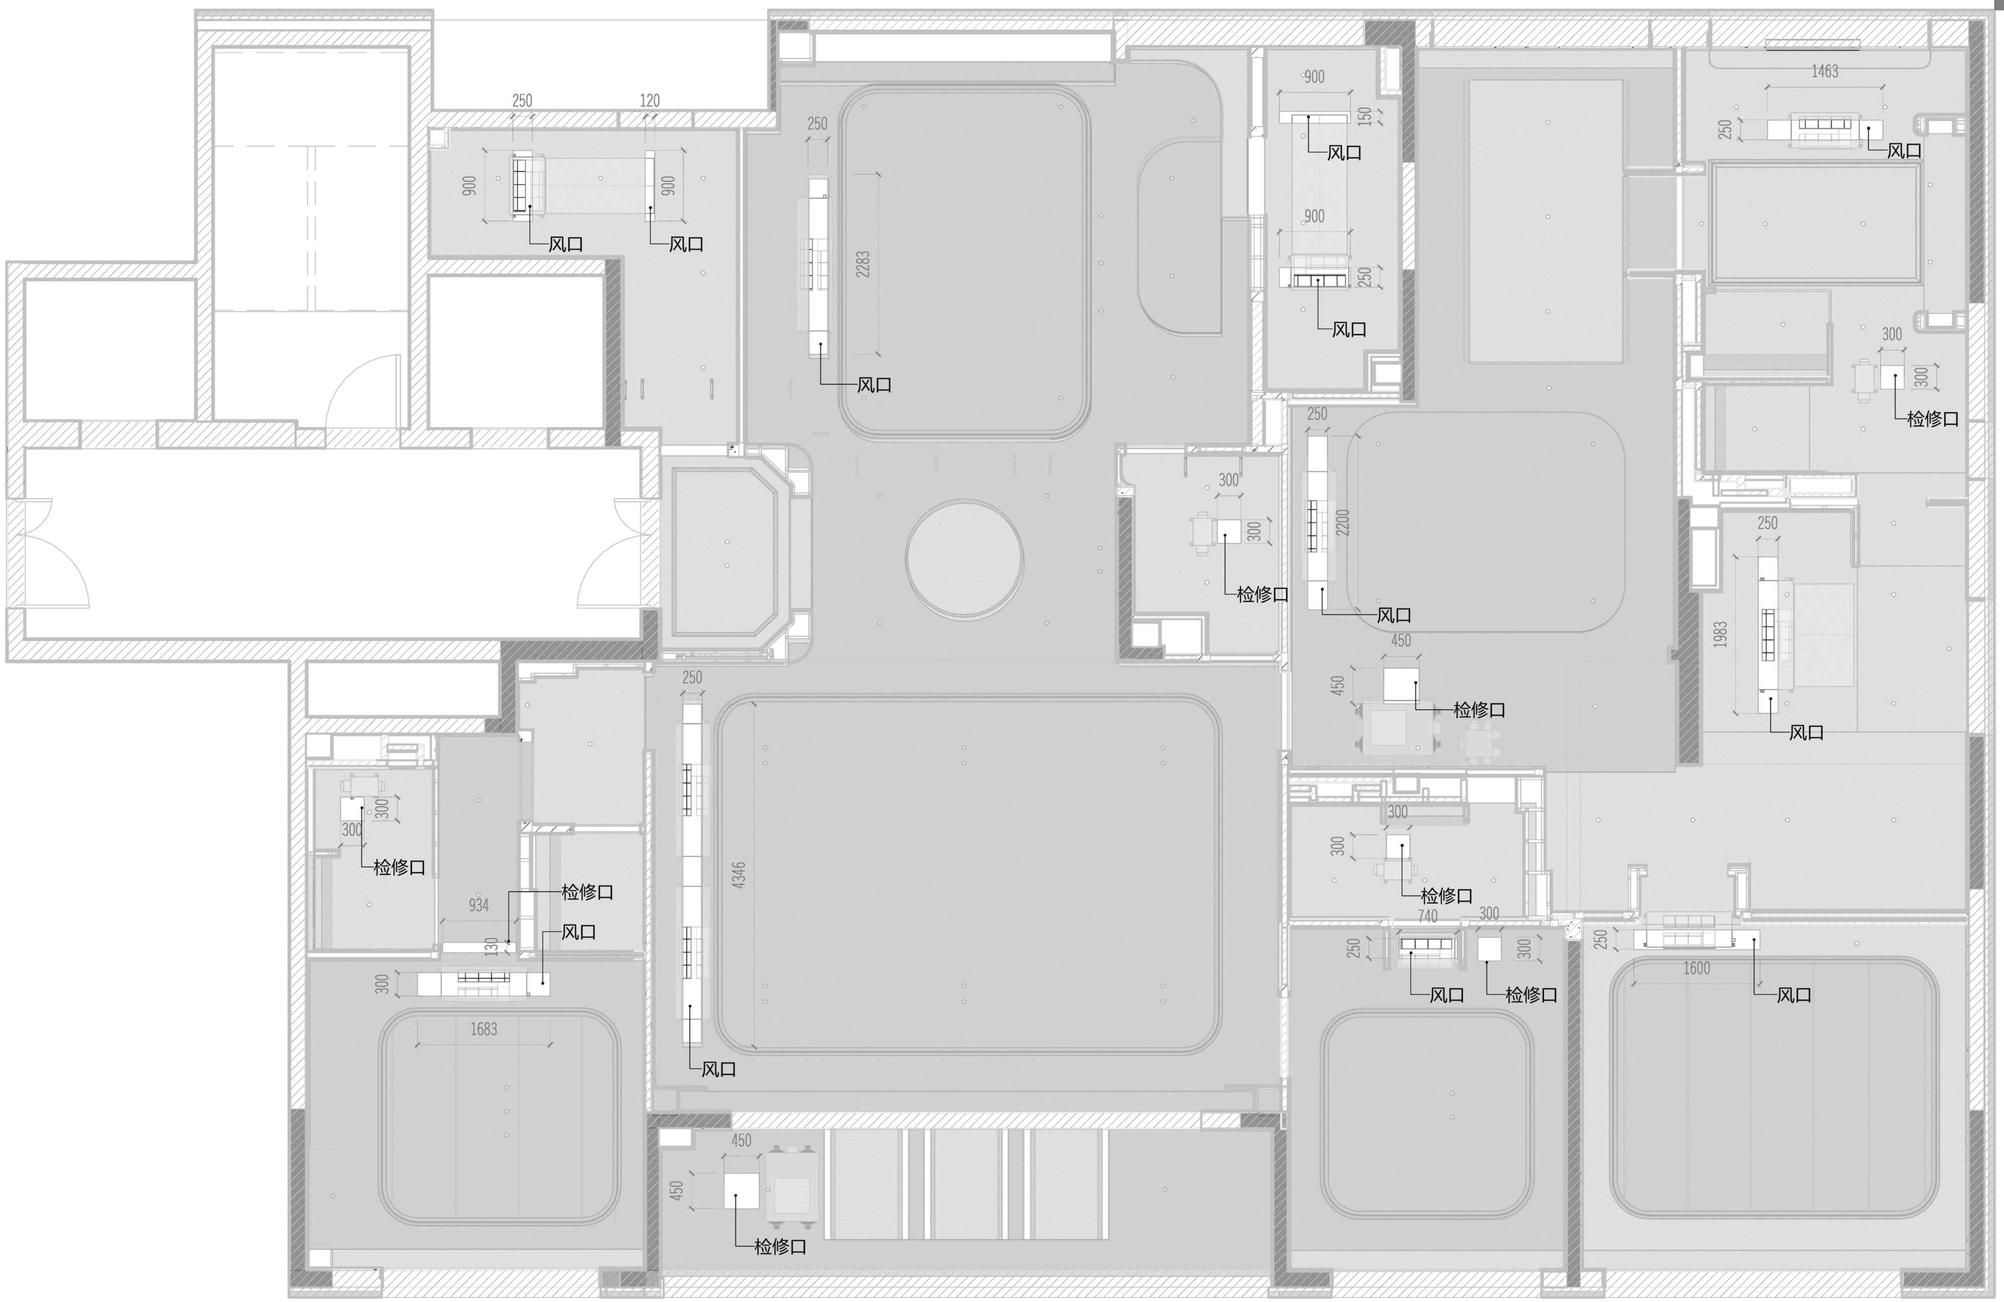

检修口与风口布置图

Scale比例 1:55@A2

1

FIBORN

图例

盖章

注释
Notes

1.本图纸如与现场尺寸有误，请施工人员与项目负责人联系。
2.施工前施工人员应认真查阅此图，如有不明确尺寸，按现场测量为准。
3.本图纸必须经甲乙双方认可并签字方可作为施工依据。

日期
Date 01/20/26

修订
Revision

1

项目
Project

潮映华岸府3-801

比例
Scale 1:55@A2

检修口与风口布置图

图纸编号
Drawing No.

MEP-07

项目编号
Project No.

©2025

冷凝水管坡度
5%

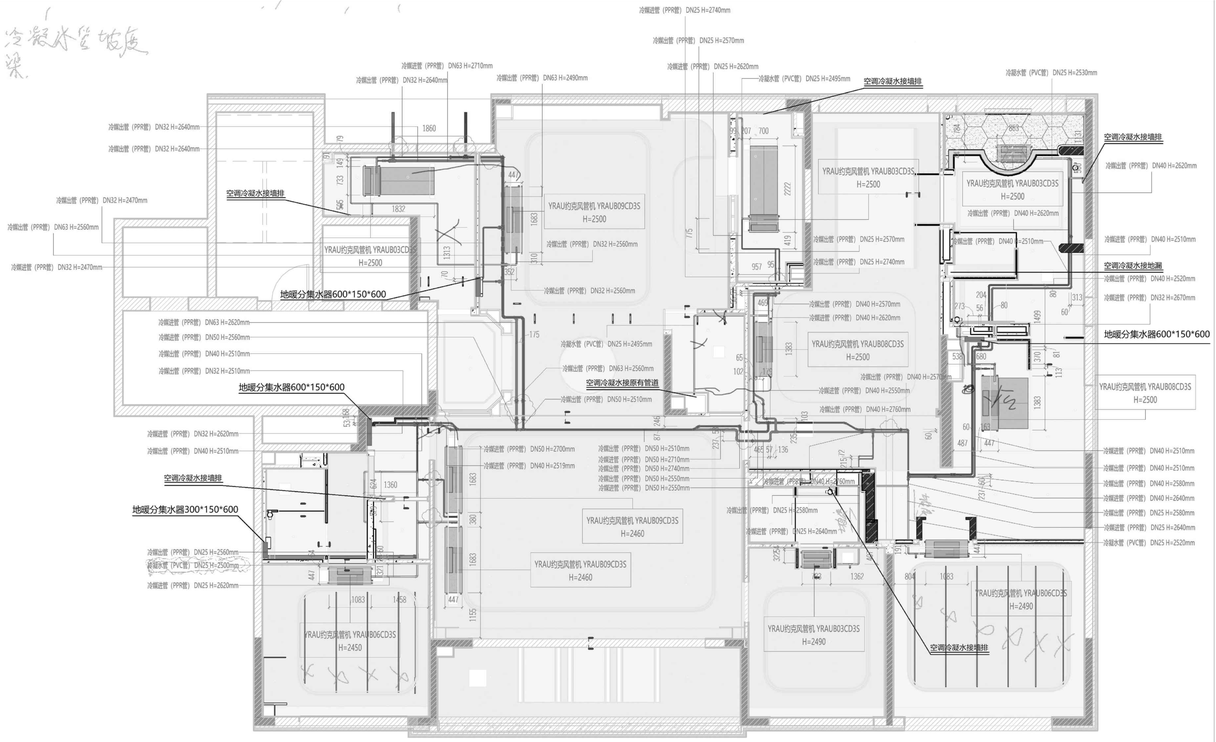

空调平面图

Scale比例 1：55@A2

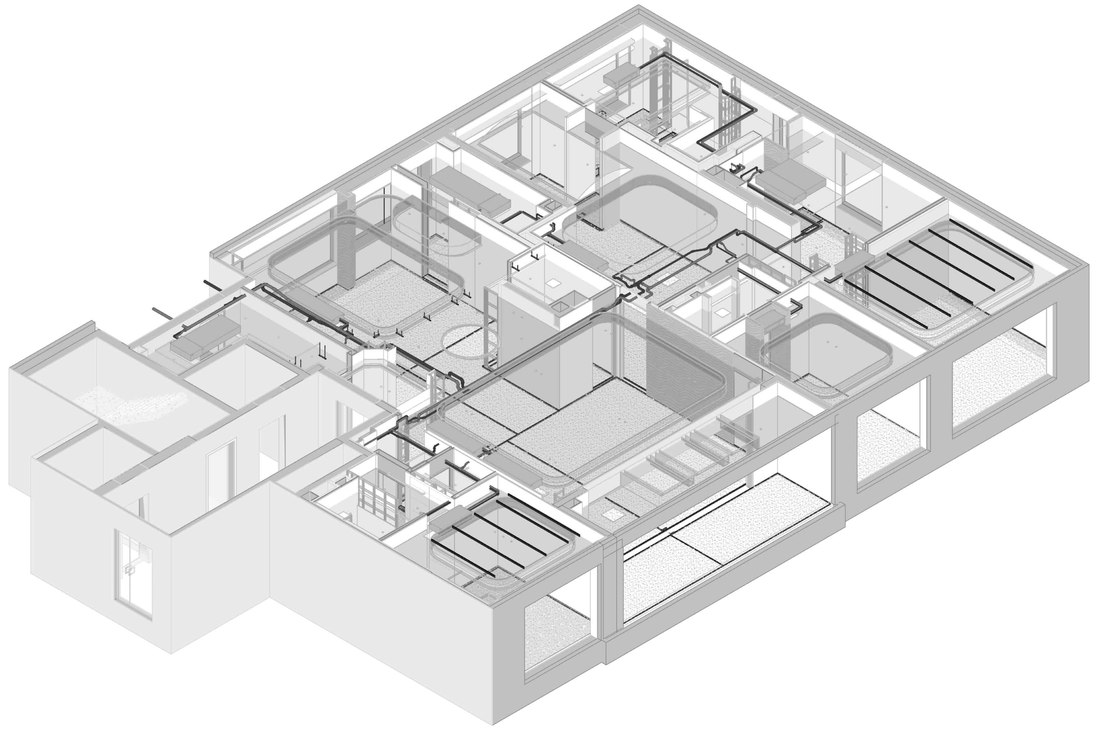

空调三维图

Scale比例 1:55@A2

注释 Notes

1.本图纸如与现场尺寸有误，请施工人员与项目负责人联系。

2.施工前施工人员应认真查阅此图，如有不明确尺寸，按现场测量为准。

3.本图纸必须经甲乙双方认可并签字方可作为施工依据。

LEGEND图例

编号	图例	说明
1		空调
2		冷媒进管
3		冷媒出管
4		冷凝水管
5		室内梁
6		设置发风系统
7		利用原有孔洞

日期 Date 01/20/26

修订 Revision 1

项目 Project

潮映华府府3-801

Scale 比例 1:55@A2

空调布置图

Drawing No. 图纸编号 MEP-08

Project No. 项目编号 ※2026

1	空调平面图	2	空调三维图
空调-01	Scale比例 1：55@A2	空调-02	Scale比例 1:55@A2

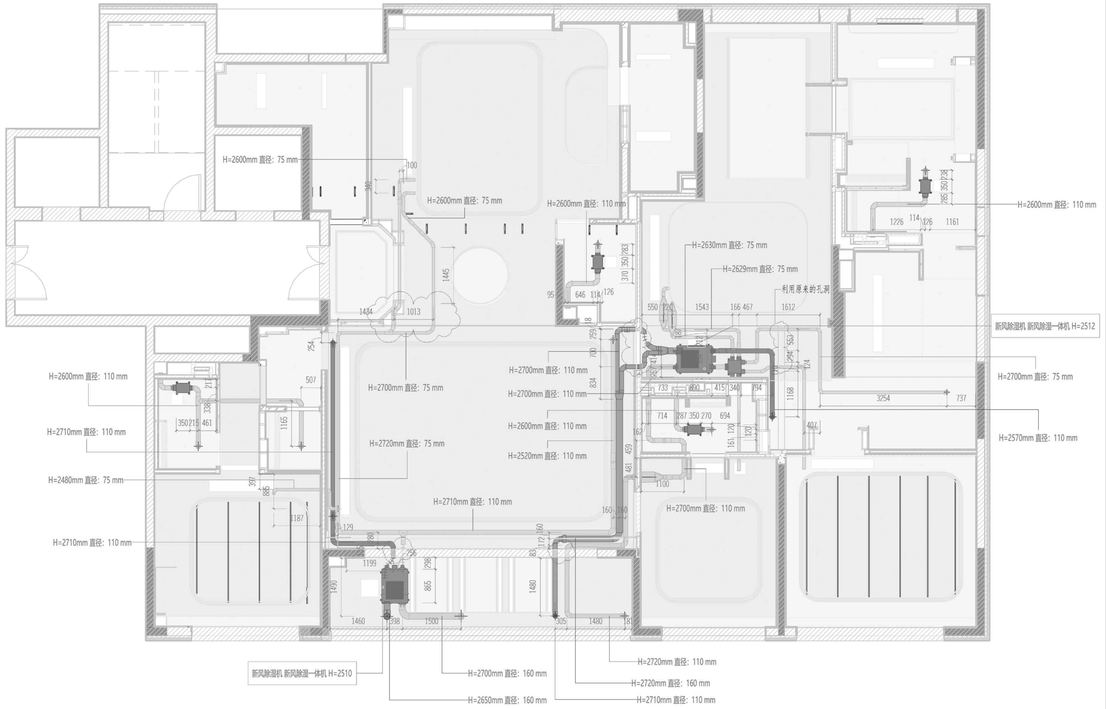

新风平面图

Scale比例 1 : 55@A2

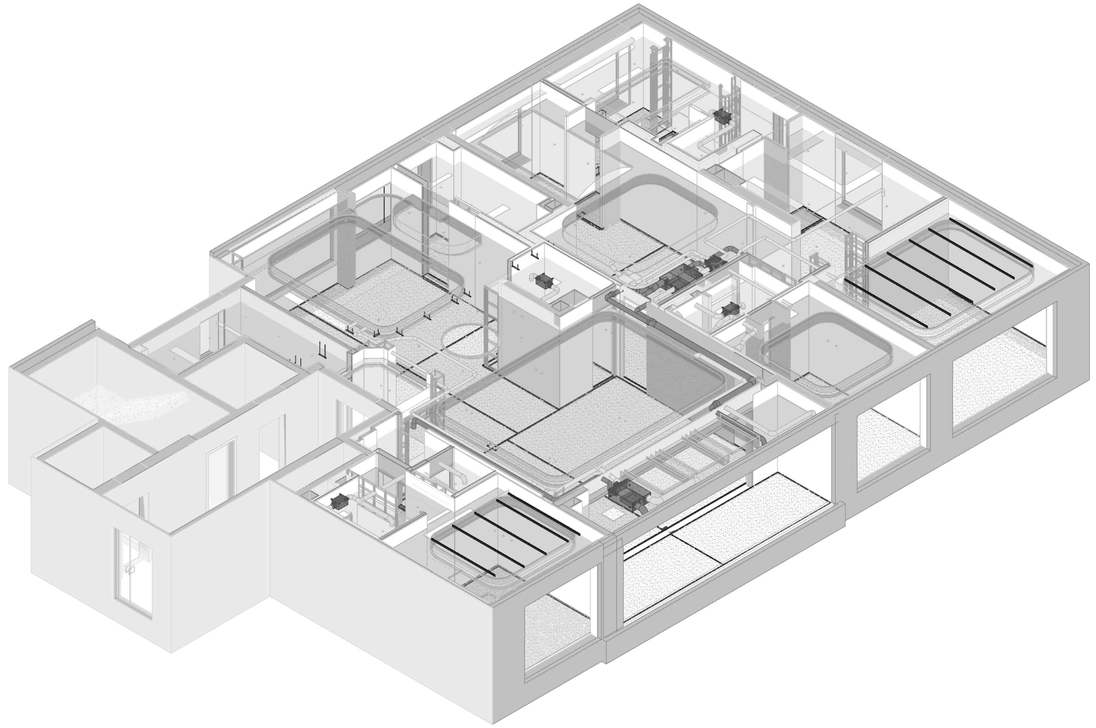

新风三维图

Scale比例 1:55@A2

注释
Notes
1.本图纸如与现场尺寸有误，请施工人员与项目负责人联系。
2.施工前施工人员应认真查阅此图，如有不明确尺寸，按现场测量为准。
3.本图纸必须结甲乙双方认可并签字方可作为施工依据。

LEGEND图例

编号	图例	说明
1		新风机
2		新风出风管
3		新风进风管
4		排风出风管
5		排风进风管
6		室内梁
7		设备支吊系统
8		利用原有孔洞

1• 换气次数：住宅卫生间≥6次/h，厨房卫生间（带淋浴）建议8~10次/h（可通过中高档空调双联）；

2• 风机运行：低速档（约150~200m³/h）常开保险丝，作低速档（300~370m³/h）按需开启（淋浴/加热后），停机超过3~5min（排净潮湿空气）。

3• 负压值：-5~-10Pa（核心标准），指保证厨味不窜室，又避免厂房合过紧、开窗倒灌等客户体验问题，不做检测。

新风过梁器

日期
Date 01/20/26

修订
Revision 1

项目
Project
潮鼓华府府3-801

Scale 1:55@A2
比例

新风布置图

Drawing No.
图纸编号
MEP-09

Project No.
项目编号

©2026

支架01 支架02 支架03 支架04 支架05 支架06 支架07 支架08 支架09 支架10 支架11 支架12

支架13 支架14 支架15 支架16 支架17 支架18 支架19 支架20 支架21 支架22 支架23

支架24 支架25 支架26 支架27 支架28 支架29 支架30 支架31 支架32 支架33 支架34 支架35 支架36 支架37 支架38

LEGEND图例

编号	图例	说明
1		水电支吊架
2		综合支吊架

1		水电支吊架布置平面图	2
支吊架-01		Scale比例 1：55@A2	支吊架-02

水电支吊架大样图A

Scale比例 1:8@A2

Notes
1.本图纸如与现场尺寸有误，请施工人员与总包负责人联系。
2.施工前施工人员认真查阅此图，如有不明确尺寸，按照详细施为准。
3.本图纸以综合净空之部分以可供参考不作为施工依据。

Date 01/09/26

Project
圆映华府府3-801

Scale 比例 1:8@A2

水电支吊架布置图A

Drawing No. 图纸编号 MEP-10A

Project No. 项目编号 e-2026

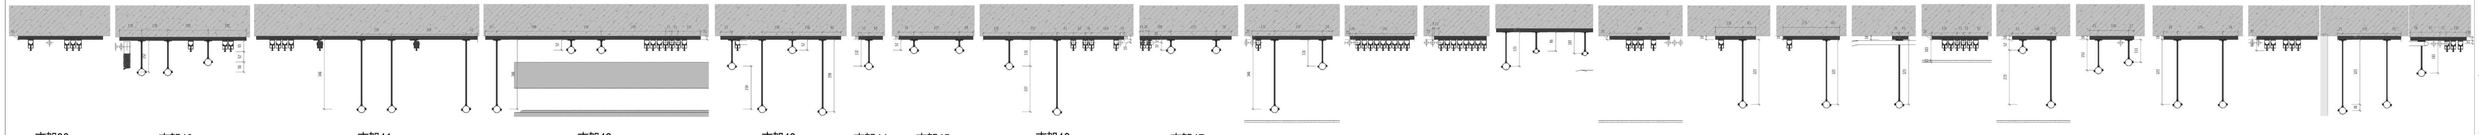

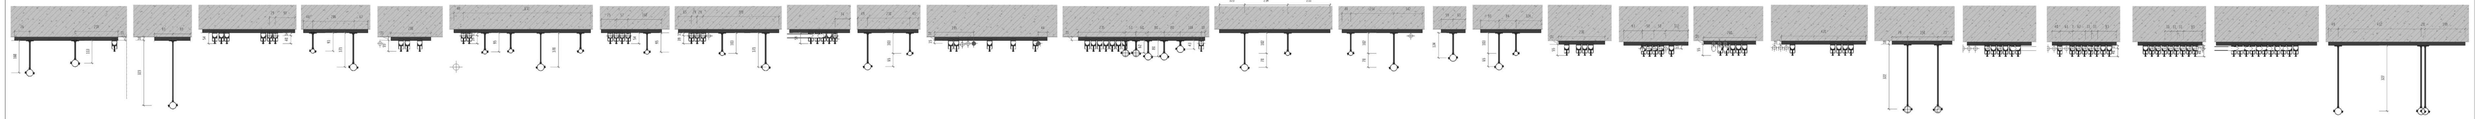

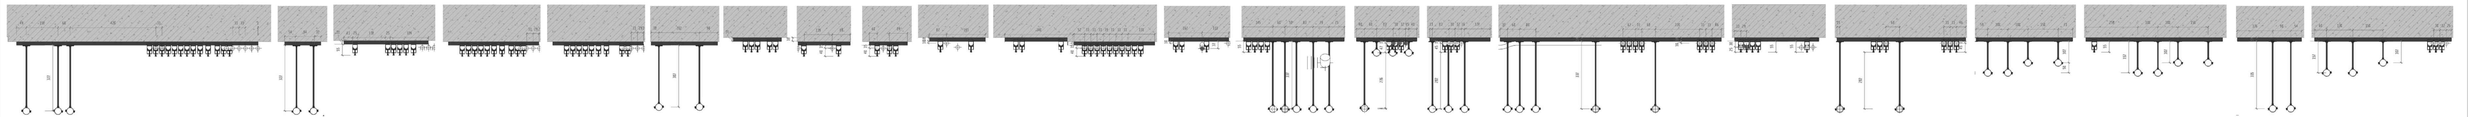

悦孚 Yue Fu China

上海服务中心
徐汇区湖南路20弄14号

日期 Date 01/09/26
修订 Revision
项目 Project 国铁华翠路3-801
比例 Scale 1:8@A2
图纸名称 水电支吊架布置图8
图纸编号 Drawing No. MEP-108
项目编号 Project No. 9025

1	水电支吊架大样图8	说明 Notes 1.本图纸如与图纸尺寸存矛盾，请施工人员与总图负责人联系。 2.施工前施工人员应认真阅读图纸，如有不明确尺寸，按图纸明确为准。 3.本图纸以总体参考之图为以可供参考为准为施工依据。
支吊架-03	Scale比例 1:8@A2	

灯具图例 灯带轮廓

灯具编号

备注

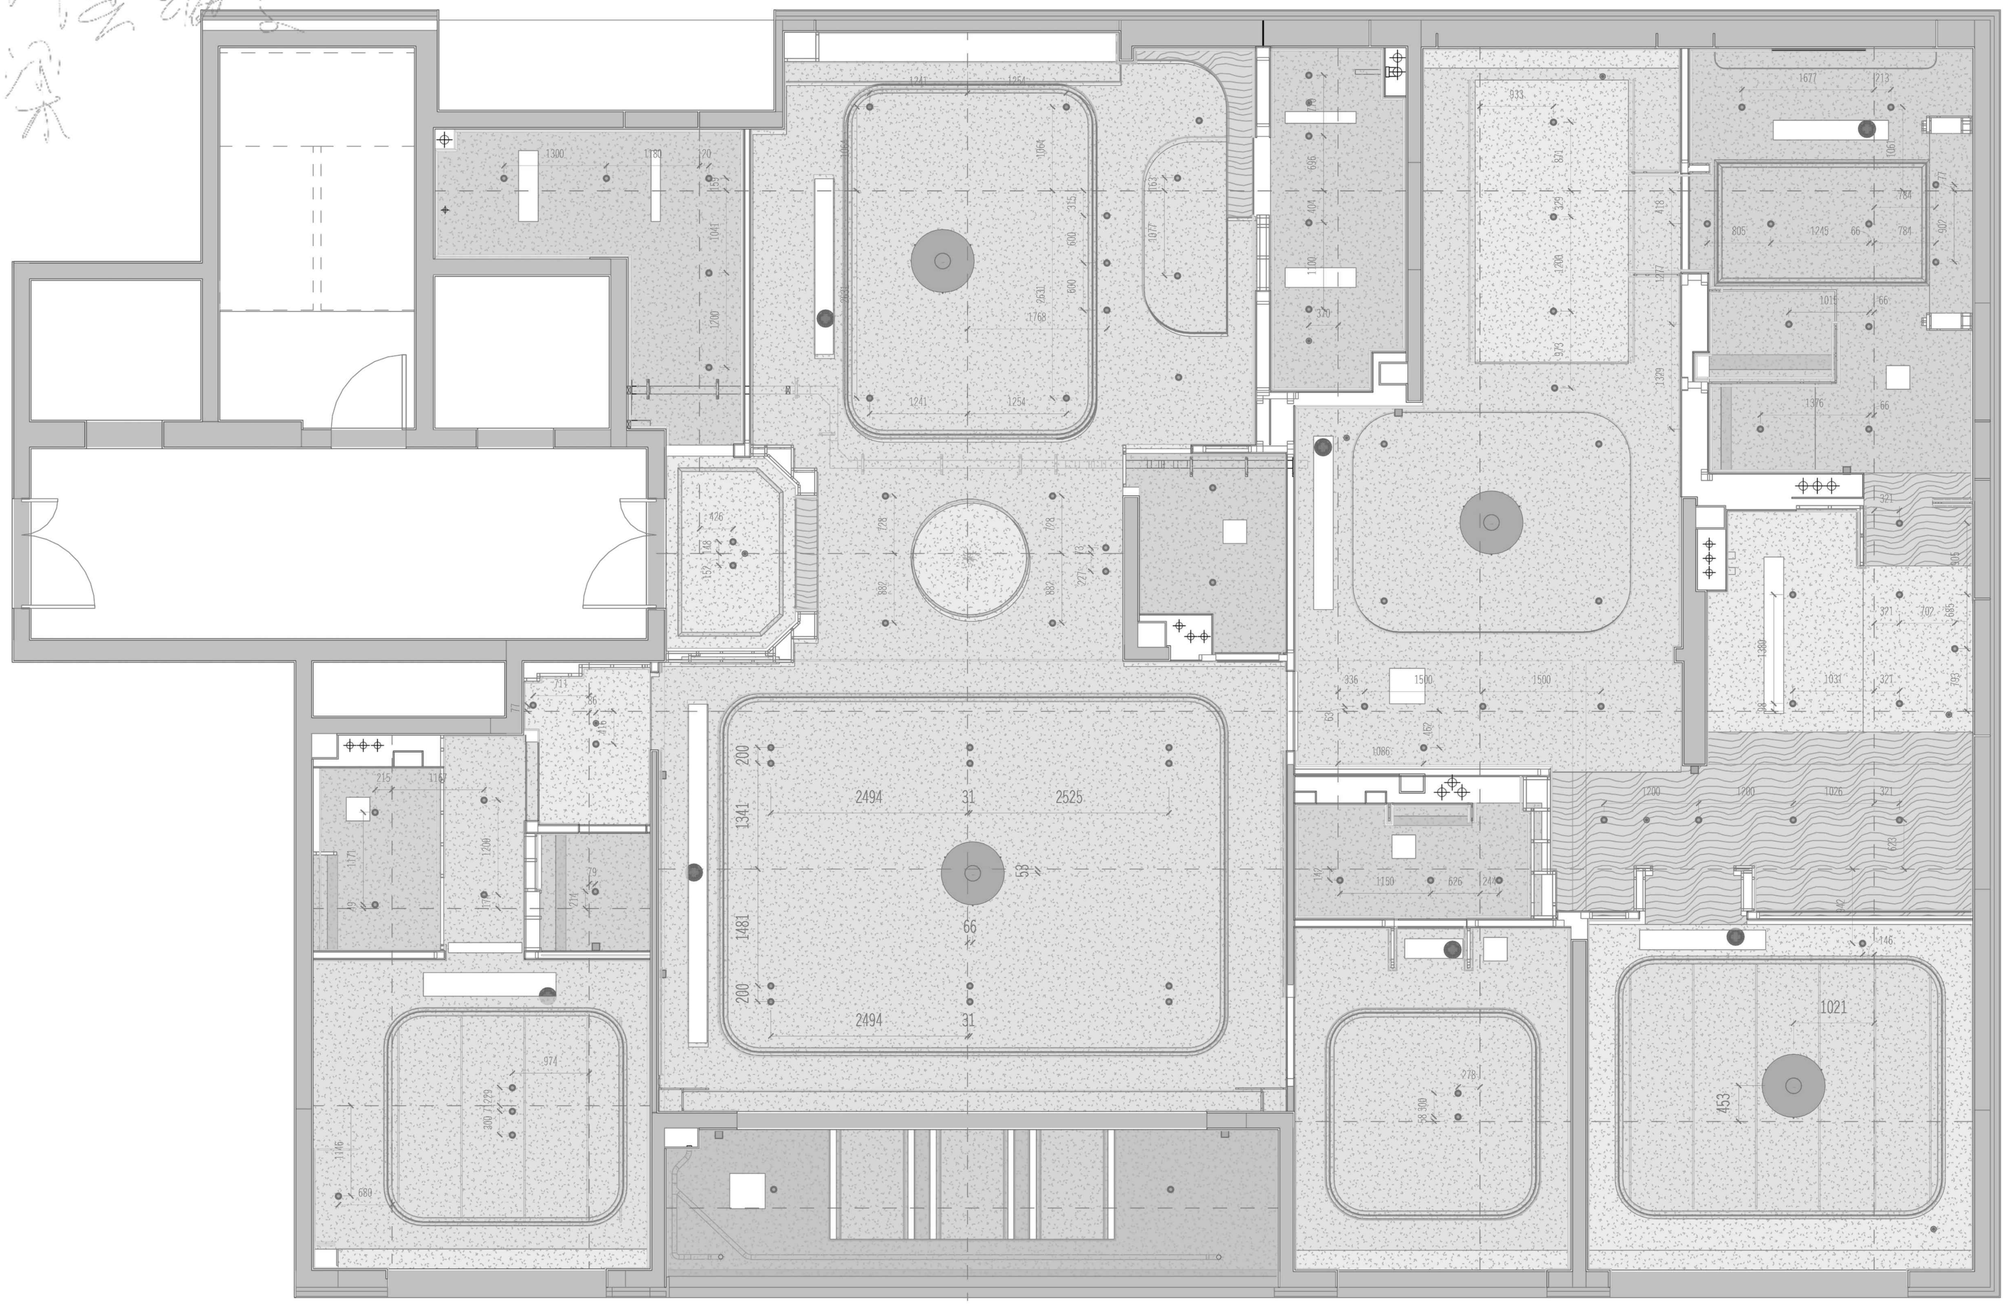

灯具定位图

Scale比例 1:55@A2

1

EIBORN

LEGEND图例

编号	图例	说明
1		9.5mm纸面石膏板
2		9.5mm防潮石膏板

灯具图例

盖章

注释
Notes

1.本图纸如与现场尺寸有误，请施工人员与项目负责人联系。
2.施工前施工人员应认真查阅此图，如有不明确尺寸，按现场测量为准。
3.本图纸必须经甲乙双方认可并签字方可作为施工依据。

日期
Date 01/24/26

修订
Revision

1

项目
Project

潮映华岸府3-801

比例
Scale 1:55@A2

灯具定位图

图纸编号
Drawing No.

MEP-11

项目编号
Project No.

©2025

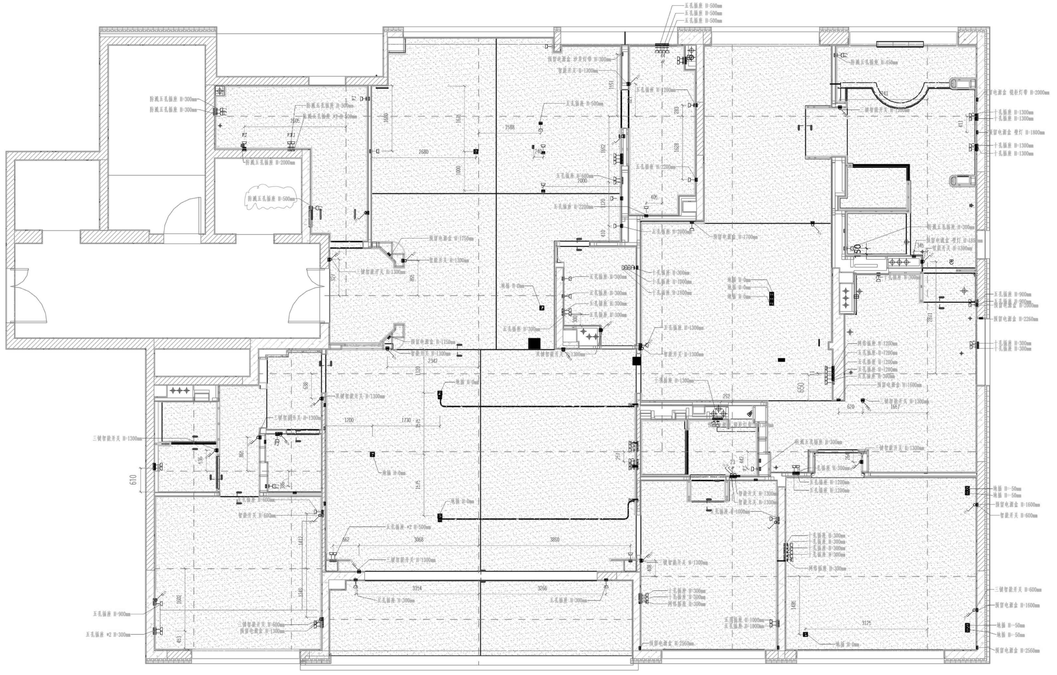

1

点位-01

点位平面图

Scale比例 1：55@A2

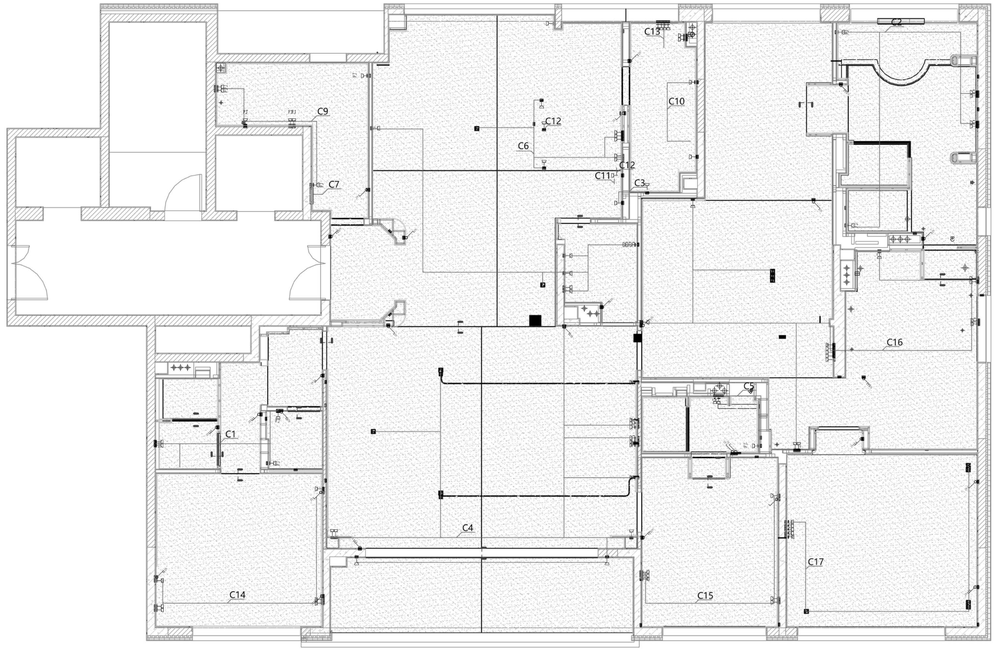

2

插座-02

插座分组平面图

Scale比例 1:55@A2

注释
Notes
1.本图纸如与现场尺寸有误，请施工人员与项目负责人联系。
2.施工前施工人员应认真查阅此图，如有不明确尺寸，按现场测量为准。
3.本图纸必须结甲乙双方认可并签字方可作为施工依据。

LEGEND图例

编号	图例	说明
1	~6	通用五孔插座
2	~6c	防溅五孔插座
3	~6	通用十孔插座
4	~6	网线插座
5	~6	单控双联开关
6		智能开关
7		双键智能开关
8		三键智能开关

日期
Date 01/24/26

修订
Revision

项目
Project

潮映华府府3-801

Scale 1:55@A2
比例

点位布置图

Drawing No.
图纸编号
MEP-12

Project No. ©2026
支吊架-02

1

桥架-01

桥架布置平面图

Scale比例 1 : 55@A2

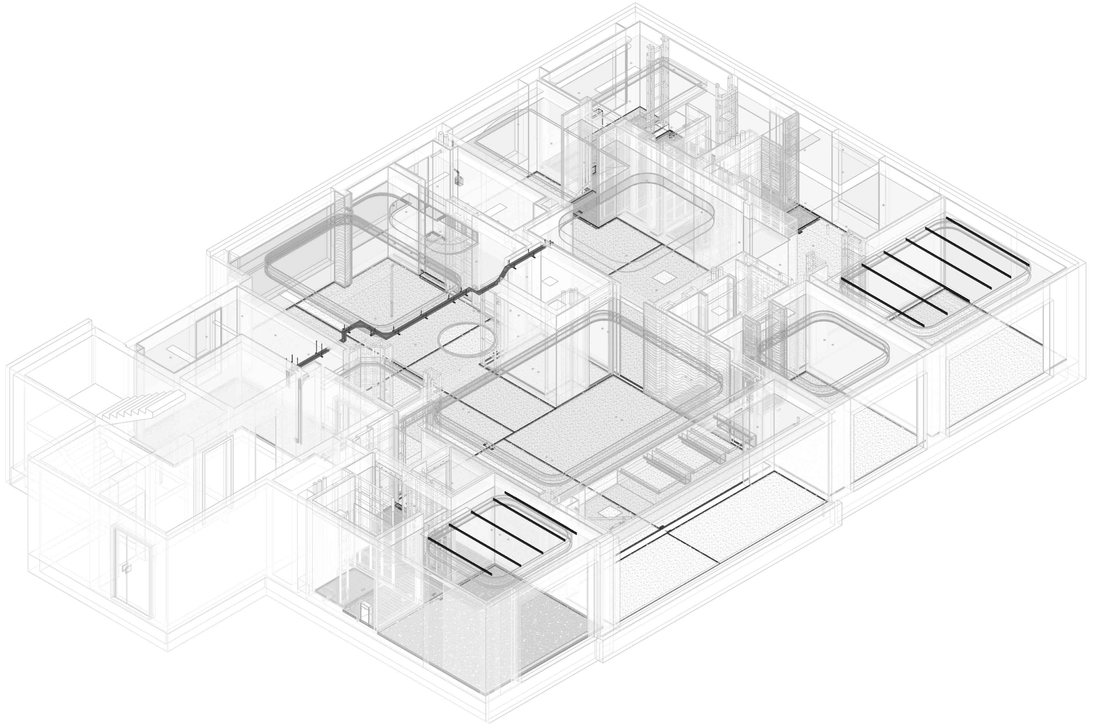

2

桥架-02

桥架布置三维图

Scale比例 1:55@A2

注释
Notes
1.本图纸如与现场尺寸有误，请施工人员与项目负责人联系。
2.施工前施工人员应认真查阅此图，如有不明确尺寸，按现场测量为准。
3.本图纸必须经甲乙双方认可并签字方可作为施工依据。

LEGEND图例

编号	图例	说明
1		桥架

下方钢架做桥架支撑

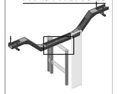

桥架跨梁节点

日期
Date
01/20/26

修订
Revision

项目
Project
澜映华府府3-801

Scale
比例
1:55@A2

桥架布置图

Drawing No.
图纸编号
MEP-13

Project No.
项目编号
#2026

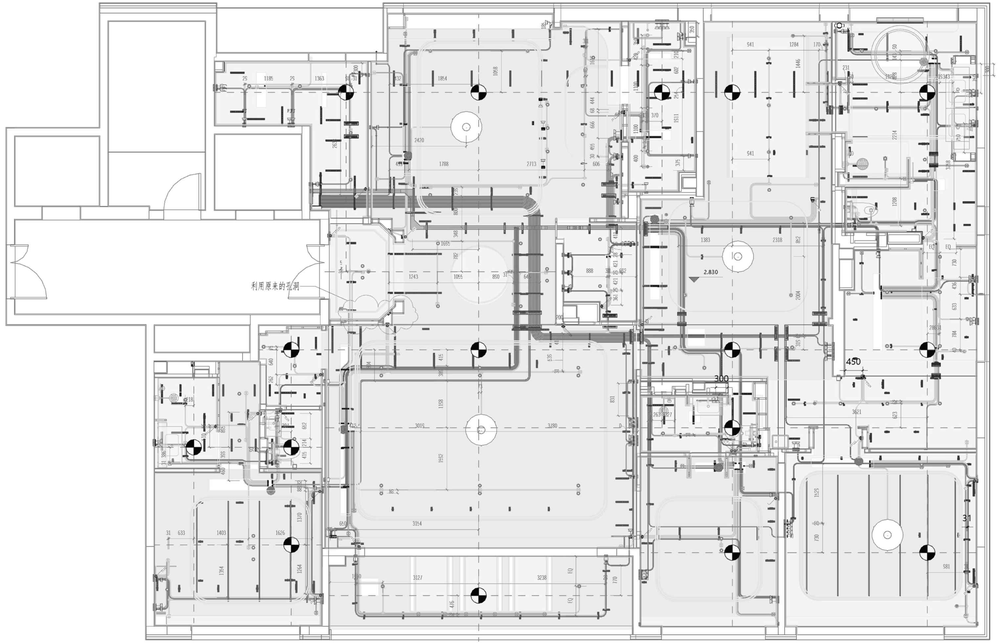

1

电路-01

天花板电路布设平面图

Scale比例 1：55@A2

2

电路-02

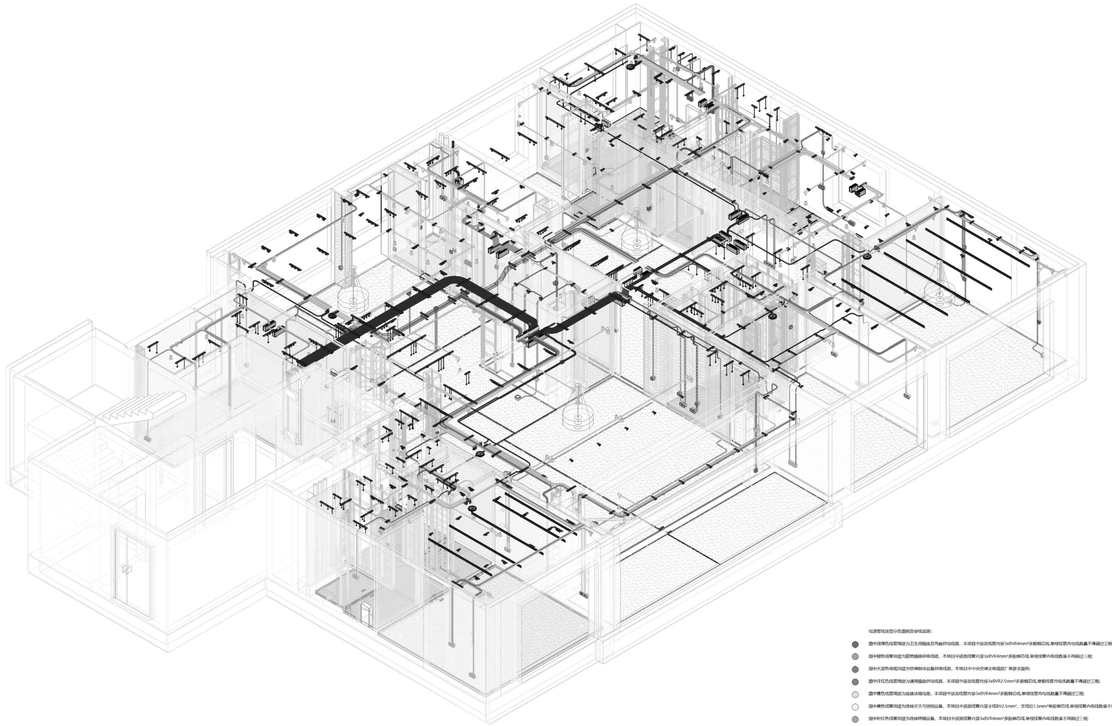

电路管线及型号选择符合规范要求：

- 图中实线表示暗埋敷设于墙体或顶板内的线路，主要用于设备间至各功能区域的主干电缆及水平桥架走线，确保线路隐蔽、安全并减少外露。
- 图中虚线表示沿墙面或顶板明装敷设的线路，主要用于临时用电、检修维护或后期增设的线路，便于拆卸与更换。
- 图中点划线表示预留管线，主要用于未来扩容或设备升级时的穿线通道，预留一定数量的备用回路，避免重复开槽施工。
- 图中带箭头的线路表示线缆走向，箭头指向配电箱、弱电间或设备机房，用于明确线缆的敷设方向和终端位置。
- 图中标注的数字表示线缆根数或回路编号，例如“3”表示该段线路内有3根线缆，“WL1”表示照明回路1，“PC2”表示插座回路2，便于施工时区分不同回路。
- 图中标注的字母表示线缆型号，例如“BV”表示铜芯聚氯乙烯绝缘线，“RVV”表示铜芯聚氯乙烯绝缘护套软线，“ZR”表示阻燃型，“NH”表示耐火型，根据不同场所的防火等级要求选用。
- 图中标注的“SC”表示钢管敷设，“PC”表示阻燃塑料管敷设，“CT”表示桥架敷设，“MR”表示金属线槽敷设，根据不同环境和安装要求选择合适的管线保护方式。

电气三维图

Scale比例 1:55@A2

注释
Notes

1.本图纸如与现场尺寸有误，请施工人员与项目负责人联系。

2.施工前施工人员应认真查阅此图，如有不明确尺寸，按现场测量为准。

3.本图纸必须结甲乙双方认可并签字方可作为施工依据。

LEGEND图例

编号	图例	说明
1		分线盒
2		桥架
3		水电支吊系统

日期
Date
01/24/26

修订
Revision
1

项目
Project
潮映华府府3-801

Scale
比例
1:55@A2

电路布置图

Drawing No.
图纸编号
MEP-14

Project No.
项目编号
©2026

AL1

配电箱

由室外电井引来

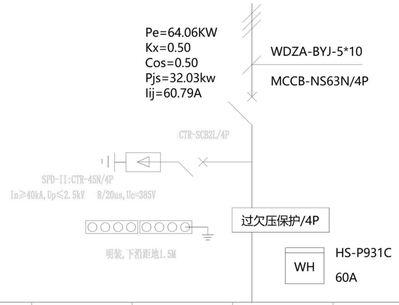

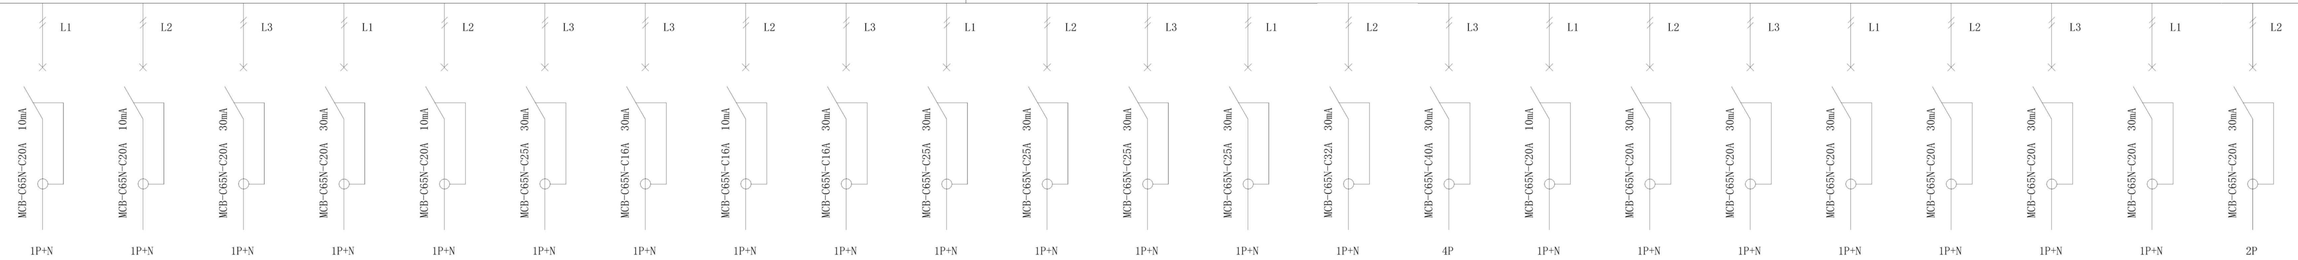

名称	C1	C2	C3	C4	C5	C6	Z2	Z1	C7	C8	C9	C10	C11	C12	k1	C13	k2	C14	C15	C16	D1	C17	b1
用途	公卫、客卫 -插座	主卫 -插座	冰箱x2 -插座	客餐厅、阳台 宠物间—插座	次卫 -插座	西厨其他 -插座	客餐厅.阳台.中厨 家政间.宠物间照明	次卫.主卧.书房 衣帽间.主卫-照明	弱电箱 -插座	中厨1 -插座	家政间 -插座	烤箱 -插座	蒸箱 -插座	岛台.烟灶一体机 -插座	空调外机 -电源	中厨2 -插座	所有空调内机 -电源	客卧 -插座	次卧 -插座	书房.衣帽间 -插座	新风机 -电源	主卧 -插座	备用
线型、配管	WDZB-BYJ- 3*2.5 Φ20PVC	WDZB-BYJ- 3*2.5 Φ20PVC	WDZB-BYJ- 3*2.5 Φ20PVC	WDZB-BYJ- 3*2.5 Φ20PVC	WDZB-BYJ- 3*2.5 Φ20PVC	WDZB-BYJ- 3*4 Φ20PVC	WDZB-BYJ- 3*2.5 Φ20PVC	WDZB-BYJ- 3*2.5 Φ20PVC	WDZB-BYJ- 3*2.5 Φ20PVC	WDZB-BYJ- 3*4 Φ20PVC	WDZB-BYJ- 3*4 Φ20PVC	WDZB-BYJ- 3*4 Φ20PVC	WDZB-BYJ- 3*4 Φ20PVC	WDZB-BYJ- 3*6 Φ20PVC	WDZB-BYJ- 5*6 Φ32PVC	WDZB-BYJ- 3*2.5 Φ20PVC	WDZB-BYJ- 3*2.5 Φ20PVC	WDZB-BYJ- 3*2.5 Φ20PVC	WDZB-BYJ- 3*2.5 Φ20PVC	WDZB-BYJ- 3*2.5 Φ20PVC	WDZB-BYJ- 3*2.5 Φ20PVC	WDZB-BYJ- 3*2.5 Φ20PVC	
敷设方式	WC CC	WC CC	WC CC	FC WC CC	WC CC	WC CC	WC CC	WC CC	WC CC	WC CC	WC CC	WC CC	WC CC	WC CC	WC CC	WC CC	WC CC	FC WC CC	FC WC CC	FC WC CC	WC CC	FC WC CC	
功率	3.5KW	3.5KW	3.5KW	3KW	3KW	3KW	1.5KW	1.5KW	1KW	4KW	4KW	3.2KW	3.2KW	8KW	10.06KW	3KW	1.0KW	2KW	2.5KW	2.5KW	0.5KW	2.5KW	

1

系统-01

注释
Notes
1.本图纸如与现场尺寸有误，请施工人员与项目负责人联系。
2.施工前施工人员应认真查阅此图，如有不明确尺寸，按现场测量为准。
3.本图纸必须经甲乙双方认可并签字方可作为施工依据。

日期 Date 01/21/26
修订 Revision
项目 Project
潮映华岸府3-801
Scale 比例
电气系统图
Drawing No. 图纸编号
MEP-15
Project No. 项目编号
©2025

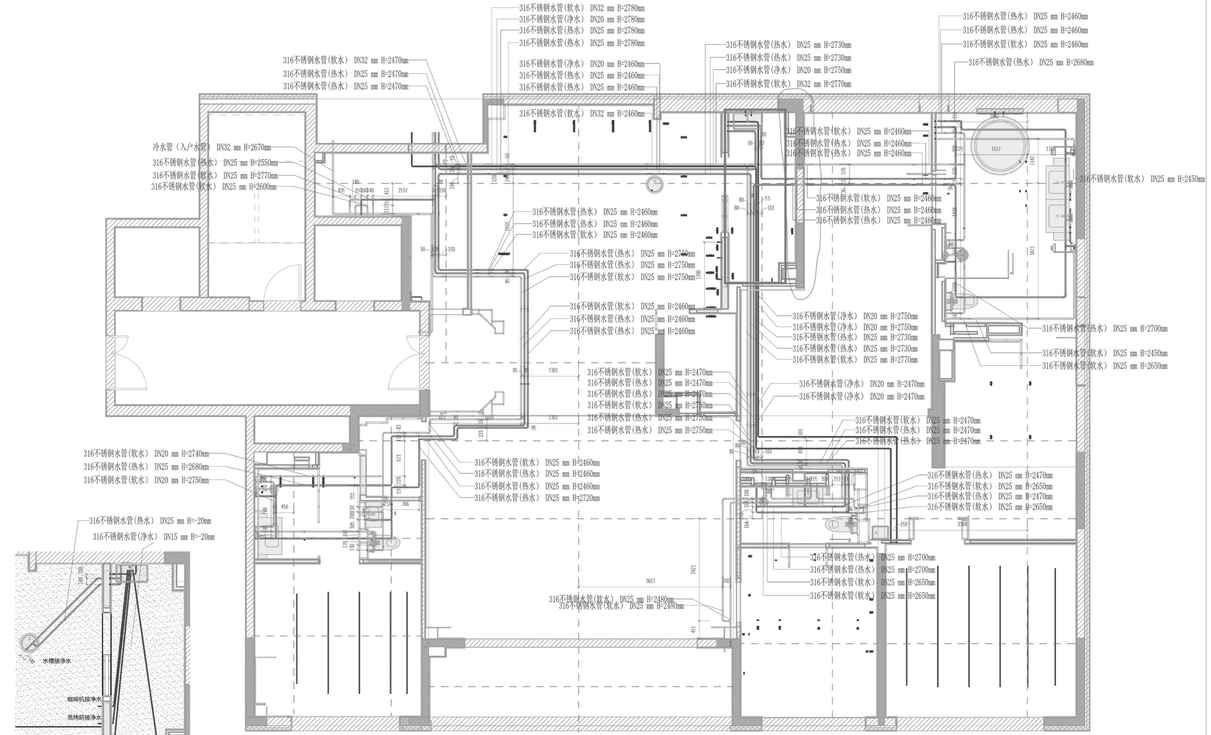
316不锈钢水管(软水) DN32 mm H=2780mm
316不锈钢水管(净水) DN20 mm H=2780mm
316不锈钢水管(热水) DN25 mm H=2780mm
316不锈钢水管(热水) DN25 mm H=2780mm
316不锈钢水管(软水) DN32 mm H=2470mm
316不锈钢水管(热水) DN25 mm H=2470mm
316不锈钢水管(热水) DN25 mm H=2470mm
316不锈钢水管(净水) DN20 mm H=2460mm
316不锈钢水管(热水) DN25 mm H=2460mm
316不锈钢水管(热水) DN25 mm H=2460mm
316不锈钢水管(软水) DN32 mm H=2460mm
316不锈钢水管(热水) DN25 mm H=2730mm
316不锈钢水管(热水) DN25 mm H=2730mm
316不锈钢水管(净水) DN20 mm H=2730mm
316不锈钢水管(软水) DN32 mm H=2770mm
316不锈钢水管(热水) DN25 mm H=2690mm
316不锈钢水管(热水) DN25 mm H=2460mm
316不锈钢水管(热水) DN25 mm H=2460mm
316不锈钢水管(软水) DN25 mm H=2460mm
316不锈钢水管(热水) DN25 mm H=2460mm
316不锈钢水管(热水) DN25 mm H=2460mm
316不锈钢水管(软水) DN25 mm H=2450mm
冷水管（入户水管） DN32 mm H=2670mm
316不锈钢水管(热水) DN25 mm H=2550mm
316不锈钢水管(软水) DN25 mm H=2770mm
316不锈钢水管(软水) DN25 mm H=2600mm
316不锈钢水管(热水) DN25 mm H=2460mm
316不锈钢水管(热水) DN25 mm H=2460mm
316不锈钢水管(软水) DN25 mm H=2460

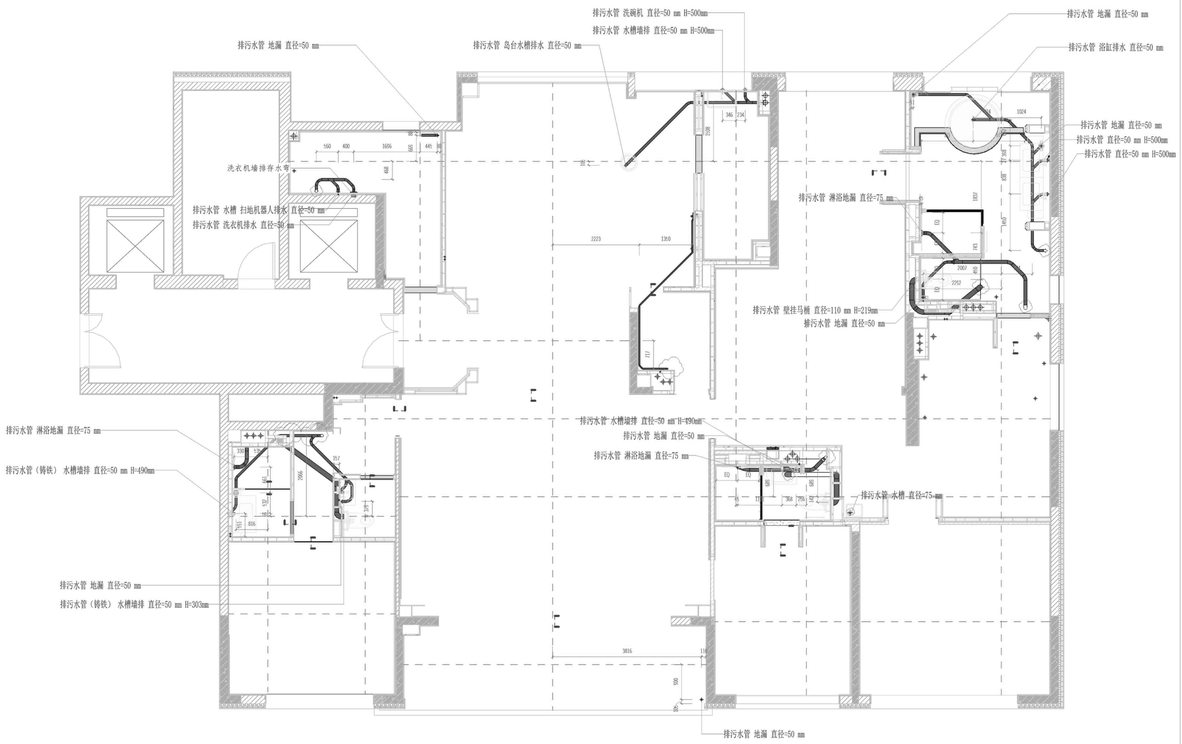

1

排水-01

排水平面图

Scale比例 1 : 55@A2

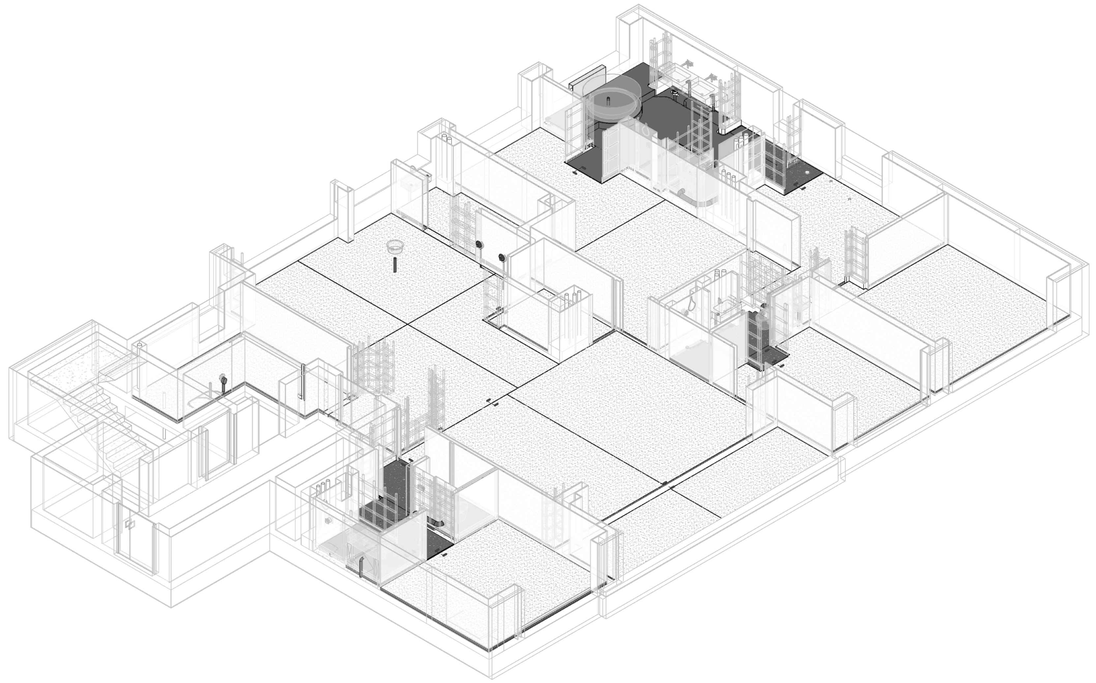

2

排水-02

排水三维图

Scale比例 1:55@A2

注释
Notes
1.本图纸如与现场尺寸有误，请施工人员与项目负责人联系。
2.施工前施工人员应认真查阅此图，如有不明确尺寸，按现场测量为准。
3.本图纸必须经甲乙双方认可并签字方可作为施工依据。

LEGEND图例

编号	图例	说明
1		排水管道
2		洁具
3		利用原来的管道

日期
Date 01/20/26

修订
Revision
1

项目
Project
潮映华府府3-801

Scale 1:55@A2
比例

排水布置图

Drawing No.
图纸编号
MEP-17

Project No. ©2026
项目编号

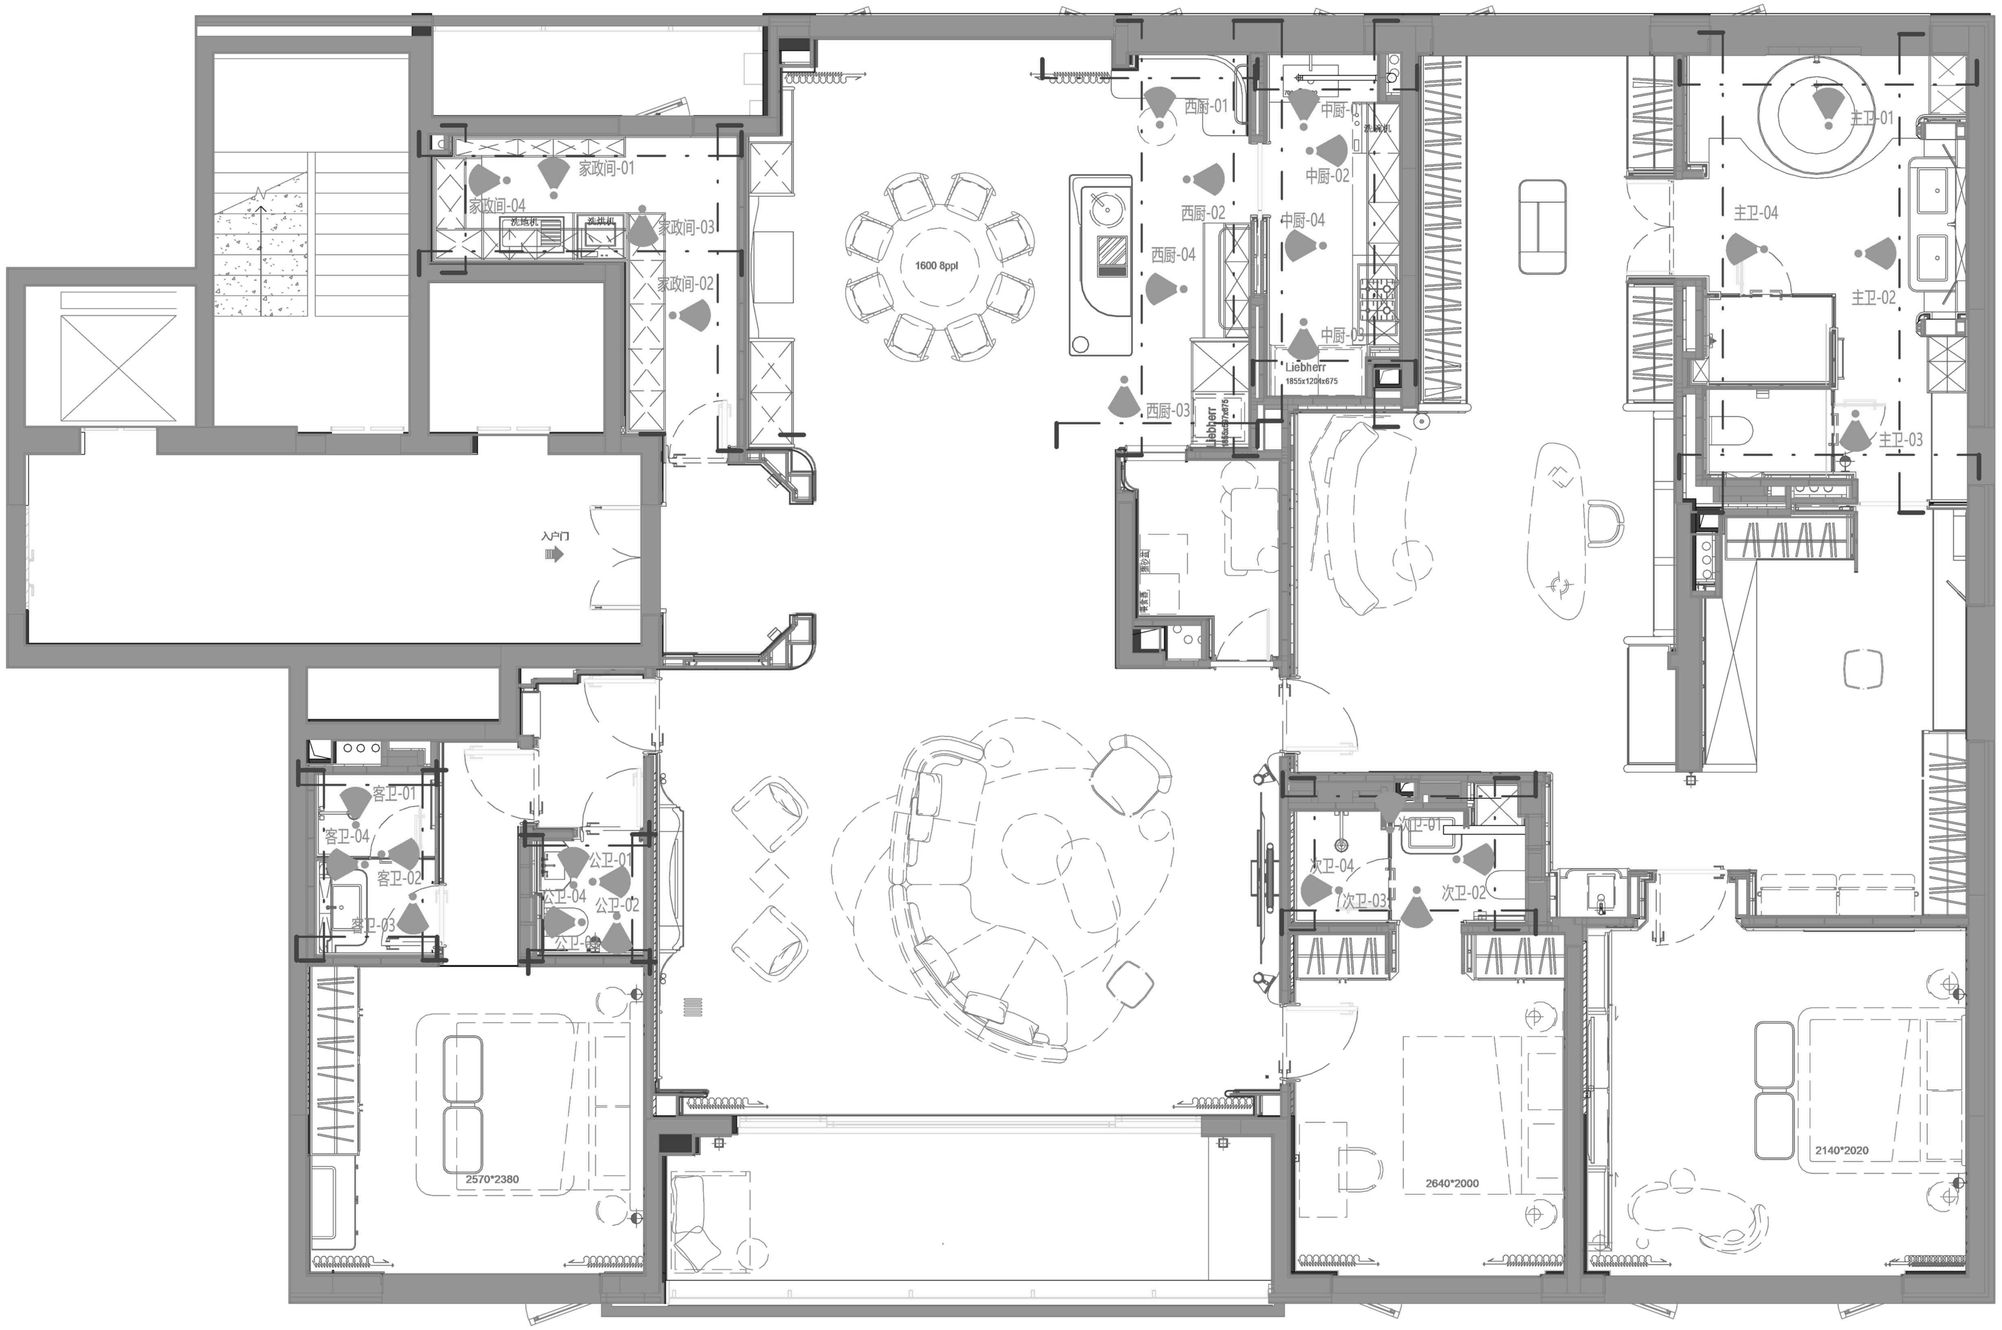

1

水电立面索引图

Scale比例 1:55@A2

FIBORN

盖章

注释
Notes

1.本图纸如与现场尺寸有误，请施工人员与项目负责人联系。
2.施工前施工人员应认真查阅此图，如有不明确尺寸，按现场测量为准。
3.本图纸必须经甲乙双方认可并签字方可作为施工依据。

日期
Date 01/20/26

修订
Revision

1

项目
Project

潮映华岸府3-801

比例
Scale 1:55@A2

水电立面索引图

图纸编号
Drawing No.

MEP-18

项目编号
Project No.

©2025

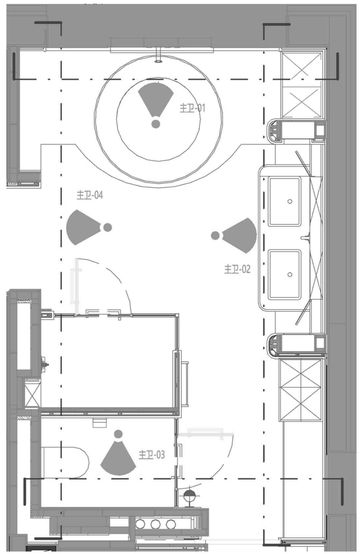

1 主卫水电索引图

平面 Scale比例 1 : 30@A2

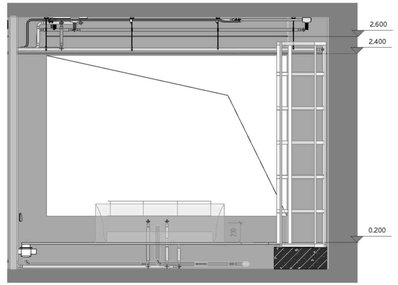

主卫-01

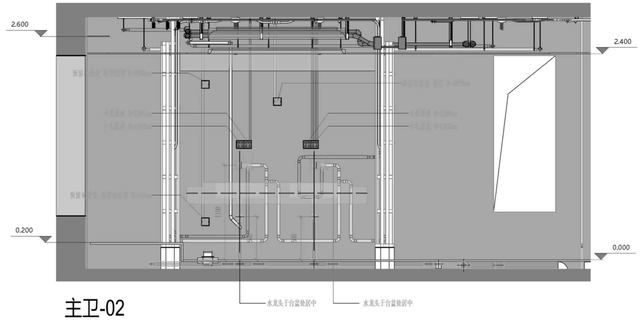

主卫-02

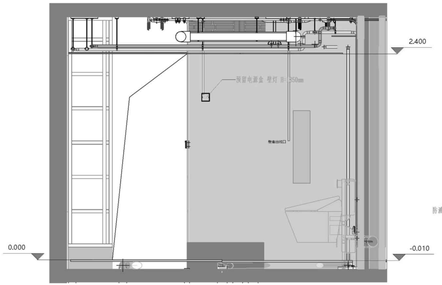

主卫-03

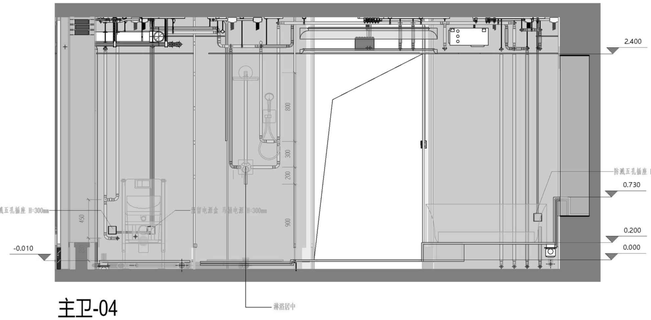

主卫-04

2 主卫水电立面图

立面 Scale比例 1 : 30@A2

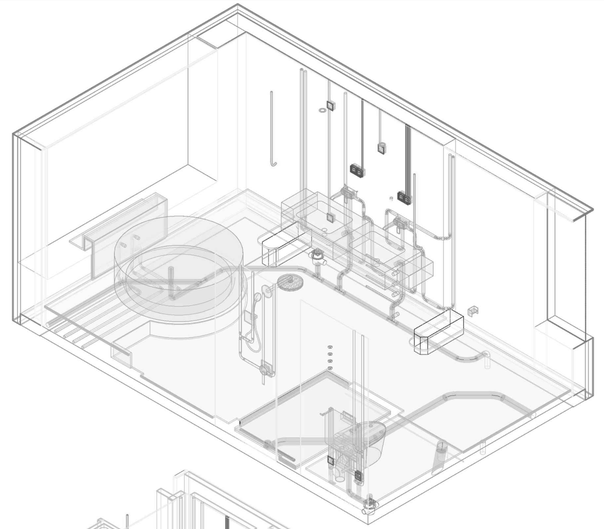

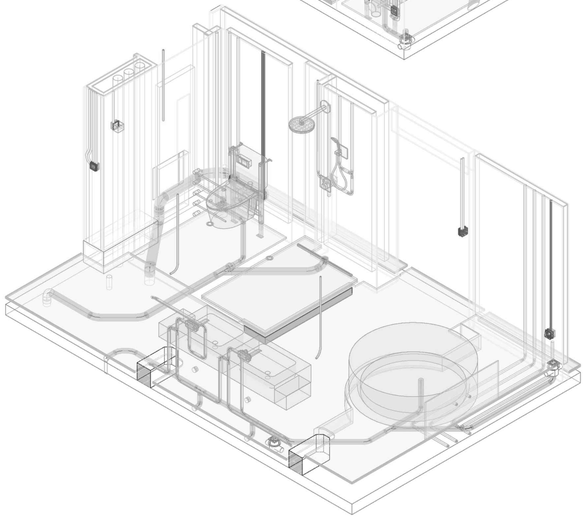

3 主卫水电三维图

三维 Scale比例 1 : 30@A2

LEGEND图例

编号	图例	说明
1		强电
2		弱电
3		给水
4		排水
5		排水(原有)
6		冷媒进管
7		冷媒出管
8		冷凝水管

盖章

注释
Notes
1.本图纸标注为现场尺寸有误，施工人员与项目负责人联系。
2.施工前施工人员需认真查阅此图，切勿不明确尺寸，按现场测量为准。
3.本图纸由德印茗艺设计以开始字方引导为施工依据。

日期
Date 01/20/26

修订
Revision
1

项目
Project
潮映华岸府3-801

比例
Scale 1:30@A2

主卫

图纸编号
Drawing No.
MEP-19

项目编号
Project No.

©2025

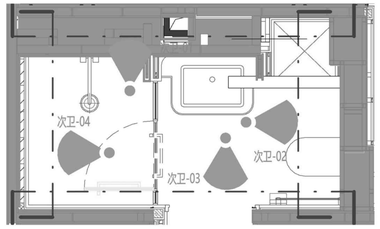

1	次卫水电索引图
平面	Scale比例 1 : 30@A2

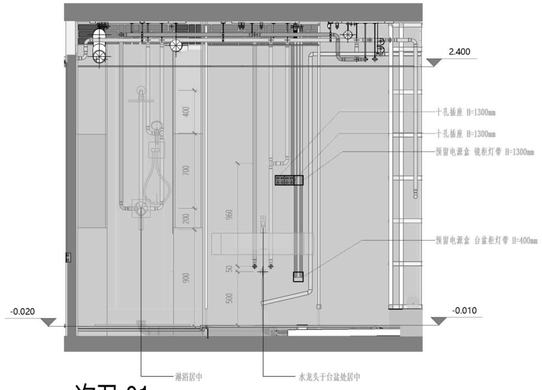

次卫-01

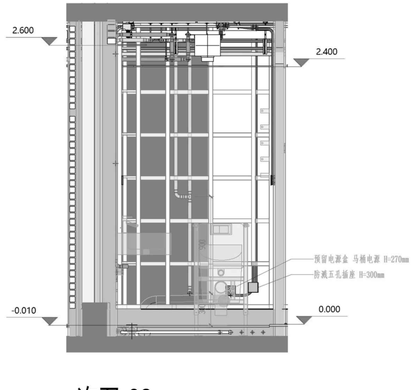

次卫-02

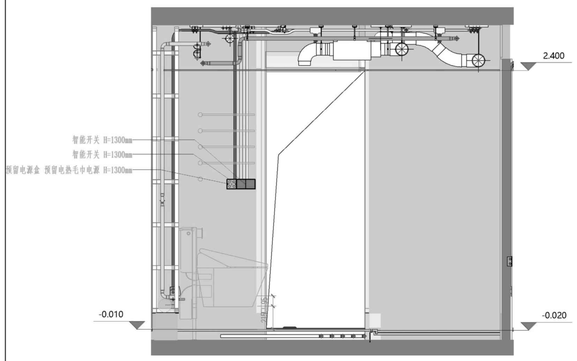

次卫-03

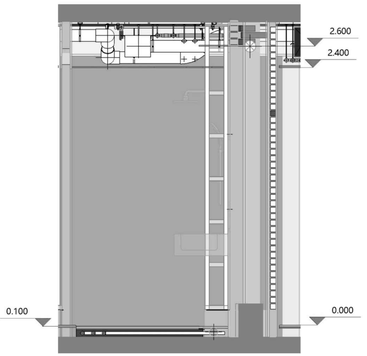

次卫-04

2	次卫水电立面图
立面	Scale比例 1 : 30@A2

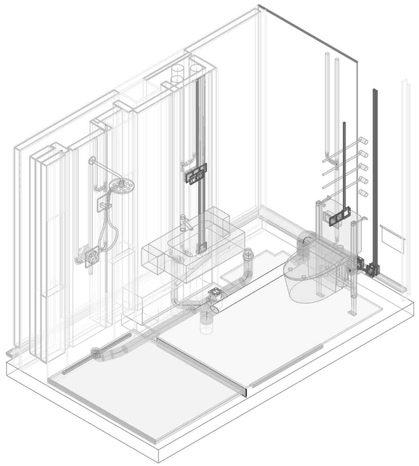

3	次卫水电三维图
三维	Scale比例 1 : 30@A2

HIBORN

1

LEGEND图例

编号	图例	说明
1		强电
2		弱电
3		给水
4		排水
5		排水(原有)
6		冷媒进管
7		冷媒出管
8		冷凝水管

盖章

注释
Notes

1.本图纸如与现场尺寸有误，请施工人员与项目负责人联系。
2.施工前施工人员应认真查阅此图，如有不明确尺寸，按现场测量为准。
3.本图纸必须经甲乙双方认可并签字方可作为施工依据。

日期
Date 01/20/26

修订
Revision

1

项目
Project
潮映华岸府3-801

比例
Scale 1:30@A2

次卫

图纸编号
Drawing No.
MEP-20

项目编号
Project No.

©2025

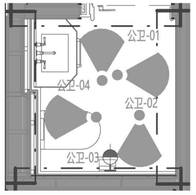

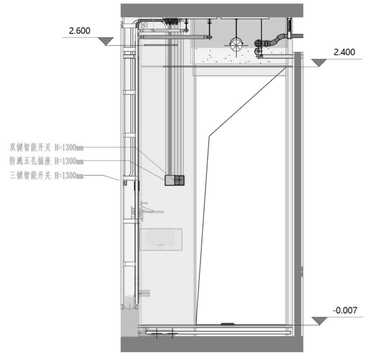

公卫-01

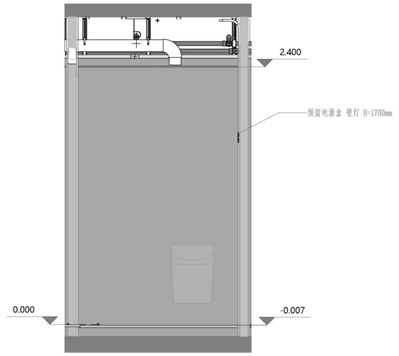

公卫-02

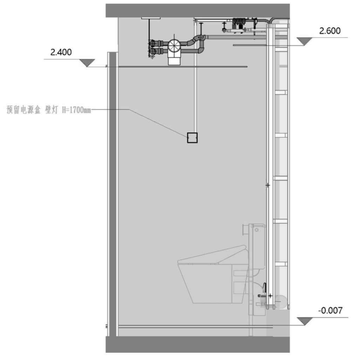

公卫-03

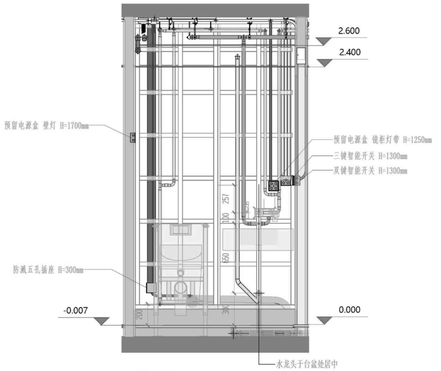

公卫-04

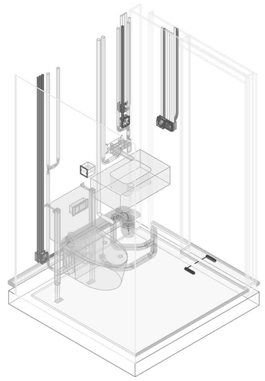

HIBORN

1

LEGEND图例

编号	图例	说明
1		强电
2		弱电
3		给水
4		排水
5		排水(原有)
6		冷媒进管
7		冷媒出管
8		冷凝水管

盖章

注释
Notes

1.本图纸如与现场尺寸有误，请施工人员与项目负责人联系。
2.施工前施工人员应认真查阅此图，如有不明确尺寸，按现场测量为准。
3.本图纸必须经甲乙双方认可并签字方可作为施工依据。

日期
Date 01/20/26

修订
Revision

1

项目
Project
潮映华岸府3-801

比例
Scale 1:30@A2

公卫

图纸编号
Drawing No.
MEP-21

项目编号
Project No.

©2025

1	公卫水电索引图	2	公卫水电立面图	3	公卫水电三维图
平面	Scale比例 1 : 30@A2	立面	Scale比例 1 : 30@A2	三维	Scale比例 1 : 30@A2

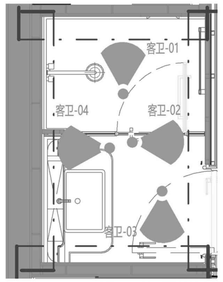

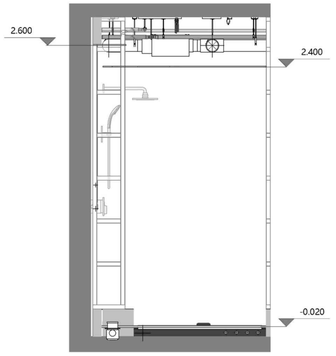

客卫-01

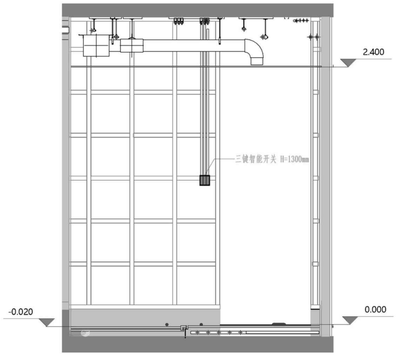

客卫-02

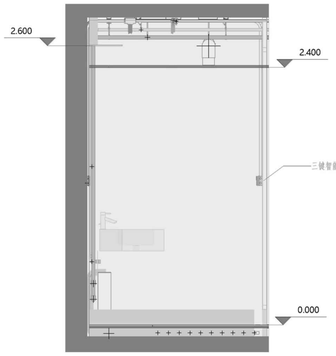

客卫-03

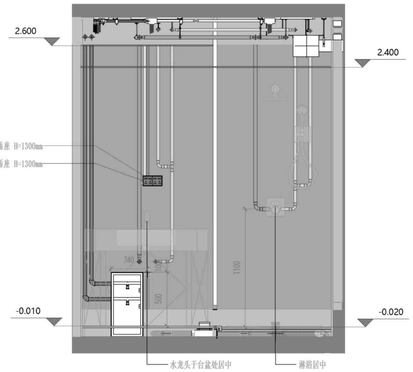

客卫-04

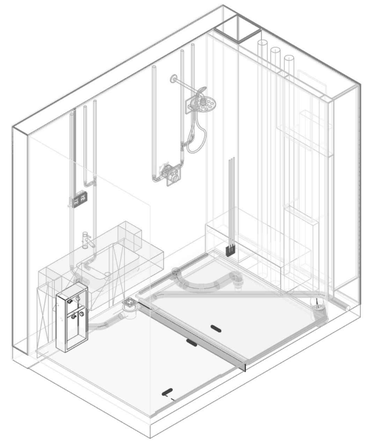

1	主卫水电索引图	2	主卫水电立面图	3	客卫水电三维图
平面	Scale比例 1 : 30@A2	立面	Scale比例 1 : 30@A2	三维	Scale比例 1 : 30@A2

HIBORN

1

LEGEND图例

编号	图例	说明
1		强电
2		弱电
3		给水
4		排水
5		排水(原有)
6		冷媒进管
7		冷媒出管
8		冷凝水管

盖章

注释
Notes

1.本图纸如与现场尺寸有误，请施工人员与项目负责人联系。
2.施工前施工人员应认真查阅此图，如有不明确尺寸，按现场测量为准。
3.本图纸必须经甲乙双方认可并签字方可作为施工依据。

日期
Date 01/20/26

修订
Revision

1

项目
Project
潮映华岸府3-801

比例
Scale 1:30@A2

客卫

图纸编号
Drawing No.
MEP-22

项目编号
Project No.

©2025

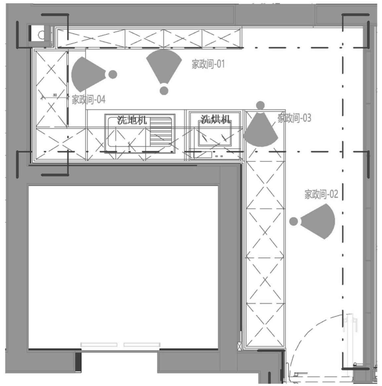

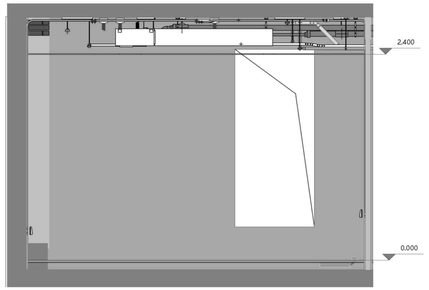

家政间-01

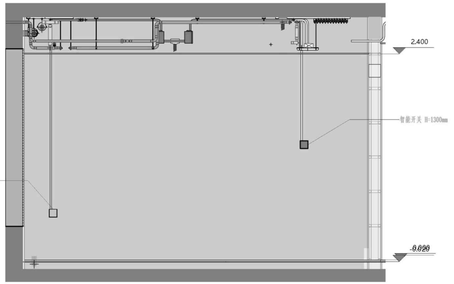

家政间-02

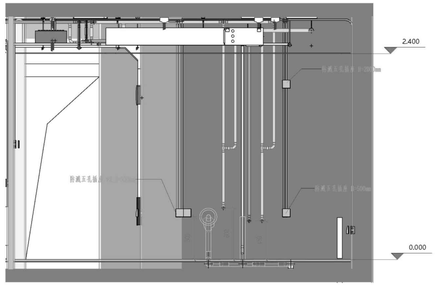

家政间-03

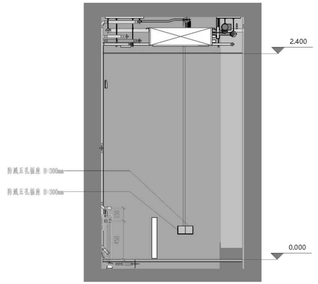

家政间-04

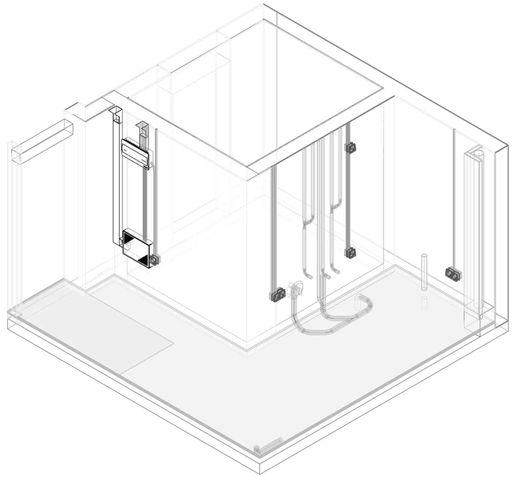

LEGEND图例

编号	图例	说明
1		强电
2		弱电
3		给水
4		排水
5		排水(原有)
6		冷媒进管
7		冷媒出管
8		冷凝水管

盖章

注释
Notes

1.本图纸标注与现场尺寸有误，施工单位与项目负责人联系。
2.施工前施工人员应认真查阅此图，如有不明确尺寸，按现场测量为准。
3.本图纸由图环境艺术公司开发平方引导为施工依据。

日期
Date 01/20/26

修订
Revision

1

项目
Project
潮映华岸府3-801

比例
Scale 1:30@A2

家政间

图纸编号
Drawing No.
MEP-23

项目编号
Project No.

©2025

1	家政间水电索引图	2	家政间水电立面图	3	家政间水电三维图
平面	Scale比例 1 : 30@A2	立面	Scale比例 1 : 30@A2	三维	Scale比例 1 : 30@A2

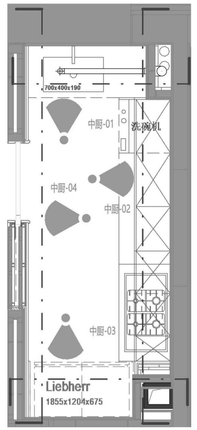

1	中厨水电索引图
平面	Scale比例 1 : 30@A2

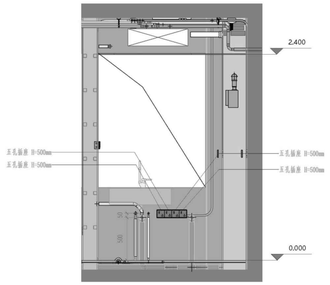

中厨-01

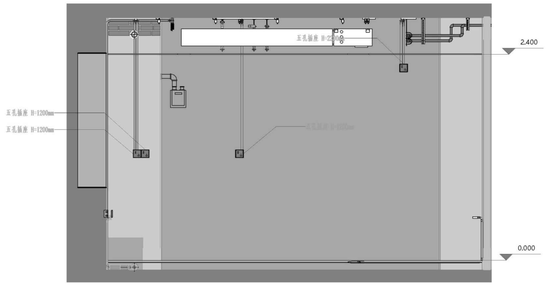

中厨-02

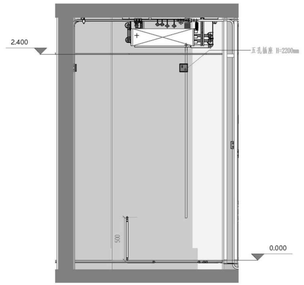

中厨-03

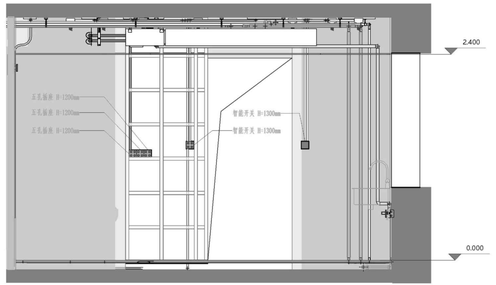

中厨-04

2	中厨水电立面图
立面	Scale比例 1 : 30@A2

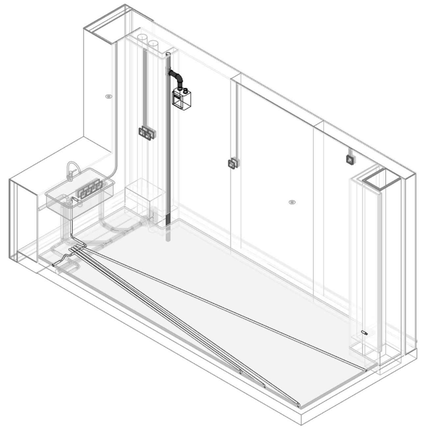

3	中厨水电三维图
三维	Scale比例 1 : 30@A2

LEGEND图例

编号	图例	说明
1		强电
2		弱电
3		给水
4		排水
5		排水(原有)
6		冷媒进管
7		冷媒出管
8		冷凝水管

盖章

注释
Notes
1.本图纸标注均现场尺寸有误，施工人员与项目负责人联系。
2.施工前施工人员应认真查阅此图，如有不明确之下，按现场测量为准。
3.本图纸标注部分单位为mm，其余单位为米为可作为施工依据。

日期
Date 01/20/26

修订
Revision
1

项目
Project
潮映华岸府3-801

比例
Scale 1:30@A2

中厨

图纸编号
Drawing No.
MEP-24

项目编号
Project No.
©2025

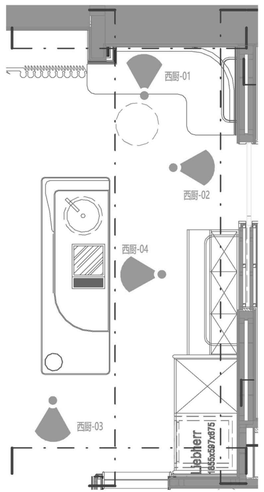

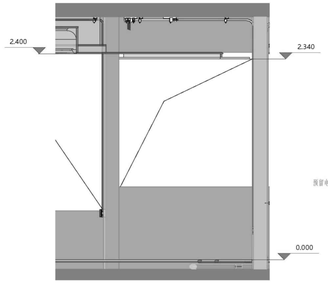

西厨-01

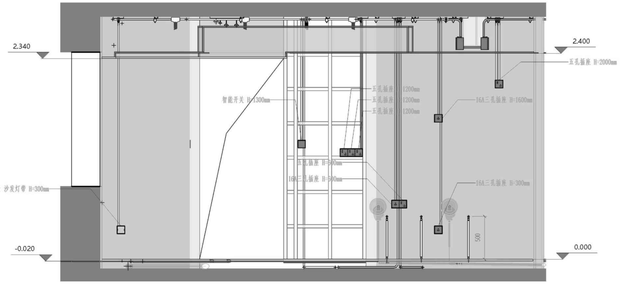

西厨-02

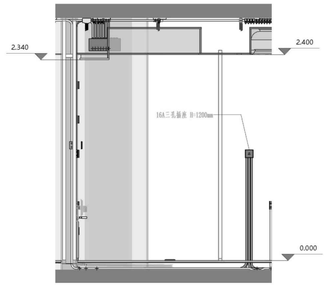

西厨-03

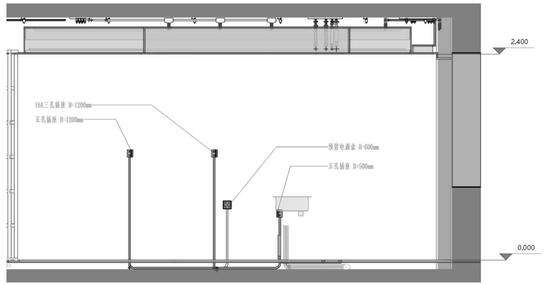

西厨-04

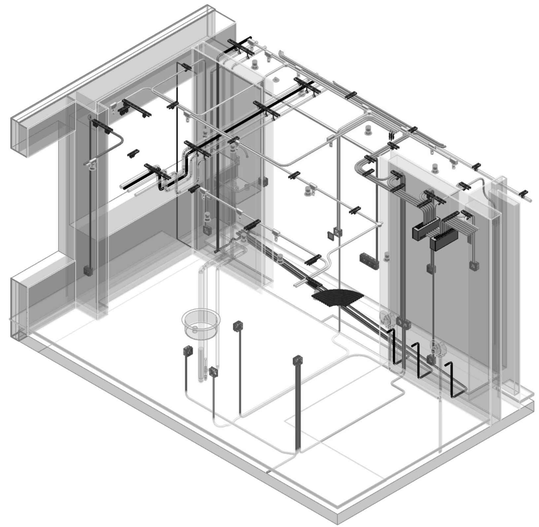

LEGEND图例

编号	图例	说明
1		强电
2		弱电
3		给水
4		排水
5		排水(原有)
6		冷媒进管
7		冷媒出管
8		冷凝水管

盖章

注释
Notes

1.本图纸标注为现场尺寸标识，施工人员与项目负责人联系。
2.施工前施工人员应认真查阅此图，如有不明确之下，按现场测量为准。
3.本图纸标注部分单位为mm以外其余为尺寸为准施工依据。

日期
Date 01/20/26

修订
Revision

1

项目
Project
潮映华岸府3-801

比例
Scale 1:30@A2

西厨

图纸编号
Drawing No. MEP-25

项目编号
Project No.

©2025

1	西厨水电索引图	2	西厨水电立面图	3	西厨水电三维图
平面	Scale比例 1 : 30@A2	立面	Scale比例 1 : 30@A2	三维	Scale比例 1 : 30@A2