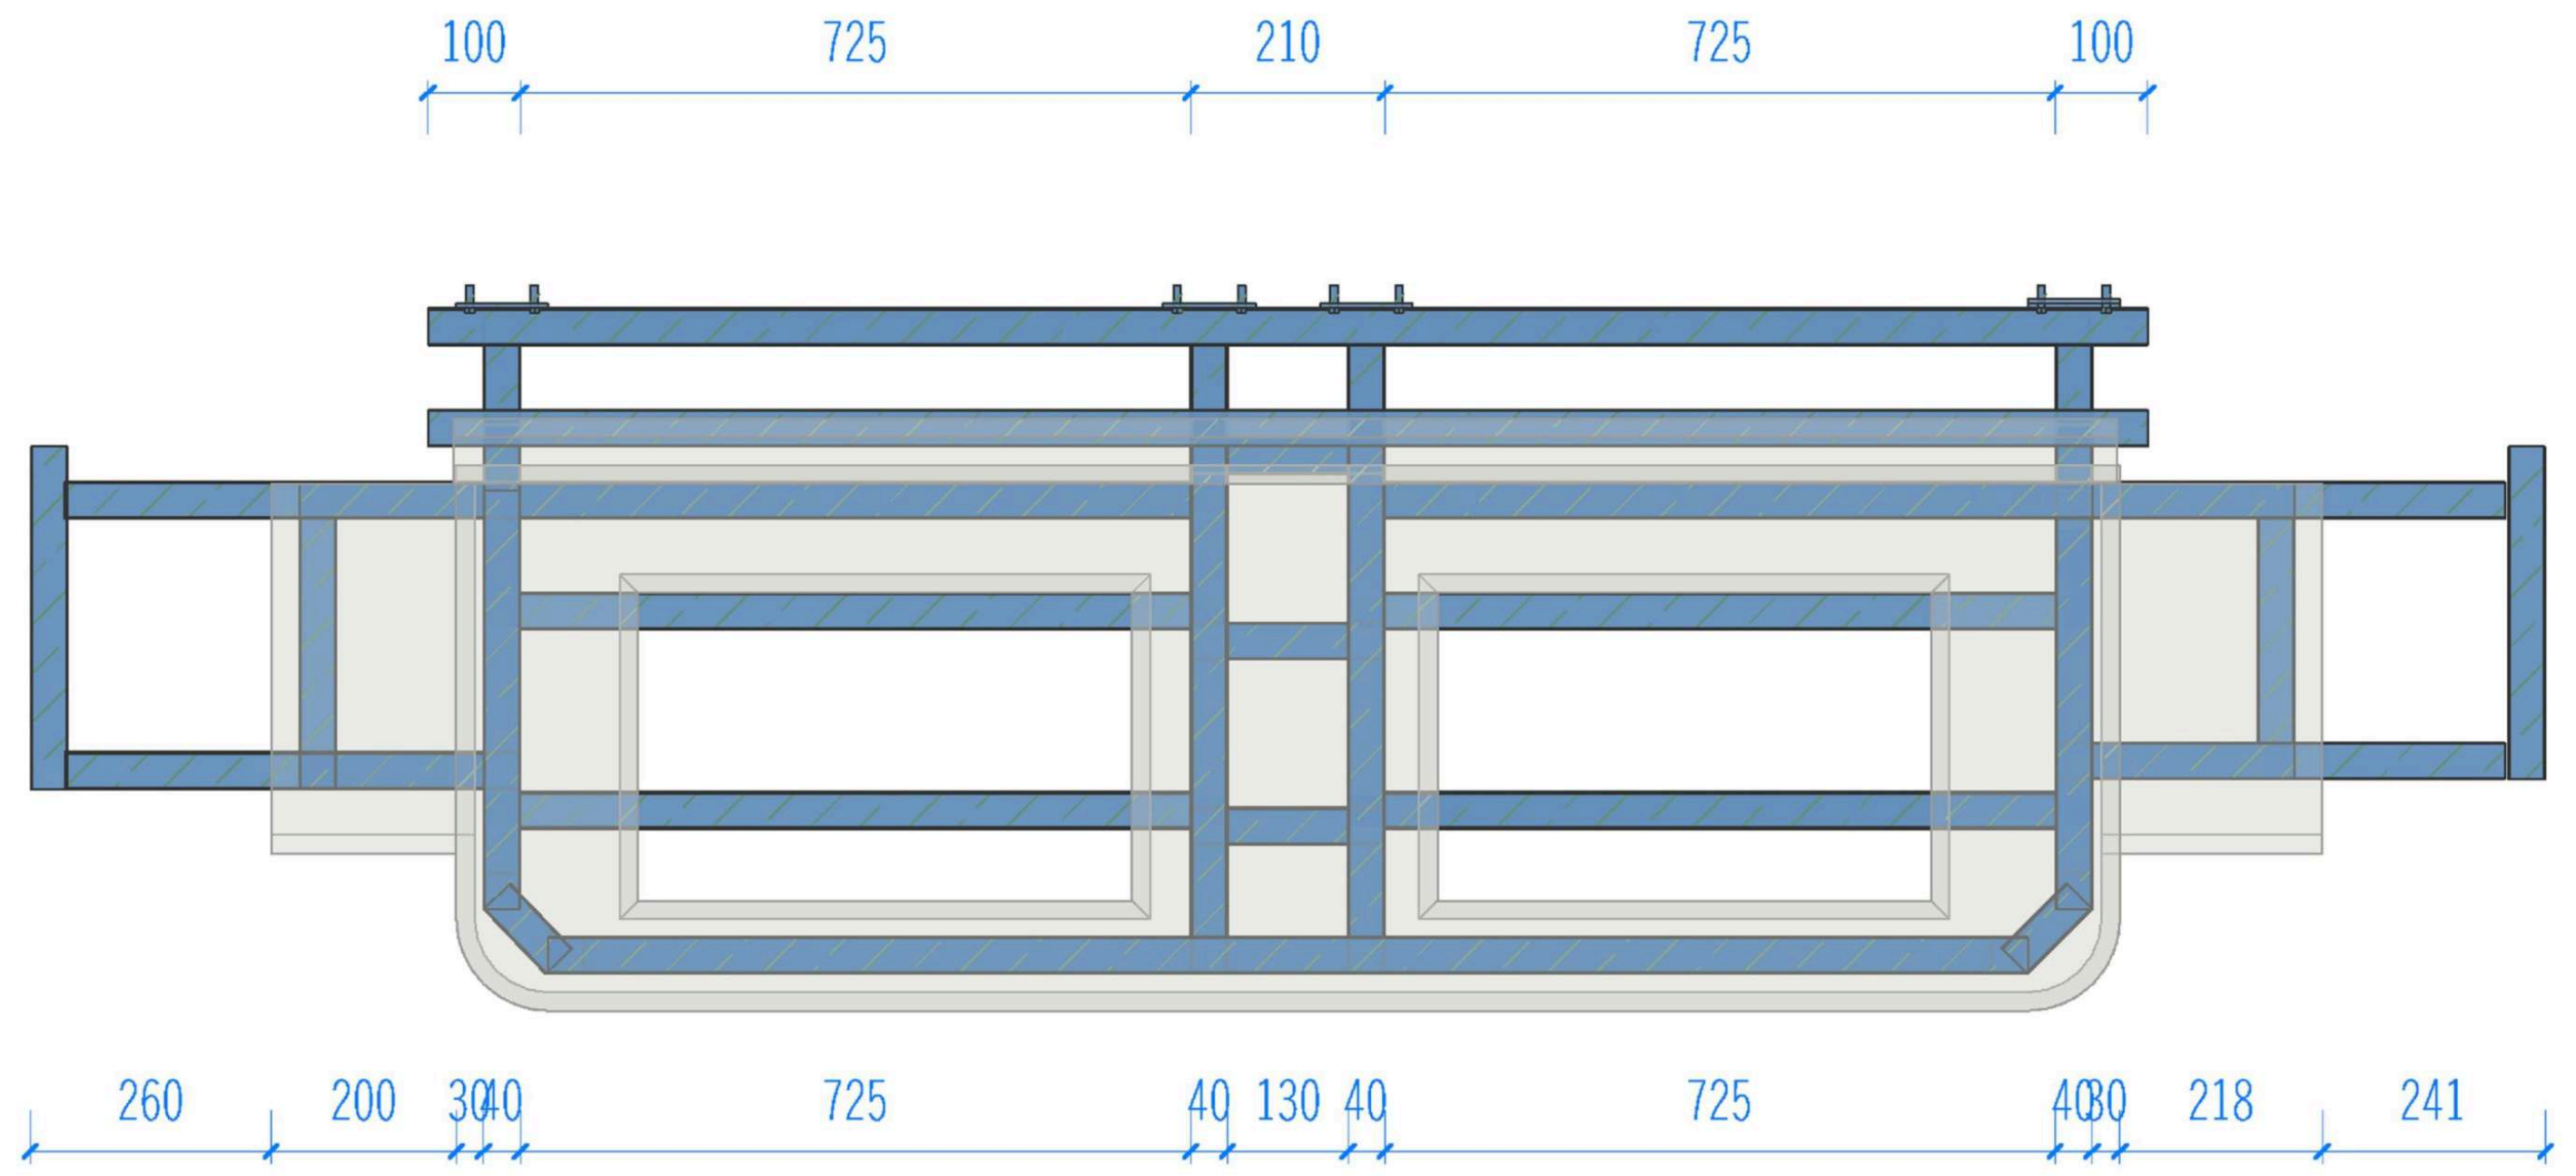
100
725
210
725
100
260
200
30
40
725
40
130
40
725
40
30
218
241

平面视图

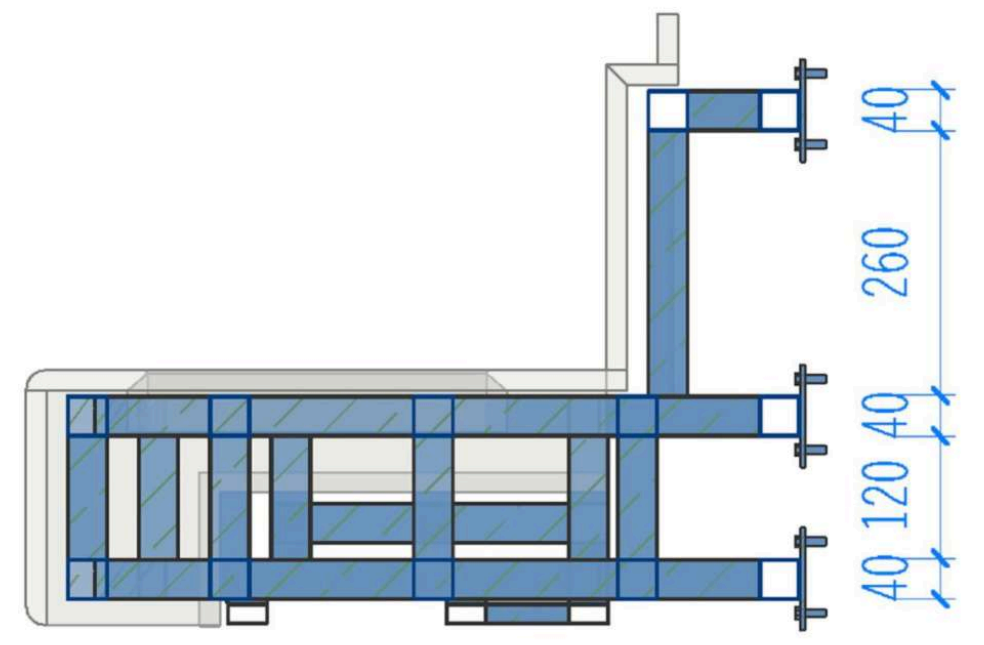
40
260
40
120
40

剖面视图

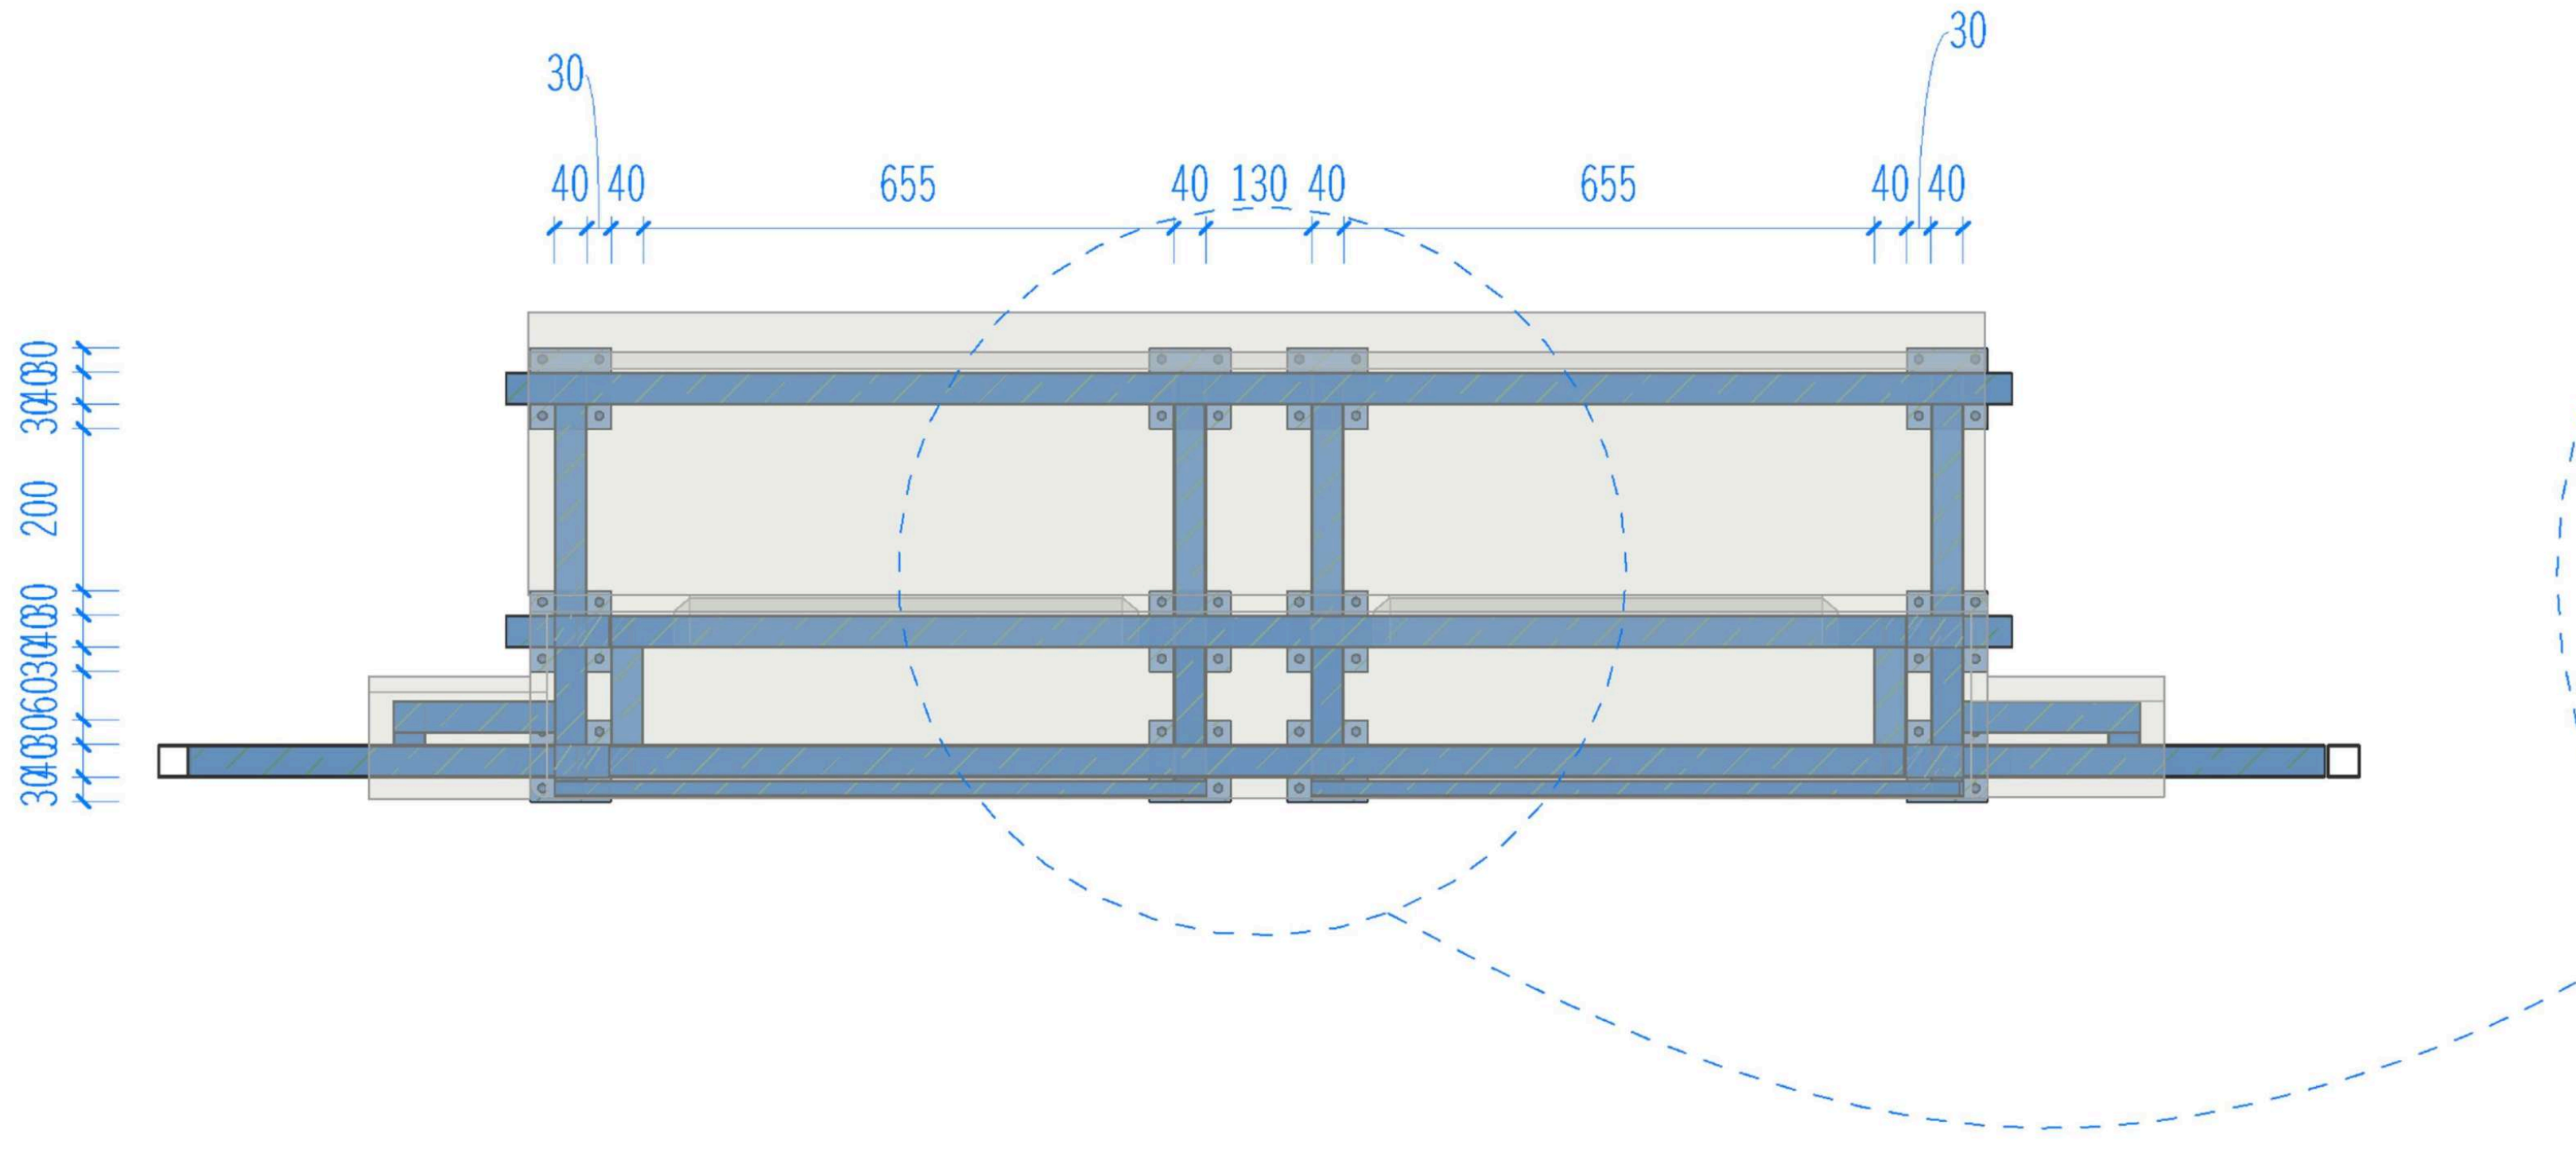
30
40
40
655
40
130
40
655
40
40
30
30 40 30
200
30 40 30 60 30 40 30

立面视图

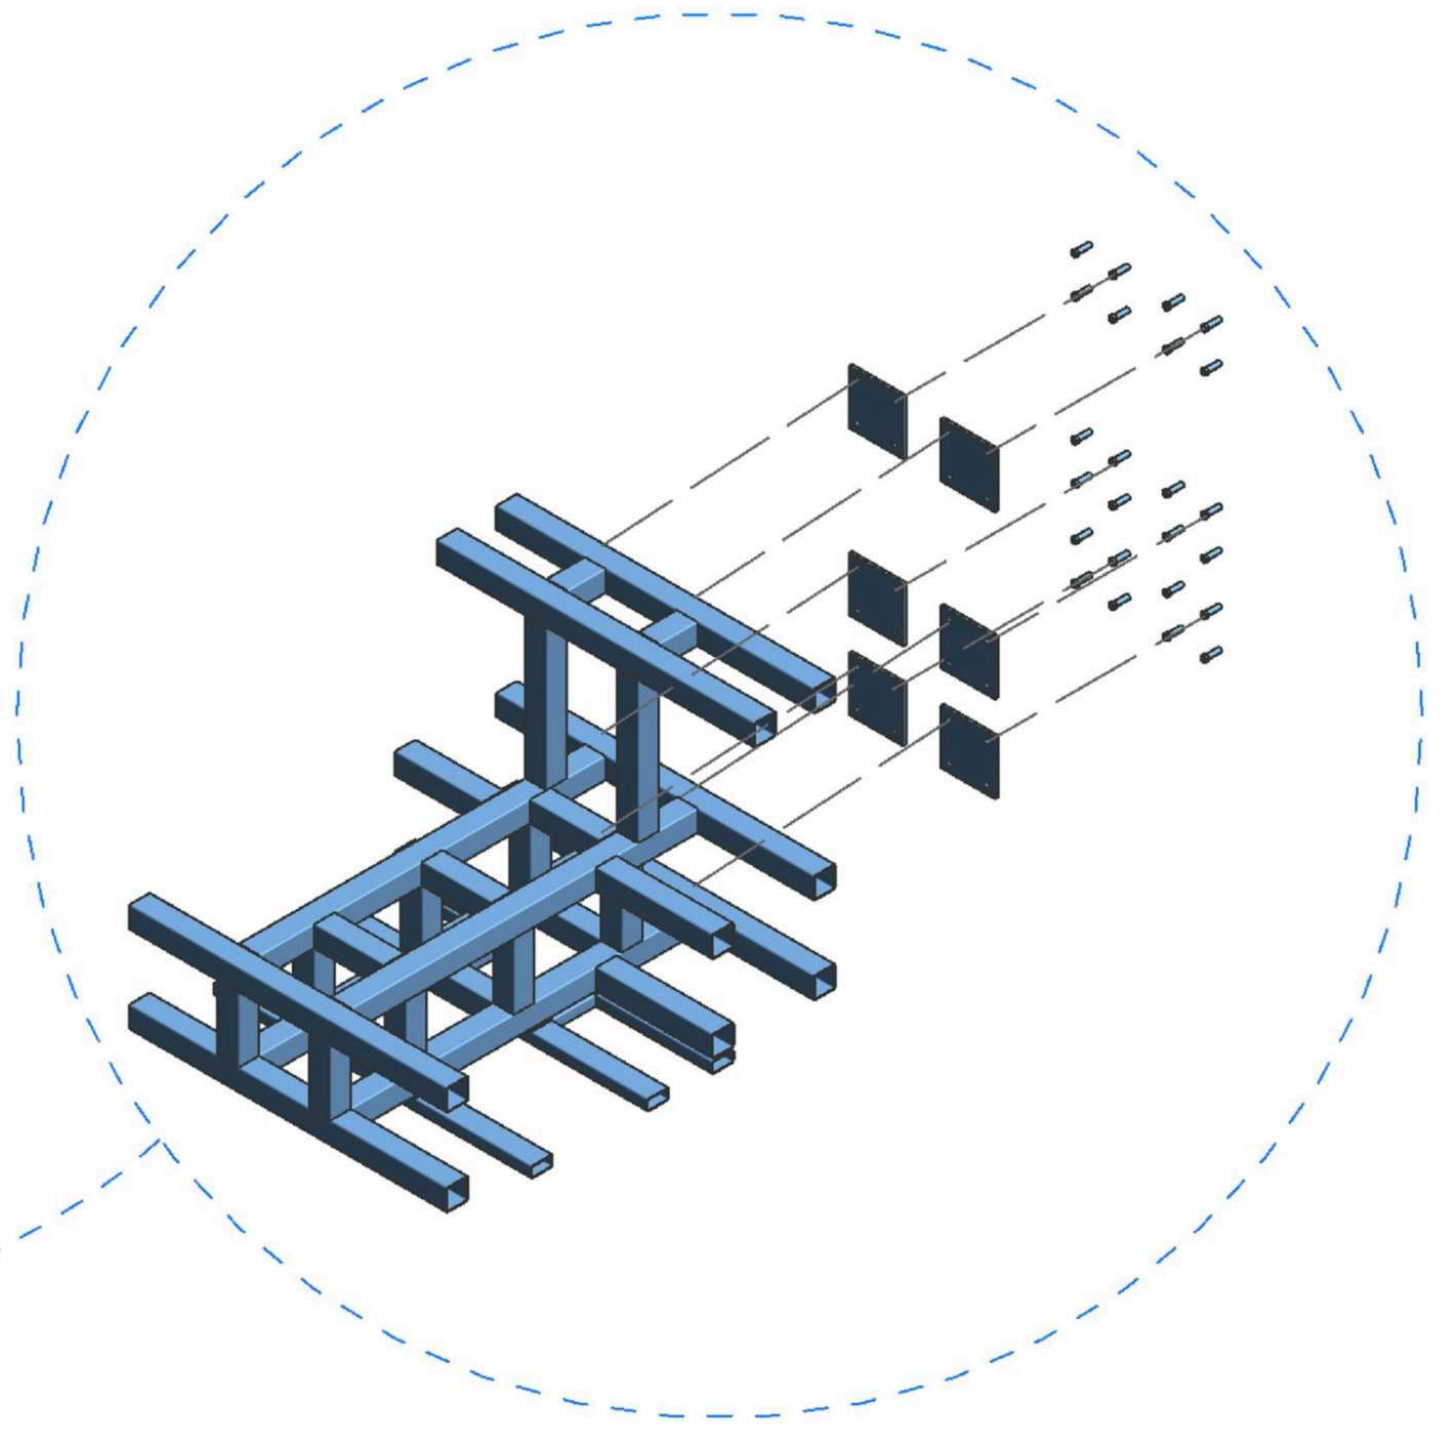

节点图

工厂预制钢架

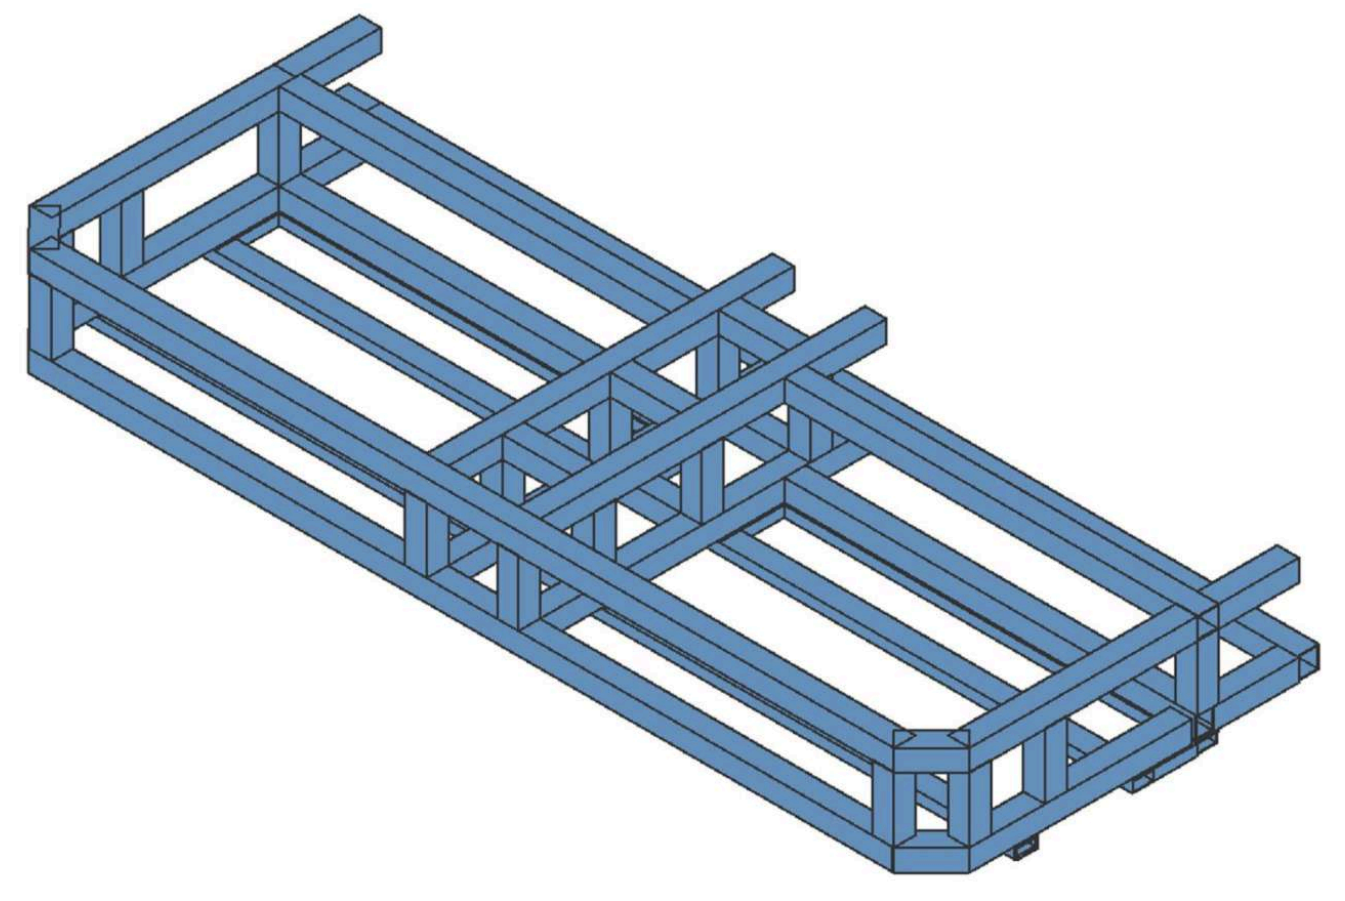

①

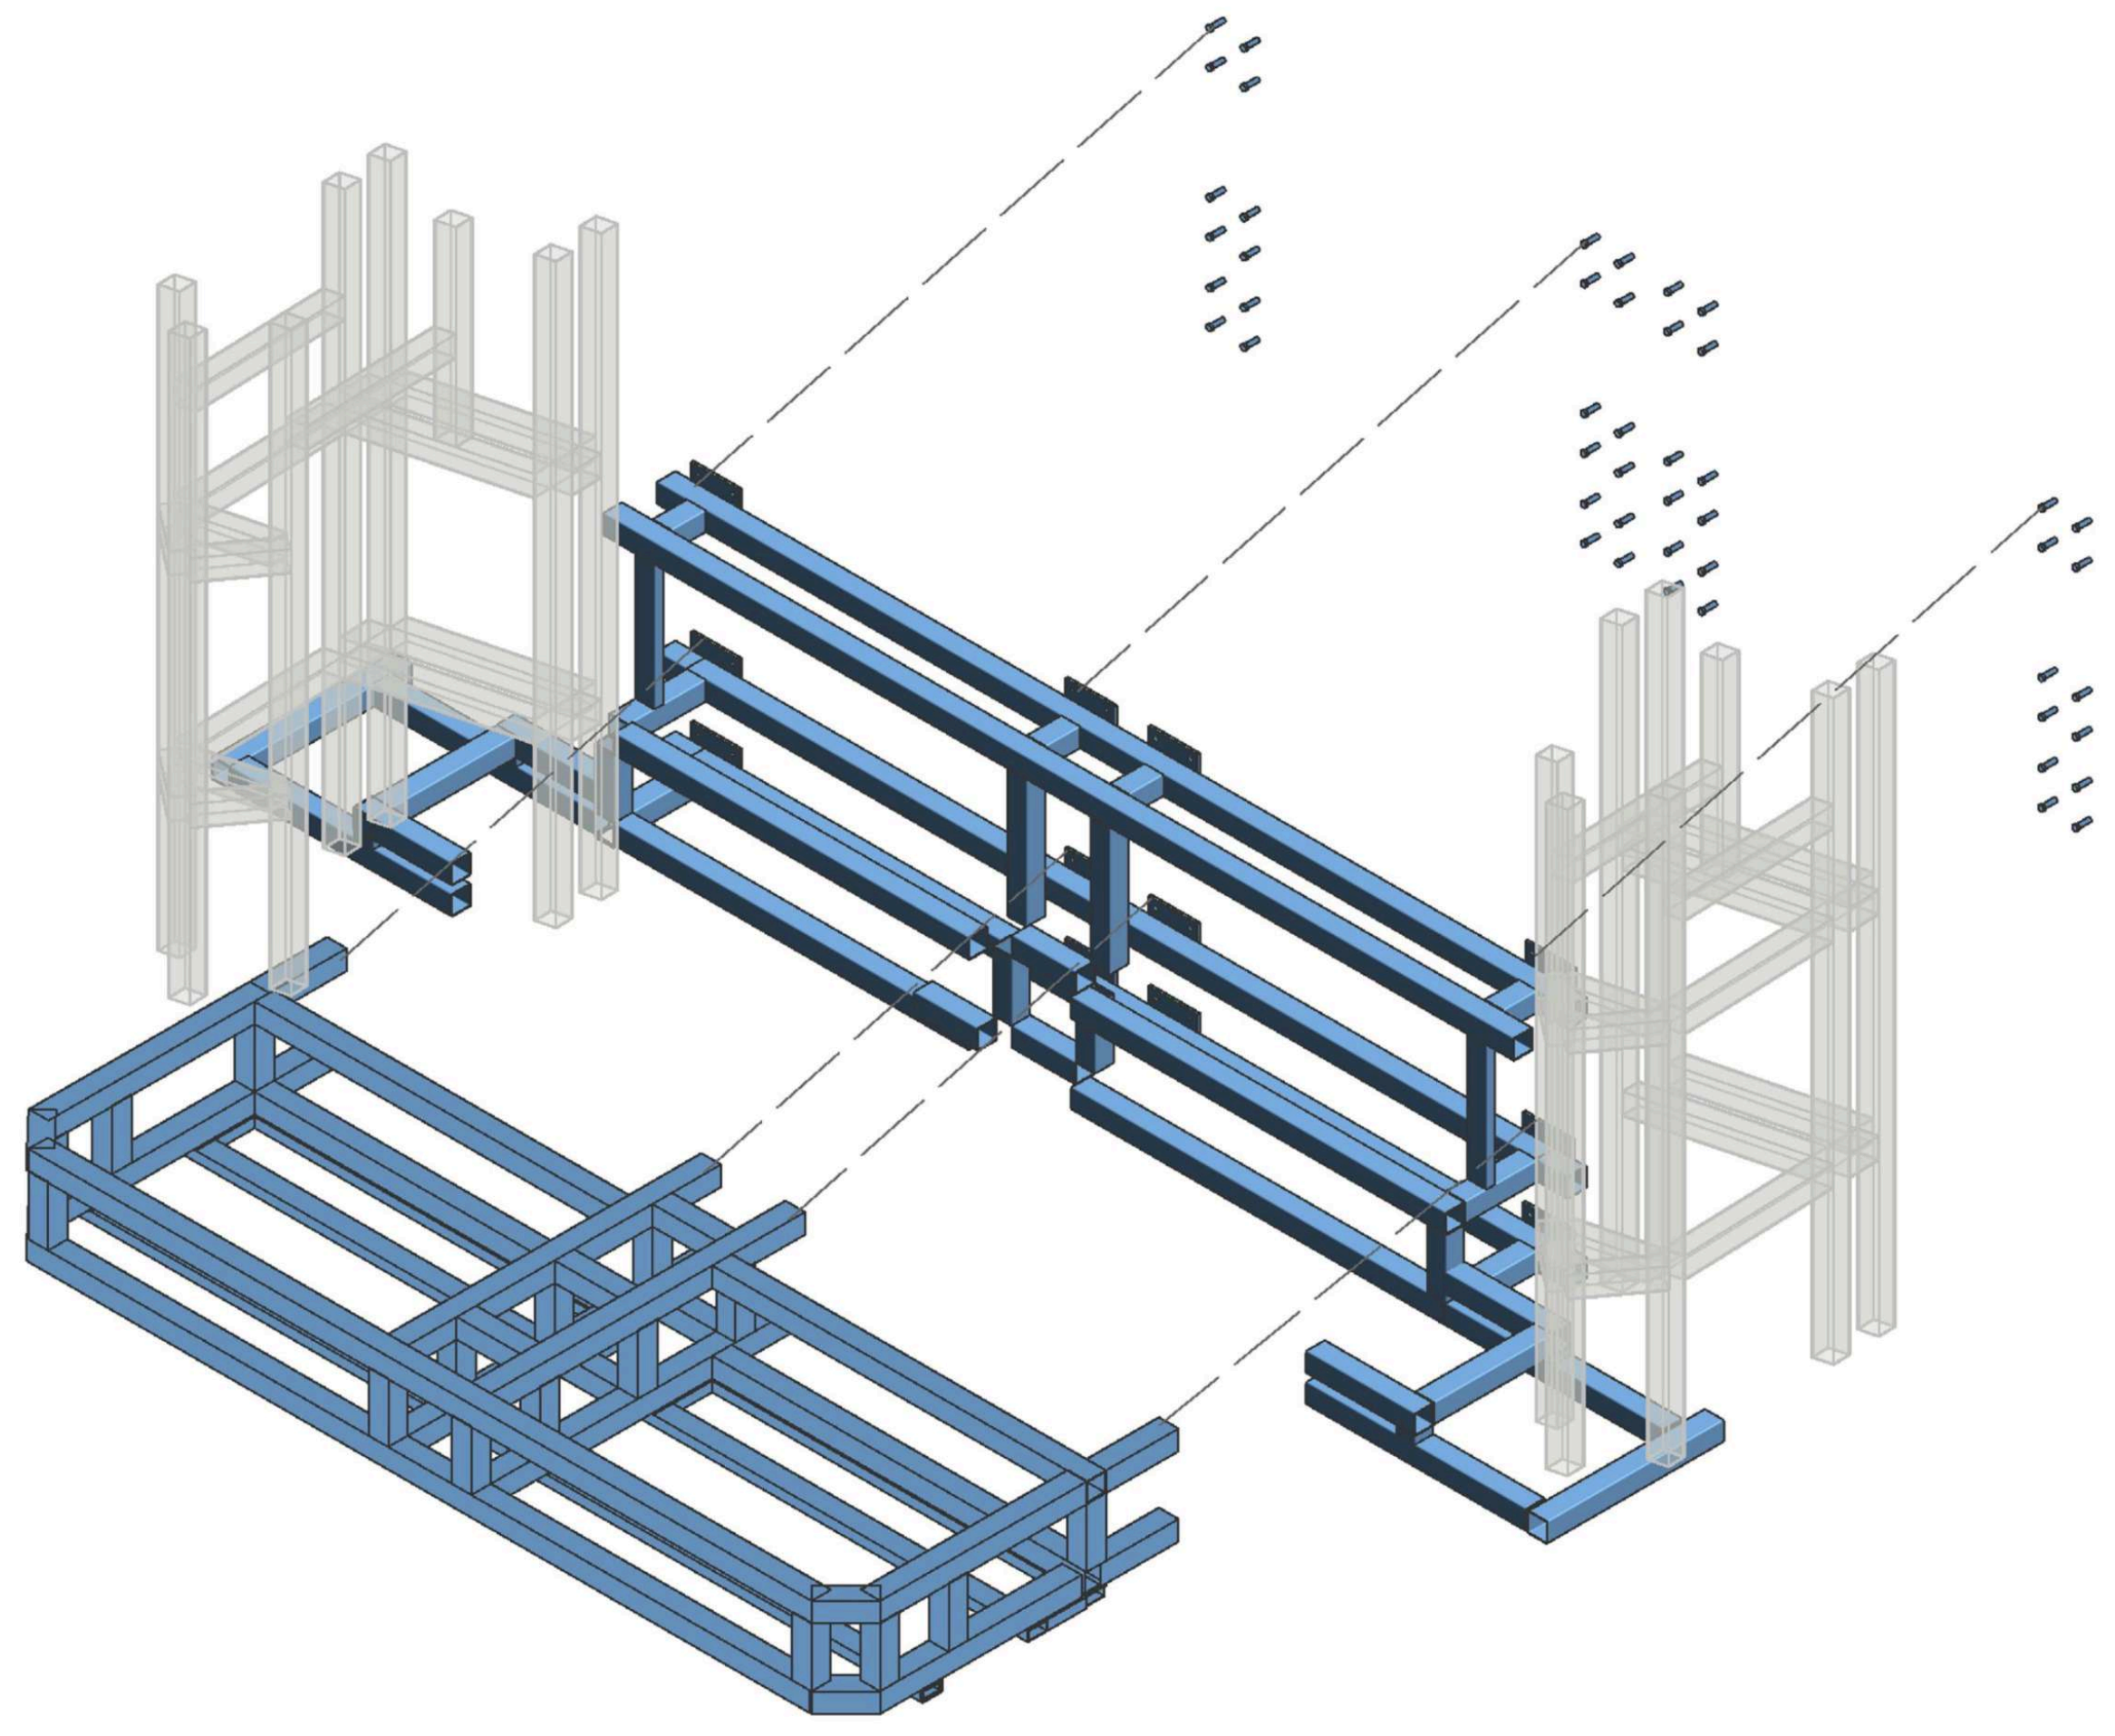

②

③

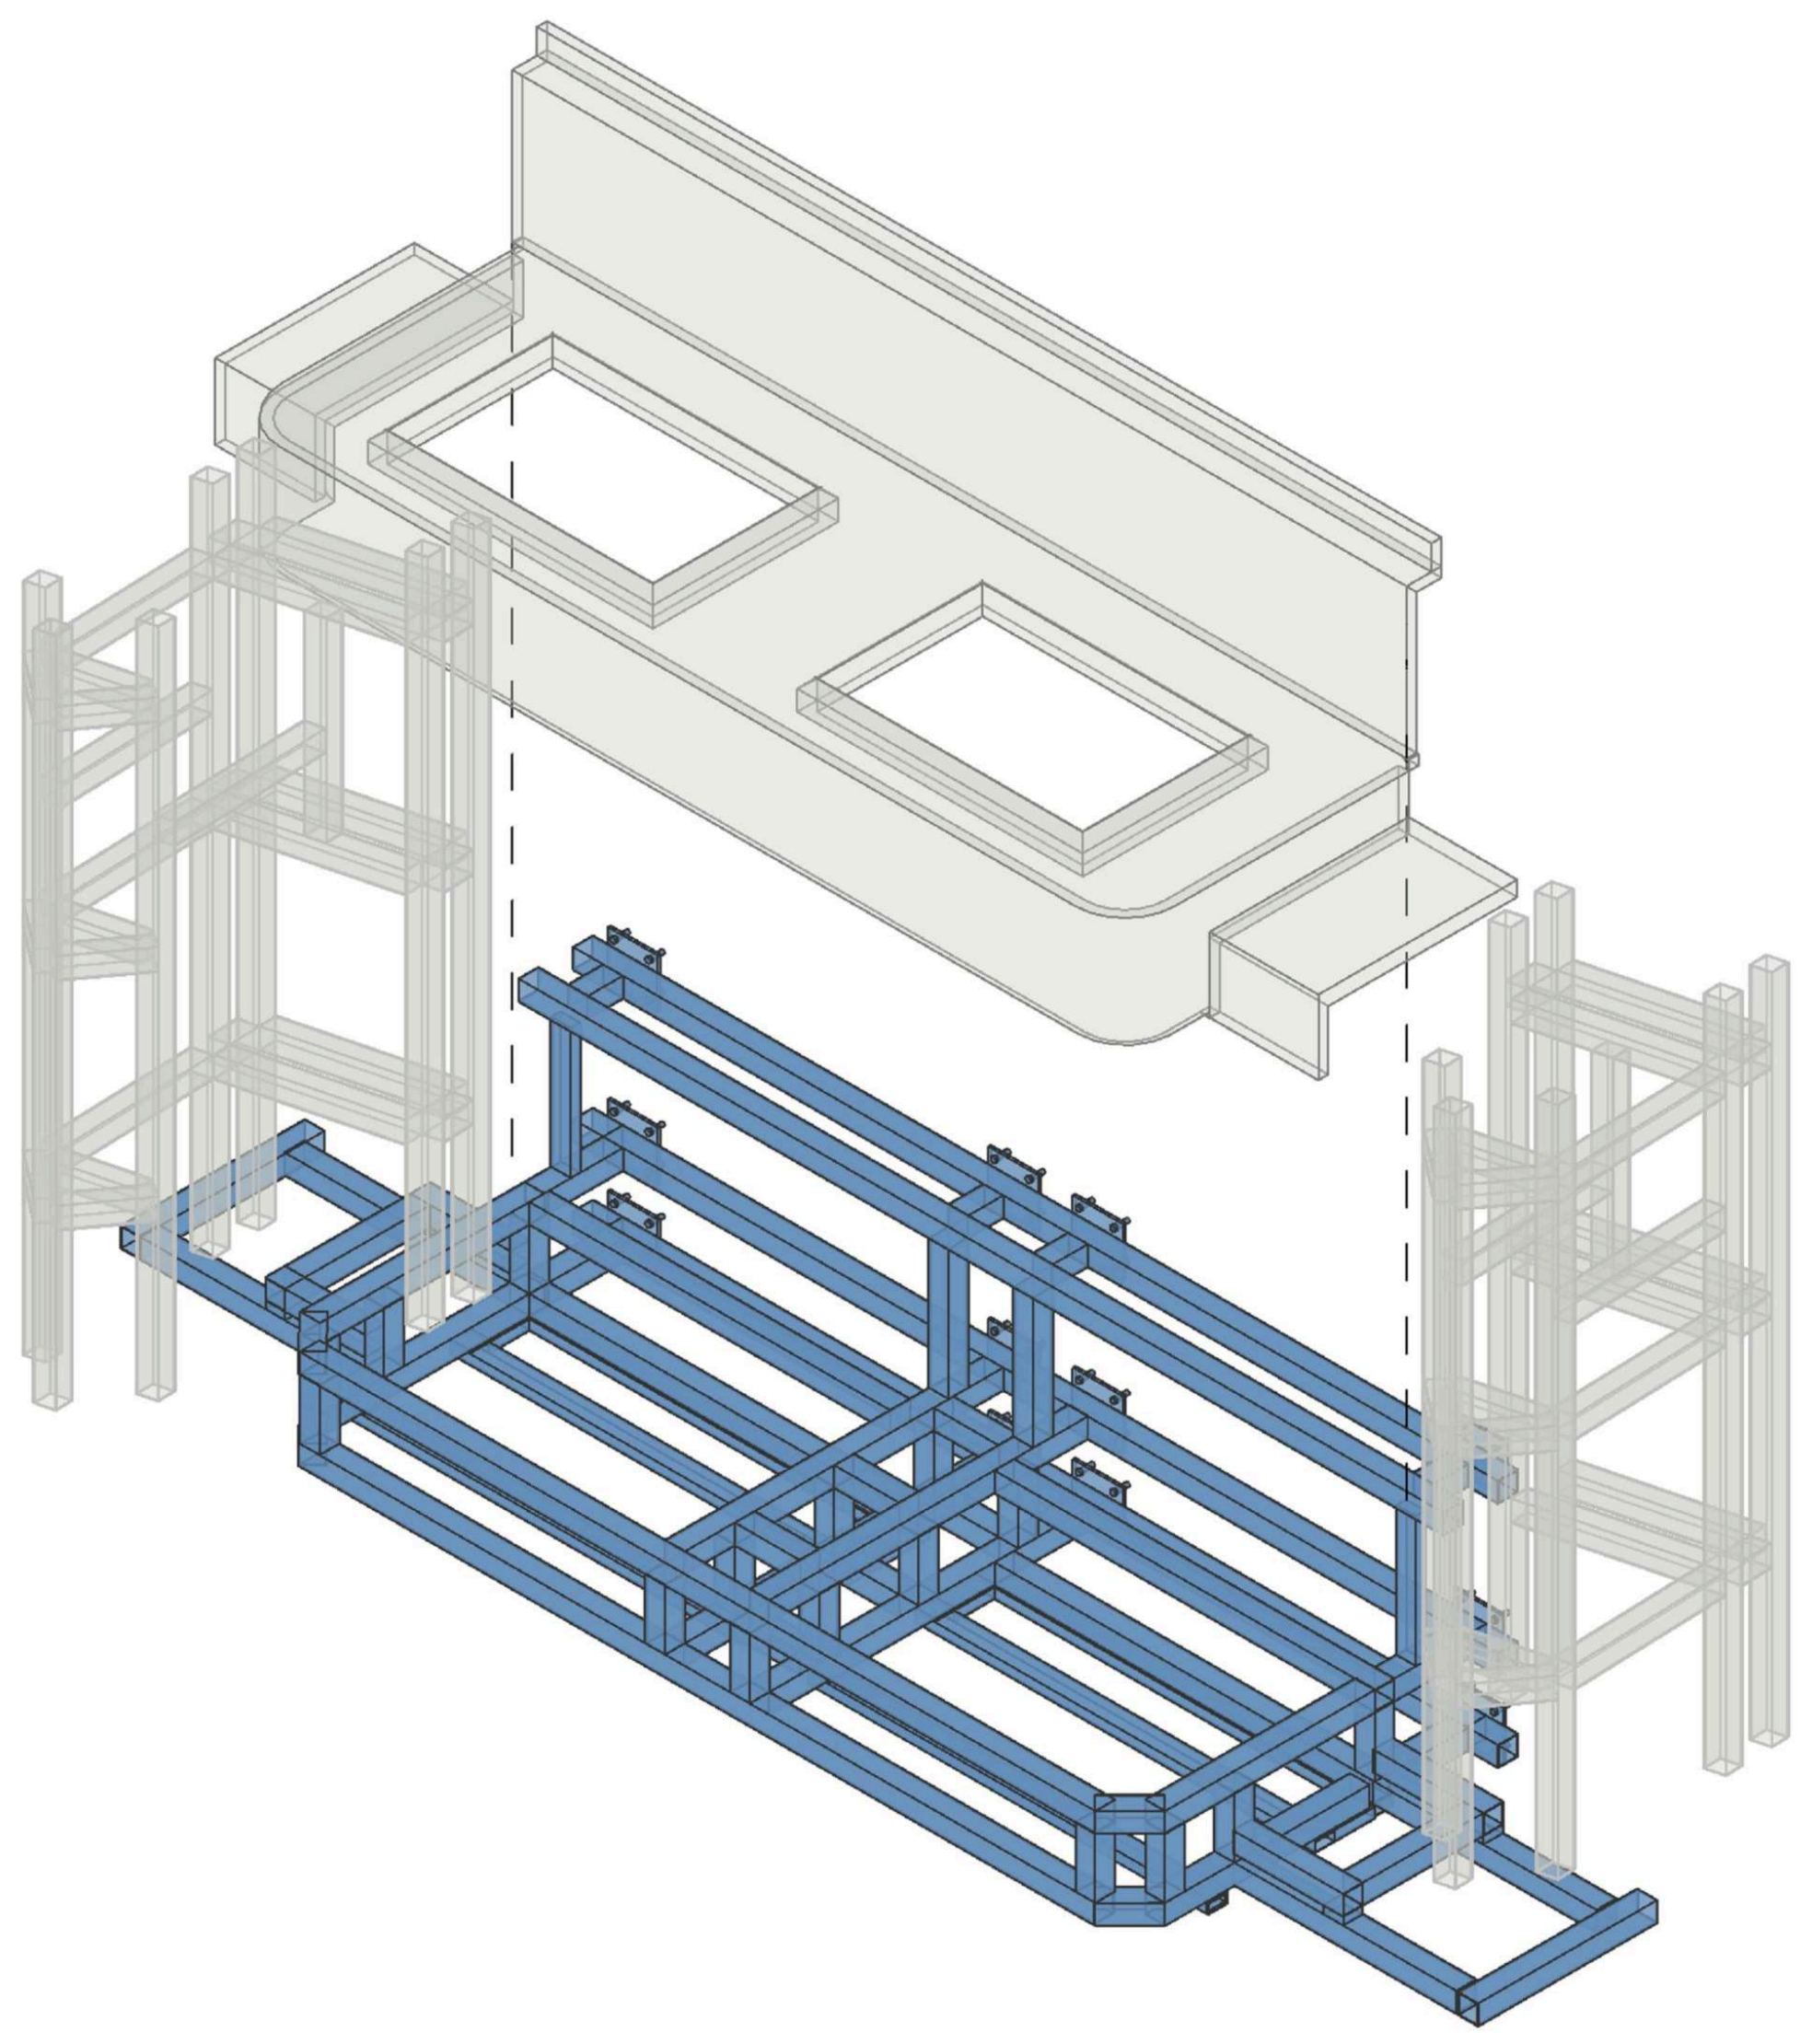

④

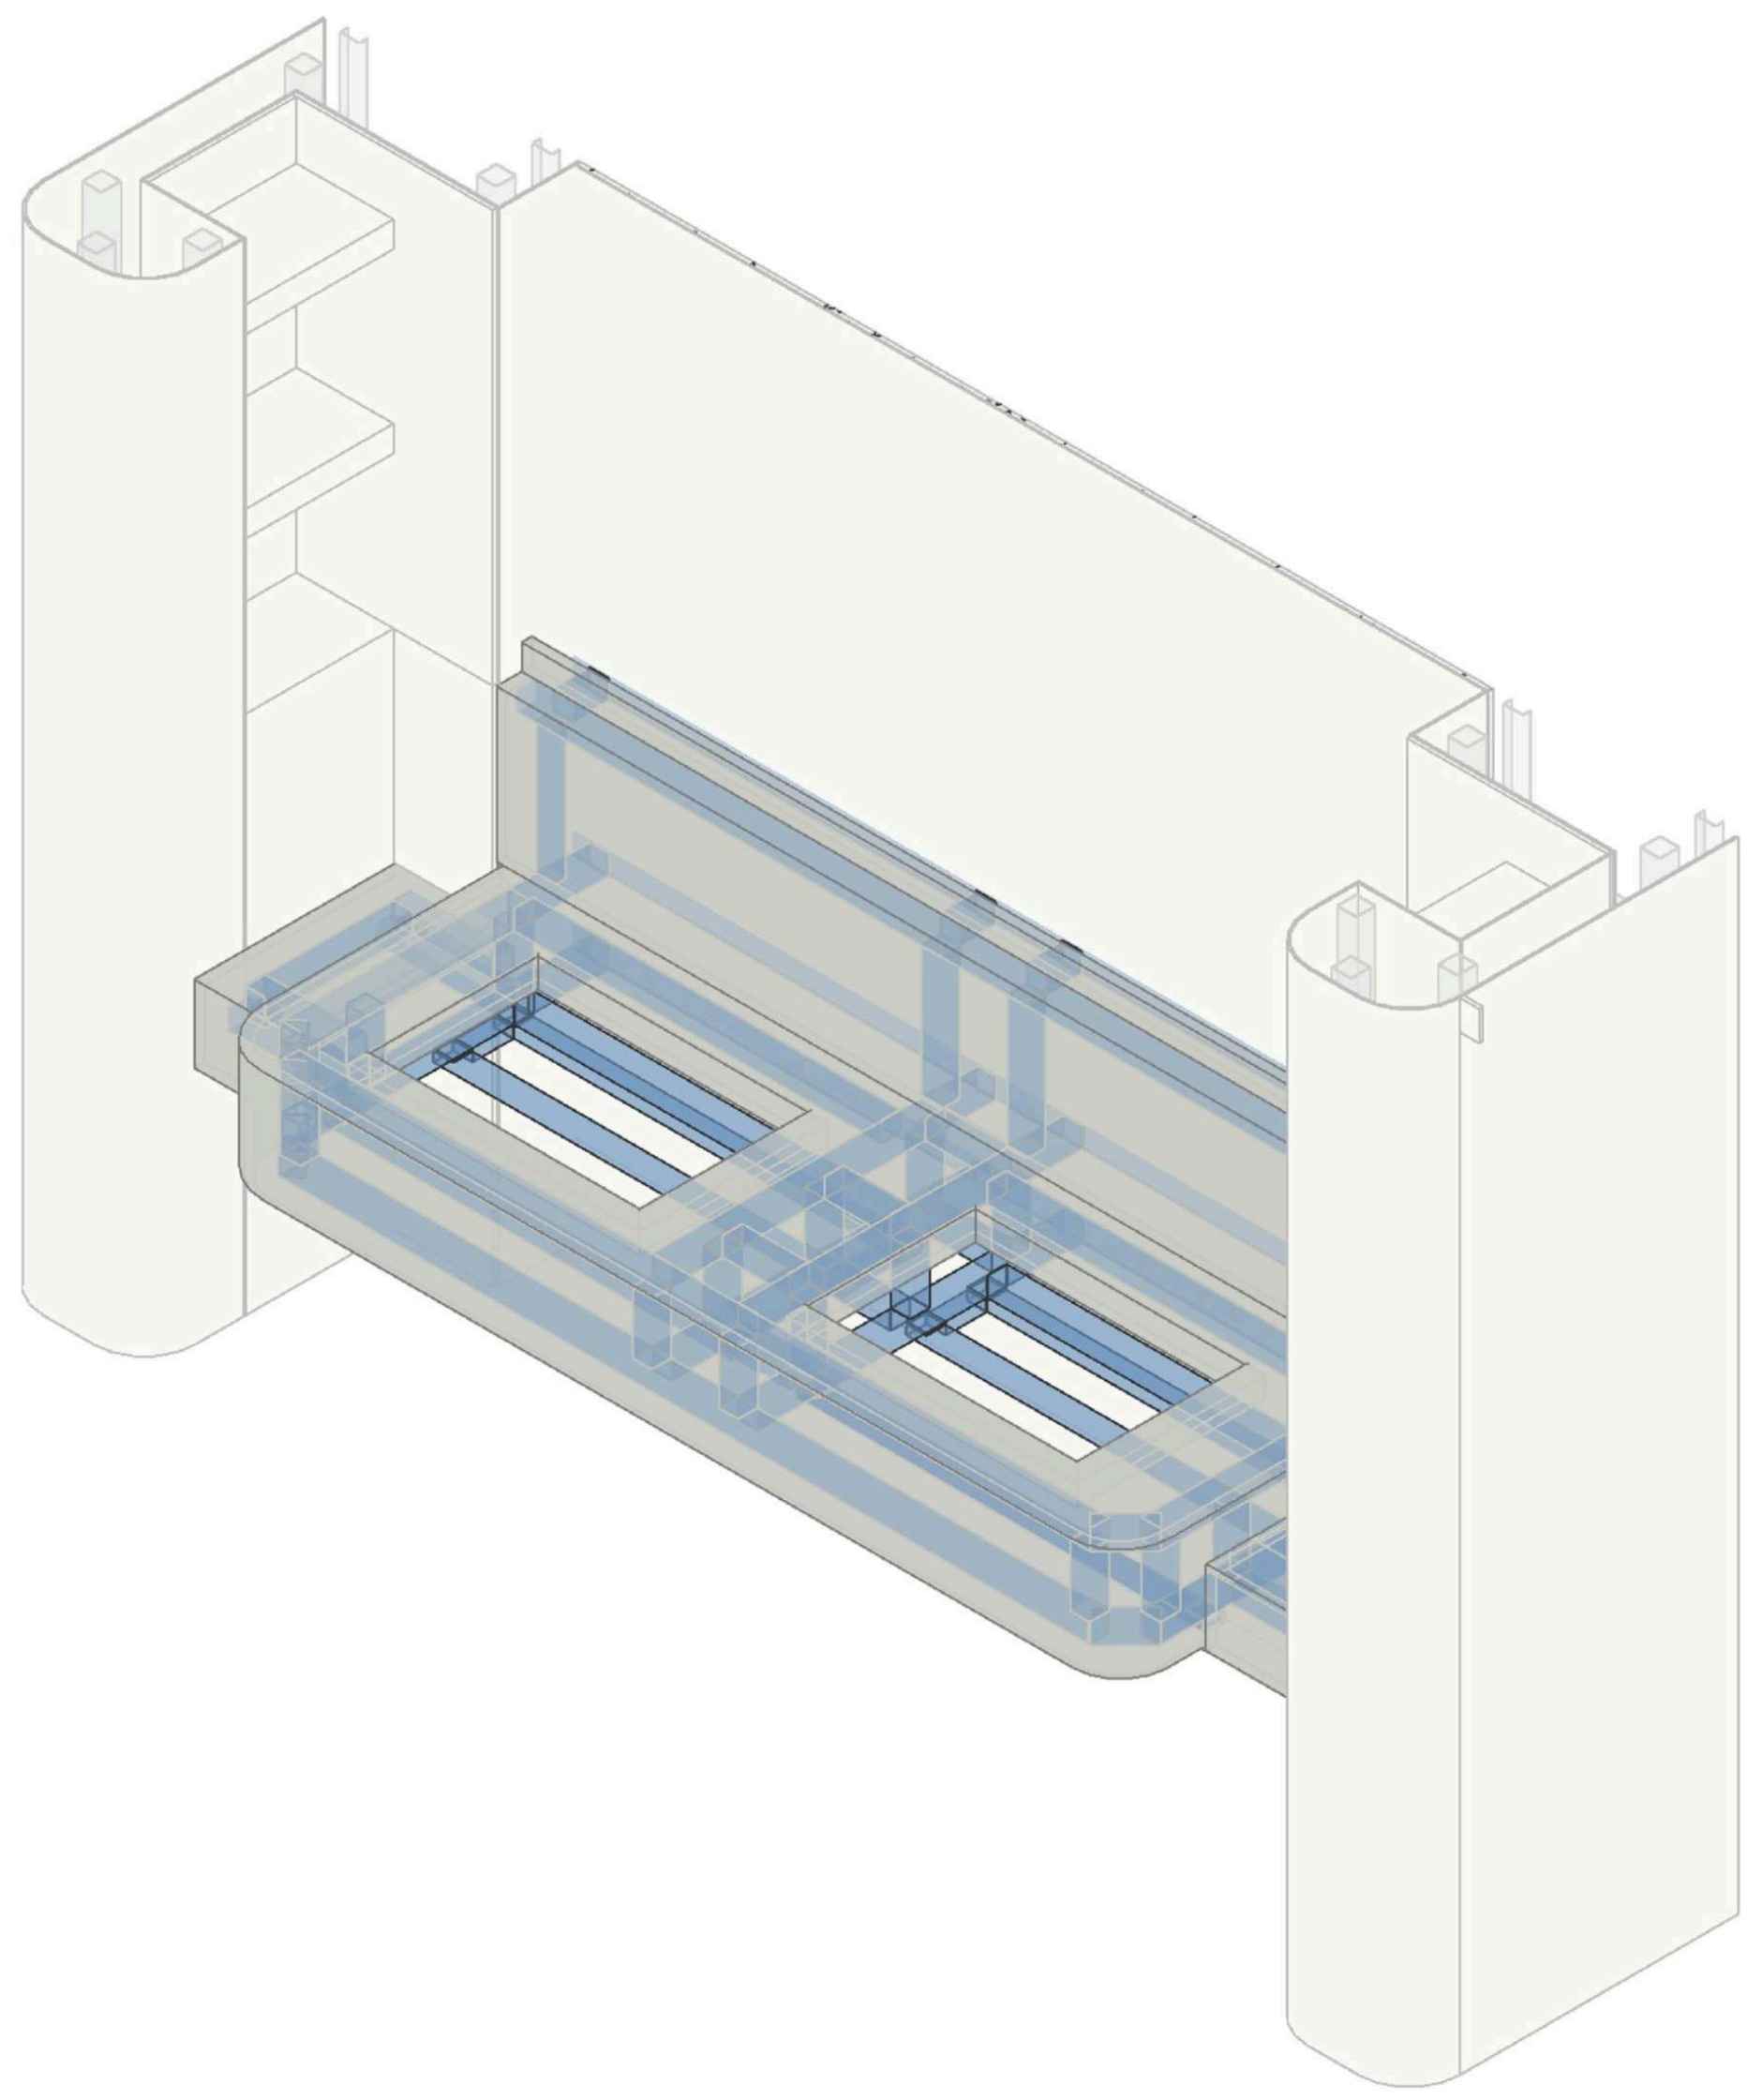

FIBORN

1

图例A
LEGEND A

编号	图例	说明
1		原始钢架
2		螺栓
3		钢片
4		钢架
5		石材

盖章

注释
Notes

1.本图纸如与现场尺寸有误，请施工人员与项目负责人联系。
2.施工前施工人员应认真查阅此图，如有不明确尺寸，按现场测量为准。
3.本图纸必须经甲乙双方认可并签字方可作为施工依据。

日期
Date 05/07/26

修订
Revision

⚠1

项目
Project
潮映华岸府3-801

比例
Scale

主卫洗手台石材钢架

图纸编号
Drawing No.
ST-01

项目编号
Project No.

©2025

1

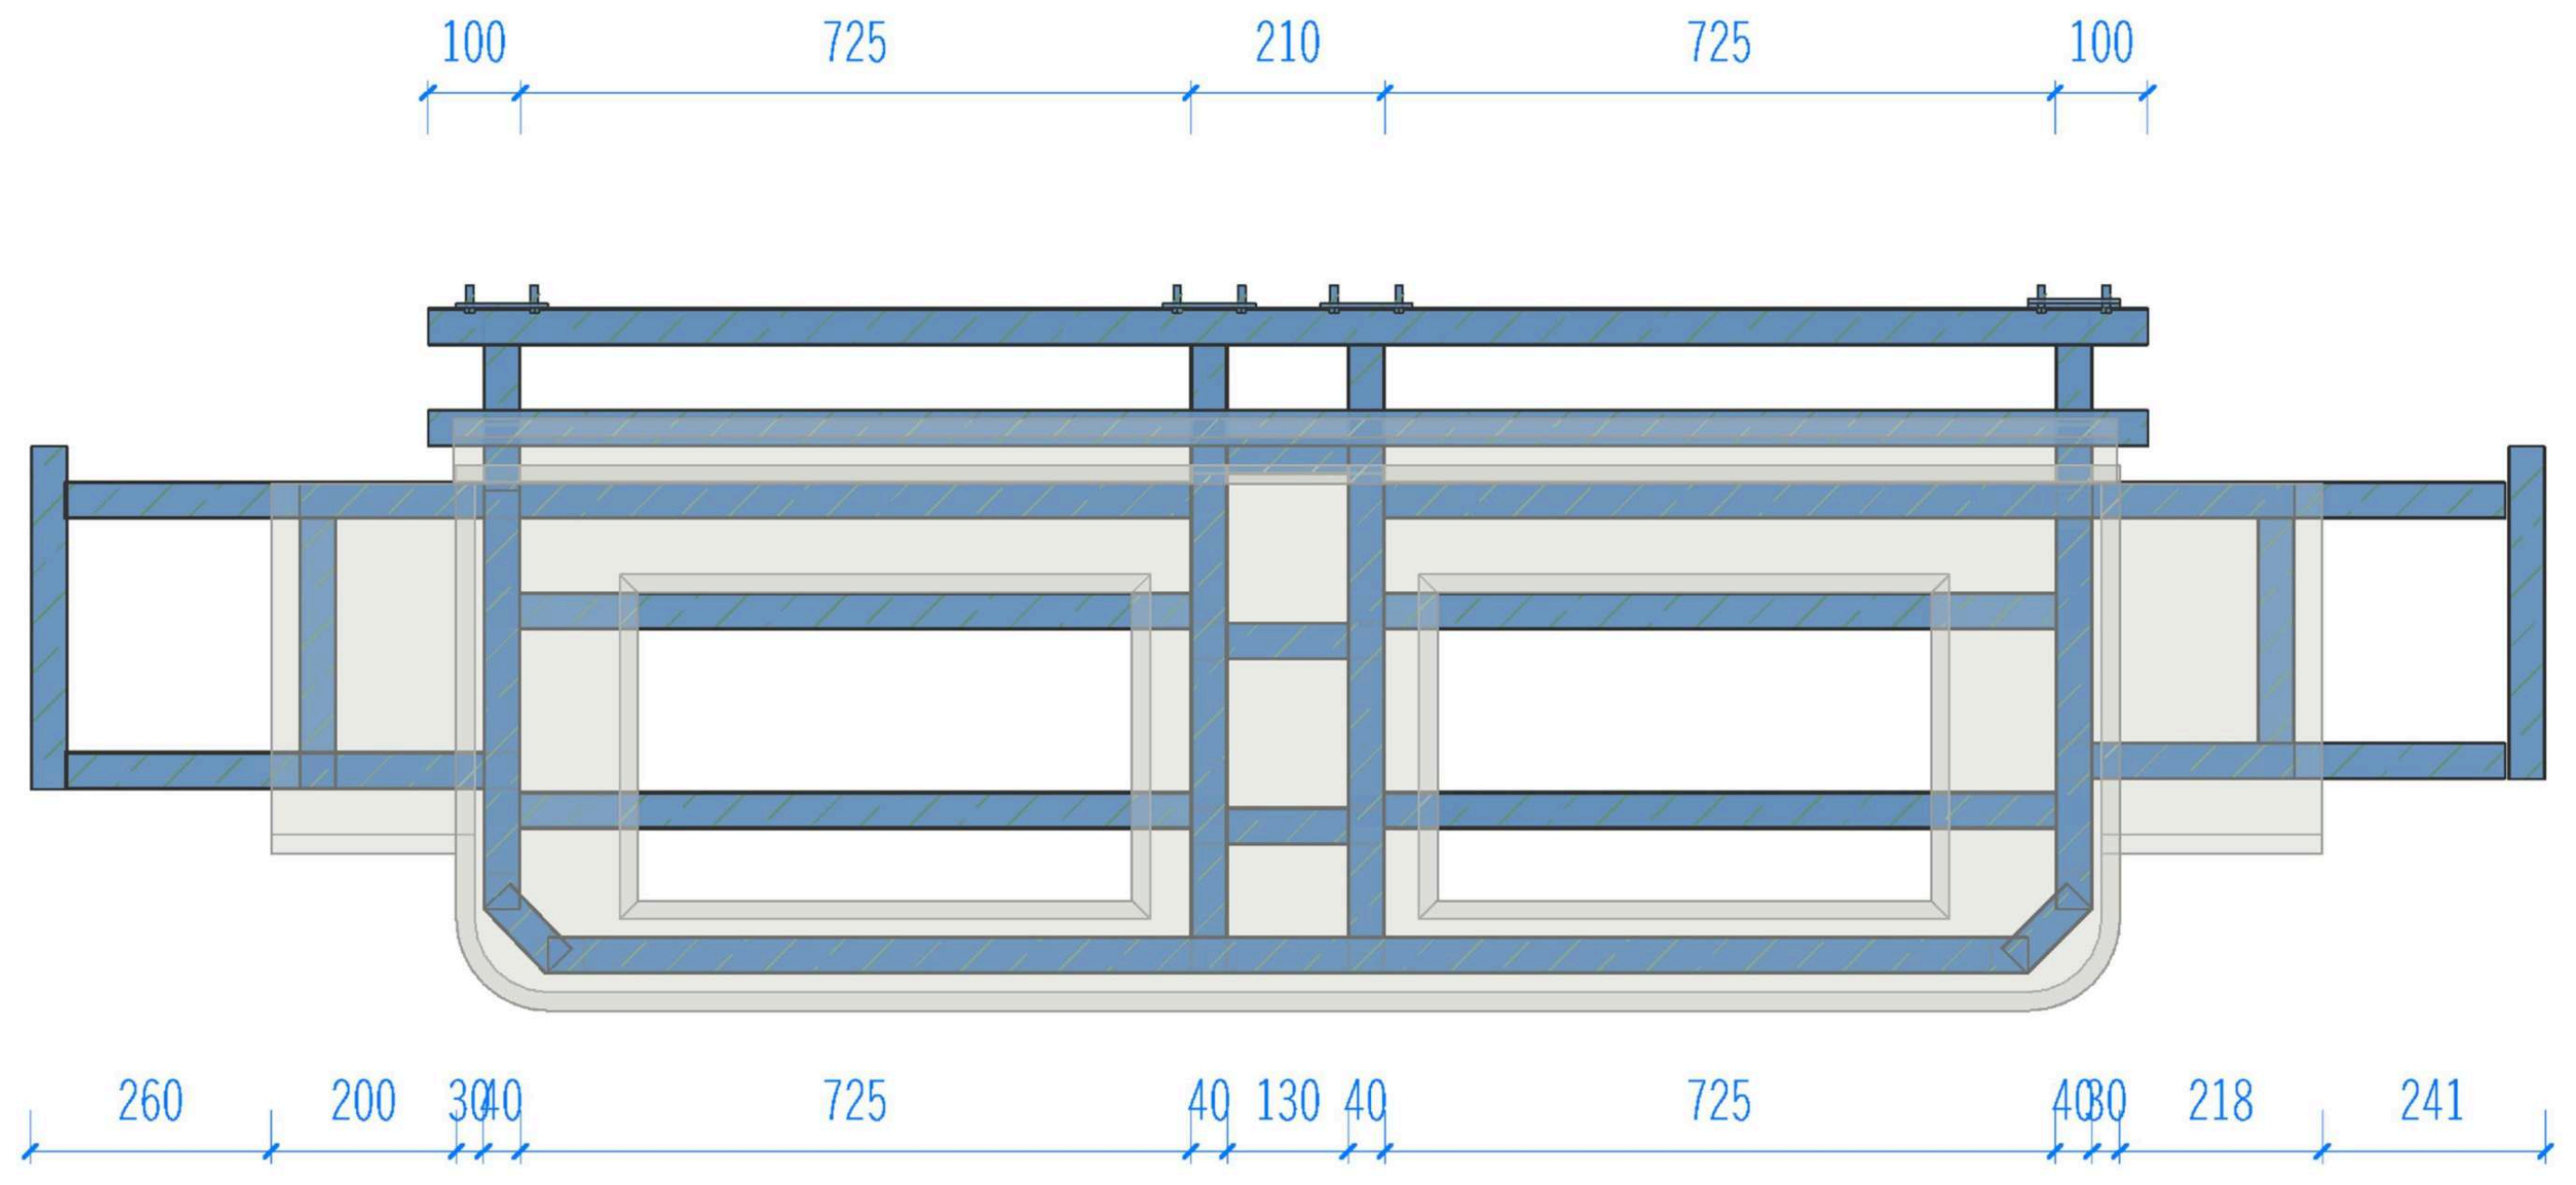
100
725
210
725
100
260
200
30
40
725
40
130
40
725
40
30
218
241

平面视图

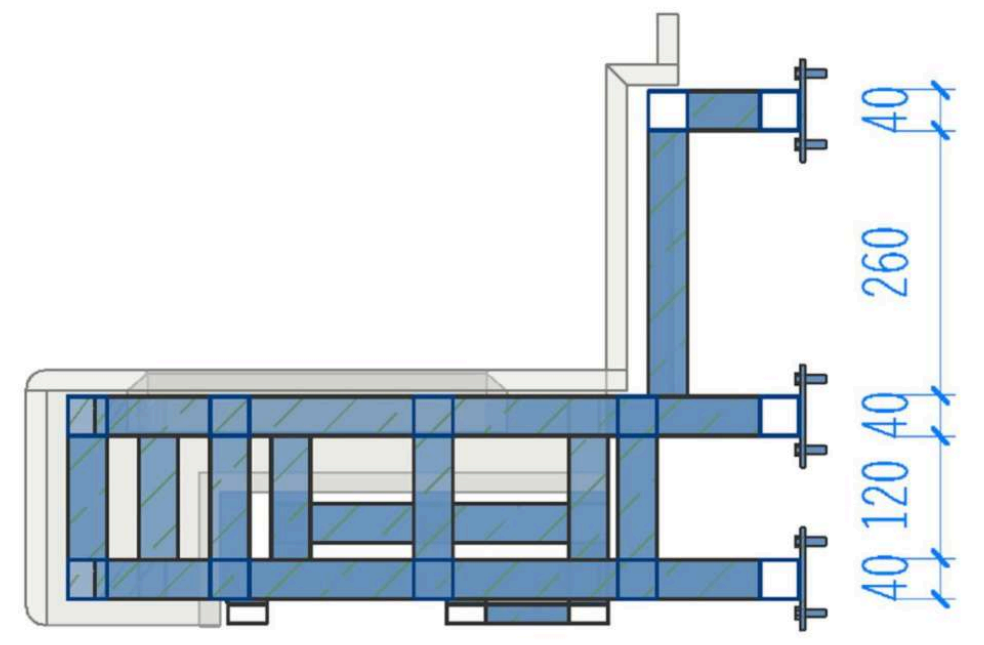
40
260
40
120
40

剖面视图

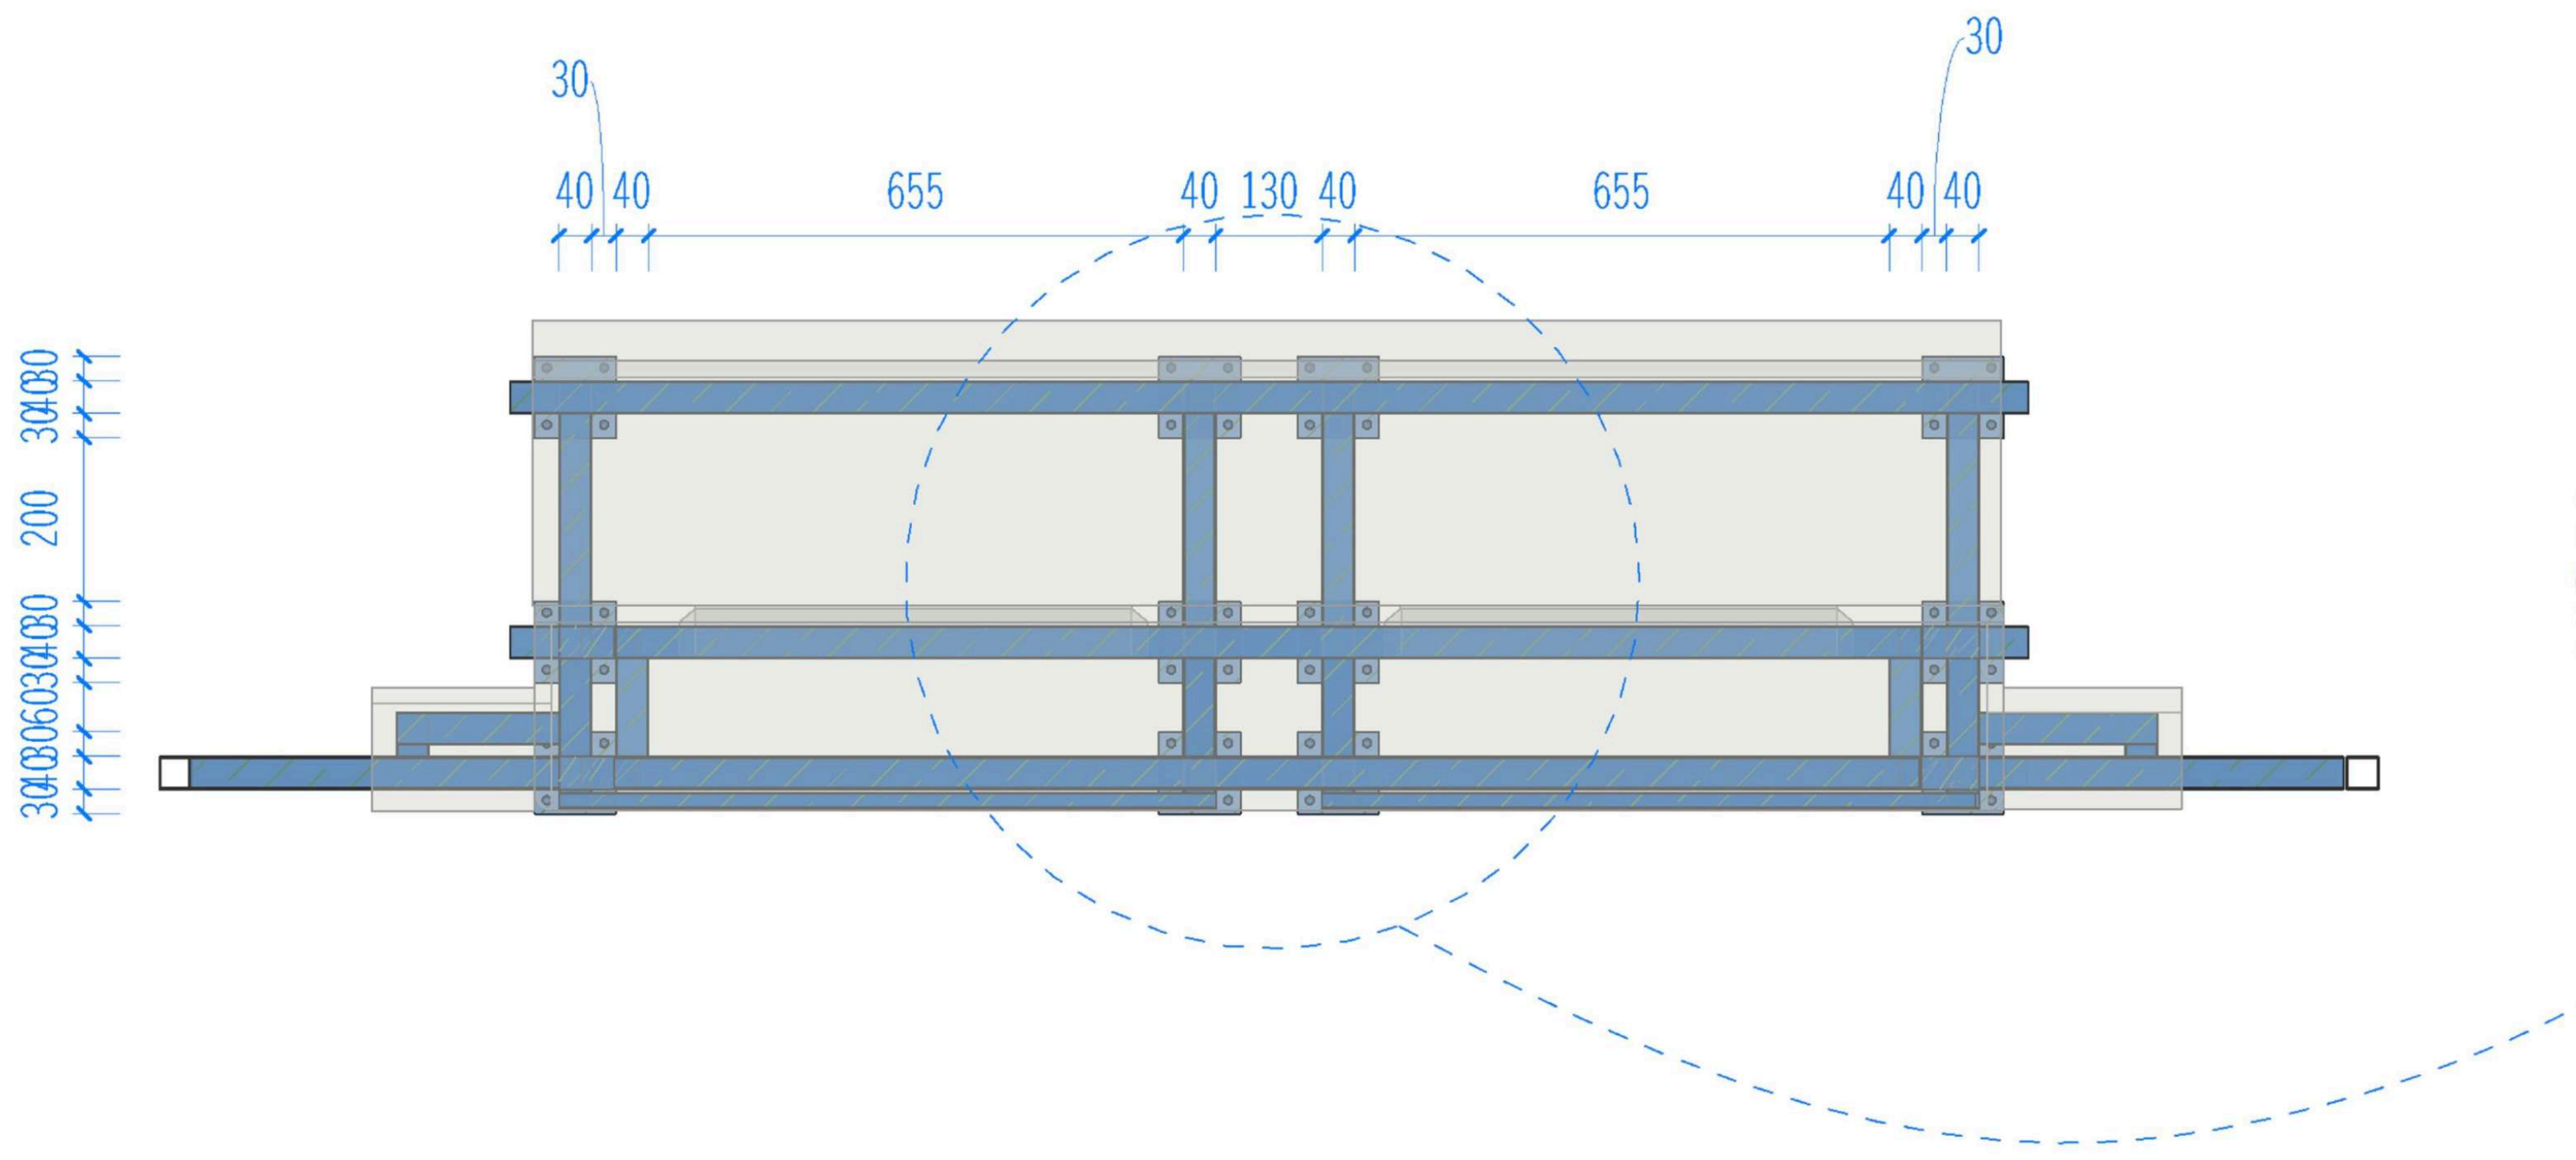
30
30
40
40
655
40
130
40
655
40
40
30
40
30
200

立面视图

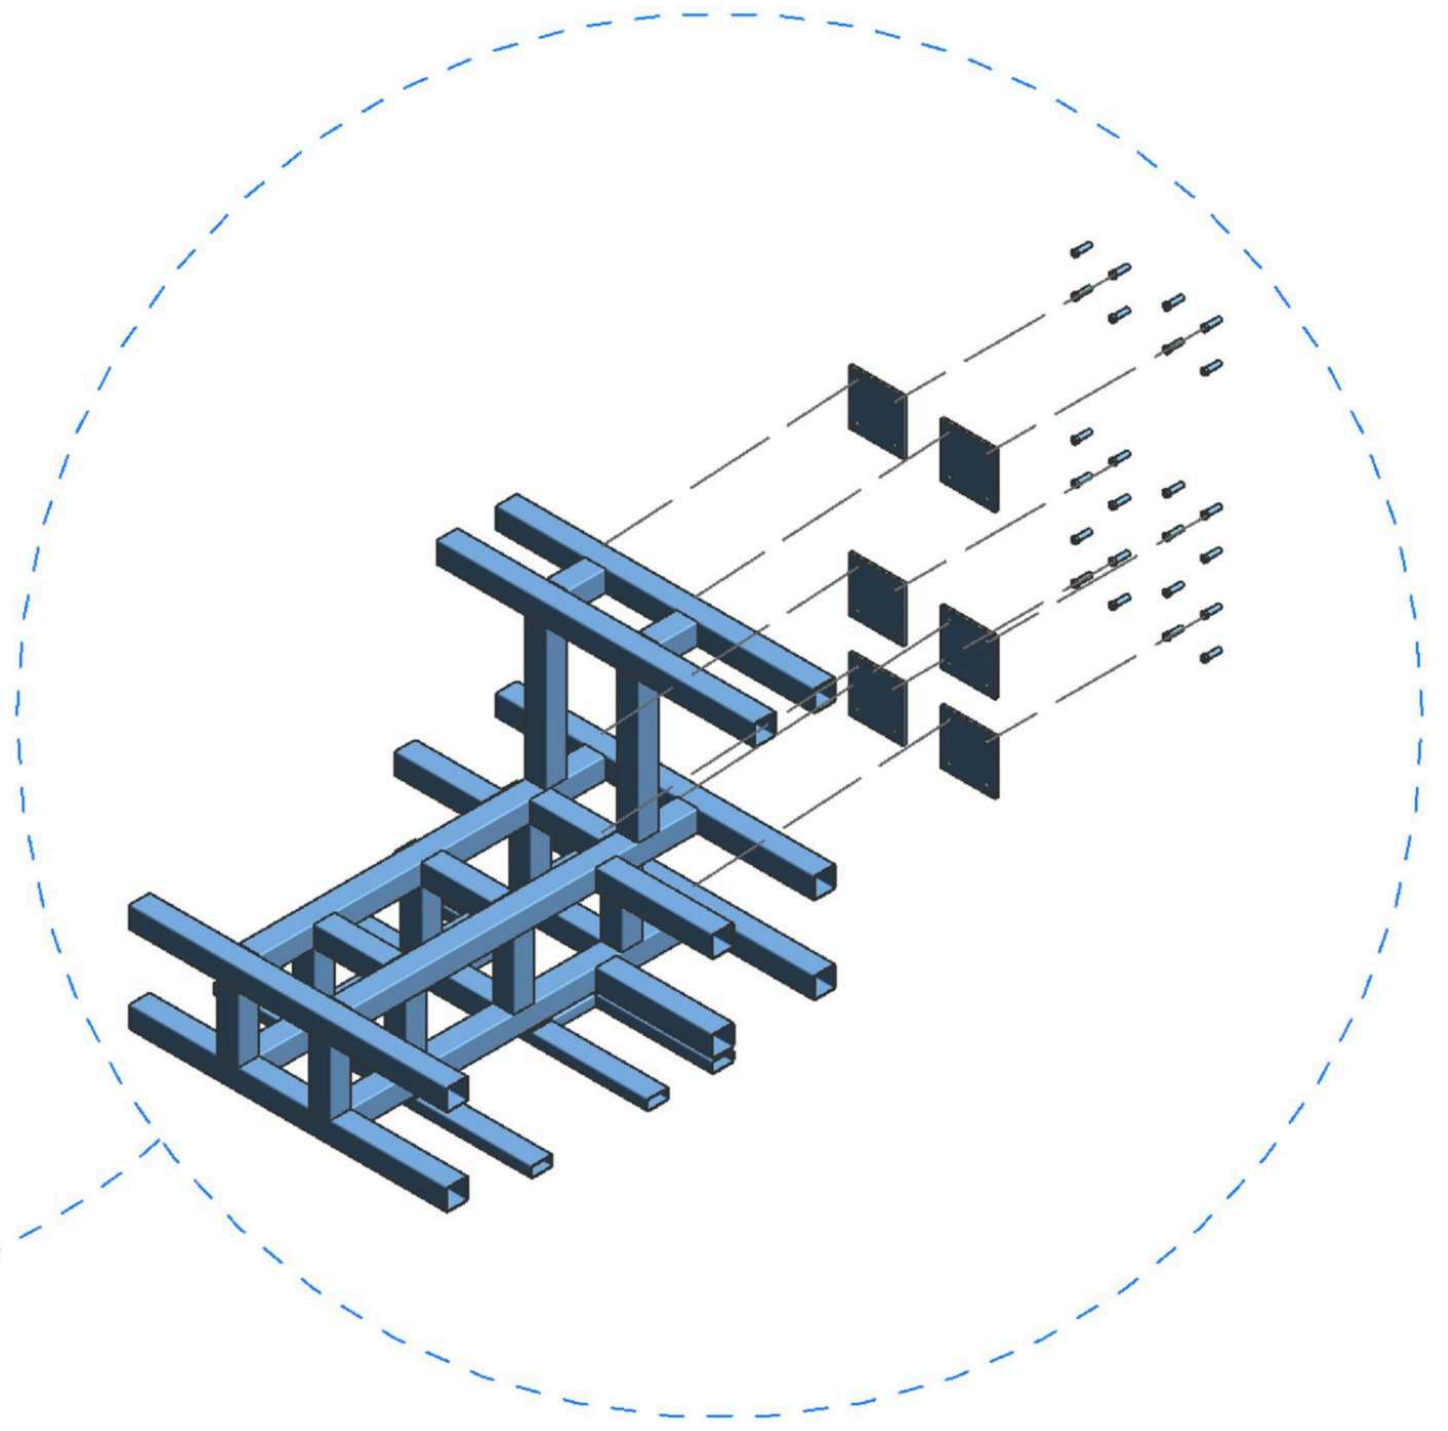

节点图

工厂预制钢架

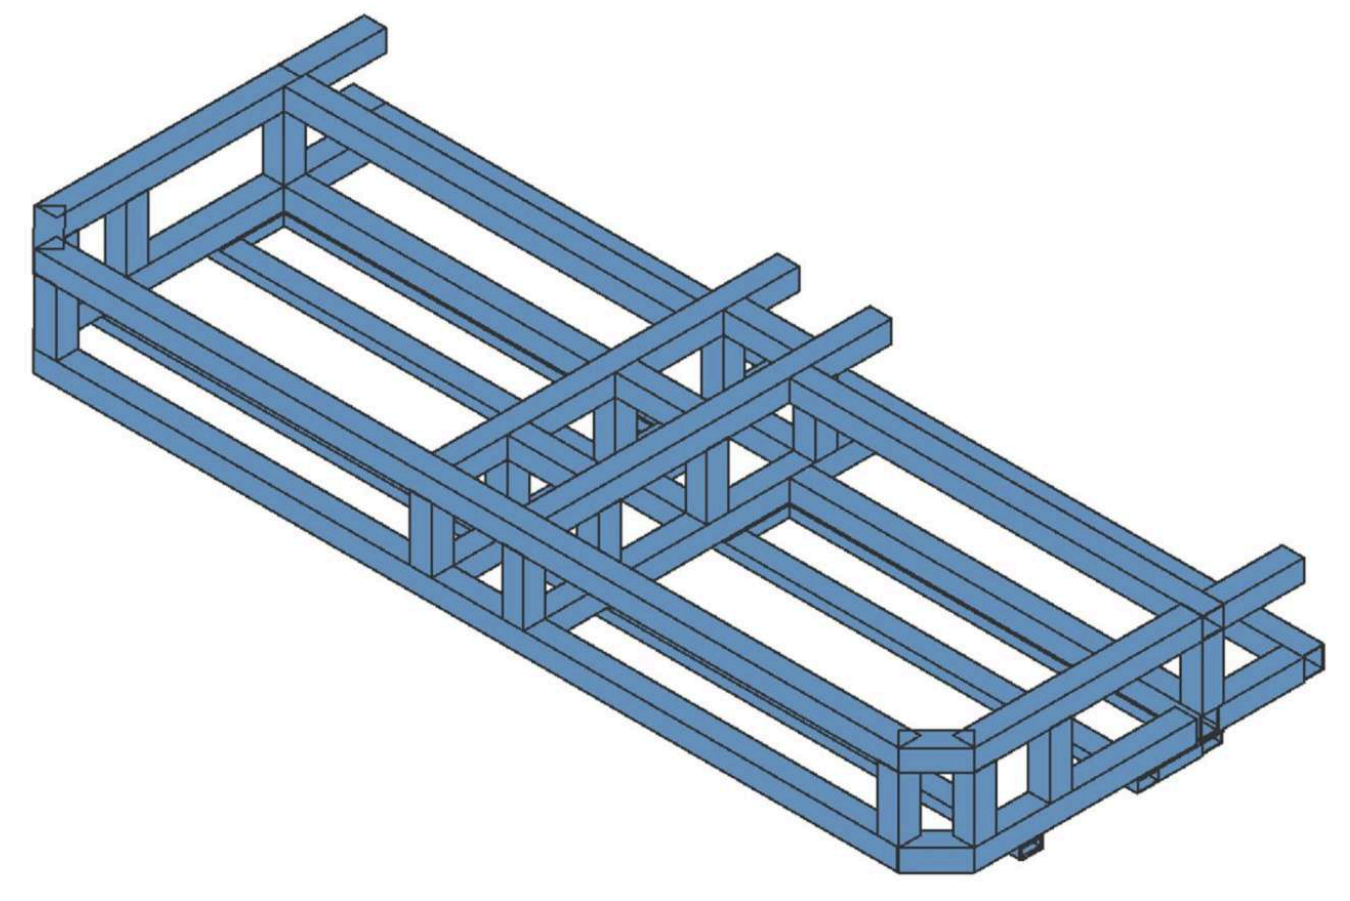

①

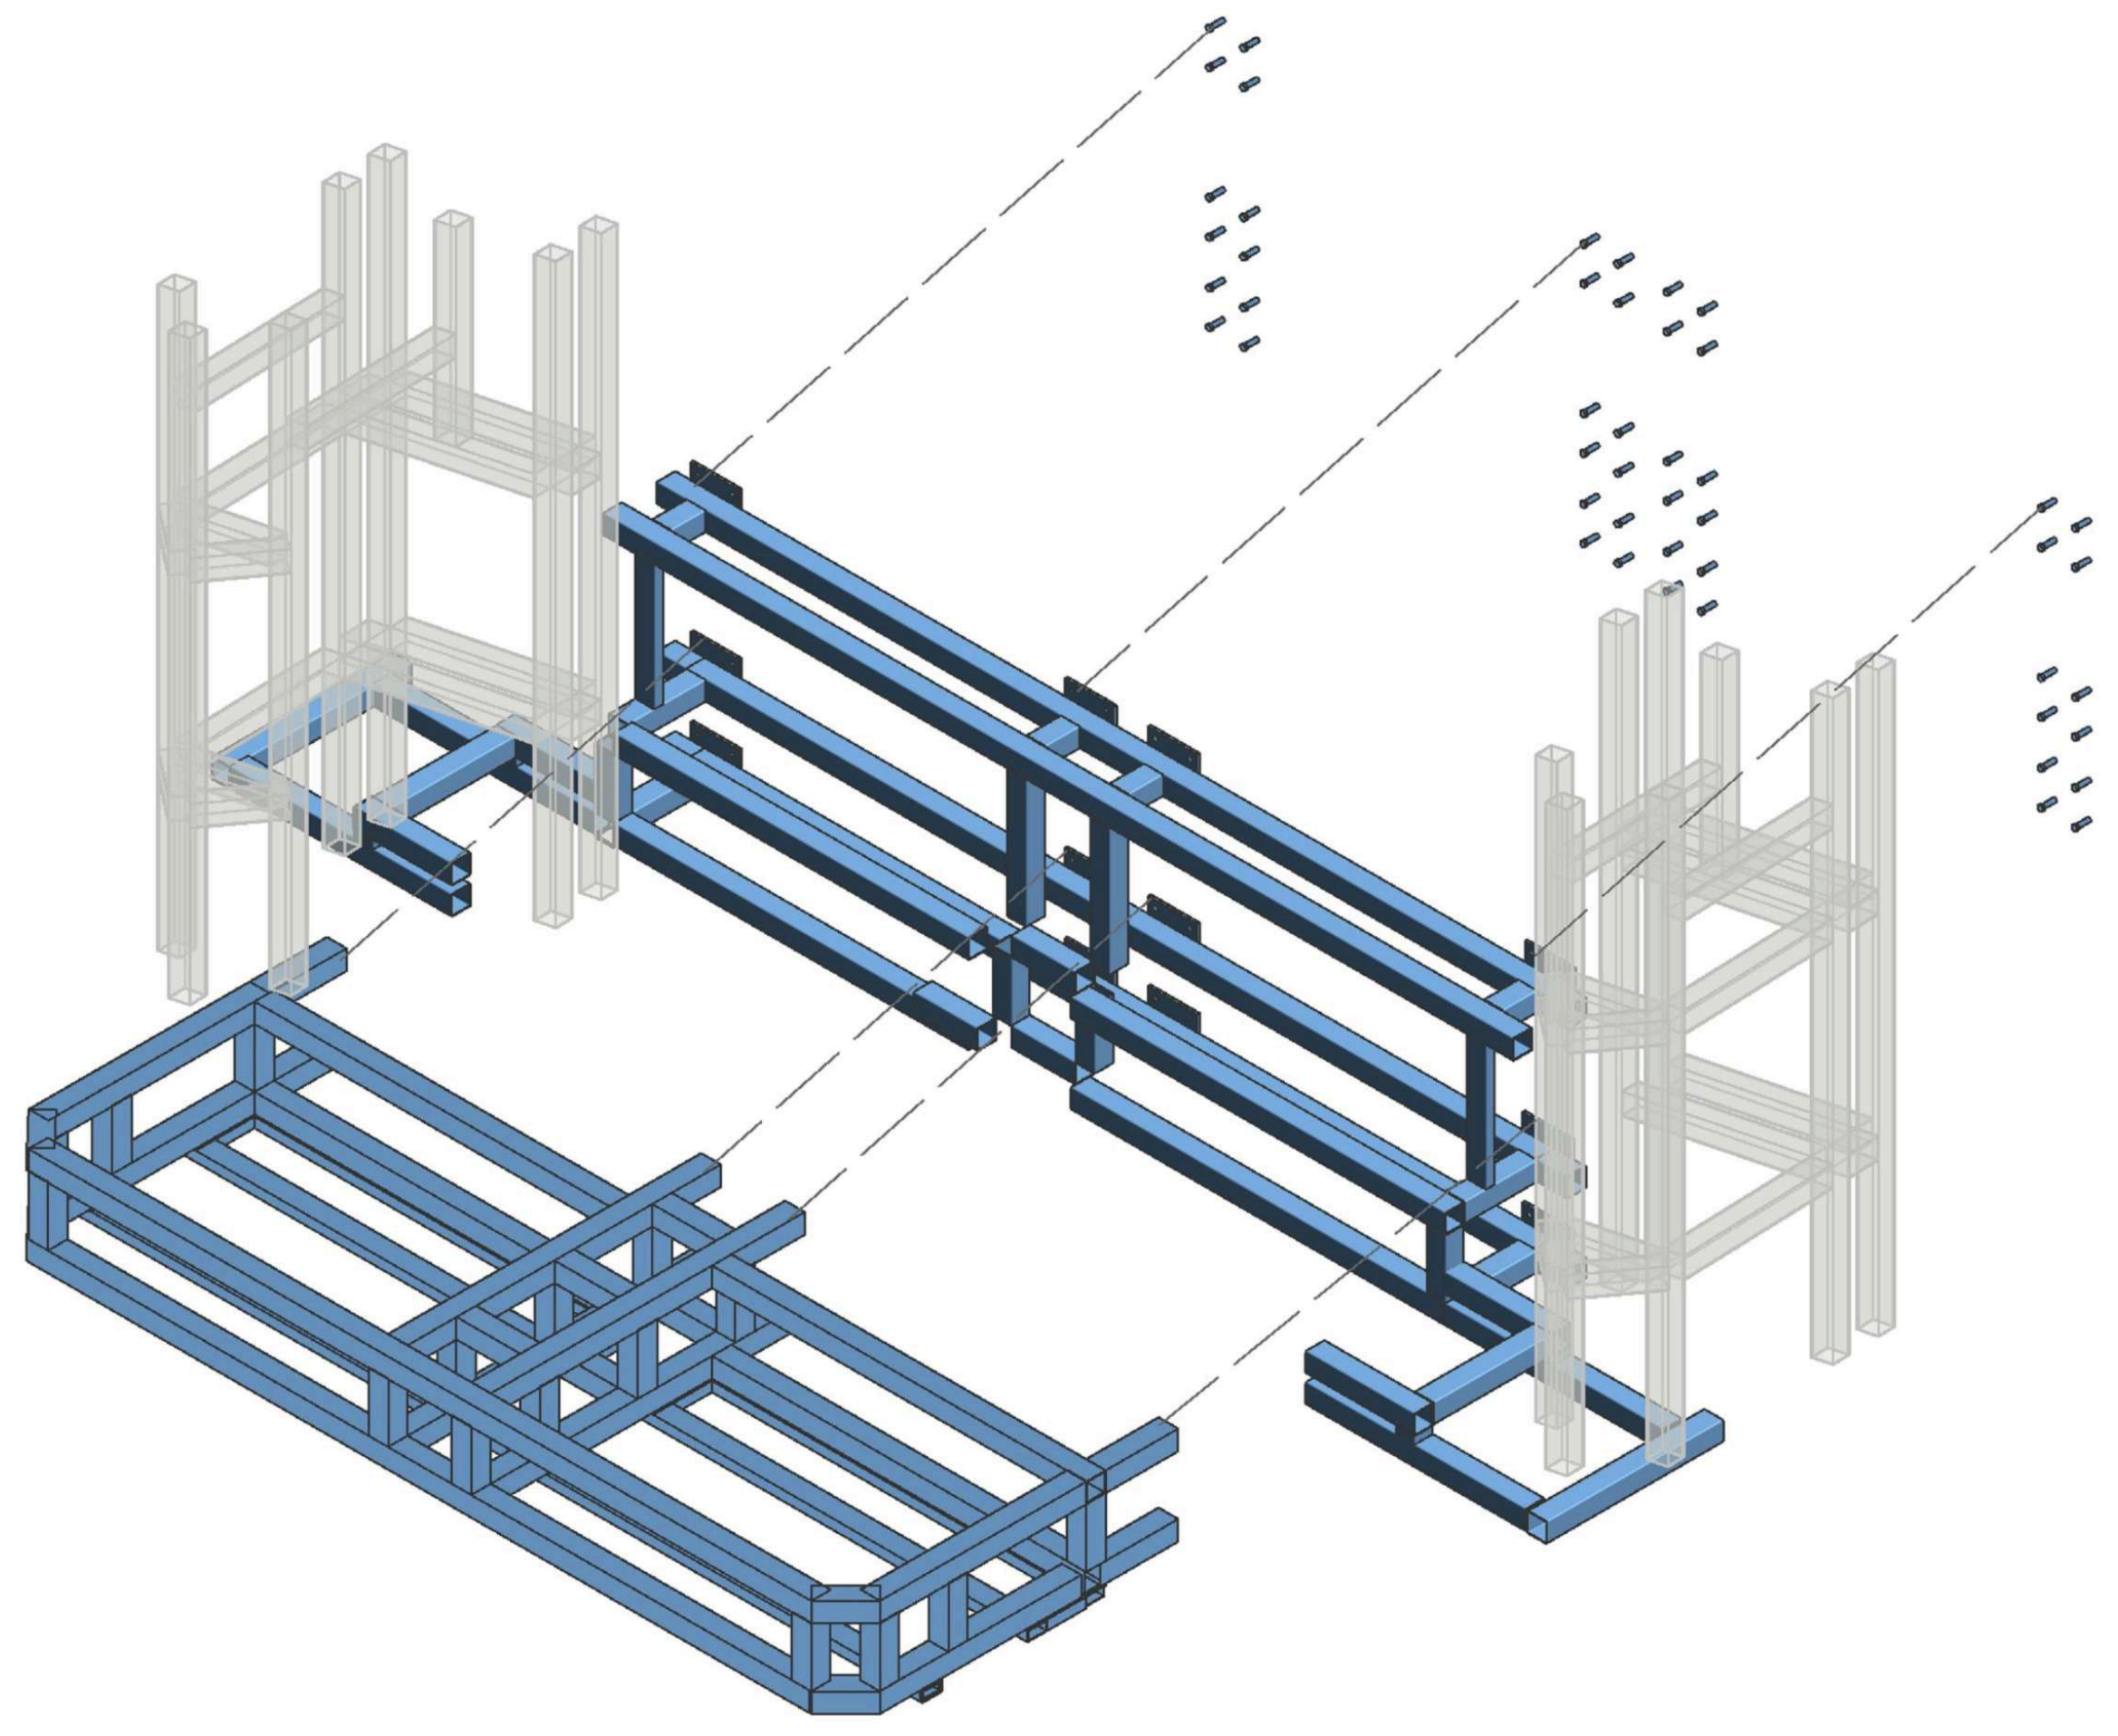

②

③

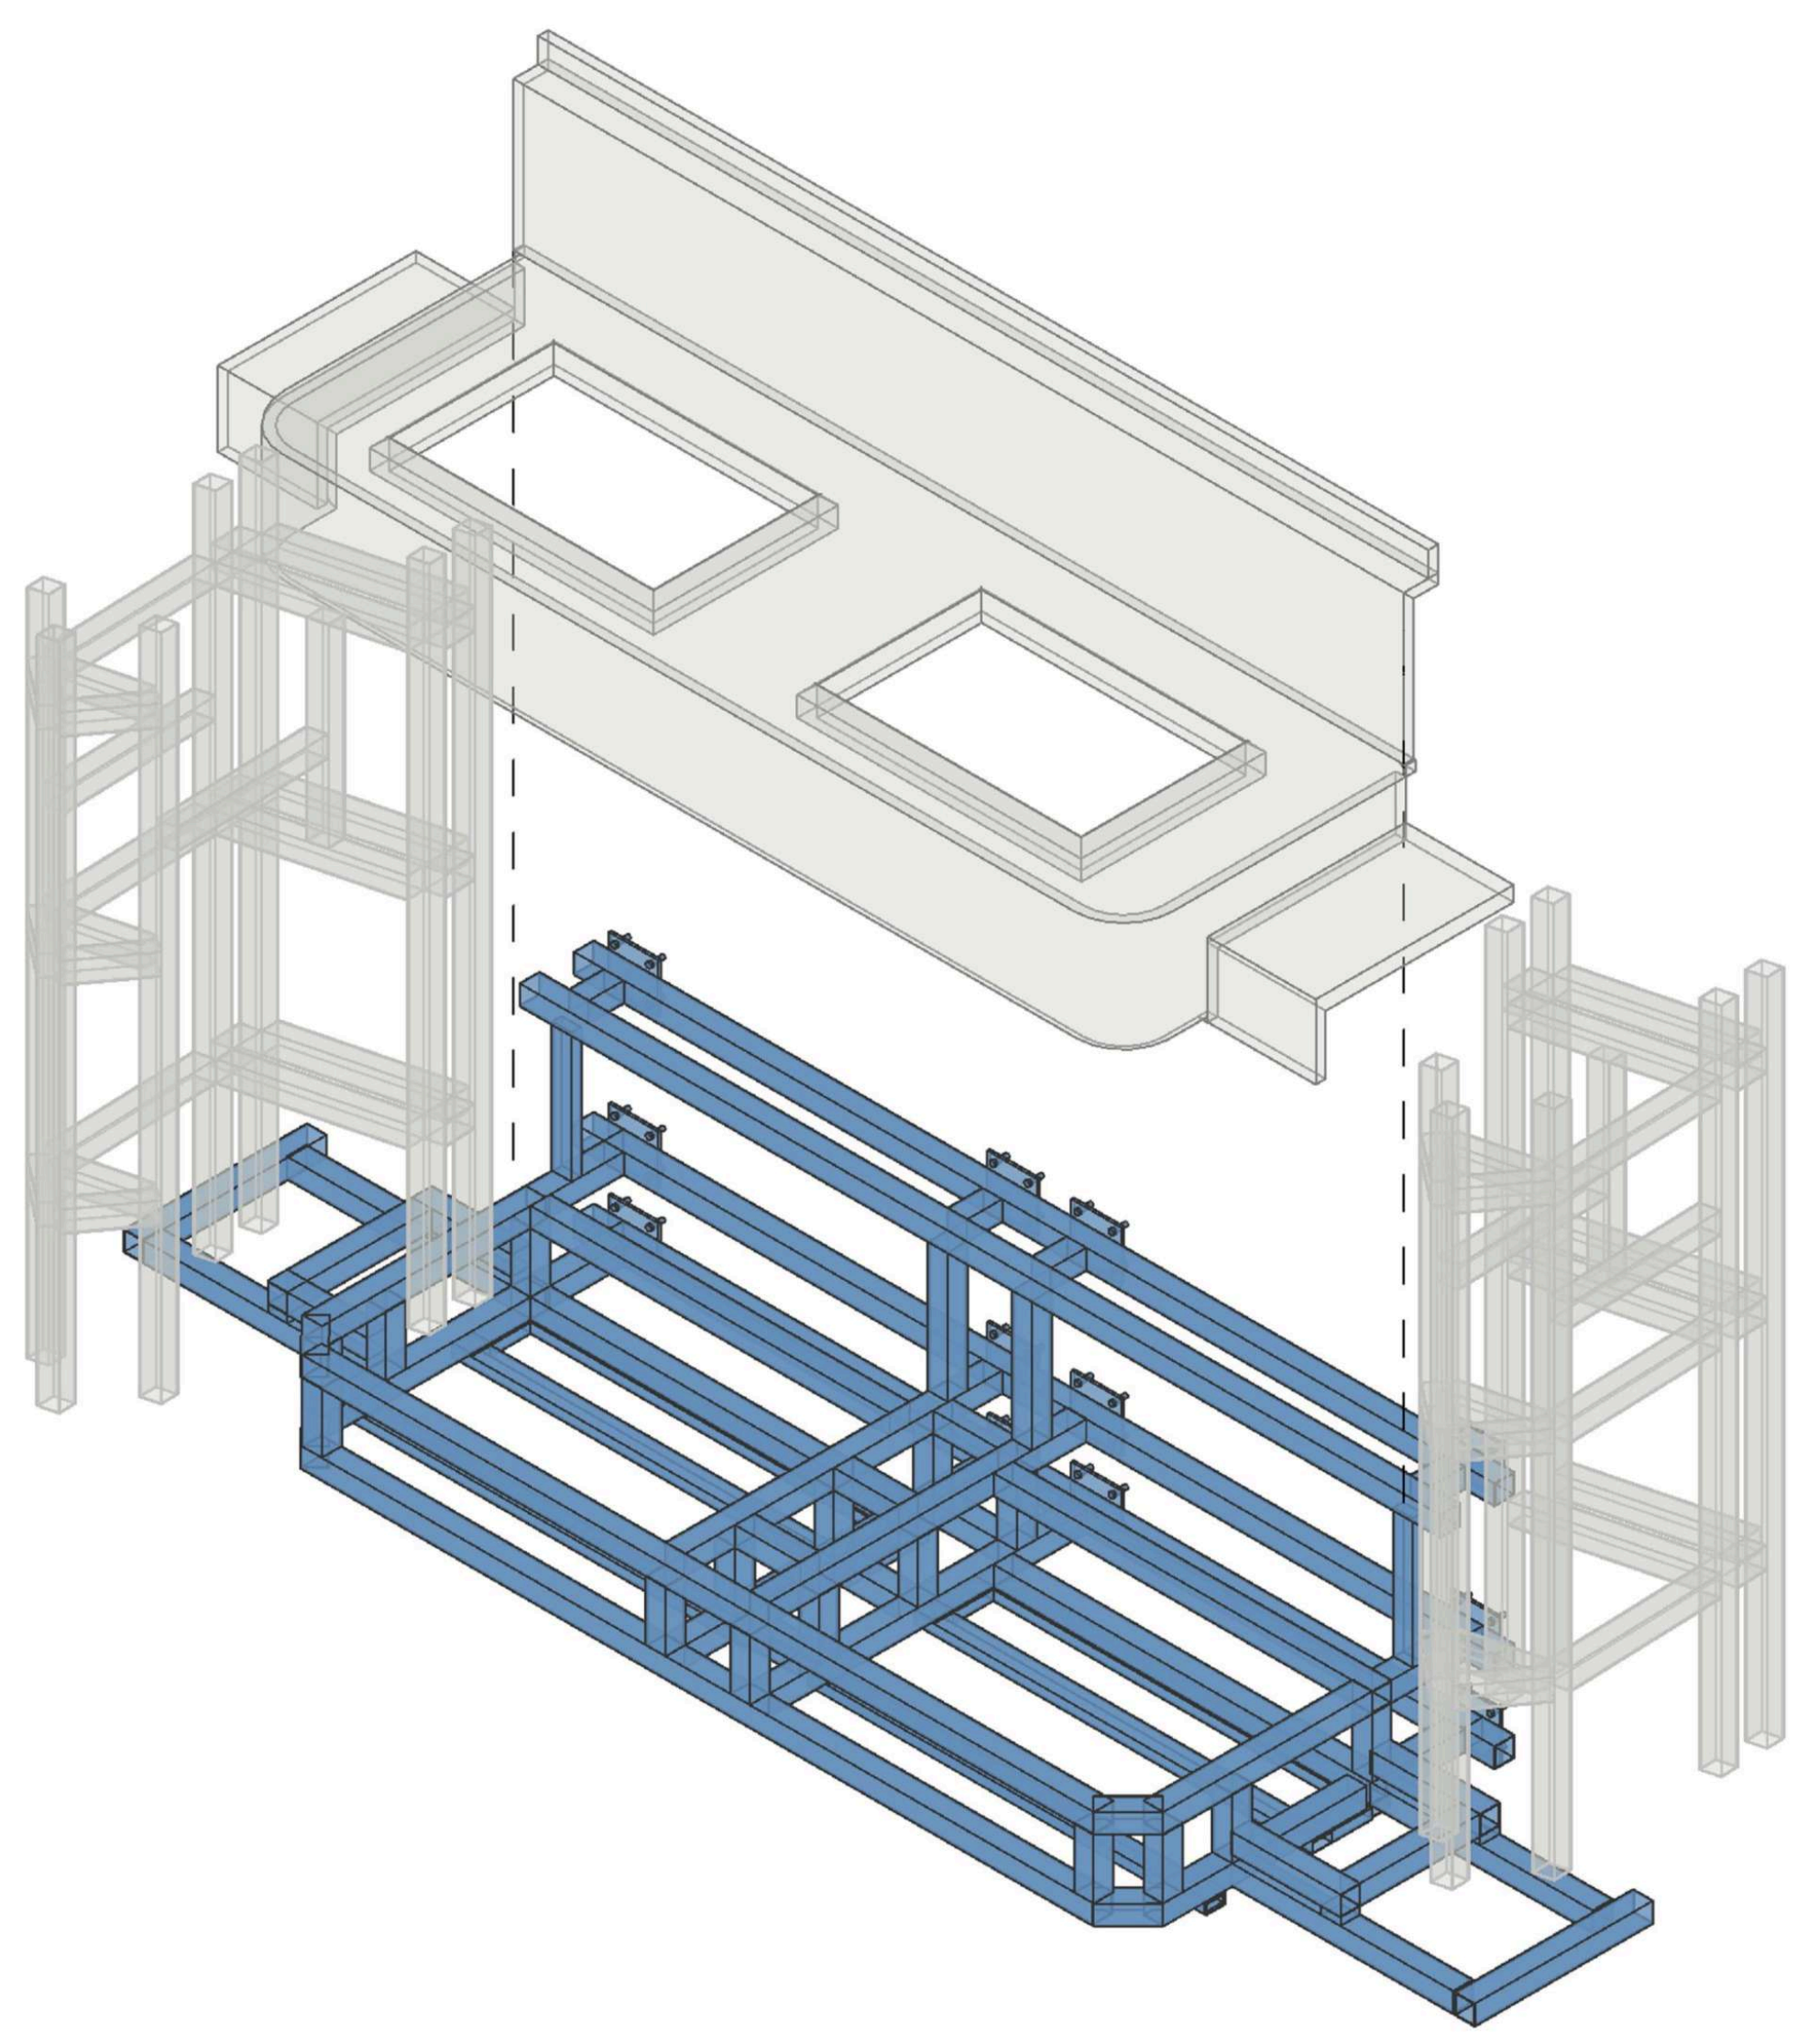

④

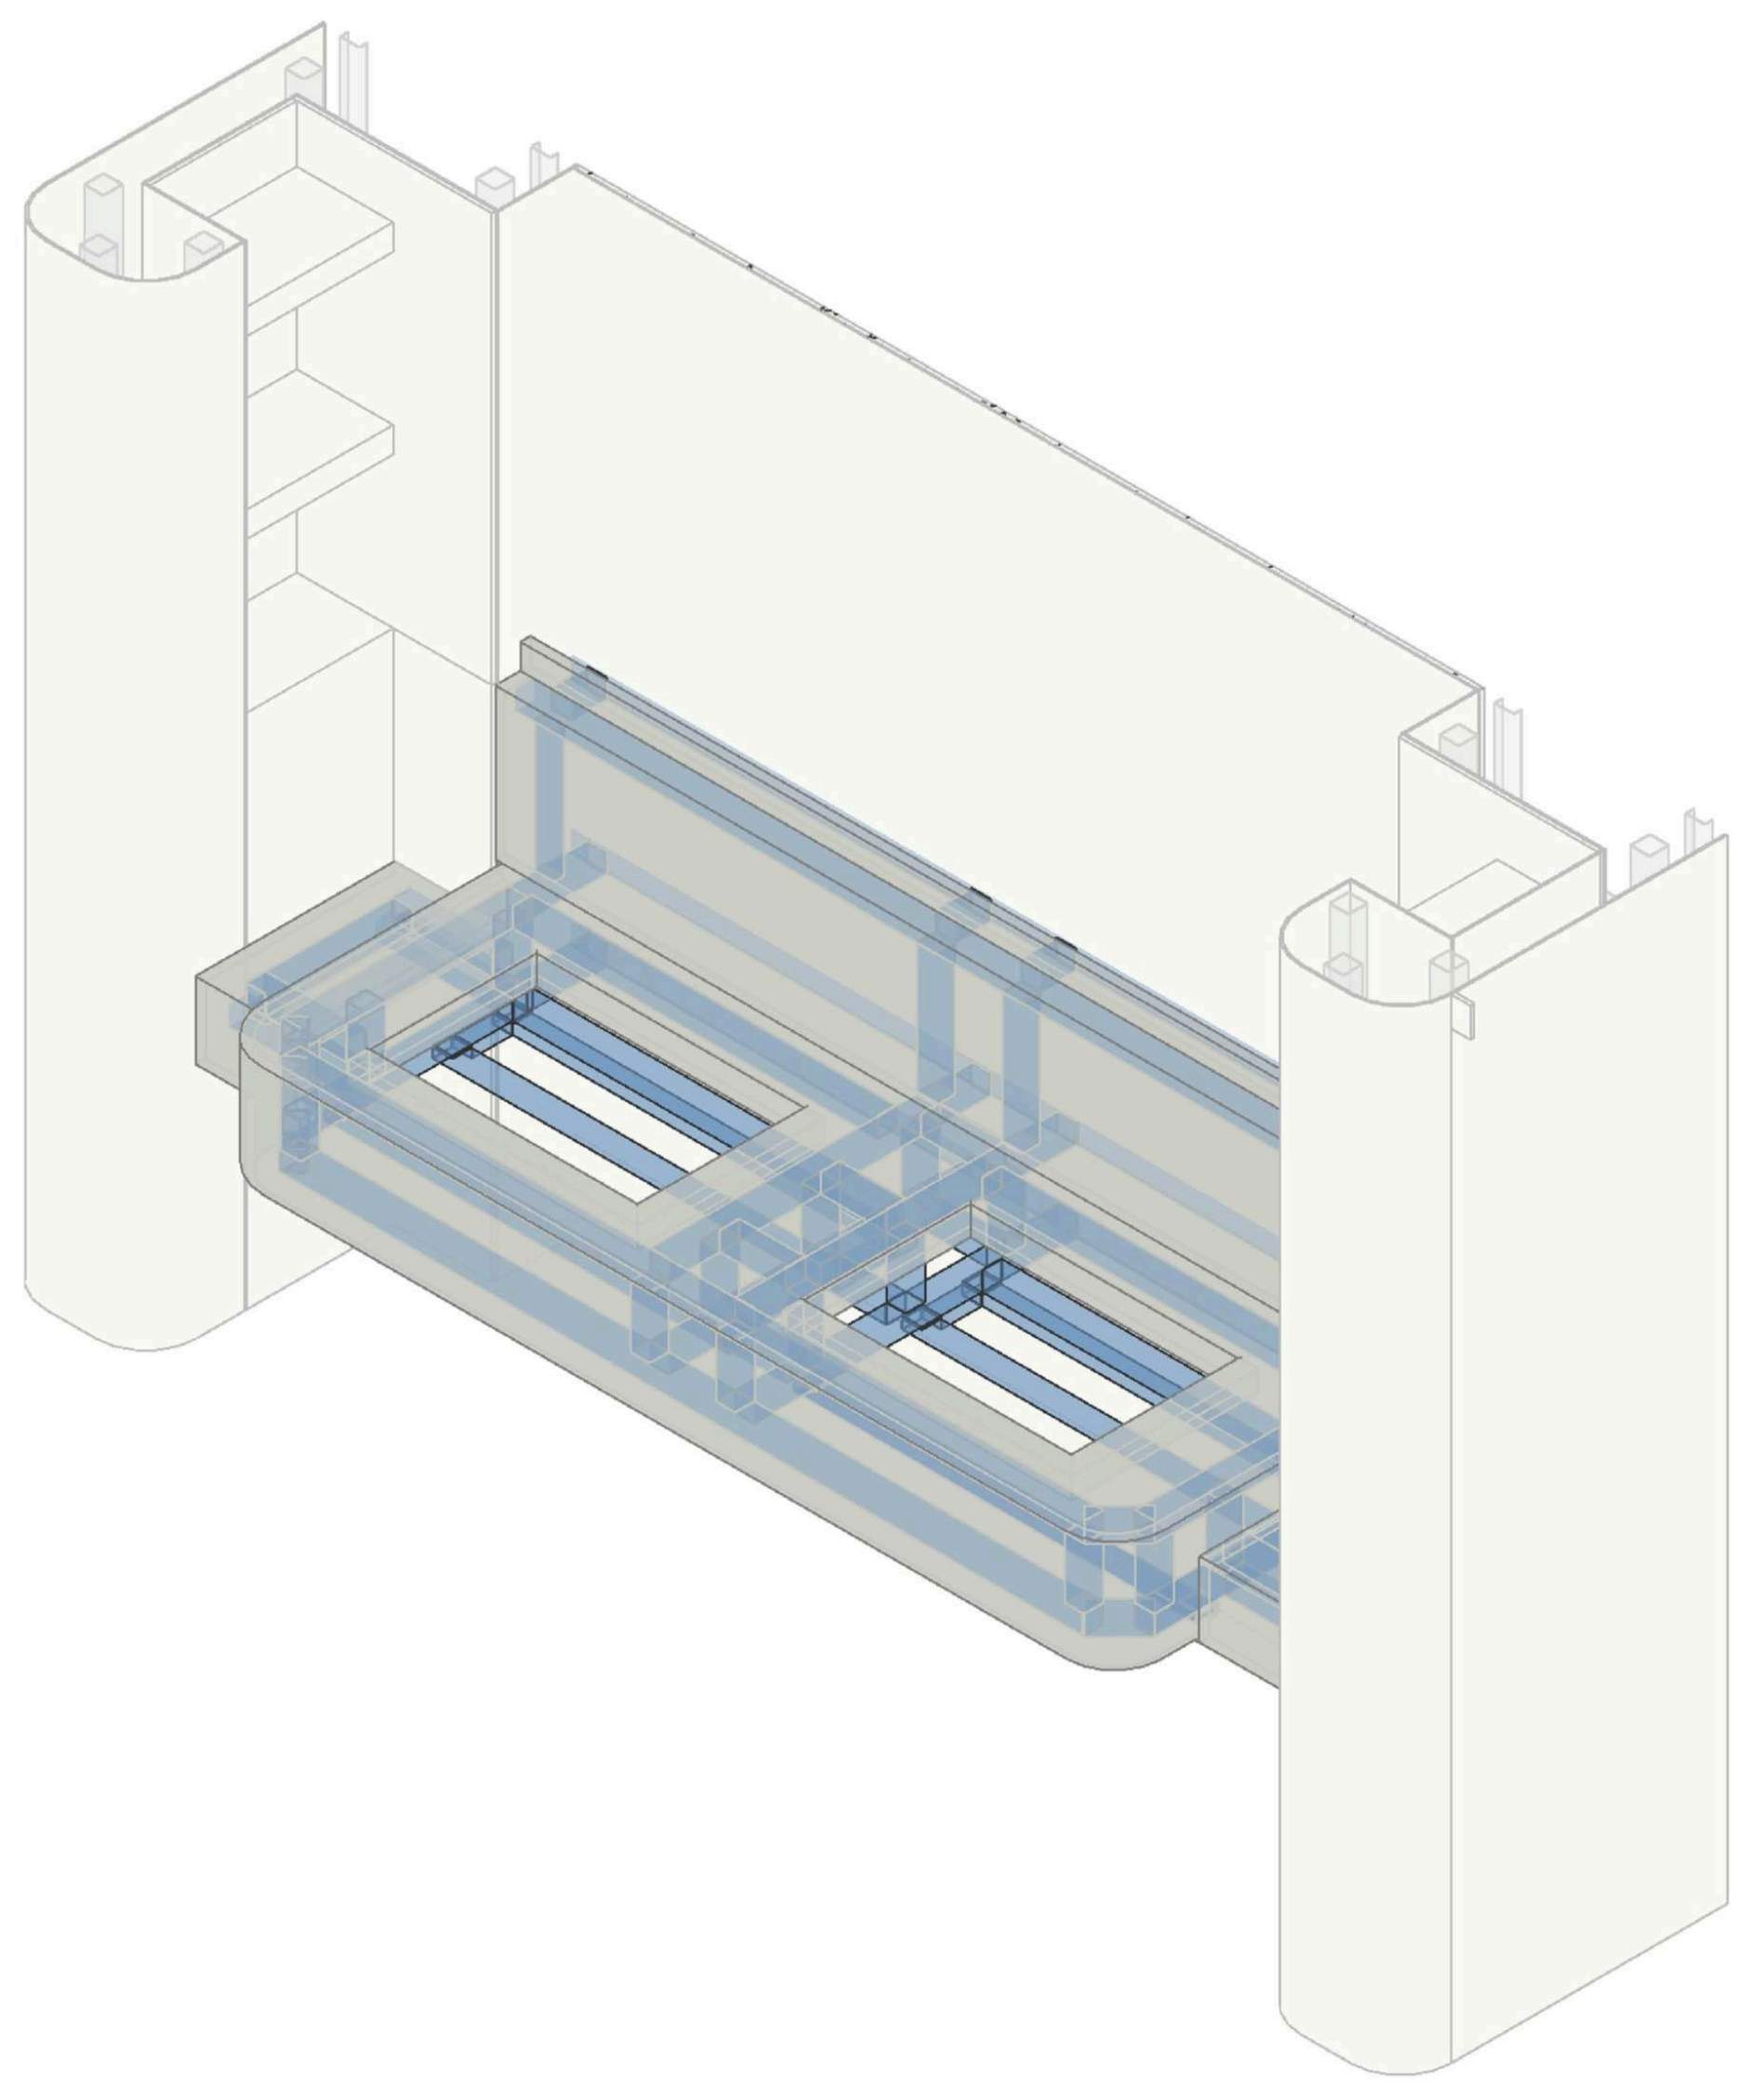

FIBORN

图例A
LEGEND A

编号	图例	说明
1		原始钢架
2		螺栓
3		钢片
4		钢架
5		石材

盖章

注释
Notes

1.本图纸如与现场尺寸有误，请施工人员与项目负责人联系。
2.施工前施工人员应认真查阅此图，如有不明确尺寸，按现场测量为准。
3.本图纸必须经甲乙双方认可并签字方可作为施工依据。

日期
Date 05/07/26

修订
Revision

△1

项目
Project
潮映华岸府3-801

比例
Scale

主卫洗手台石材钢架

图纸编号
Drawing No.
ST-01

项目编号
Project No.

©2025

1

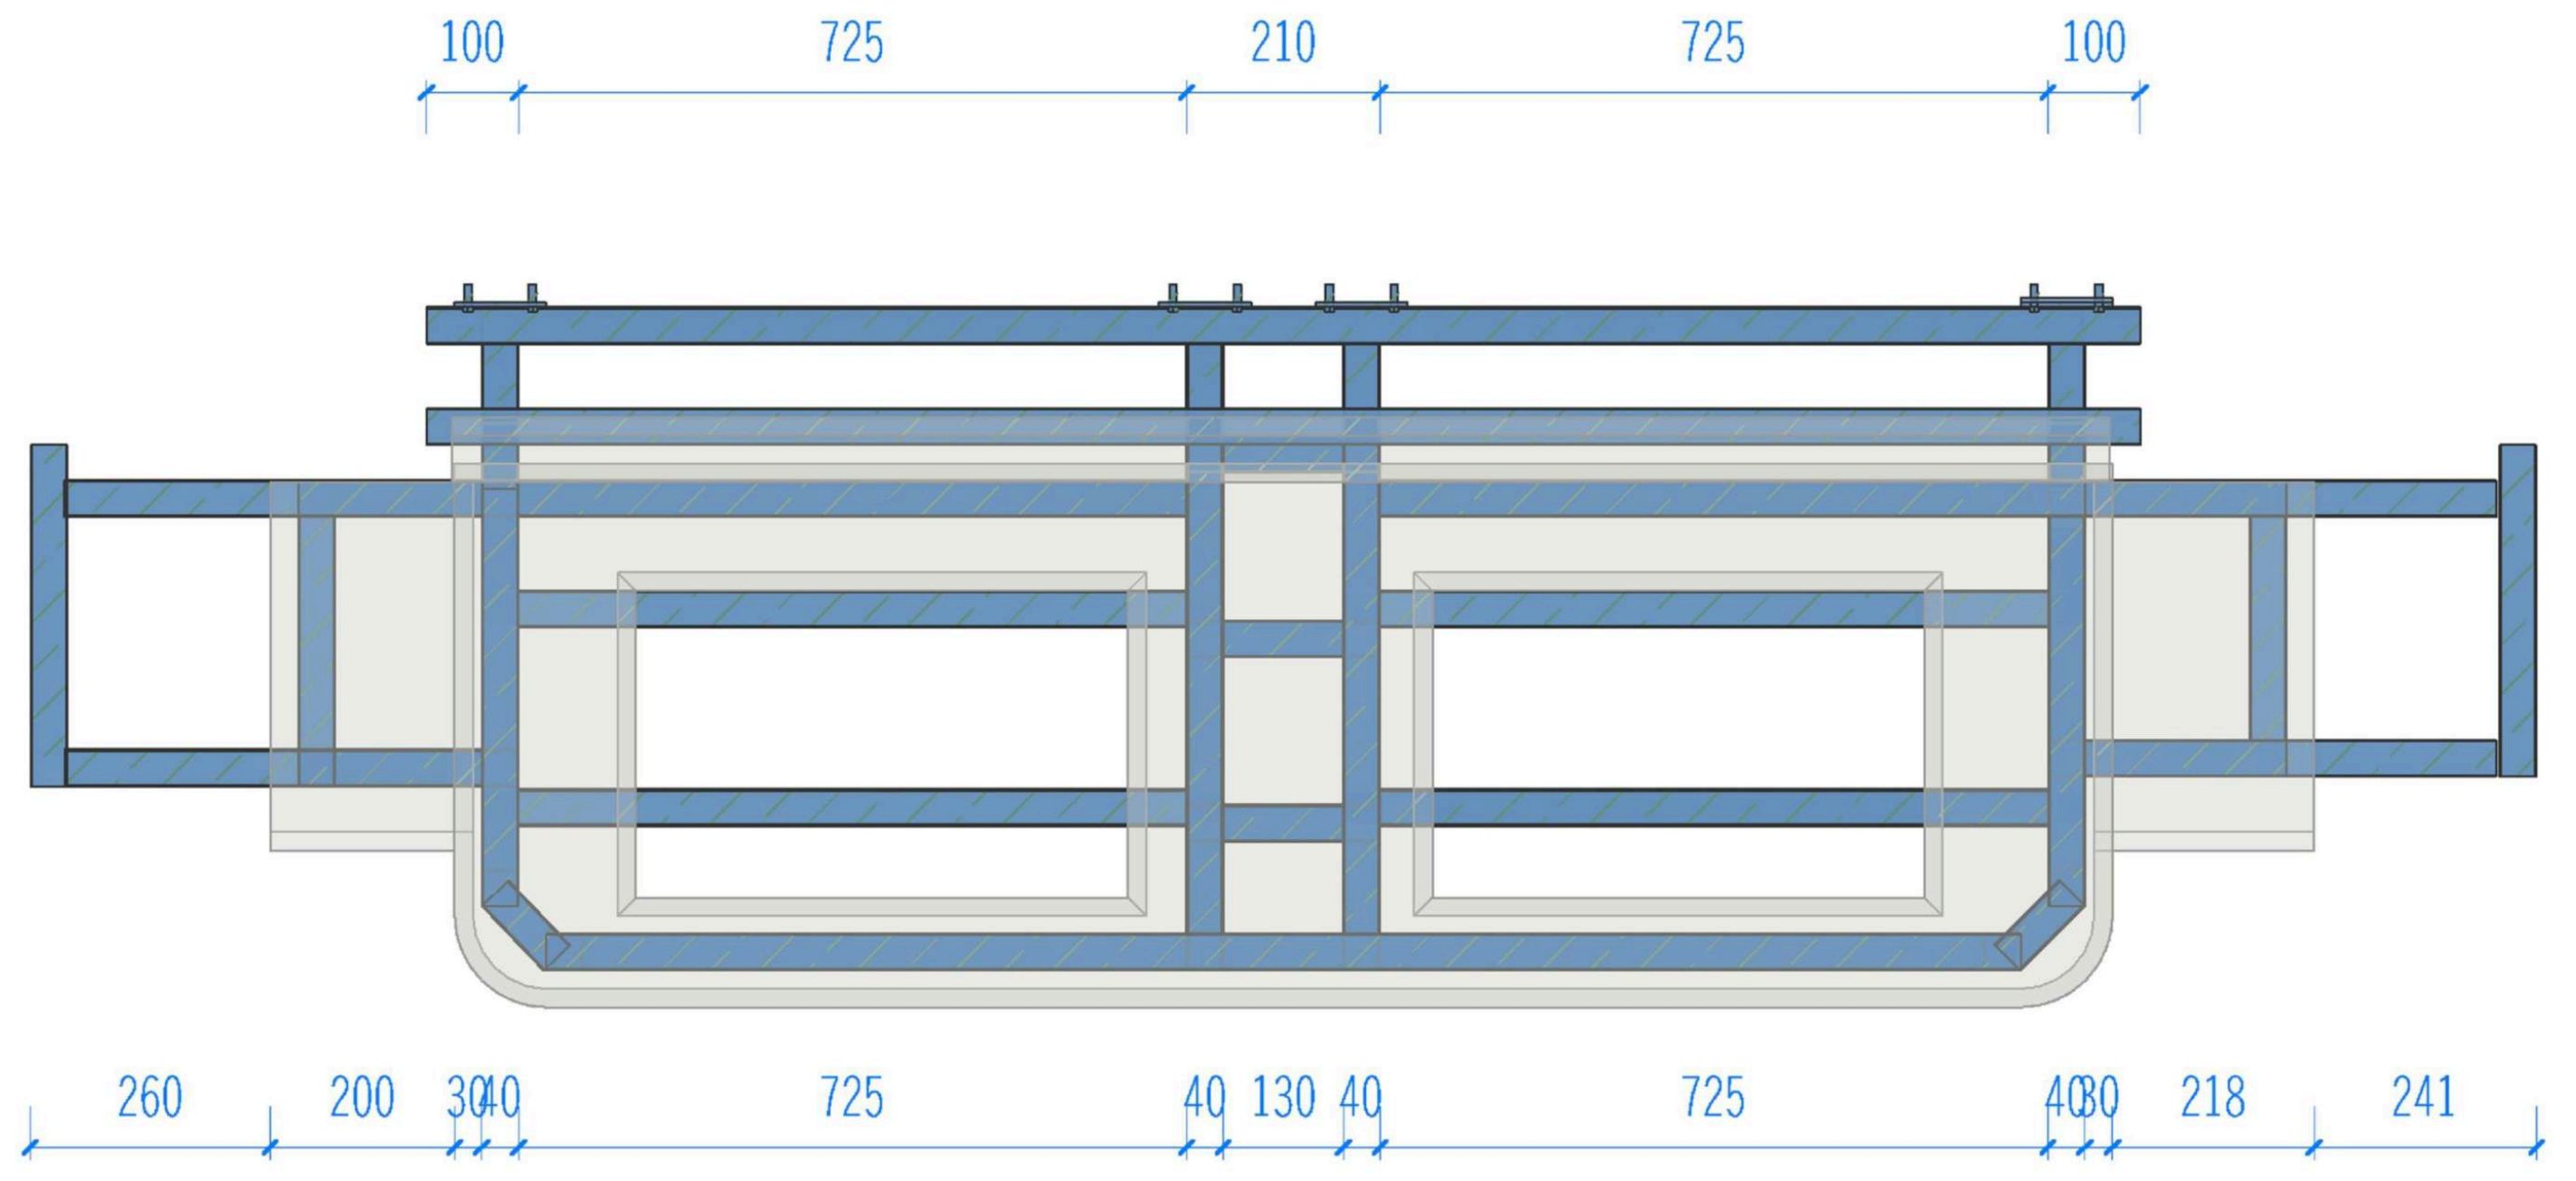
100
725
210
725
100
260
200
30
40
725
40
130
40
725
40
30
218
241

平面视图

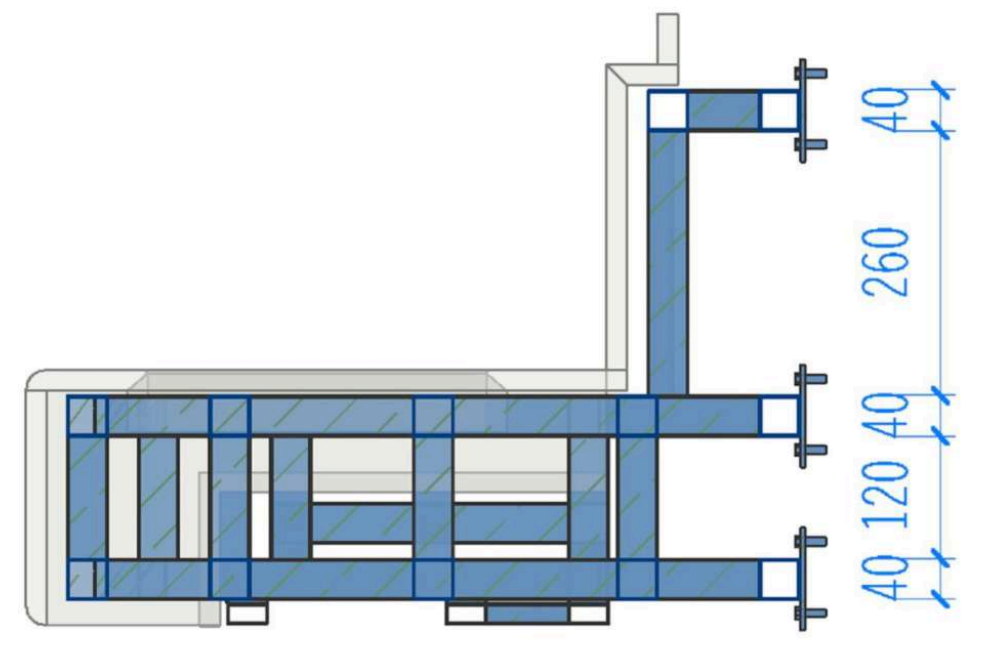
40
260
40
120
40

剖面视图

工厂预制钢架

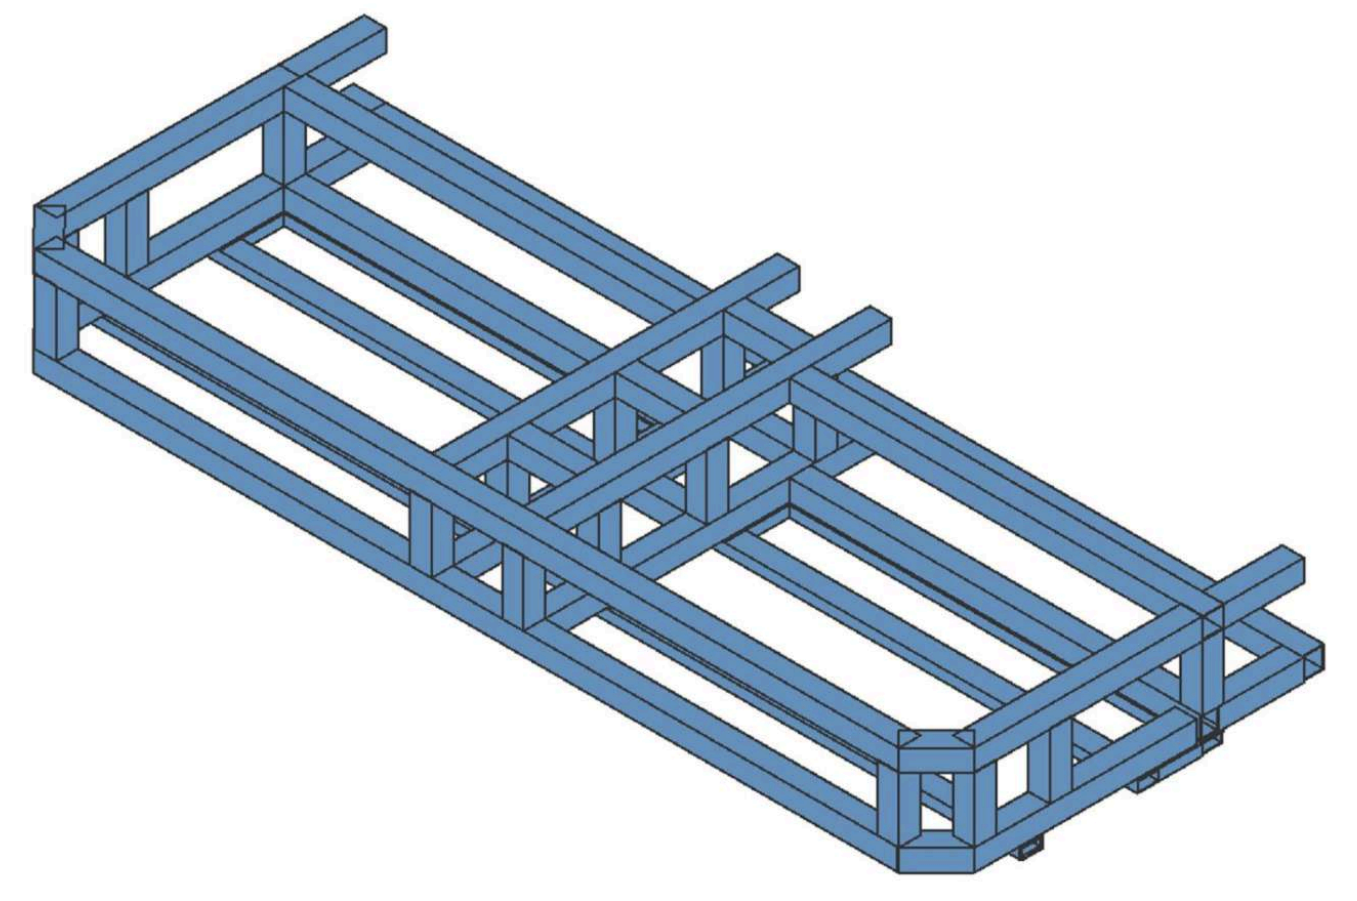

①

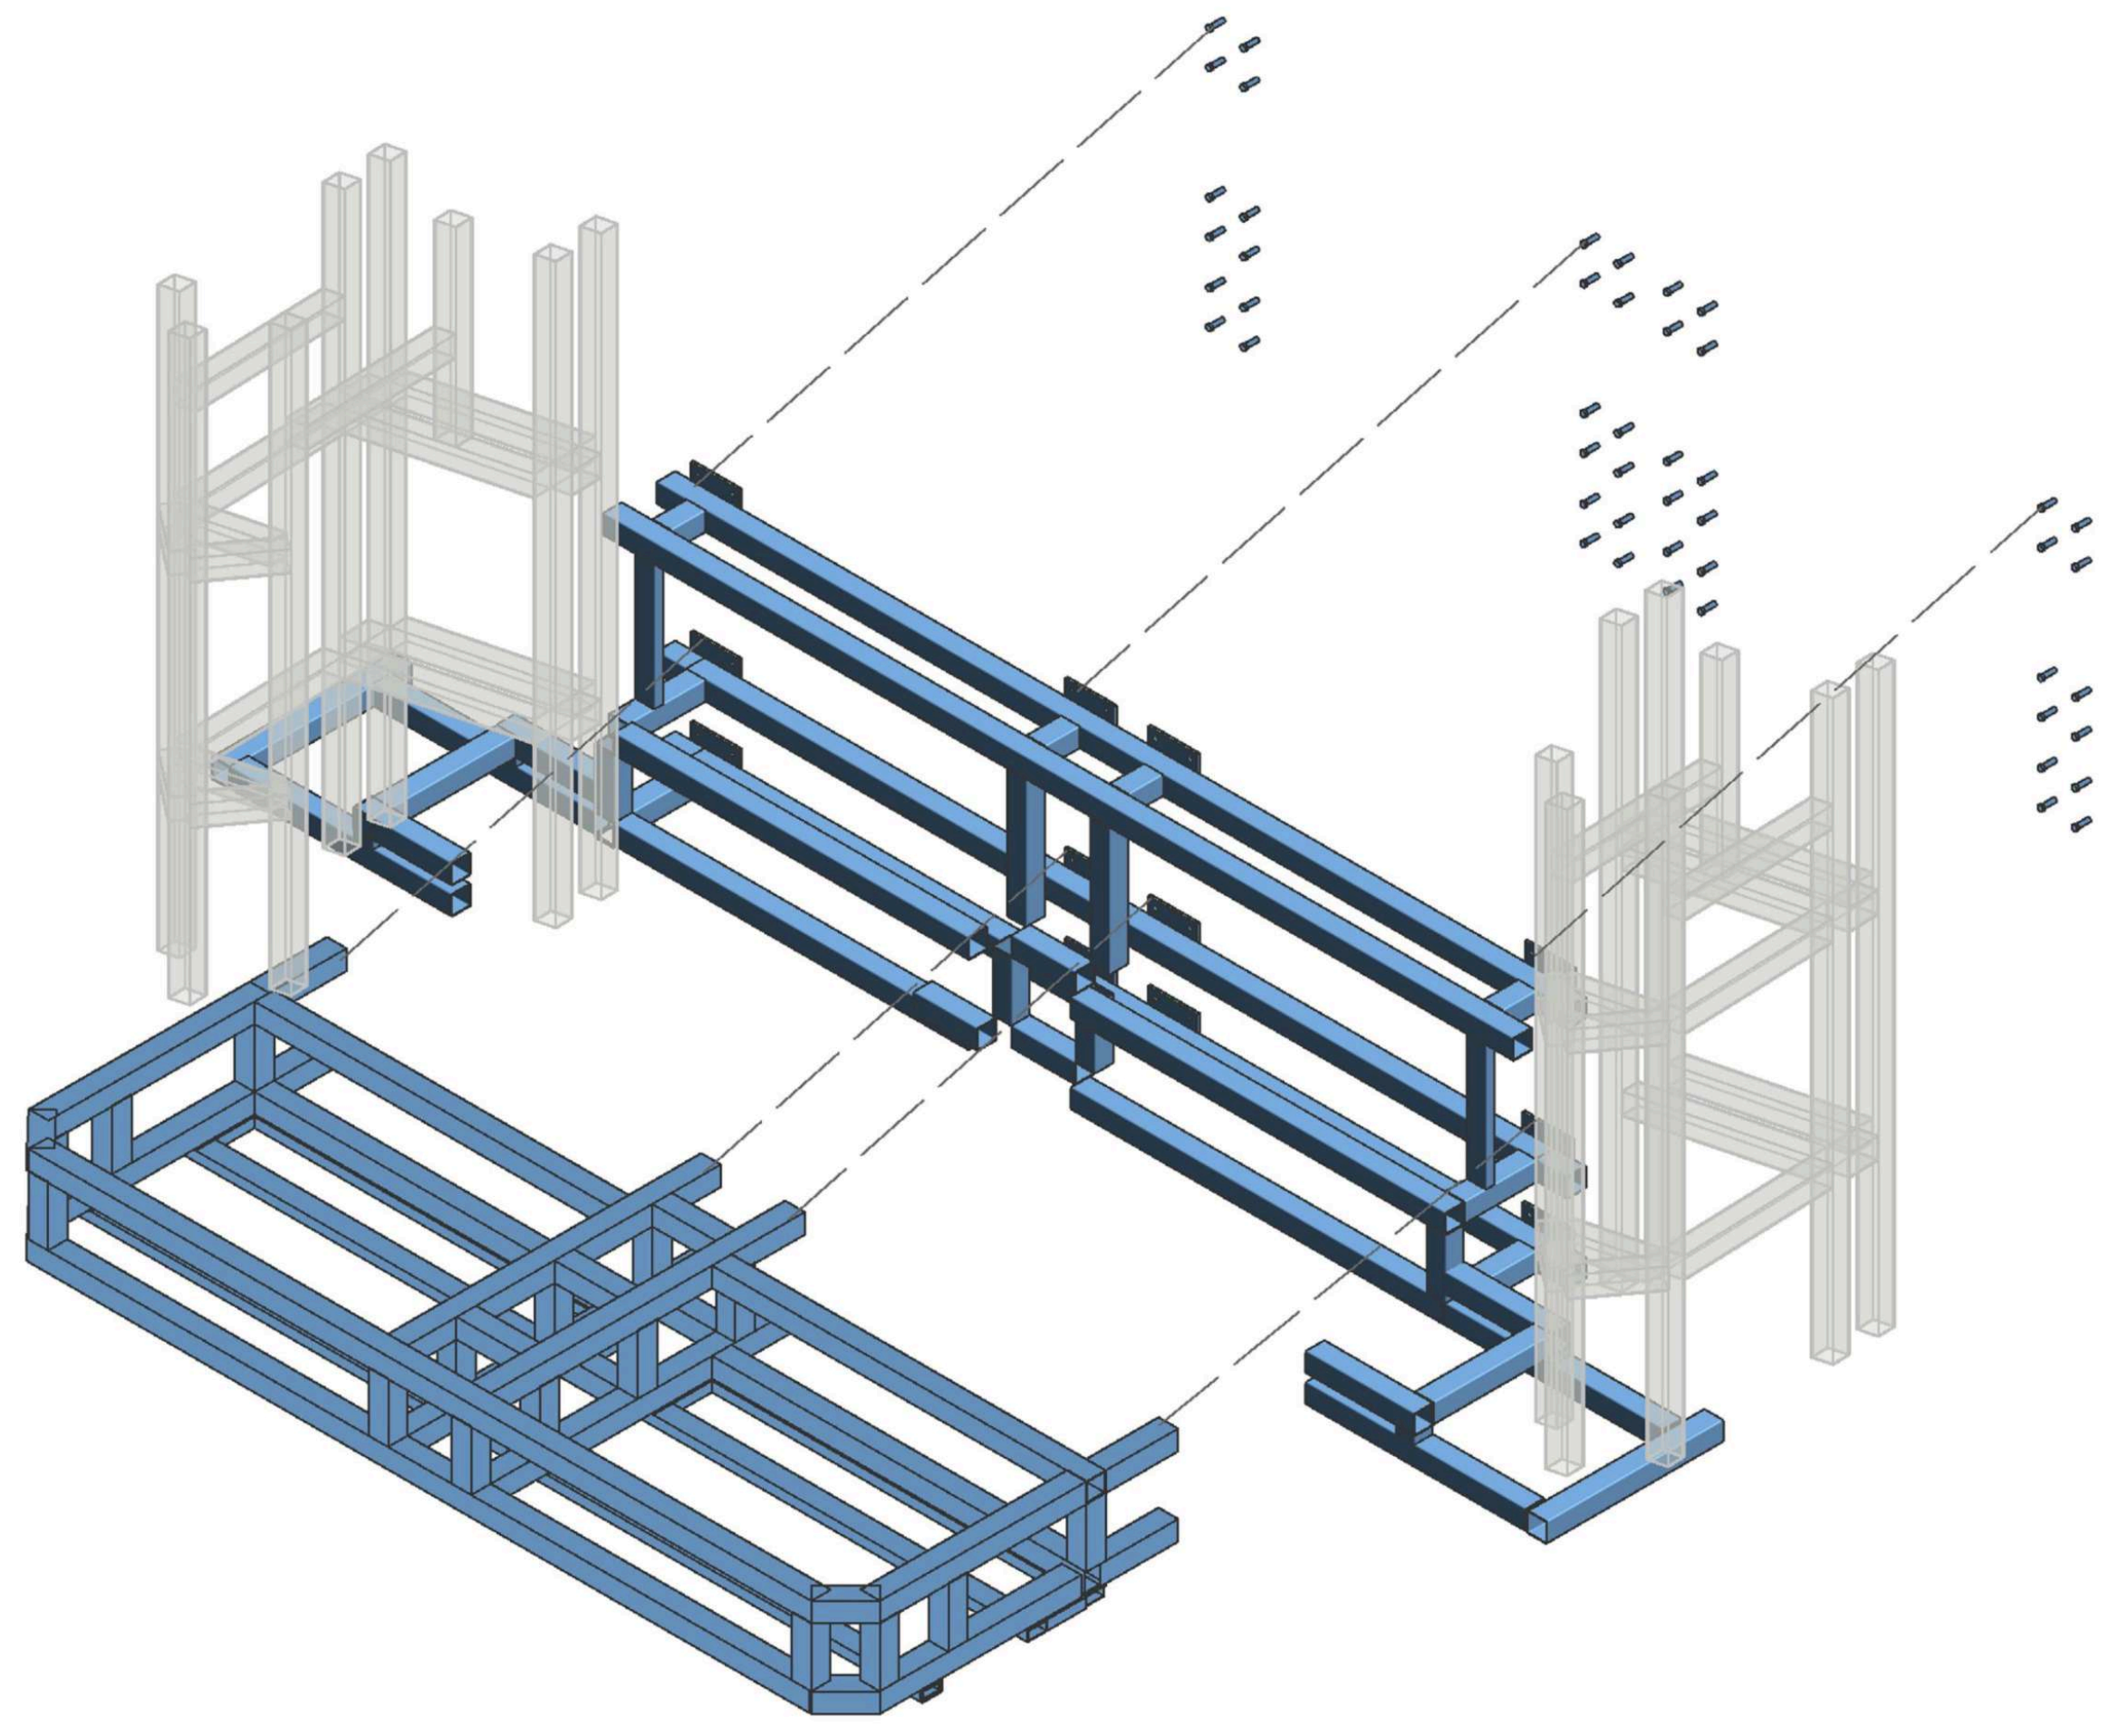

②

③

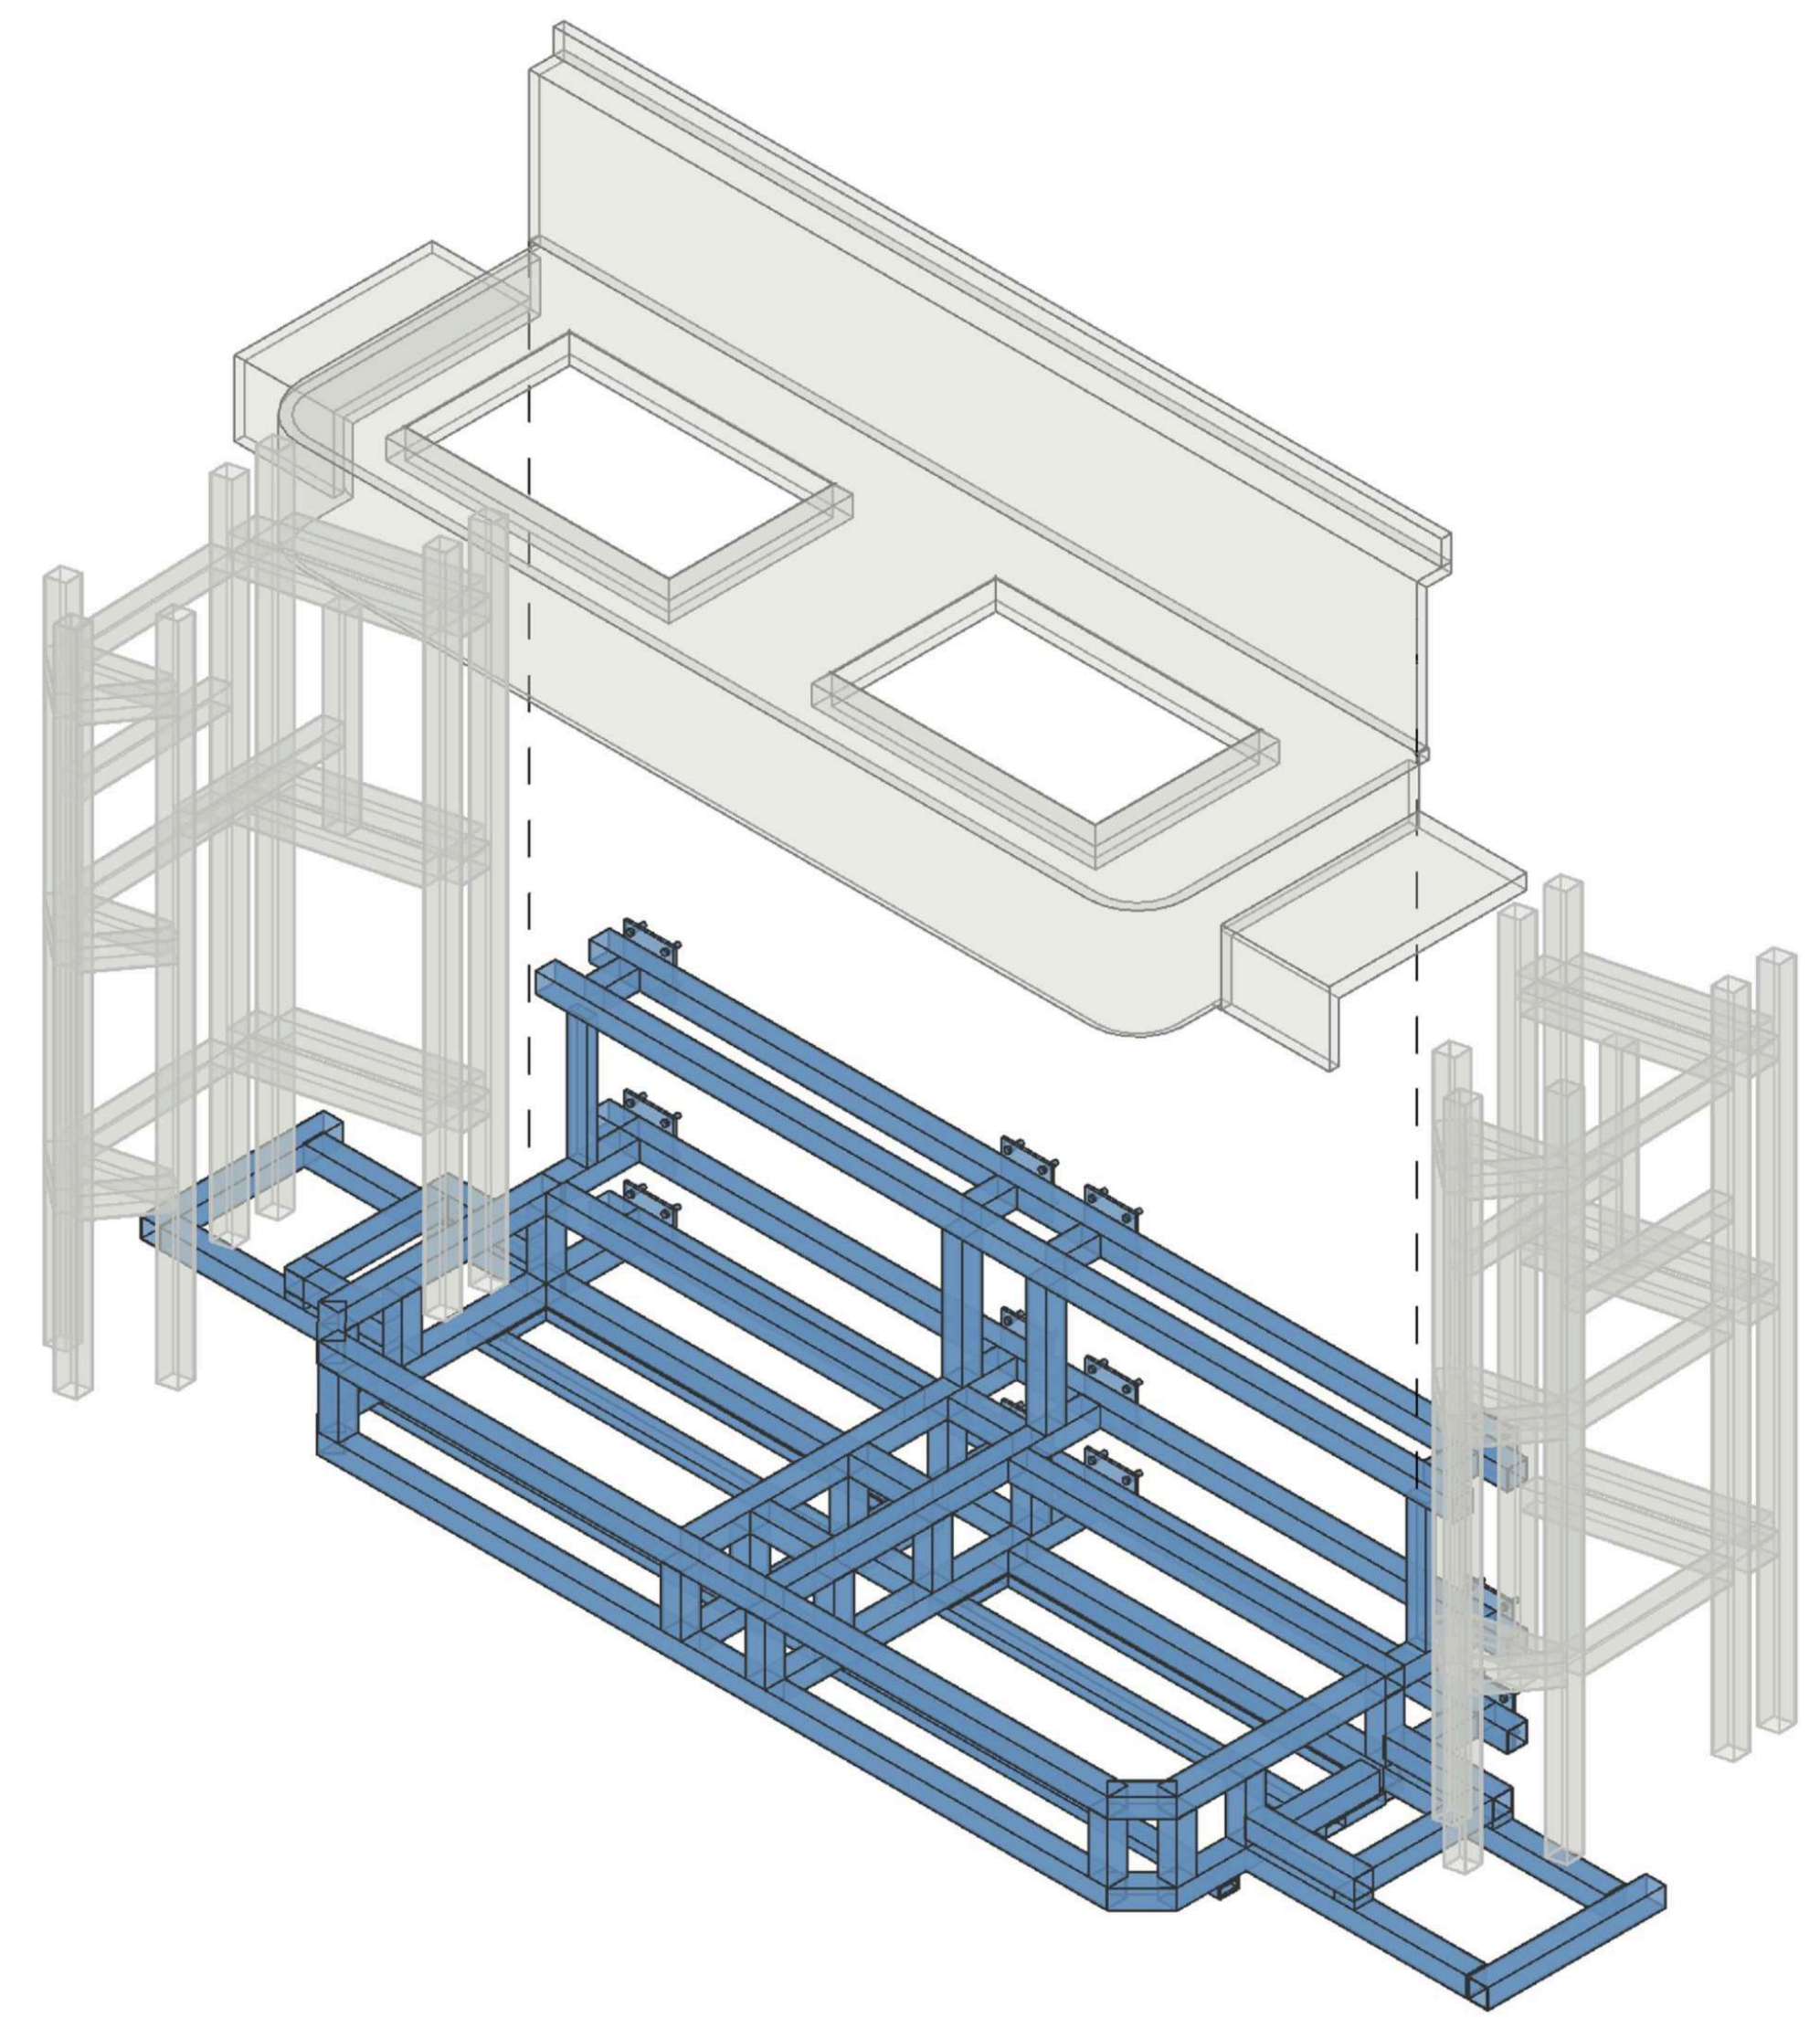

④

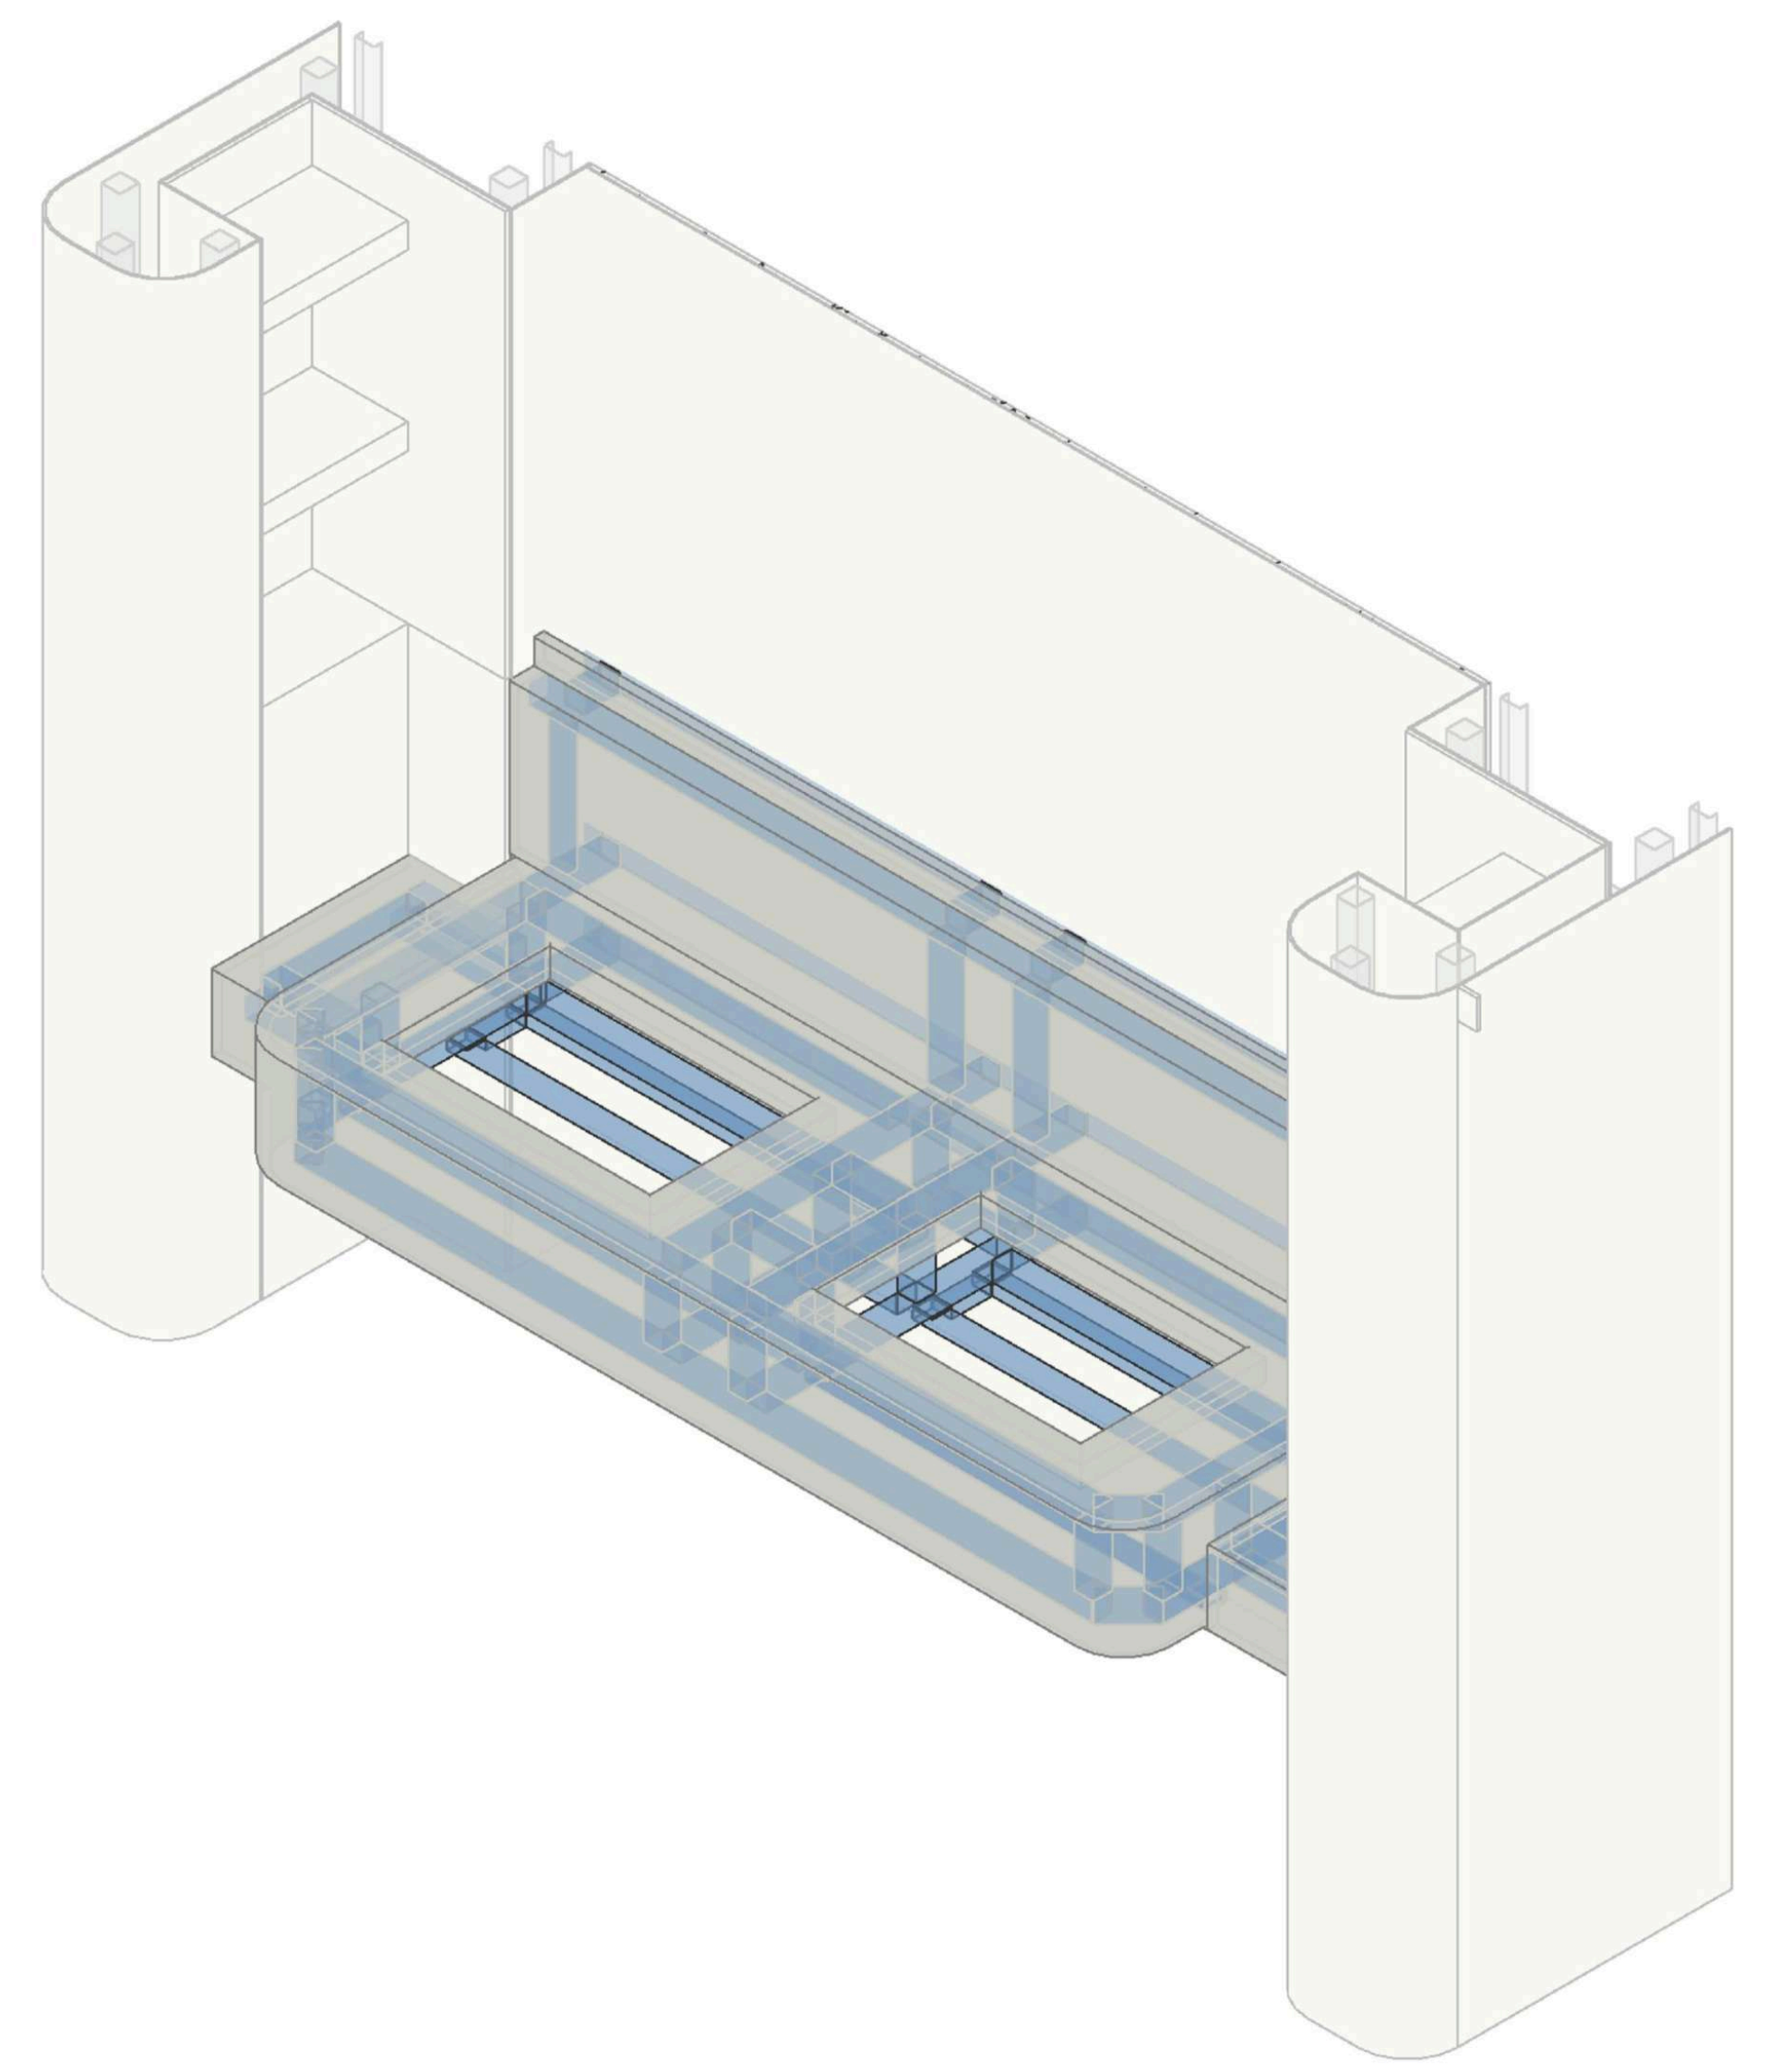

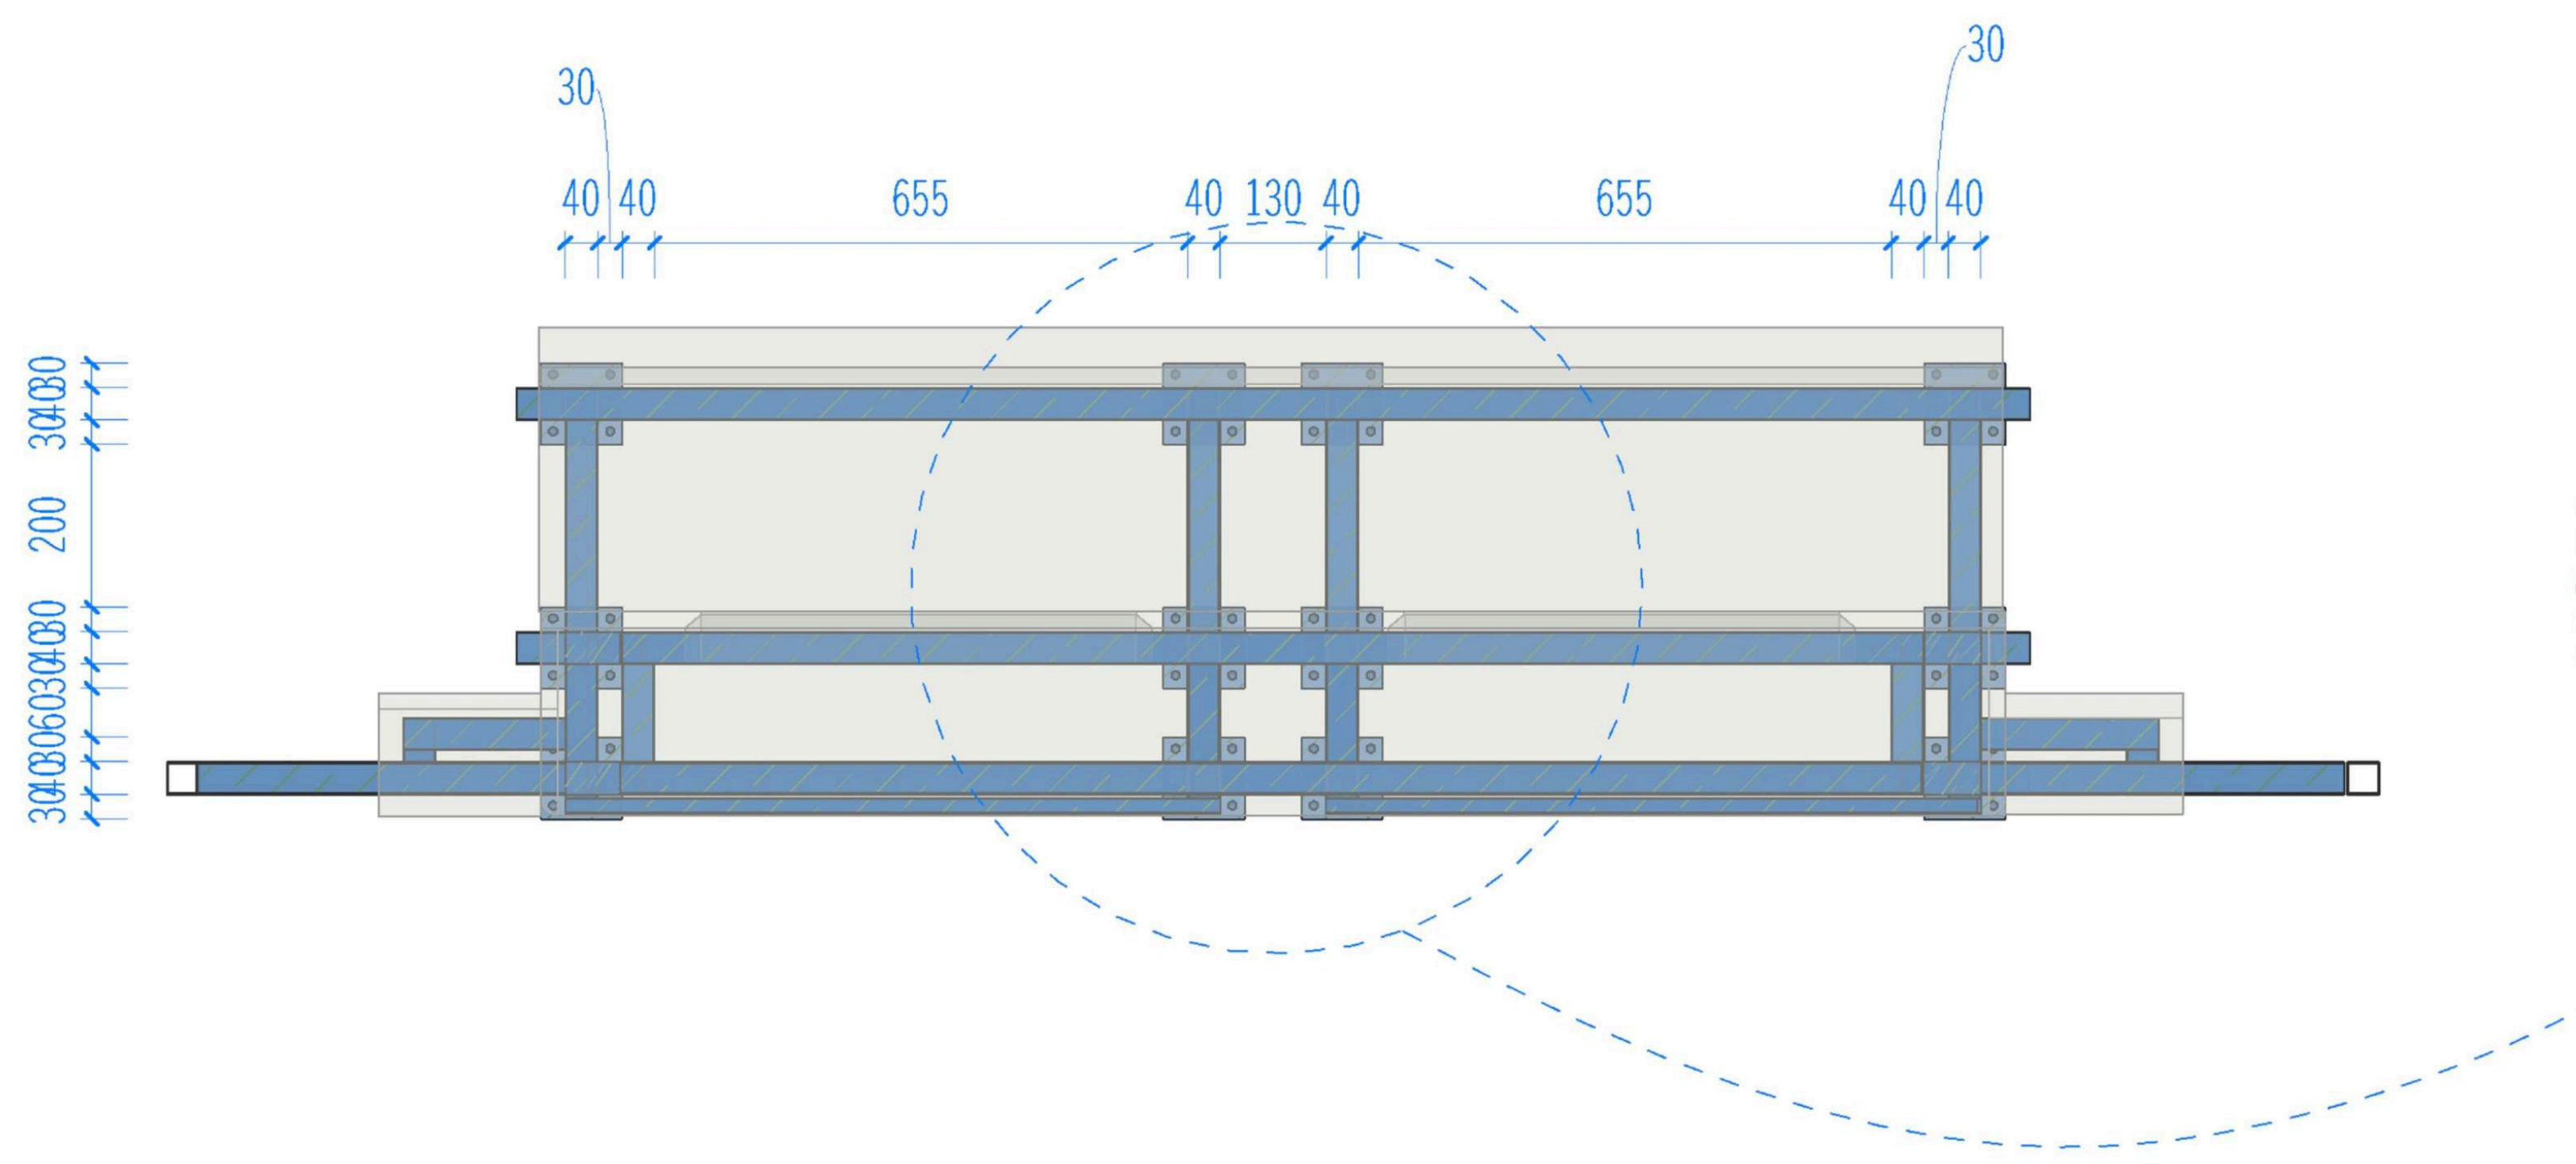
30
30
40
40
655
40
130
40
655
40
40
30 40 30
200
30 40 30 40 60 30 40 30 40 30

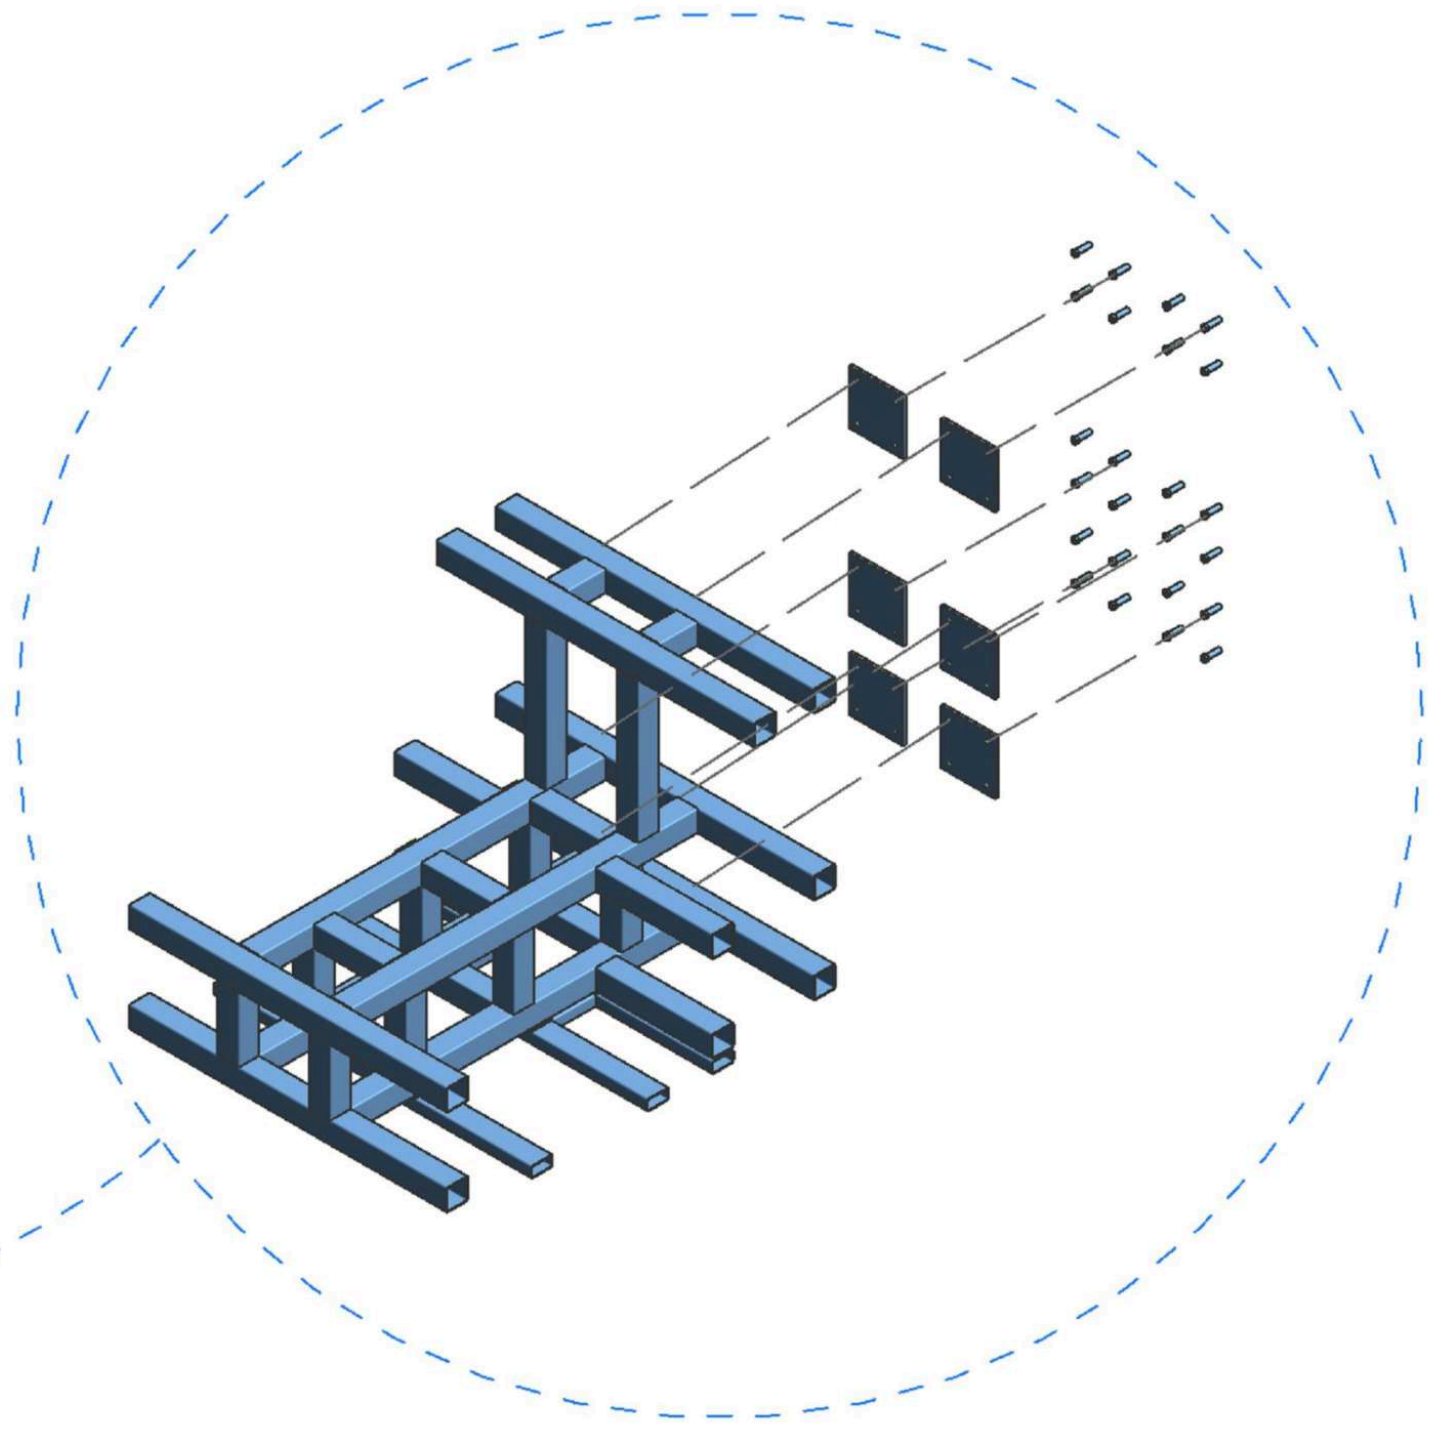

立面视图

节点图

图例A
LEGEND A

编号	图例	说明
1	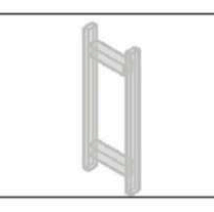	原始钢架
2		螺栓
3	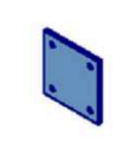	钢片
4	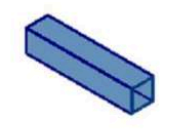	钢架
5	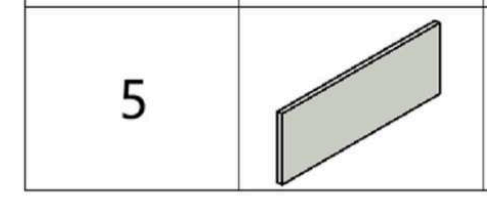	石材

1

盖章

注释
Notes

1.本图纸如与现场尺寸有误，请施工人员与项目负责人联系。
2.施工前施工人员应认真查阅此图，如有不明确尺寸，按现场测量为准。
3.本图纸必须经甲乙双方认可并签字方可作为施工依据。

日期
Date 05/07/26

修订
Revision

△1

项目
Project
潮映华岸府3-801

比例
Scale

主卫洗手台石材钢架

图纸编号
Drawing No.
ST-01

项目编号
Project No.

©2025

1

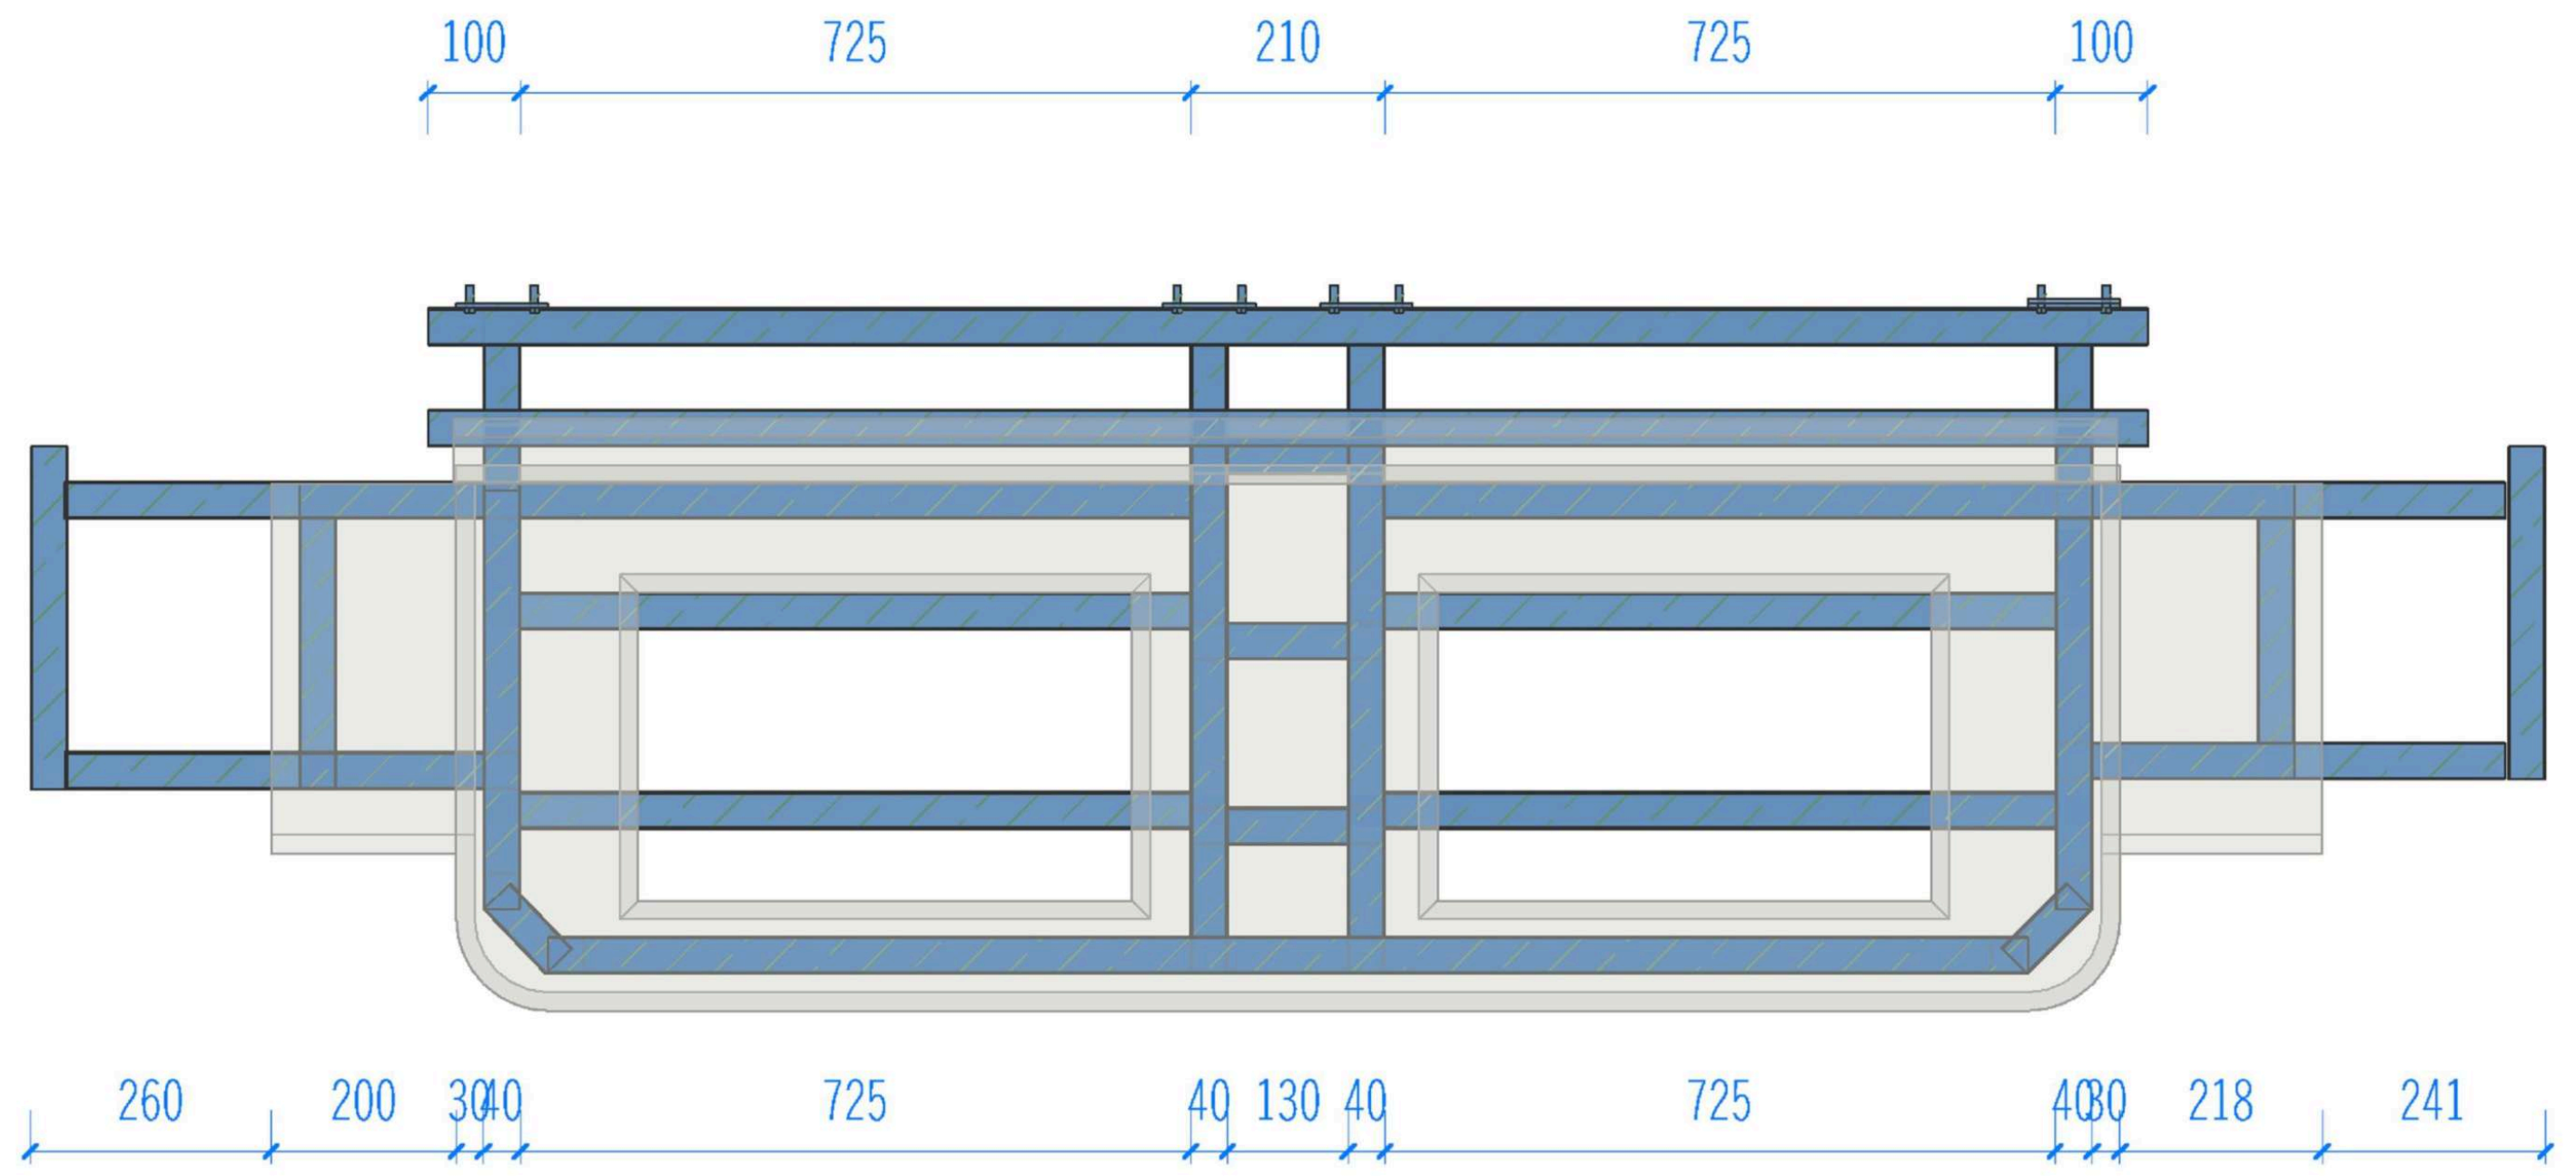
100
725
210
725
100
260
200
30
40
725
40
130
40
725
40
30
218
241

平面视图

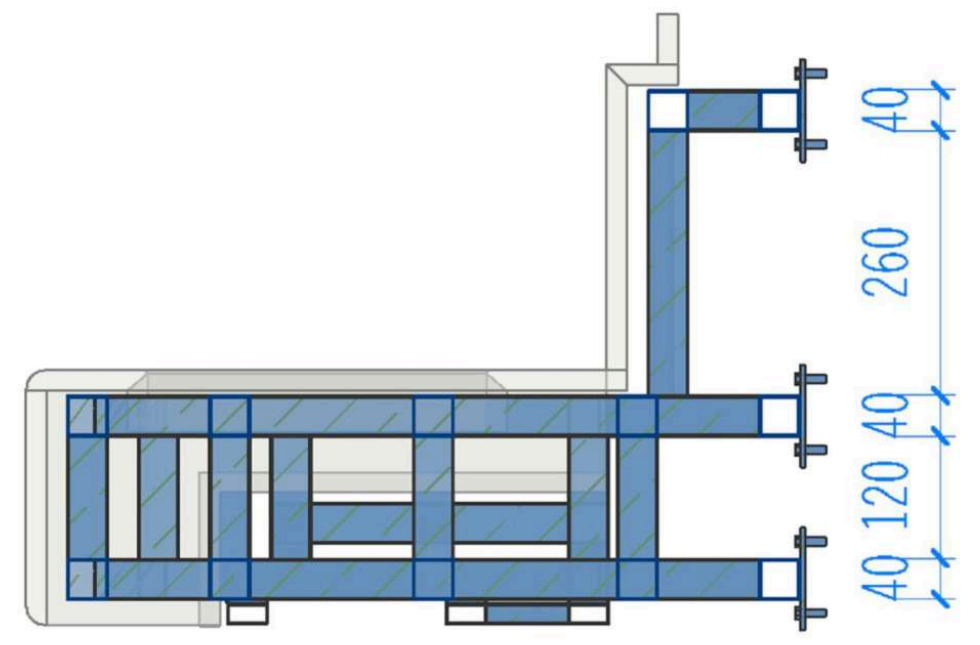
40
260
40
120
40

剖面视图

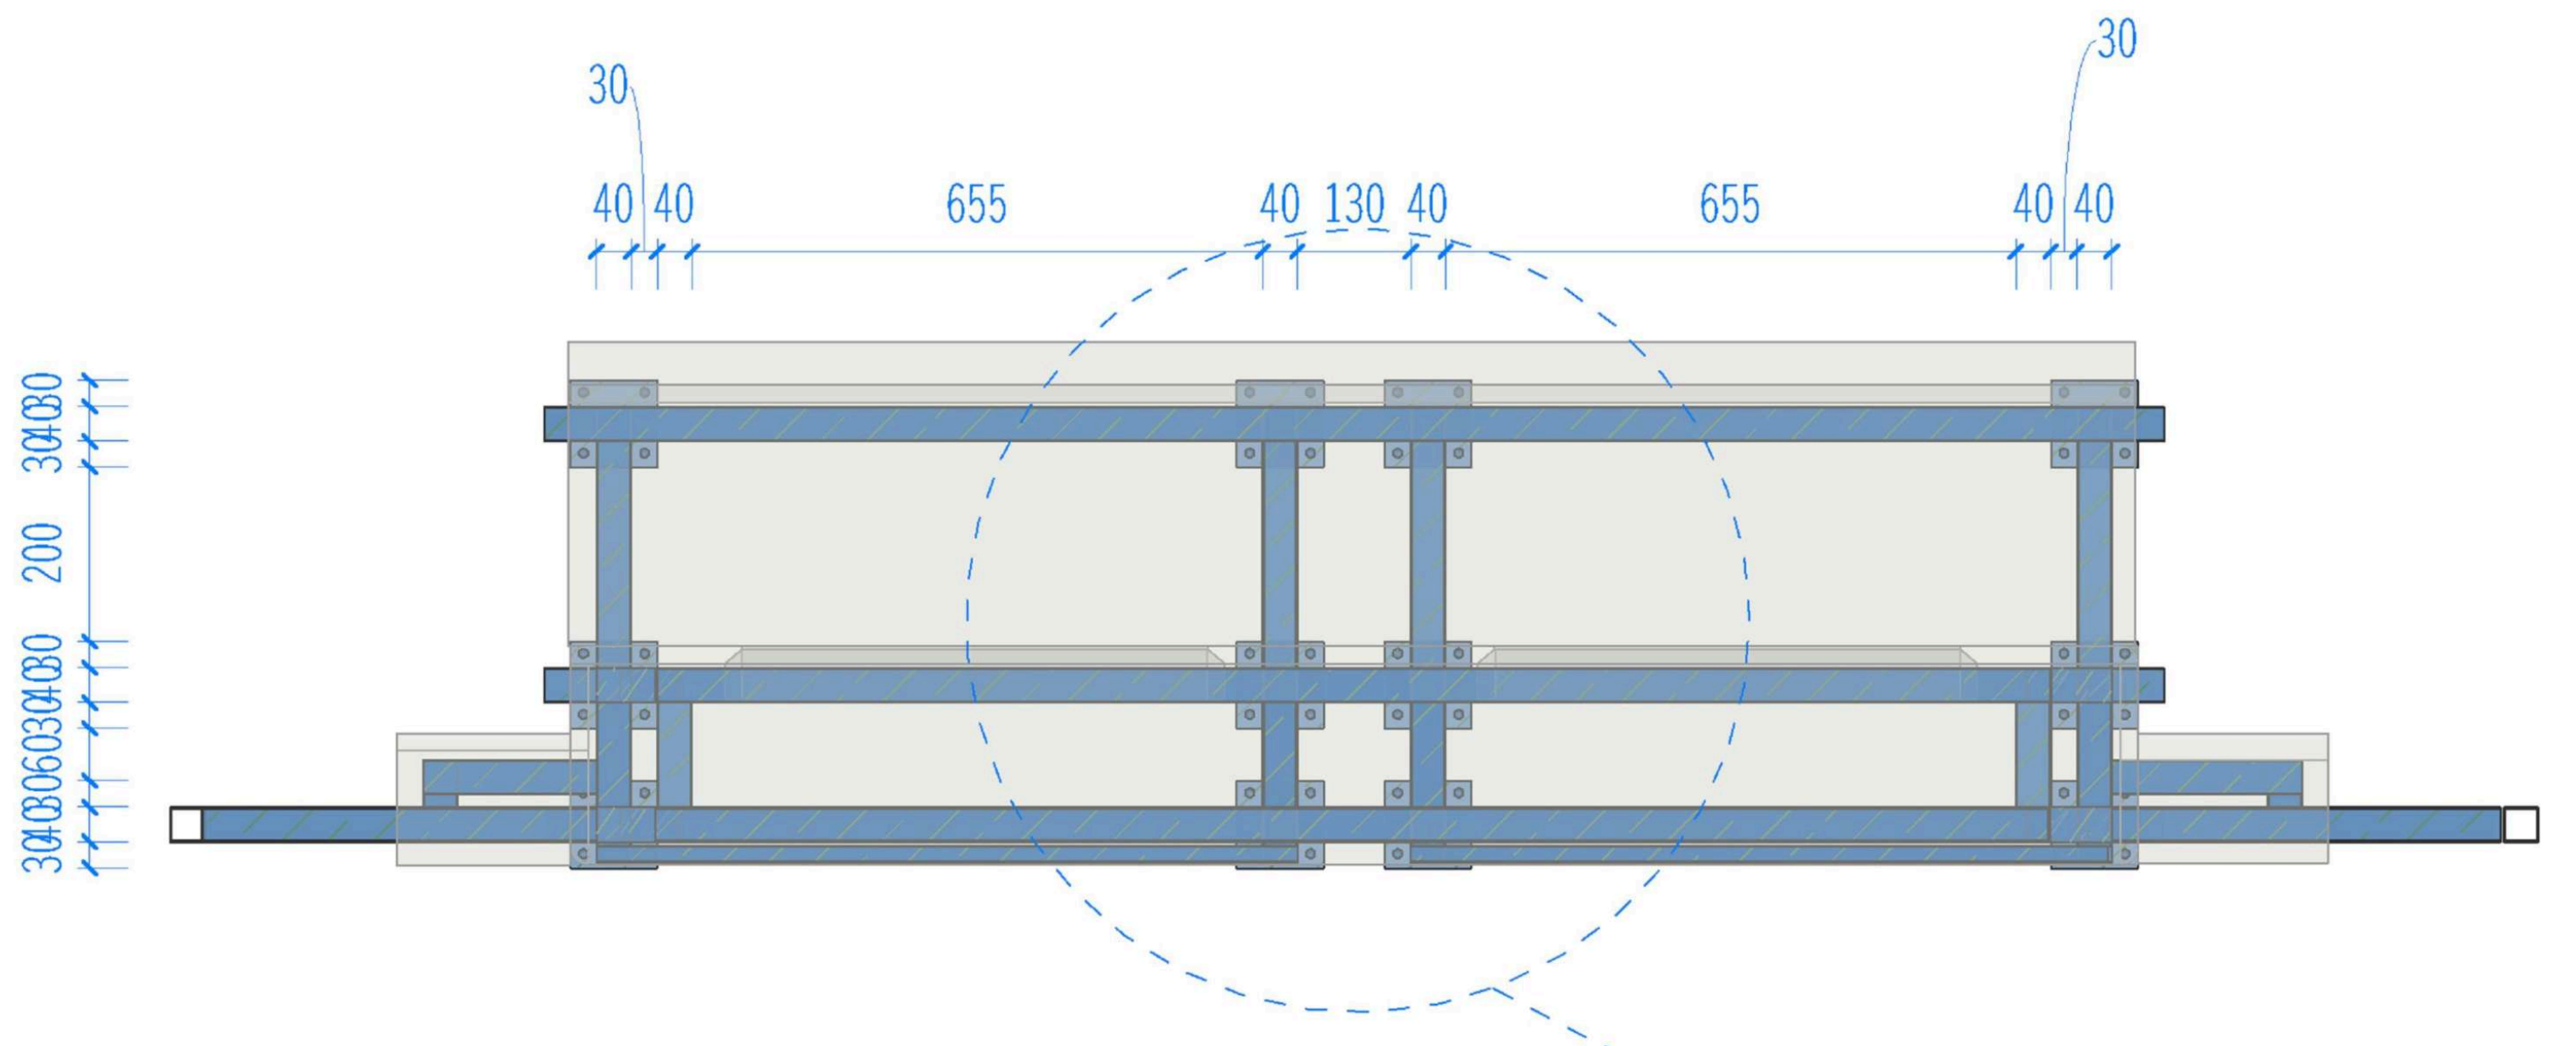
30
30
40
40
655
40
130
40
655
40
40
200

立面视图

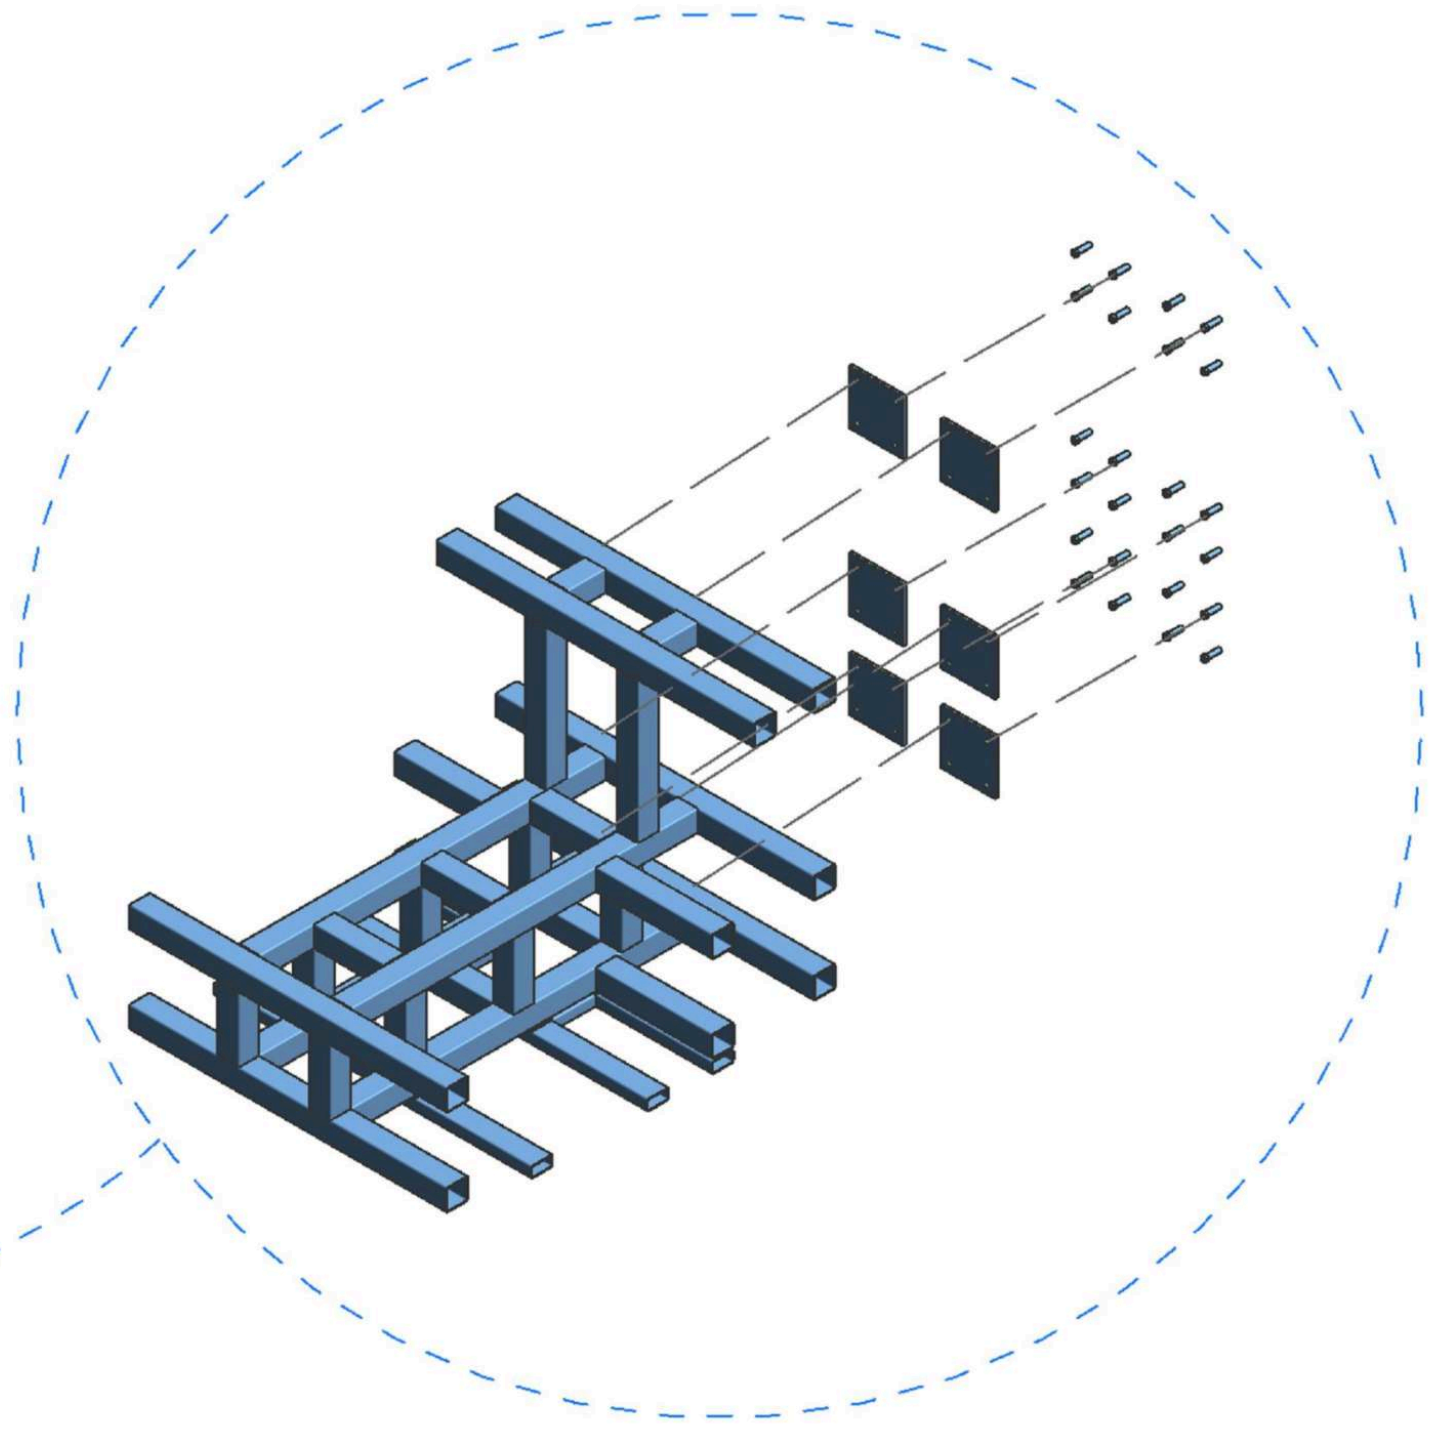

节点图

工厂预制钢架

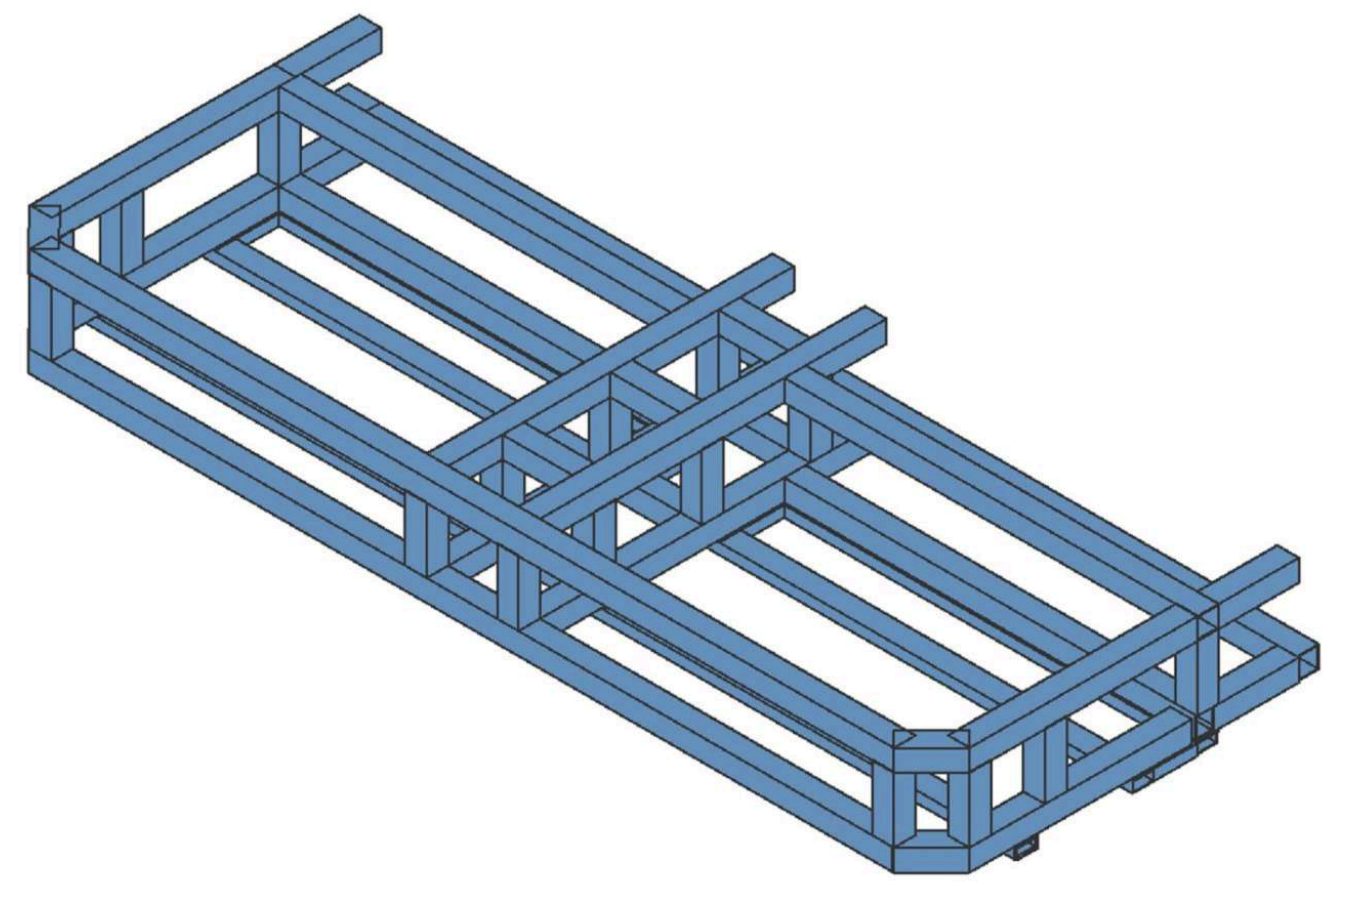

①

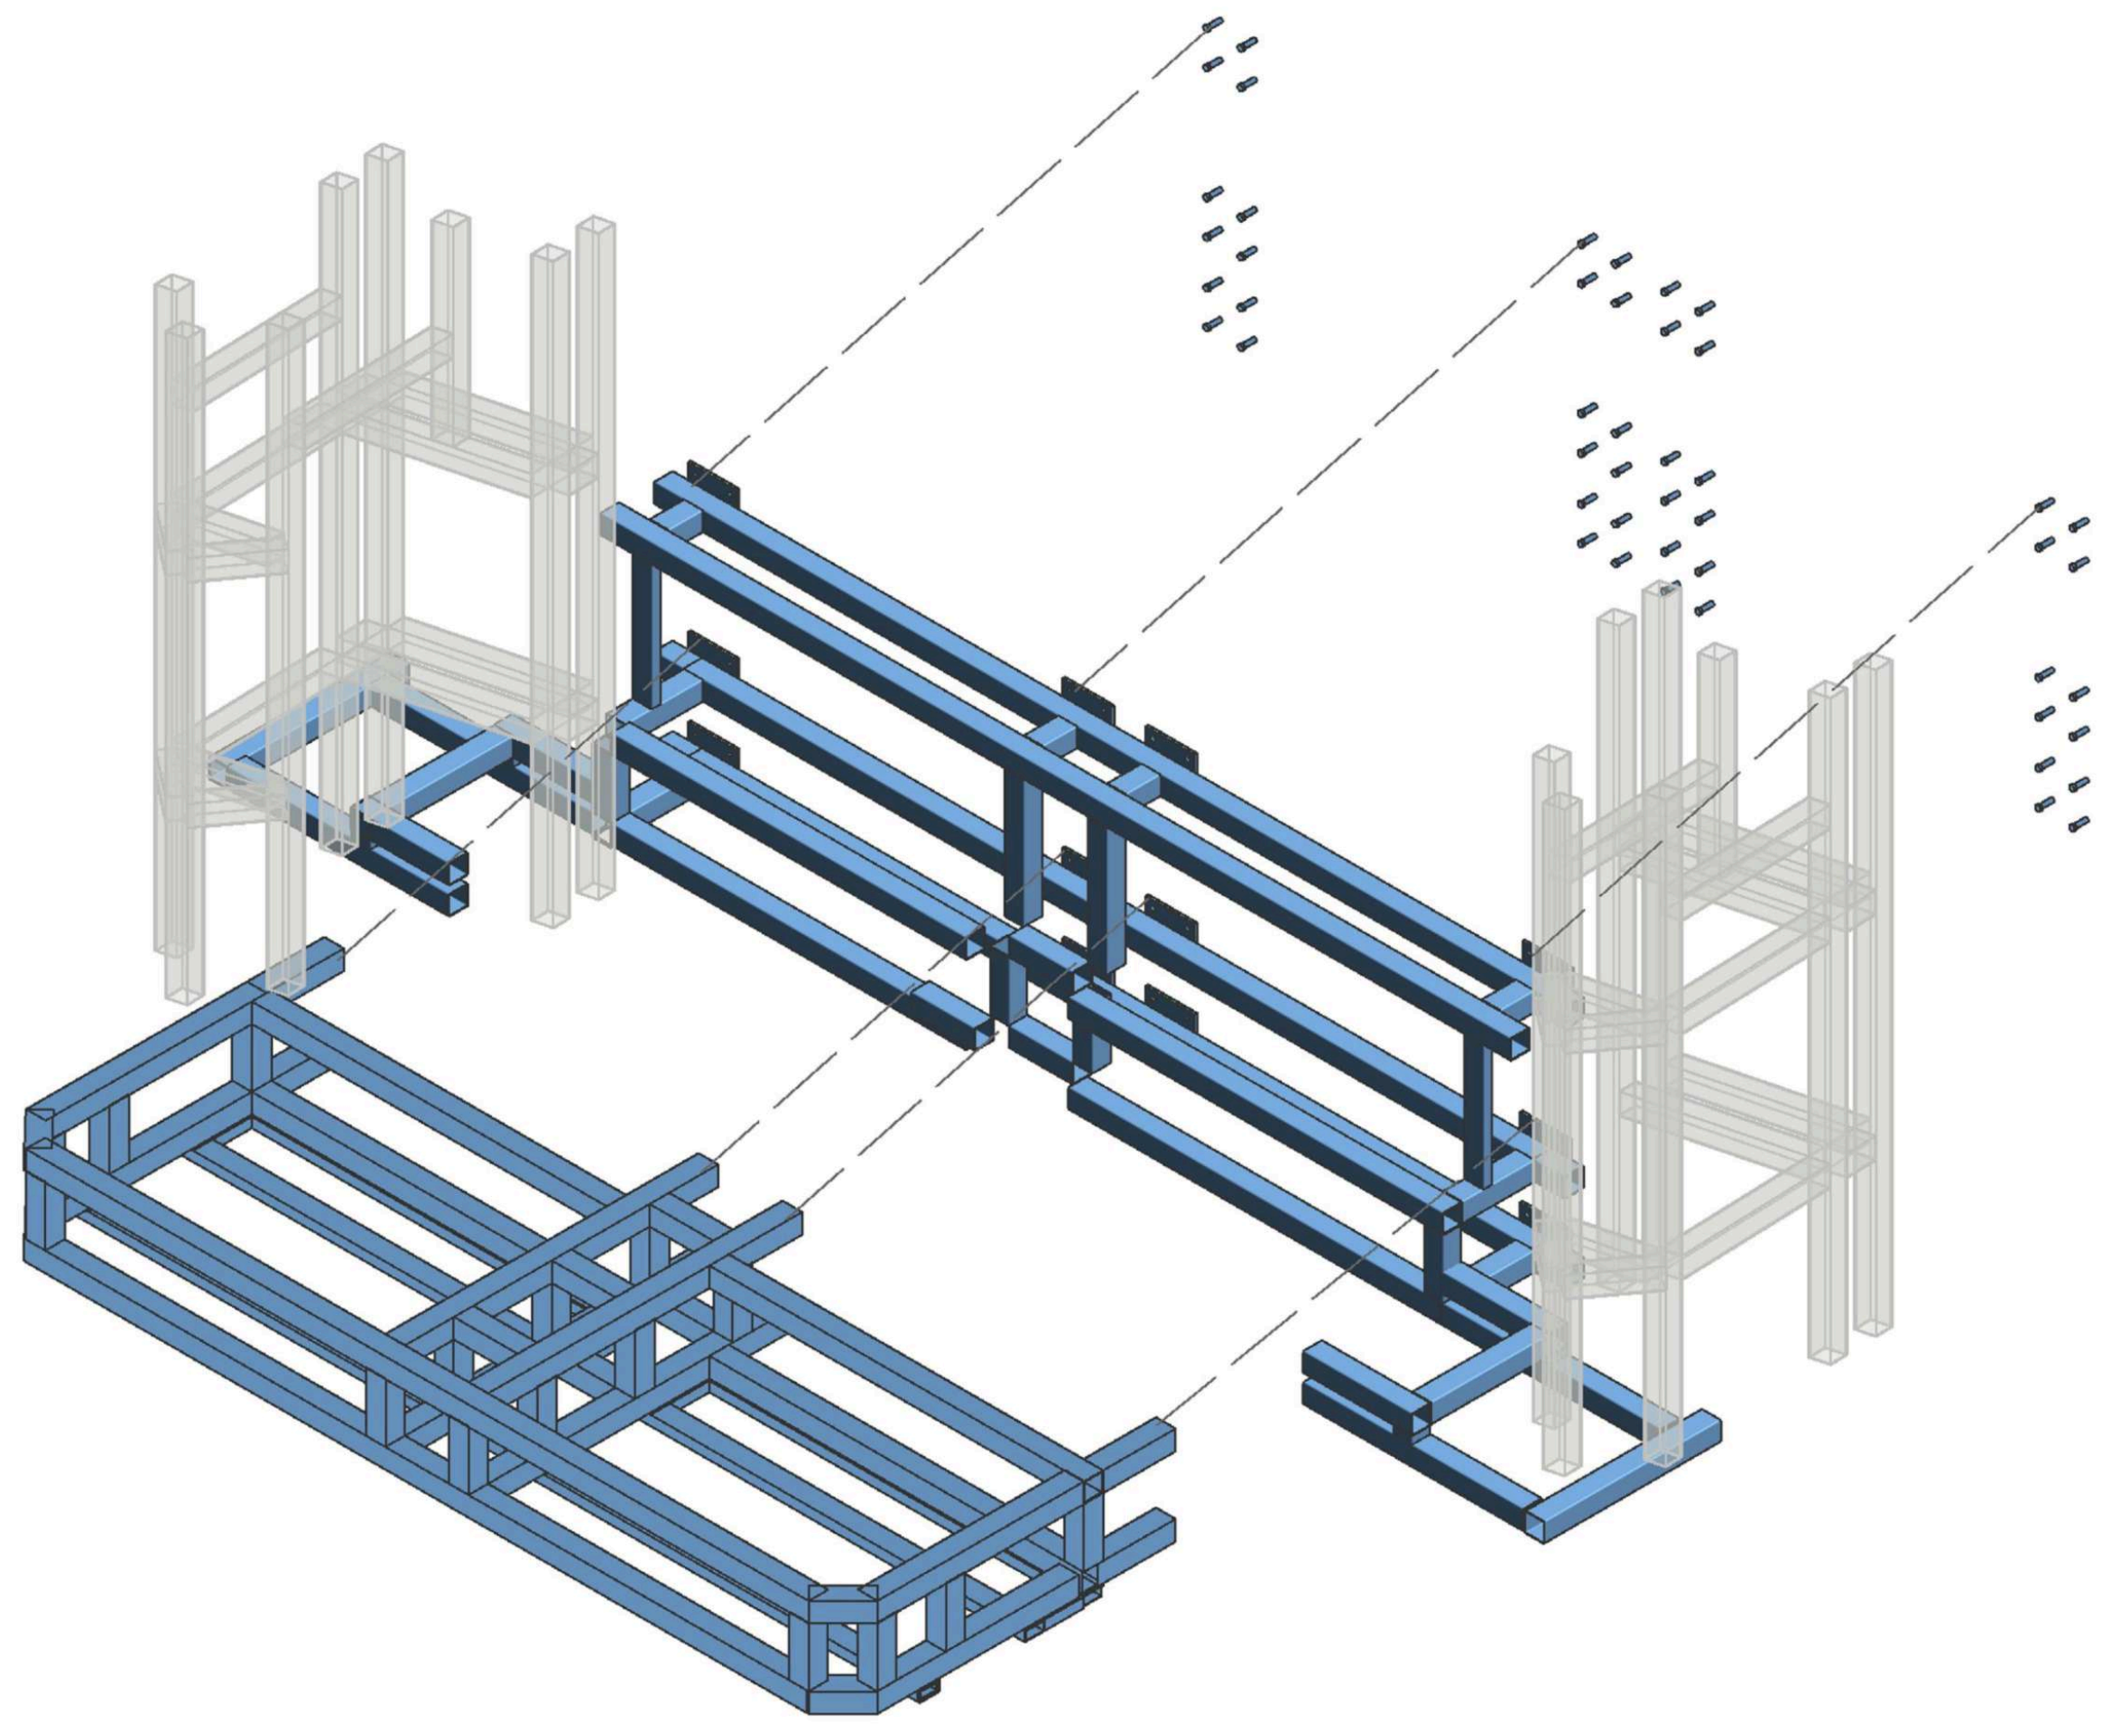

②

③

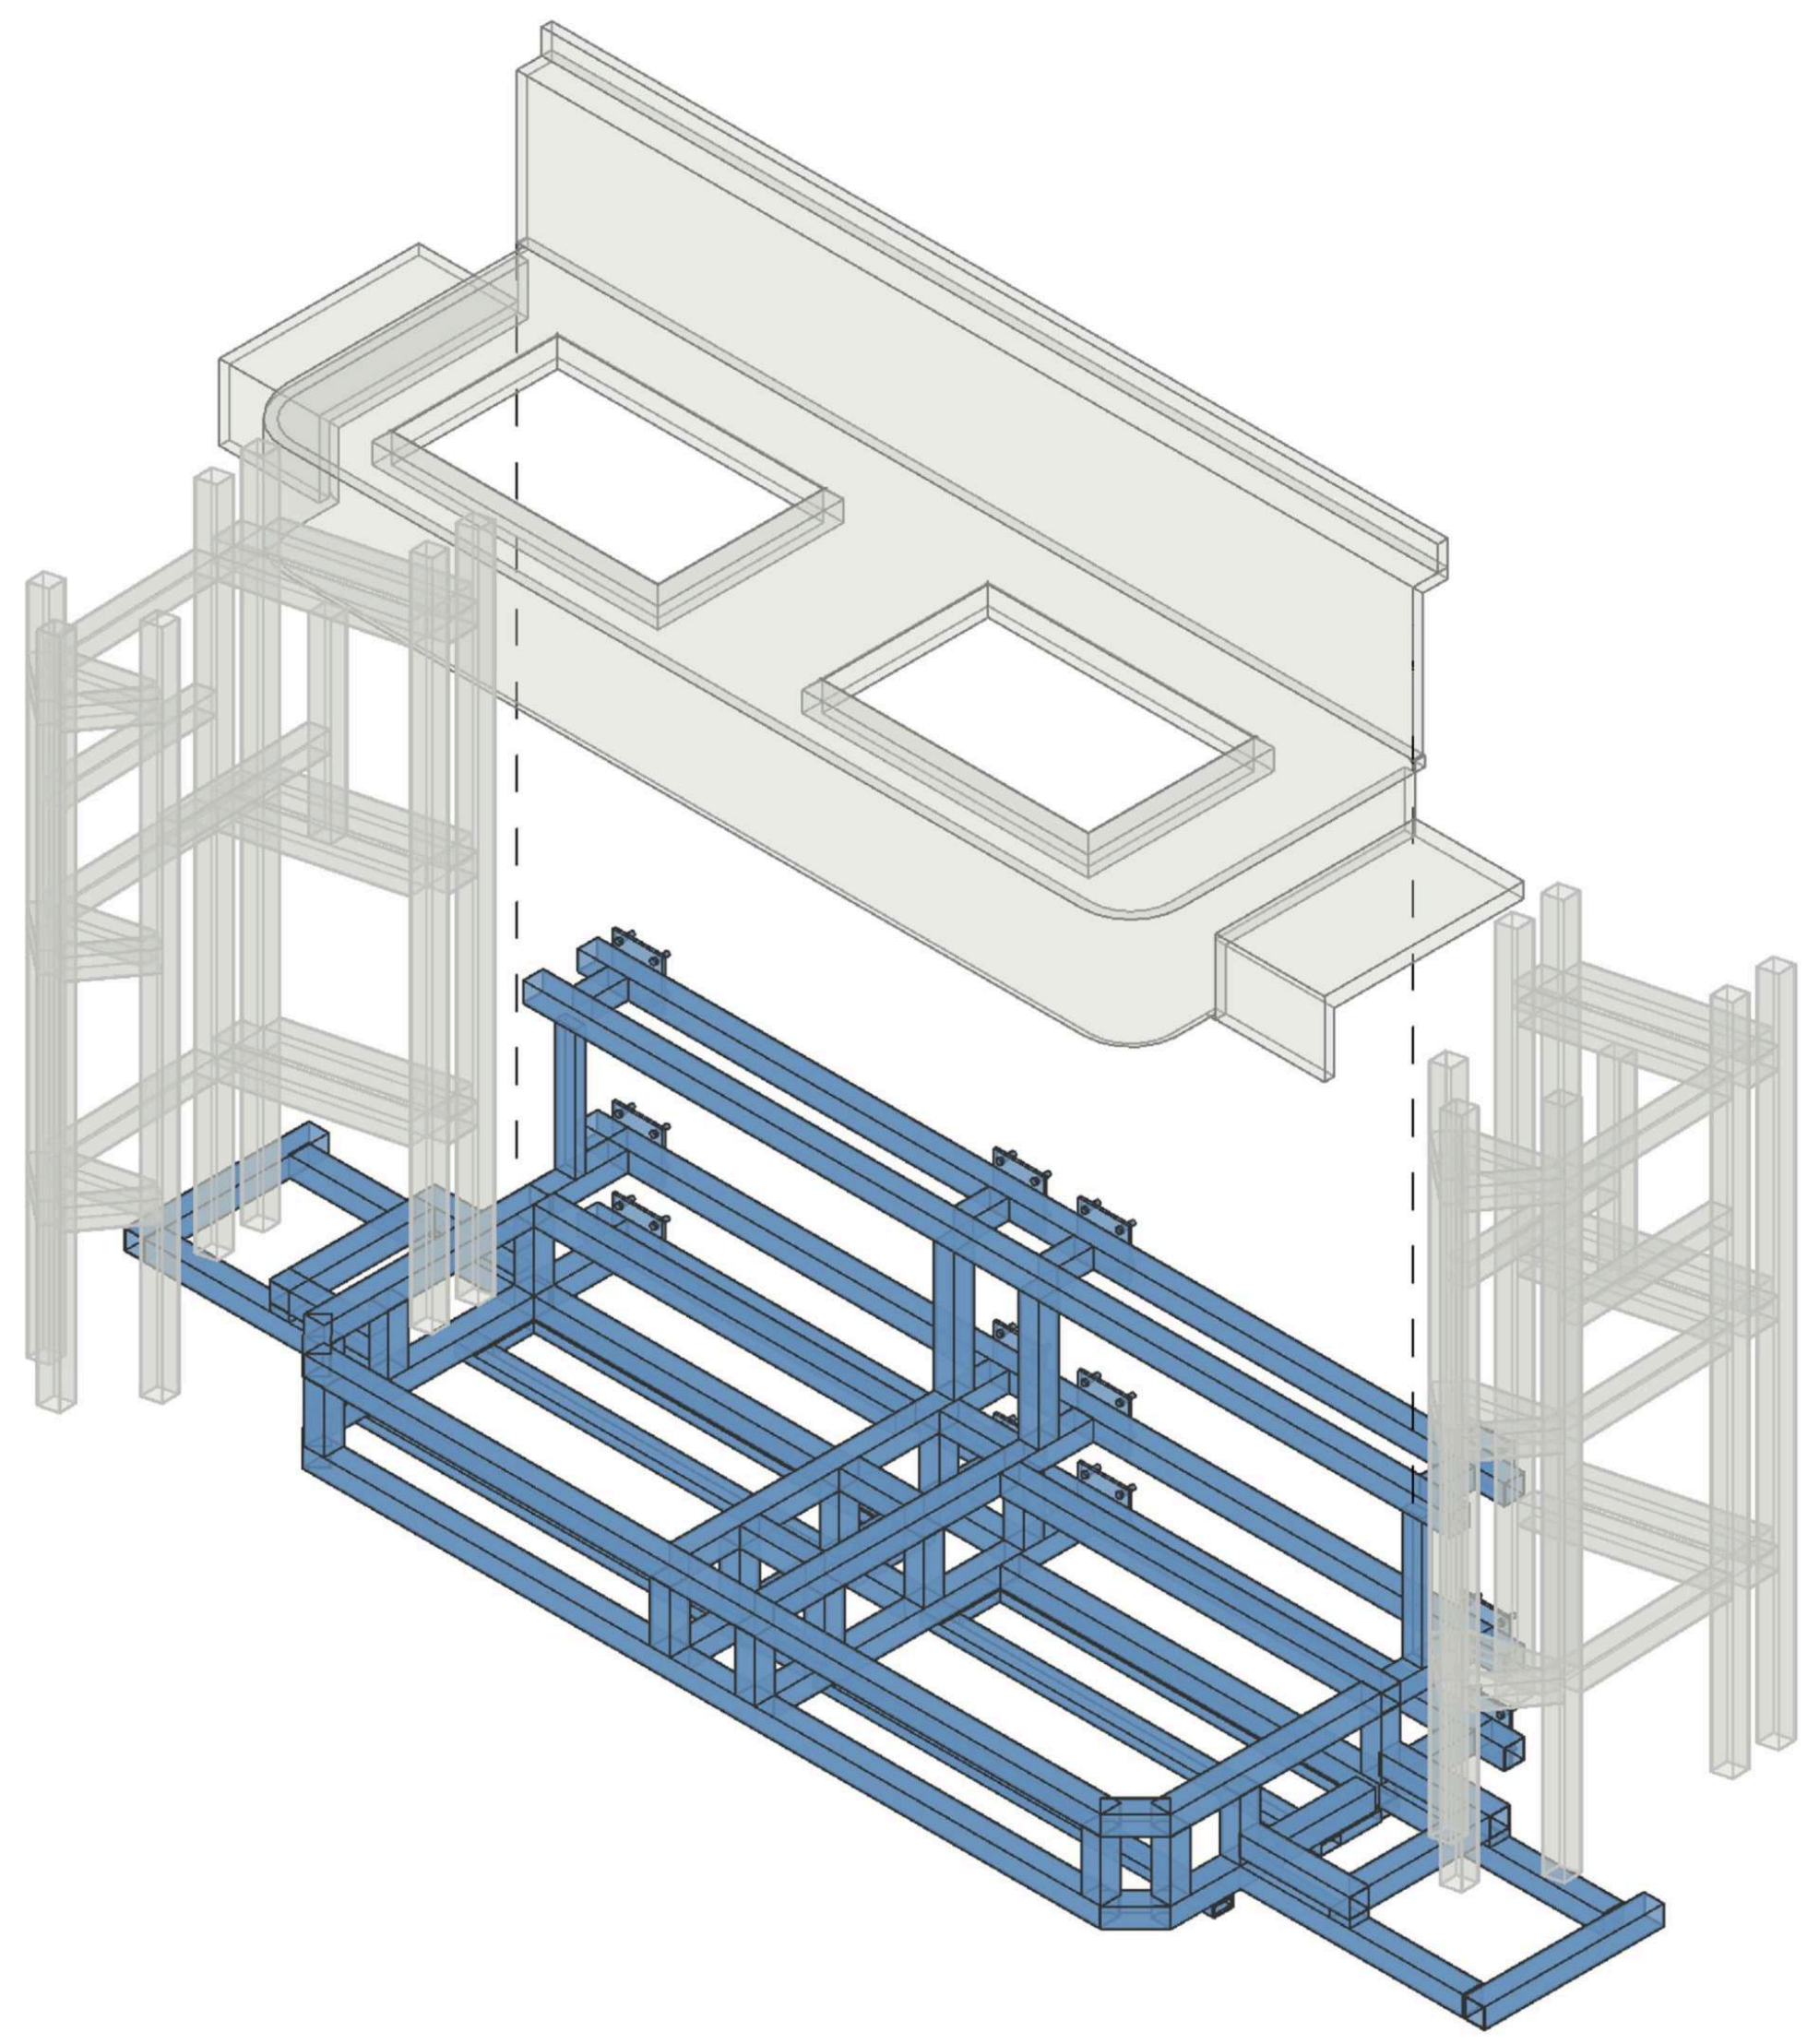

④

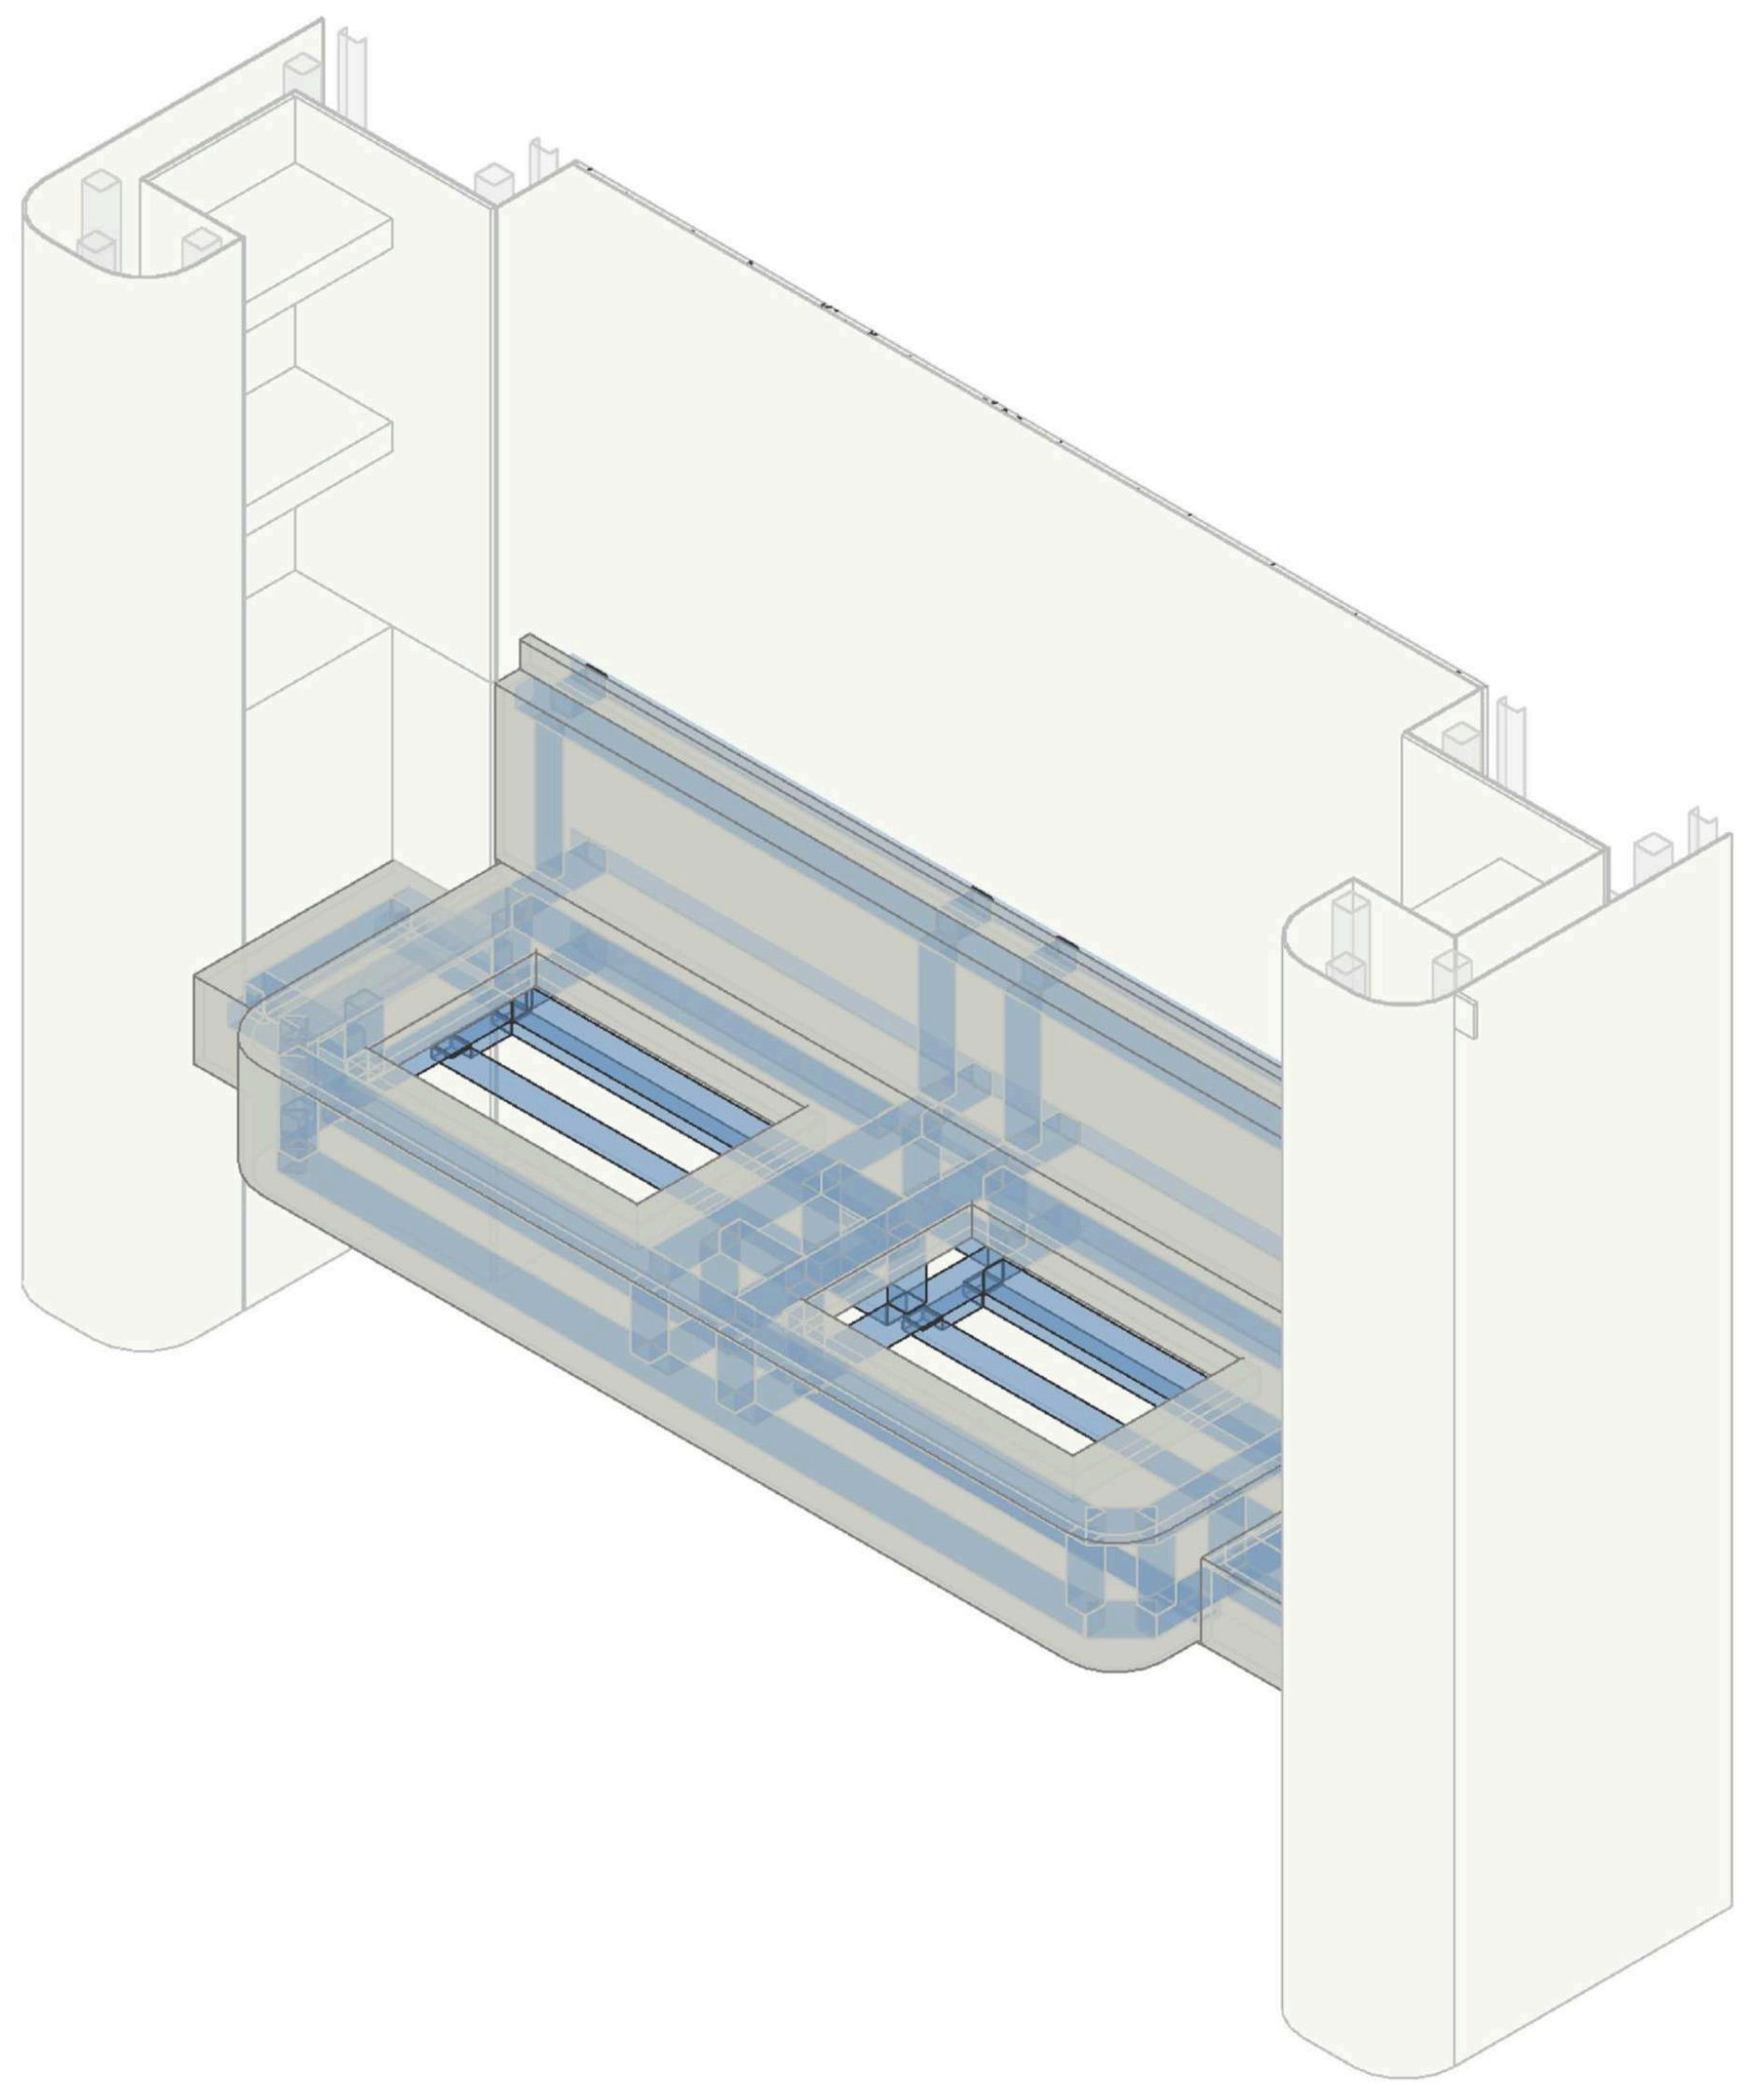

1

图例A
LEGEND A

编号	图例	说明
1		原始钢架
2		螺栓
3		钢片
4		钢架
5		石材

盖章

注释
Notes

1.本图纸如与现场尺寸有误，请施工人员与项目负责人联系。
2.施工前施工人员应认真查阅此图，如有不明确尺寸，按现场测量为准。
3.本图纸必须经甲乙双方认可并签字方可作为施工依据。

日期
Date 05/07/26

修订
Revision

1

项目
Project
潮映华岸府3-801

比例
Scale

主卫洗手台石材钢架

图纸编号
Drawing No.
ST-01

项目编号
Project No.

©2025

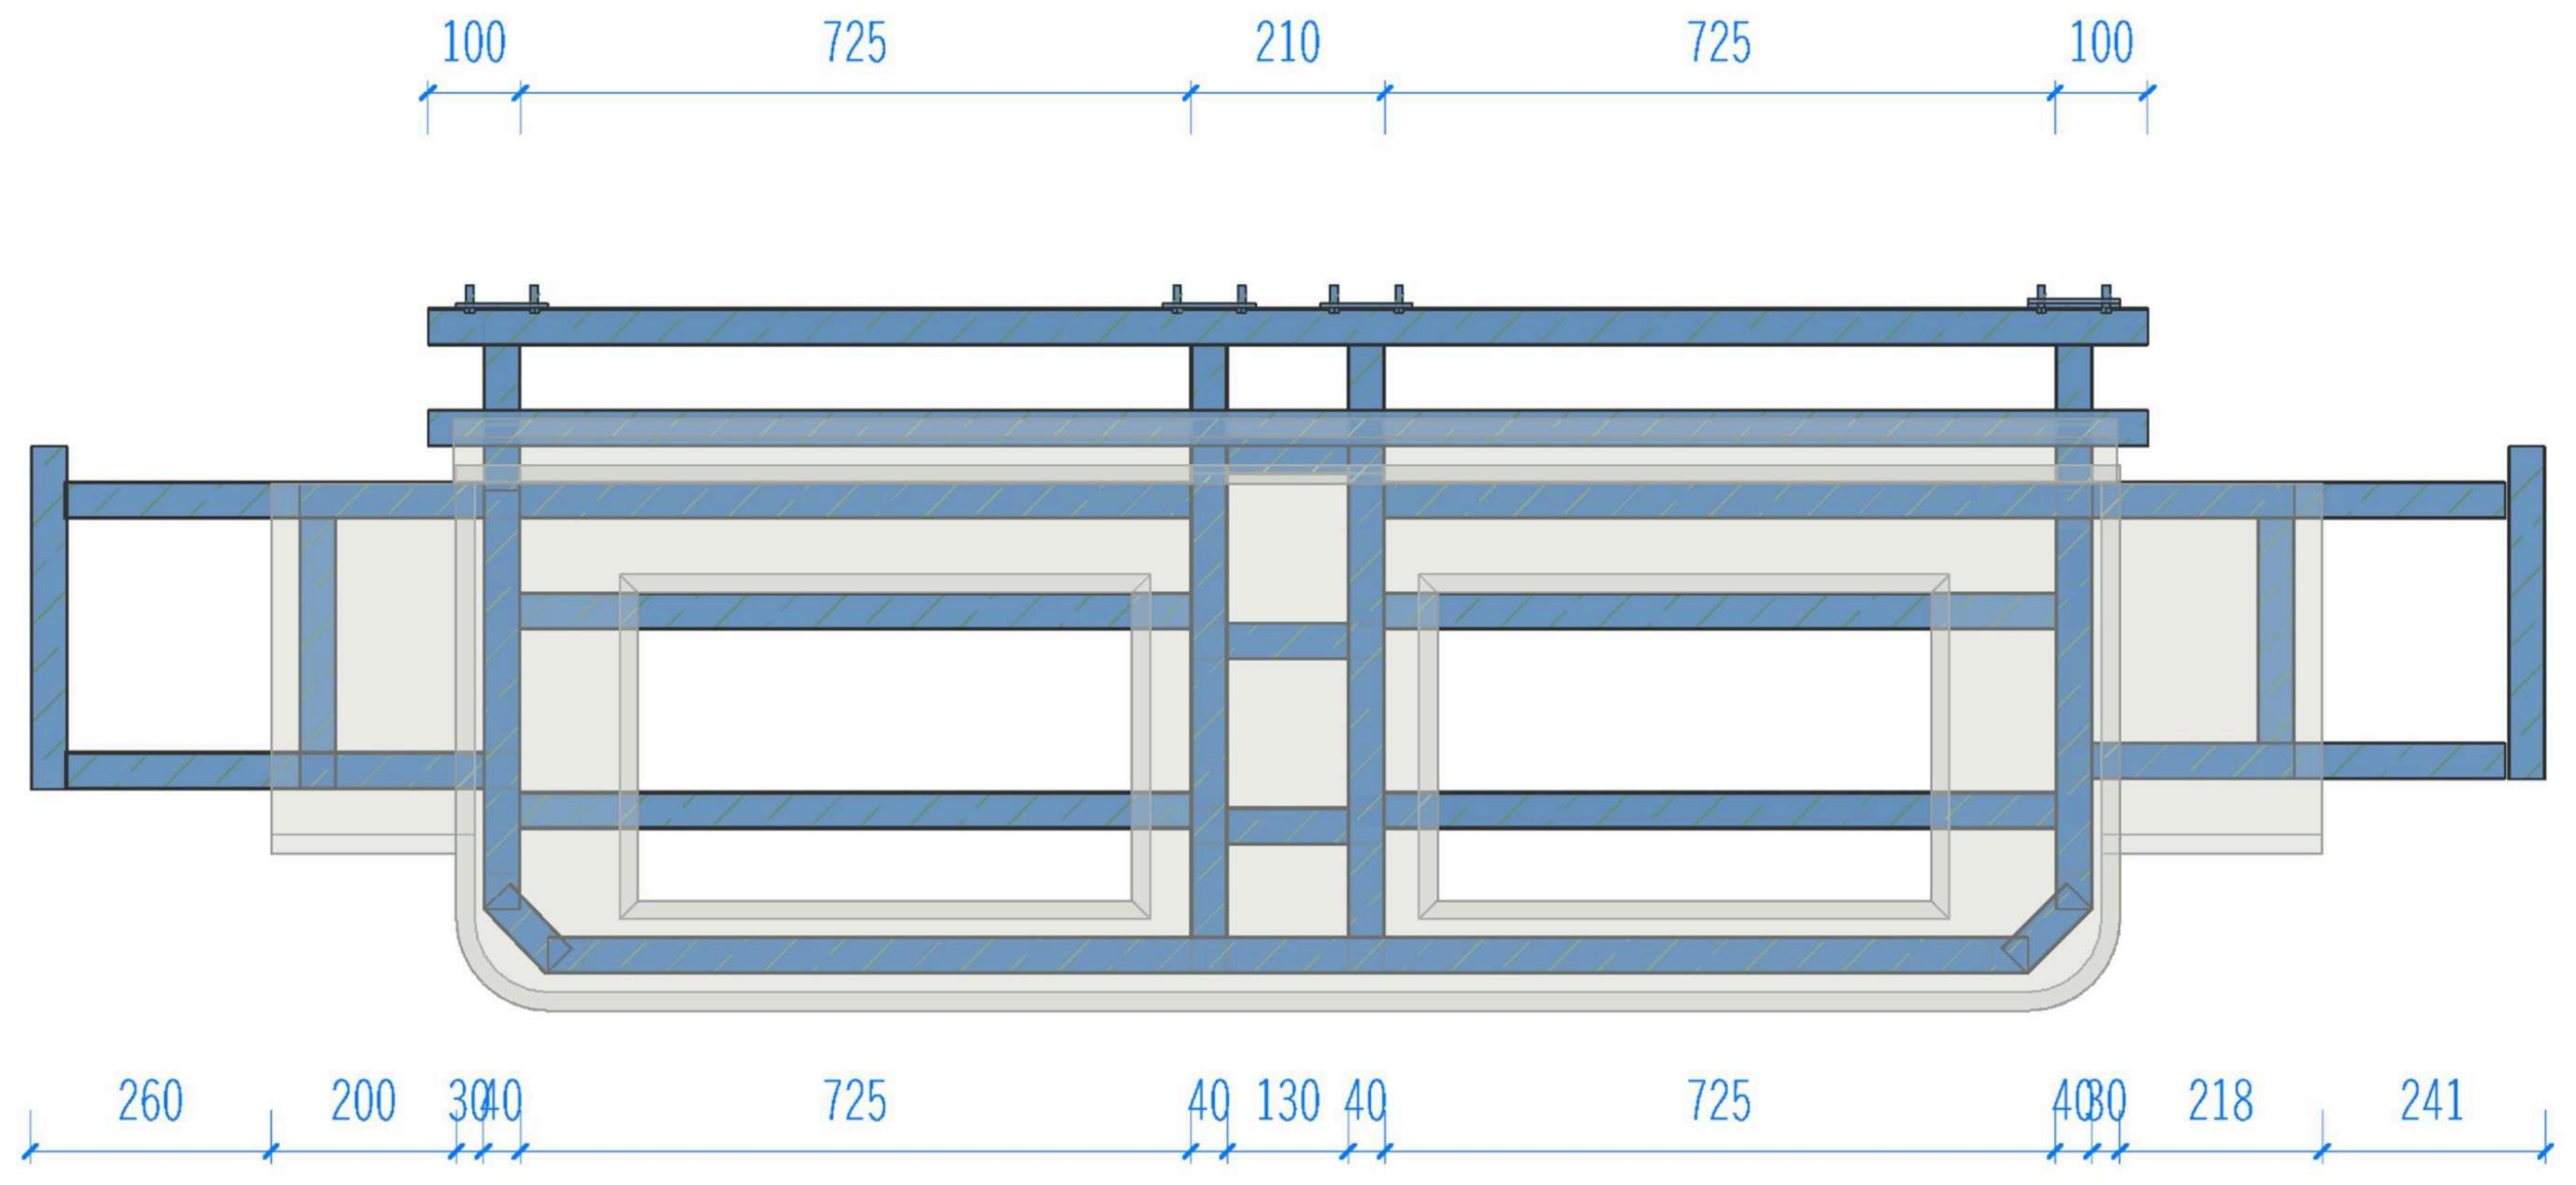
100
725
210
725
100
260
200
30
40
725
40
130
40
725
40
30
218
241

平面视图

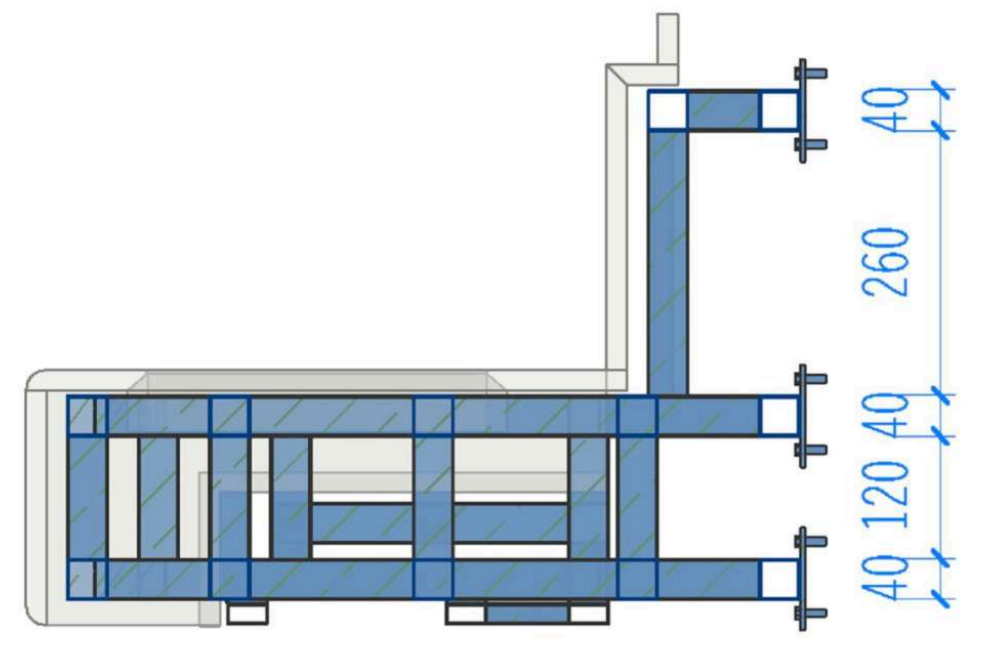
40
260
40
120
40

剖面视图

工厂预制钢架

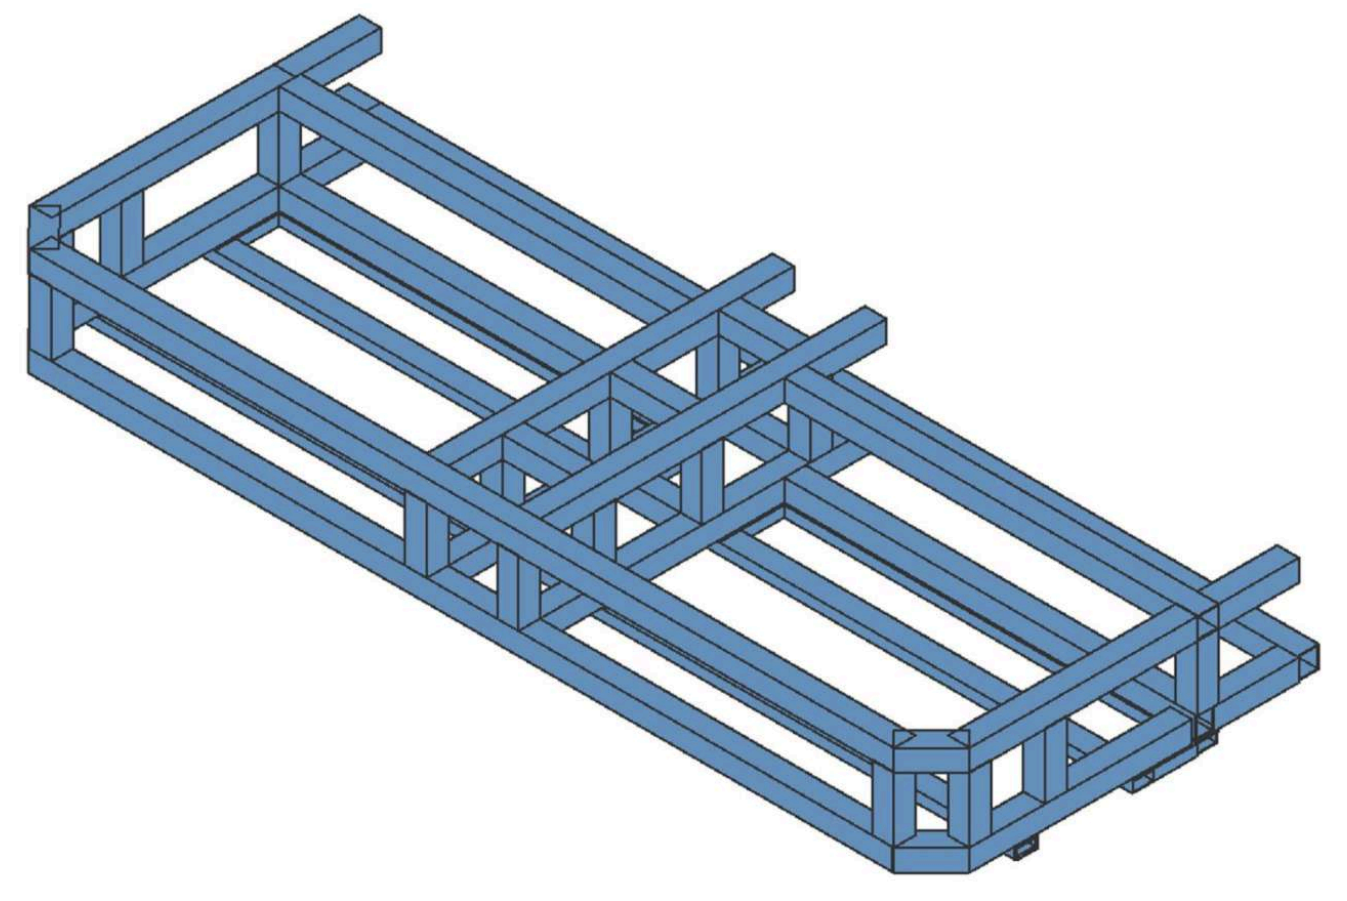

①

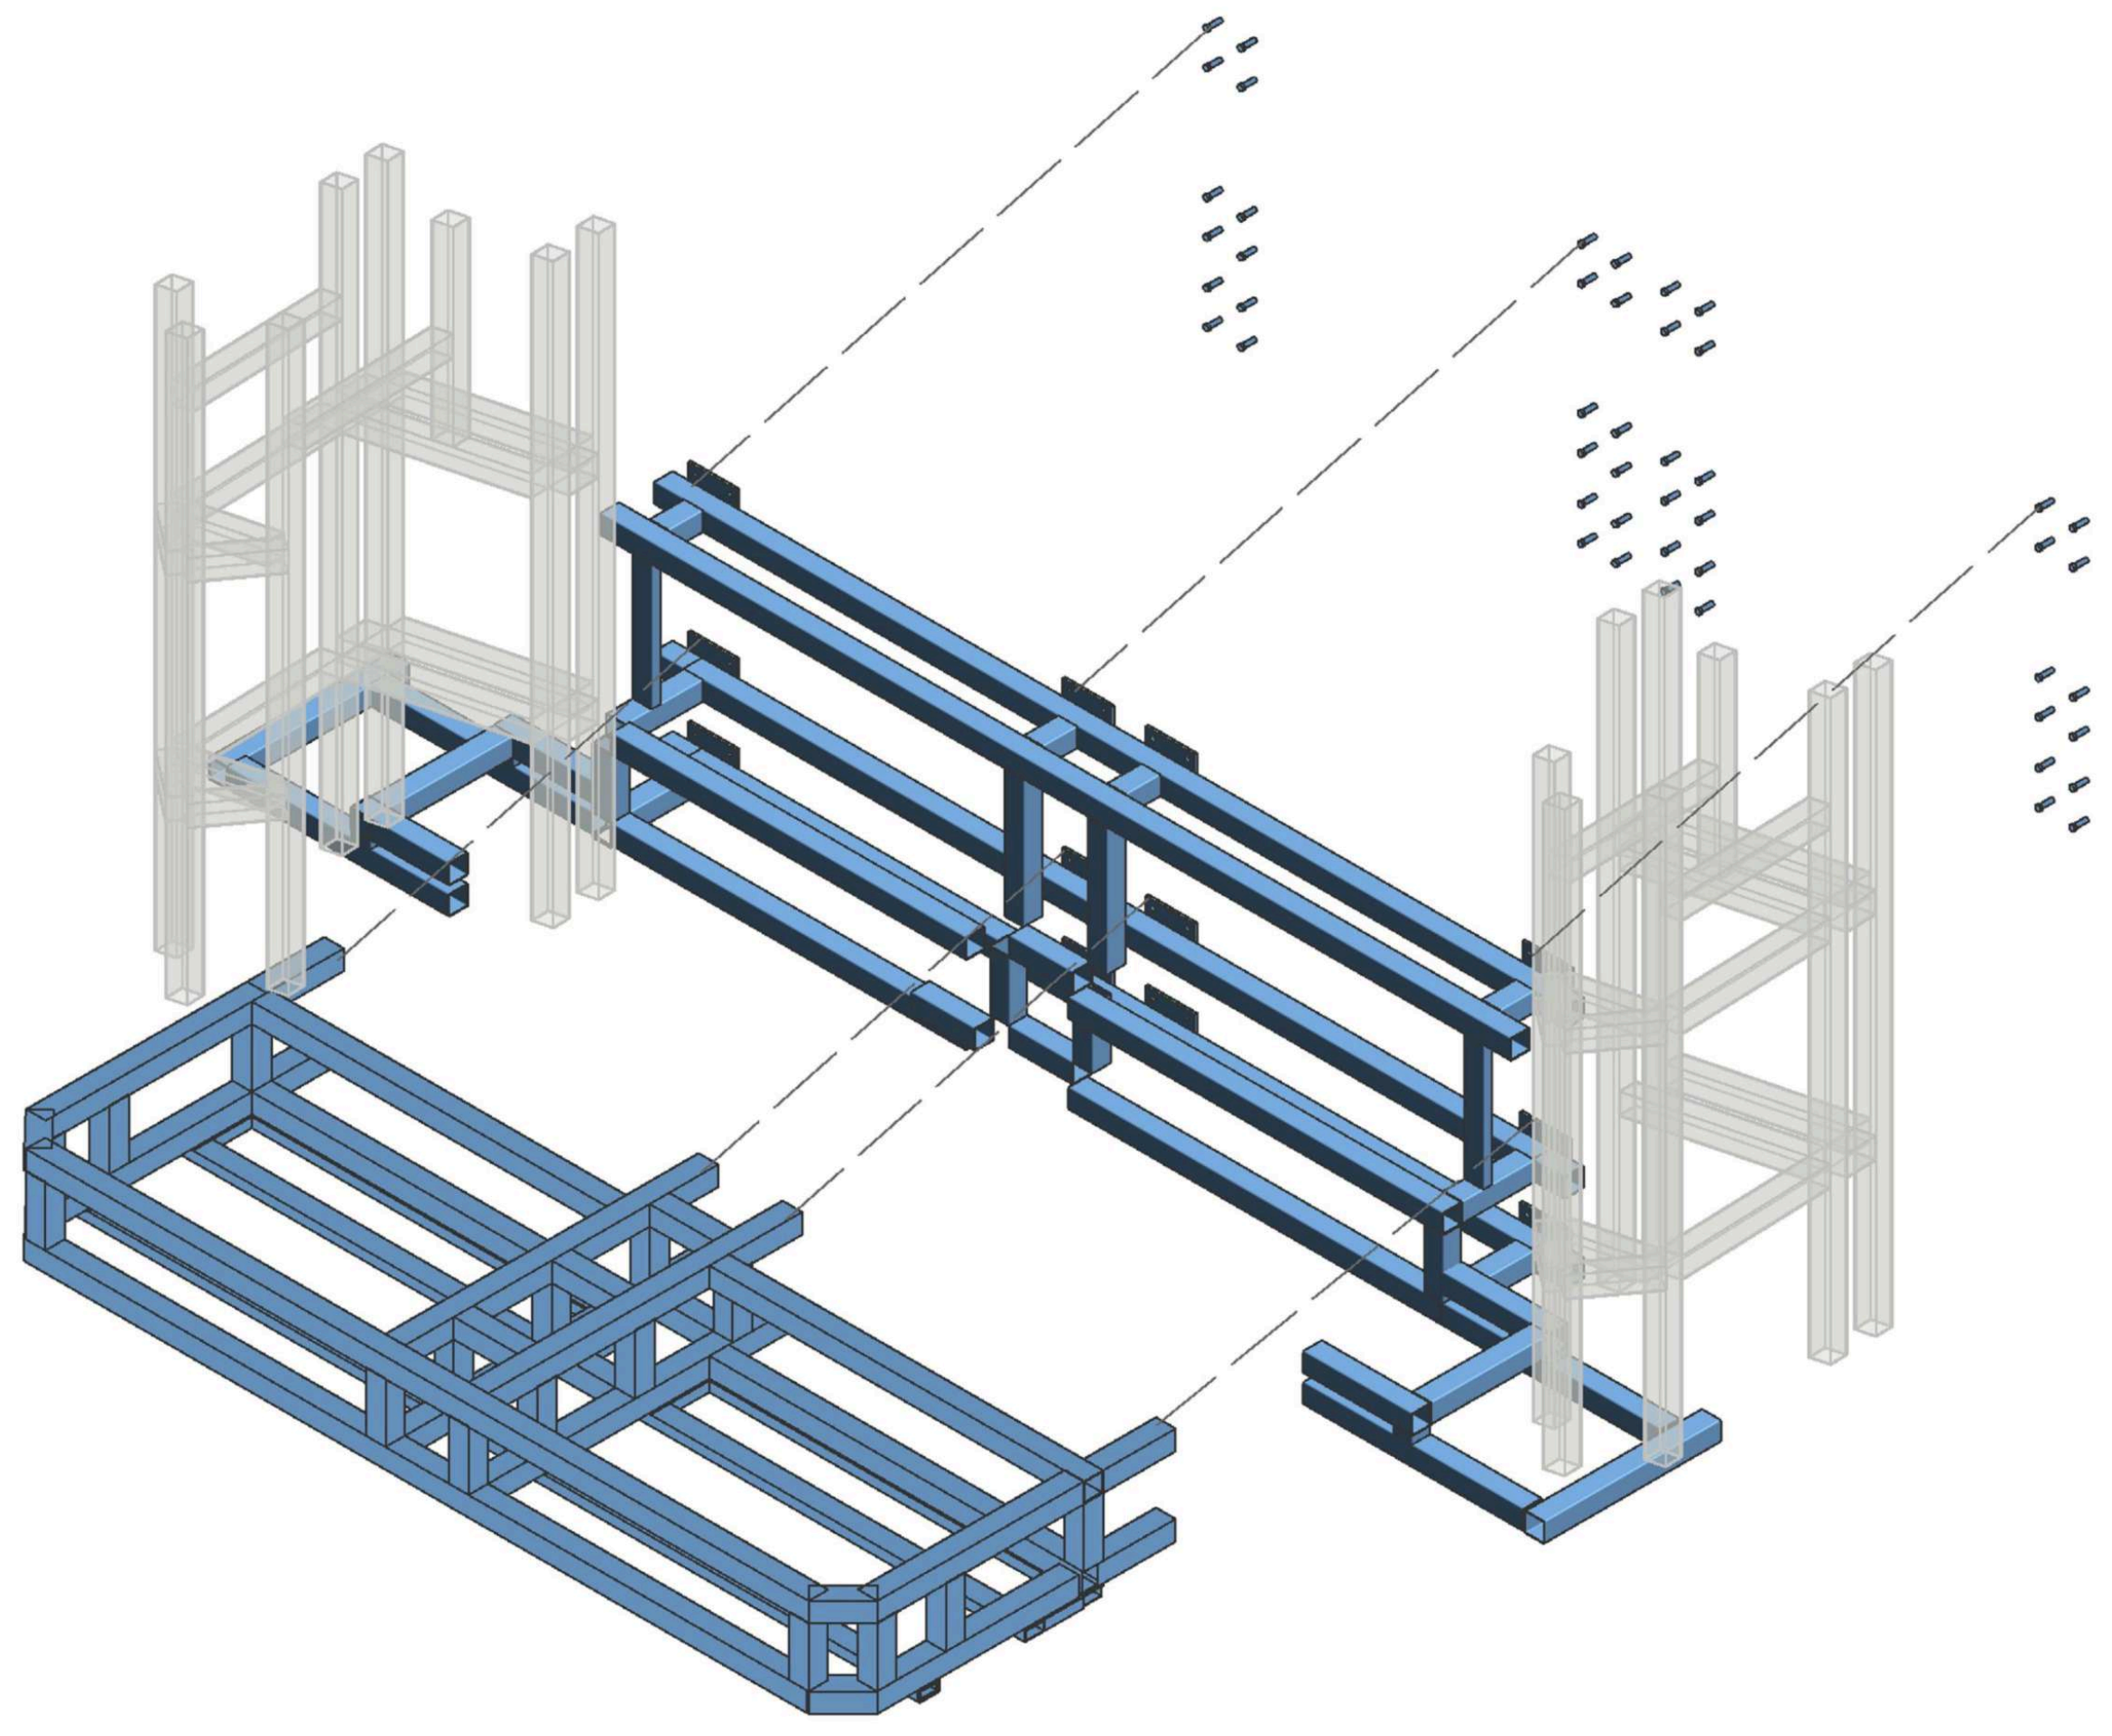

②

③

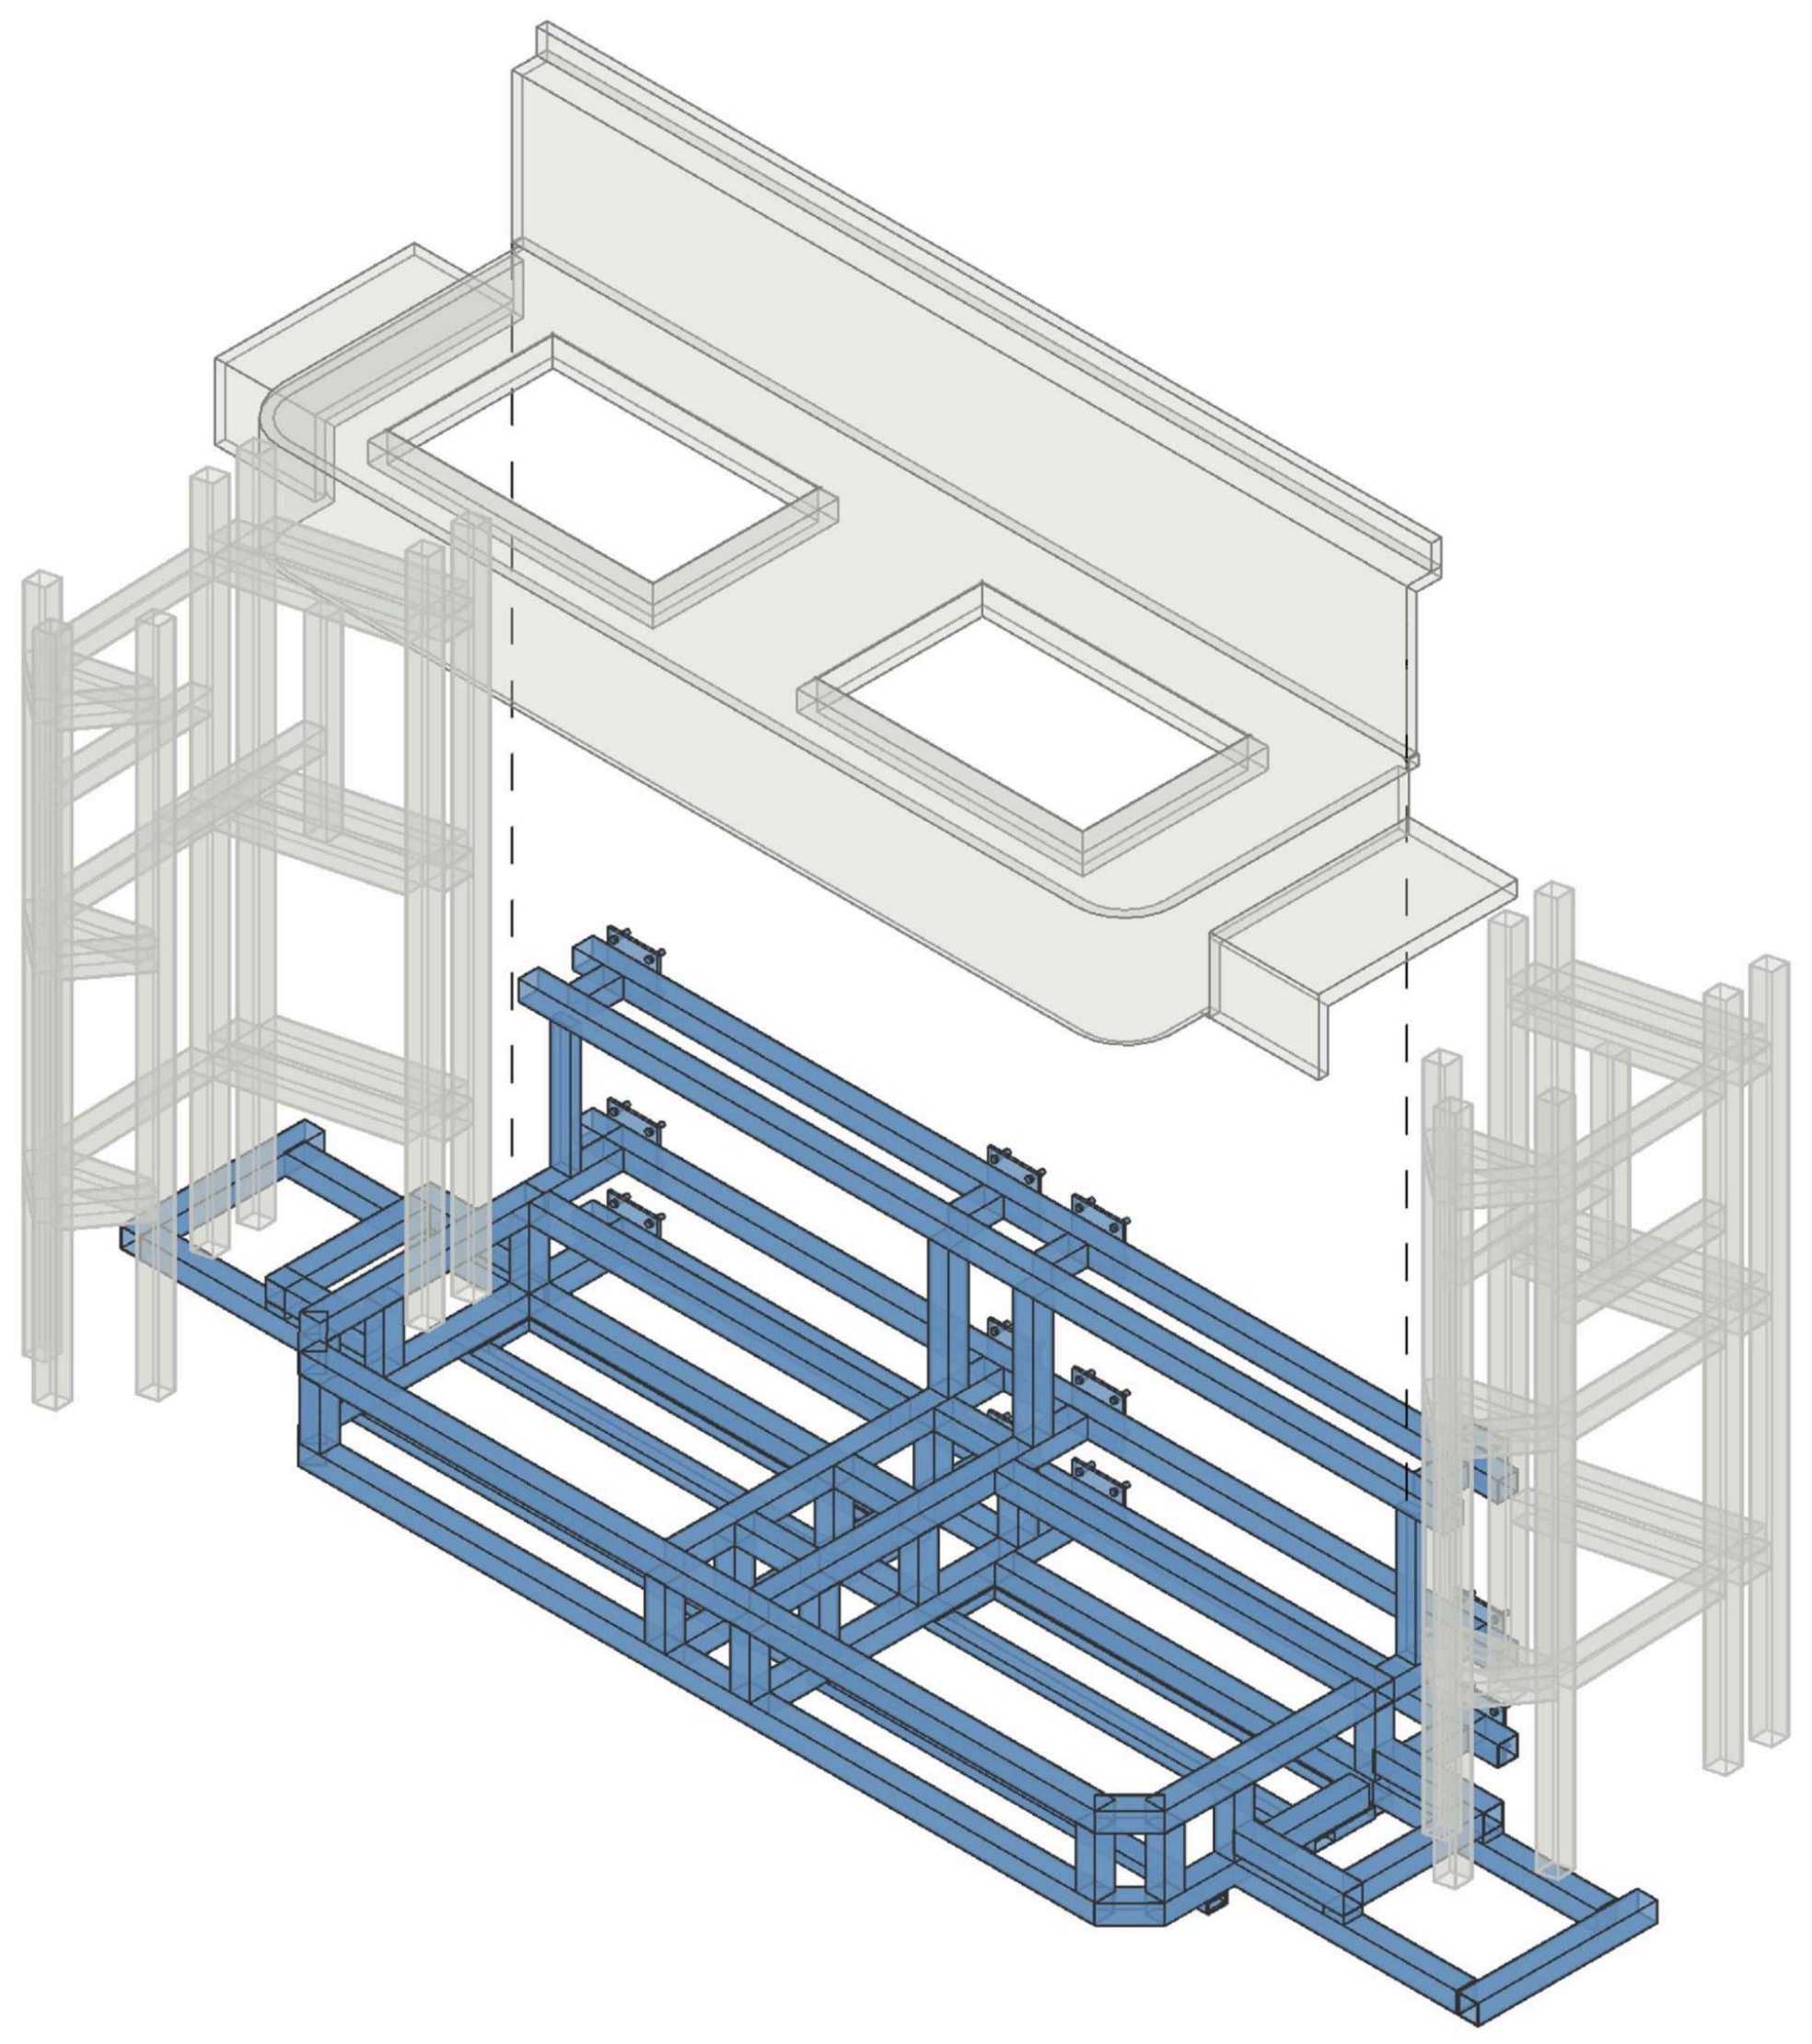

④

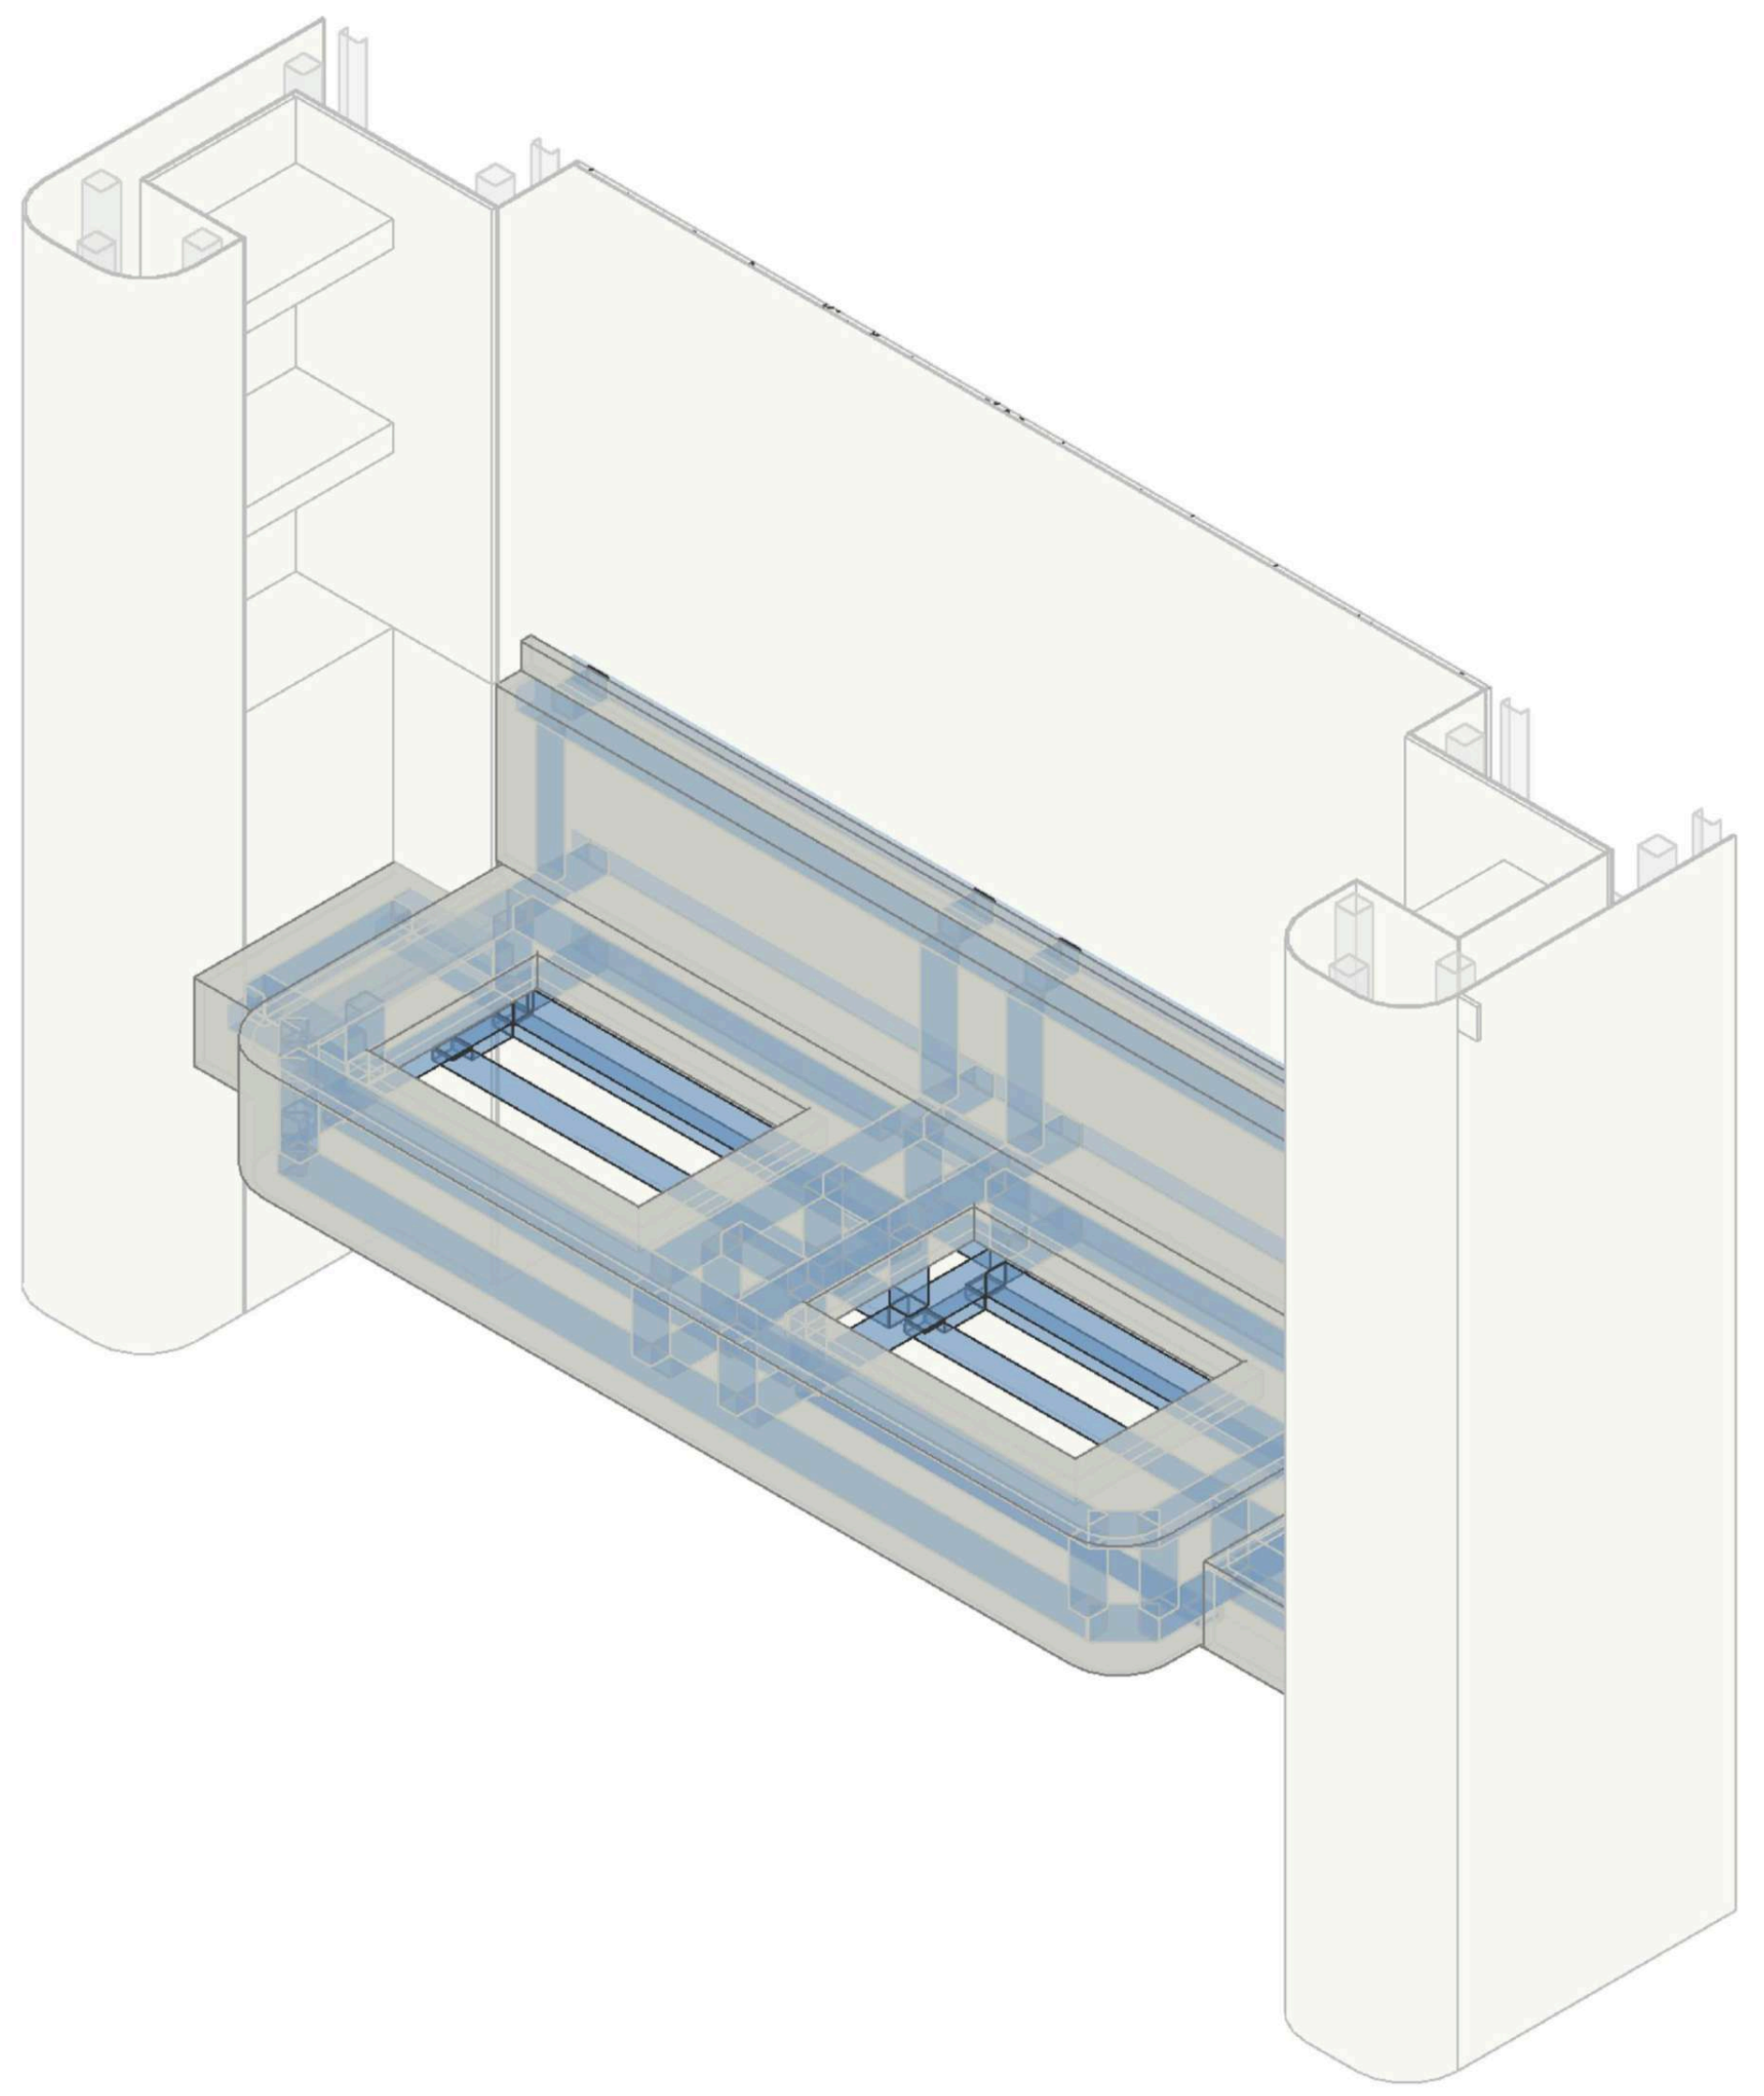

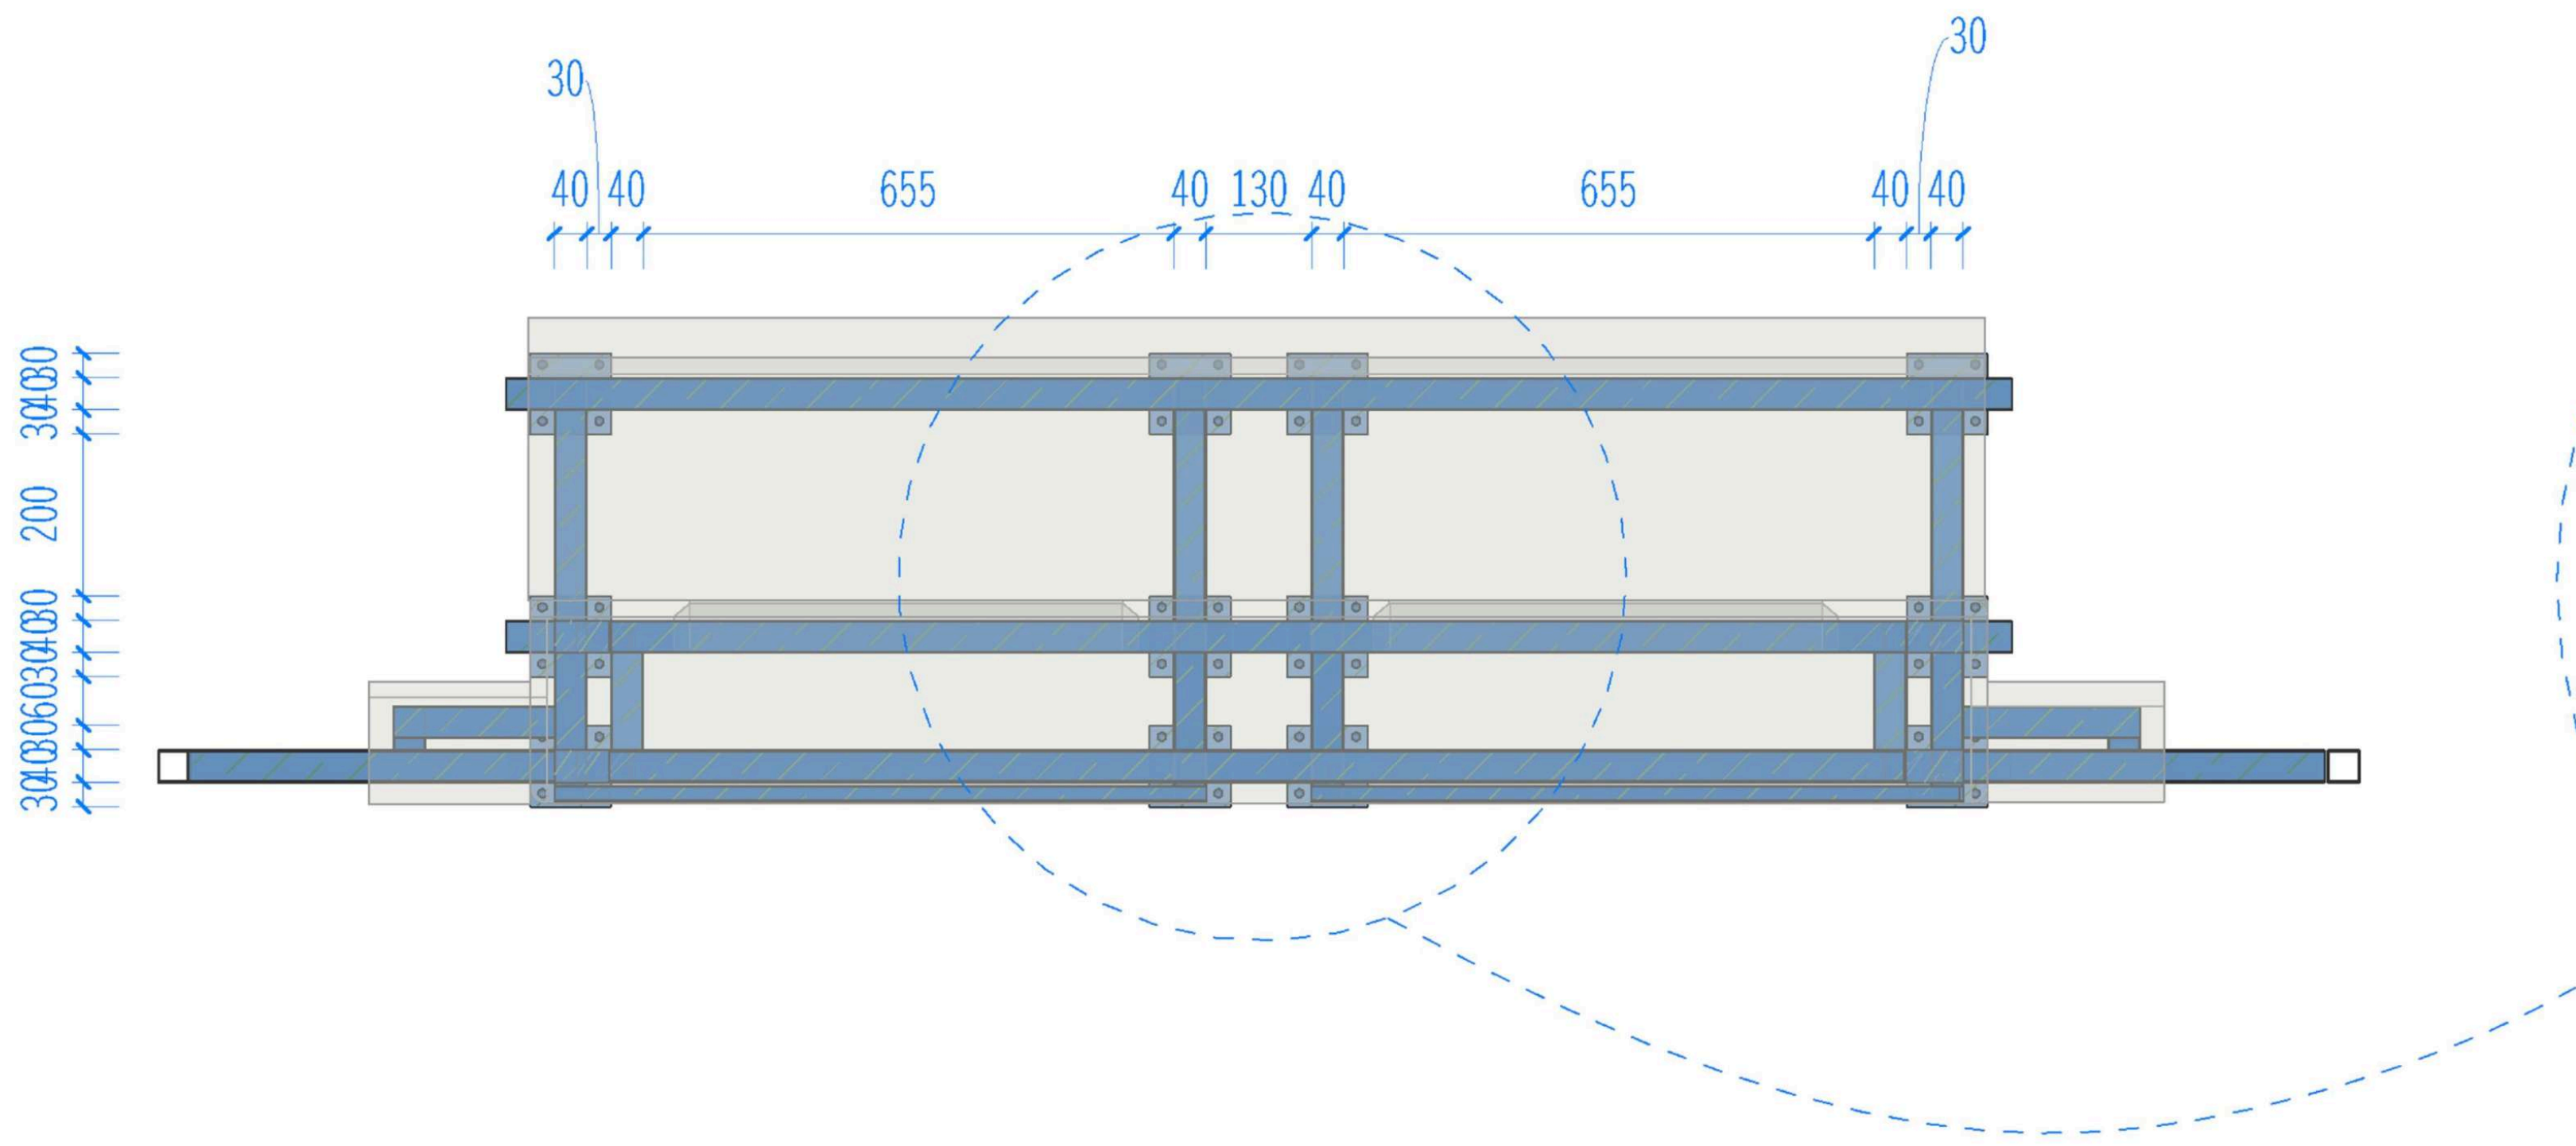
30
30
40
40
655
40
130
40
655
40
40
30
40
30
200
30
40
30
60
30
40
30

立面视图

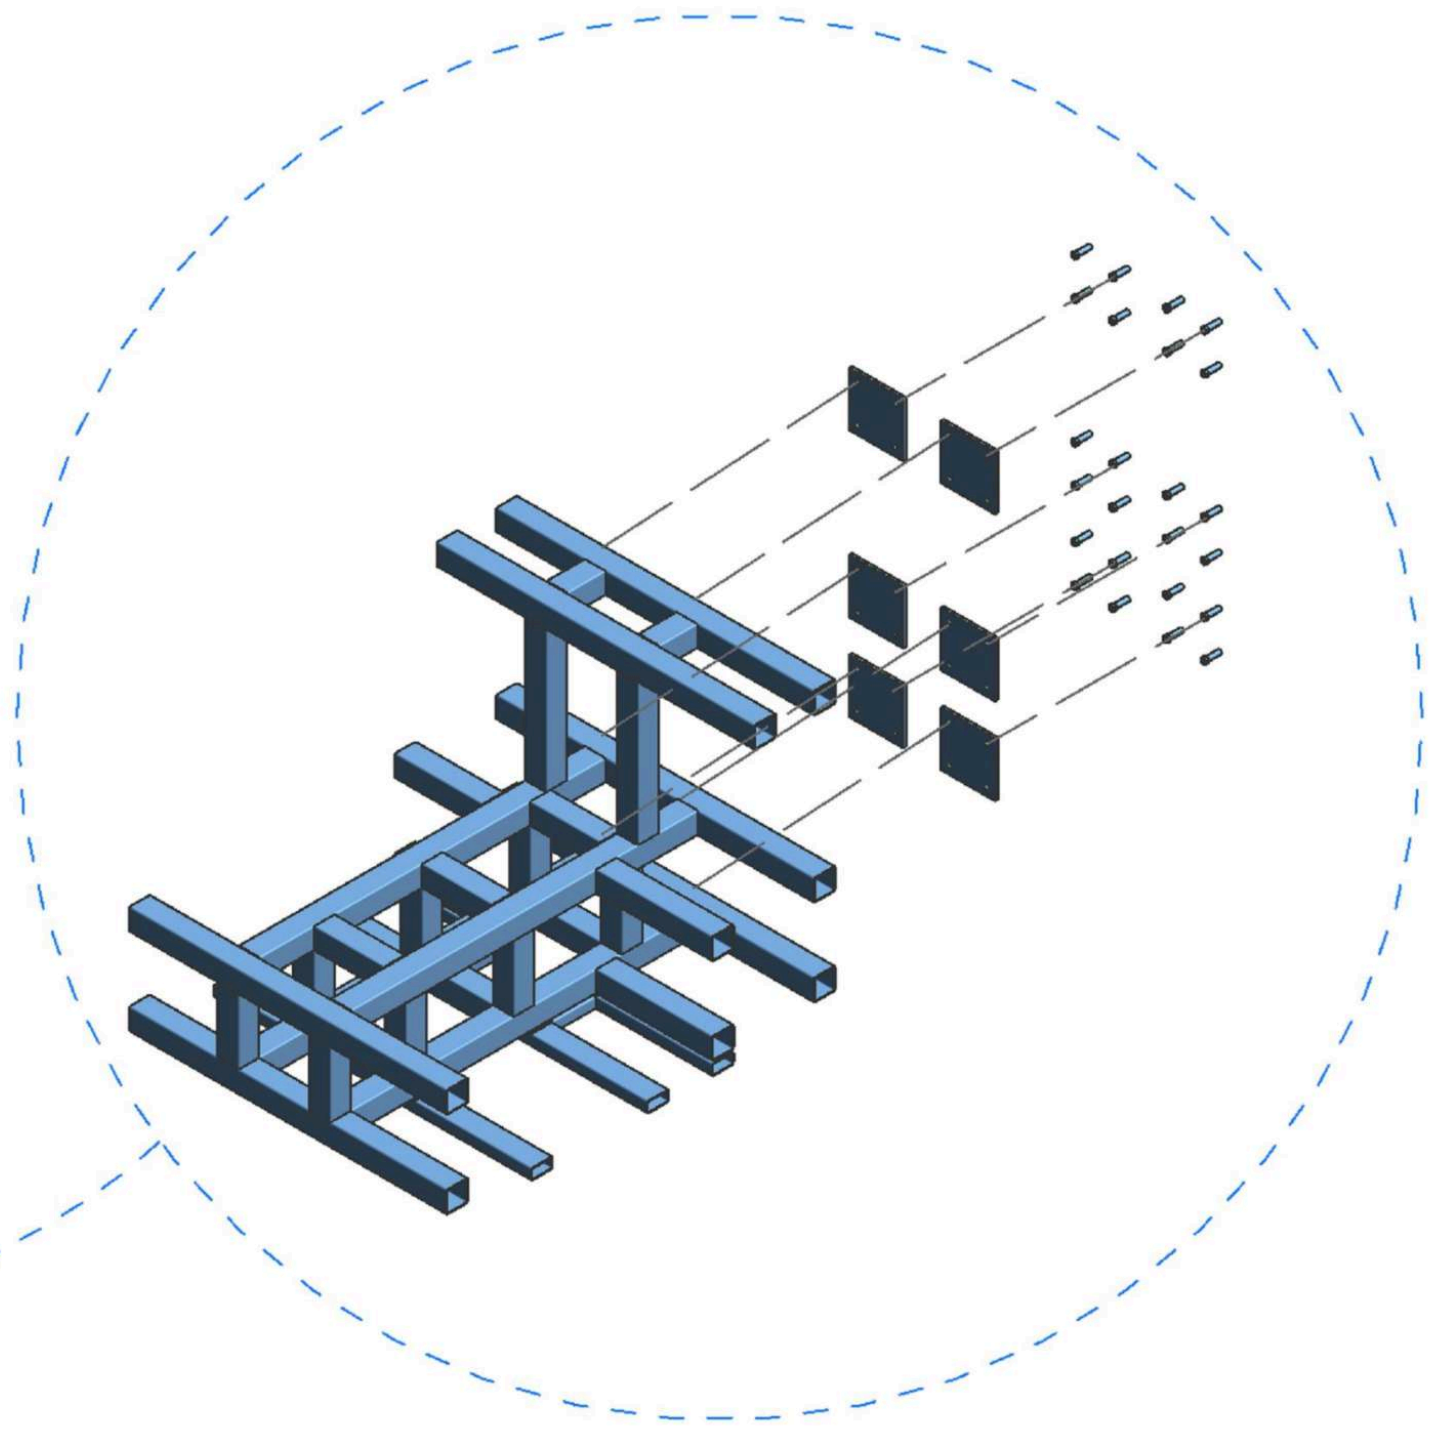

节点图

FIBORN

1

图例A
LEGEND A

编号	图例	说明
1		原始钢架
2		螺栓
3		钢片
4		钢架
5		石材

盖章

注释
Notes
1.本图纸如与现场尺寸有误，请施工人员与项目负责人联系。
2.施工前施工人员应认真查阅此图，如有不明确尺寸，按现场测量为准。
3.本图纸必须经甲乙双方认可并签字方可作为施工依据。

日期
Date 05/07/26

修订
Revision

△1

项目
Project
潮映华岸府3-801

比例
Scale

主卫洗手台石材钢架

图纸编号
Drawing No.
ST-01

项目编号
Project No.

©2025

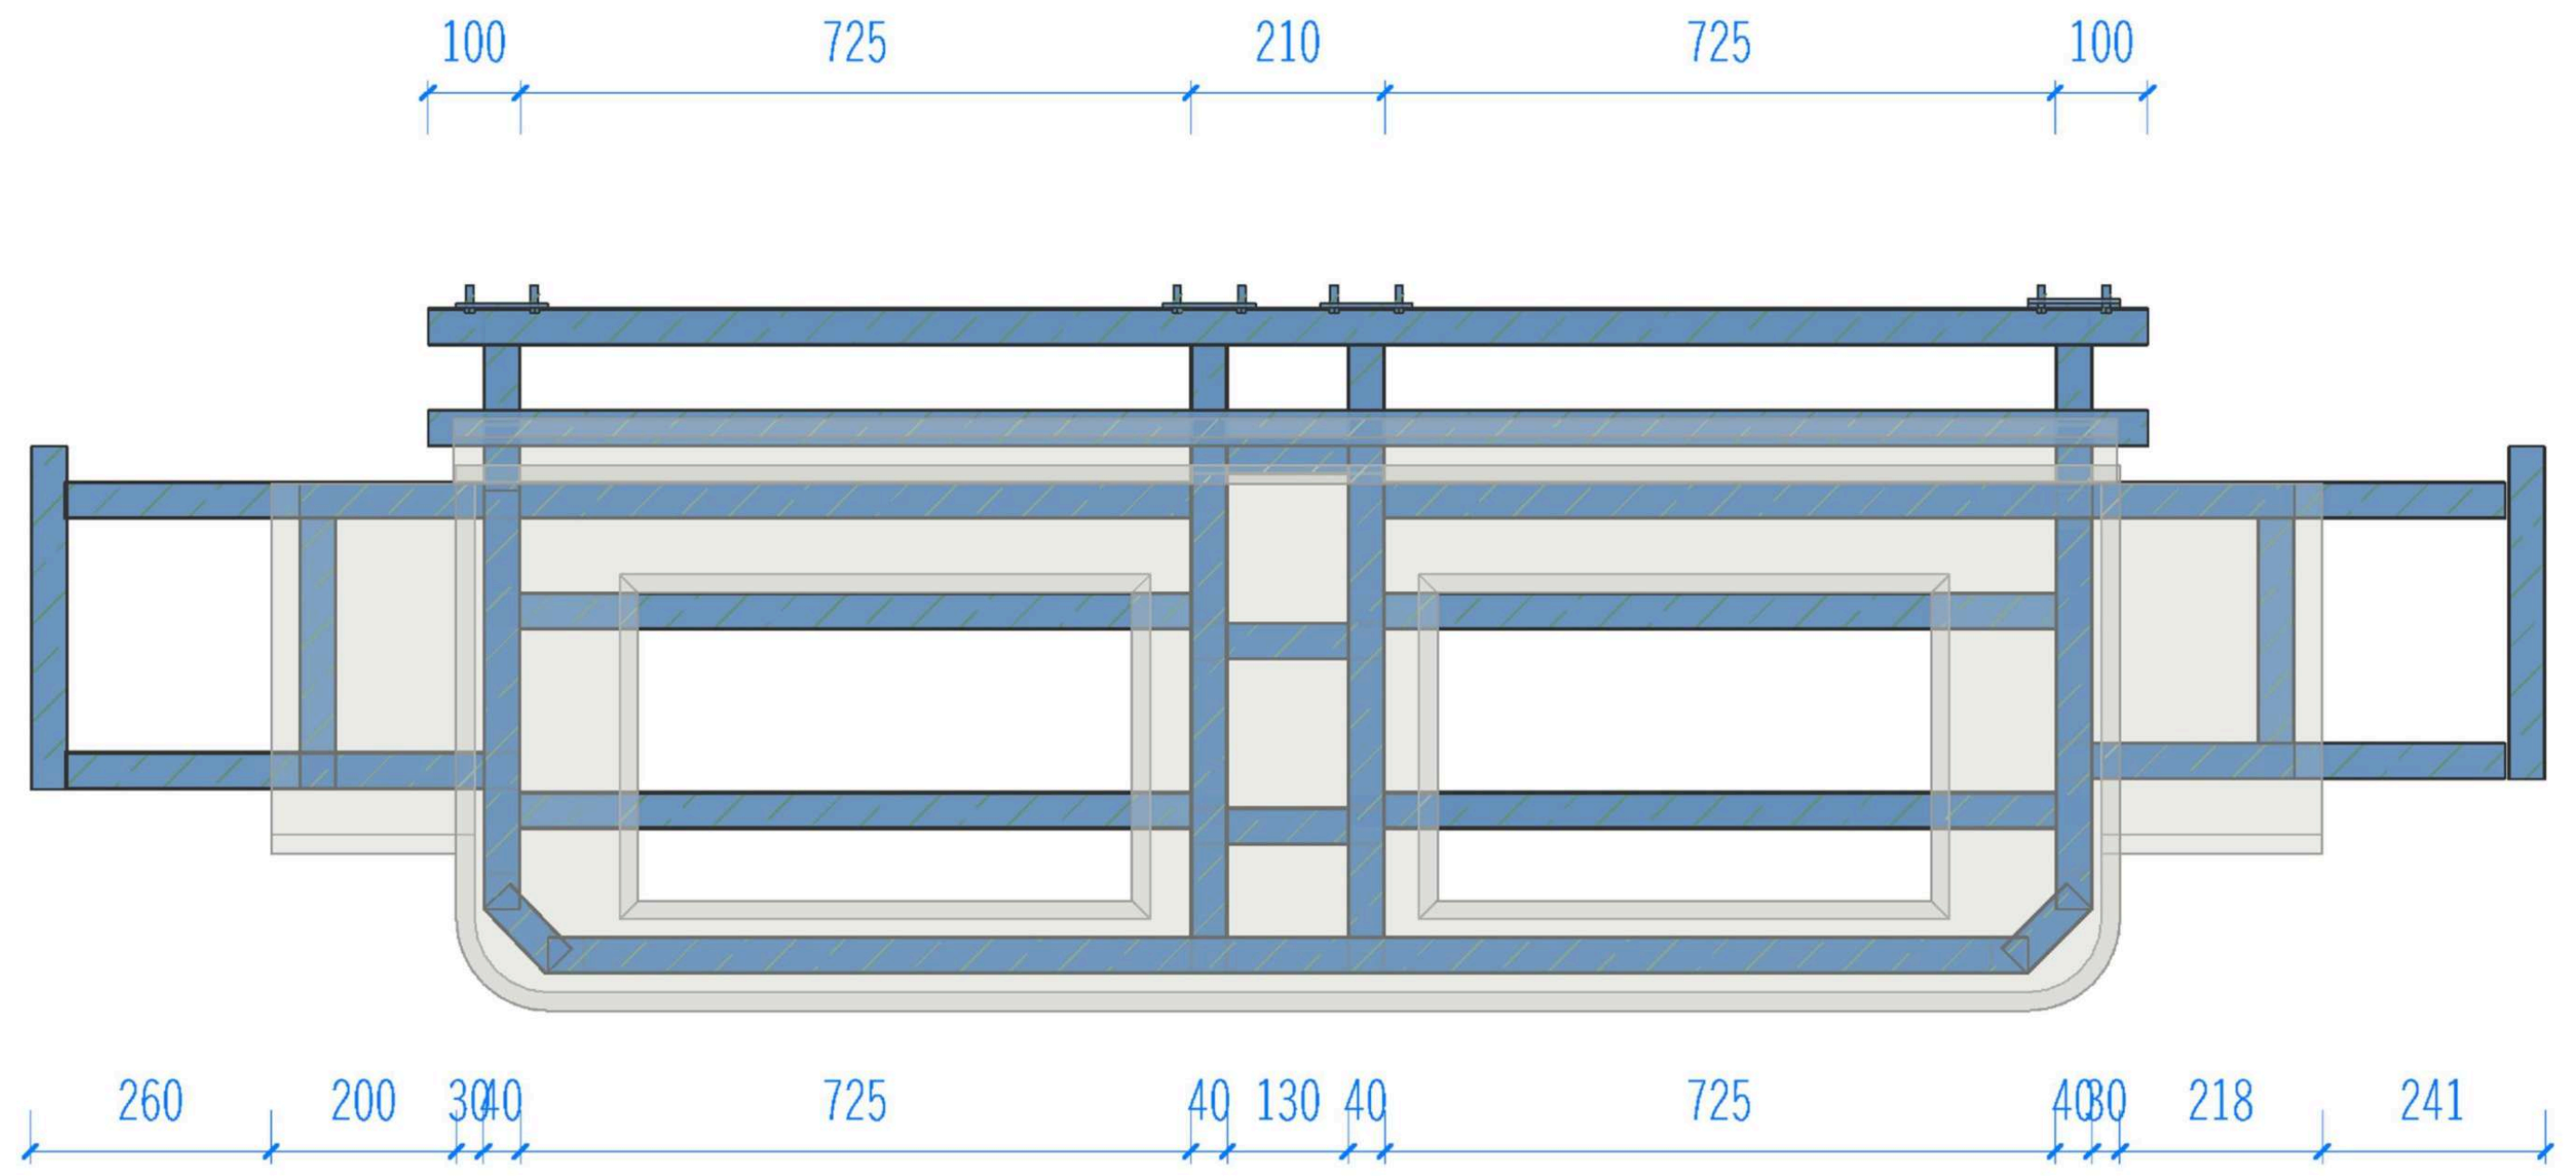
100
725
210
725
100
260
200
30
40
725
40
130
40
725
40
30
218
241

平面视图

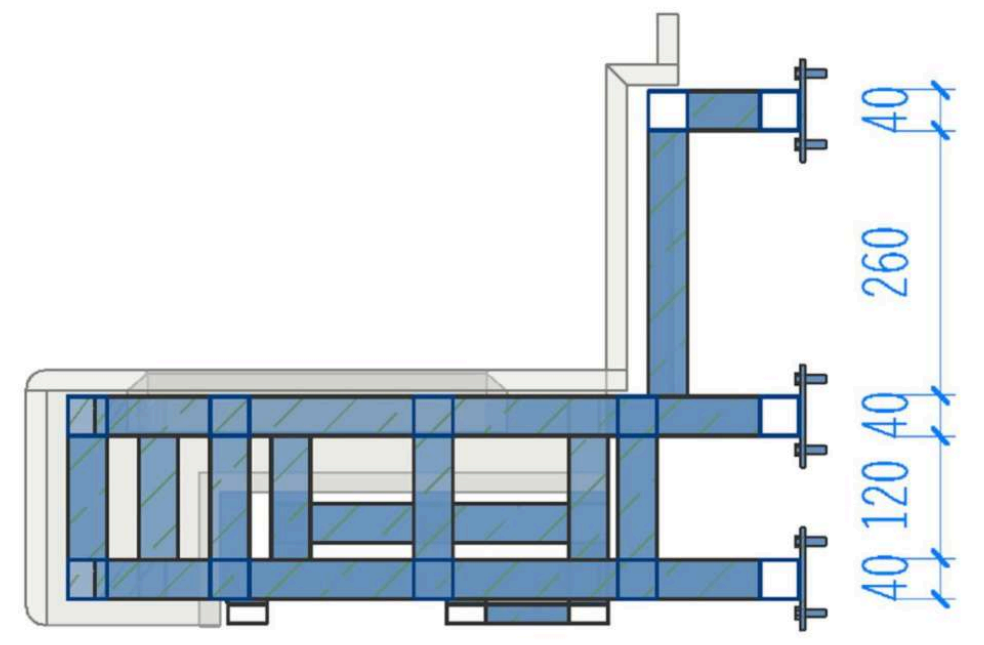
40
260
40
120
40

剖面视图

工厂预制钢架

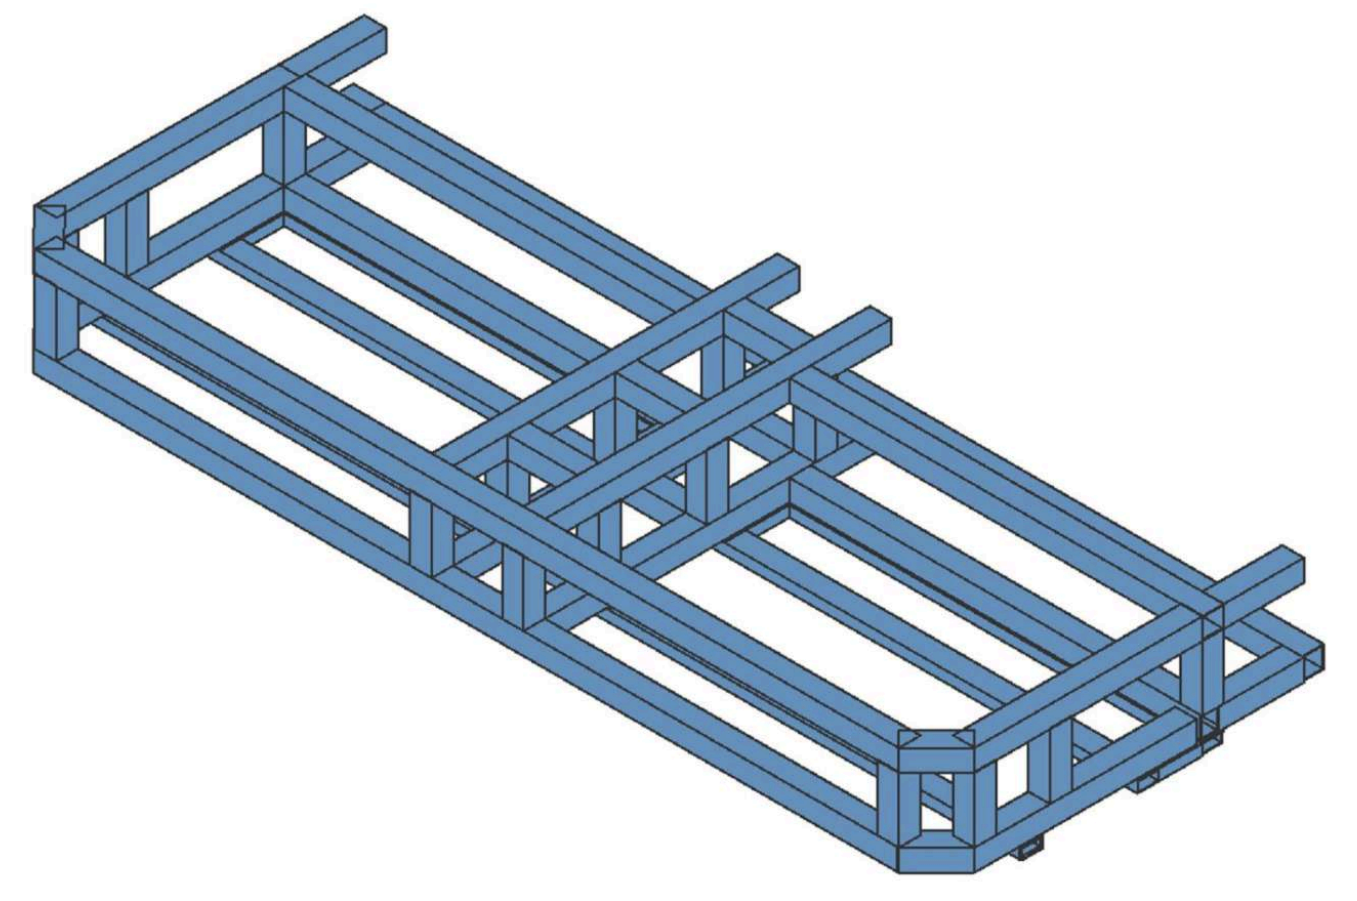

①

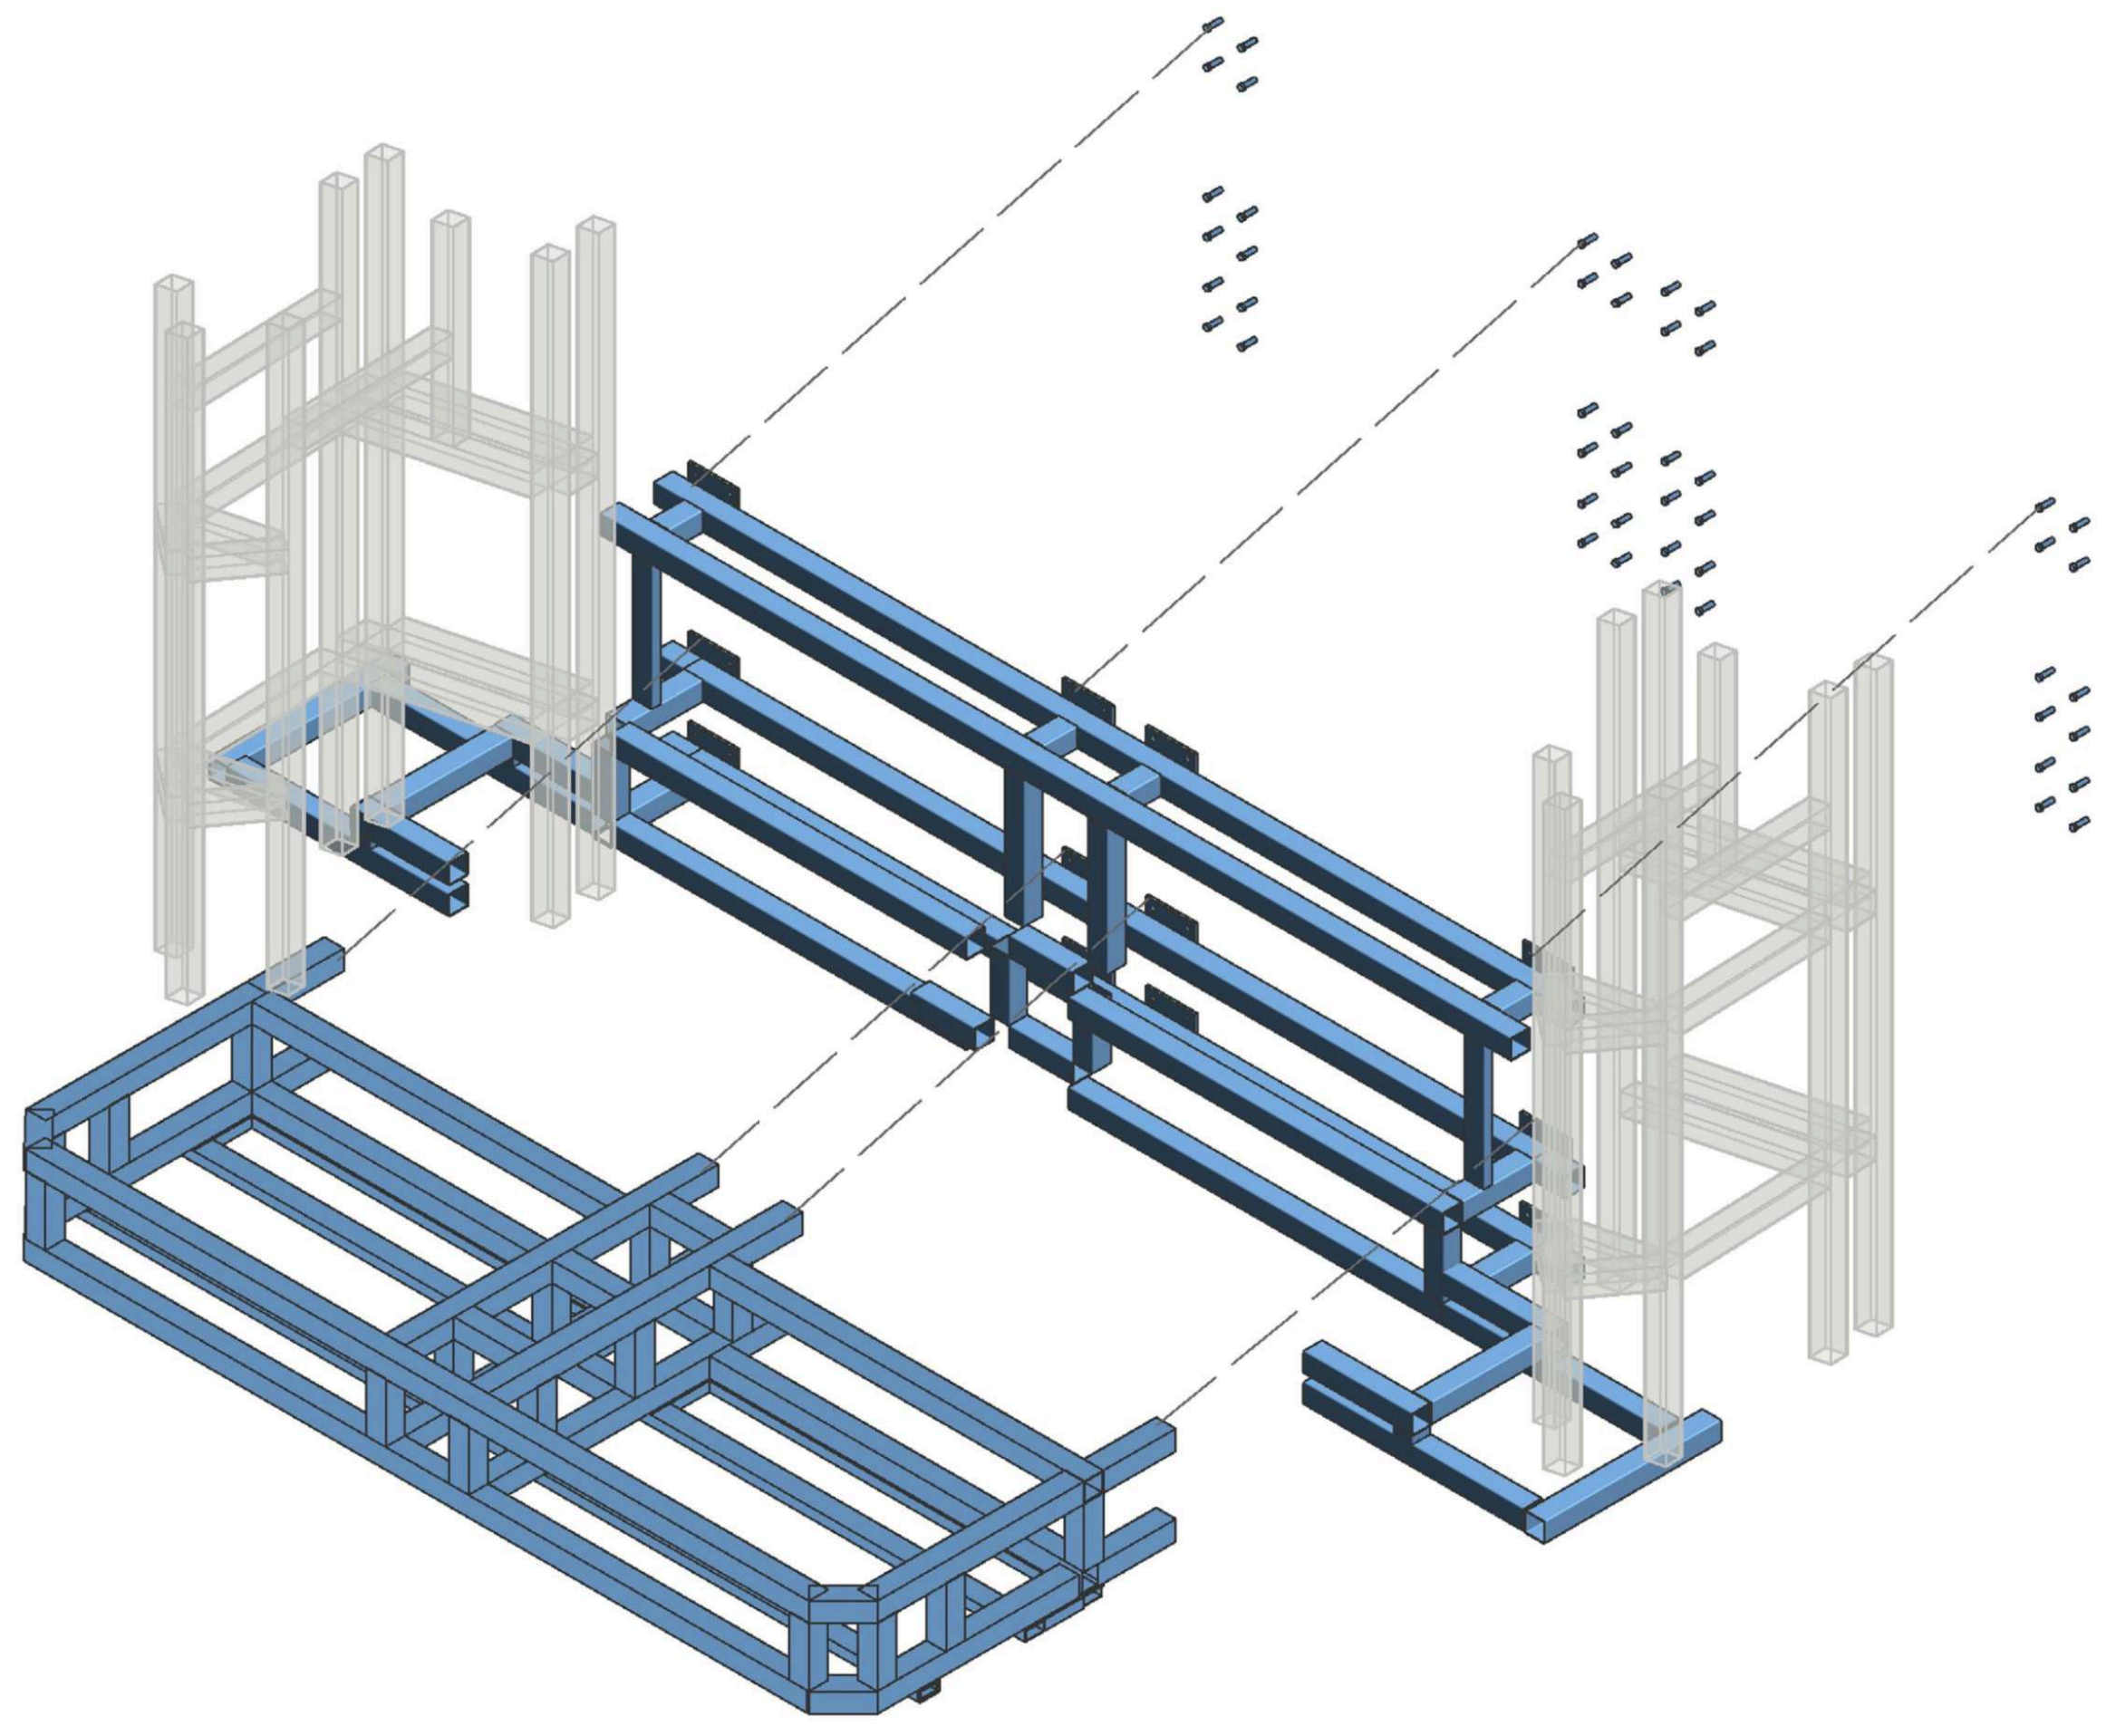

②

③

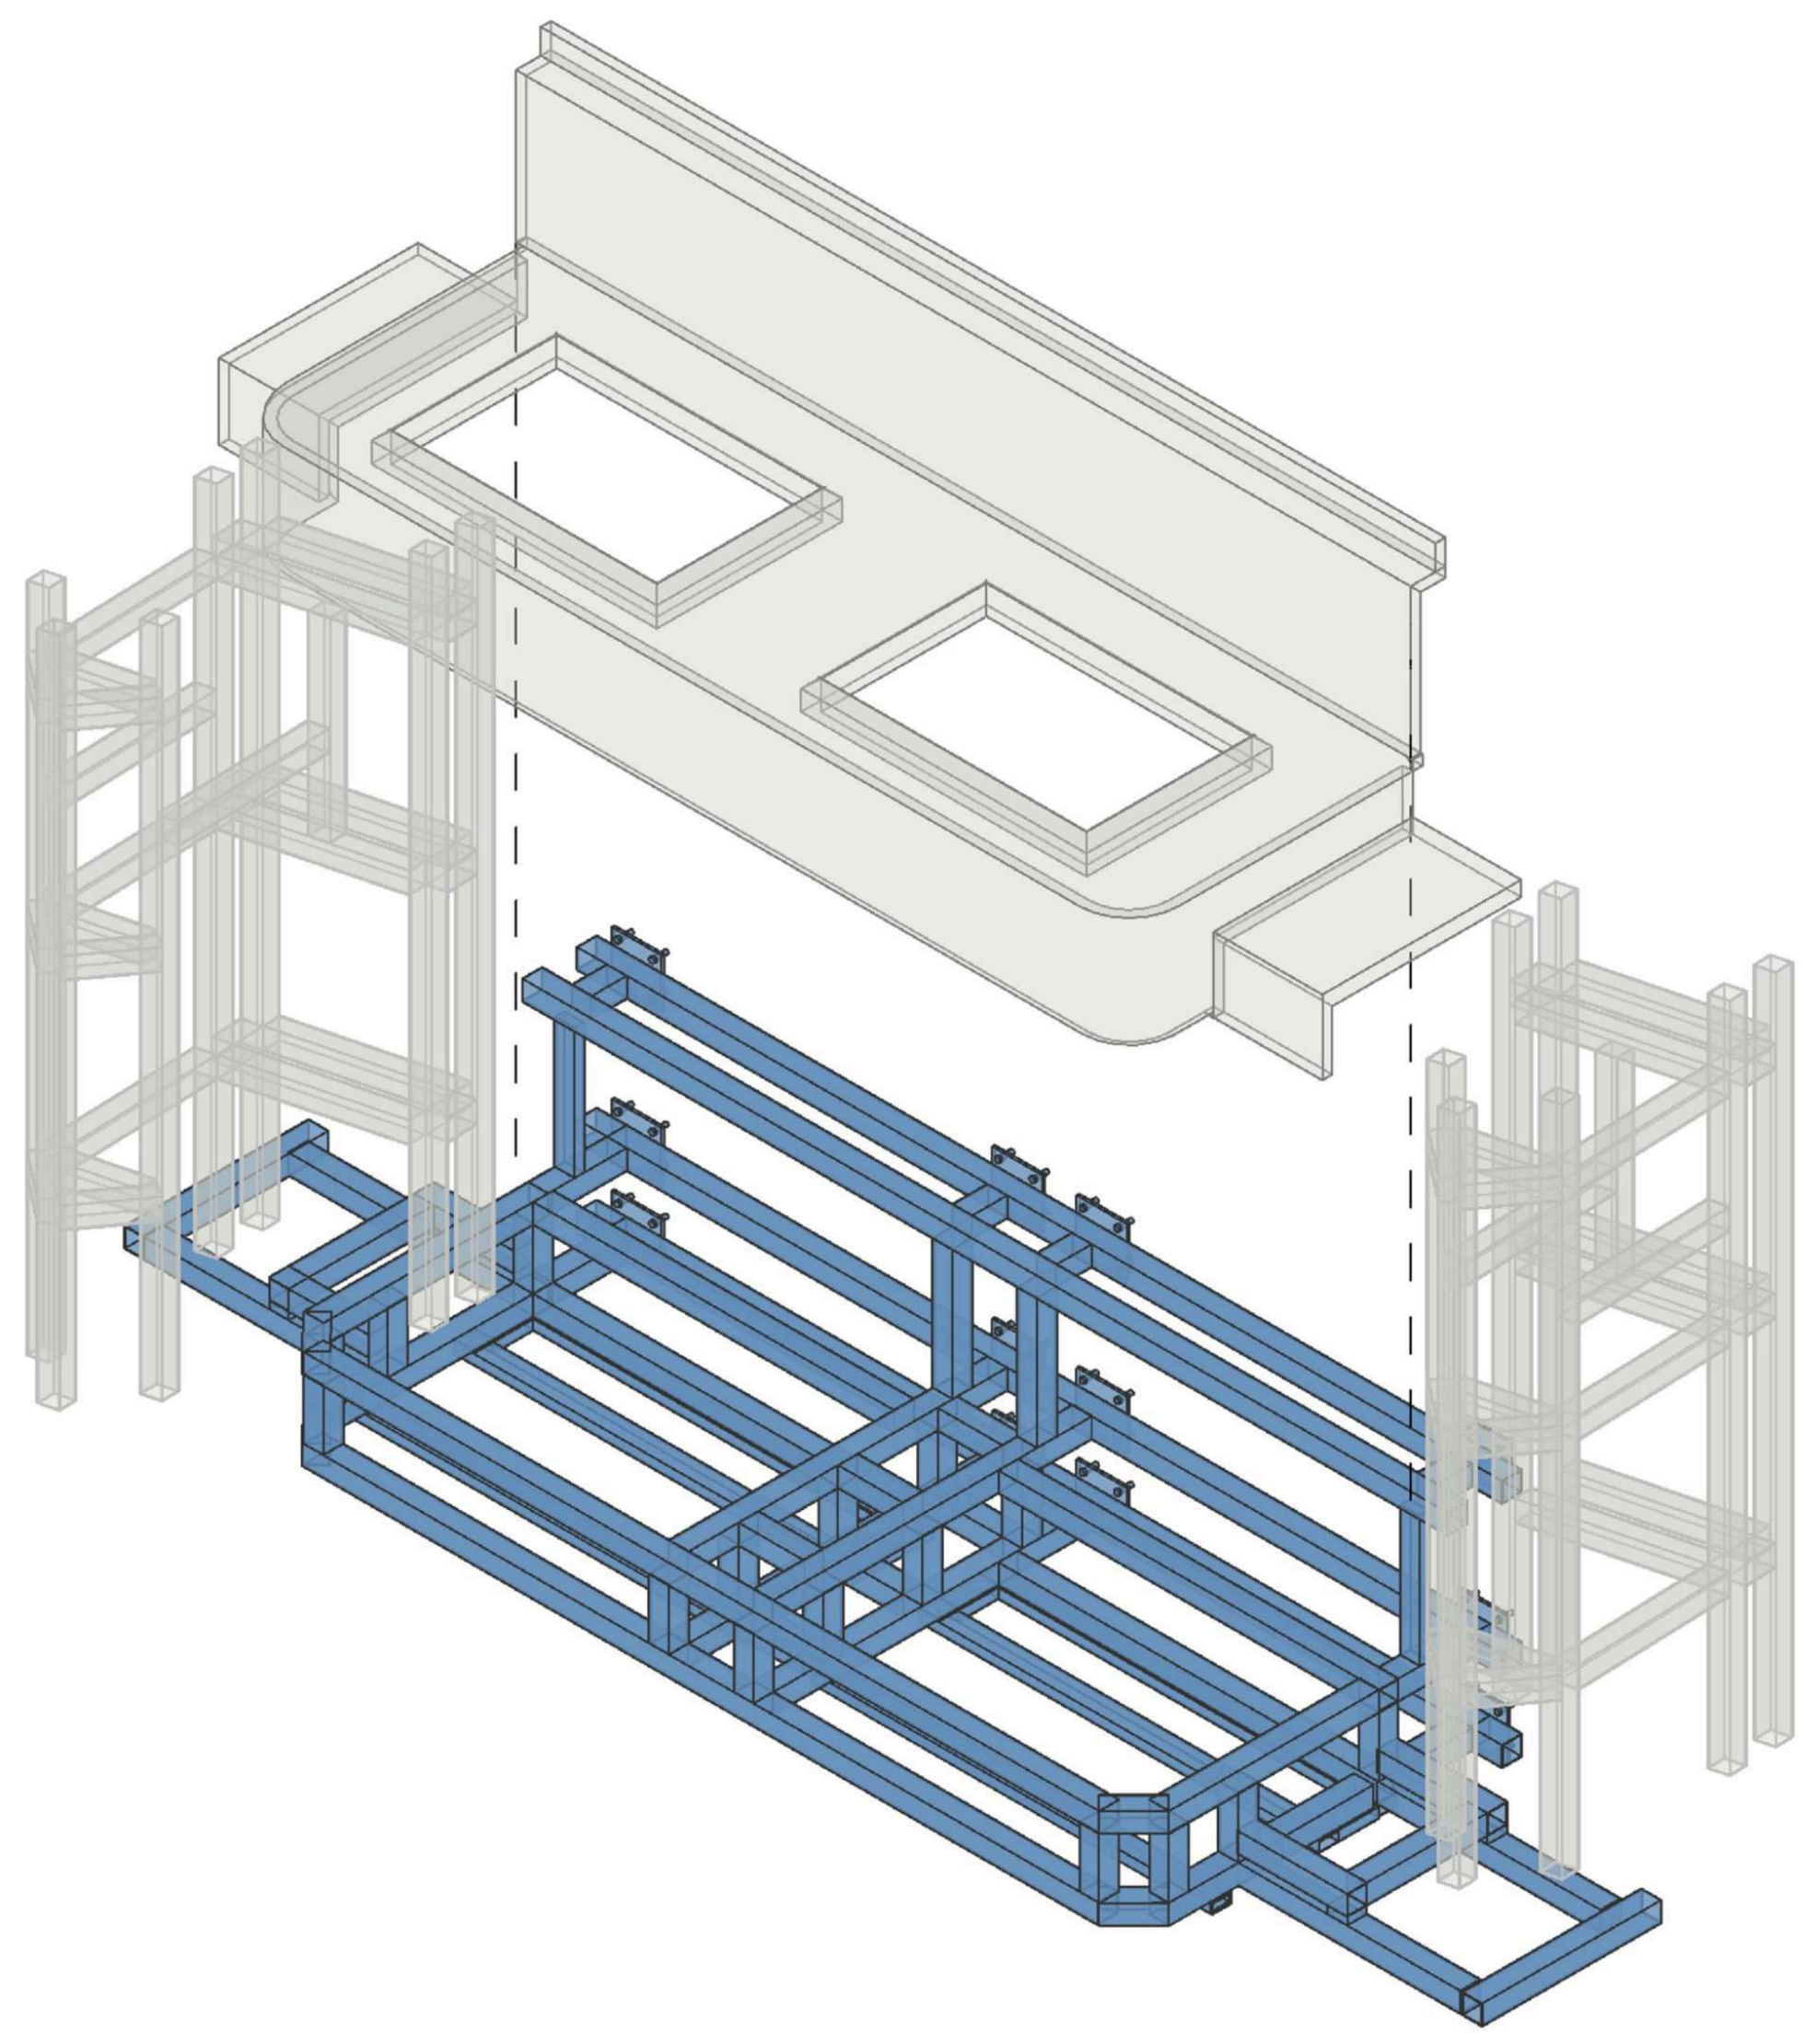

④

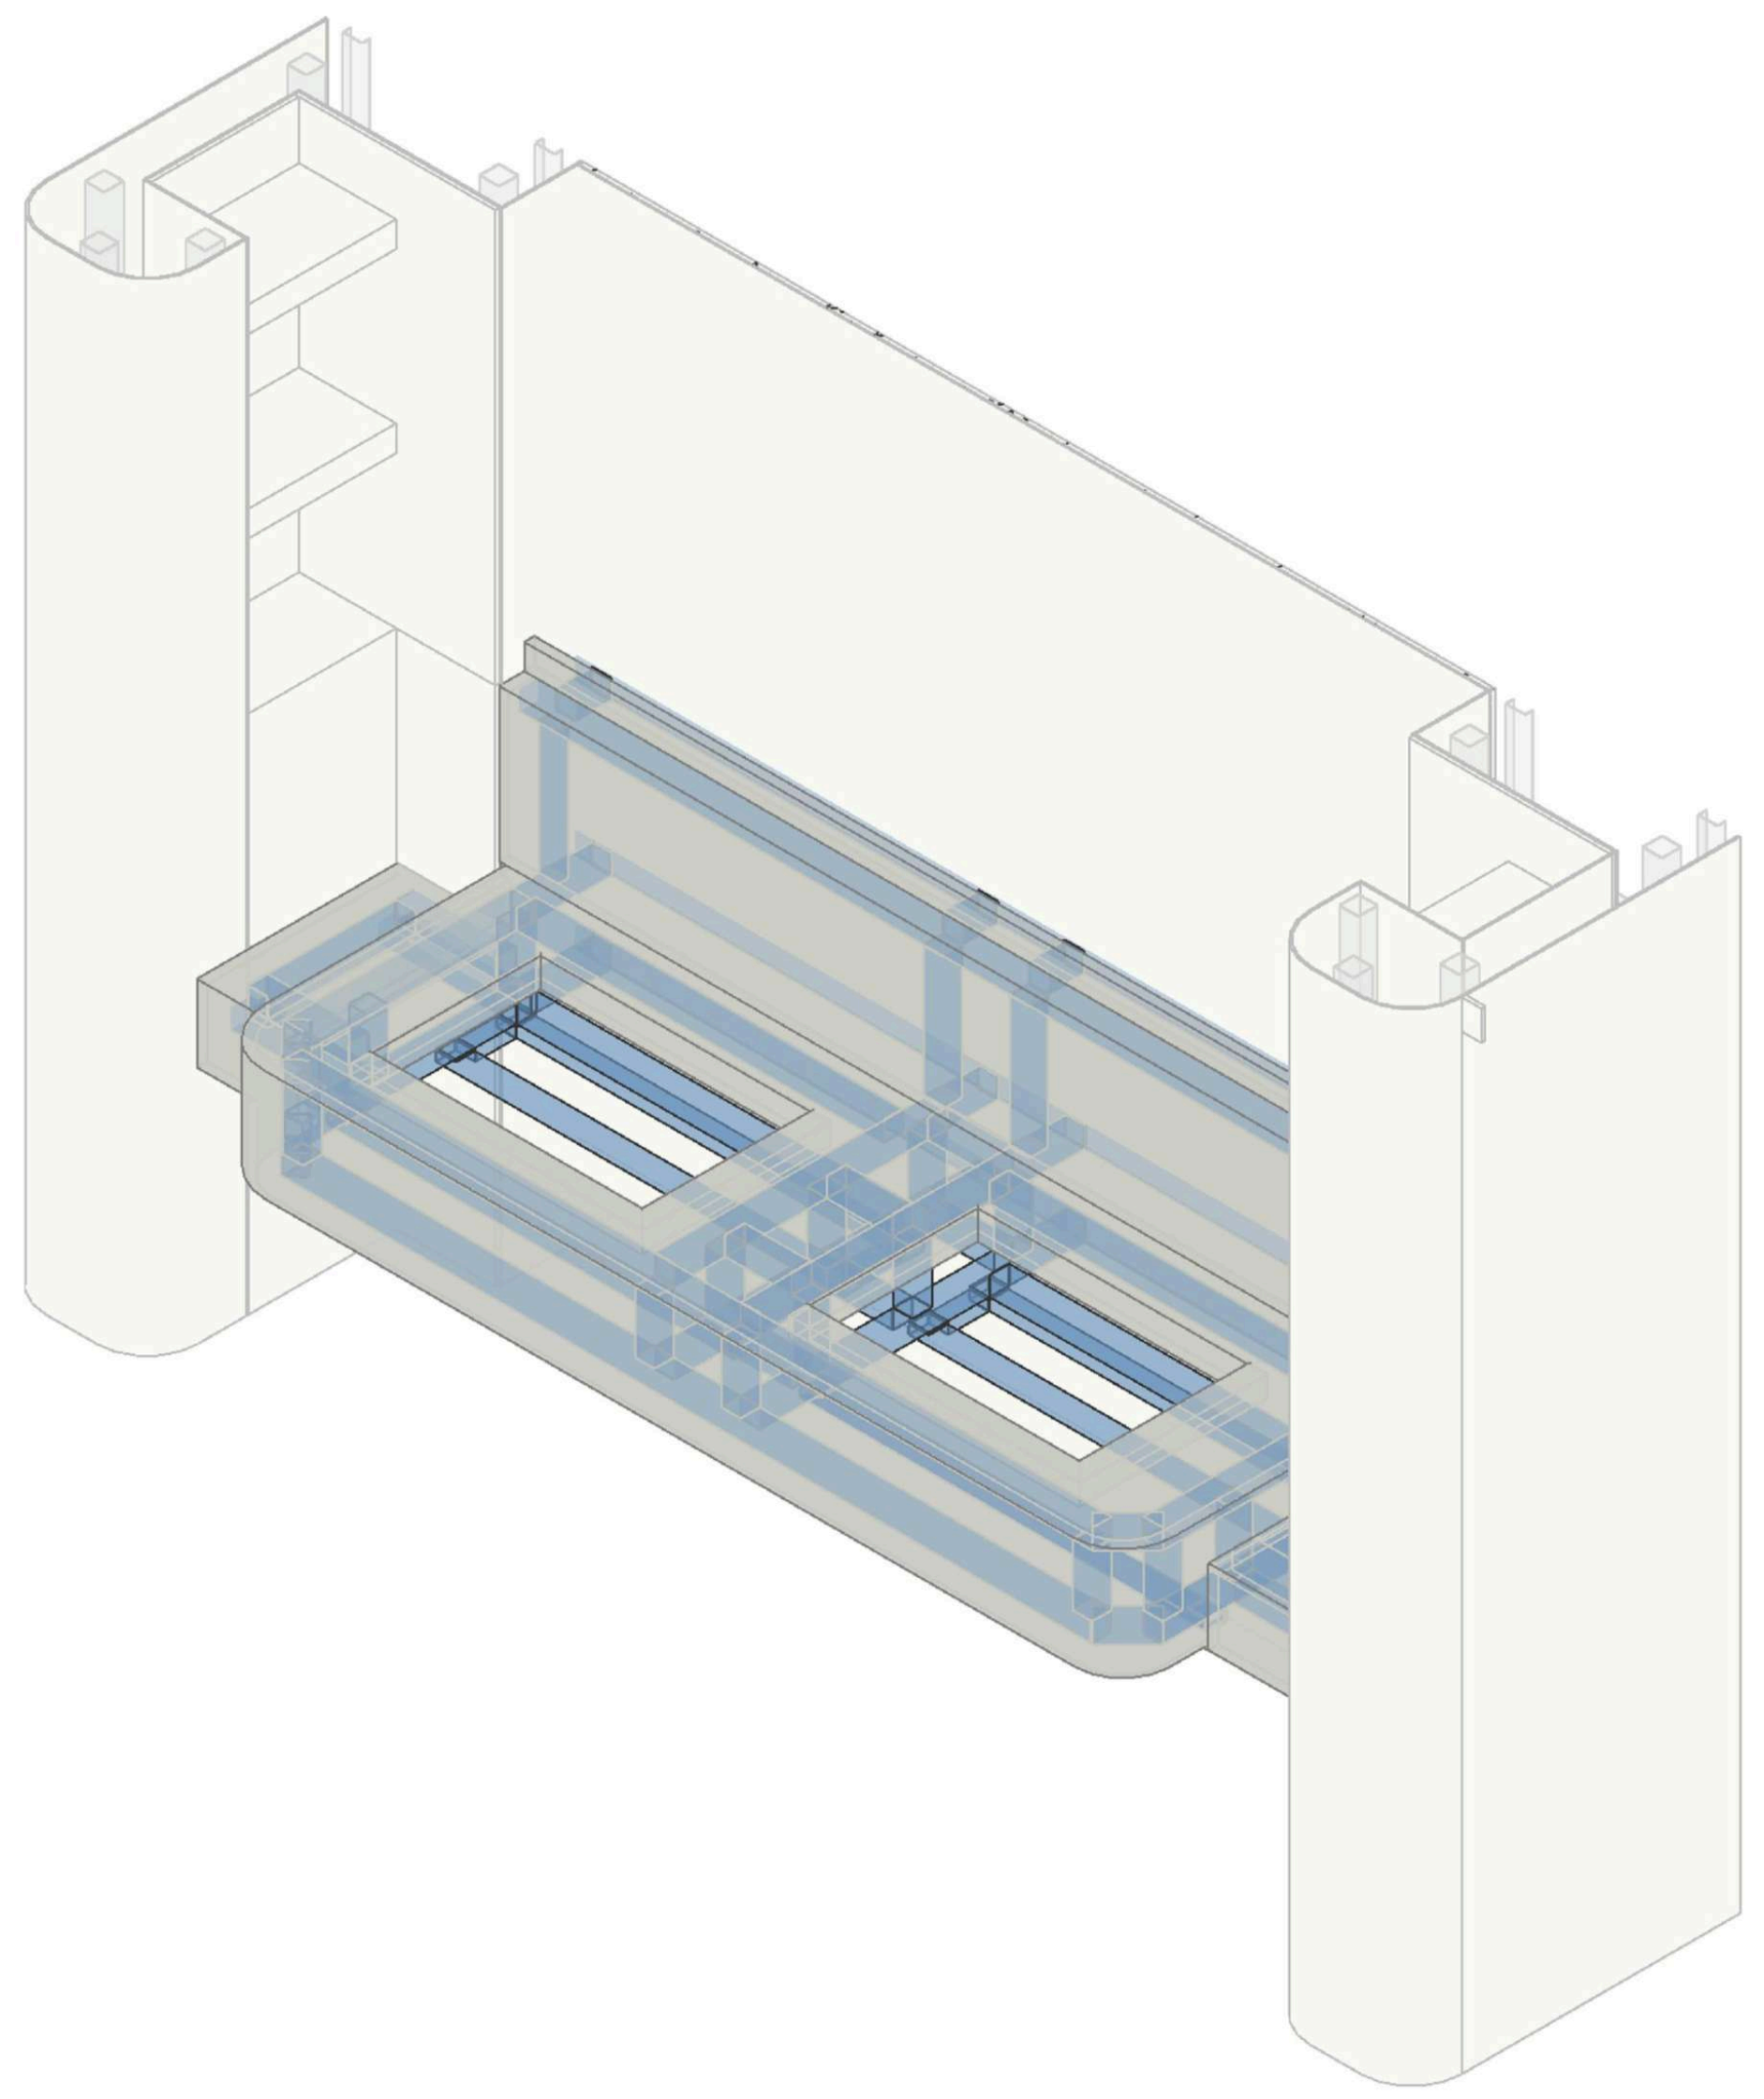

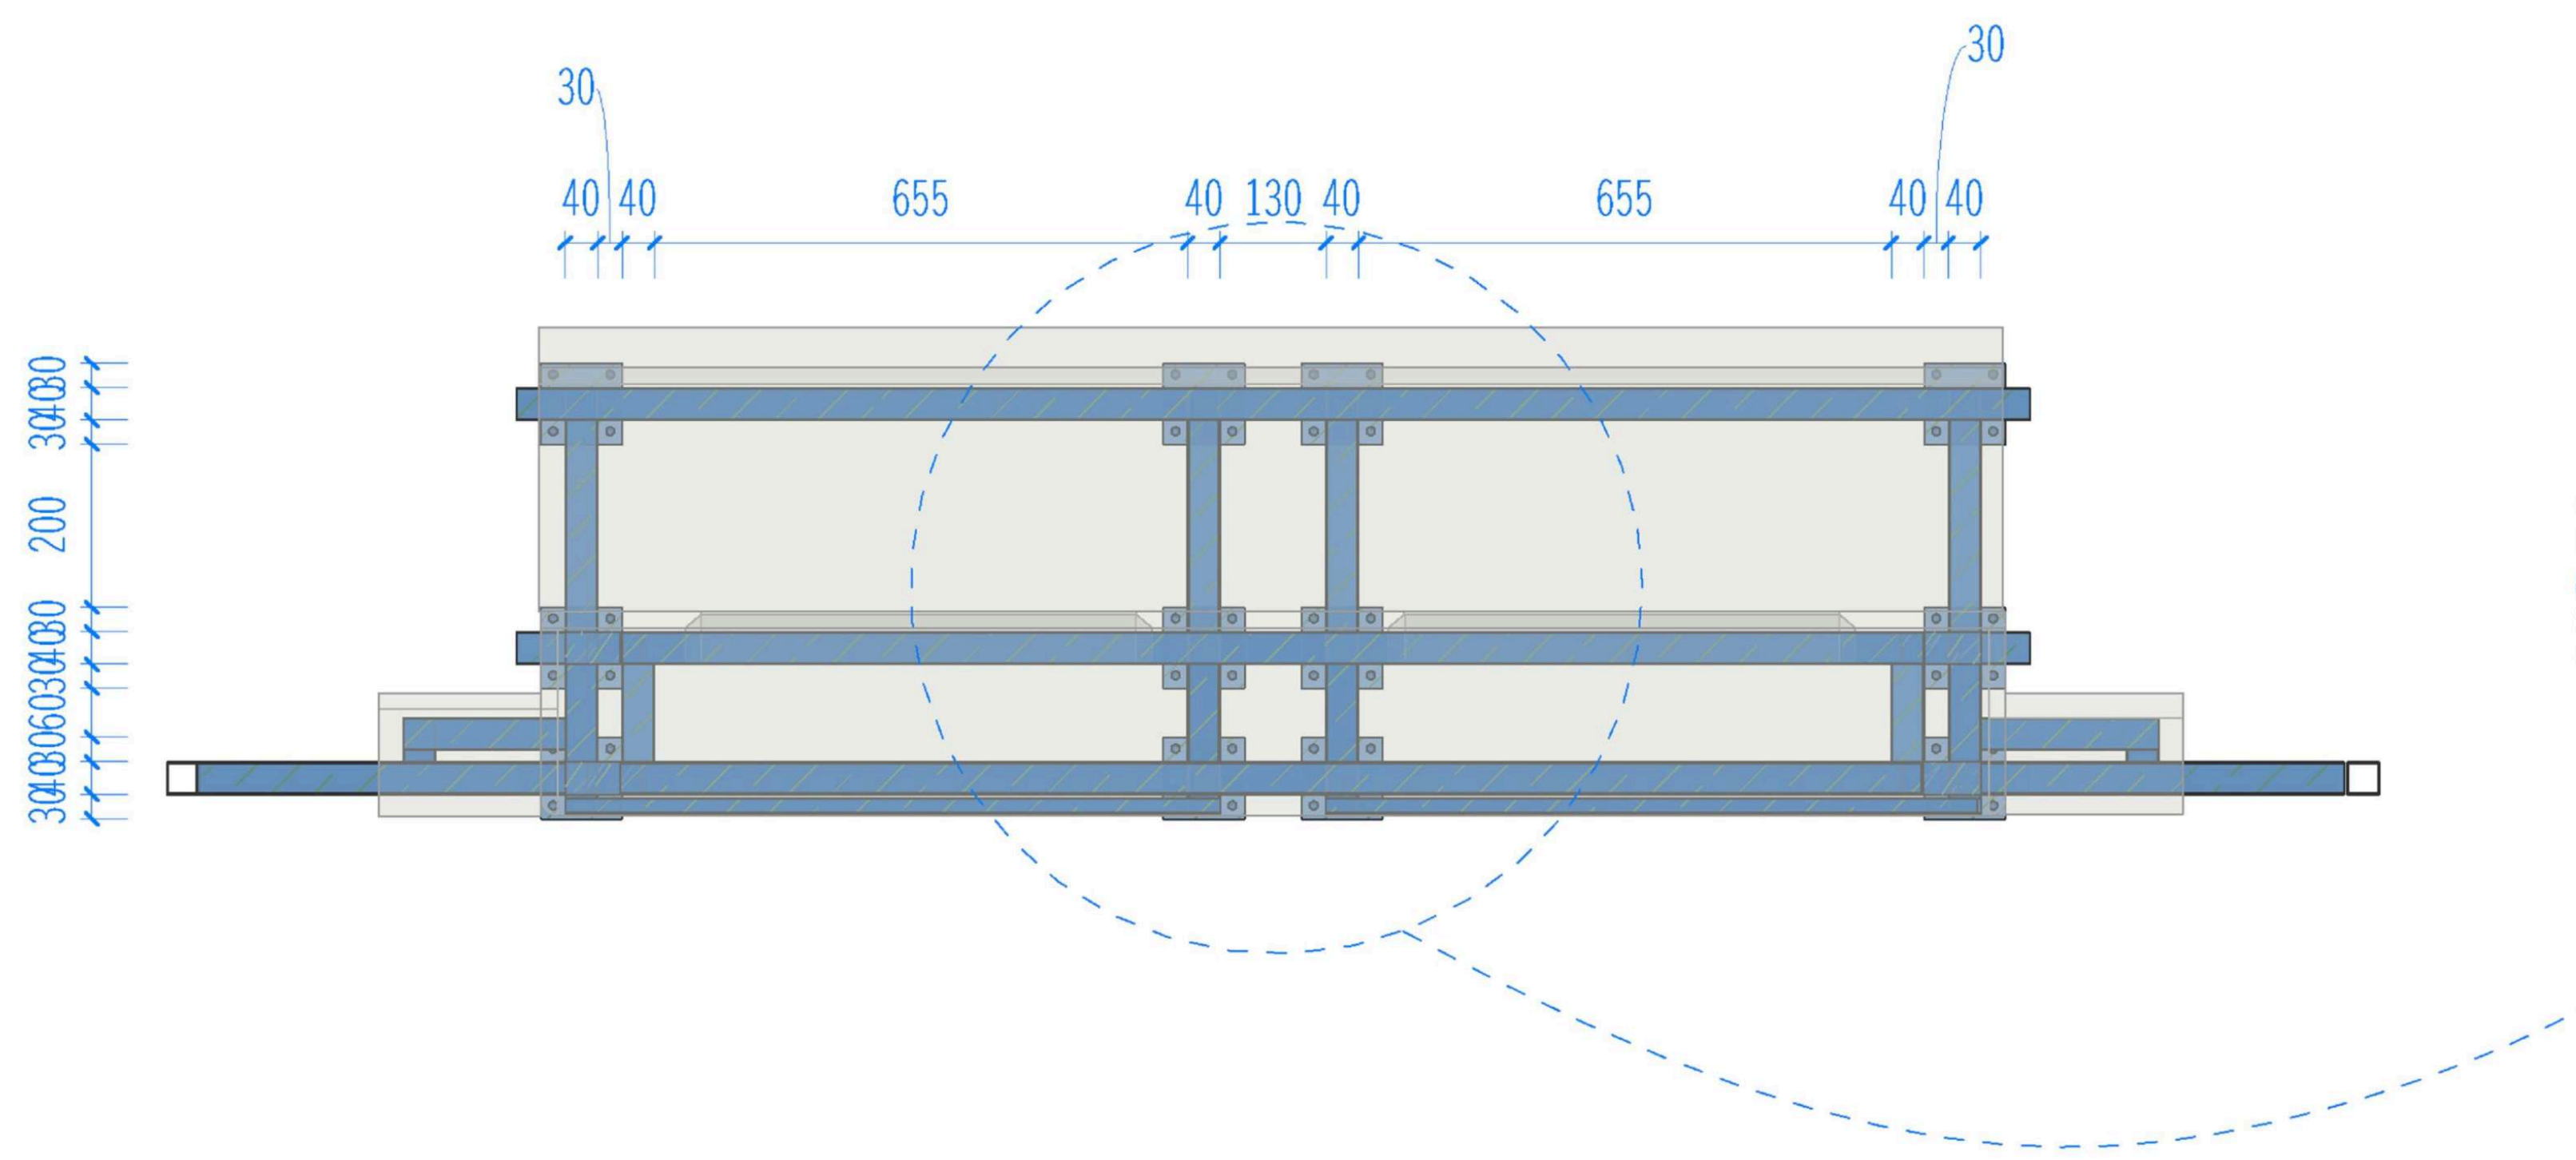
30
30
40
40
655
40
130
40
655
40
40
30
40
30
200
30
40
30
60
30
40
30

立面视图

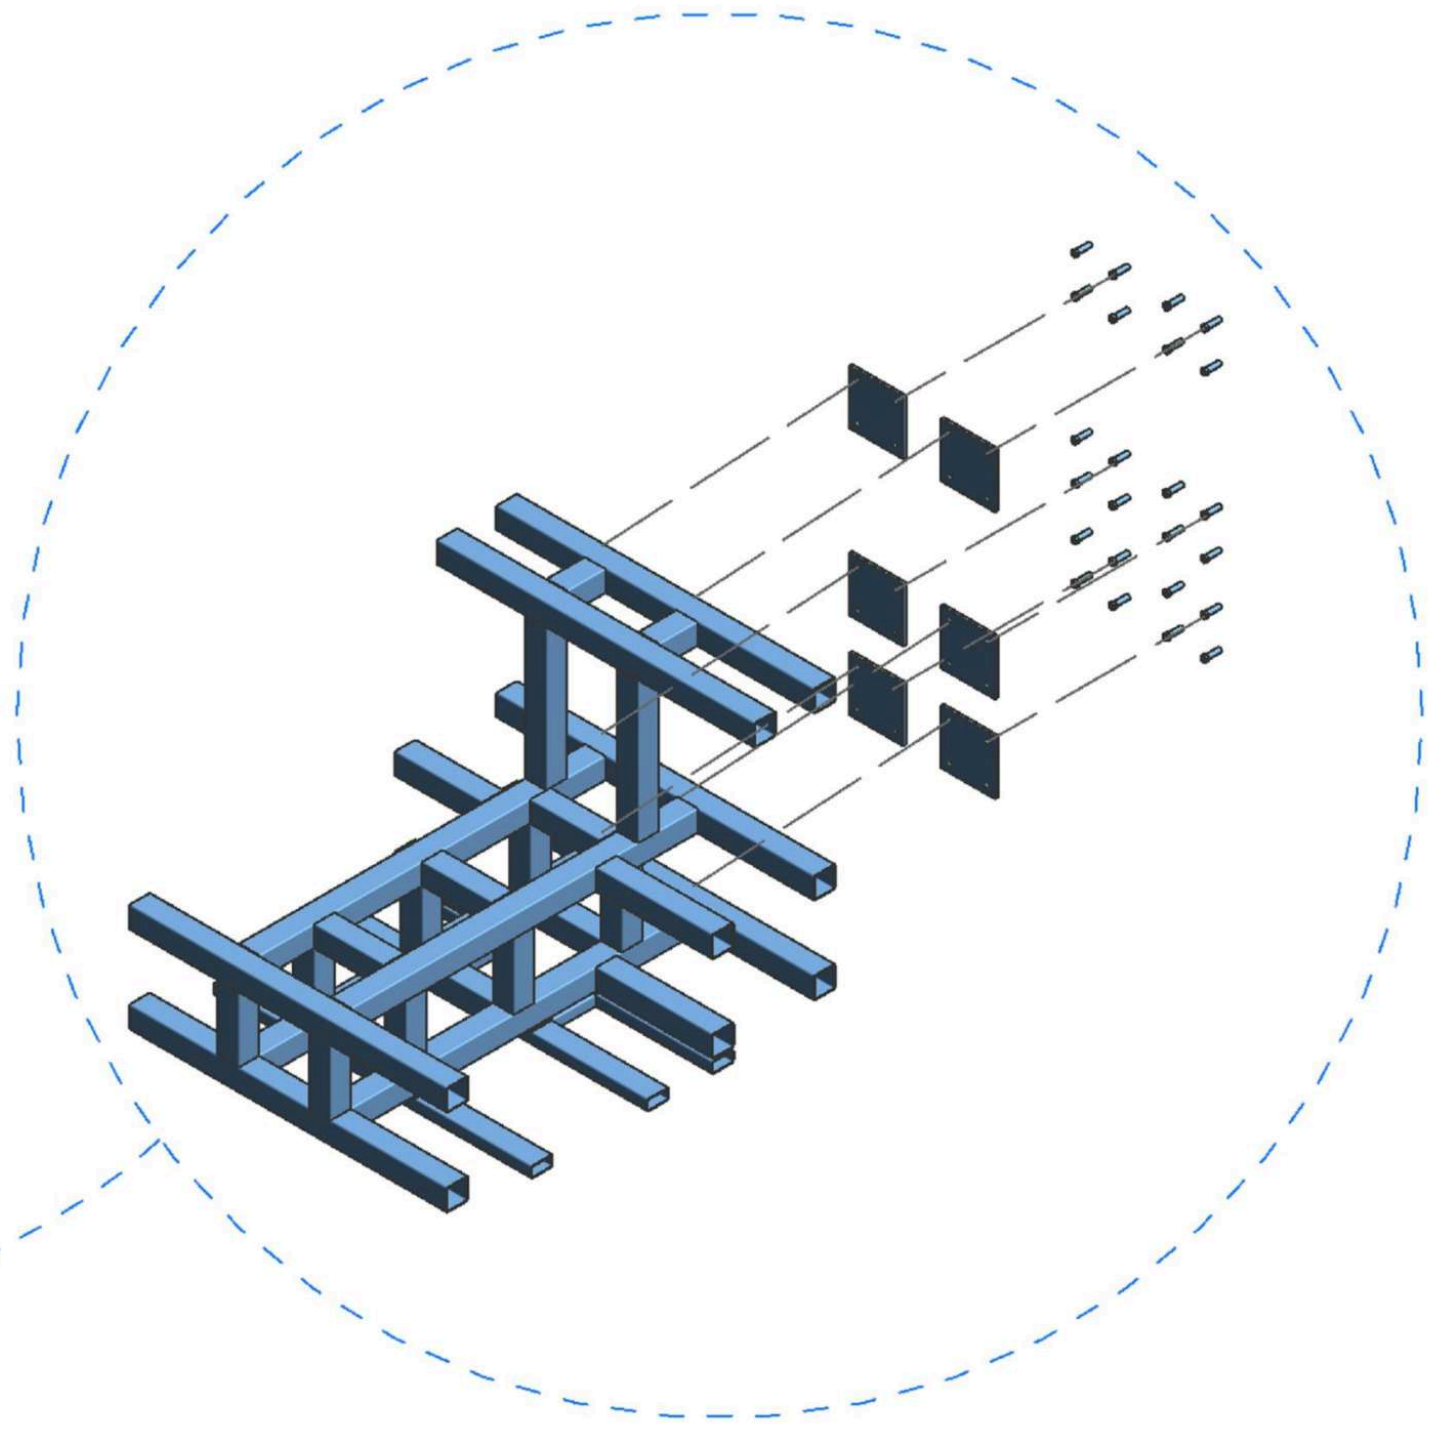

节点图

1

FIBORN

图例A
LEGEND A

编号	图例	说明
1	▯	原始钢架
2	⚲	螺栓
3	◆	钢片
4	▬	钢架
5	▱	石材

盖章

注释
Notes

1.本图纸如与现场尺寸有误，请施工人员与项目负责人联系。
2.施工前施工人员应认真查阅此图，如有不明确尺寸，按现场测量为准。
3.本图纸必须经甲乙双方认可并签字方可作为施工依据。

日期
Date 05/07/26

修订
Revision

⚠1

项目
Project
潮映华岸府3-801

比例
Scale

主卫洗手台石材钢架

图纸编号
Drawing No.
ST-01

项目编号
Project No.

©2025

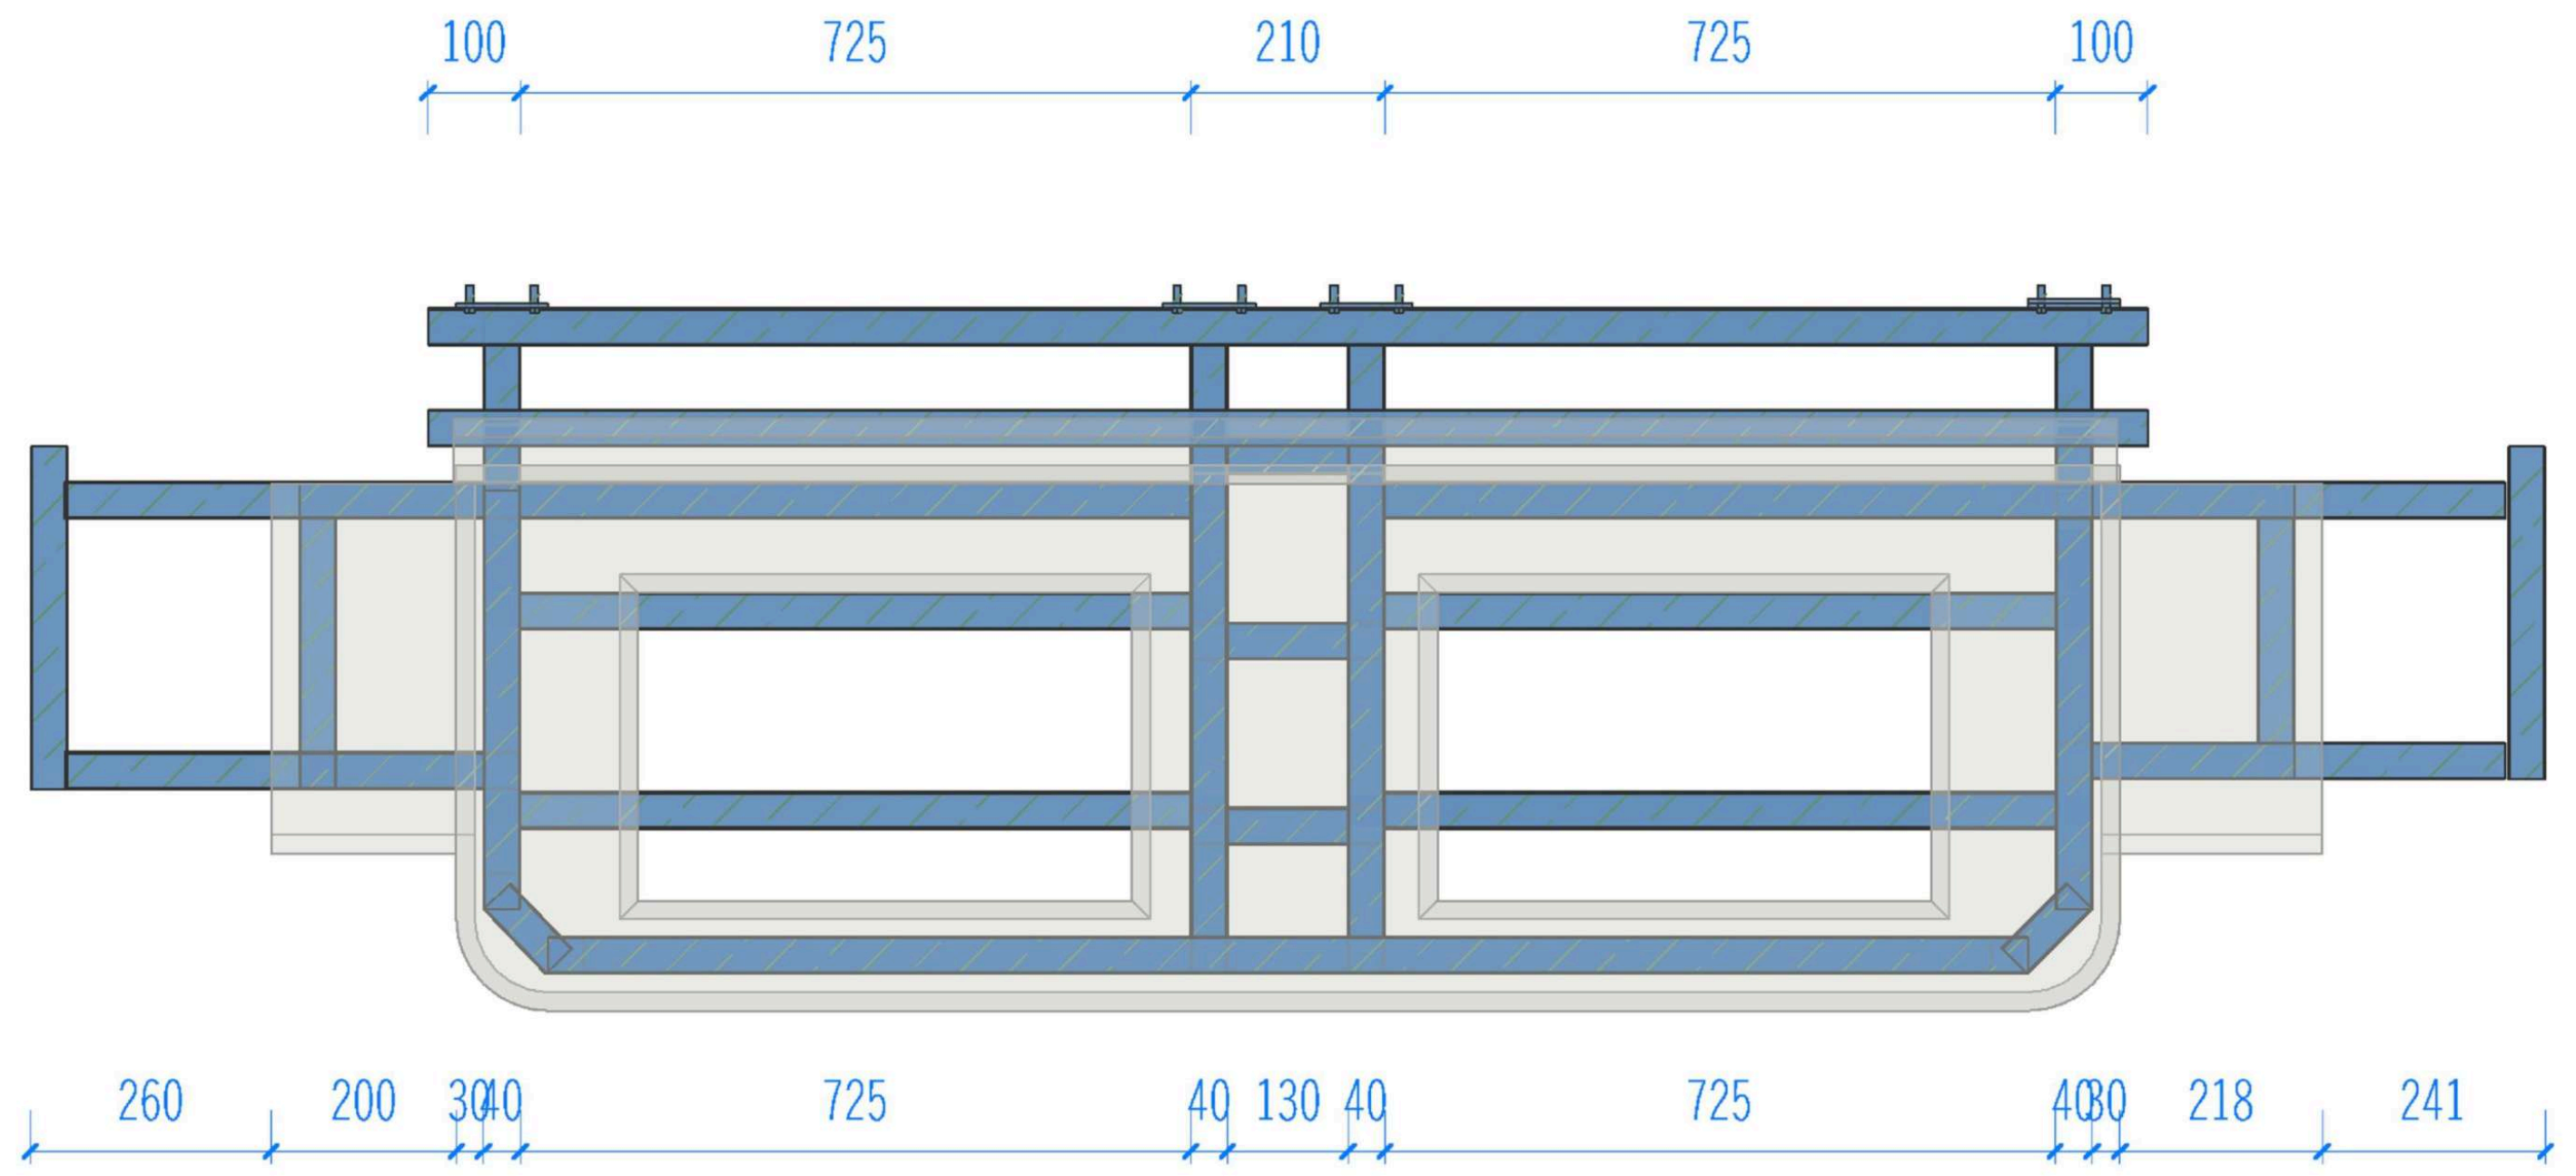
100
725
210
725
100
260
200
30
40
725
40
130
40
725
40
30
218
241

平面视图

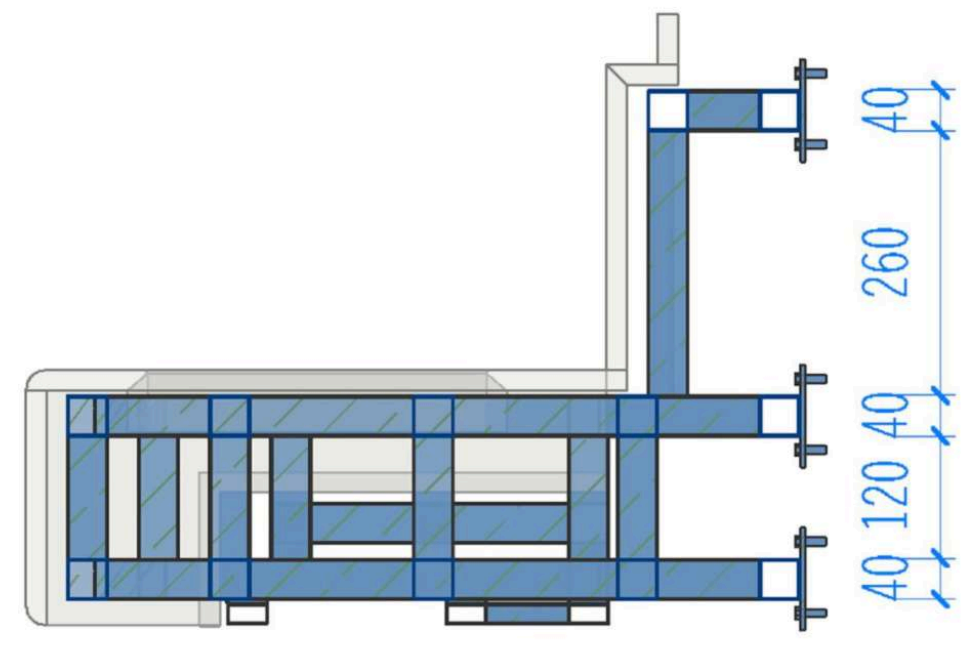
40
260
40
120
40

剖面视图

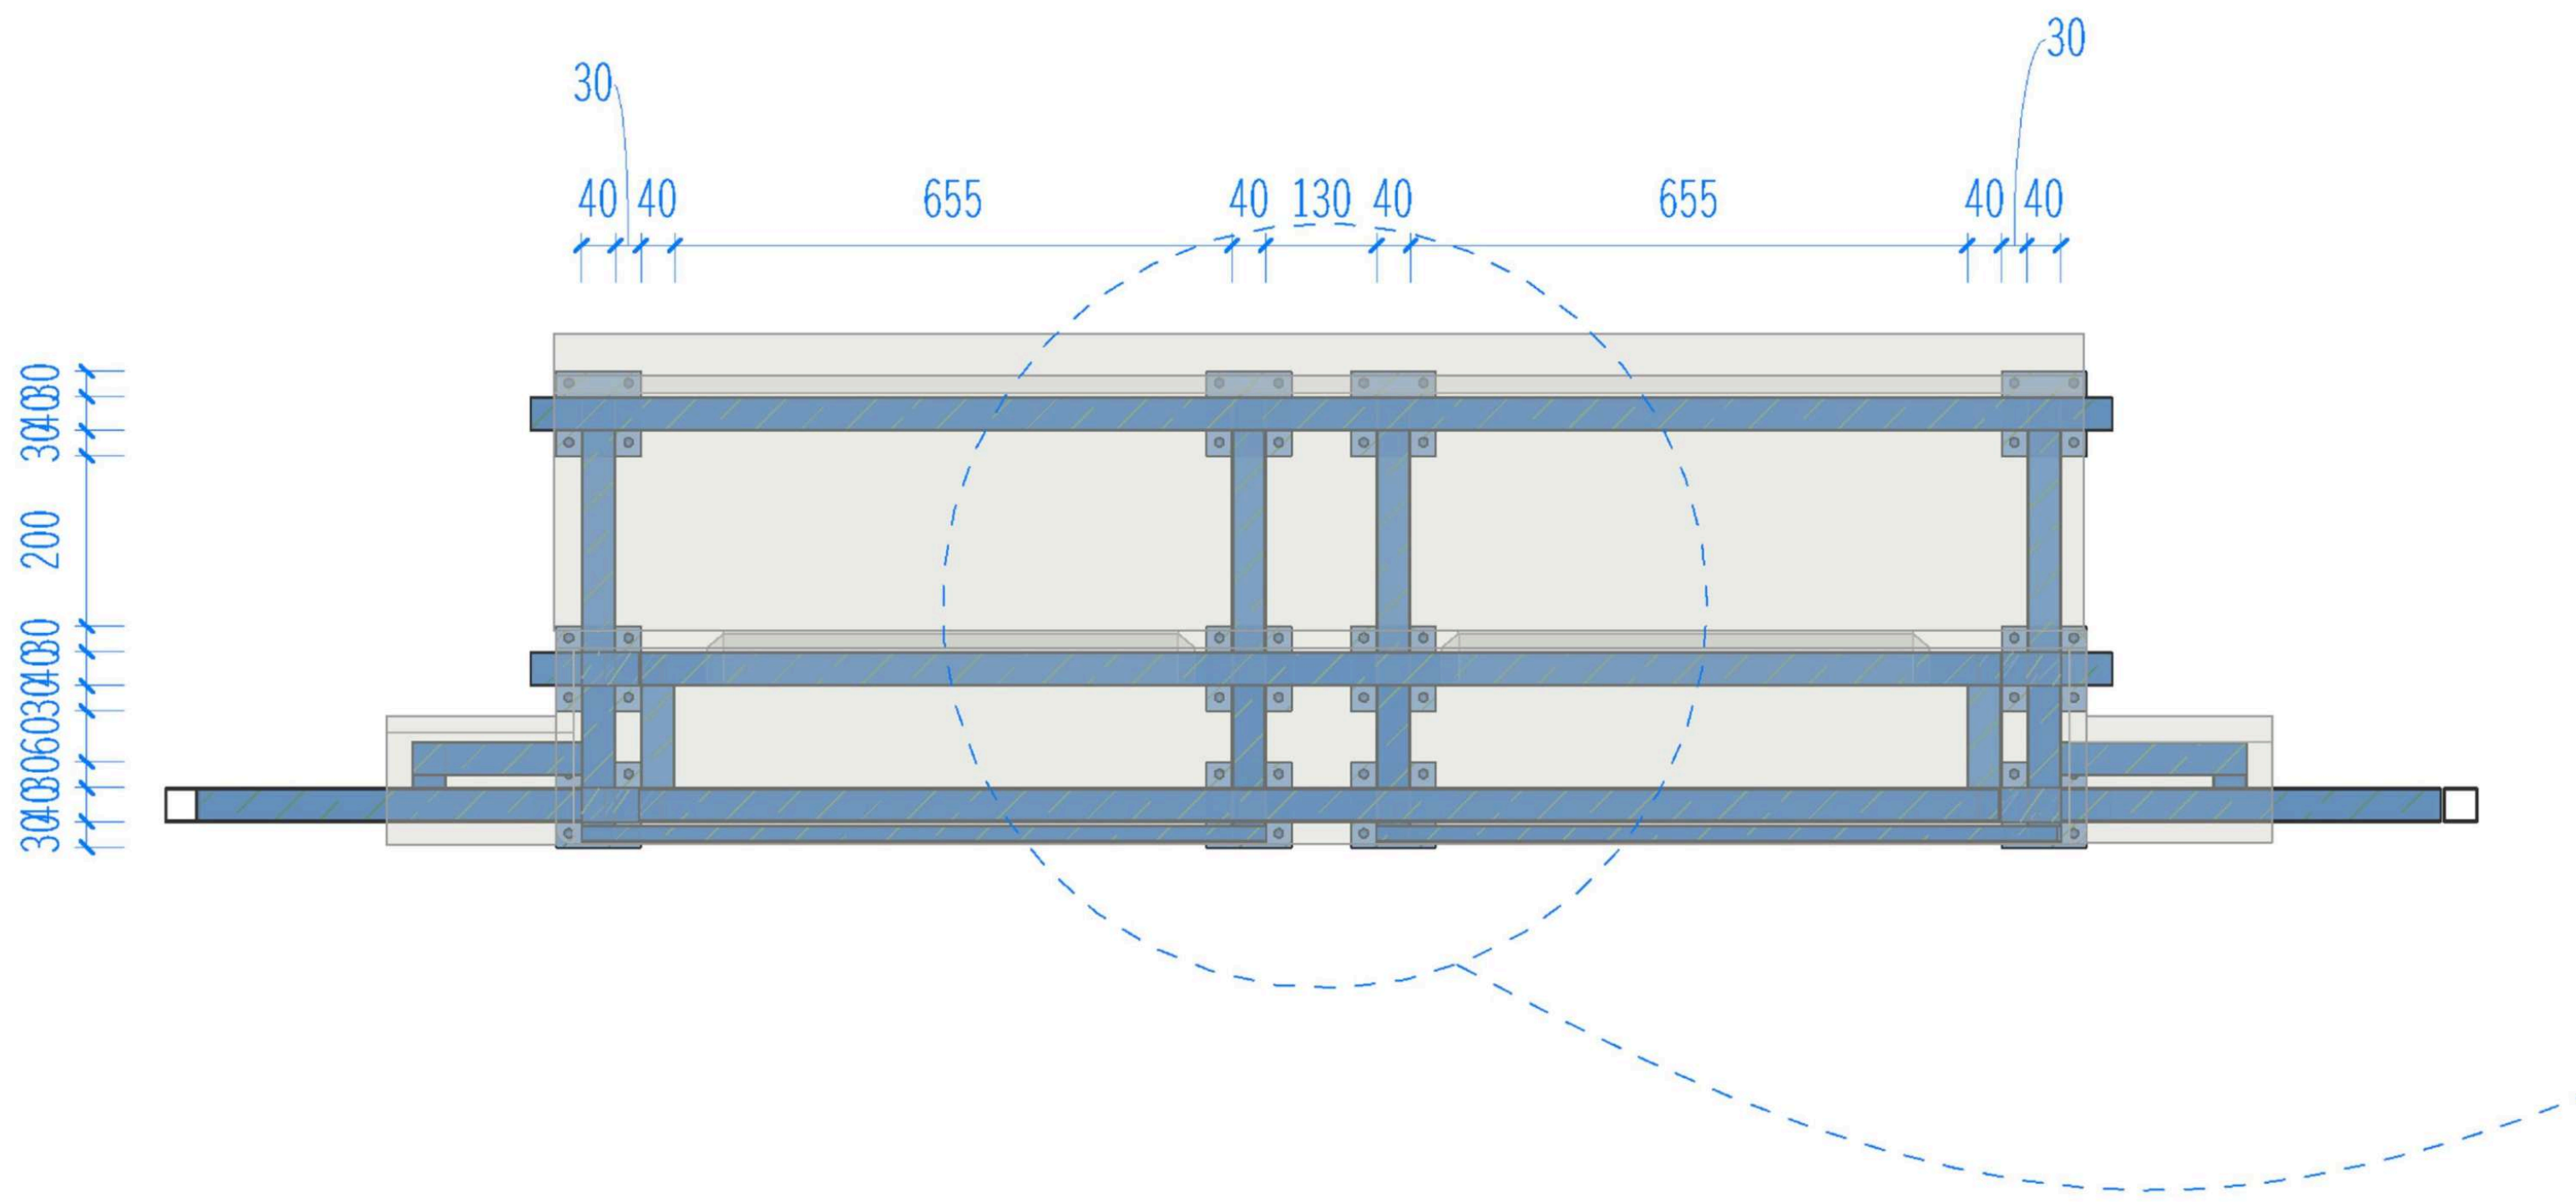
30
30
40
40
655
40
130
40
655
40
40
30
40
30
200
30
40
30
60
30
40
30

立面视图

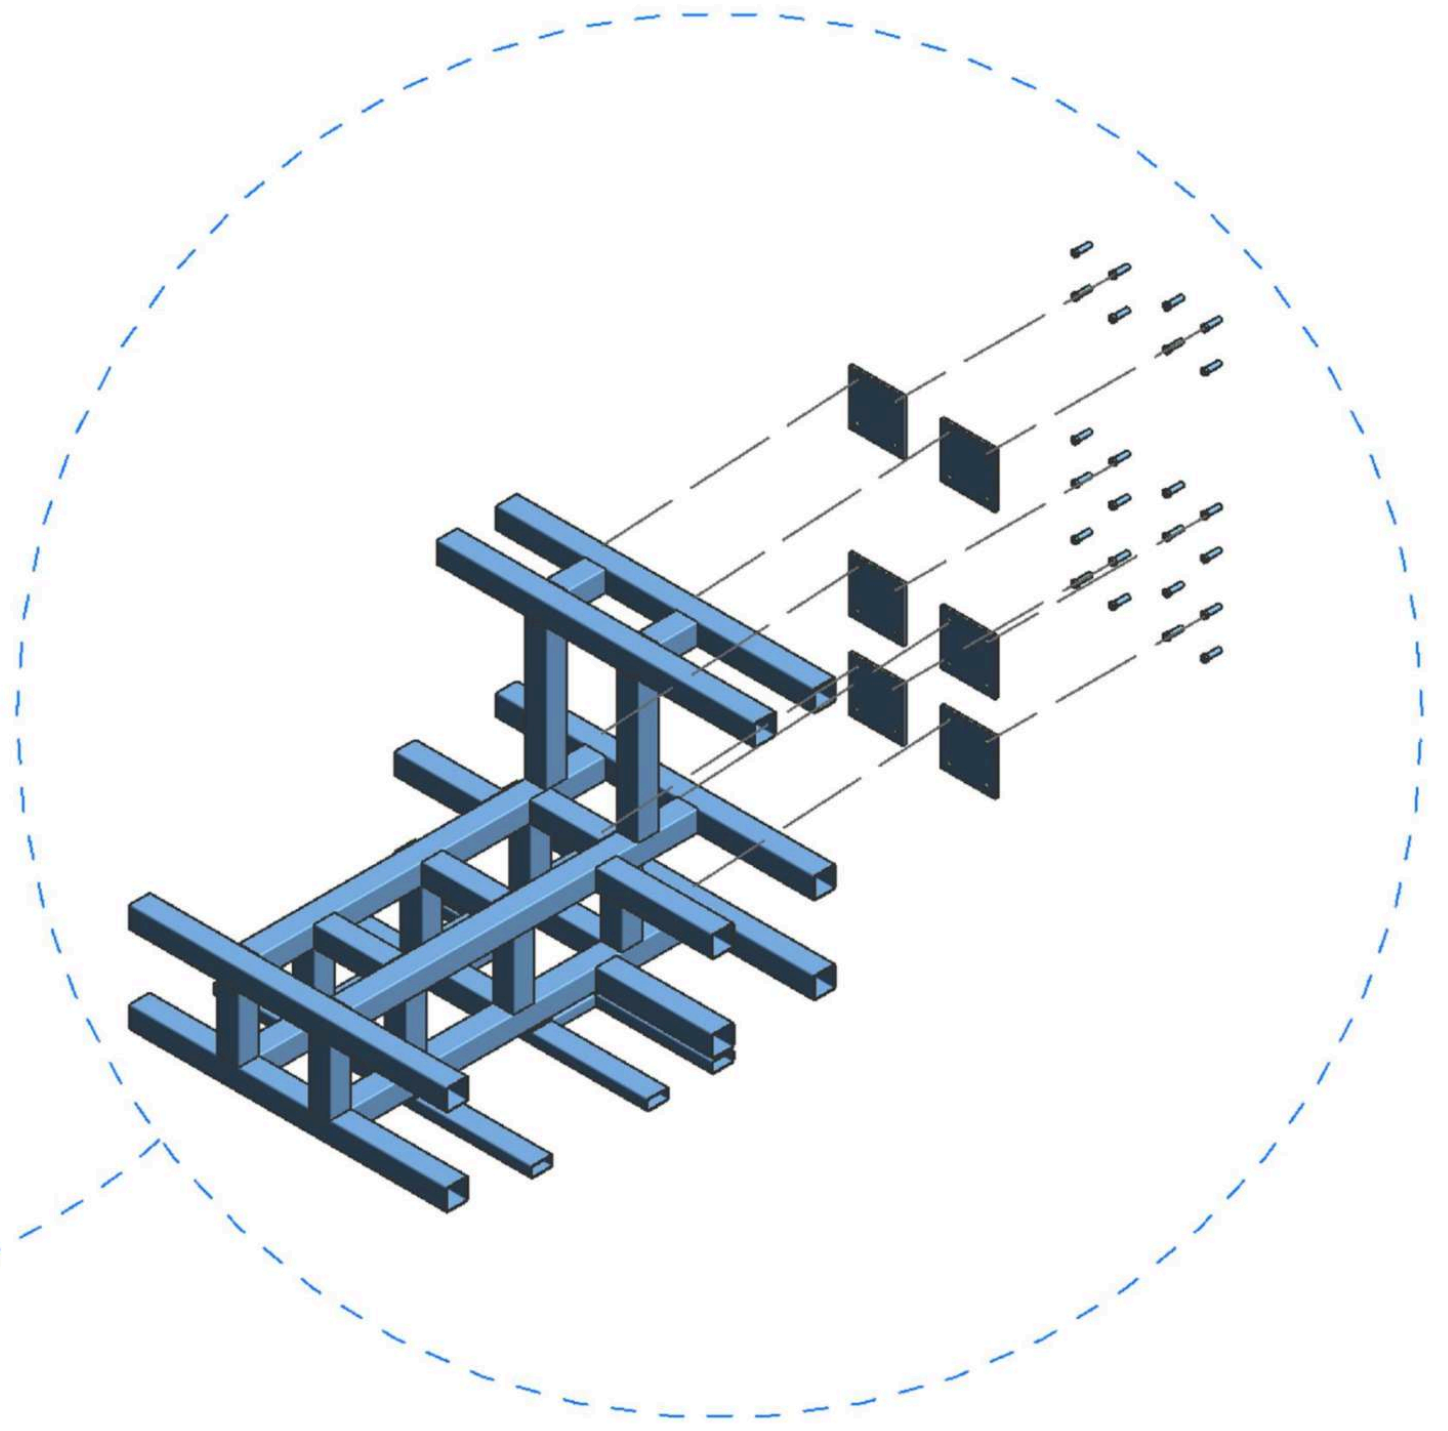

节点图

1

工厂预制钢架

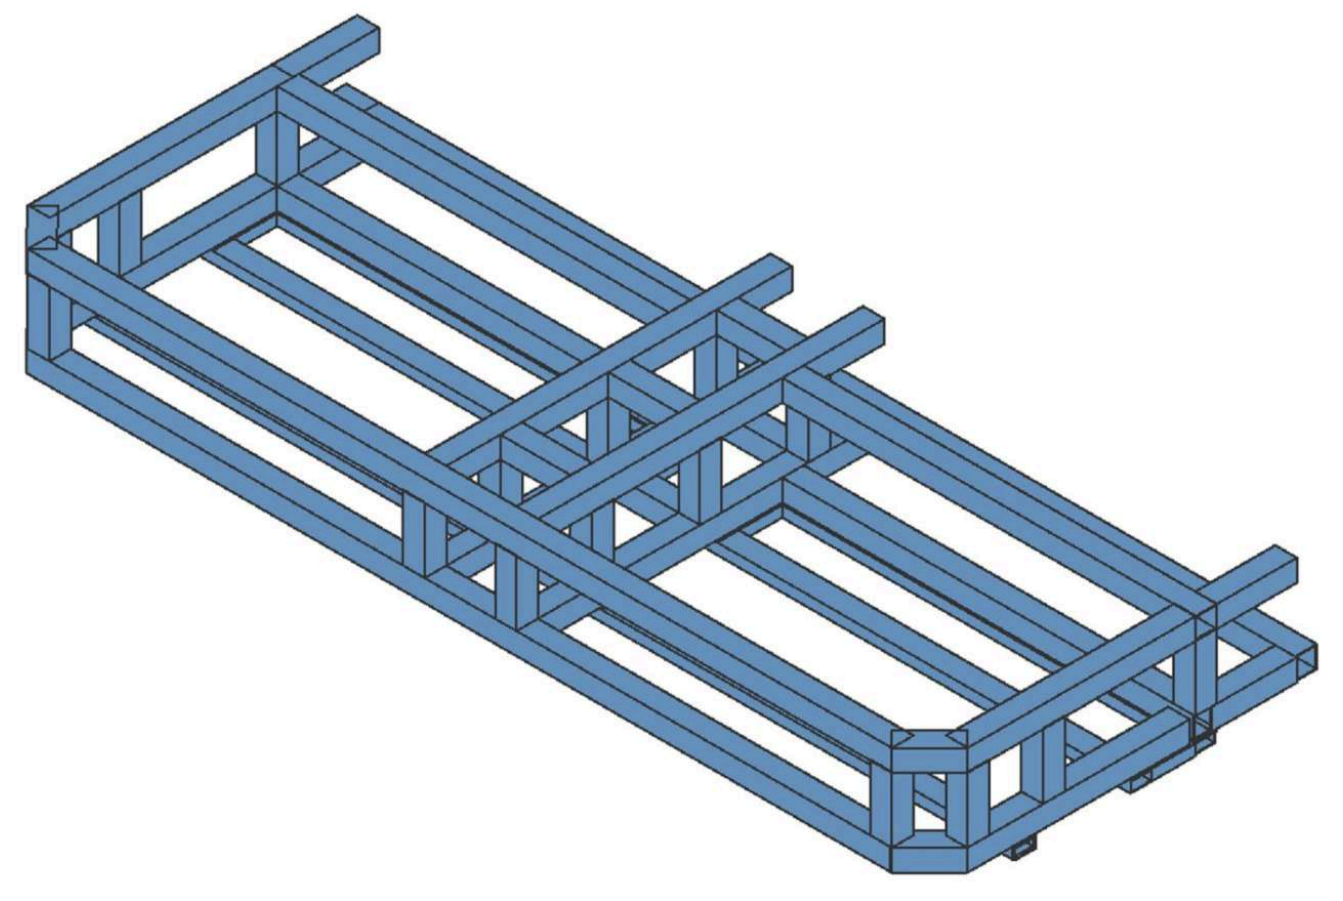

①

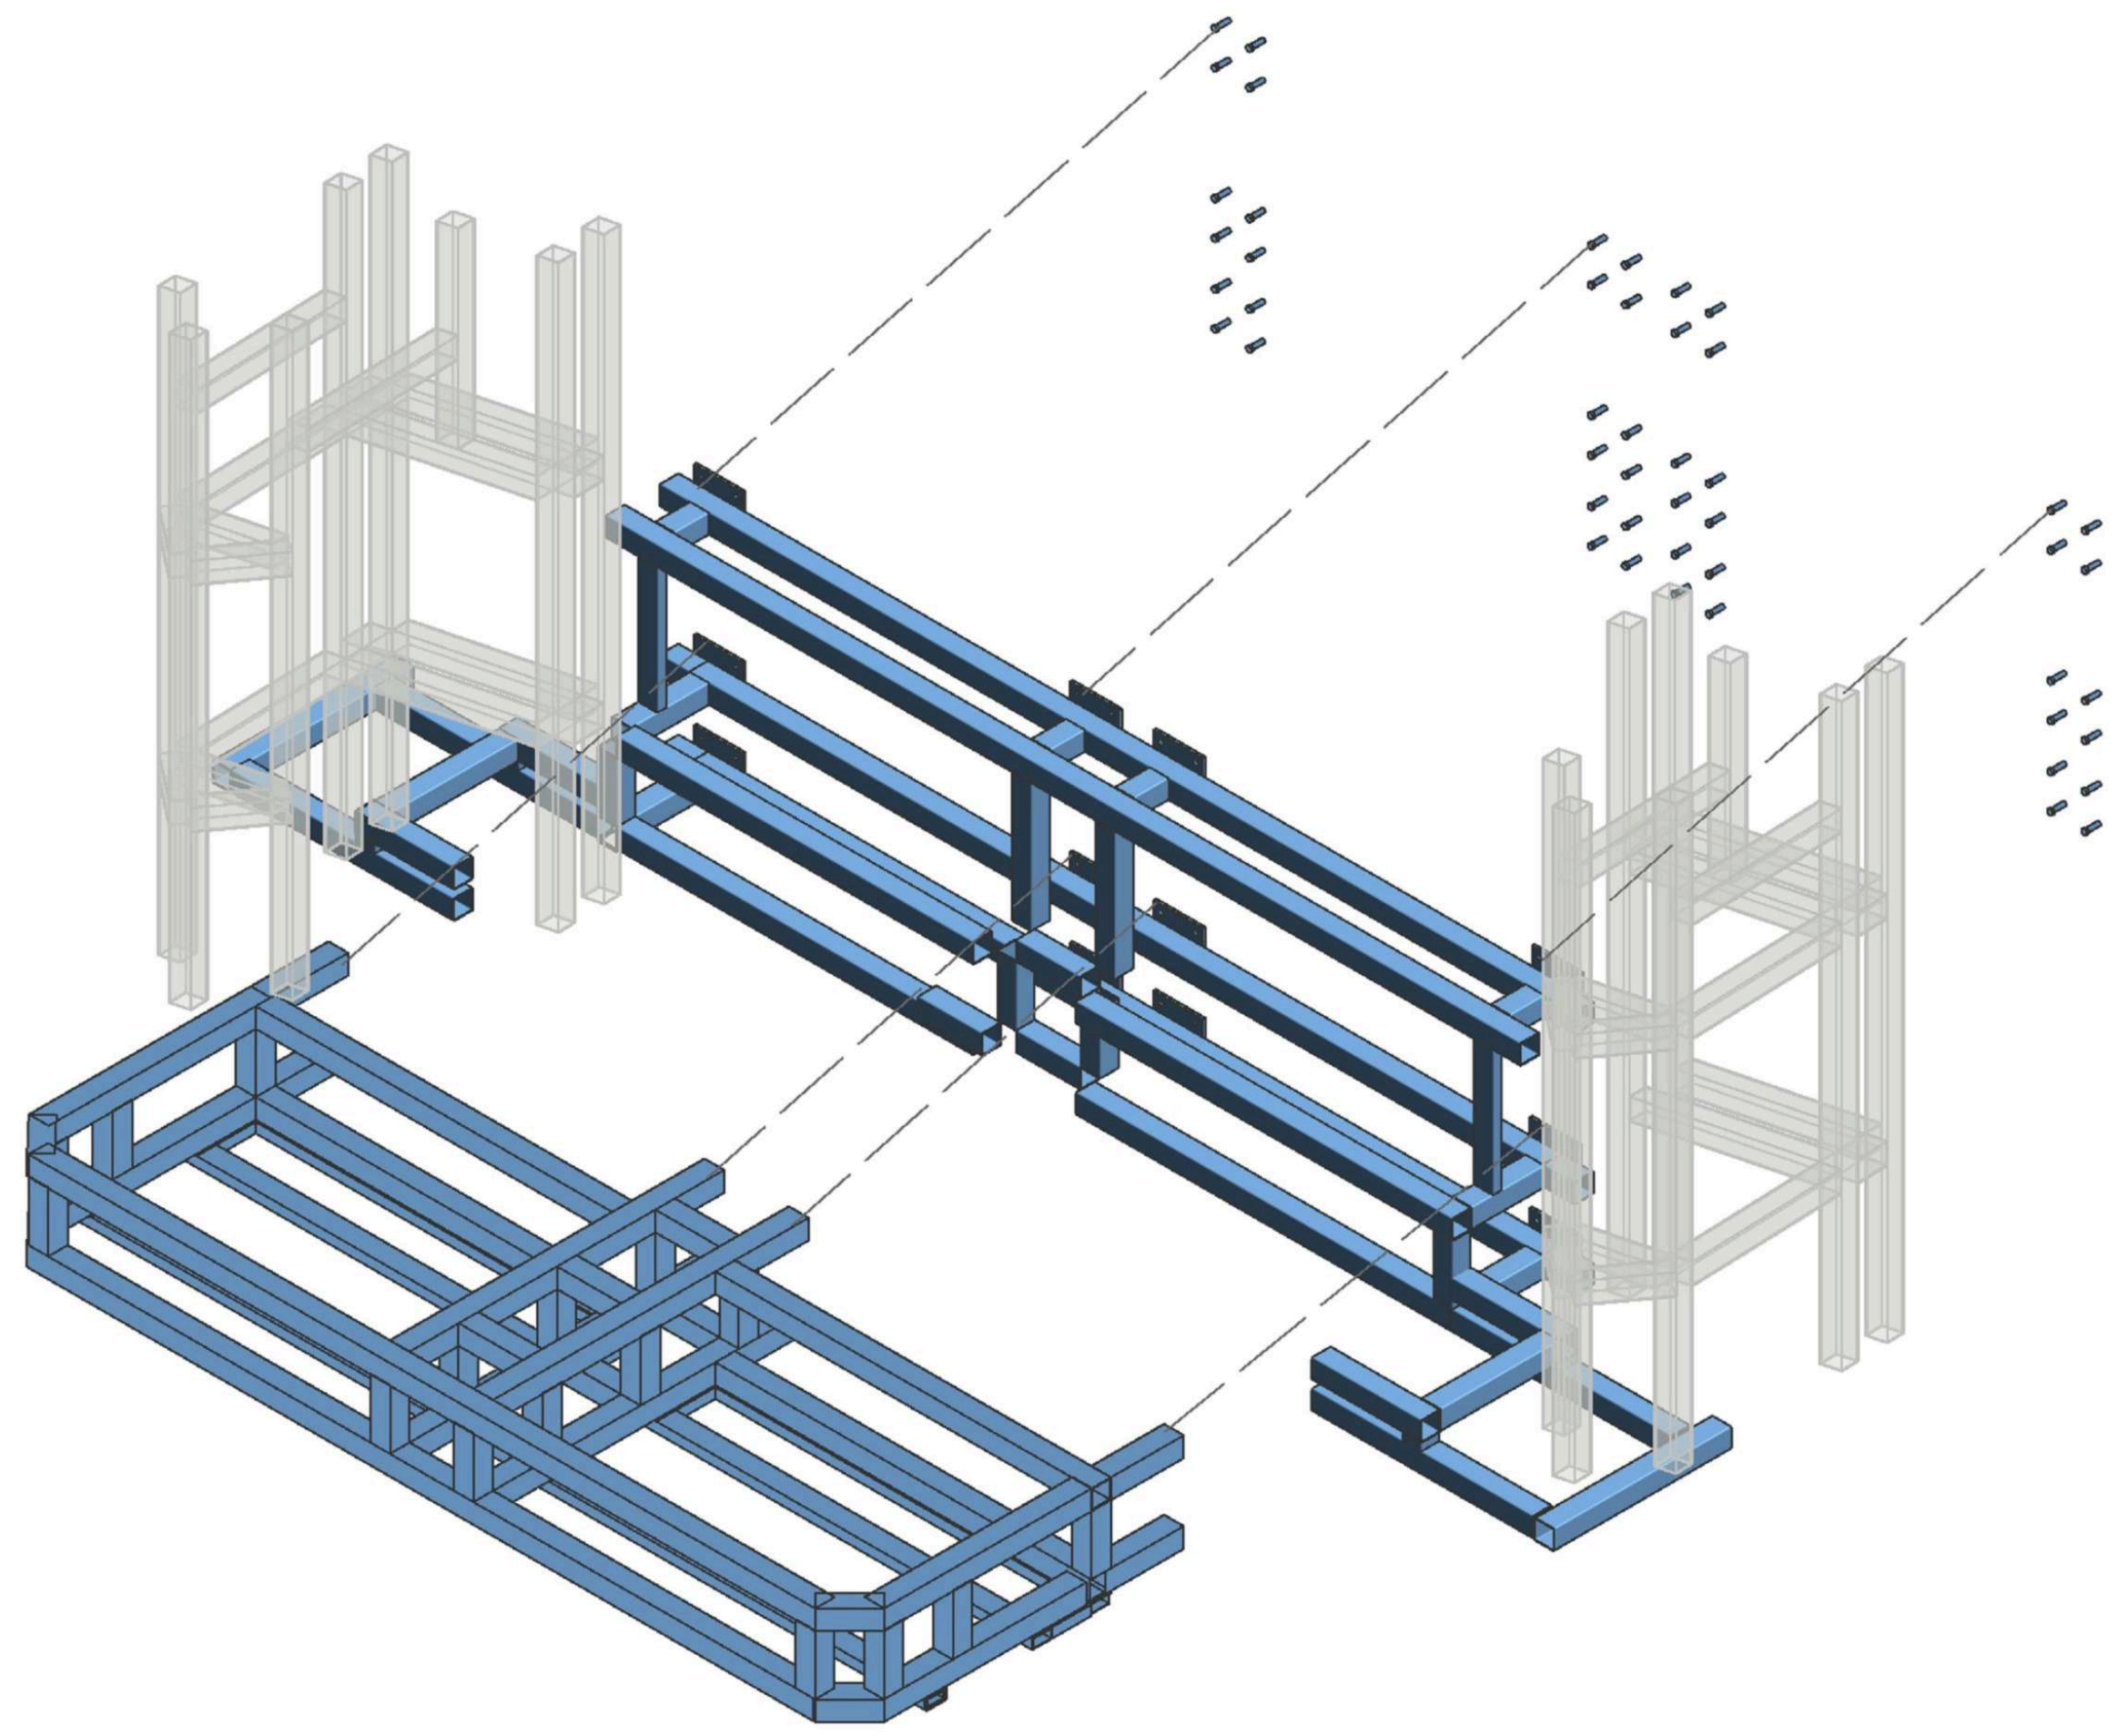

②

③

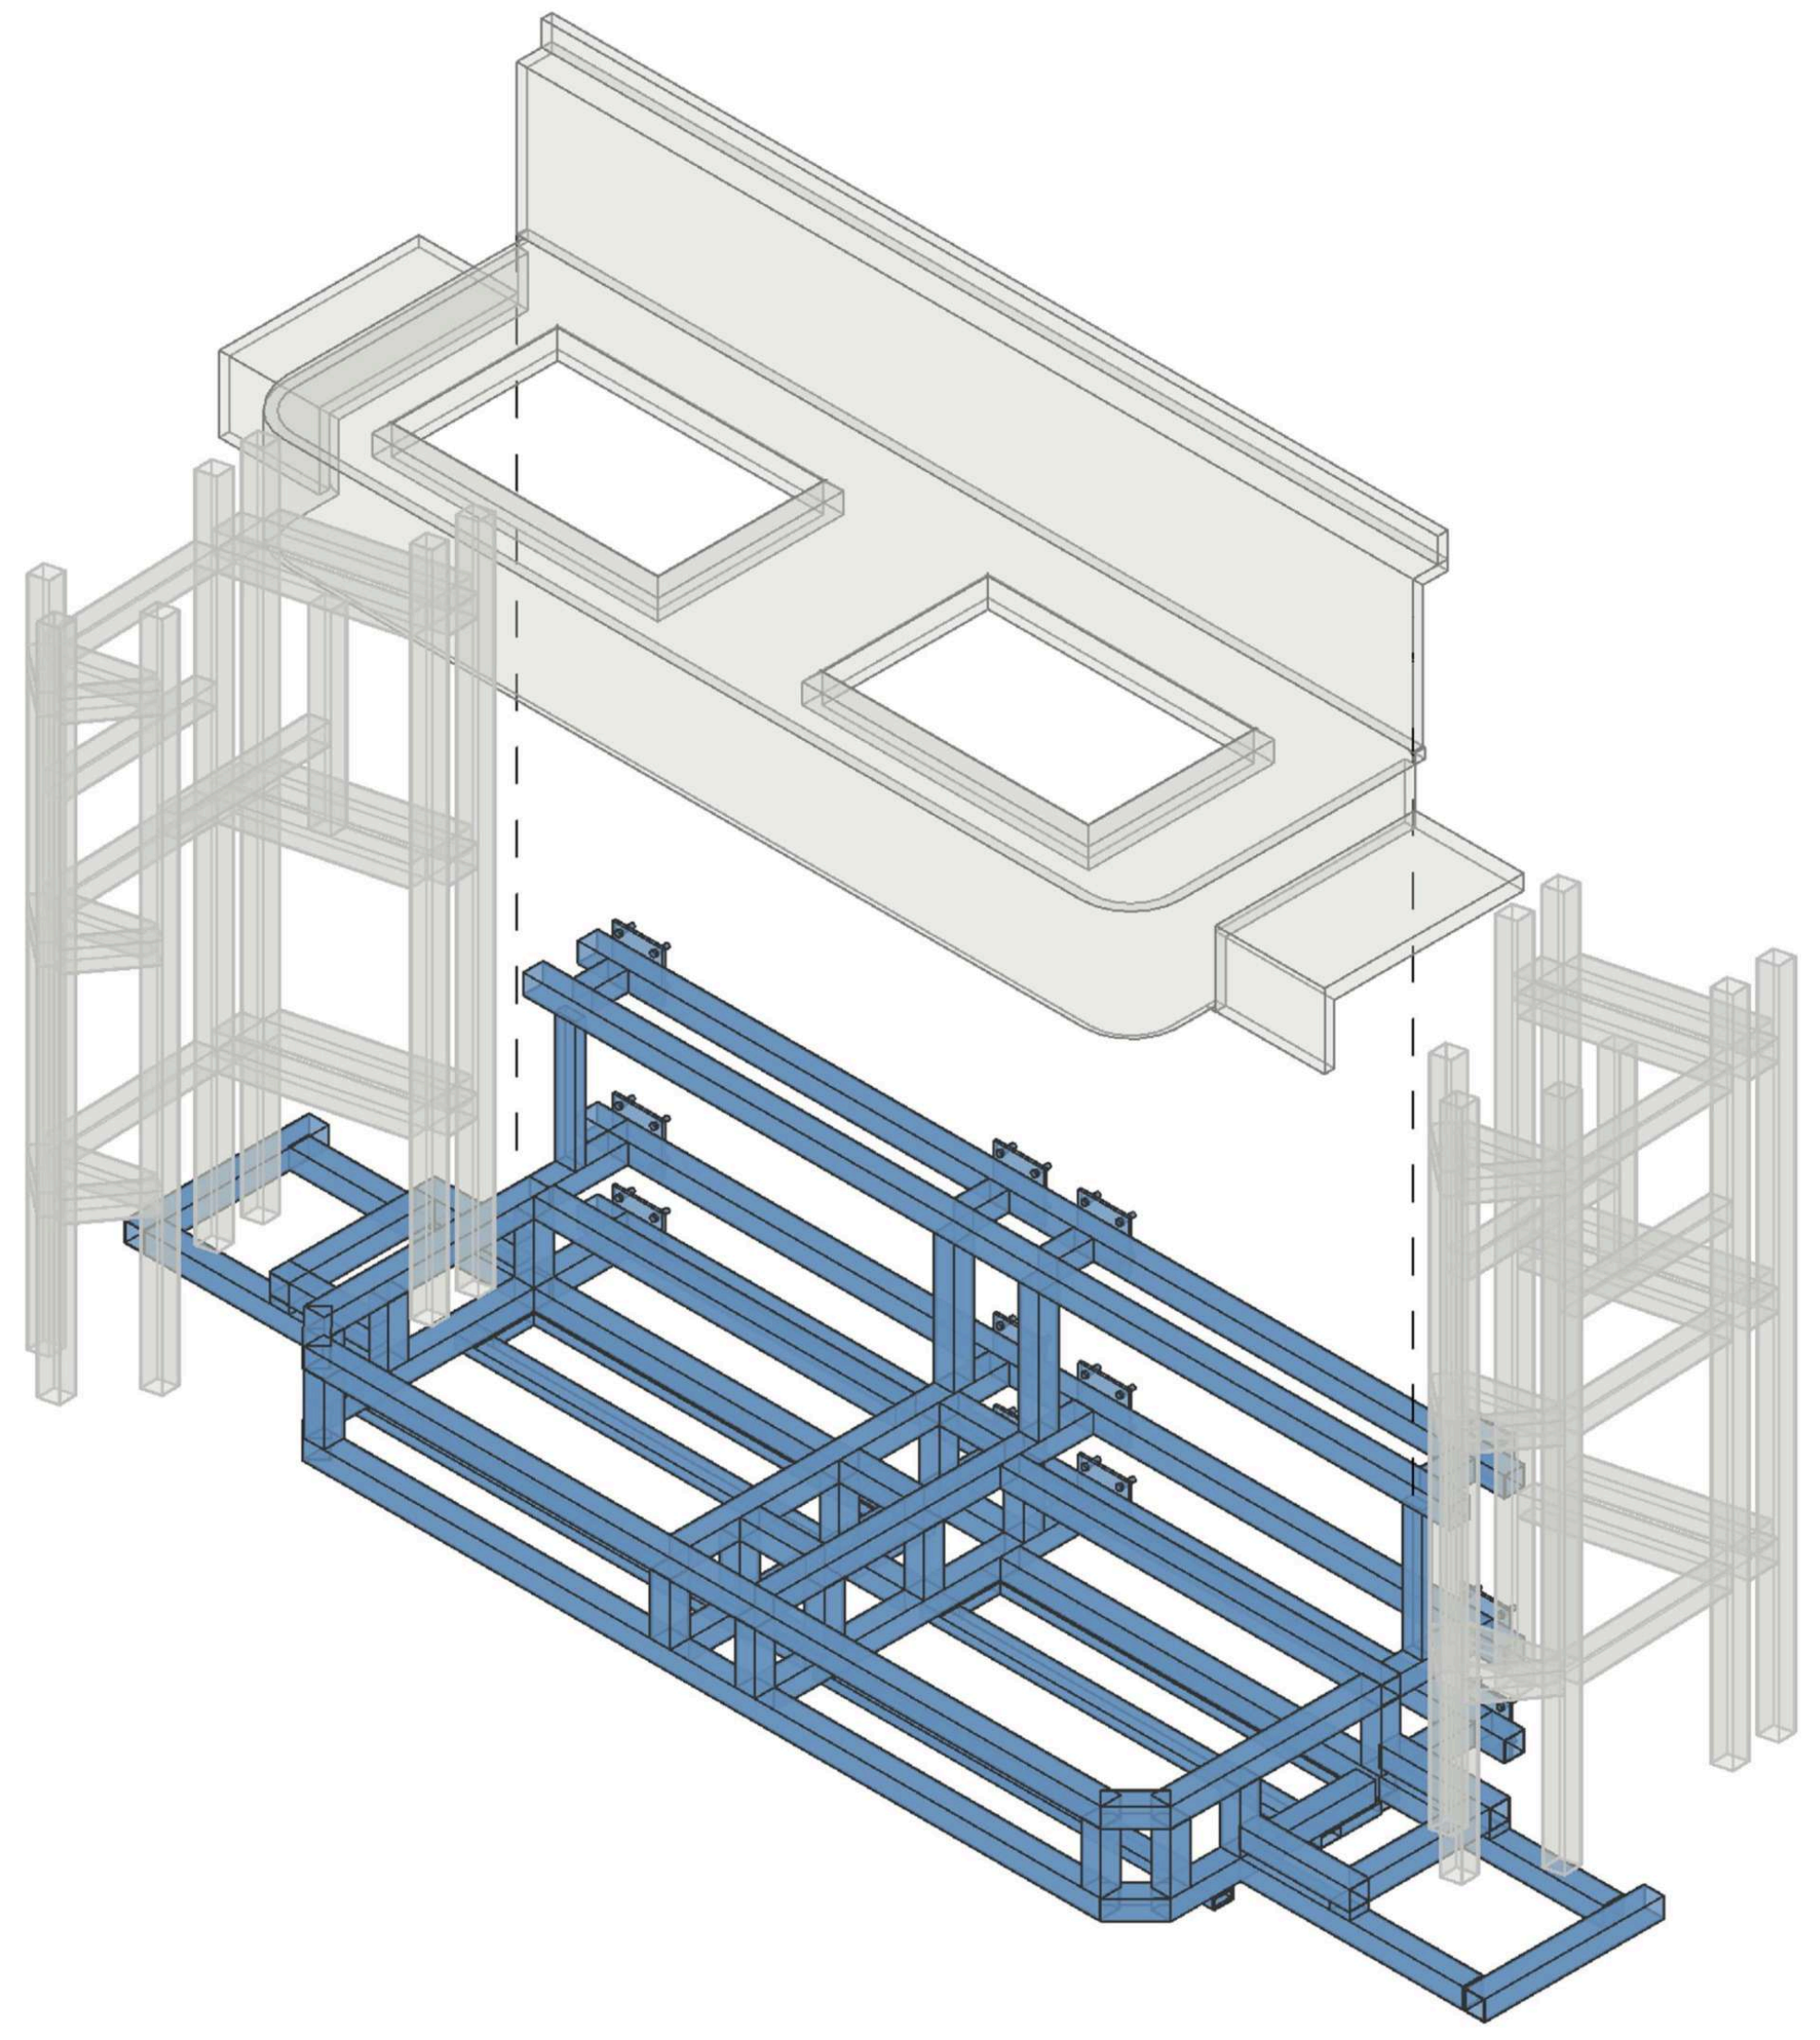

④

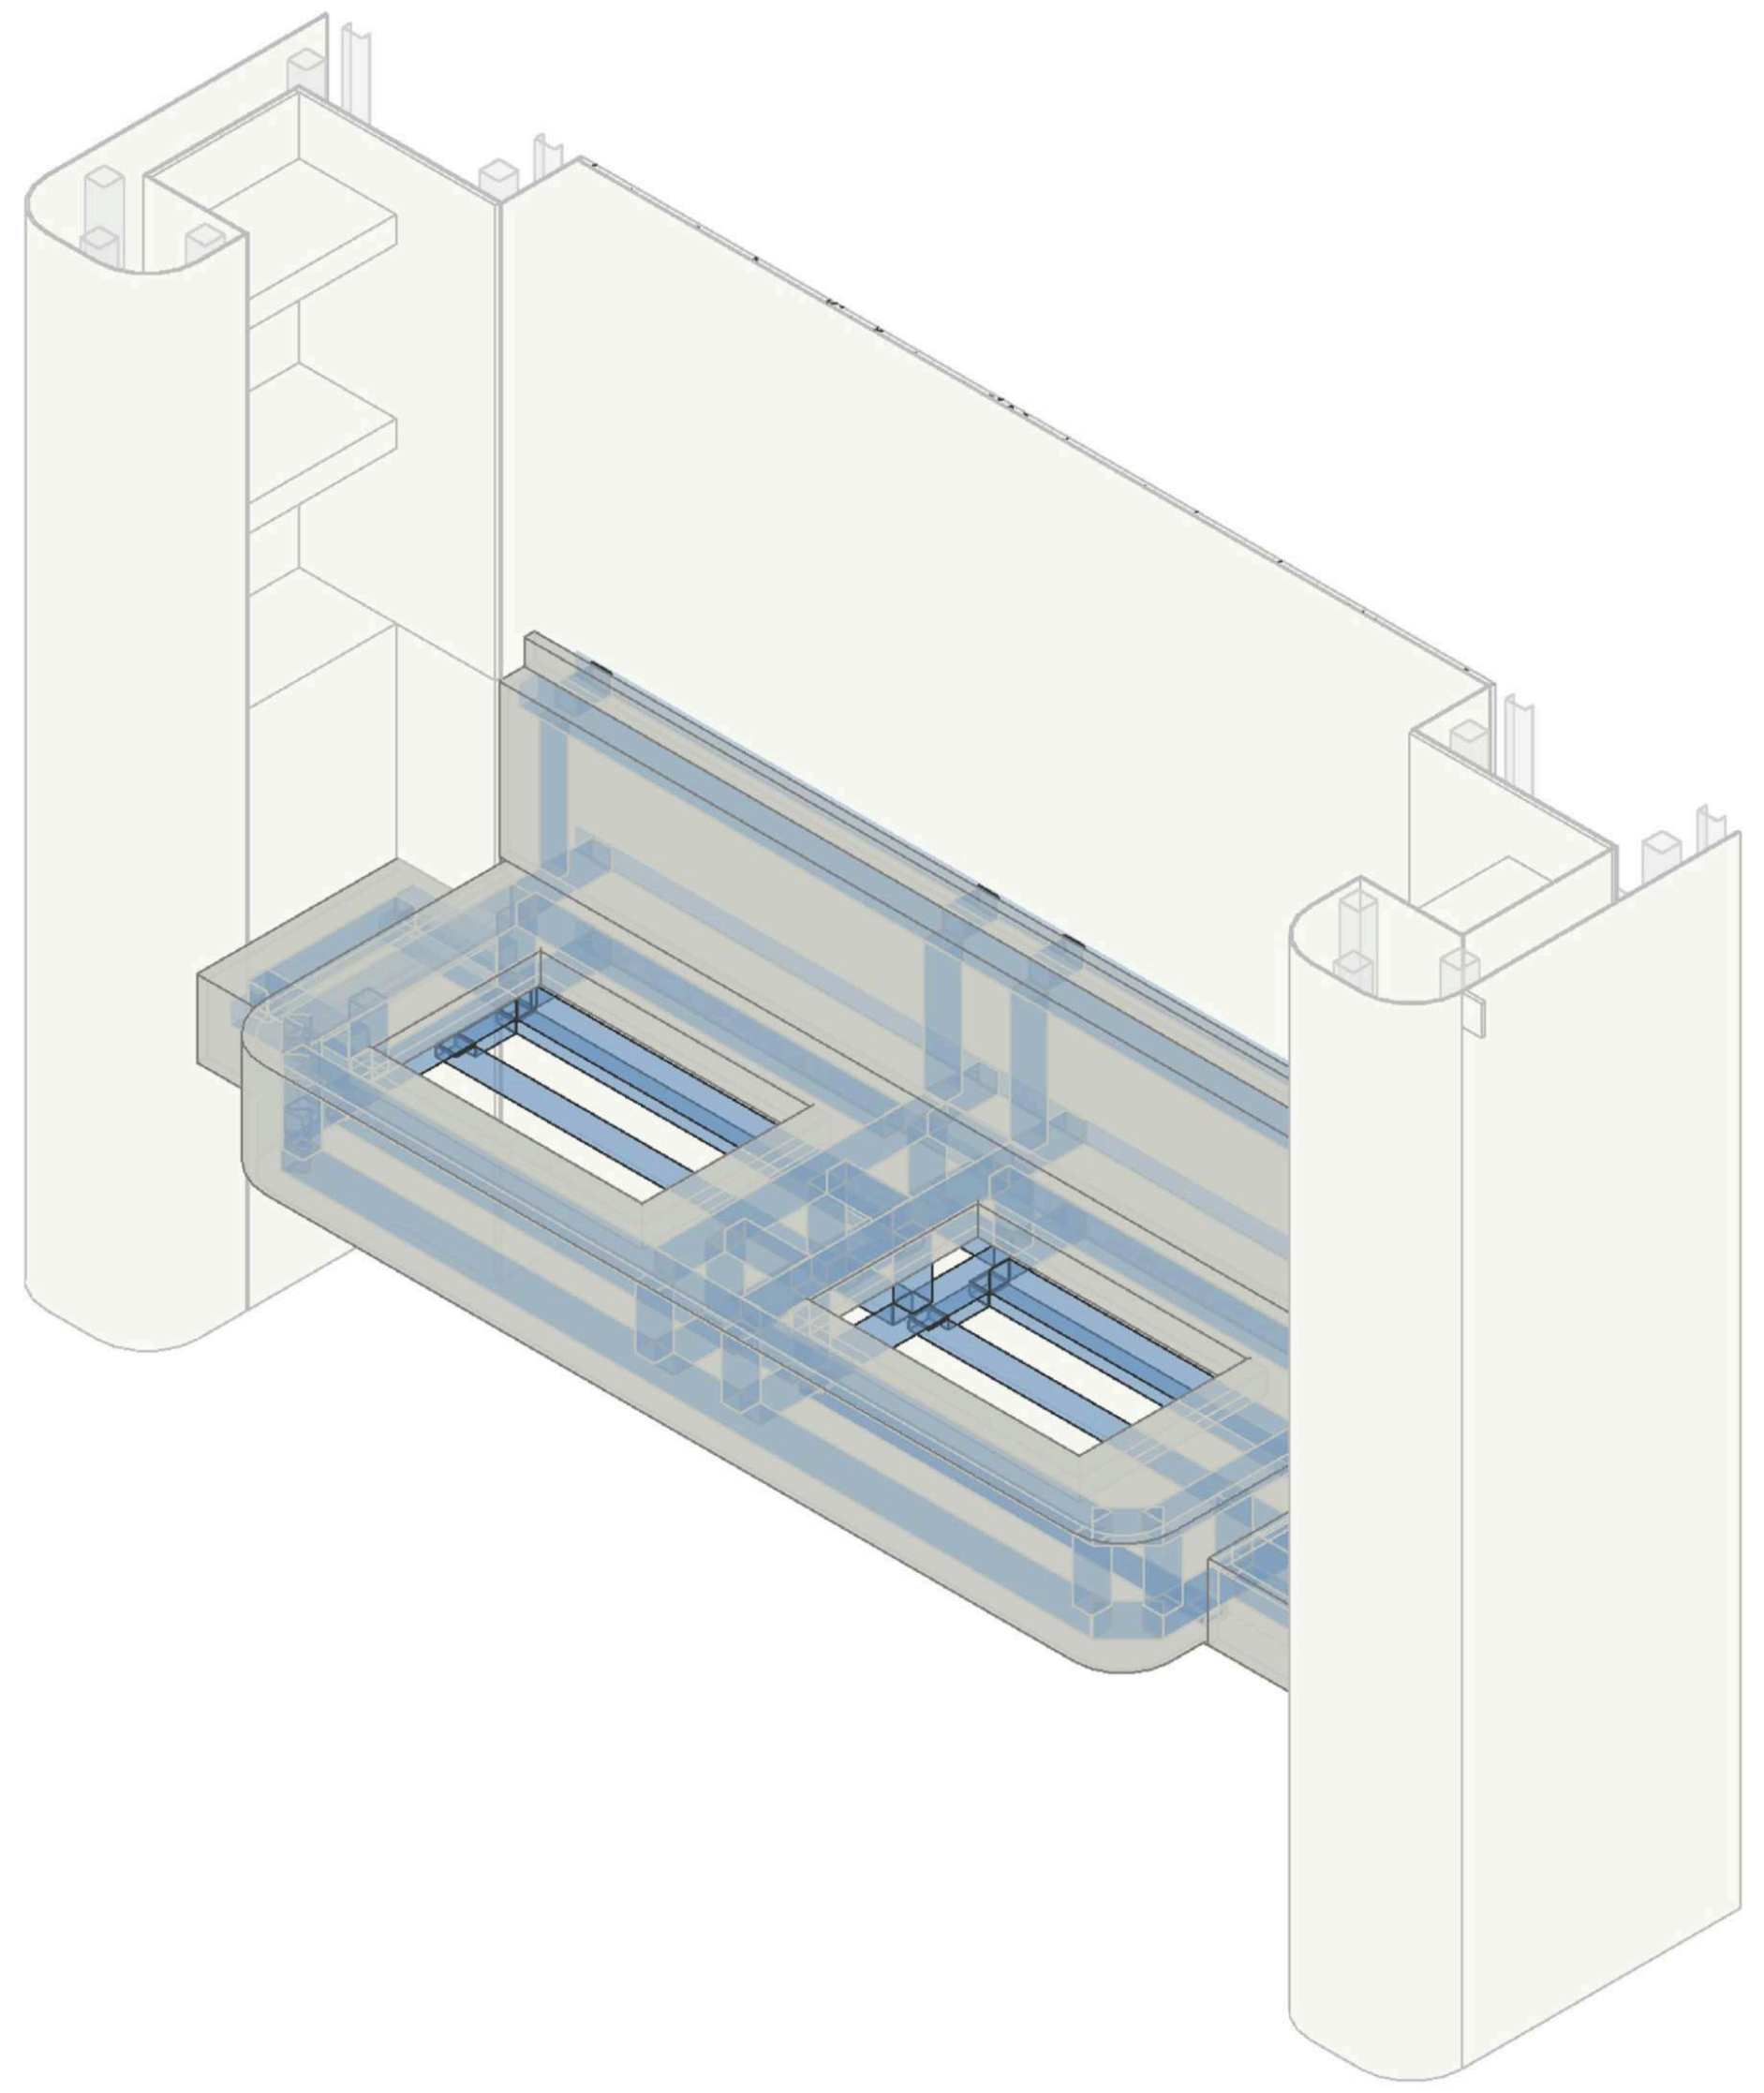

FIBORN

图例A
LEGEND A

编号	图例	说明
1		原始钢架
2		螺栓
3		钢片
4		钢架
5		石材

盖章

注释
Notes

1.本图纸如与现场尺寸有误，请施工人员与项目负责人联系。
2.施工前施工人员应认真查阅此图，如有不明确尺寸，按现场测量为准。
3.本图纸必须经甲乙双方认可并签字方可作为施工依据。

日期
Date 05/07/26

修订
Revision

1

项目
Project
潮映华岸府3-801

比例
Scale

主卫洗手台石材钢架

图纸编号
Drawing No.
ST-01

项目编号
Project No.

©2025

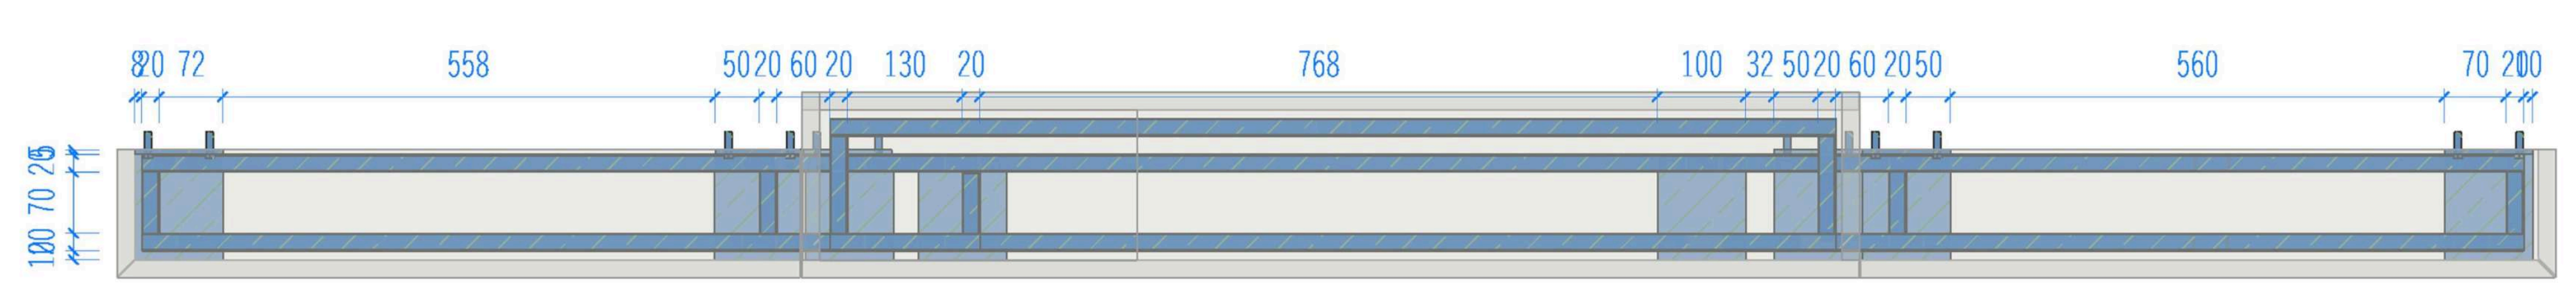
8 20 72
558
50 20 60 20 130 20
768
100 32 50 20 60 20 50
560
70 20 10
10 20 70 20 5

平面视图

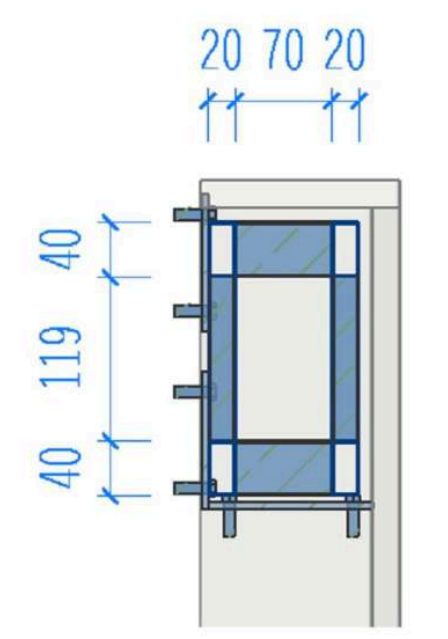
20 70 20
40
119
40

剖面视图

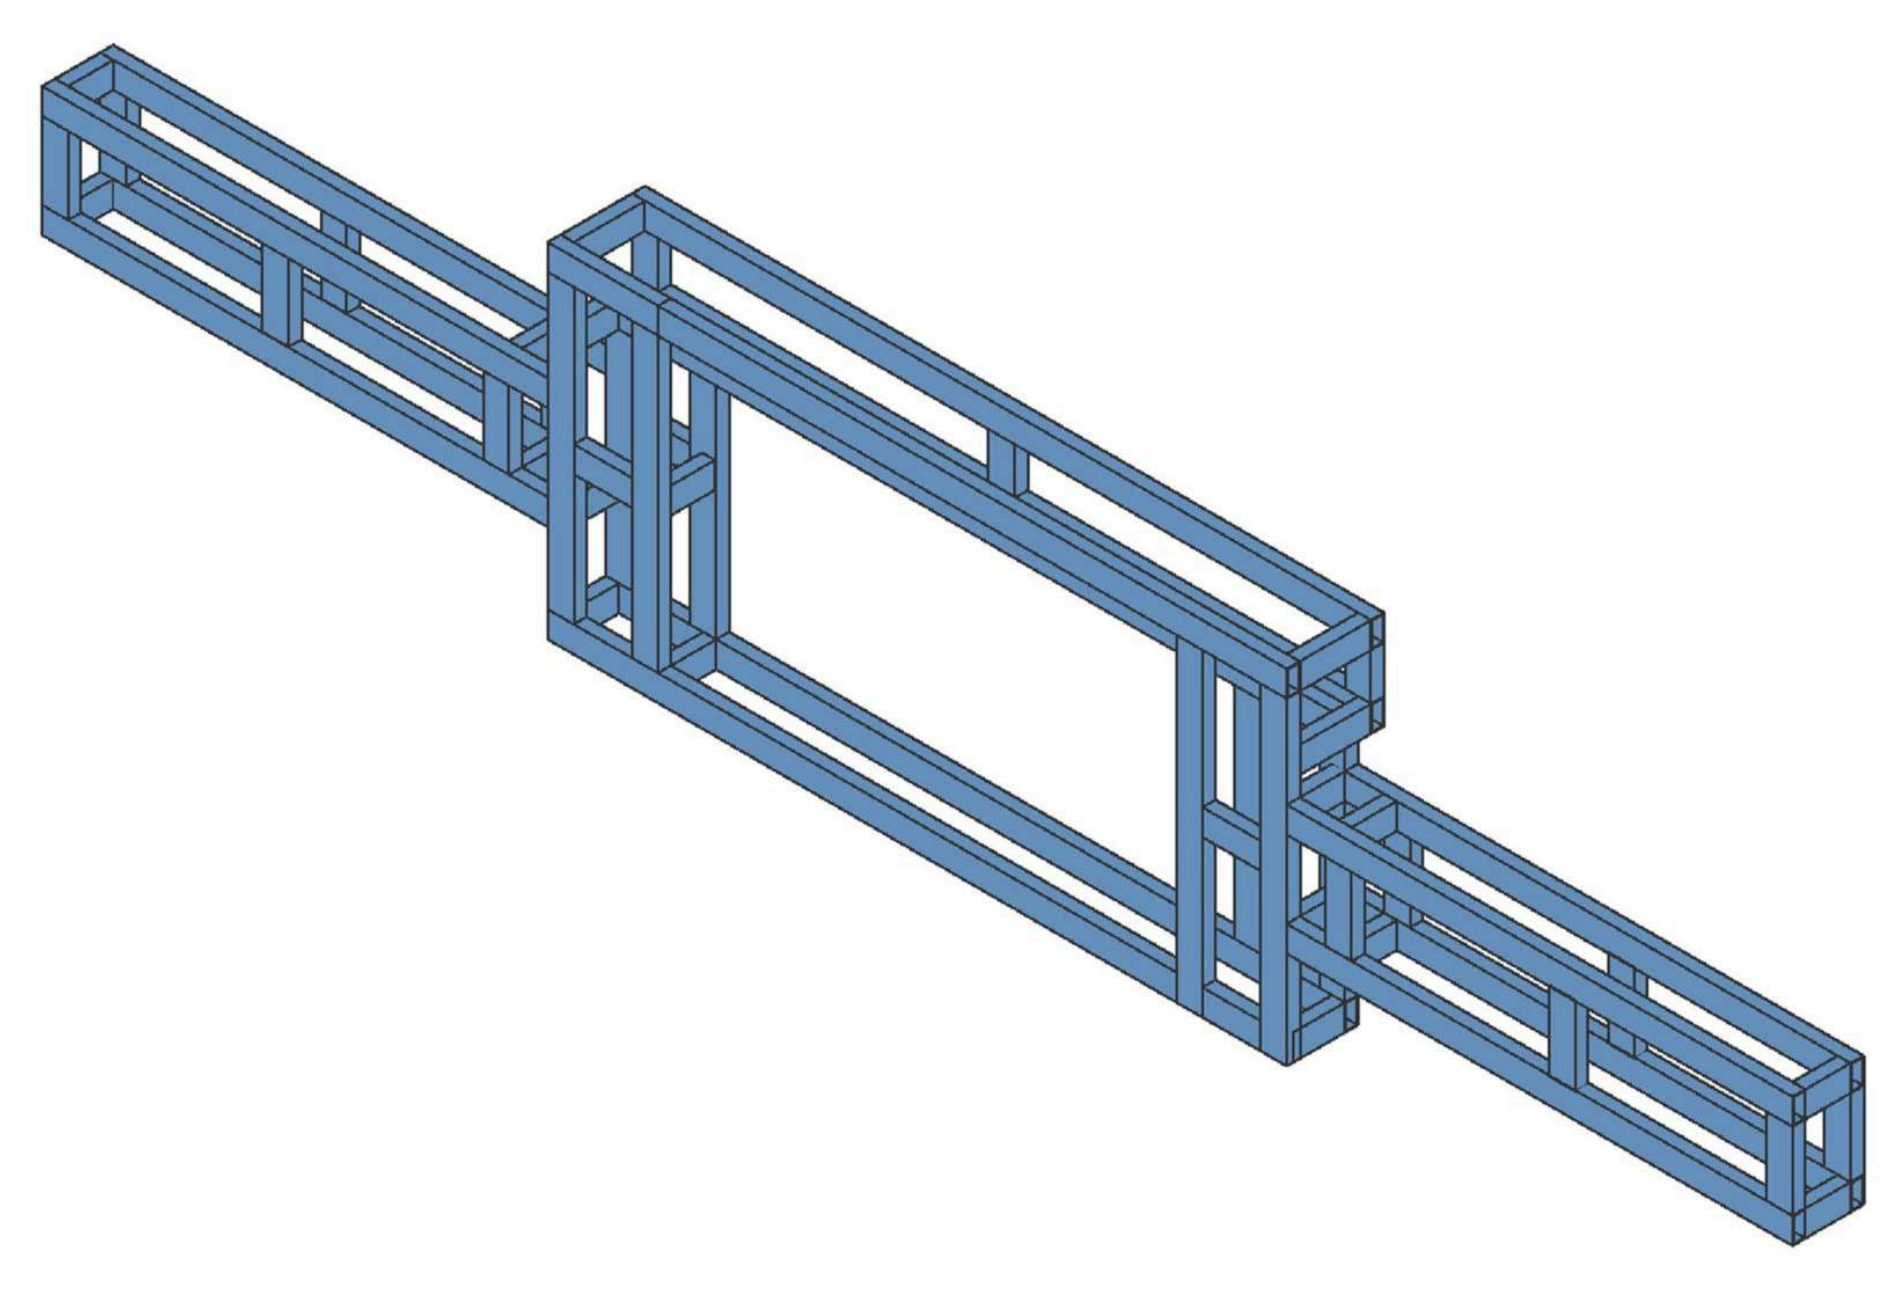

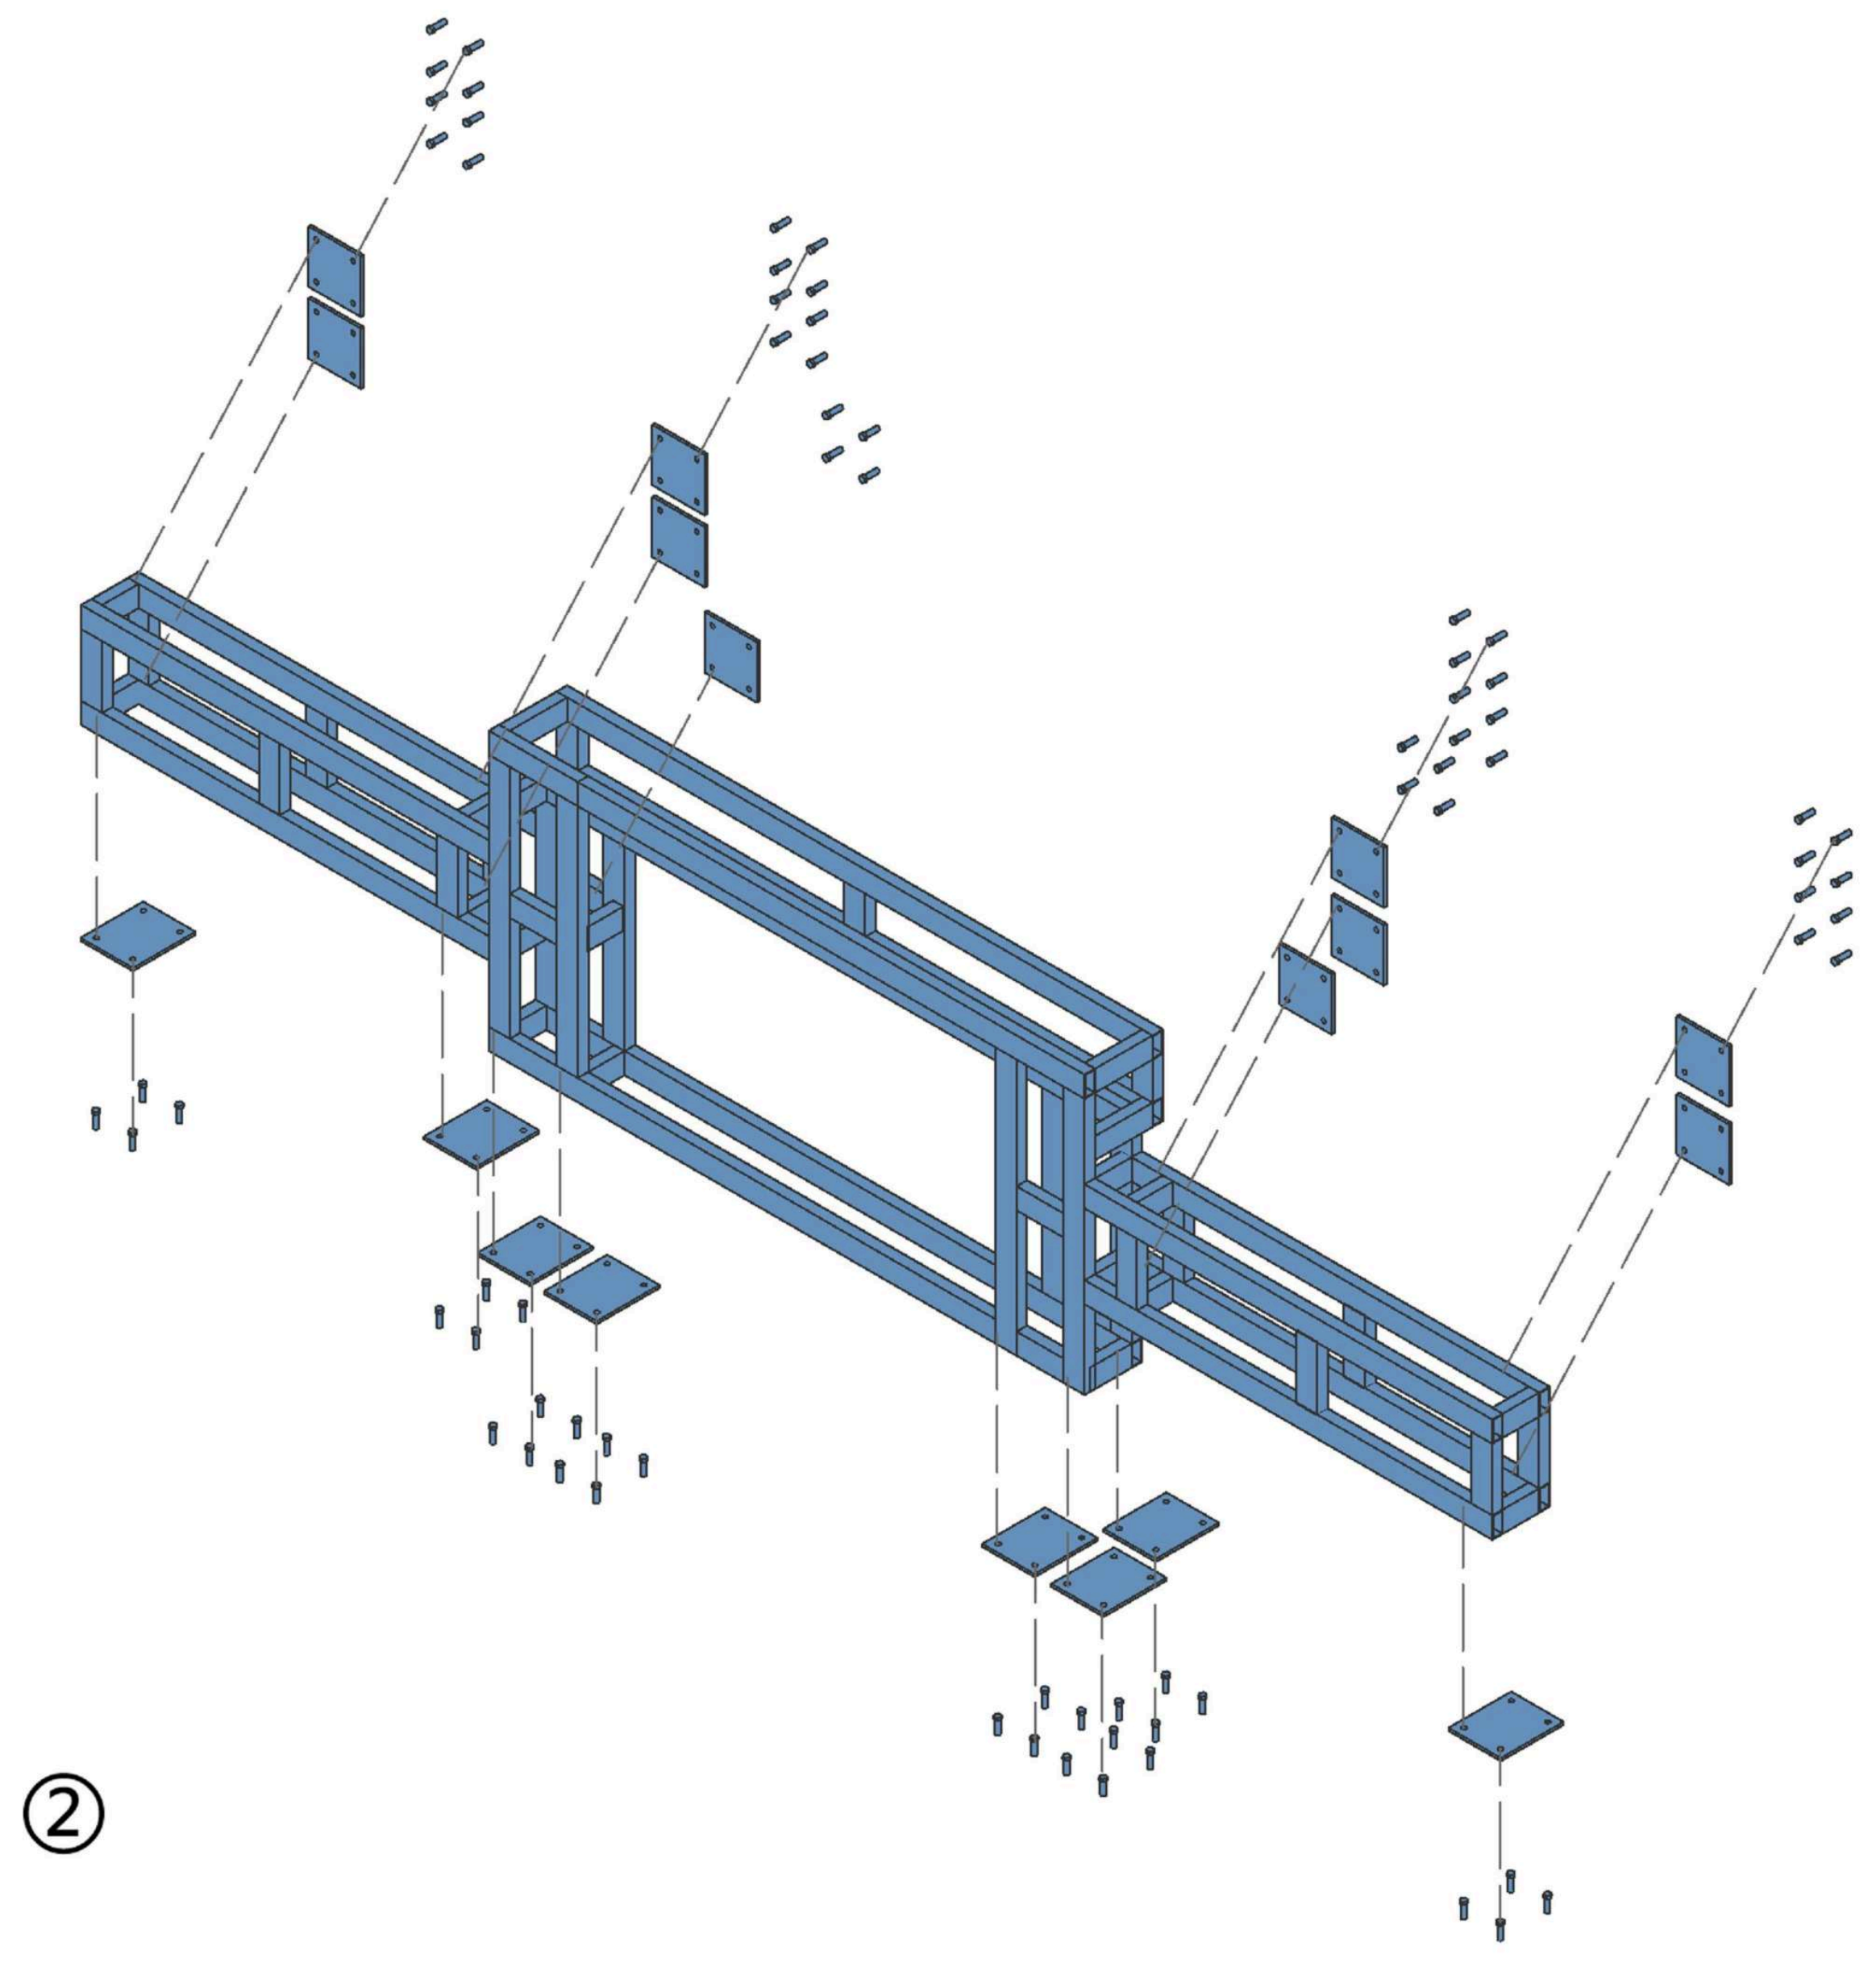

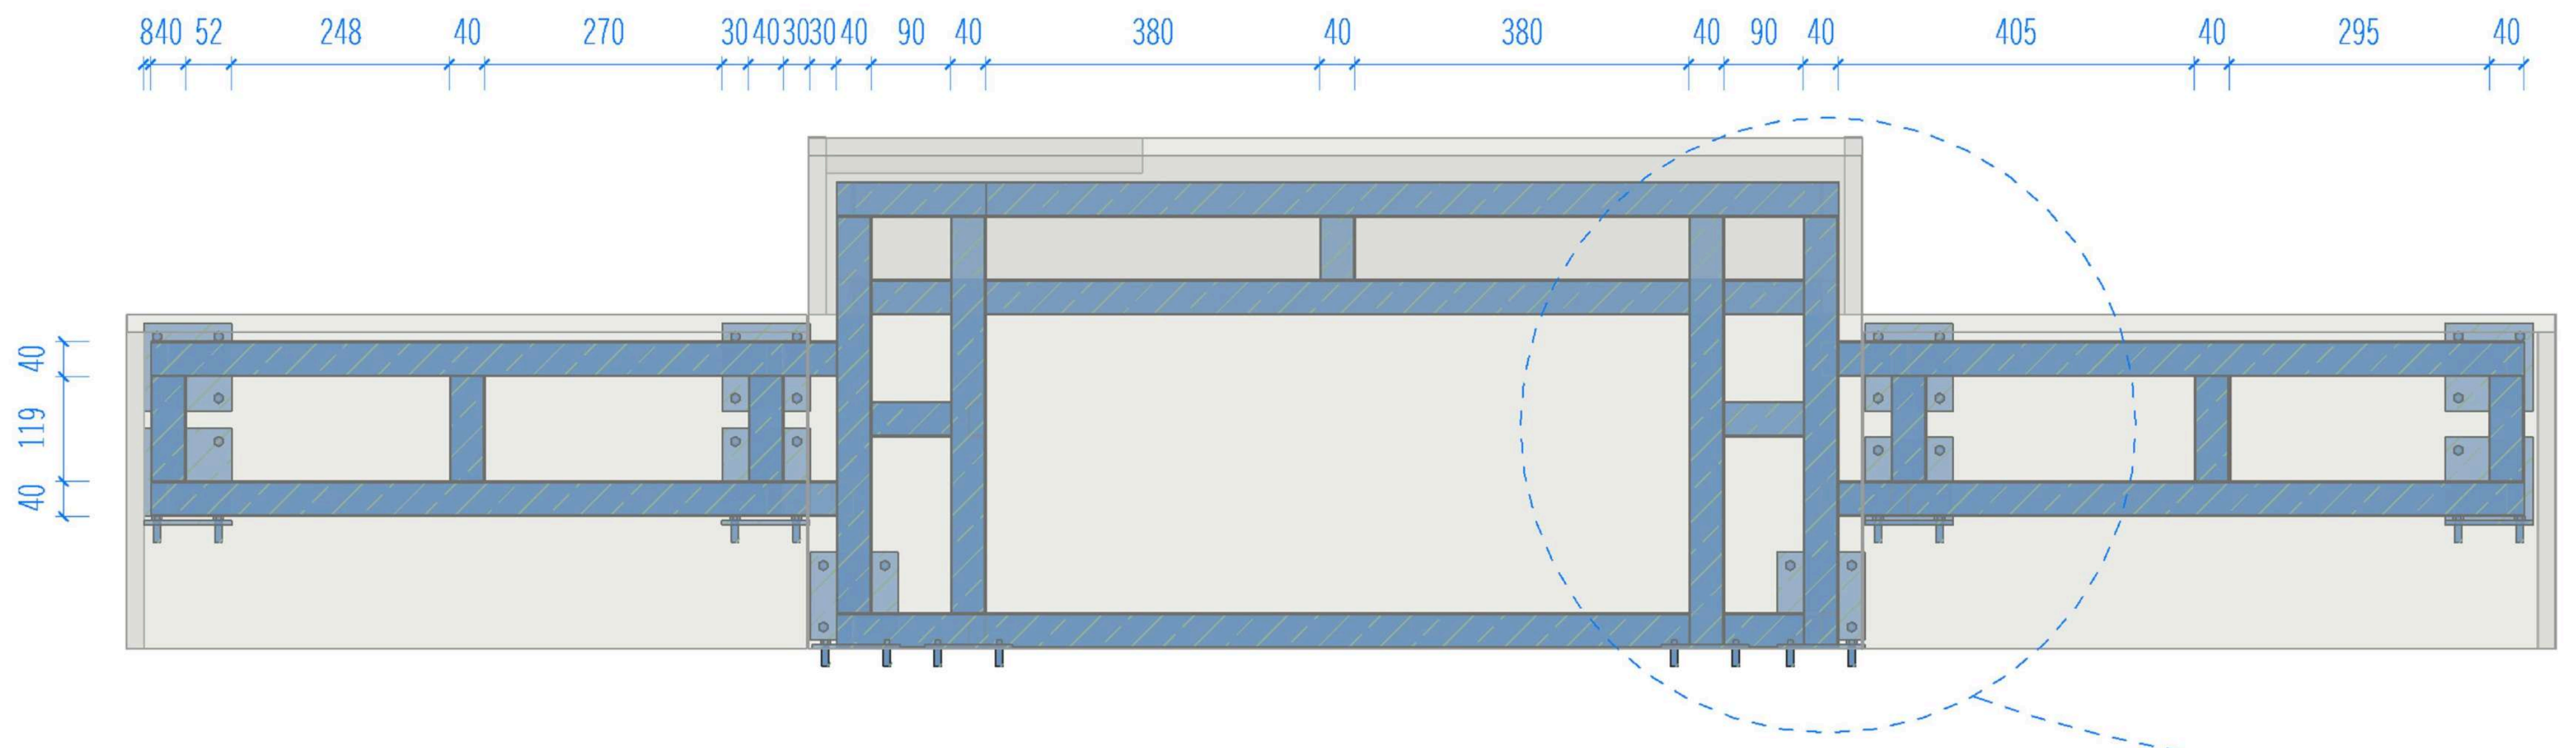
8 40 52 248 40 270 30 40 30 30 40 90 40 380 40 380 40 90 40 405 40 295 40
40
119
40

立面视图

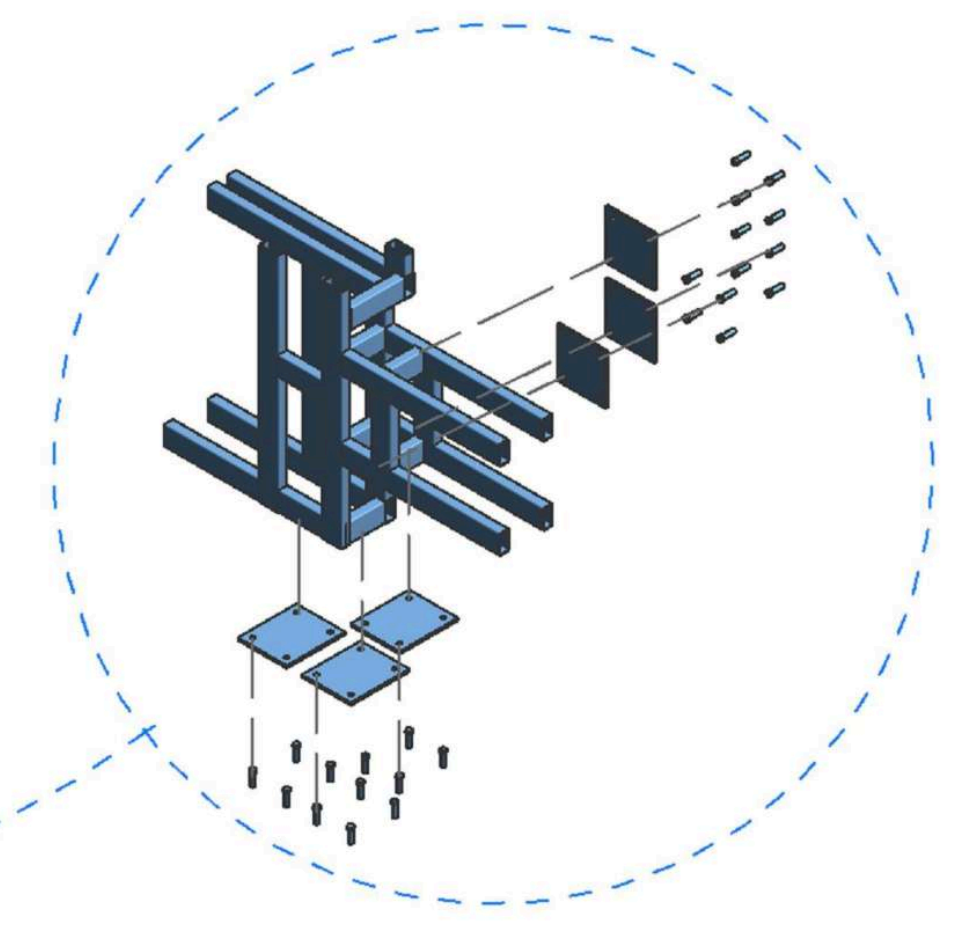

节点图

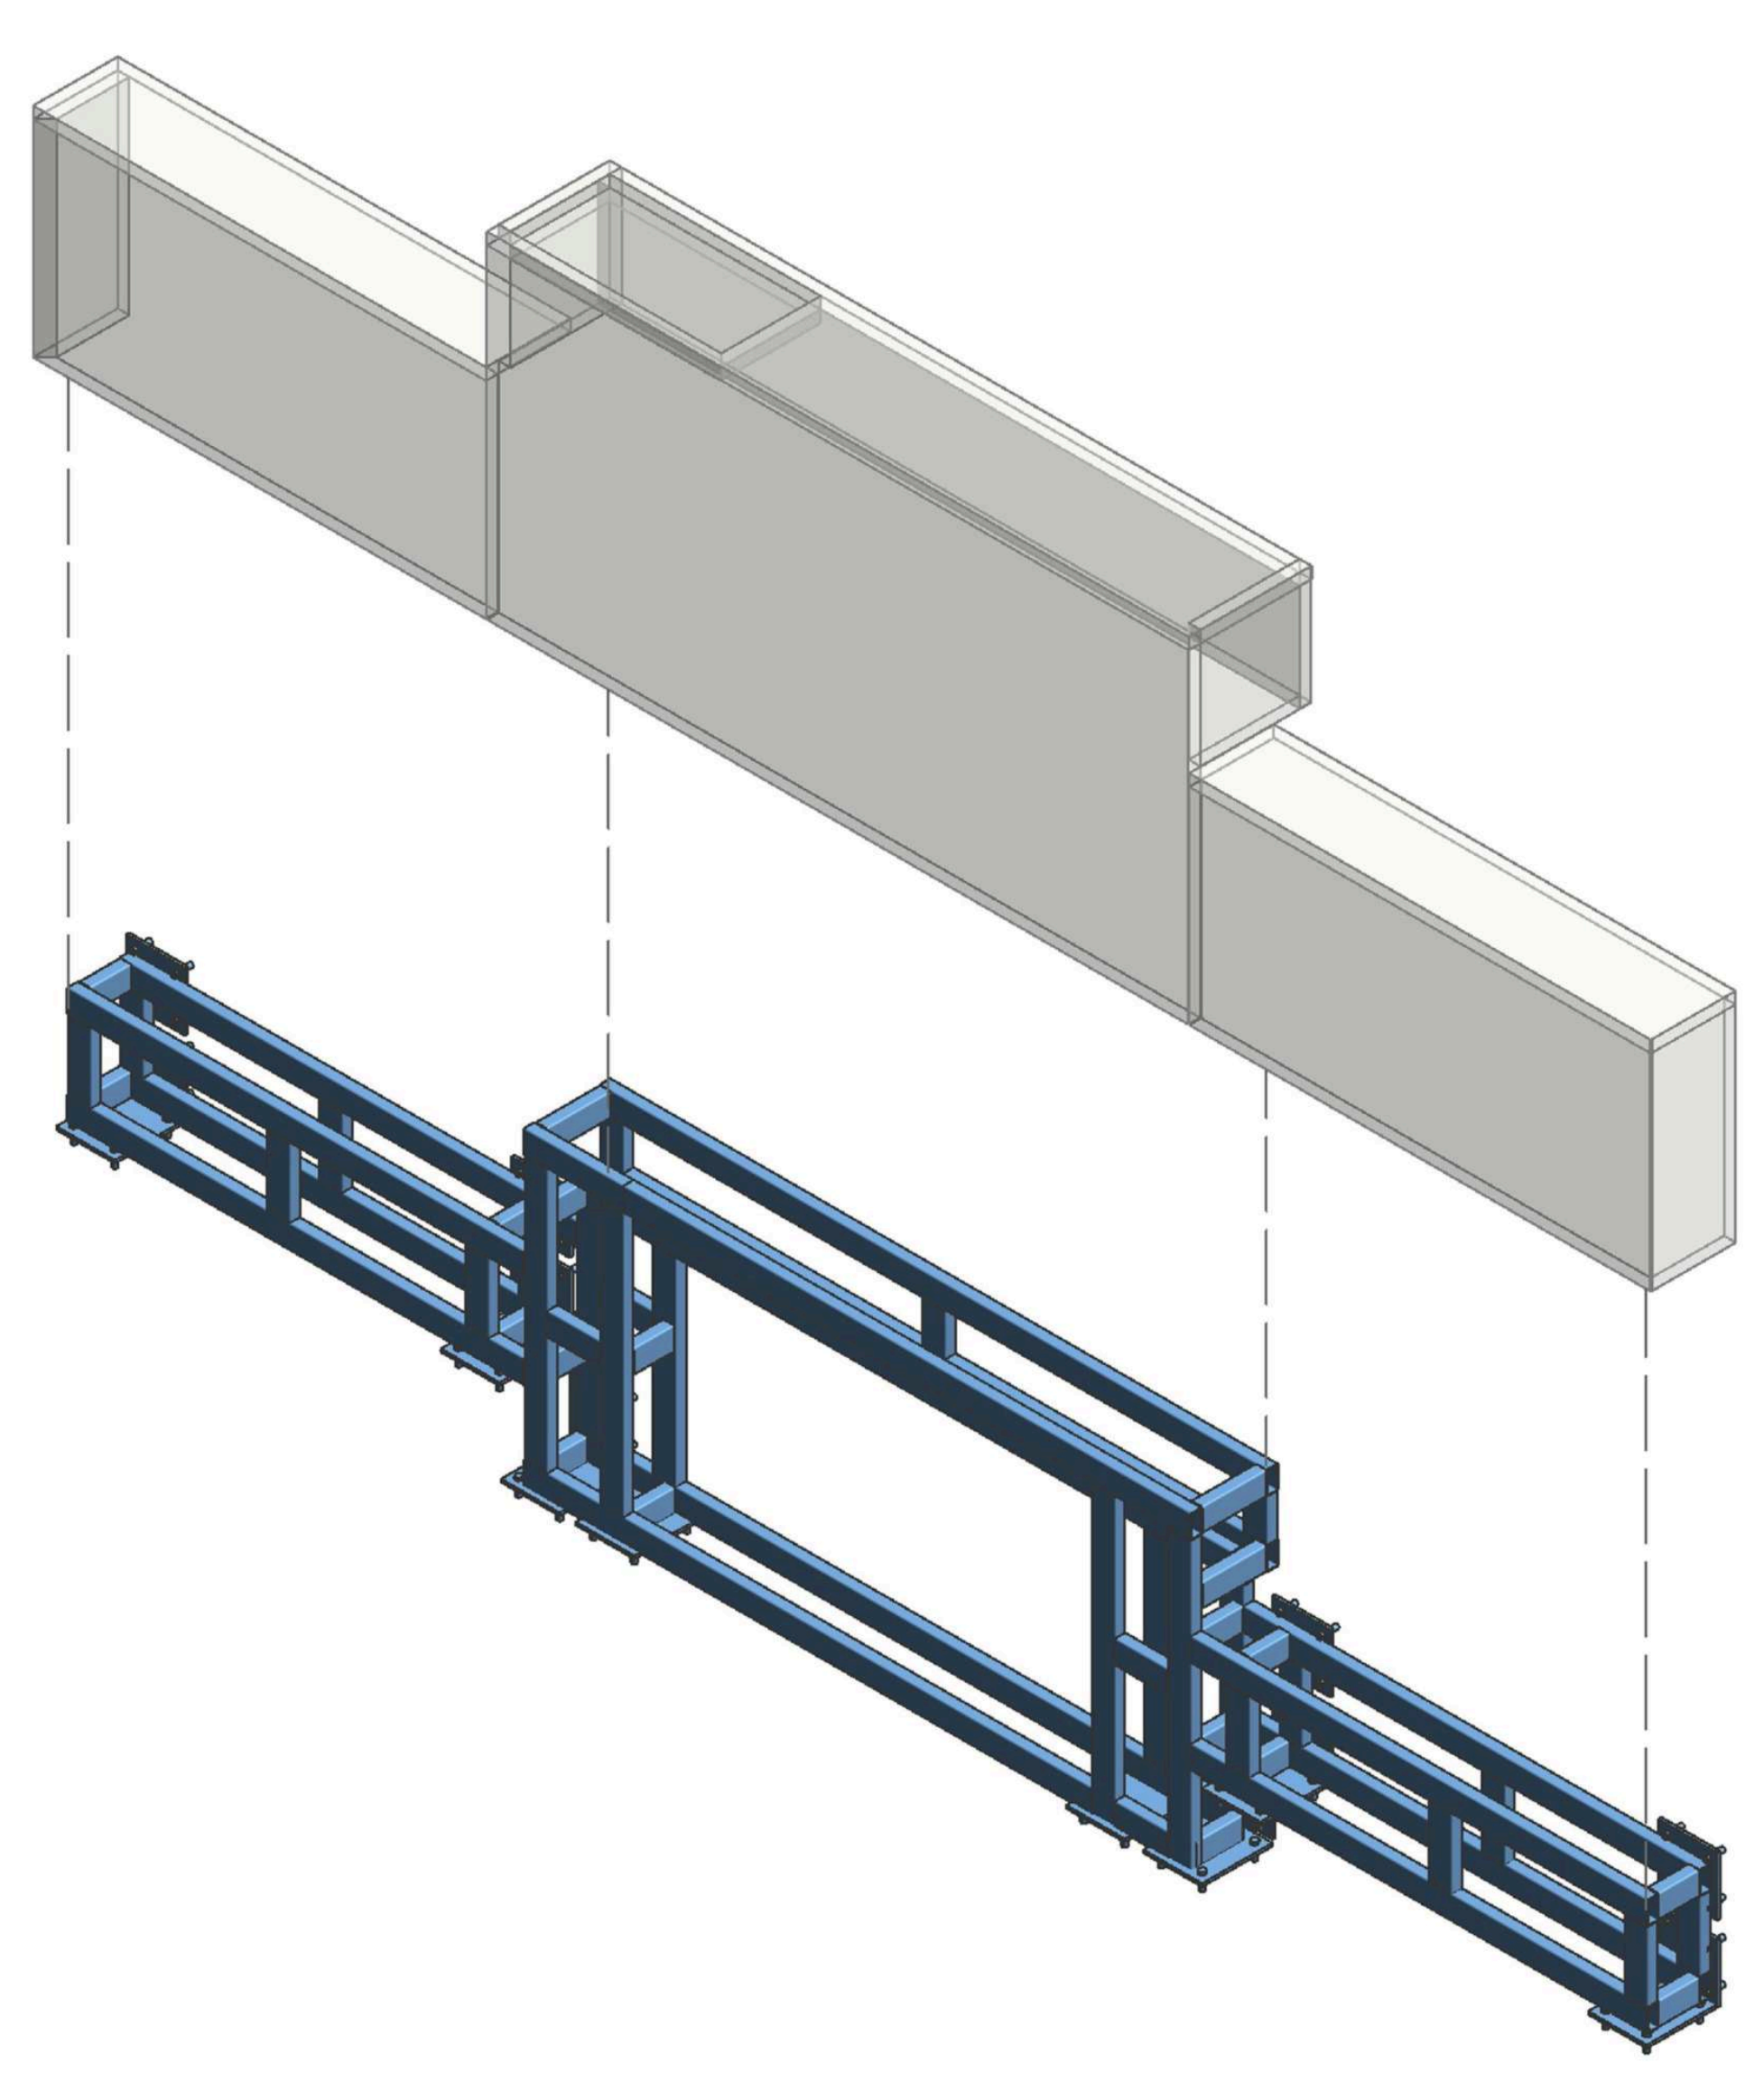

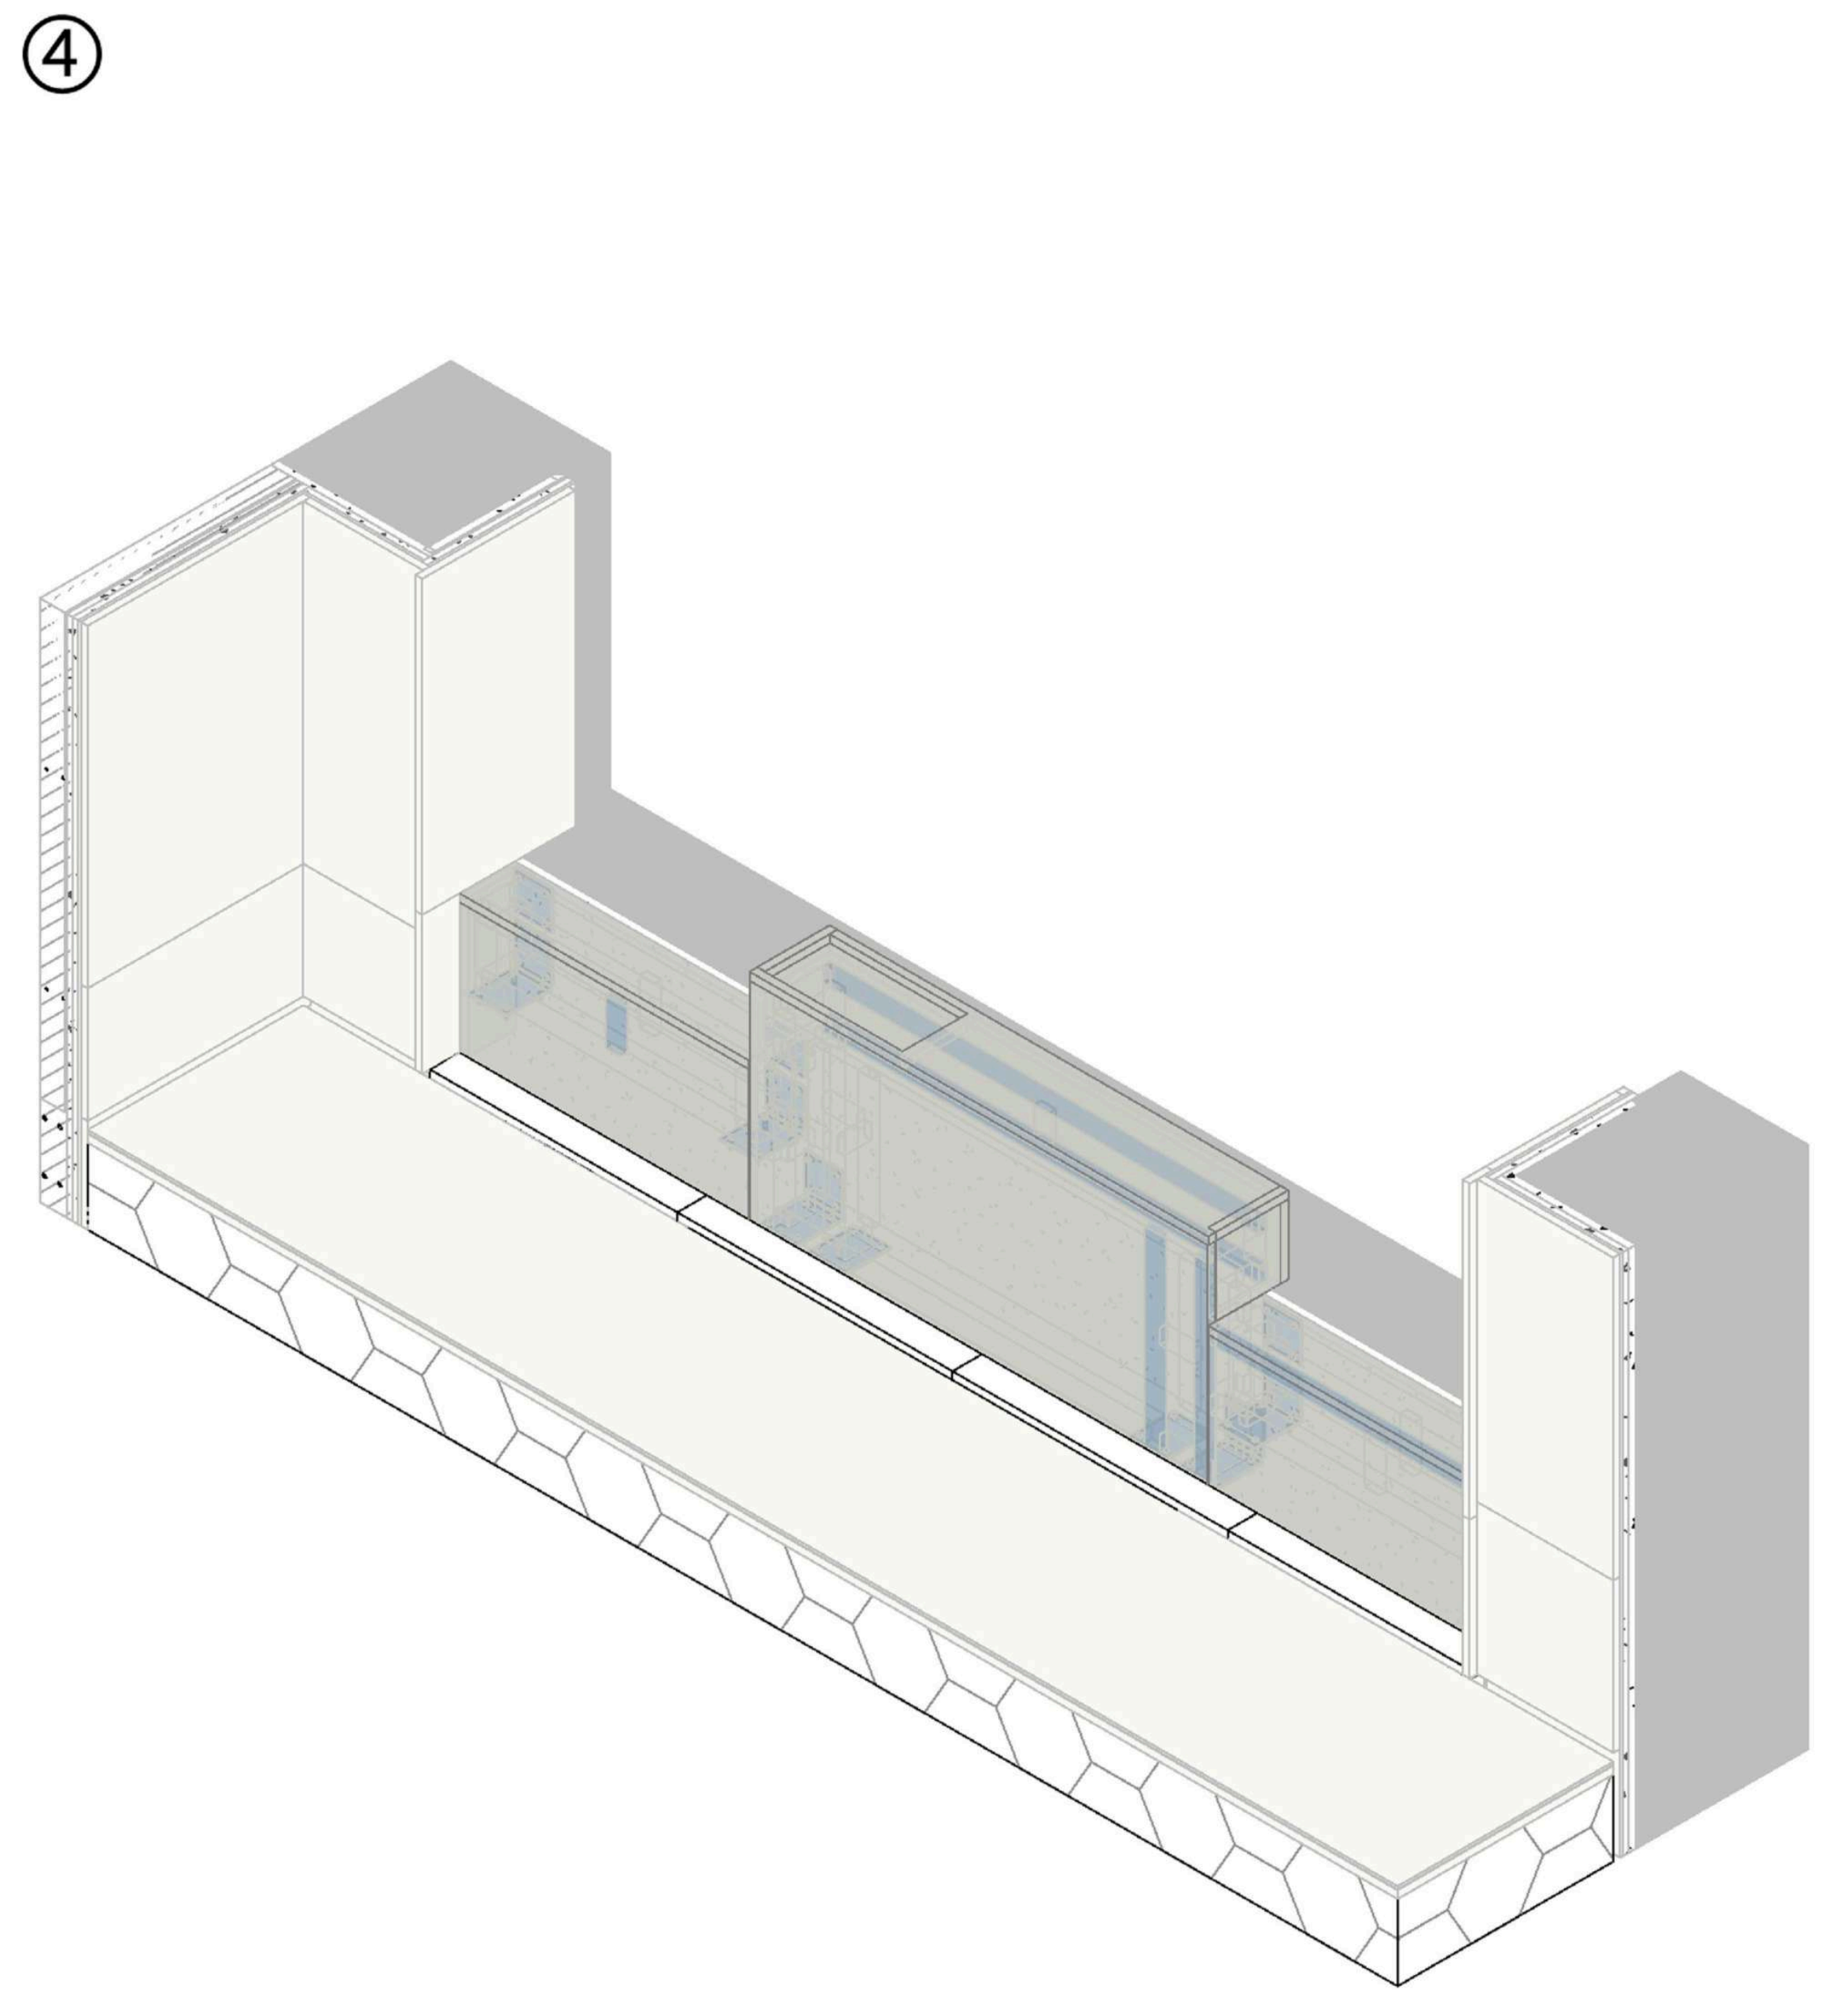

图例A
LEGEND A

编号	图例	说明
1		原始钢架
2		螺栓
3		钢片
4		钢架
5		石材

盖章

注释
Notes

1.本图纸如与现场尺寸有误，请施工人员与项目负责人联系。
2.施工前施工人员应认真查阅此图，如有不明确尺寸，按现场测量为准。
3.本图纸必须经甲乙双方认可并签字方可作为施工依据。

日期
Date 04/24/26

修订
Revision

1

项目
Project
潮映华岸府3-801

比例
Scale
主卫浴缸石材钢架

图纸编号
Drawing No.
ST-02

项目编号
Project No.
©2025

1

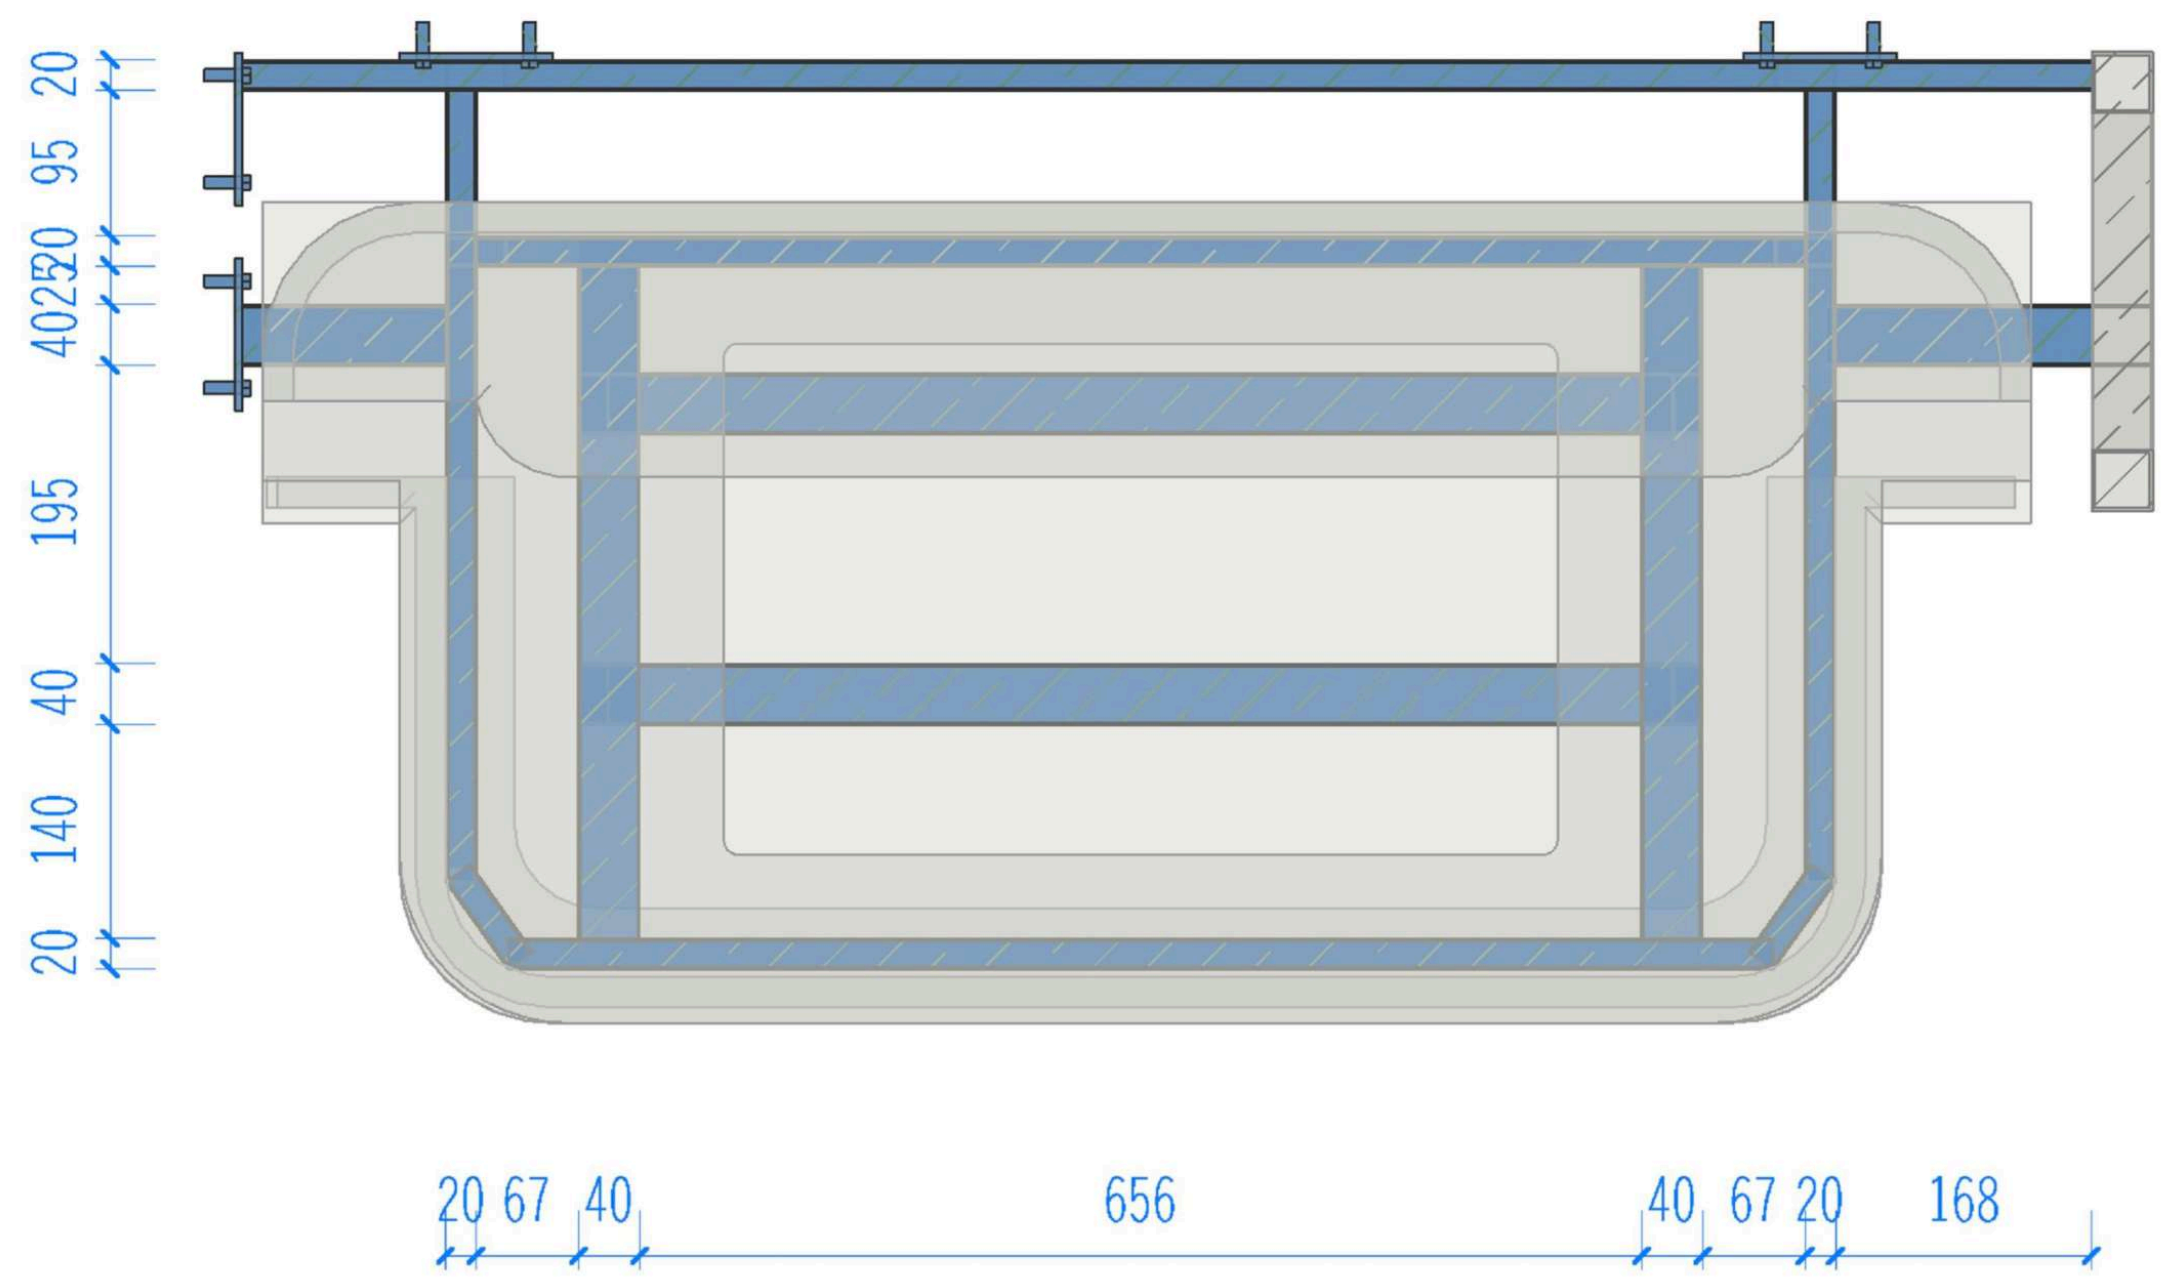
20
95
20
40
25
195
40
140
20
20 67 40
656
40 67 20
168

平面视图

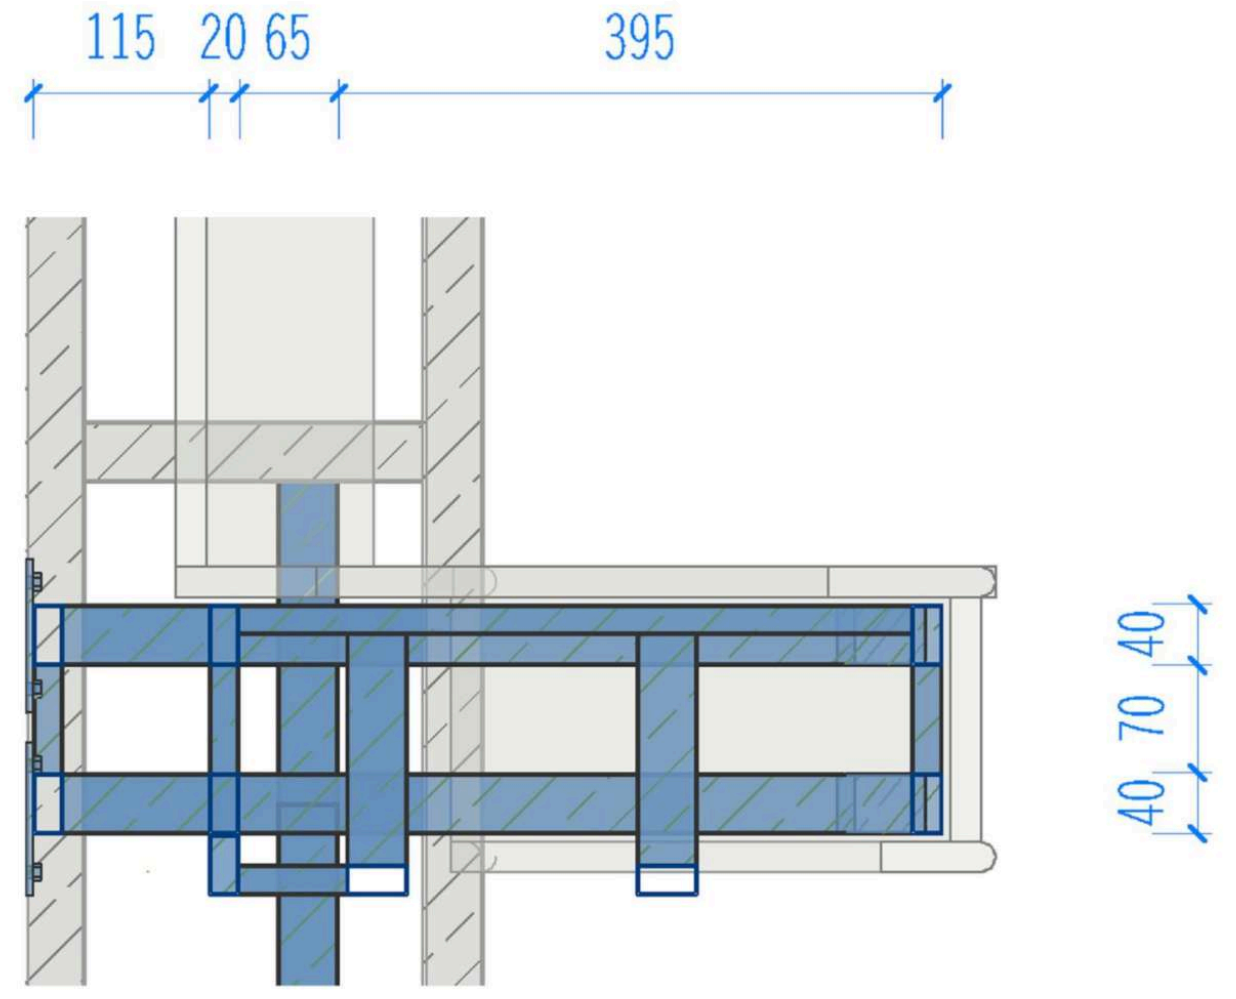
115
20 65
395
40
70
40

剖面视图

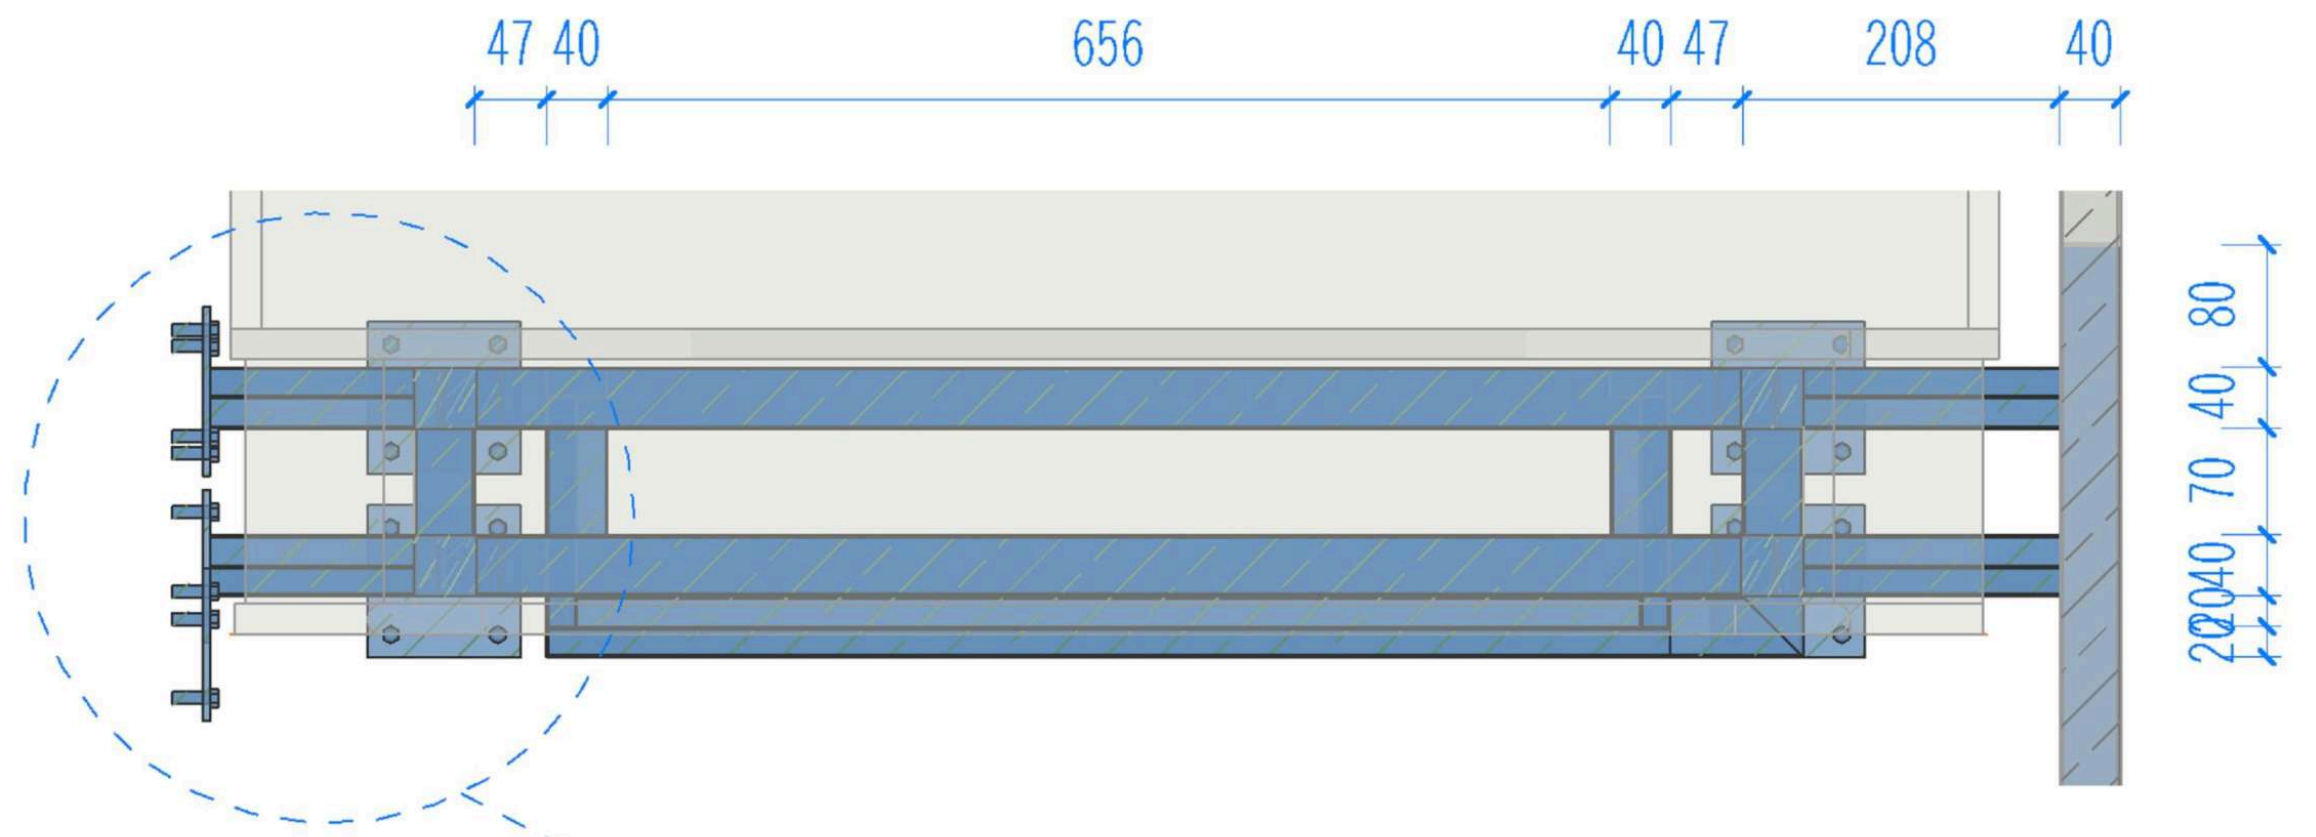
47 40
656
40 47
208
40
80
40
70
40
20
20

立面视图

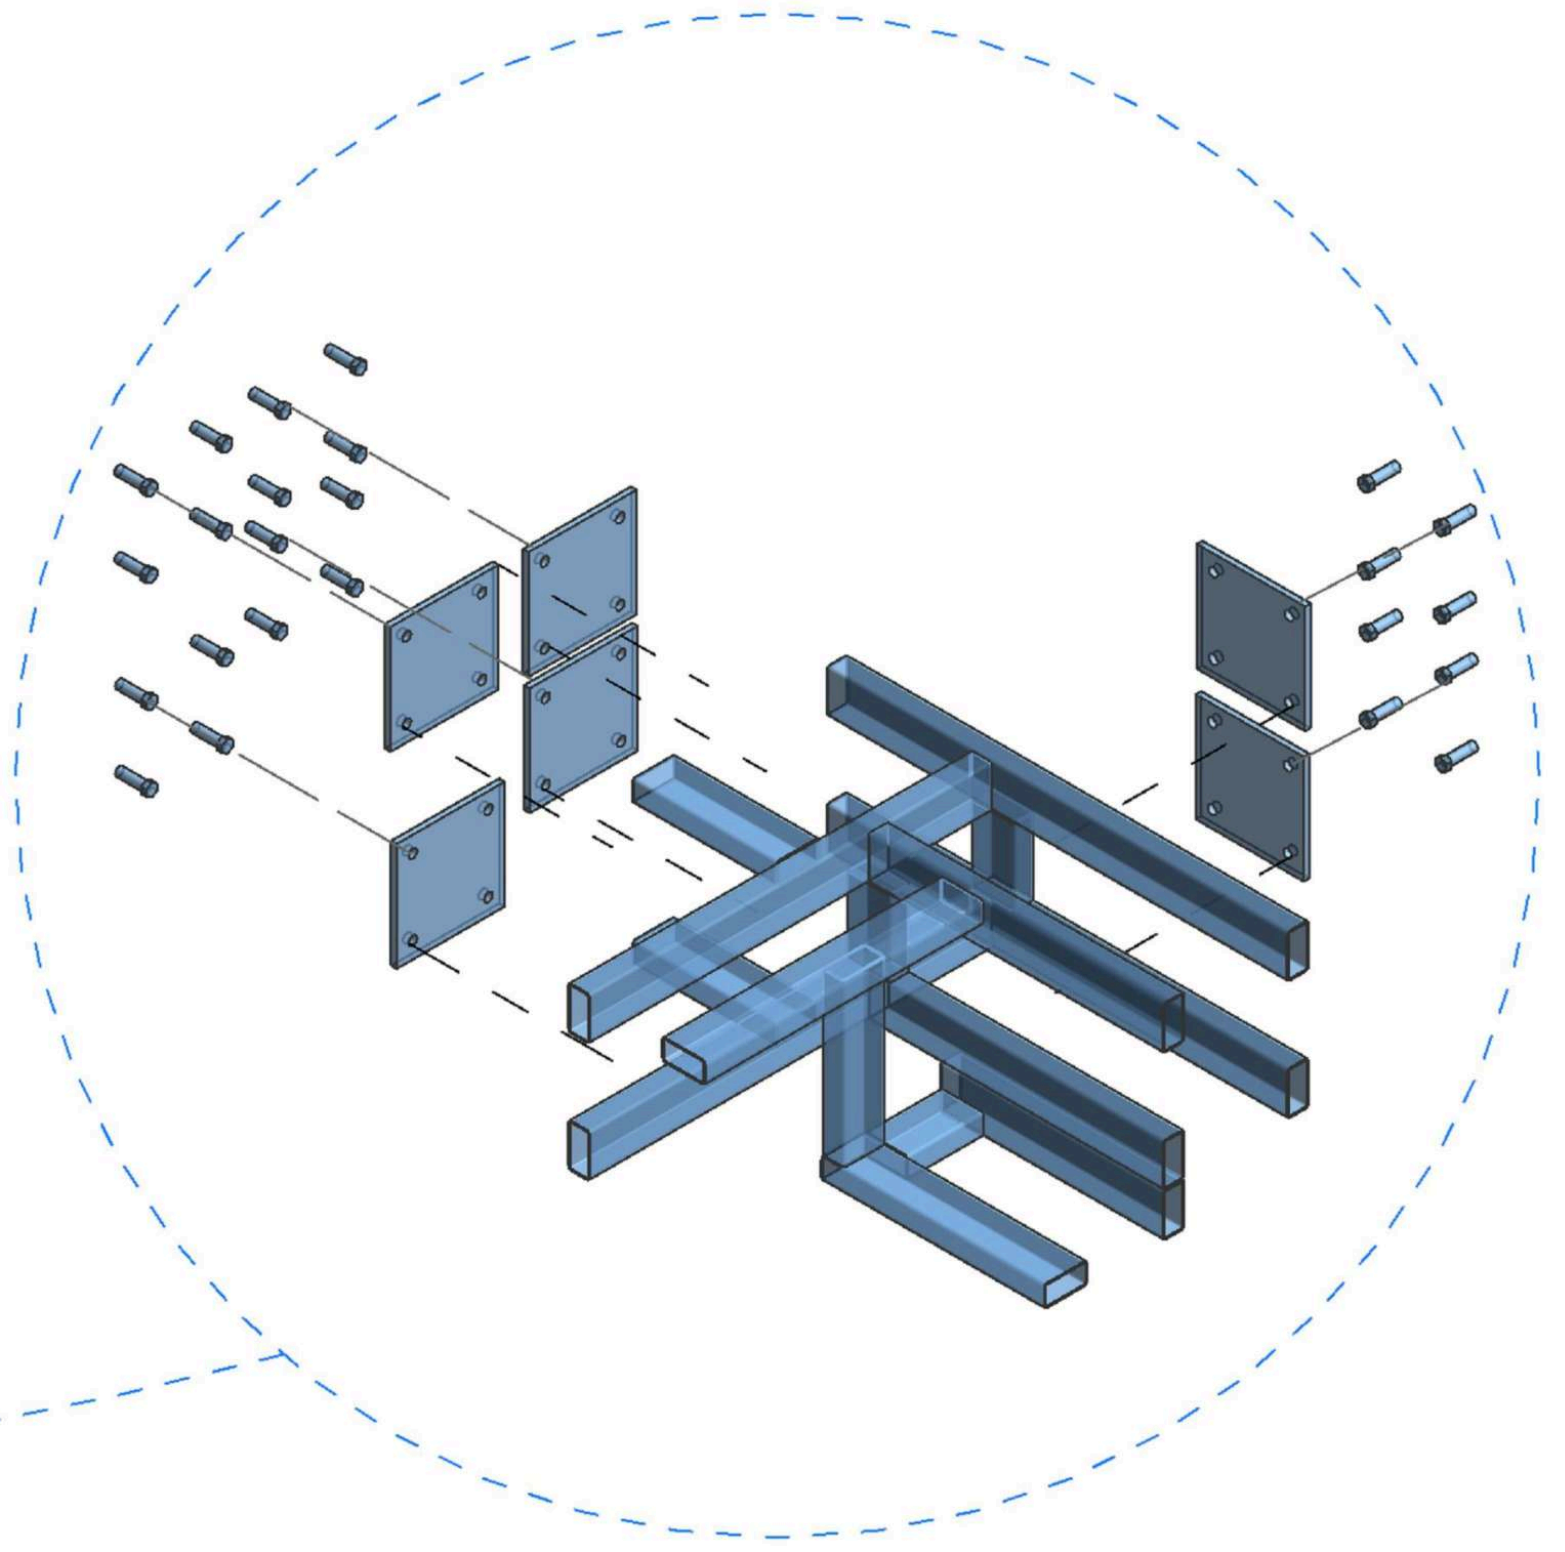

节点图

工厂预制钢架

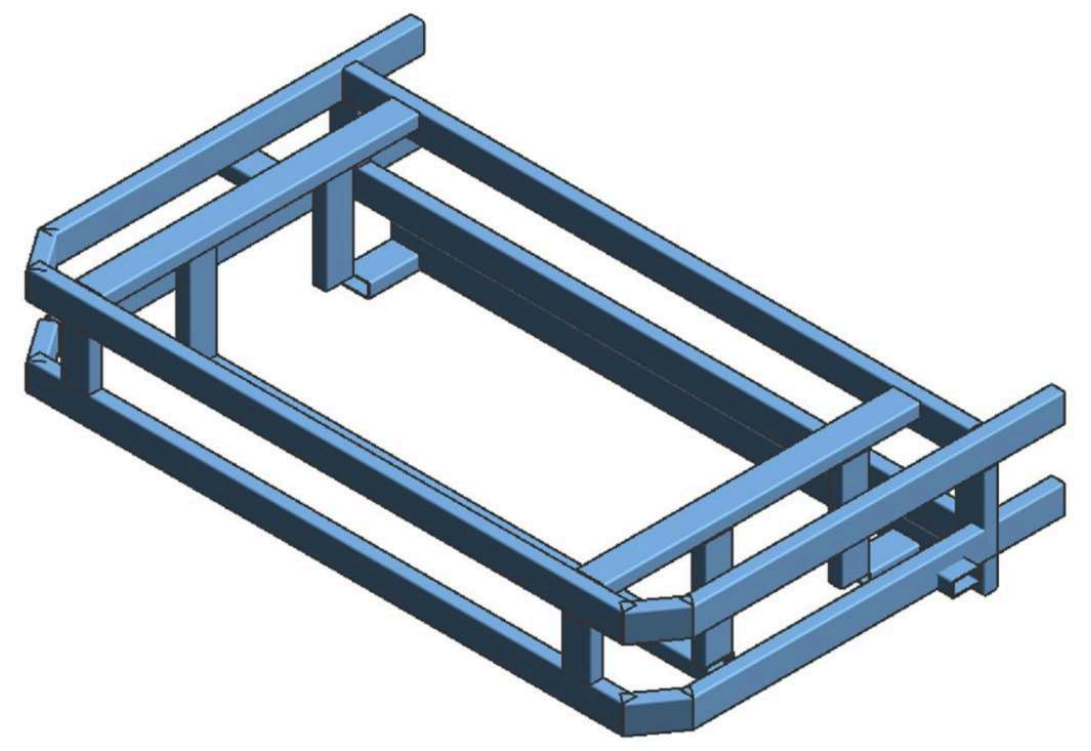

①

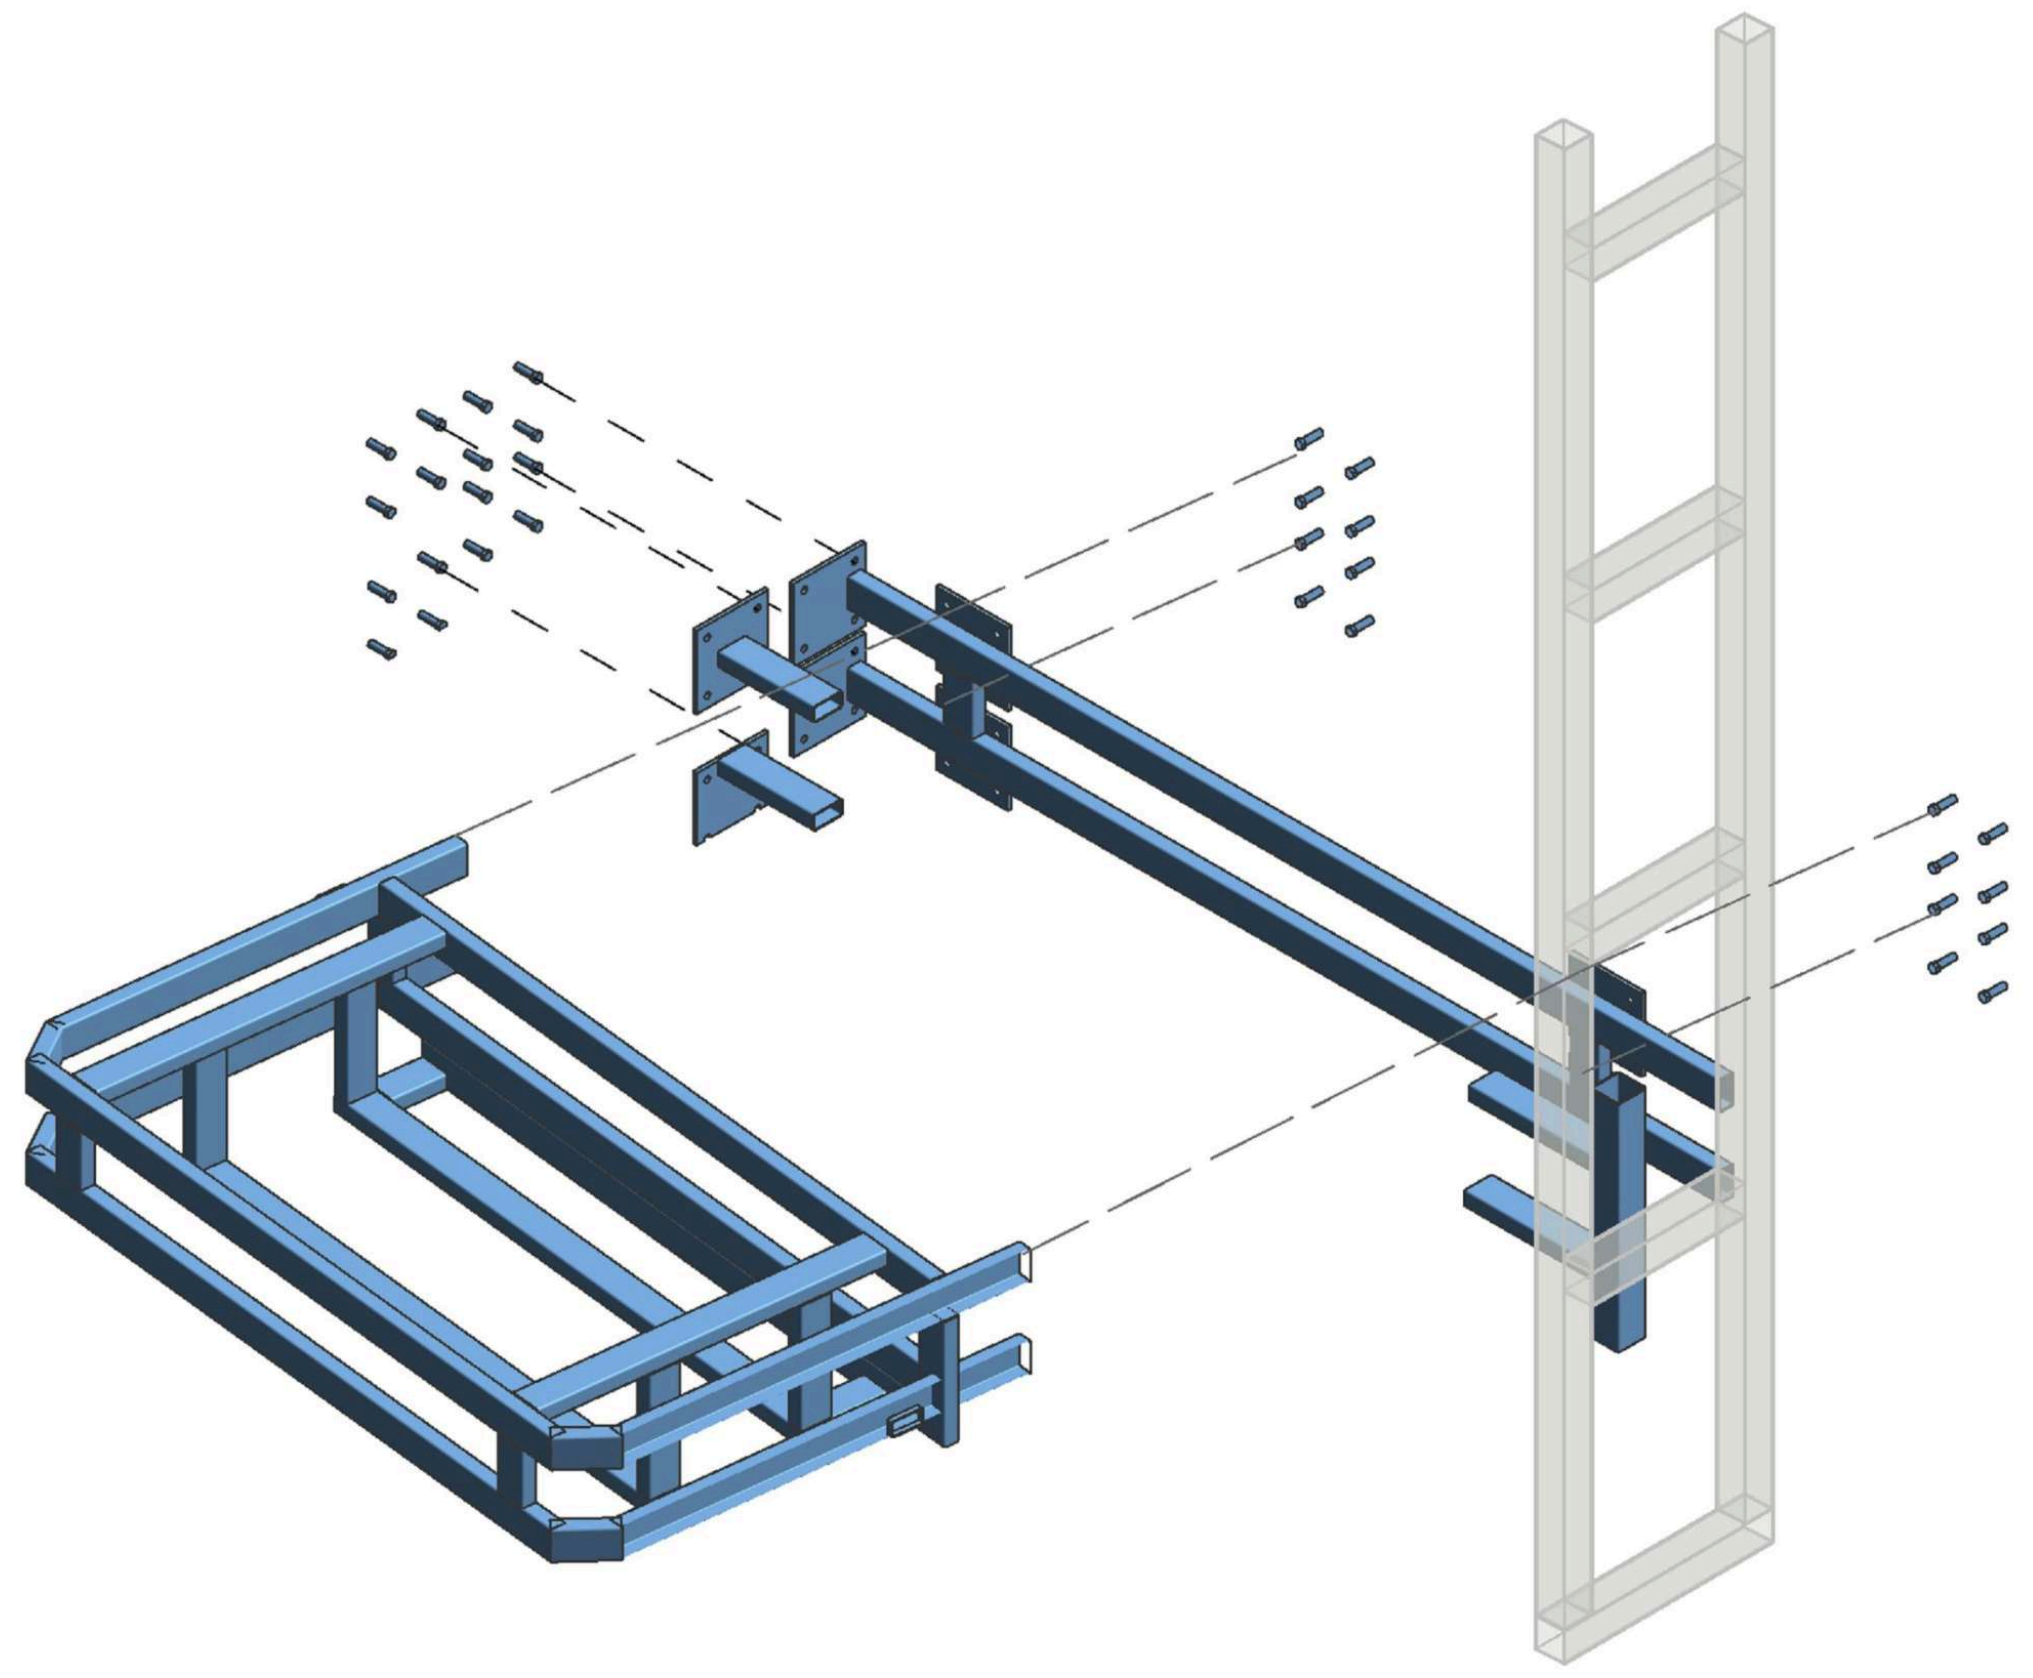

②

③

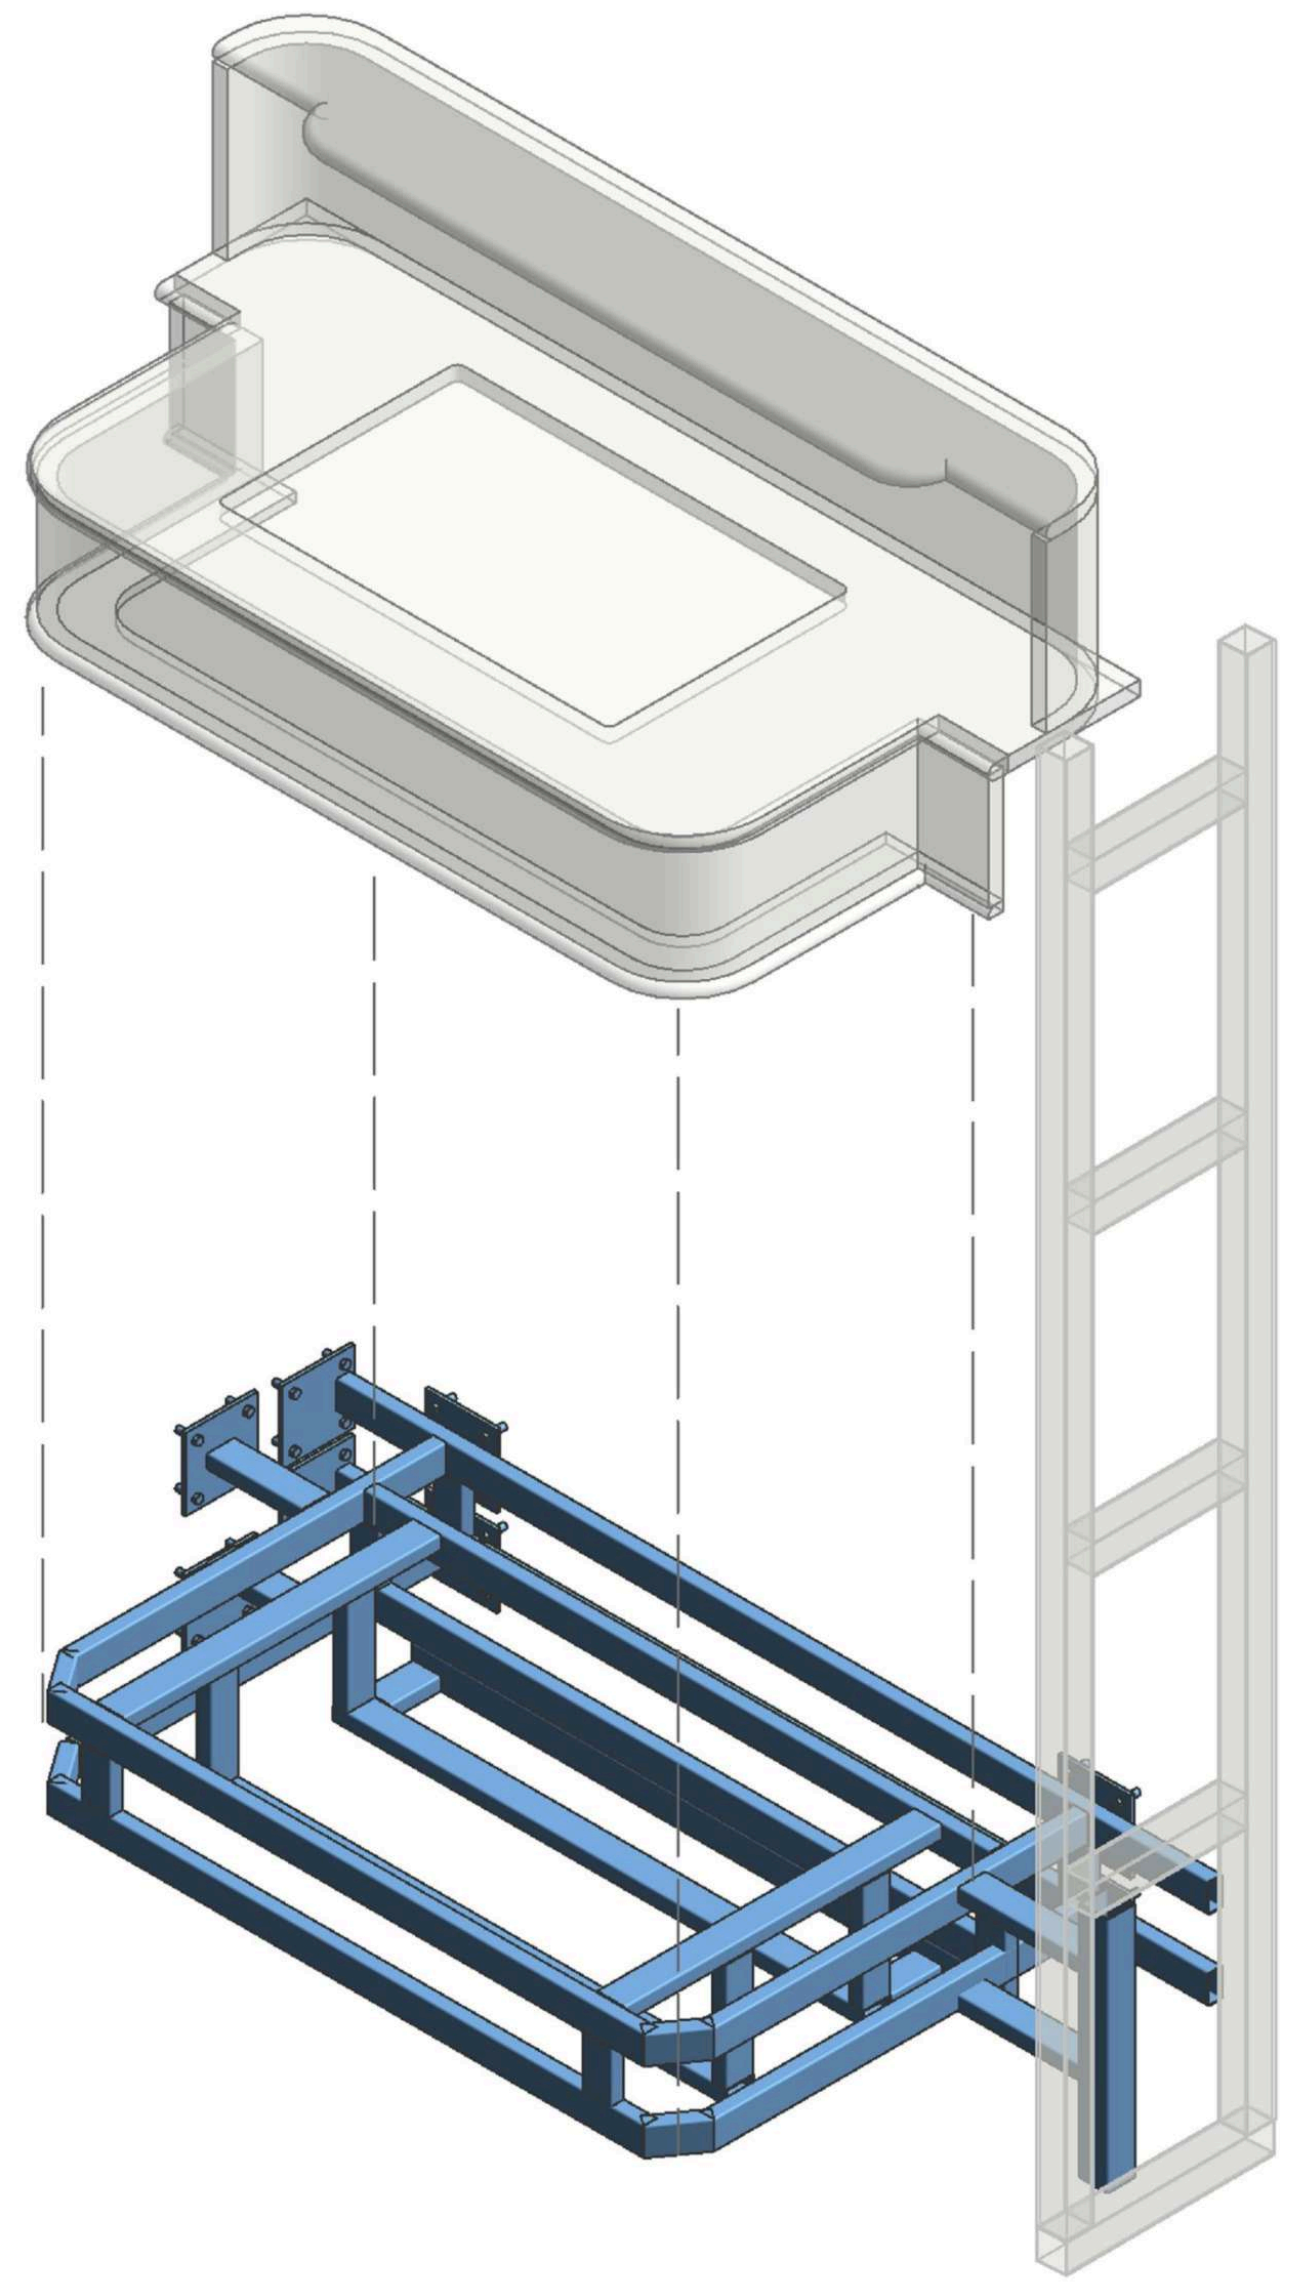

④

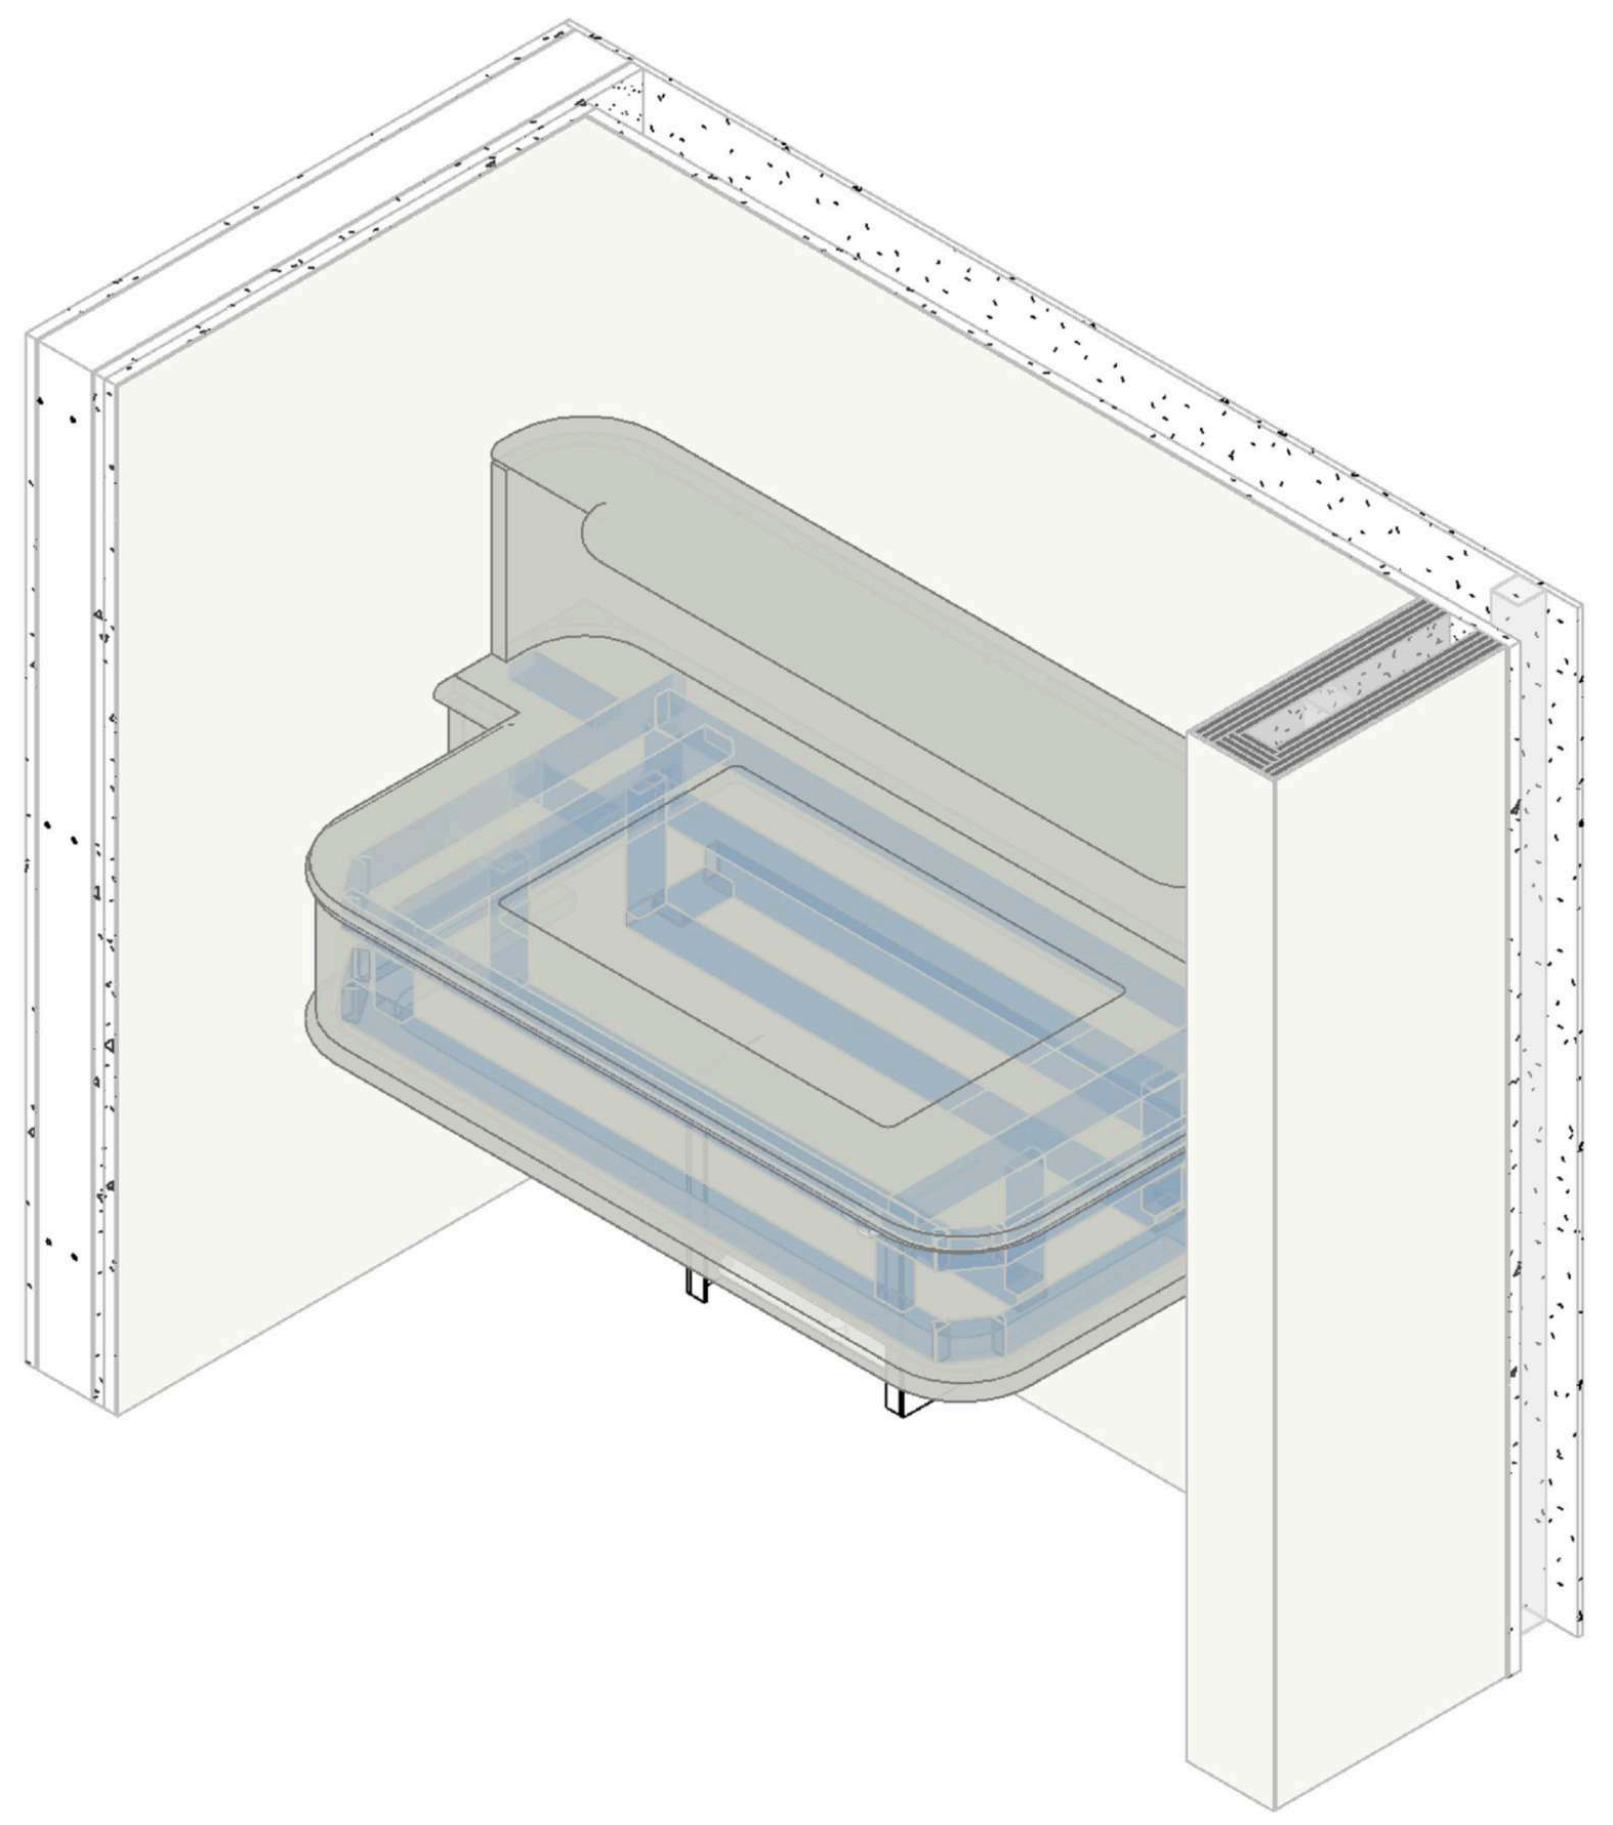

图例A
LEGEND A

编号	图例	说明
1		原始钢架
2		螺栓
3		钢片
4		钢架
5		石材

盖章

注释
Notes

1.本图纸如与现场尺寸有误，请施工人员与项目负责人联系。
2.施工前施工人员应认真查阅此图，如有不明确尺寸，按现场测量为准。
3.本图纸必须经甲乙双方认可并签字方可作为施工依据。

日期
Date 04/24/26

修订
Revision

△1

项目
Project
潮映华岸府3-801

比例
Scale
客卫洗手台石材钢架

图纸编号
Drawing No.
ST-03

项目编号
Project No.

©2025

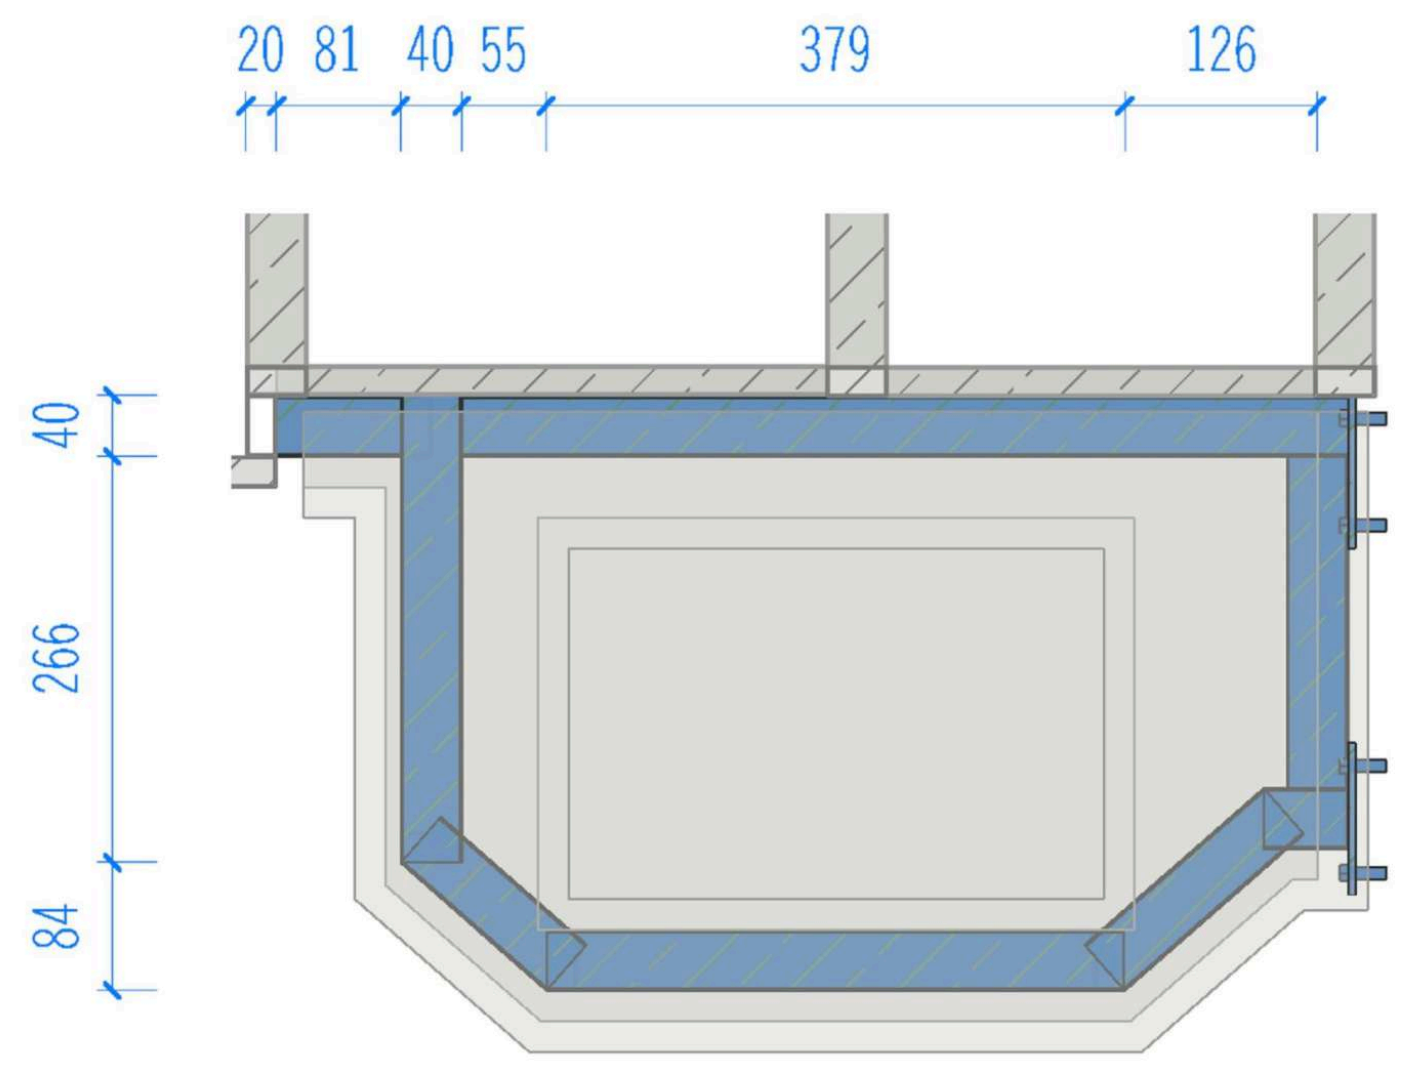
20
81
40
55
379
126
40
266
84

平面视图

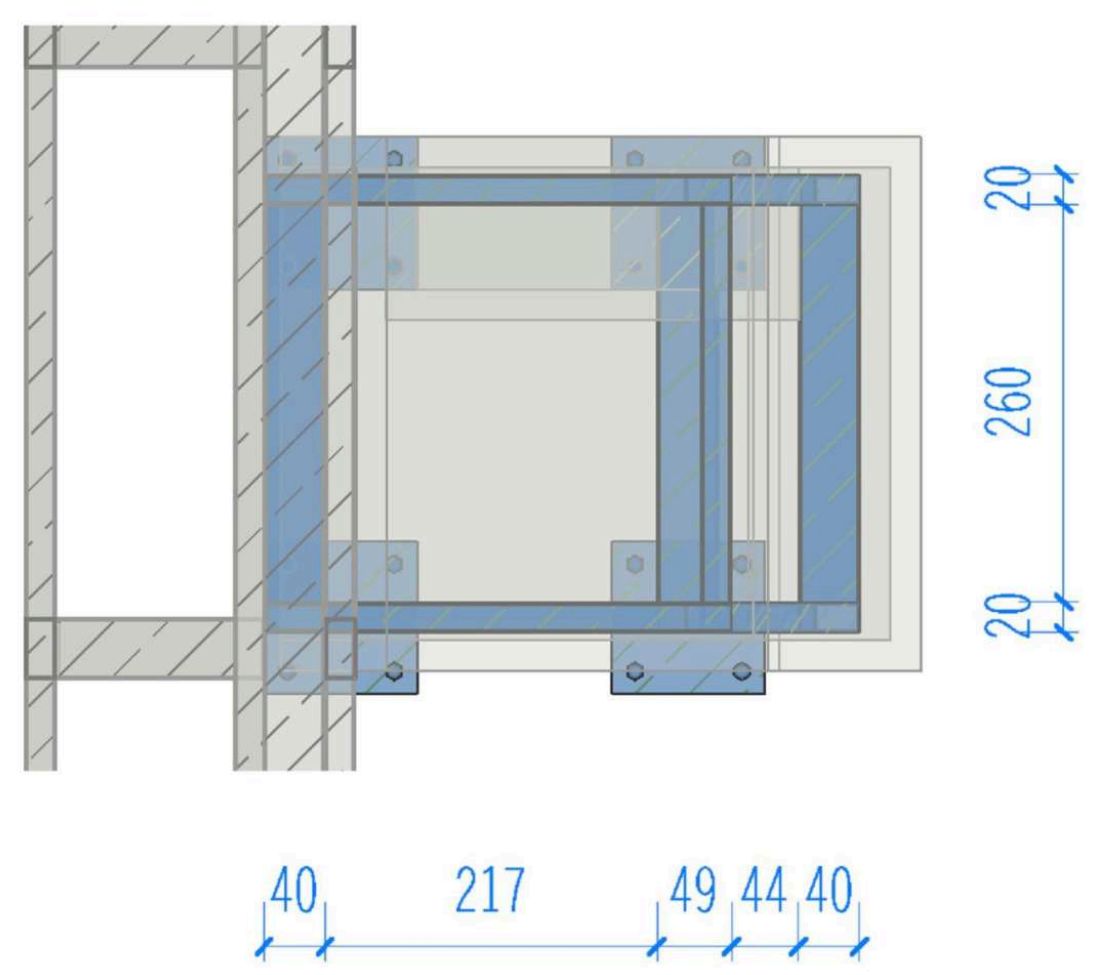
20
260
20
40
217
49
44
40

剖面视图

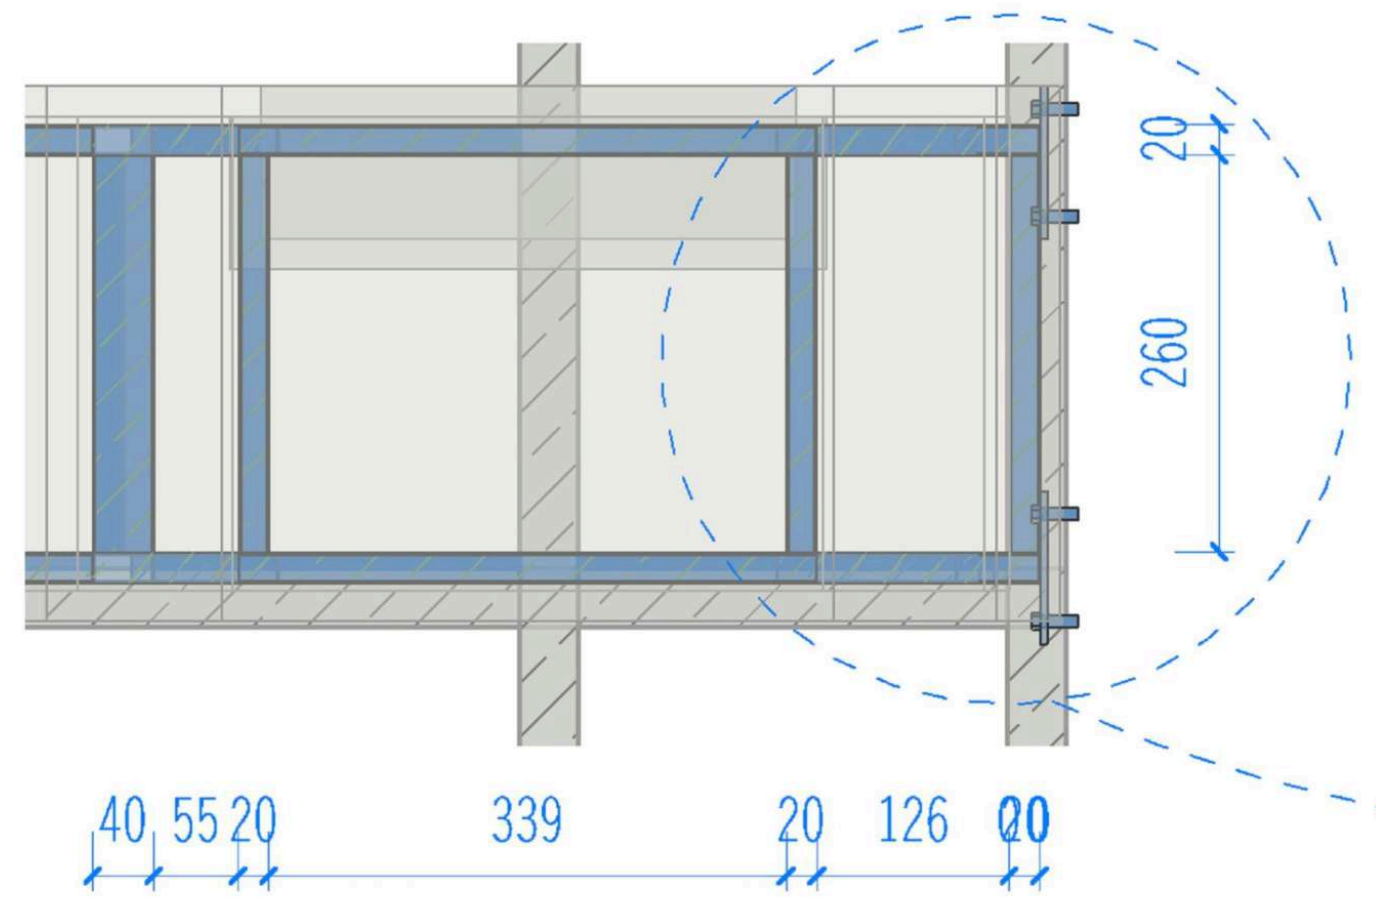
20
260
40
55
20
339
20
126
20

立面视图

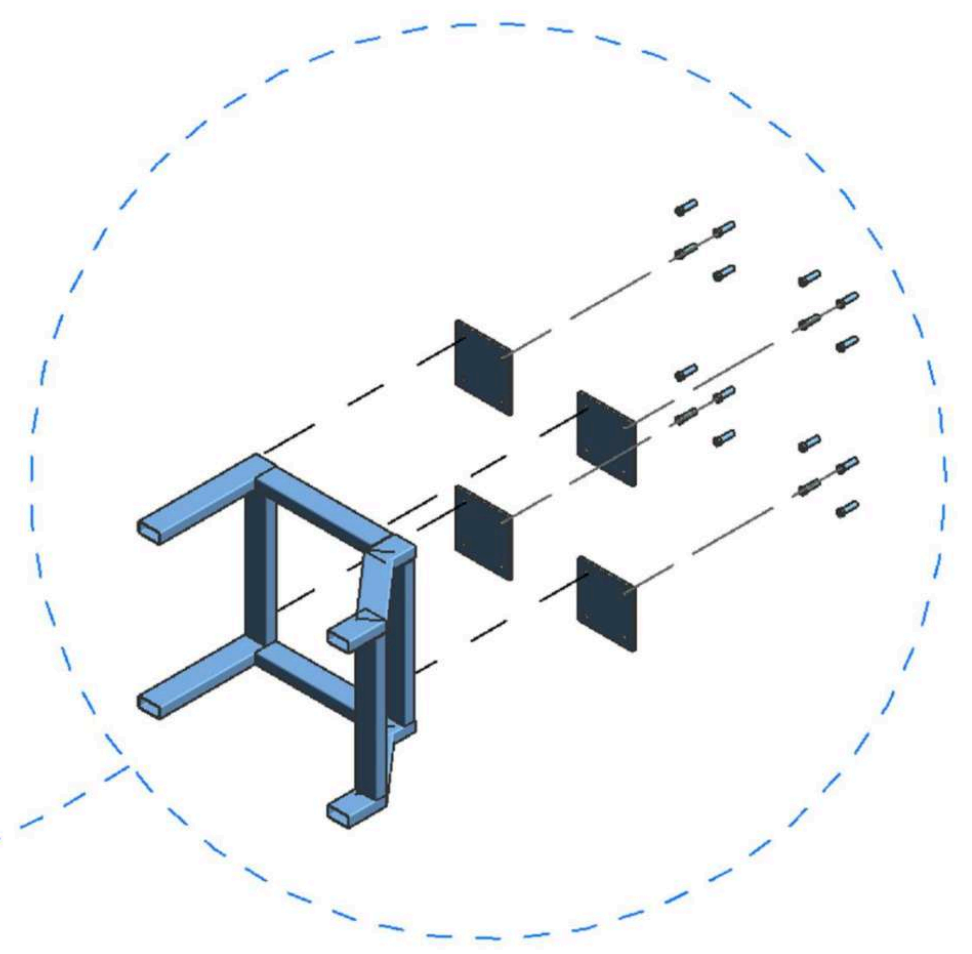

节点图

工厂预制钢架

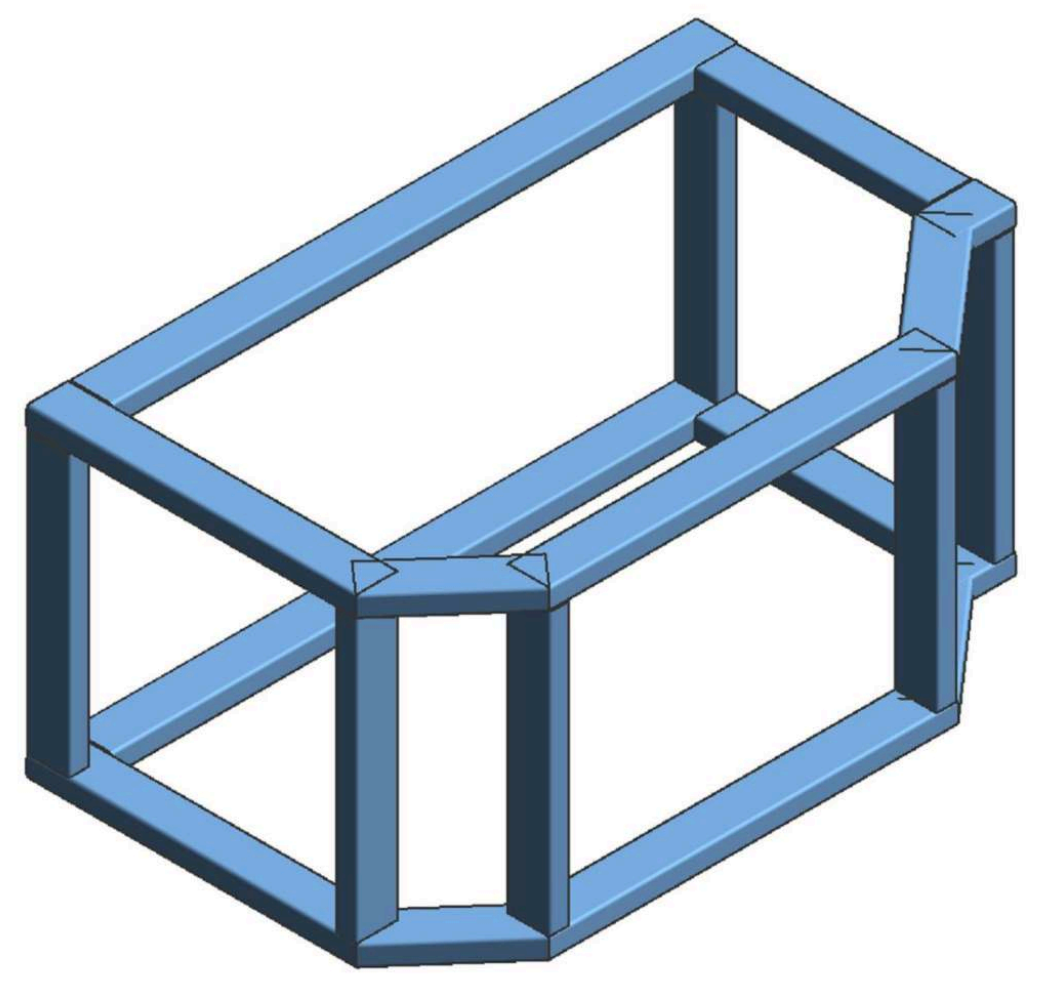

①

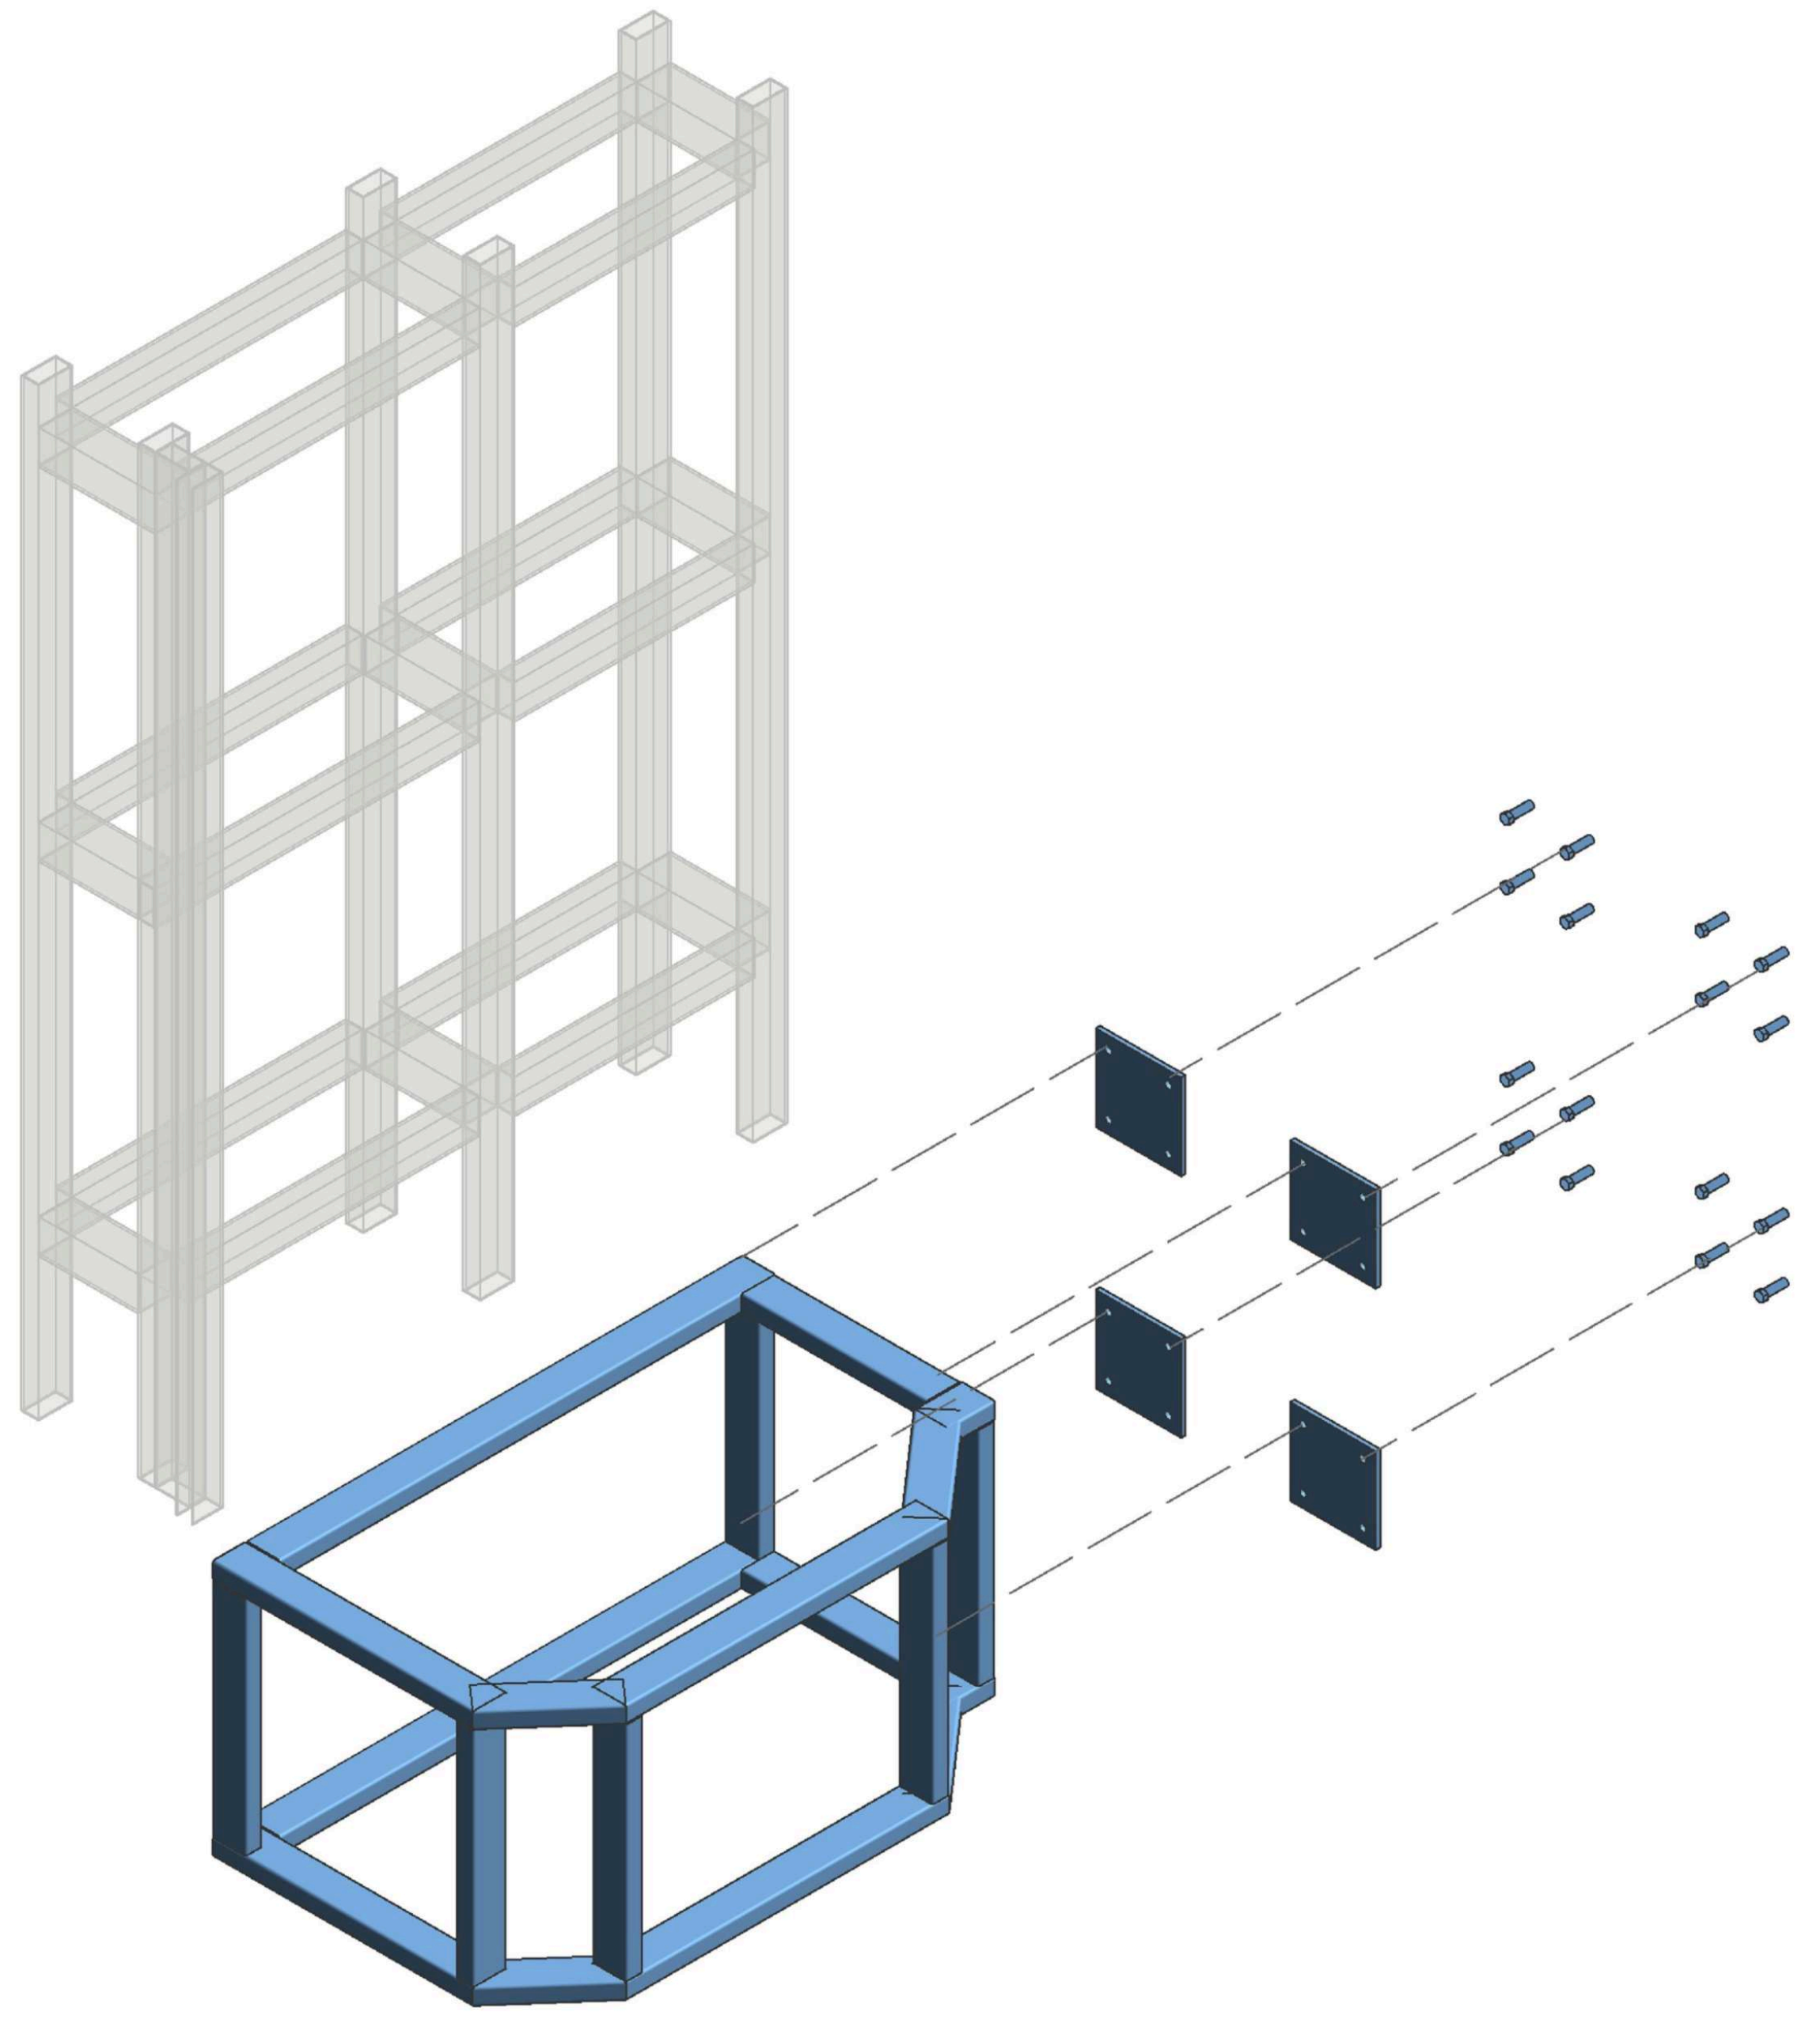

②

③

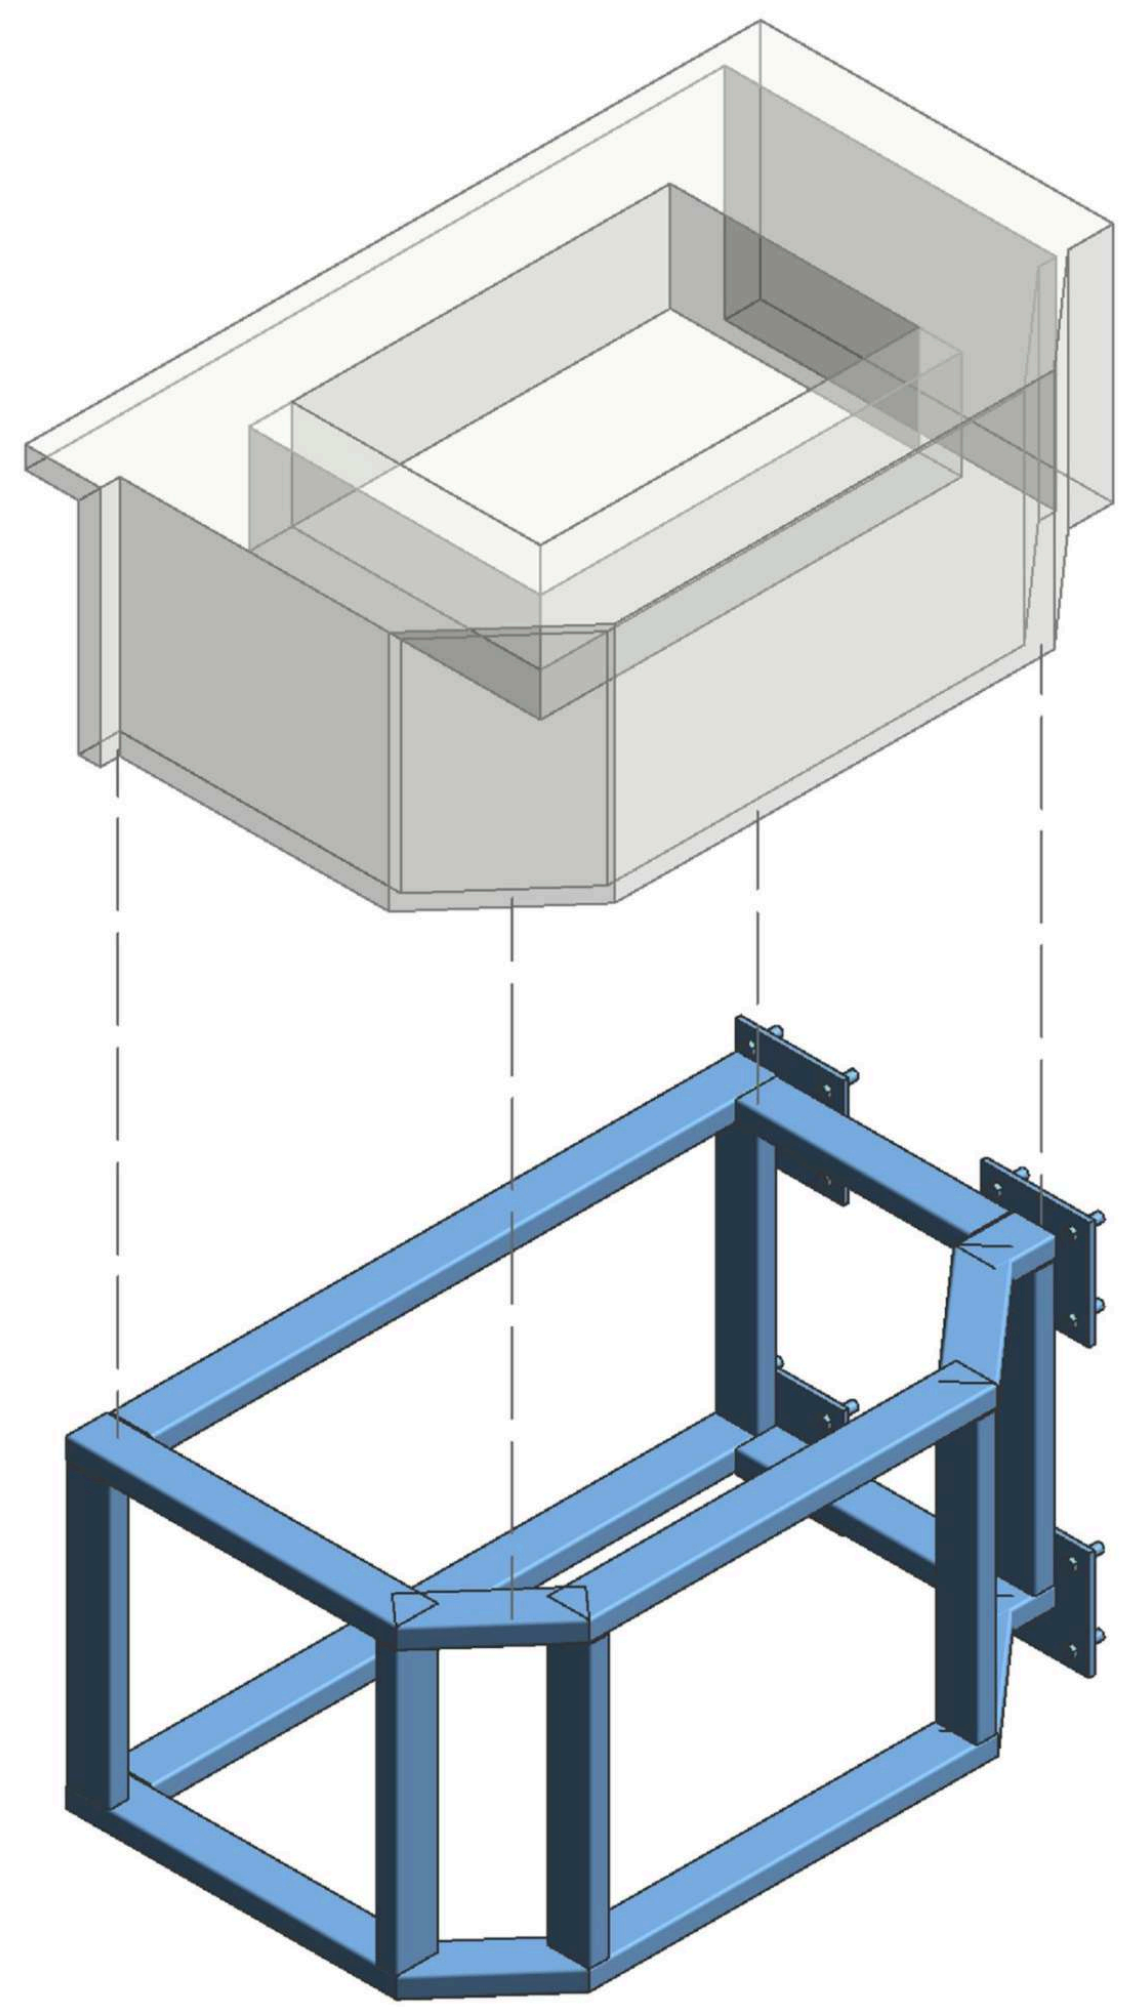

④

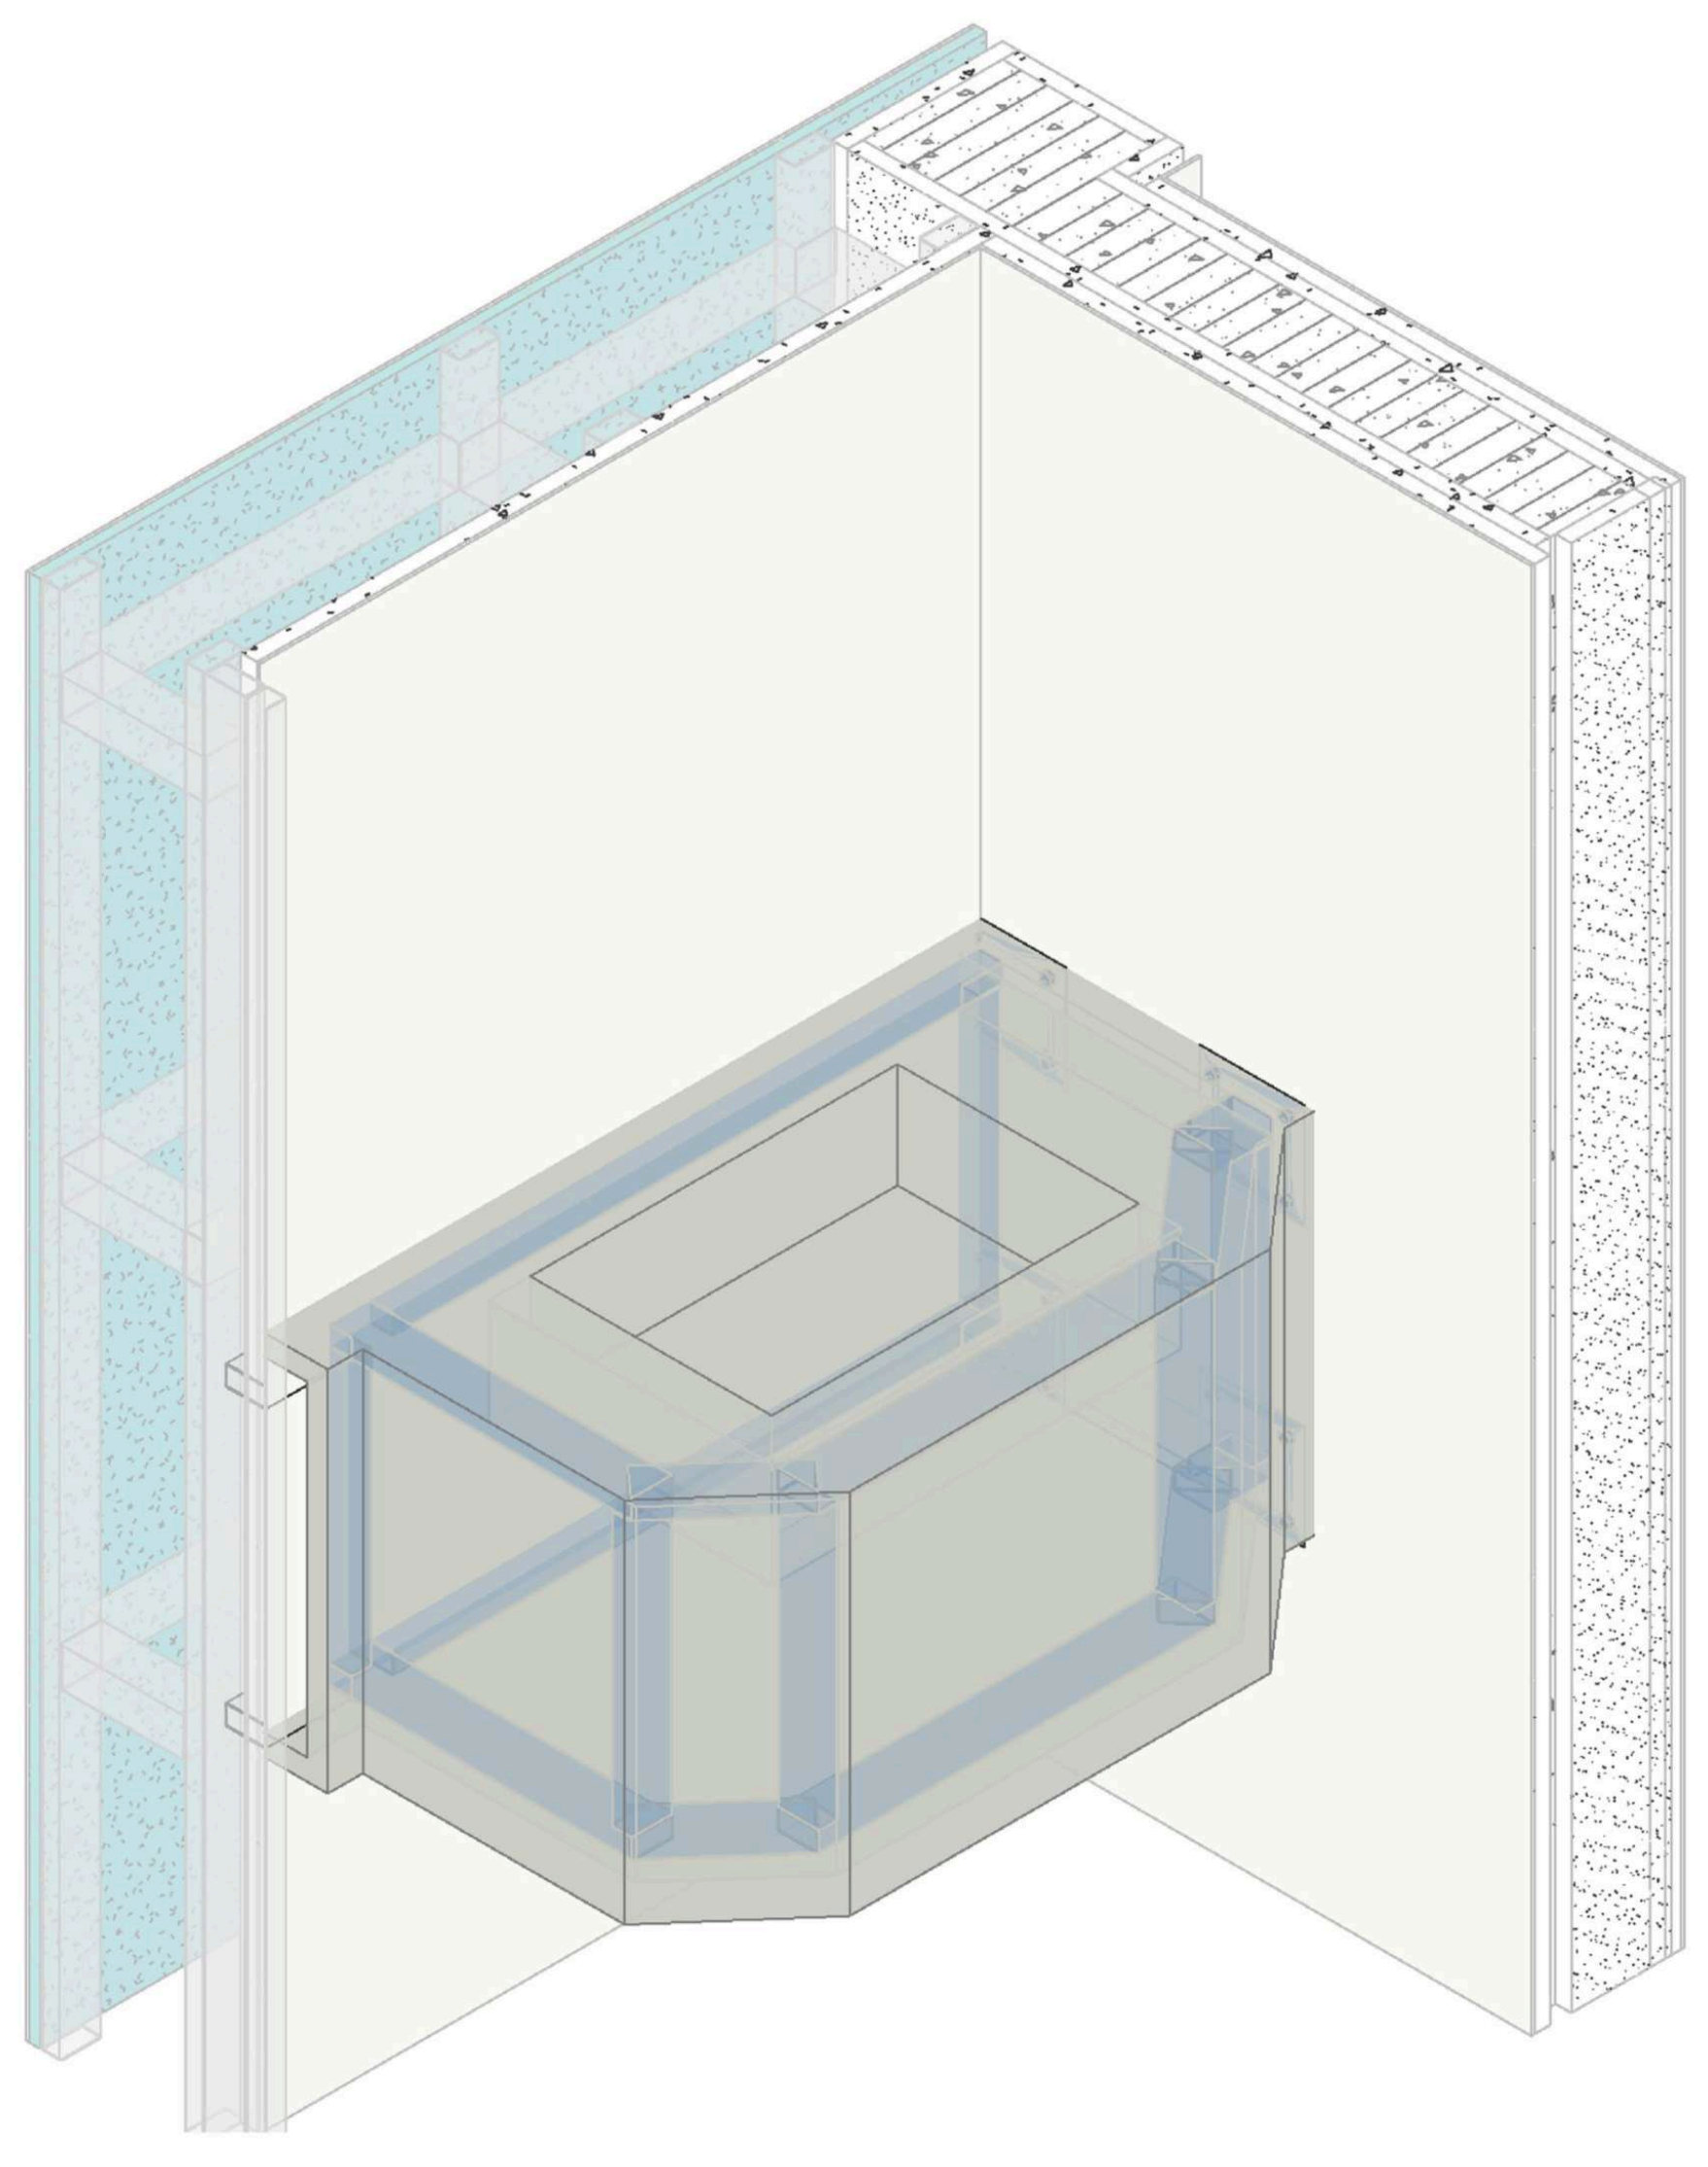

图例A
LEGEND A

编号	图例	说明
1		原始钢架
2		螺栓
3		钢片
4		钢架
5		石材

盖章

注释
Notes

1.本图纸如与现场尺寸有误，请施工人员与项目负责人联系。
2.施工前施工人员应认真查阅此图，如有不明确尺寸，按现场测量为准。
3.本图纸必须经甲乙双方认可并签字方可作为施工依据。

日期
Date 04/24/26

修订
Revision

△1

项目
Project

潮映华岸府3-801

比例
Scale

公卫洗手台石材钢架

图纸编号
Drawing No.

ST-04

项目编号
Project No.

©2025

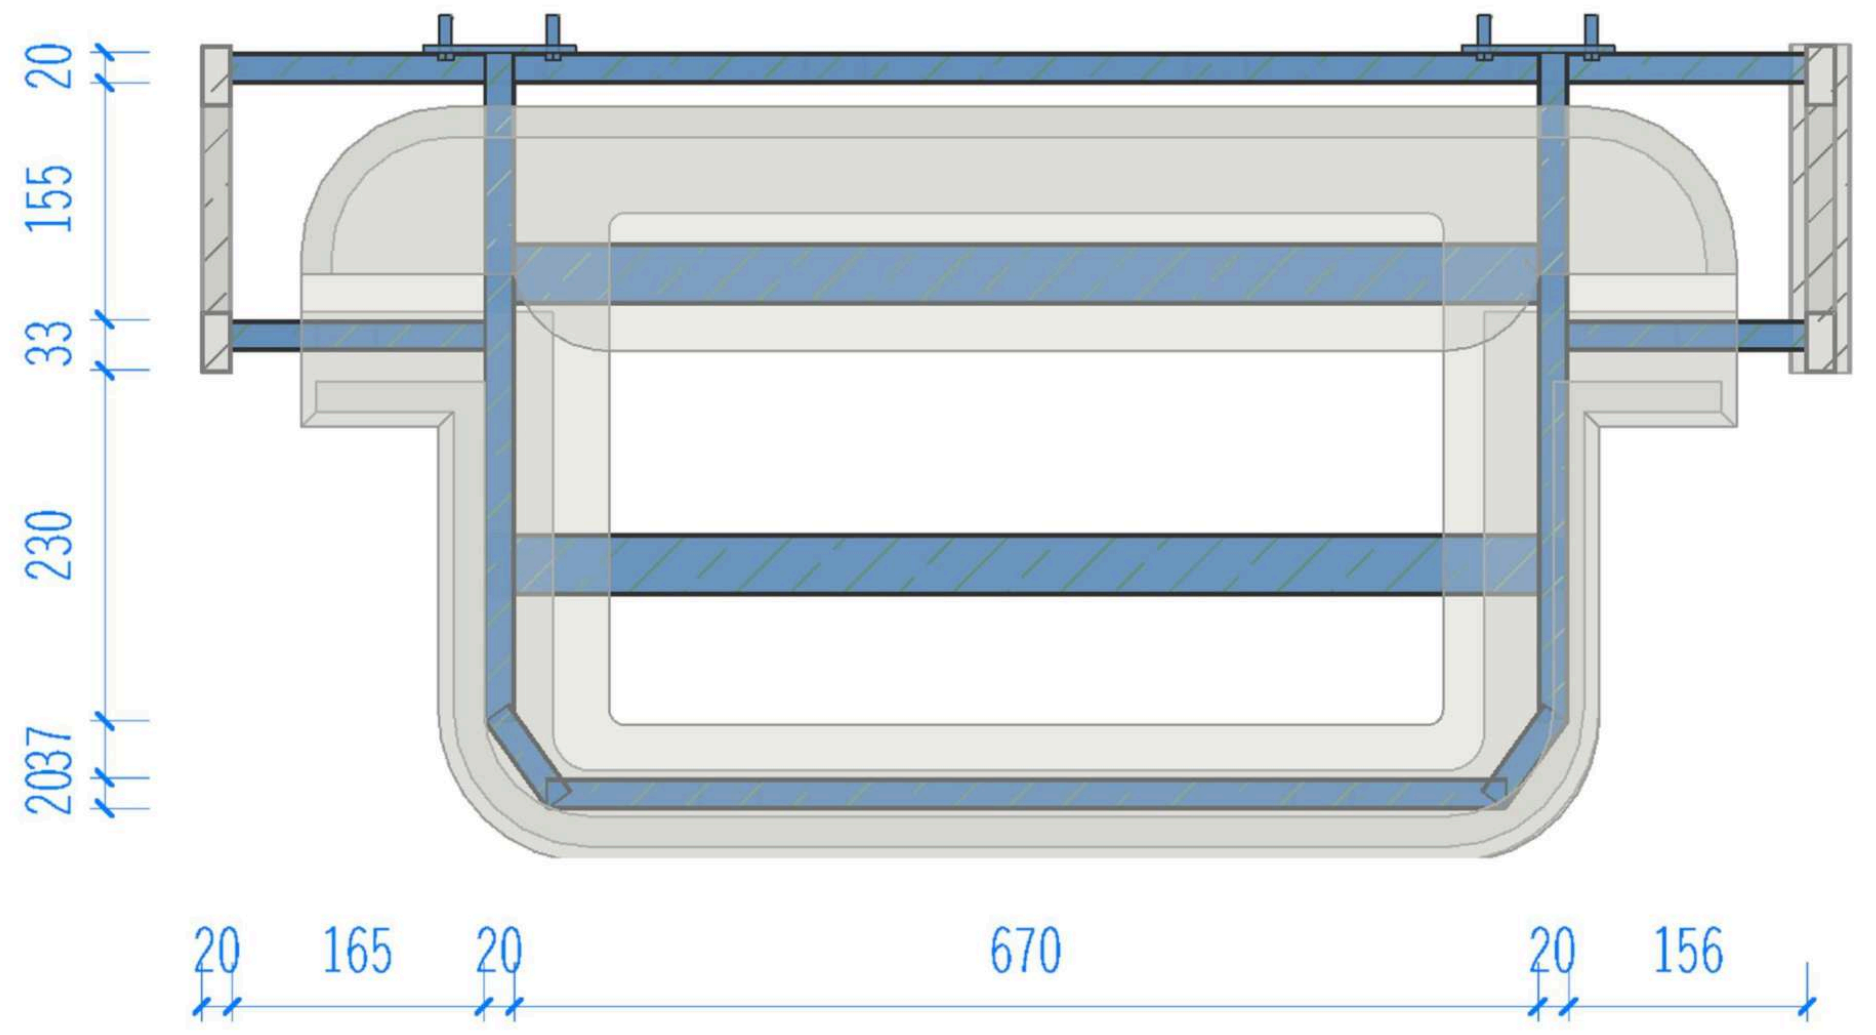
20
155
33
230
2037
20
165
20
670
20
156

平面视图

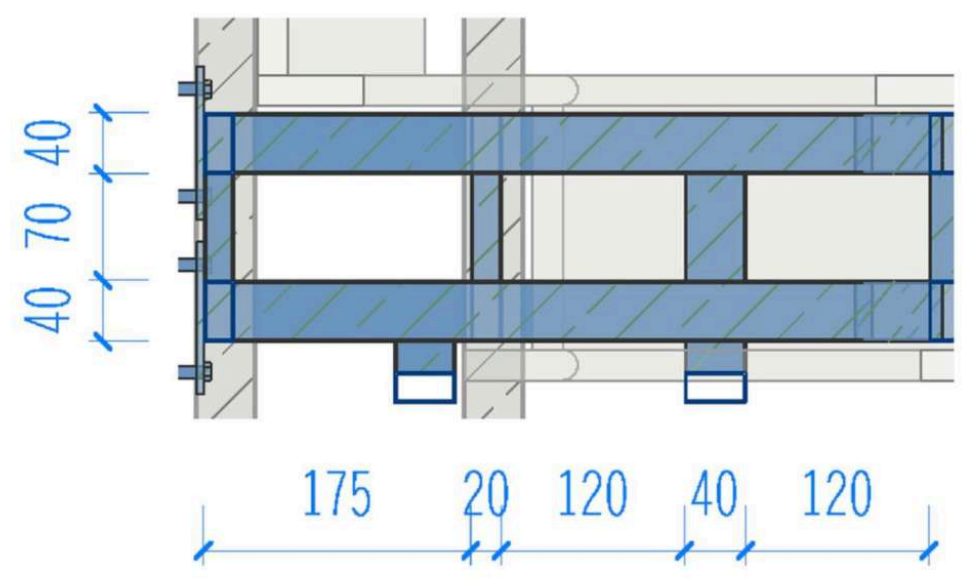
40
70
40
175
20
120
40
120

剖面视图

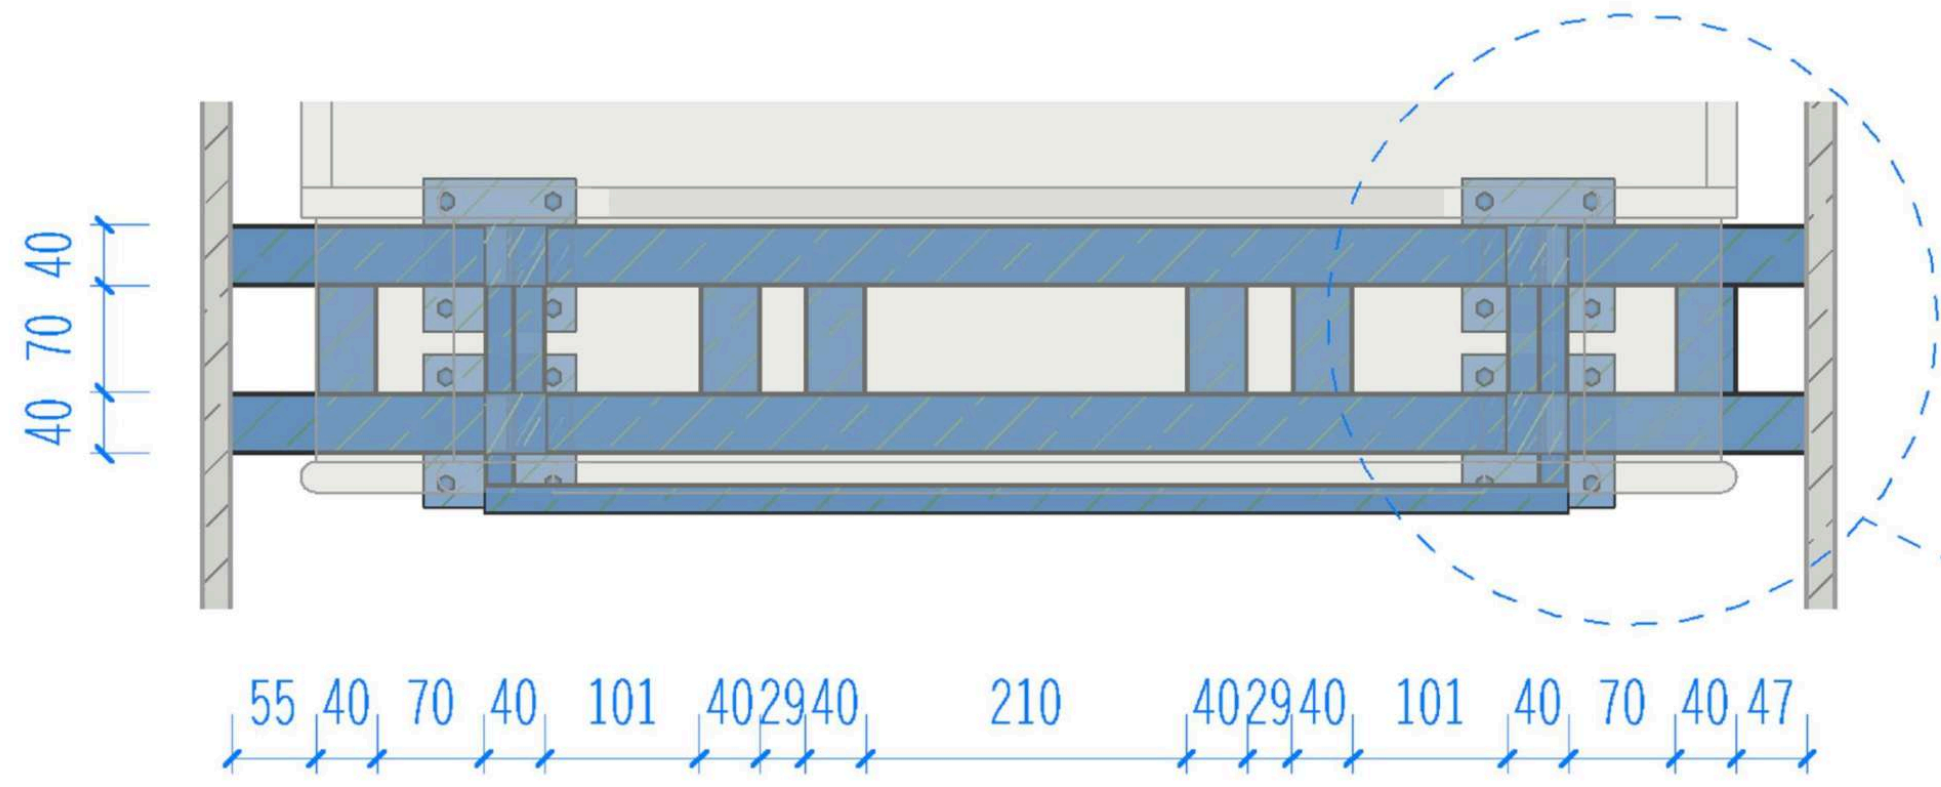
40
70
40
55
40
70
40
101
40
29
40
210
40
29
40
101
40
70
40
47

立面视图

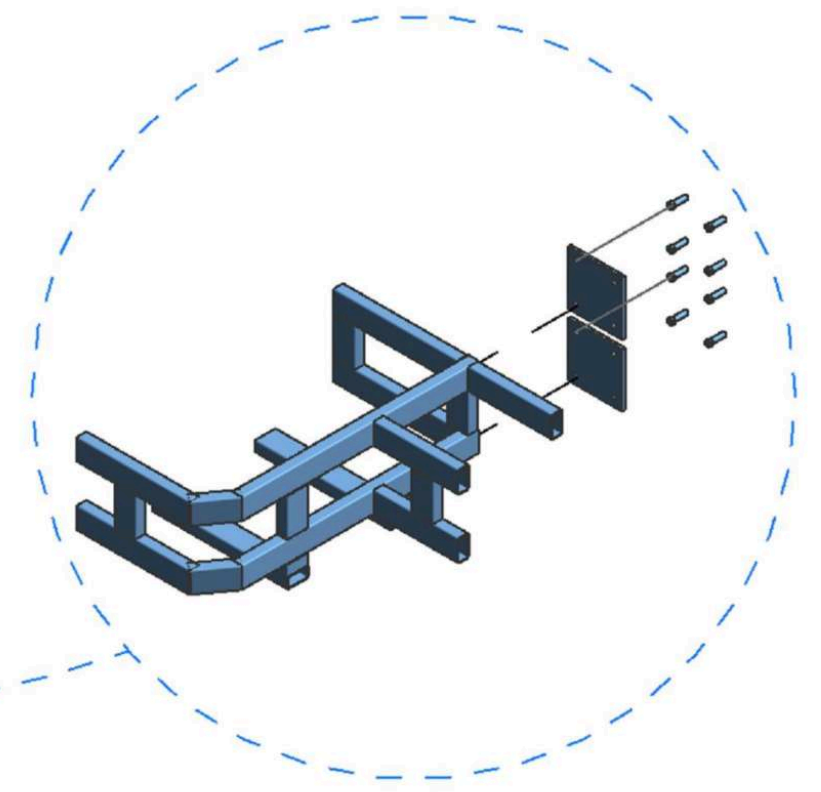

节点图

工厂预制钢架

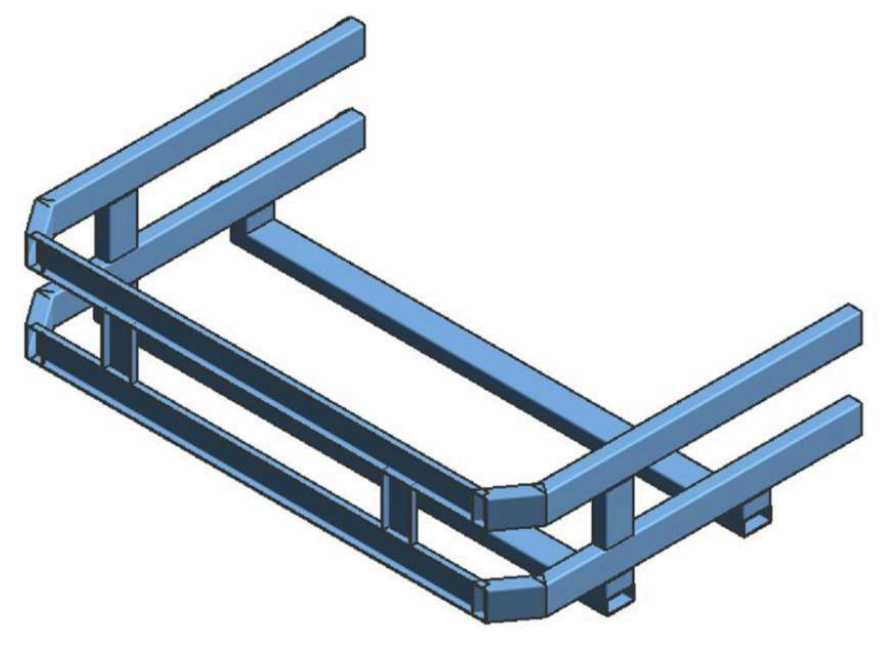

①

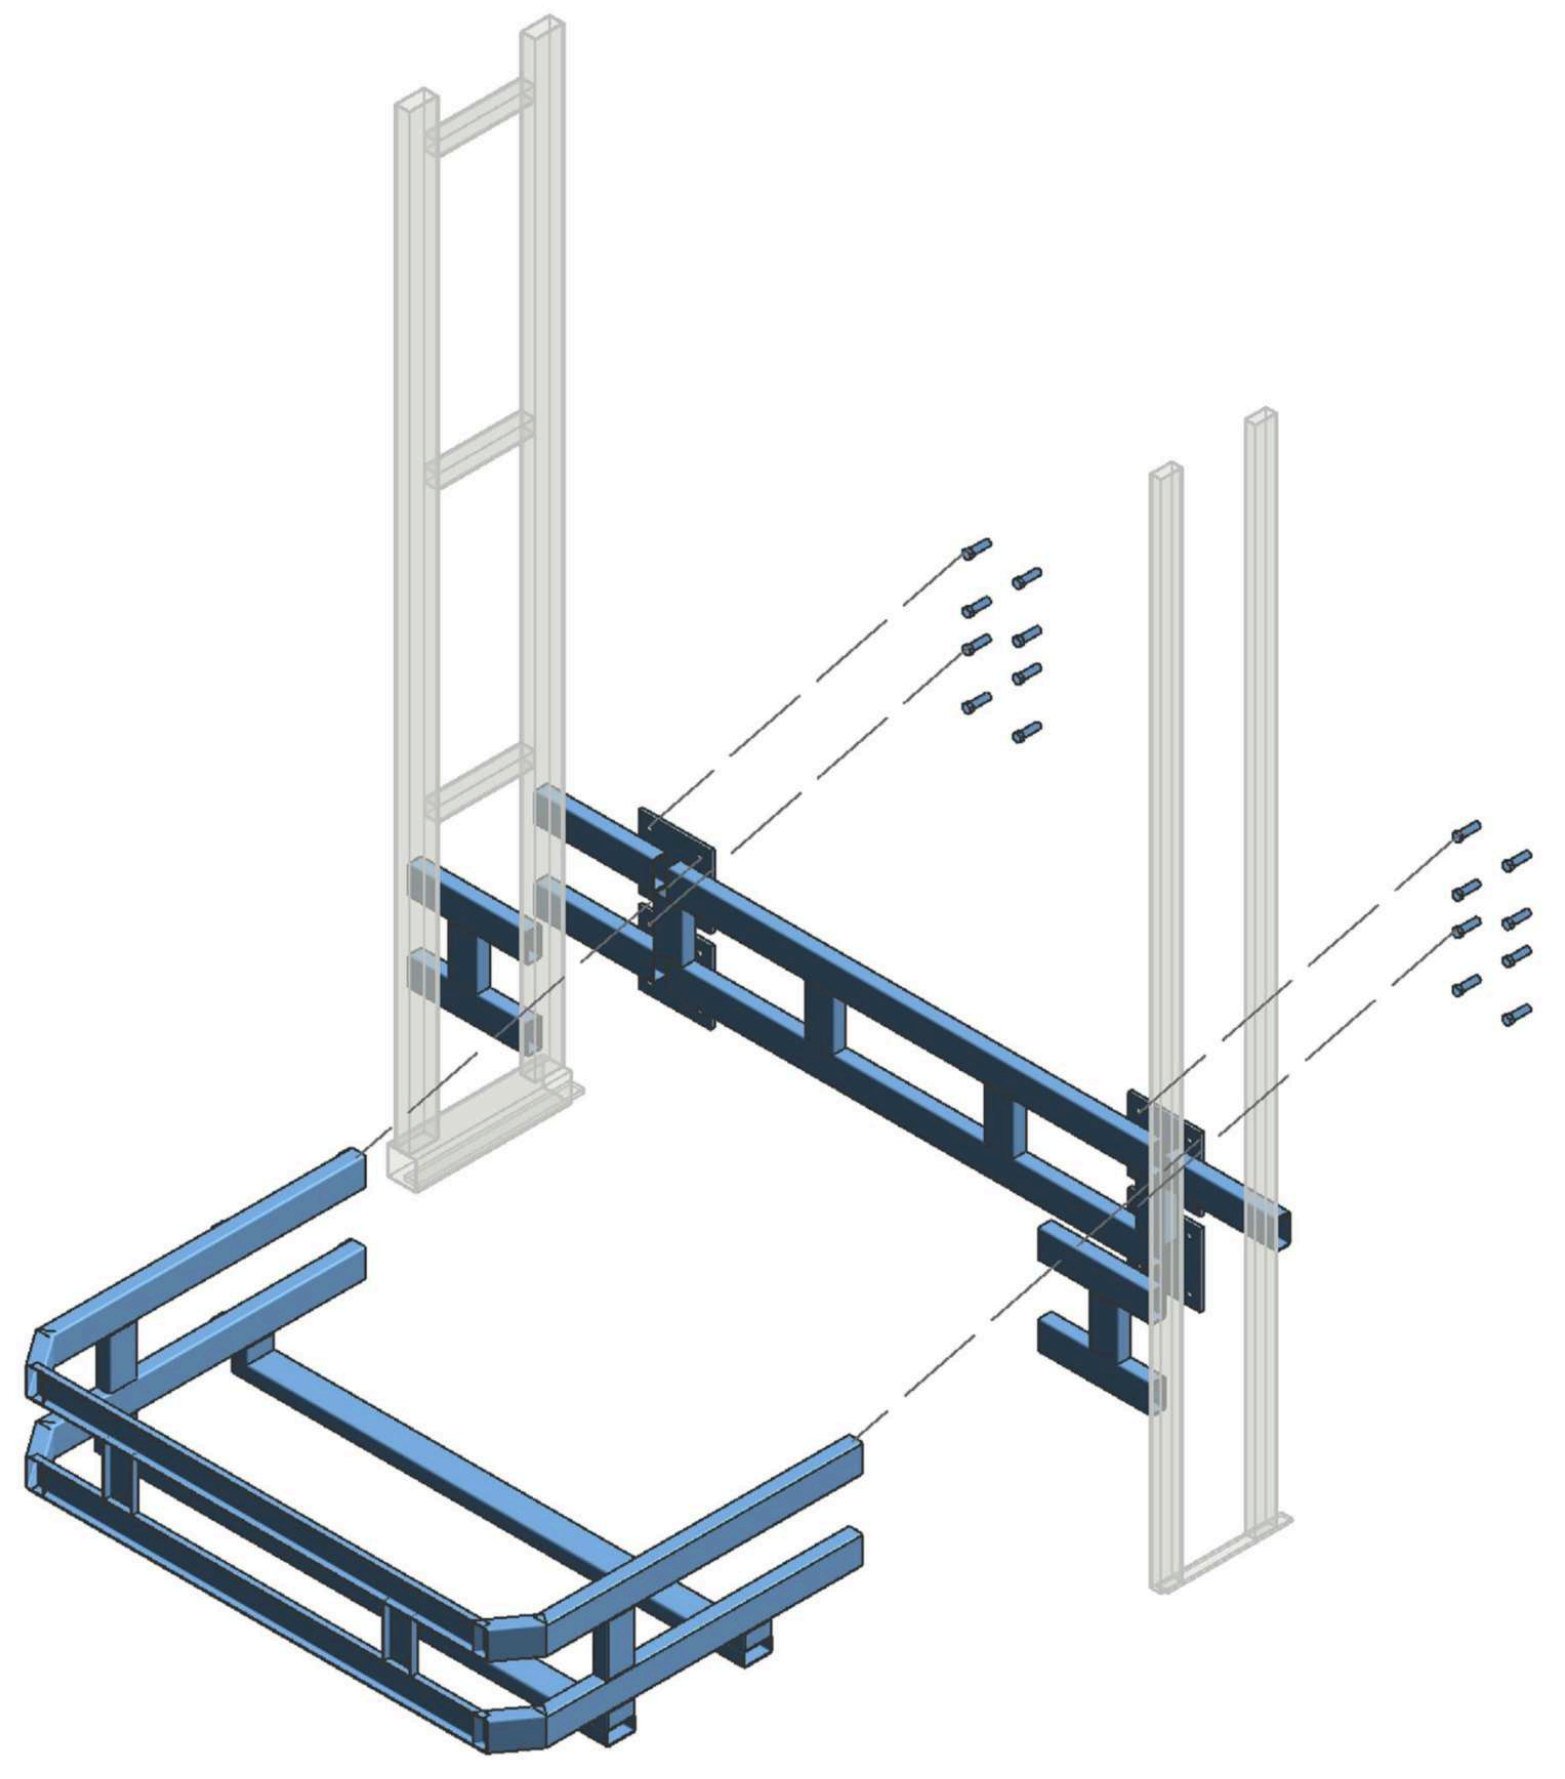

②

③

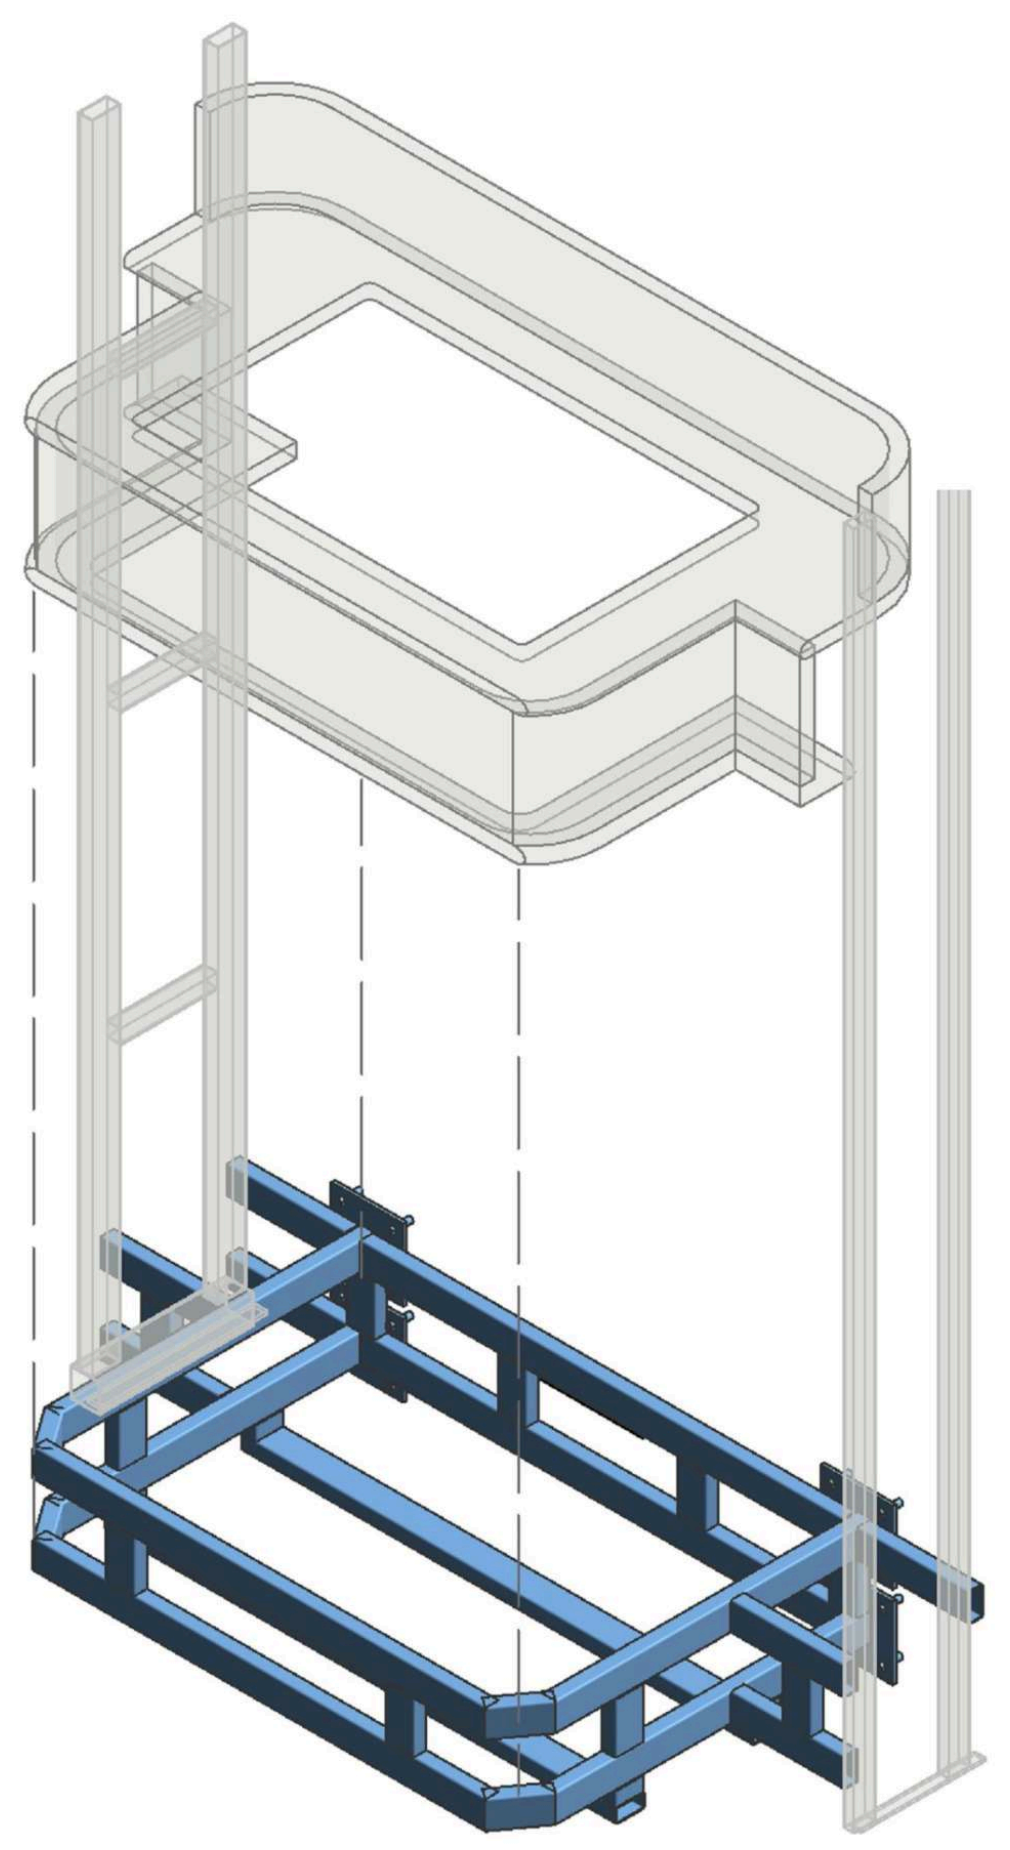

④

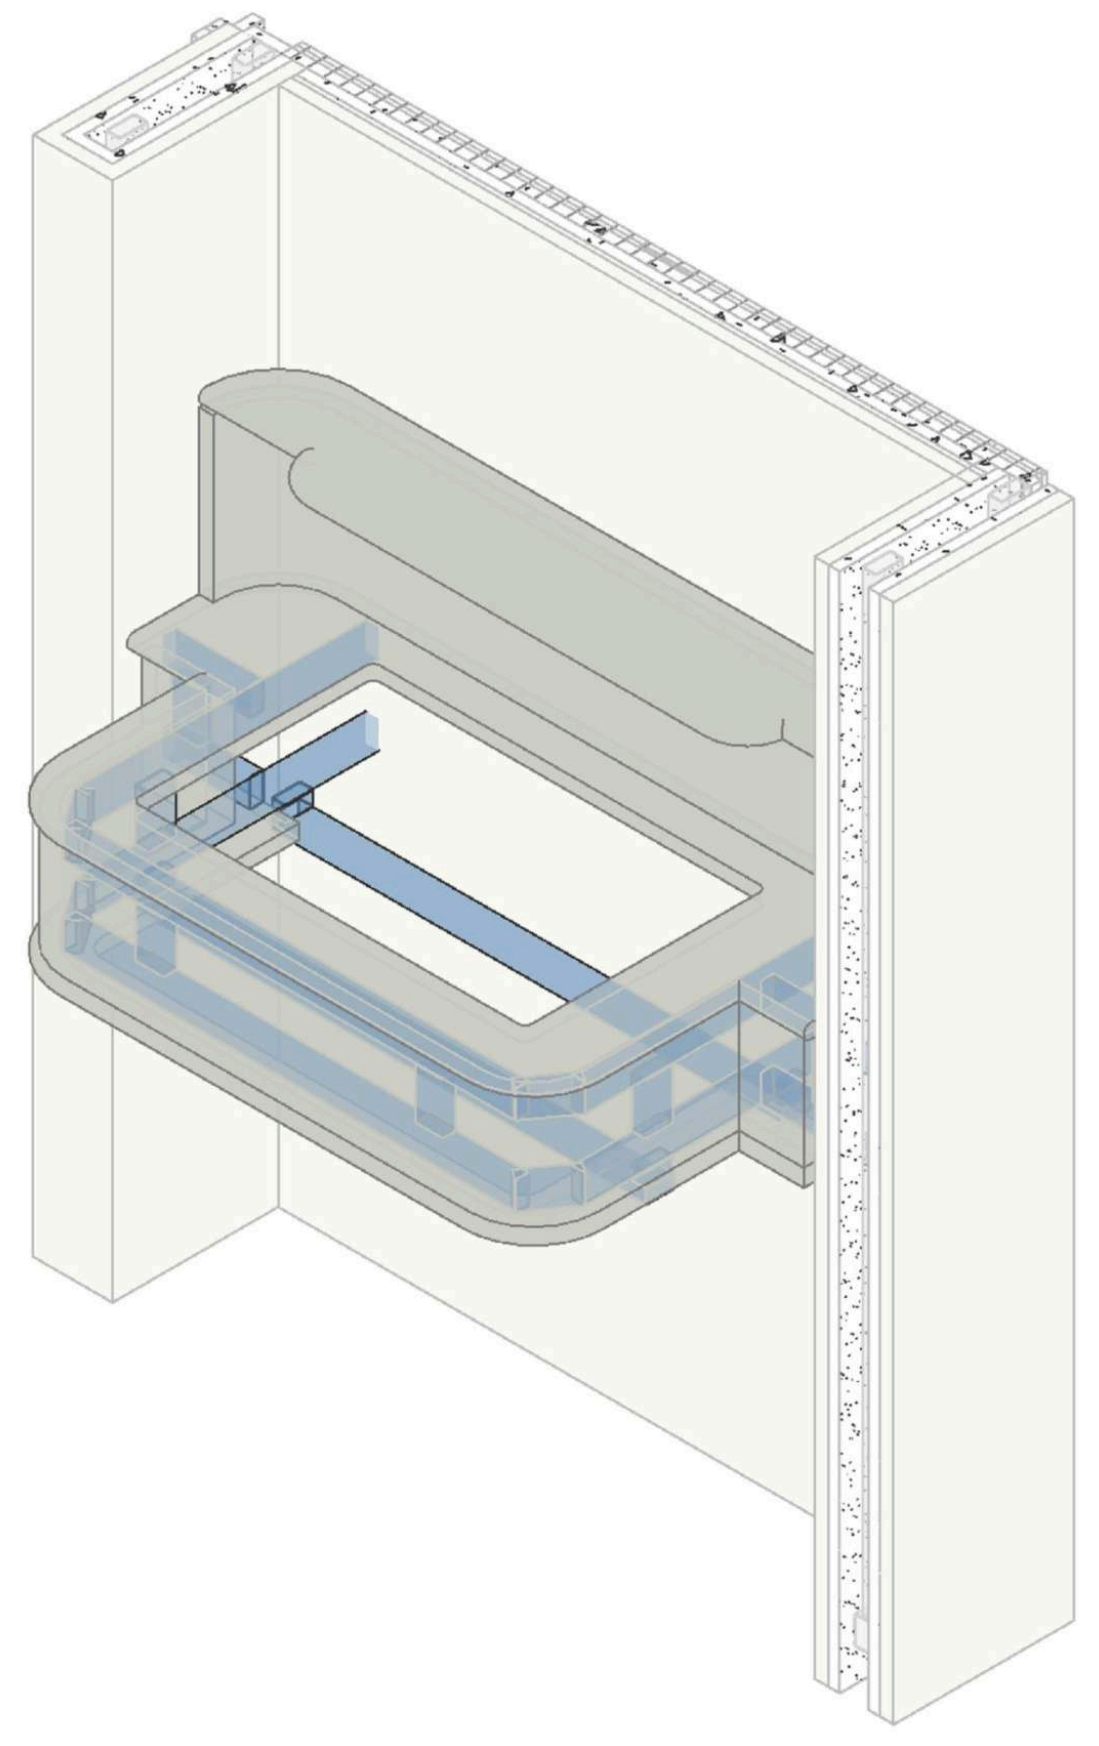

图例A
LEGEND A

编号	图例	说明
1		原始钢架
2		螺栓
3		钢片
4		钢架
5		石材

盖章

注释
Notes

1.本图纸如与现场尺寸有误，请施工人员与项目负责人联系。
2.施工前施工人员应认真查阅此图，如有不明确尺寸，按现场测量为准。
3.本图纸必须经甲乙双方认可并签字方可作为施工依据。

日期
Date 04/24/26

修订
Revision

△1

项目
Project
潮映华岸府3-801

比例
Scale

次卫洗手台石材钢架

图纸编号
Drawing No.
ST-05

项目编号
Project No.

©2025

1

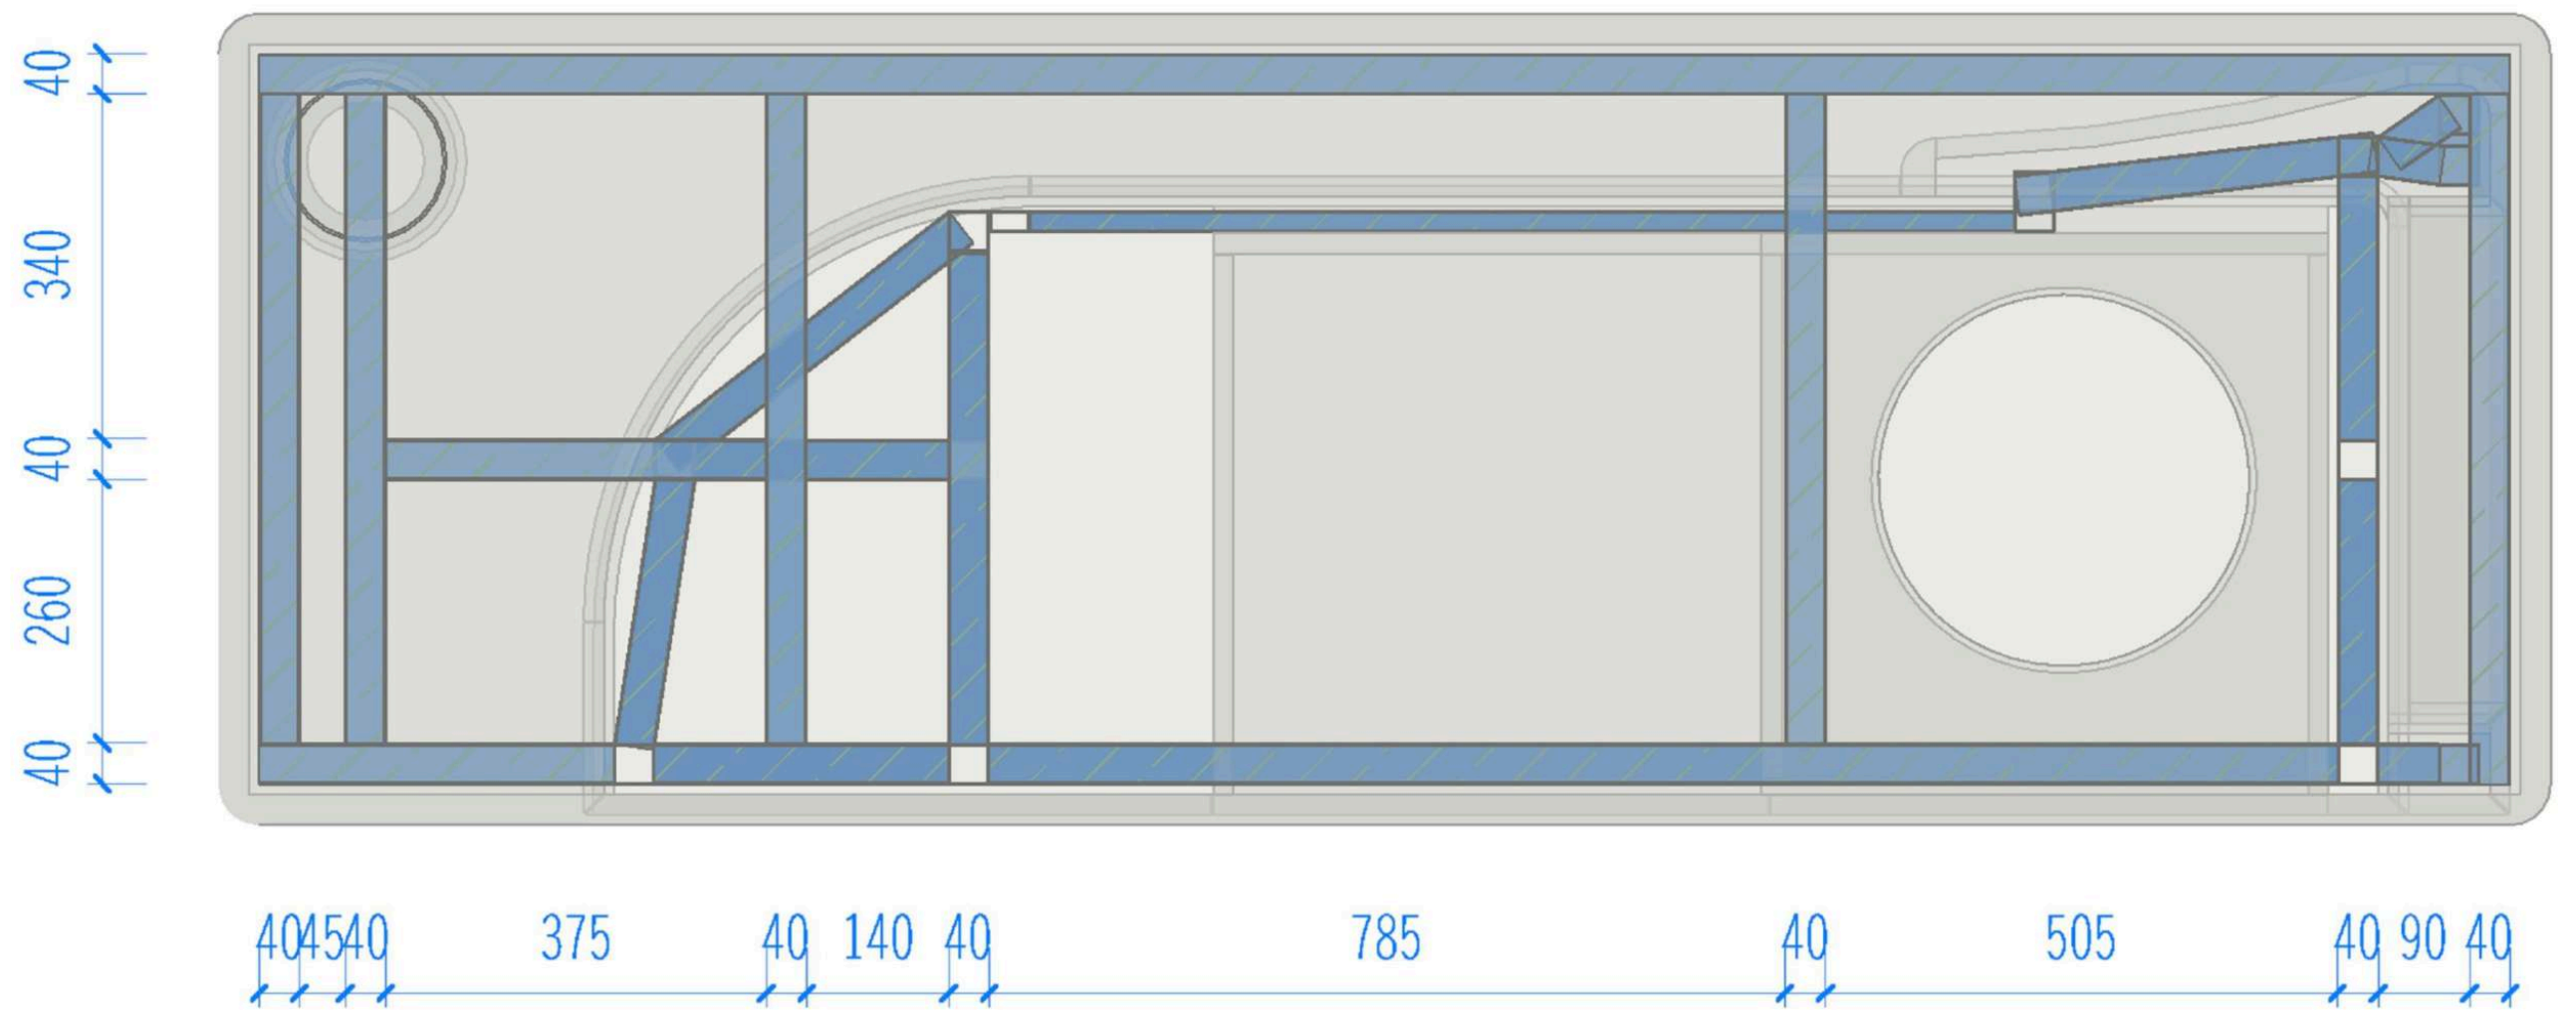
40
340
40
260
40
40 45 40
375
40
140
40
785
40
505
40
90
40

平面视图

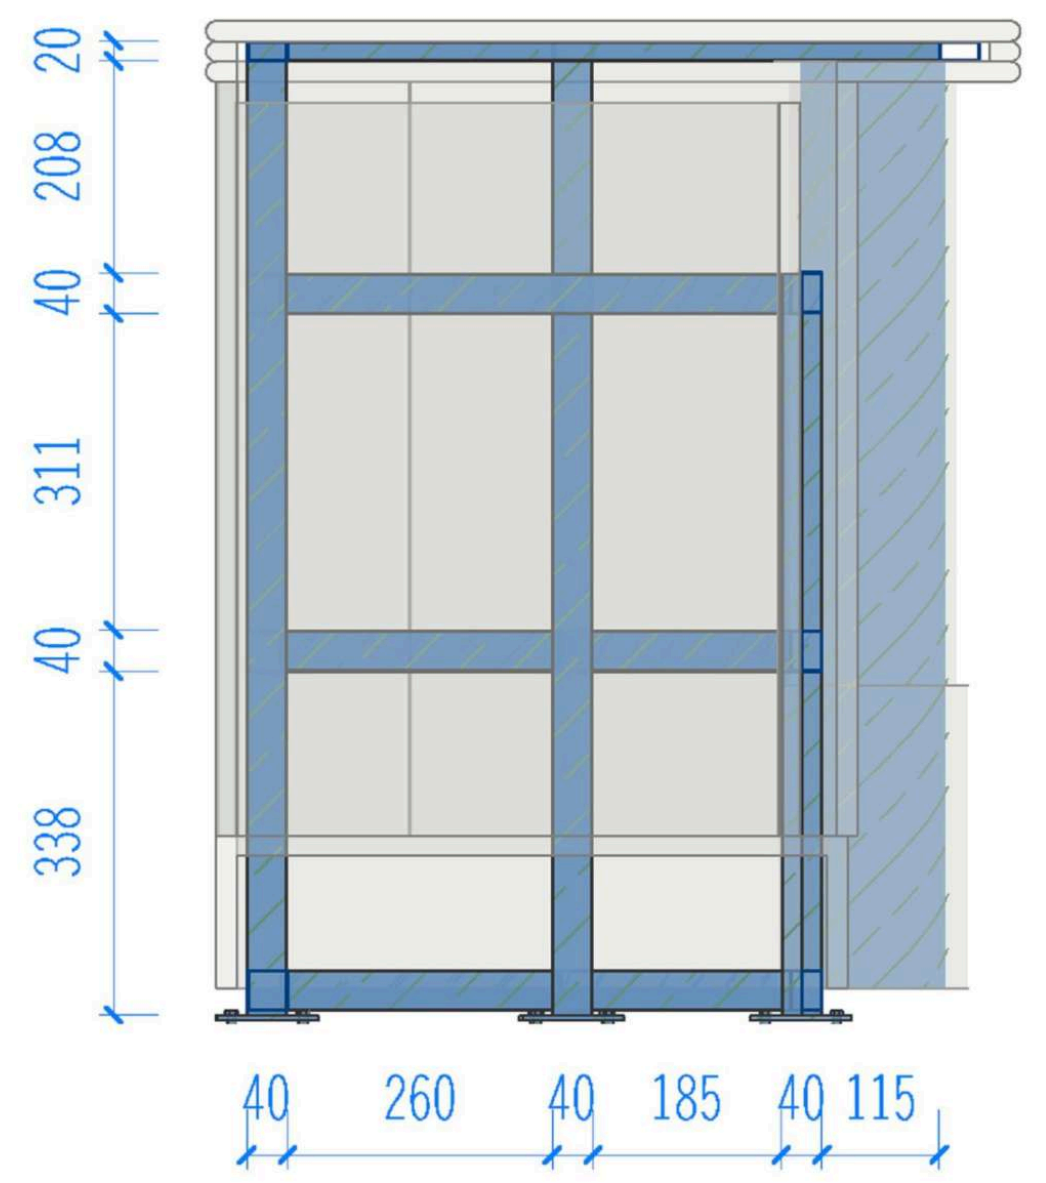
20
208
40
311
40
338
40
260
40
185
40
115

剖面视图

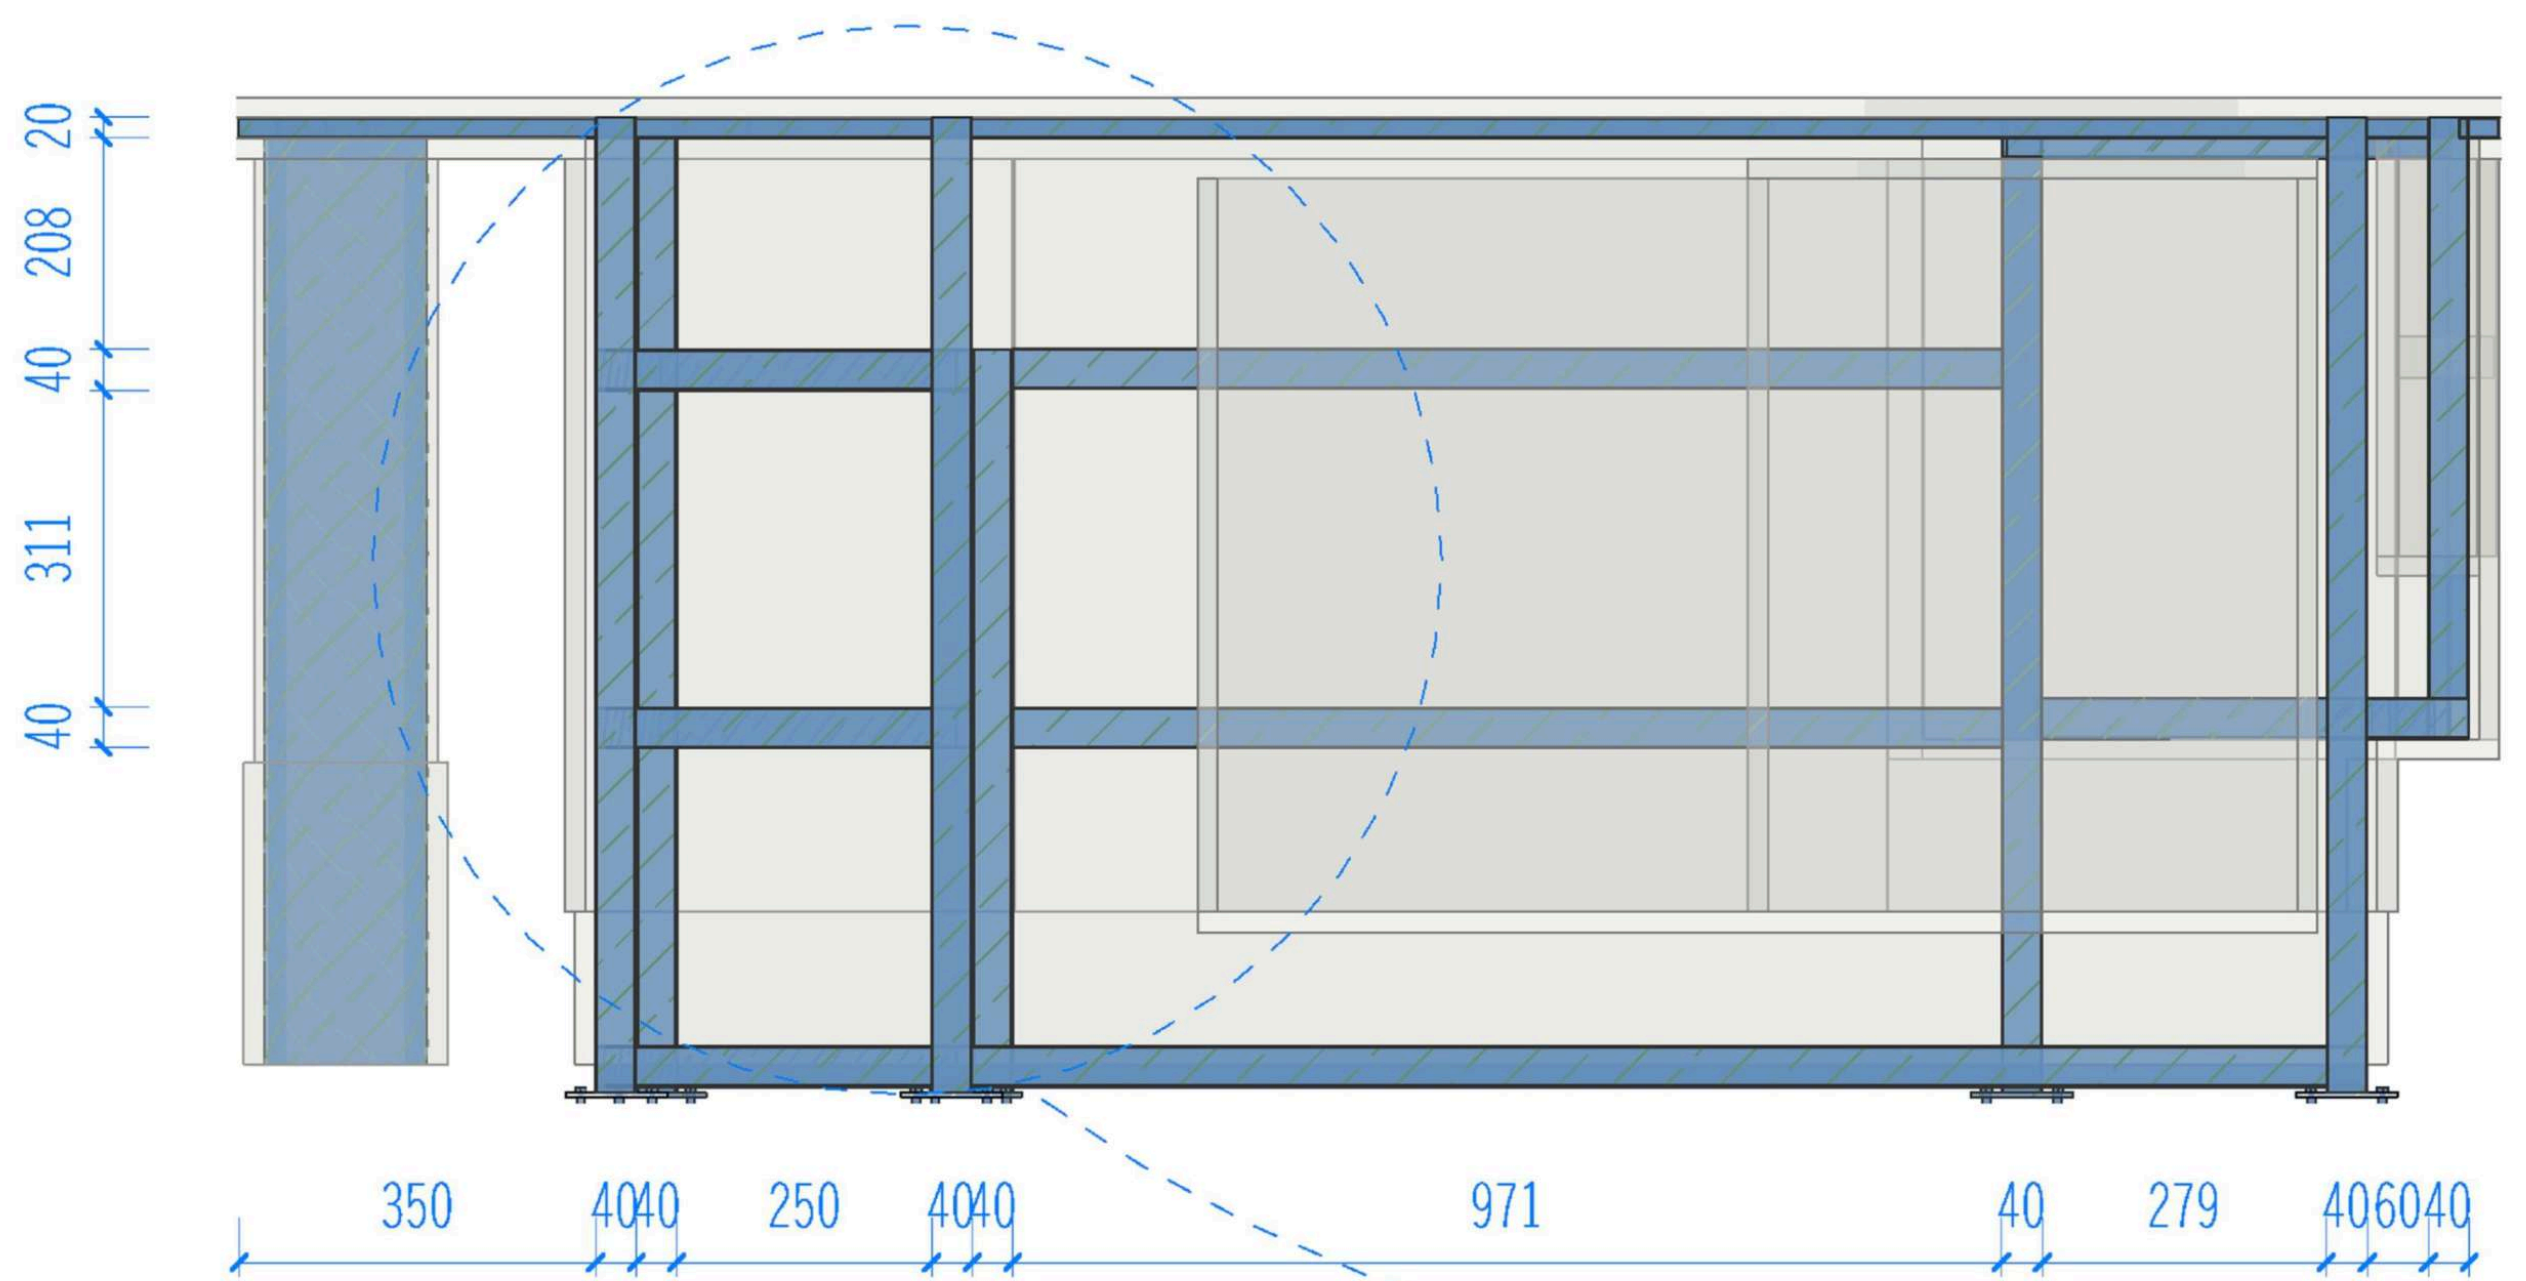
20
208
40
311
40
350
40
40
250
40
40
971
40
279
40
60
40

立面视图

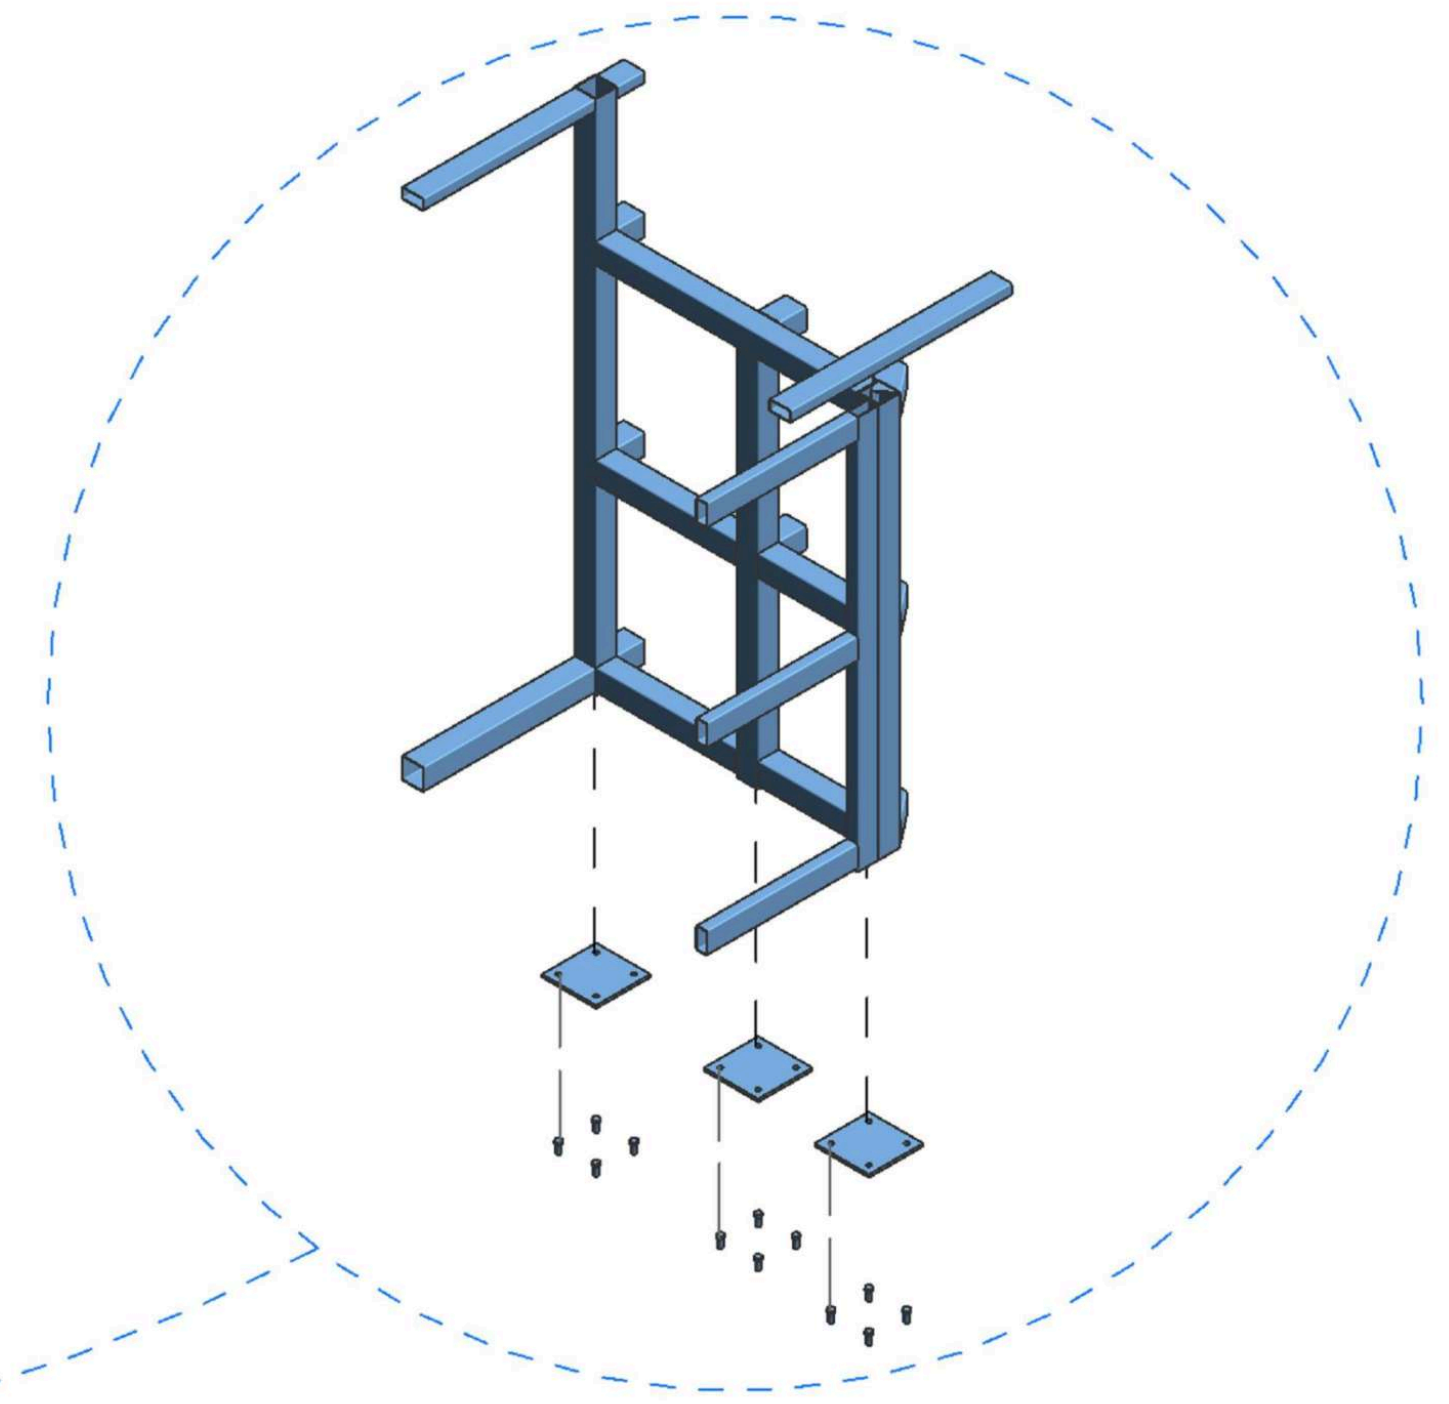

节点图

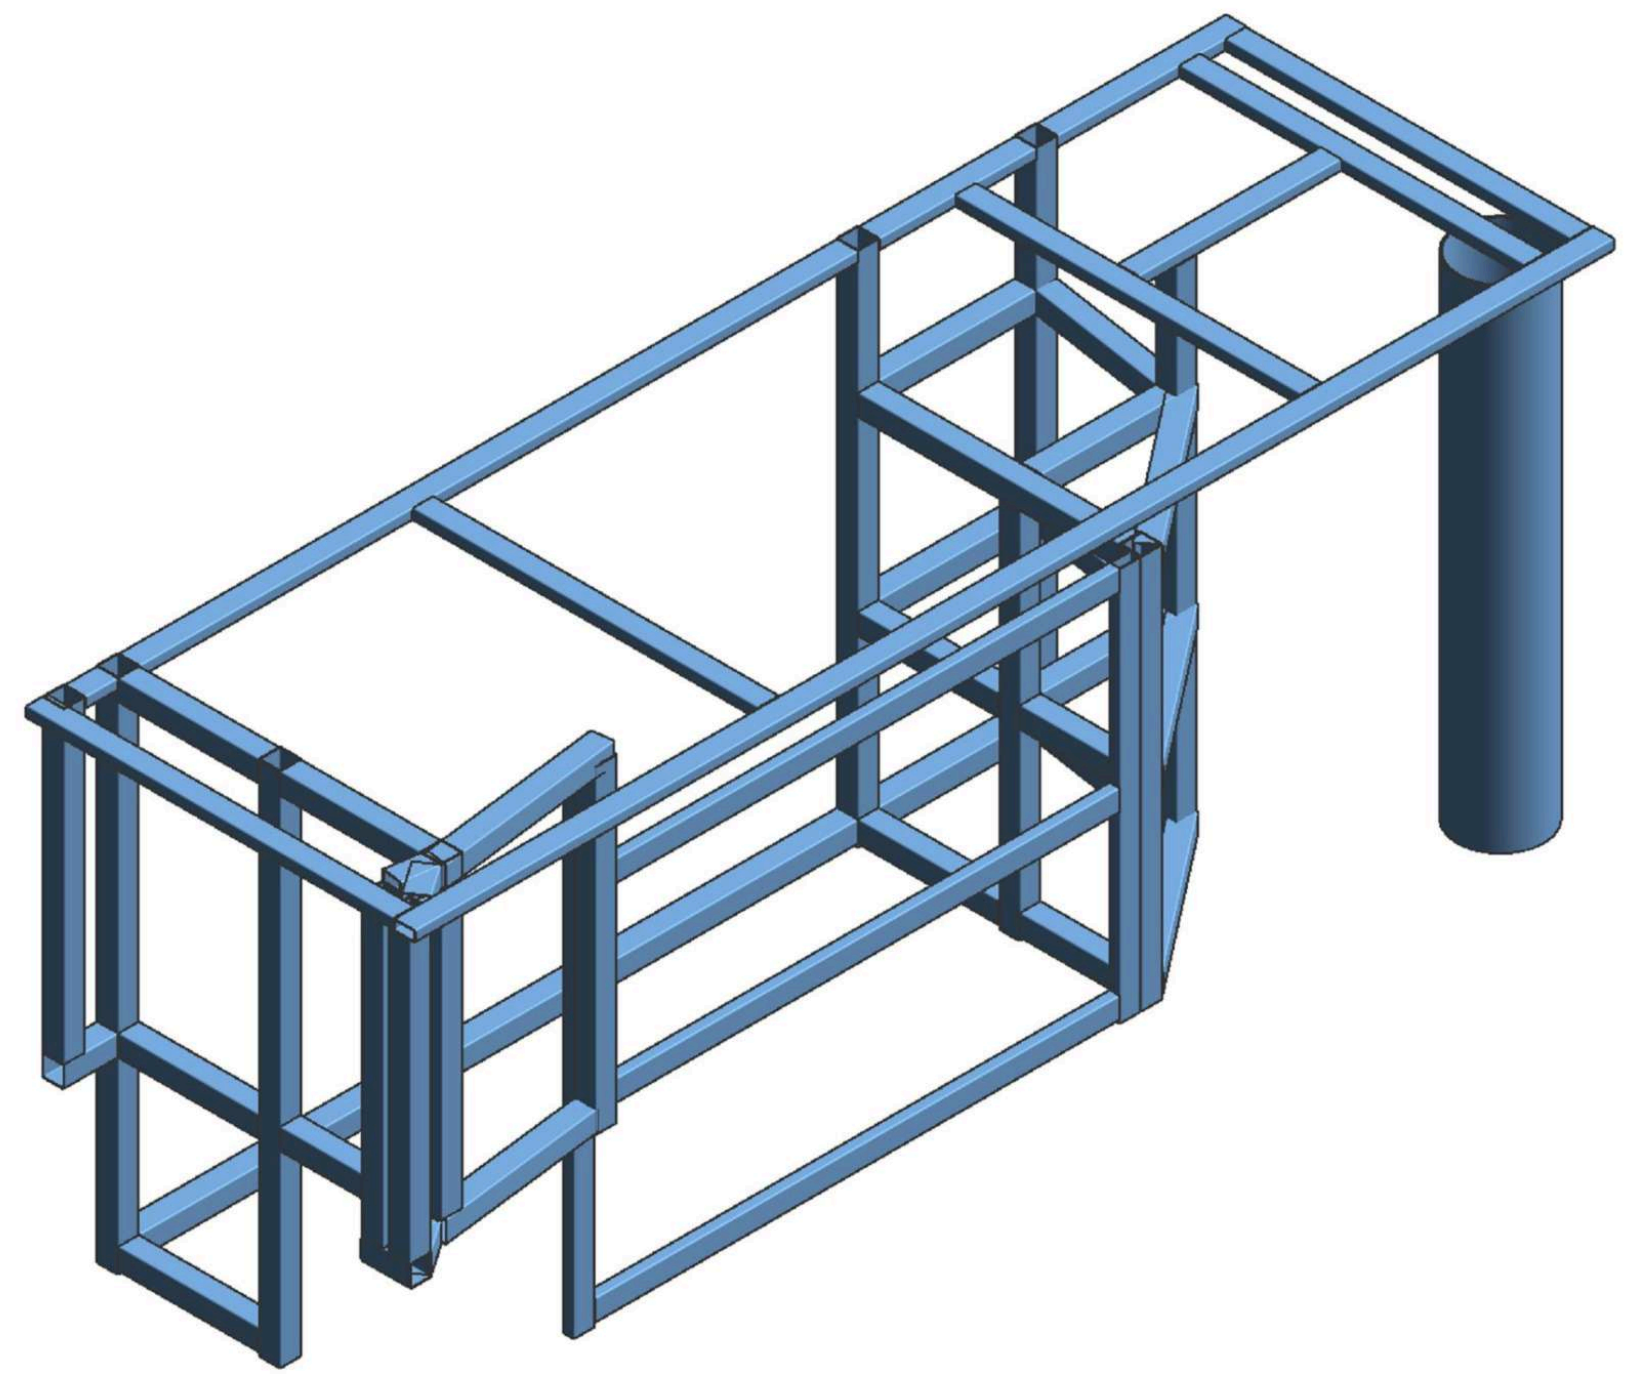

①

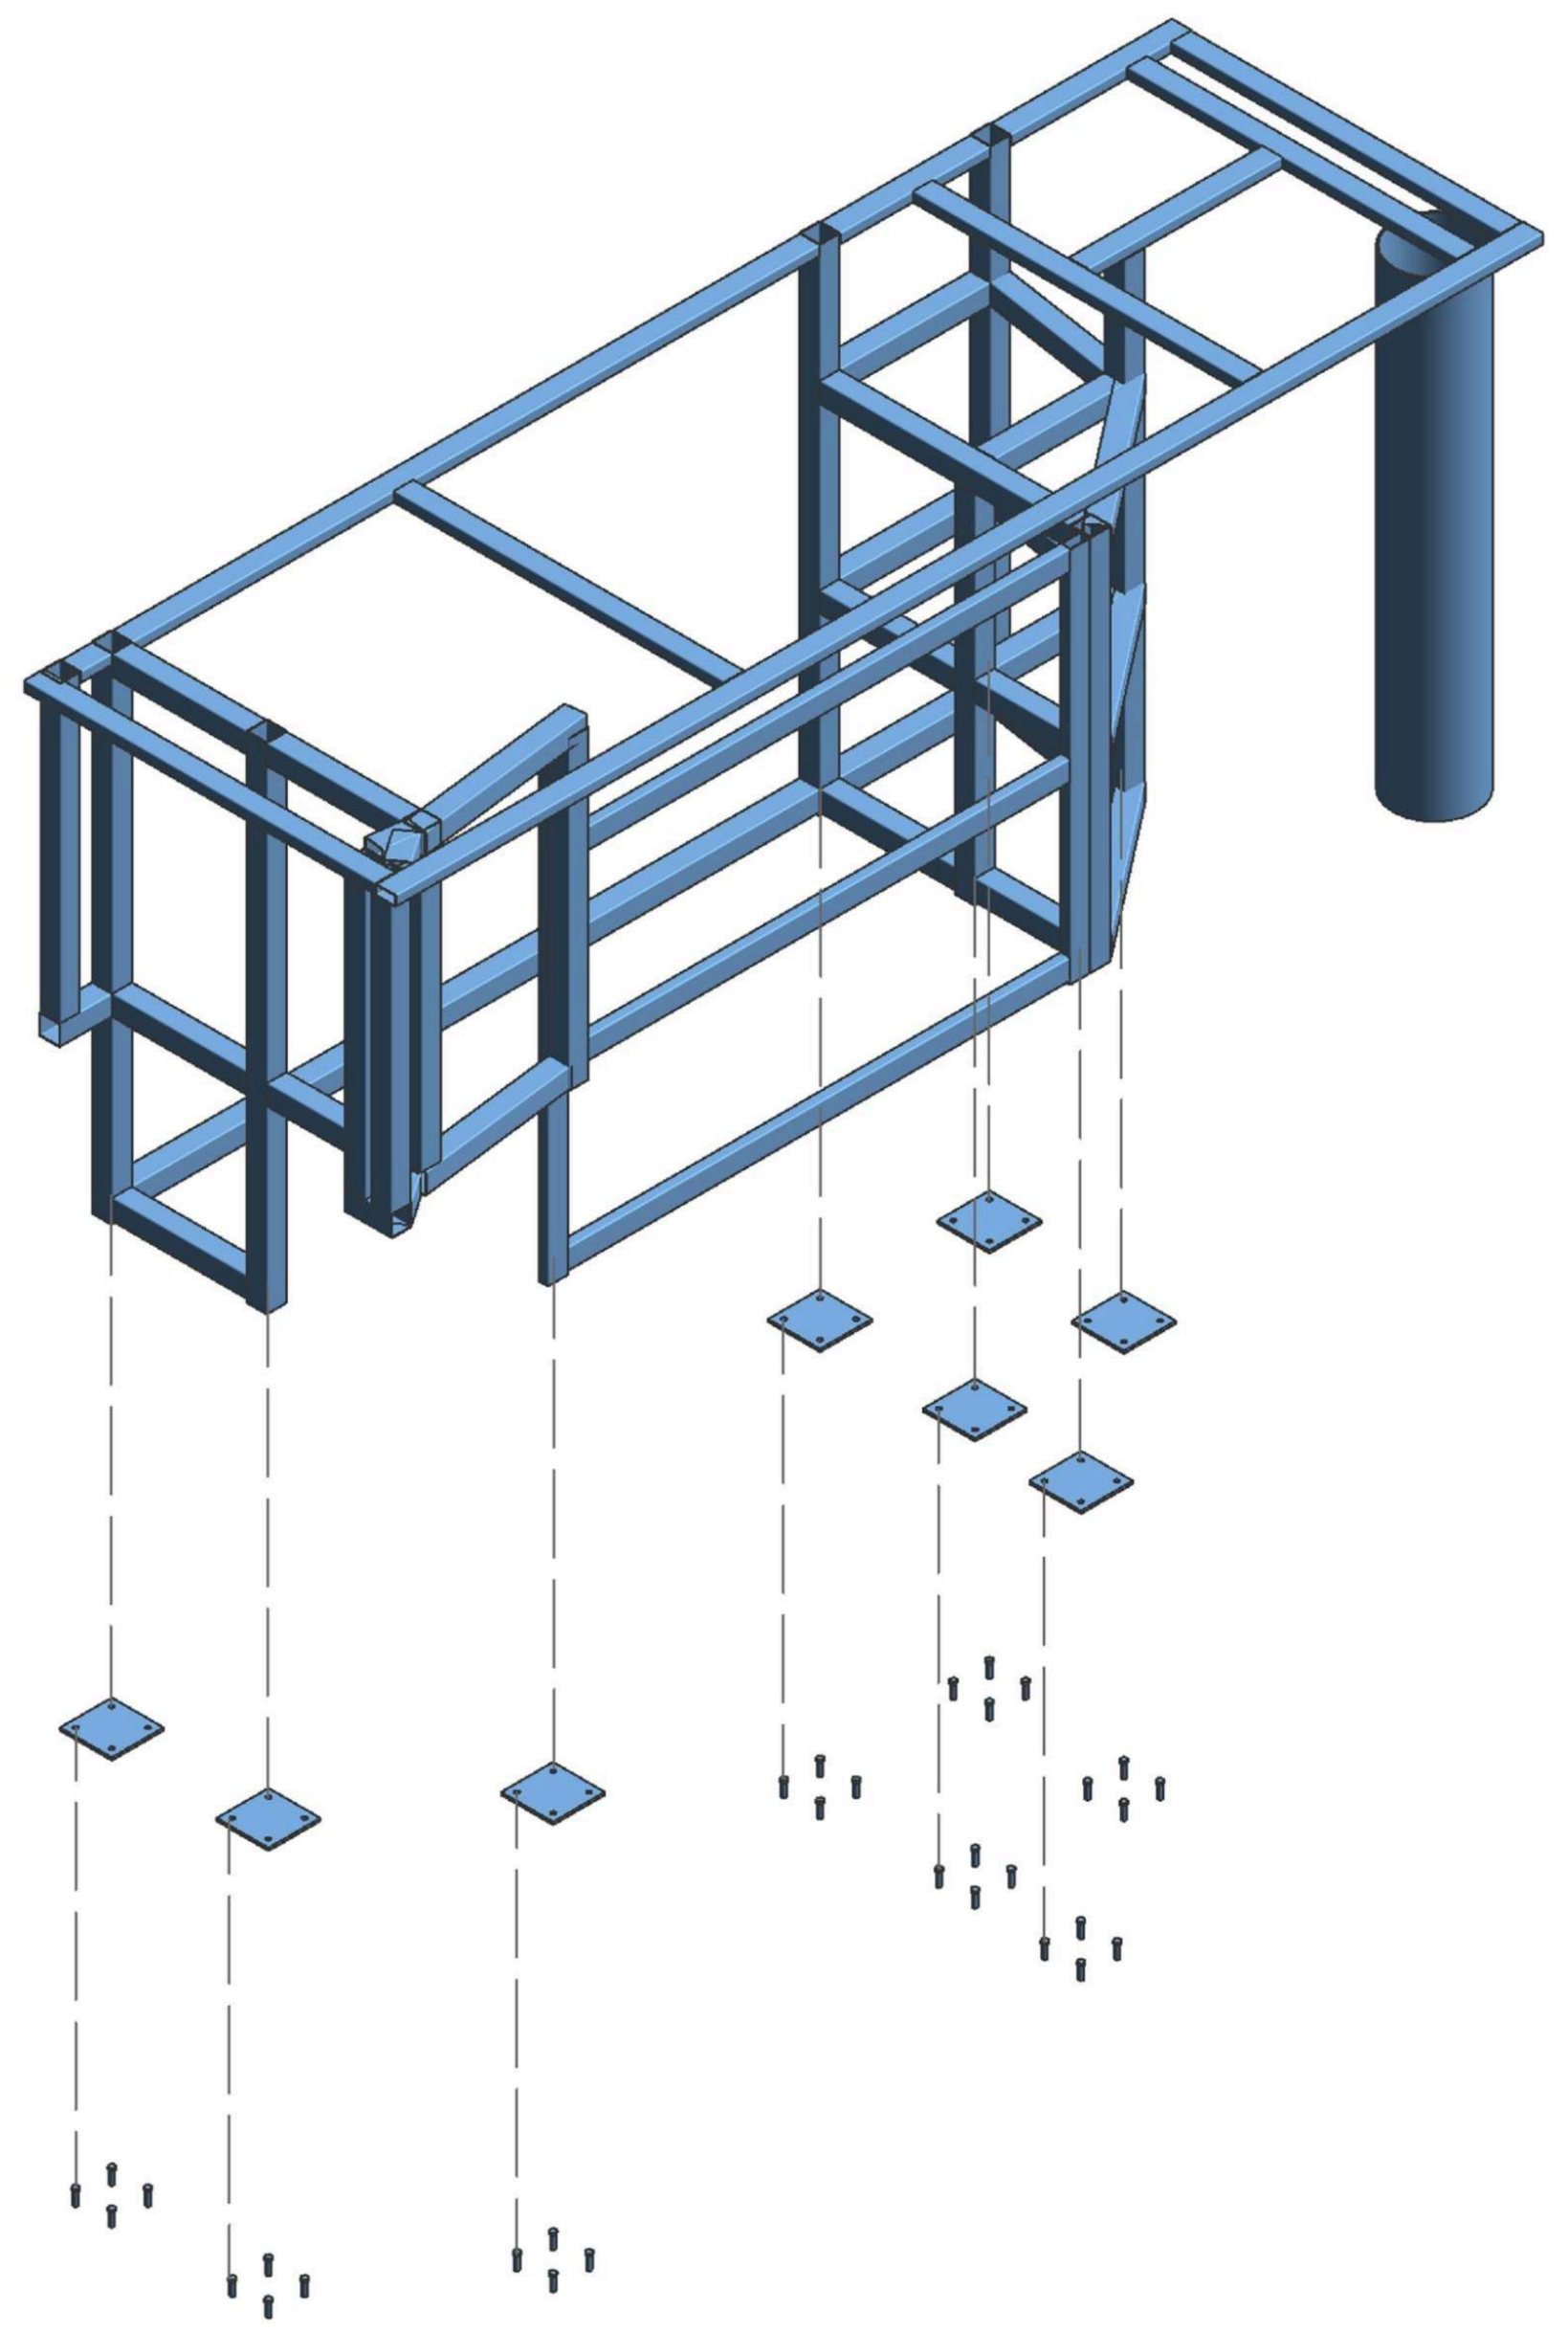

②

③

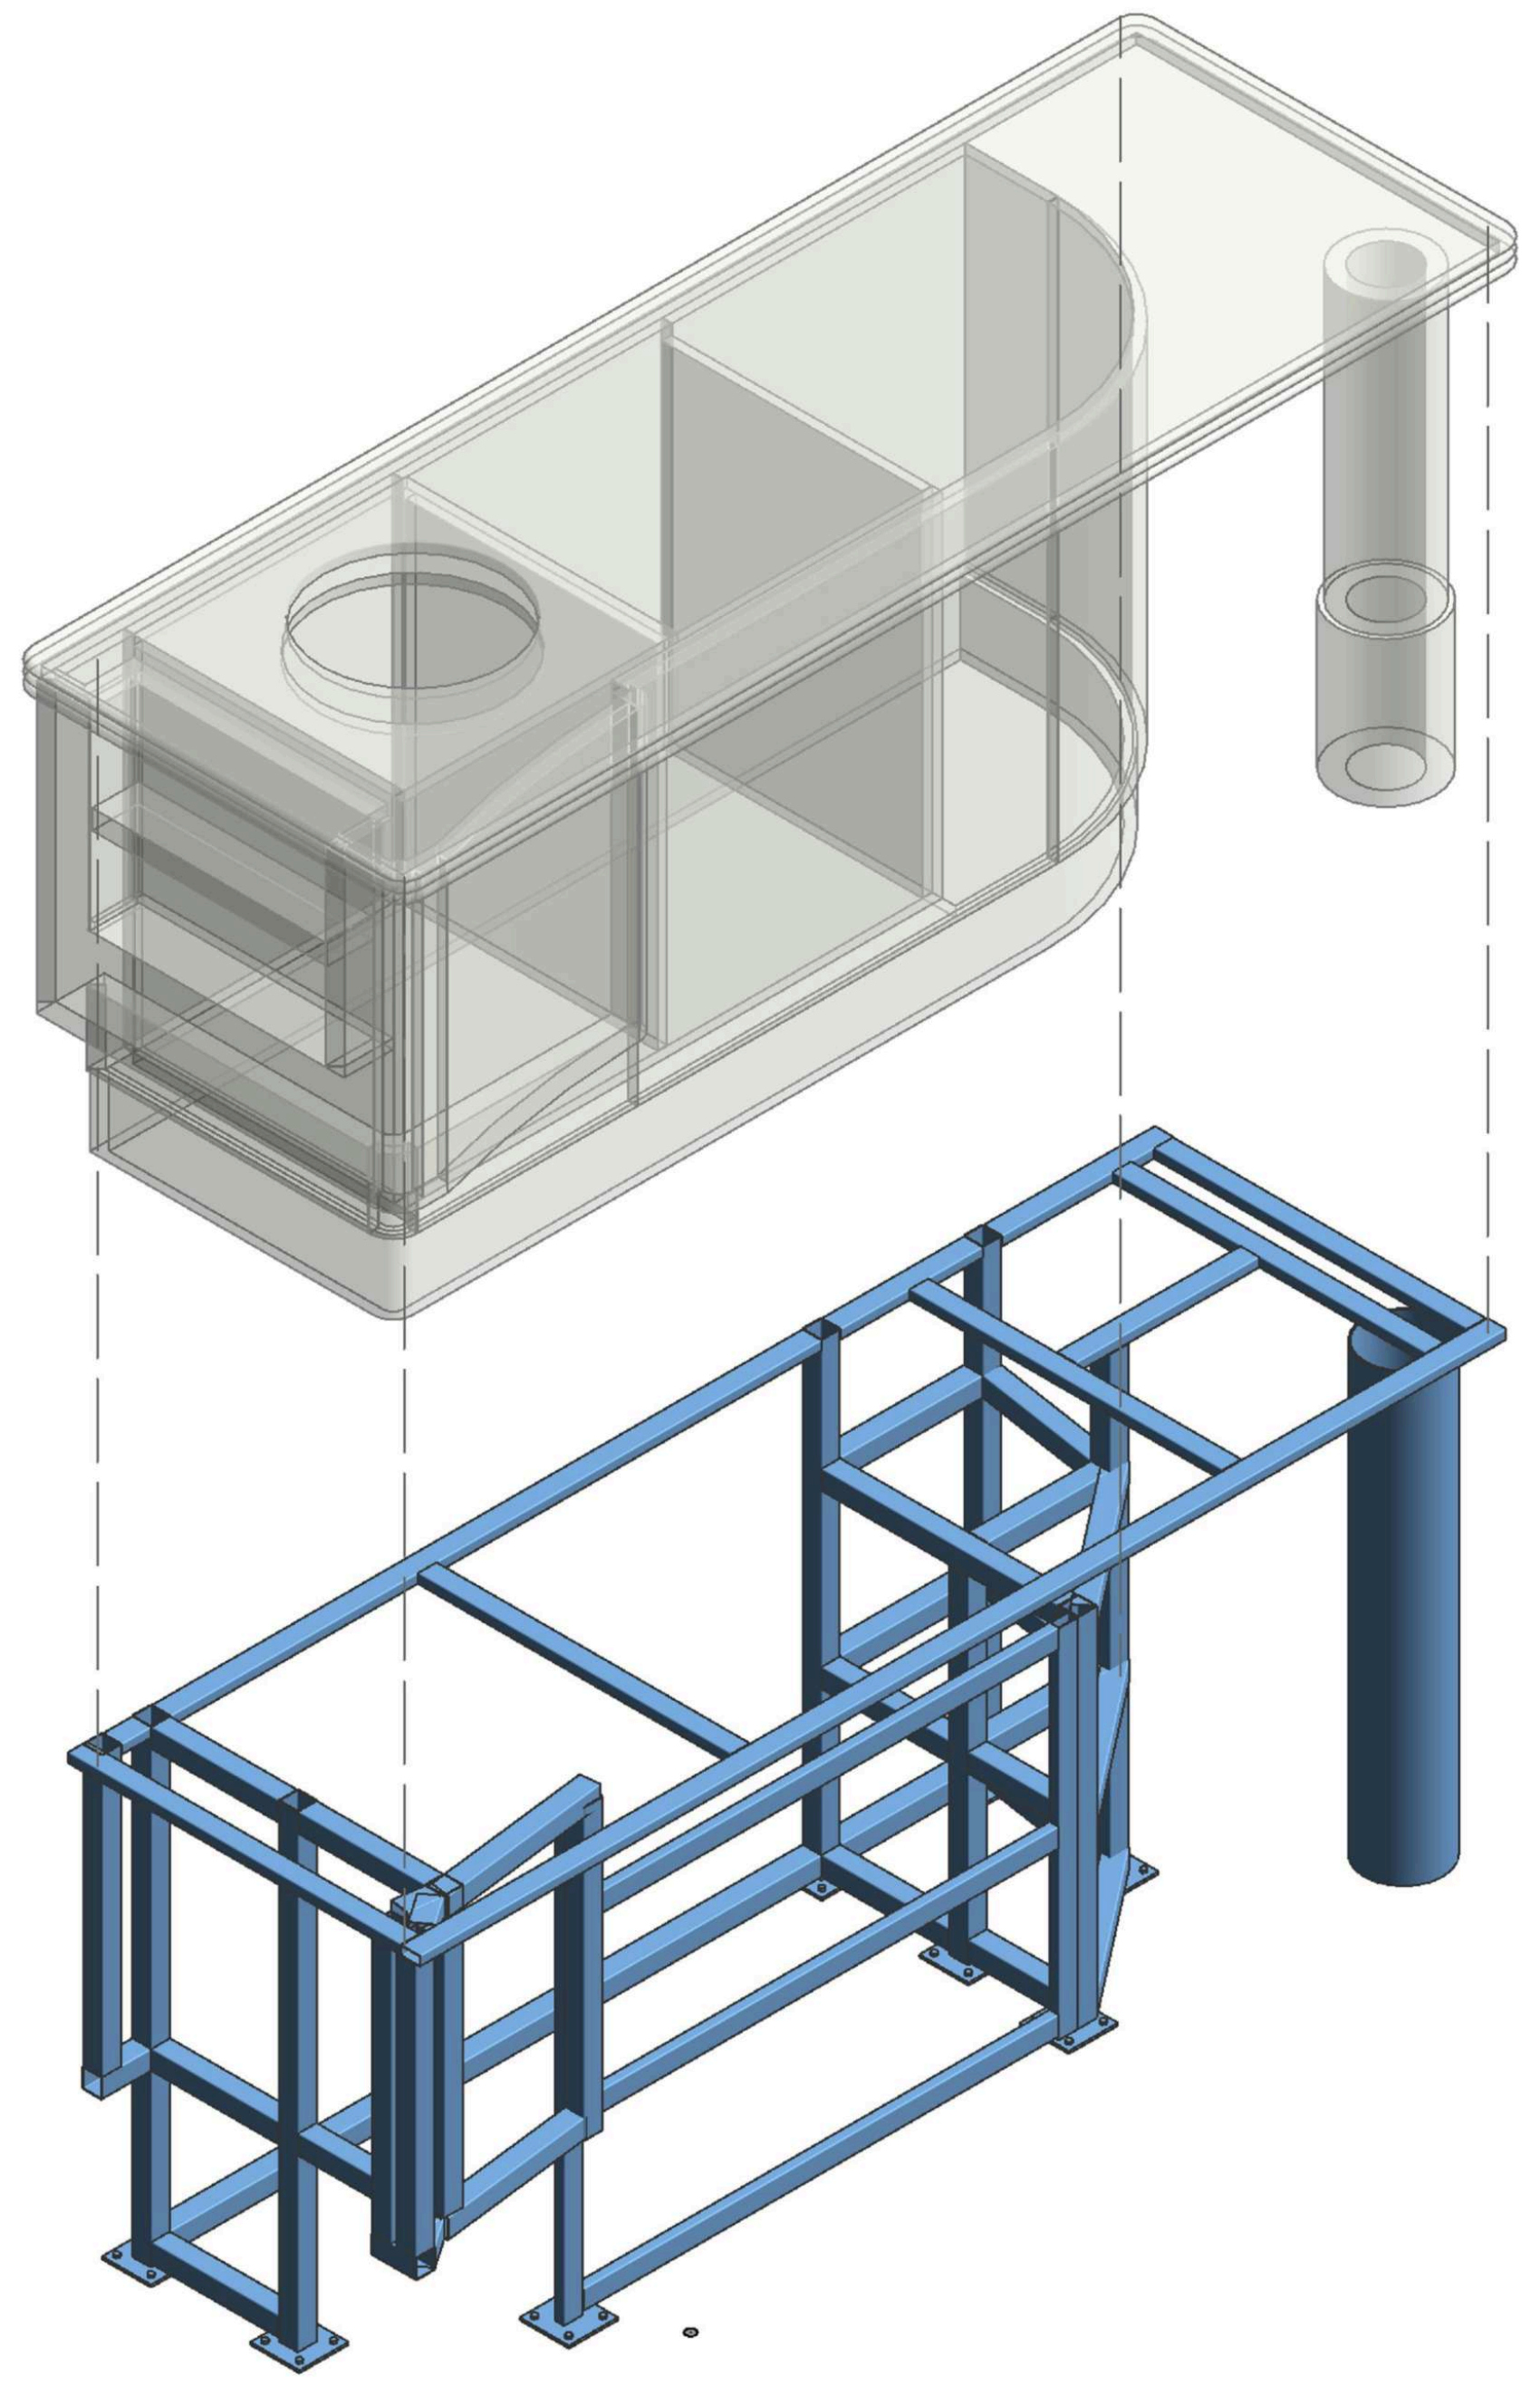

④

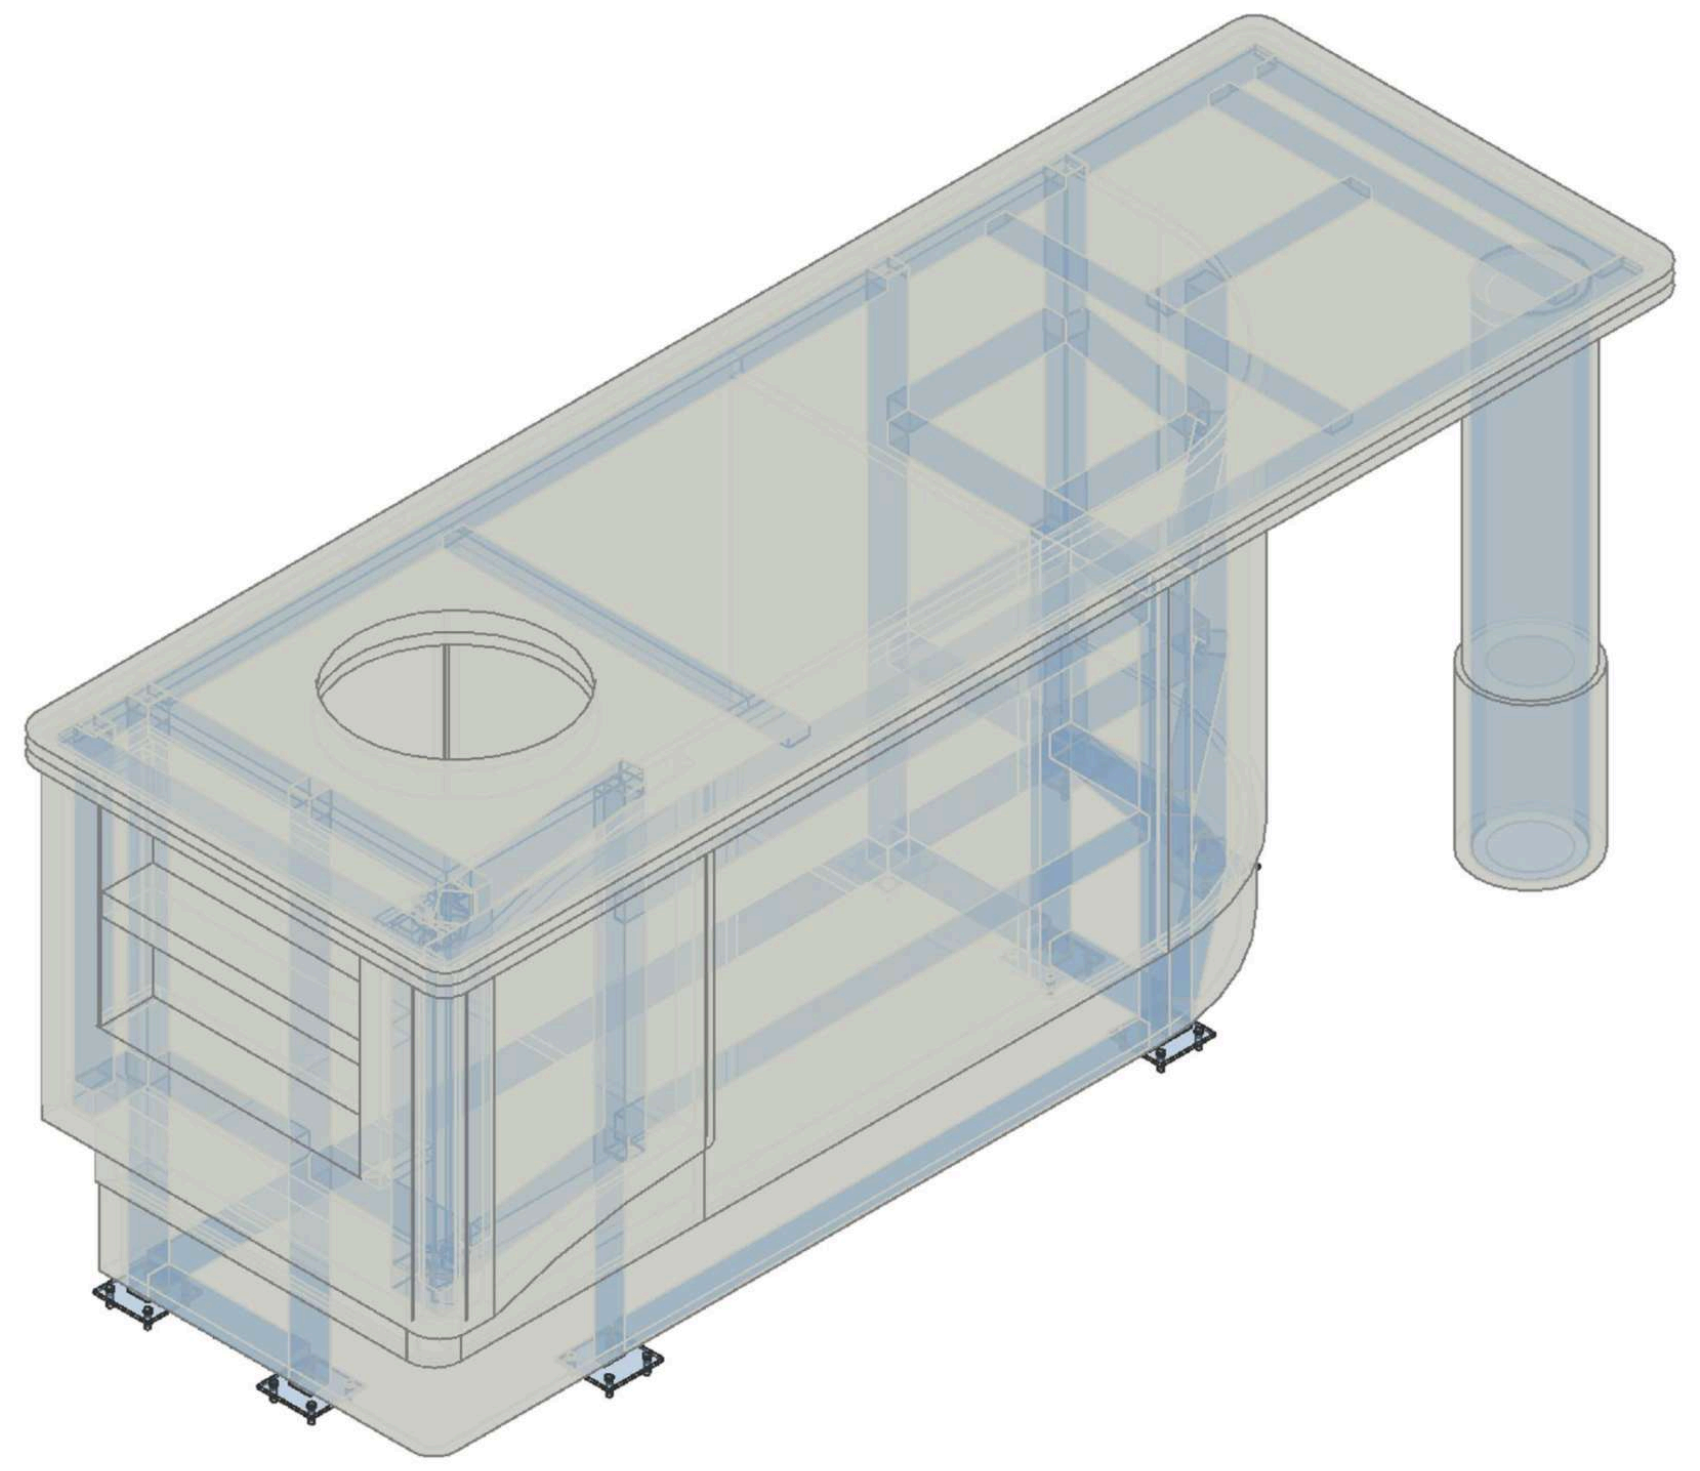

EIBORN

图例A
LEGEND A

编号	图例	说明
1		原始钢架
2		螺栓
3		钢片
4		钢架
5		石材

盖章

注释
Notes

1.本图纸如与现场尺寸有误，请施工人员与项目负责人联系。
2.施工前施工人员应认真查阅此图，如有不明确尺寸，按现场测量为准。
3.本图纸必须经甲乙双方认可并签字方可作为施工依据。

日期
Date 04/24/26

修订
Revision

1

项目
Project
潮映华岸府3-801

比例
Scale

西厨岛台石材钢架

图纸编号
Drawing No.
ST-06

项目编号
Project No.

©2025

1

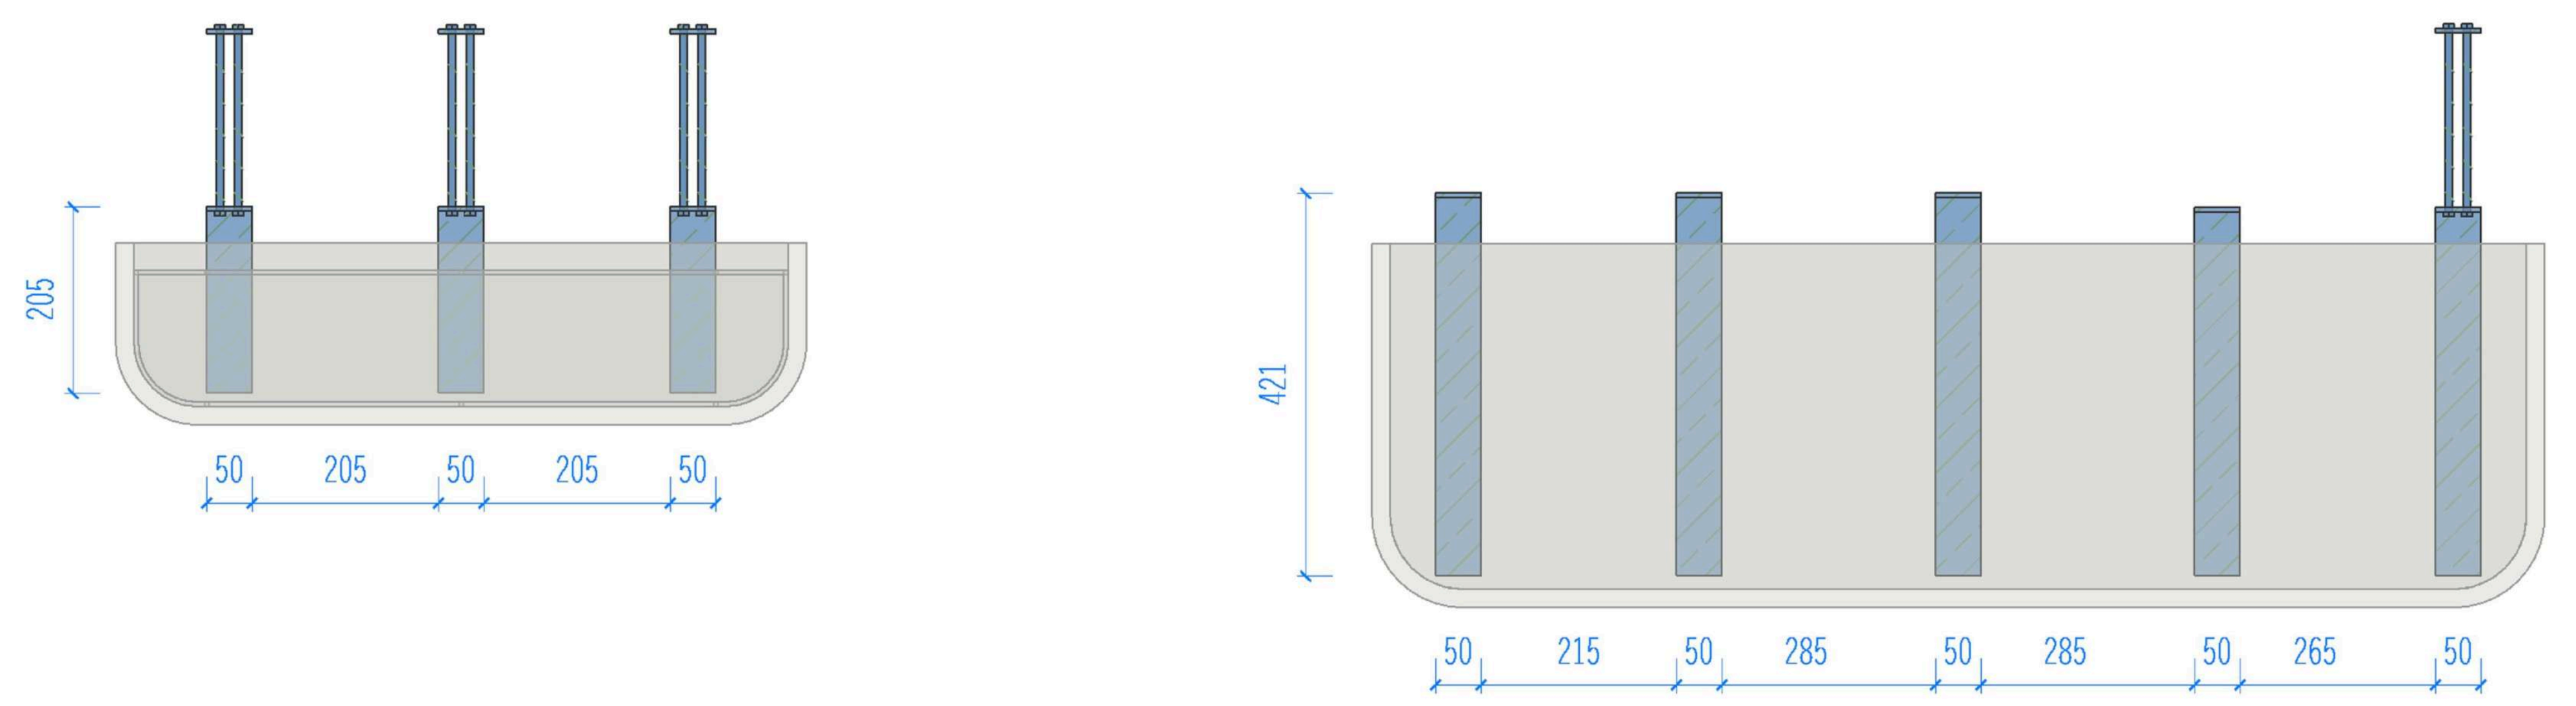
205
50
205
50
205
50
421
50
215
50
285
50
285
50
265
50

平面视图

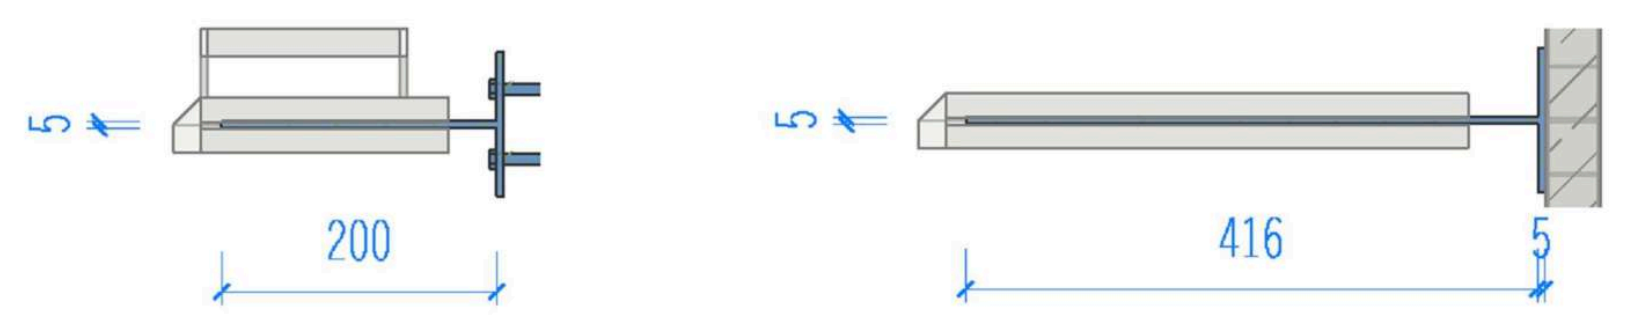

剖面视图

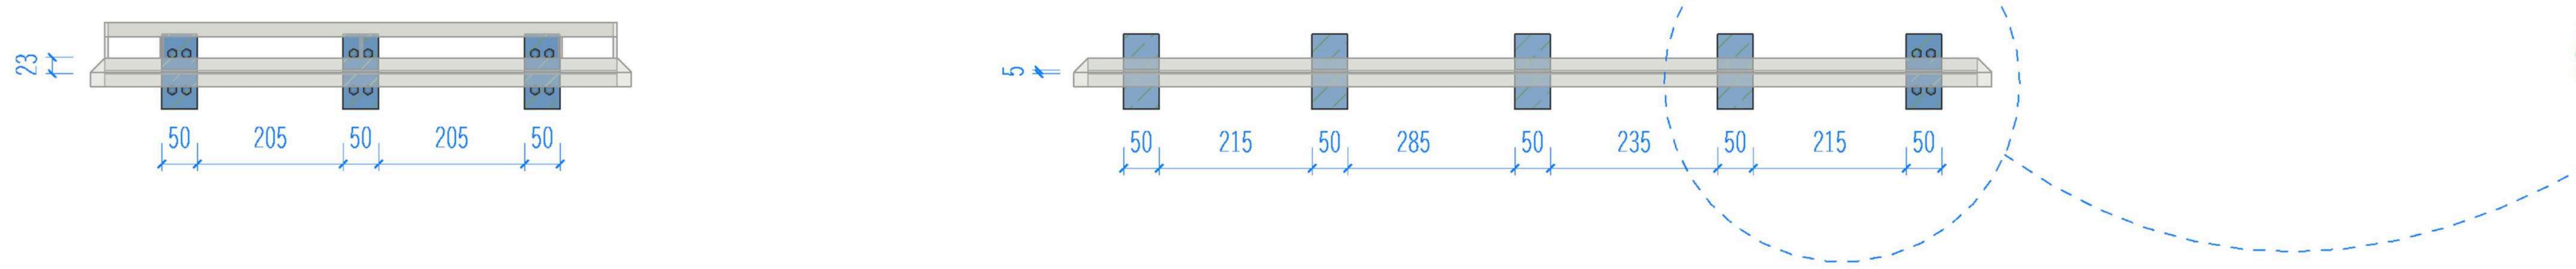
23
50
205
50
205
50
5
50
215
50
285
50
235
50
215
50

立面视图

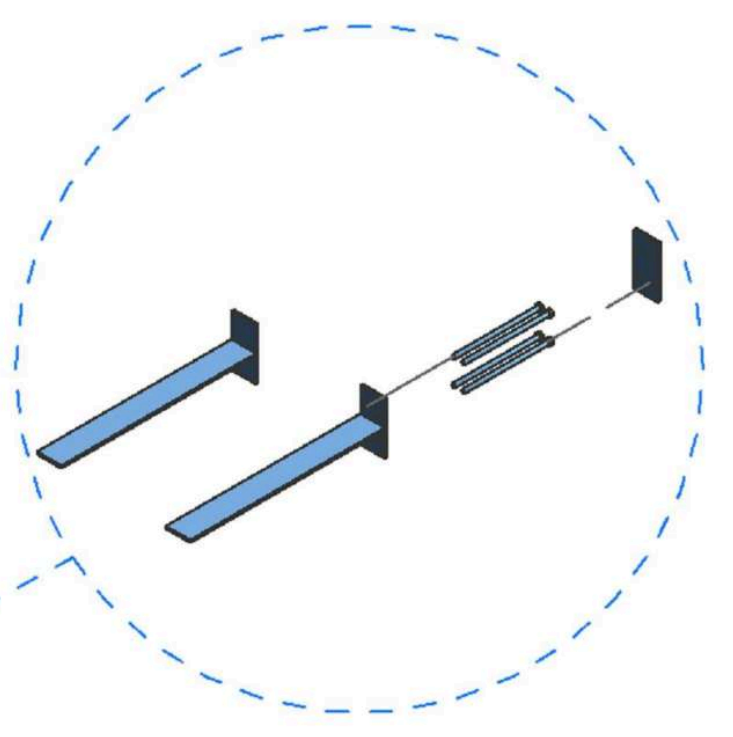

节点图

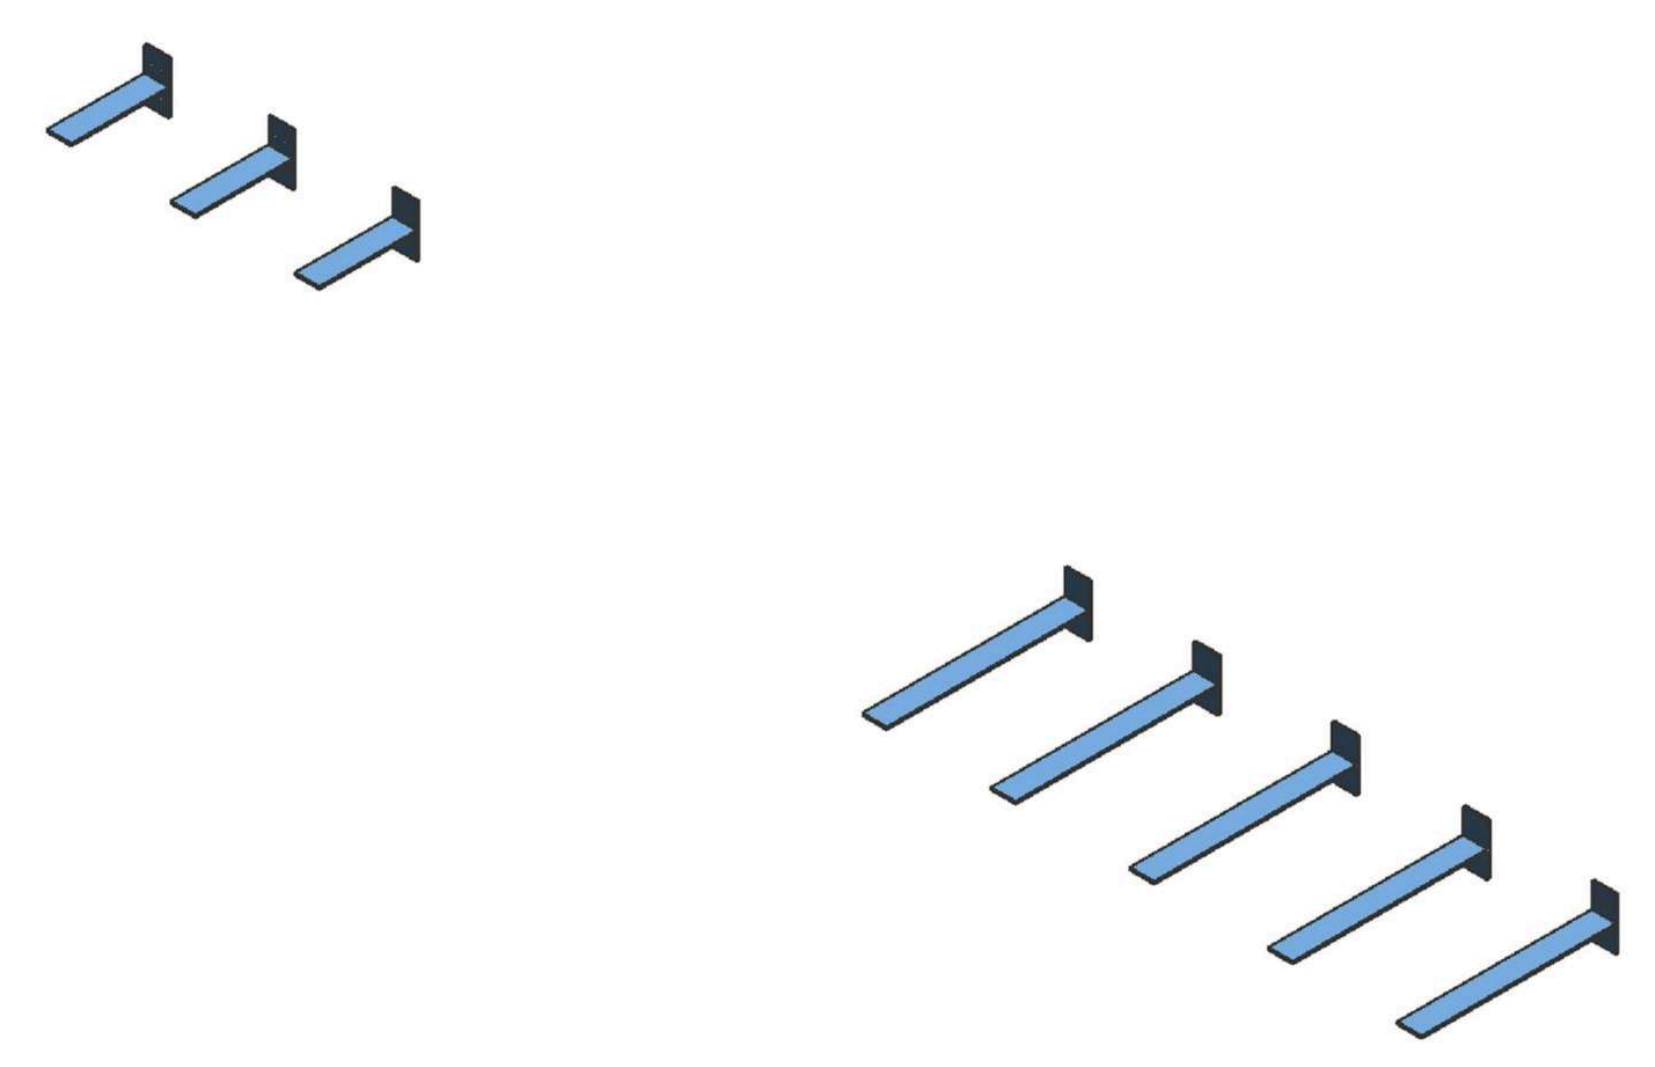

①

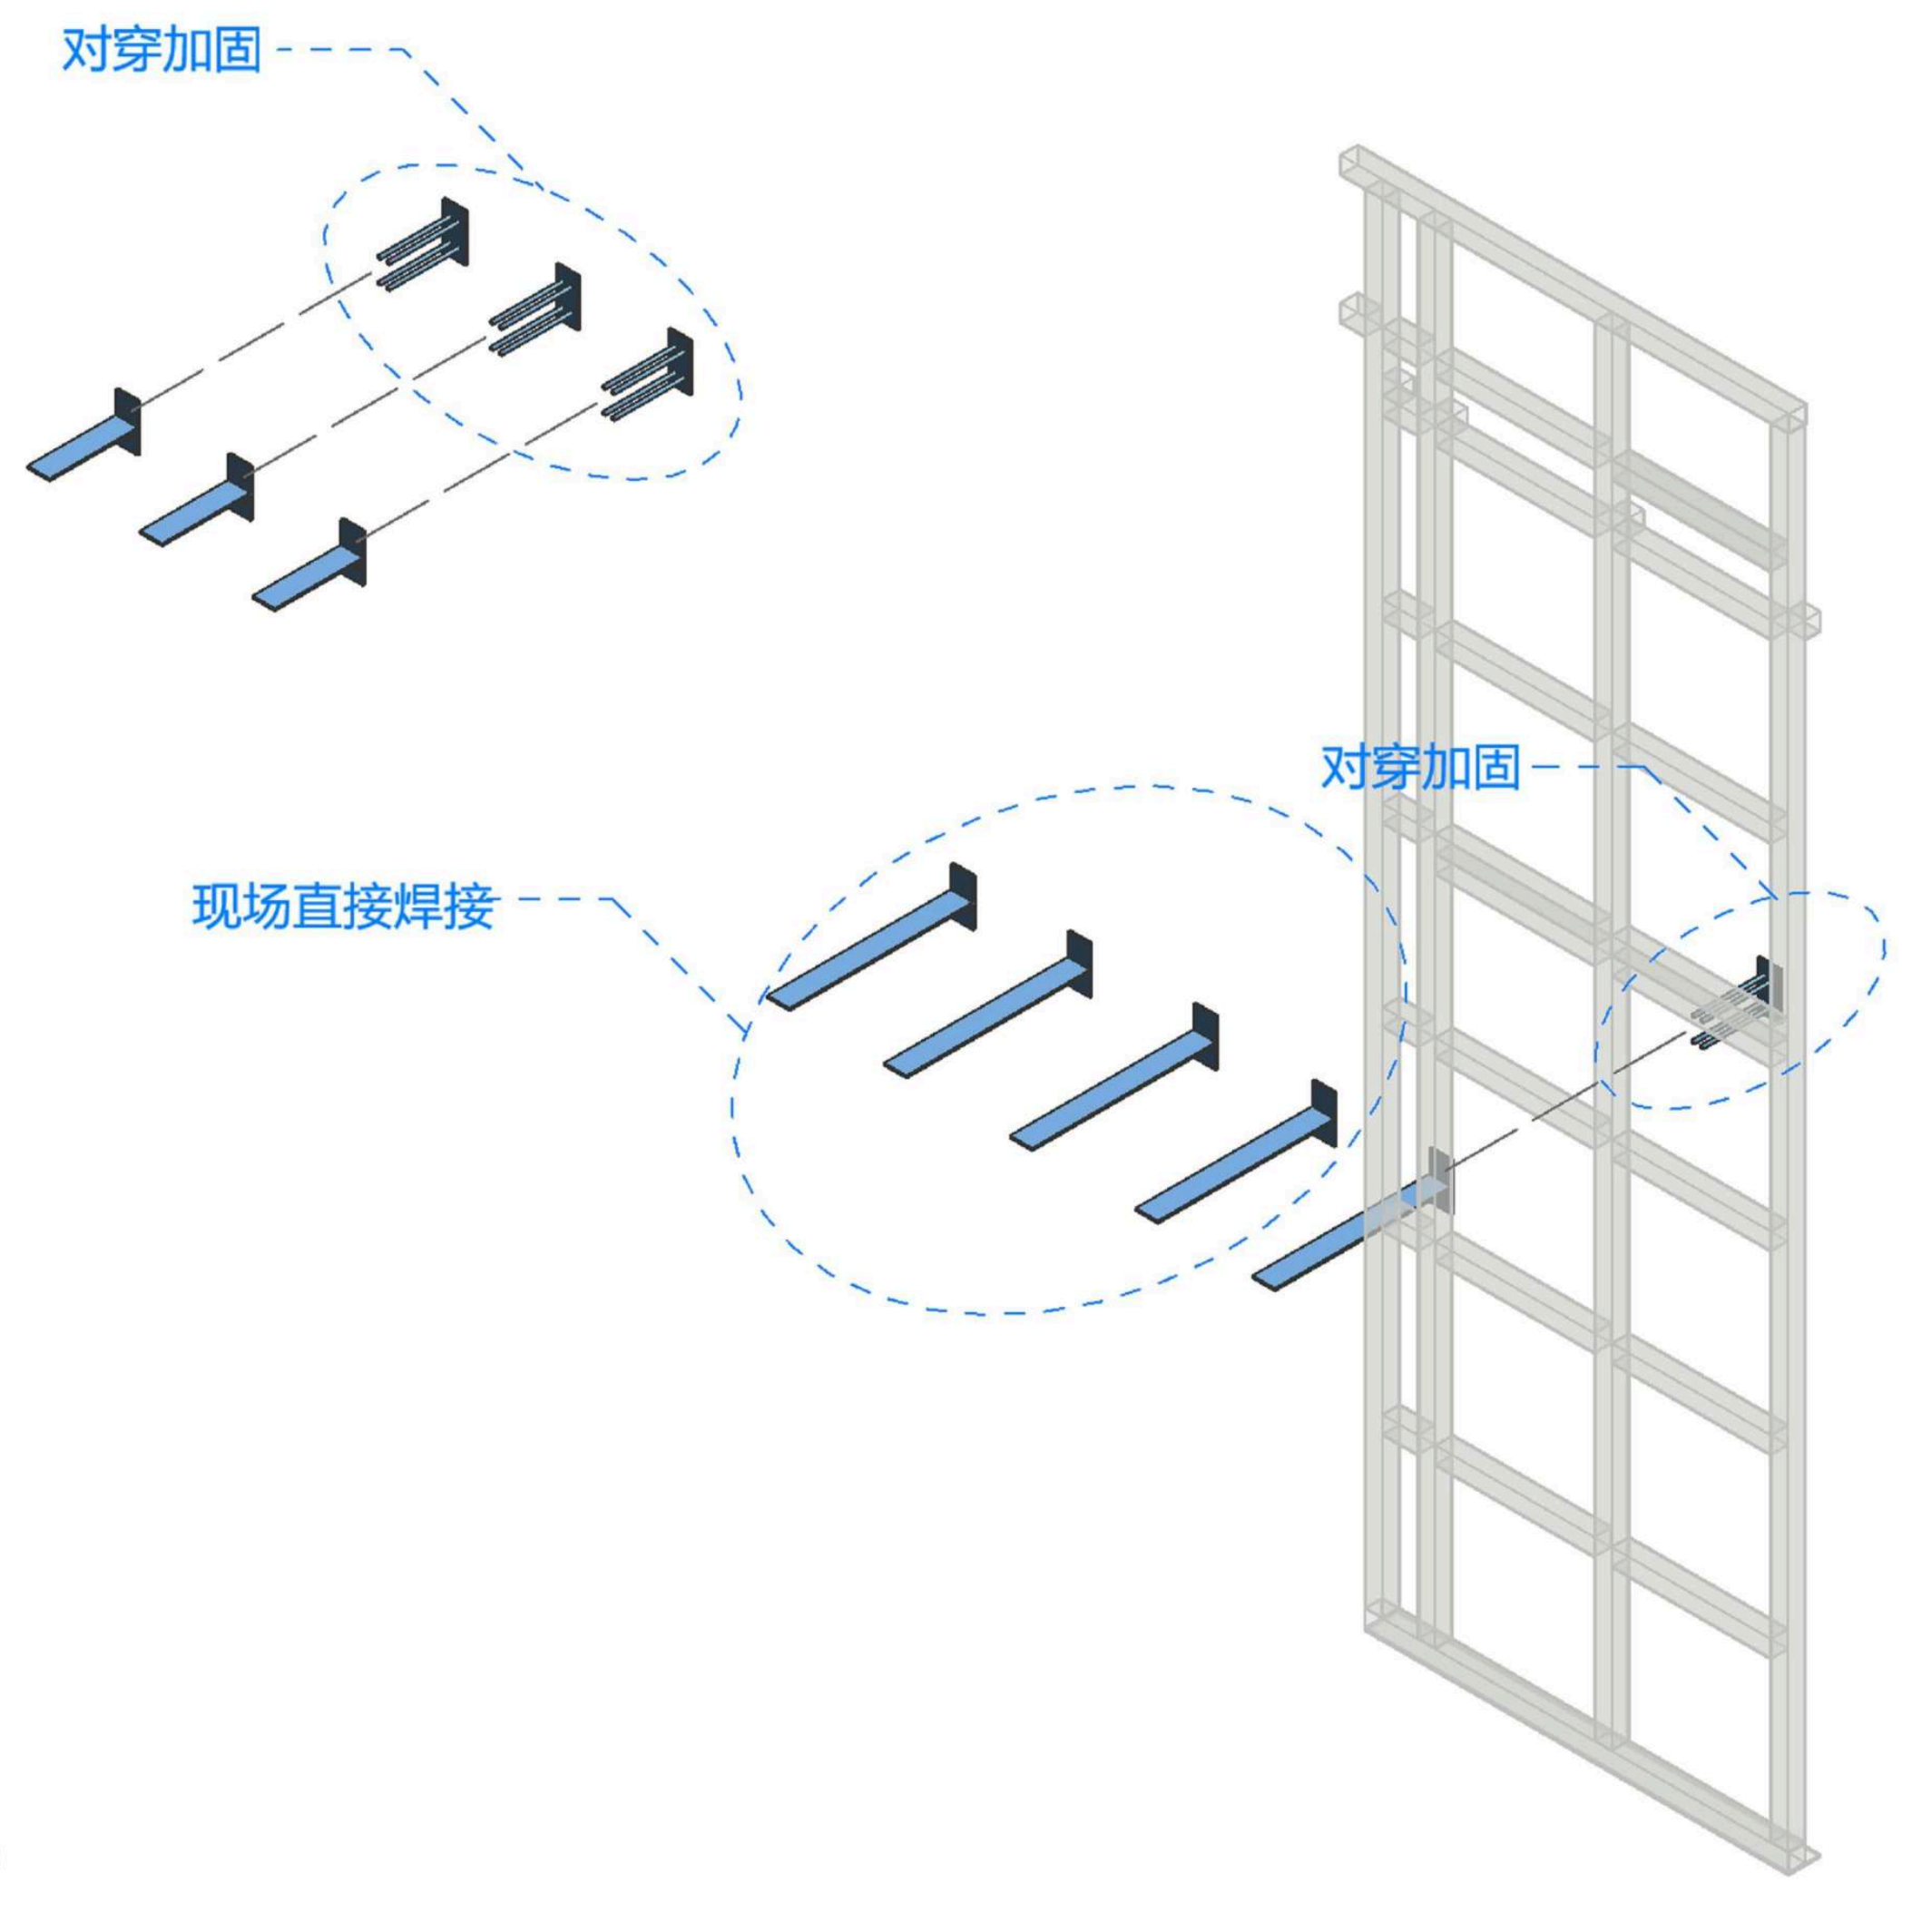
对穿加固
对穿加固
现场直接焊接

②

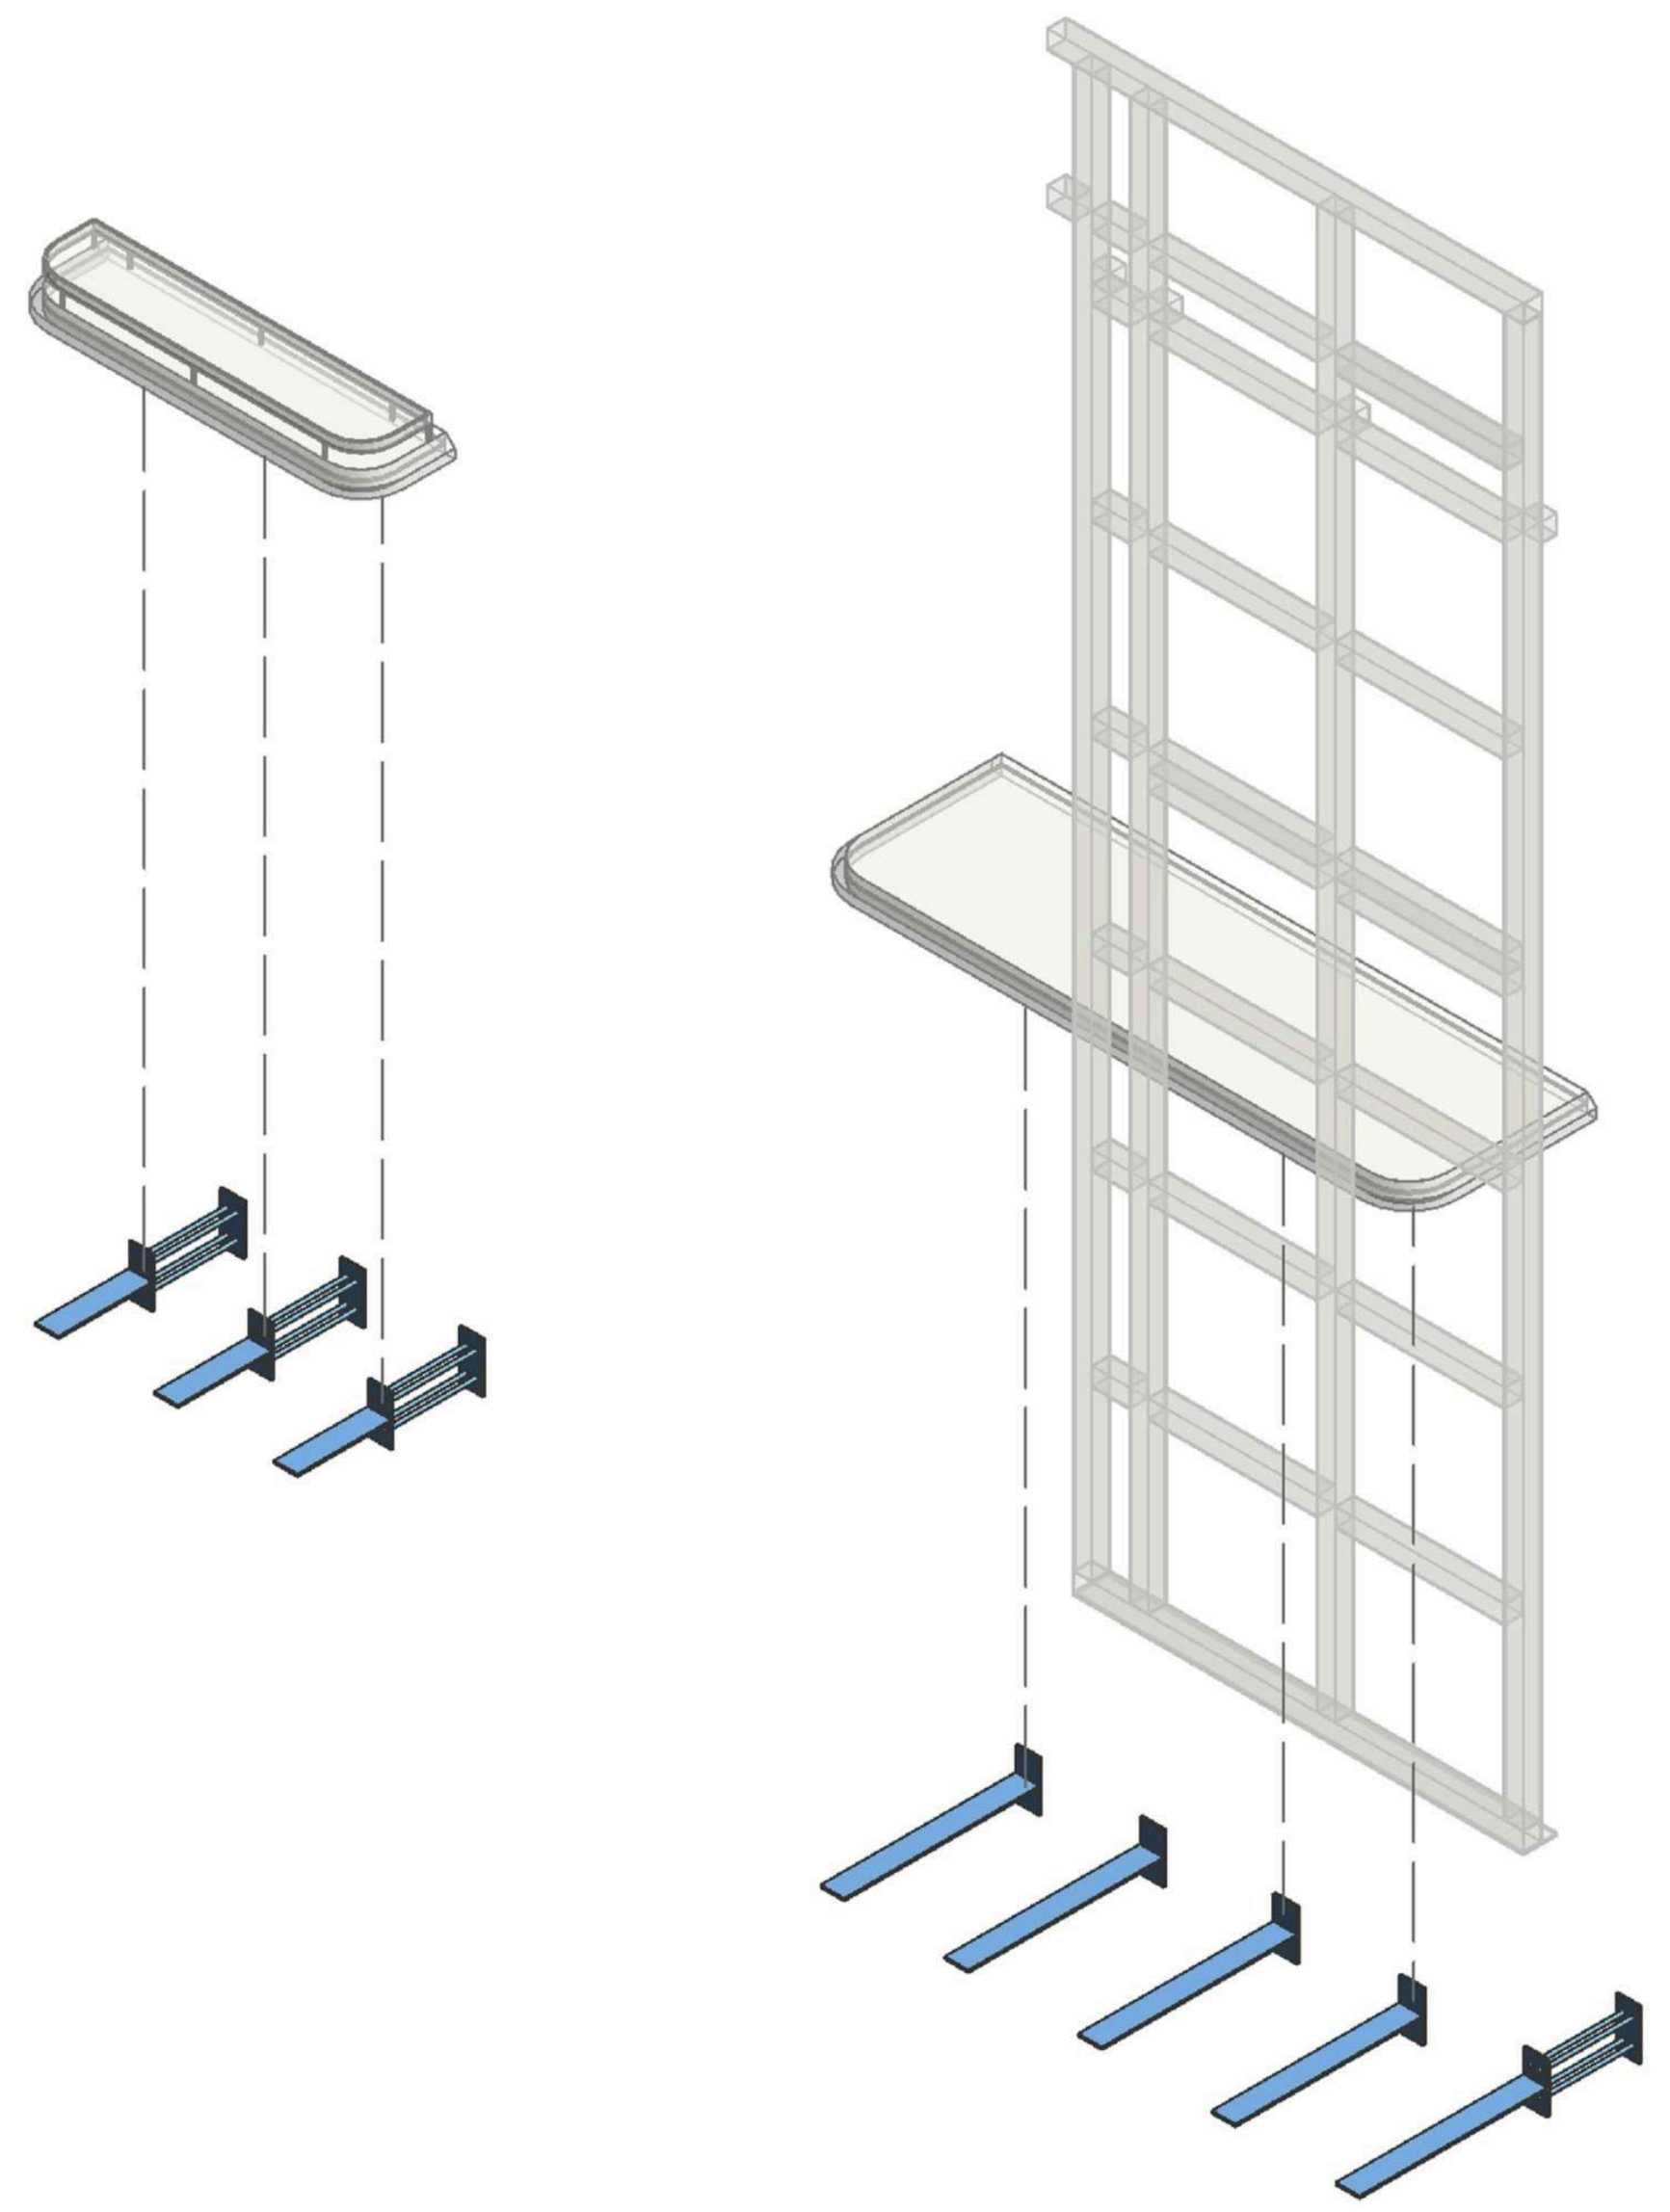

③

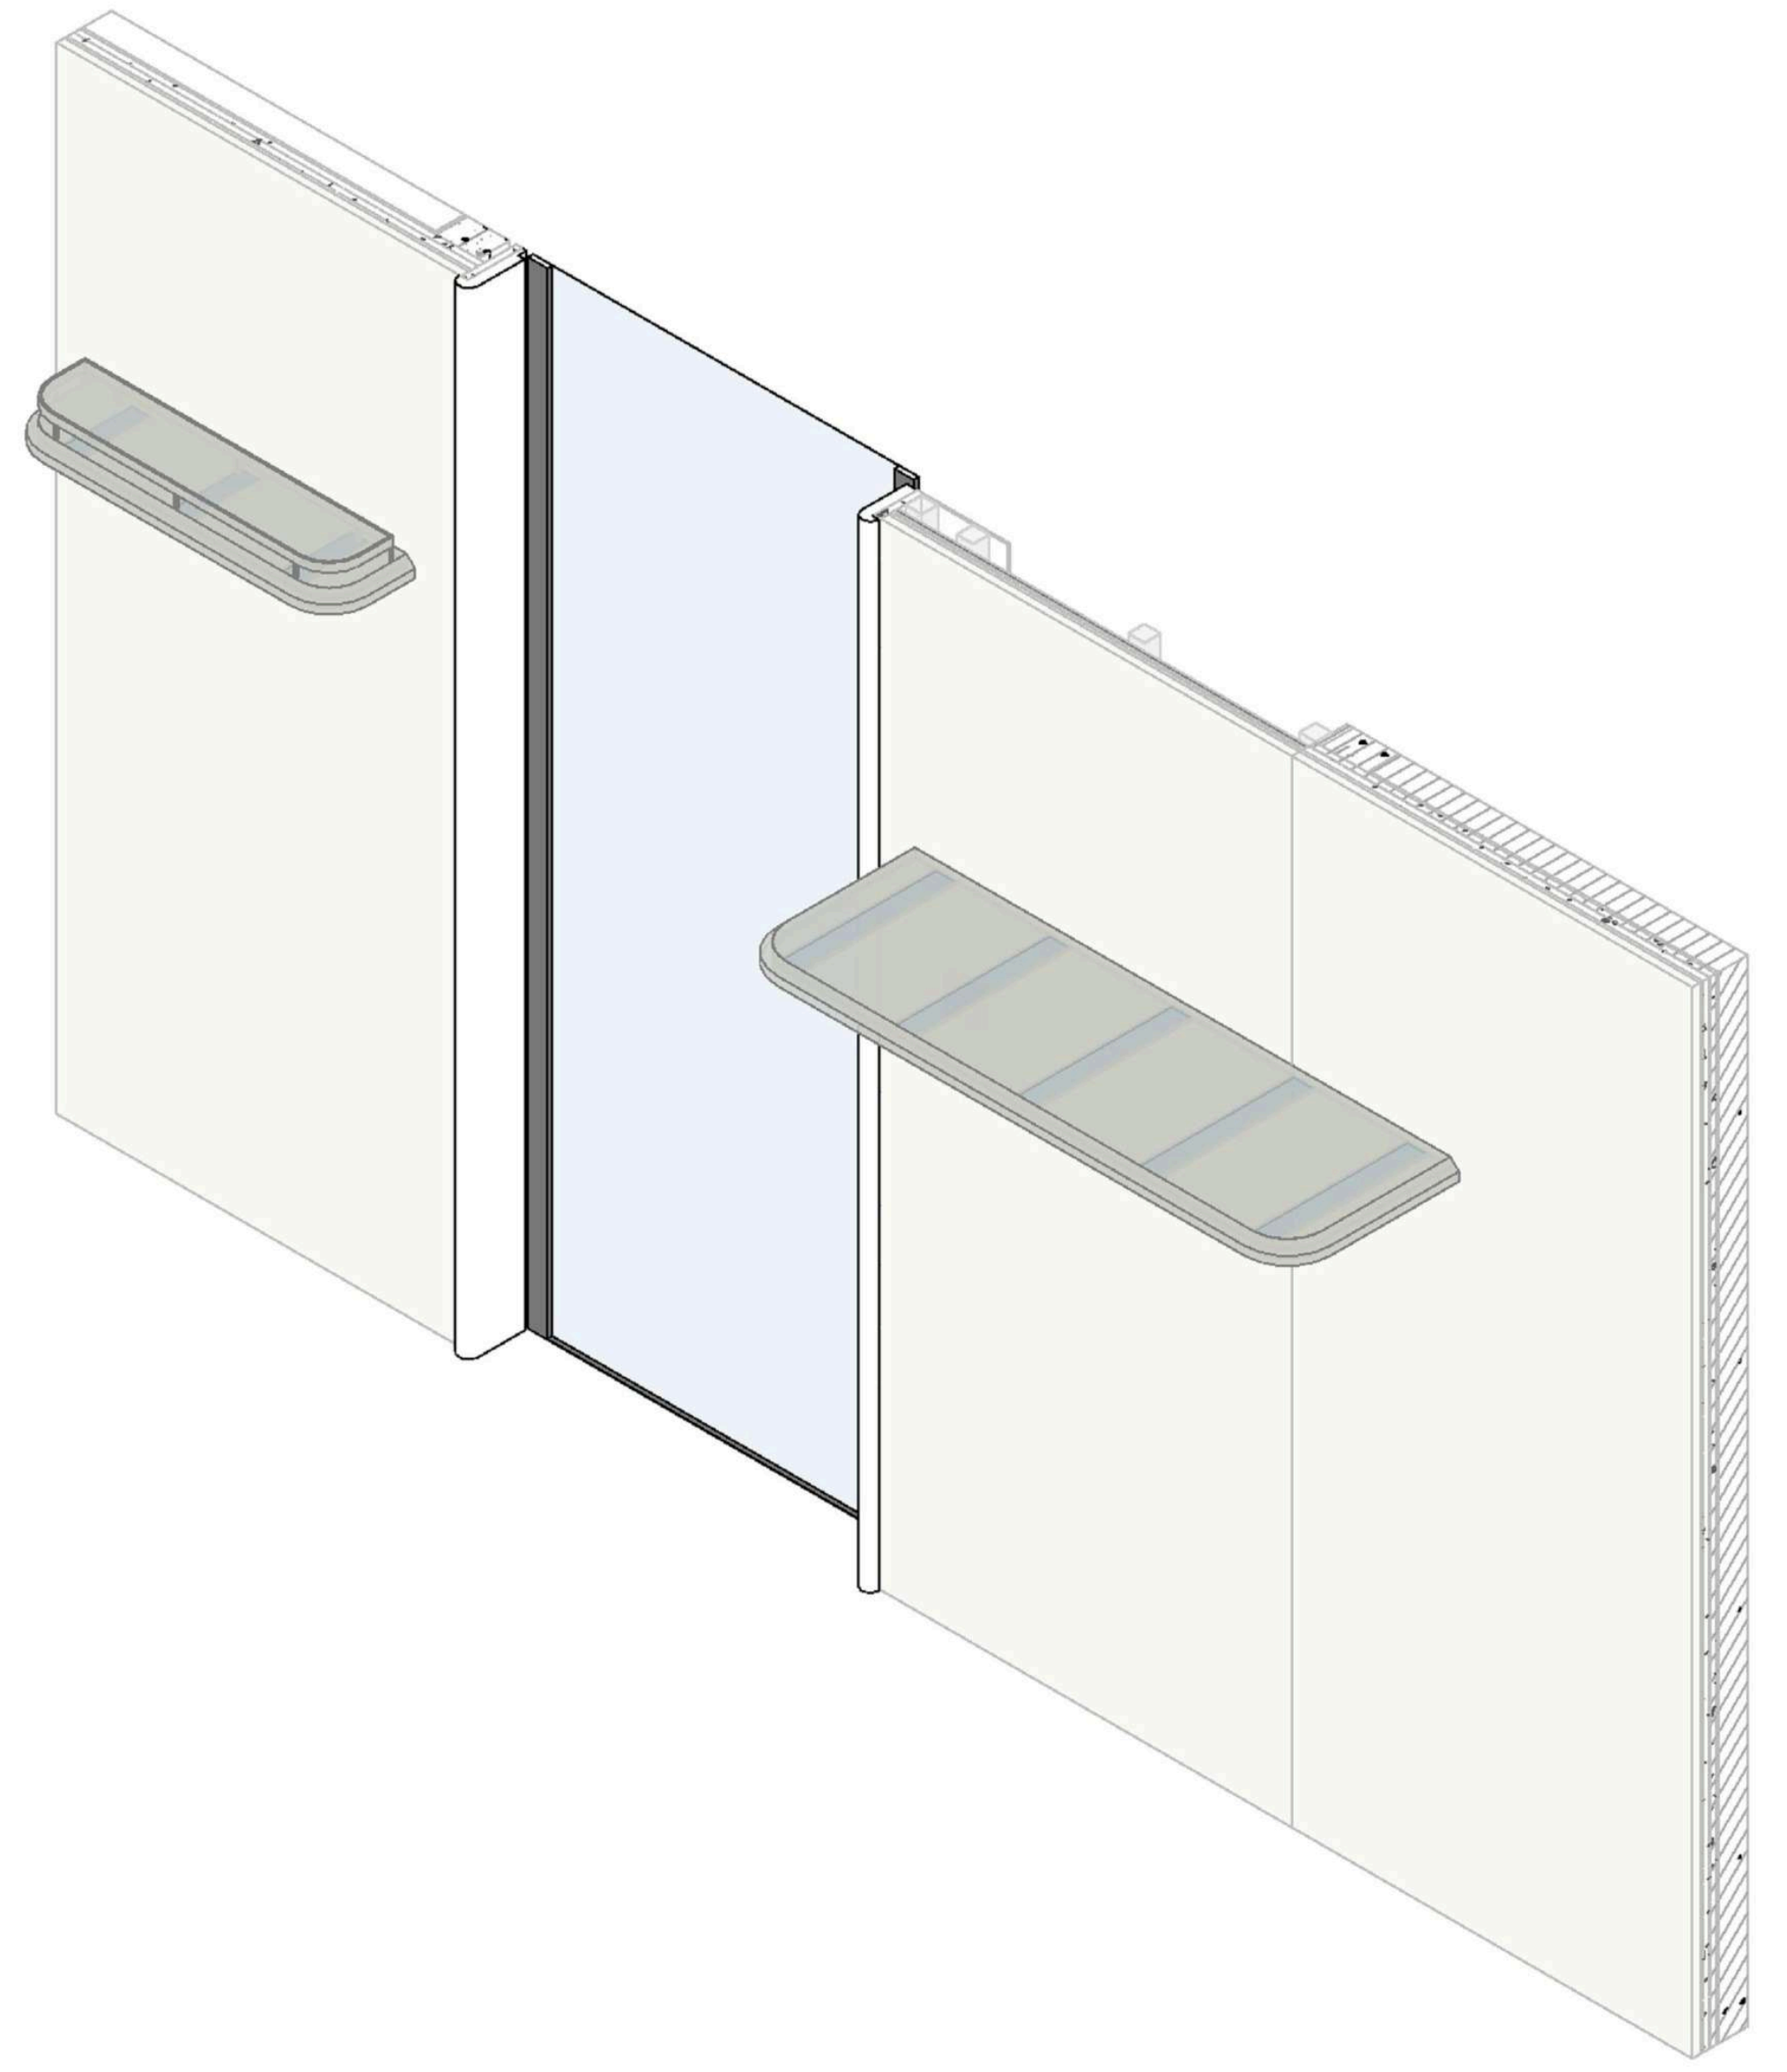

④

图例A
LEGEND A

编号	图例	说明
1	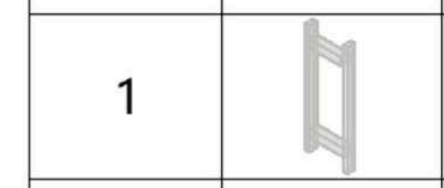	原始钢架
2		螺栓
3		钢片
4		角铁挑件
5	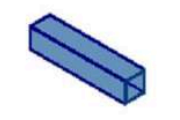	钢架
6	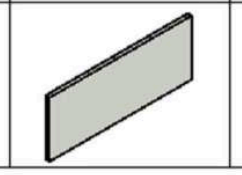	石材

盖章

注释
Notes

1.本图纸如与现场尺寸有误，请施工人员与项目负责人联系。
2.施工前施工人员应认真查阅此图，如有不明确尺寸，按现场测量为准。
3.本图纸必须经甲乙双方认可并签字方可作为施工依据。

日期
Date 04/24/26

修订
Revision

1

项目
Project
潮映华岸府3-801

比例
Scale

西厨岛台背景墙石材钢架

图纸编号
Drawing No.
ST-07

项目编号
Project No.

©2025

1

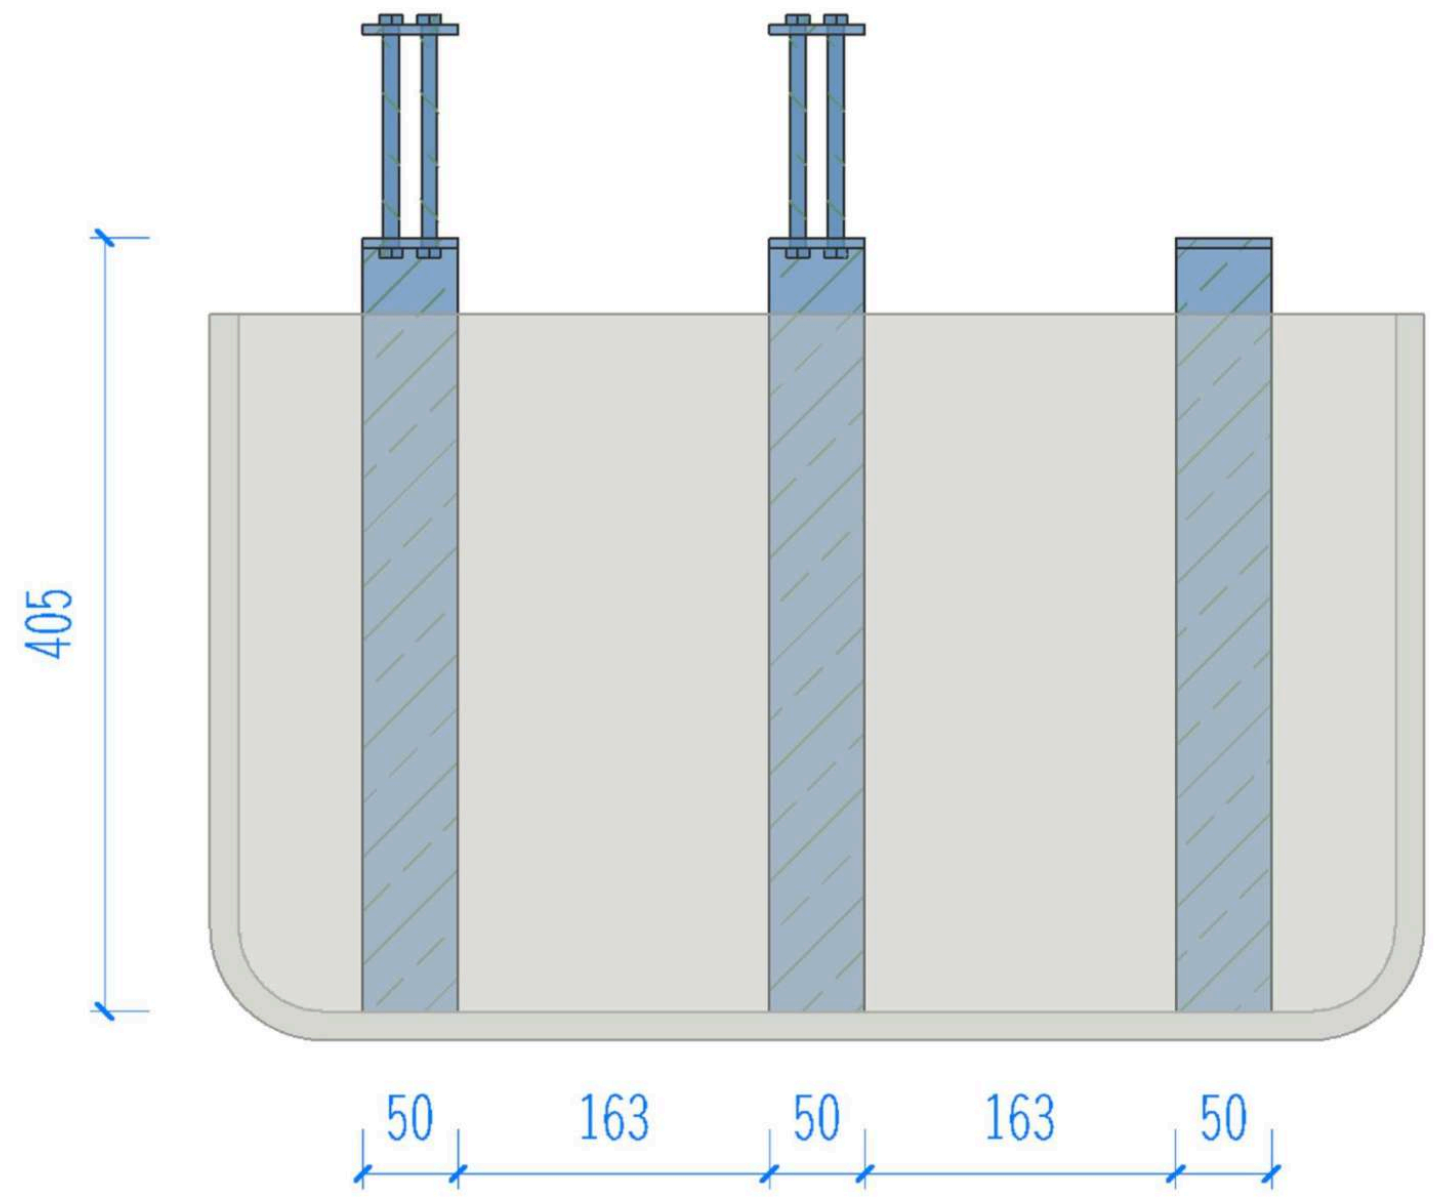
405
50
163
50
163
50

平面视图

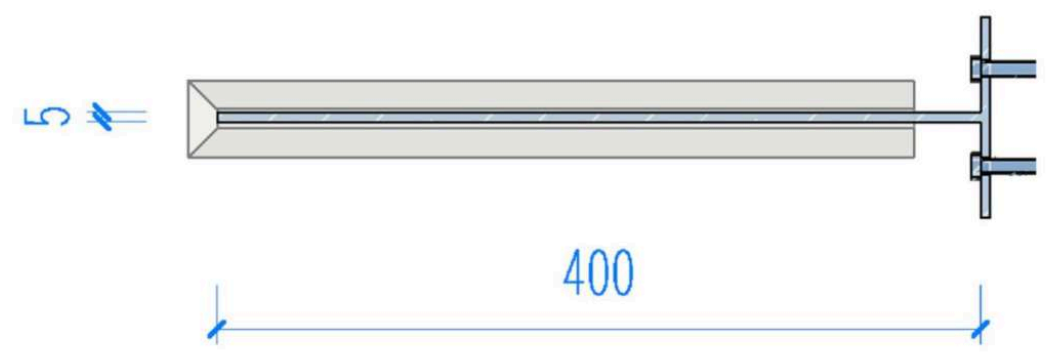

剖面视图

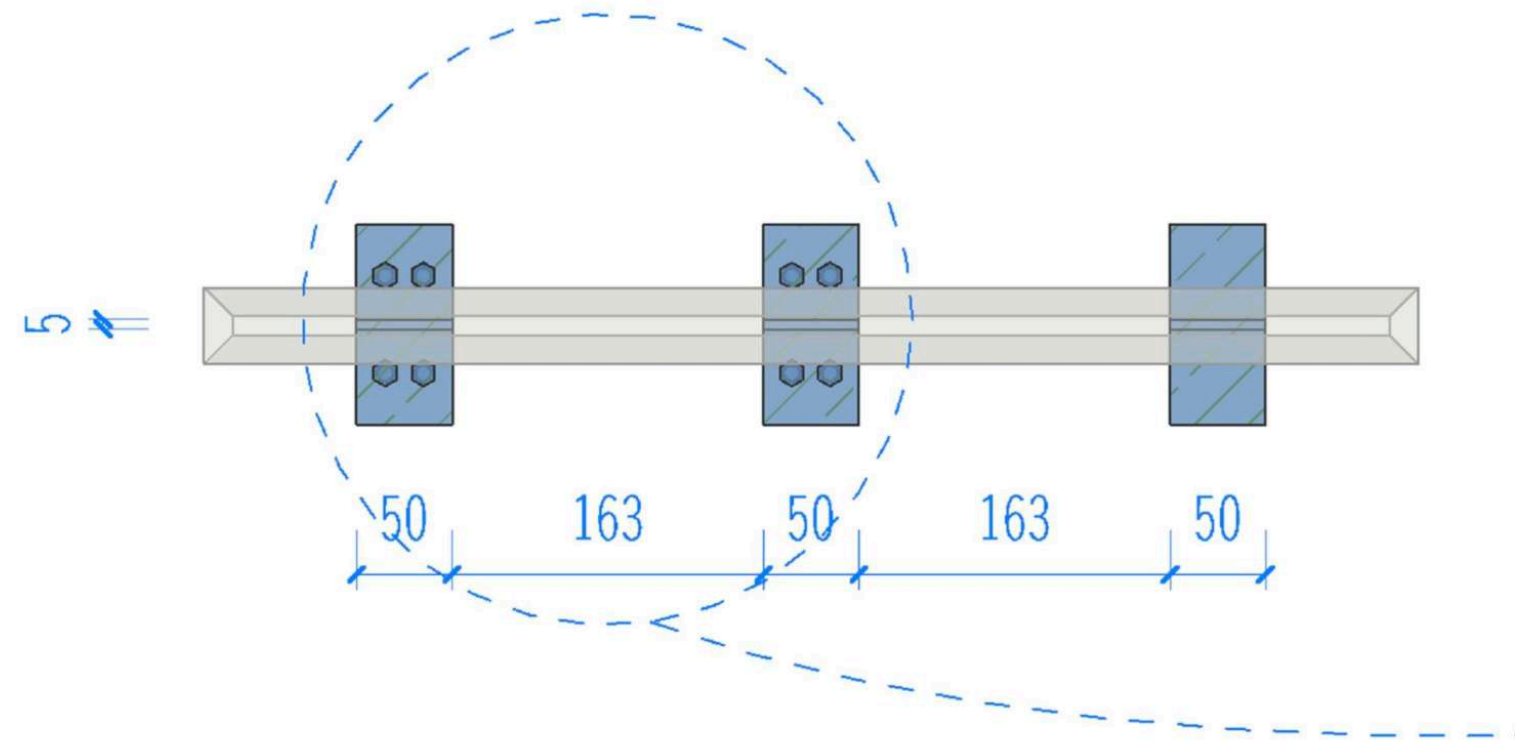
5
50
163
50
163
50

立面视图

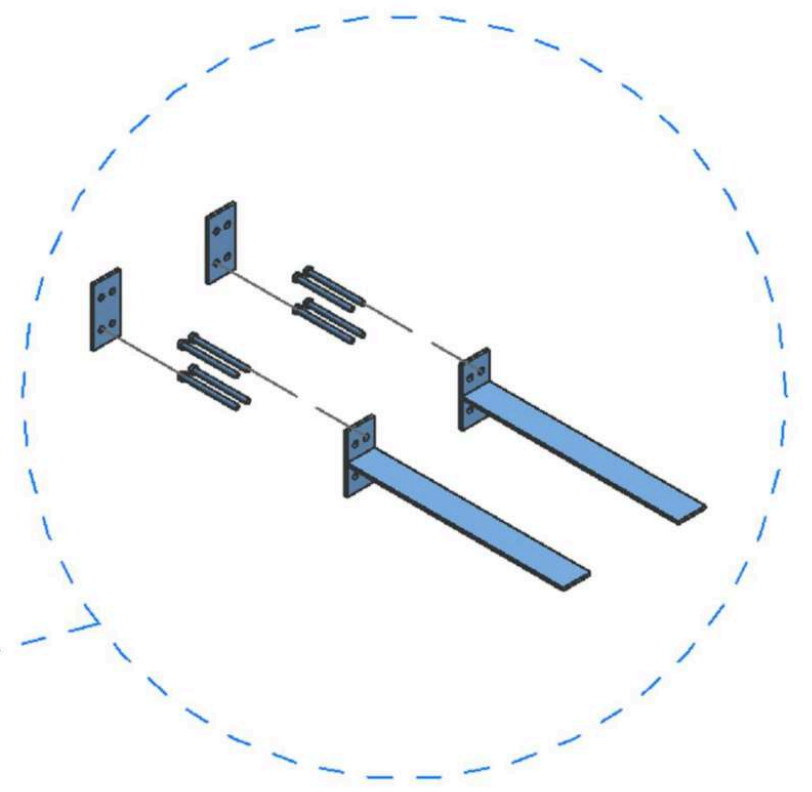

节点图

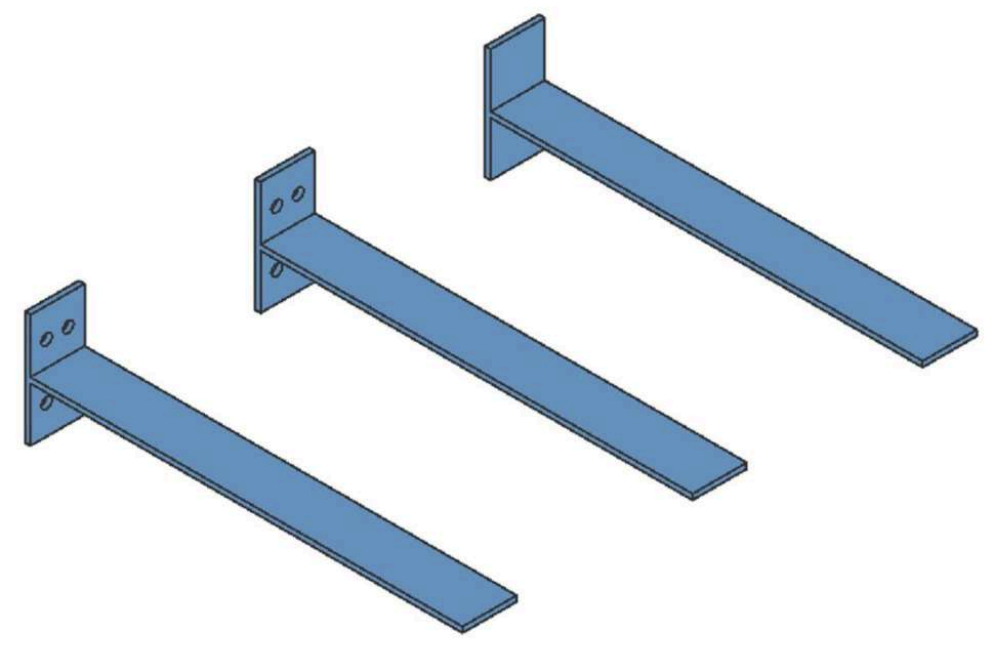

①

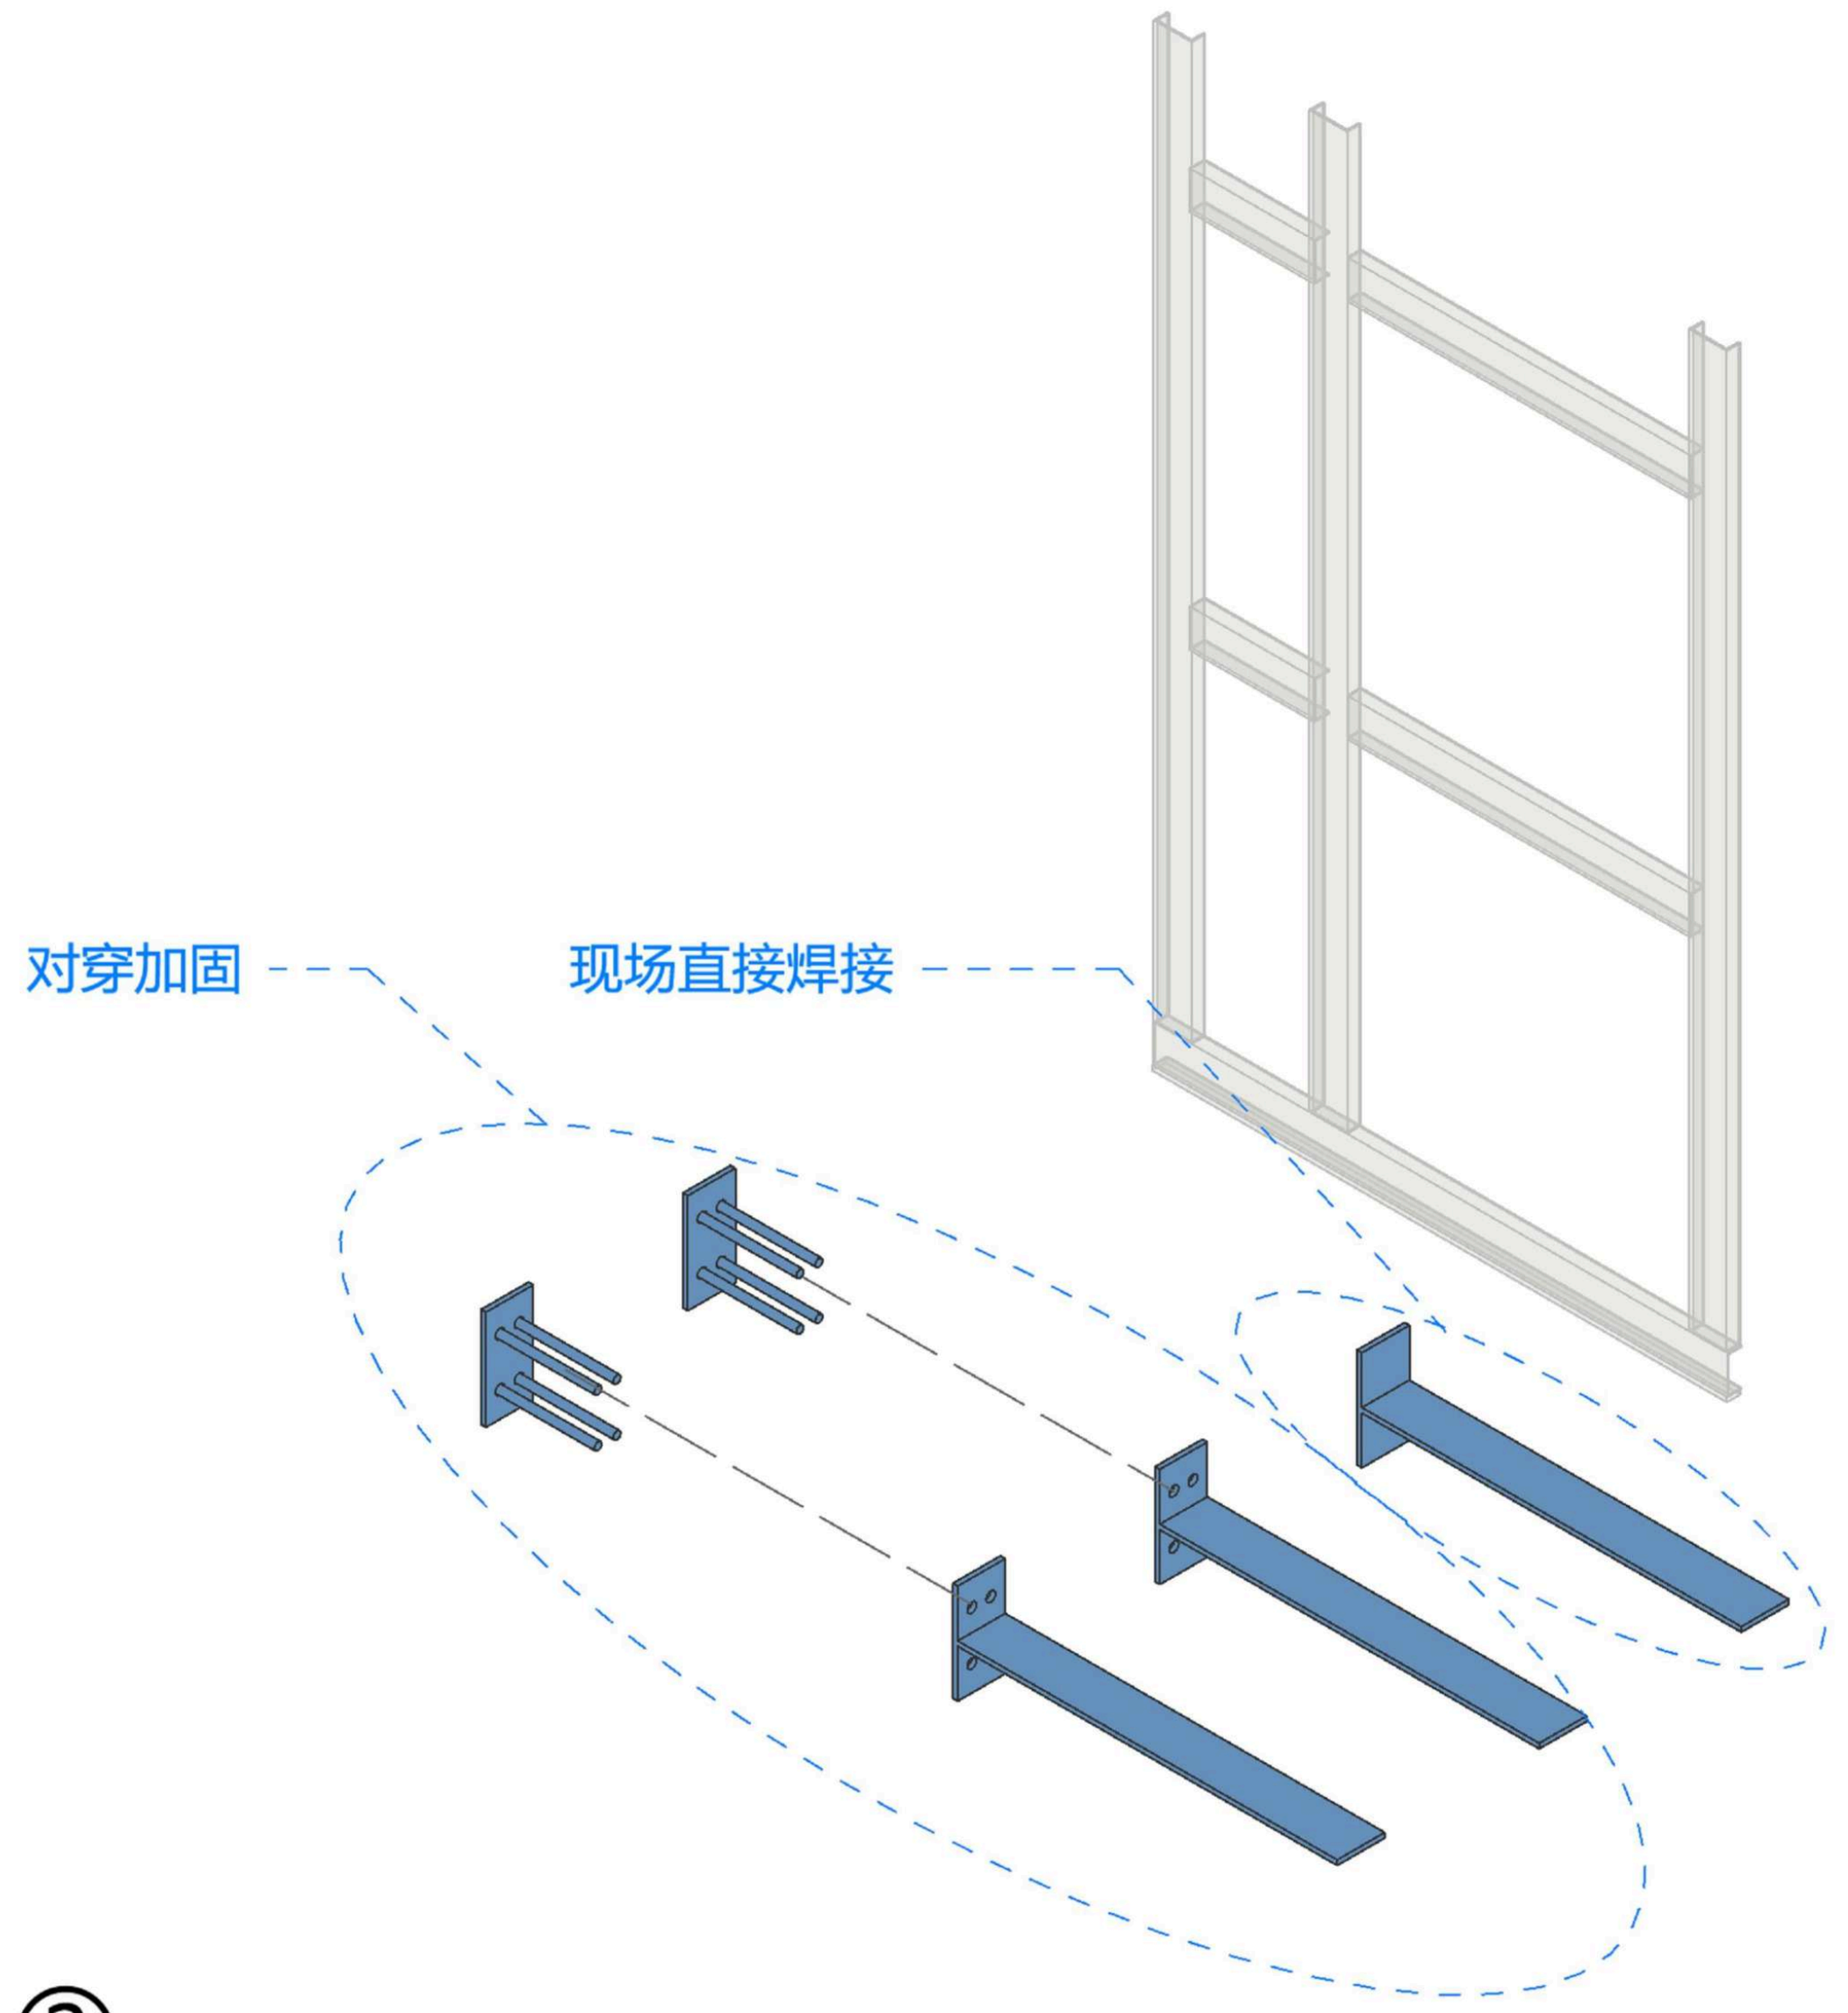
对穿加固
现场直接焊接

②

③

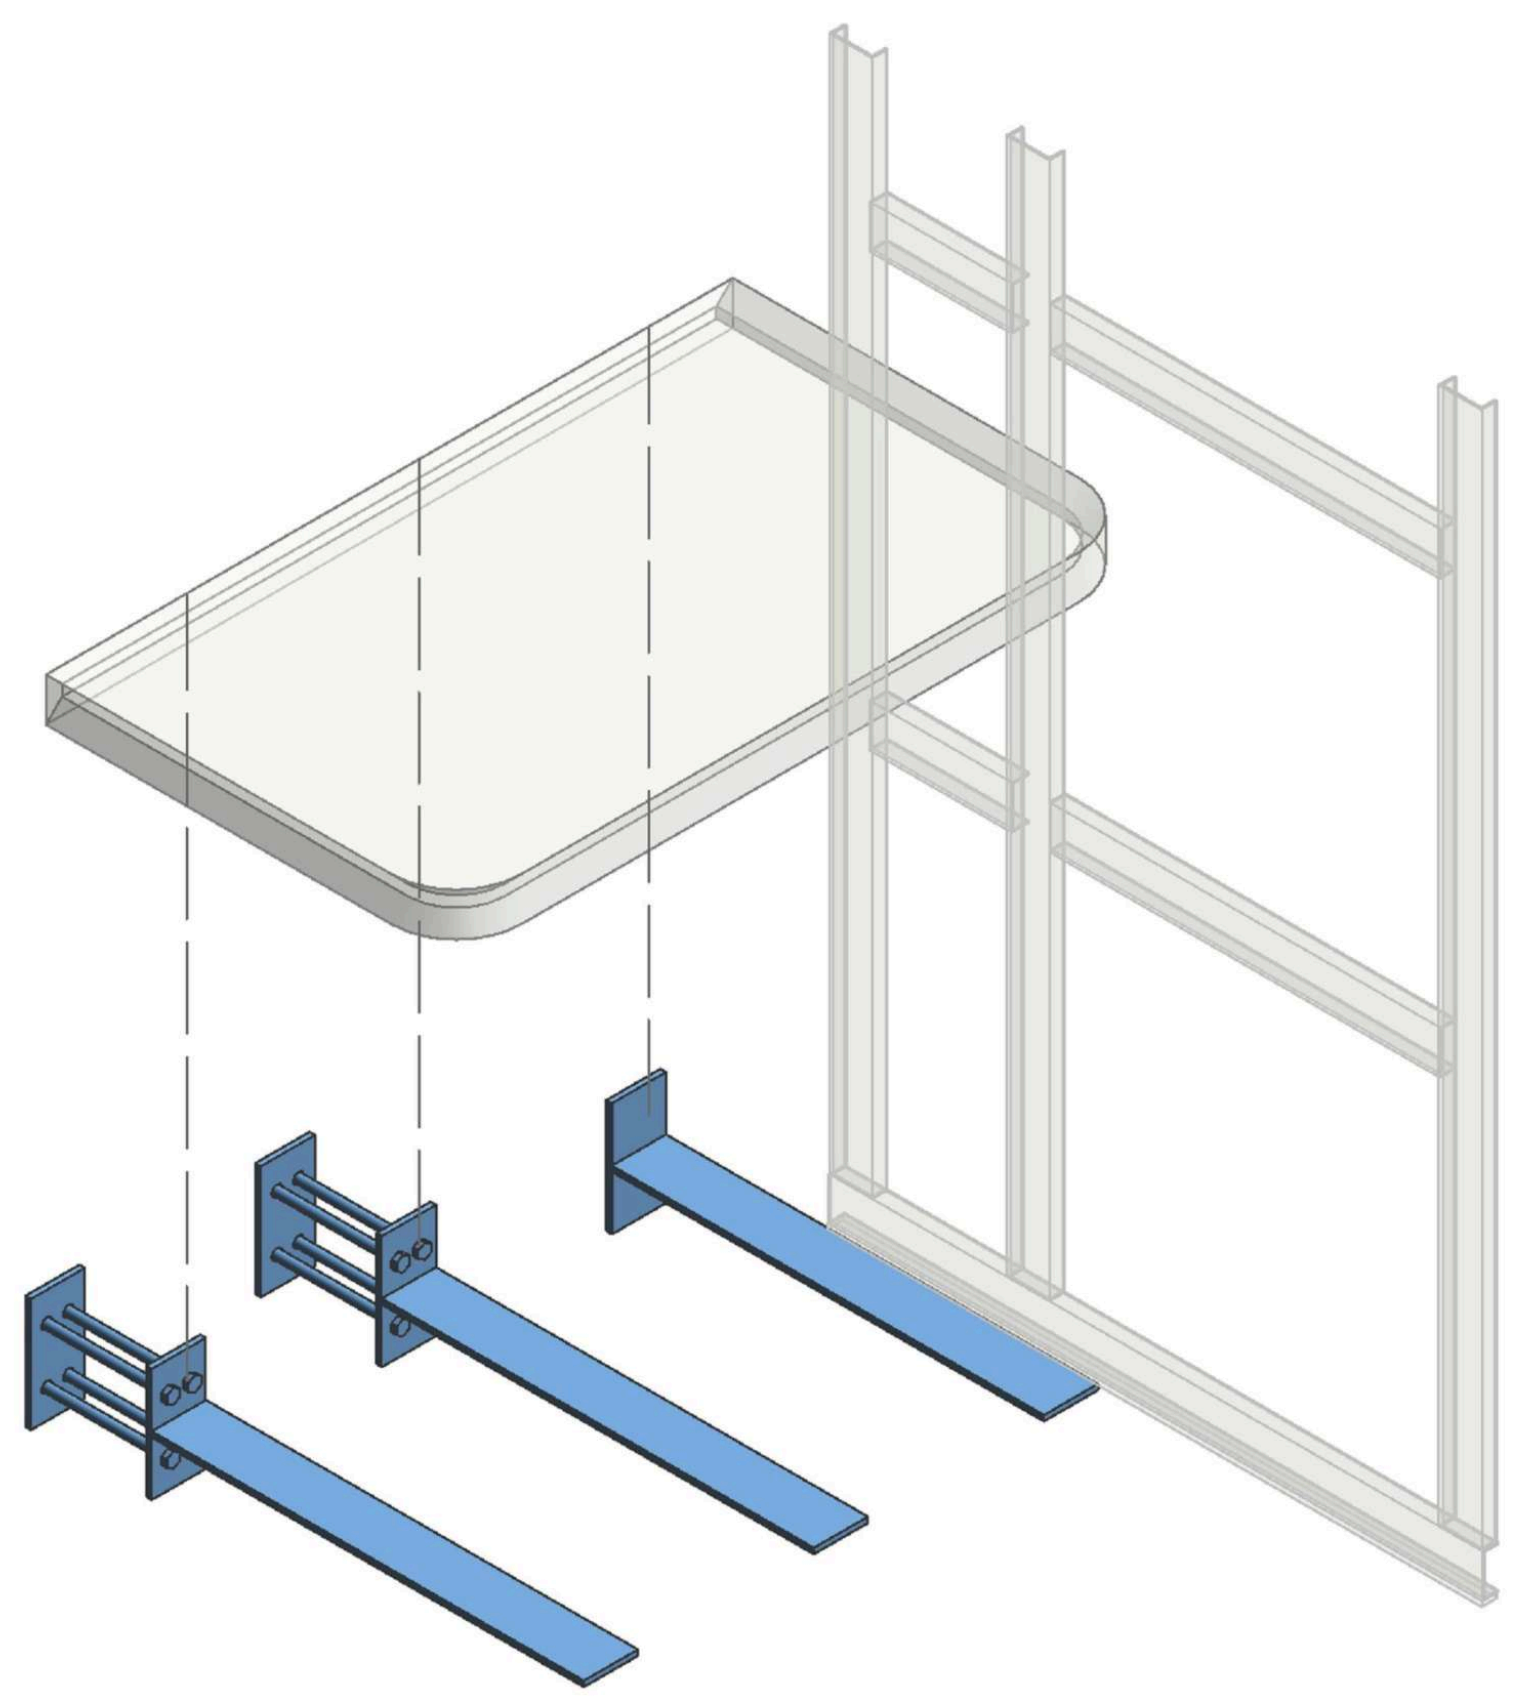

④

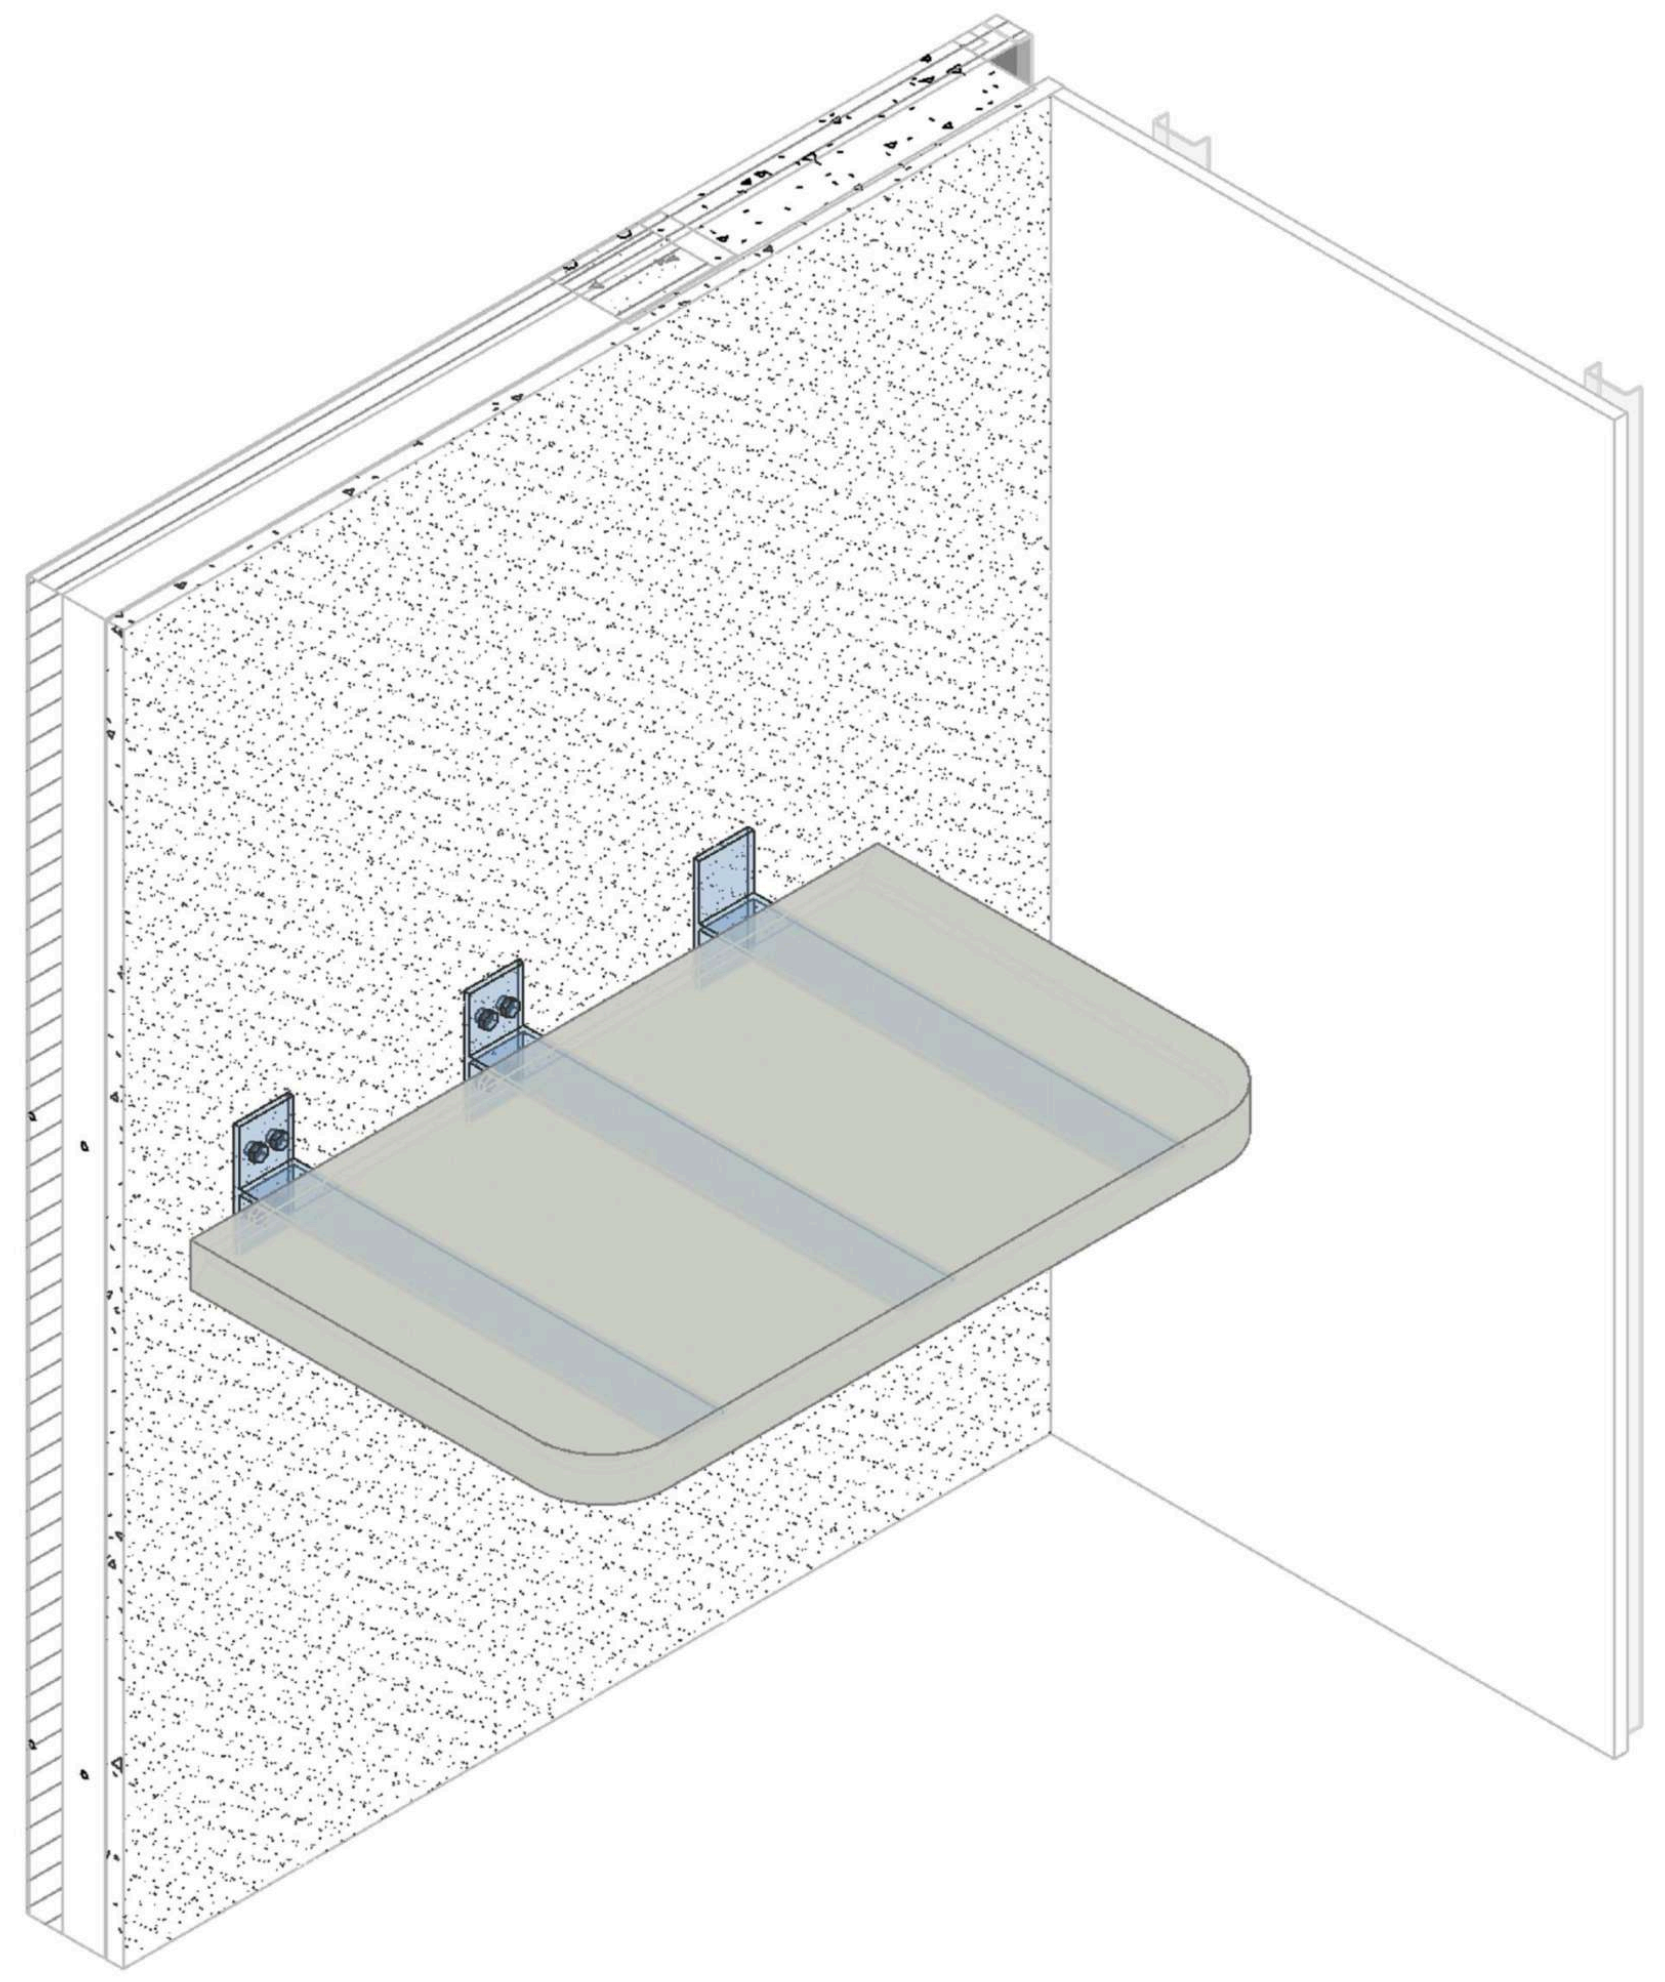

图例A
LEGEND A

编号	图例	说明
1		原始钢架
2		螺栓
3		钢片
4		角铁挑件
5	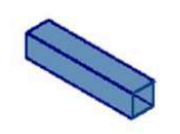	钢架
6	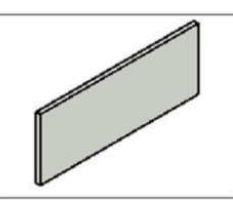	石材

盖章

注释
Notes

1.本图纸如与现场尺寸有误，请施工人员与项目负责人联系。
2.施工前施工人员应认真查阅此图，如有不明确尺寸，按现场测量为准。
3.本图纸必须经甲乙双方认可并签字方可作为施工依据。

日期
Date 04/24/26

修订
Revision

△1

项目
Project
潮映华岸府3-801

比例
Scale

衣帽间洗手台石材钢架

图纸编号
Drawing No.
ST-08

项目编号
Project No.

©2025

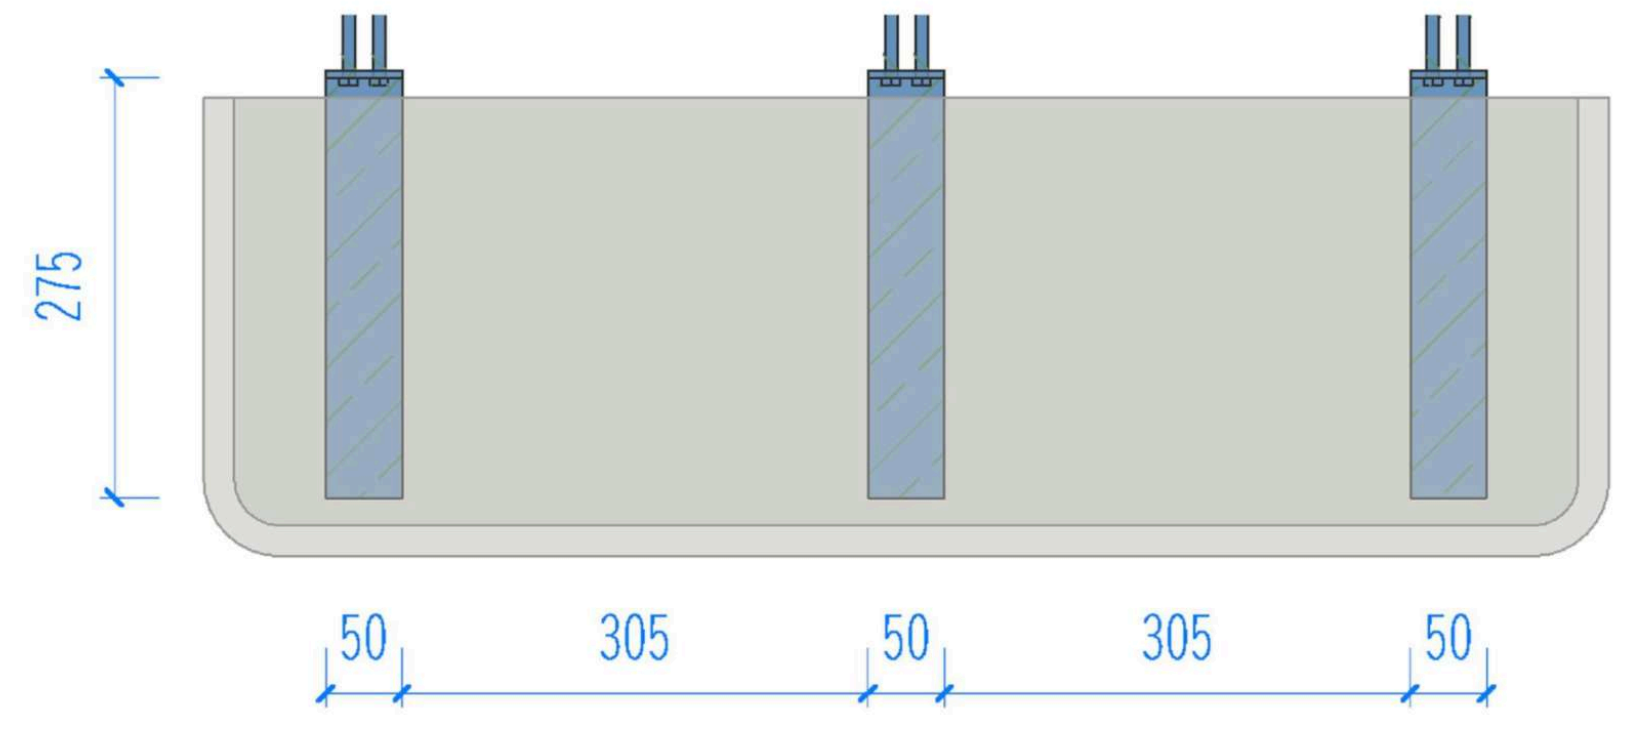
275
50
305
50
305
50

平面视图

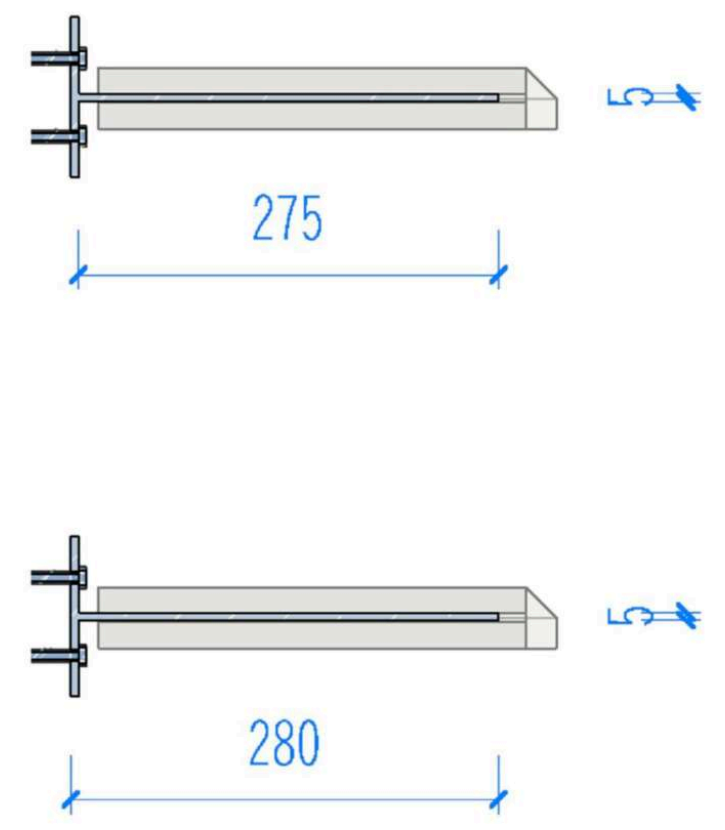

剖面视图

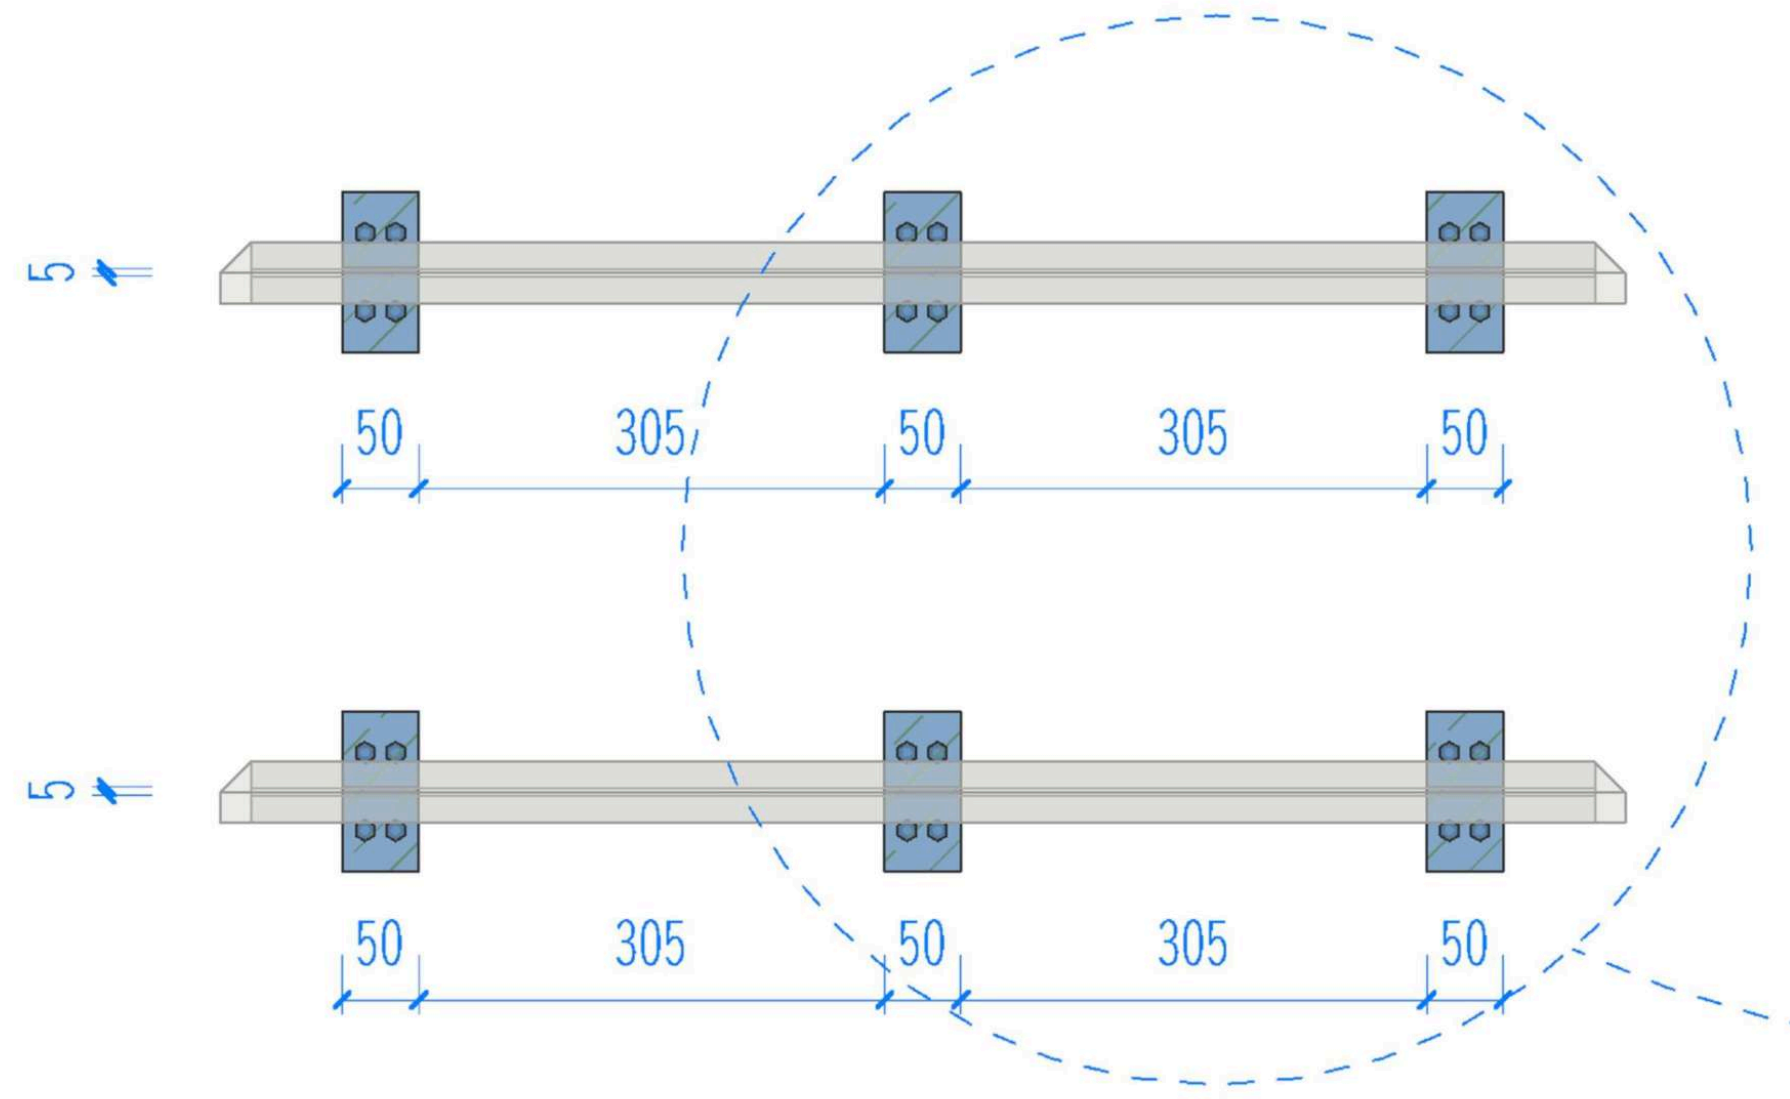
5
50
305
50
305
50
5
50
305
50
305
50

立面视图

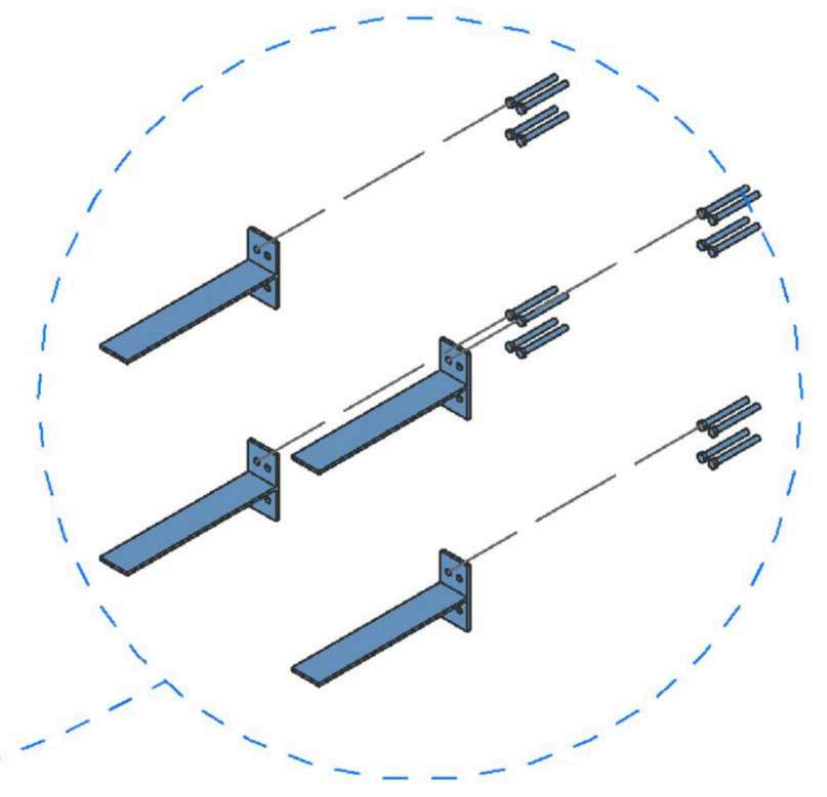

节点图

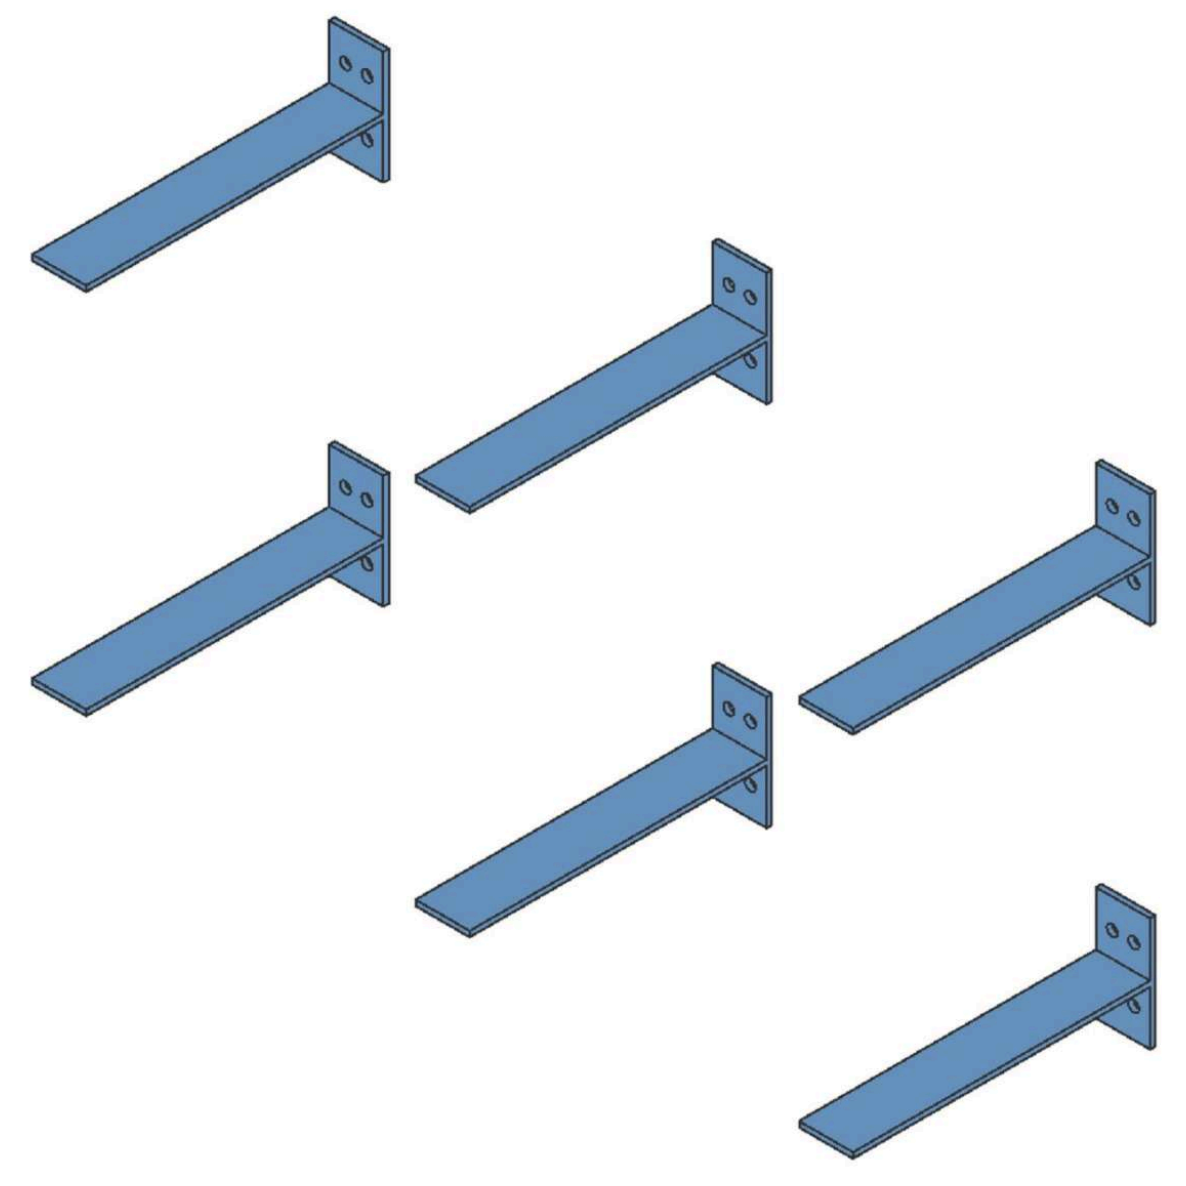

①

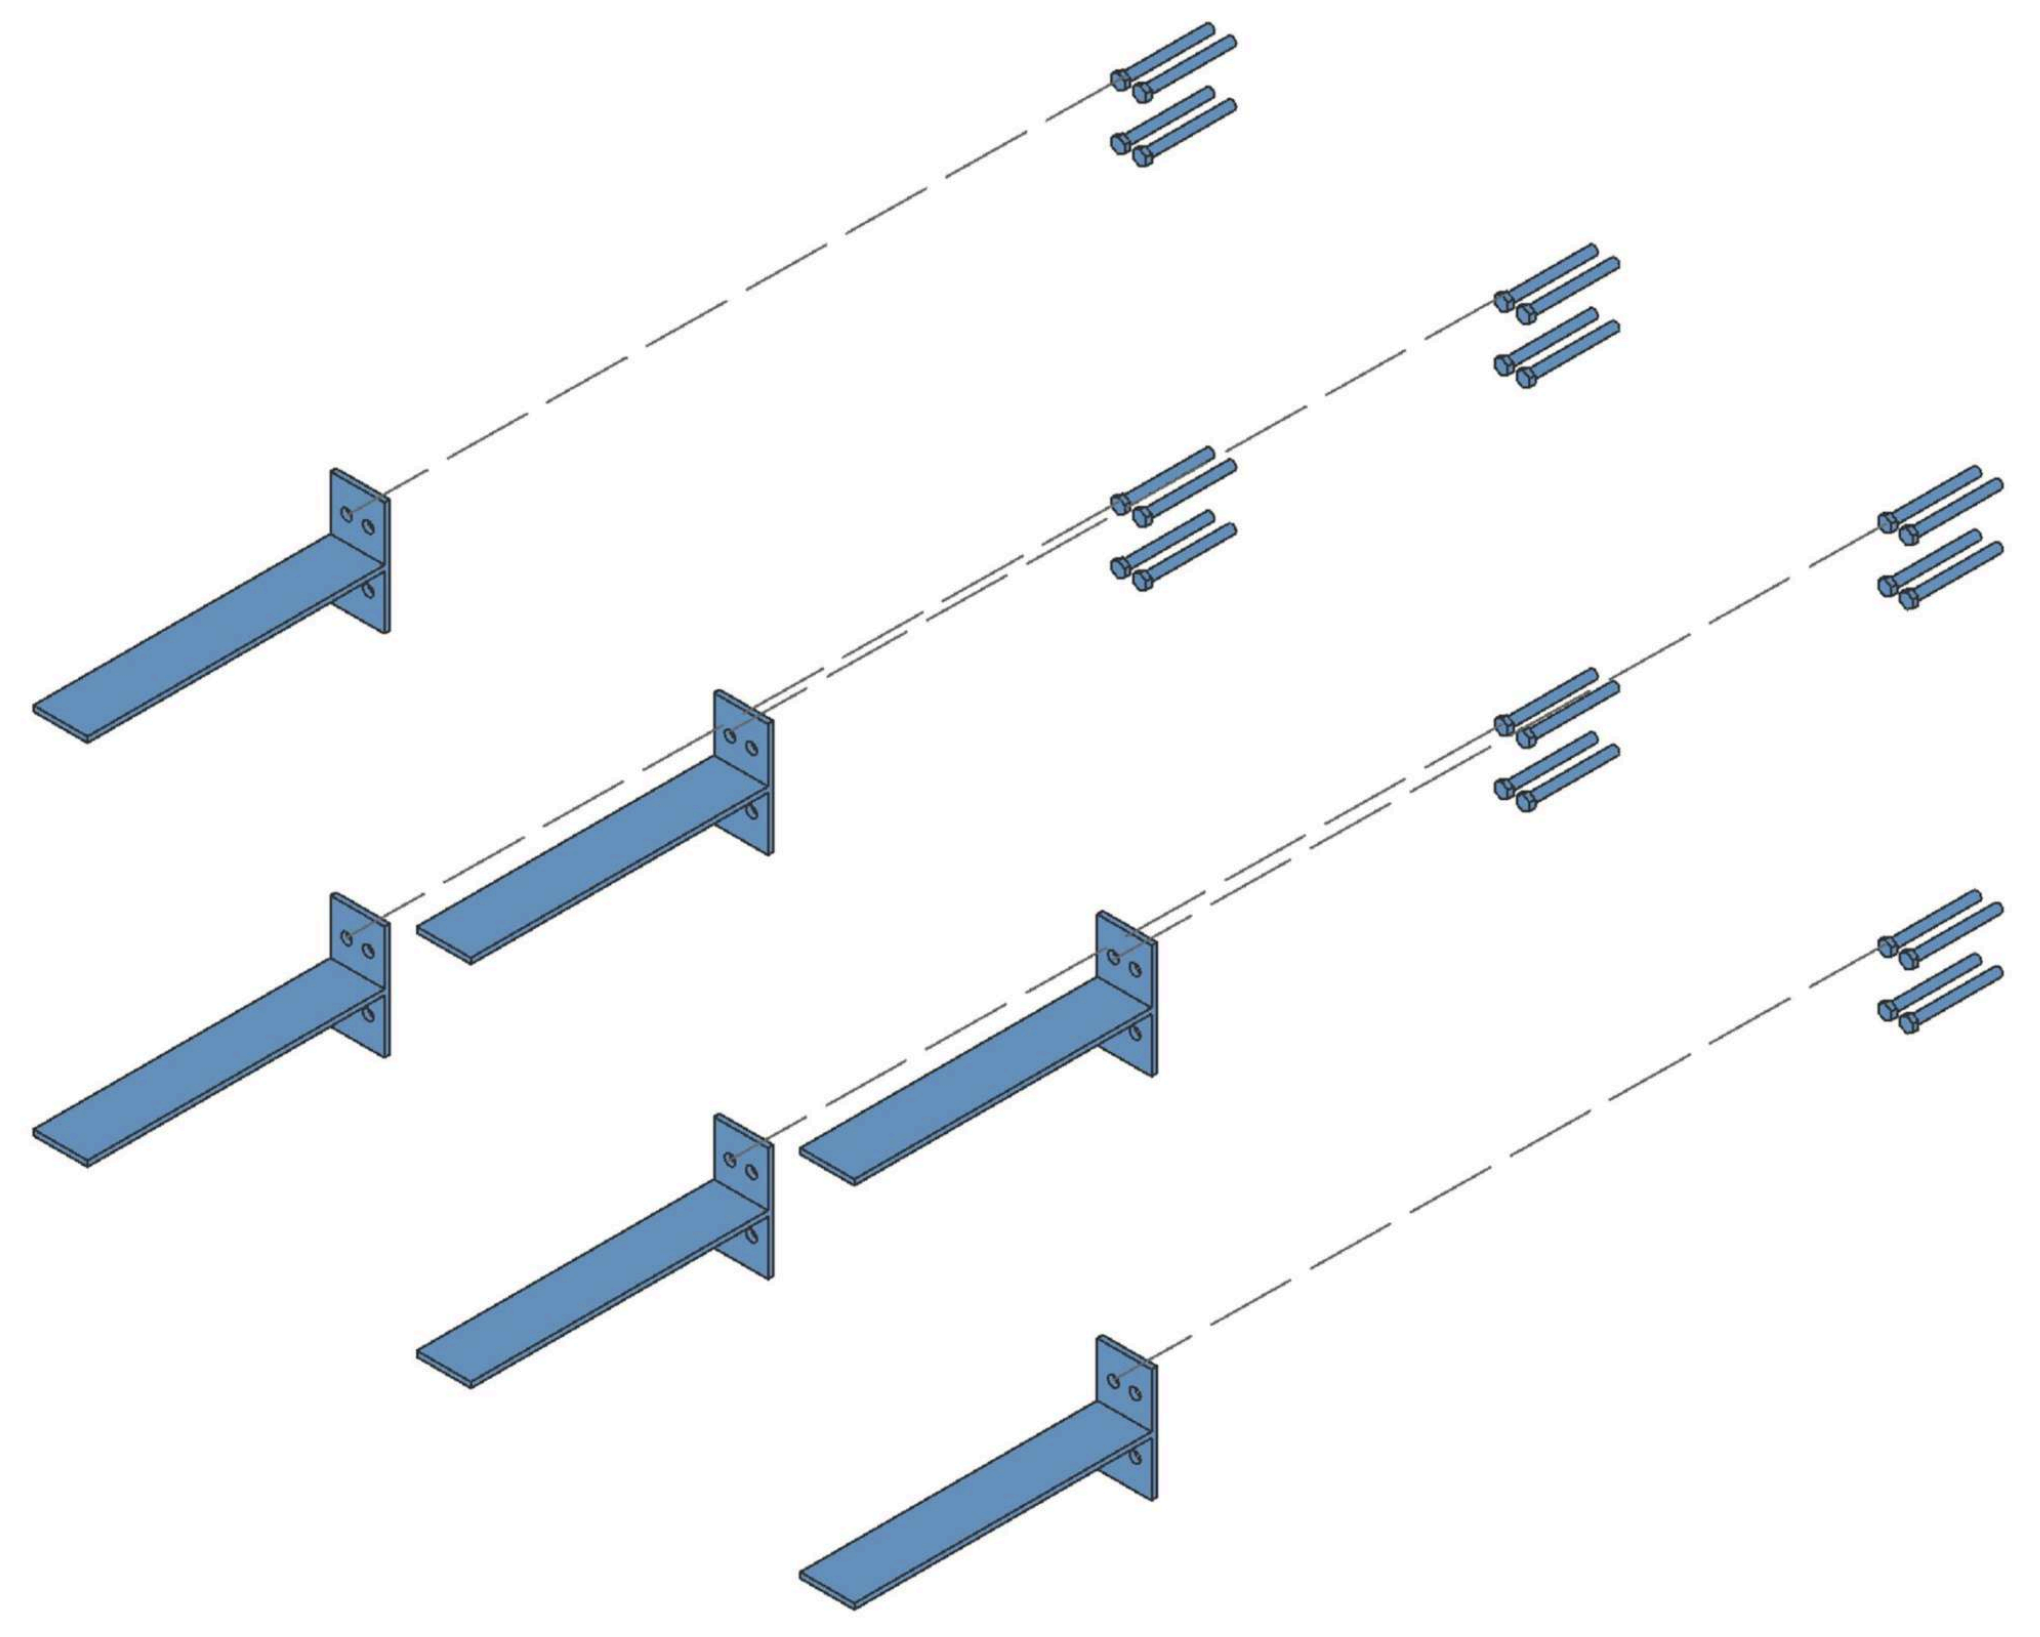

②

③

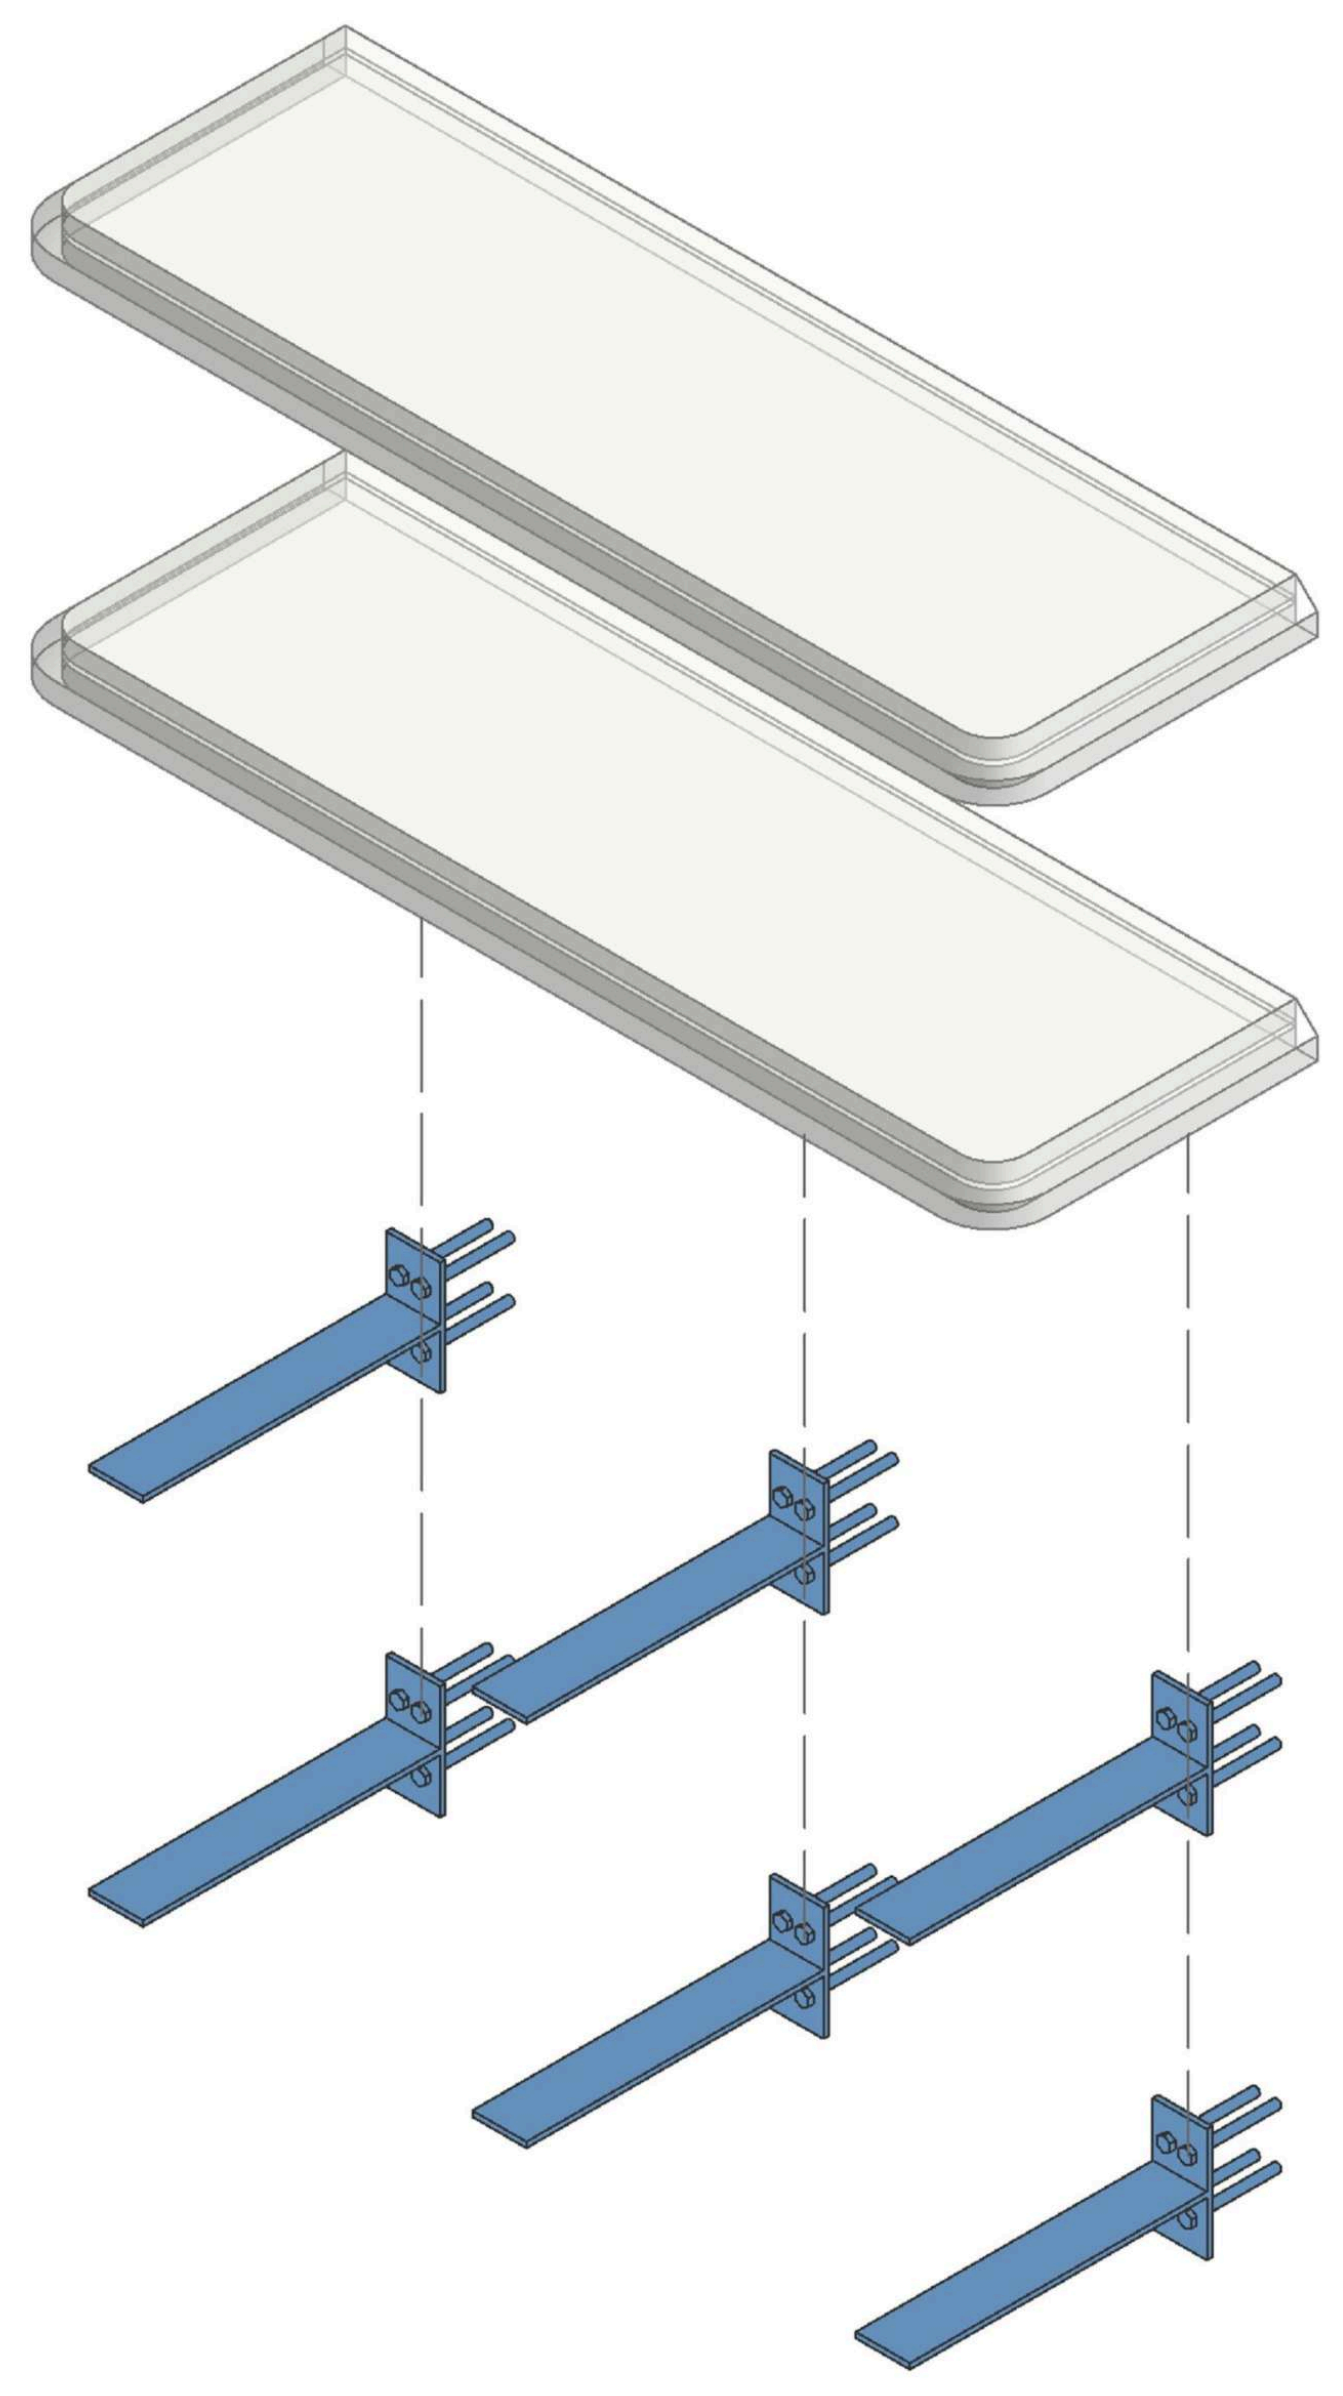

④

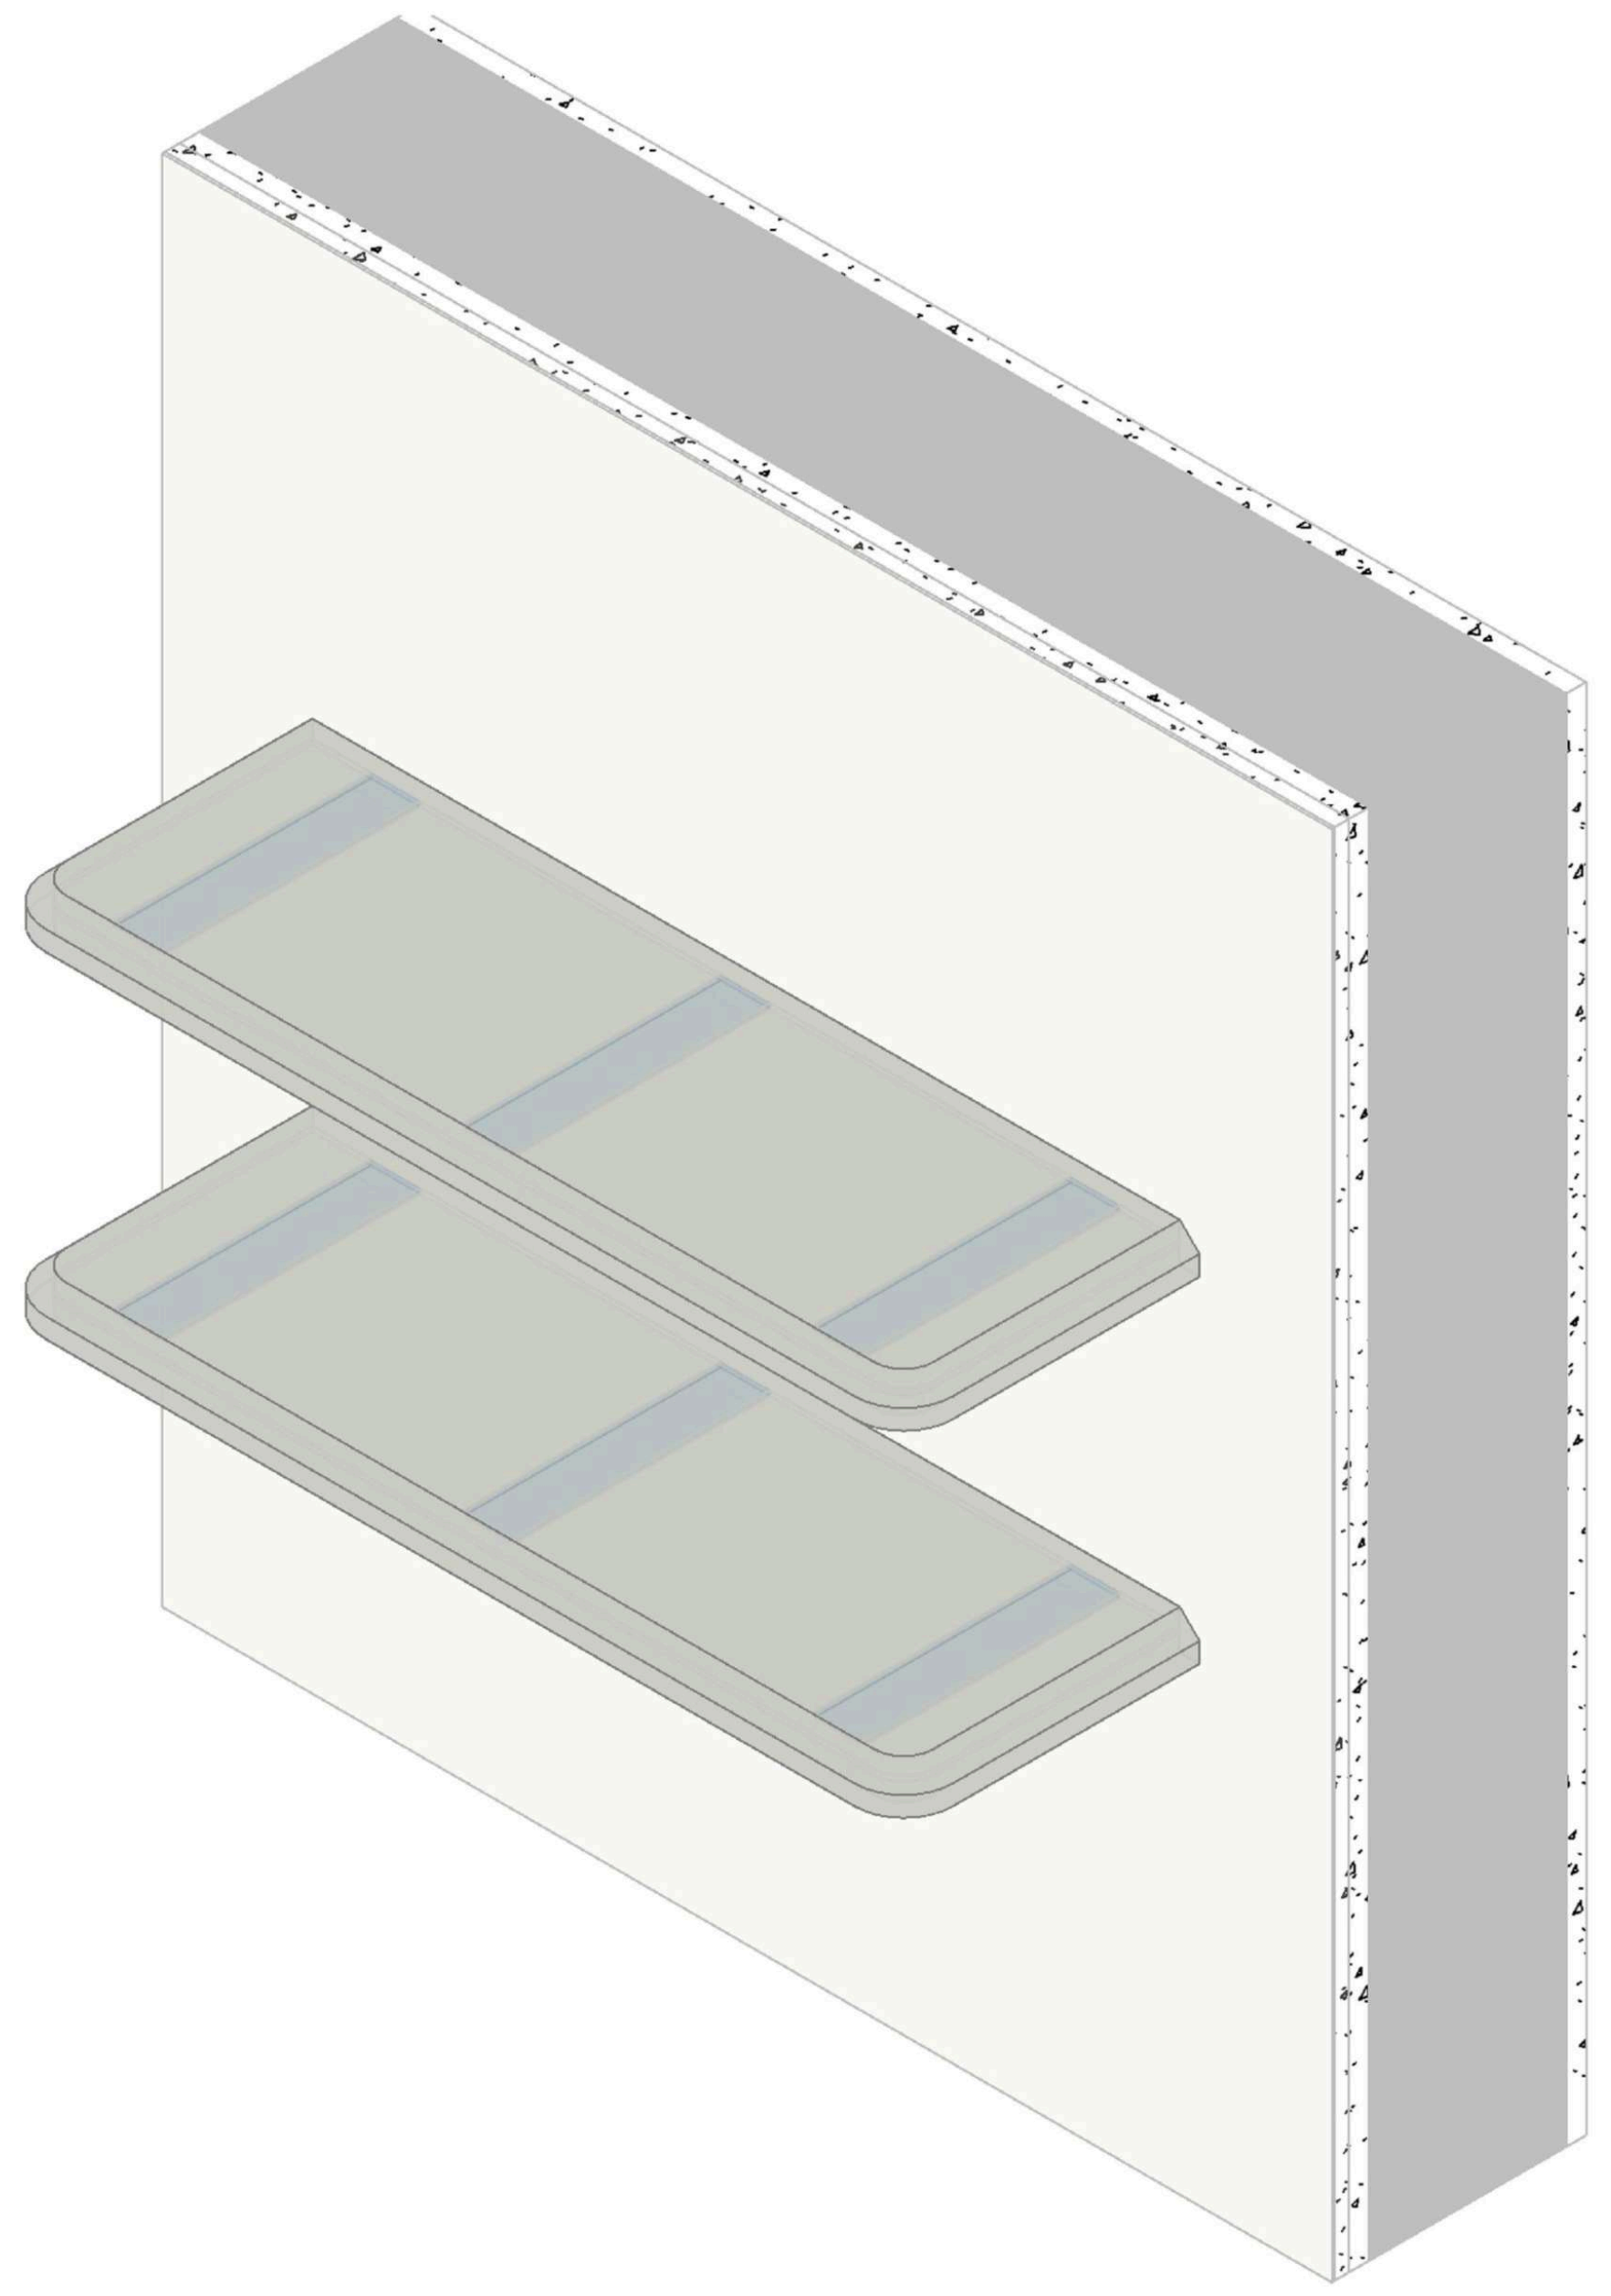

图例A
LEGEND A

编号	图例	说明
1	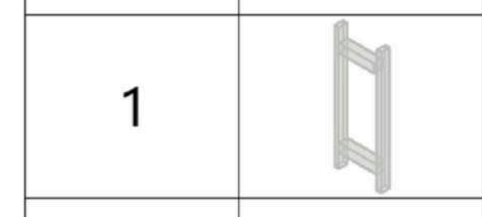	原始钢架
2		螺栓
3		钢片
4		角铁挑件
5	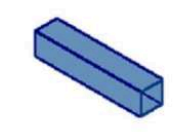	钢架
6	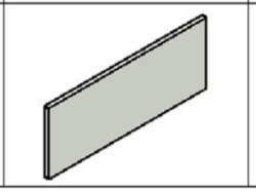	石材

盖章

注释
Notes
1.本图纸如与现场尺寸有误，请施工人员与项目负责人联系。
2.施工前施工人员应认真查阅此图，如有不明确尺寸，按现场测量为准。
3.本图纸必须经甲乙双方认可并签字方可作为施工依据。

日期
Date 04/24/26

修订
Revision
1

项目
Project
潮映华岸府3-801

比例
Scale
客卧台面石材钢架

图纸编号
Drawing No.
ST-09

项目编号
Project No.
©2025

1

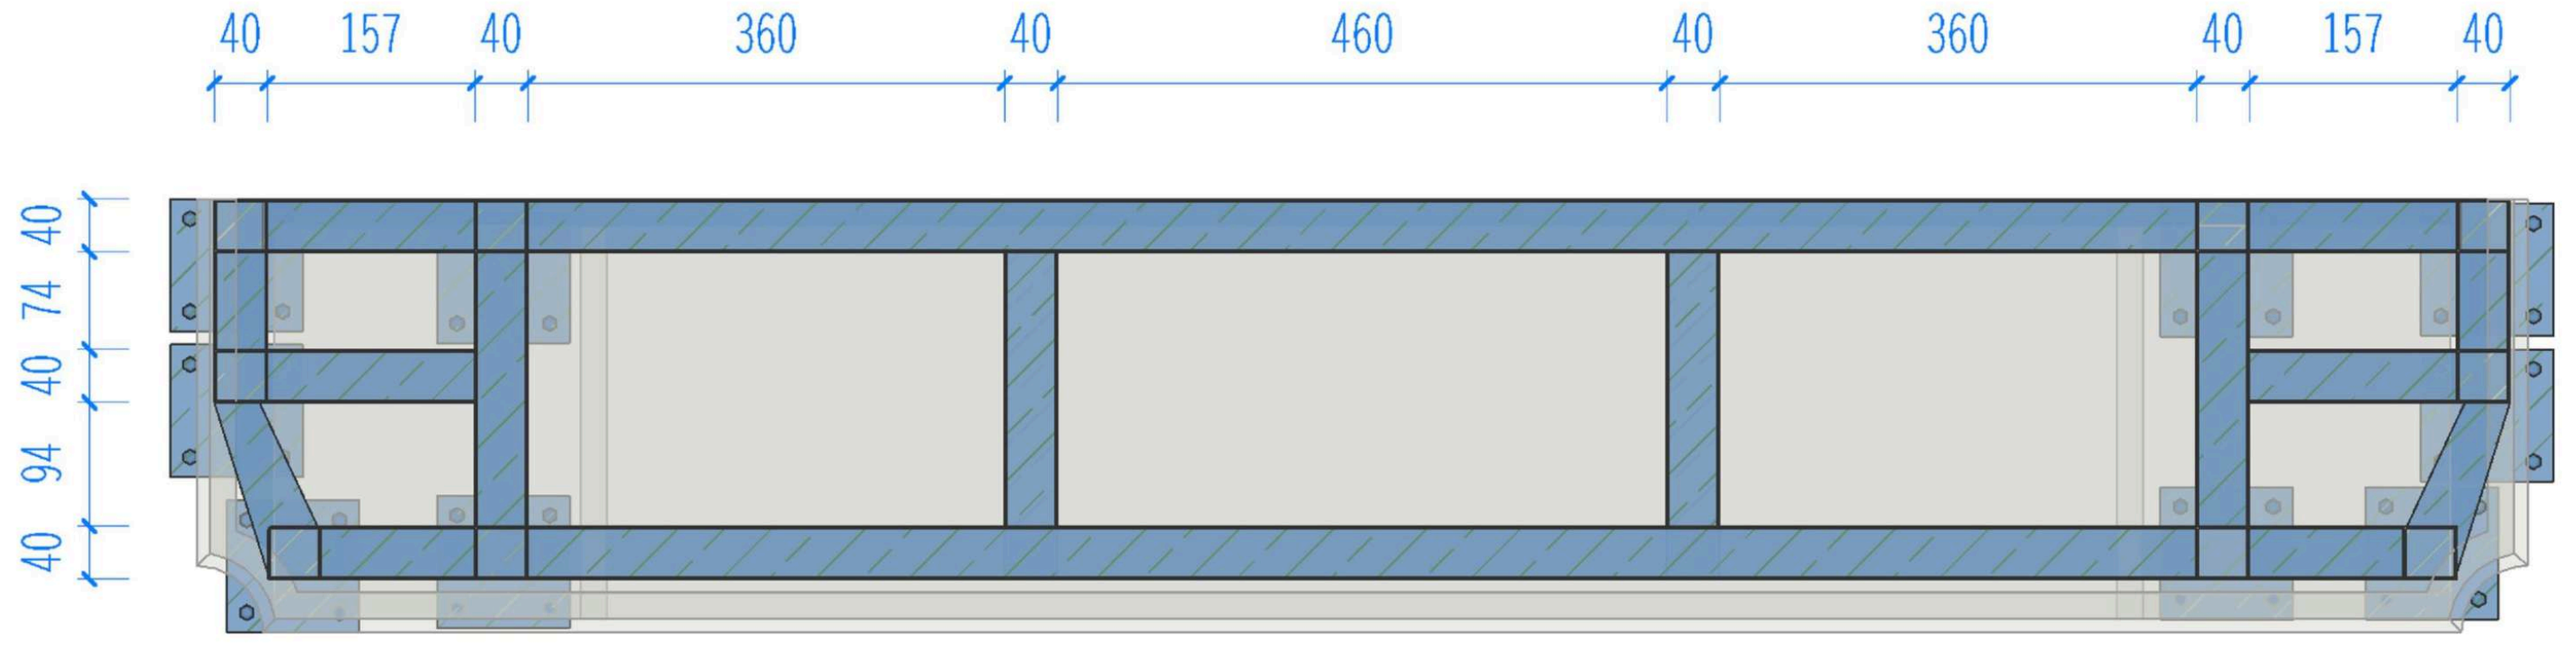
40
157
40
360
40
460
40
360
40
157
40
40
74
40
94
40

平面视图

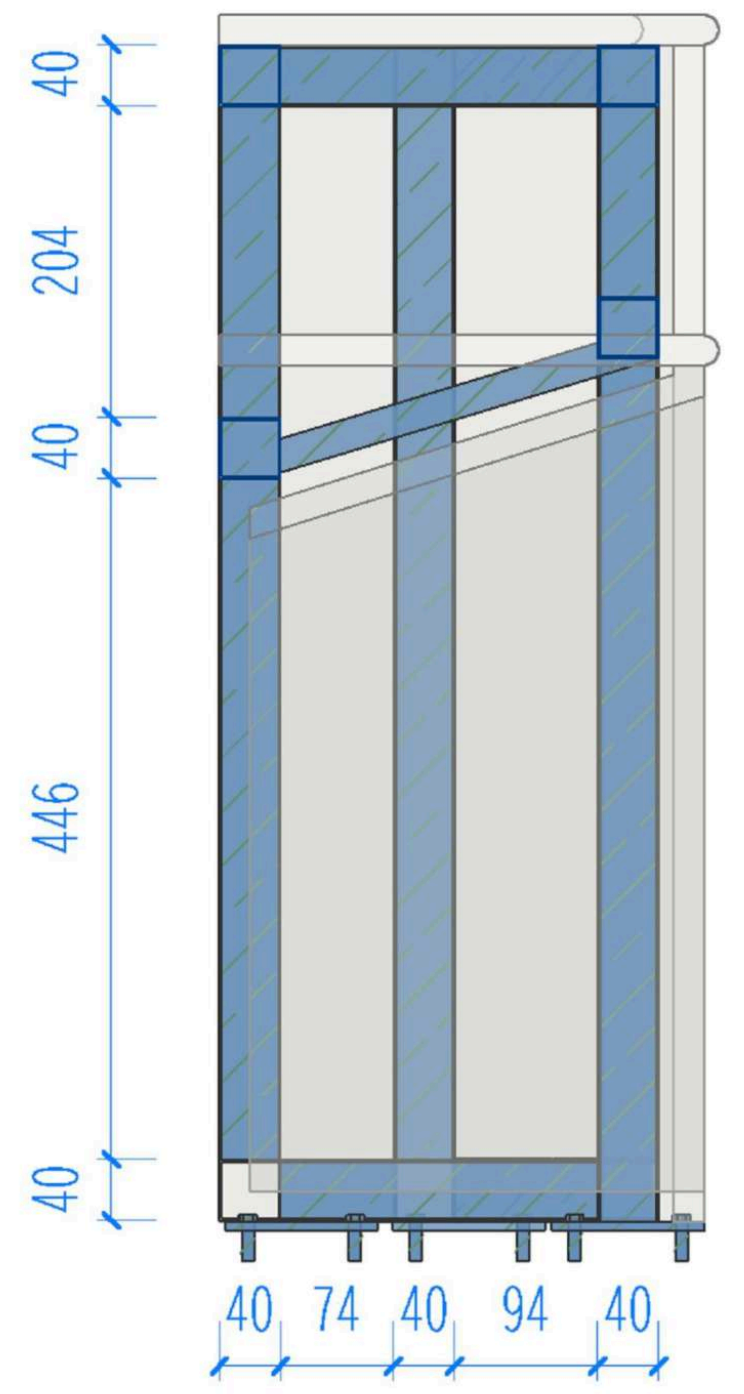
40
204
40
446
40
40
74
40
94
40

剖面视图

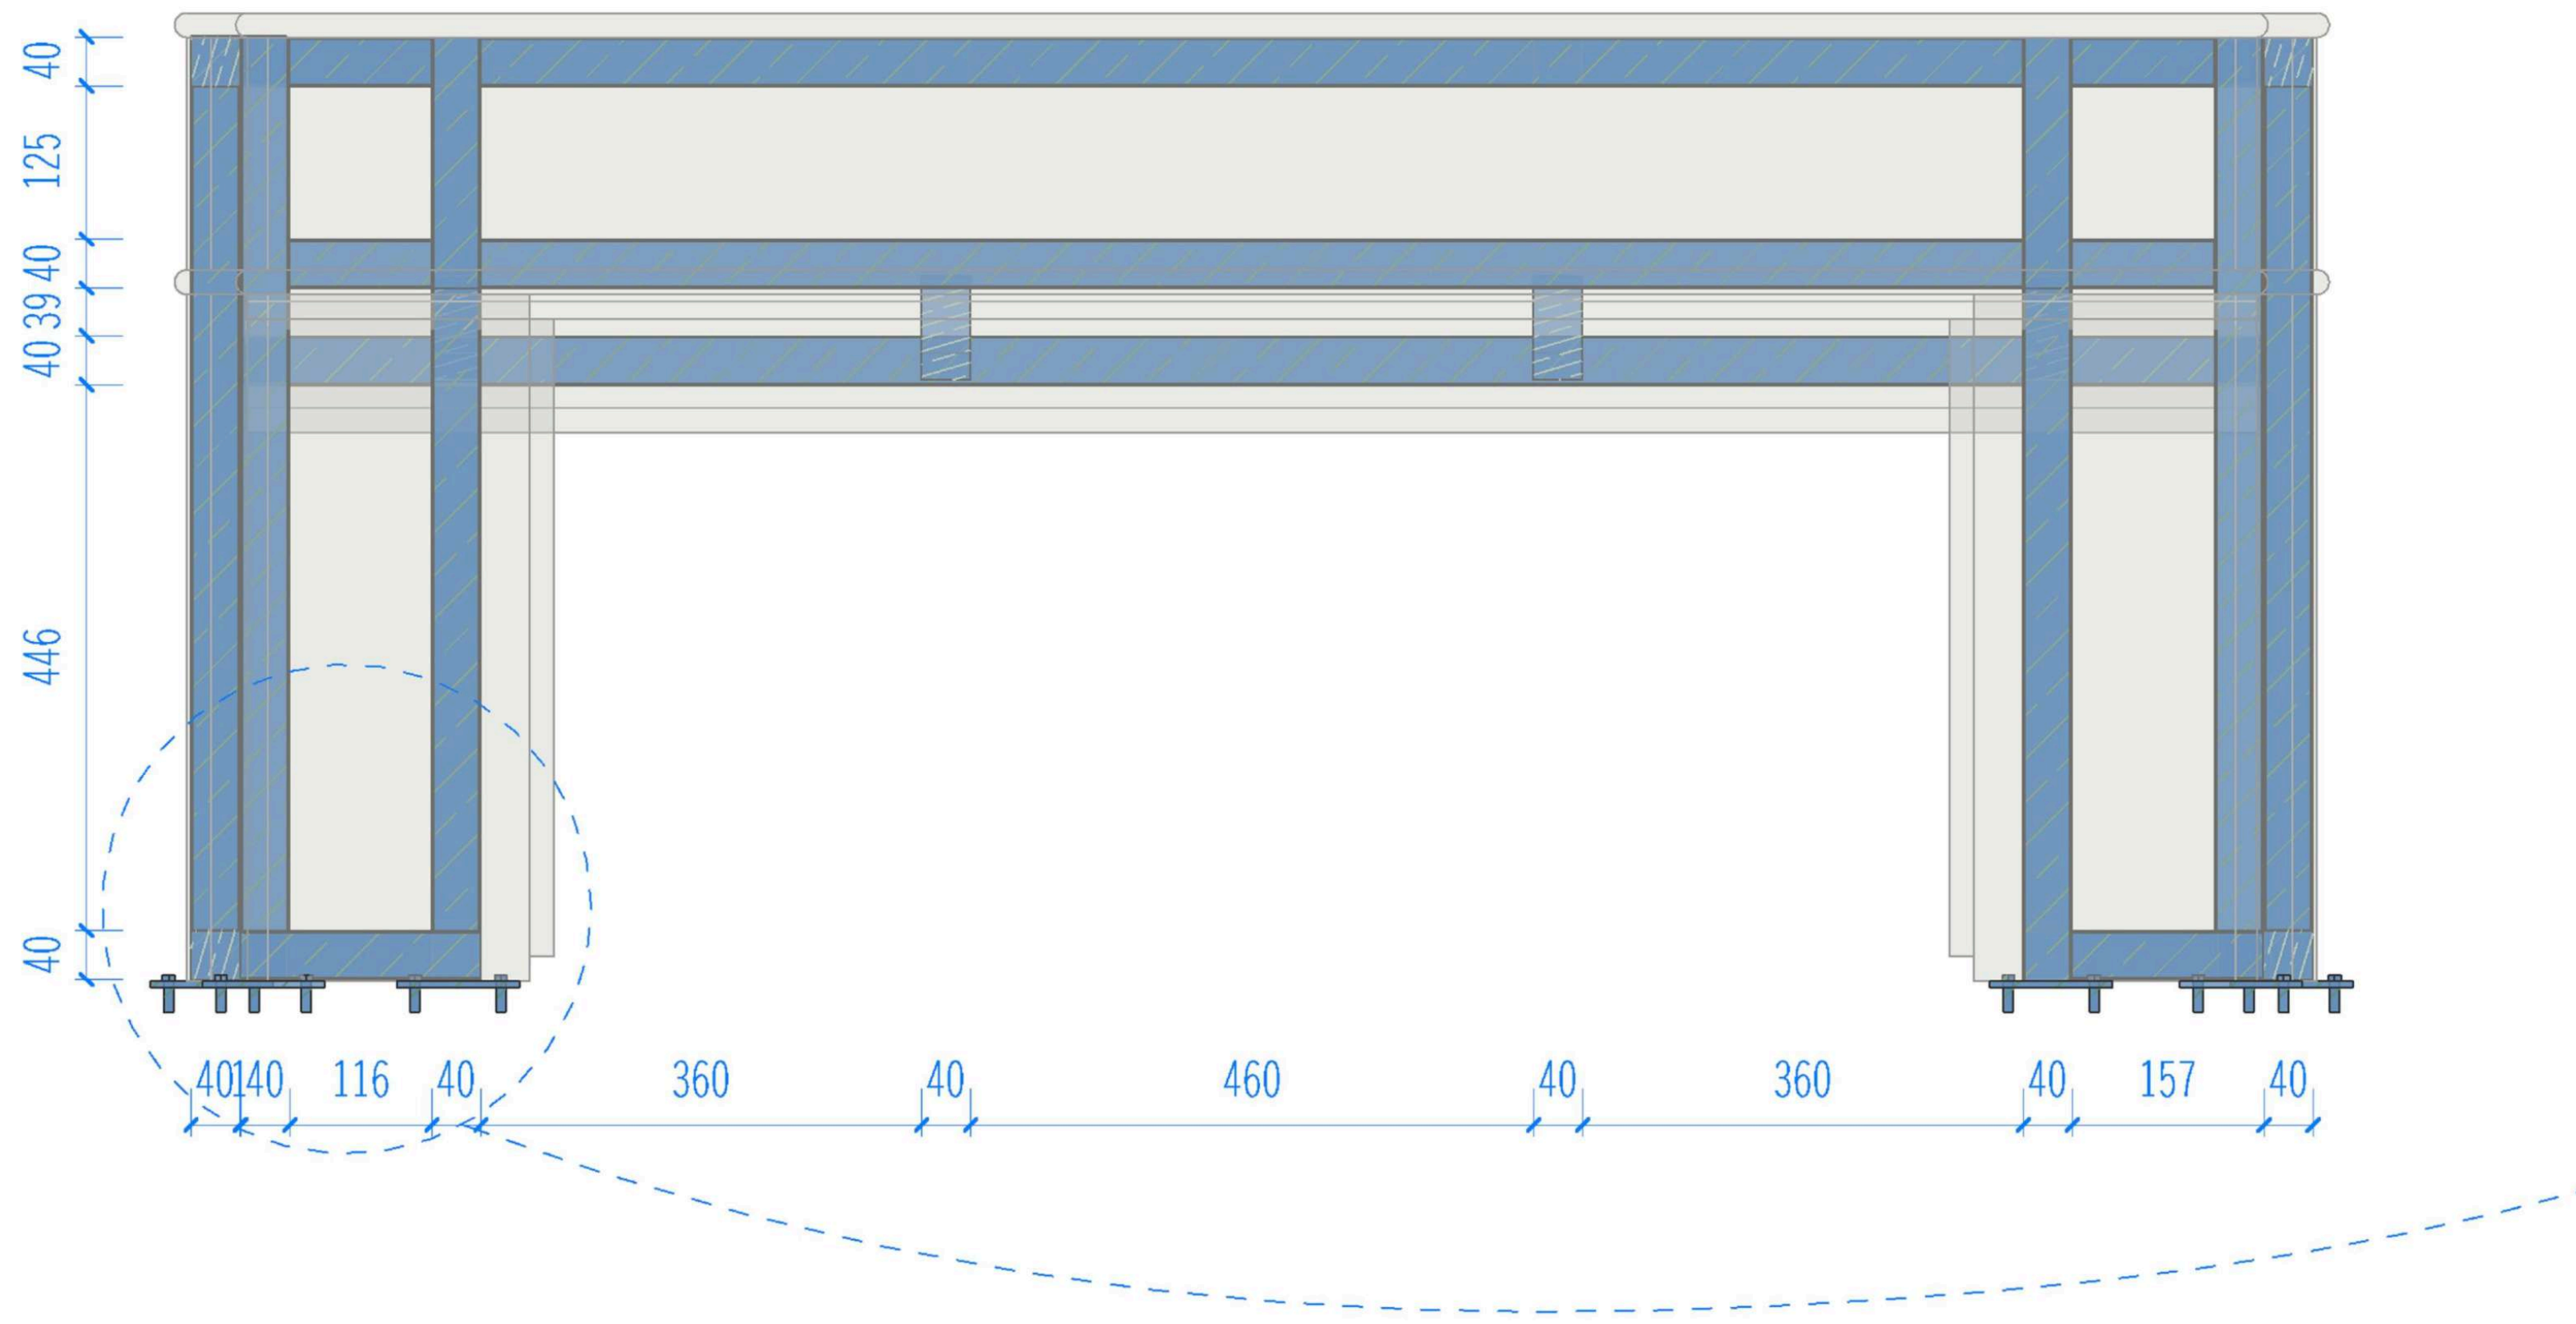
40
125
40
39
40
446
40
40
40
116
40
360
40
460
40
360
40
157
40

立面视图

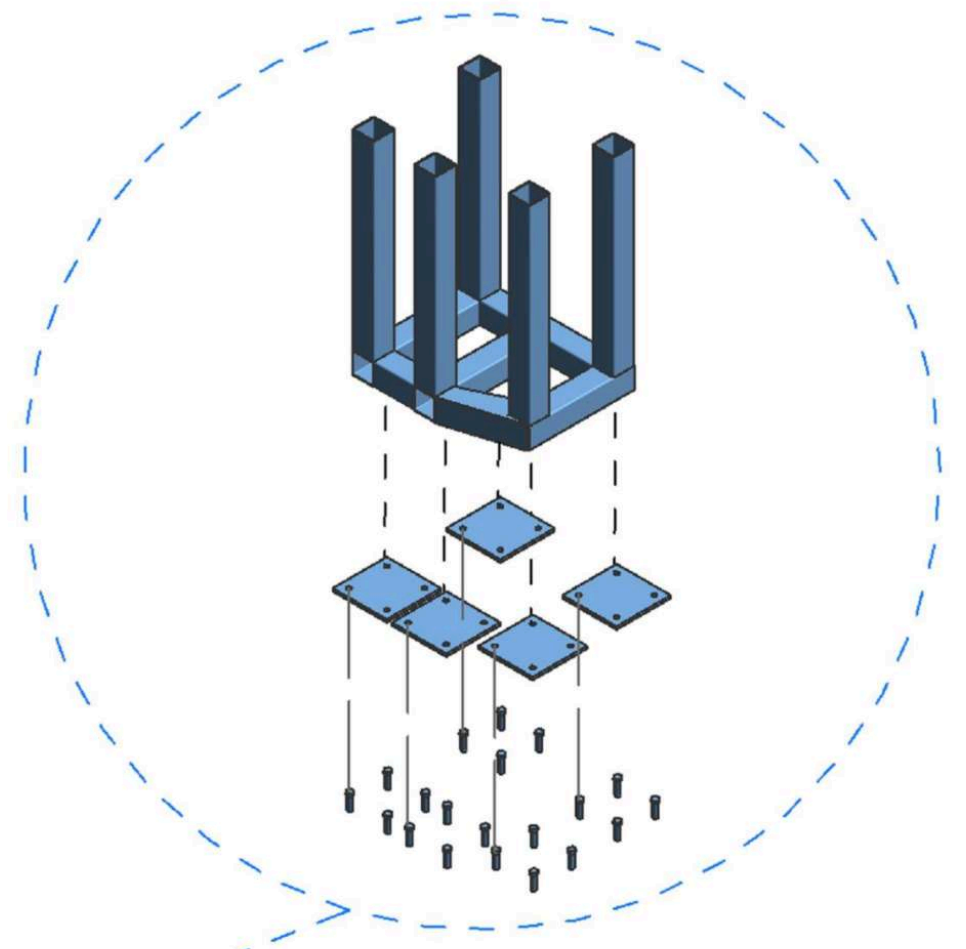

节点图

工厂预制钢架

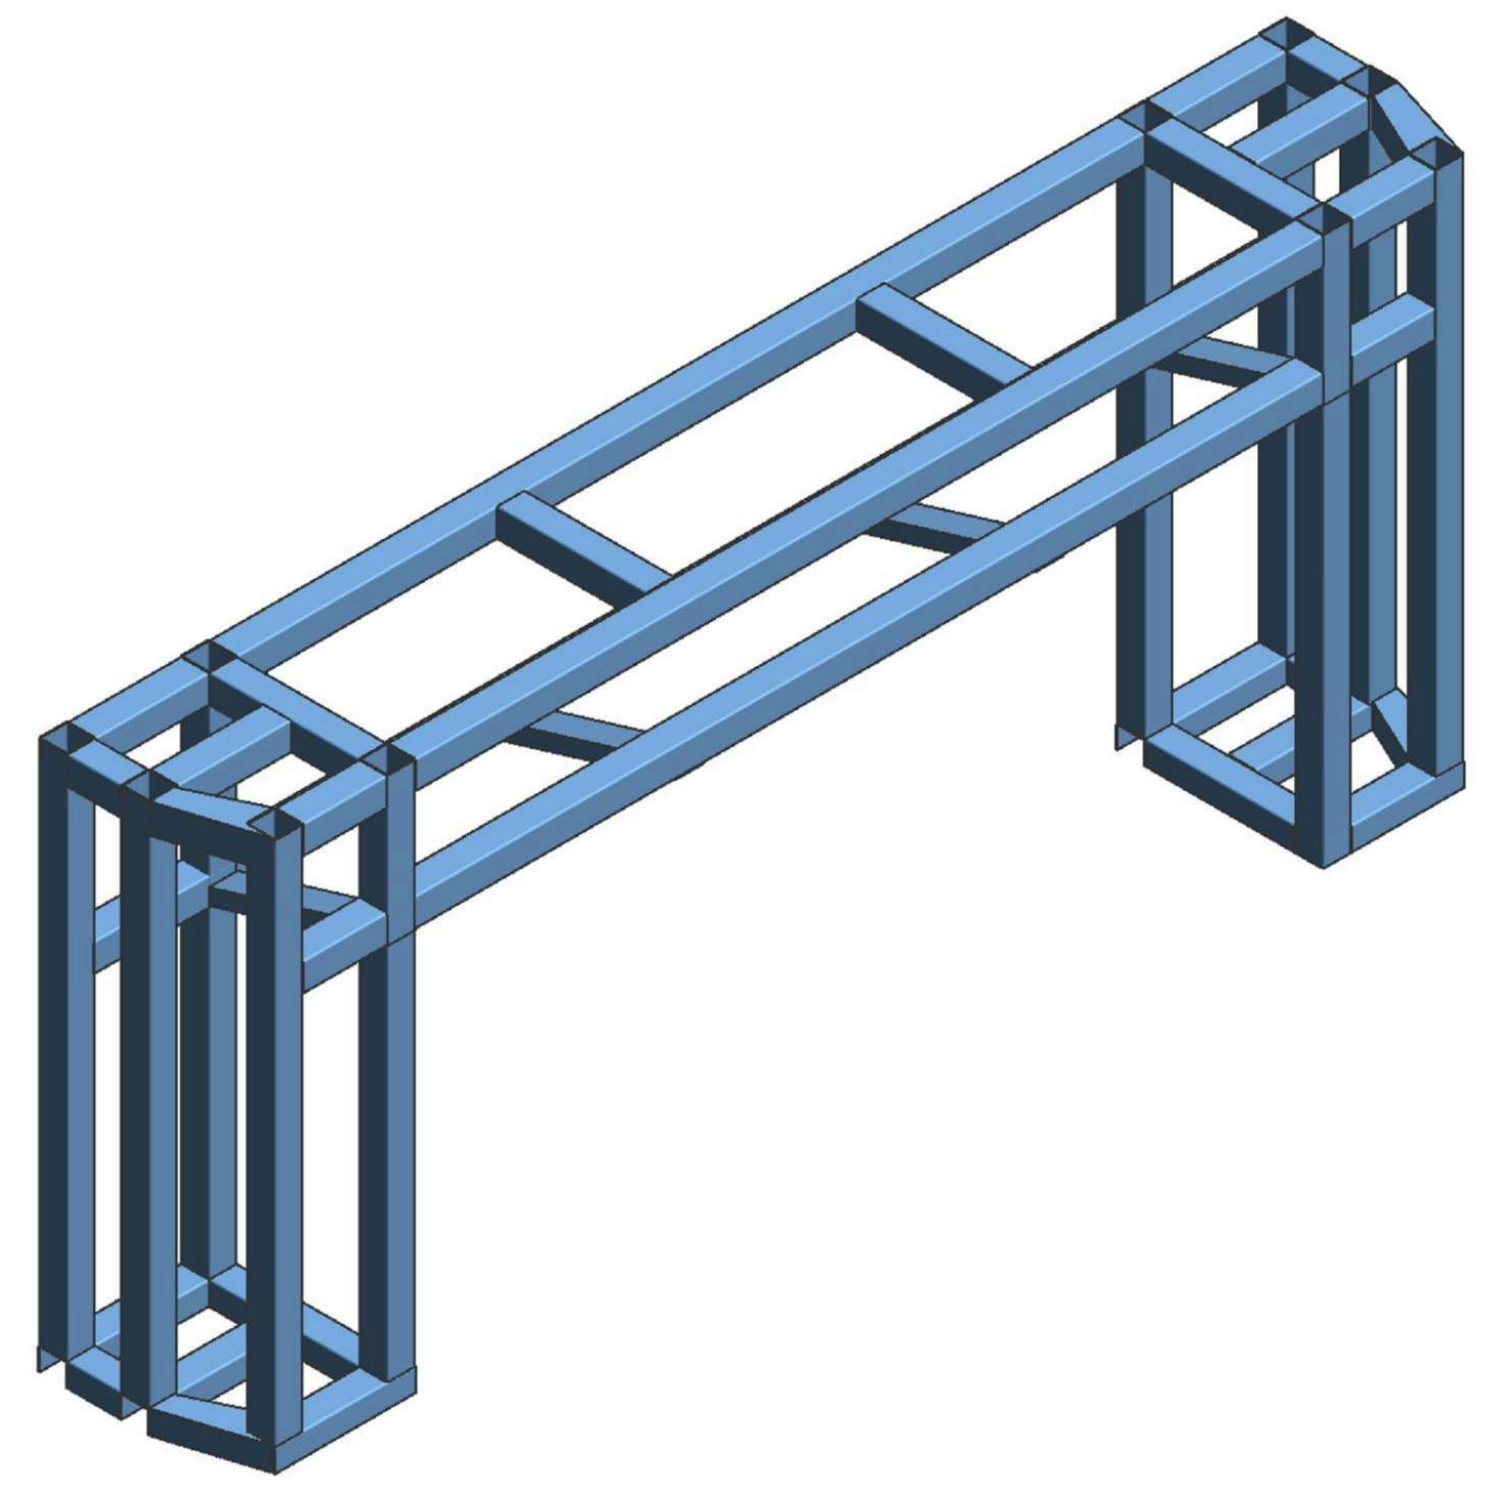

①

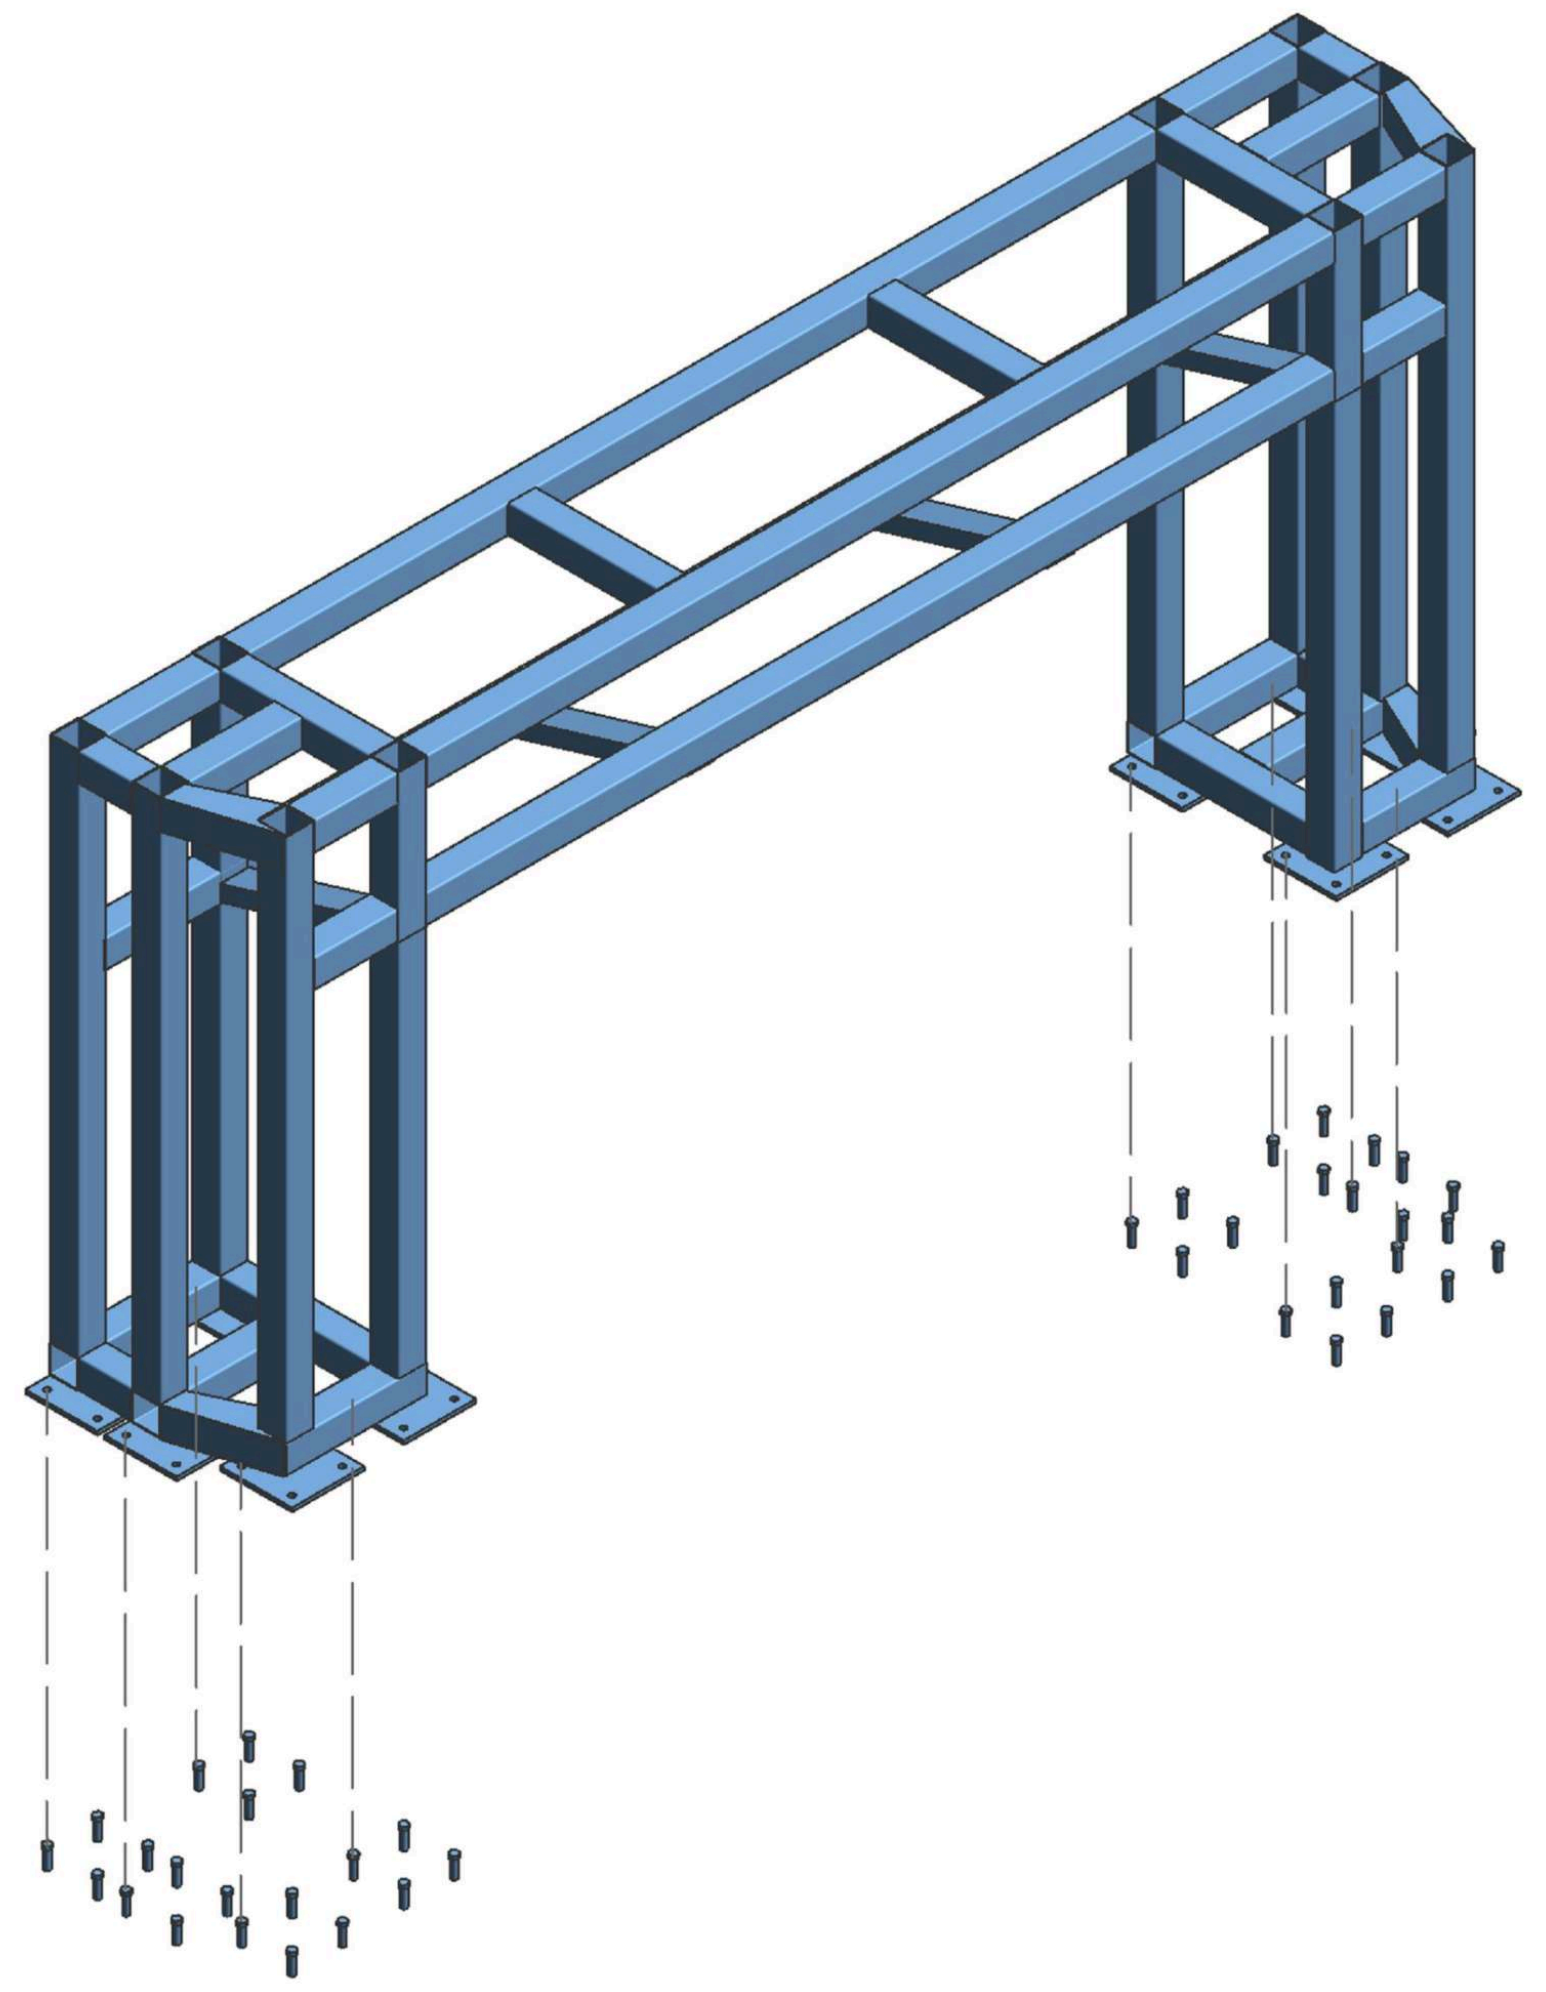

②

③

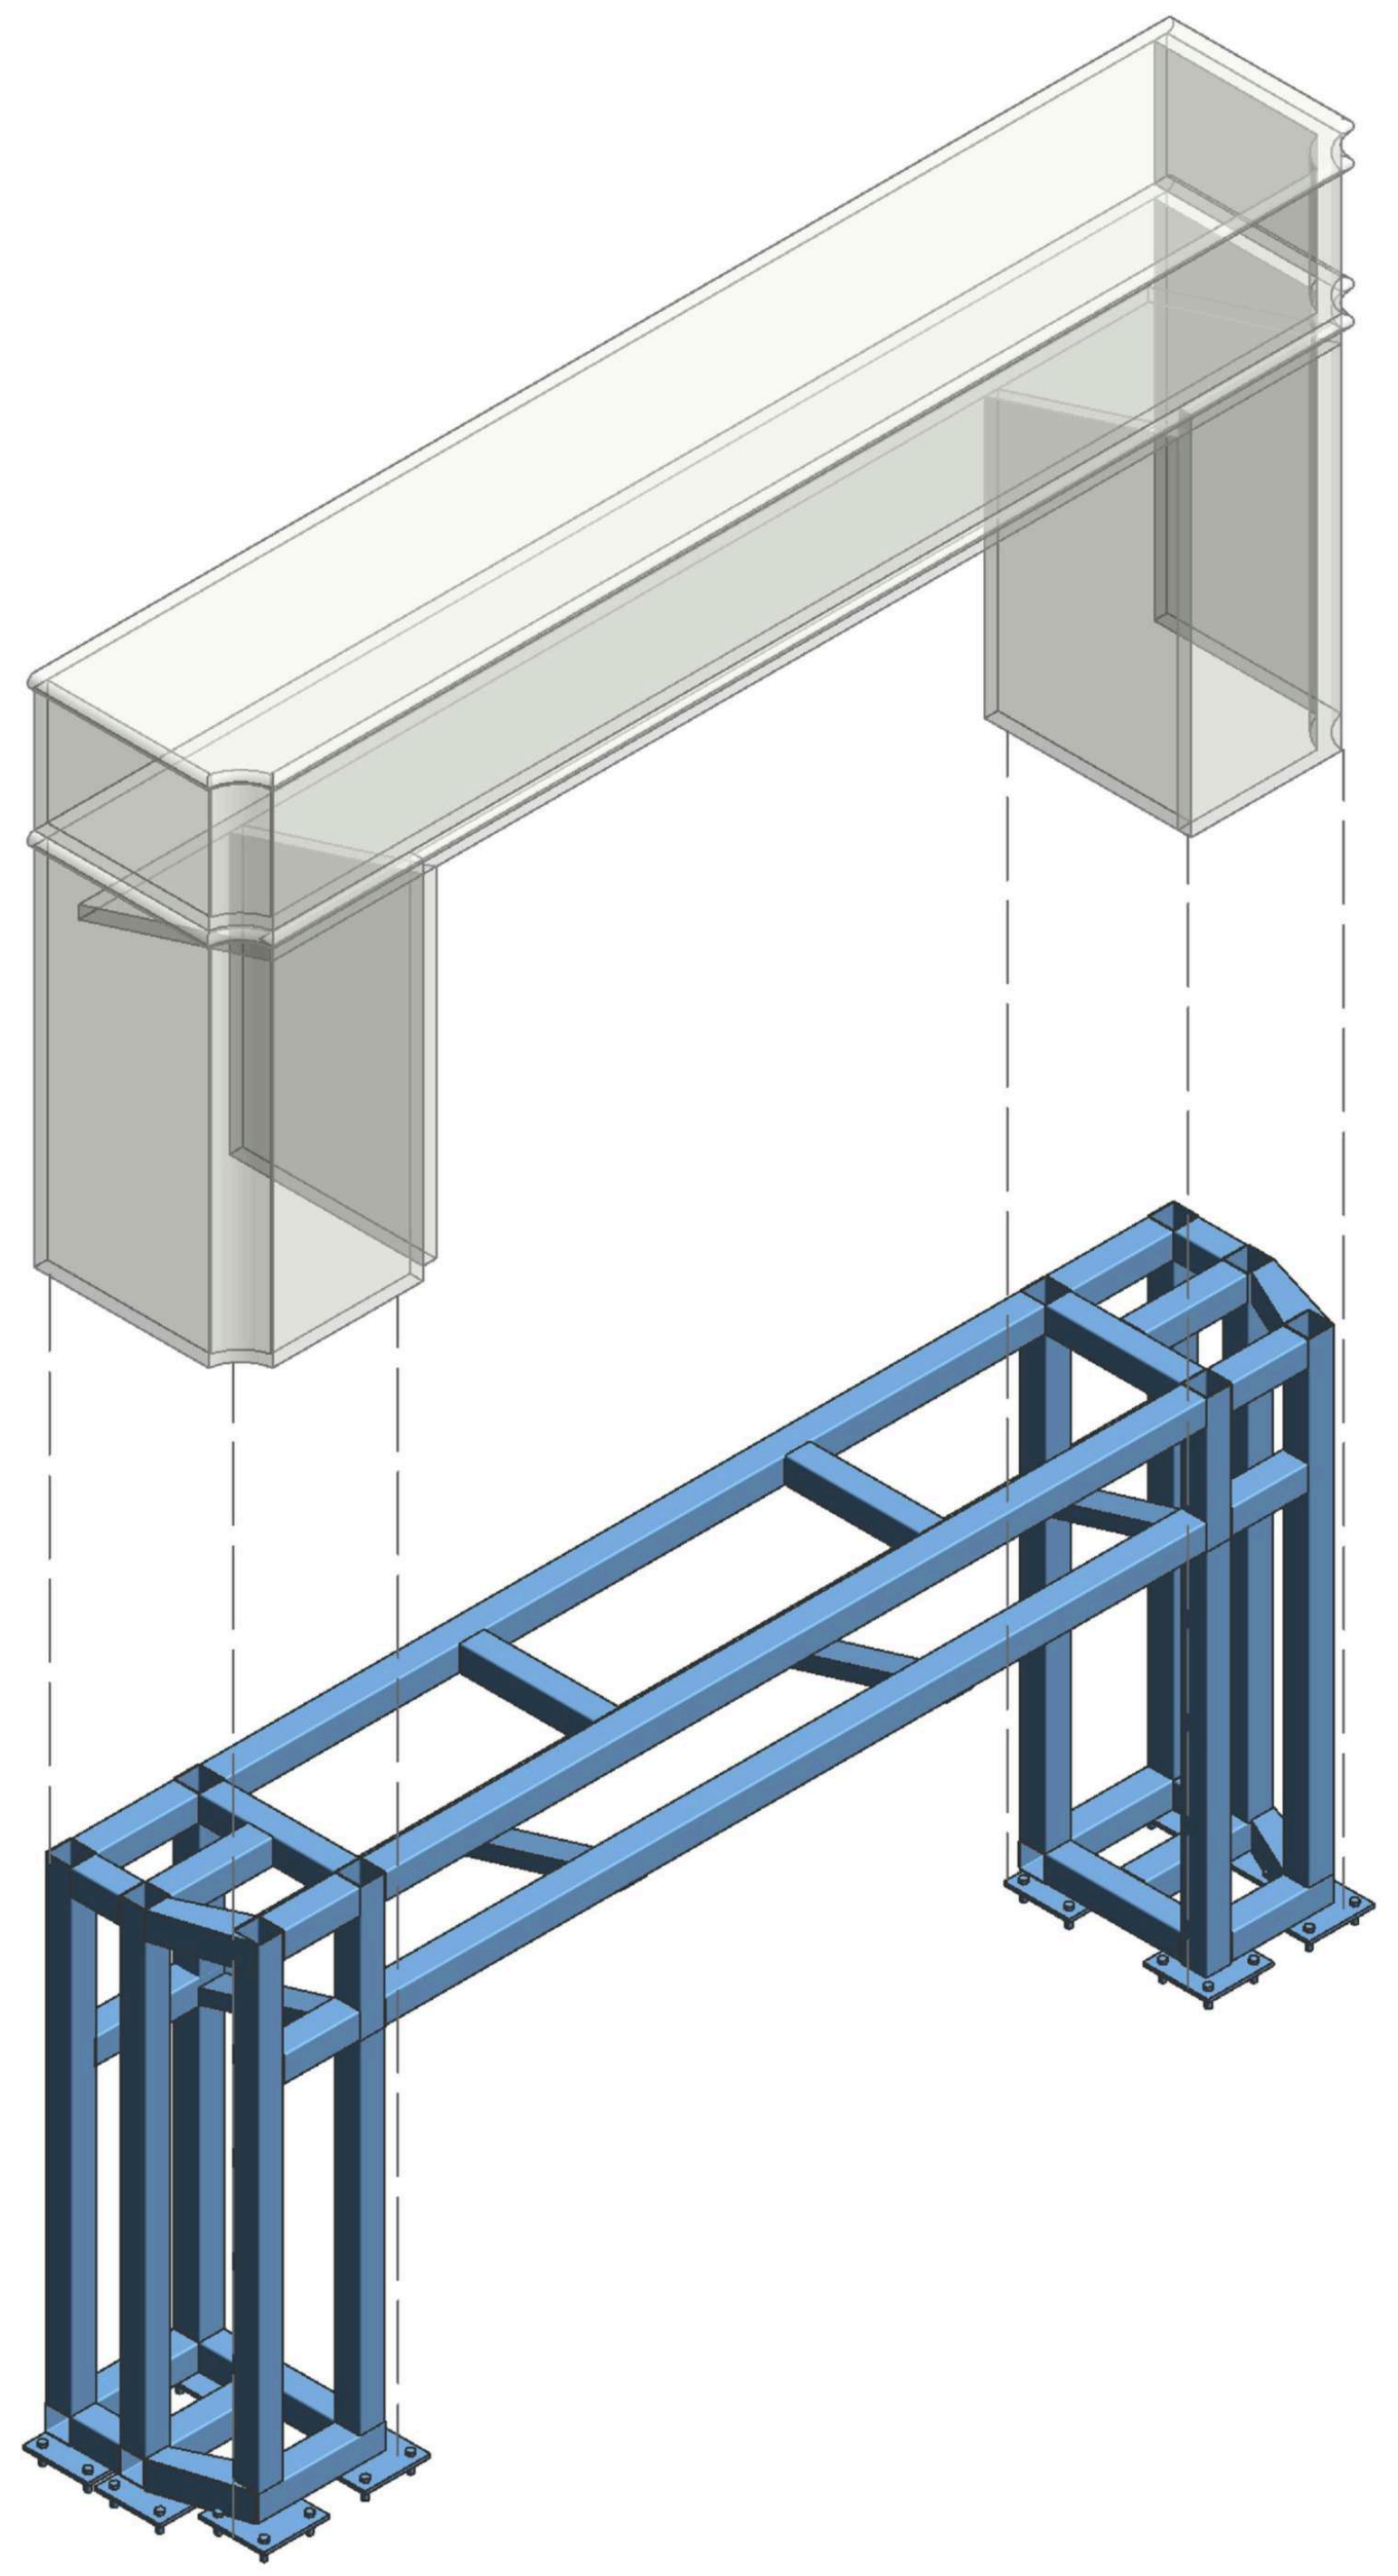

④

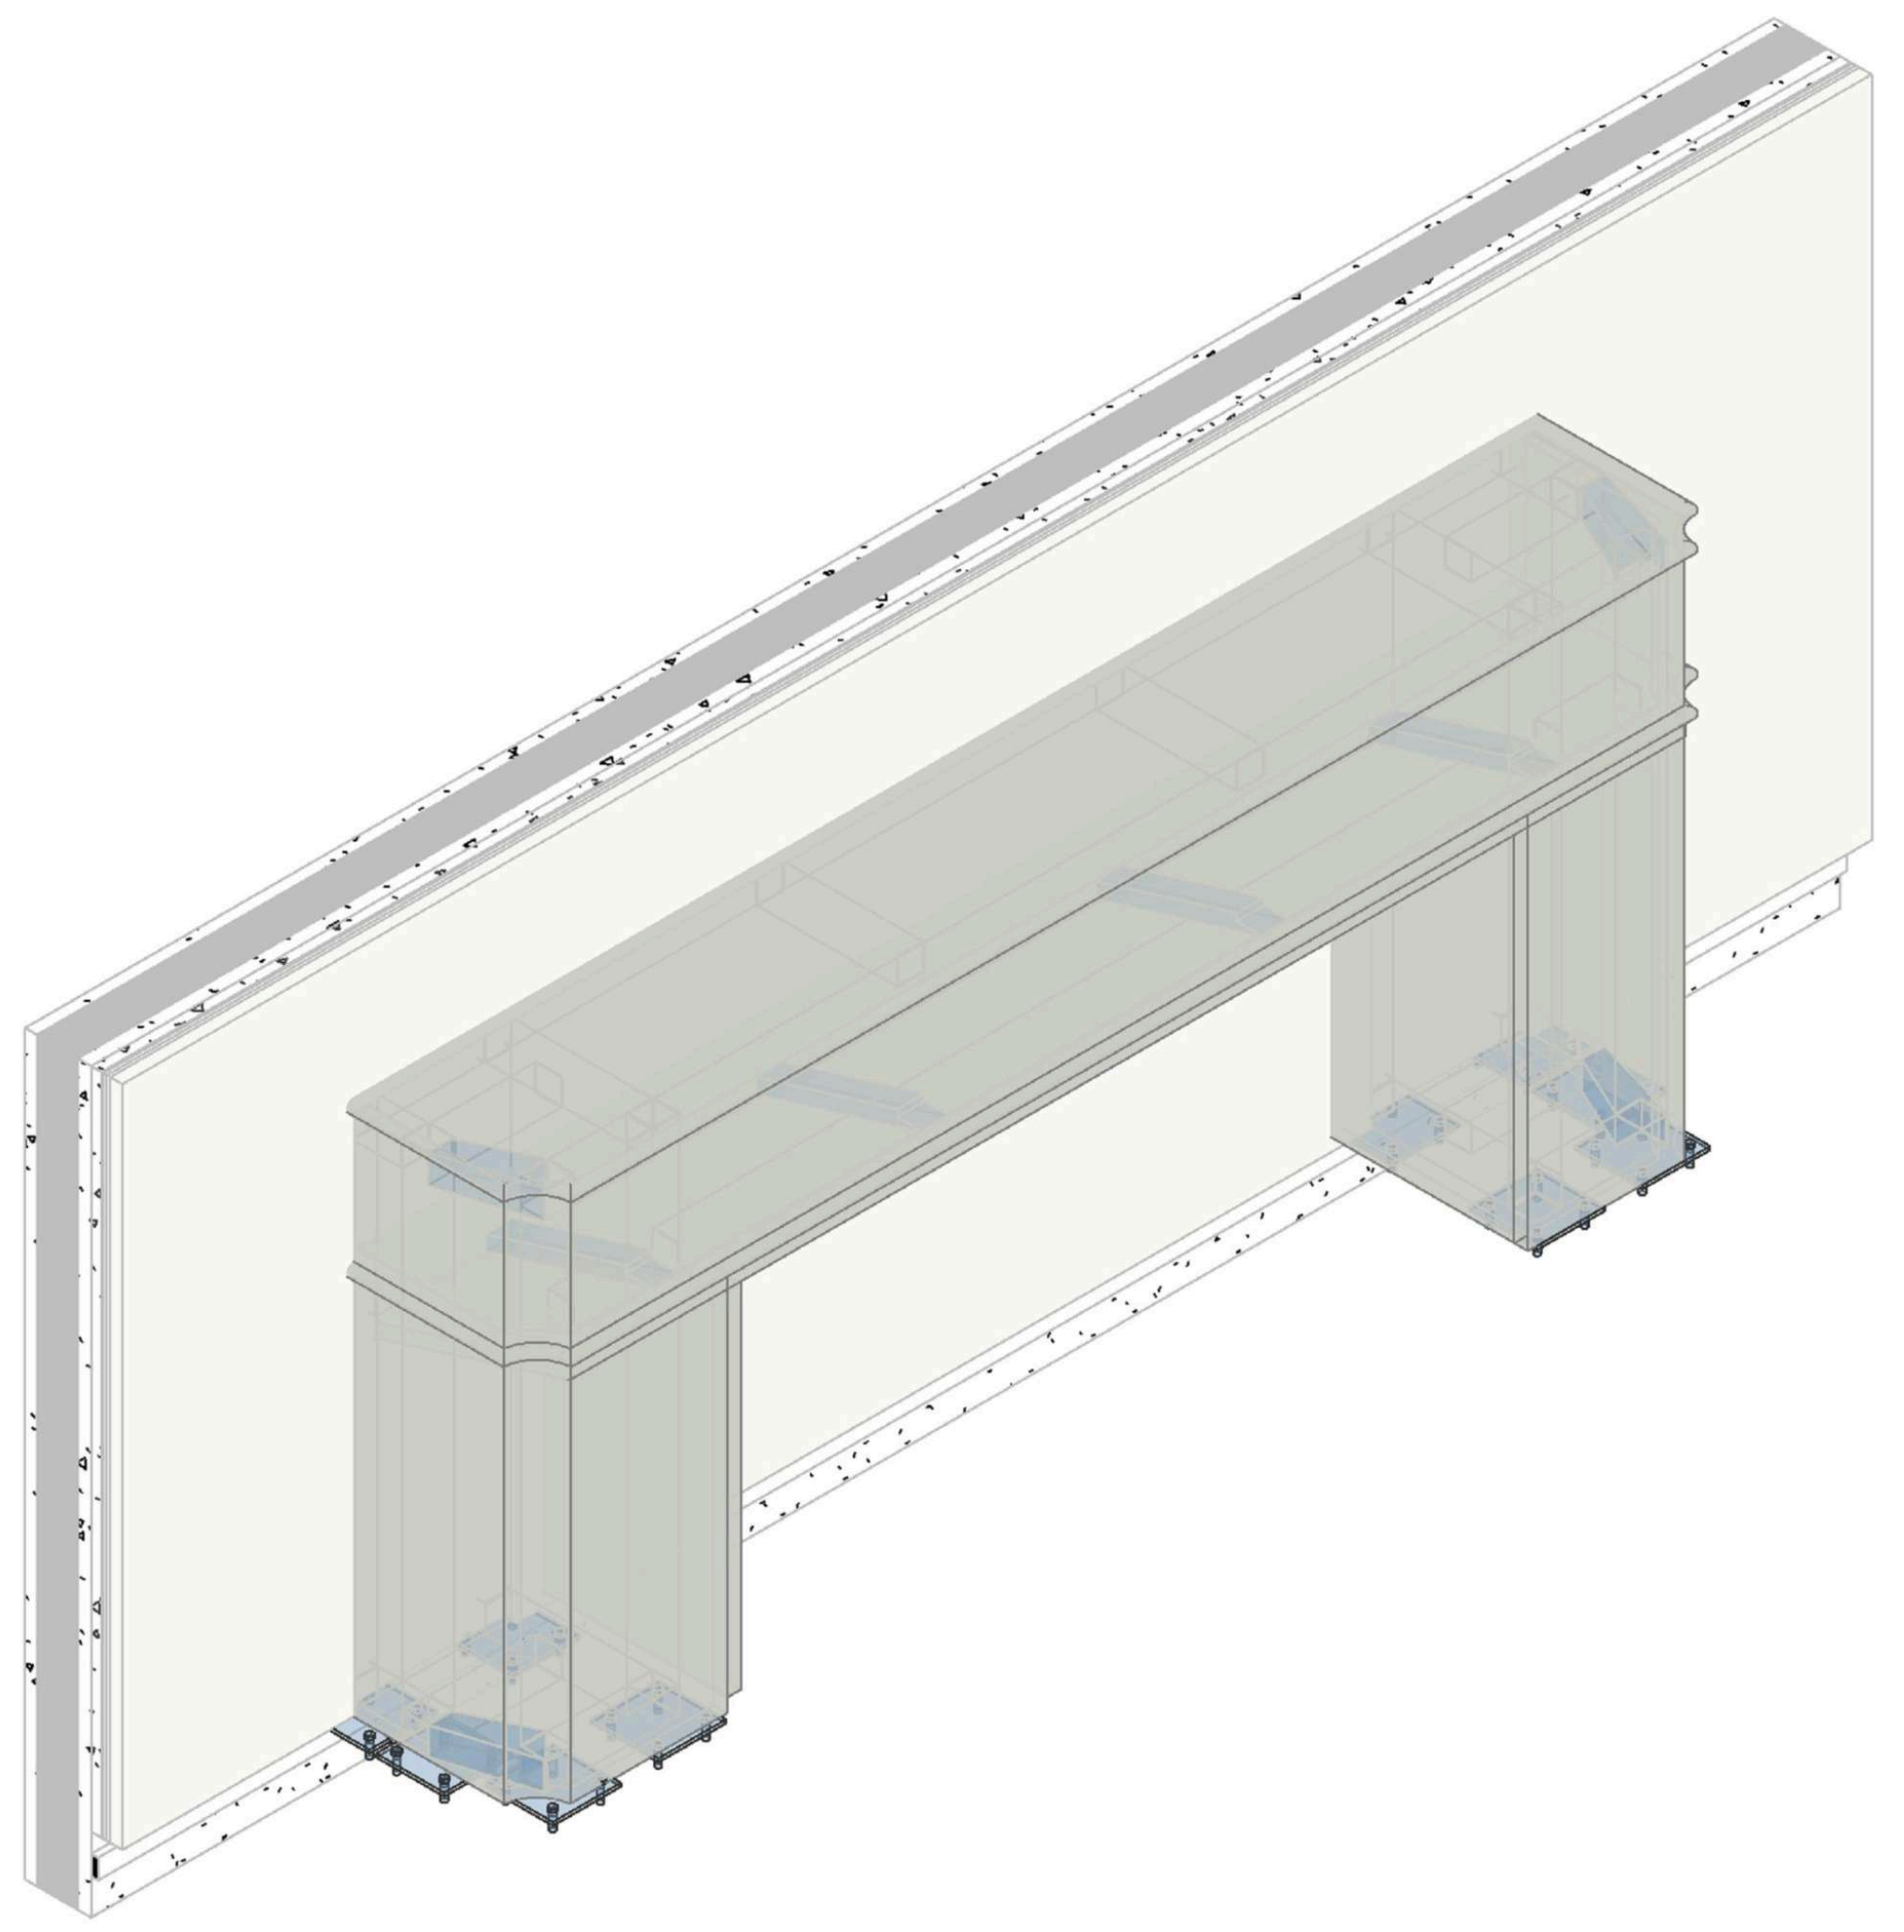

FIBORN

图例A
LEGEND A

编号	图例	说明
1		原始钢架
2		螺栓
3		钢片
4		钢架
5		石材

盖章

注释
Notes

1.本图纸如与现场尺寸有误，请施工人员与项目负责人联系。
2.施工前施工人员应认真查阅此图，如有不明确尺寸，按现场测量为准。
3.本图纸必须经甲乙双方认可并签字方可作为施工依据。

日期
Date 04/24/26

修订
Revision

△1

项目
Project
潮映华岸府3-801

比例
Scale

客厅壁炉石材钢架

图纸编号
Drawing No.
ST-10

项目编号
Project No.

©2025

1

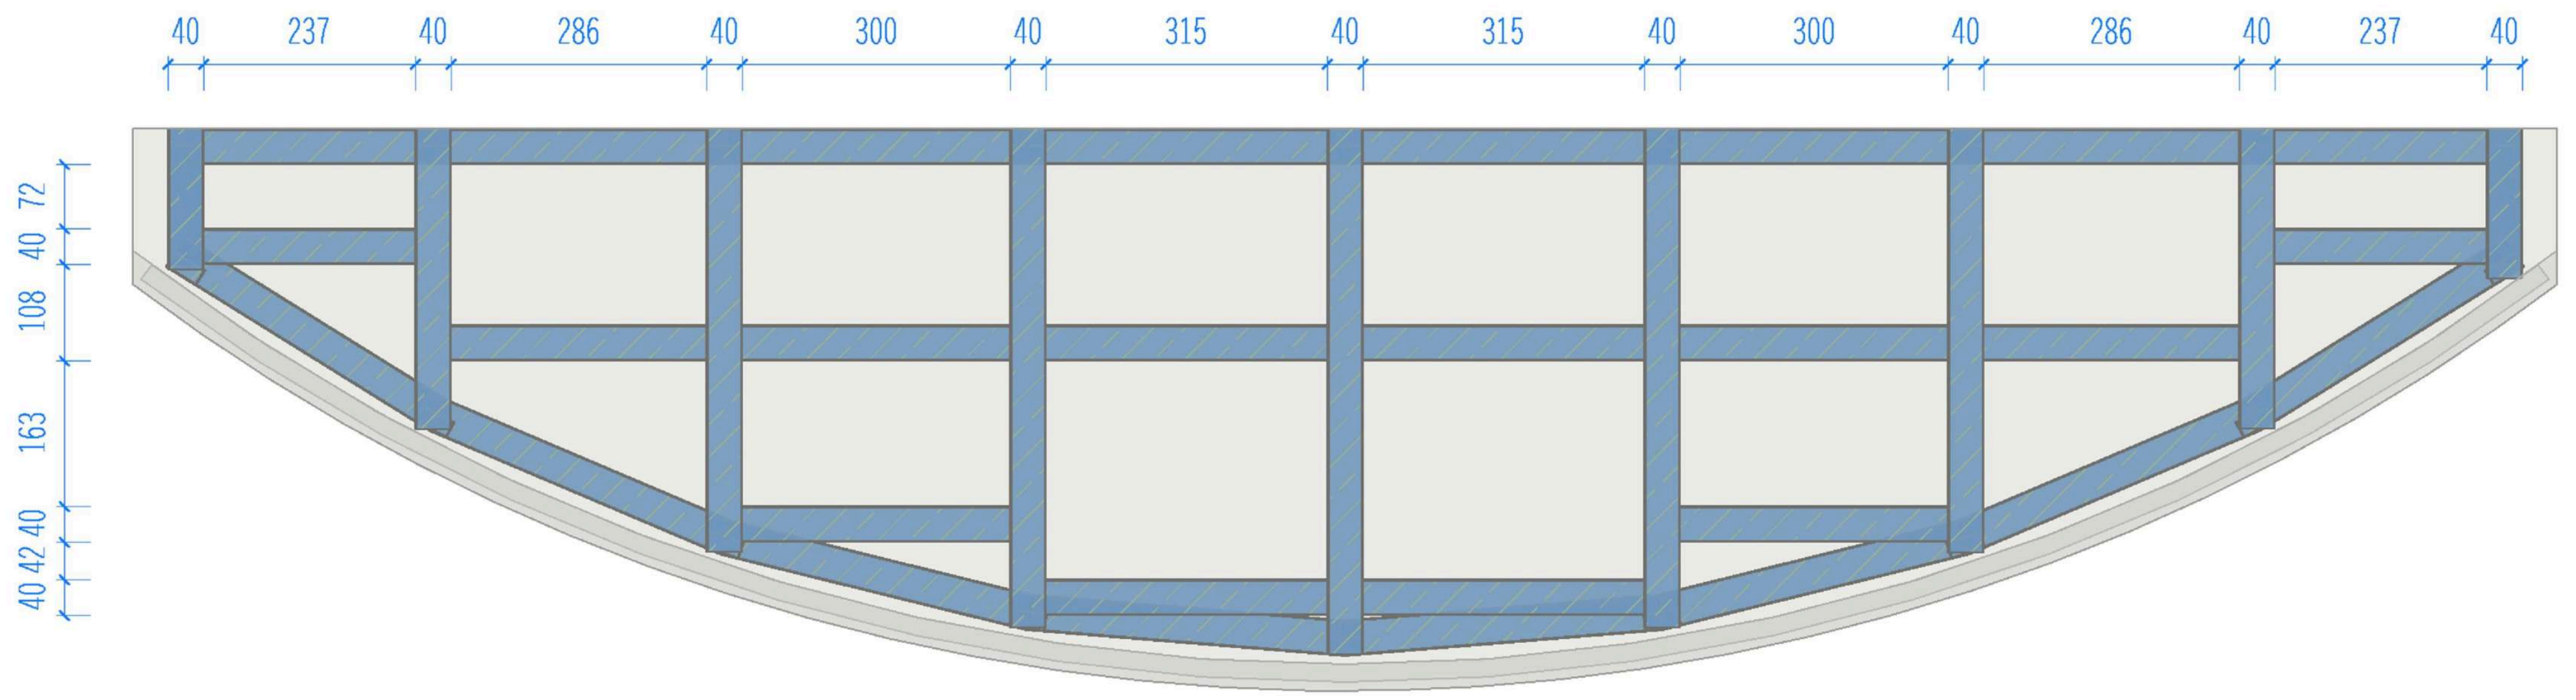
40
237
40
286
40
300
40
315
40
315
40
300
40
286
40
237
40
72
40
108
163
40
42
40
40

平面视图

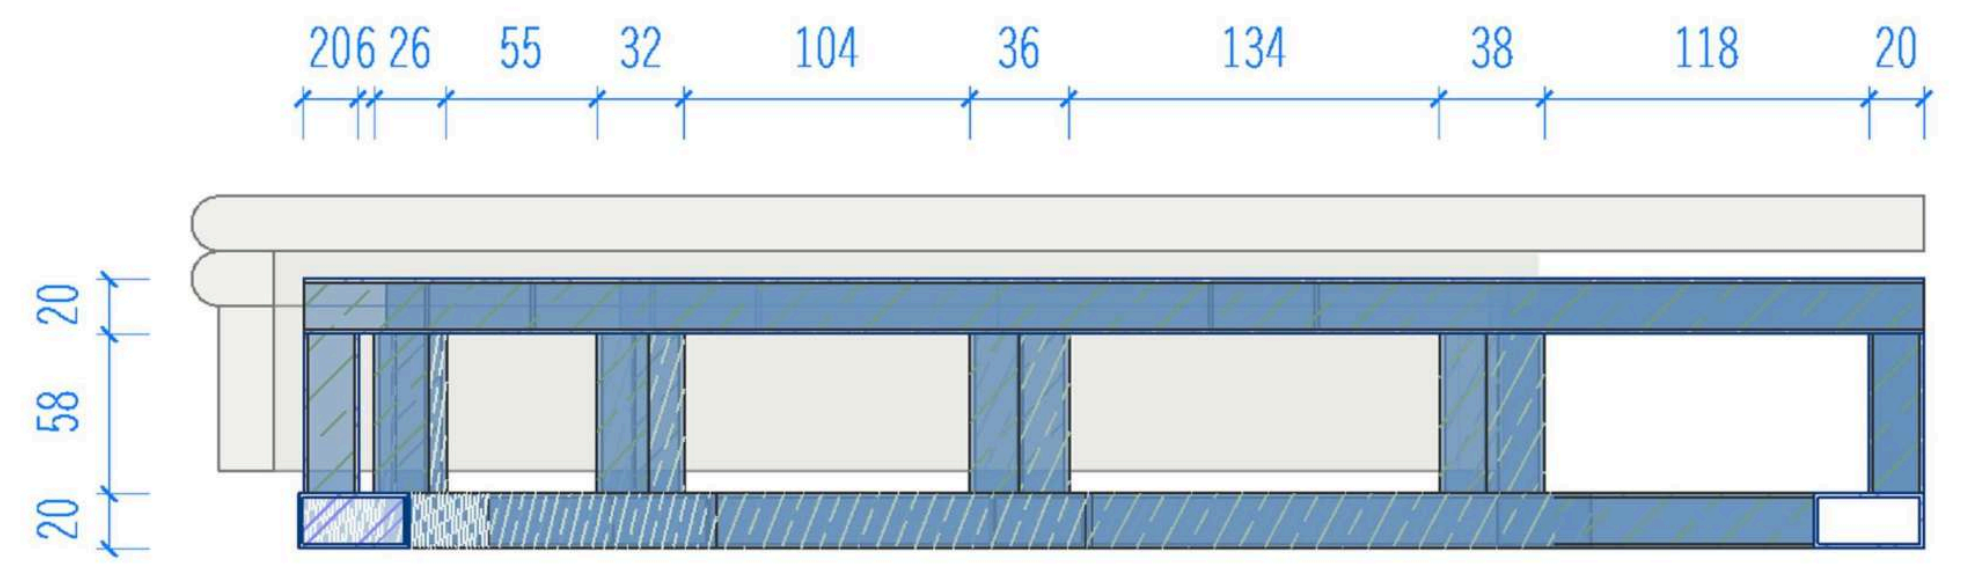
20
6
26
55
32
104
36
134
38
118
20
20
58
20

剖面视图

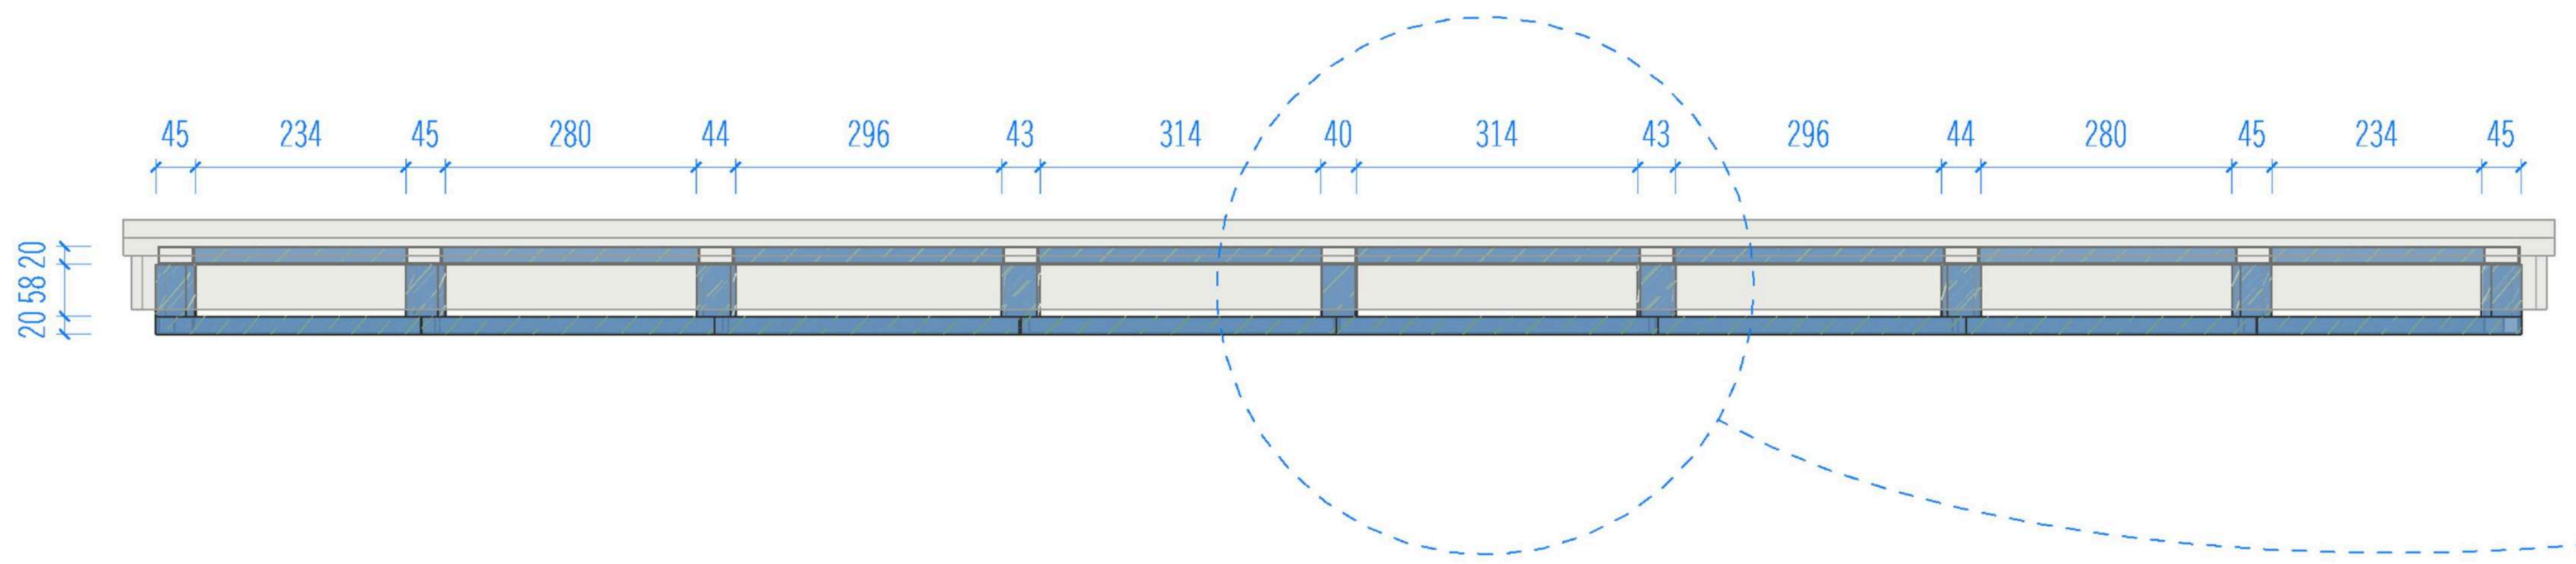
45
234
45
280
44
296
43
314
40
314
43
296
44
280
45
234
45
20
58
20

立面视图

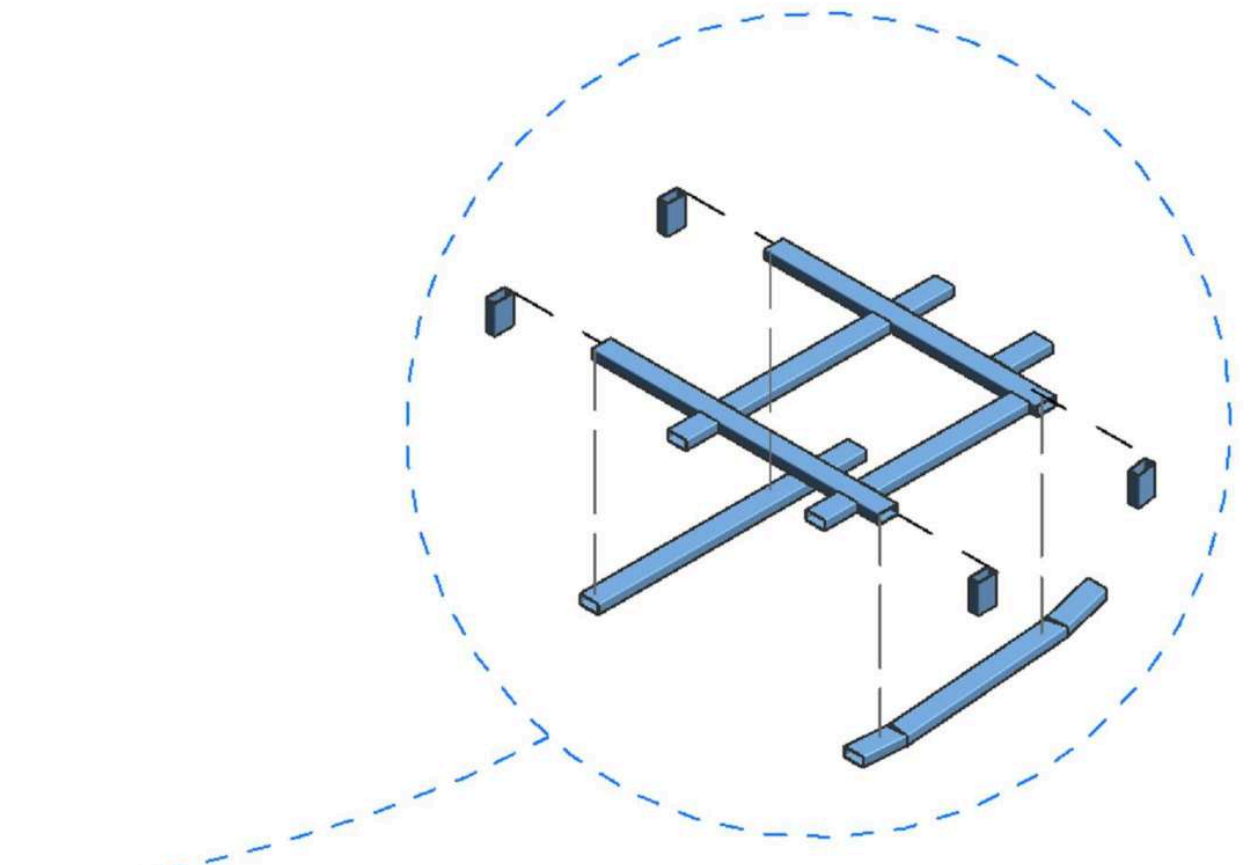

节点图

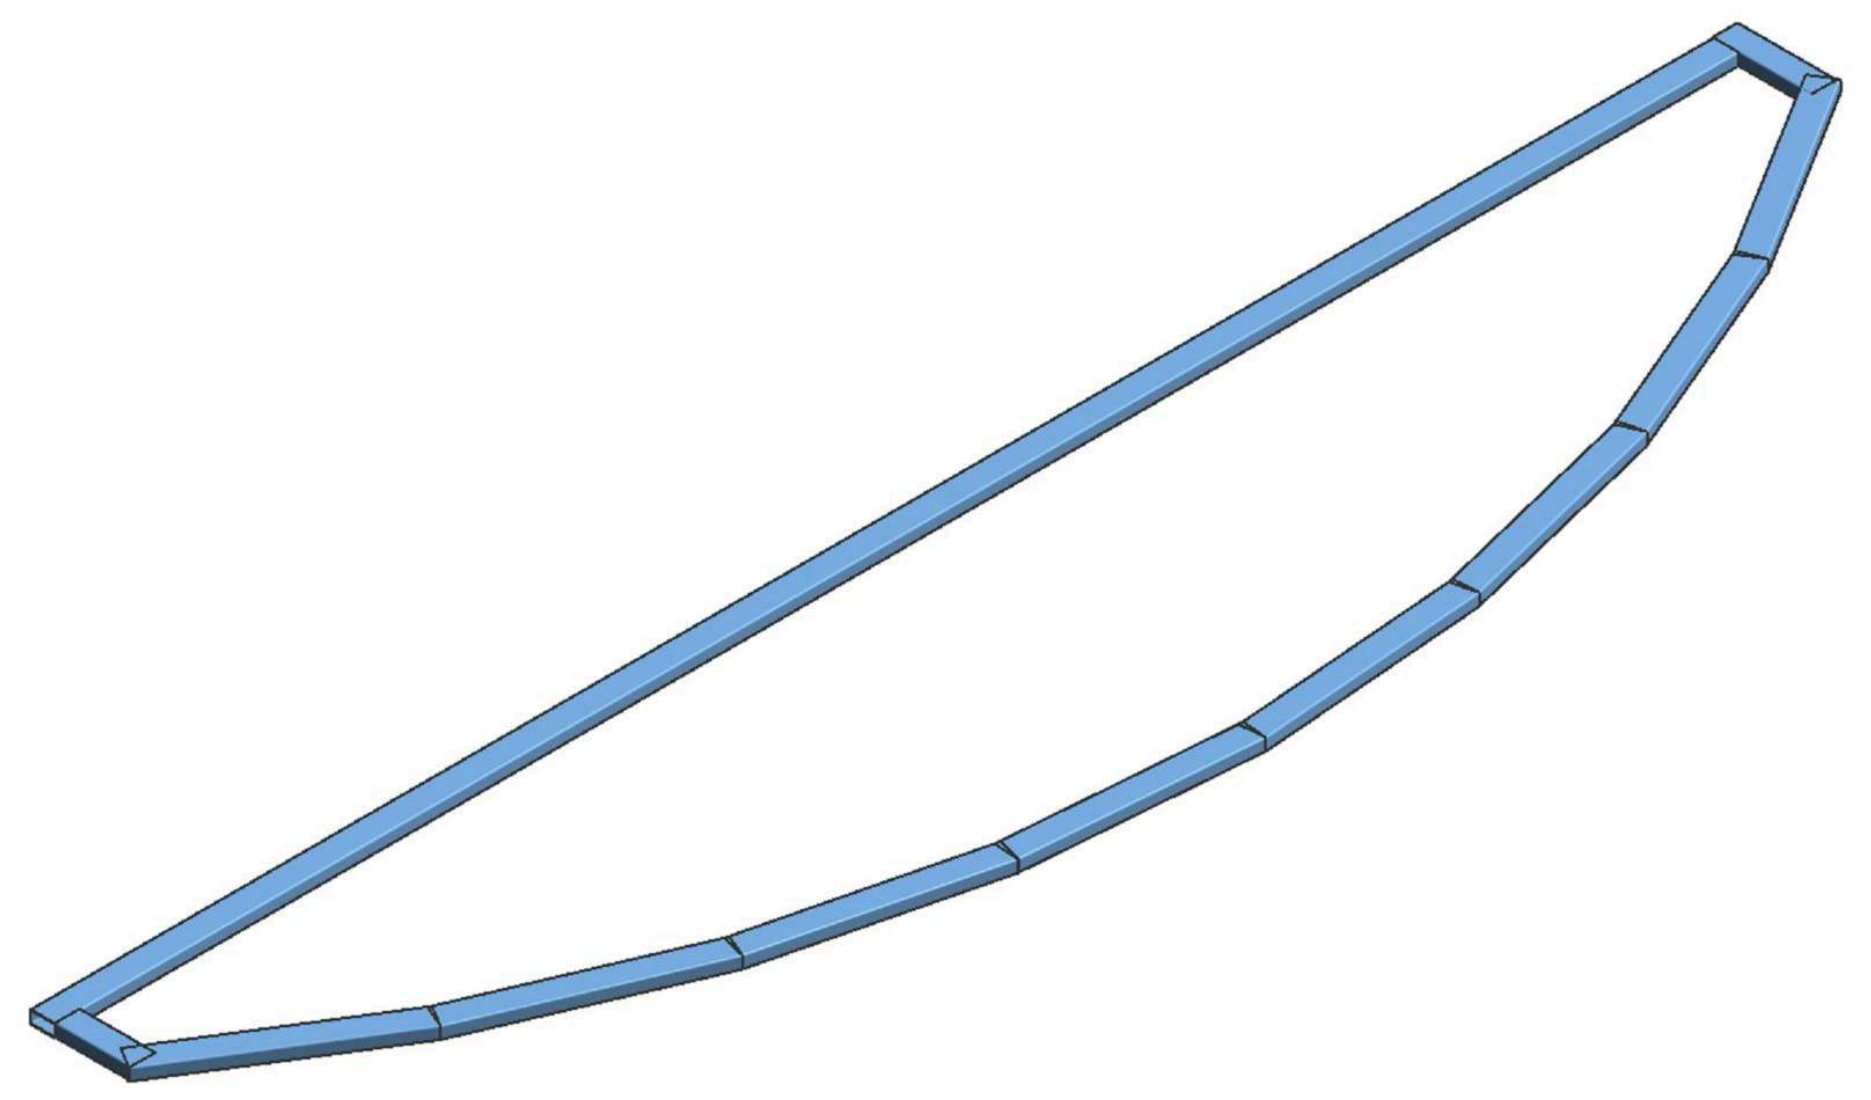

①

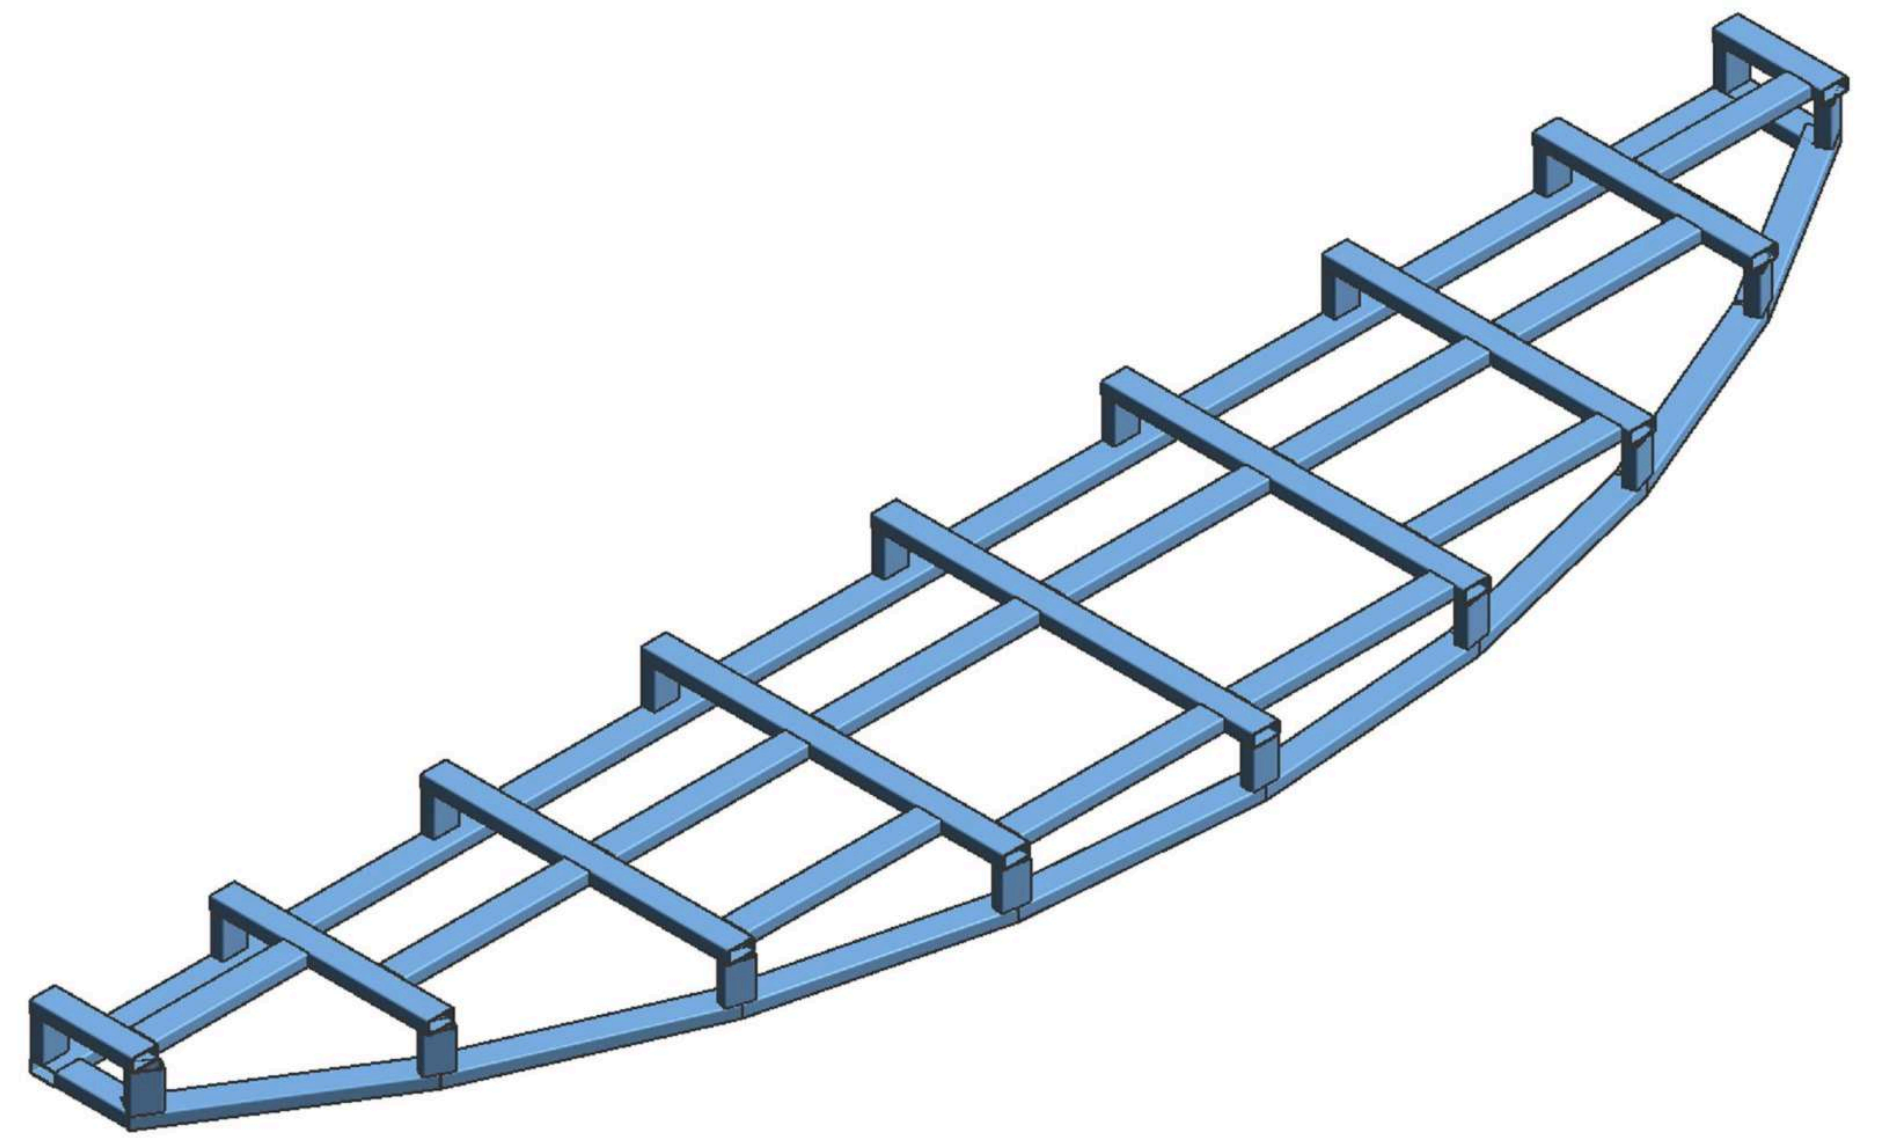

②

③

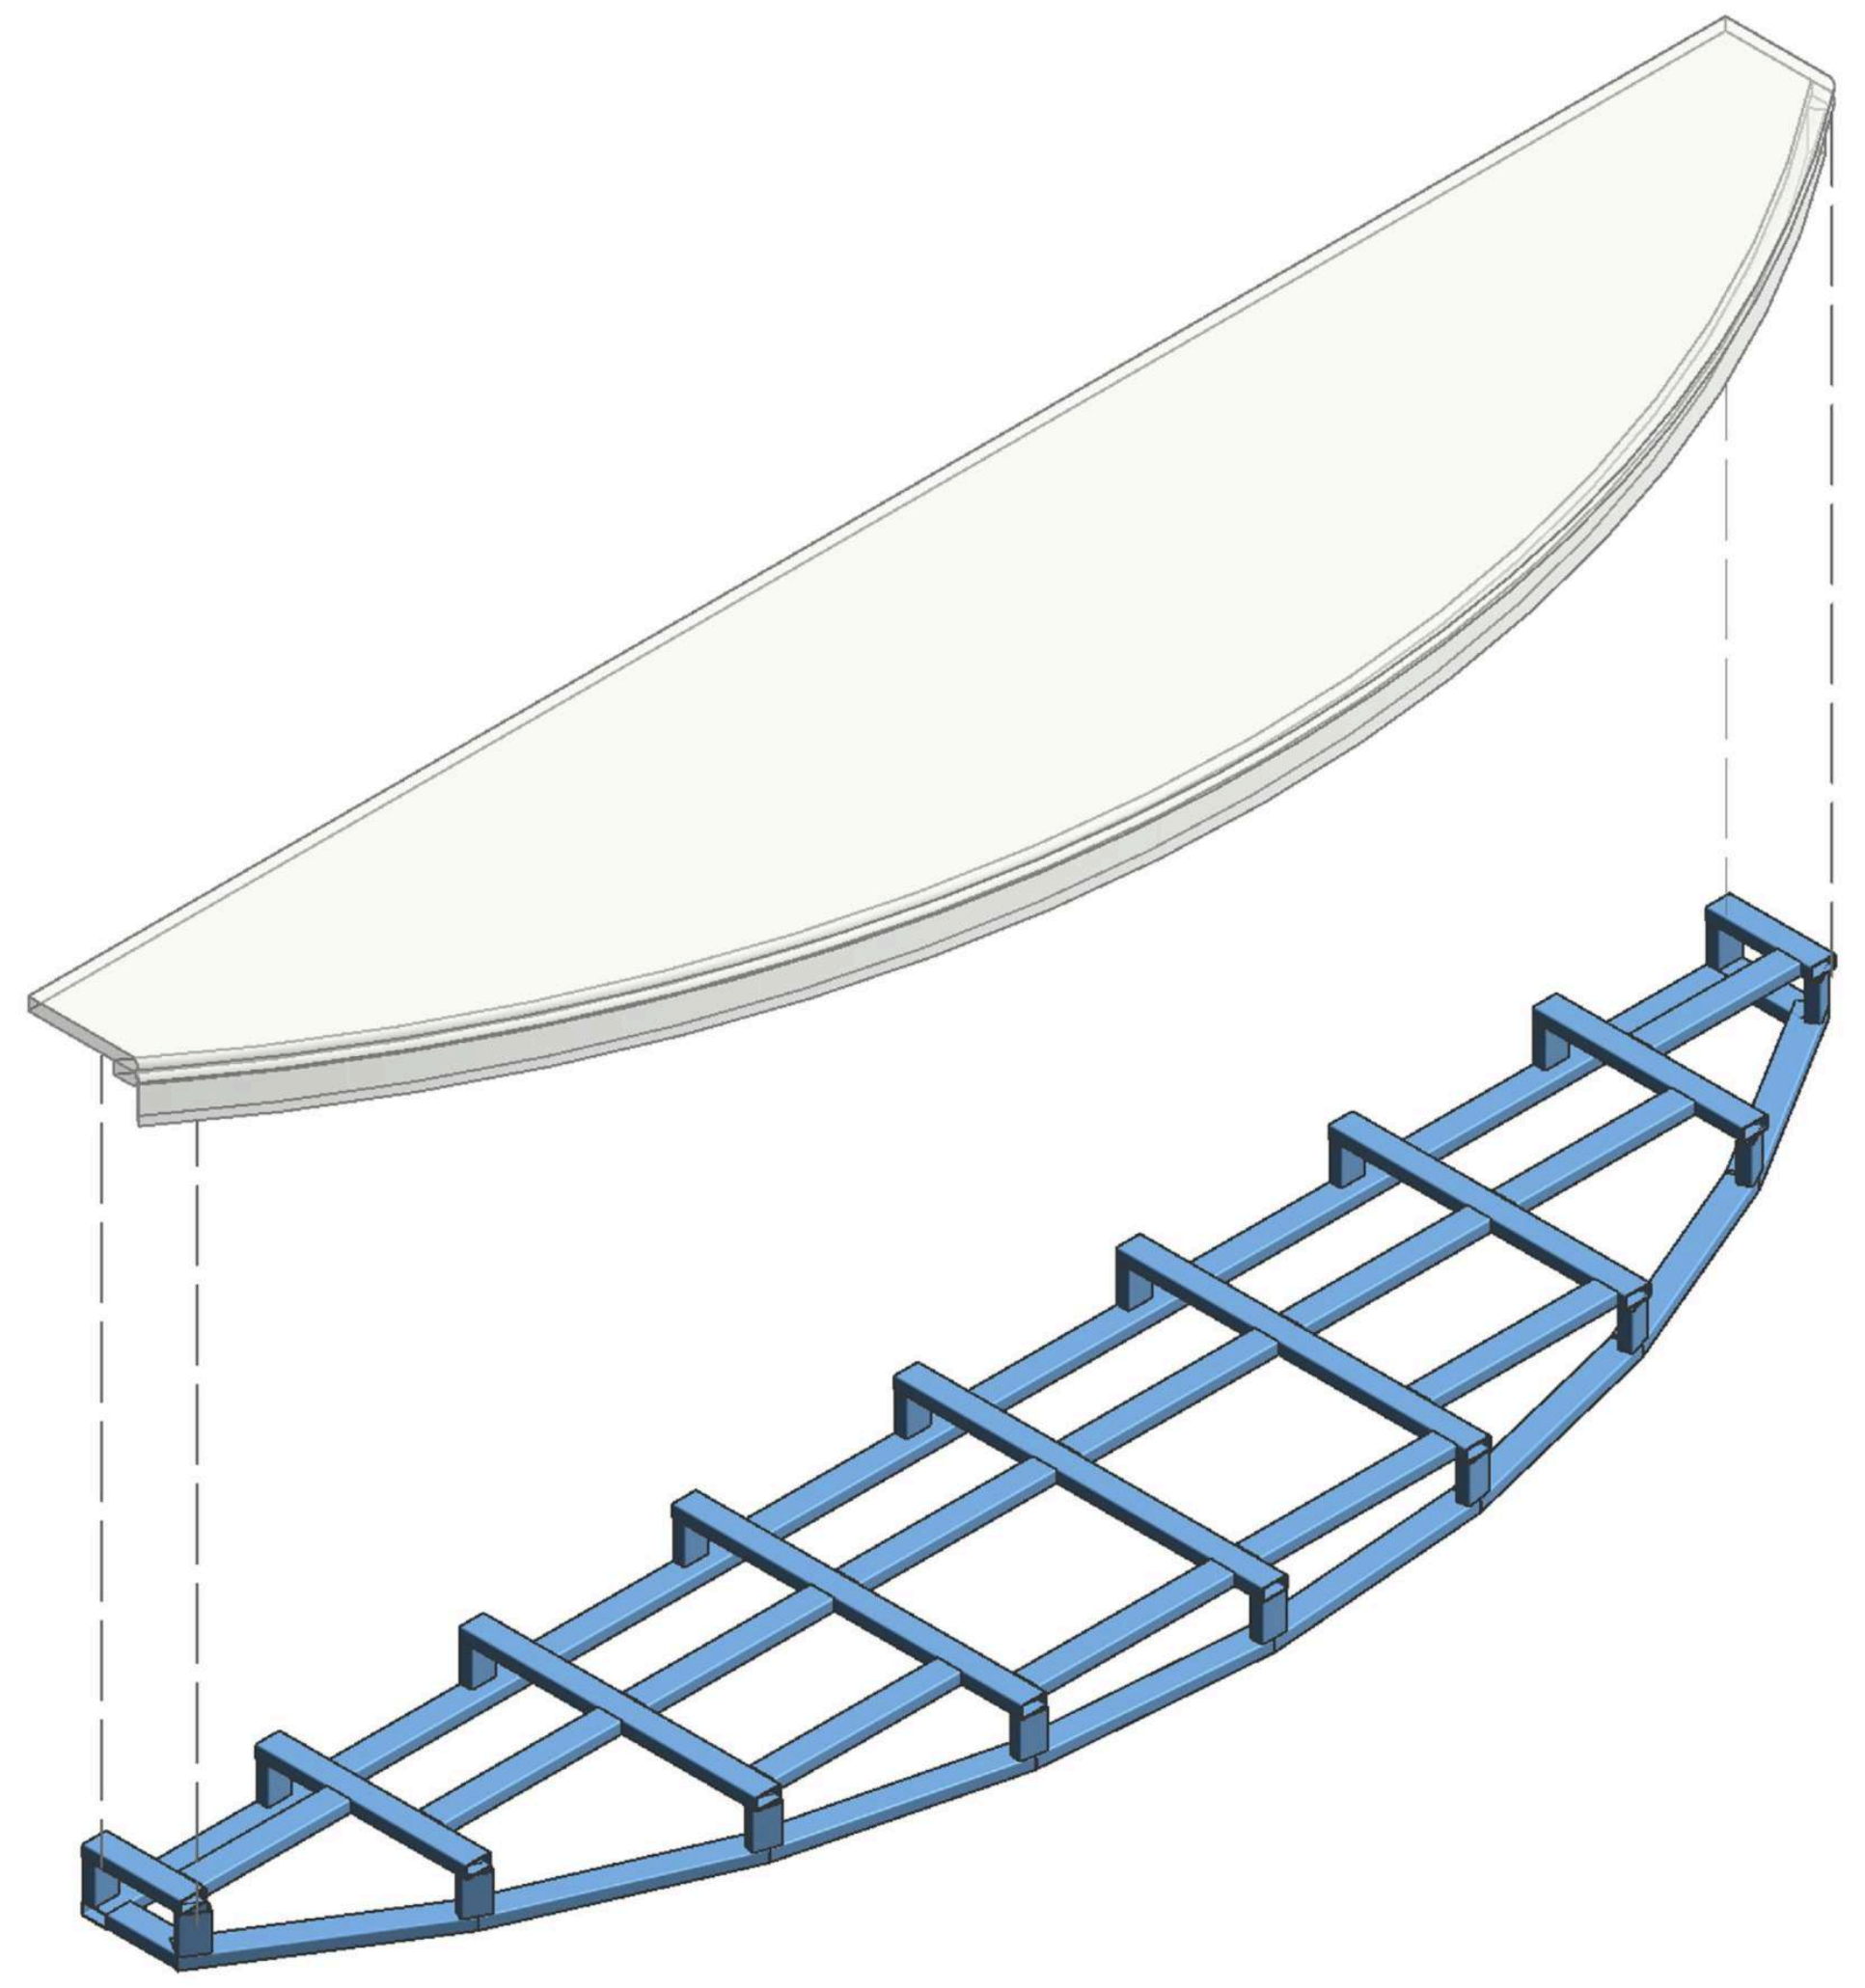

④

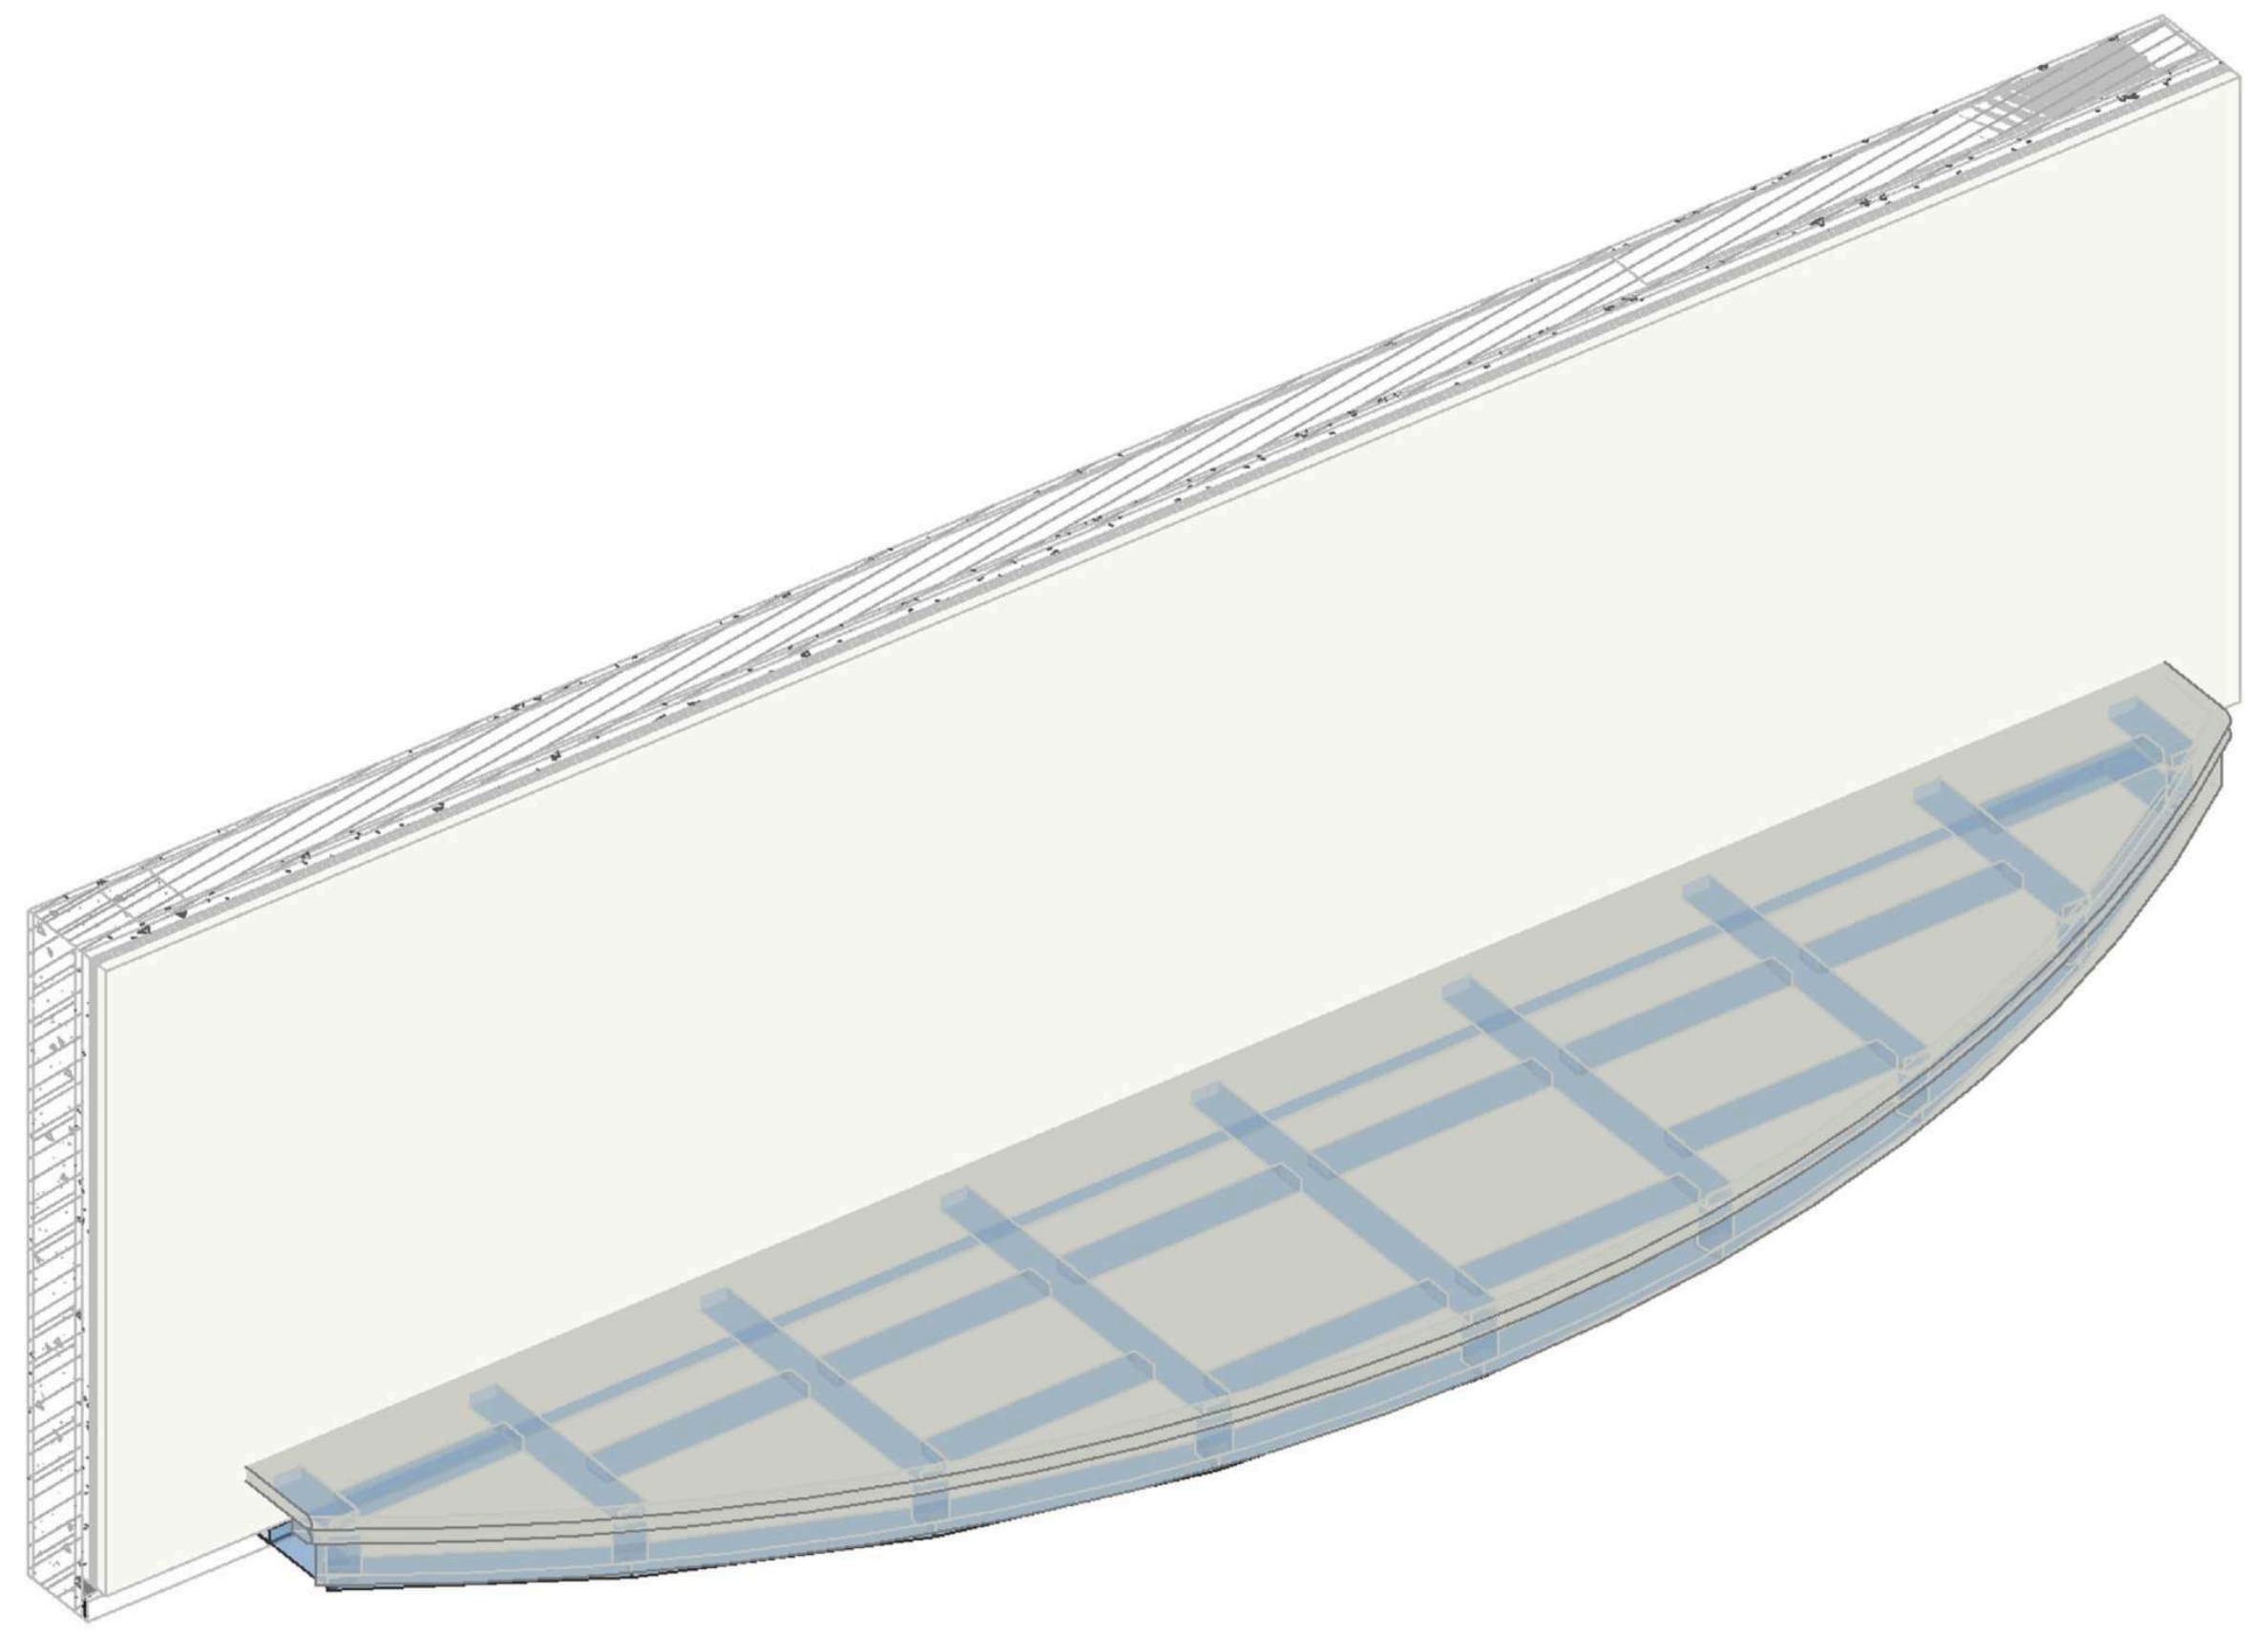

图例A
LEGEND A

编号	图例	说明
1	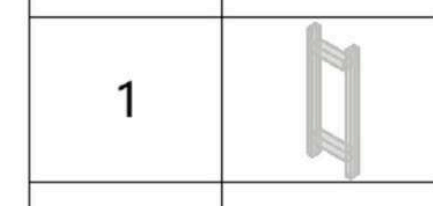	原始钢架
2		螺栓
3		钢片
4	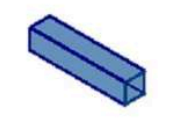	钢架
5	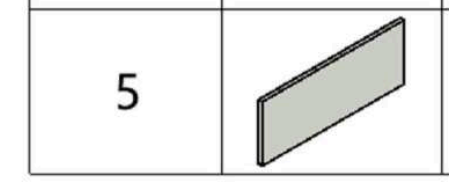	石材

盖章

注释
Notes
1.本图纸如与现场尺寸有误，请施工人员与项目负责人联系。
2.施工前施工人员应认真查阅此图，如有不明确尺寸，按现场测量为准。
3.本图纸必须经甲乙双方认可并签字方可作为施工依据。

日期
Date 04/24/26

修订
Revision
1

项目
Project
潮映华岸府3-801

比例
Scale
客厅电视地台石材钢架

图纸编号
Drawing No.
ST-11

项目编号
Project No.
©2025