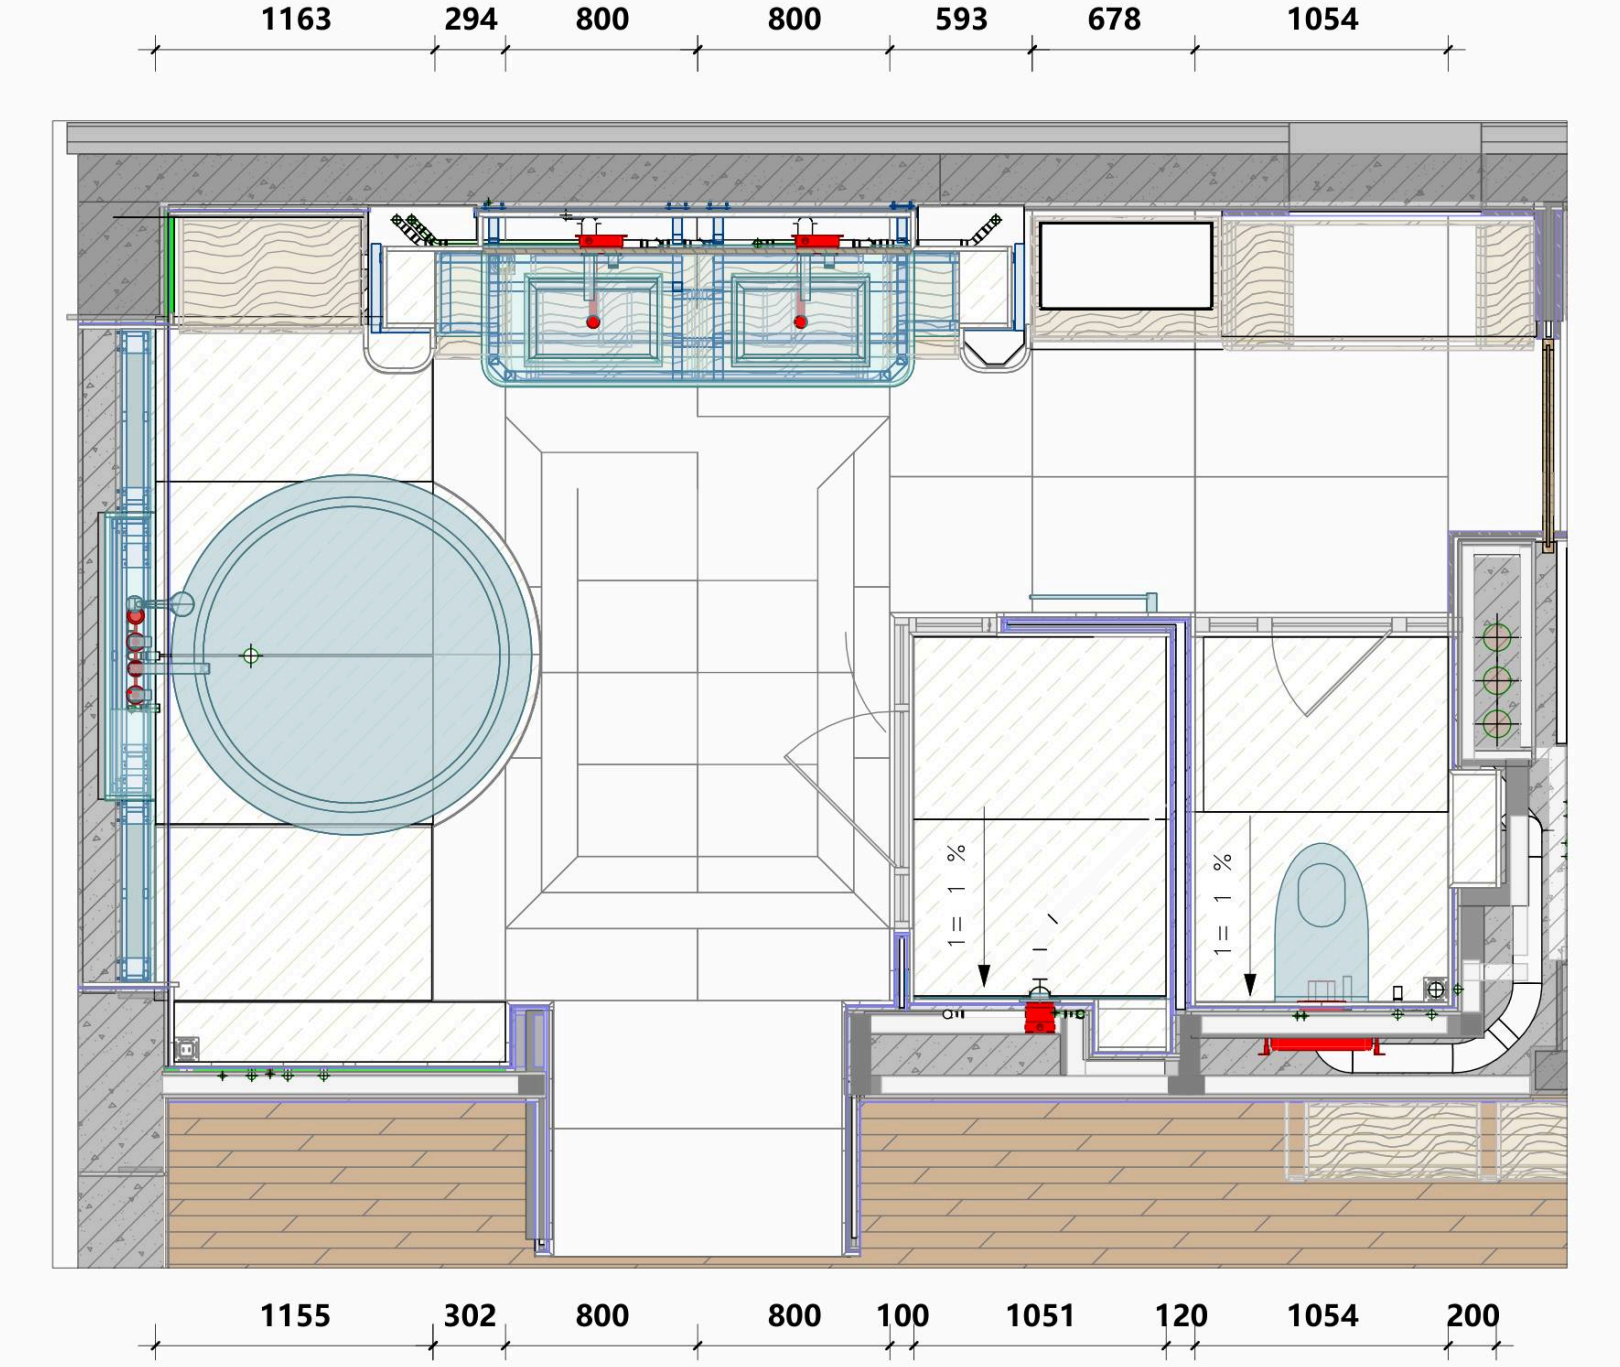
1163
294
800
800
593
678
1054
634
720
720
722
256
536
566
667
729
790
529
533
1155
302
800
800
100
1051
120
1054
200

地面铺贴图

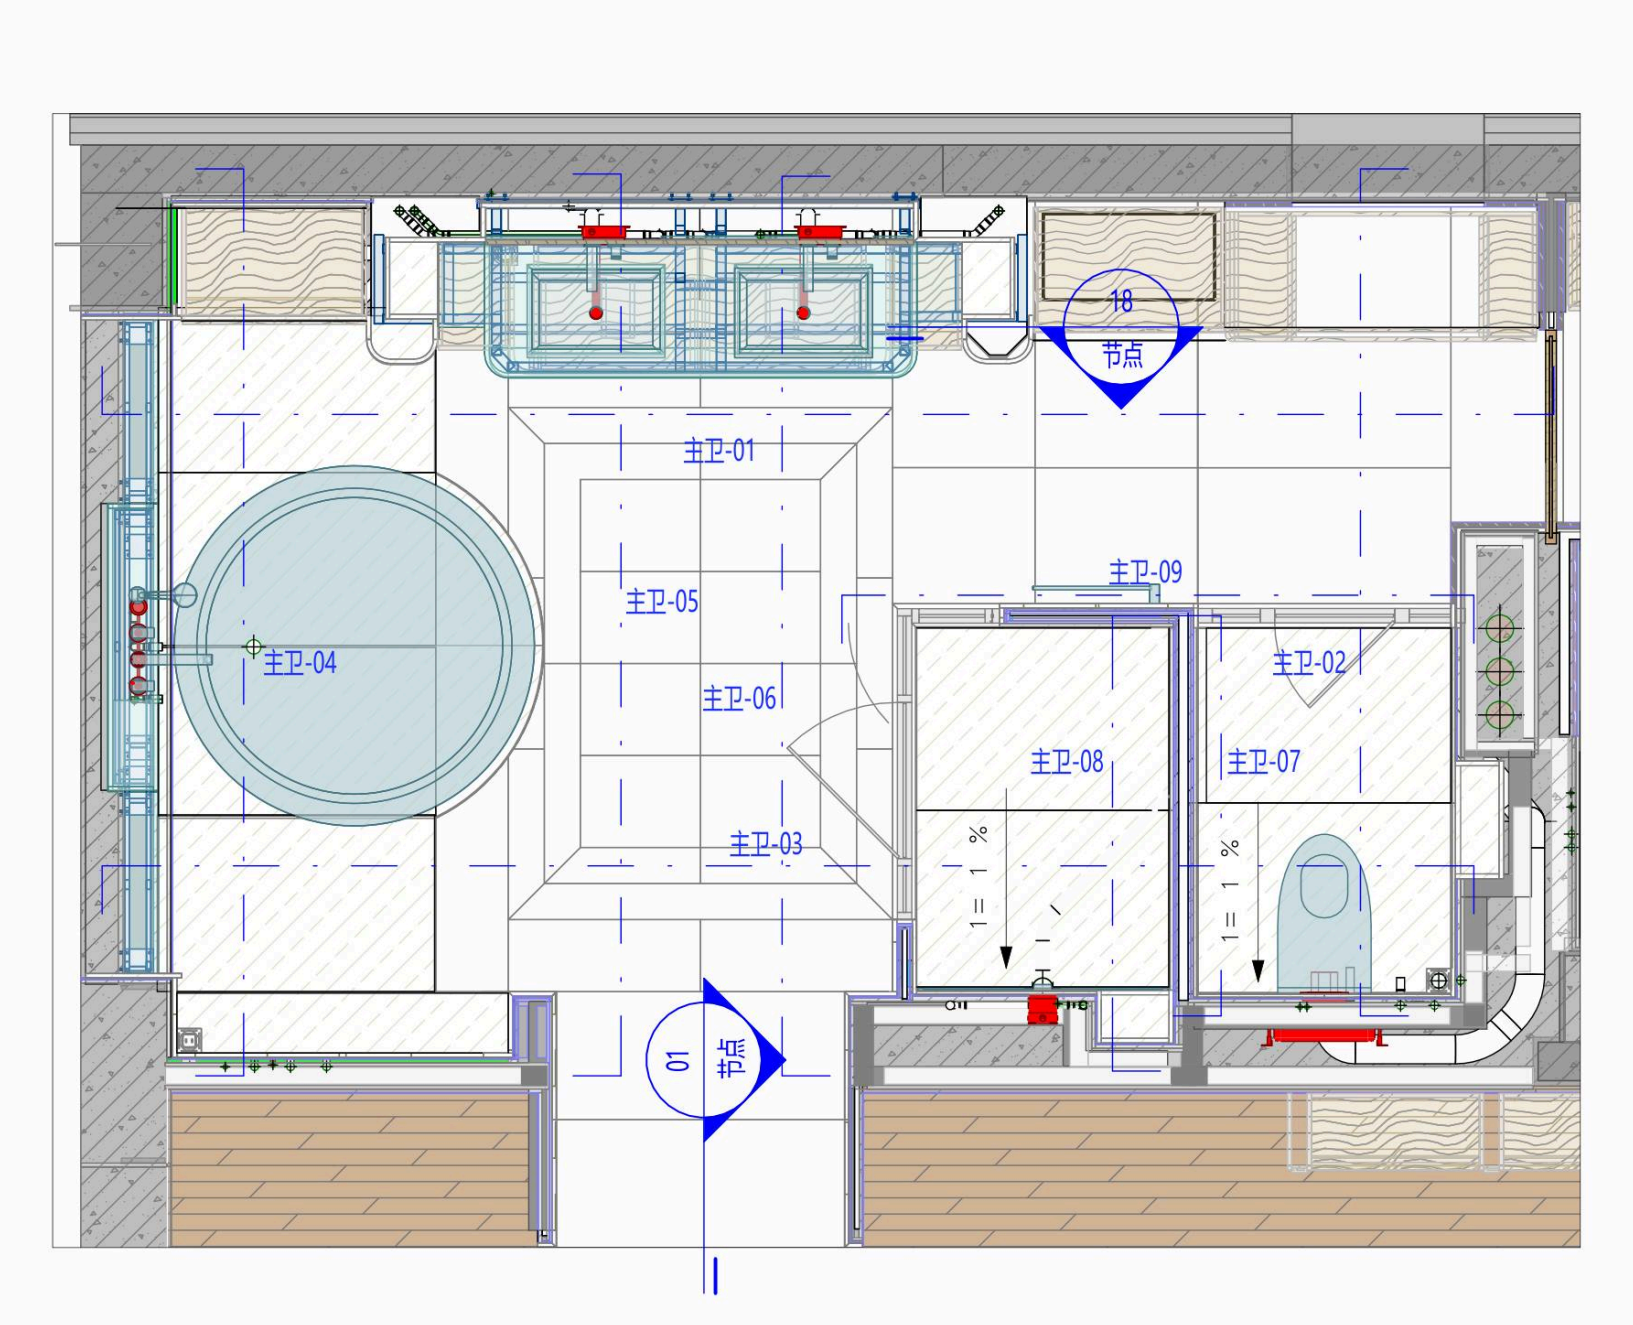
16 节点
主卫-01
主卫-05
主卫-06
主卫-03
主卫-04
主卫-09
主卫-08
主卫-02
主卫-07
01 节点

索引图

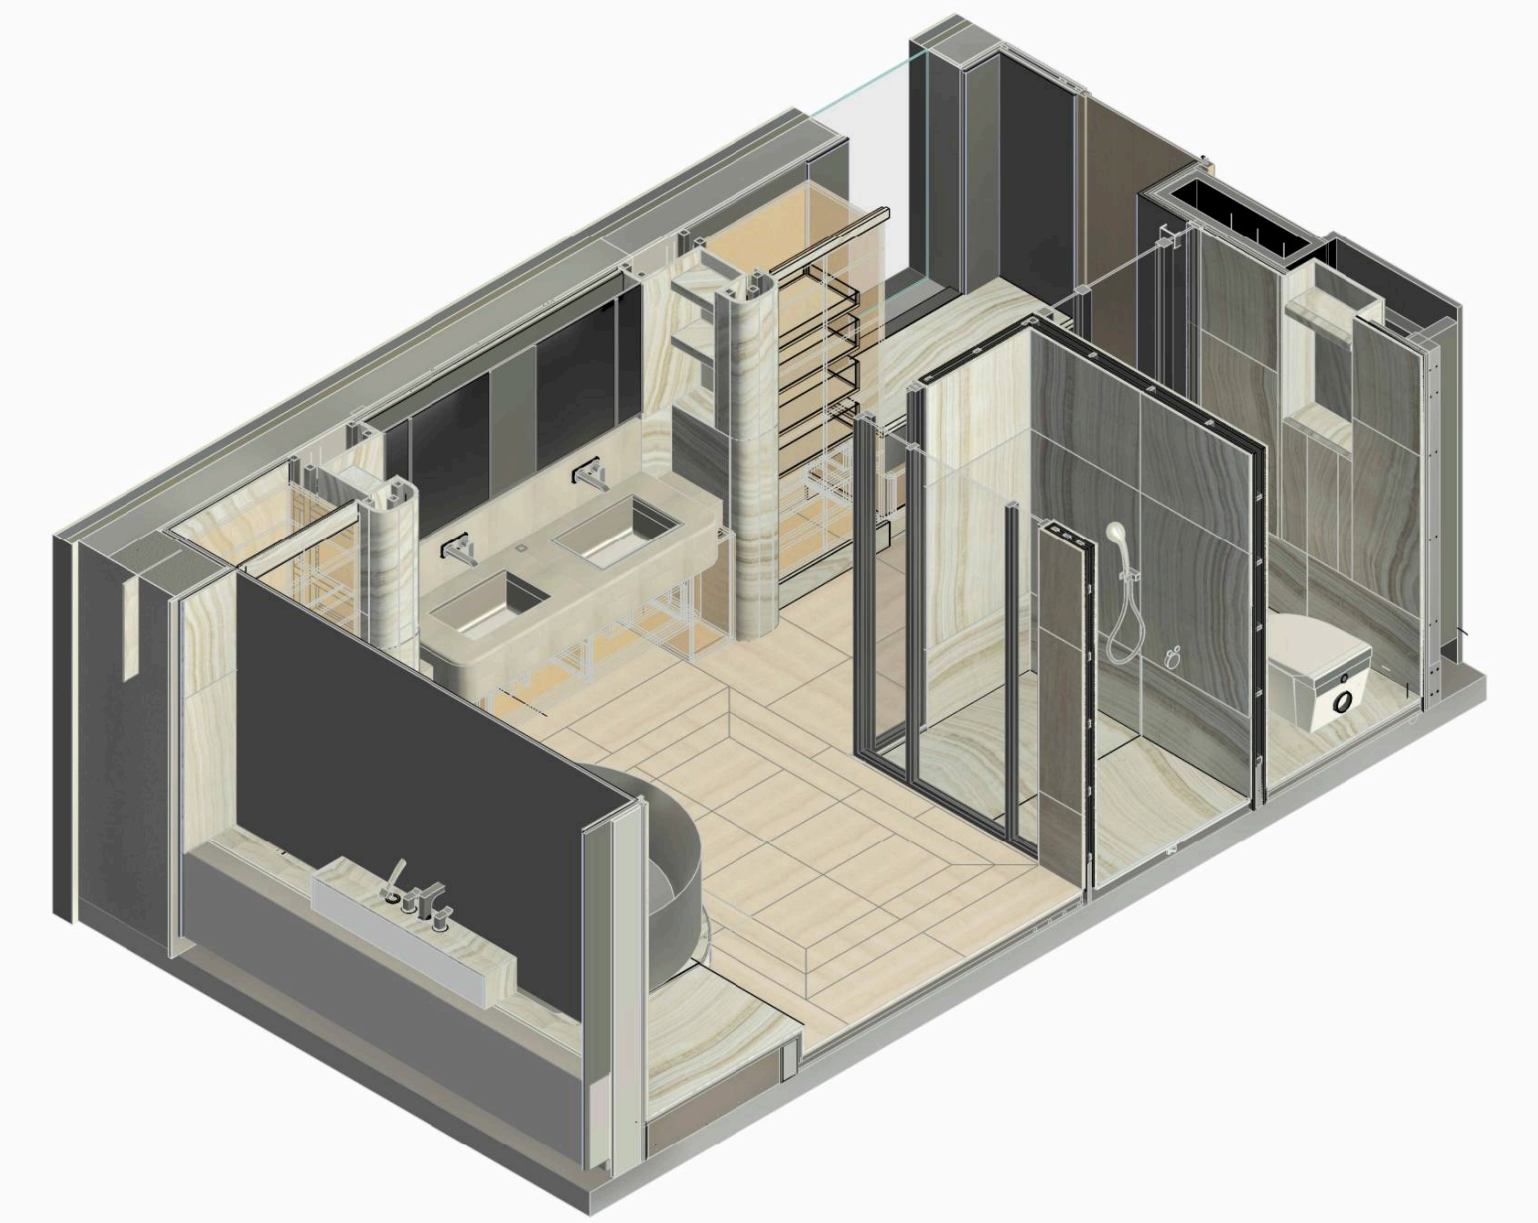

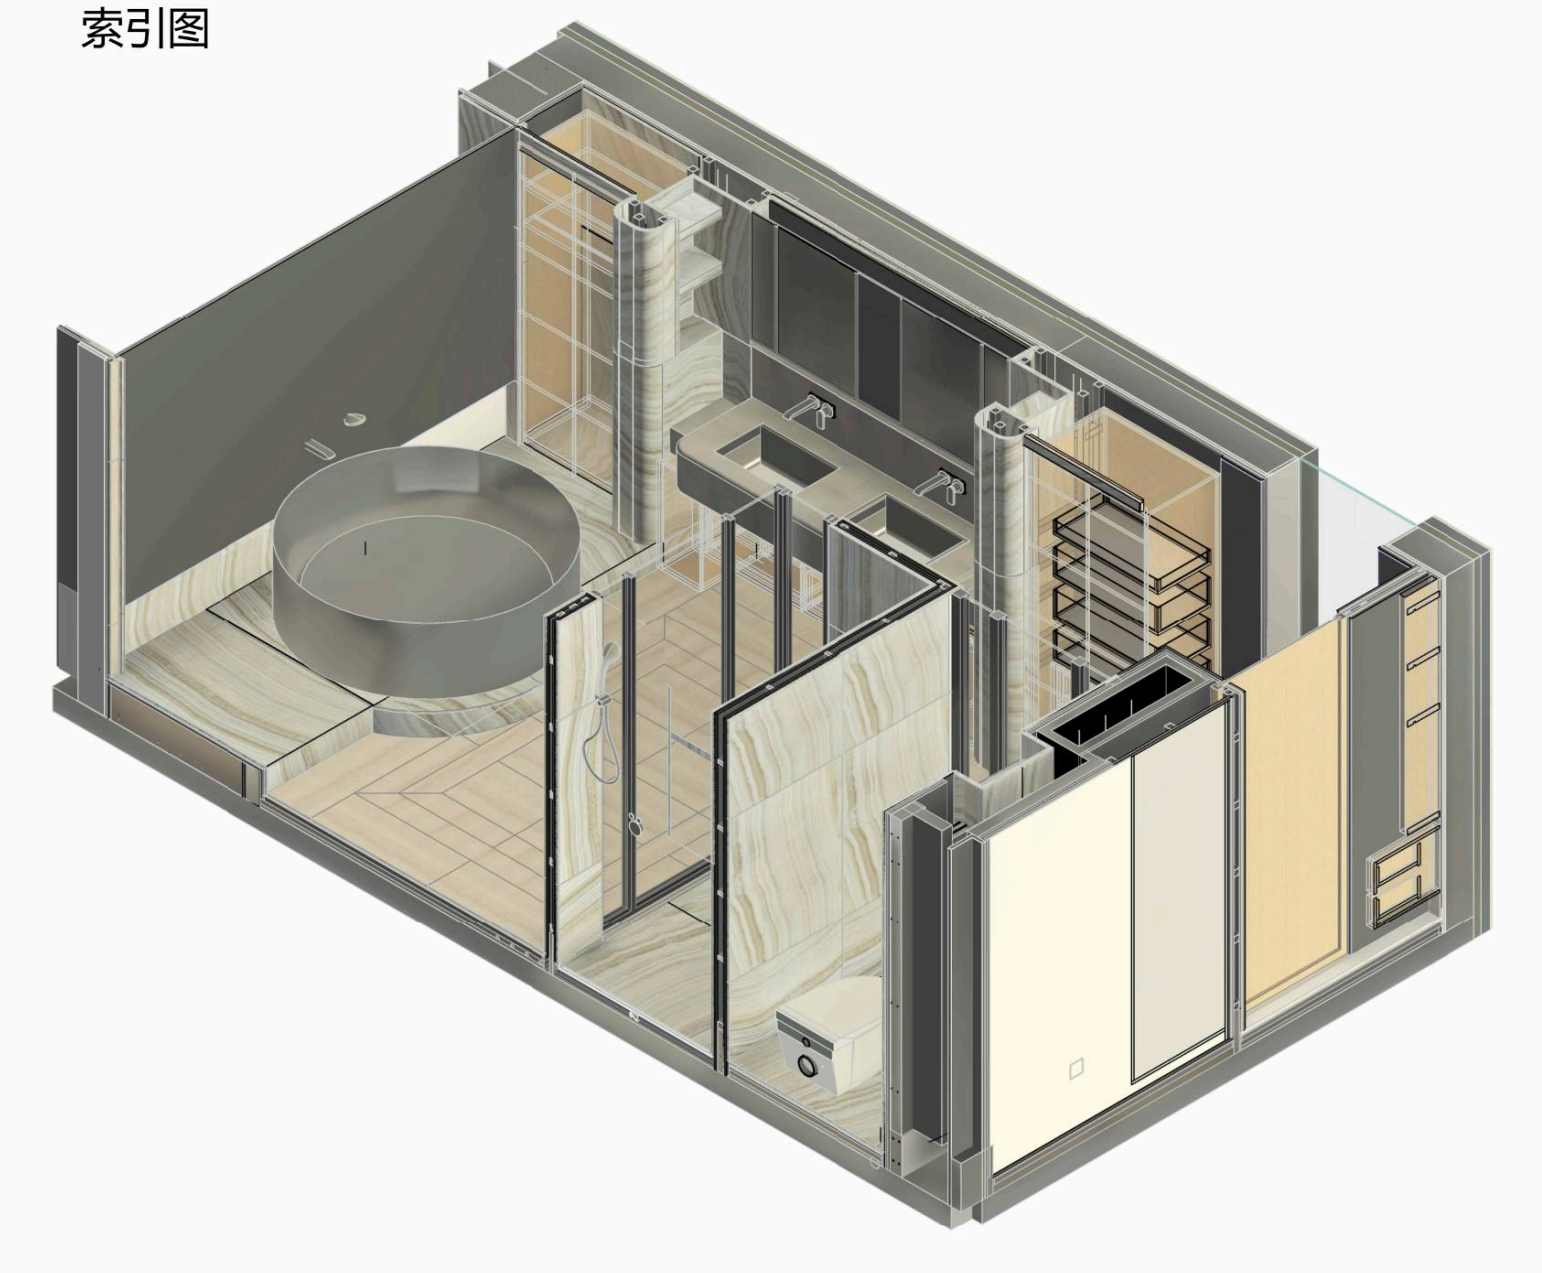

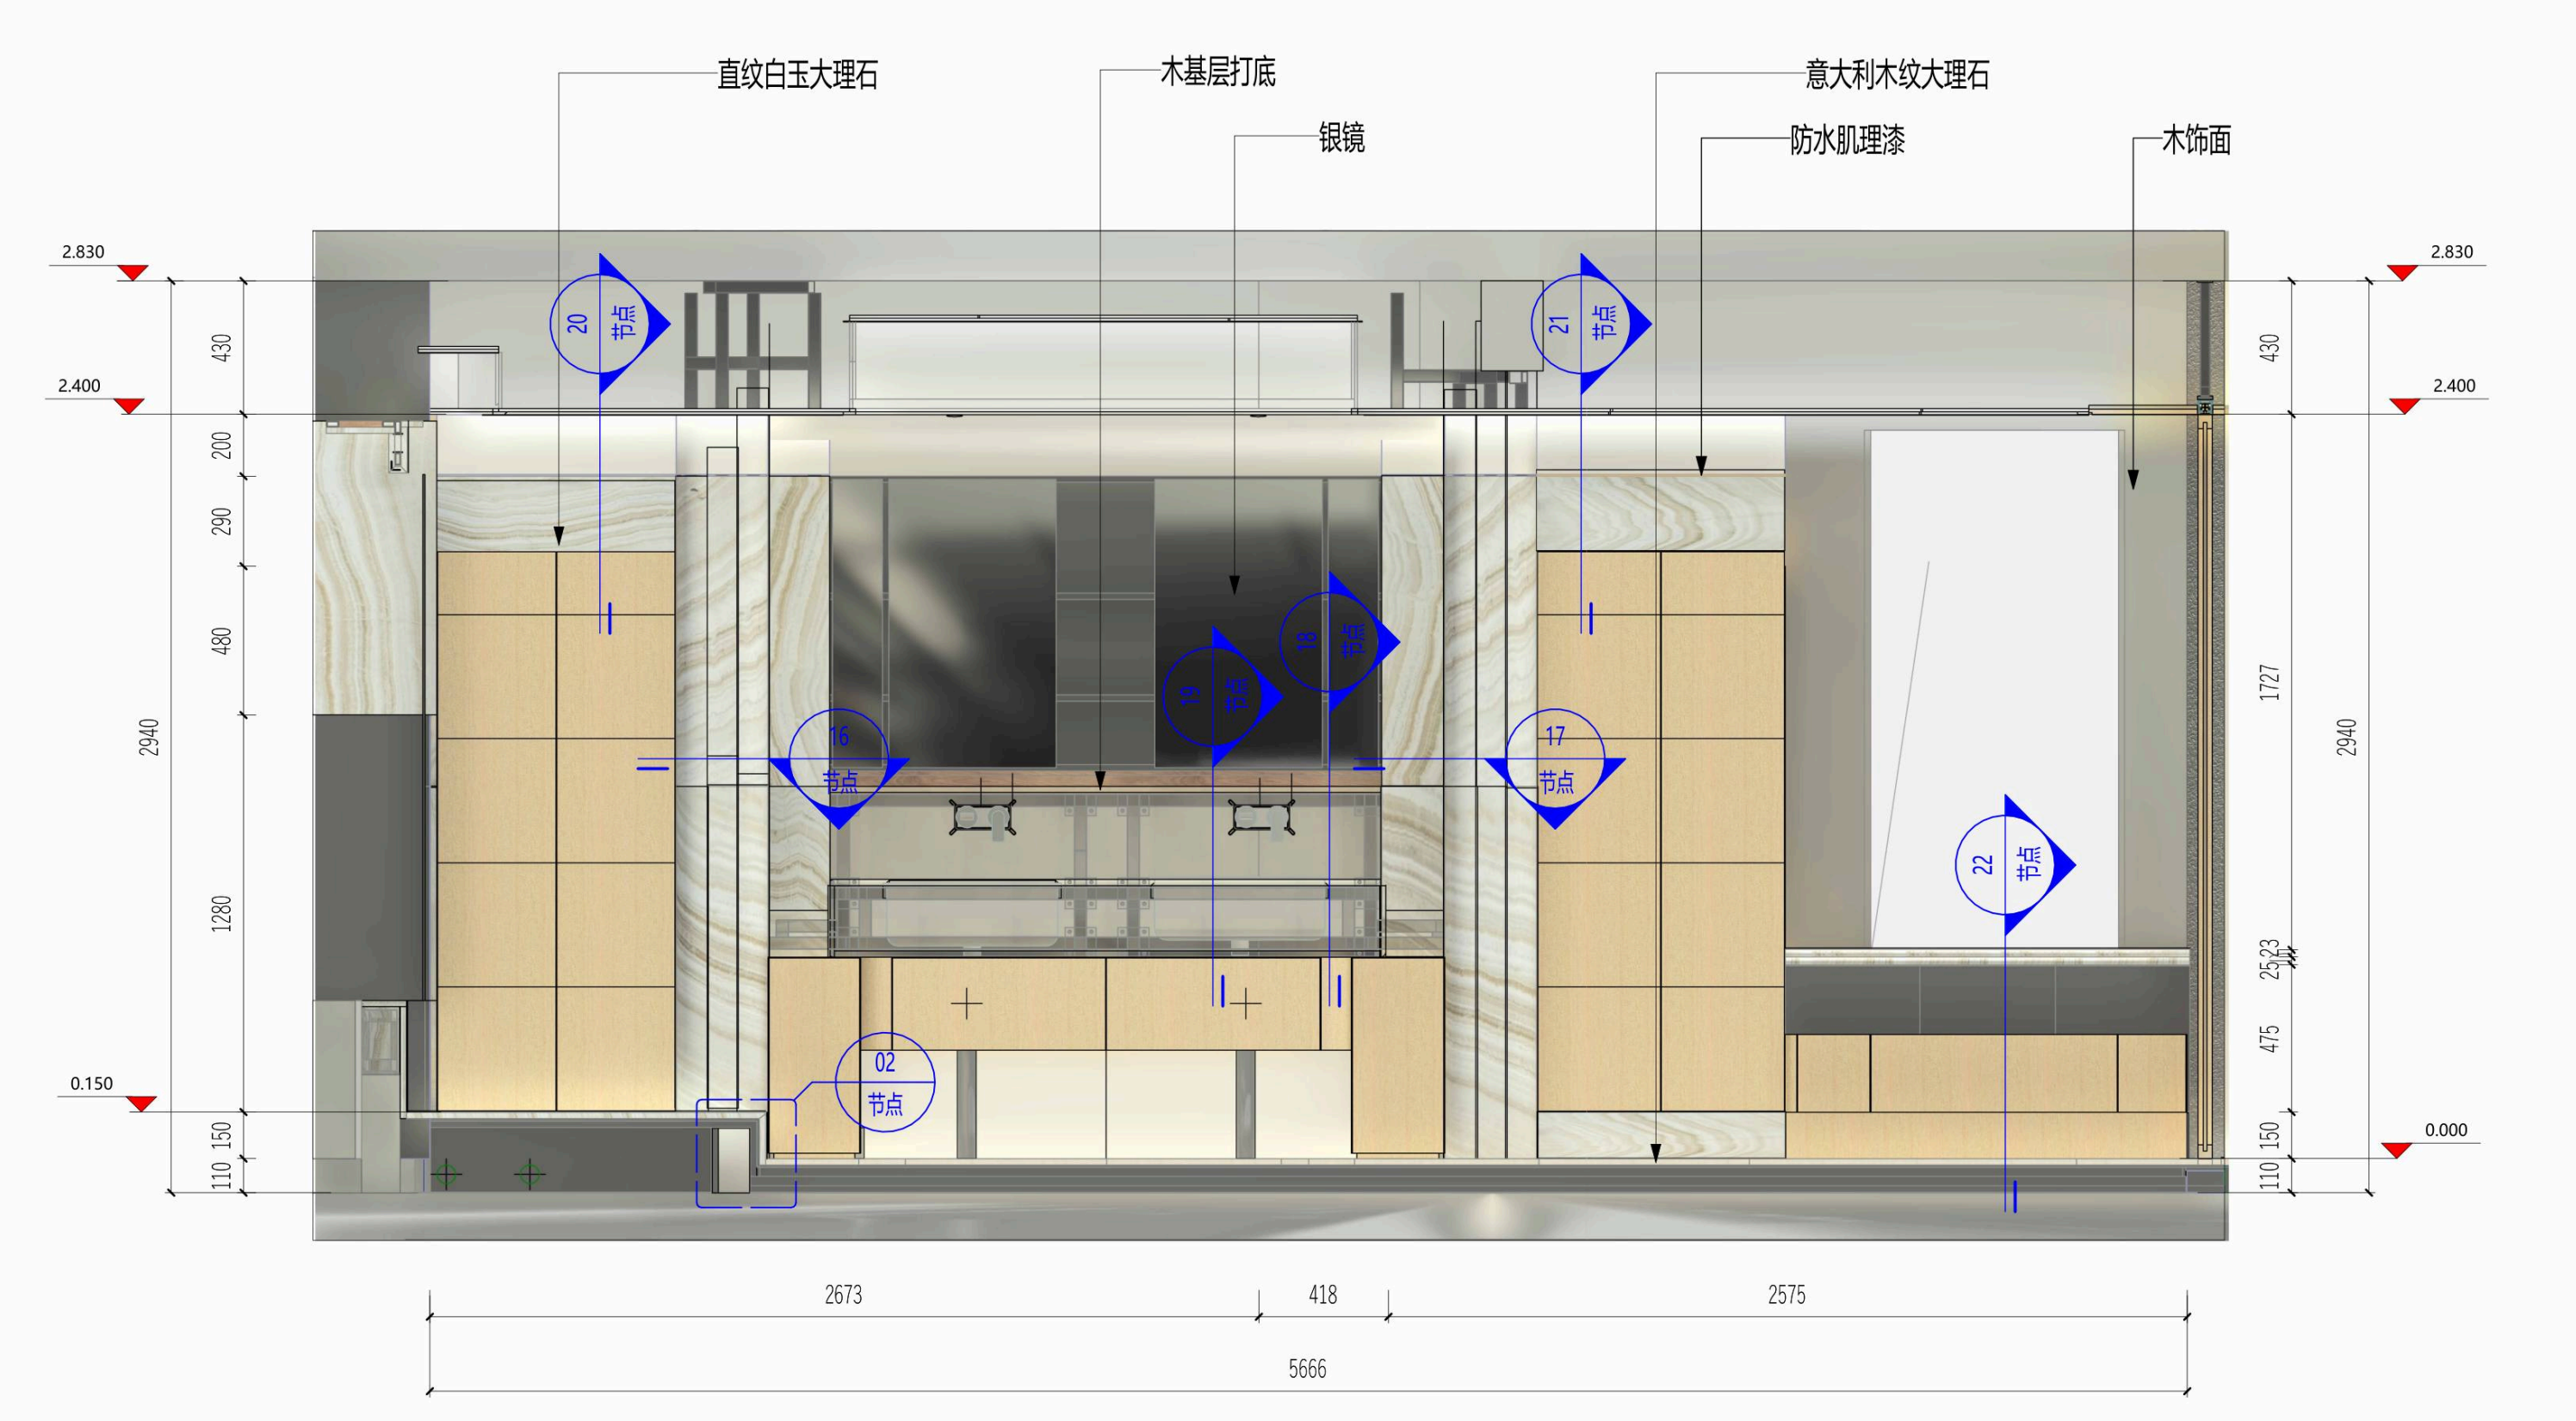
直纹白玉大理石
木基层打底
银镜
意大利木纹大理石
防水肌理漆
木饰面
2.830
2.400
0.150
2.830
2.400
0.000
20 节点
21 节点
02 节点
17 节点
22 节点
430
200
290
480
1280
150
110
2940
1727
2523
475
2673
418
2575
5666

主卫-01

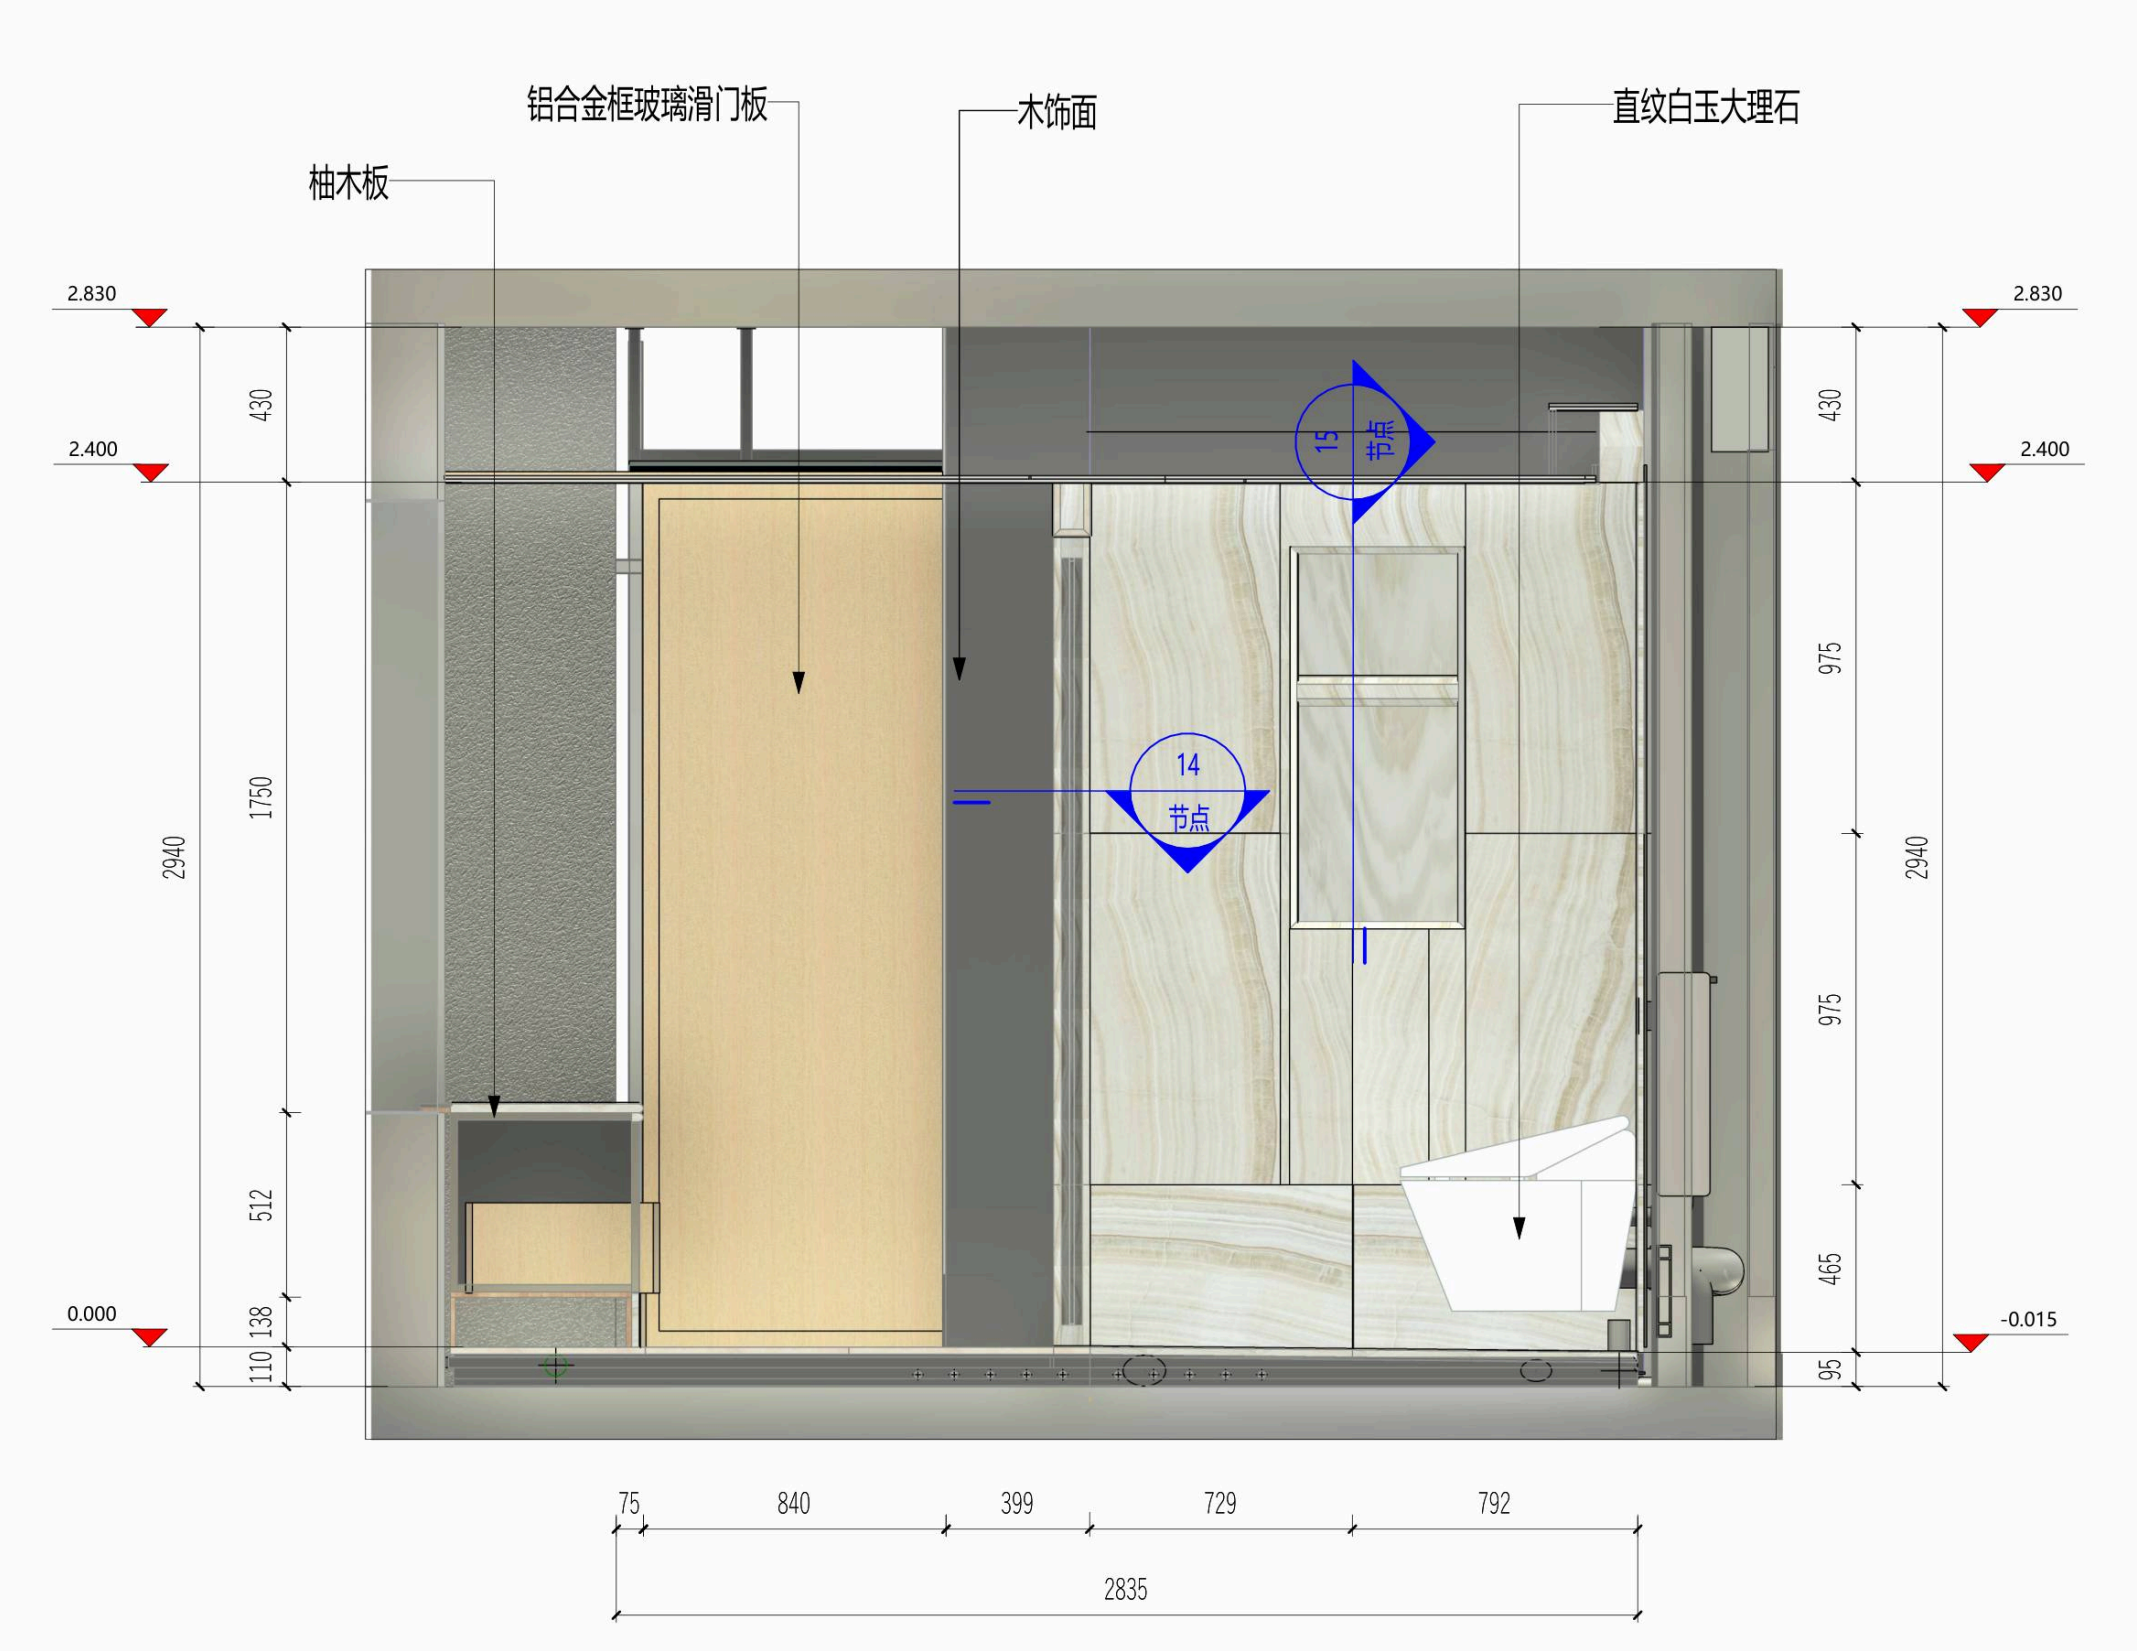
铝合金框玻璃滑门板
柚木板
木饰面
直纹白玉大理石
2.830
2.400
0.000
2.830
2.400
-0.015
15 节点
14 节点
430
1750
512
138
2940
975
975
465
75
840
399
729
792
2835

主卫-02

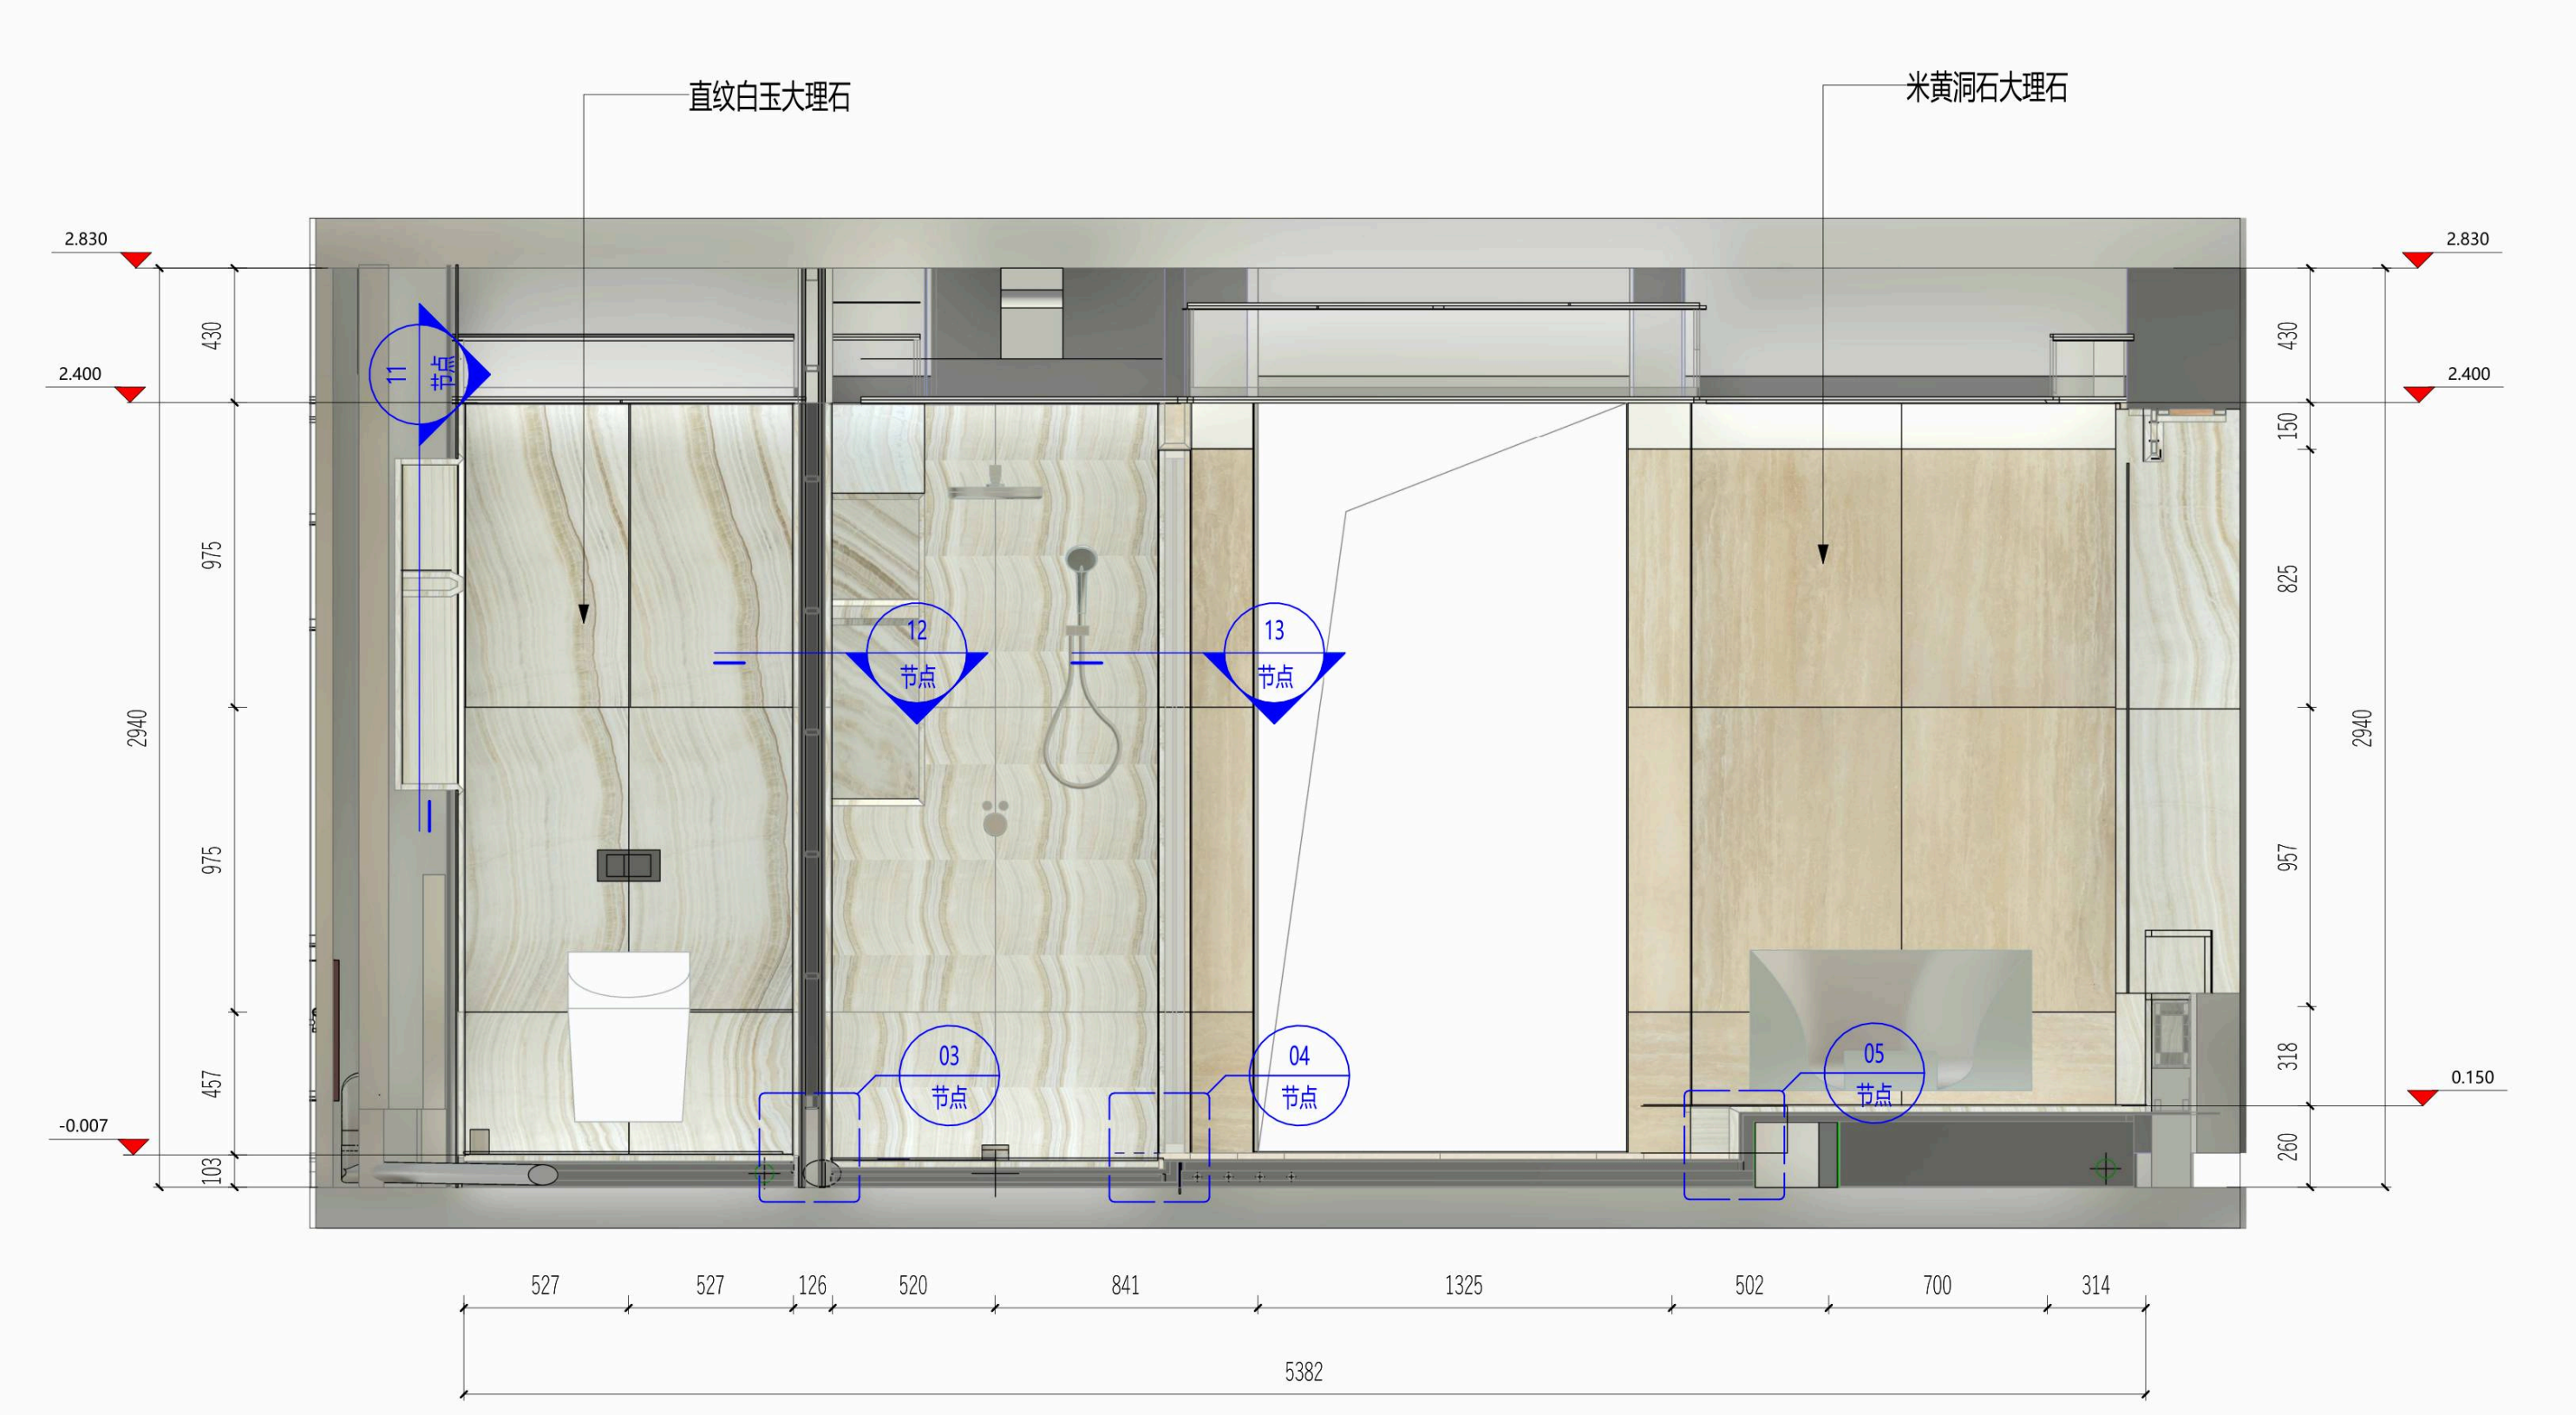
直纹白玉大理石
米黄洞石大理石
2.830
2.400
-0.007
2.830
2.400
0.150
11 节点
12 节点
13 节点
03 节点
04 节点
05 节点
430
975
975
2940
457
103
150
825
957
318
260
527
527
126
520
841
1325
502
700
314
5382

主卫-03

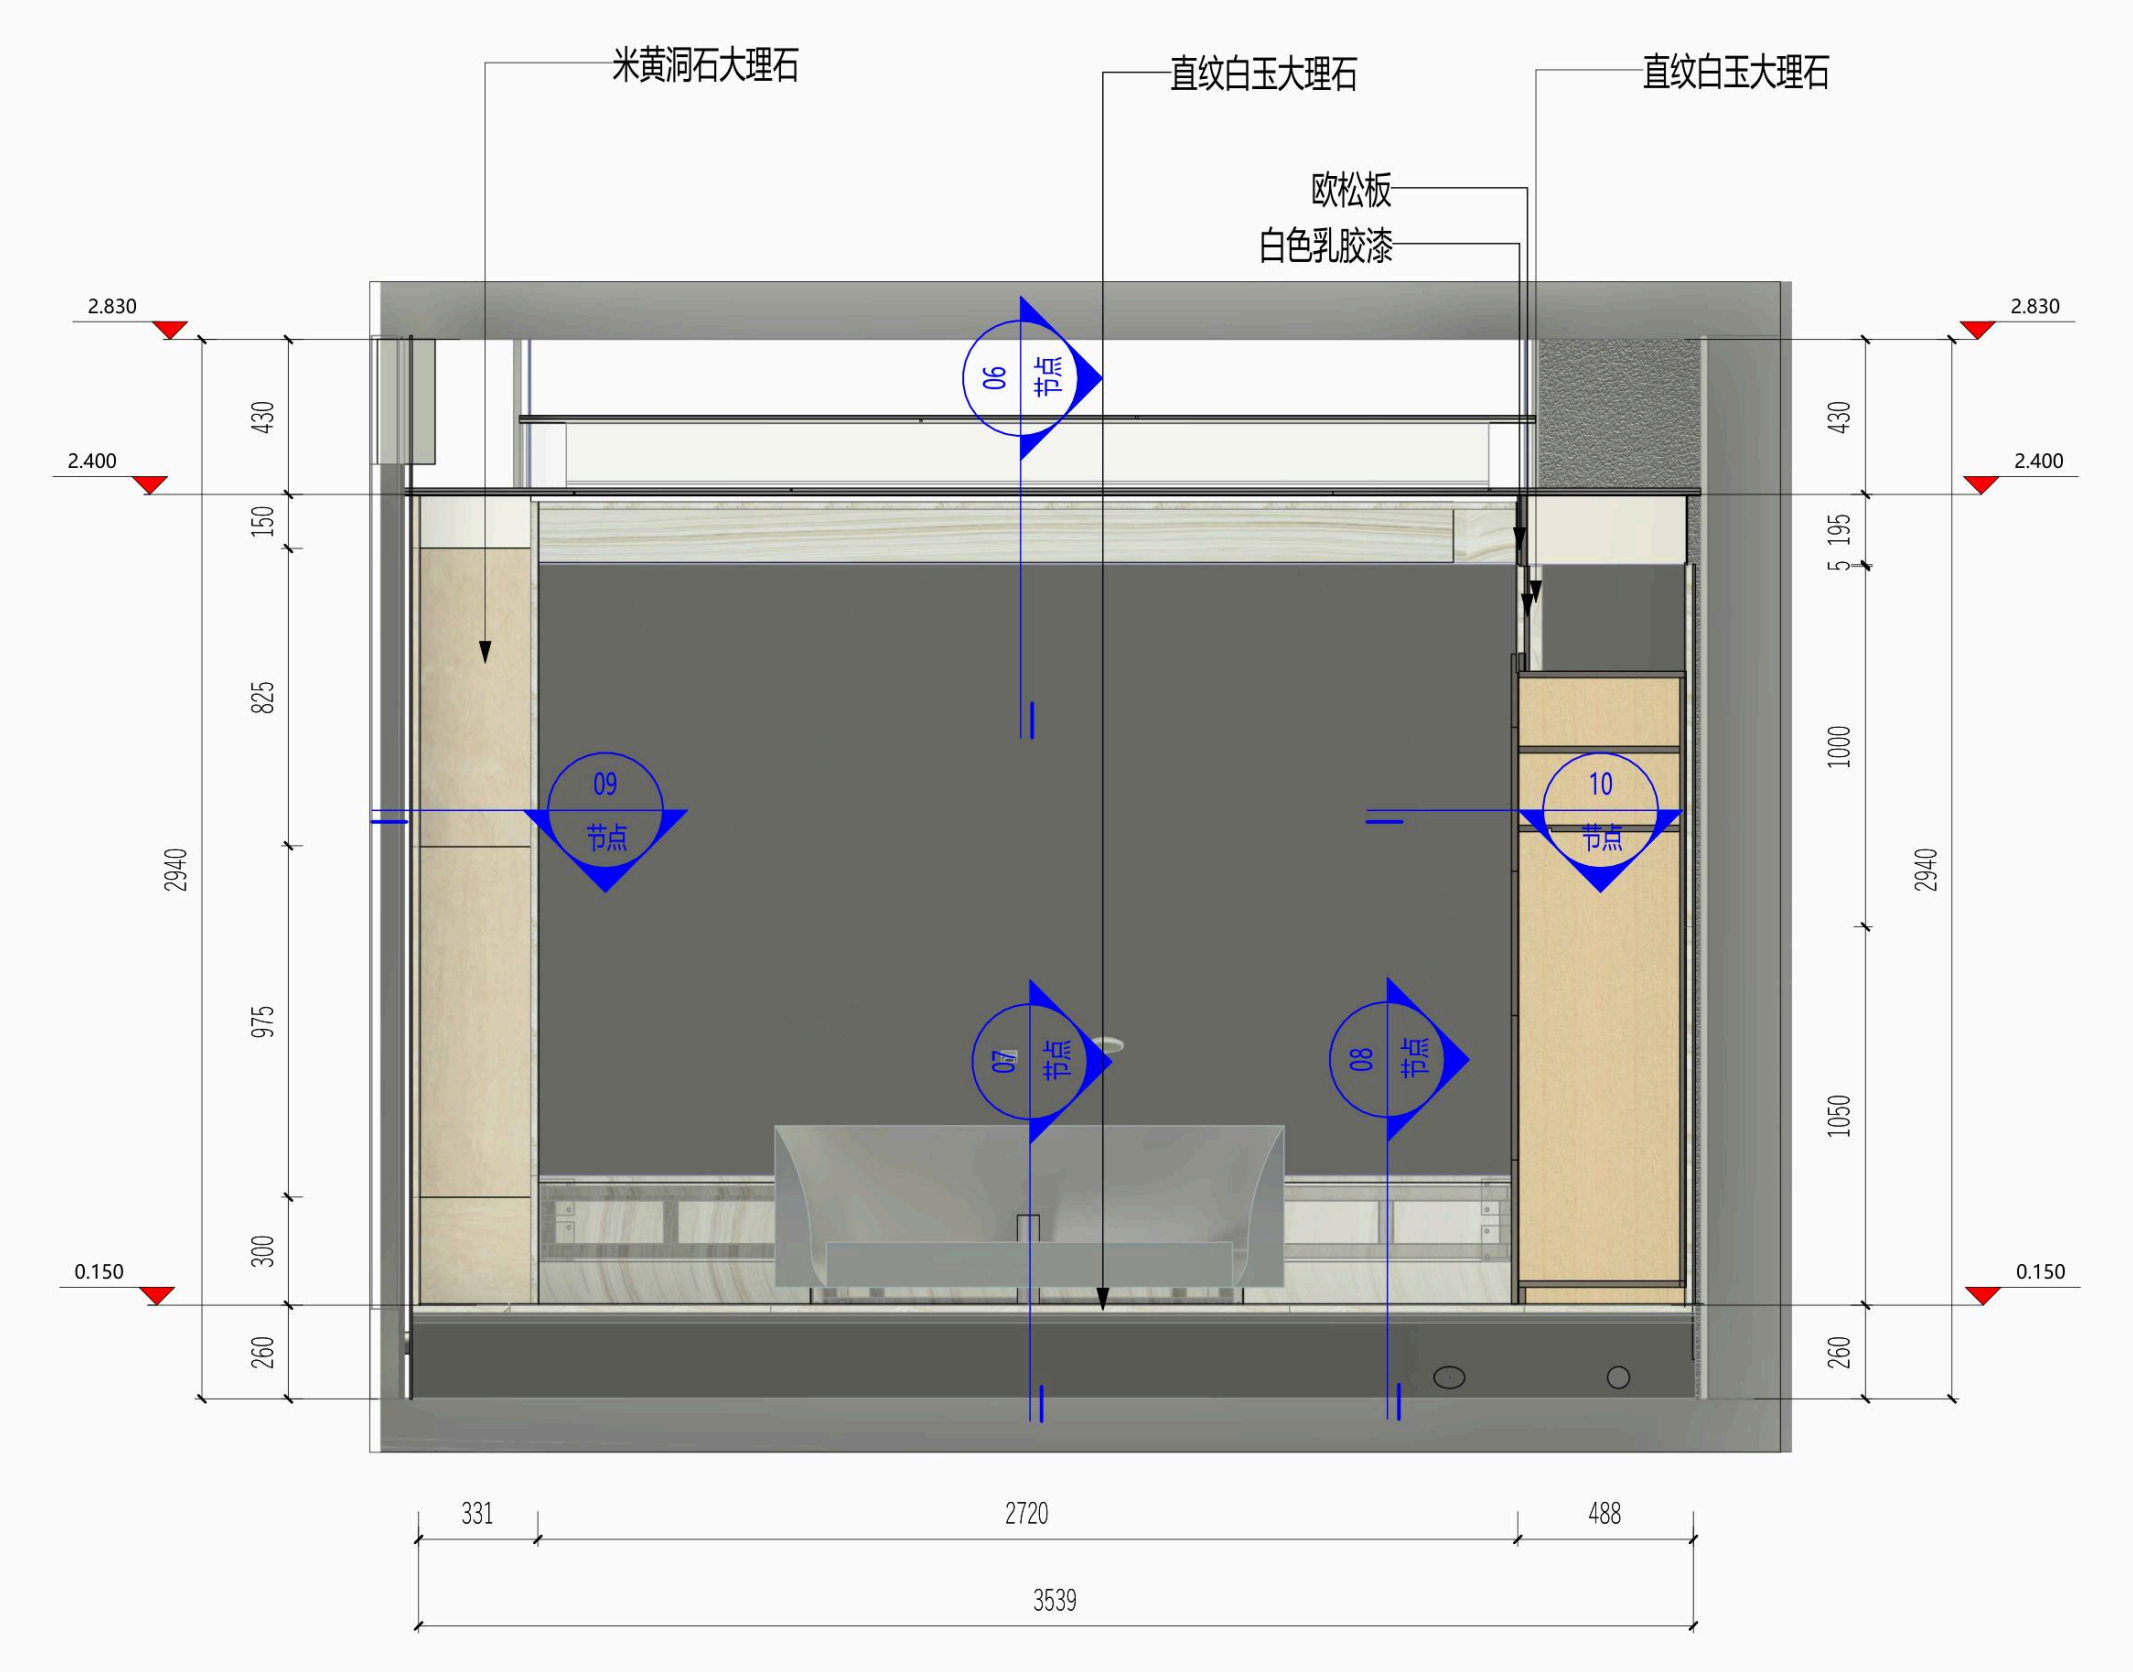
米黄洞石大理石
直纹白玉大理石
直纹白玉大理石
欧松板
白色乳胶漆
2.830
2.400
0.150
2.830
2.400
0.150
09 节点
10 节点
07 节点
08 节点
331
2720
488
3539

主卫-04

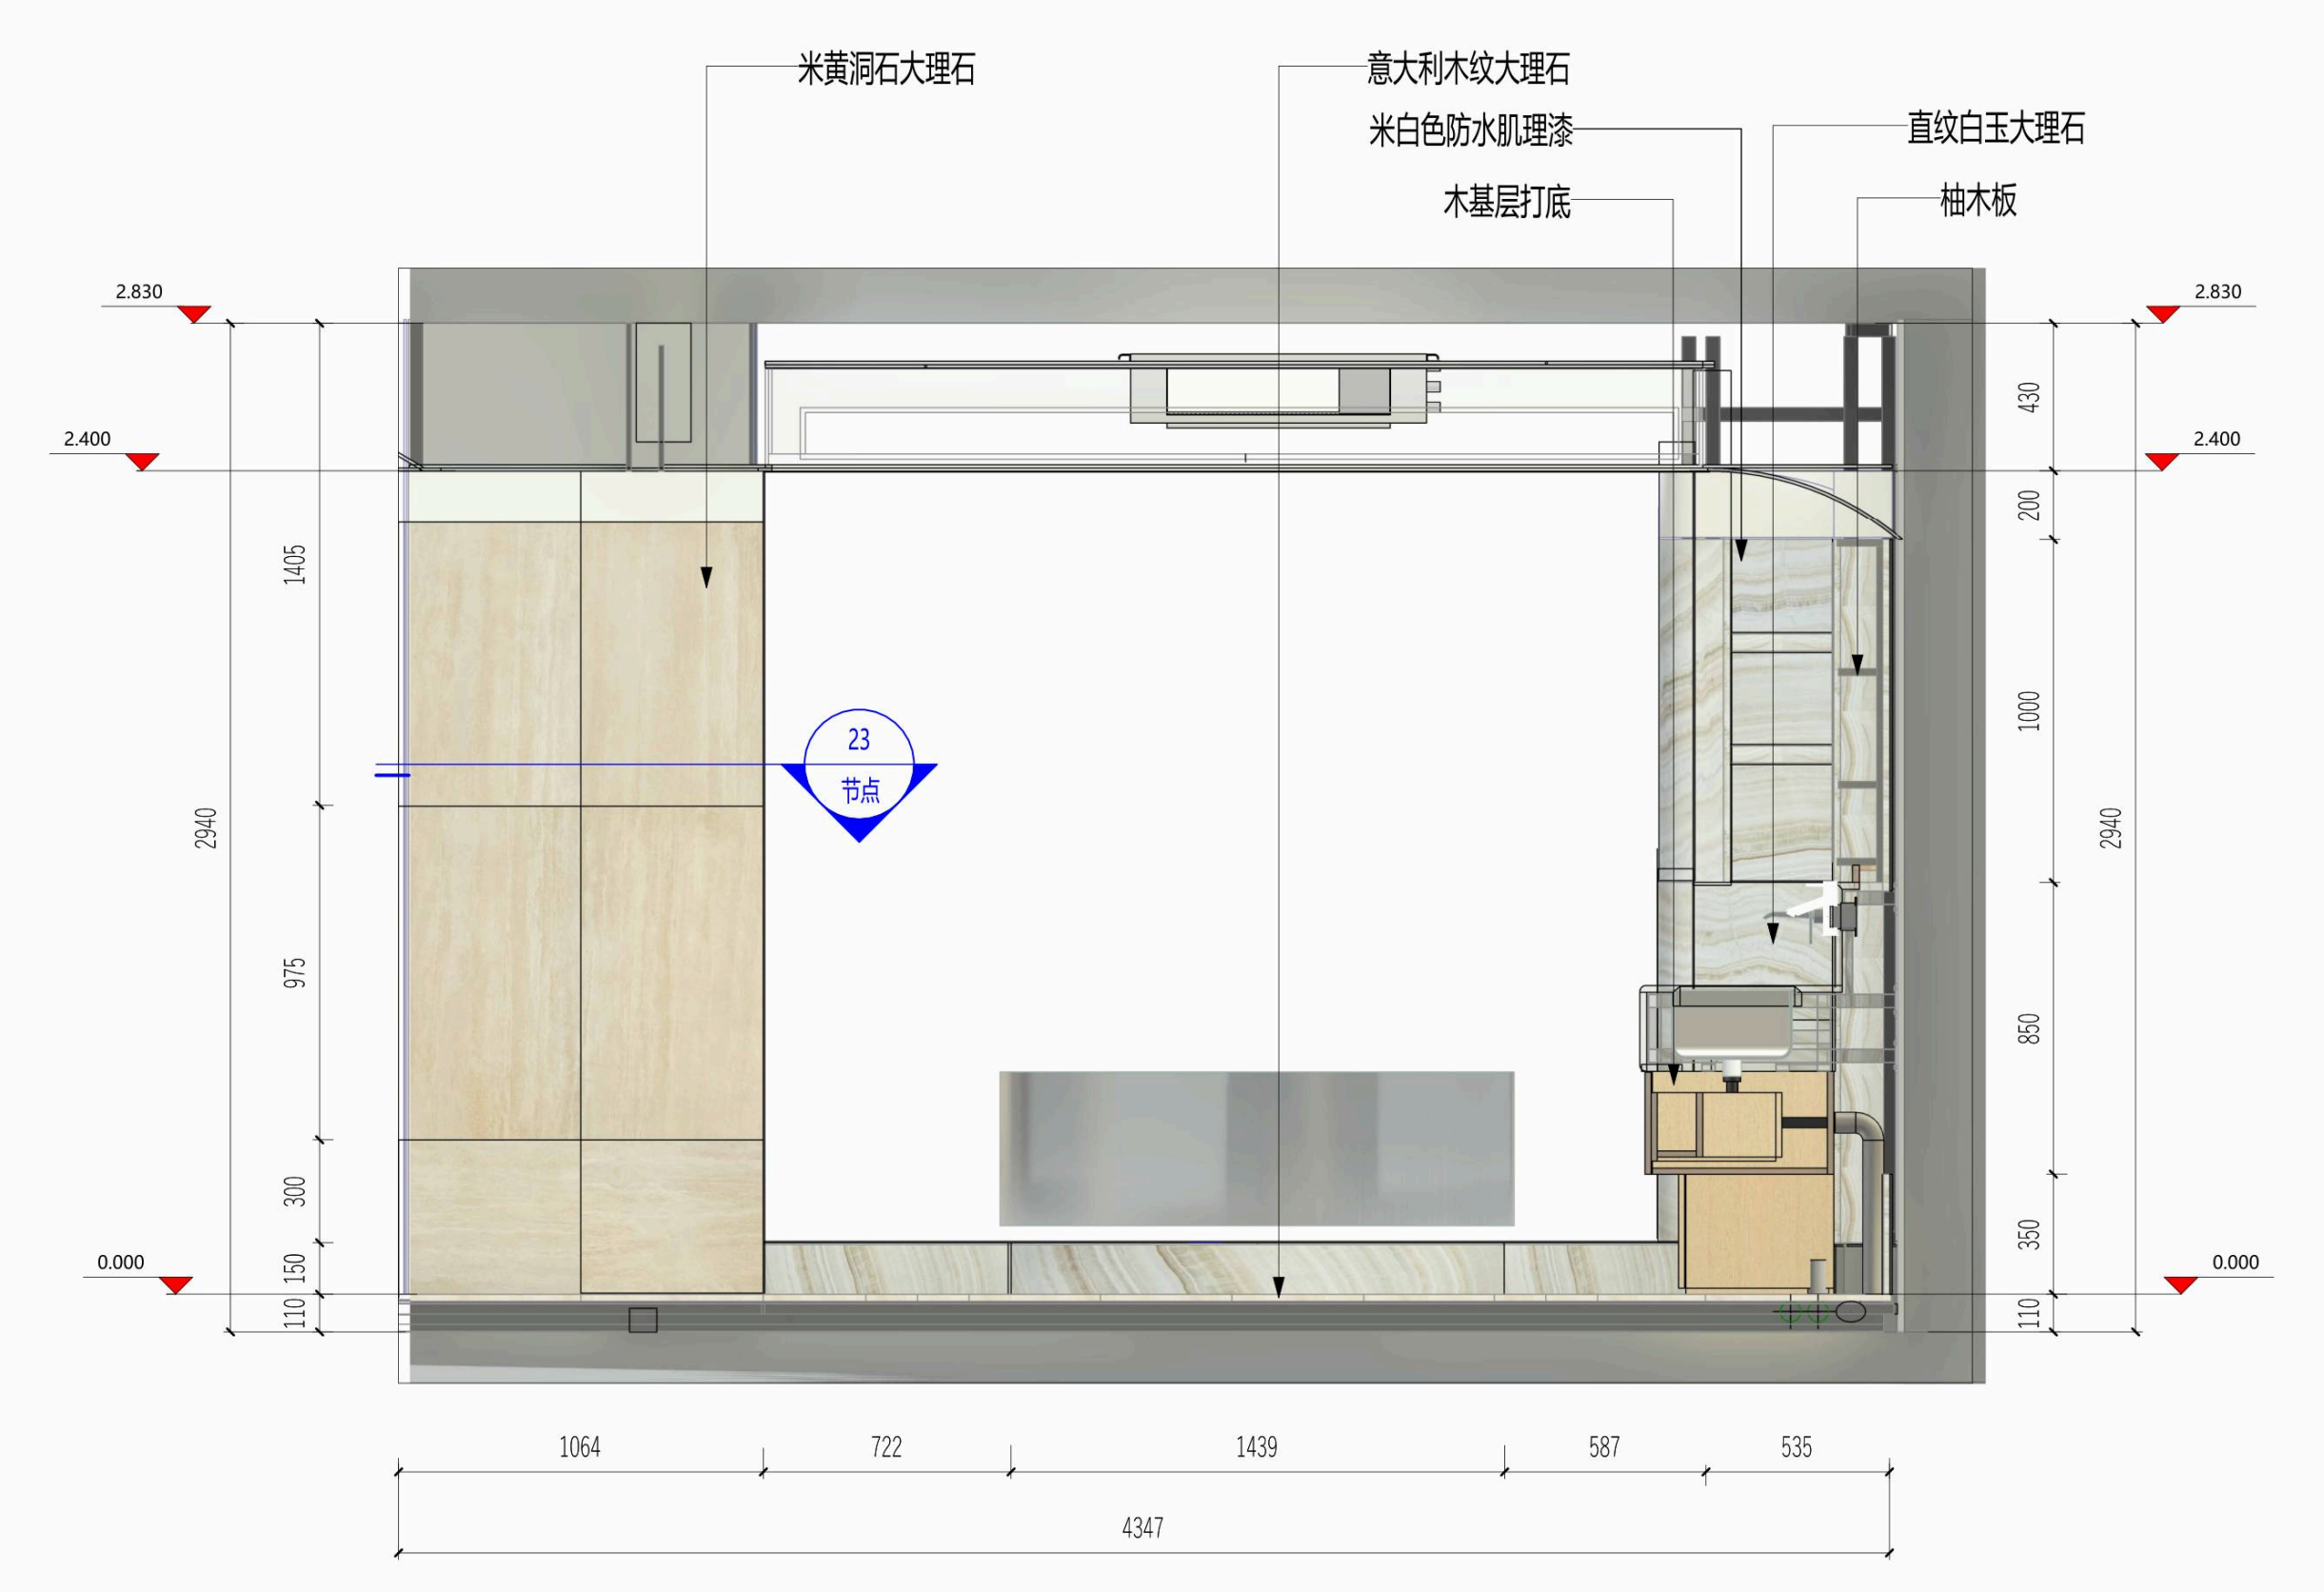
米黄洞石大理石
意大利木纹大理石
米白色防水肌理漆
木基层打底
直纹白玉大理石
柚木板
2.830
2.400
0.000
2.830
2.400
0.000
23 节点
1405
975
300
430
200
1000
850
350
2940
1064
722
1439
587
535
4347

主卫-05

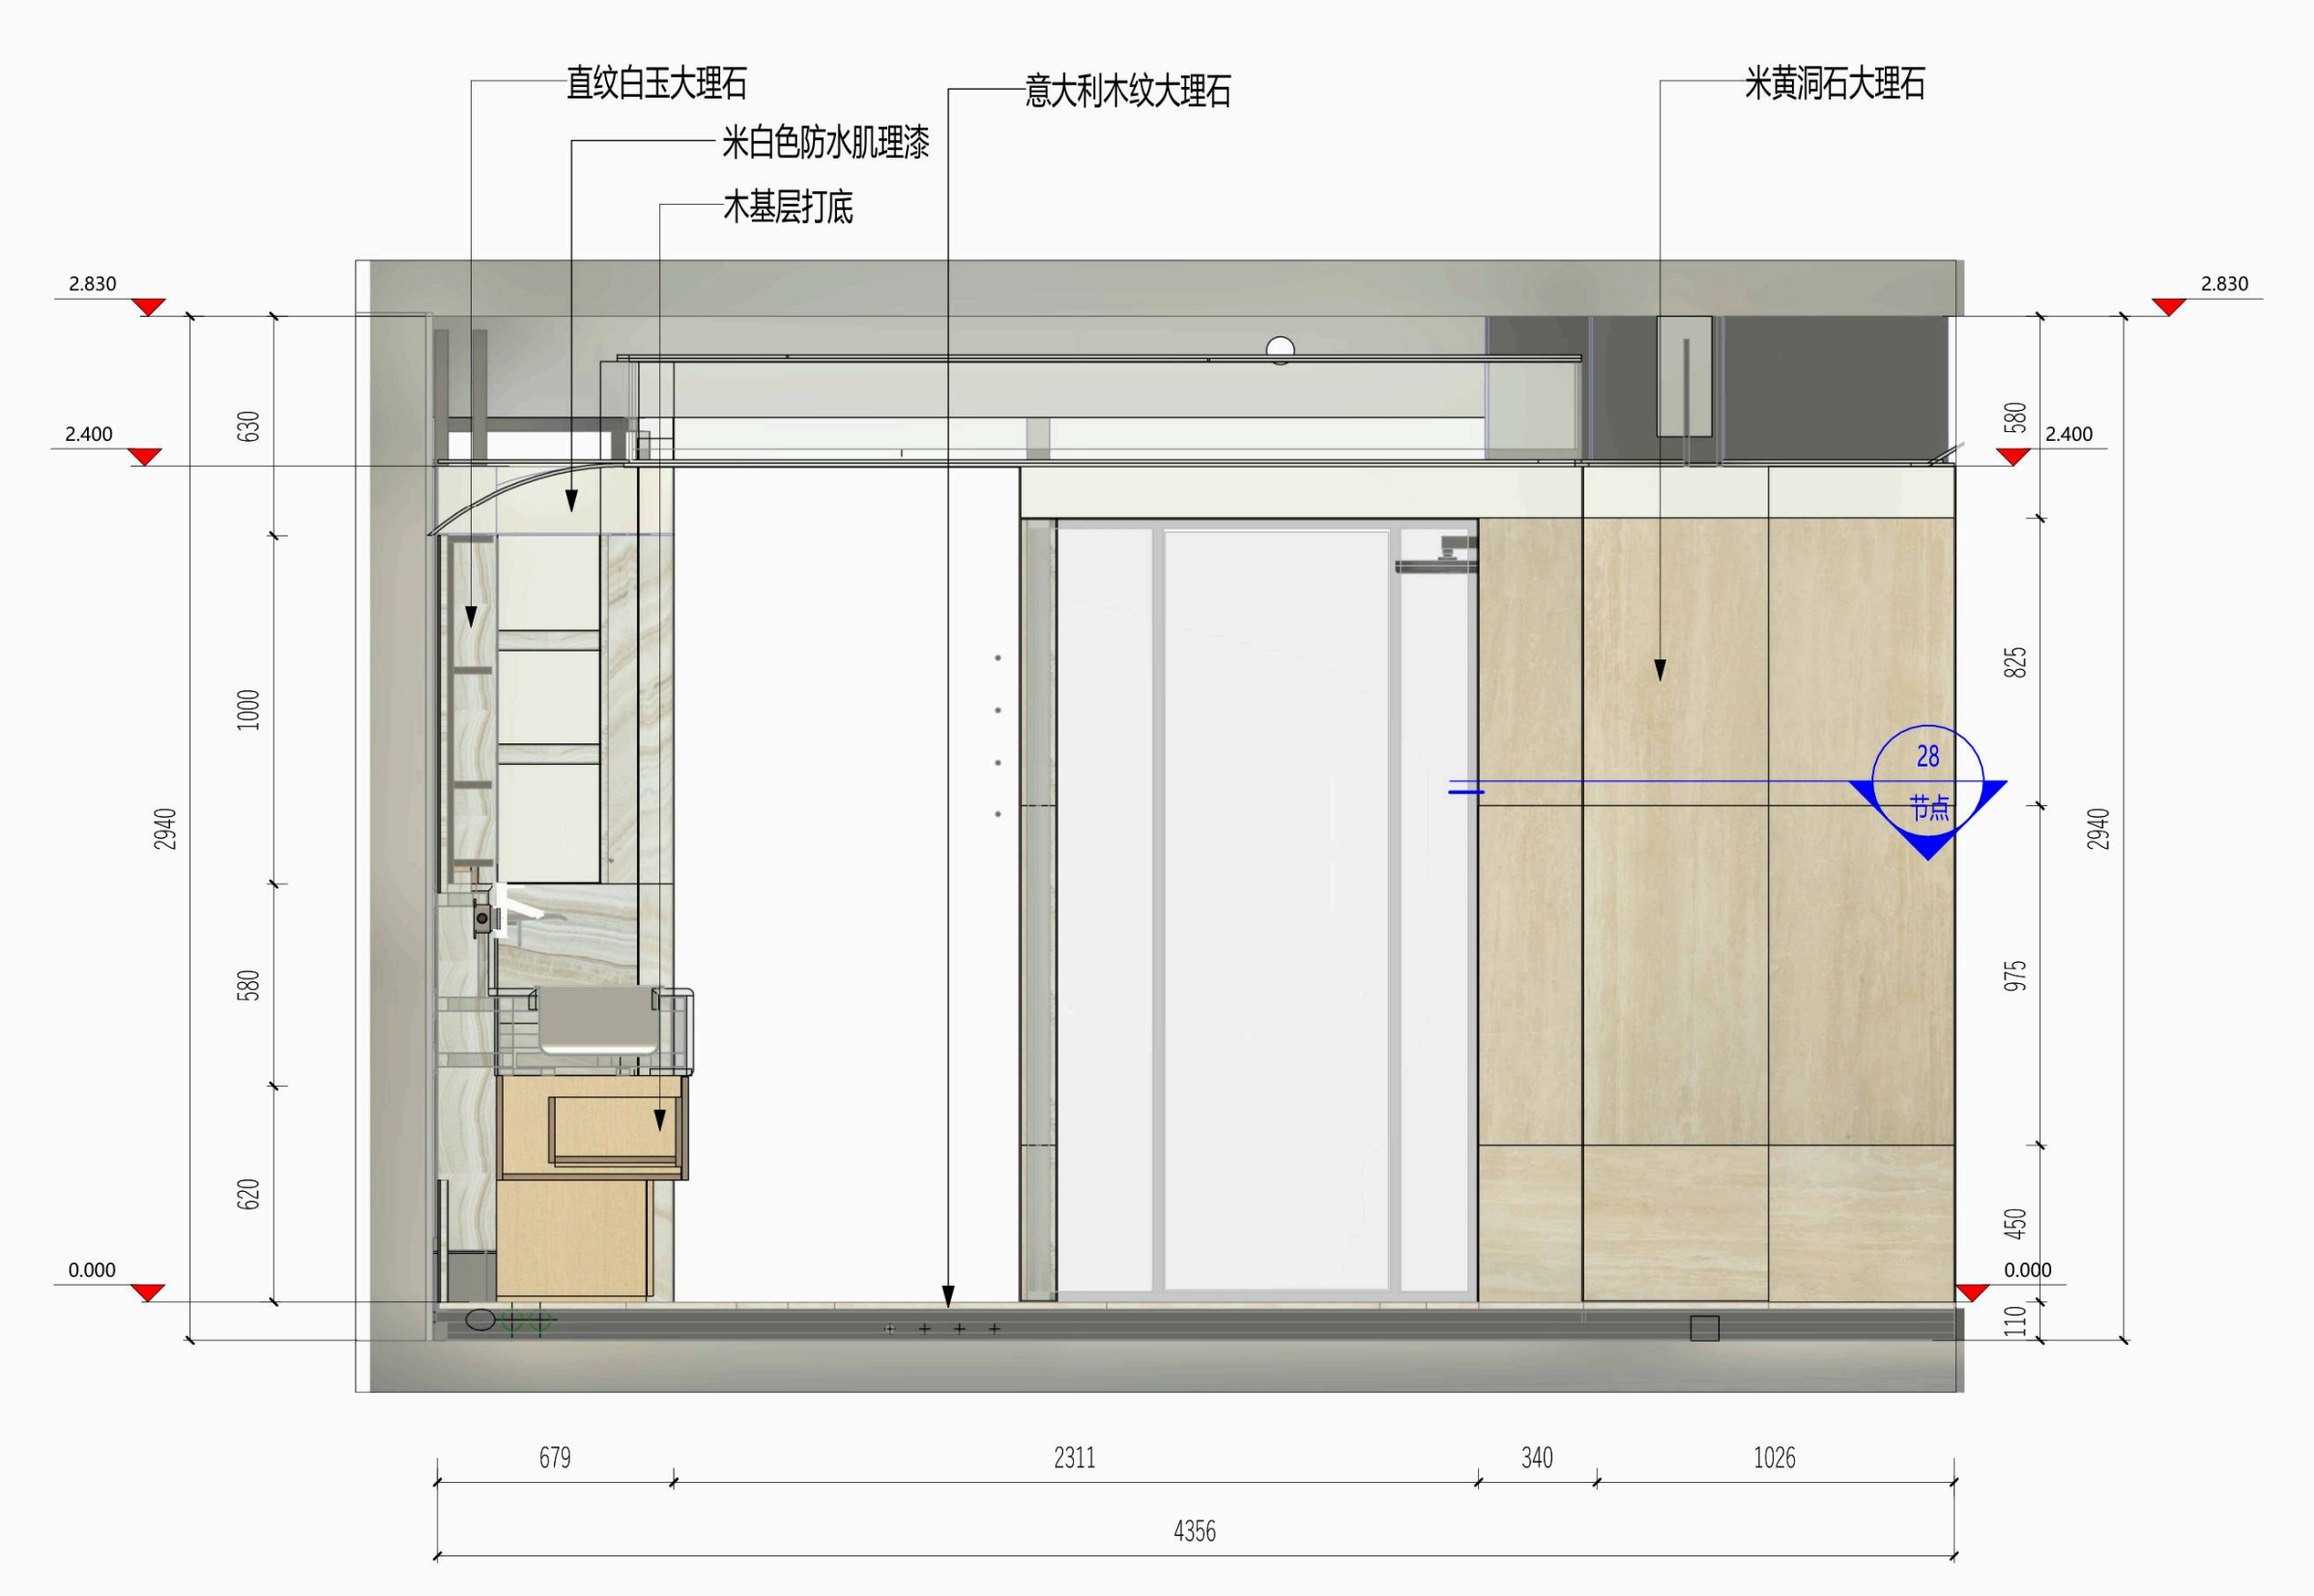
直纹白玉大理石
米白色防水肌理漆
木基层打底
意大利木纹大理石
米黄洞石大理石
2.830
2.400
0.000
2.830
2.400
0.000
28 节点
630
1000
580
620
2940
580
825
975
450
679
2311
340
1026
4356

主卫-06

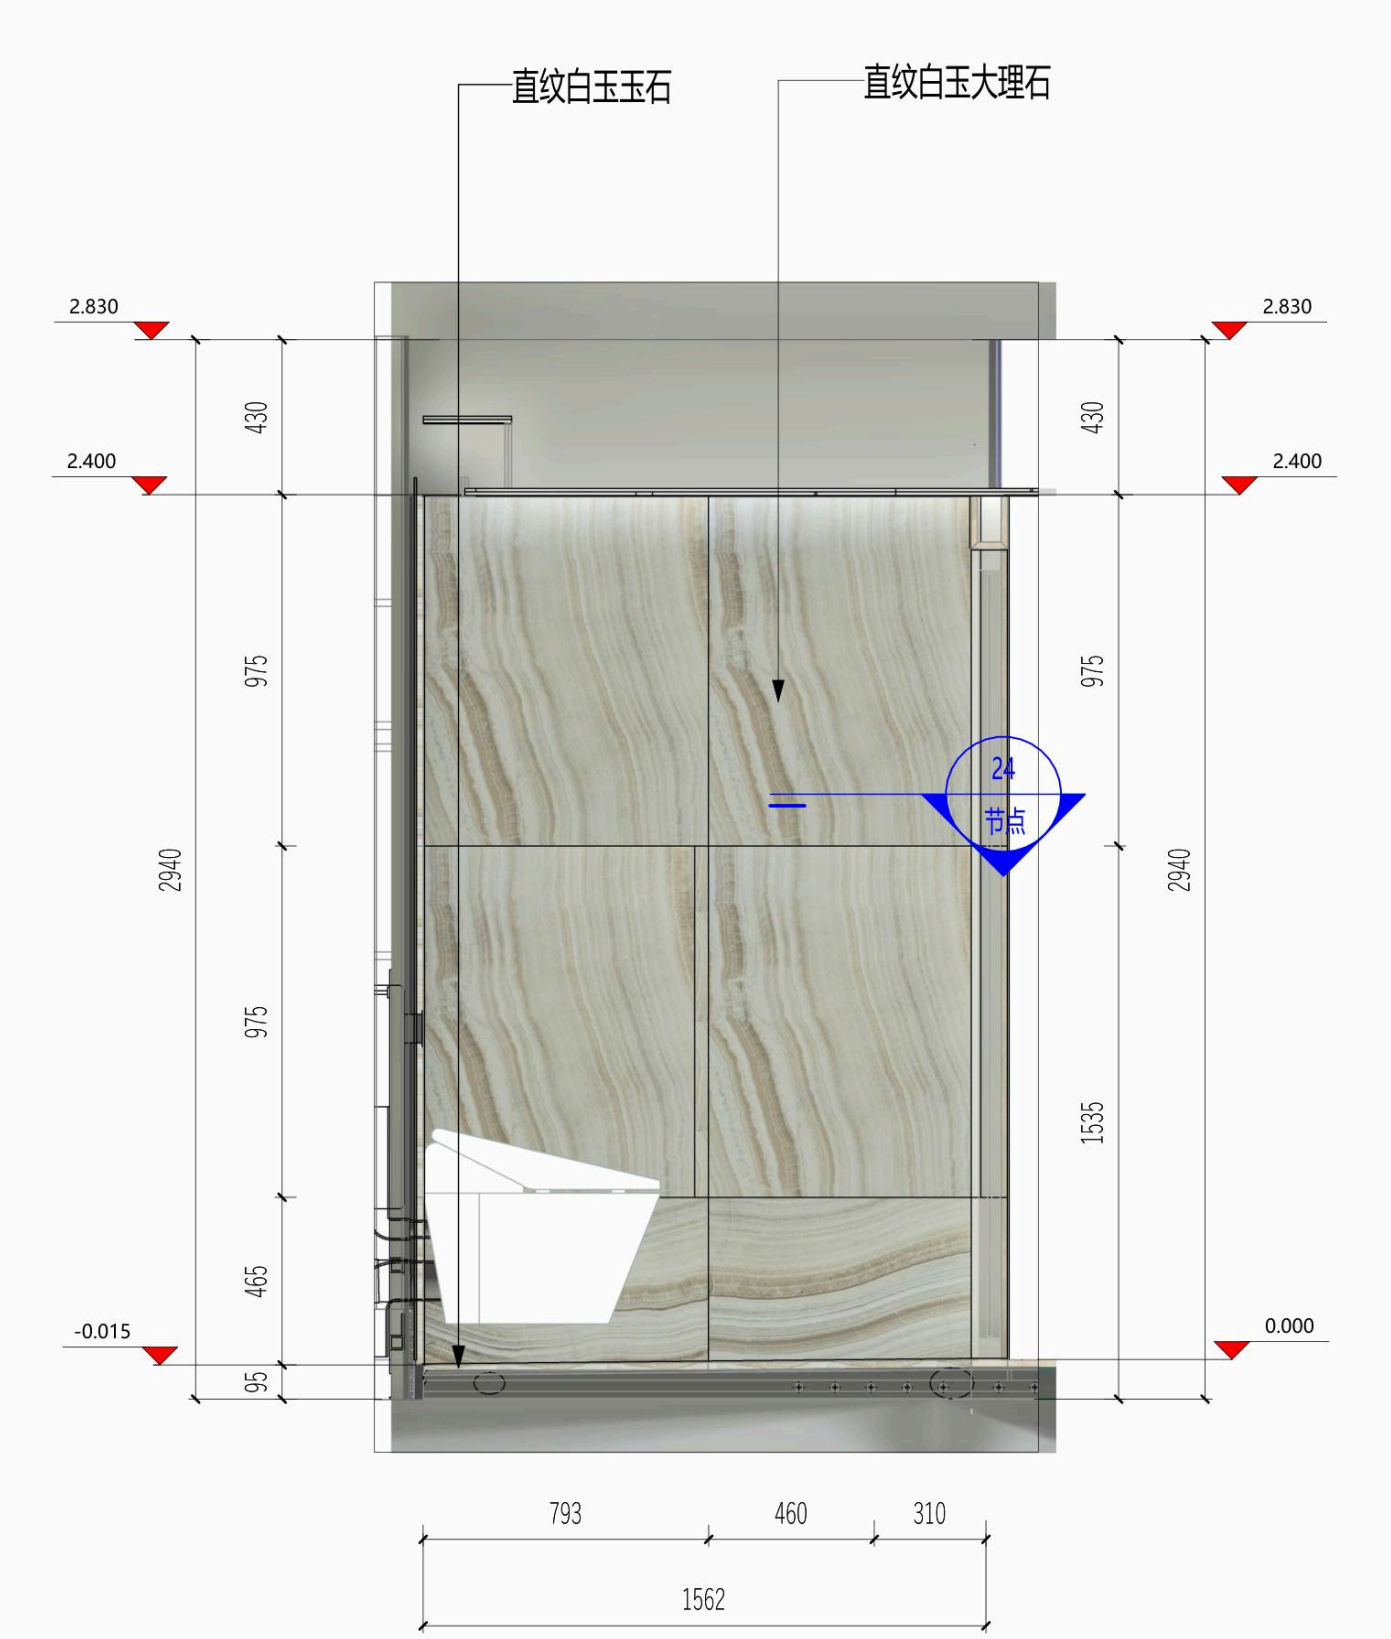
直纹白玉石
直纹白玉大理石
2.830
2.400
-0.015
2.830
2.400
0.000
24 节点
430
975
975
465
2940
1535
793
460
310
1562

主卫-07

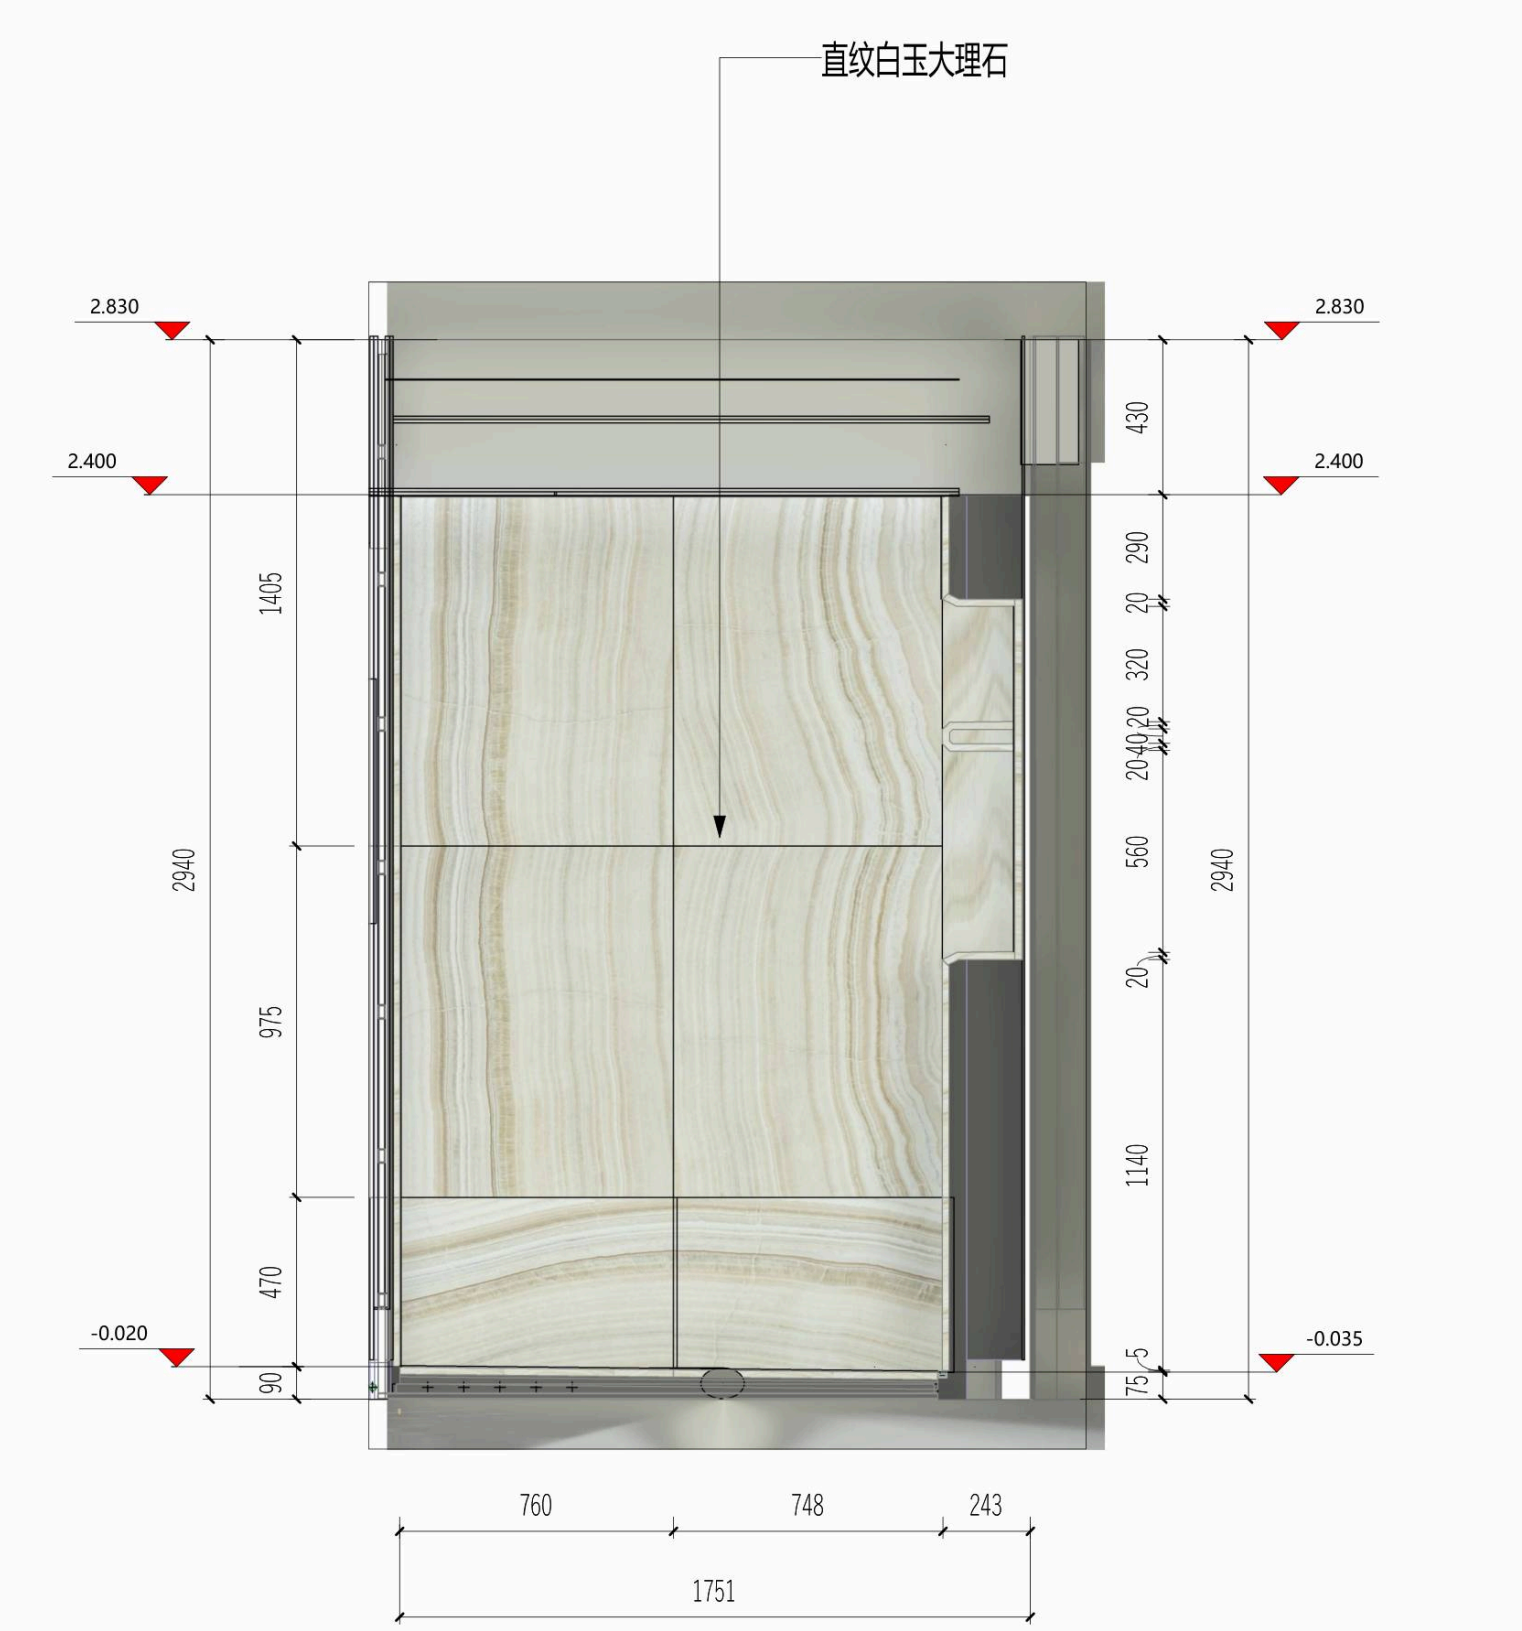
直纹白玉大理石
2.830
2.400
-0.020
2.830
2.400
-0.035
1405
975
470
2940
1140
560
760
748
243
1751

主卫-08

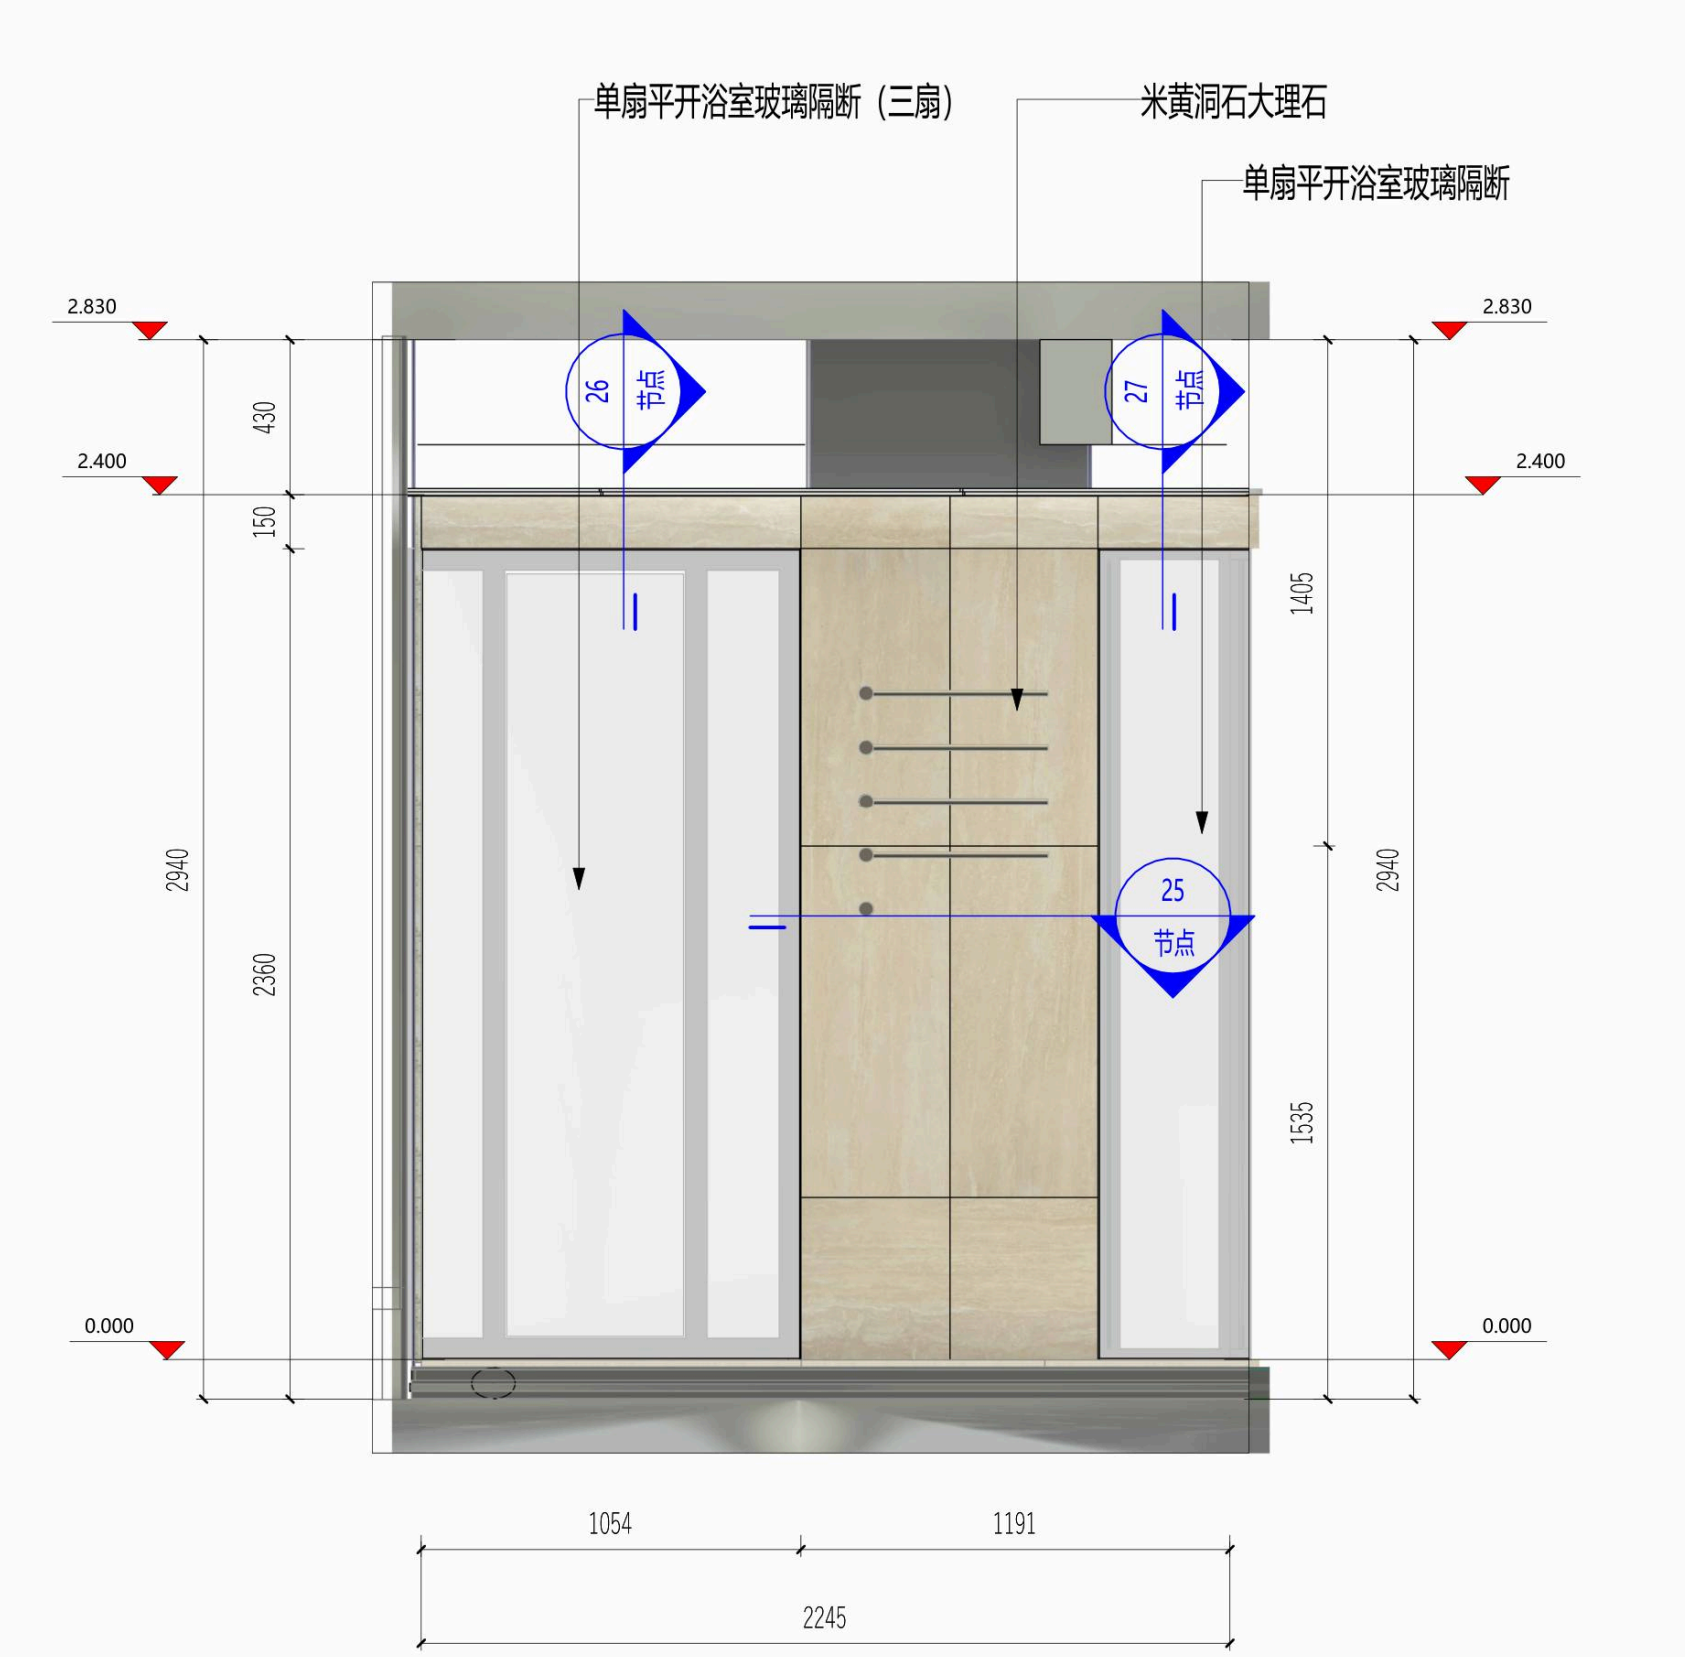
单扇平开浴室玻璃隔断（三扇）
米黄洞石大理石
单扇平开浴室玻璃隔断
2.830
2.400
0.000
2.830
2.400
0.000
26 节点
27 节点
25 节点
430
150
2360
1405
1535
2940
1054
1191
2245

主卫-09

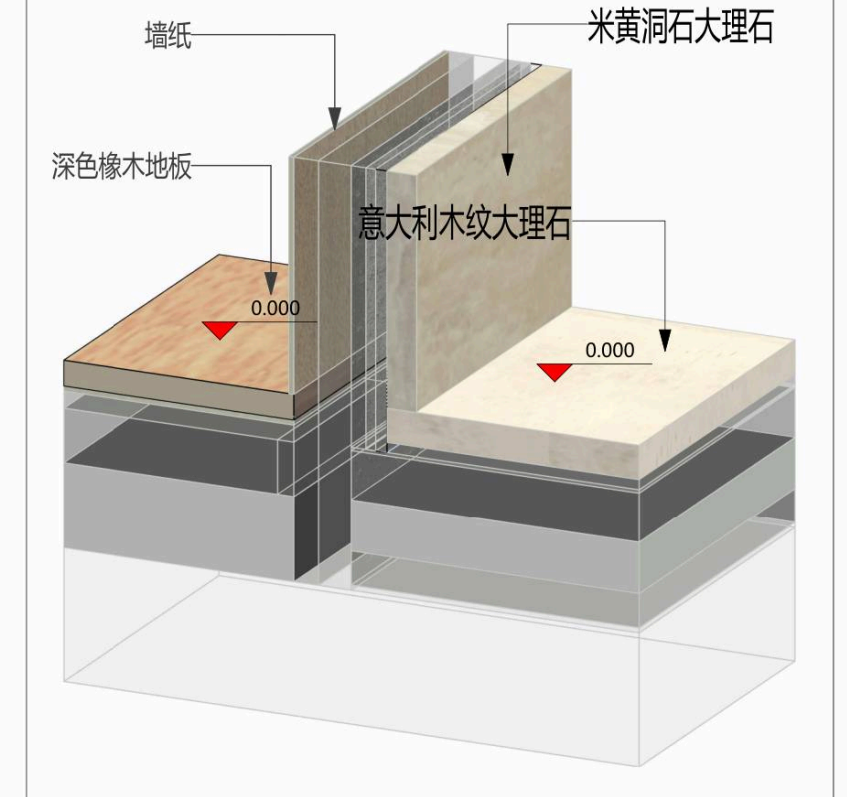
墙纸
米黄洞石大理石
深色橡木地板
意大利木纹大理石
0.000
0.000

节点-01

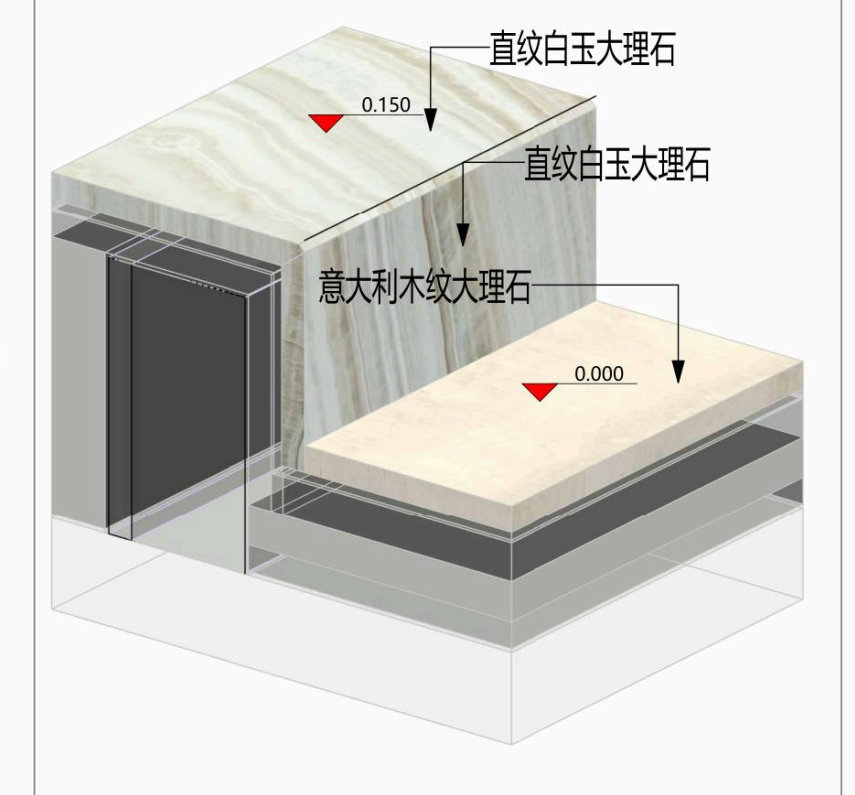
直纹白玉大理石
0.150
直纹白玉大理石
意大利木纹大理石
0.000

节点-02

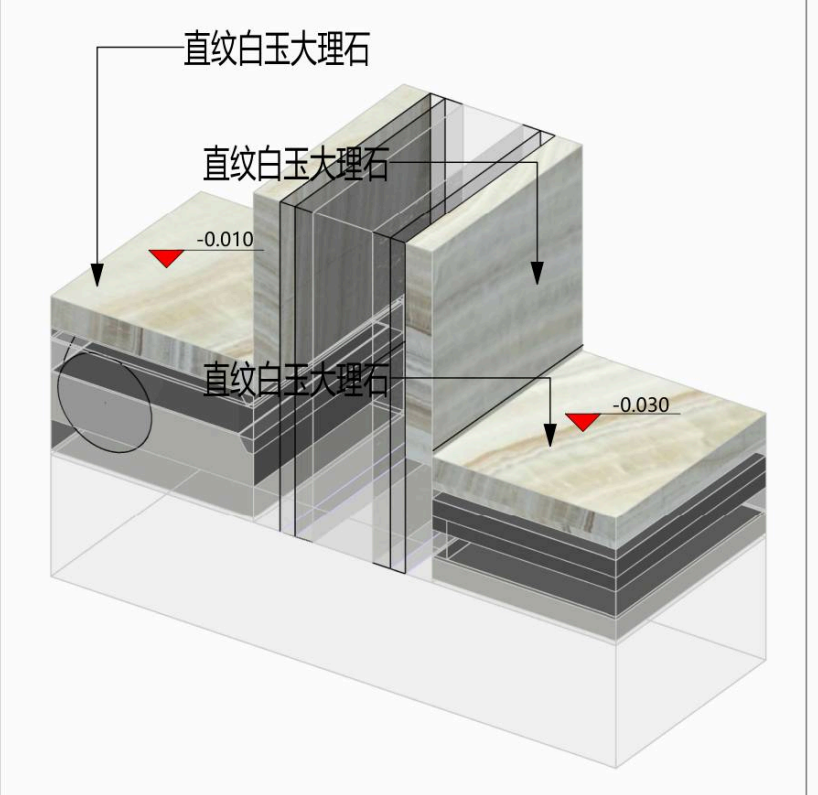
直纹白玉大理石
直纹白玉大理石
-0.010
直纹白玉大理石
-0.030

节点-03

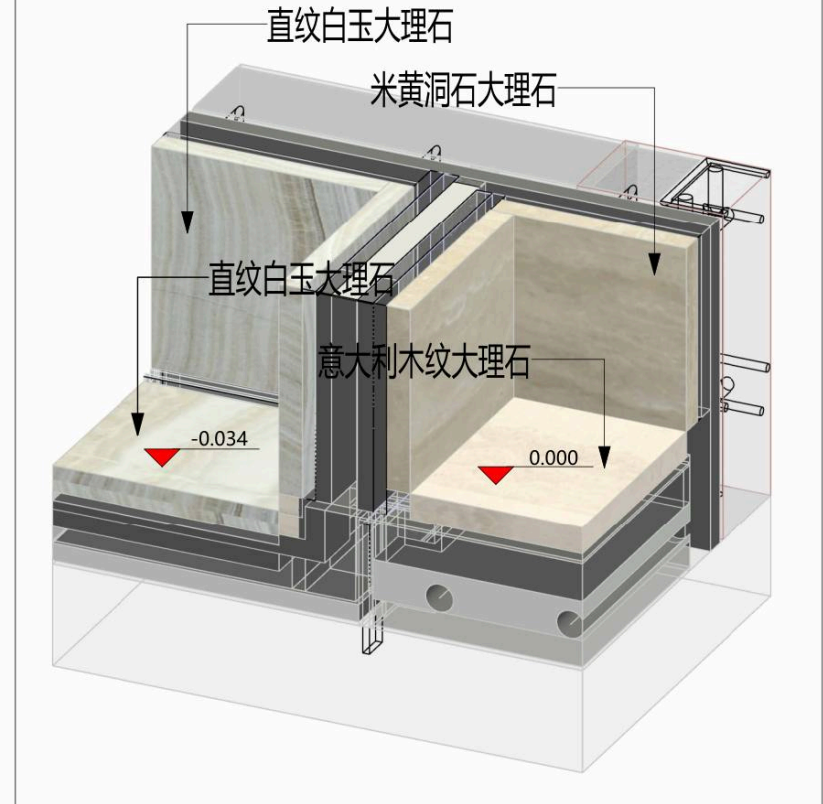
直纹白玉大理石
米黄洞石大理石
直纹白玉大理石
意大利木纹大理石
-0.034
0.000

节点-04

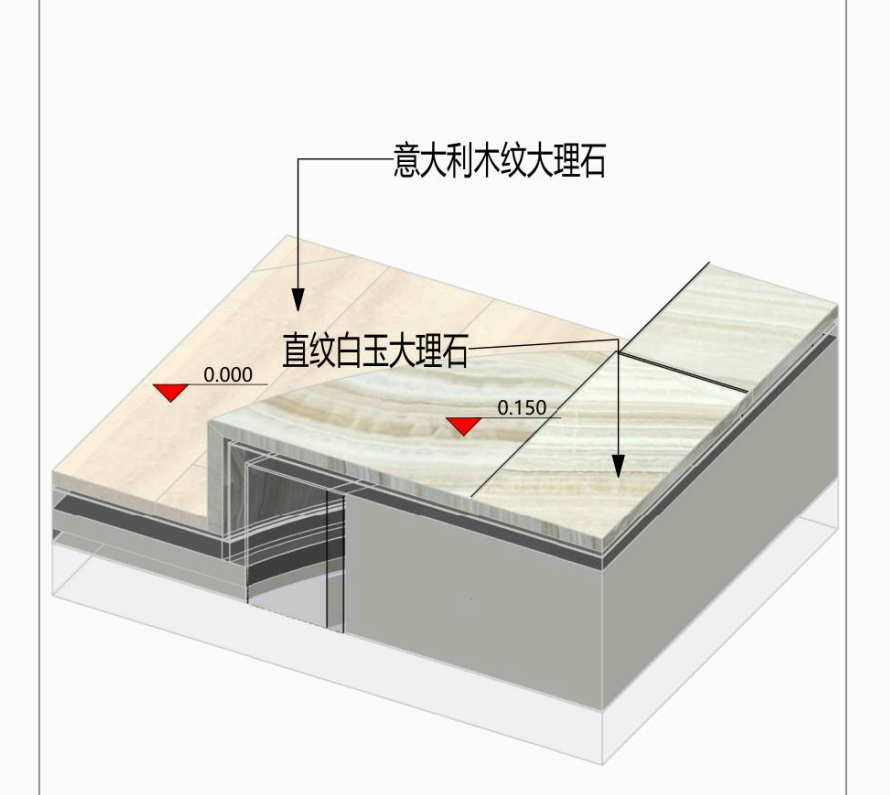
意大利木纹大理石
直纹白玉大理石
0.000
0.150

节点-05

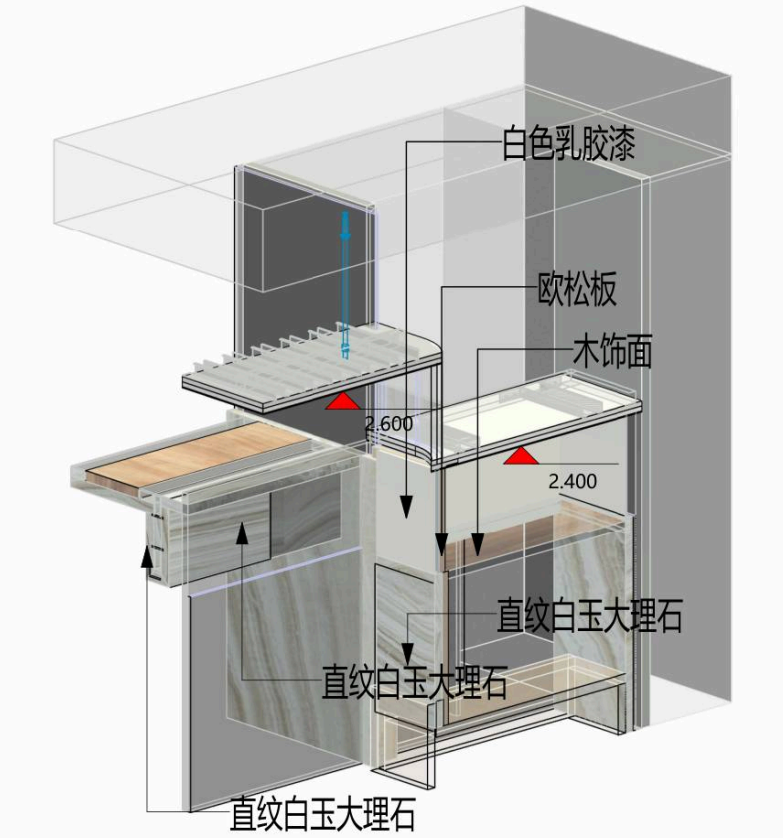
白色乳胶漆
欧松板
木饰面
2.400
直纹白玉大理石
直纹白玉大理石
直纹白玉大理石

节点-06

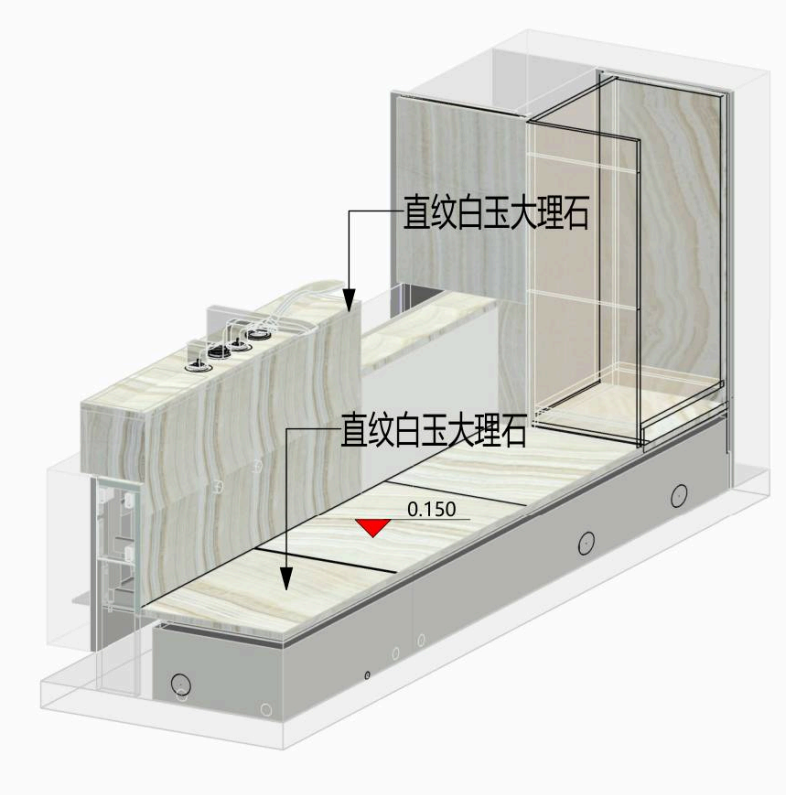
直纹白玉大理石
直纹白玉大理石
0.150

节点-07

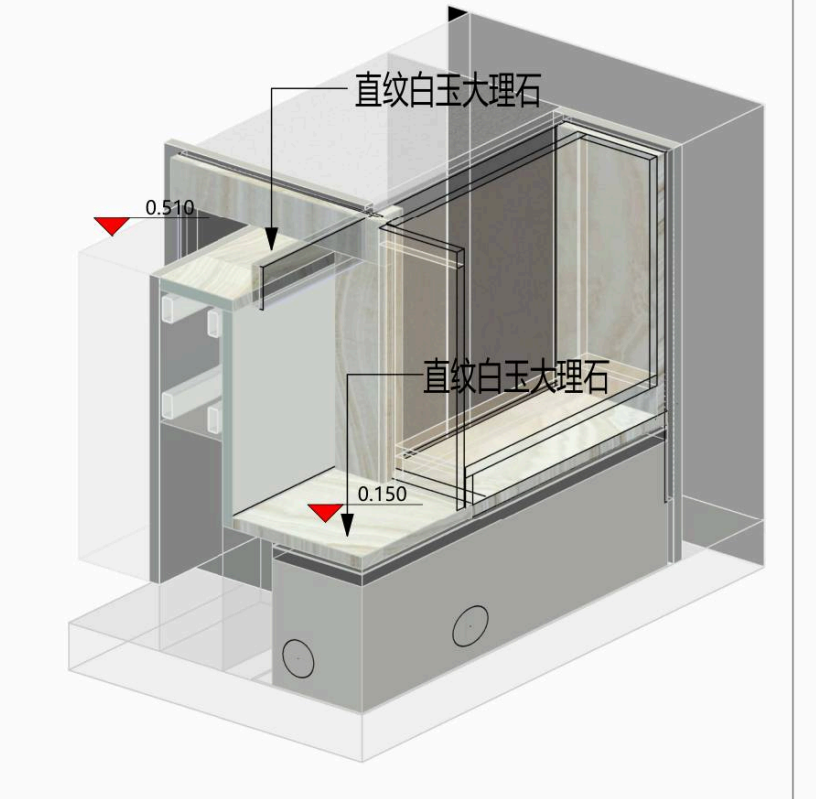
直纹白玉大理石
直纹白玉大理石
0.150

节点-08

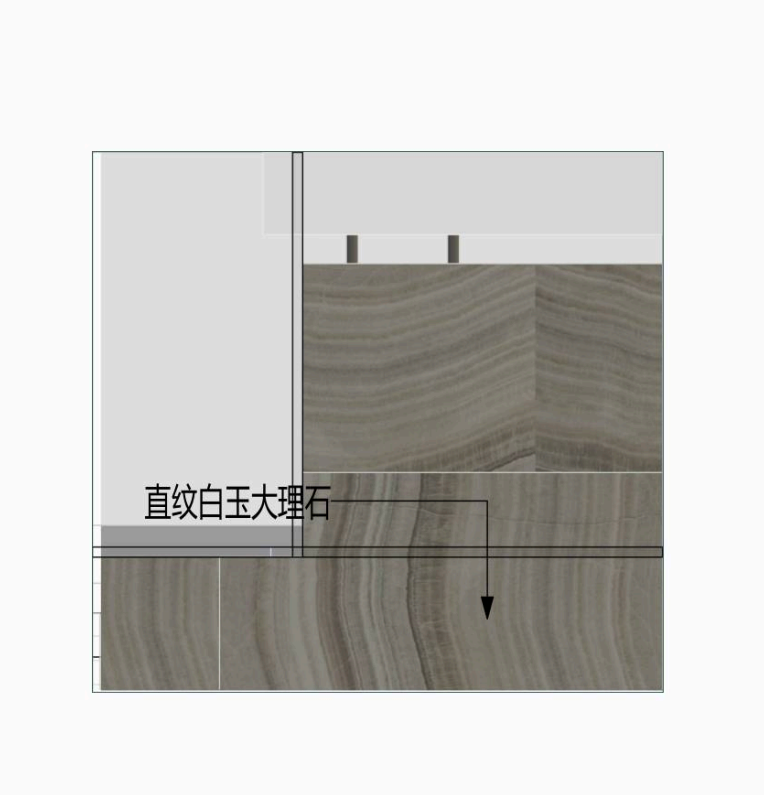

节点-09

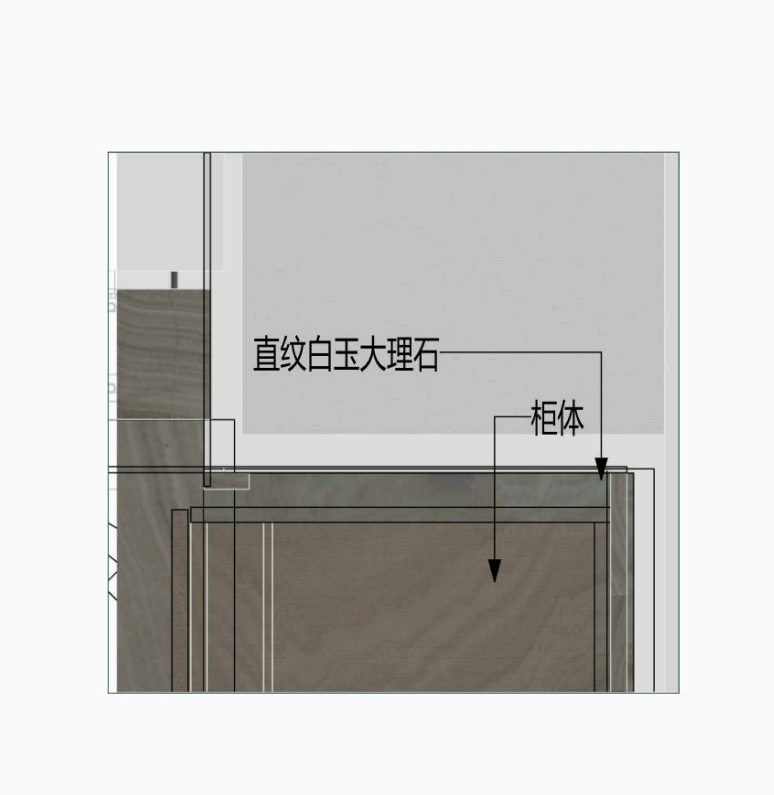

节点-10

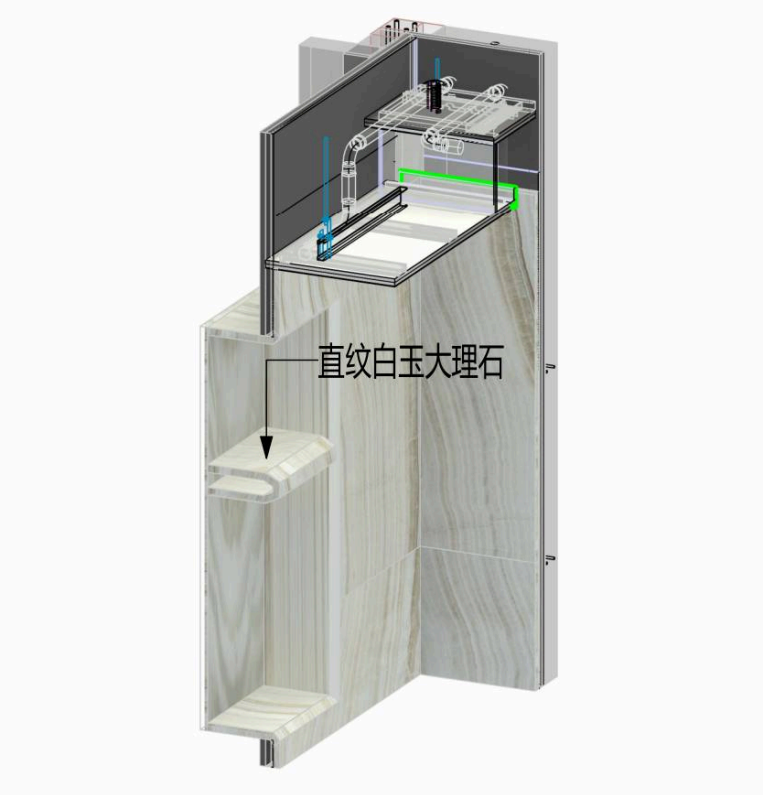

节点-11

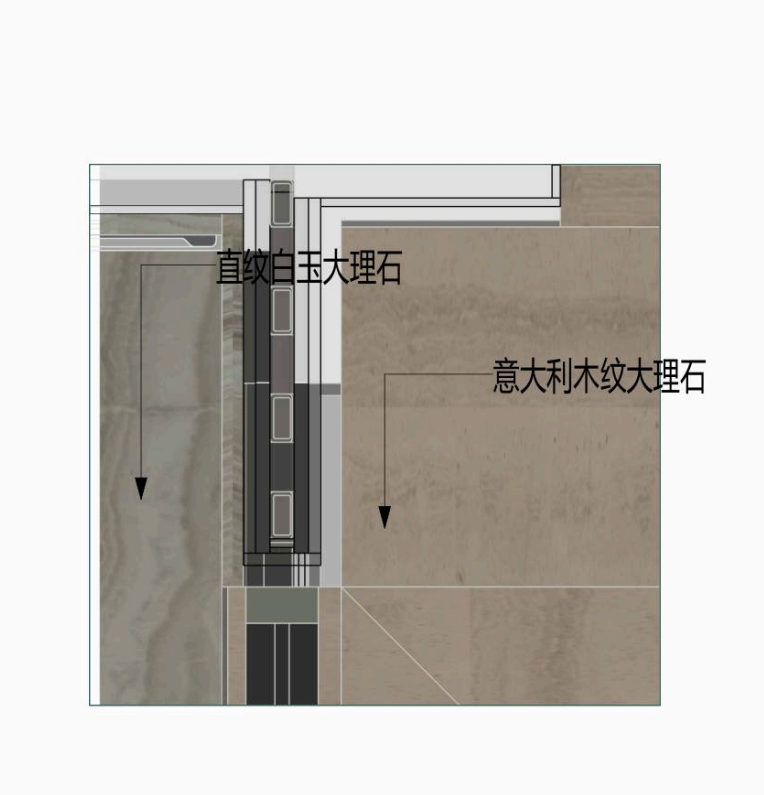
直纹白玉大理石
意大利木纹大理石

节点-12

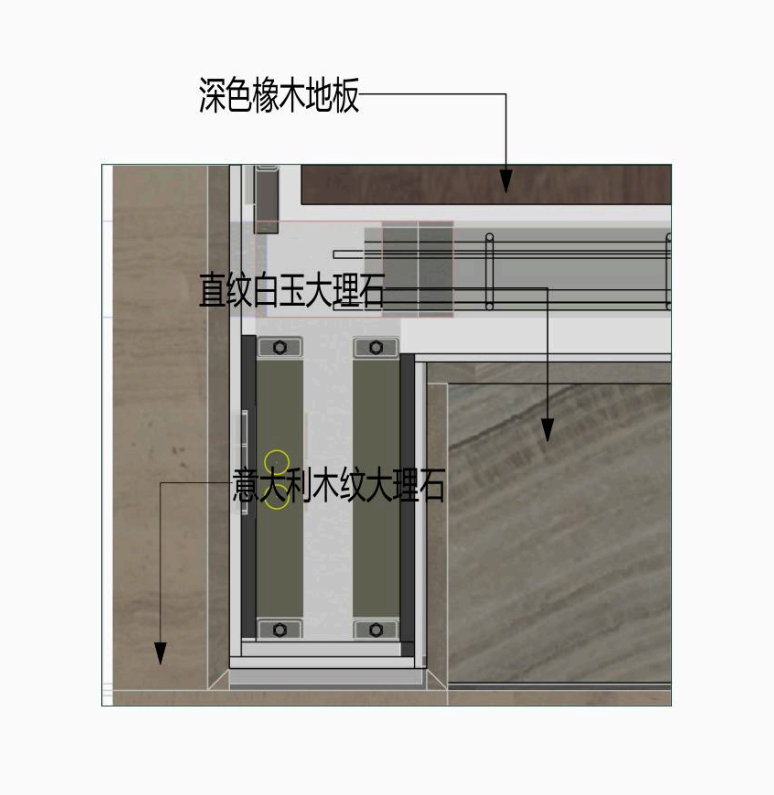
深色橡木地板
直纹白玉大理石
意大利木纹大理石

节点-13

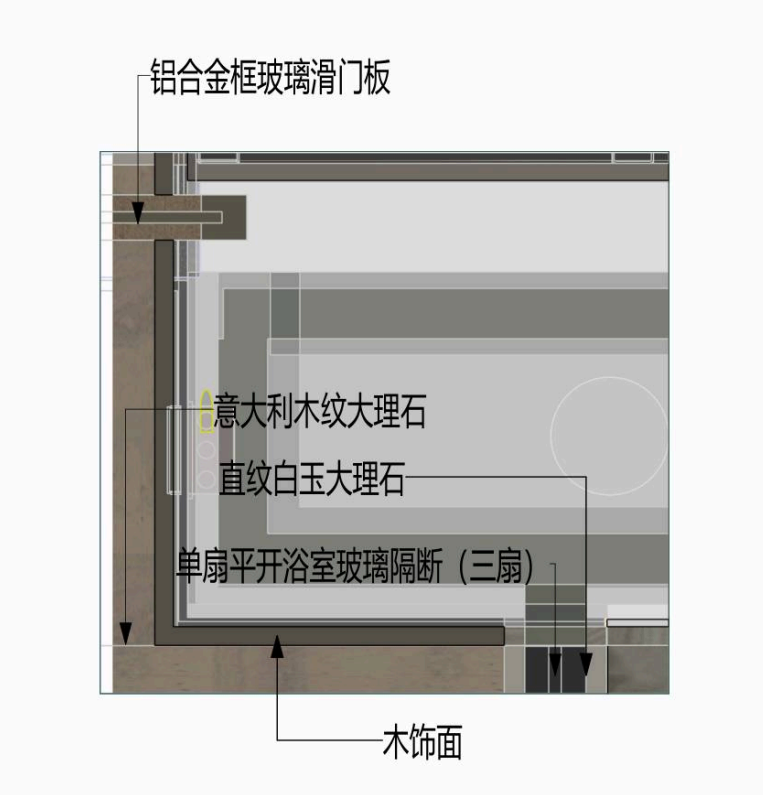
铝合金框玻璃滑门板
意大利木纹大理石
直纹白玉大理石
单扇平开浴室玻璃隔断（三扇）
木饰面

节点-14

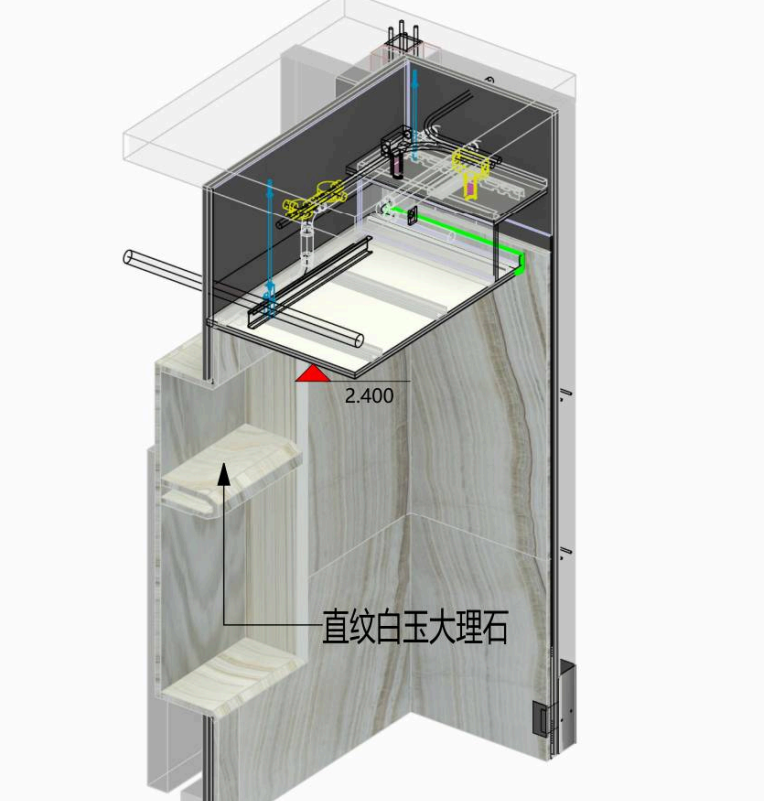
2.400
直纹白玉大理石

节点-15

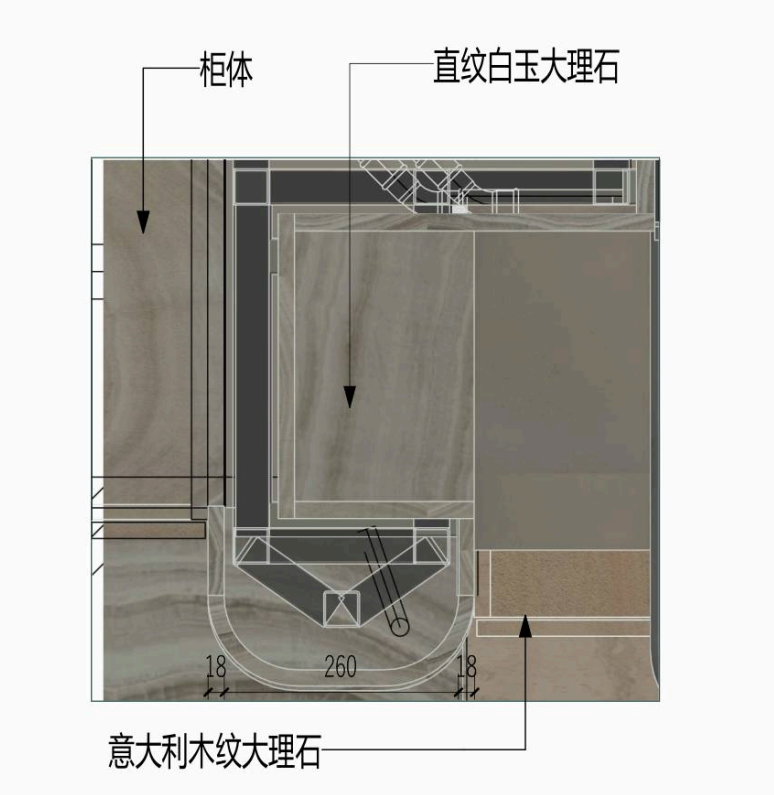
柜体
直纹白玉大理石
意大利木纹大理石

节点-16

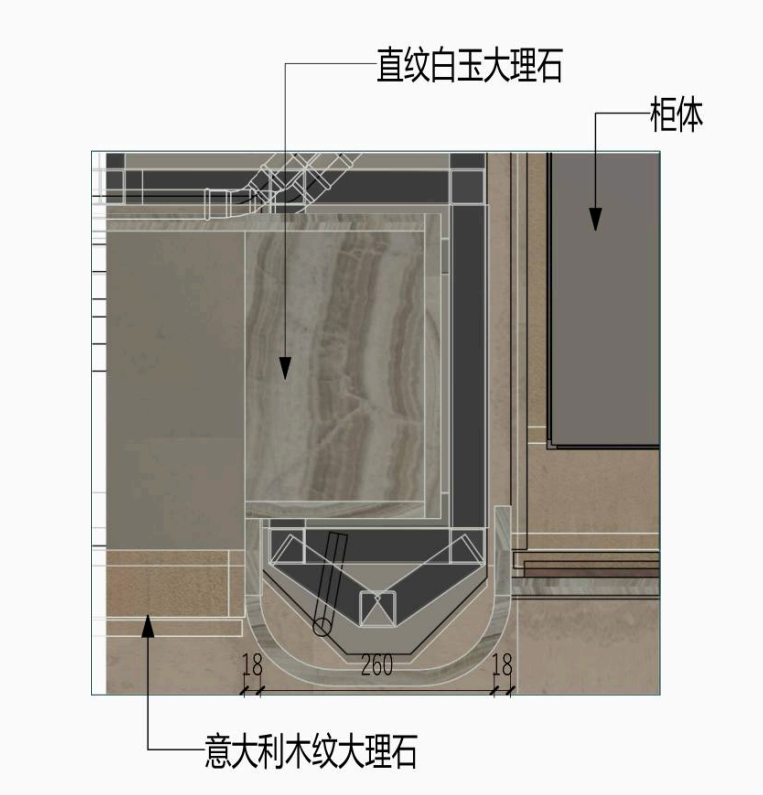
直纹白玉大理石
柜体
意大利木纹大理石

节点-17

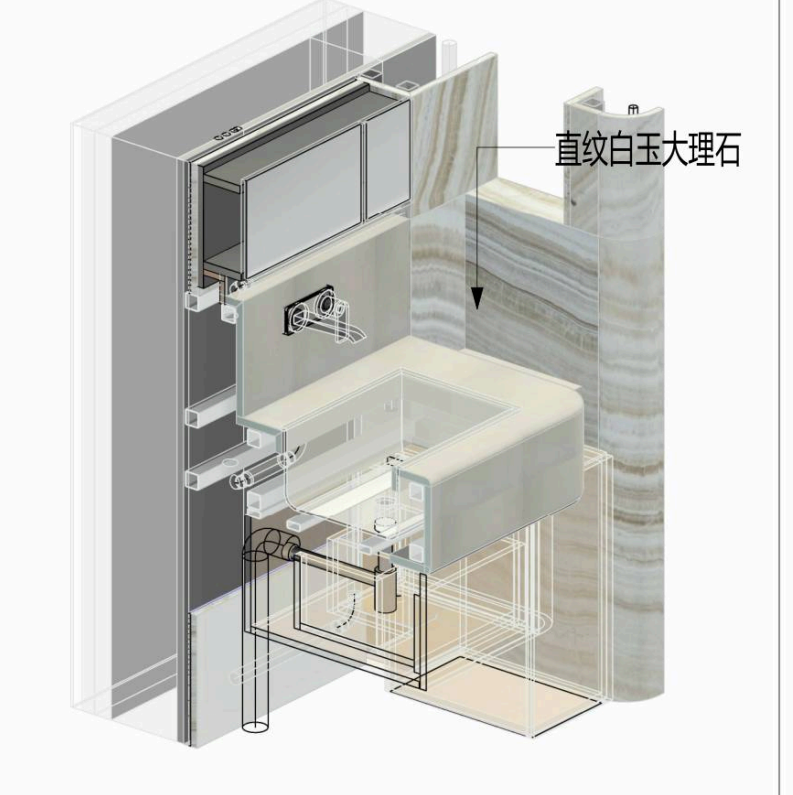

节点-18

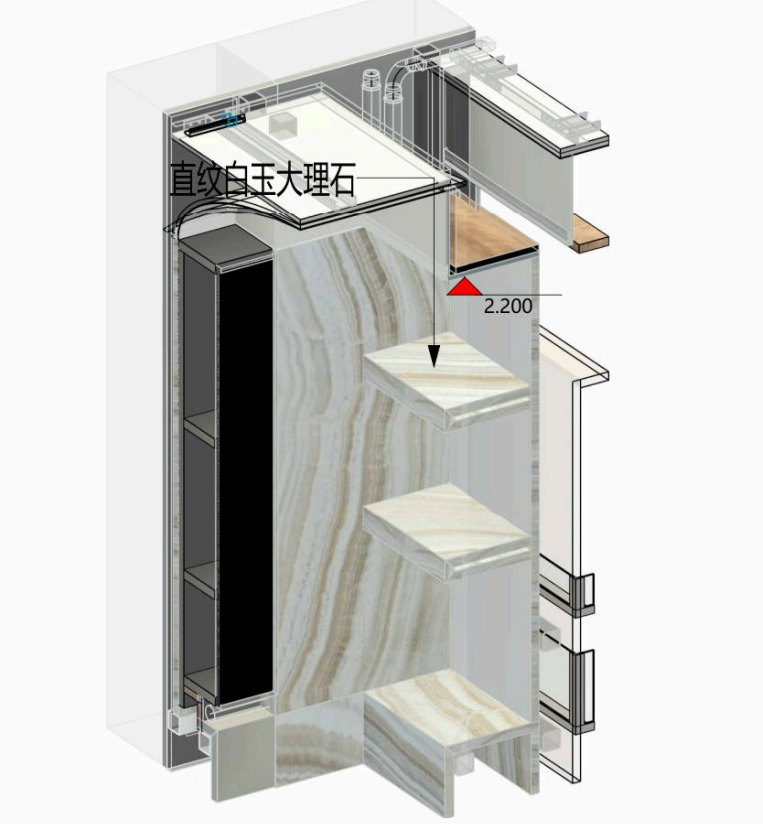
直纹白玉大理石
2.200

节点-19

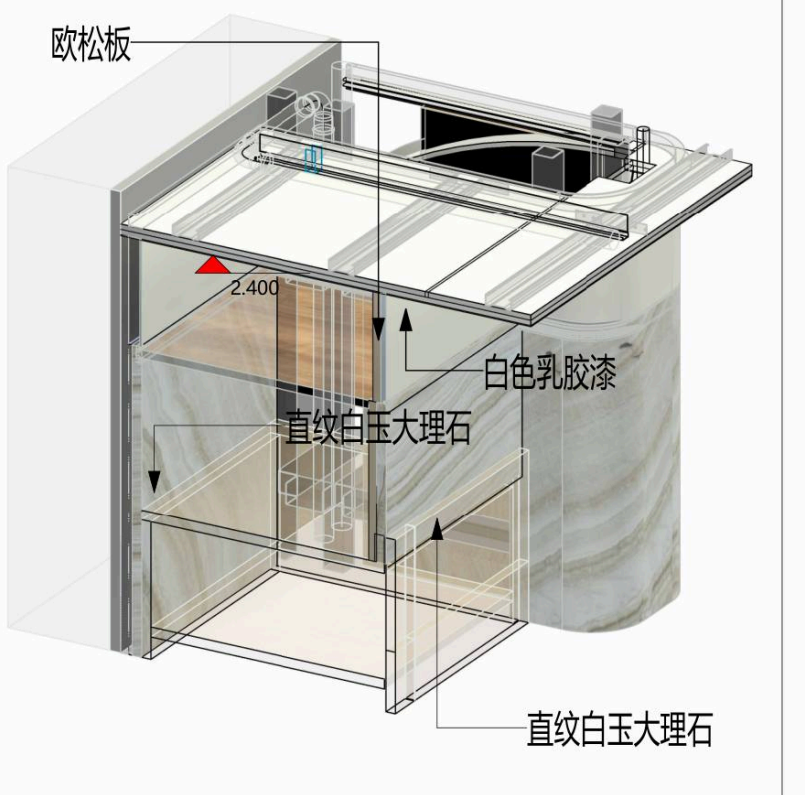
欧松板
2.400
白色乳胶漆
直纹白玉大理石
直纹白玉大理石

节点-20

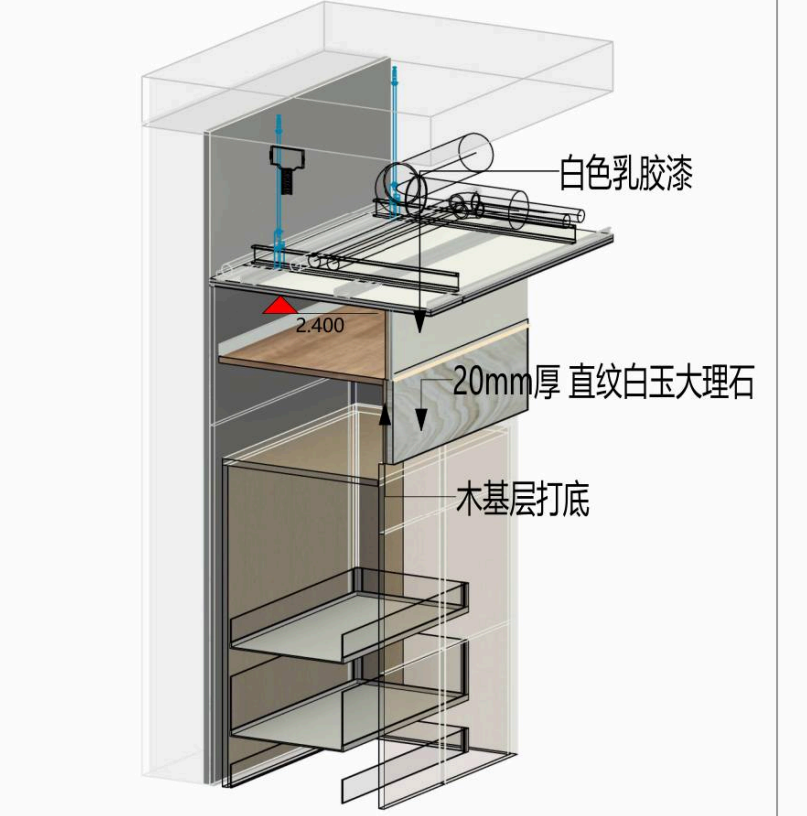
白色乳胶漆
2.400
20mm厚 直纹白玉大理石
木基层打底

节点-21

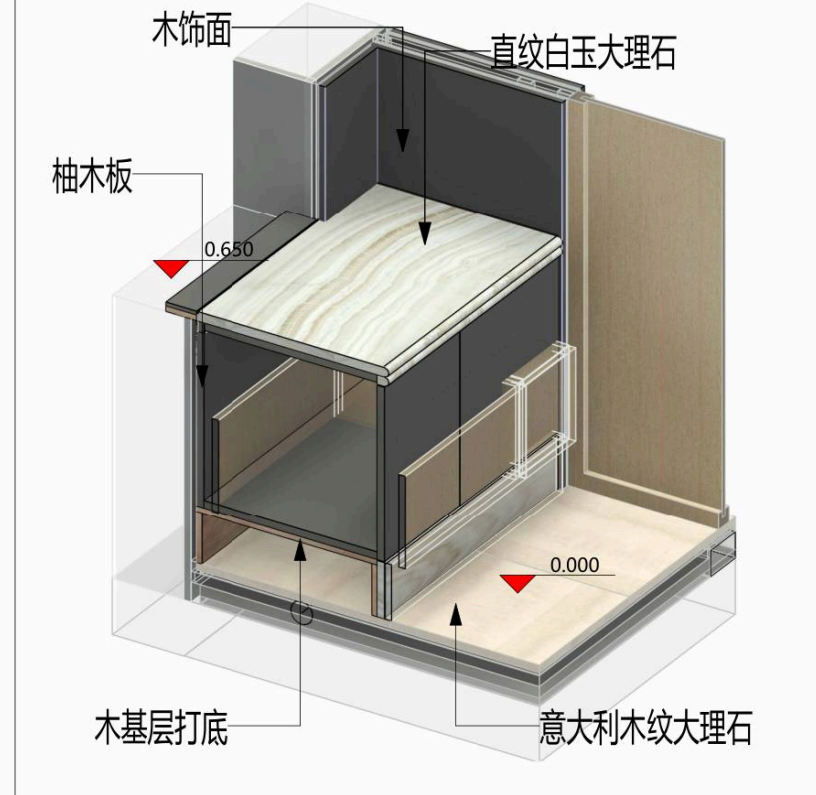
木饰面
直纹白玉大理石
柚木板
木基层打底
0.000
意大利木纹大理石

节点-22

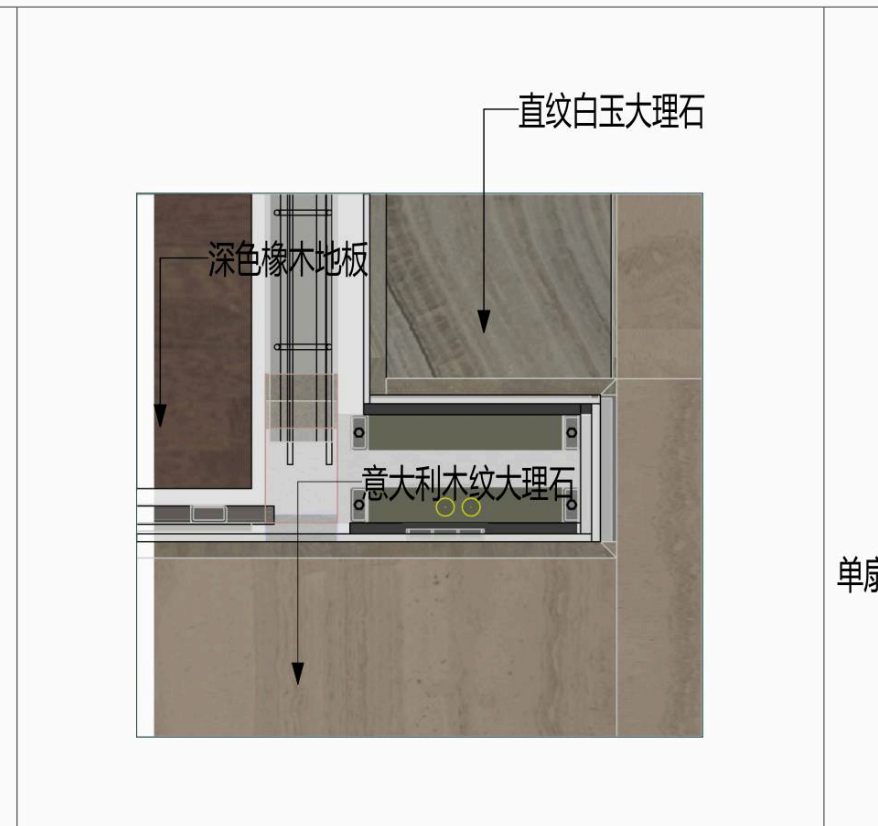
直纹白玉大理石
深色橡木地板
意大利木纹大理石

节点-23

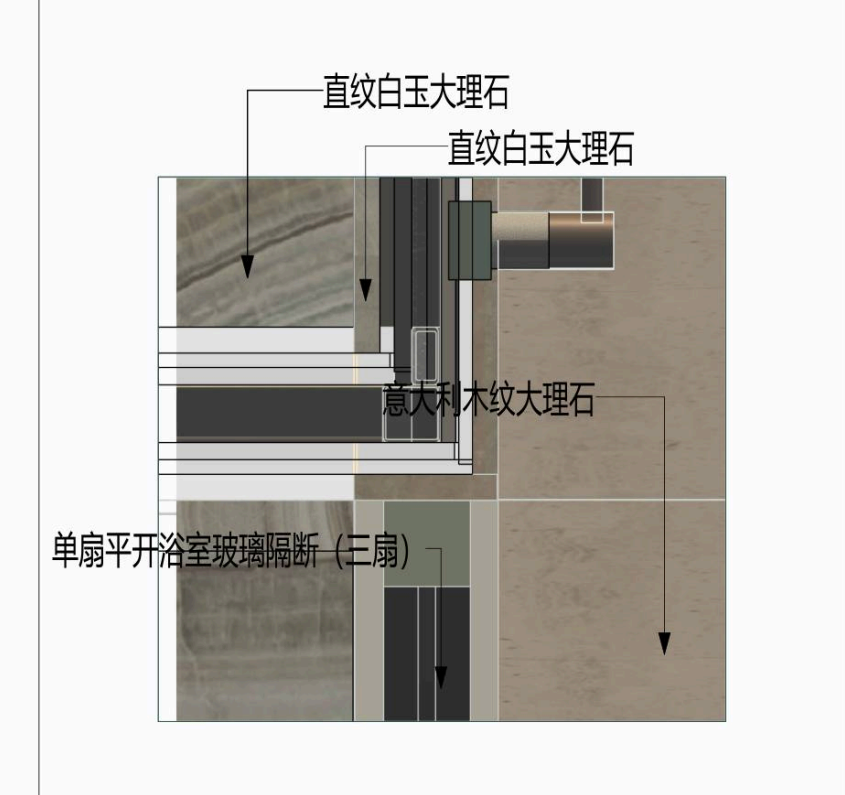
直纹白玉大理石
直纹白玉大理石
意大利木纹大理石
单扇平开浴室玻璃隔断（三扇）

节点-24

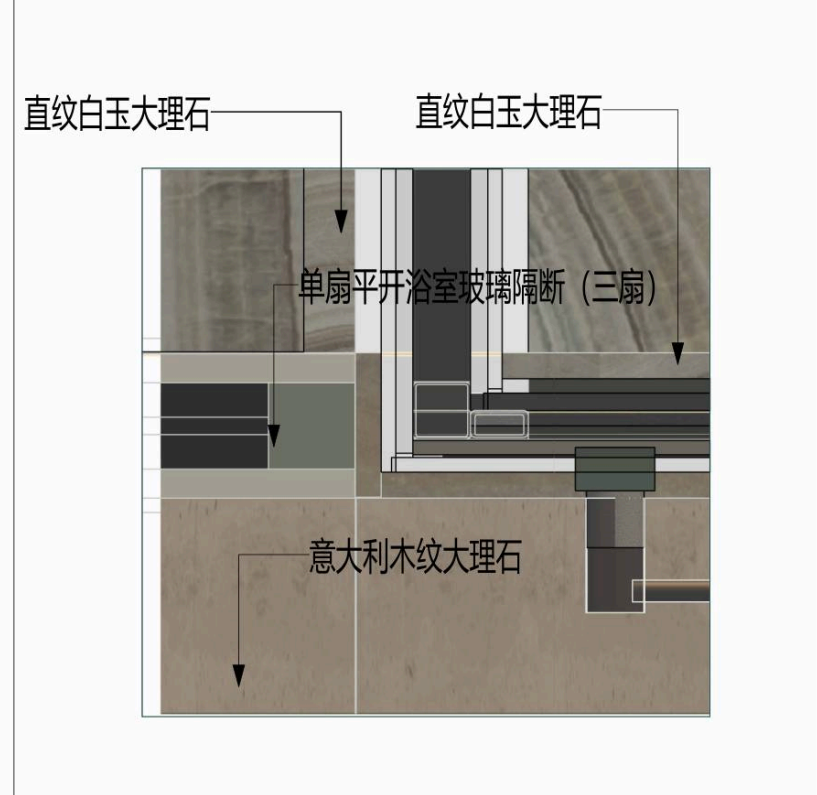
直纹白玉大理石
直纹白玉大理石
单扇平开浴室玻璃隔断（三扇）
意大利木纹大理石

节点-25

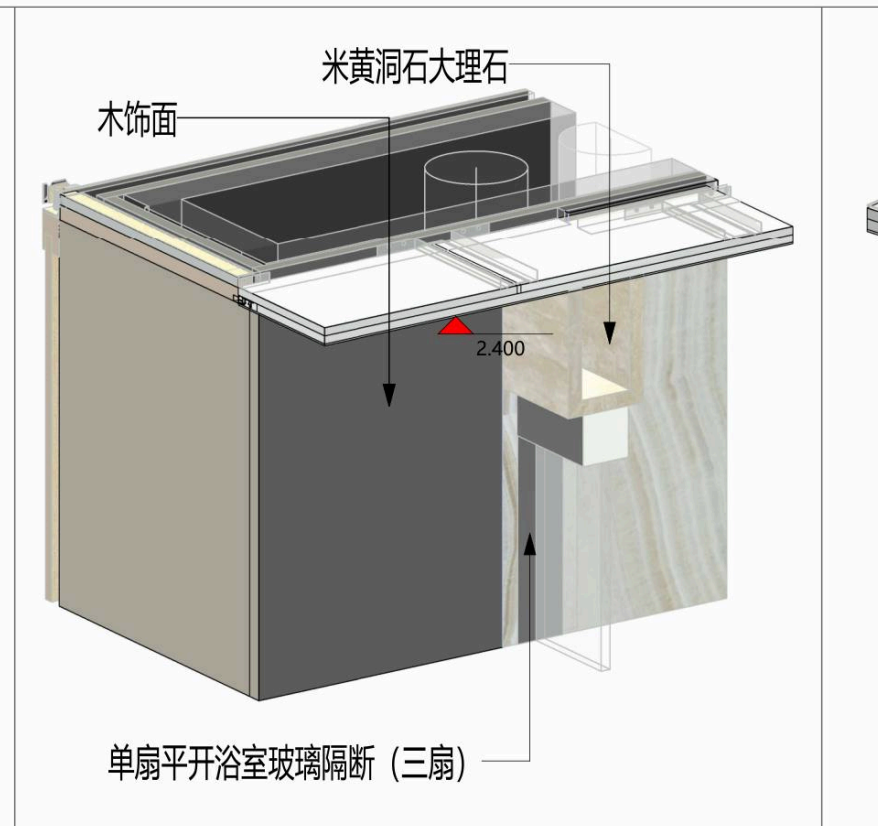
米黄洞石大理石
木饰面
2.400
单扇平开浴室玻璃隔断（三扇）

节点-26

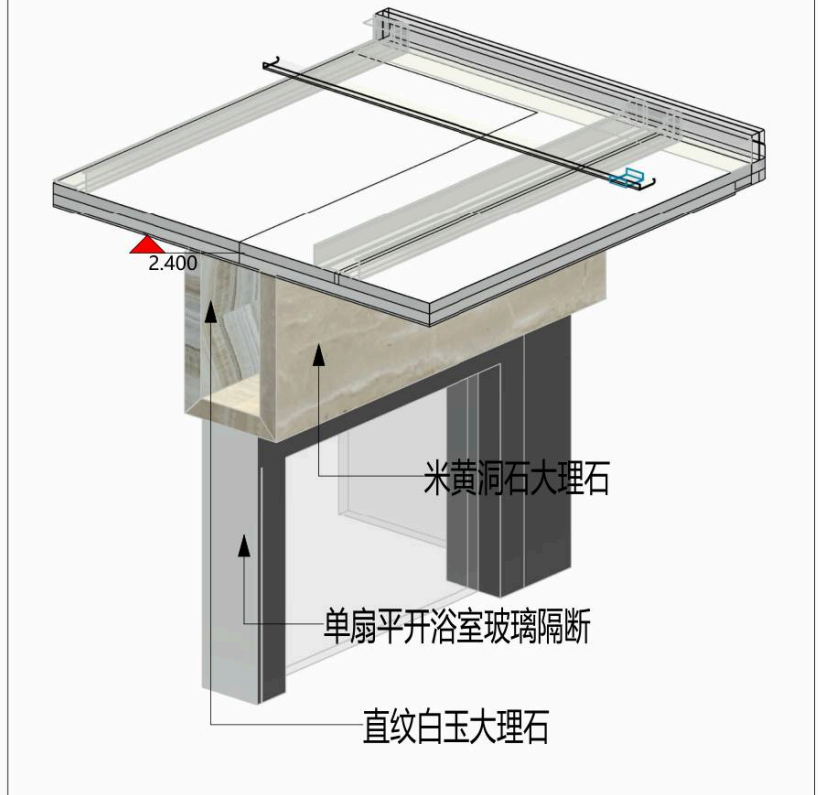
2.400
米黄洞石大理石
单扇平开浴室玻璃隔断
直纹白玉大理石

节点-27

编号	图例	名称
1	▨	丹枫白露大理石
2	▨	直纹白玉大理石
3	▨	米白色防水肌理漆
4	▨	红色防水肌理漆
5	▨	米黄洞石大理石
6	▨	伊朗绿大理石
7	▨	黑白根大理石
8	▨	意大利木纹
9	▨	白木纹石
10	▨	塔维勒莱姆石
11	▨	木饰面
12	▨	木地板
13	▨	墙布

盖章

注释
Notes
1.本图纸如与现场尺寸有误，请施工人员与项目负责人联系。
2.施工前施工人员应认真查阅此图，如有不明确尺寸，按现场测量为准。
3.本图纸必须经甲乙双方认可并签字方可作为施工依据。

日期
Date 05/20/26

修订
Revision
△1

项目
Project
潮映华岸府3-801

比例
Scale

主卫石材铺贴

图纸编号
Drawing No.
ST-12

项目编号
Project No.

©2025

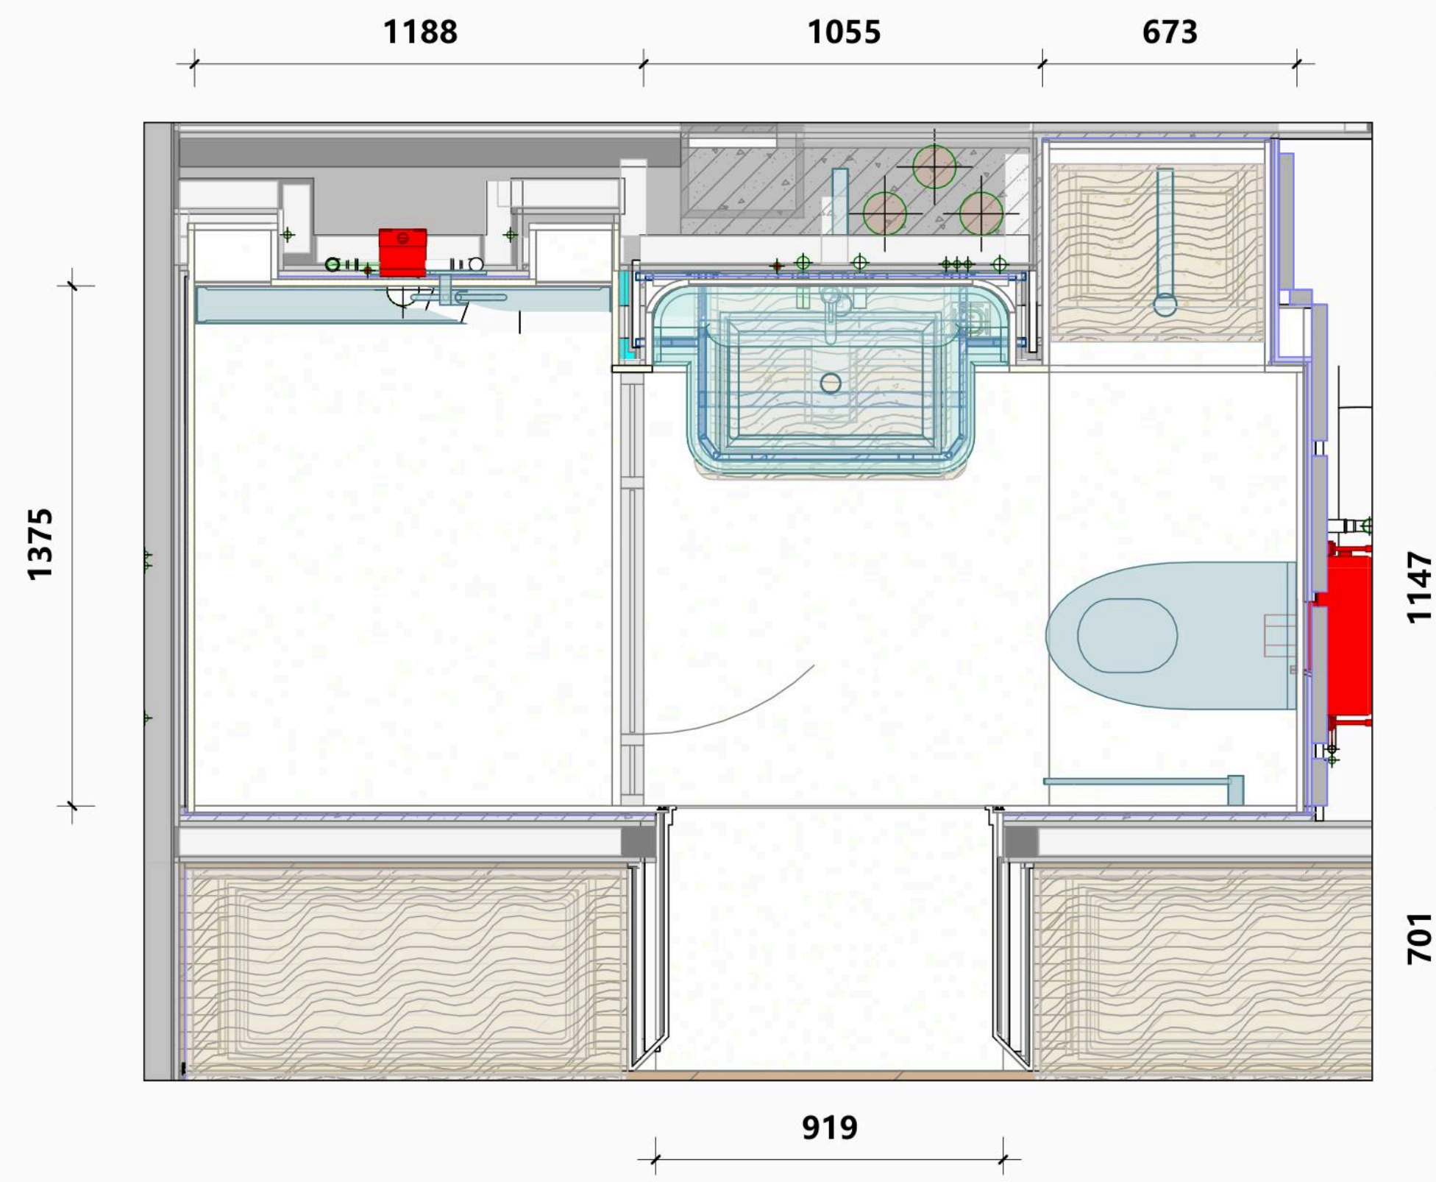
1188
1055
673
1375
1147
701
919

地面铺贴图

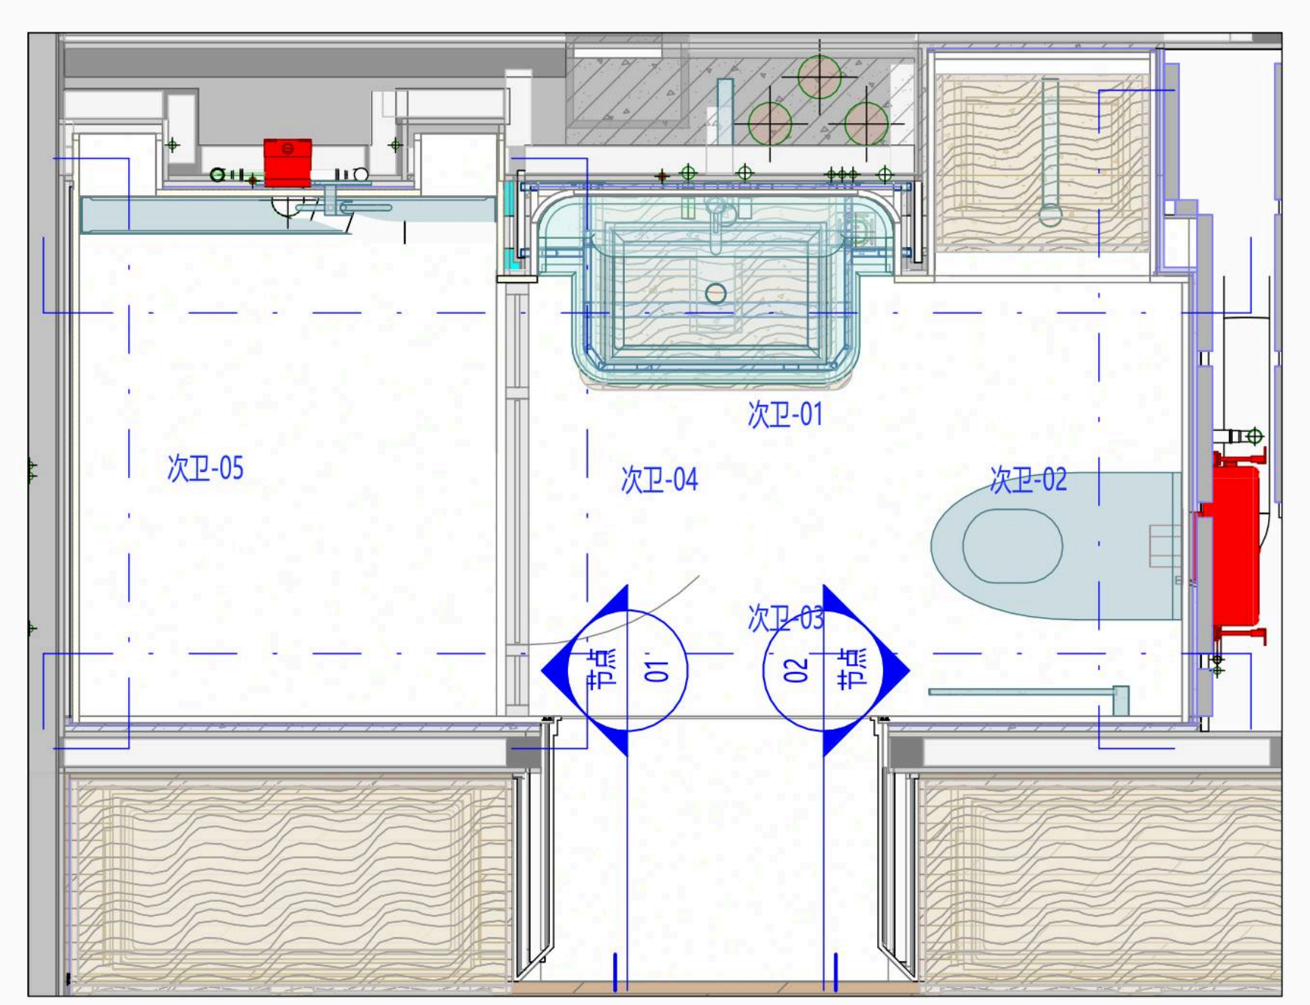
次卫-01
次卫-02
次卫-03
次卫-04
次卫-05
01 节点
02 节点

索引图

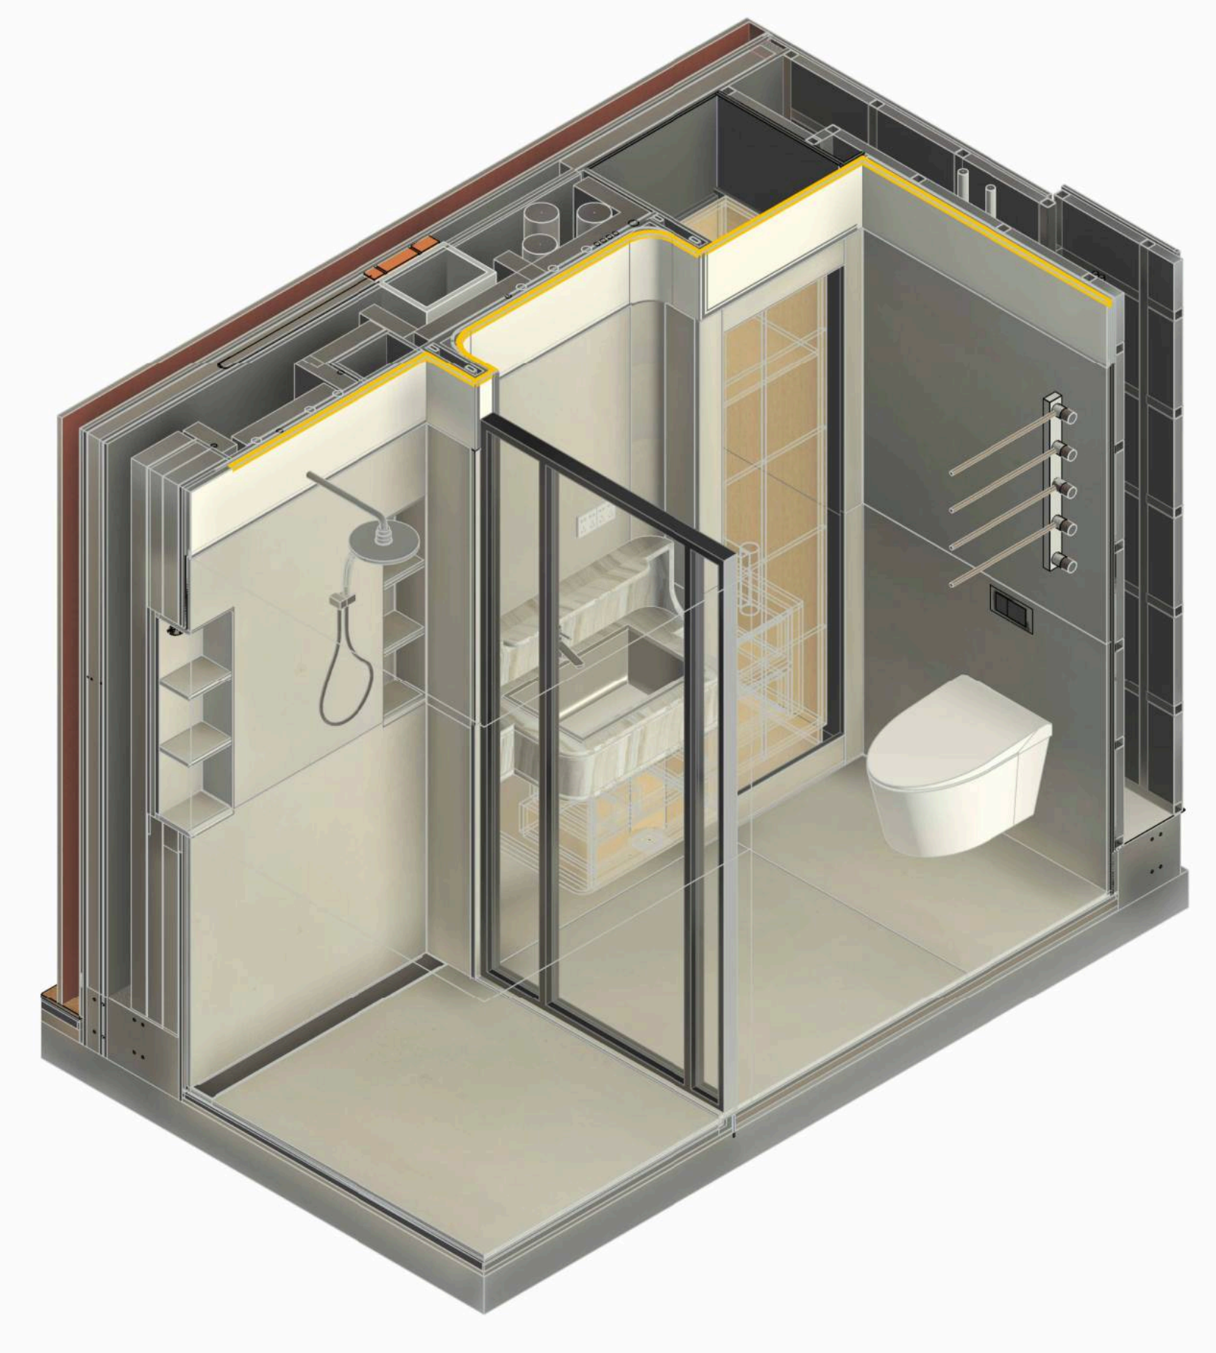

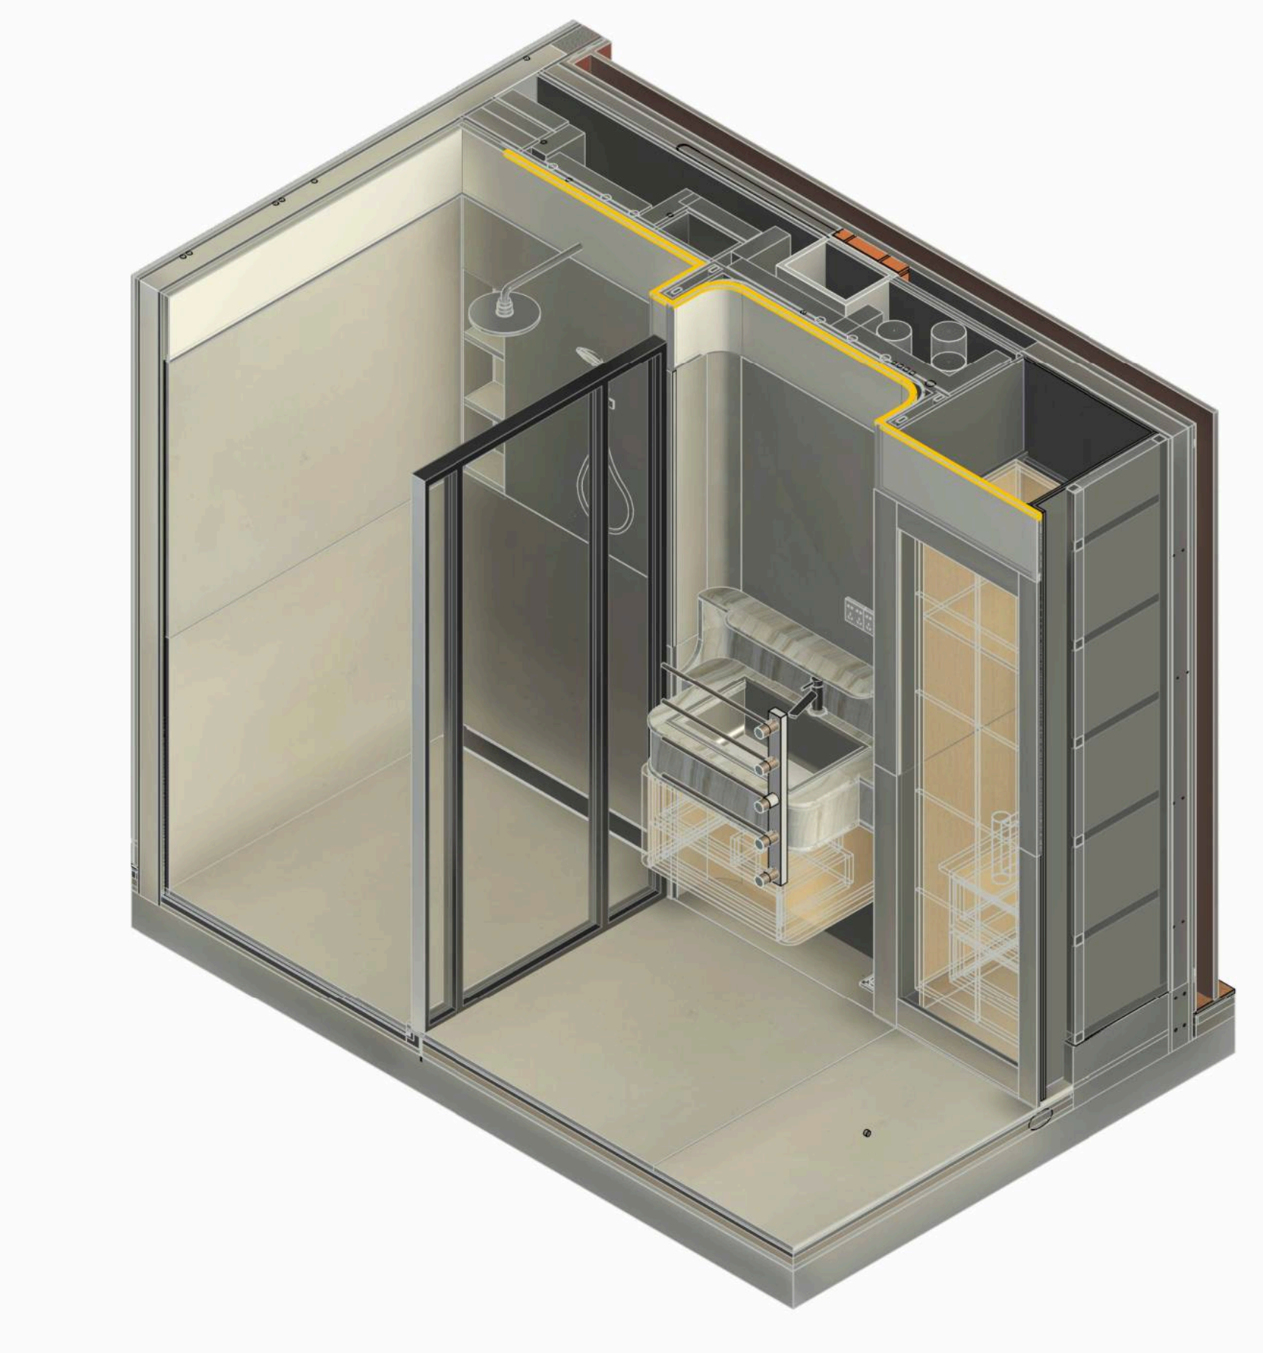

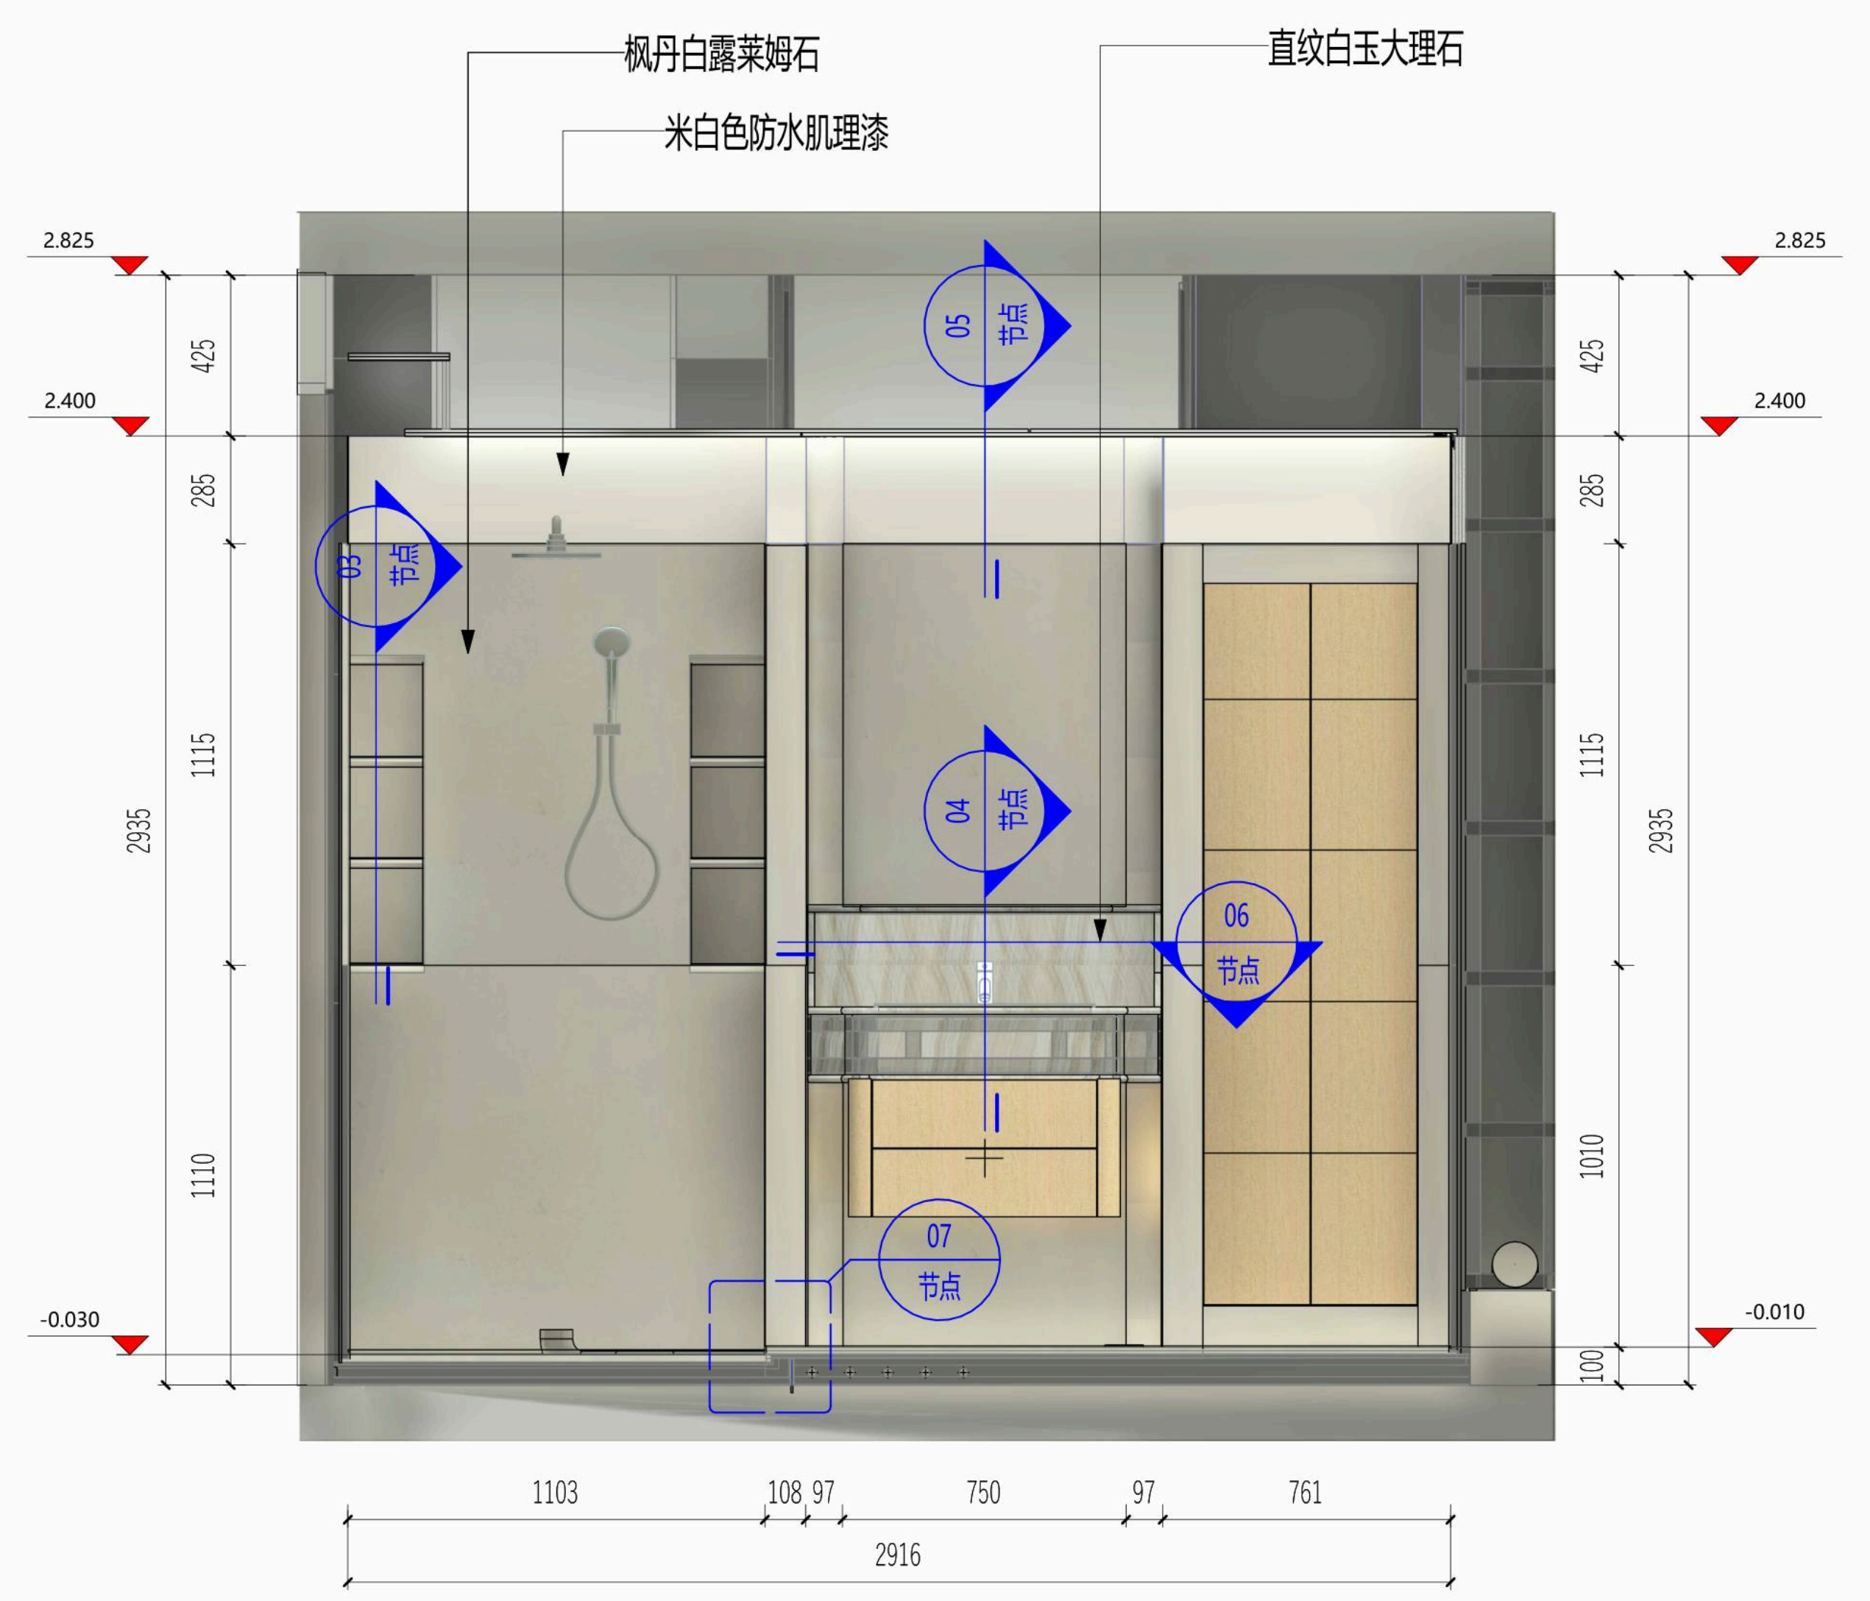
枫丹白露莱姆石
米白色防水肌理漆
直纹白玉大理石
2.825
2.400
-0.030
-0.010
05 节点
03 节点
04 节点
06 节点
07 节点
425
285
1115
1110
1010
100
2935
1103
108
97
750
97
761
2916

次卫-01

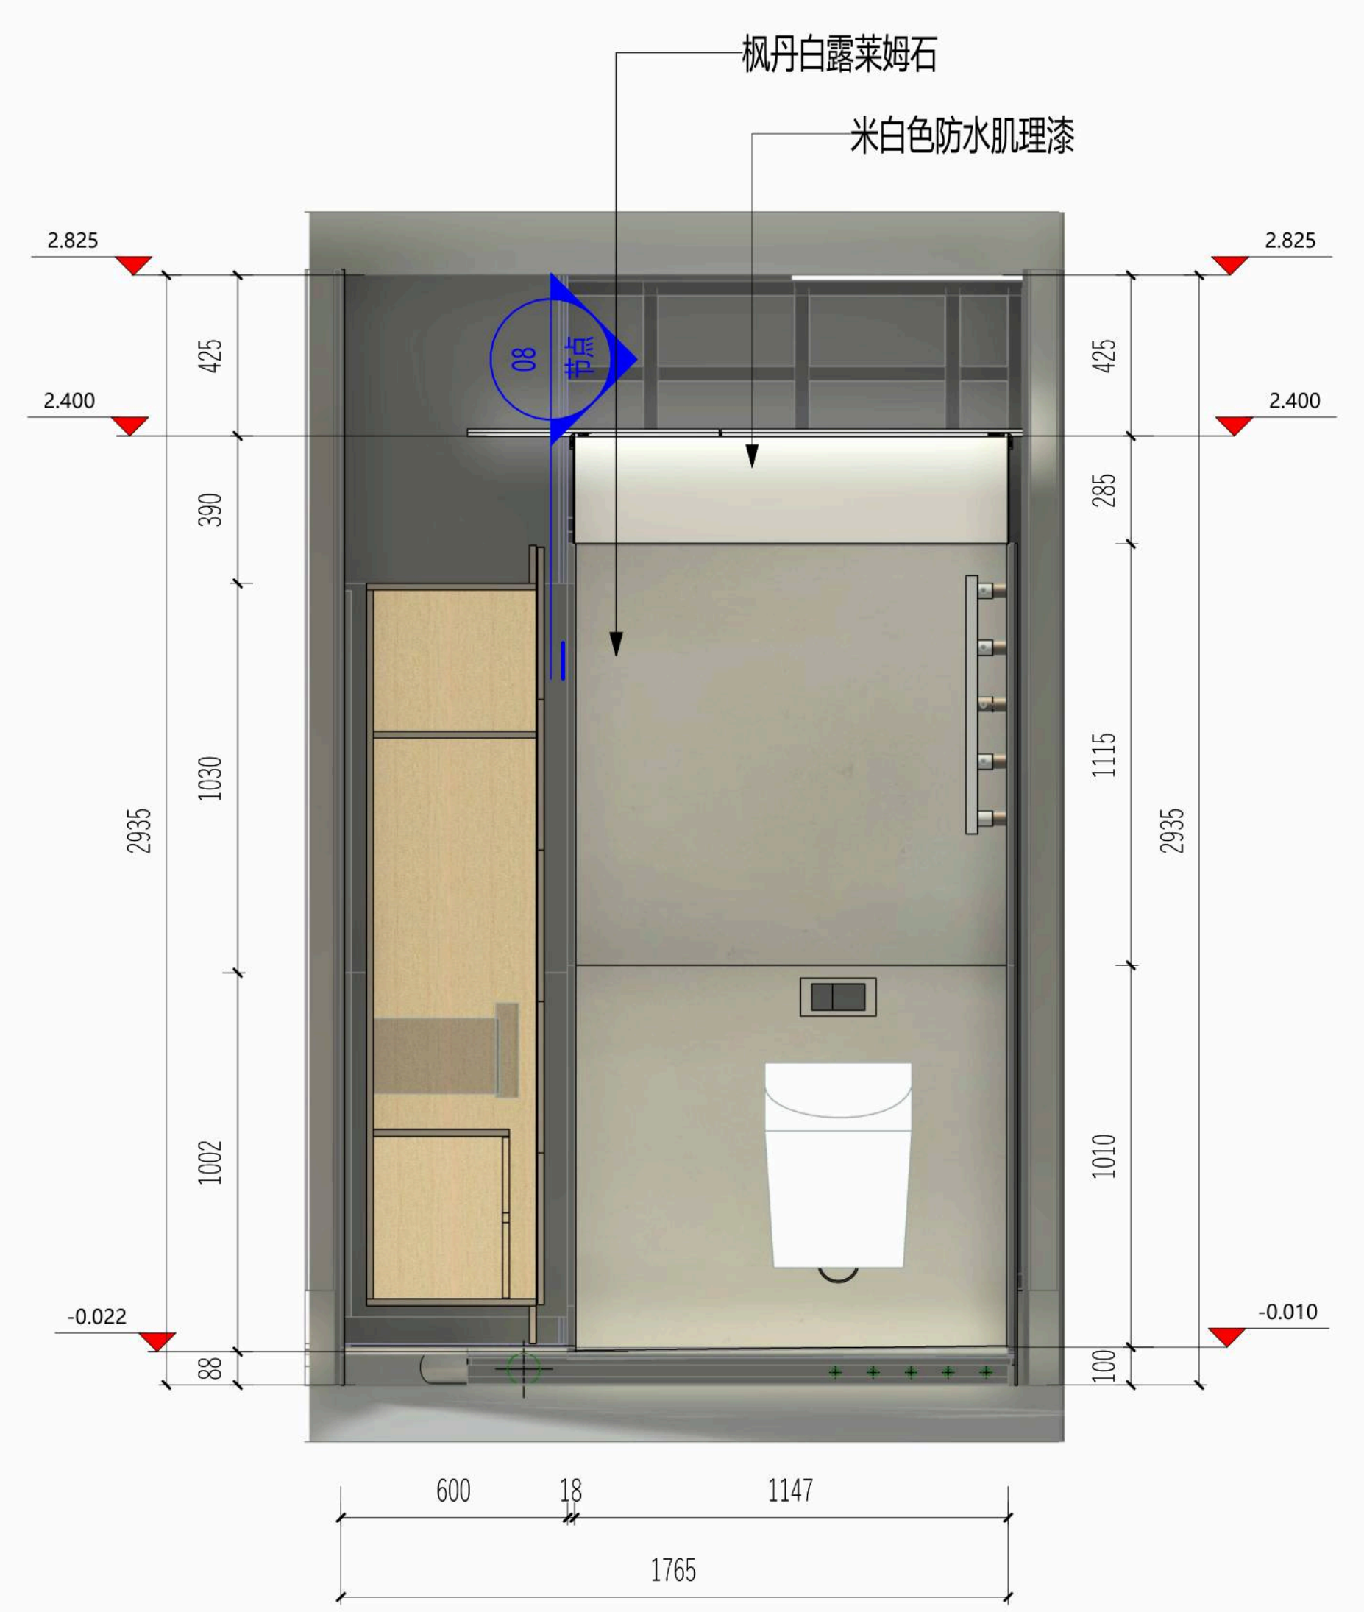
枫丹白露莱姆石
米白色防水肌理漆
2.825
2.400
-0.022
-0.010
08 节点
425
390
1030
1002
88
285
1115
1010
100
2935
600
18
1147
1765

次卫-02

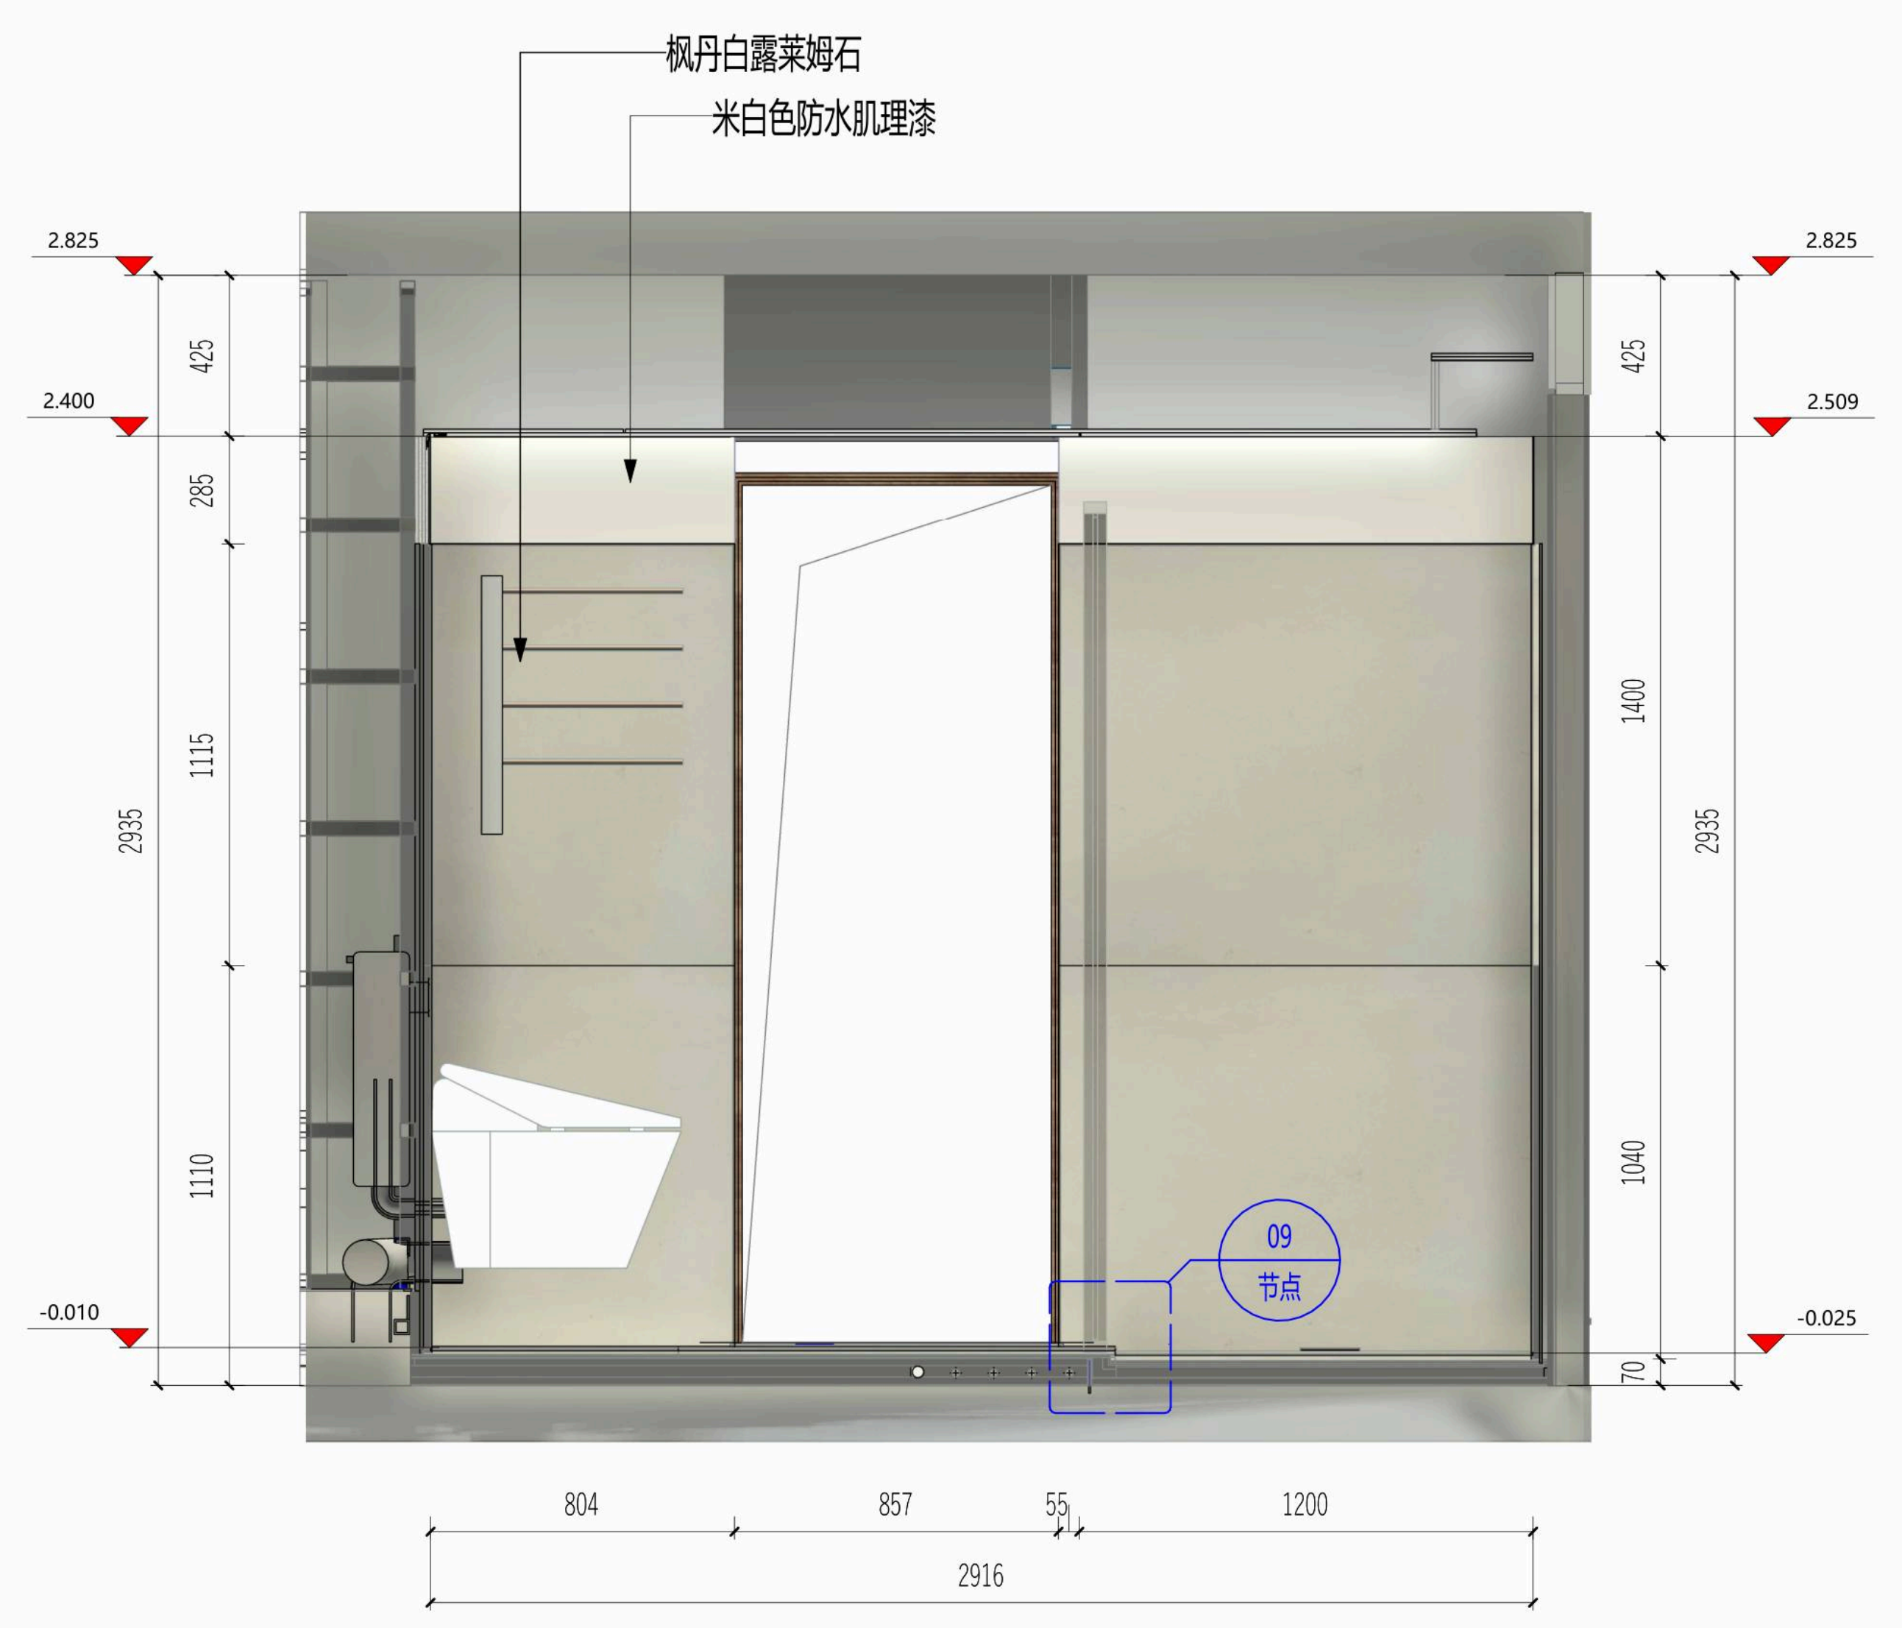
枫丹白露莱姆石
米白色防水肌理漆
2.825
2.400
2.509
-0.010
-0.025
09 节点
425
285
1115
1110
1400
1040
70
2935
804
857
55
1200
2916

次卫-03

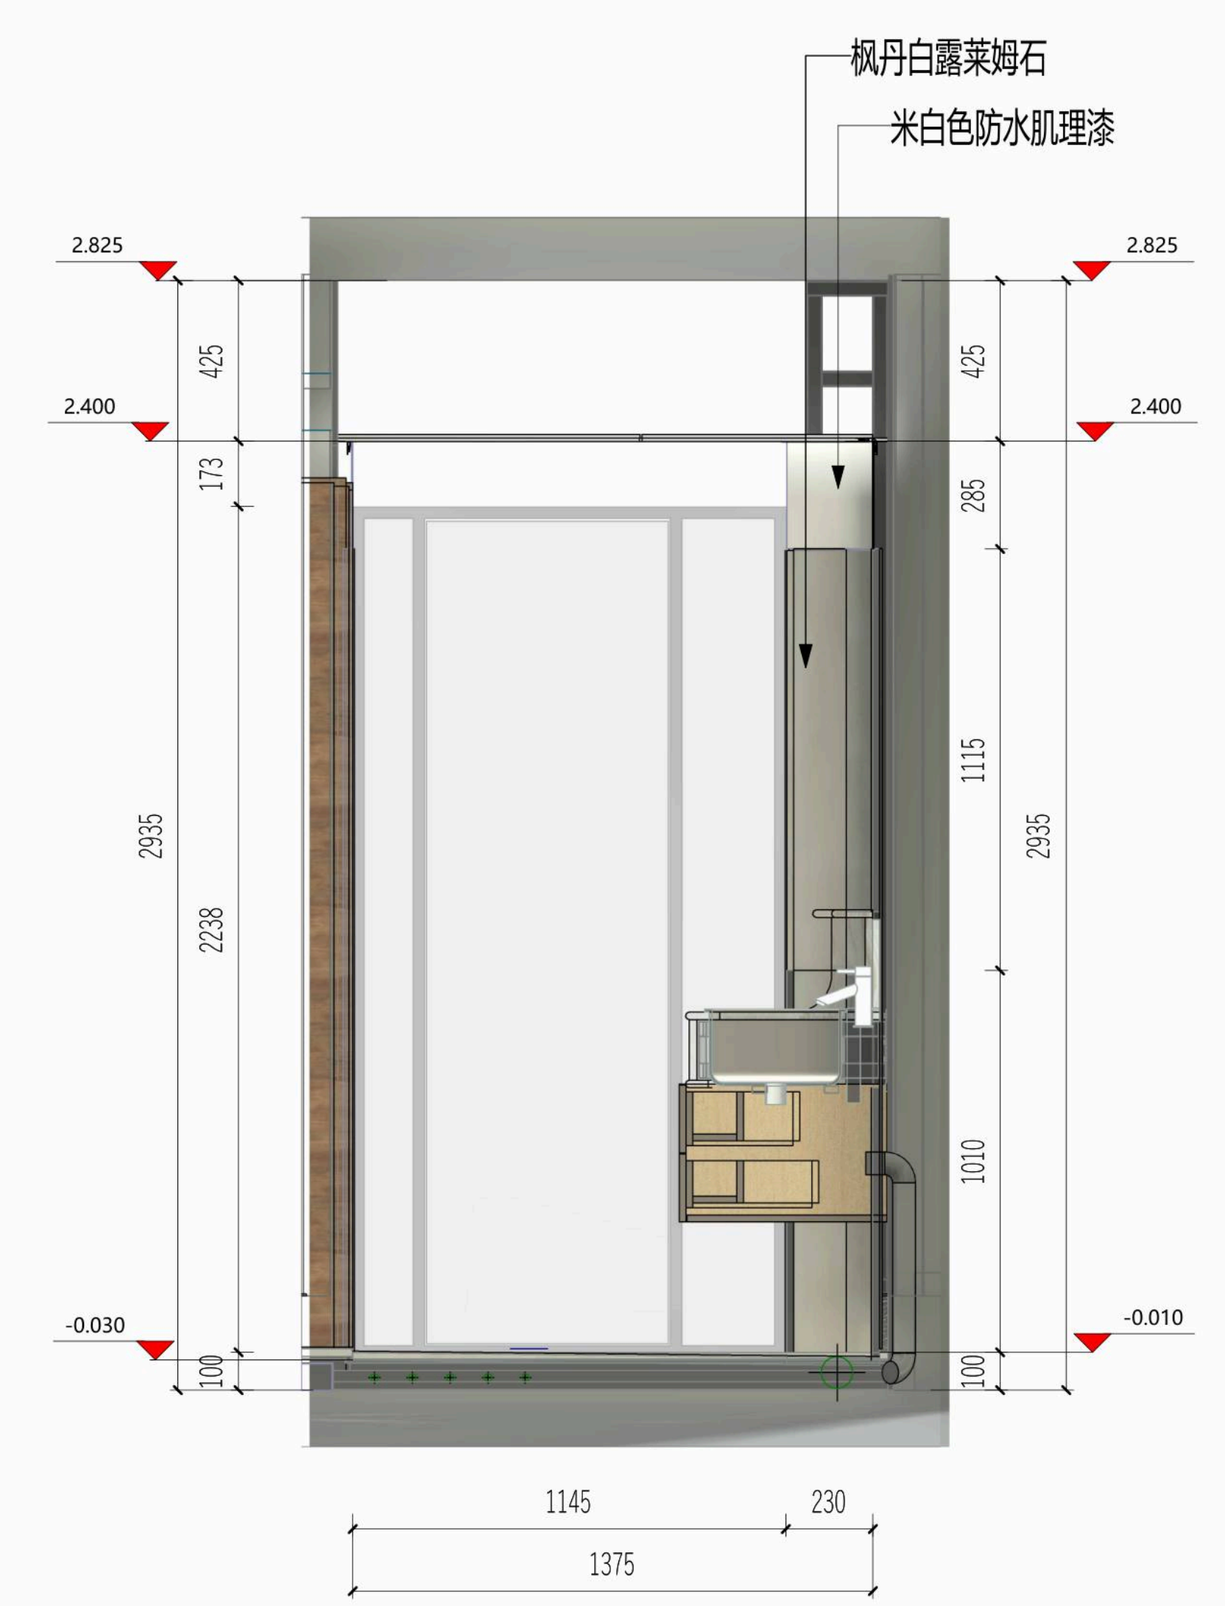
枫丹白露莱姆石
米白色防水肌理漆
2.825
2.400
-0.030
-0.010
425
173
2238
100
285
1115
1010
2935
1145
230
1375

次卫-04

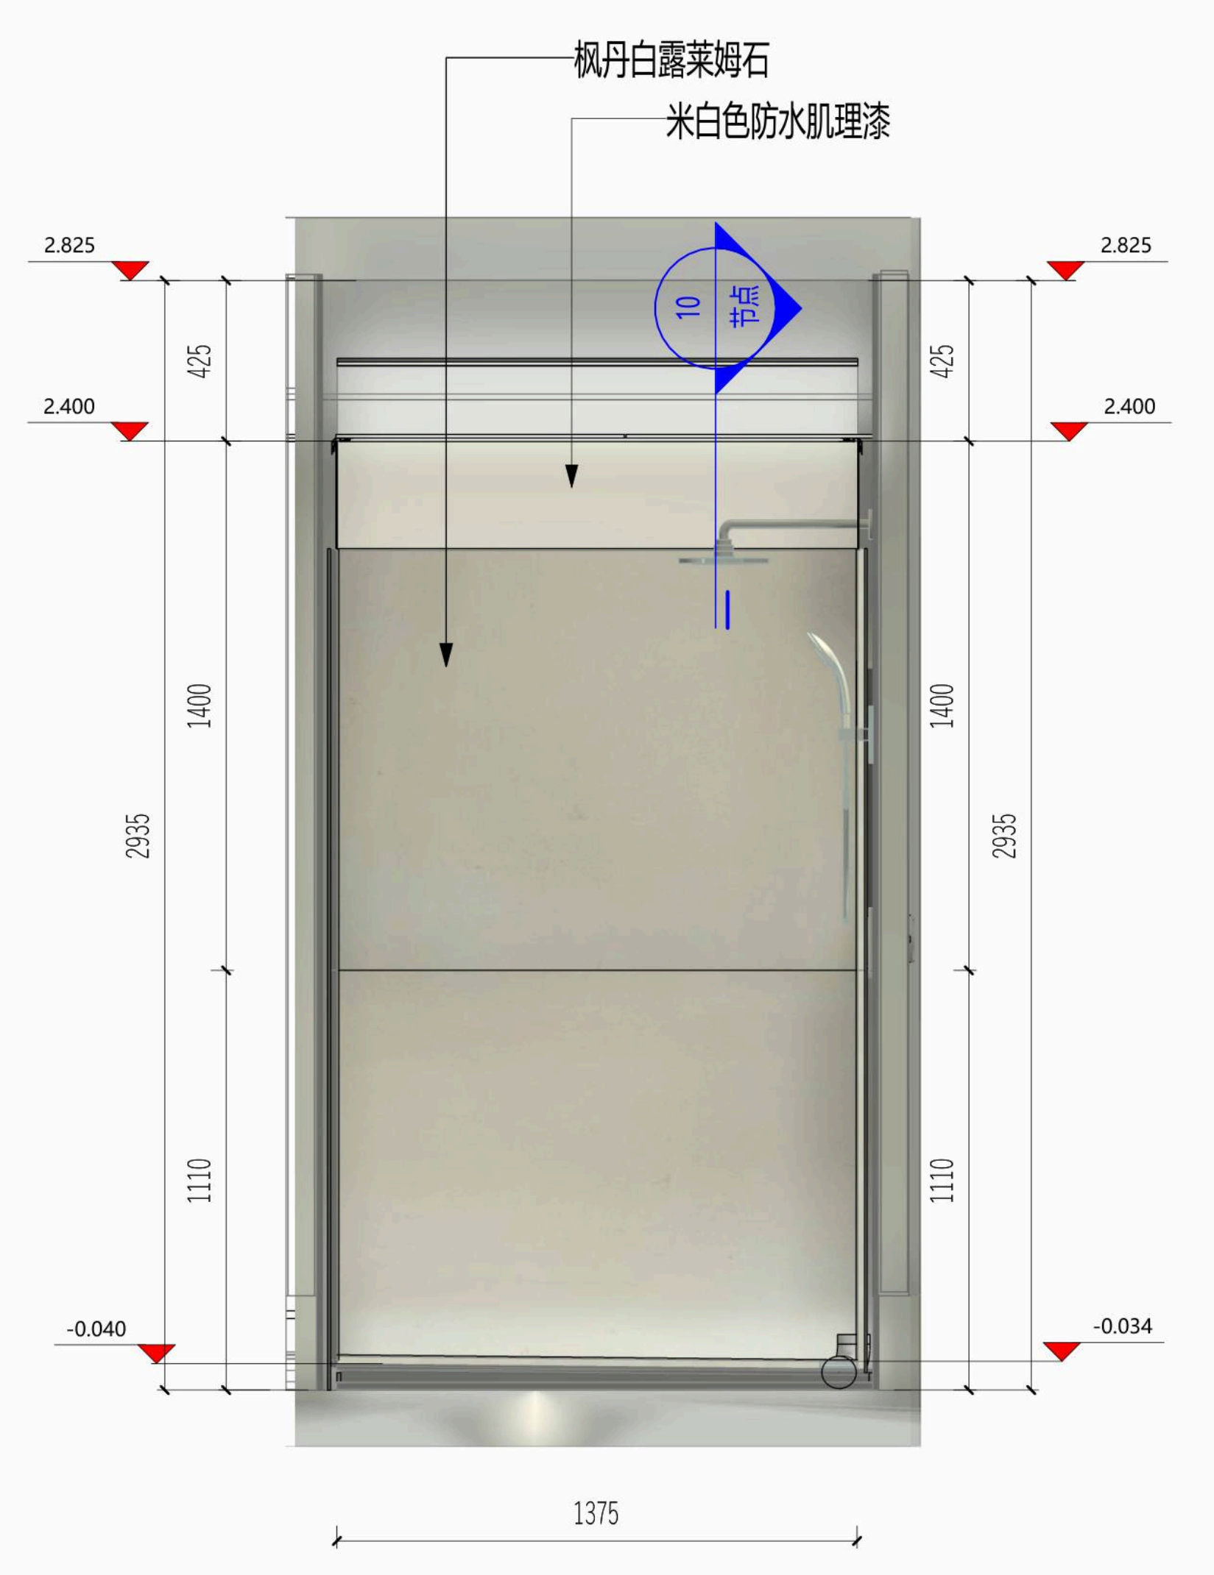
枫丹白露莱姆石
米白色防水肌理漆
2.825
2.400
-0.040
-0.034
10 节点
425
1400
1110
2935
1375

次卫-05

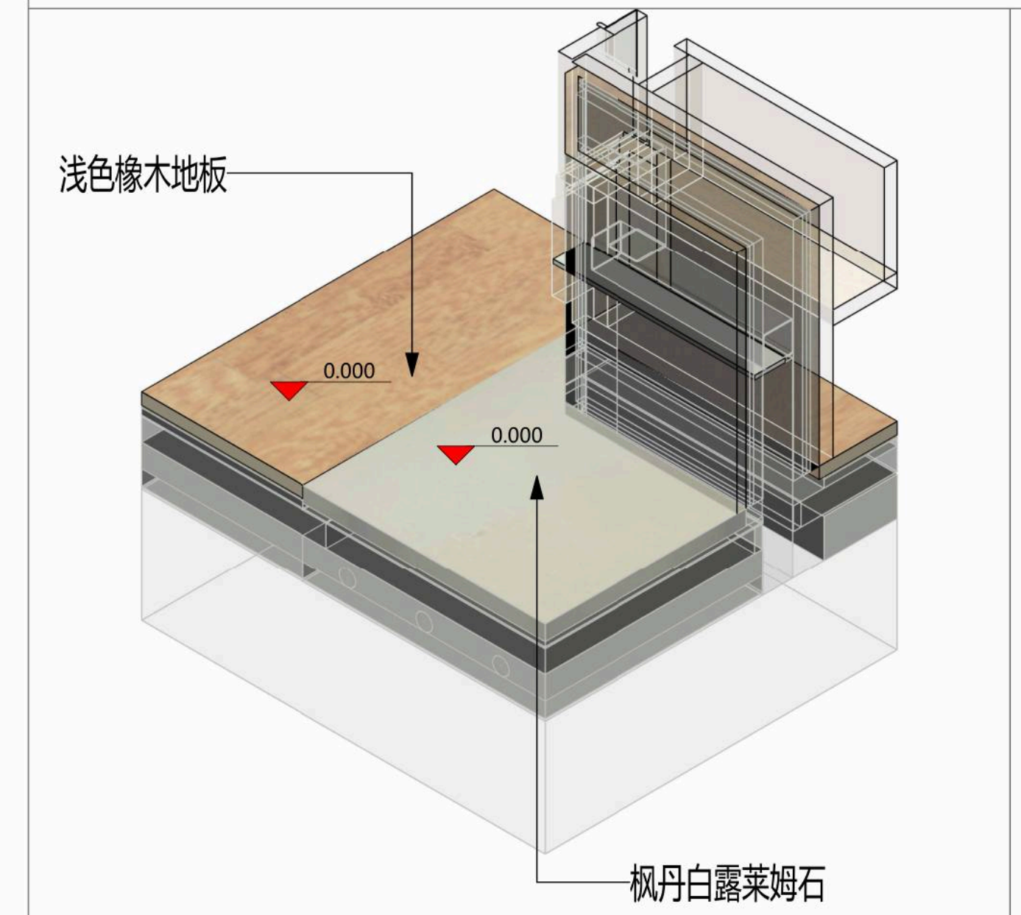
浅色橡木地板
0.000
0.000
枫丹白露莱姆石

节点-01

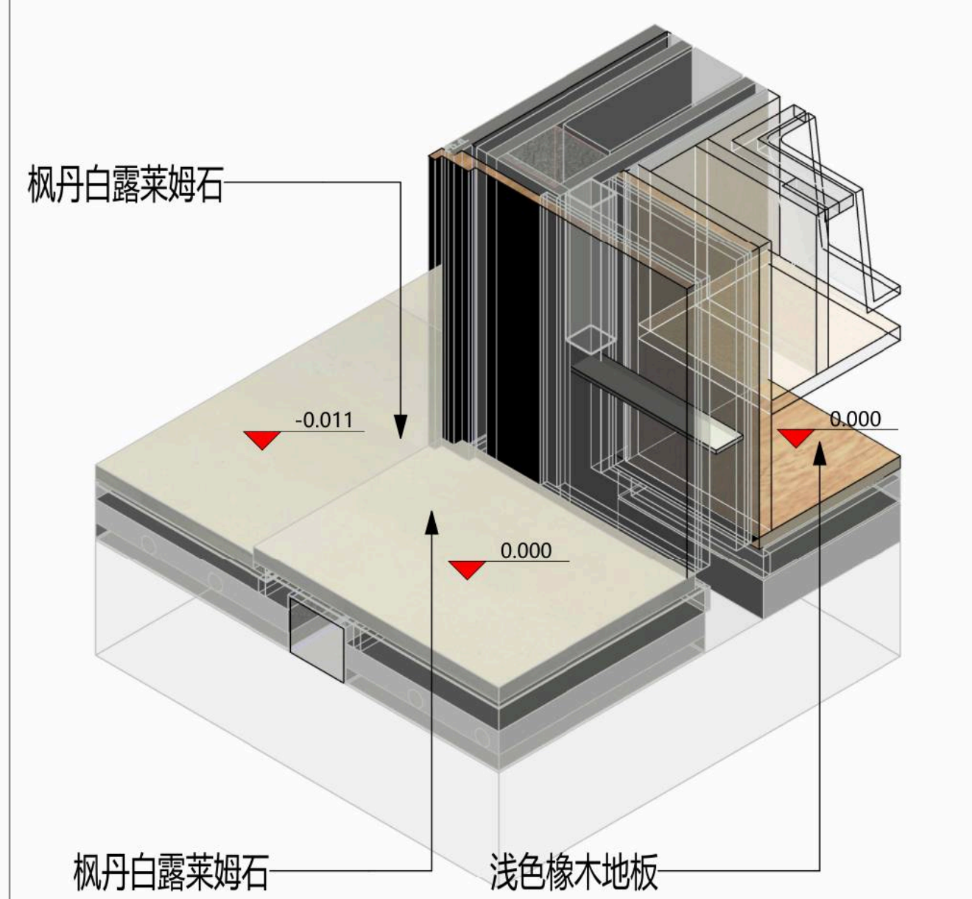
枫丹白露莱姆石
-0.011
0.000
0.000
枫丹白露莱姆石
浅色橡木地板

节点-02

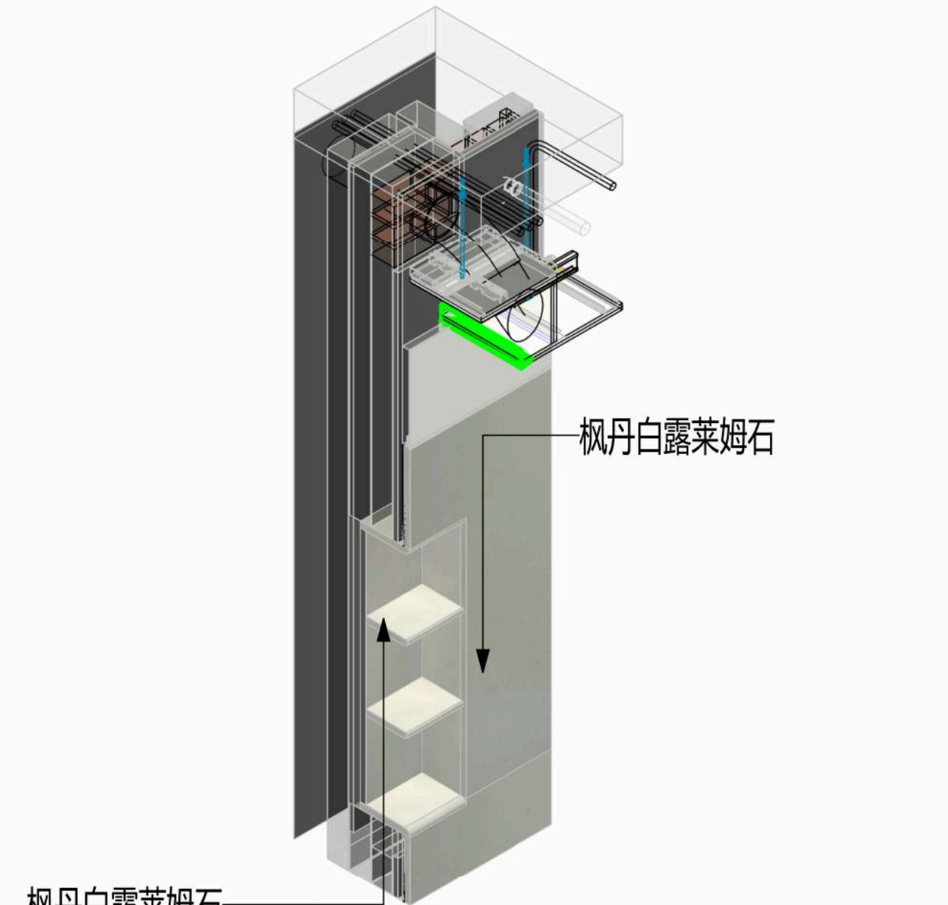
枫丹白露莱姆石
枫丹白露莱姆石

节点-03

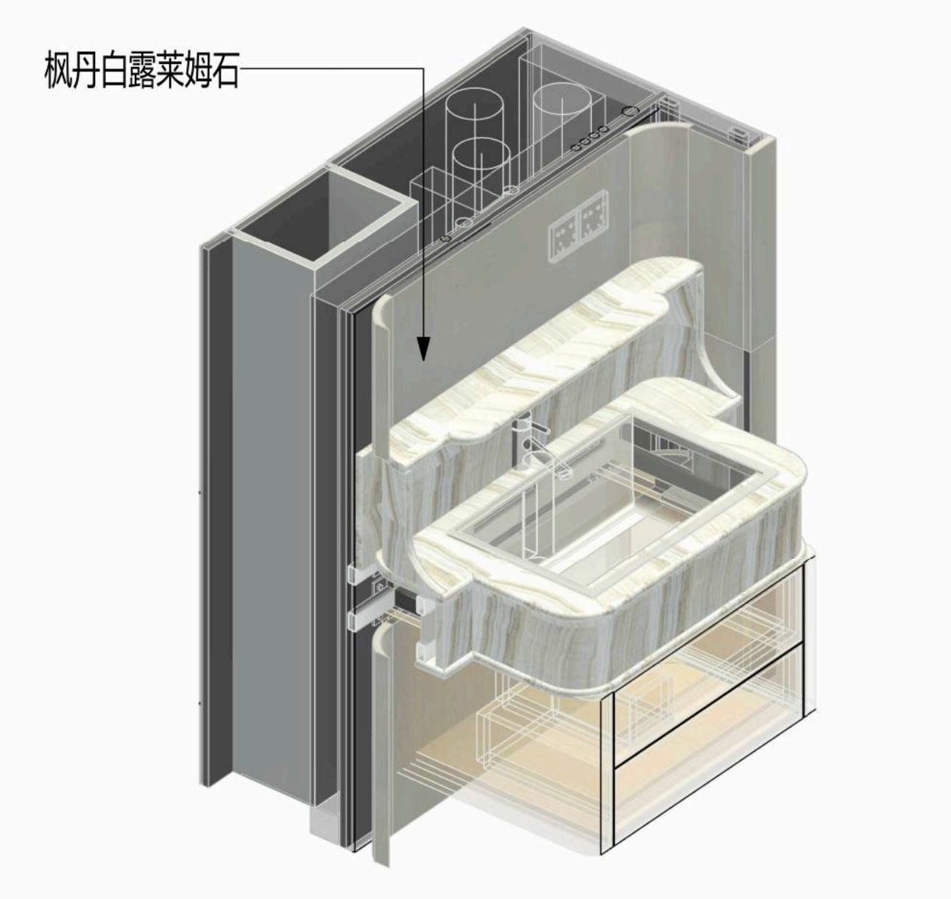

节点-04

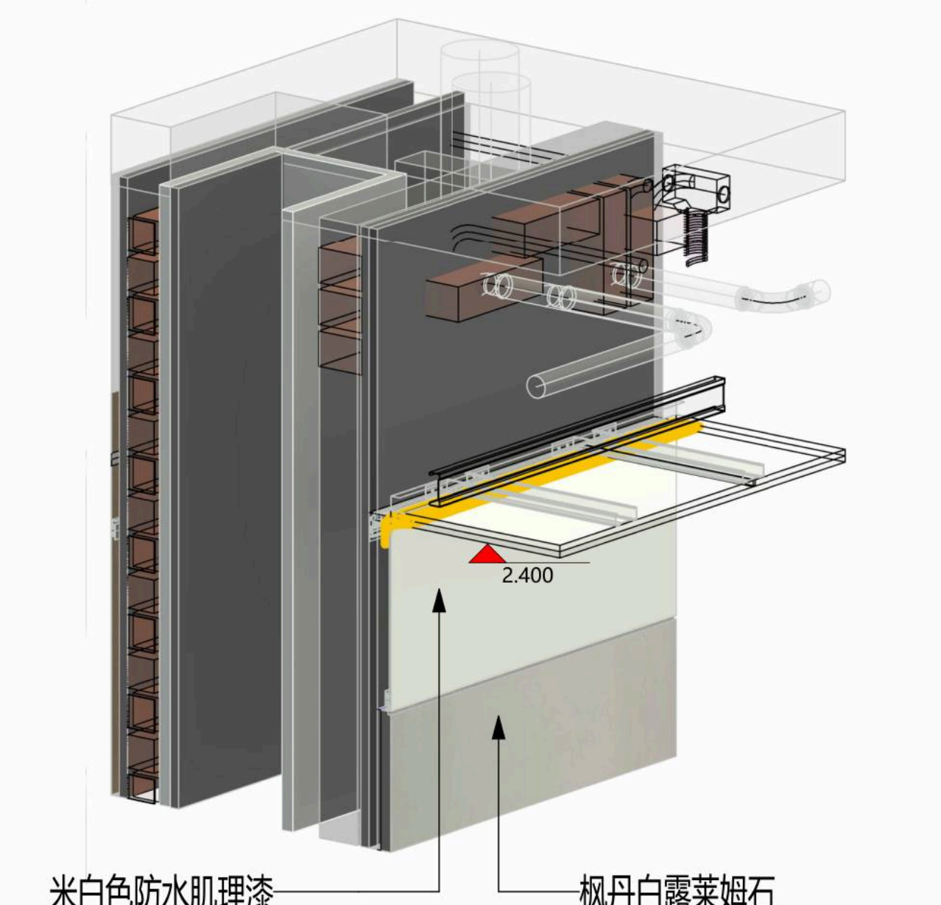
2.400
米白色防水肌理漆
枫丹白露莱姆石

节点-05

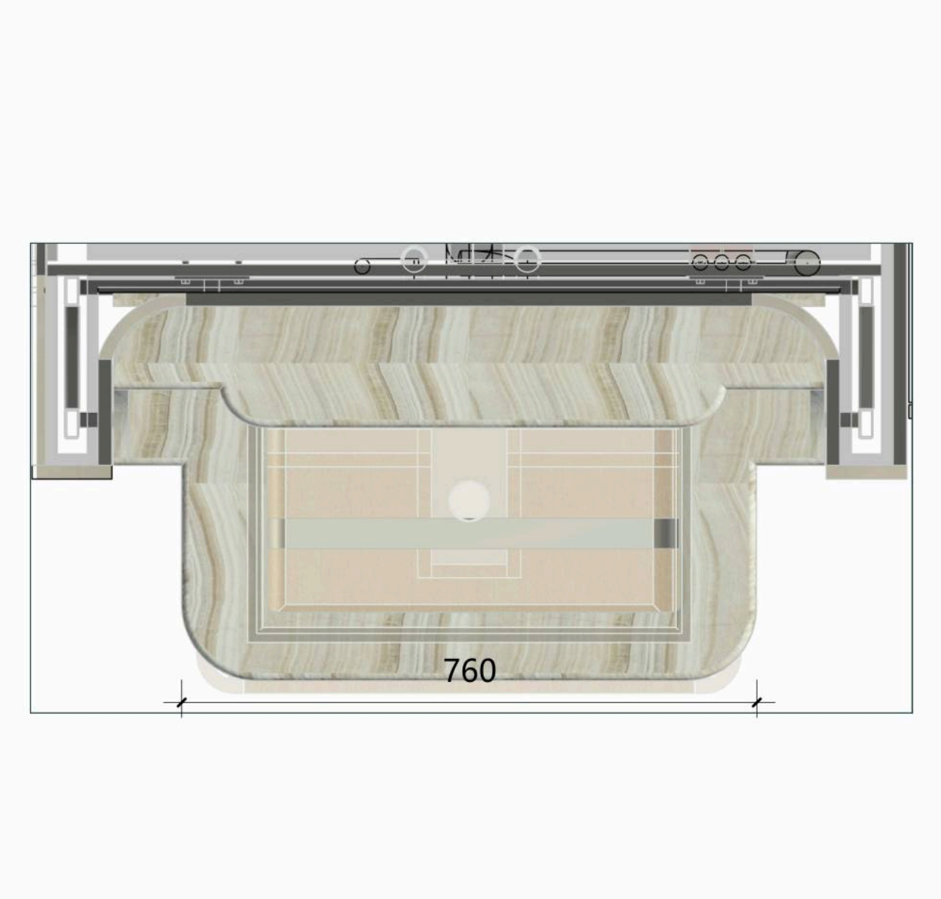

节点-06

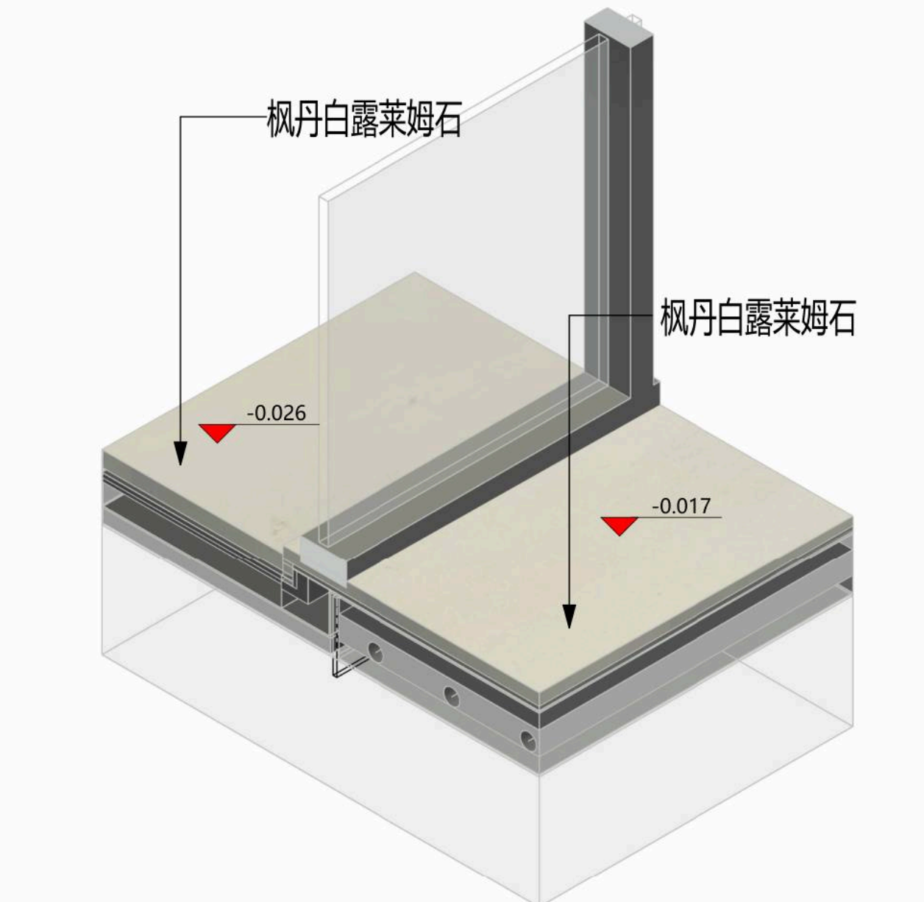
枫丹白露莱姆石
枫丹白露莱姆石
-0.026
-0.017

节点-07

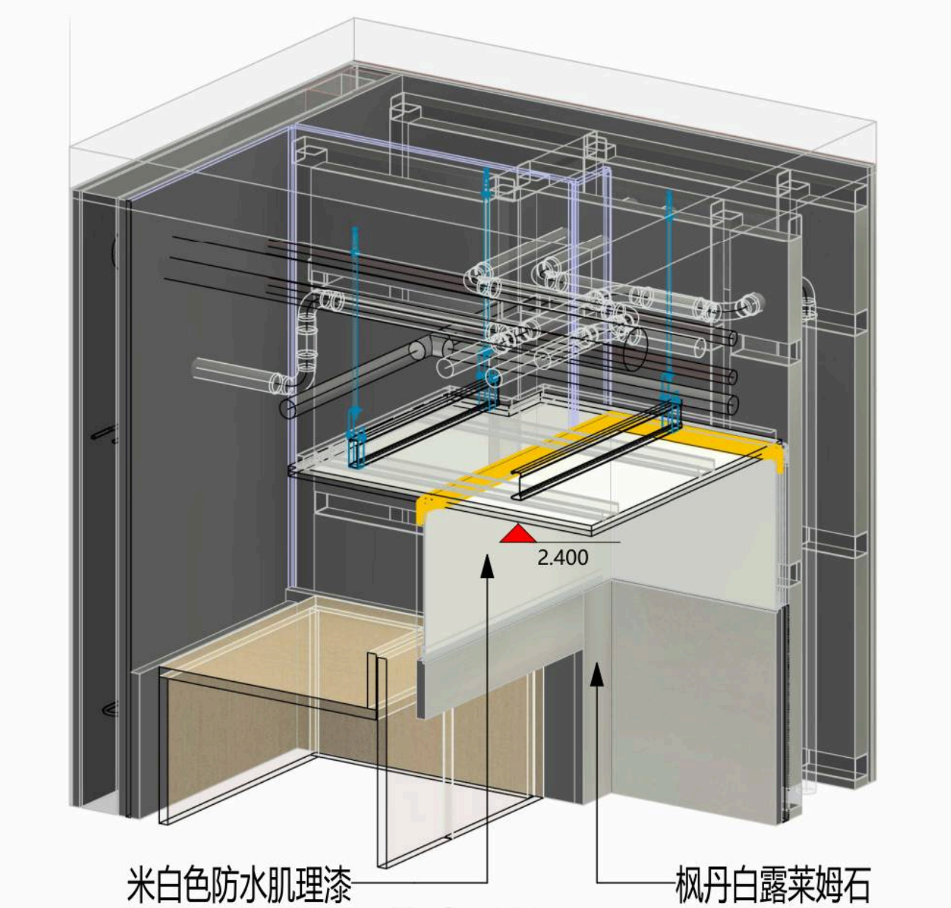
2.400
米白色防水肌理漆
枫丹白露莱姆石

节点-08

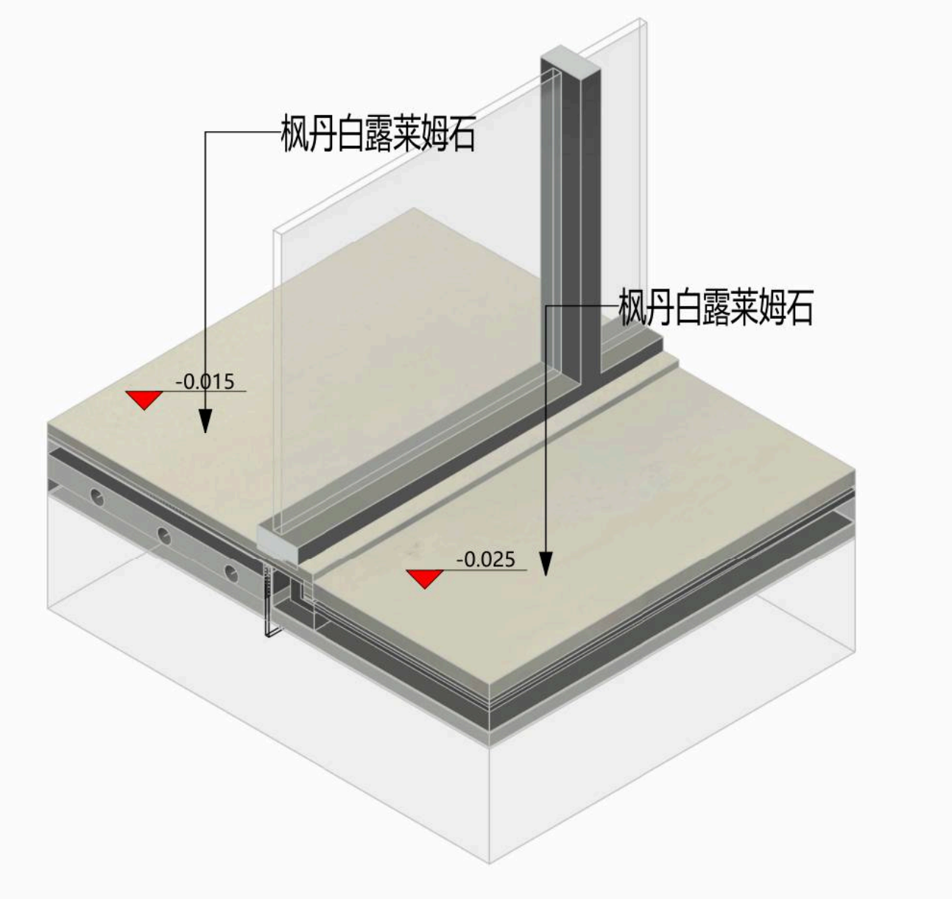
枫丹白露莱姆石
枫丹白露莱姆石
-0.015
-0.025

节点-09

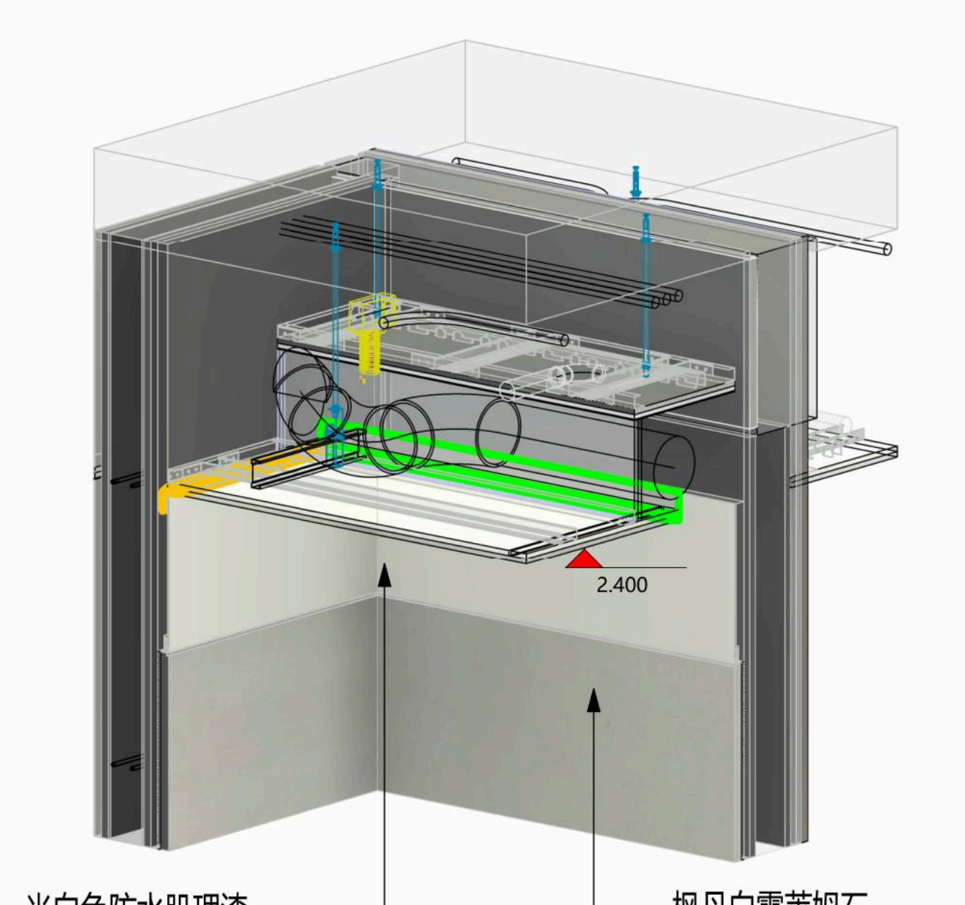
2.400
米白色防水肌理漆
枫丹白露莱姆石

节点-10

编号	图例	名称
1	▨	丹枫白露大理石
2	▨	直纹白玉大理石
3	▨	米白色防水肌理漆
4	▨	红色防水肌理漆
5	▨	米黄洞石大理石
6	▨	伊朗绿大理石
7	■	黑白根大理石
8	▨	意大利木纹
9	▨	白木纹石
10	▨	塔维勒莱姆石
11	▨	木饰面
12	▨	木地板
13	▨	墙布

盖章

注释
Notes
1.本图纸如与现场尺寸有误，请施工人员与项目负责人联系。
2.施工前施工人员应认真查阅此图，如有不明确尺寸，按现场测量为准。
3.本图纸必须经甲乙双方认可并签字方可作为施工依据。

日期
Date 05/20/26

修订
Revision
△1

项目
Project
潮映华岸府3-801

比例
Scale
次卫石材铺贴

图纸编号
Drawing No.
ST-13

项目编号
Project No.

©2025

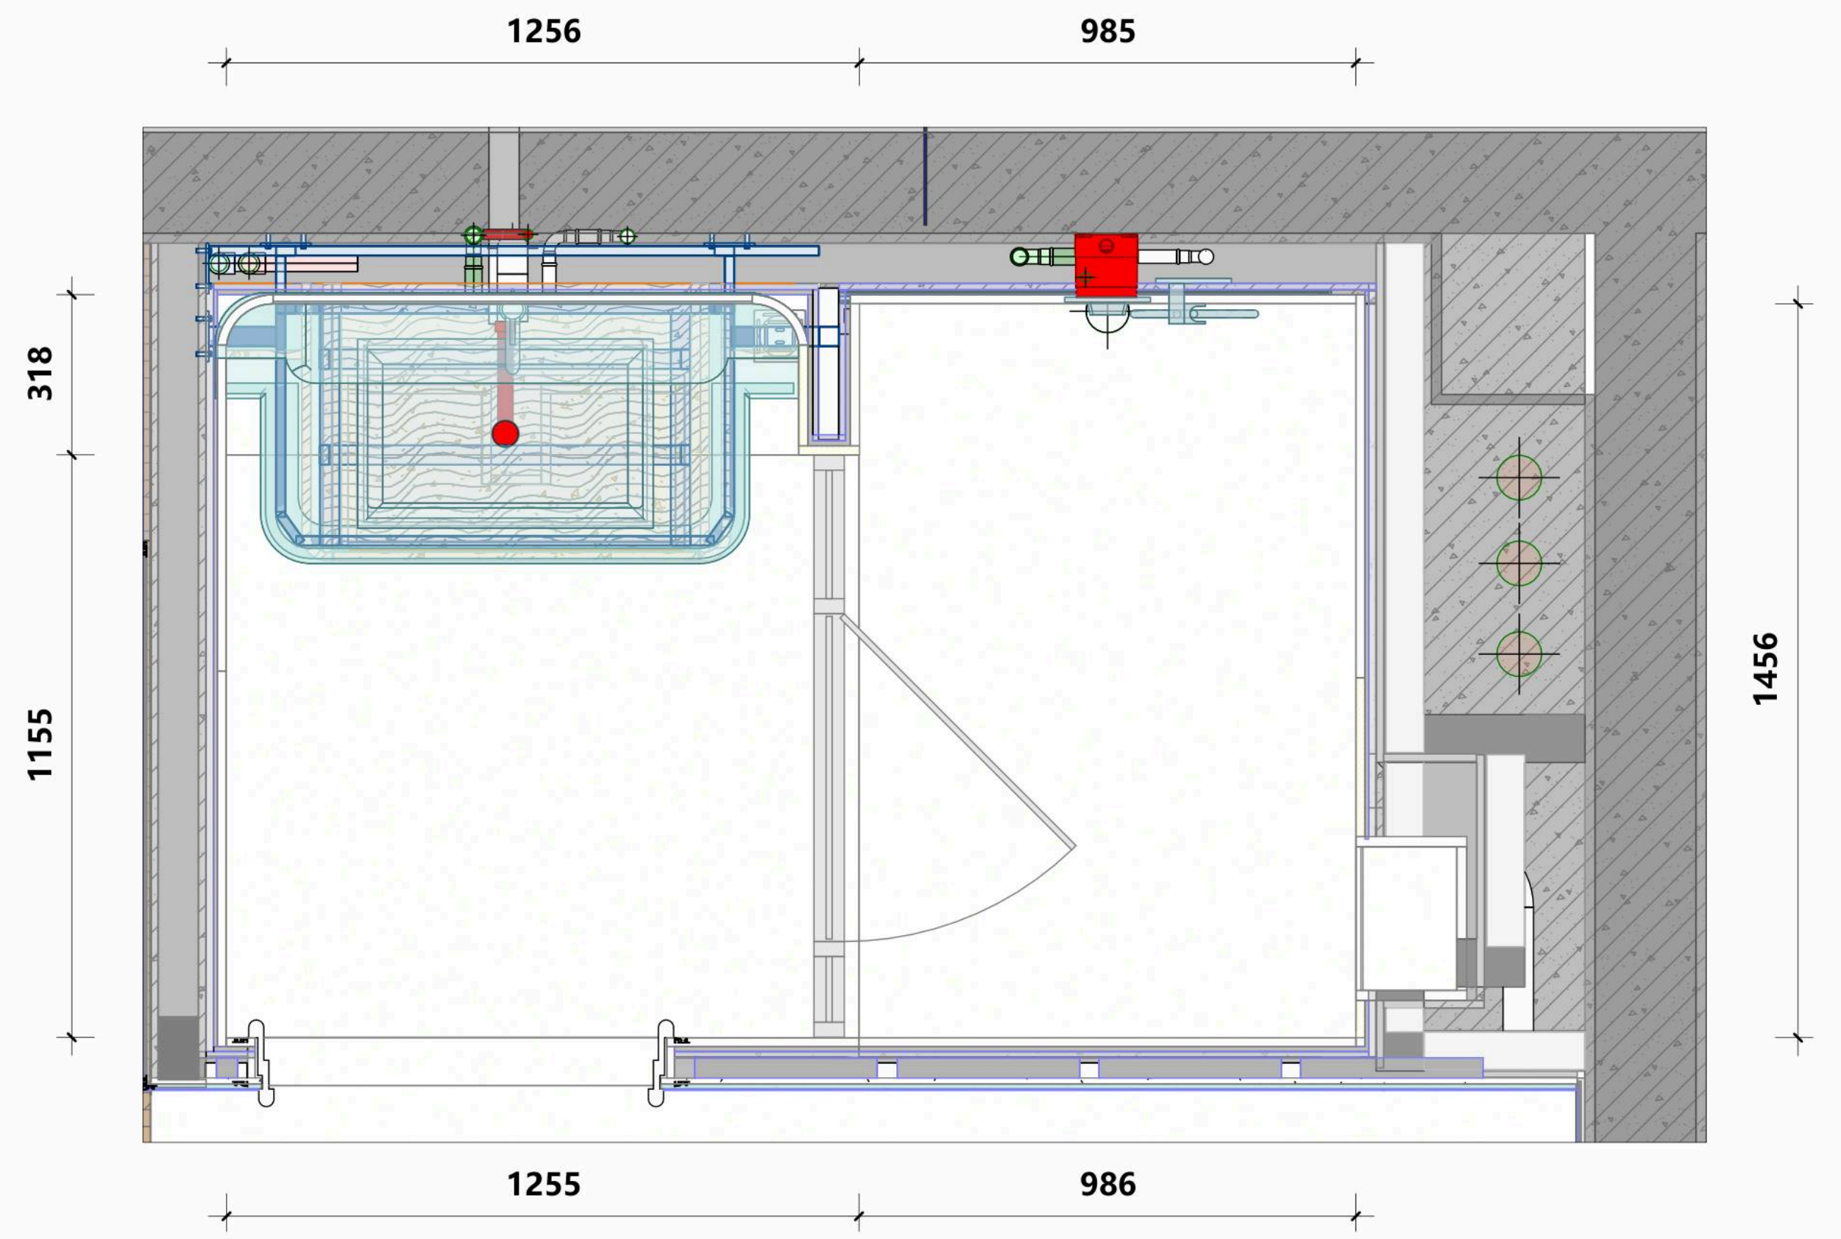
1256
985
318
1155
1456
1255
986

地面铺贴图

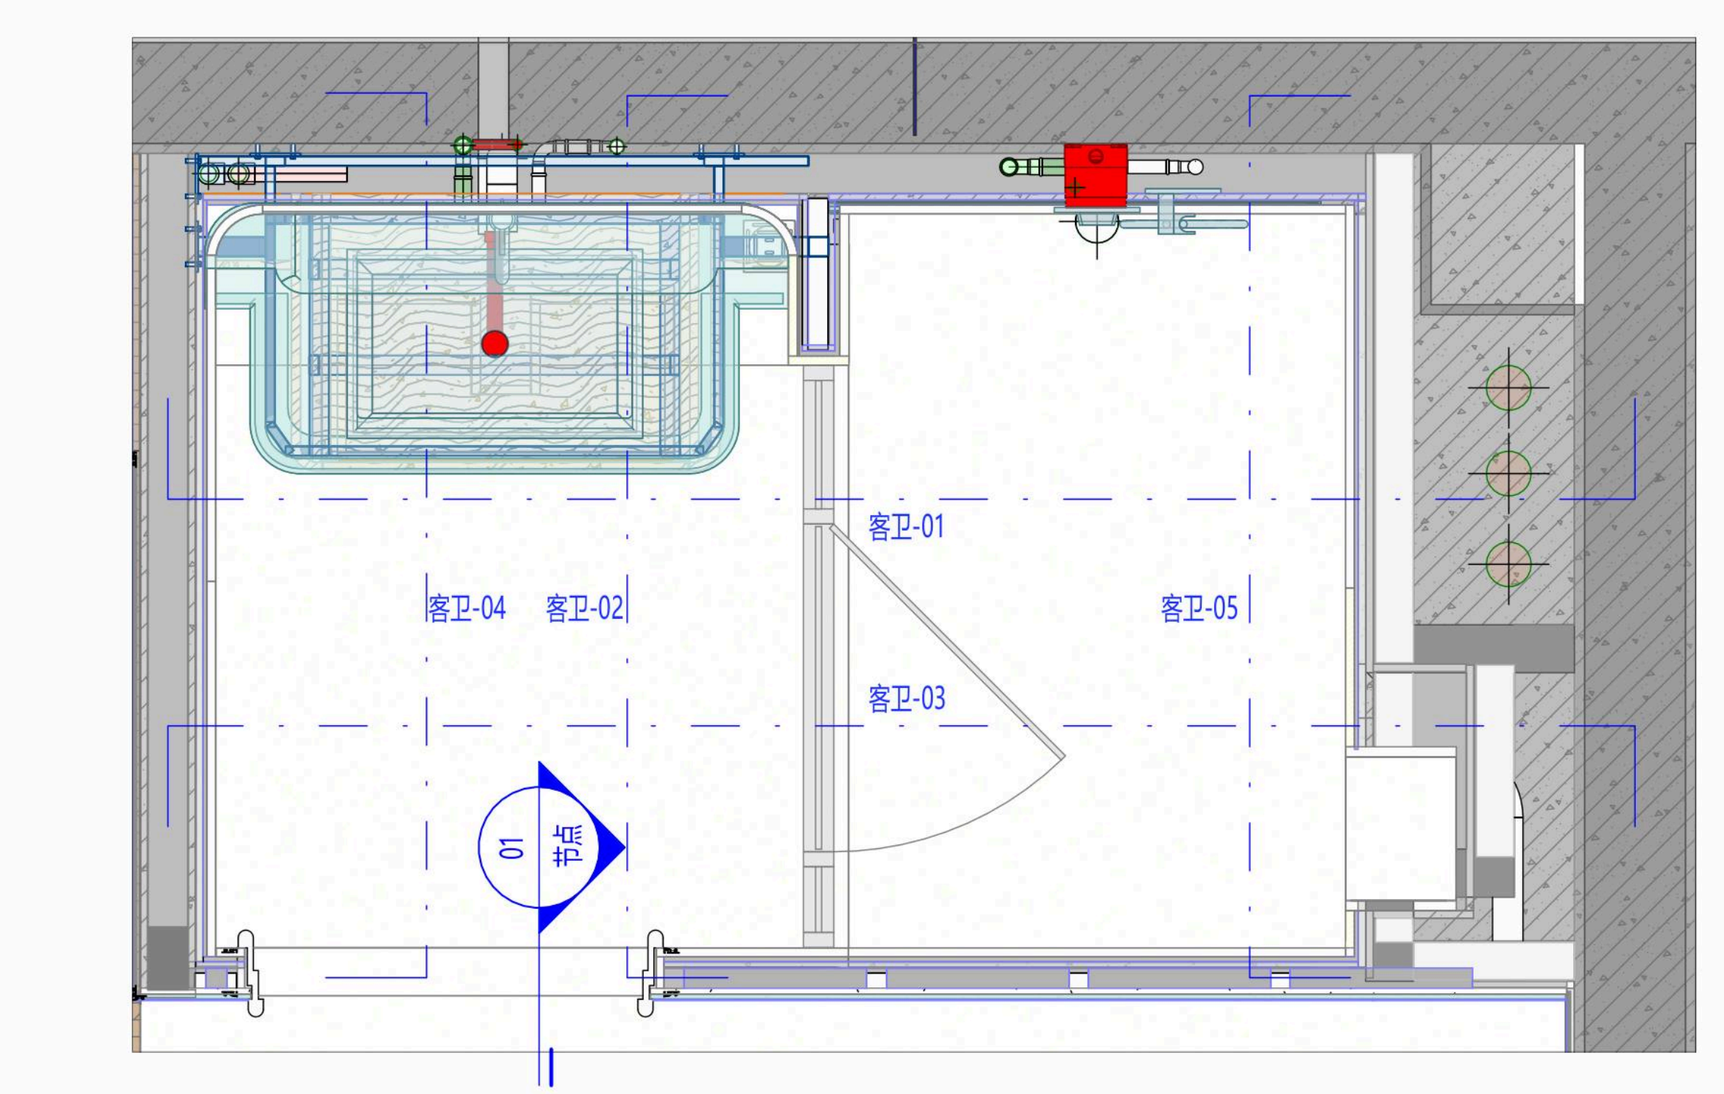
客卫-01
客卫-04
客卫-02
客卫-05
客卫-03
01
节点

索引图

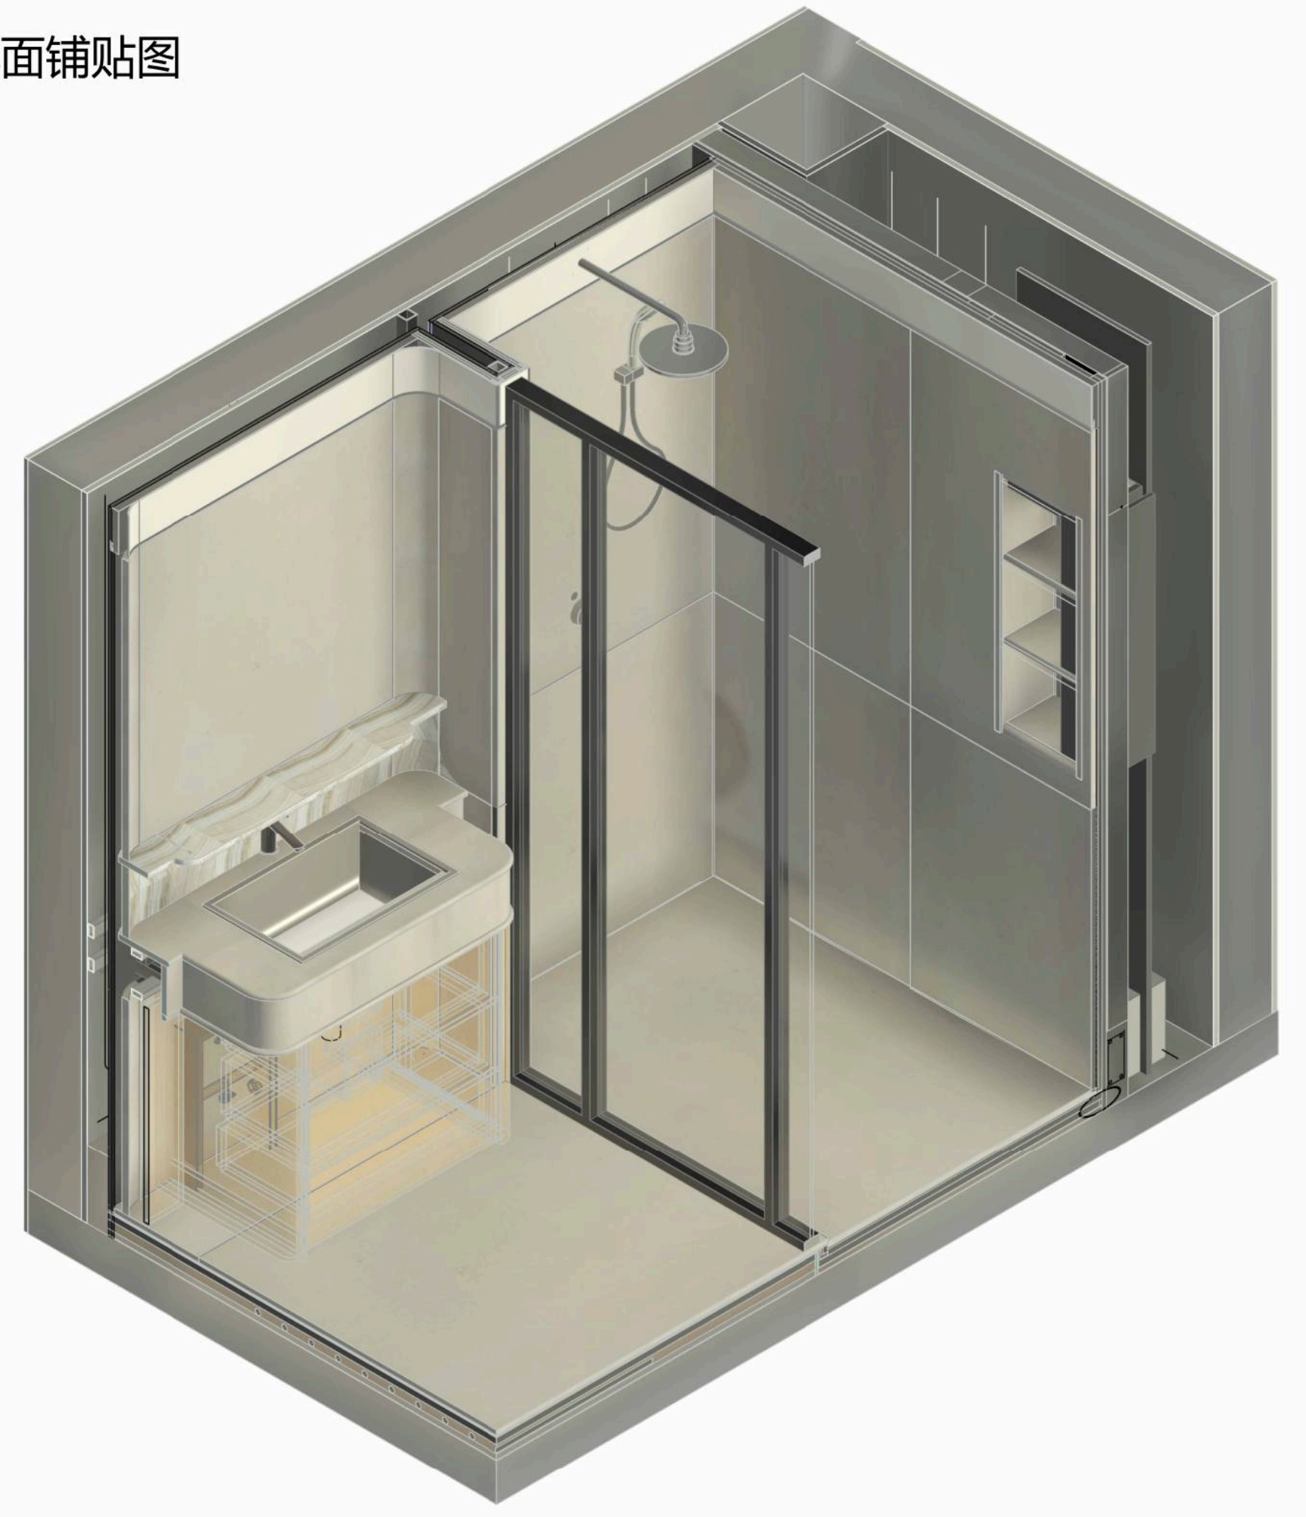

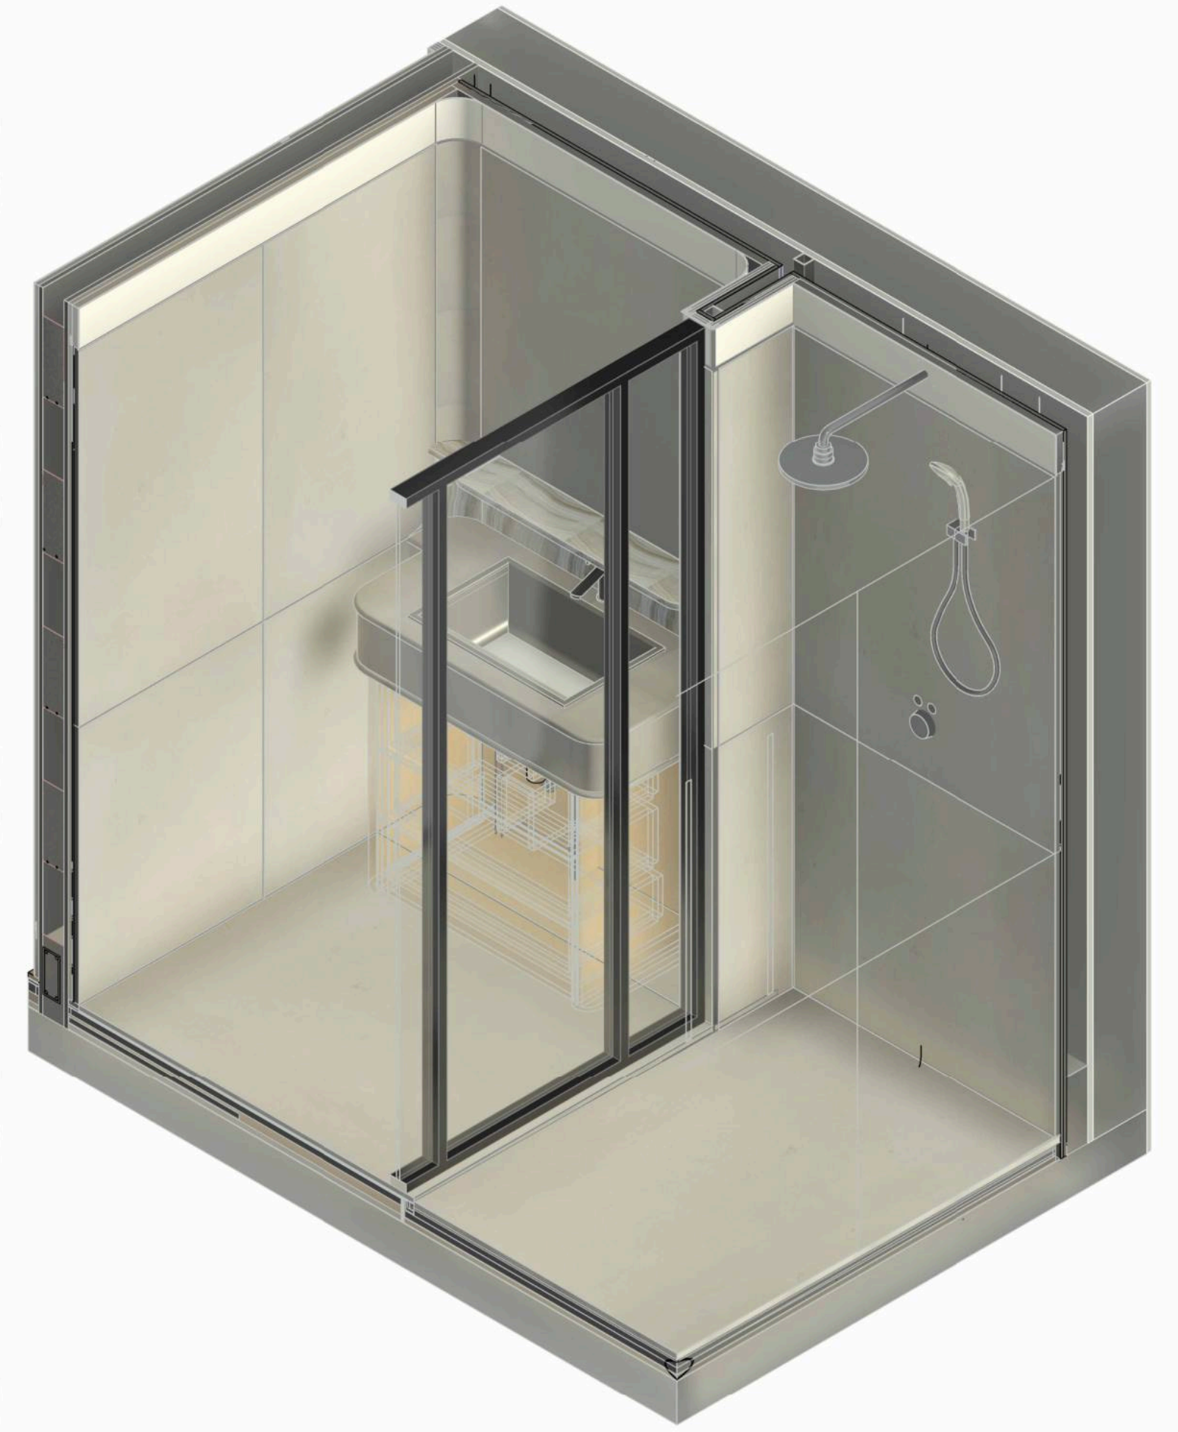

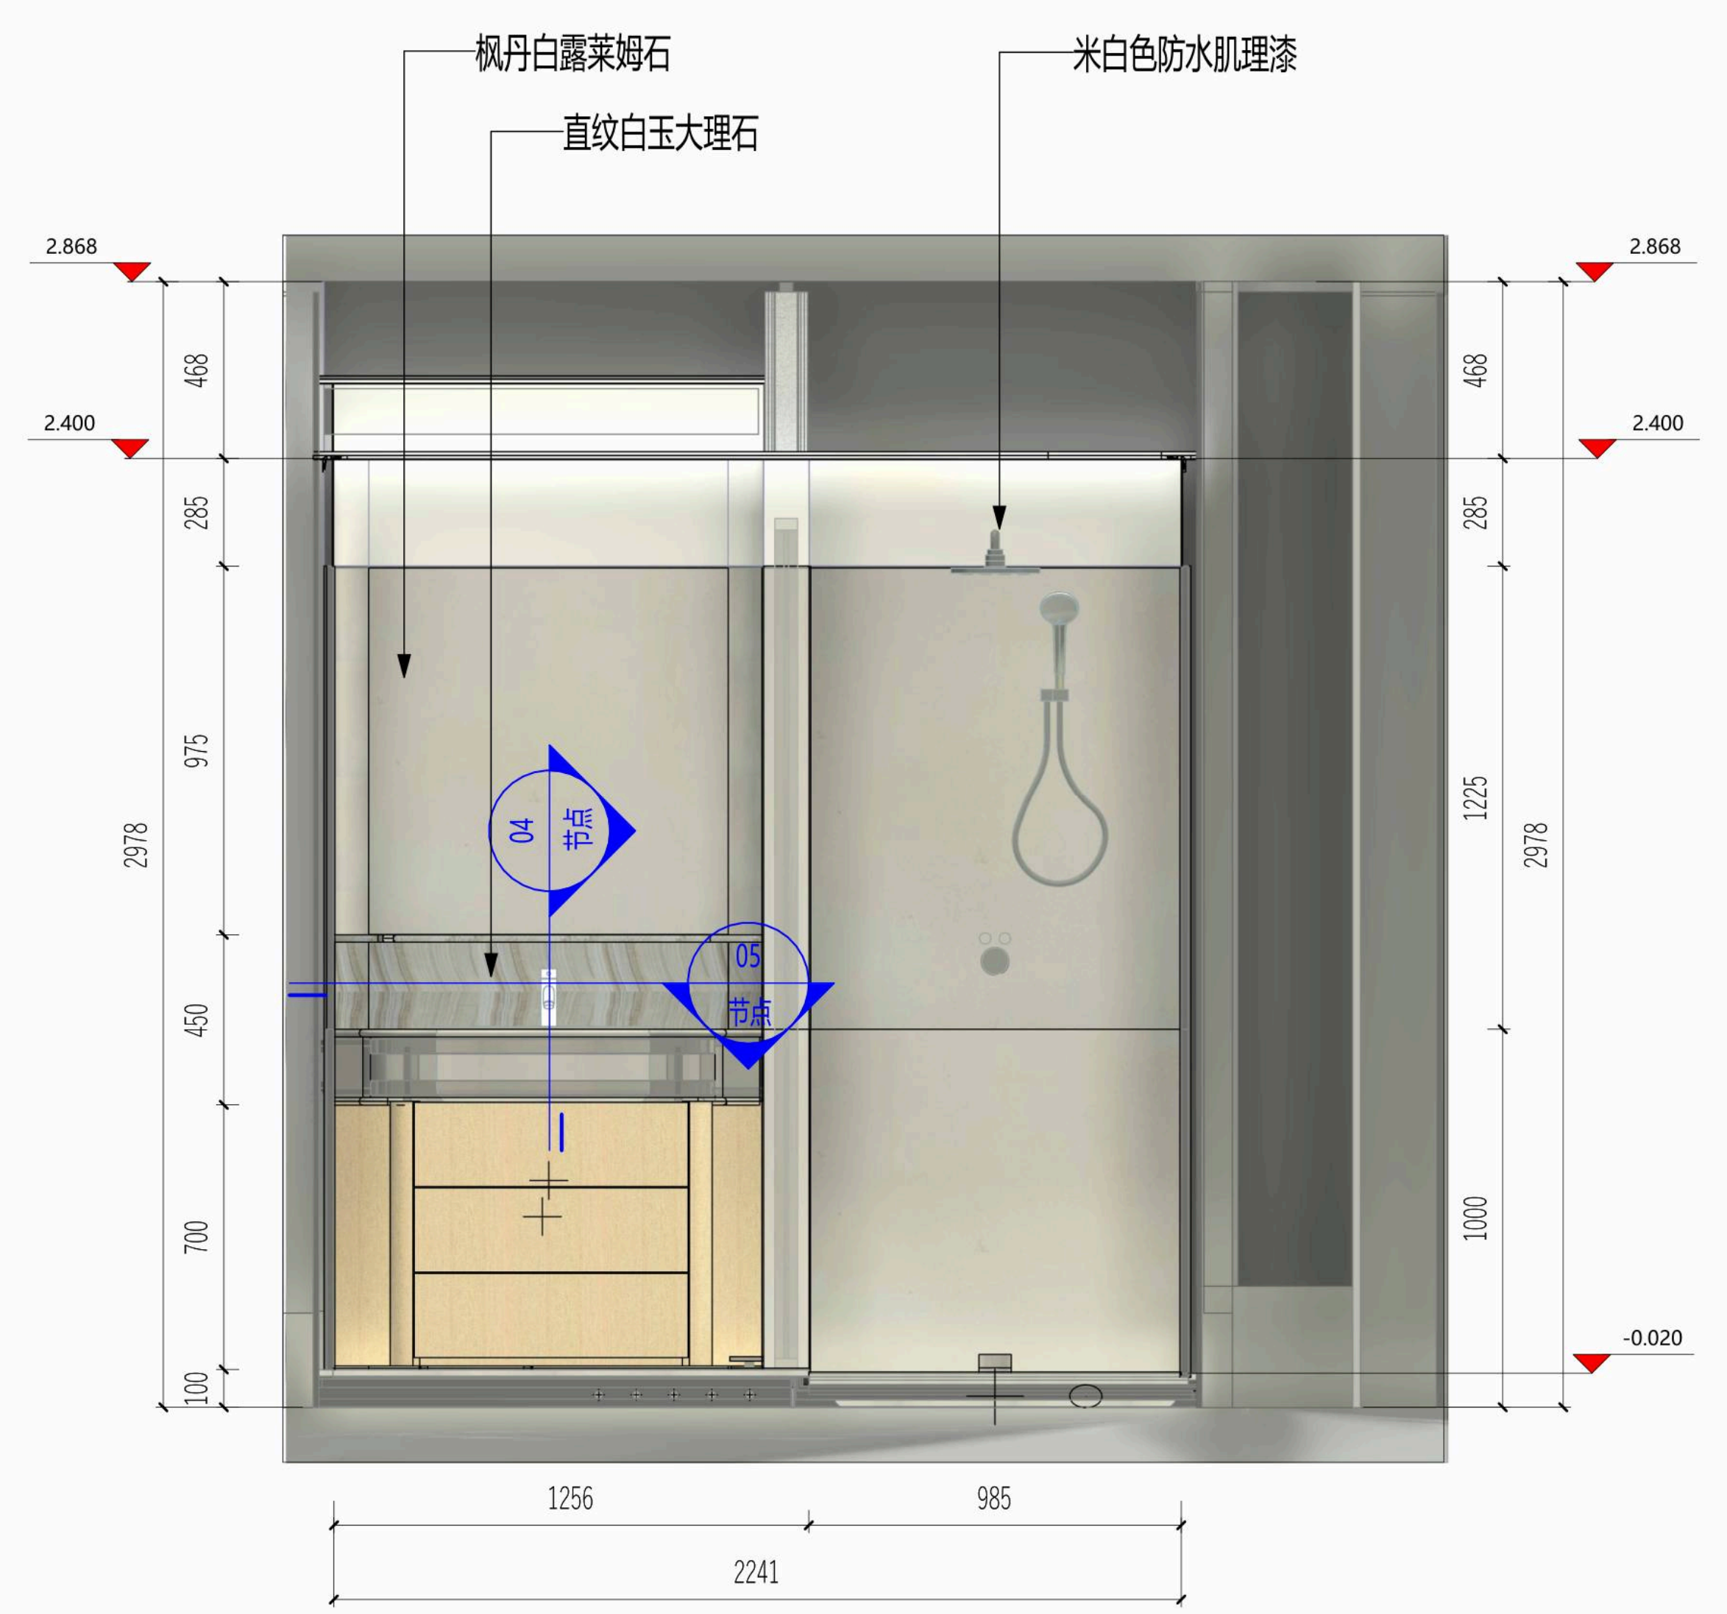
枫丹白露莱姆石
直纹白玉大理石
米白色防水肌理漆
2.868
2.400
-0.020
468
285
975
450
700
100
2978
1225
1000
04
节点
05
节点
1256
985
2241

客卫-01

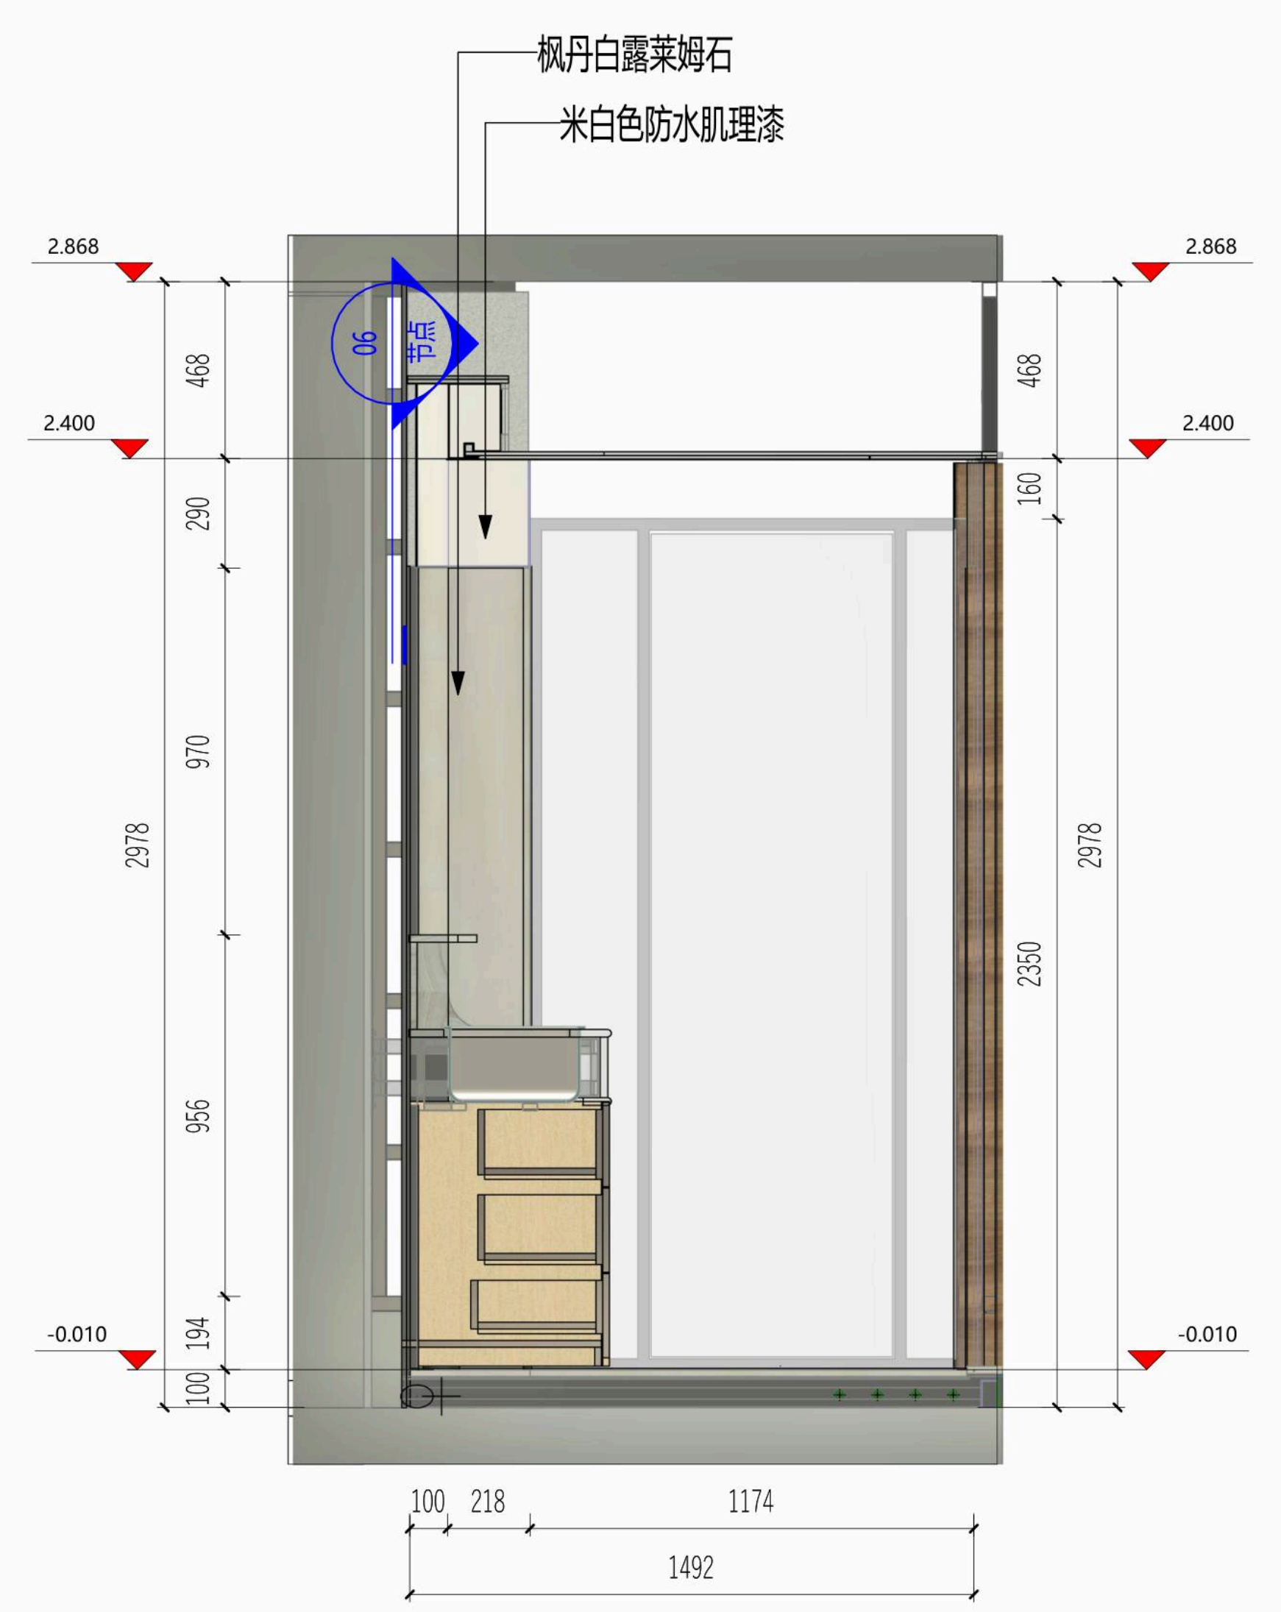
枫丹白露莱姆石
米白色防水肌理漆
2.868
2.400
-0.010
468
290
970
956
194
100
2978
160
2350
06
节点
100
218
1174
1492

客卫-02

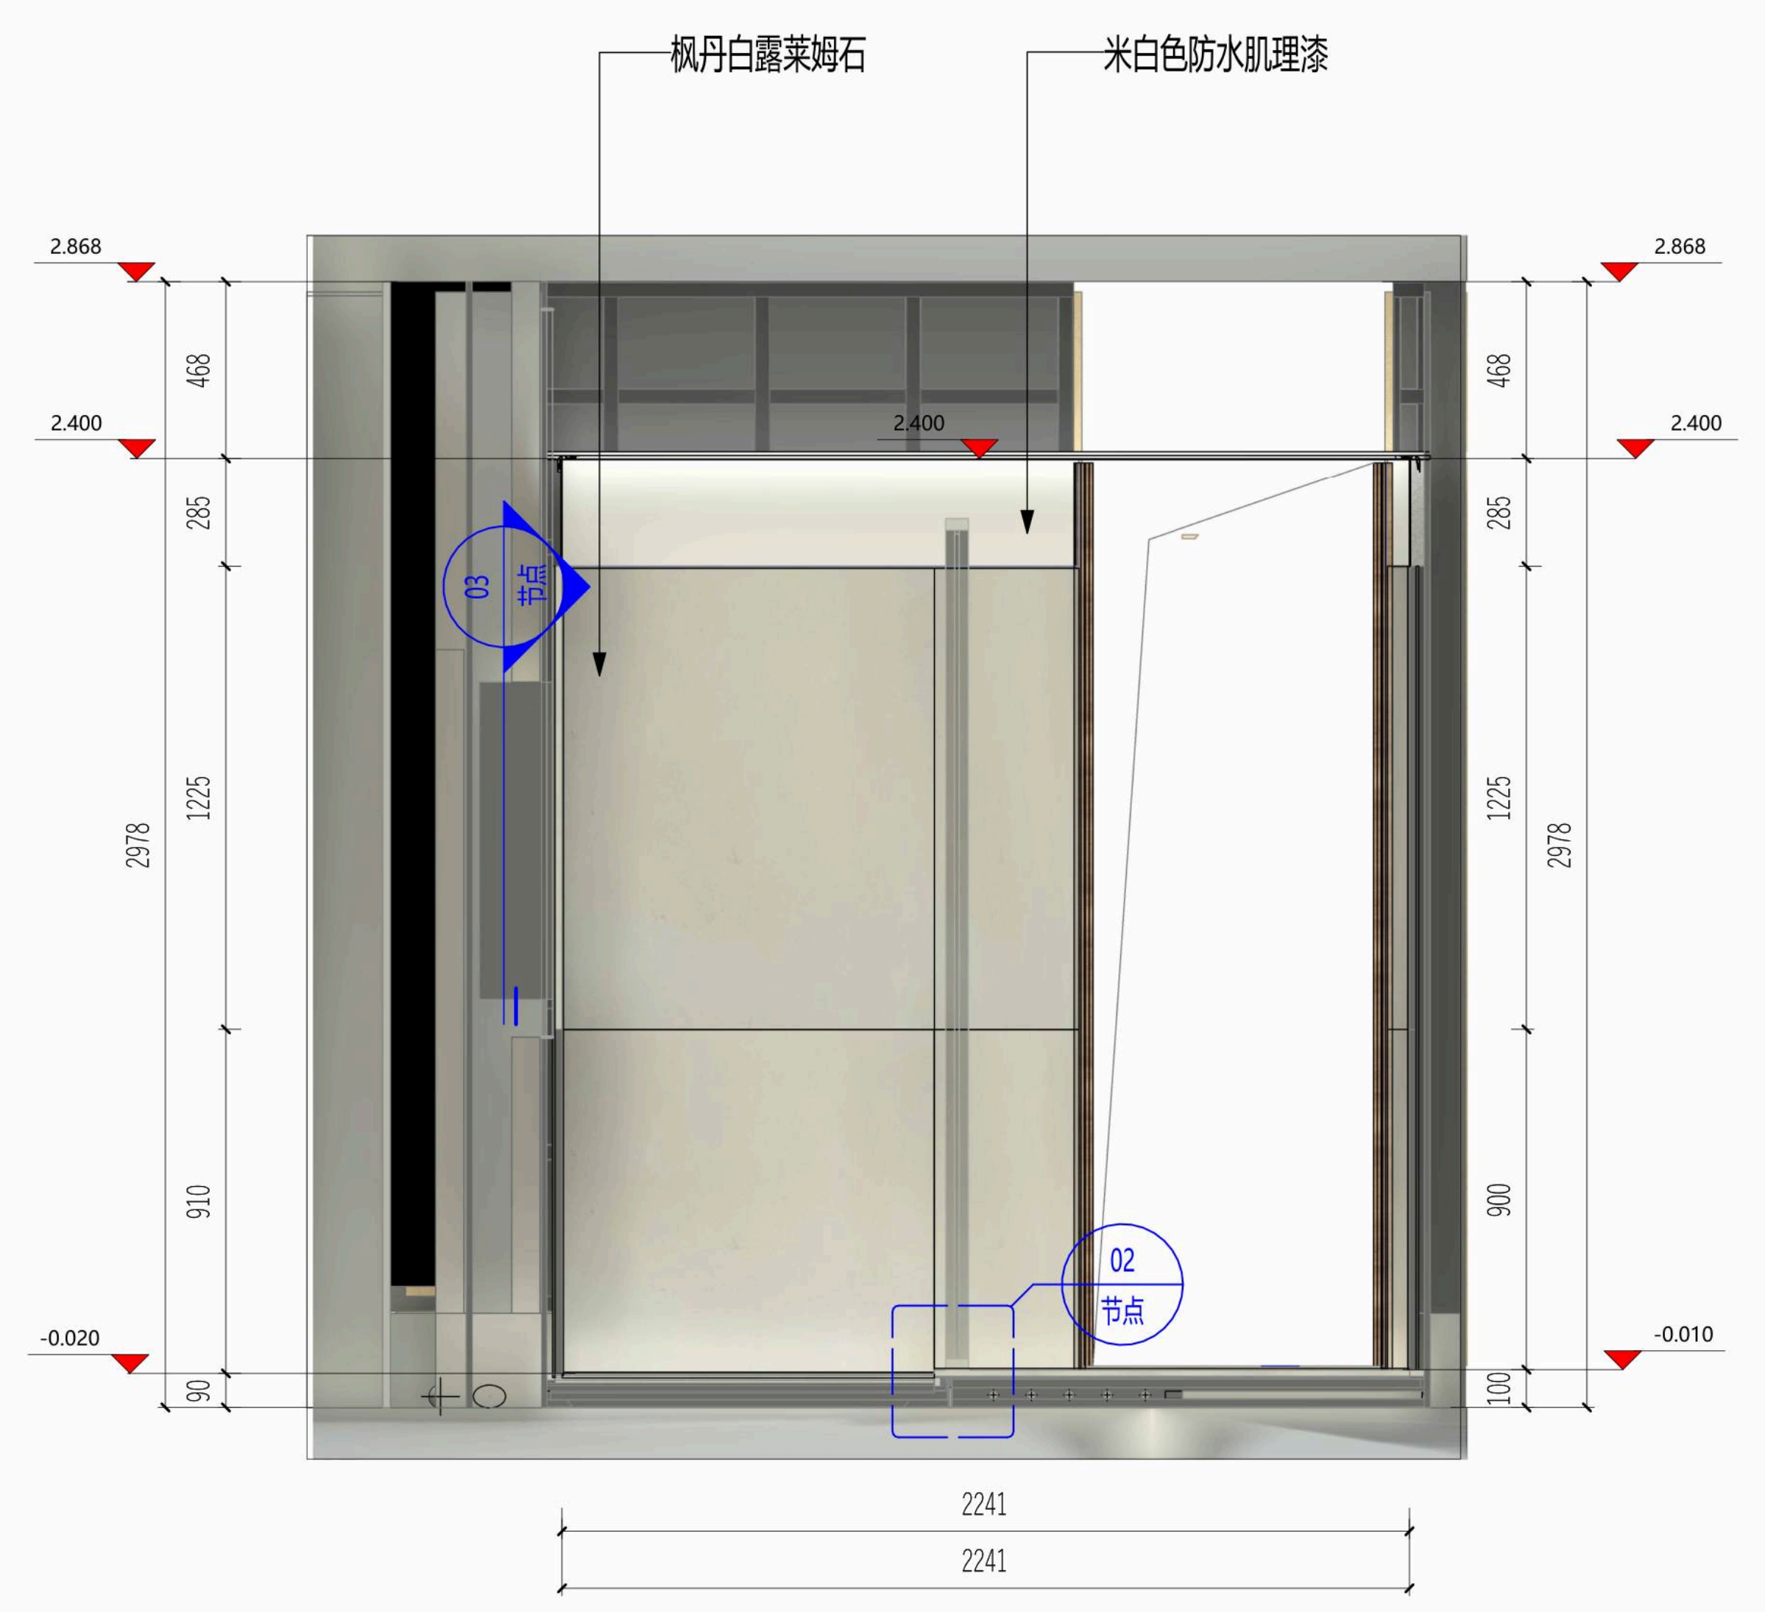
枫丹白露莱姆石
米白色防水肌理漆
2.868
2.400
-0.020
-0.010
468
285
1225
910
900
90
100
2978
03
节点
02
节点
2241
2241

客卫-03

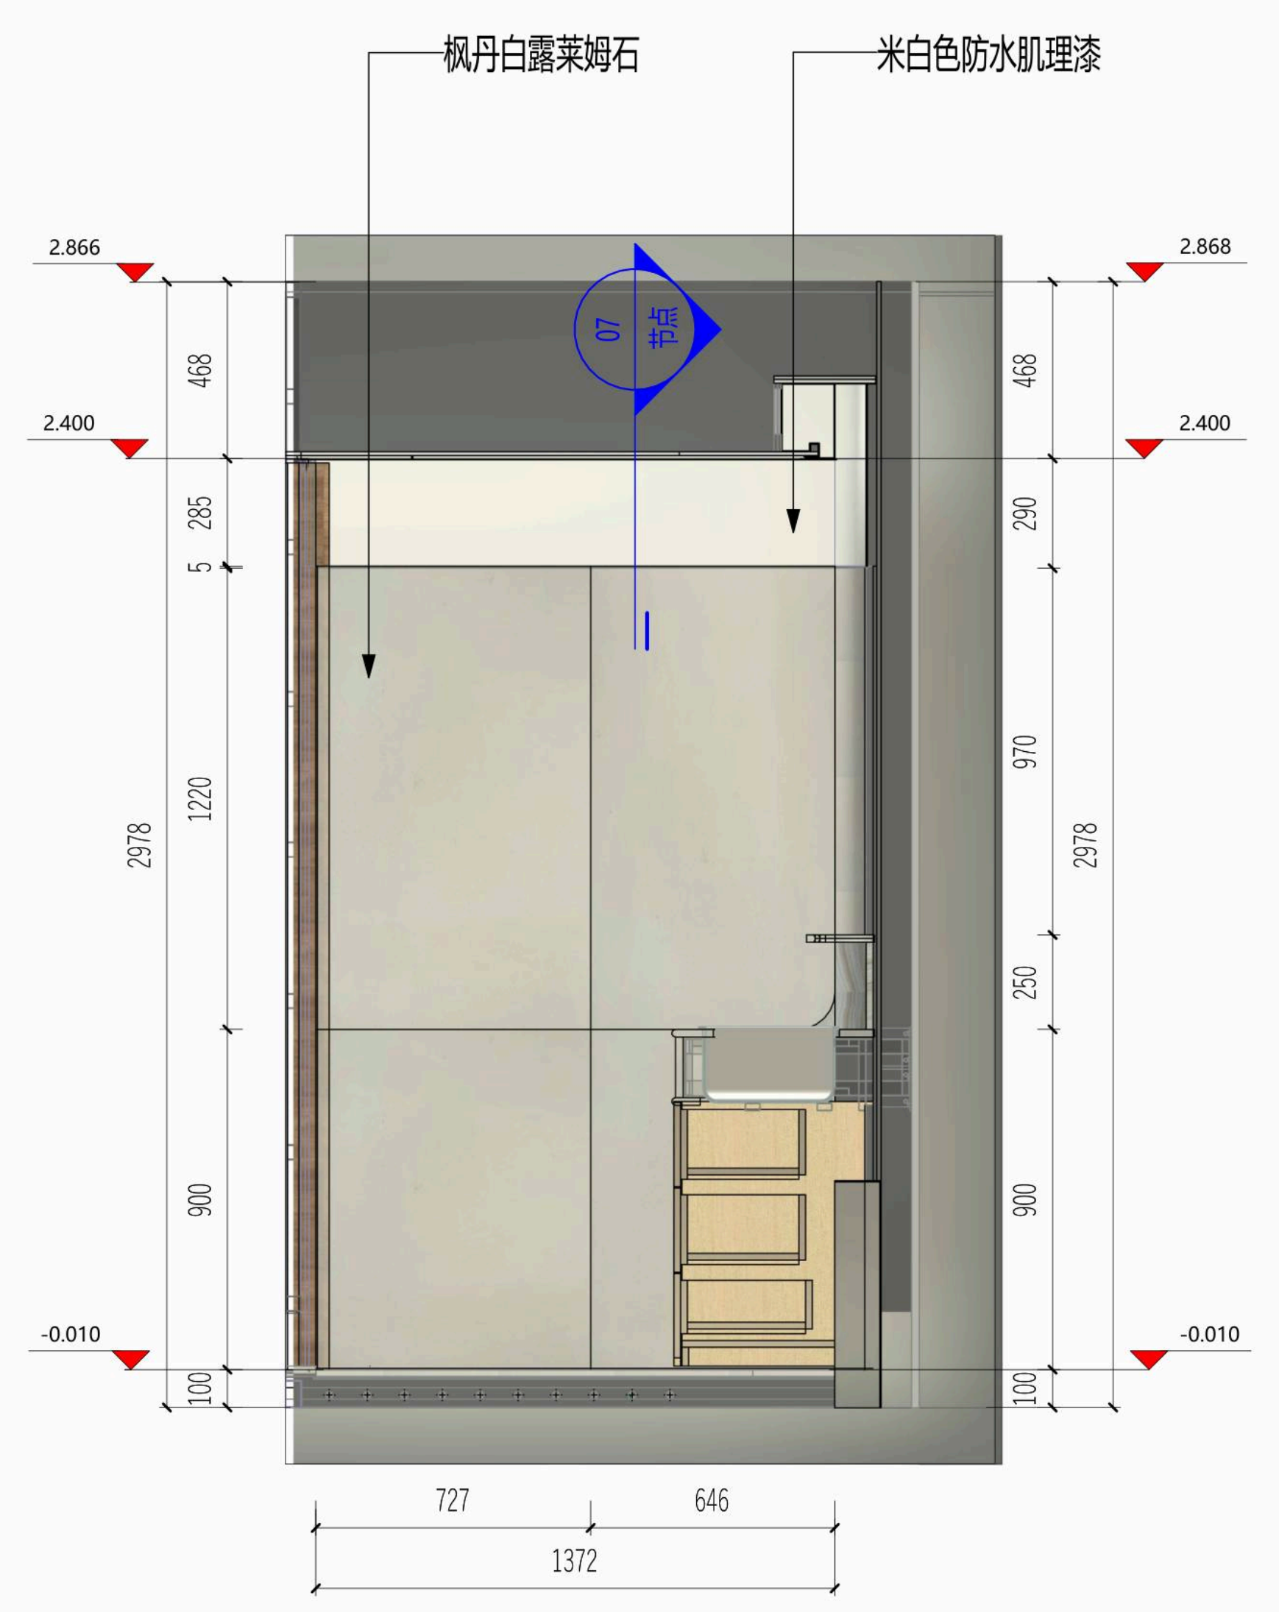
枫丹白露莱姆石
米白色防水肌理漆
2.866
2.868
2.400
-0.010
468
285
5
1220
900
100
2978
290
970
250
07
节点
727
646
1372

客卫-04

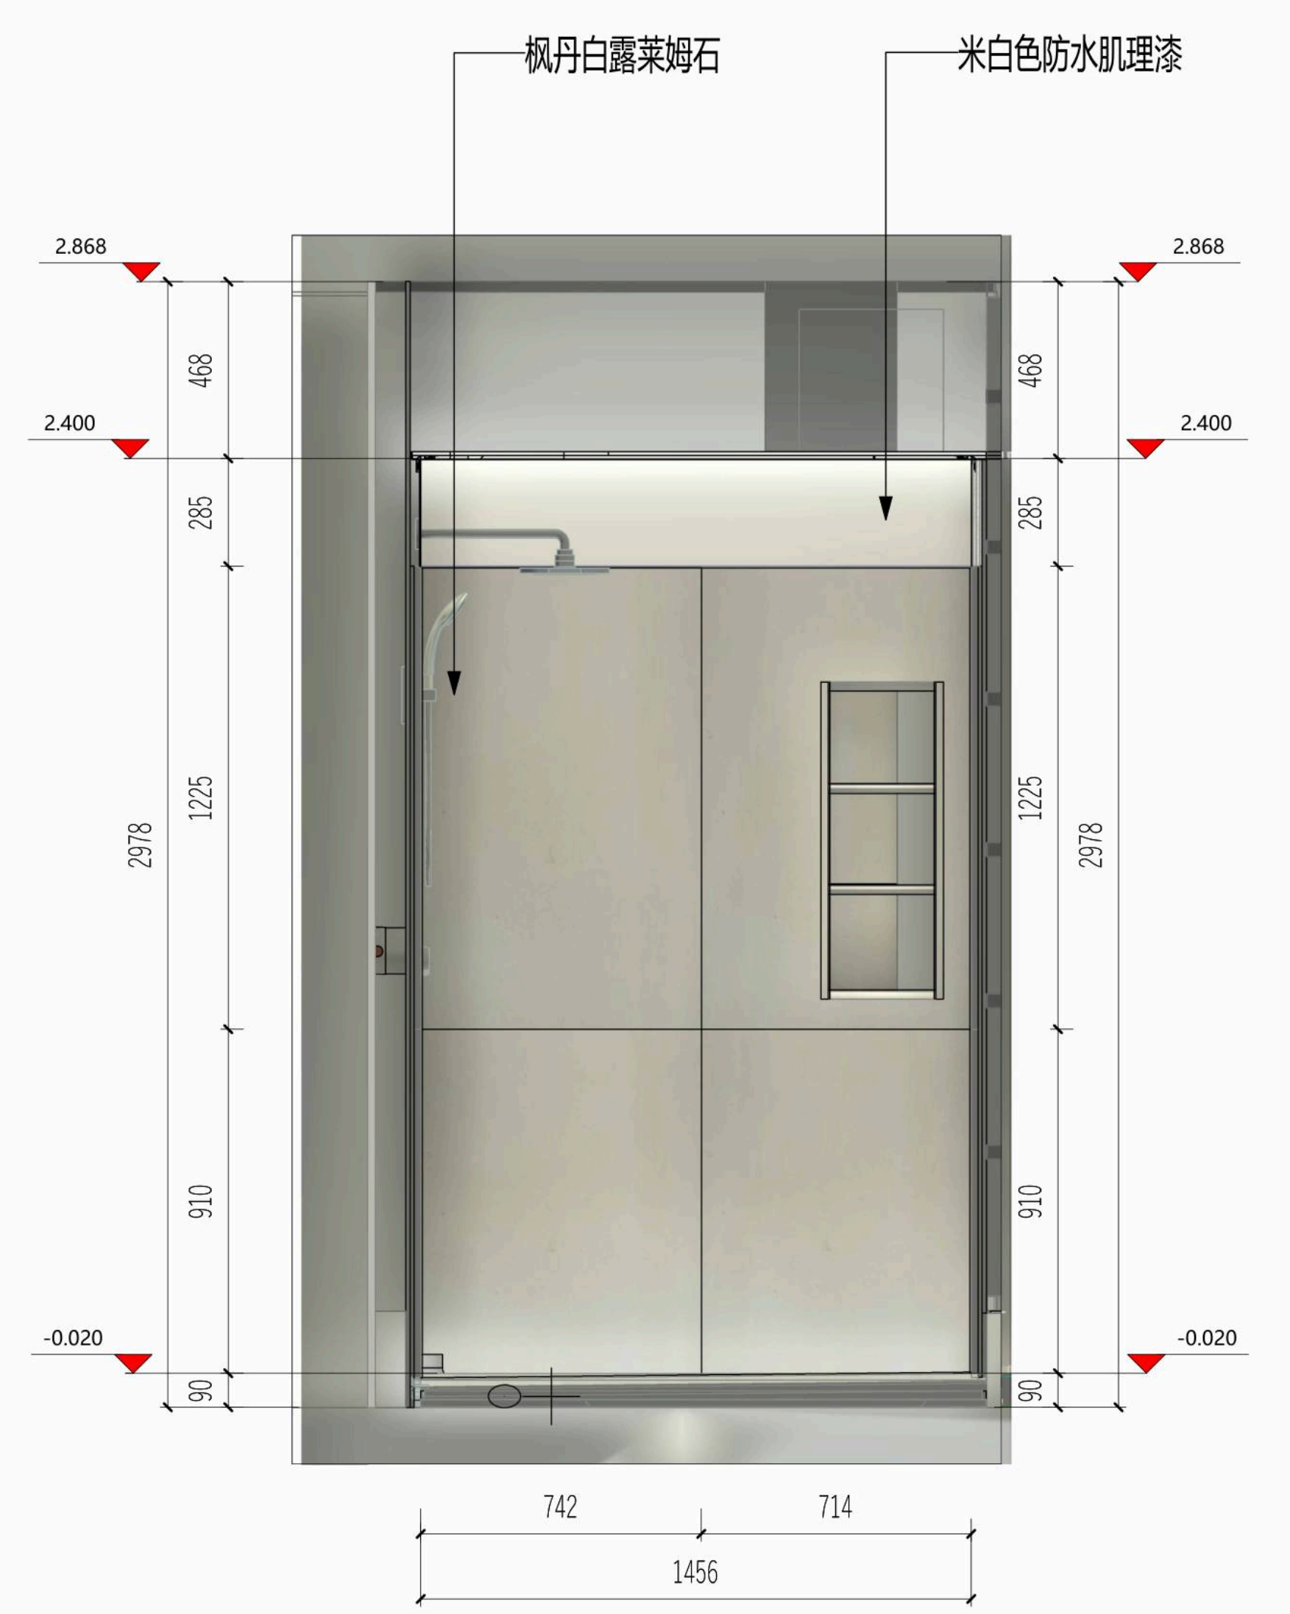
枫丹白露莱姆石
米白色防水肌理漆
2.868
2.400
-0.020
468
285
1225
910
90
2978
742
714
1456

客卫-05

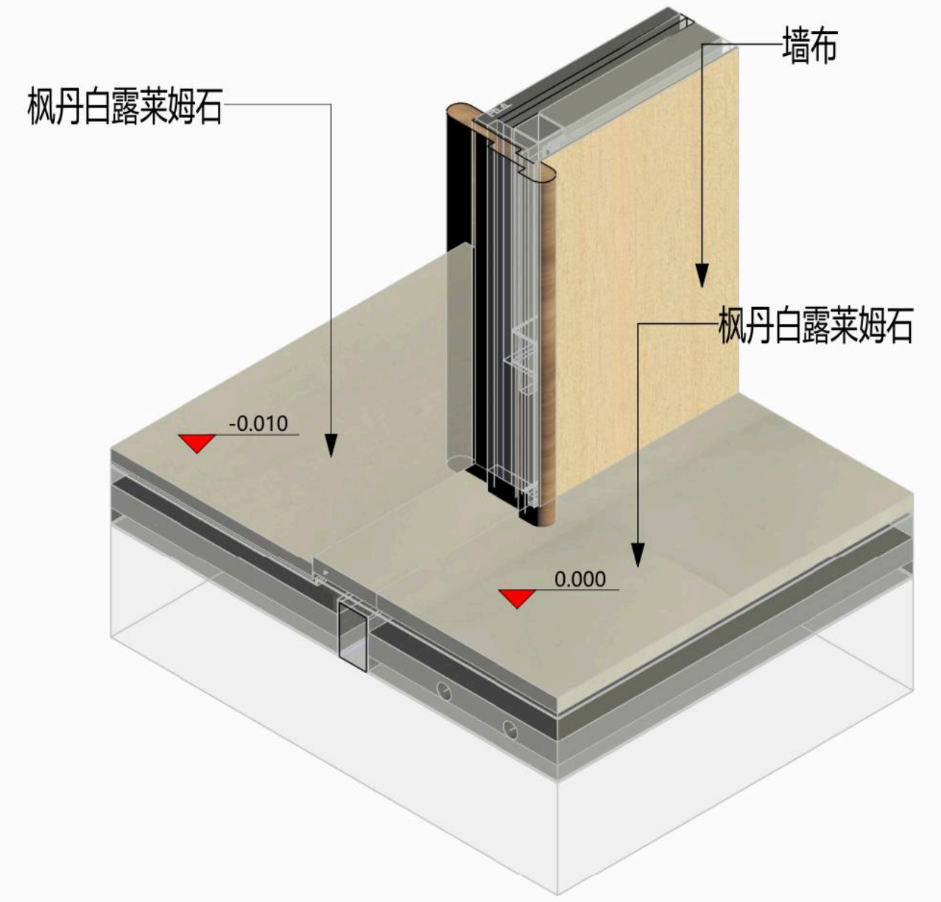
枫丹白露莱姆石
墙布
枫丹白露莱姆石
-0.010
0.000

节点-01

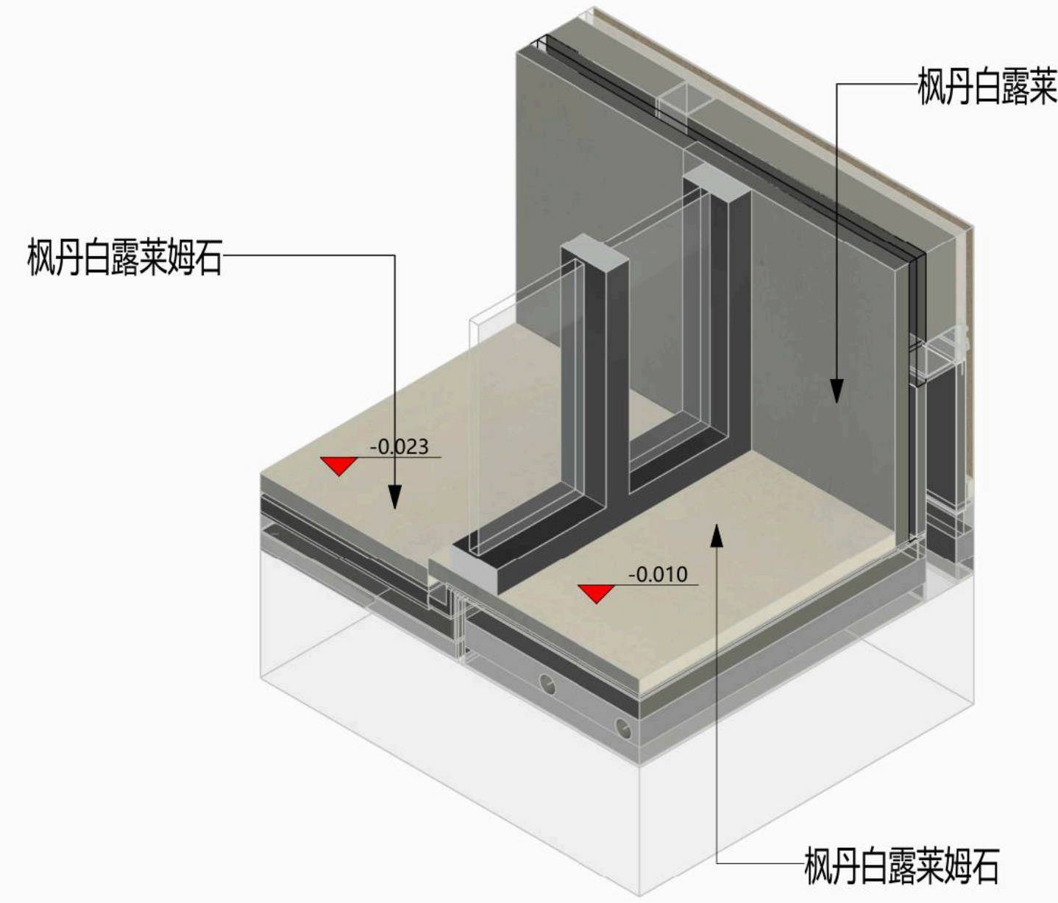
枫丹白露莱姆石
枫丹白露莱姆石
-0.023
-0.010
枫丹白露莱姆石

节点-02

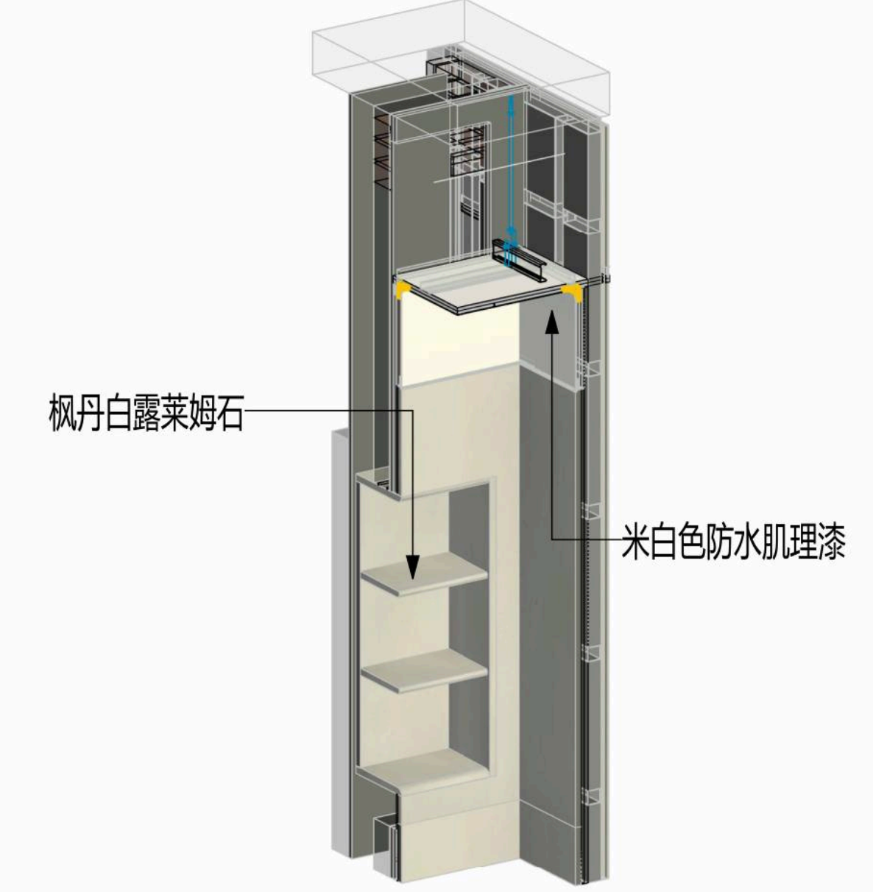
枫丹白露莱姆石
米白色防水肌理漆

节点-03

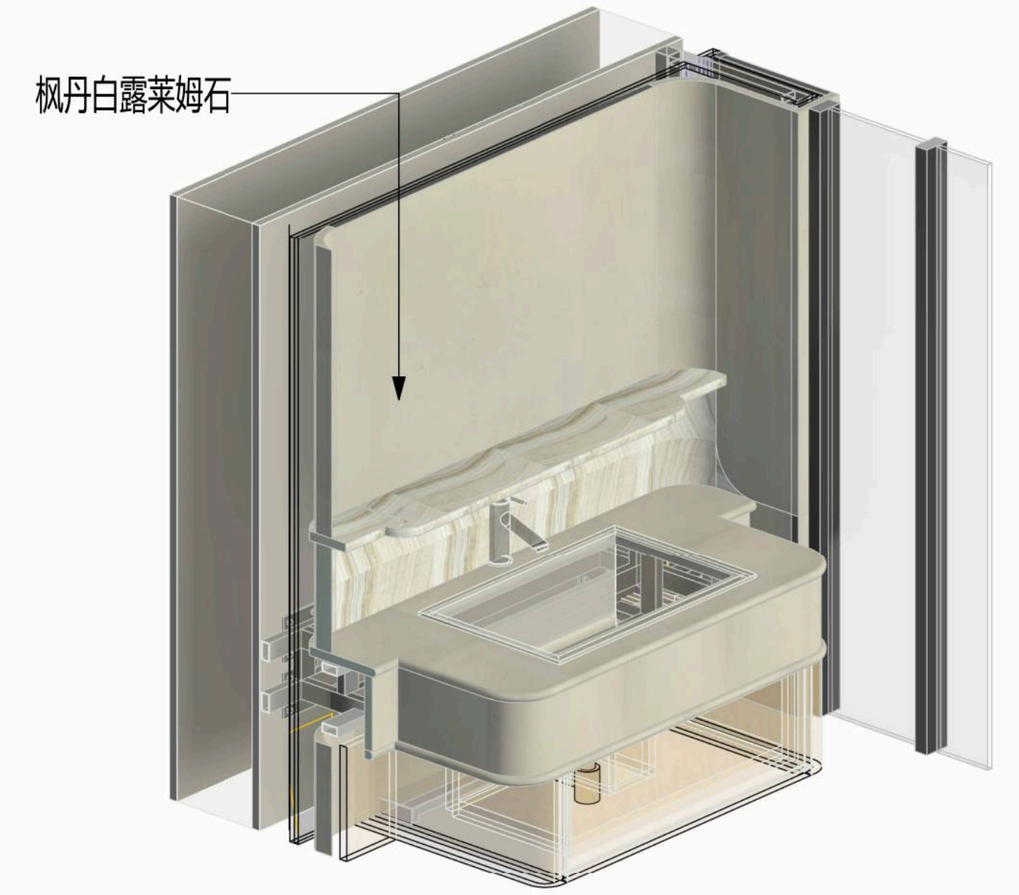

节点-04

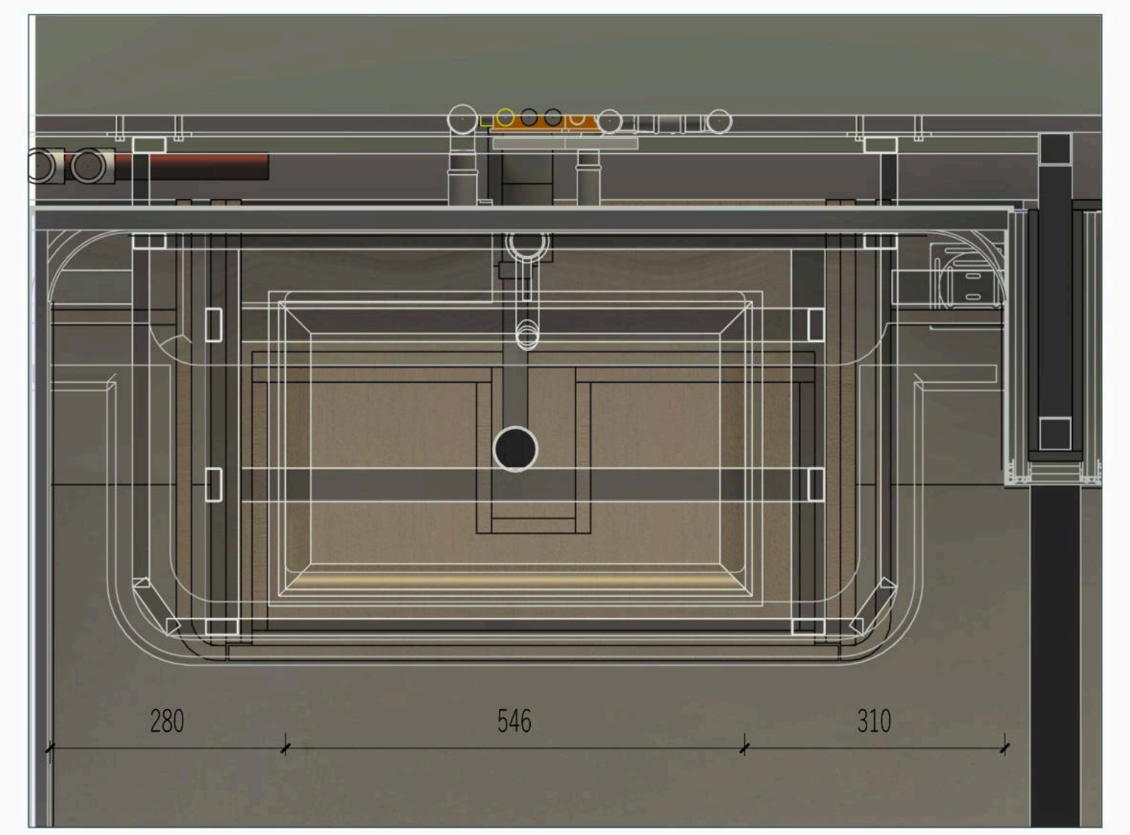

节点-05

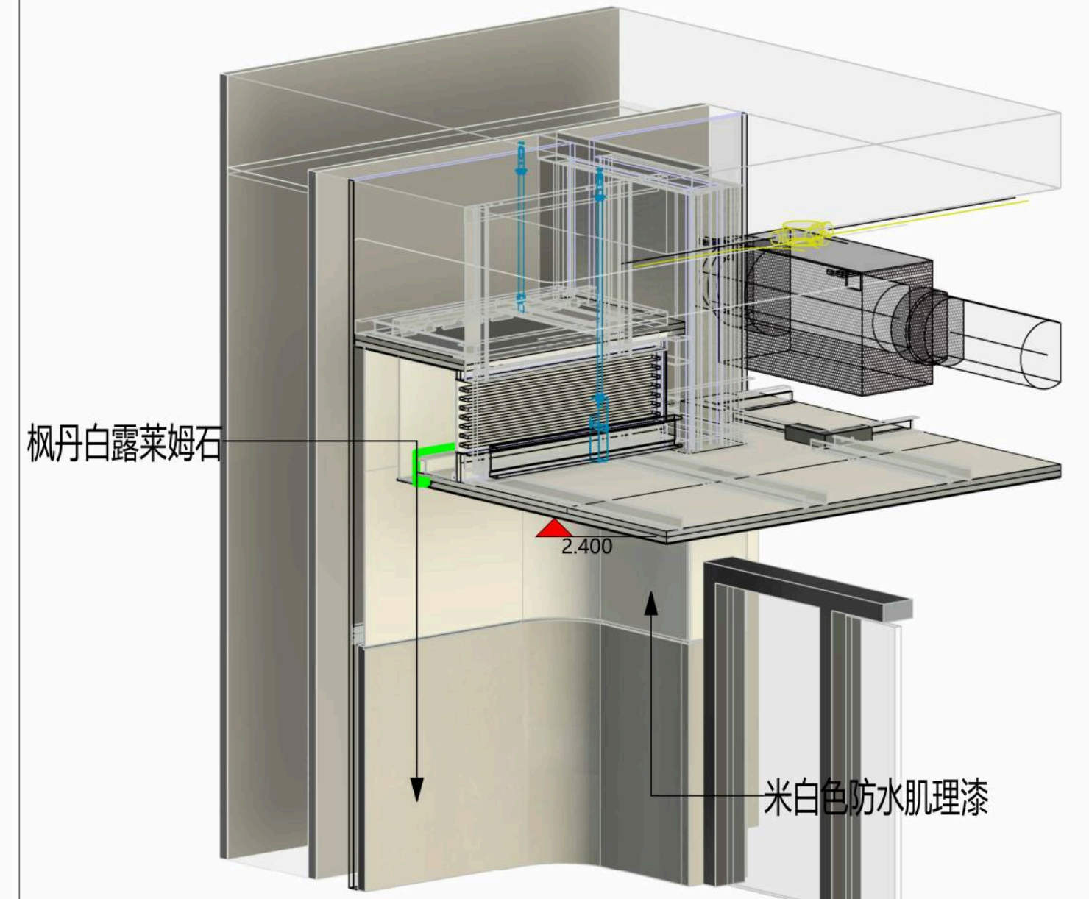
枫丹白露莱姆石
2.400
米白色防水肌理漆

节点-06

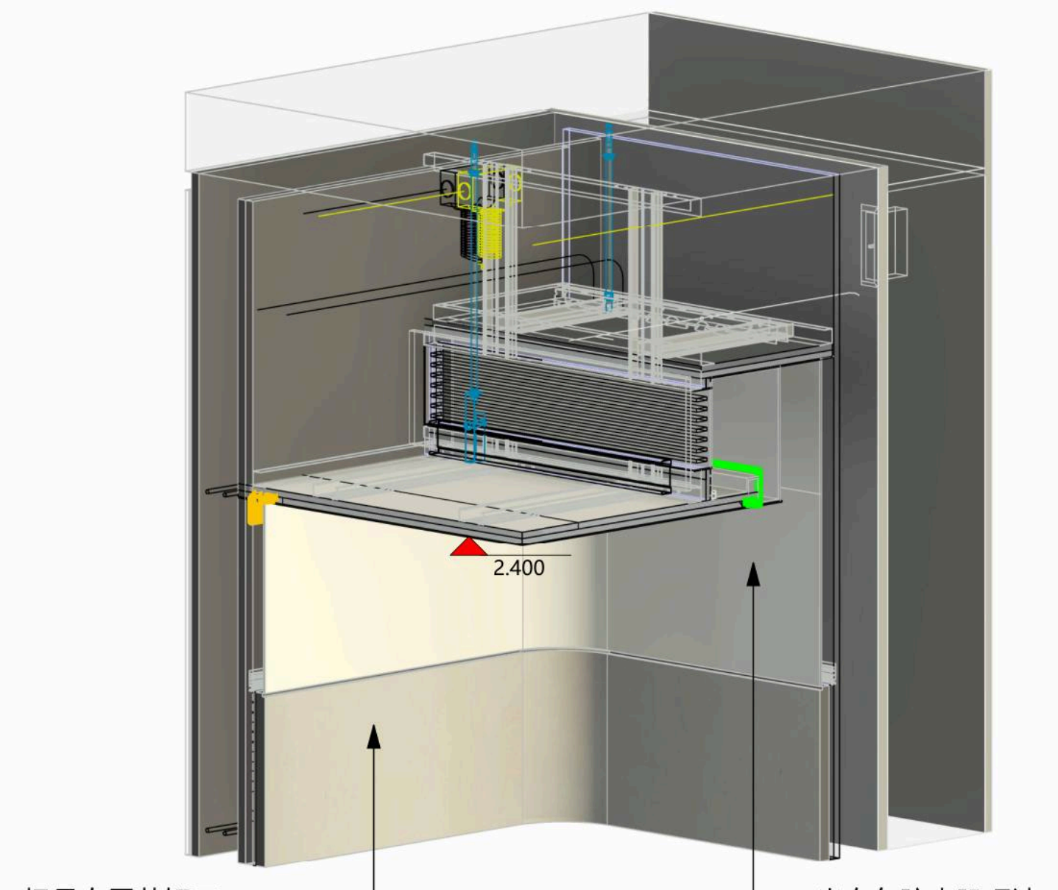
2.400
枫丹白露莱姆石
米白色防水肌理漆

节点-07

编号	图例	名称
1	▨	丹枫白露大理石
2	▨	直纹白玉大理石
3	▨	米白色防水肌理漆
4	▨	红色防水肌理漆
5	▨	米黄洞石大理石
6	▨	伊朗绿大理石
7	▨	黑白根大理石
8	▨	意大利木纹
9	▨	白木纹石
10	▨	塔维勒莱姆石
11	▨	木饰面
12	▨	木地板
13	▨	墙布

盖章

注释
Notes
1.本图纸如与现场尺寸有误，请施工人员与项目负责人联系。
2.施工前施工人员应认真查阅此图，如有不明确尺寸，按现场测量为准。
3.本图纸必须经甲乙双方认可并签字方可作为施工依据。

日期
Date 05/20/26

修订
Revision
1

项目
Project
潮映华岸府3-801

比例
Scale

客卫石材铺贴

图纸编号
Drawing No.
ST-14

项目编号
Project No.

©2025

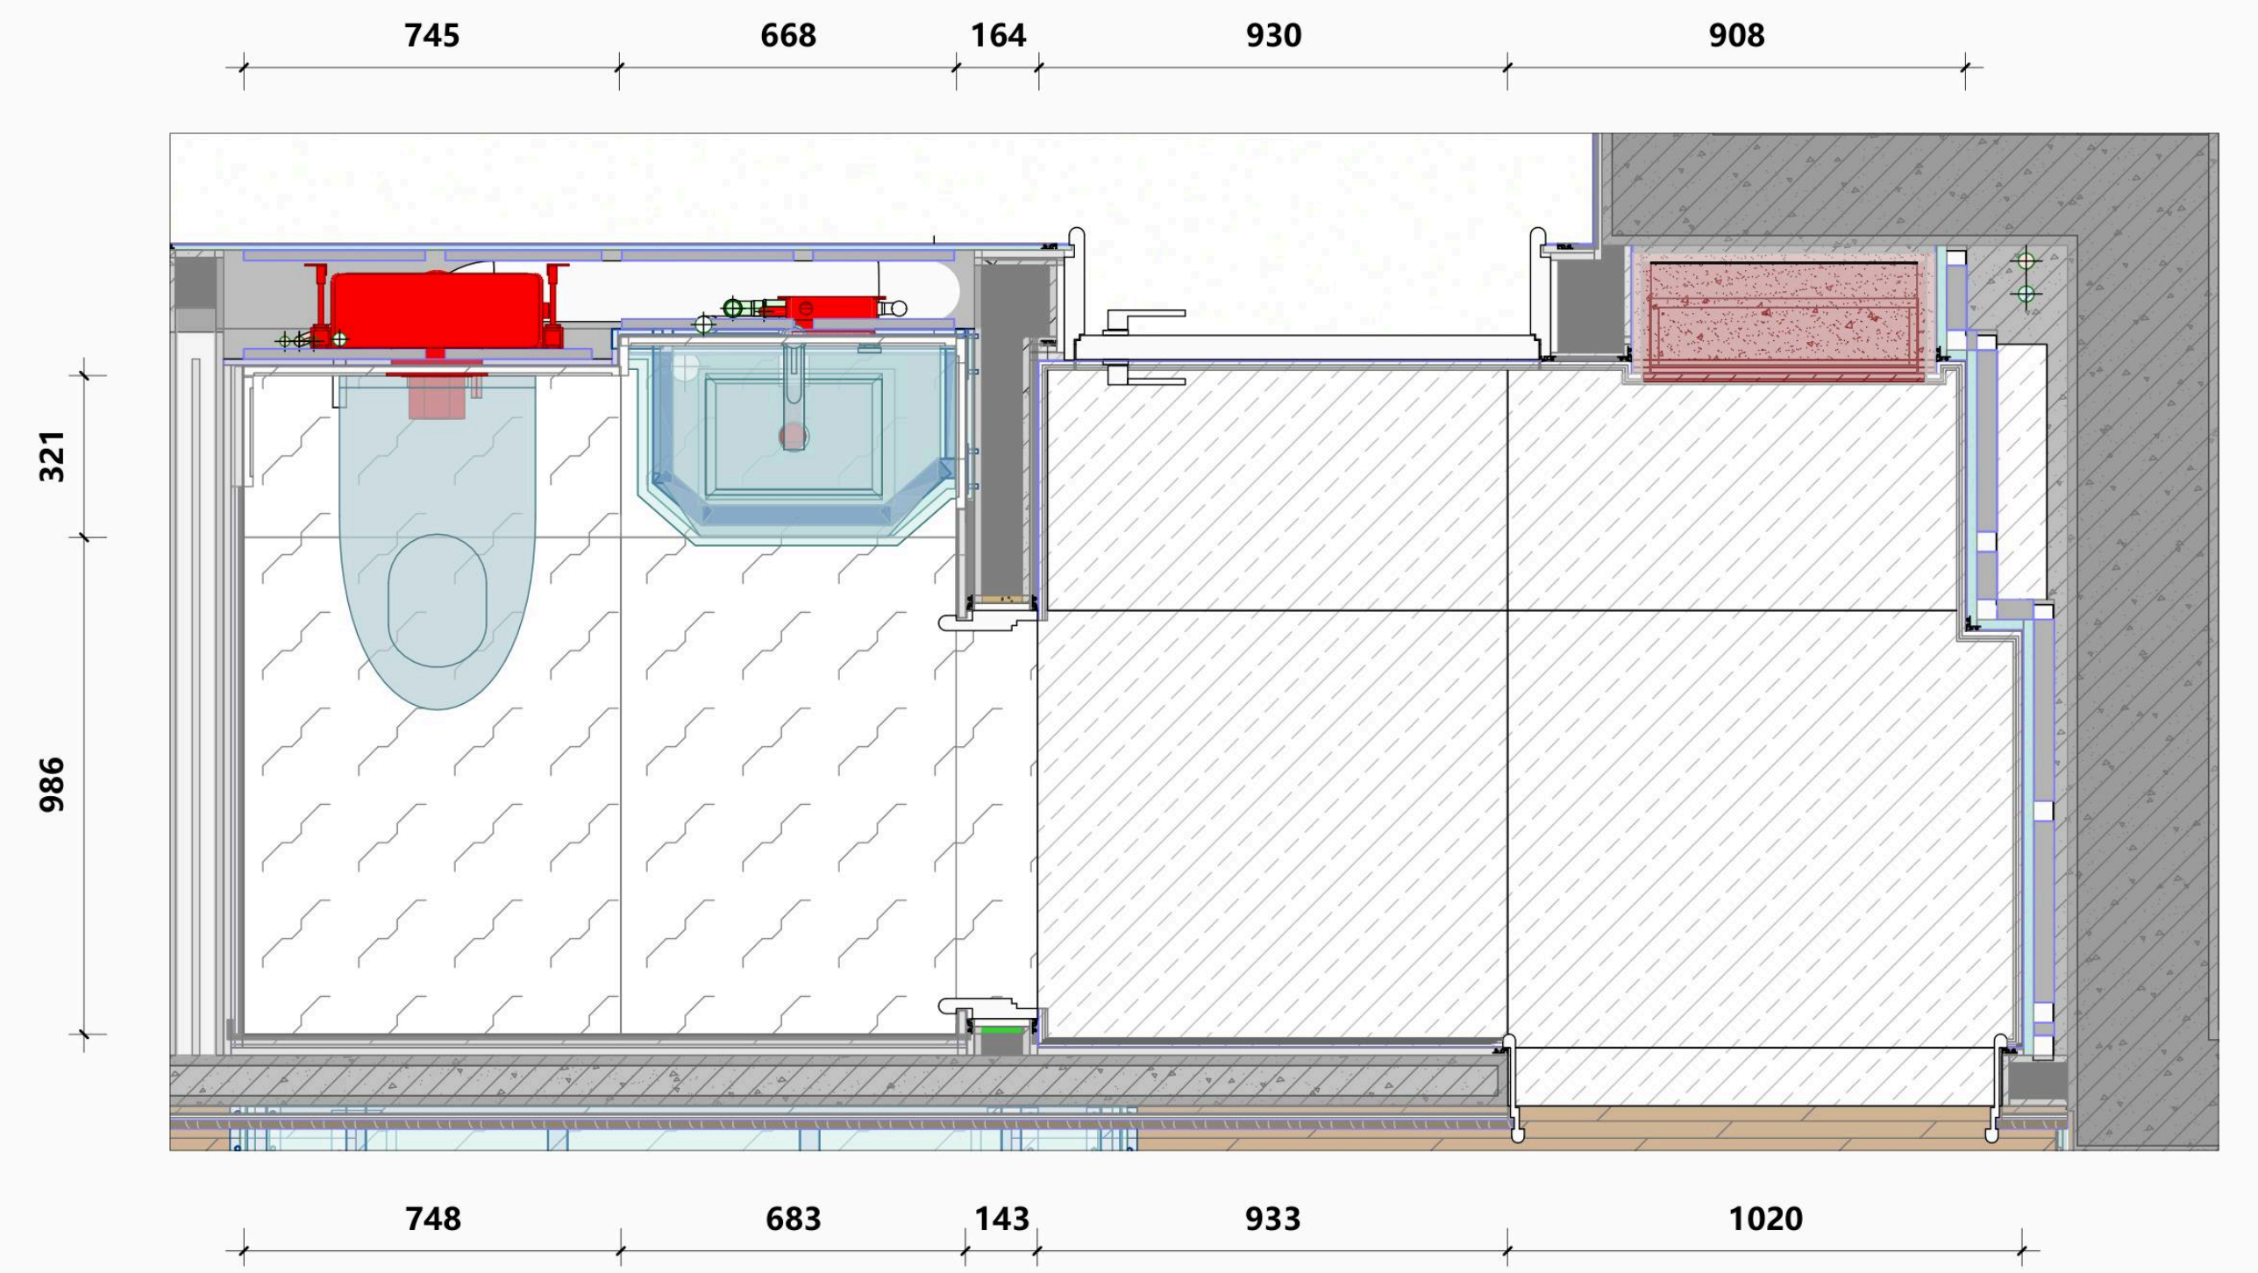
745
668
164
930
908
321
986
464
868
115
748
683
143
933
1020

地面铺贴图

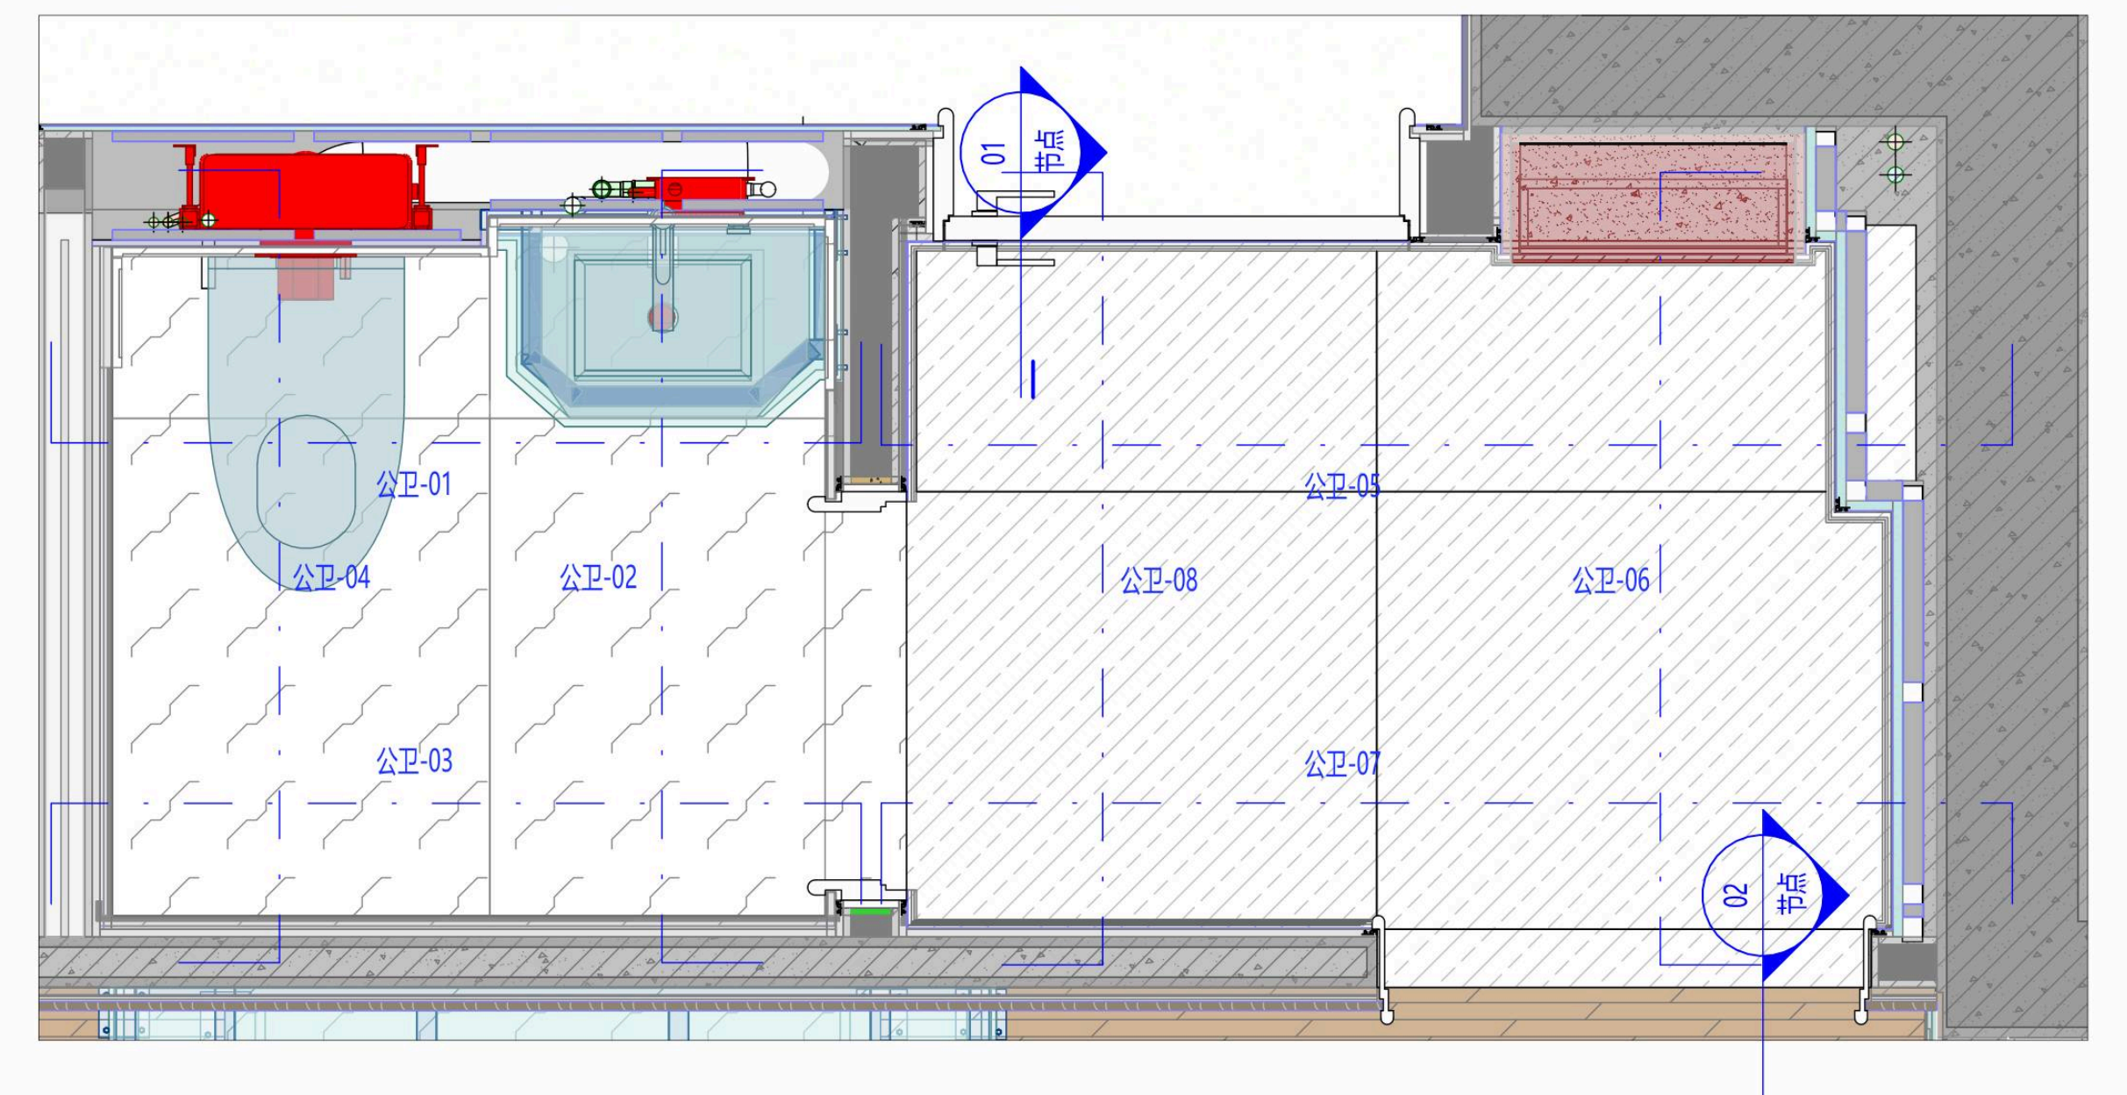
01 节点
02 节点
03 节点
04 节点
公卫-01
公卫-02
公卫-03
公卫-04
公卫-05
公卫-06
公卫-07
公卫-08

索引图

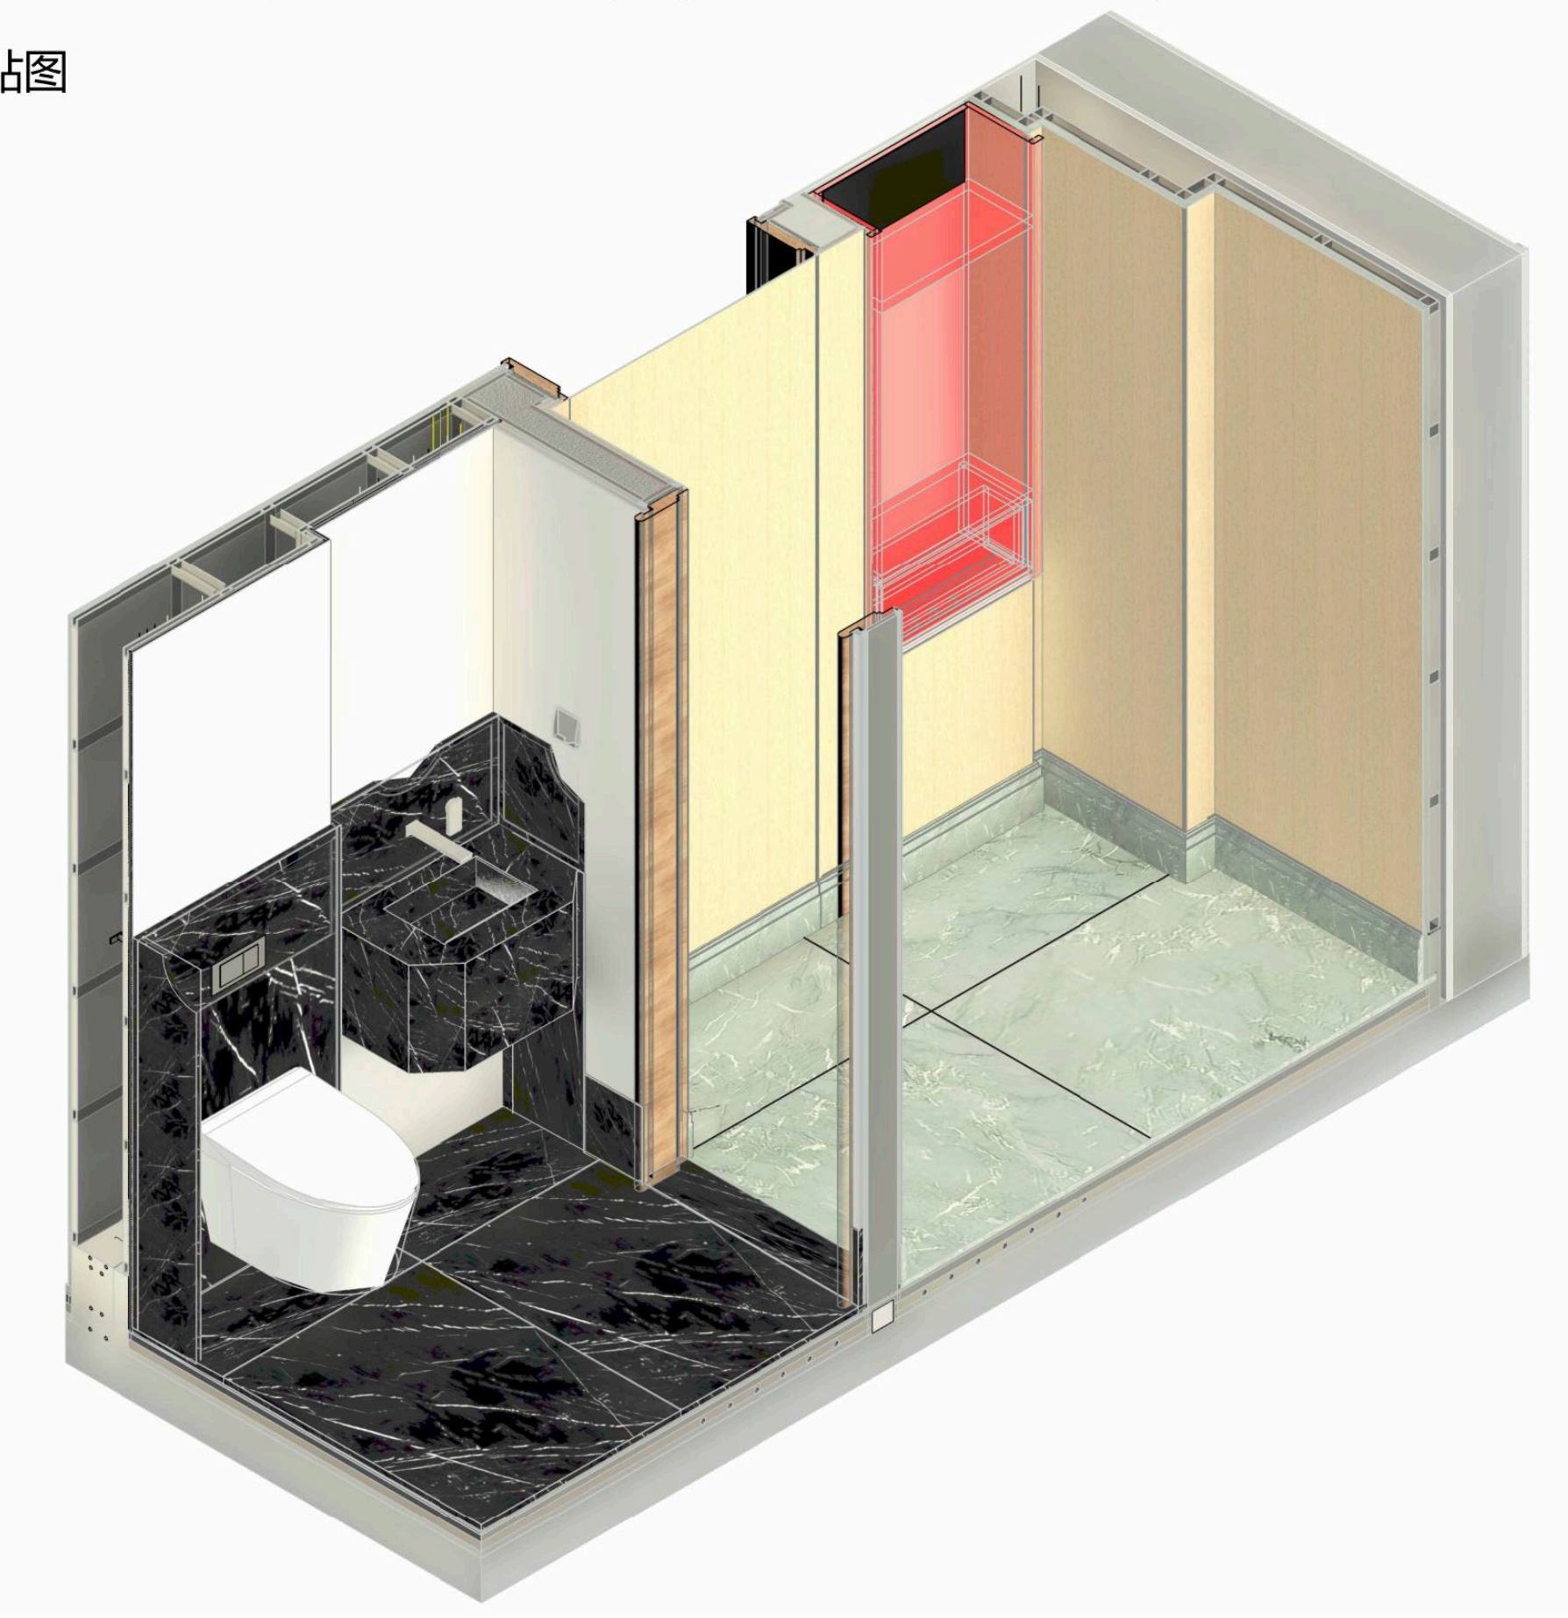

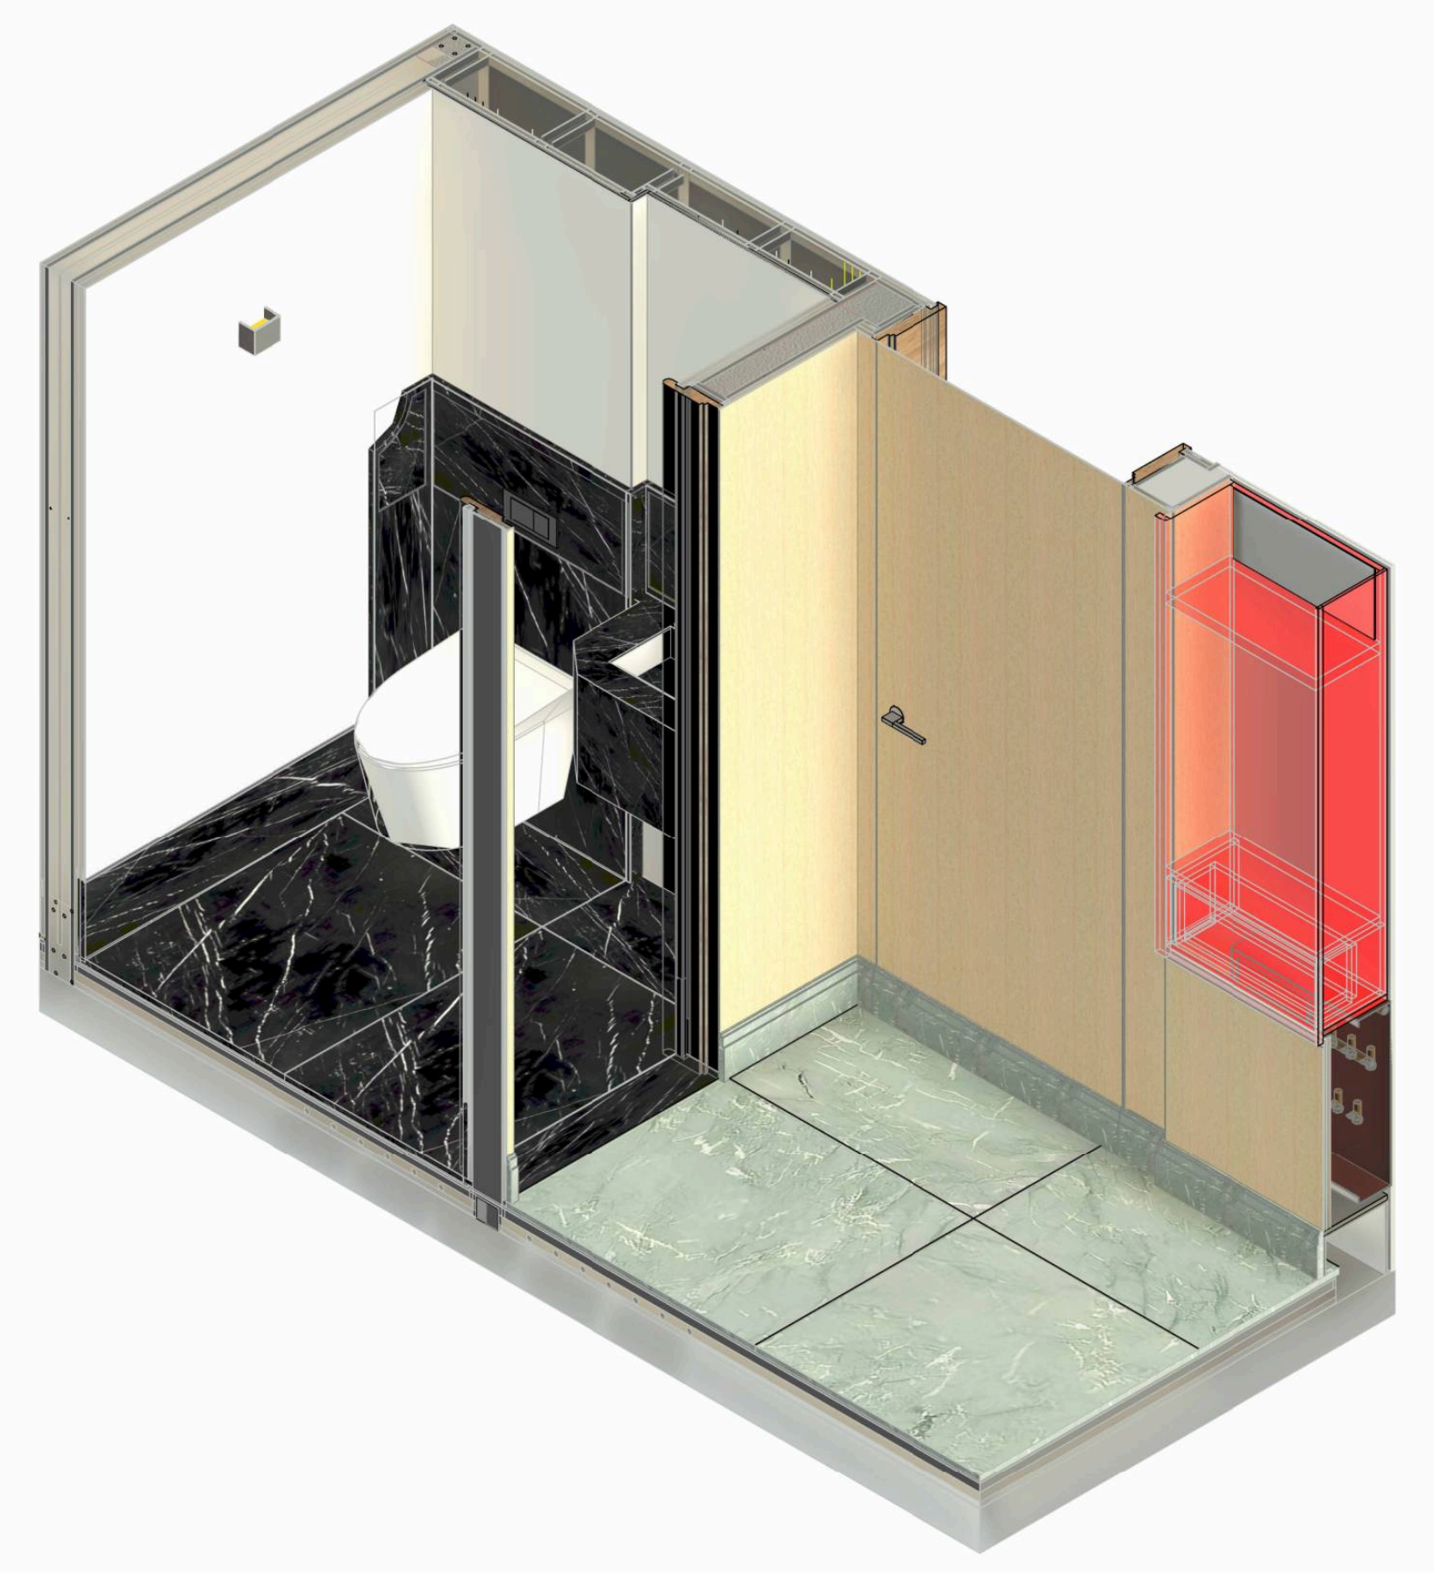

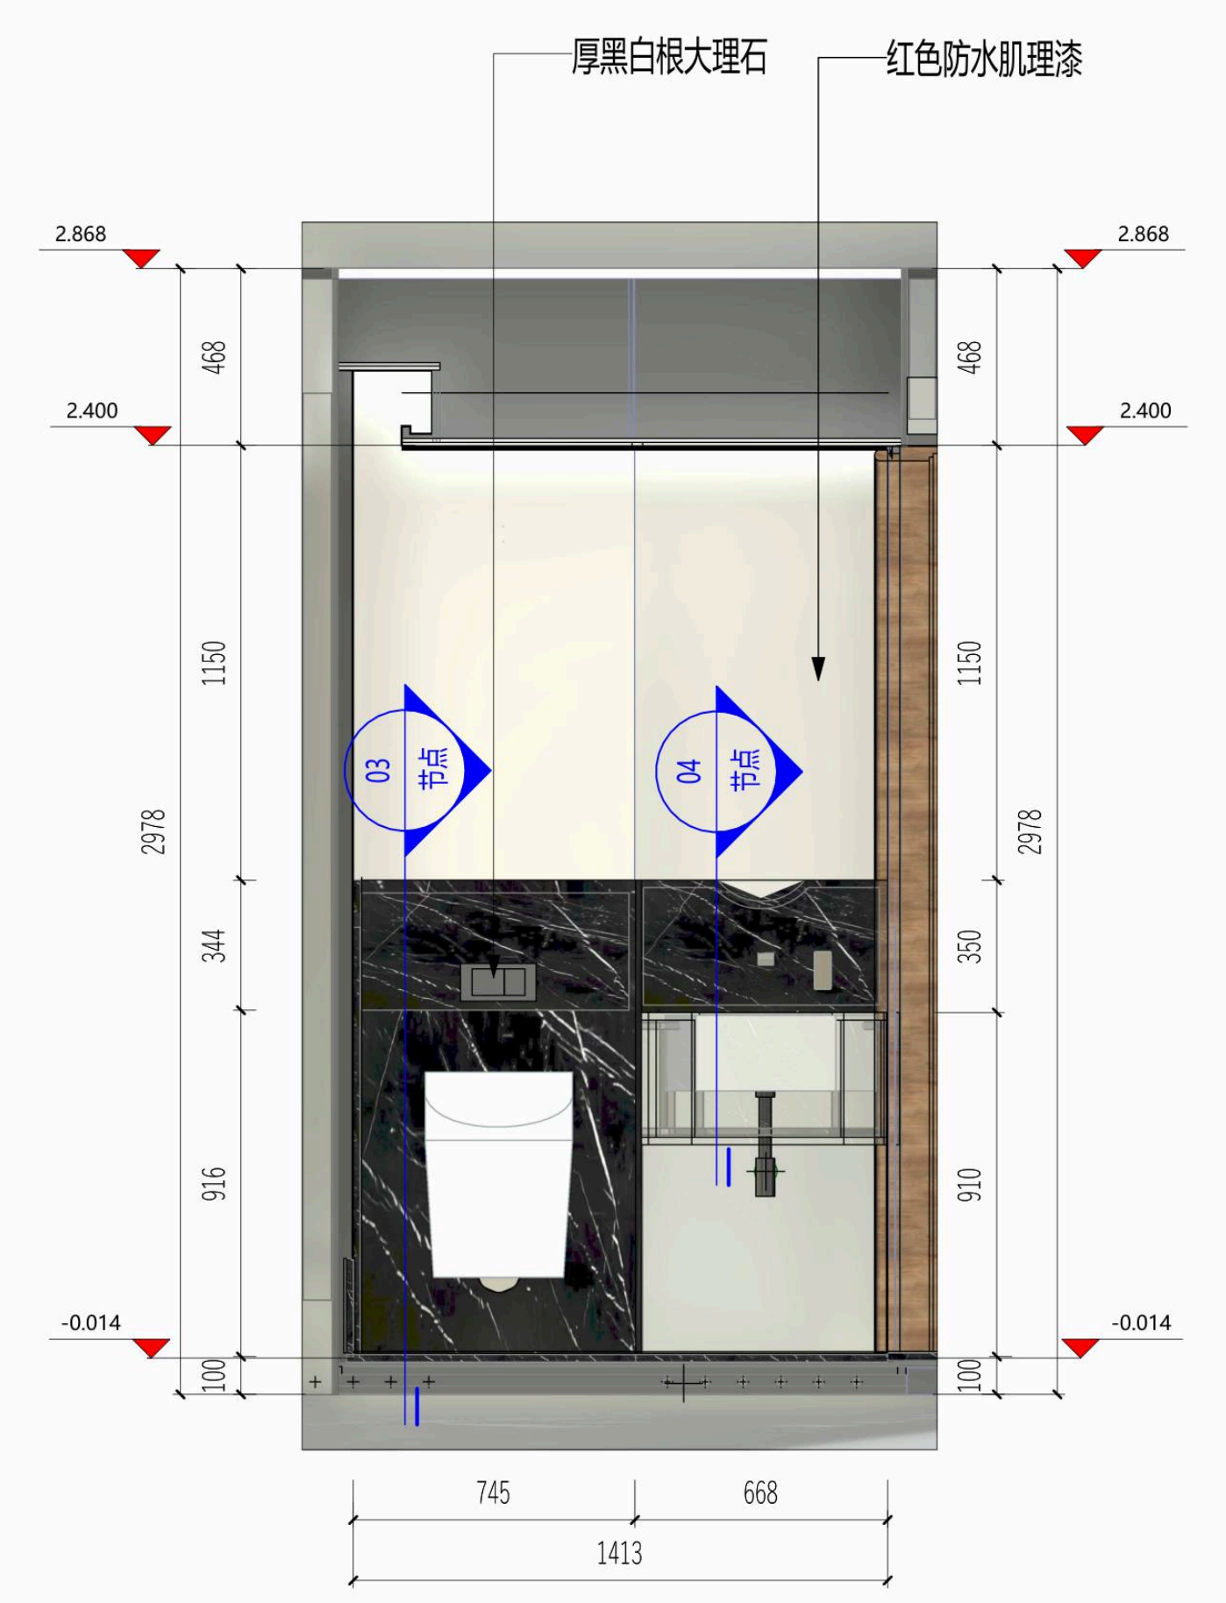
厚黑白根大理石
红色防水肌理漆
2.868
2.400
-0.014
468
1150
344
916
100
2978
350
910
03 节点
04 节点
745
668
1413

公卫-01

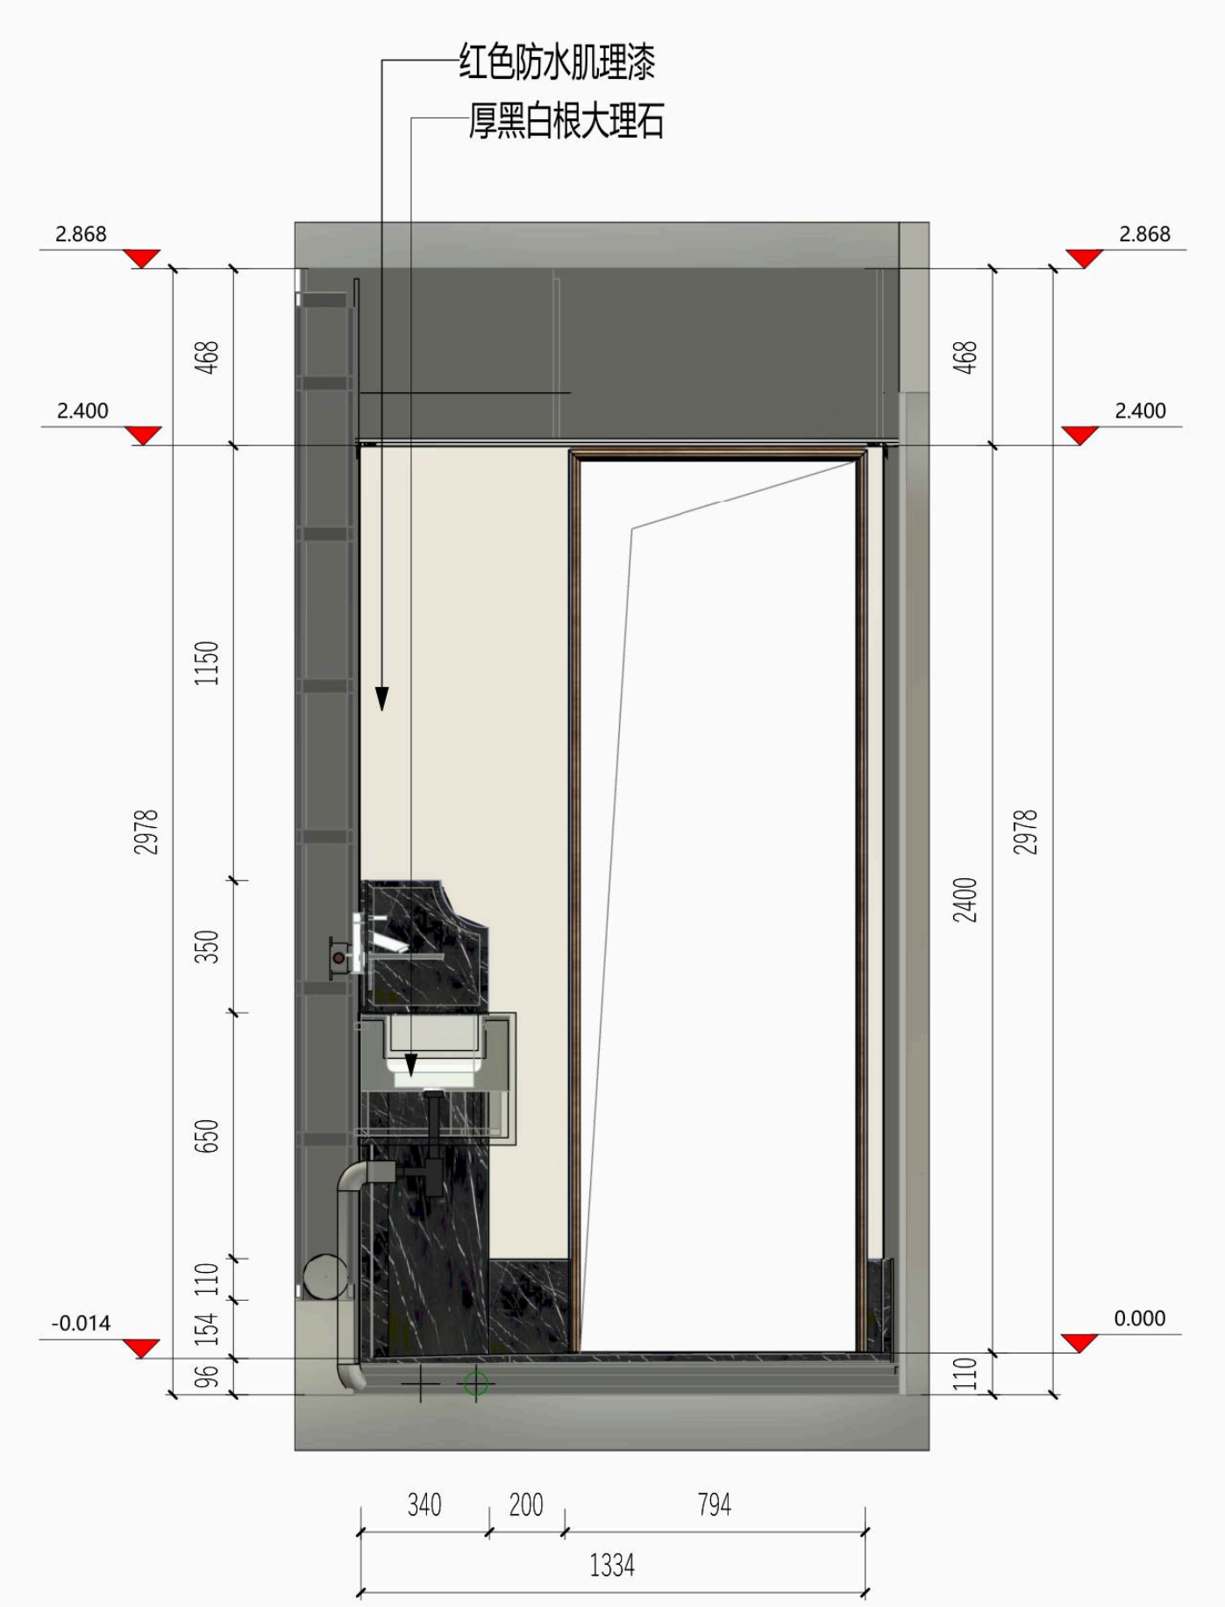
红色防水肌理漆
厚黑白根大理石
2.868
2.400
-0.014
0.000
468
1150
350
650
110
154
96
2978
2400
110
340
200
794
1334

公卫-02

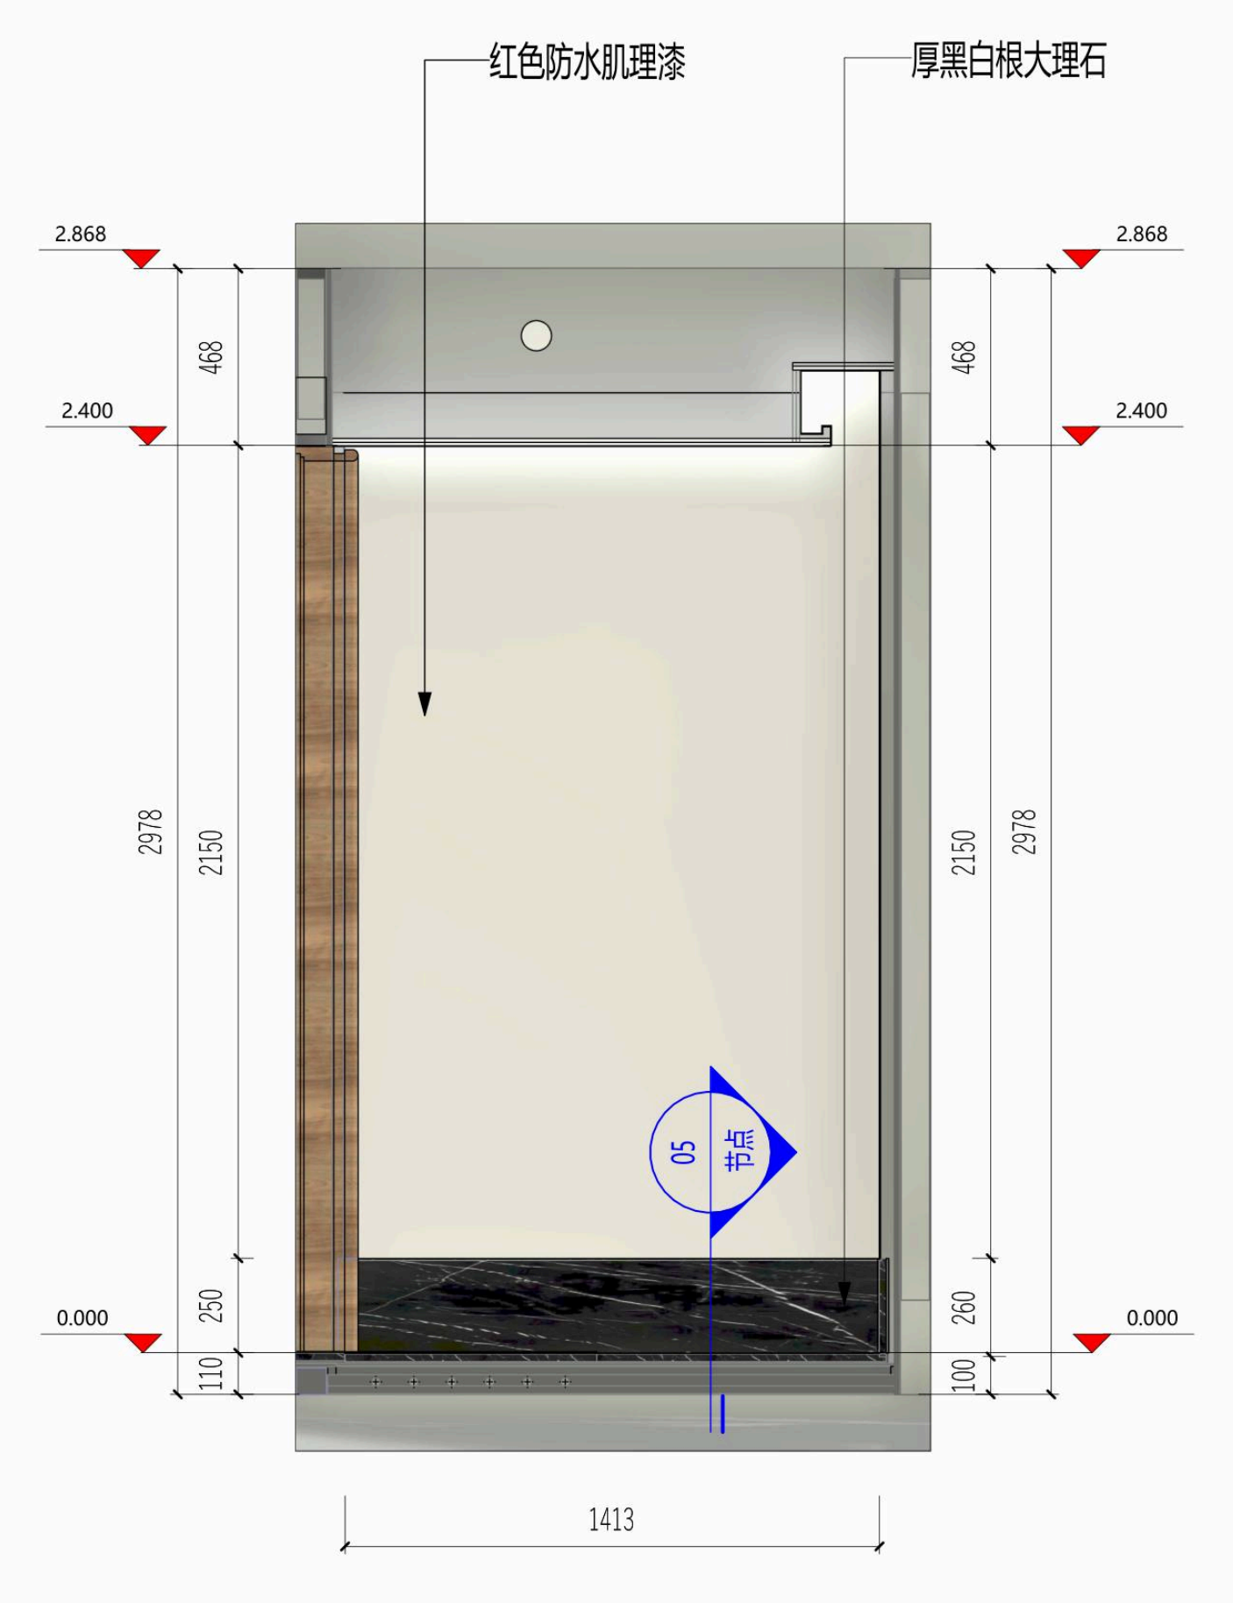
红色防水肌理漆
厚黑白根大理石
2.868
2.400
0.000
468
2150
250
110
2978
260
100
05 节点
1413

公卫-03

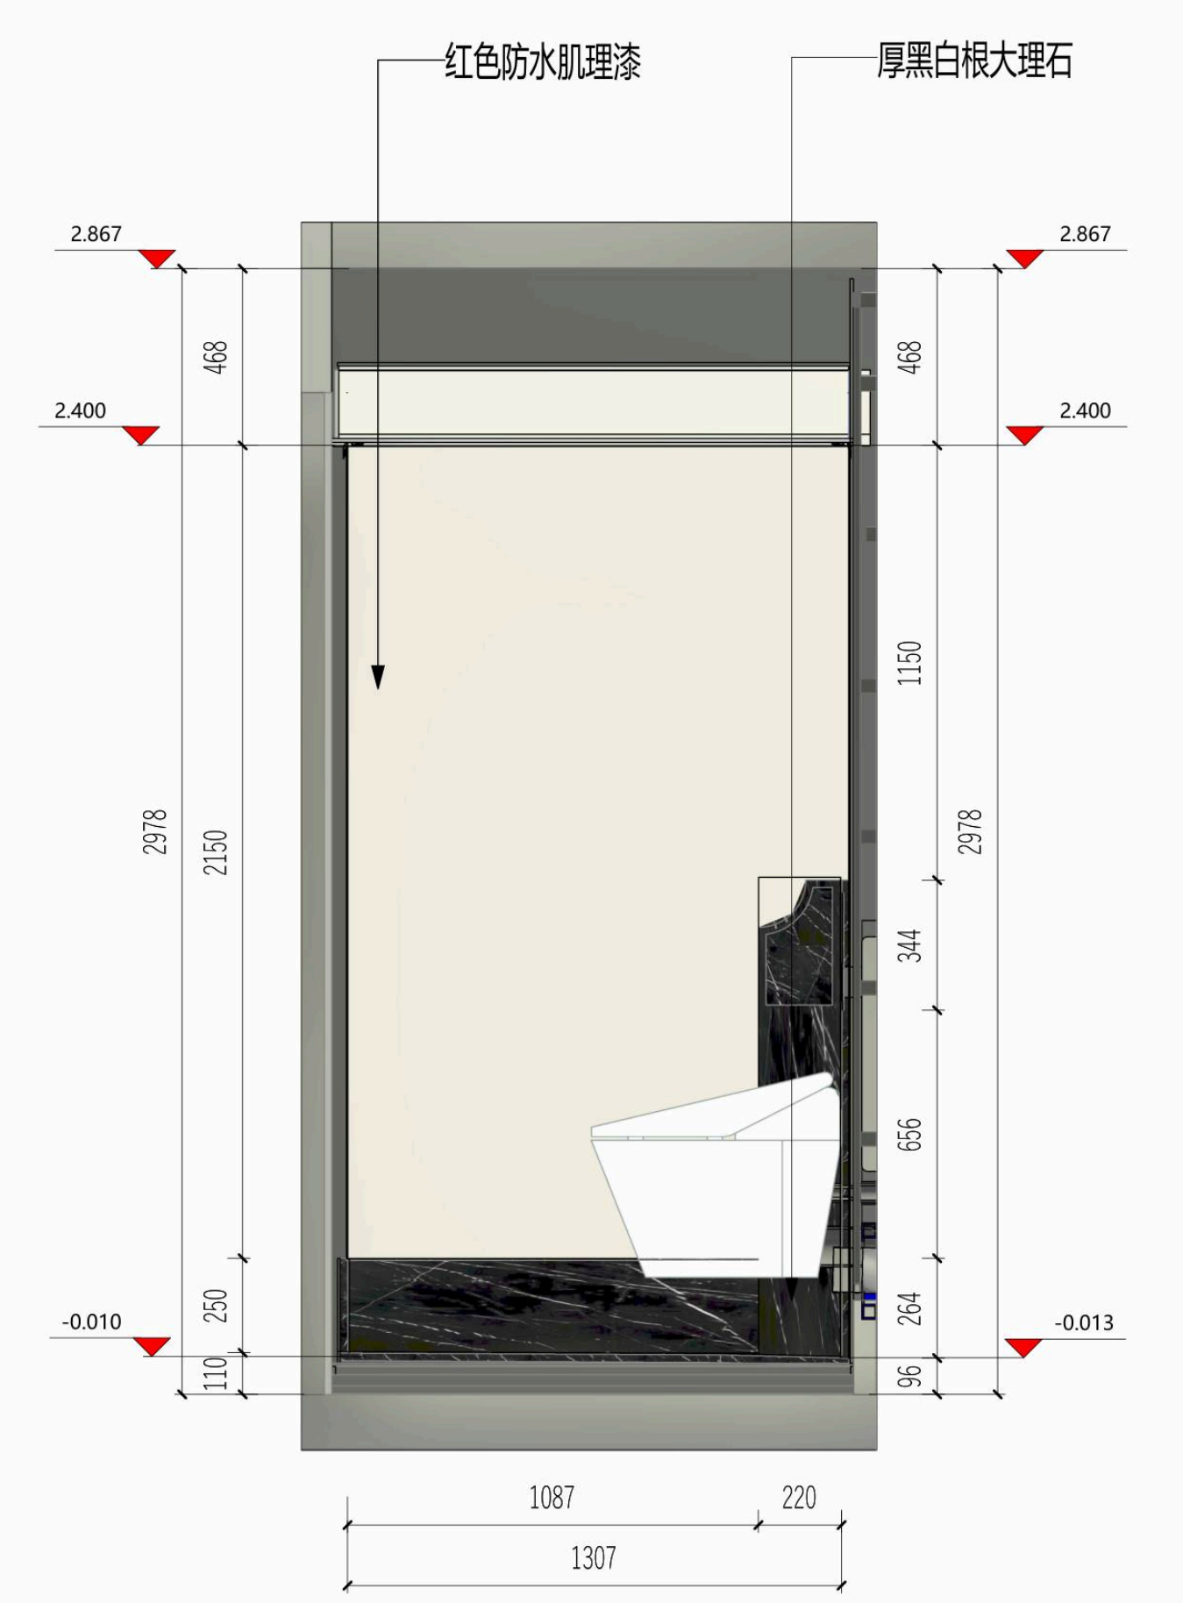
红色防水肌理漆
厚黑白根大理石
2.867
2.400
-0.010
-0.013
468
2150
250
110
2978
1150
344
656
264
96
1087
220
1307

公卫-04

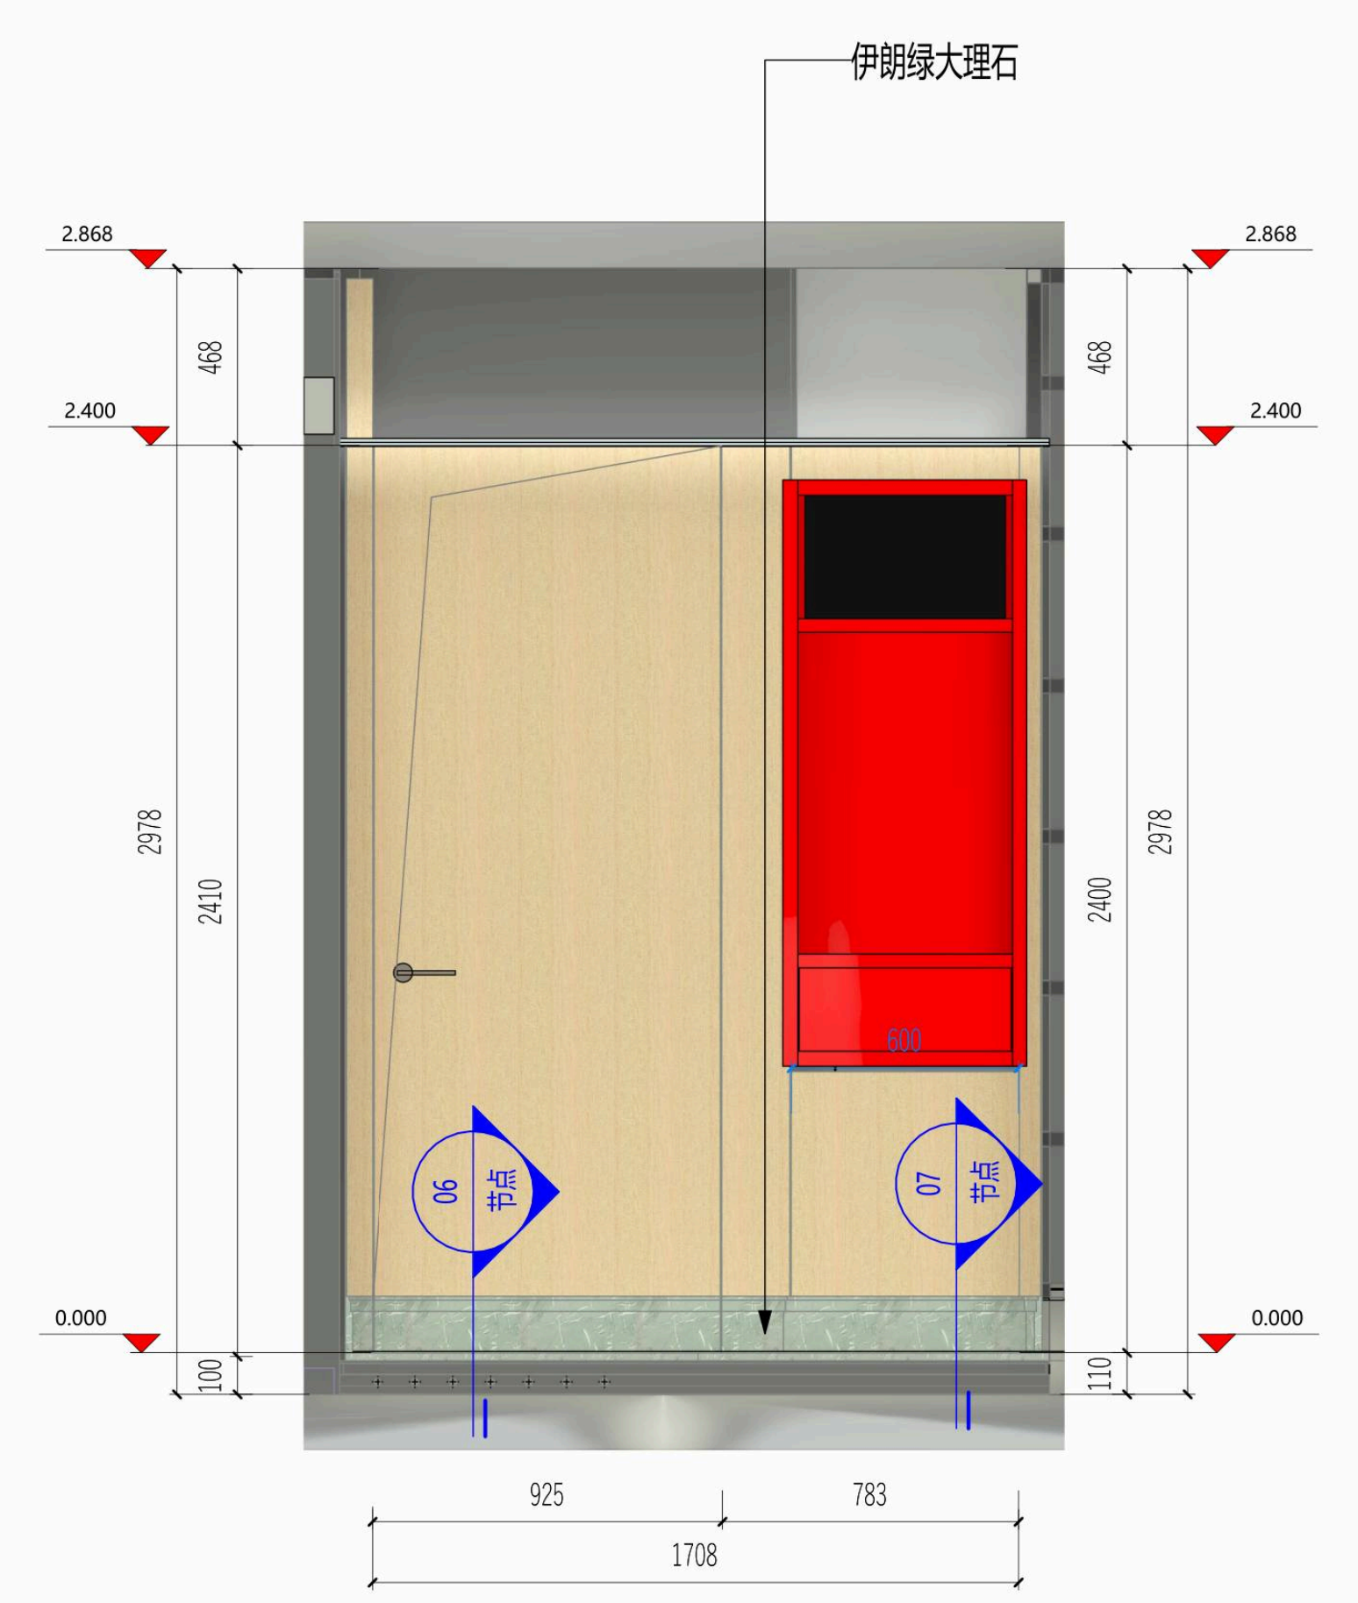
伊朗绿大理石
2.868
2.400
0.000
468
2410
100
2978
2400
110
06 节点
07 节点
925
783
1708

公卫-05

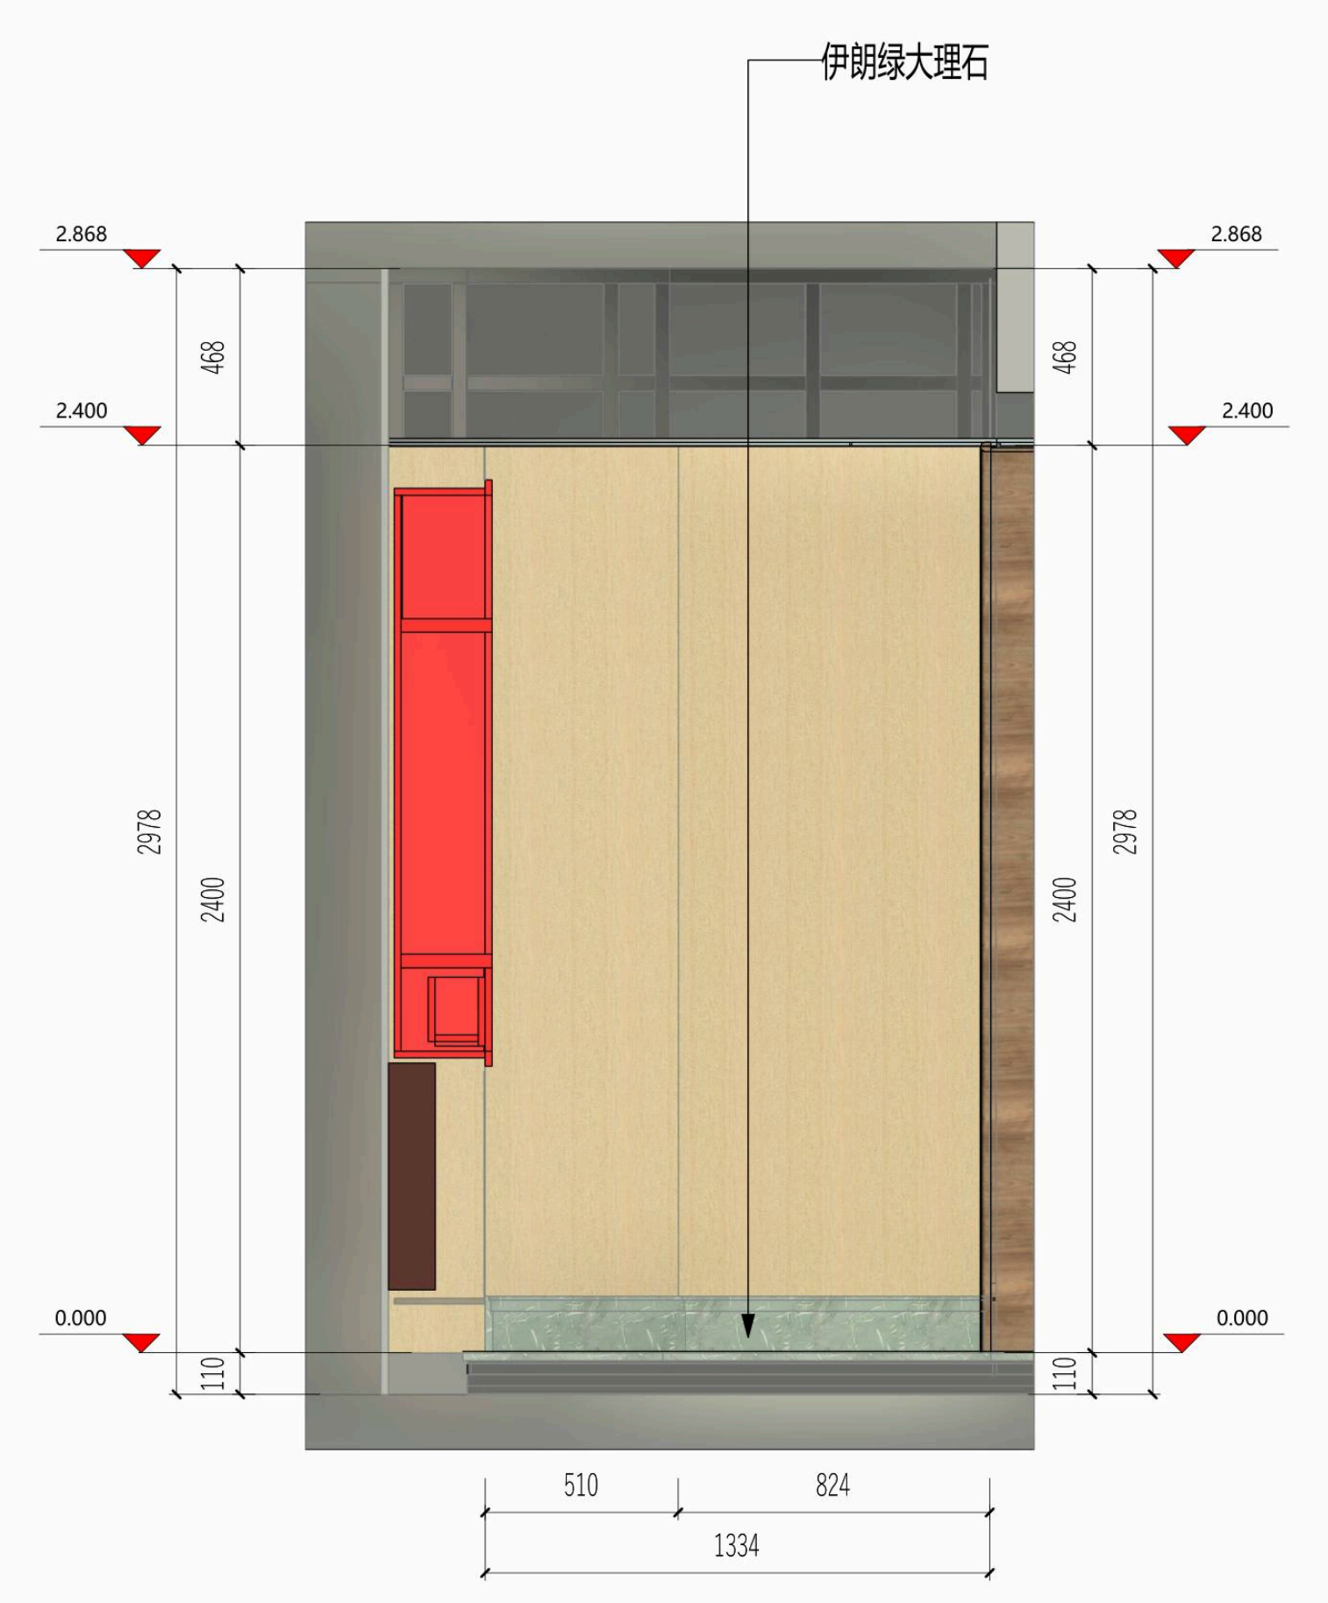
伊朗绿大理石
2.868
2.400
0.000
468
2978
2400
110
510
824
1334

公卫-06

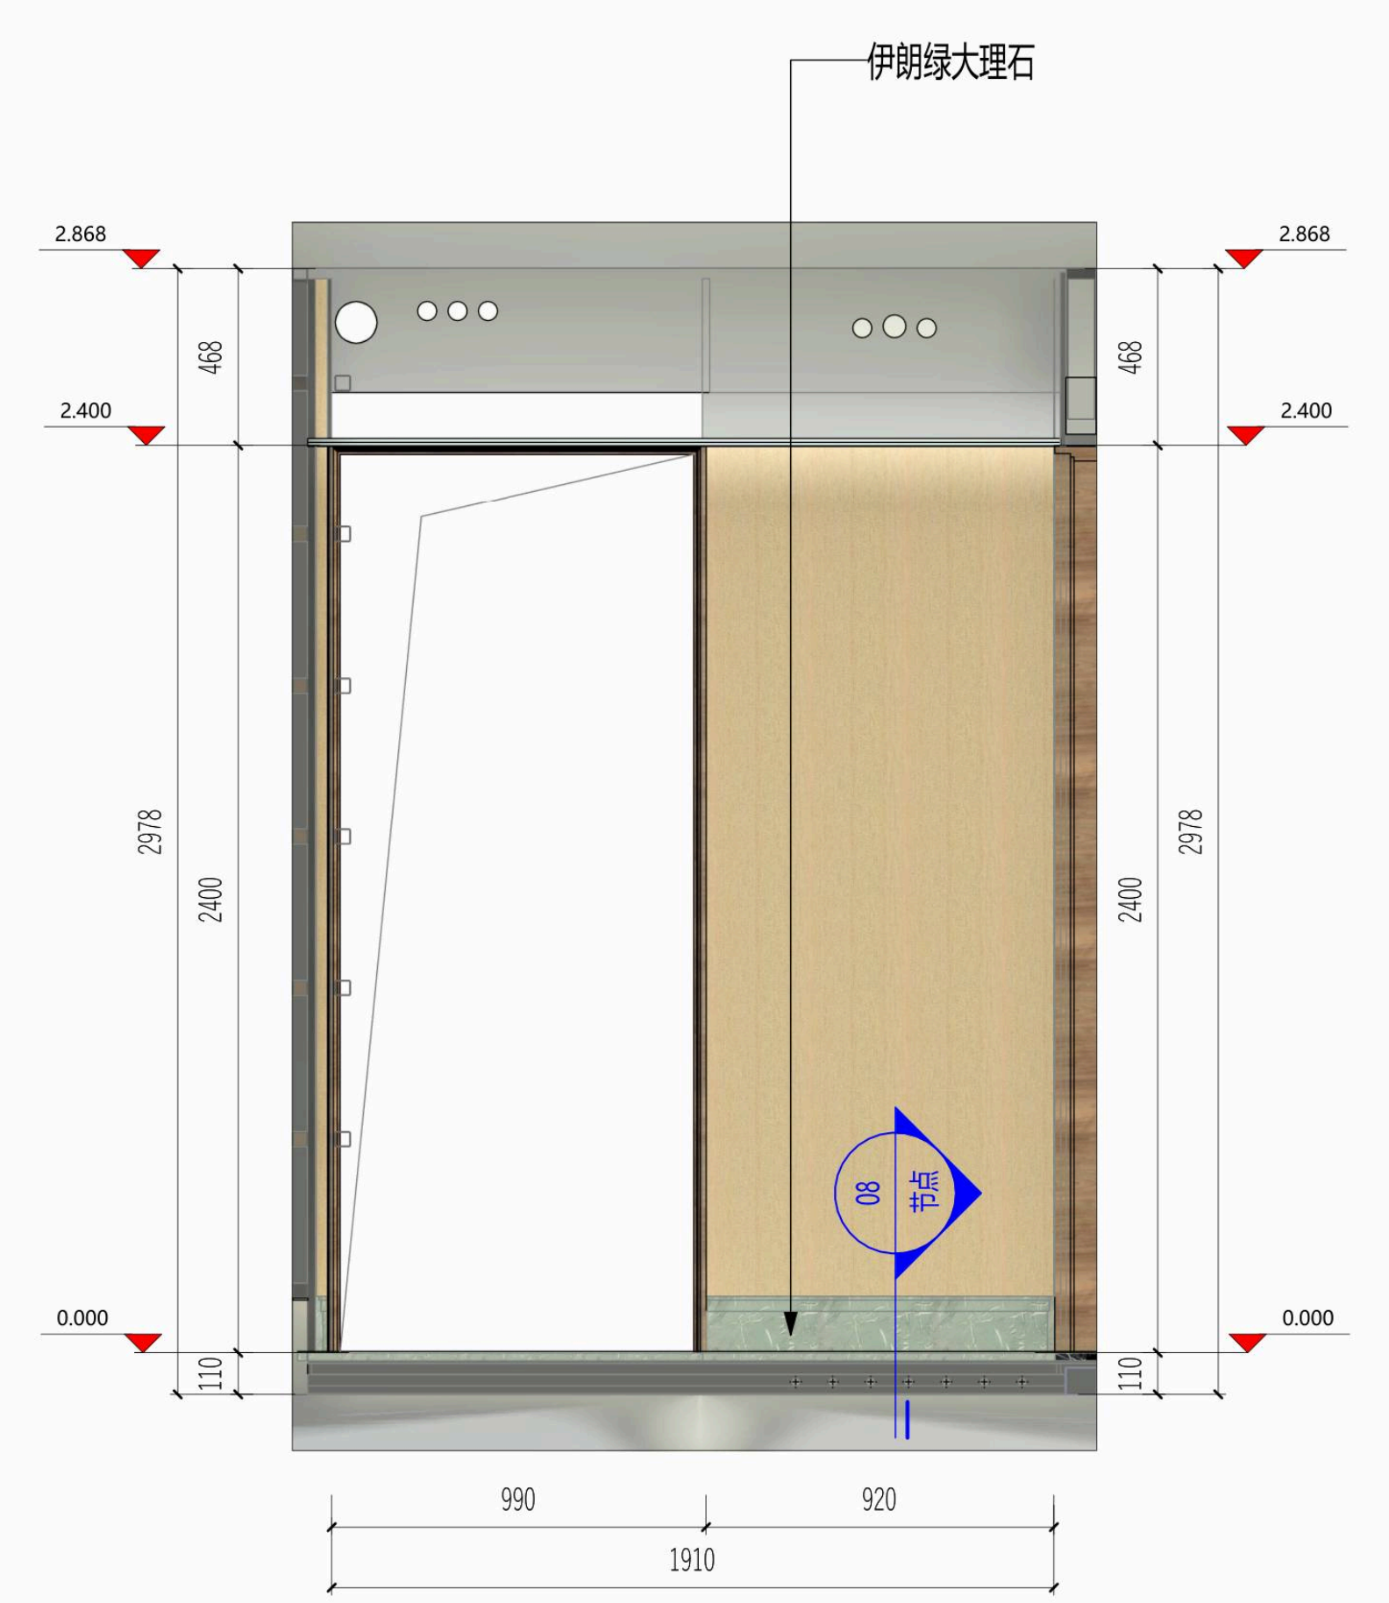
伊朗绿大理石
2.868
2.400
0.000
468
2978
2400
110
08 节点
990
920
1910

公卫-07

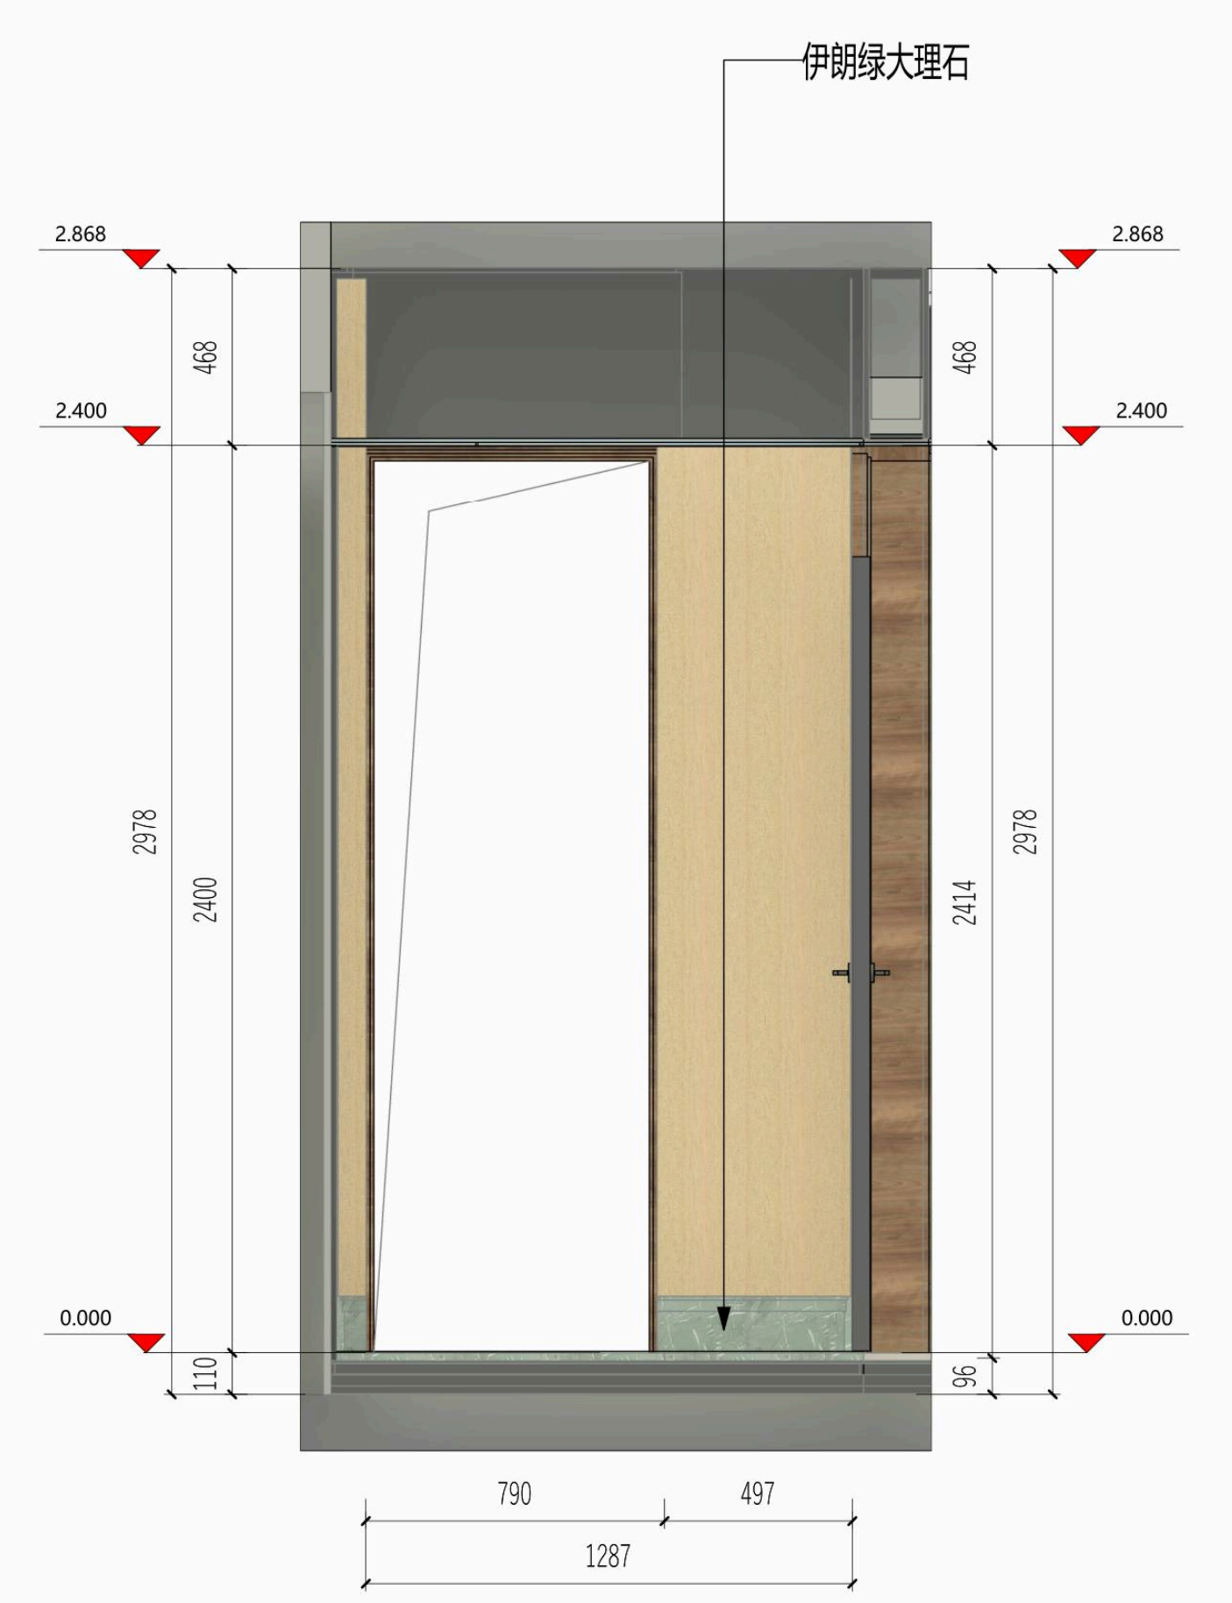
伊朗绿大理石
2.868
2.400
0.000
468
2978
2400
110
2414
96
790
497
1287

公卫-08

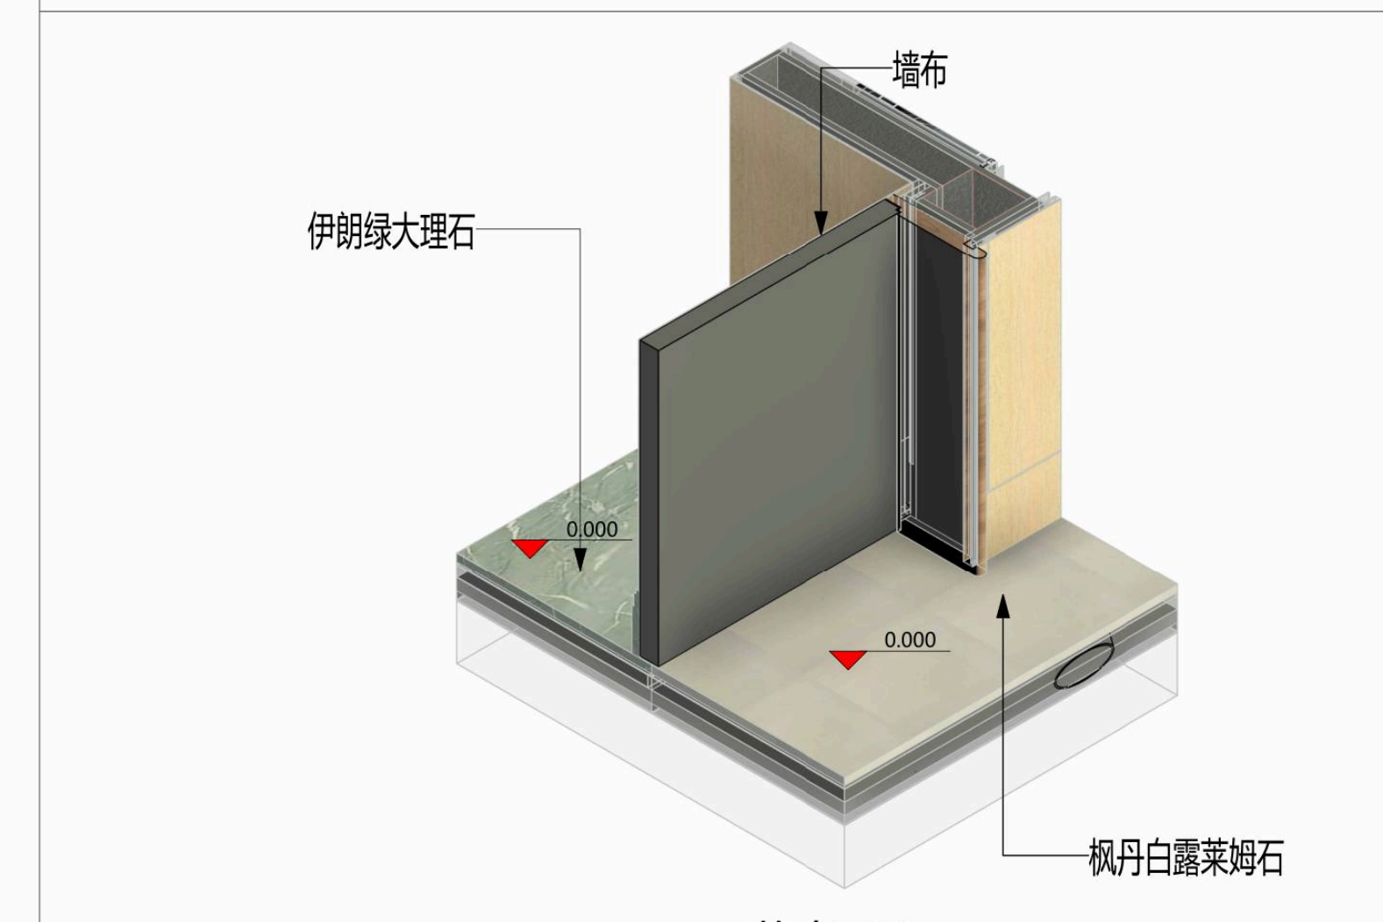
墙布
伊朗绿大理石
0.000
0.000
枫丹白露莱姆石

节点-01

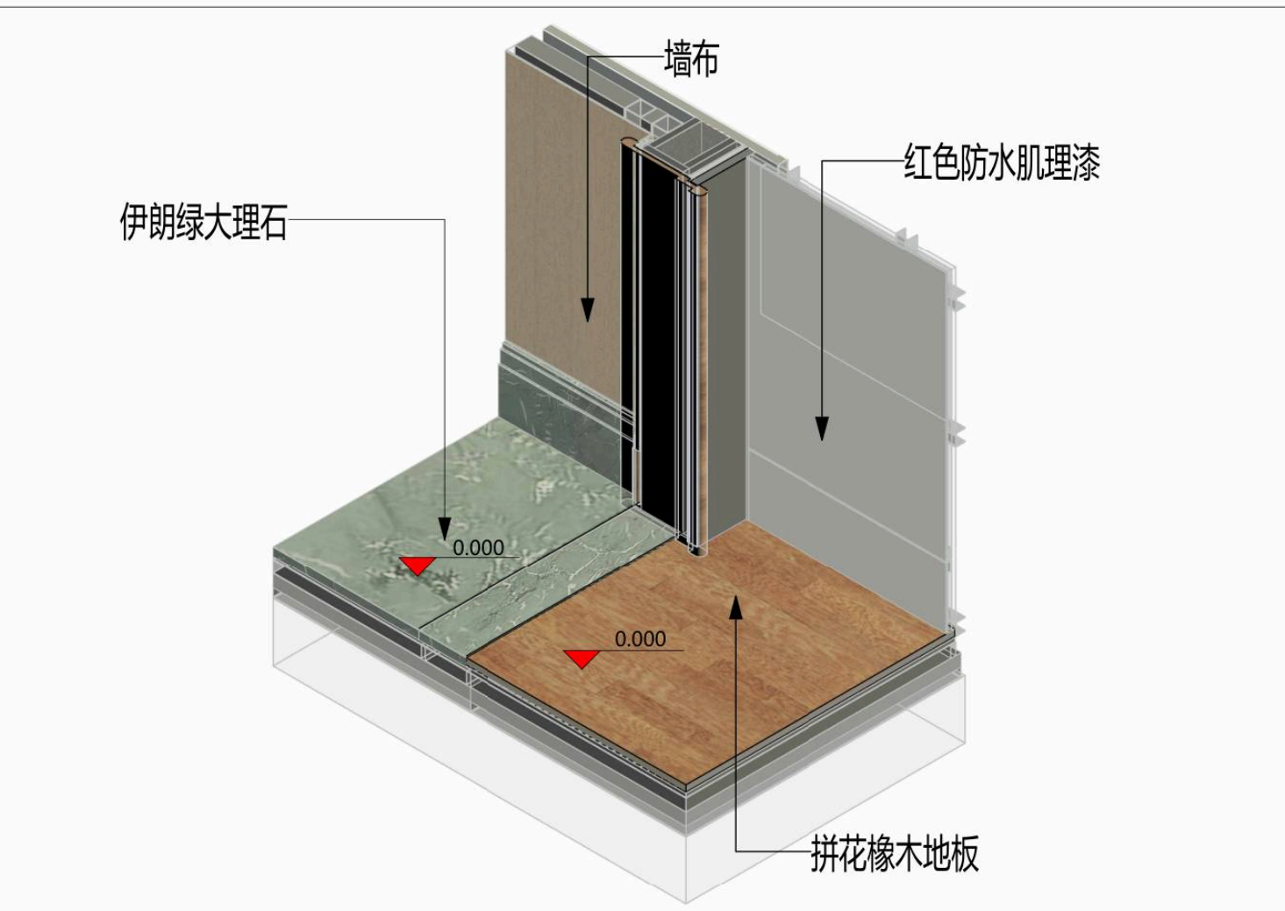
墙布
红色防水肌理漆
伊朗绿大理石
0.000
0.000
拼花橡木地板

节点-02

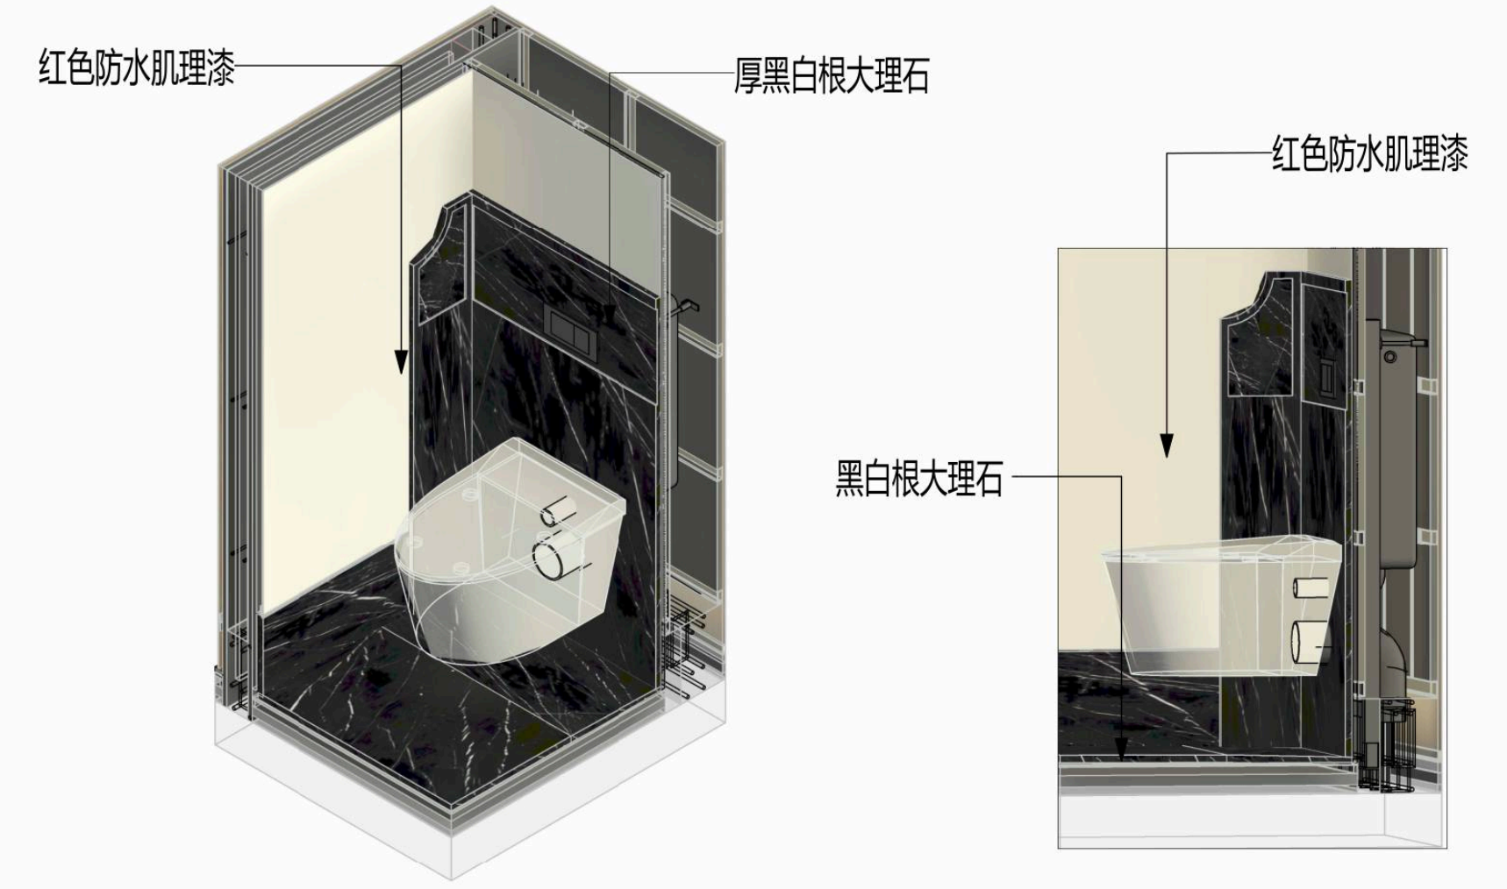
红色防水肌理漆
厚黑白根大理石
红色防水肌理漆
黑白根大理石

节点-03

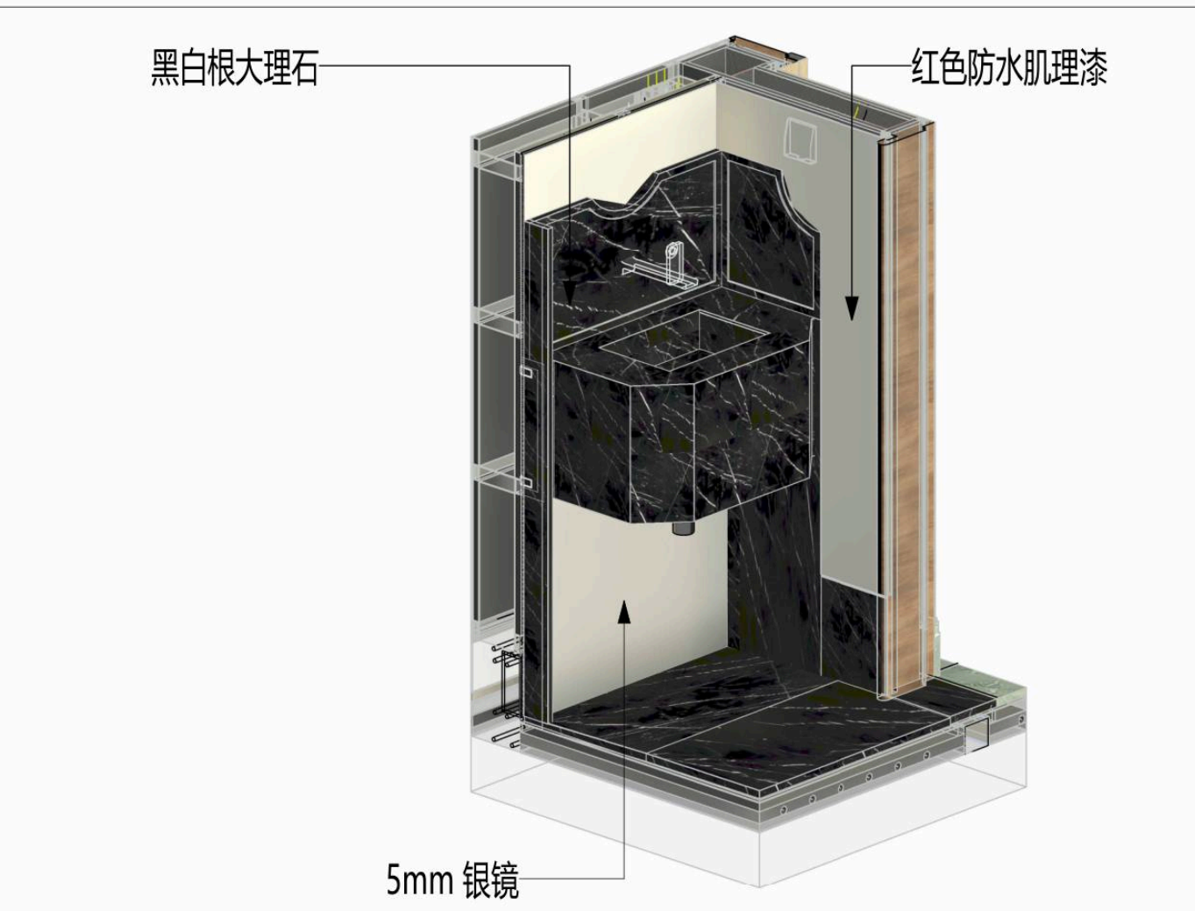
黑白根大理石
红色防水肌理漆
5mm 银镜

节点-04

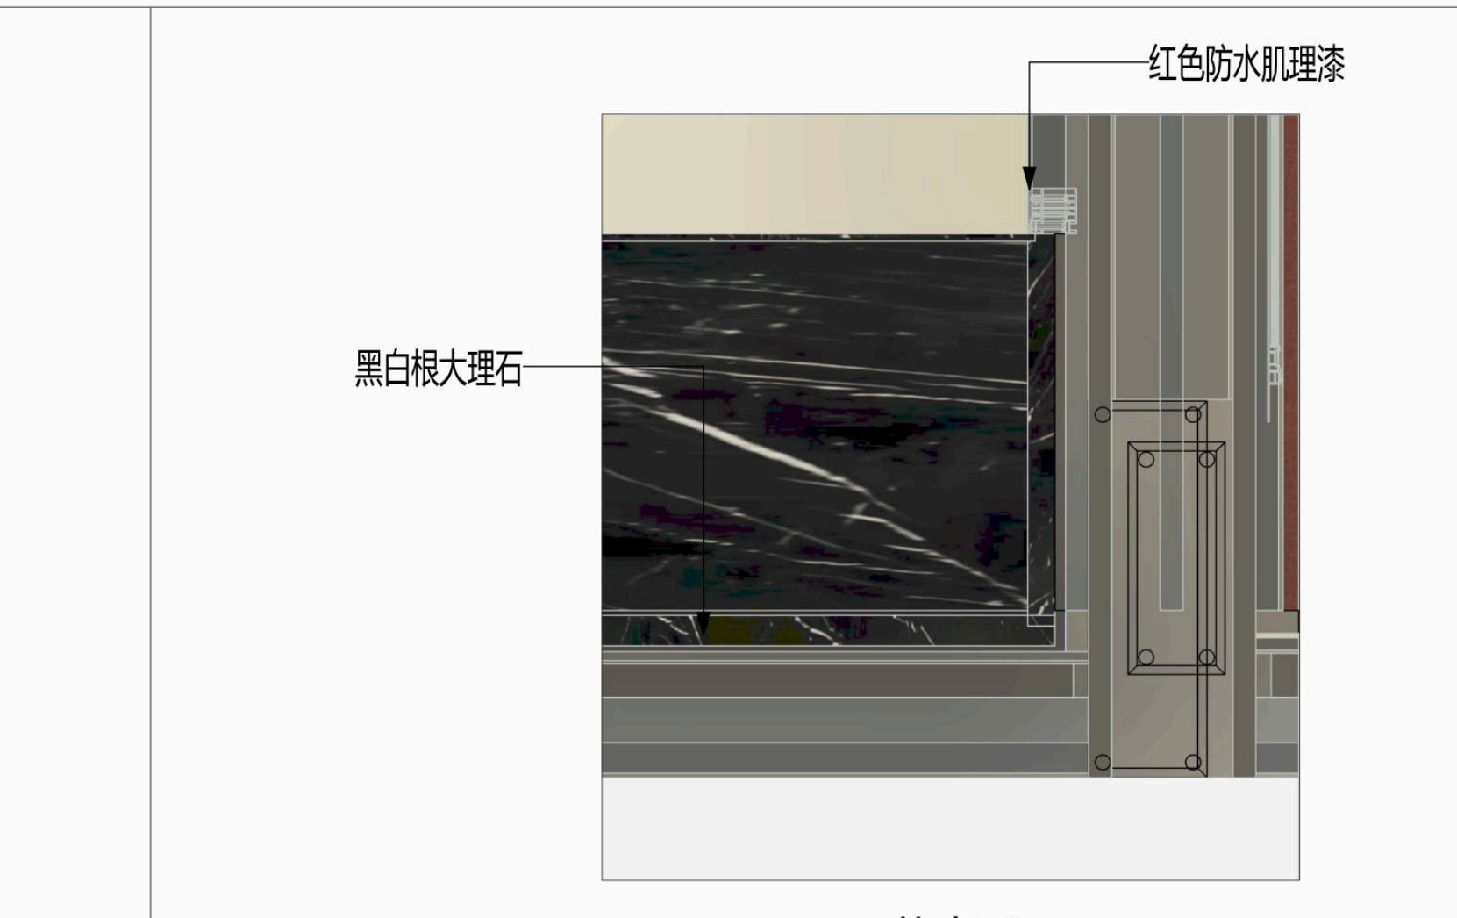
红色防水肌理漆
黑白根大理石

节点-05

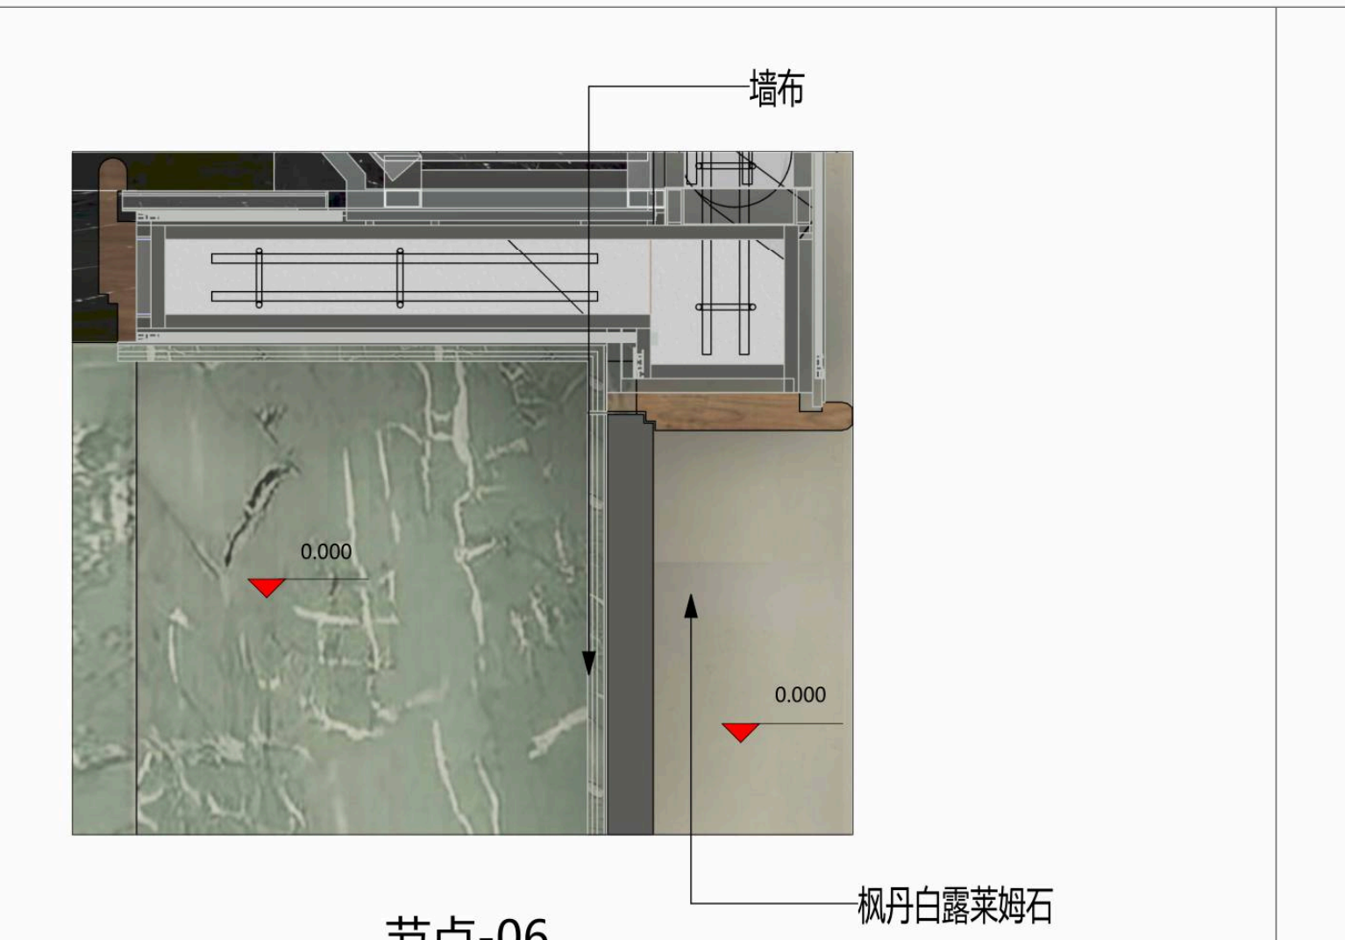
墙布
0.000
0.000
枫丹白露莱姆石

节点-06

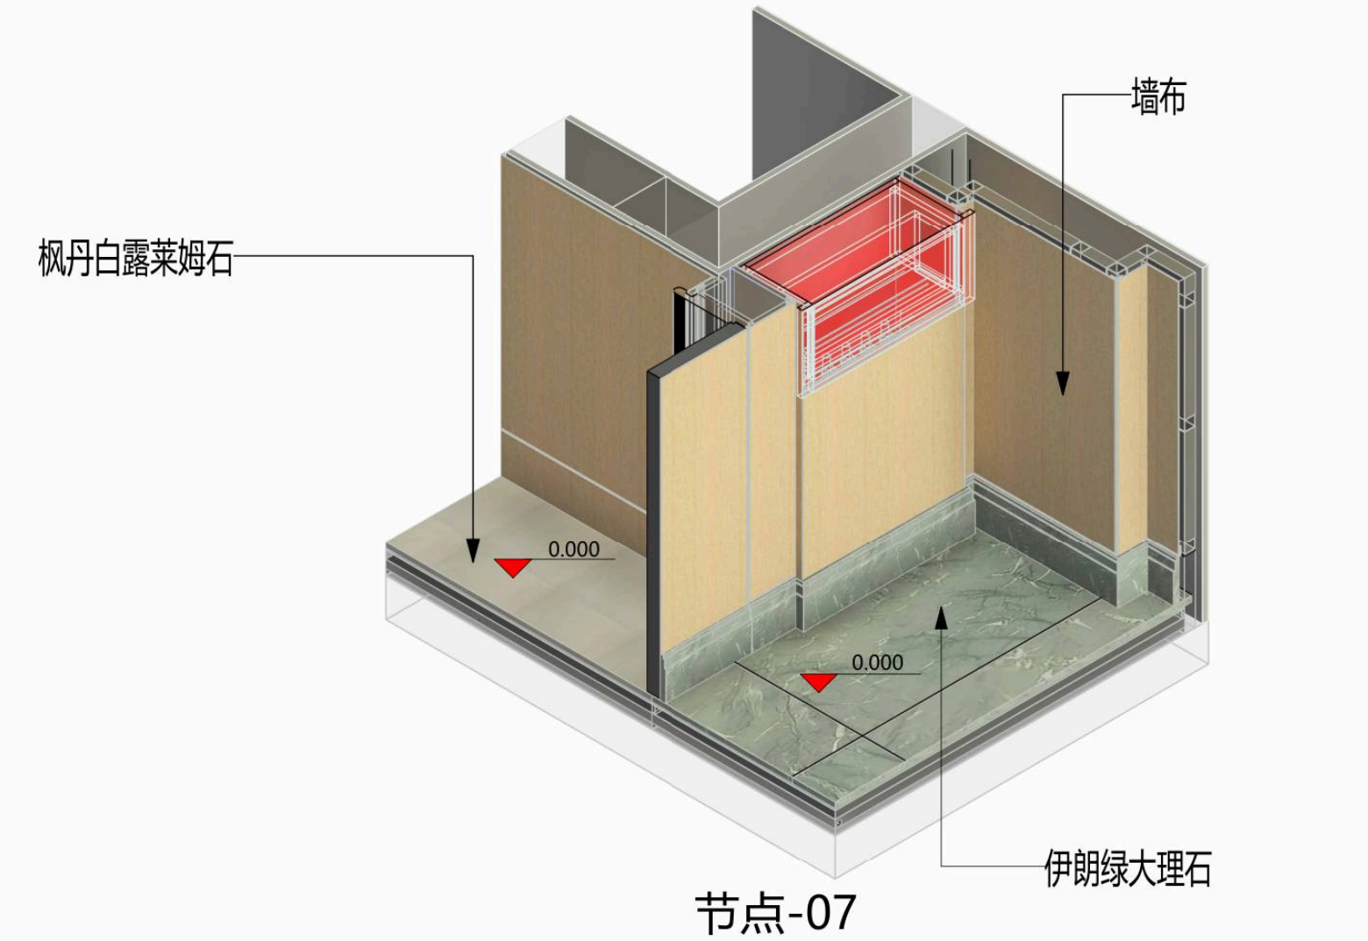
墙布
枫丹白露莱姆石
0.000
0.000
伊朗绿大理石

节点-07

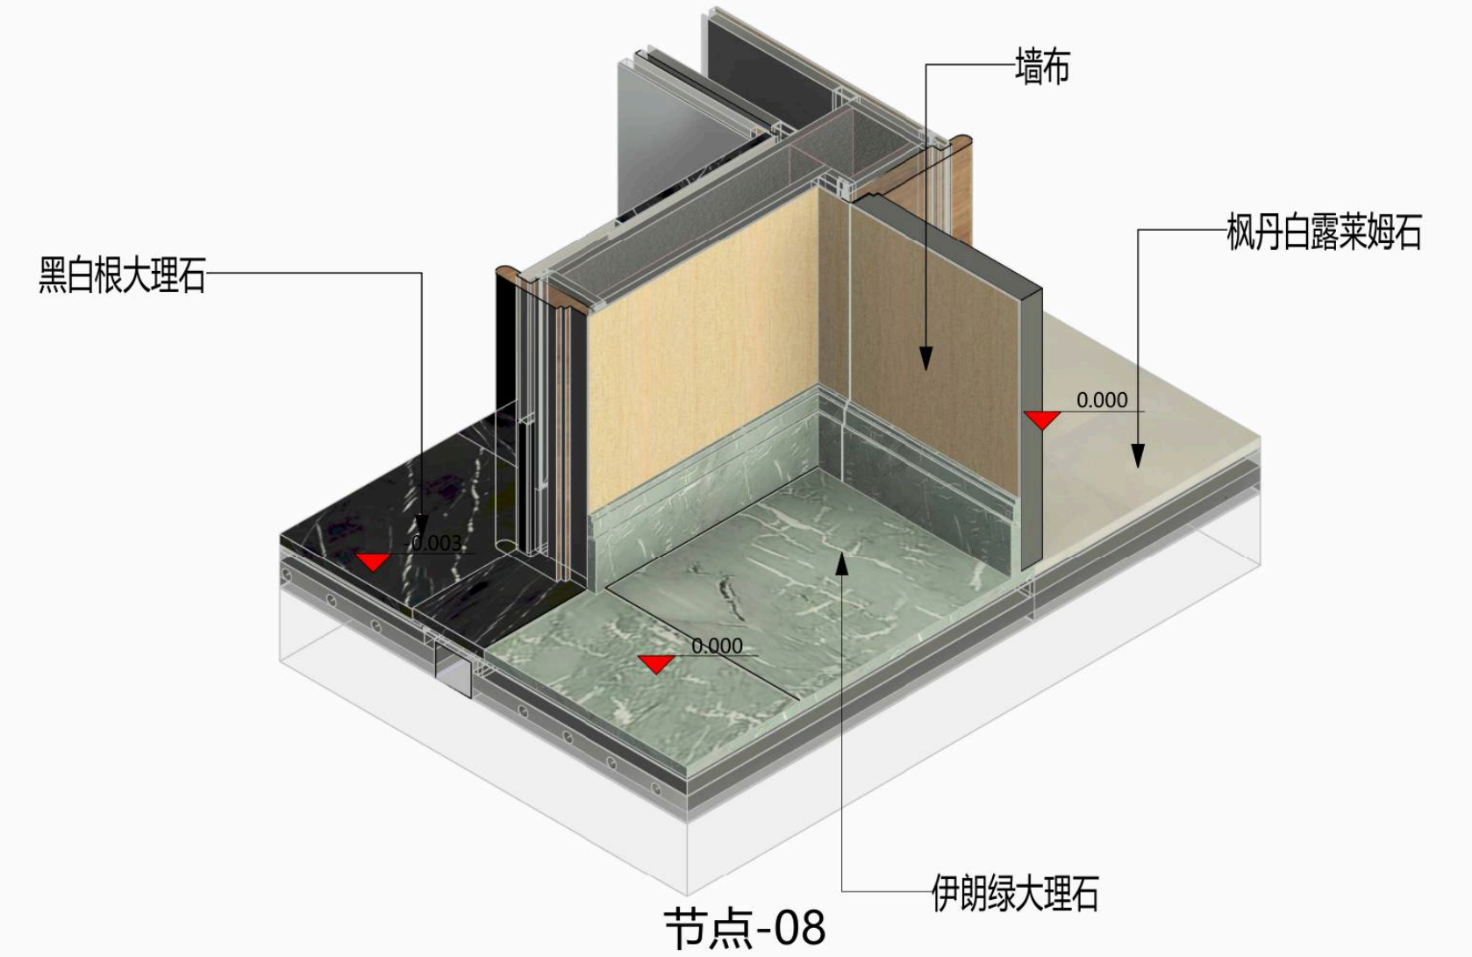
墙布
黑白根大理石
枫丹白露莱姆石
0.000
0.000
伊朗绿大理石

节点-08

编号	图例	名称
1	▨	丹枫白露大理石
2	▨	直纹白玉大理石
3	▨	米白色防水肌理漆
4	▨	红色防水肌理漆
5	▨	米黄洞石大理石
6	▨	伊朗绿大理石
7	■	黑白根大理石
8	▨	意大利木纹
9	▨	白木纹石
10	▨	塔维勒莱姆石
11	▨	木饰面
12	▨	木地板
13	▨	墙布

盖章

注释
Notes

1.本图纸如与现场尺寸有误，请施工人员与项目负责人联系。
2.施工前施工人员应认真查阅此图，如有不明确尺寸，按现场测量为准。
3.本图纸必须经甲乙双方认可并签字方可作为施工依据。

日期
Date 05/20/26

修订
Revision
△1

项目
Project
潮映华岸府3-801

比例
Scale

公卫石材铺贴

图纸编号
Drawing No.
ST-15

项目编号
Project No.

©2025

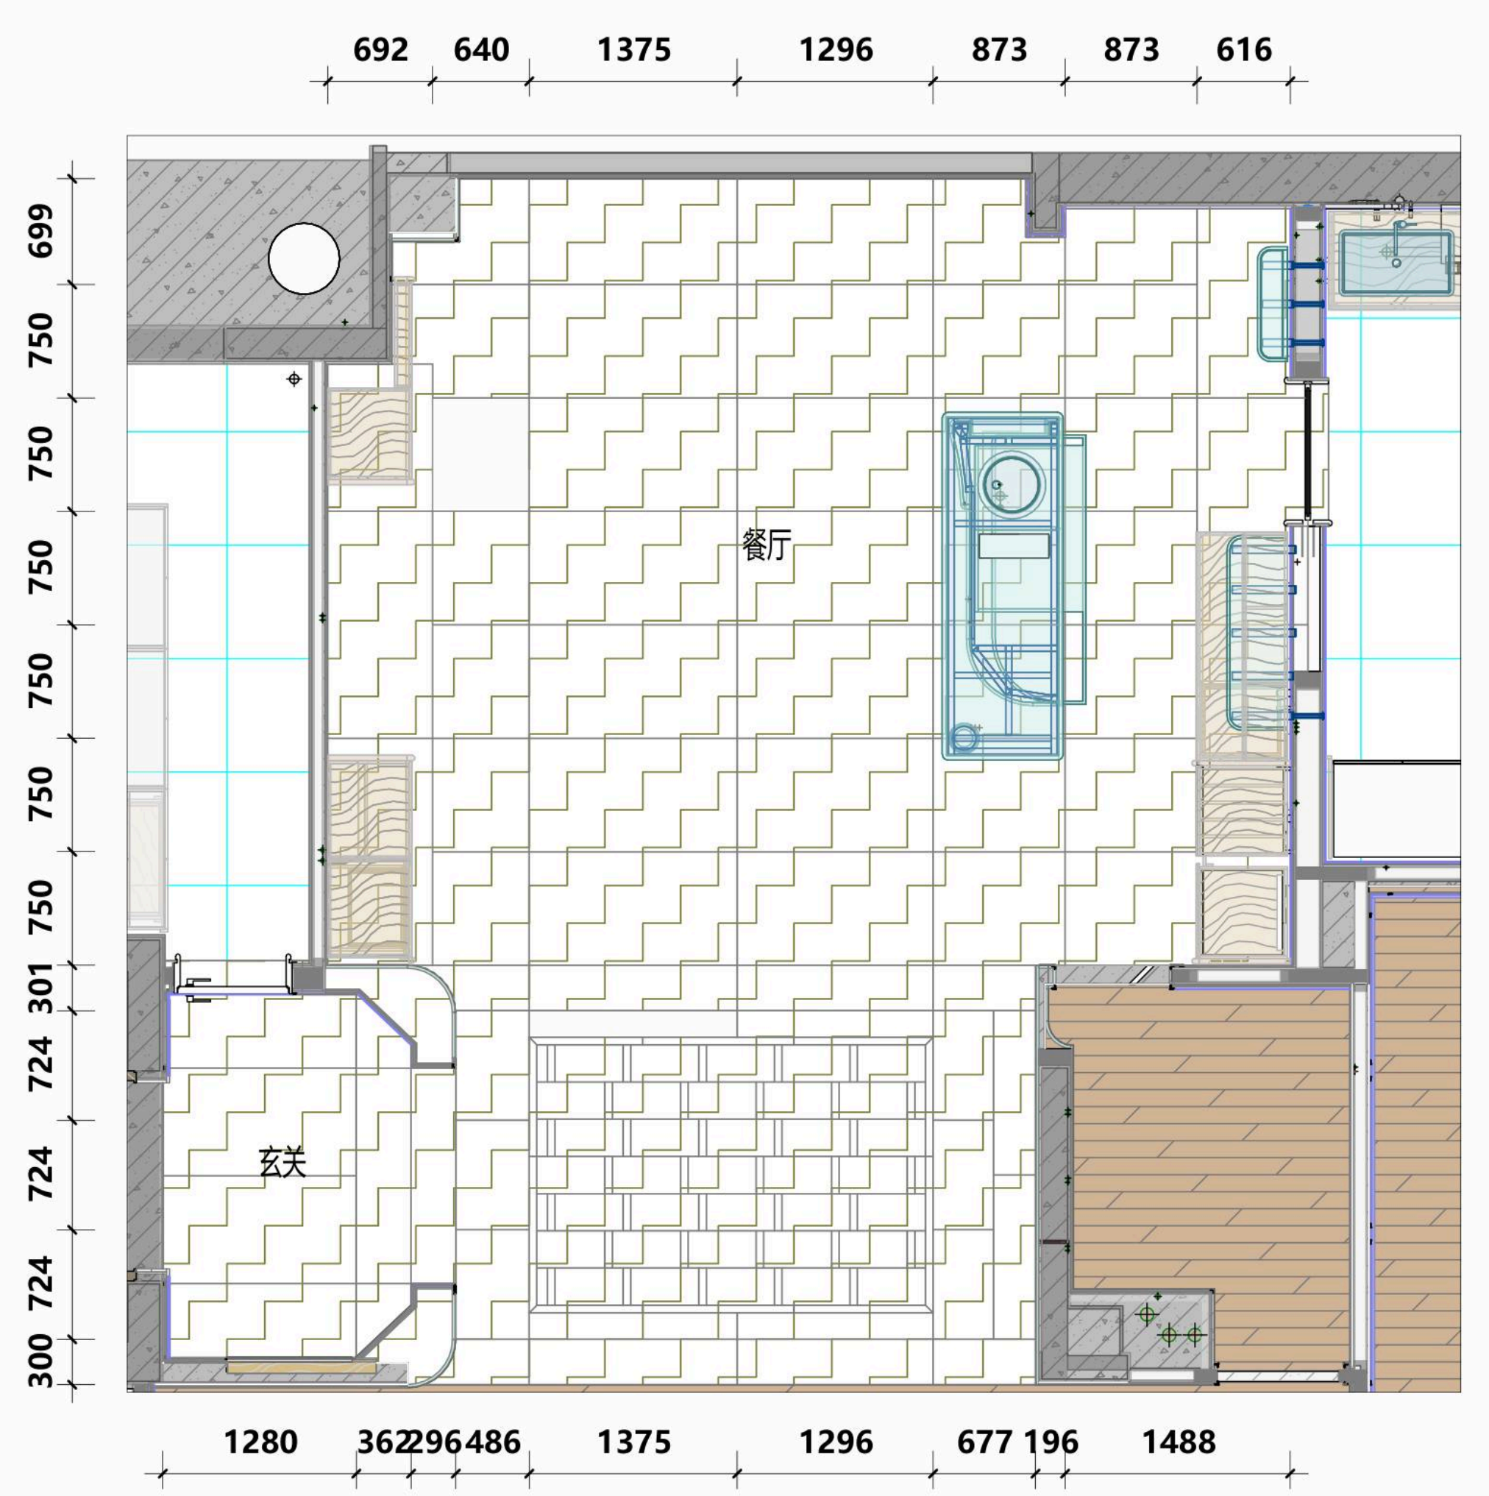
692
640
1375
1296
873
873
616
699
750
750
750
750
750
750
301
724
724
724
300
500
750
750
750
750
750
750
300
725
1448
300
餐厅
玄关
1280
362
296
486
1375
1296
677
196
1488

地面铺贴图

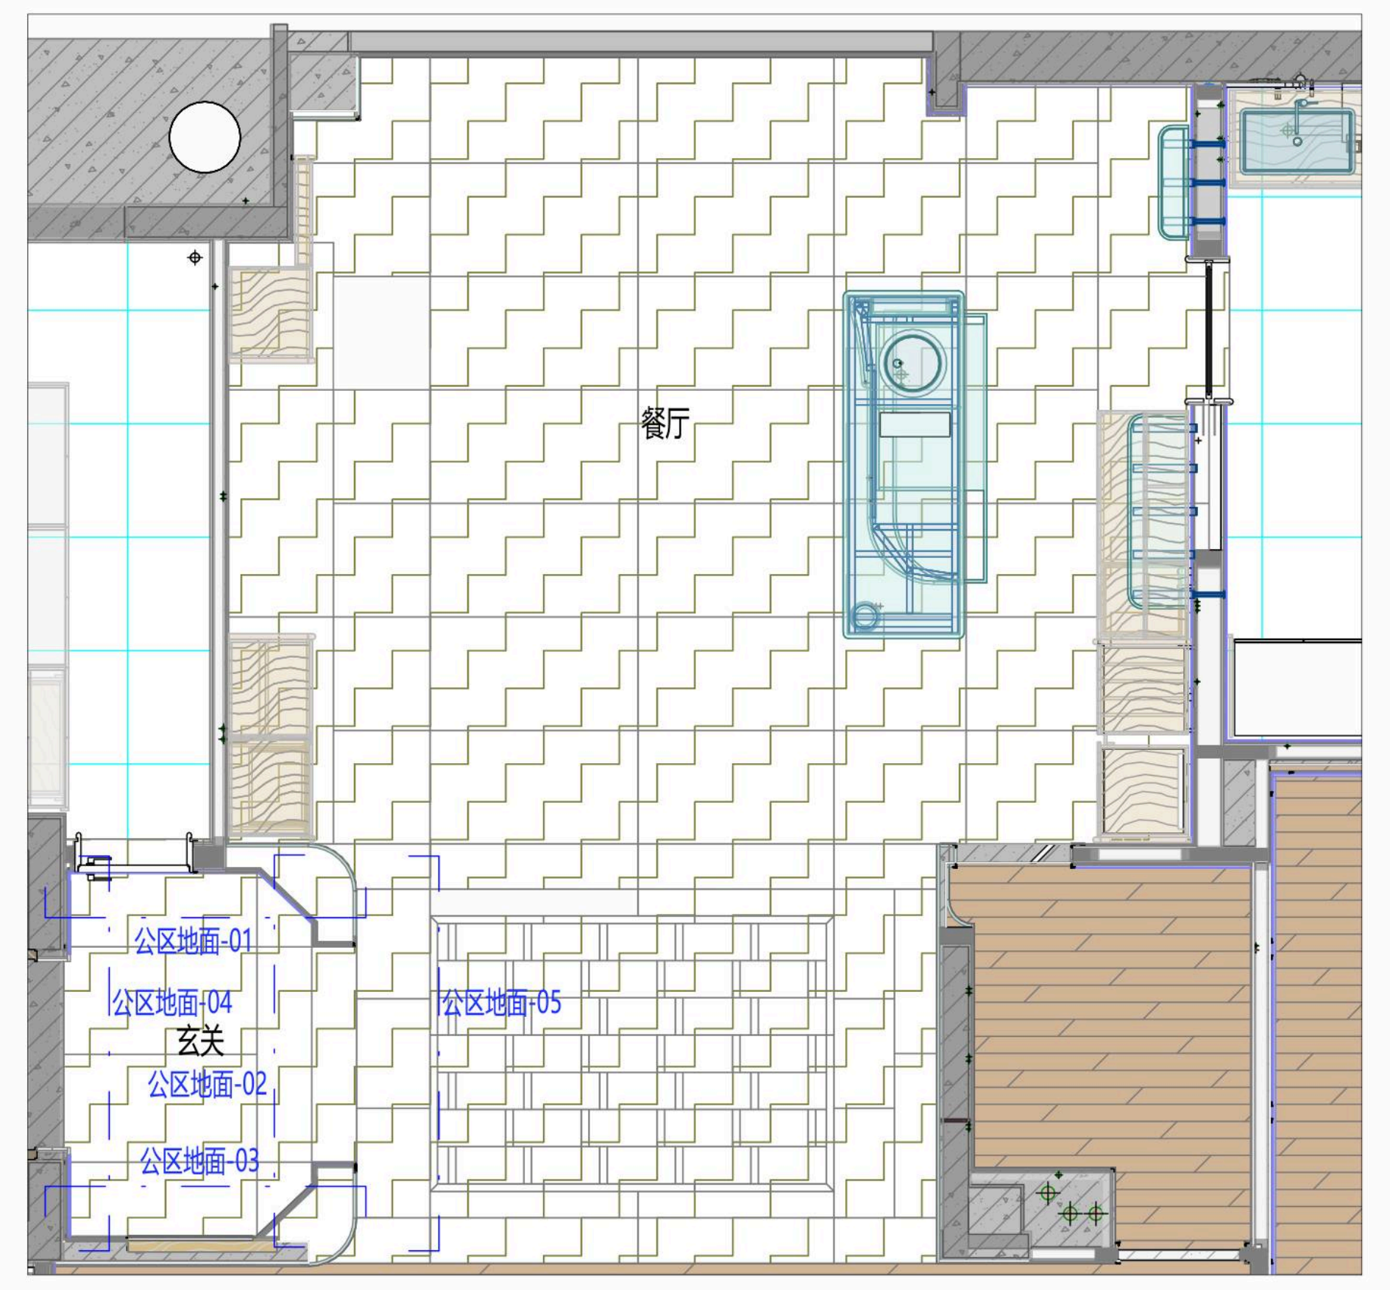
餐厅
玄关
公区地面-01
公区地面-04
公区地面-02
公区地面-03
公区地面-05

索引图

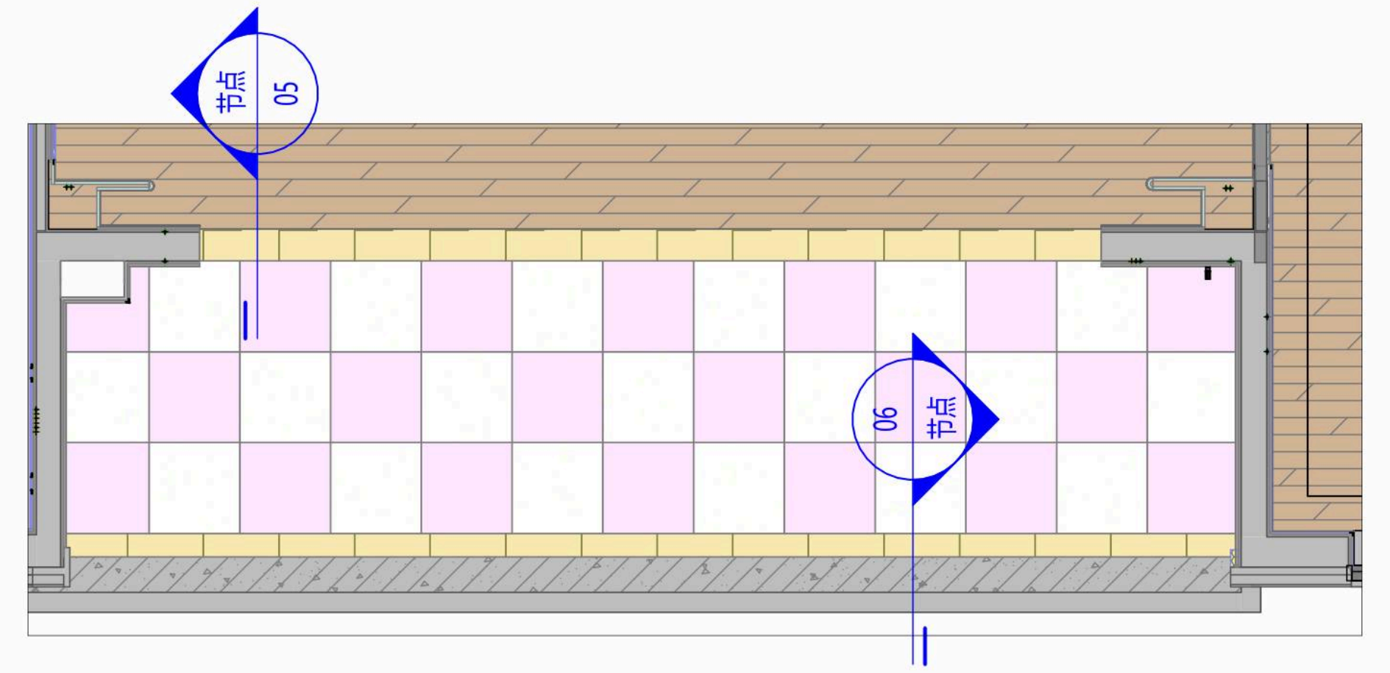

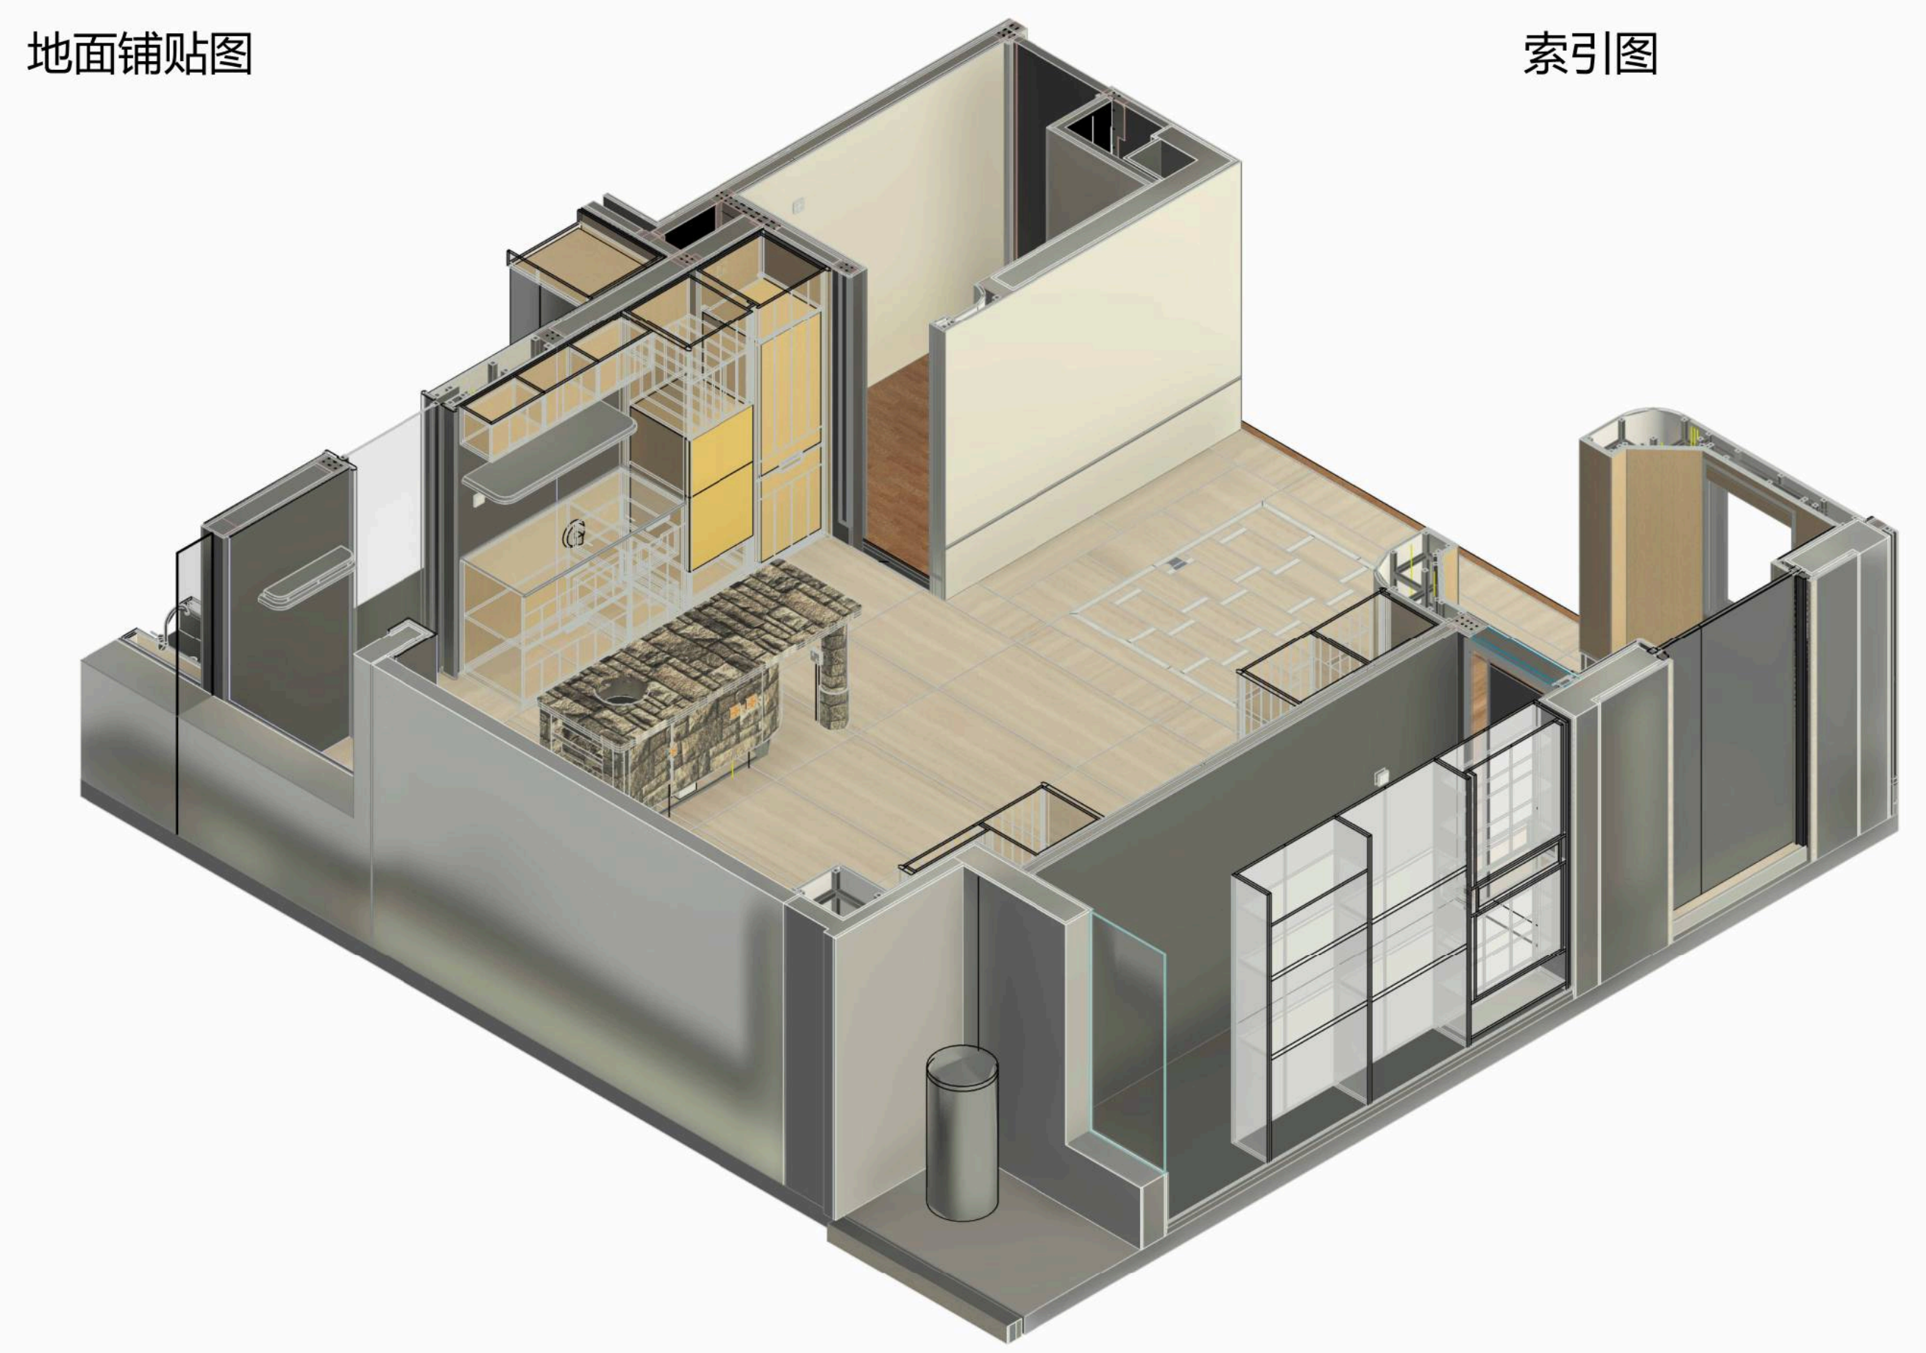

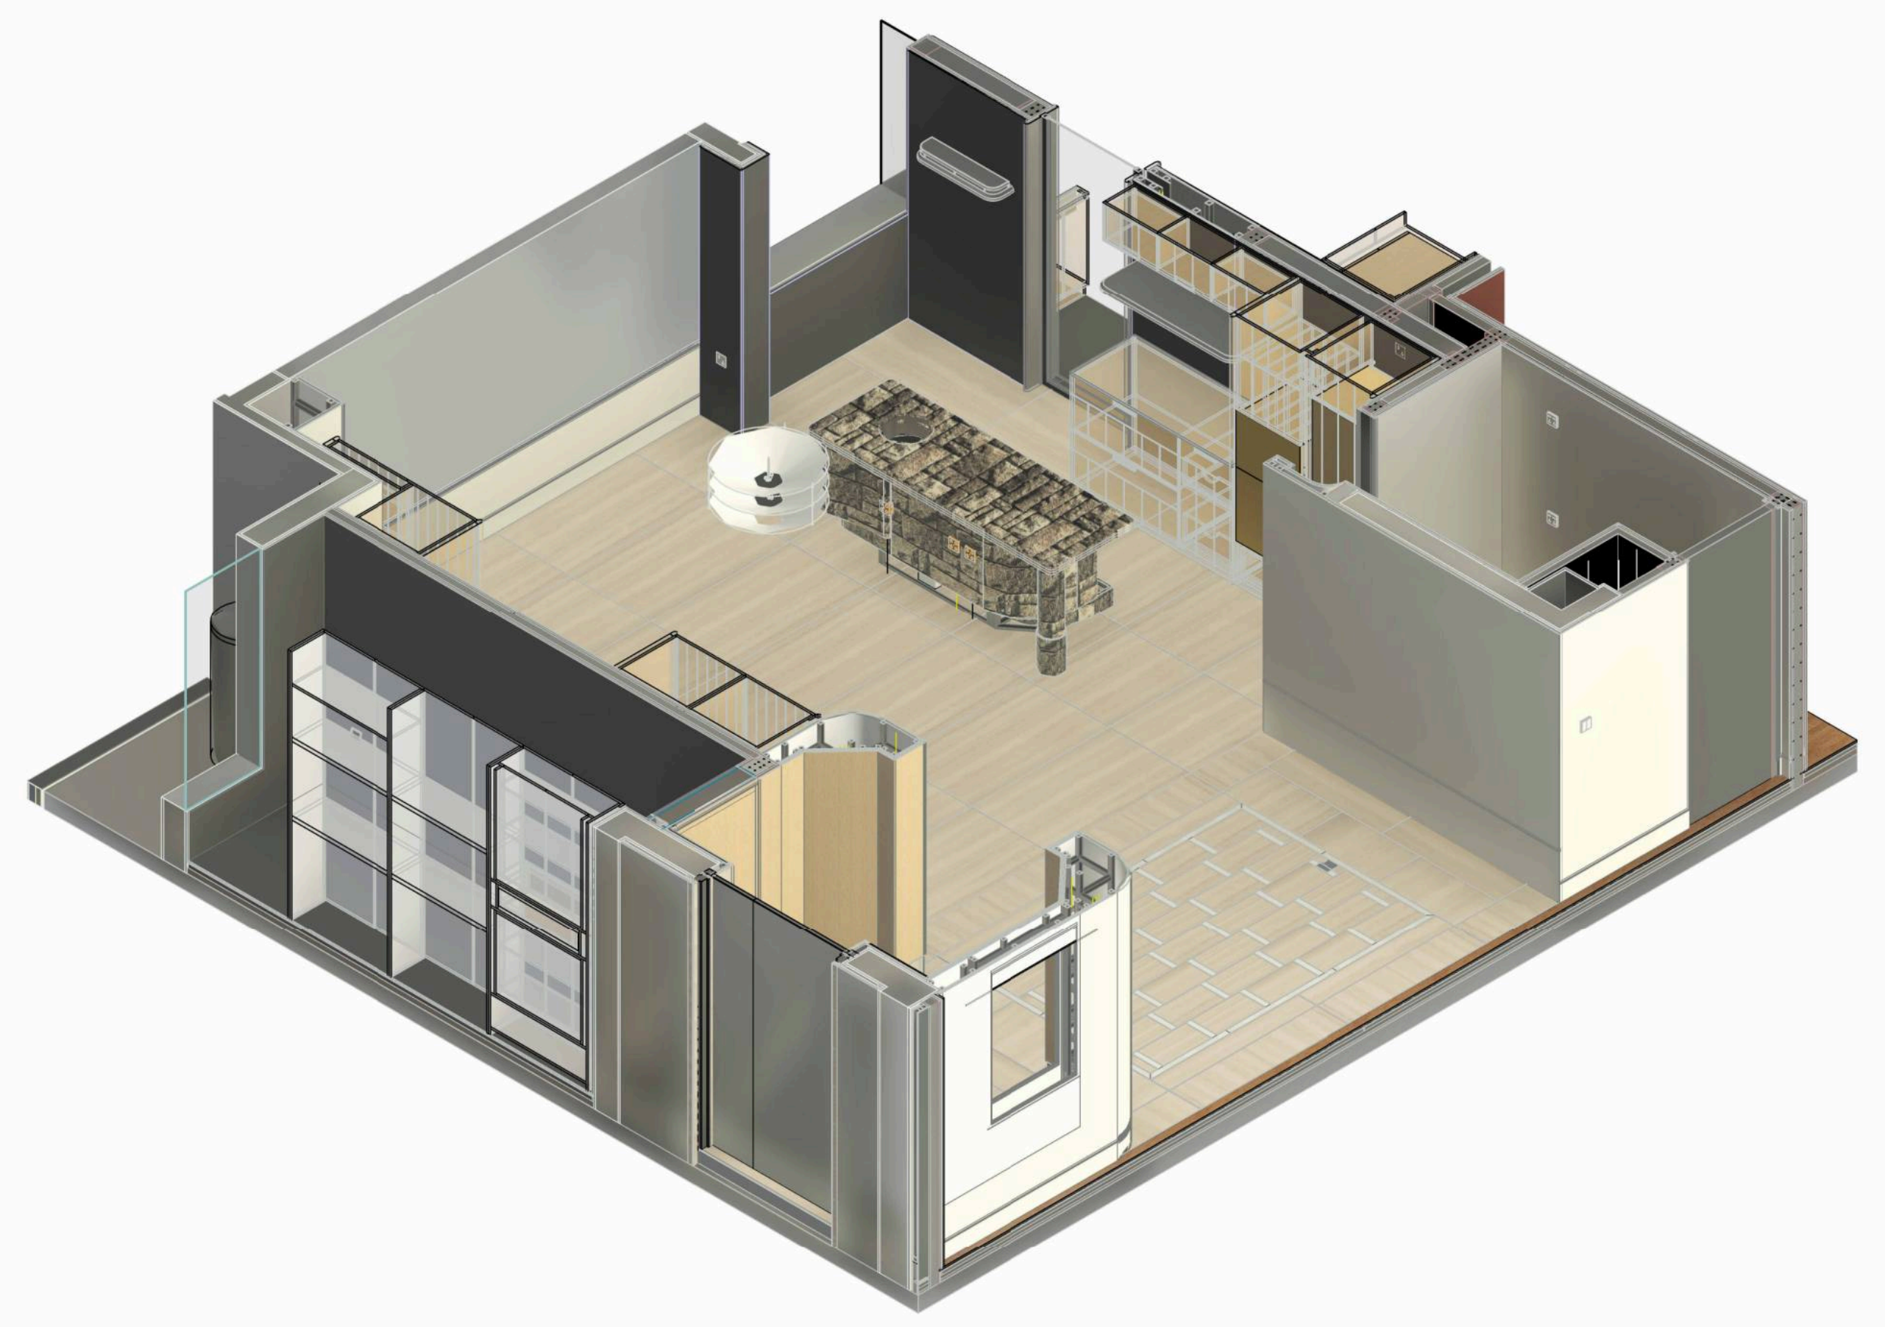

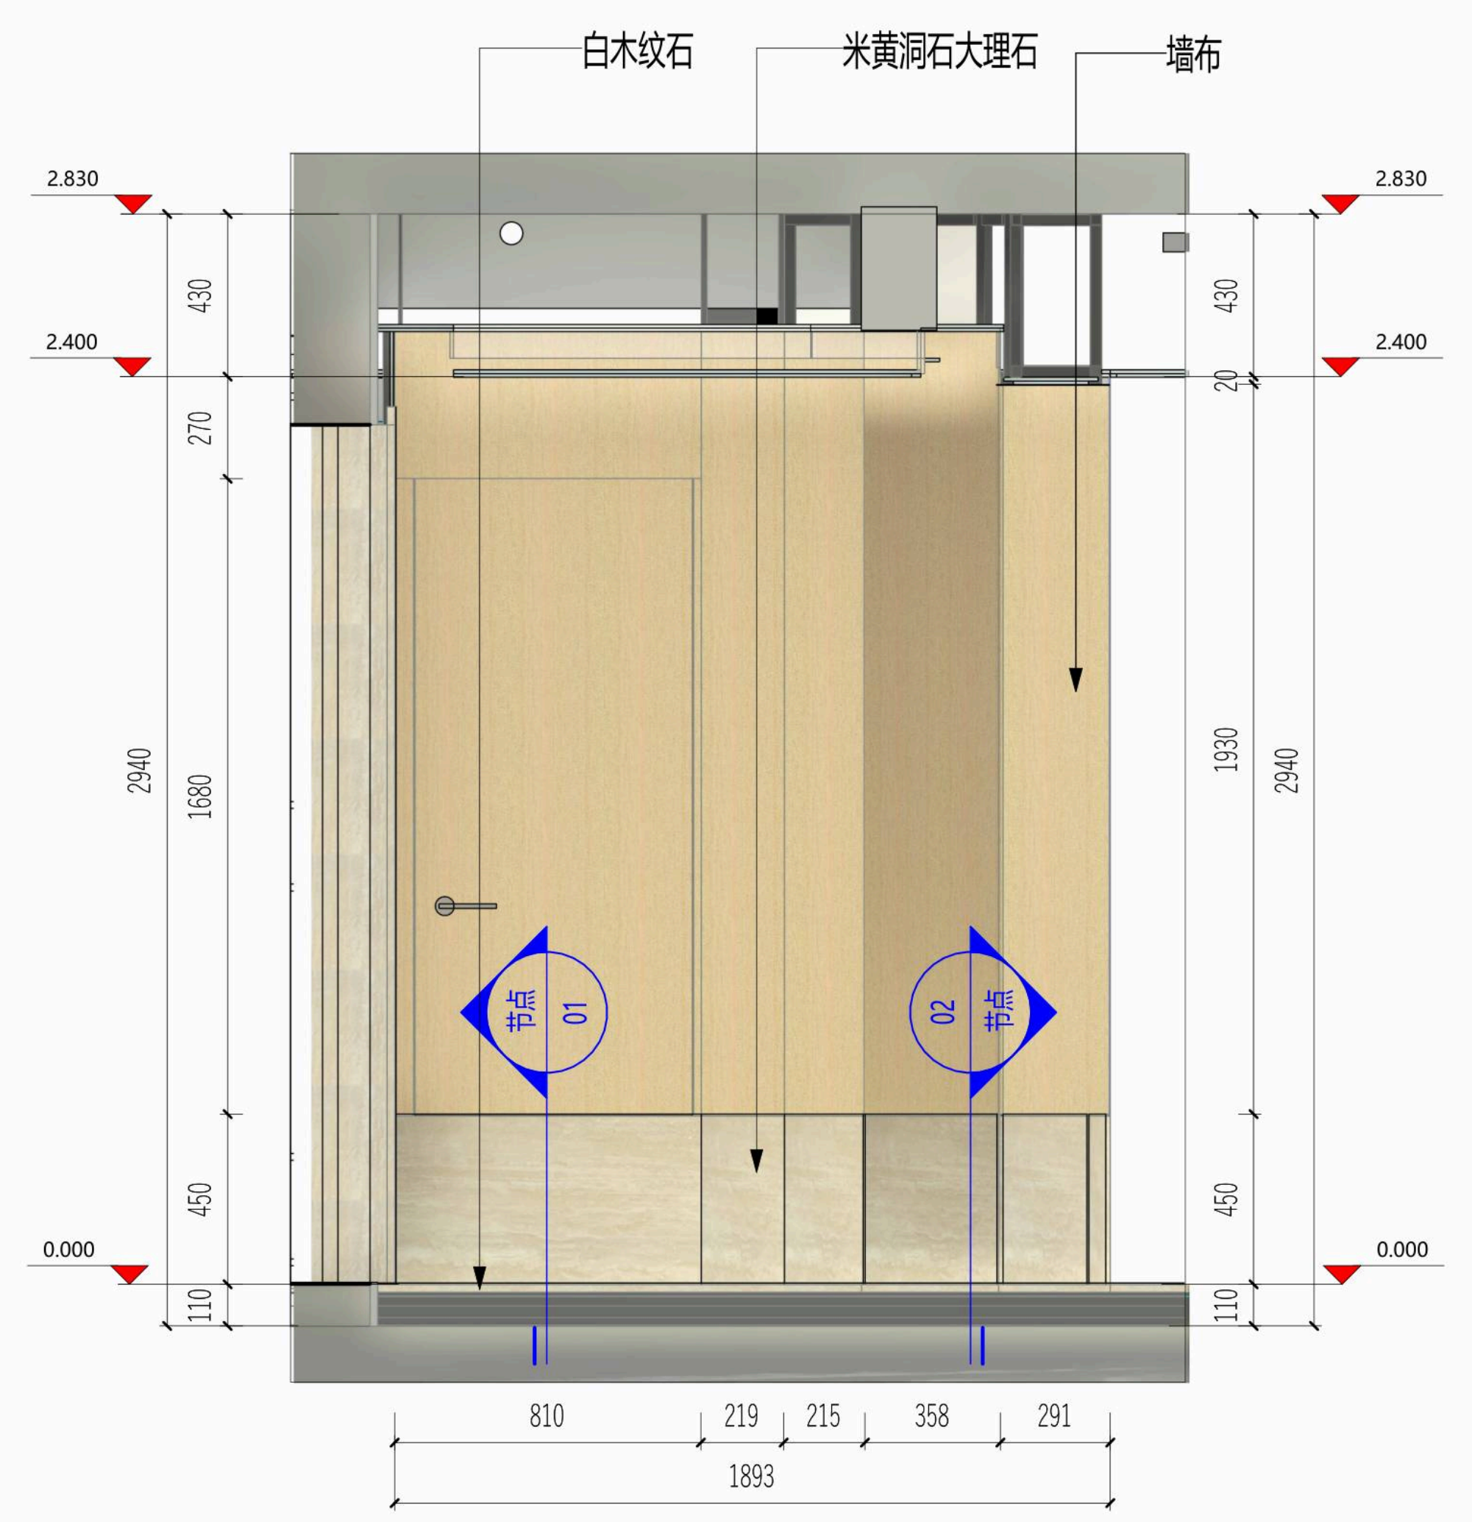
白木纹石
米黄洞石大理石
墙布
2.830
2.400
0.000
430
270
1680
450
110
2940
20
1930
节点
01
02
节点
810
219
215
358
291
1893

公区地面-01

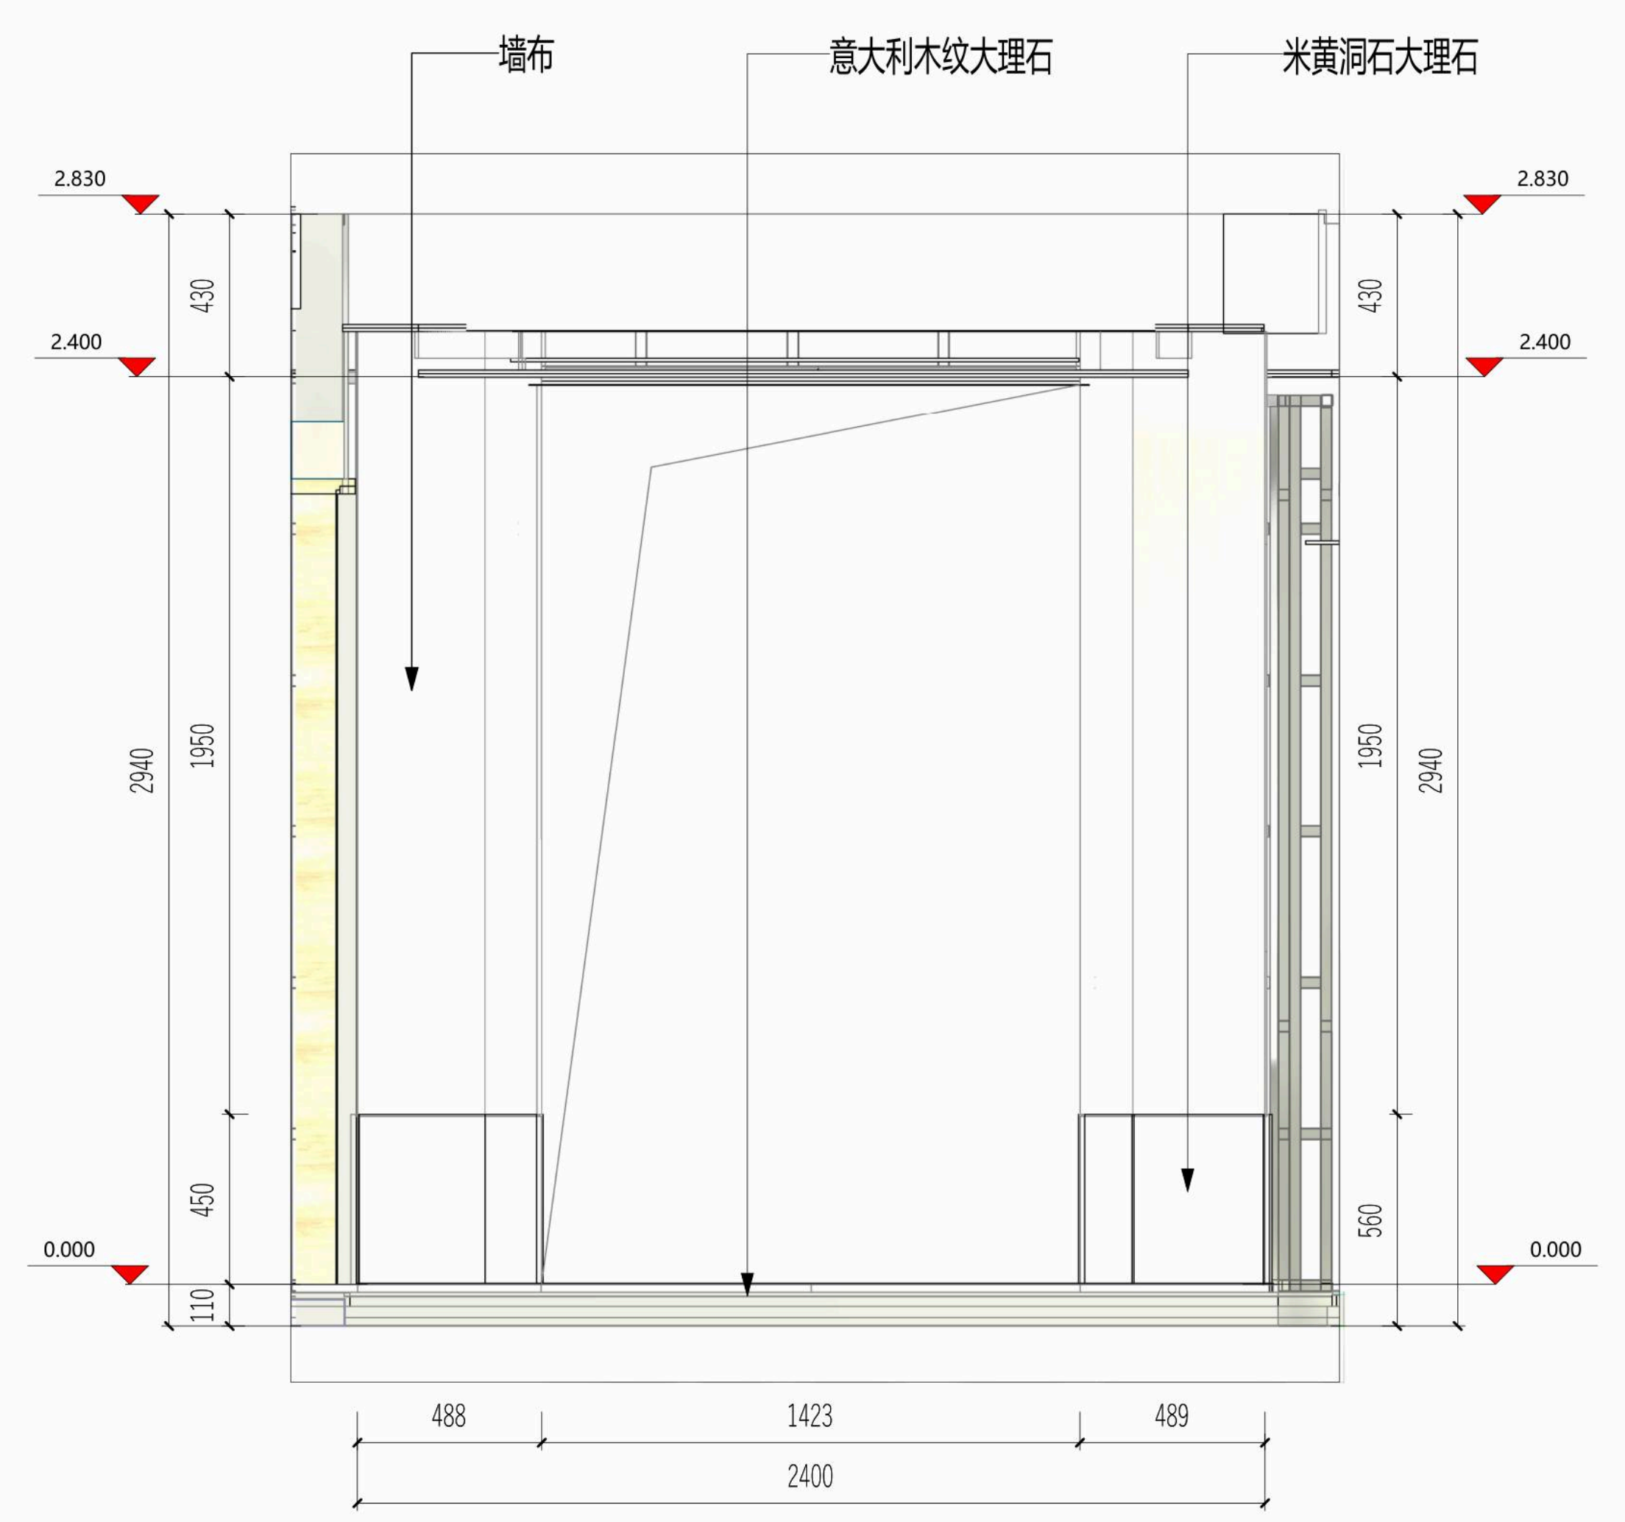
墙布
意大利木纹大理石
米黄洞石大理石
2.830
2.400
0.000
430
1950
450
110
2940
560
488
1423
489
2400

公区地面-02

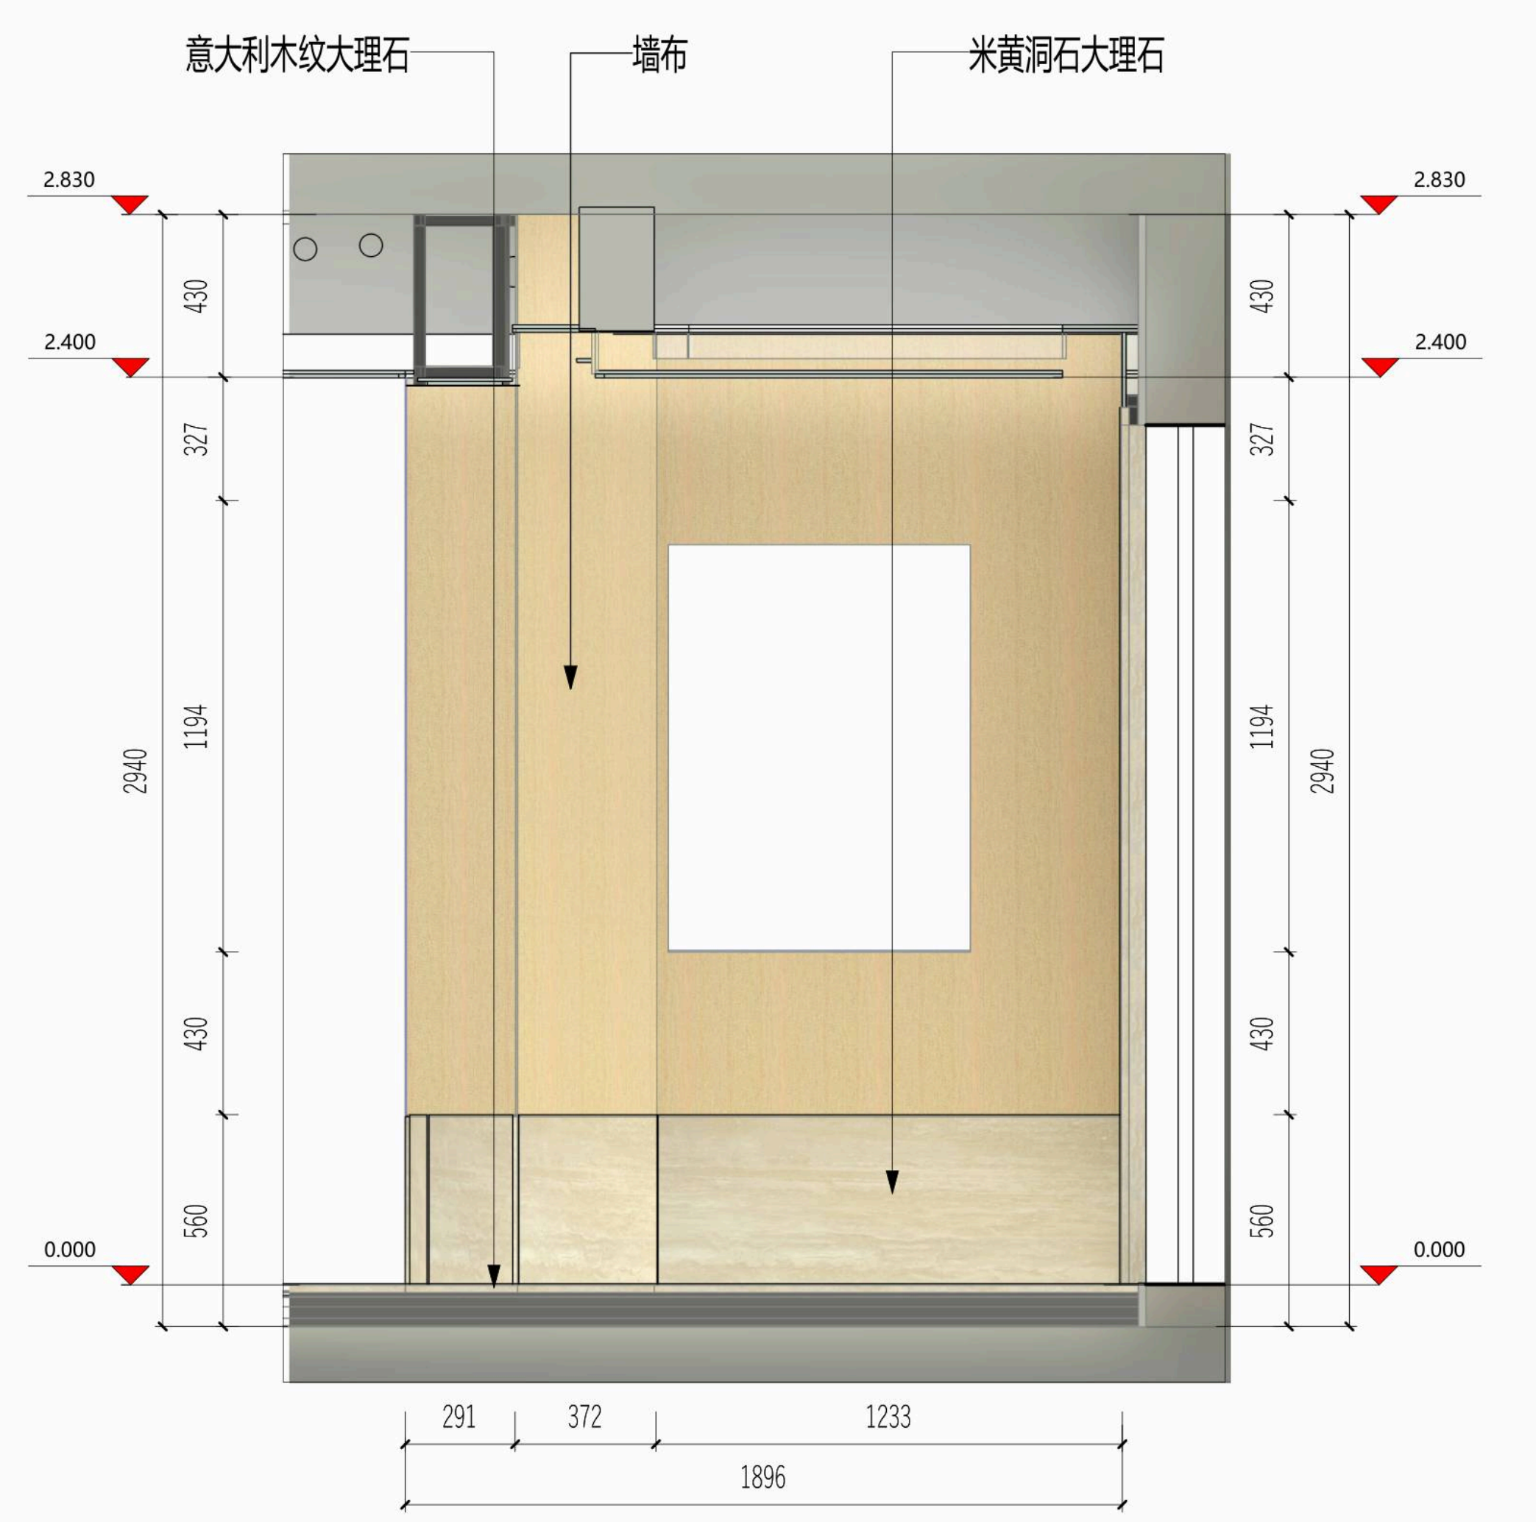
意大利木纹大理石
墙布
米黄洞石大理石
2.830
2.400
0.000
430
327
1194
430
560
2940
291
372
1233
1896

公区地面-03

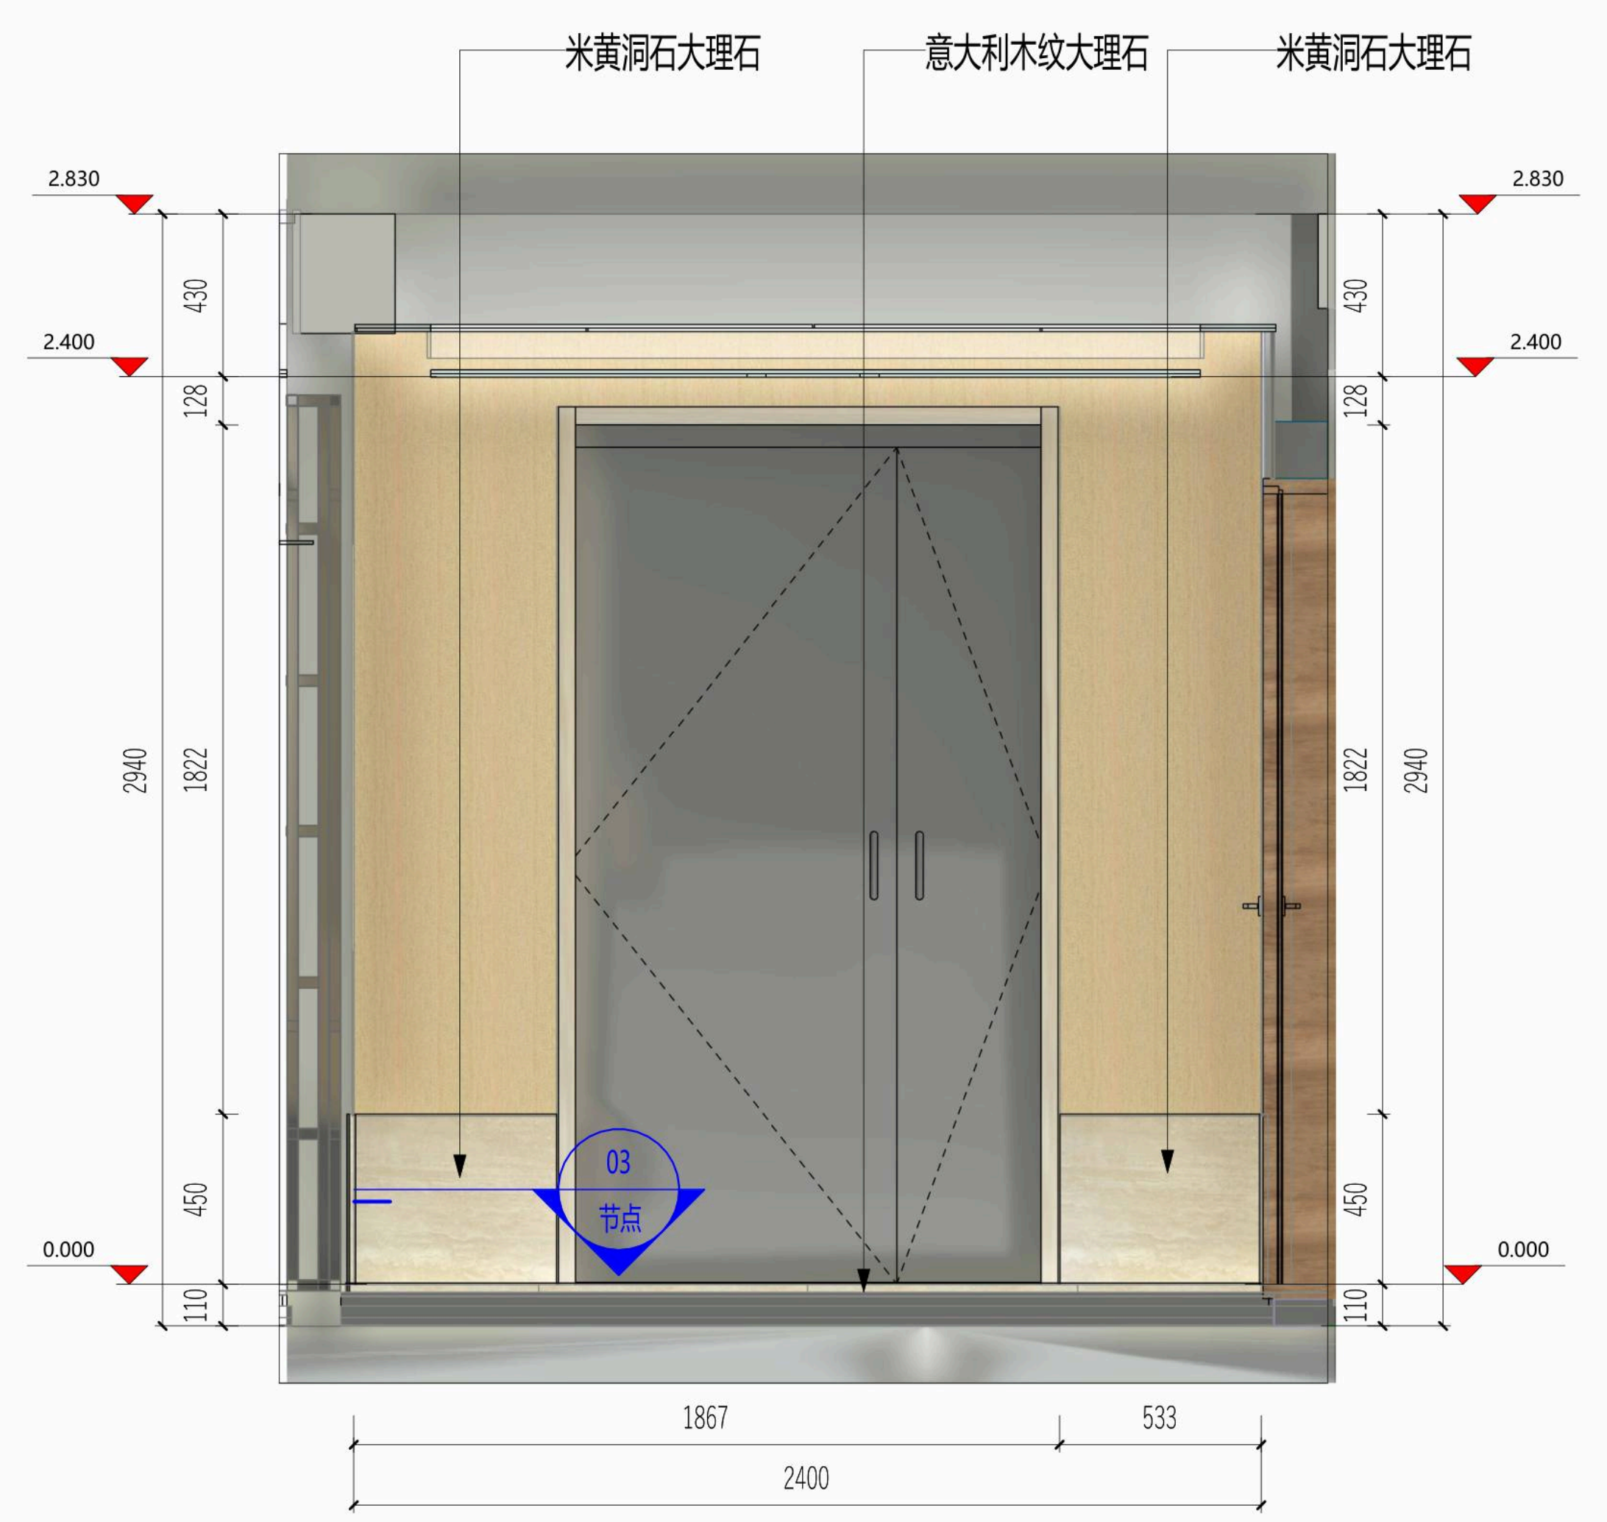
米黄洞石大理石
意大利木纹大理石
米黄洞石大理石
2.830
2.400
0.000
430
128
1822
450
110
2940
03
节点
1867
533
2400

公区地面-04

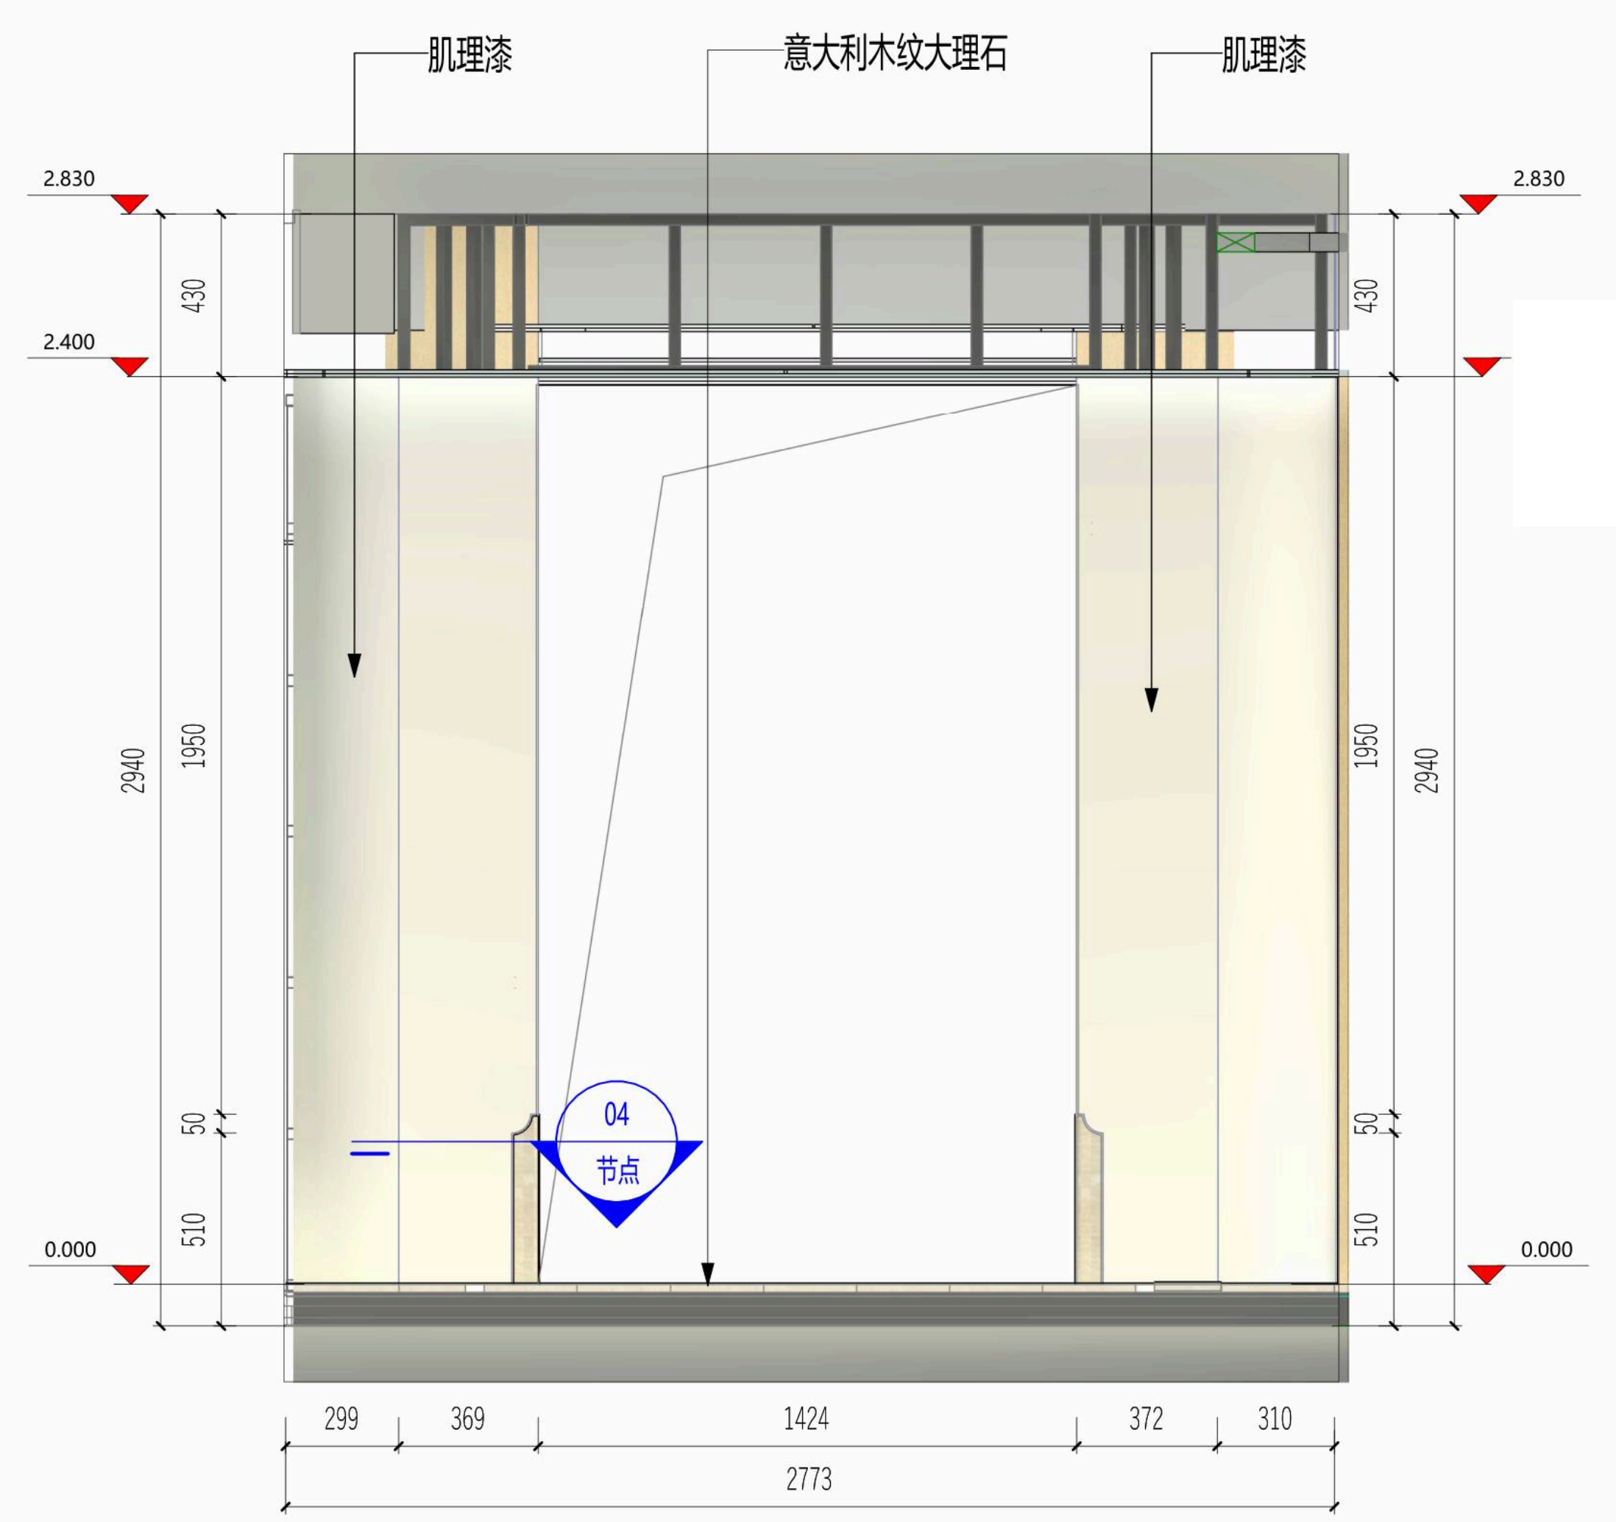
肌理漆
意大利木纹大理石
肌理漆
2.830
2.400
0.000
430
1950
50
510
2940
04
节点
299
369
1424
372
310
2773

公区地面-05

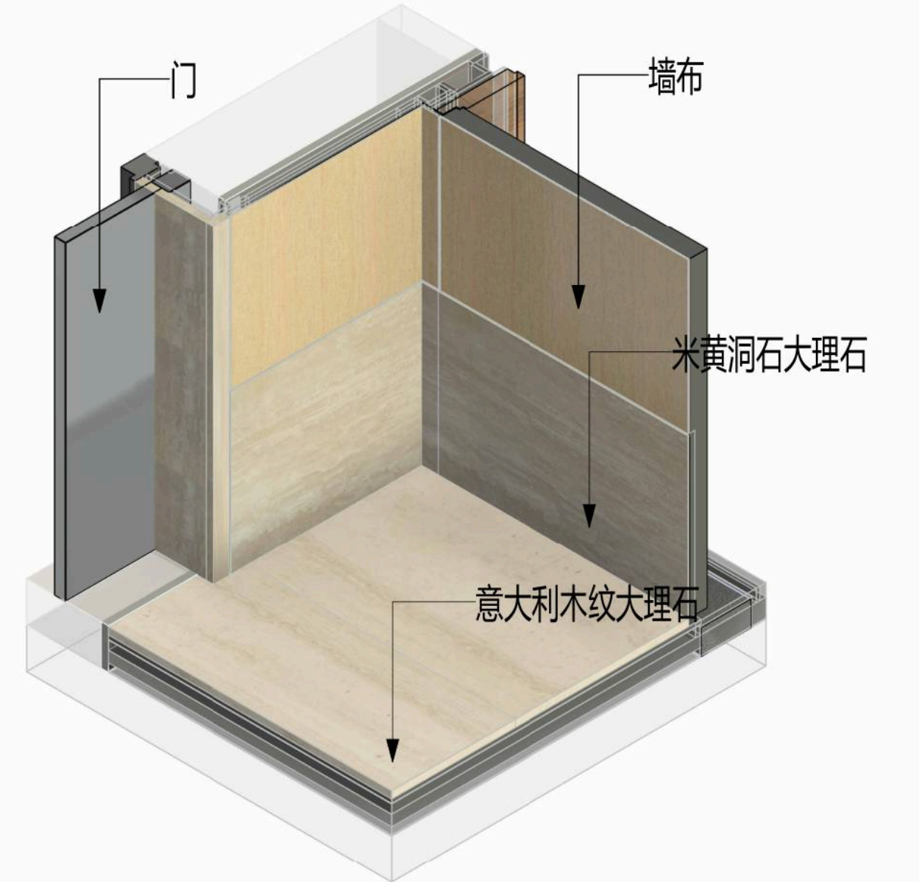
门
墙布
米黄洞石大理石
意大利木纹大理石

节点-01

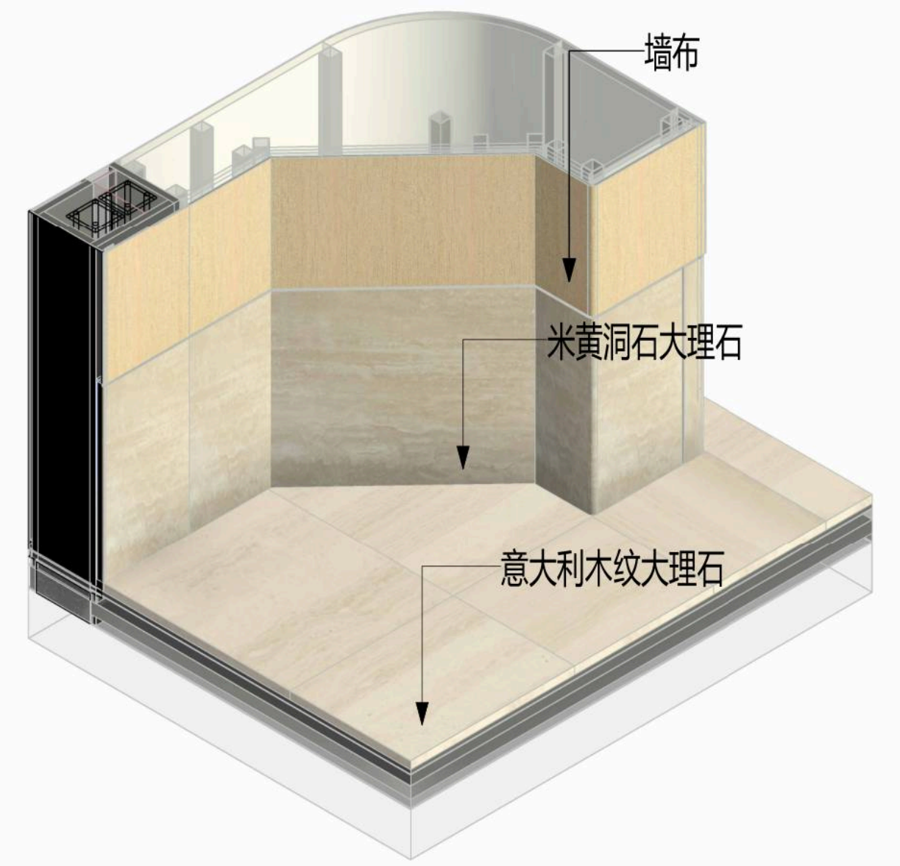
墙布
米黄洞石大理石
意大利木纹大理石

节点-02

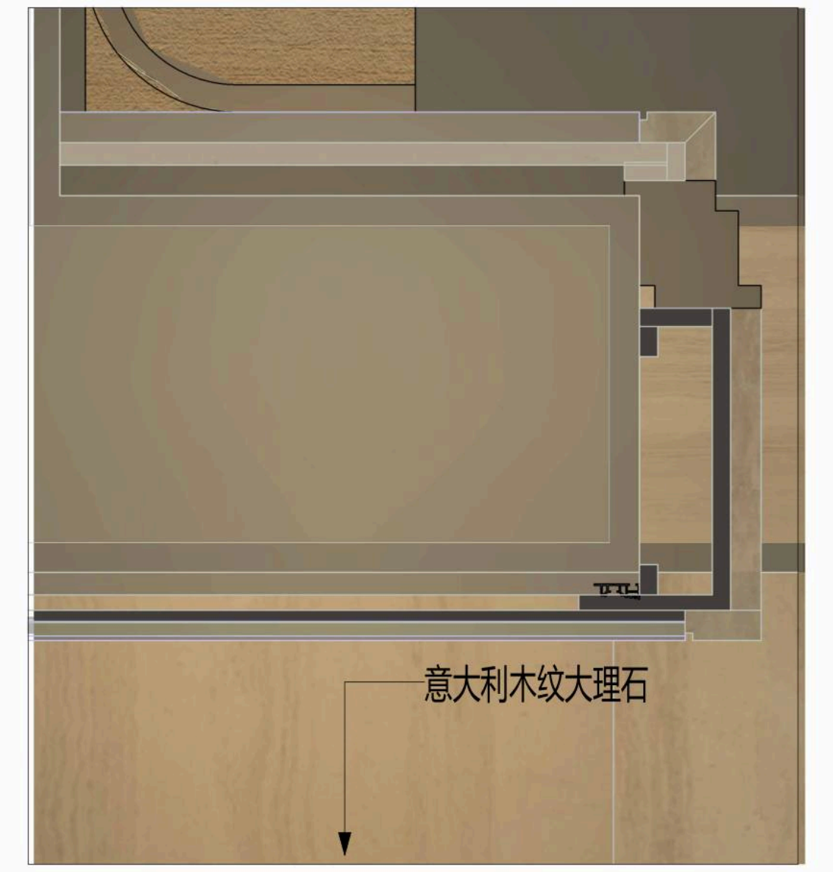

节点-03

节点-04

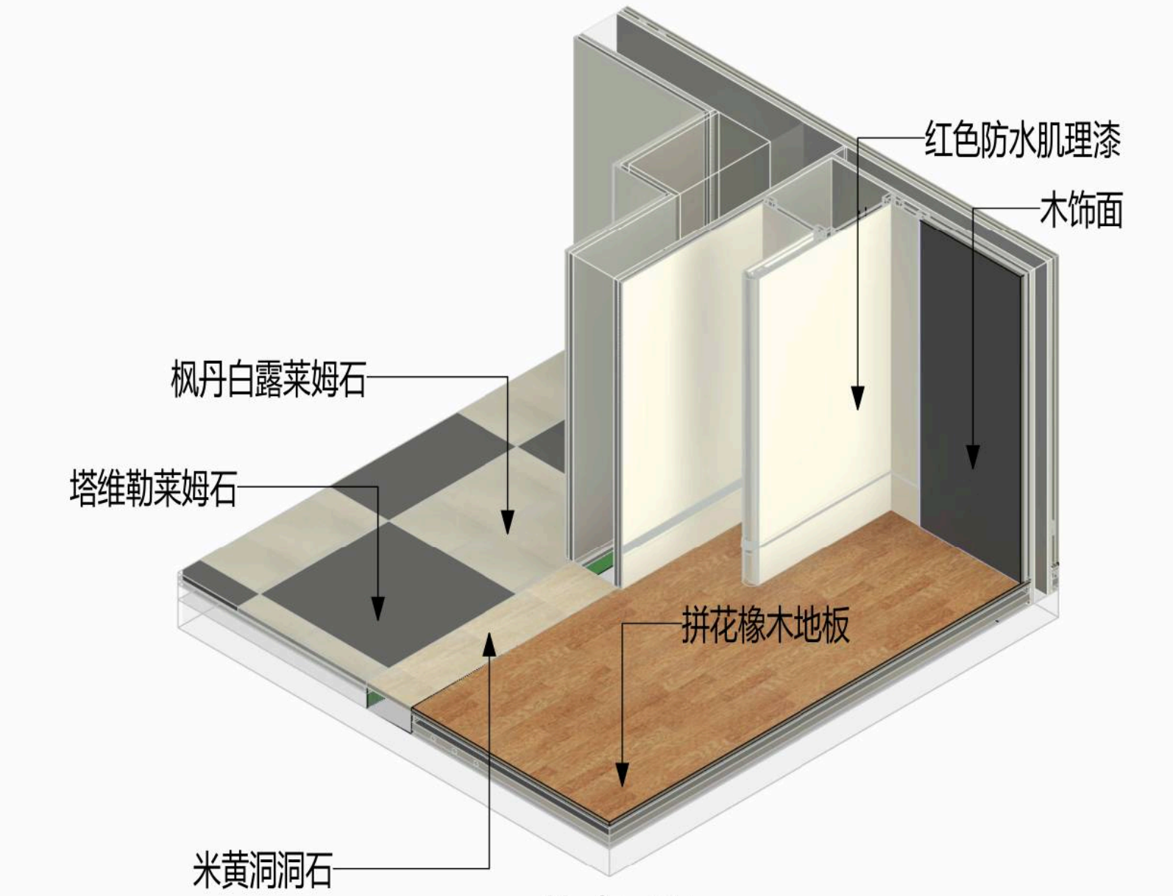
红色防水肌理漆
木饰面
枫丹白露莱姆石
塔维勒莱姆石
拼花橡木地板
米黄洞洞石

节点-05

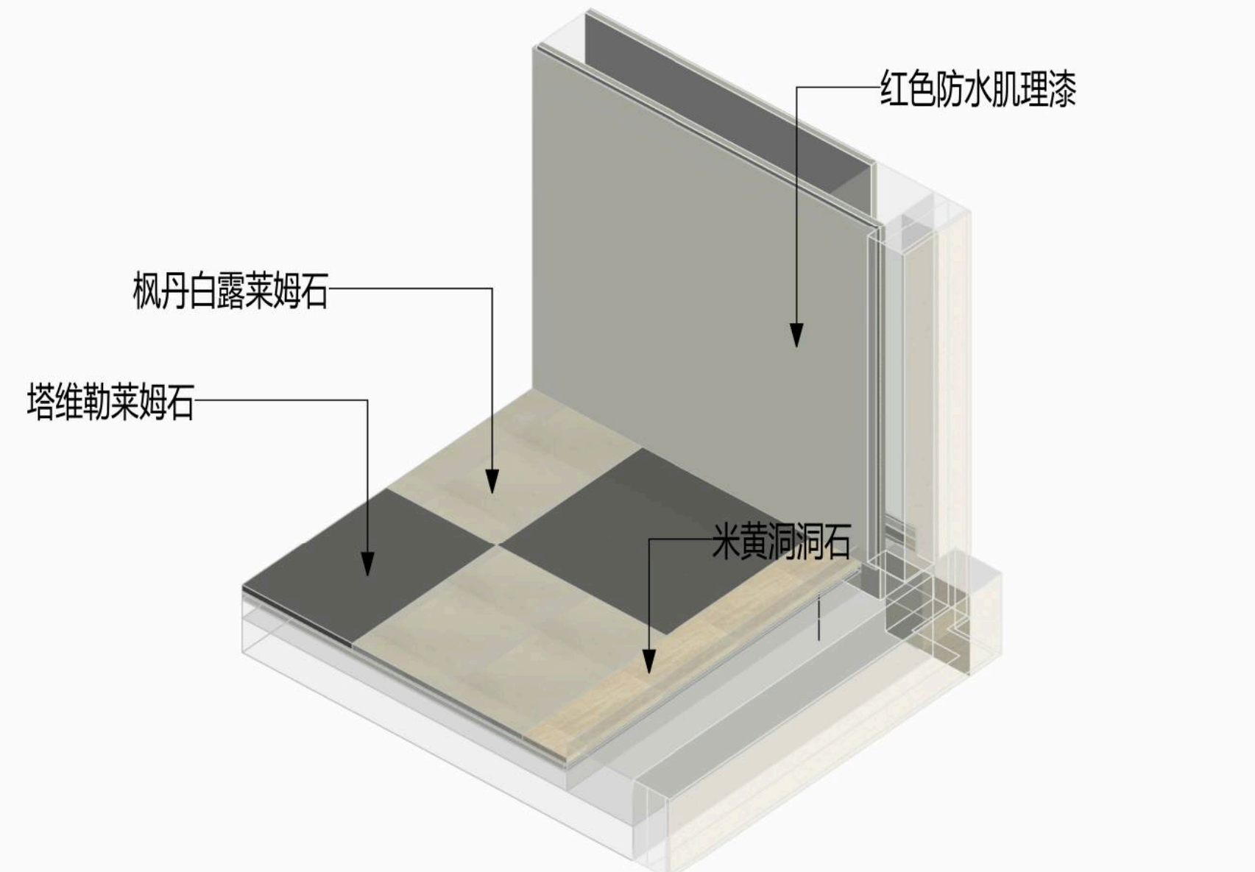
红色防水肌理漆
枫丹白露莱姆石
塔维勒莱姆石
米黄洞石

节点-06

编号	图例	名称
1	▨	丹枫白露大理石
2	▨	直纹白玉大理石
3	▨	米白色防水肌理漆
4	▨	红色防水肌理漆
5	▨	米黄洞石大理石
6	▨	伊朗绿大理石
7	▨	黑白根大理石
8	▨	意大利木纹
9	▨	白木纹石
10	▨	塔维勒莱姆石
11	▨	木饰面
12	▨	木地板
13	▨	墙布

盖章

注释
Notes
1.本图纸如与现场尺寸有误，请施工人员与项目负责人联系。
2.施工前施工人员应认真查阅此图，如有不明确尺寸，按现场测量为准。
3.本图纸必须经甲乙双方认可并签字方可作为施工依据。

日期
Date 05/20/26

修订
Revision
△1

项目
Project
潮映华岸府3-801

比例
Scale

公区地面石材铺贴

图纸编号
Drawing No.
ST-16

项目编号
Project No.

©2025