


DETAIL THINKING 细节构想

Master Bathroom
主卫

三维石材预安装

- 台盆细节构想
- 隔板及灯沟细节构想
- 墙面分隔细节构想
- 壁灯及镜子安装细节构想
- 插座点位分析
- 壁龛细节分析

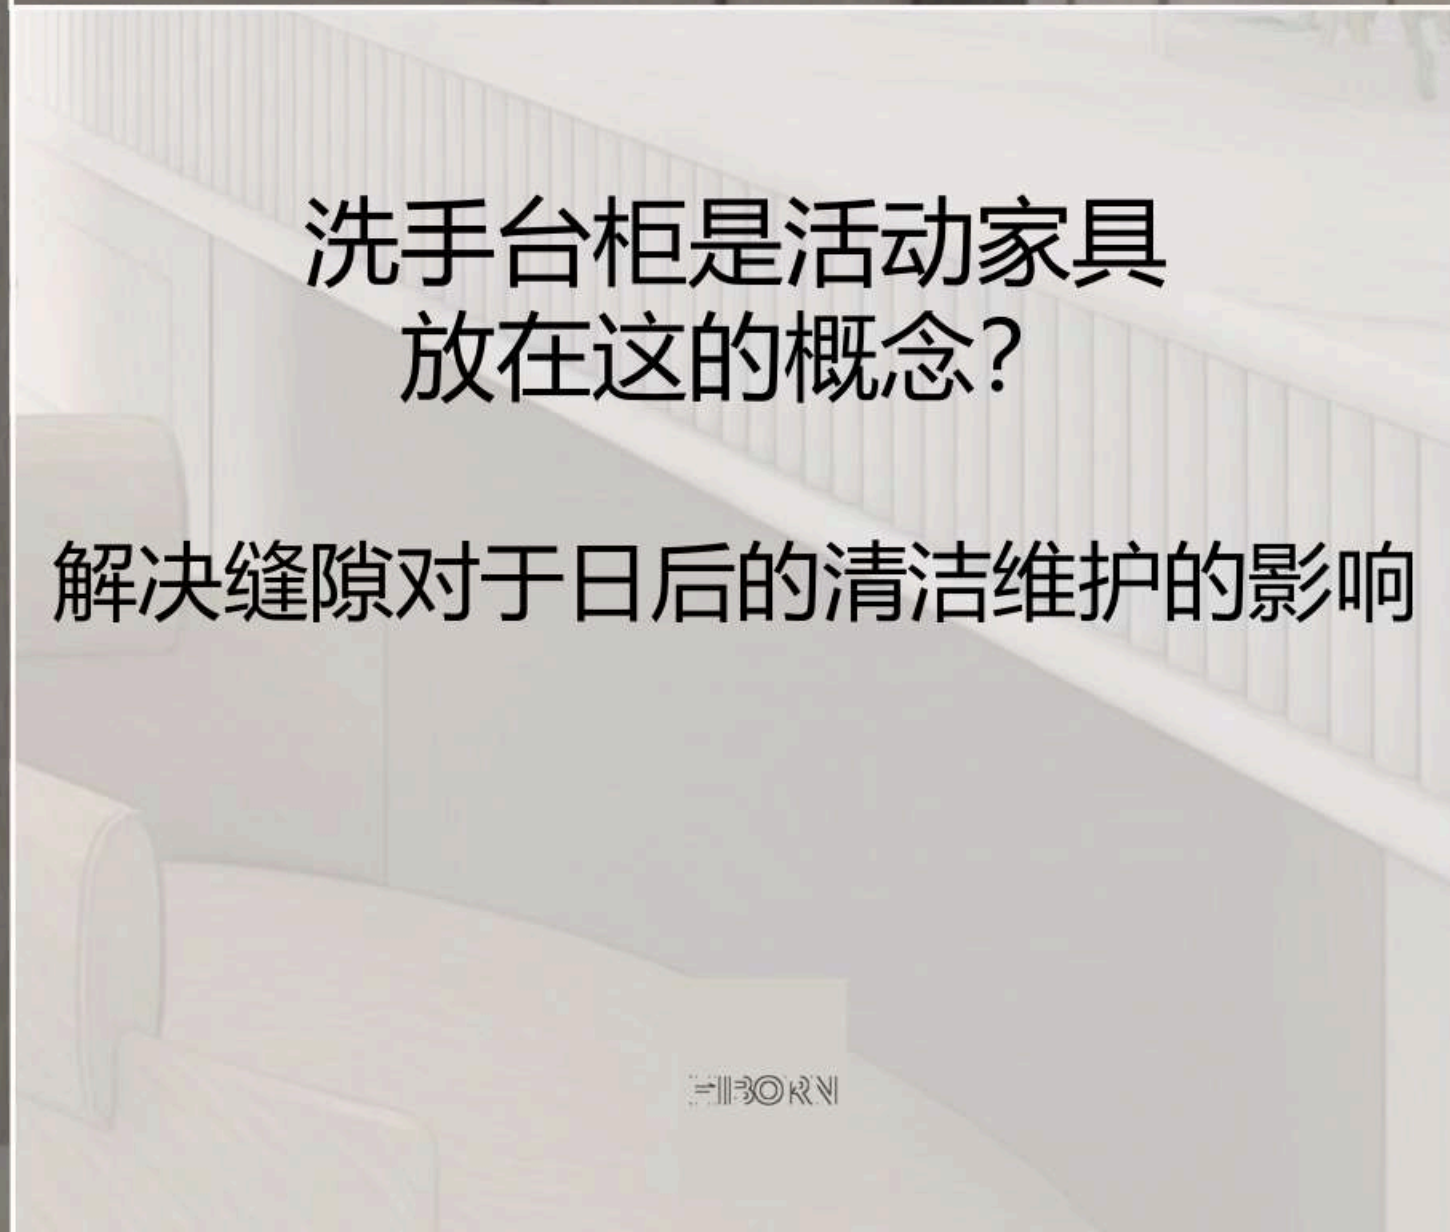


DETAIL THINKING 细节构想

Master Bathroom
主卫

- 台盆细节构想
- 隔板及灯沟细节构想
- 插座点位分析
- 壁龛细节分析
- 壁灯及镜子安装细节构想
- 淋浴房座凳细节
- 墙面分隔细节构想

三维石材预安装

台面缝隙进水解决方案

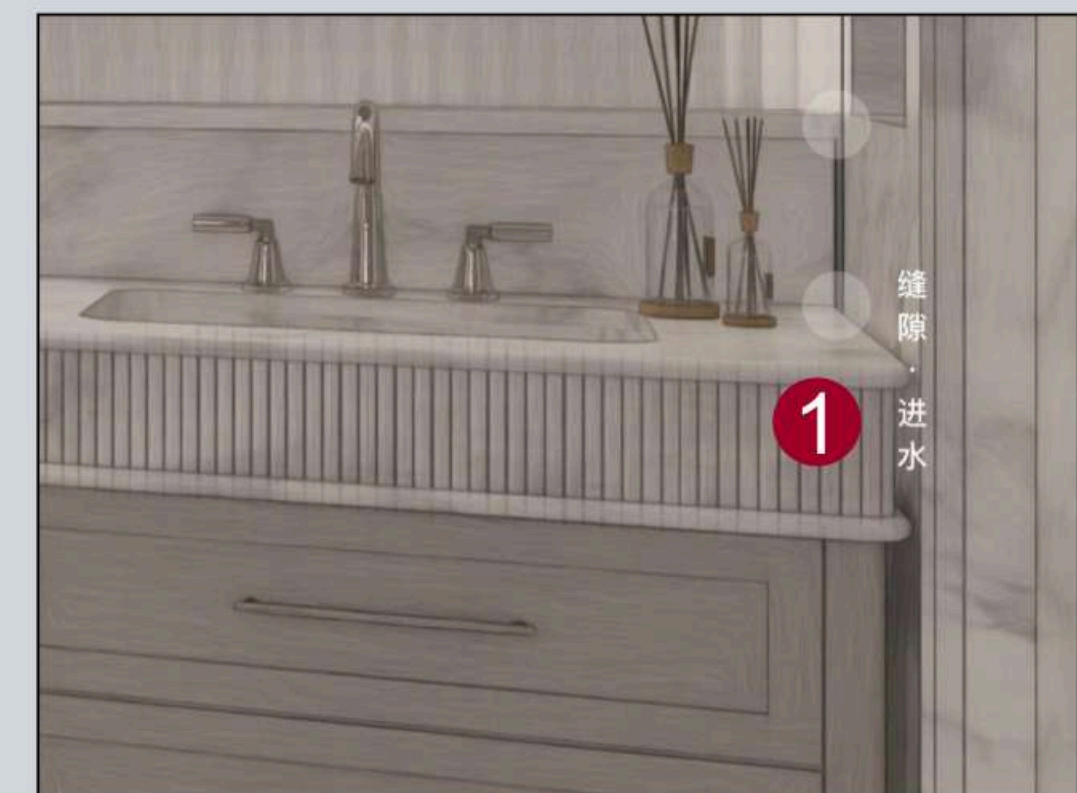

• 台面周围放坡挡水

• 台面和侧墙密接·无缝

• 腰线和侧墙密接·无缝

DETAIL THINKING 细节构想

Master Bathroom
主卫

- 台盆细节构想
- 隔板及灯沟细节构想
- 插座点位分析
- 壁龛细节分析
- 壁灯及镜子安装细节构想
- 淋浴房座凳细节
- 墙面分隔细节构想

侧面密封解决方案



• 柜子弧线背后为阶梯，封板盖在阶梯后方

• 石材或漆面封板

DETAIL THINKING 细节构想

Master Bathroom
主卫


- 台盆细节构想
- 隔板及灯沟细节构想
- 插座点位分析
- 壁龛细节分析
- 壁灯及镜子安装细节构想
- 淋浴房座凳细节
- 墙面分隔细节构想

三维石材预安装

台面防渗解决方案



挡水细节

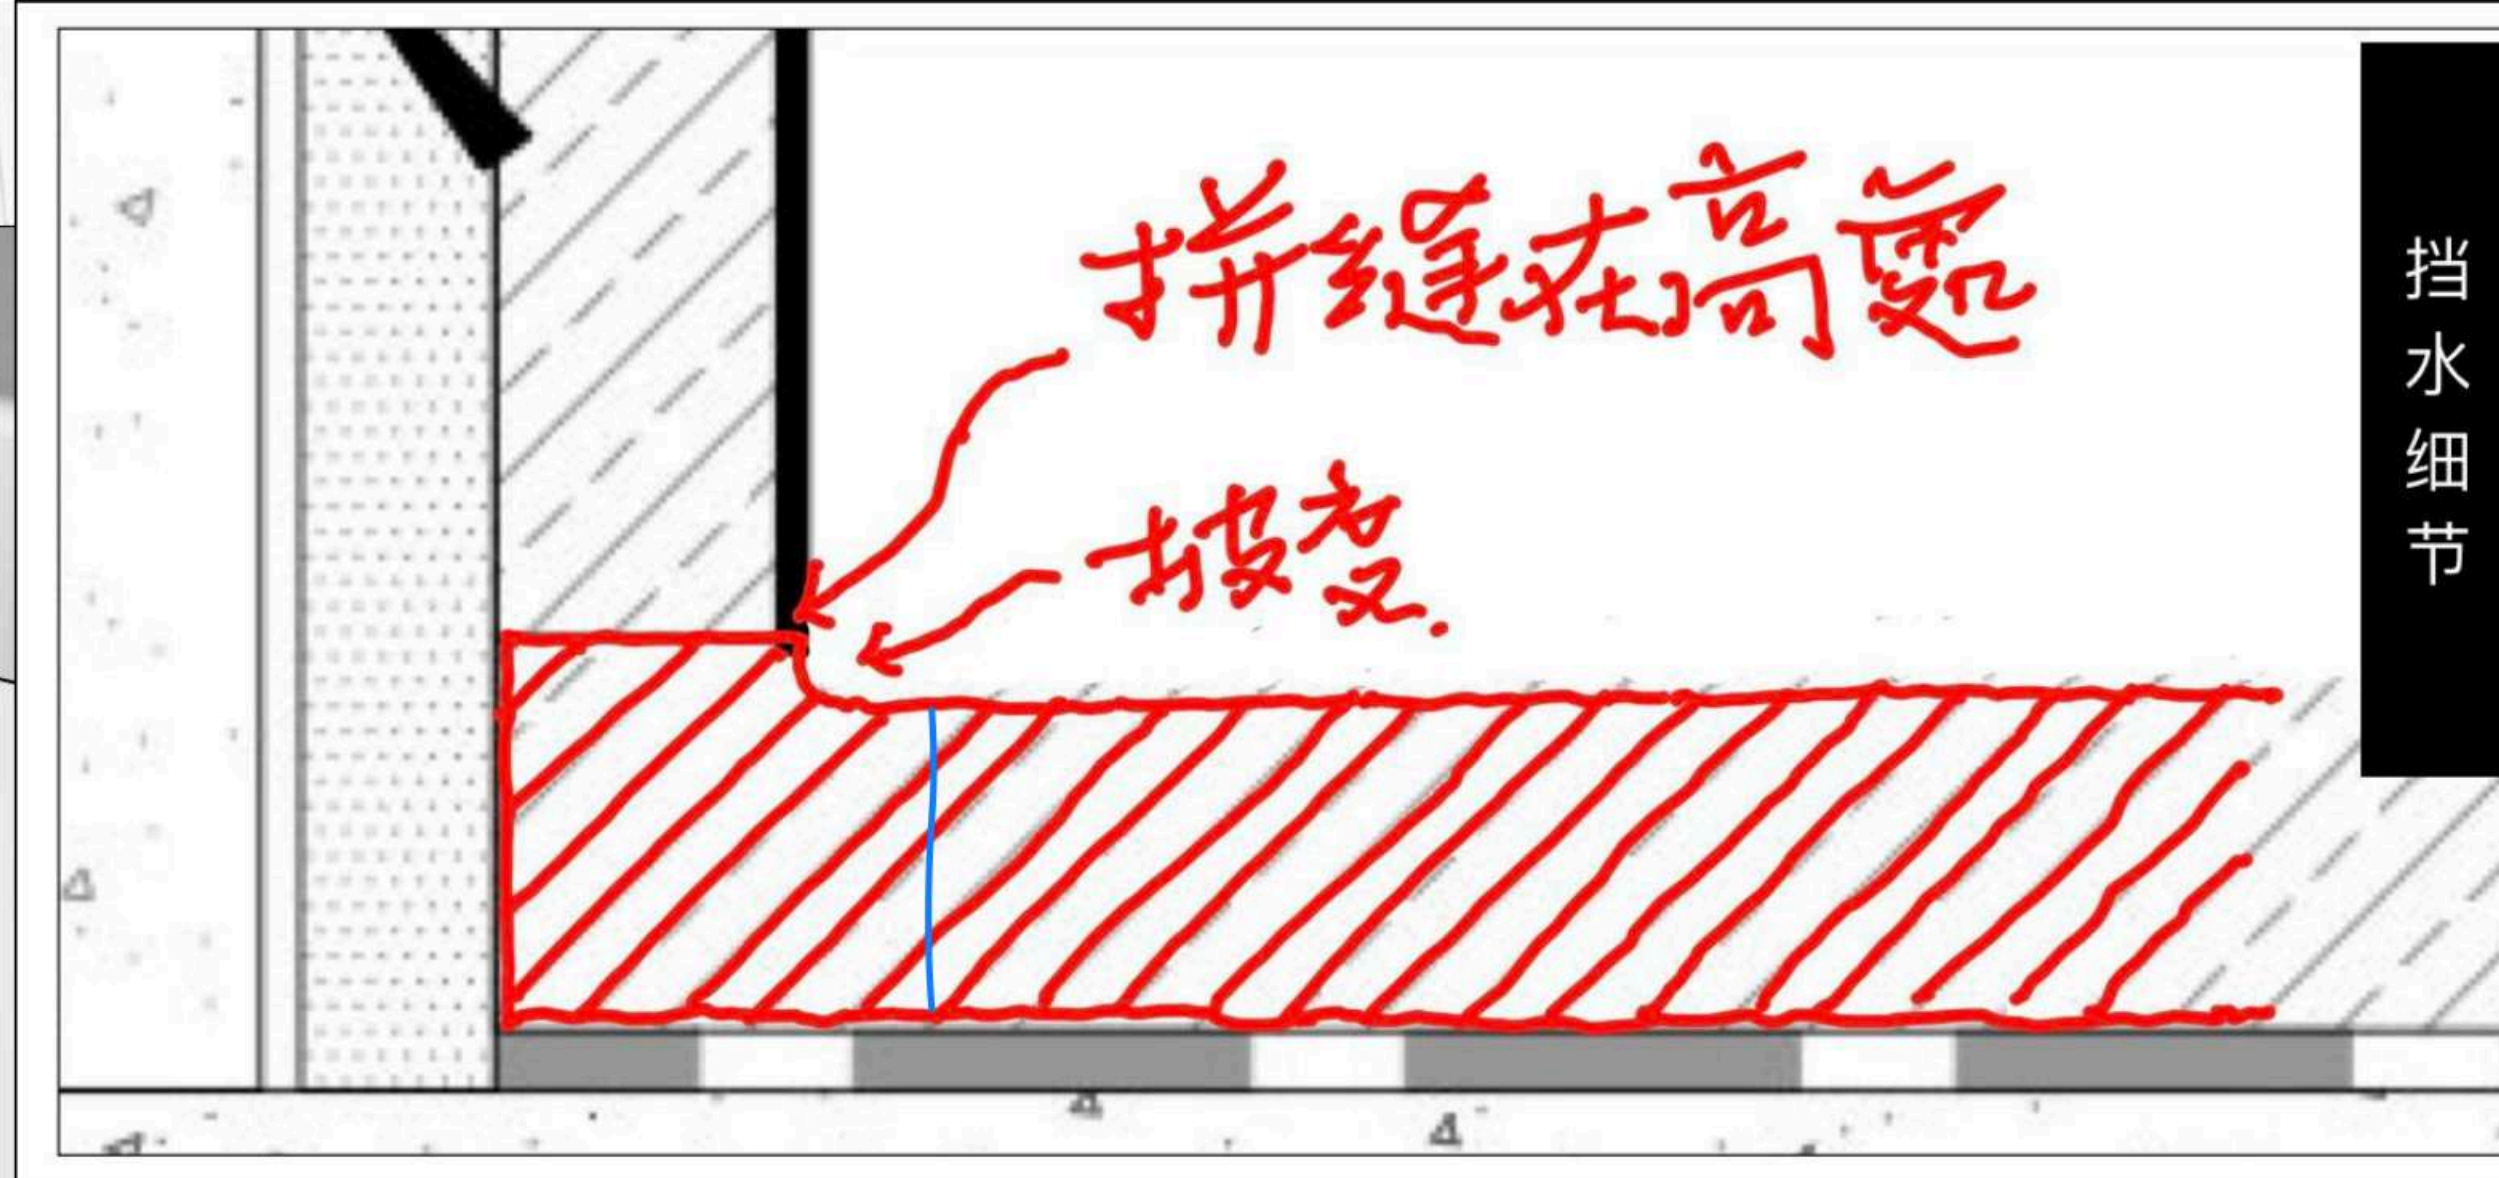

和墙面加厚，内层嵌板，让台面和立面石材碰接在高处


DETAIL THINKING 细节构想

Master Bathroom
主卫

- 台盆细节构想
- 隔板及灯沟细节构想
- 插座点位分析
- 壁龛细节分析
- 壁灯及镜子安装细节构想
- 淋浴房座凳细节
- 墙面分隔细节构想

三维石材预安装

立面及台面缝隙解决方案

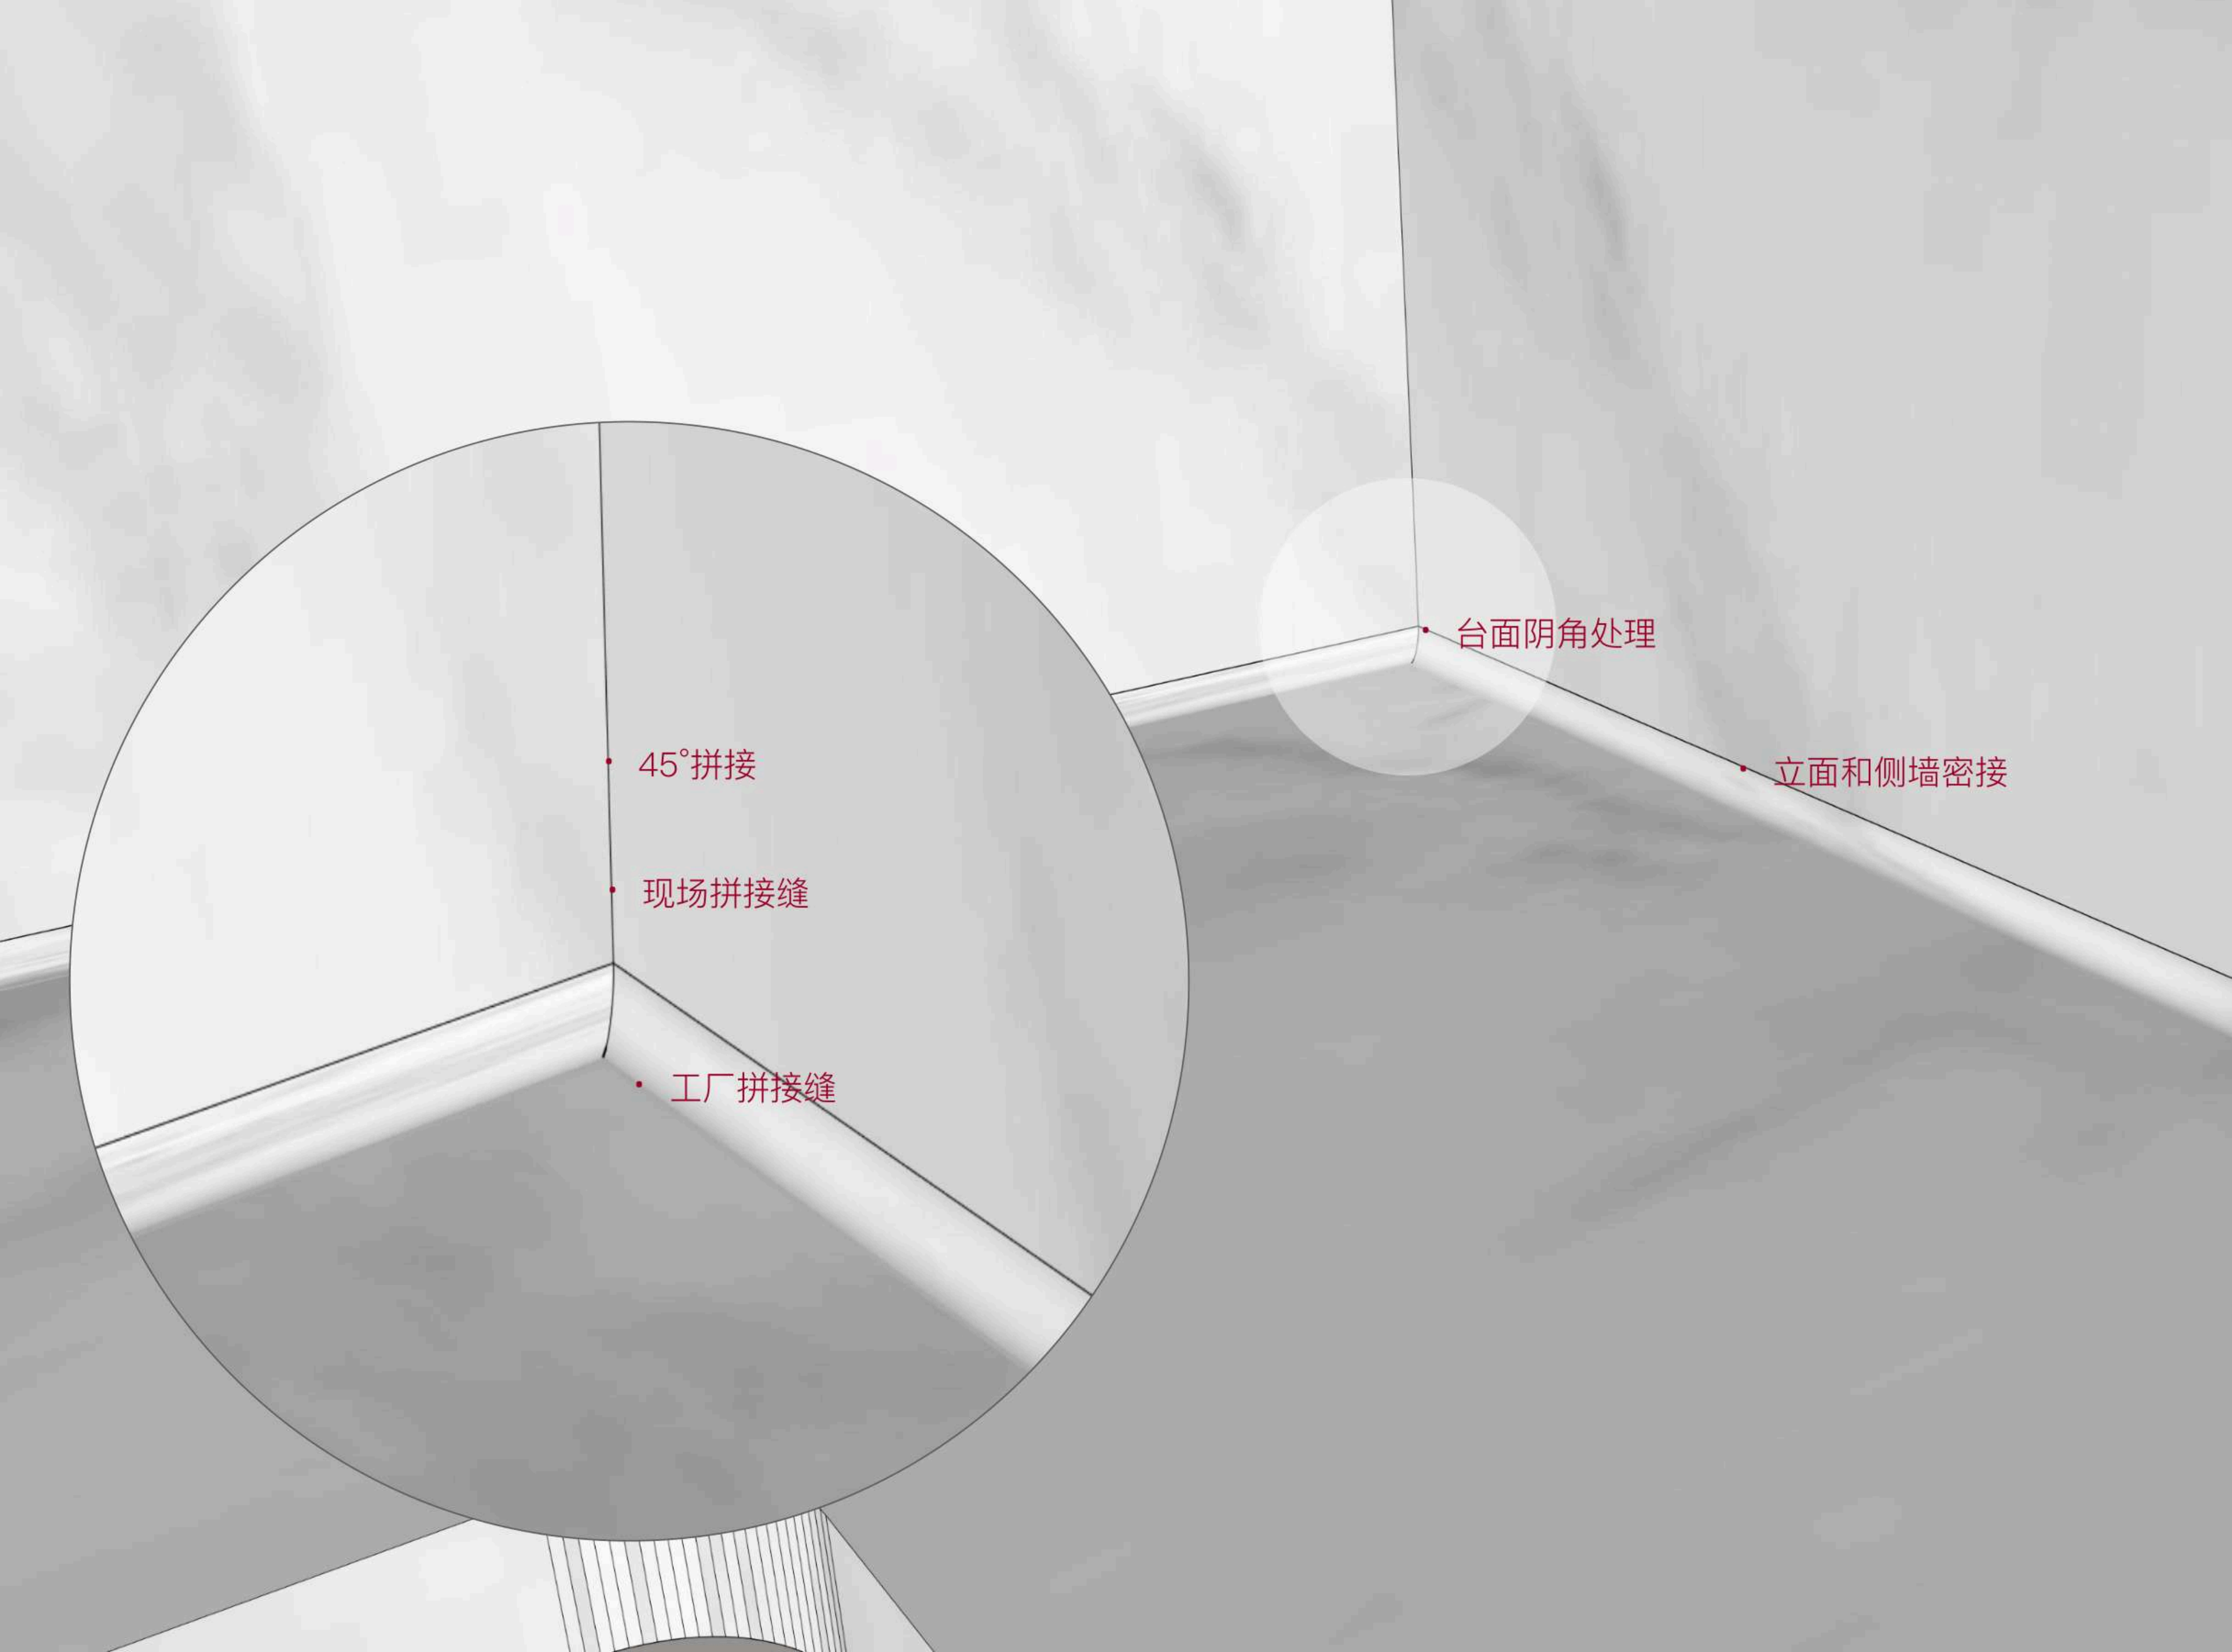



DETAIL THINKING 细节构想

Master Bathroom
主卫

- 台盆细节构想
- 隔板及灯沟细节构想
- 插座点位分析
- 壁龛细节分析
- 壁灯及镜子安装细节构想
- 淋浴房座凳细节
- 墙面分隔细节构想

三维石材预安装

台面及墙面节点拆分

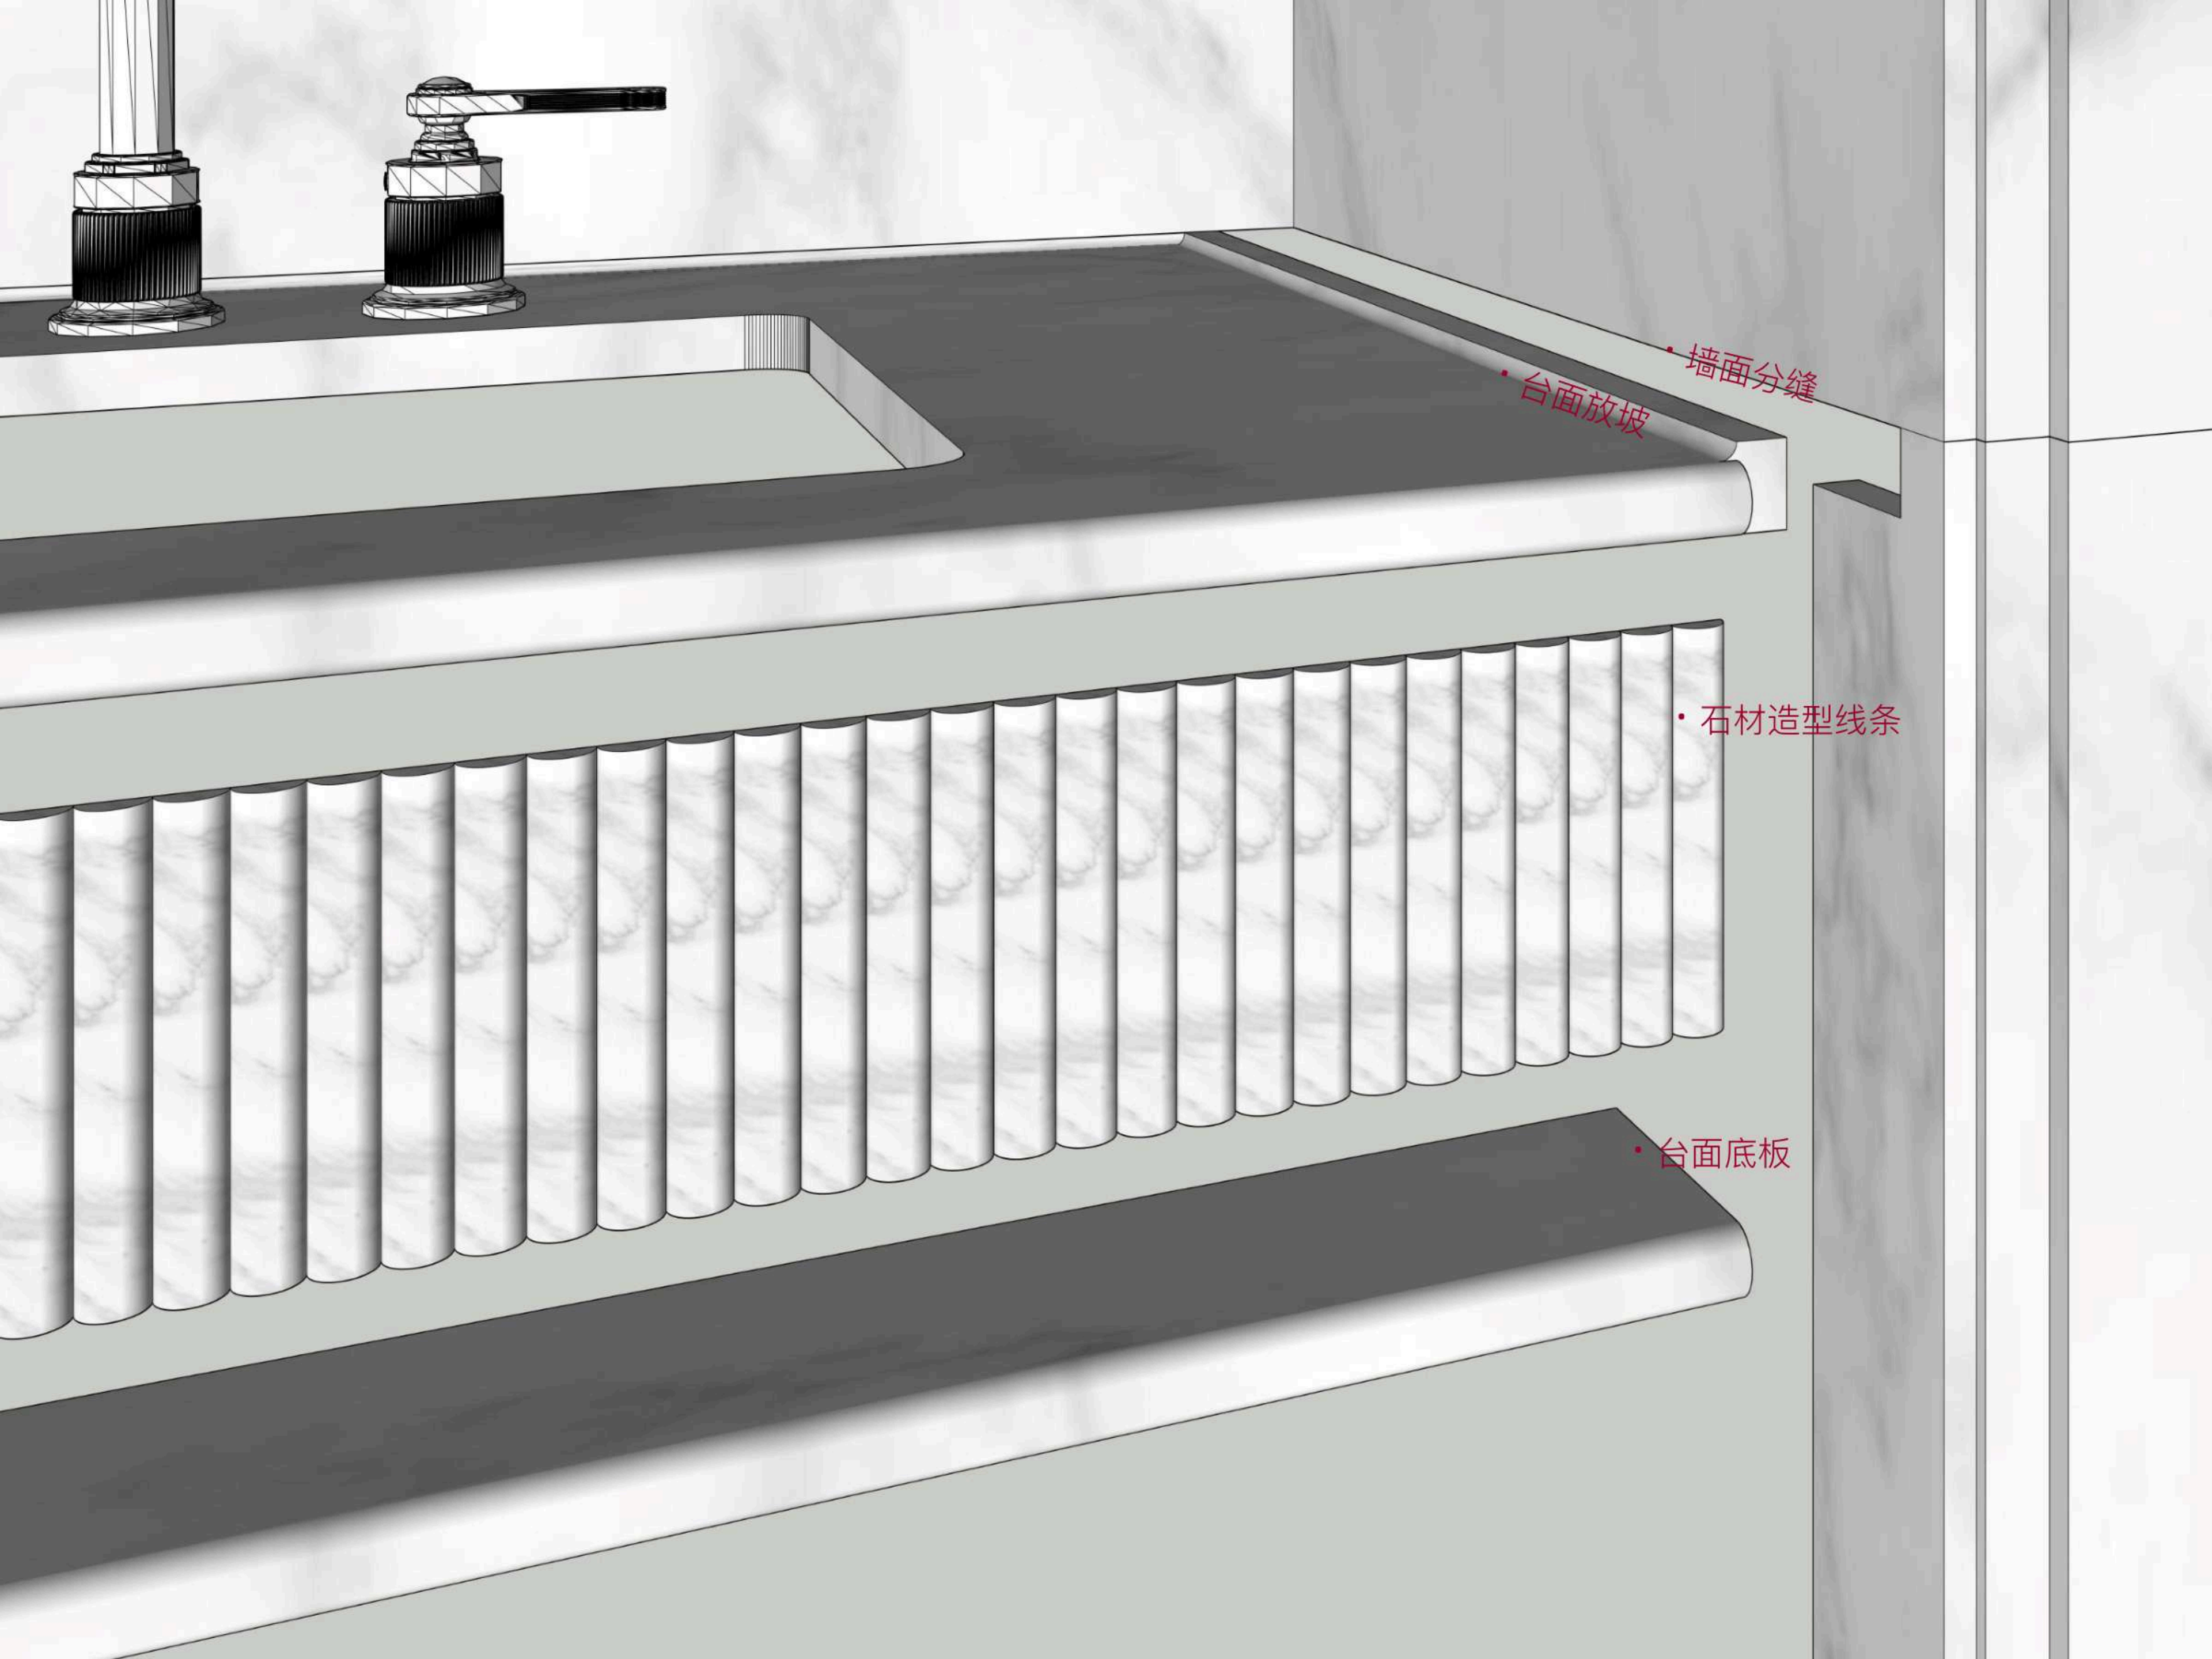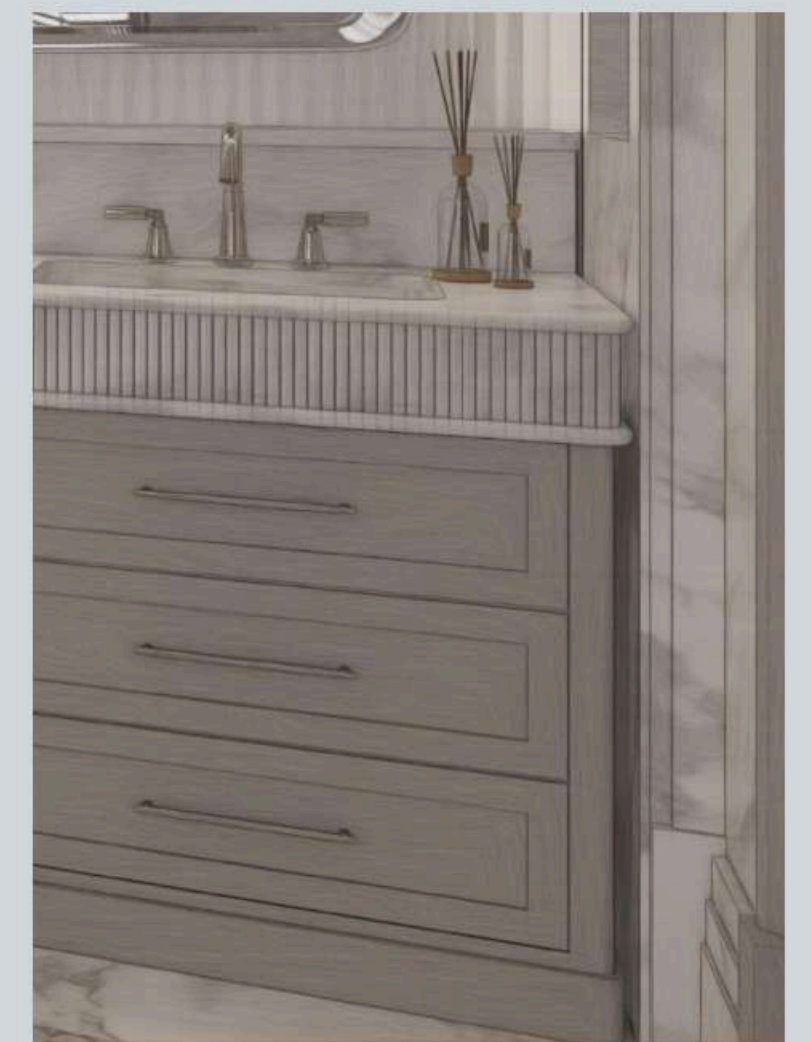

DETAIL THINKING 细节构想

Master Bathroom
主卫



- 台盆细节构想
- 隔板及灯沟细节构想
- 插座点位分析
- 壁龛细节分析
- 壁灯及镜子安装细节构想
- 淋浴房座凳细节
- 墙面分隔细节构想

三维石材预安装

龙头开启及安装分析

• 墙面层板对龙头开启安装无影响


隔板对龙头安装及提拉杆的使用无影响

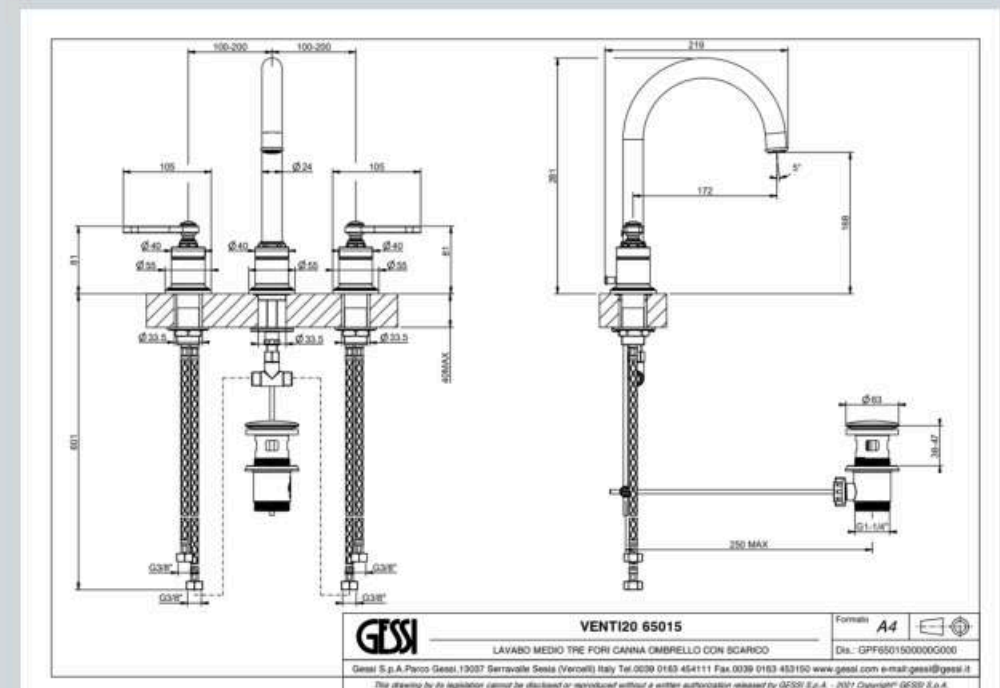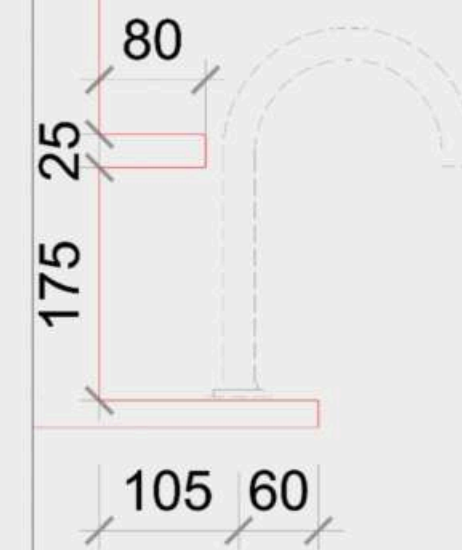


DETAIL THINKING 细节构想




Master Bathroom
主卫

- 台盆细节构想
- 隔板及灯沟细节构想
- 插座点位分析
- 壁龛细节分析
- 壁灯及镜子安装细节构想
- 淋浴房座凳细节
- 墙面分隔细节构想

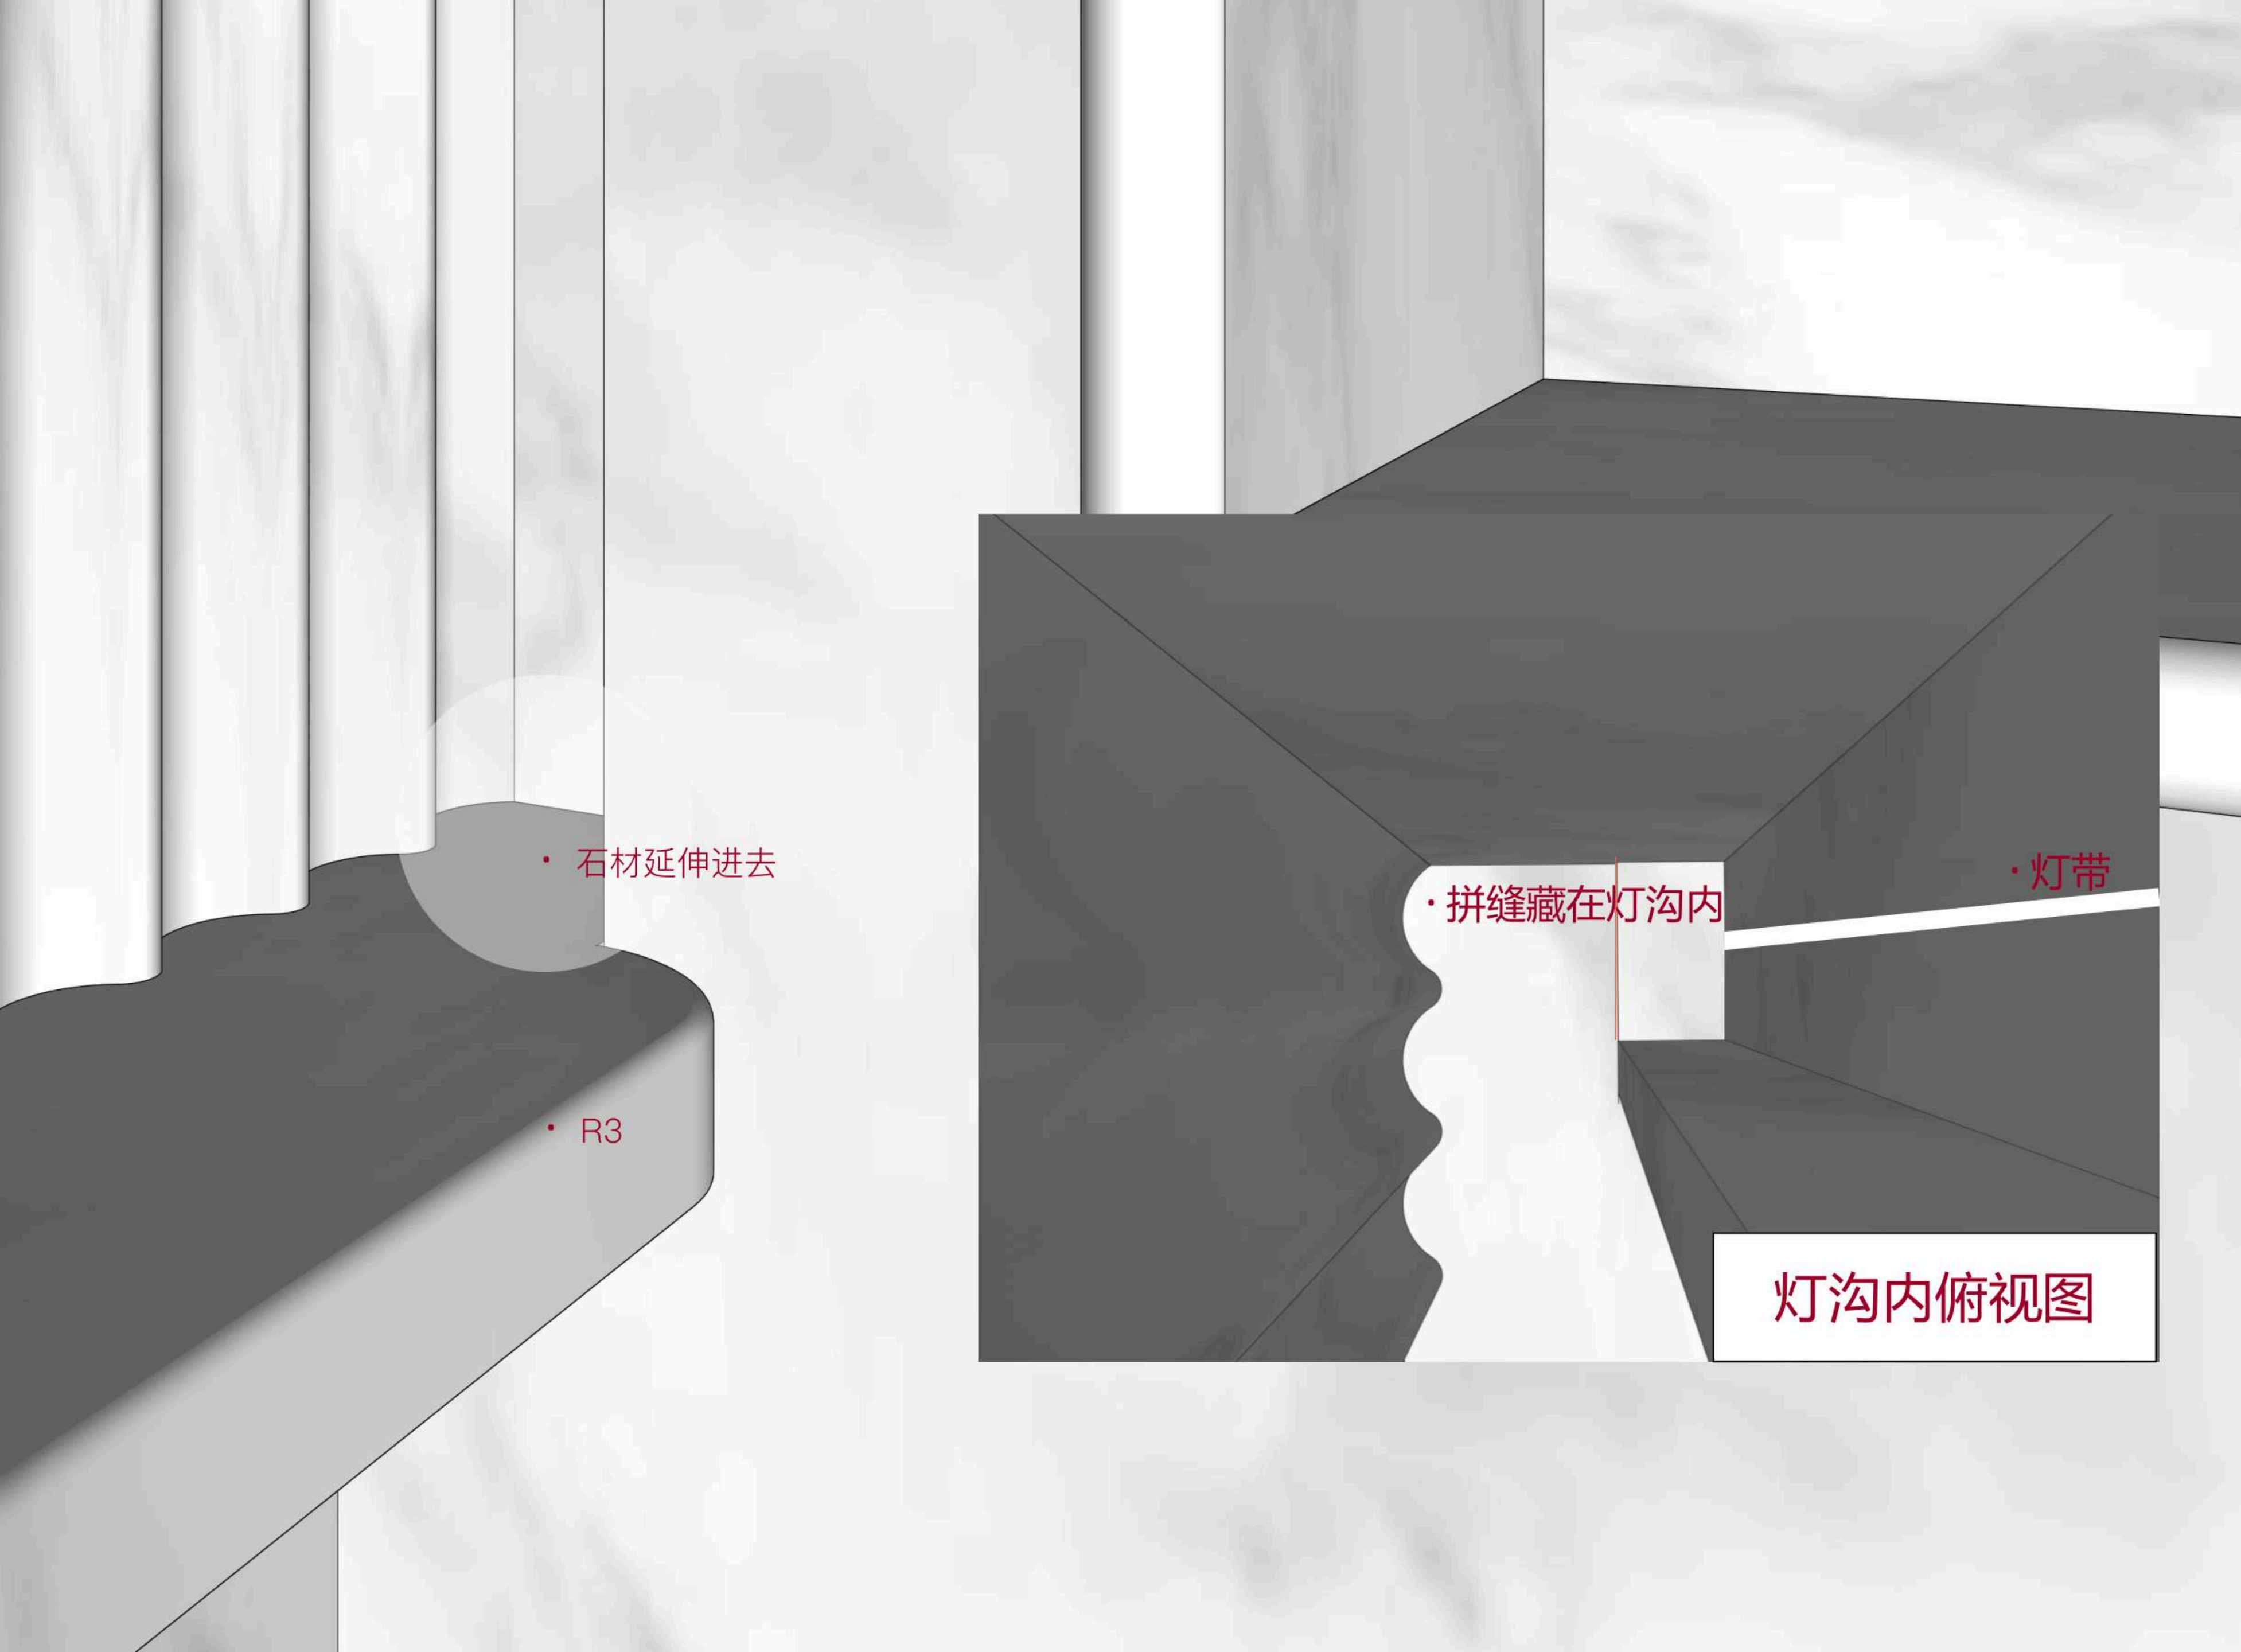

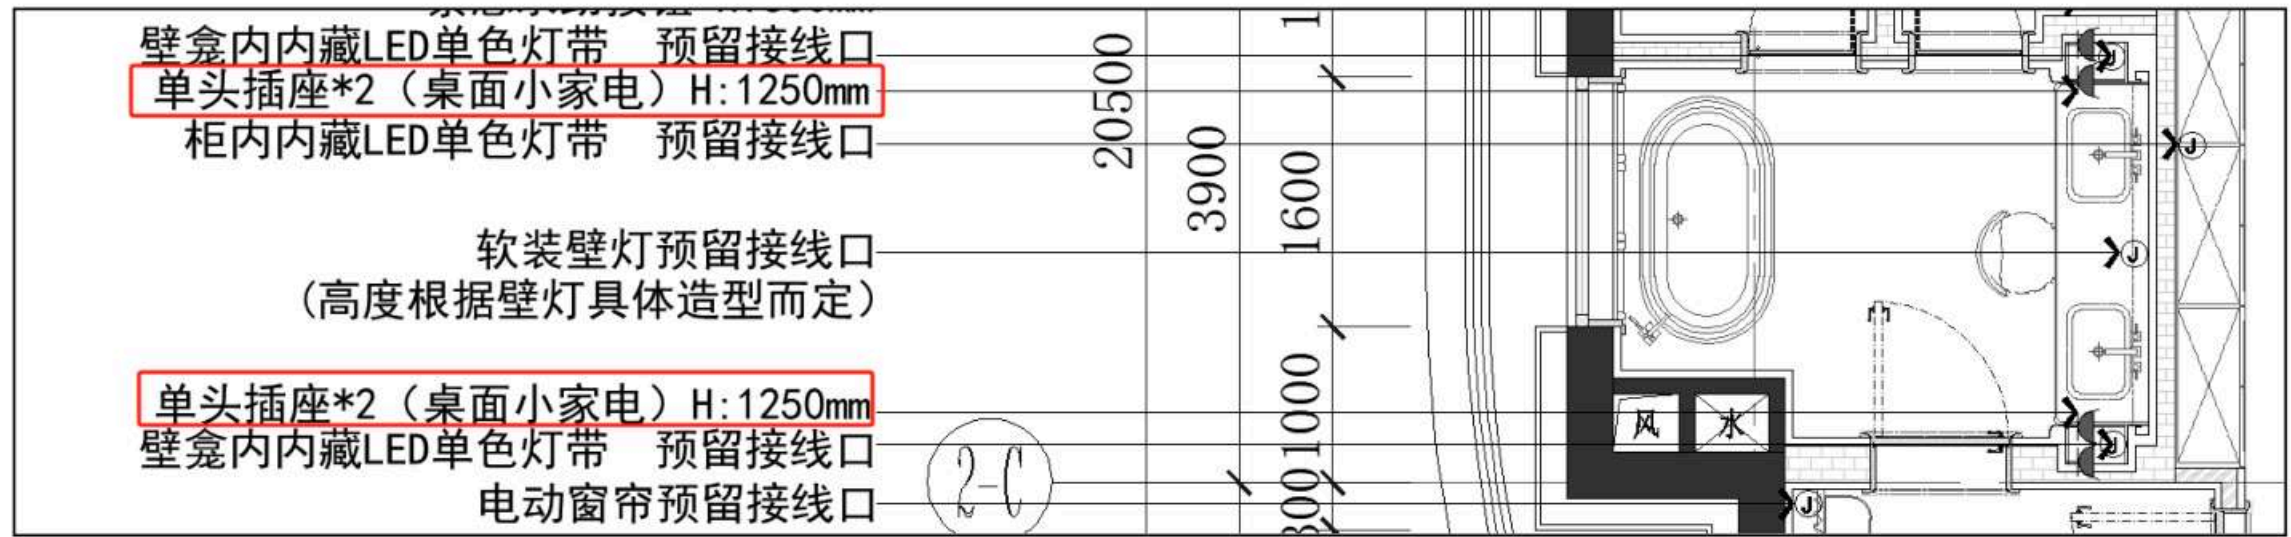

请明确壁龛插座安装位置

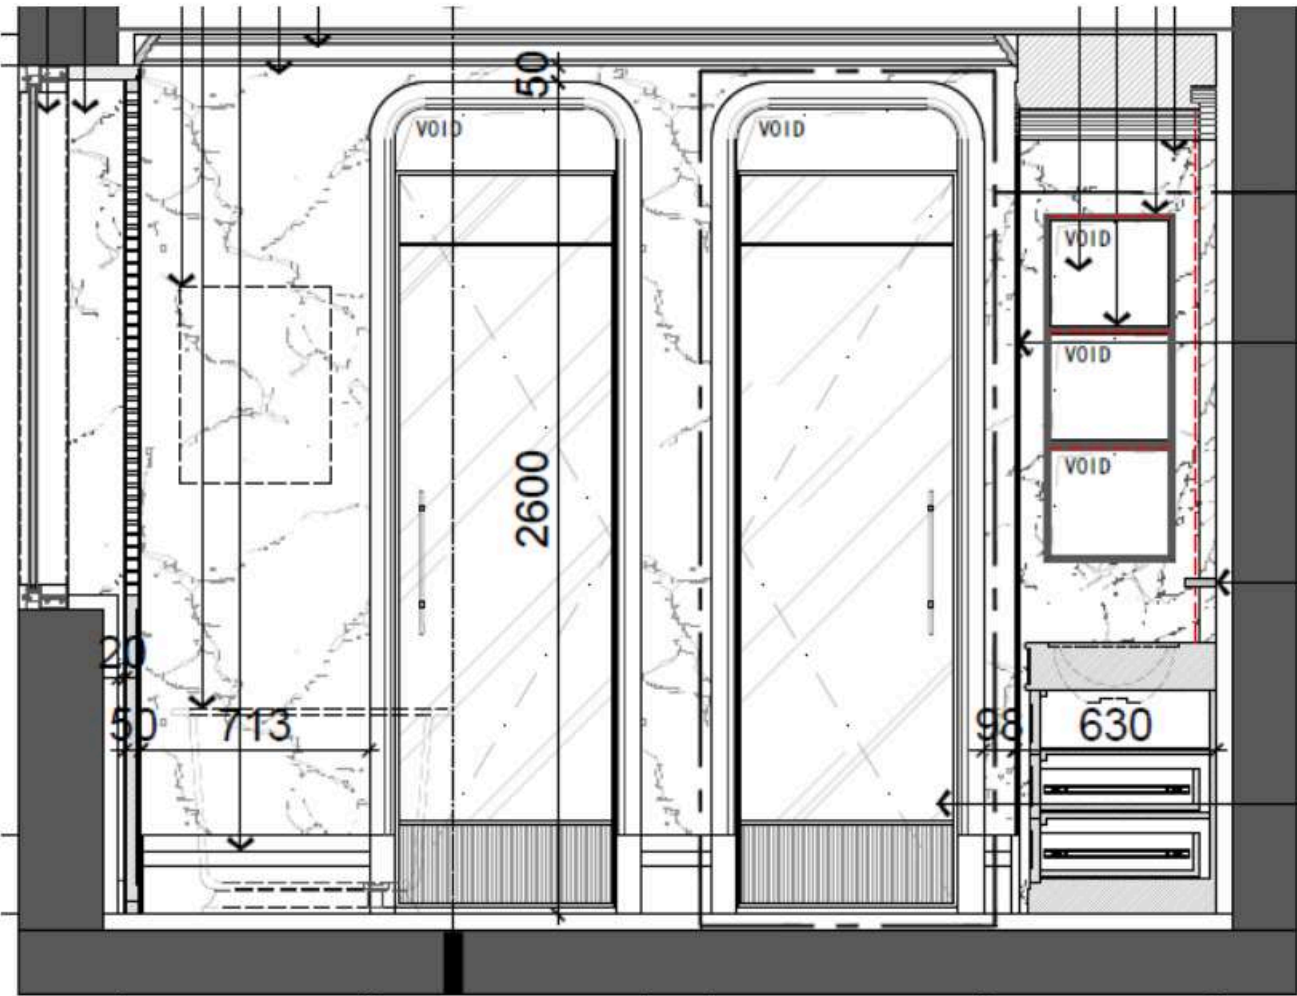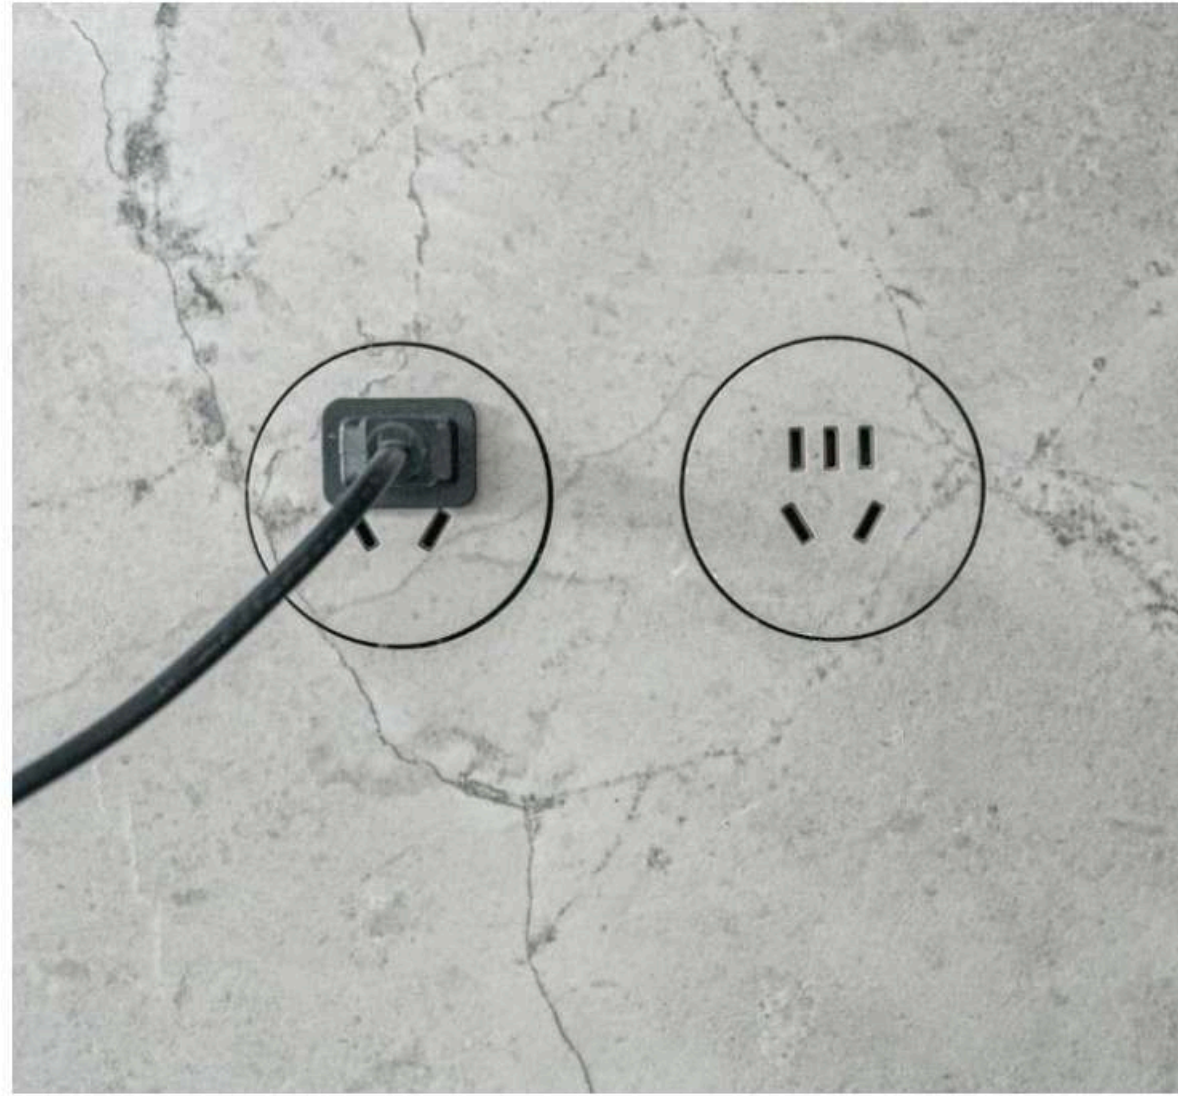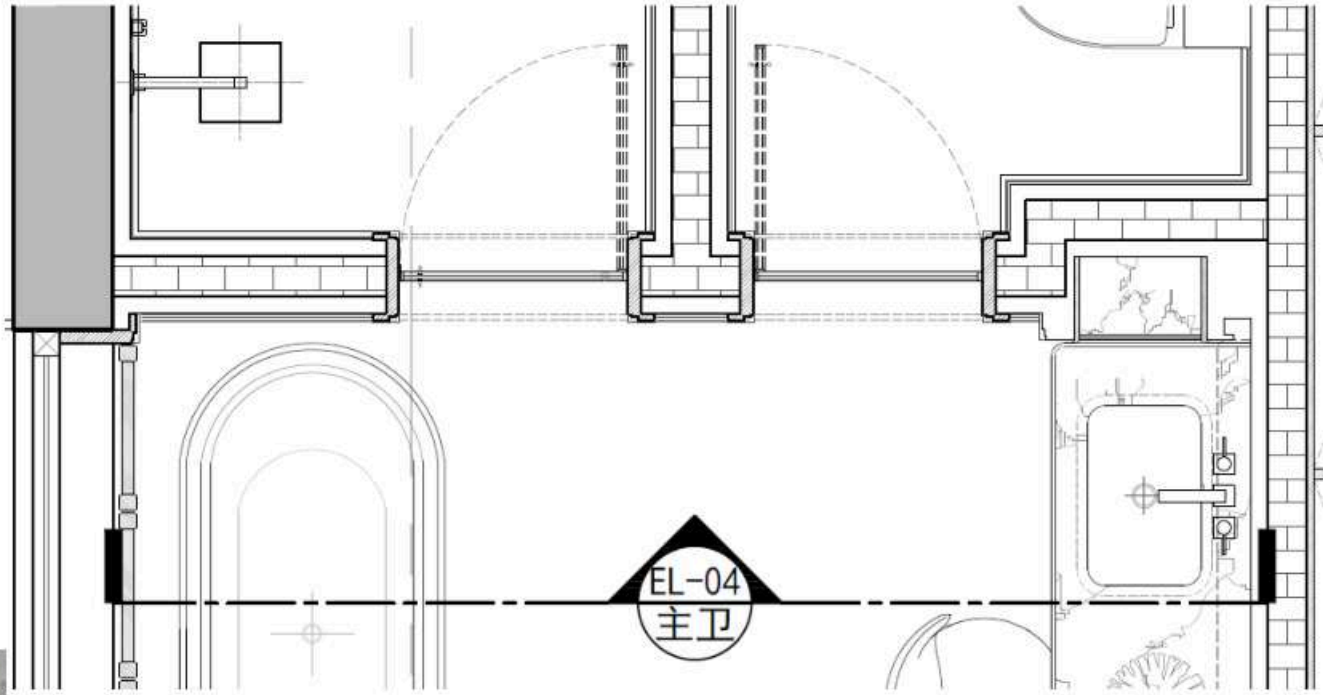

DETAIL THINKING 细节构想

Master Bathroom
主卫

- 台盆细节构想
- 隔板及灯沟细节构想
- 插座点位分析
- 壁龛细节分析
- 壁灯及镜子安装细节构想
- 淋浴房座凳细节
- 墙面分隔细节构想

三维石材预安装

插座点位分析




DETAIL THINKING 细节构想

Master Bathroom
主卫

- 台盆细节构想
- 隔板及灯沟细节构想
- 插座点位分析
- **壁龛细节分析**
- 壁灯及镜子安装细节构想
- 淋浴房座凳细节
- 墙面分隔细节构想

三维石材预安装


隔板与壁龛的关系分析

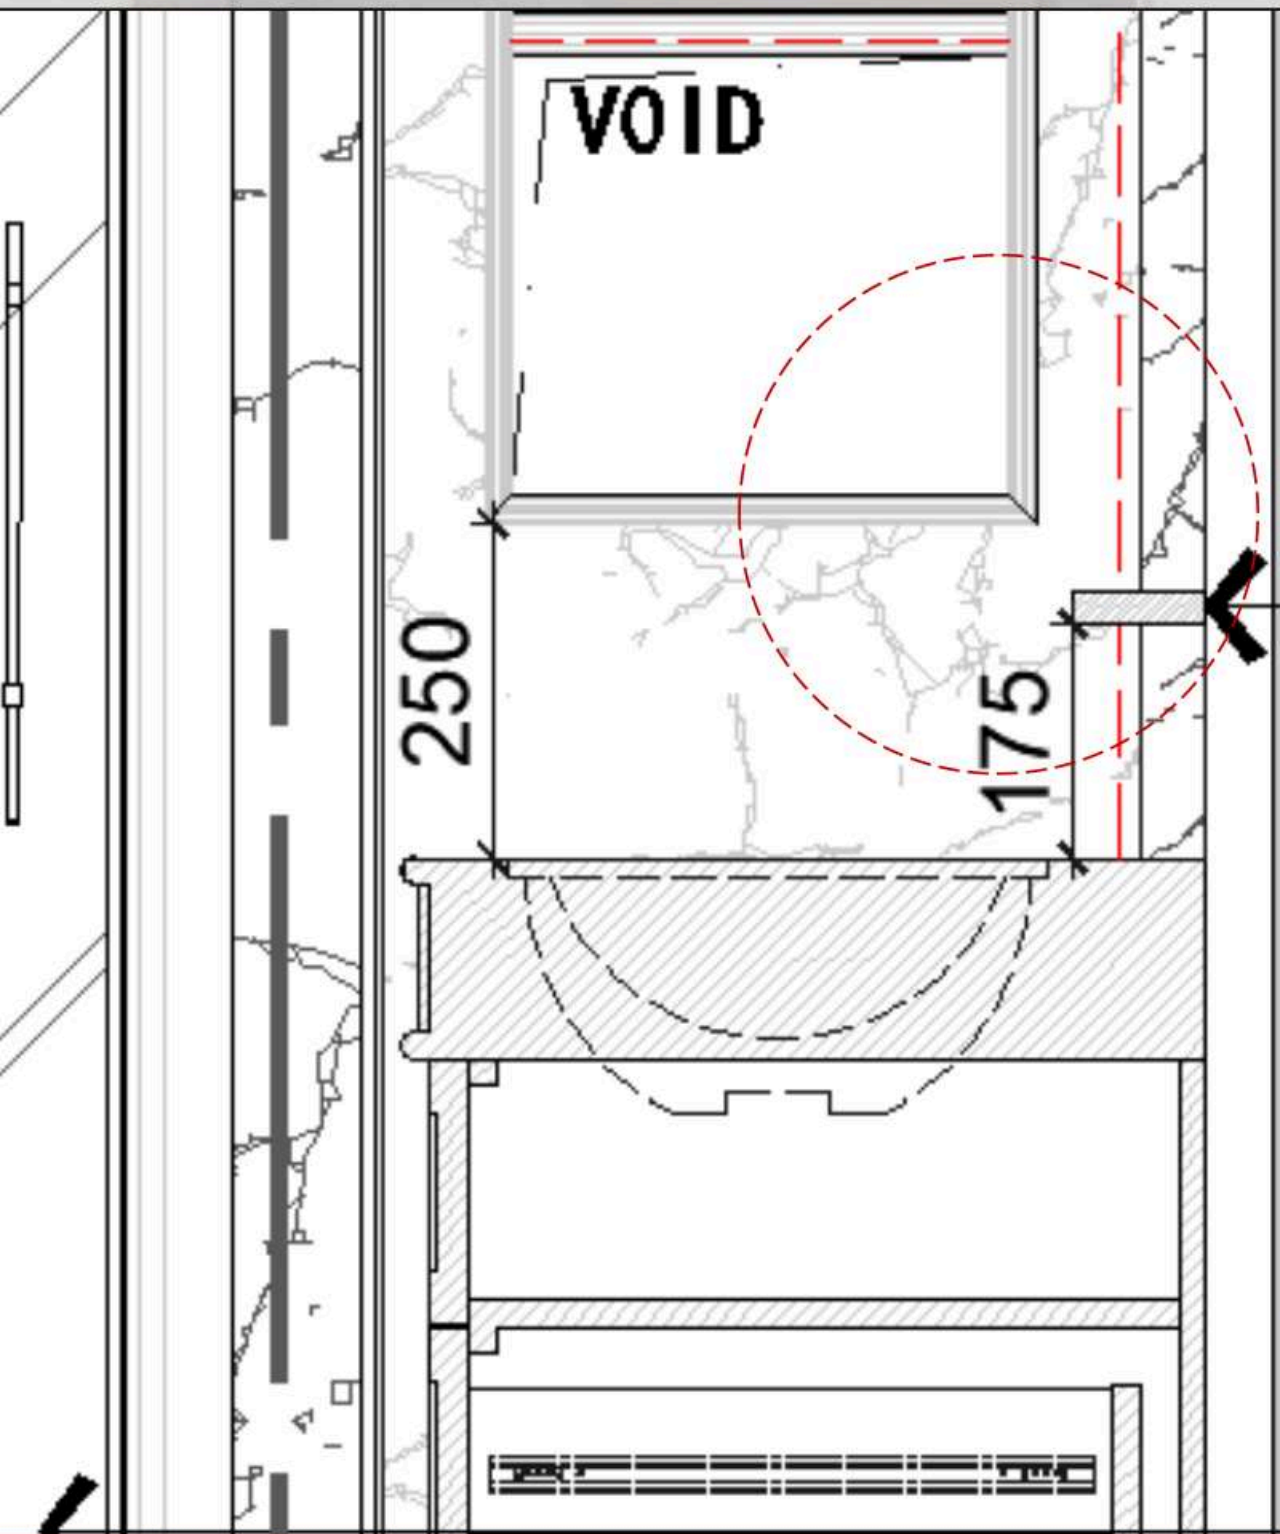

层板与壁龛施工图有高差



• 墙面层板与壁龛建议齐平

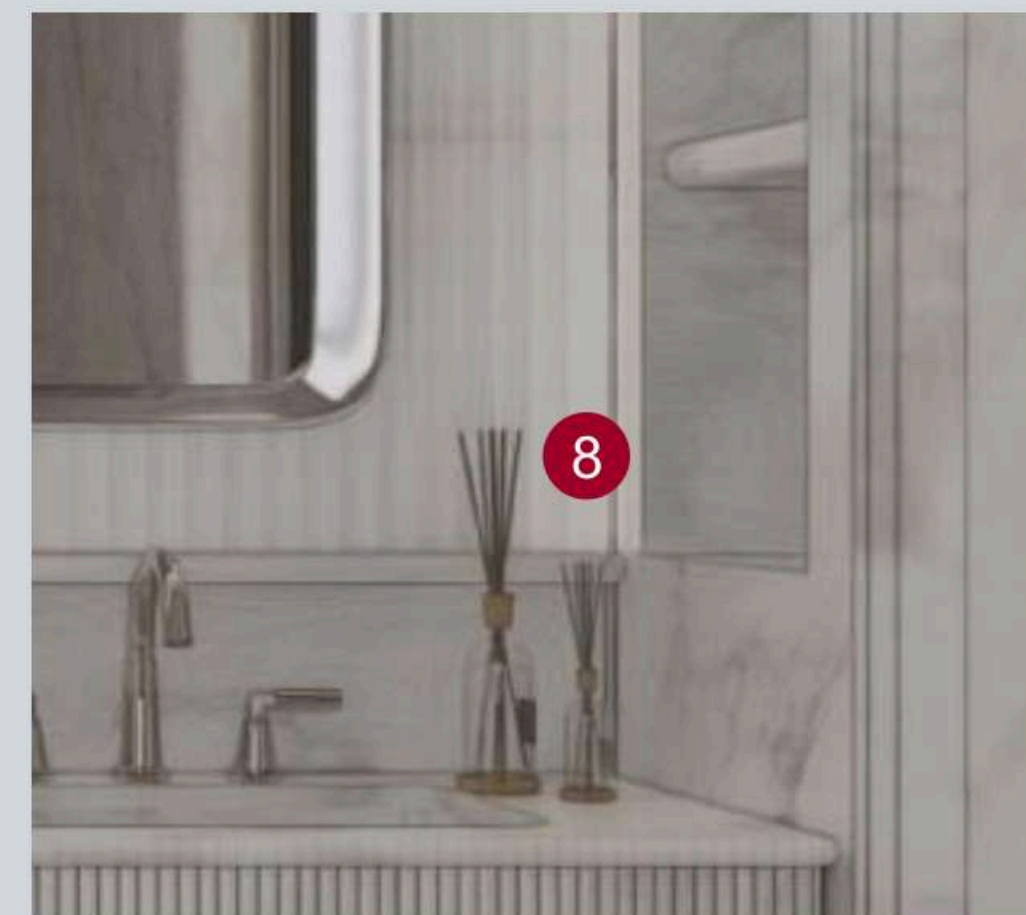

DETAIL THINKING 细节构想

Master Bathroom
主卫

- 台盆细节构想
- 隔板及灯沟细节构想
- 插座点位分析
- **壁龛细节分析**
- 壁灯及镜子安装细节构想
- 淋浴房座凳细节
- 墙面分隔细节构想

三维石材预安装

壁龛灯带分析







请明确壁龛灯具尺寸

(壁龛灯带) : 配12*10型材

尺寸: Lx12x10mm


适用: 10mm软灯带/硬灯条

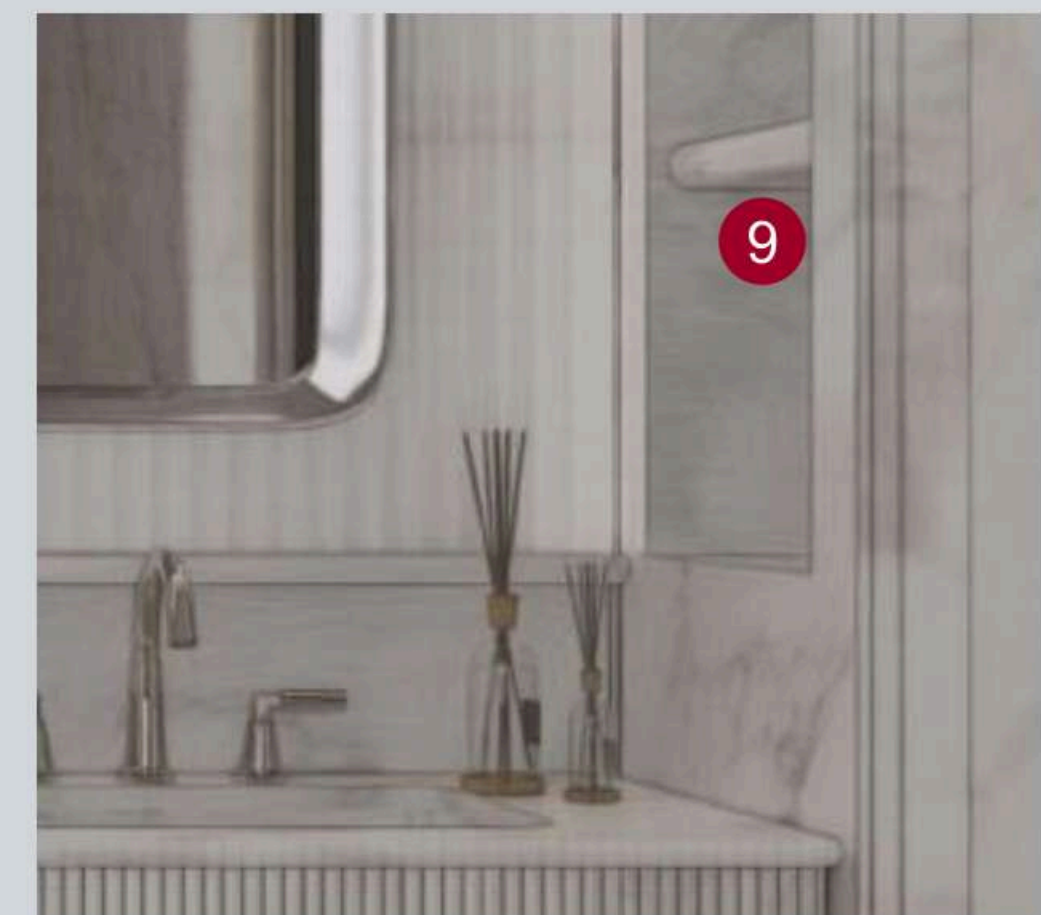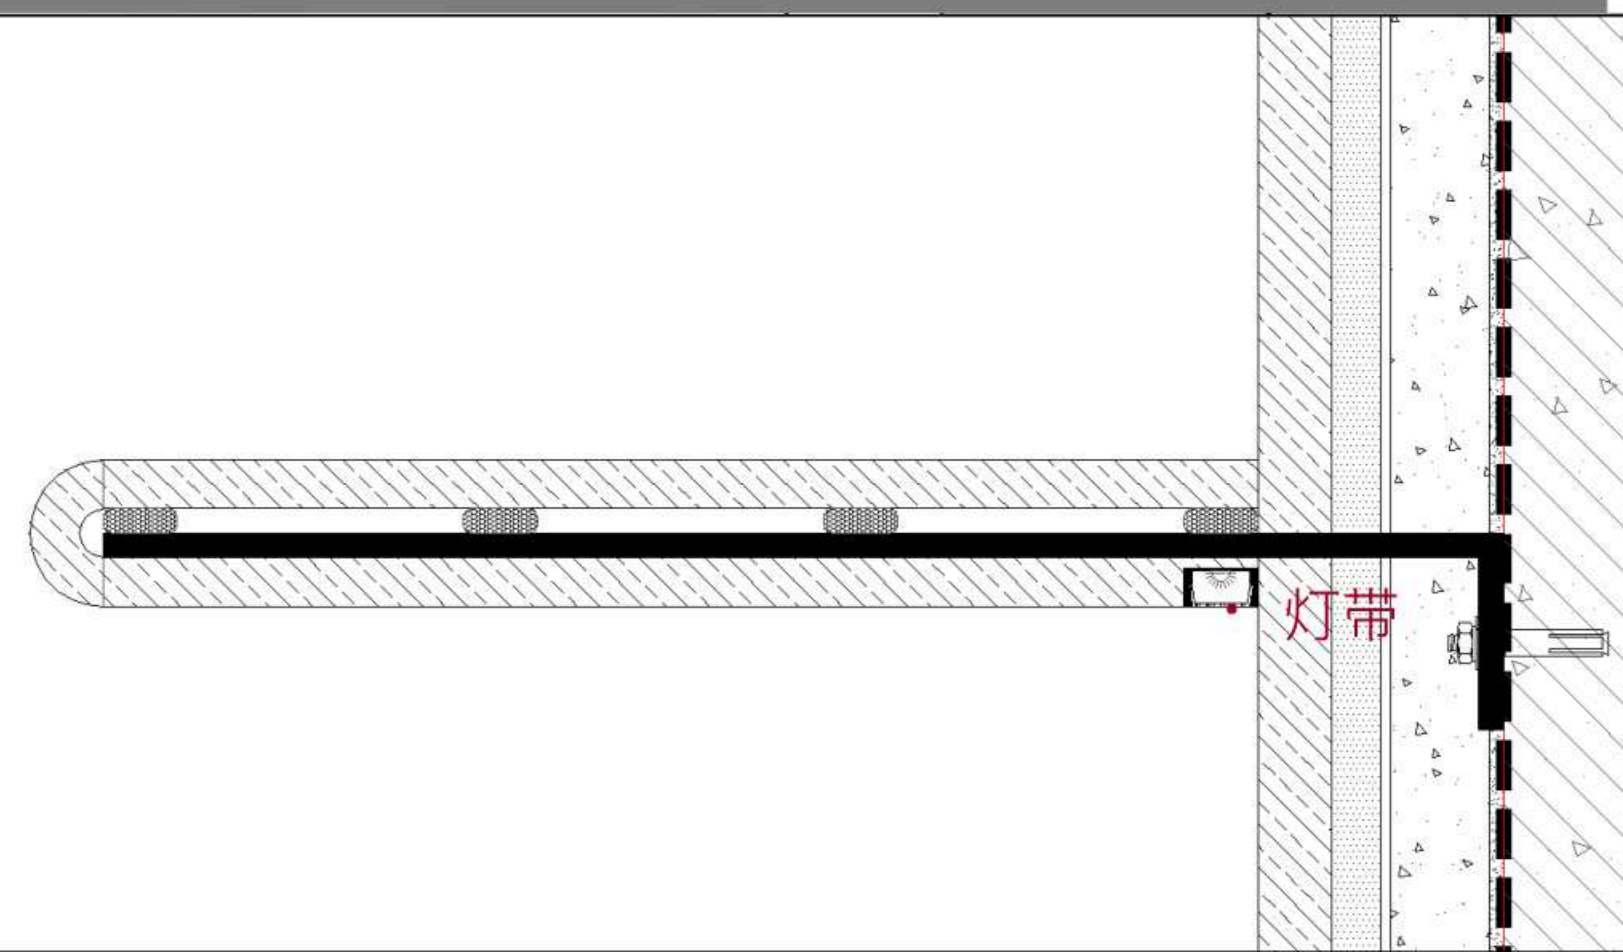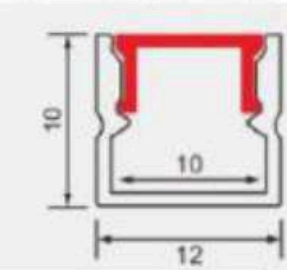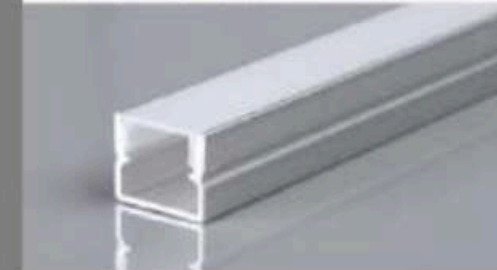

请提供灯具底座尺寸
及镜子安装方式



灯具安装前效果

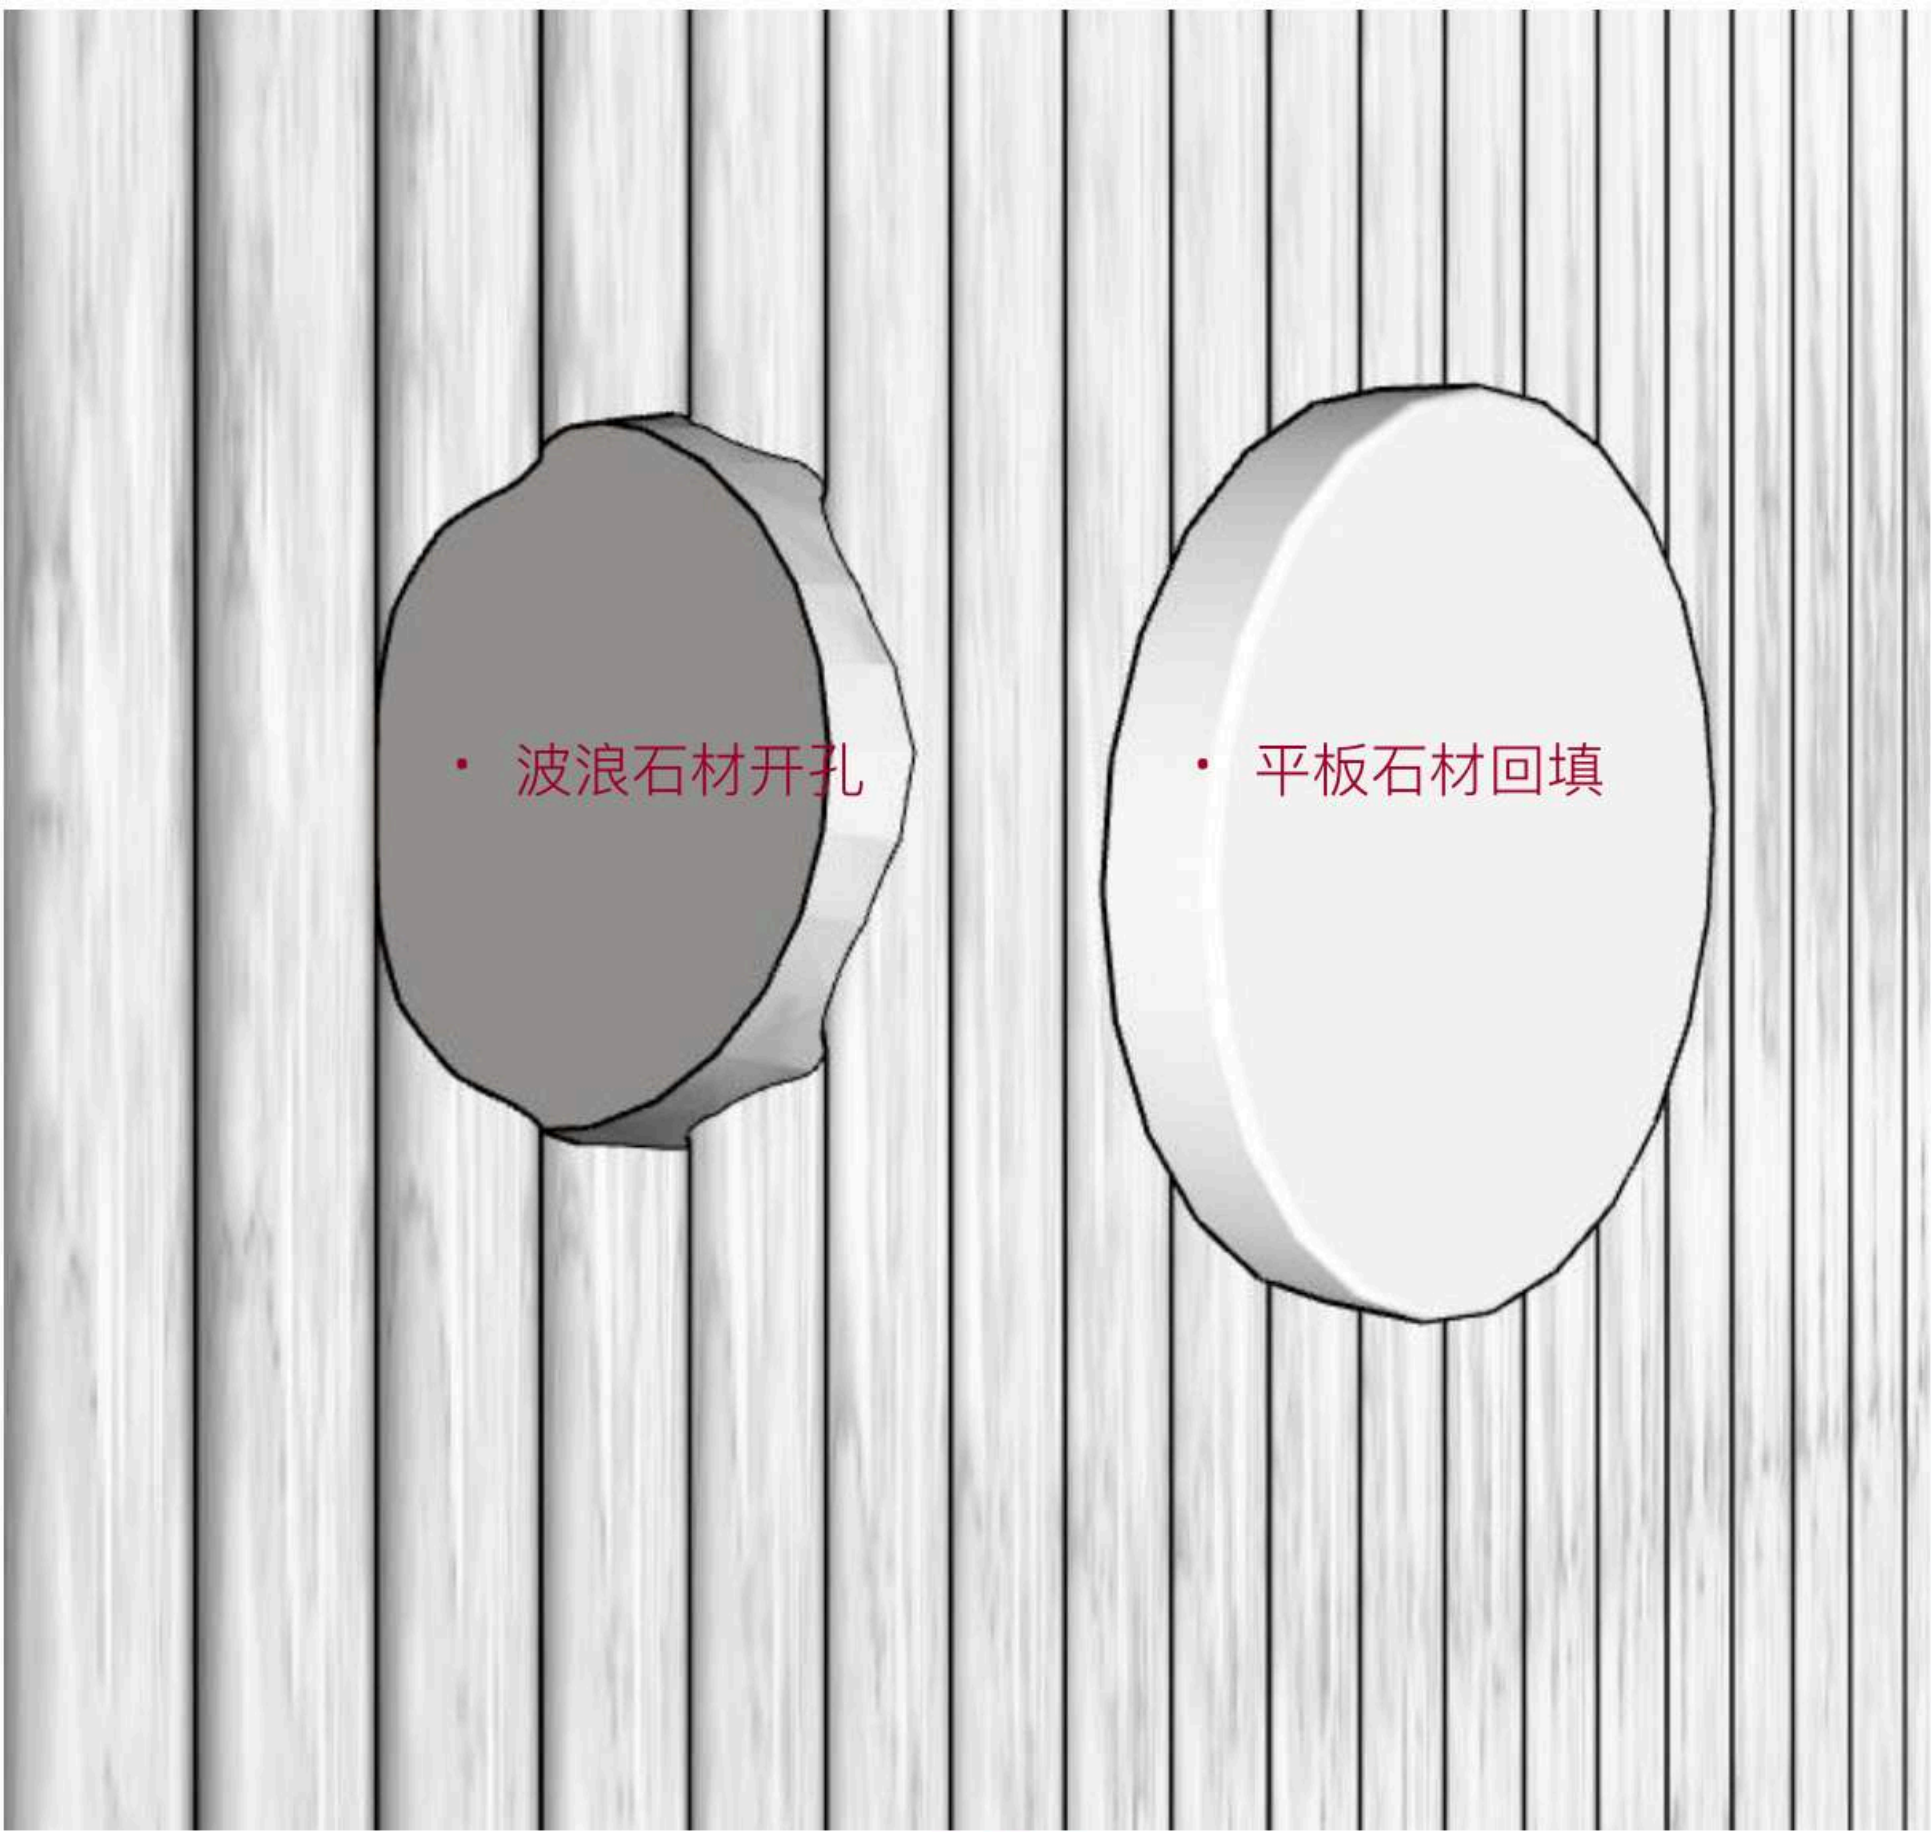

分解效果

DETAIL THINKING
细节构想

Master Bathroom
主卫

- 台盆细节构想
- 隔板及灯沟细节构想
- 插座点位分析
- 壁龛细节分析
- 壁灯及镜子安装细节构想
- 淋浴房座凳细节
- 墙面分隔细节构想

三维石材预安装

壁灯安装解决方案




DETAIL THINKING 细节构想

Master Bathroom
主卫


- 台盆细节构想
- 隔板及灯沟细节构想
- 插座点位分析
- 壁龛细节分析
- 壁灯及镜子安装细节构想
- 淋浴房座凳细节
- 墙面分隔细节构想

三维石材预安装

石材分割 · 拼接构想

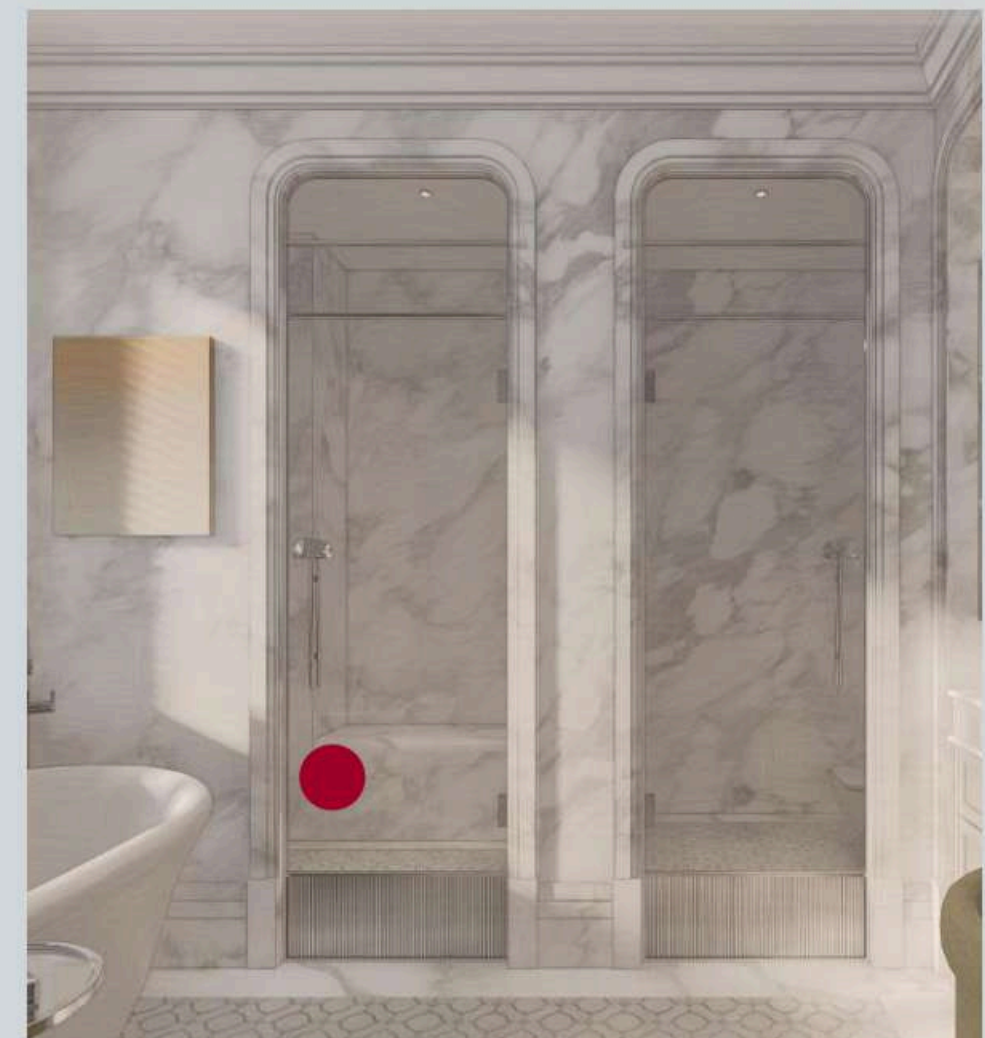

HIBORNI

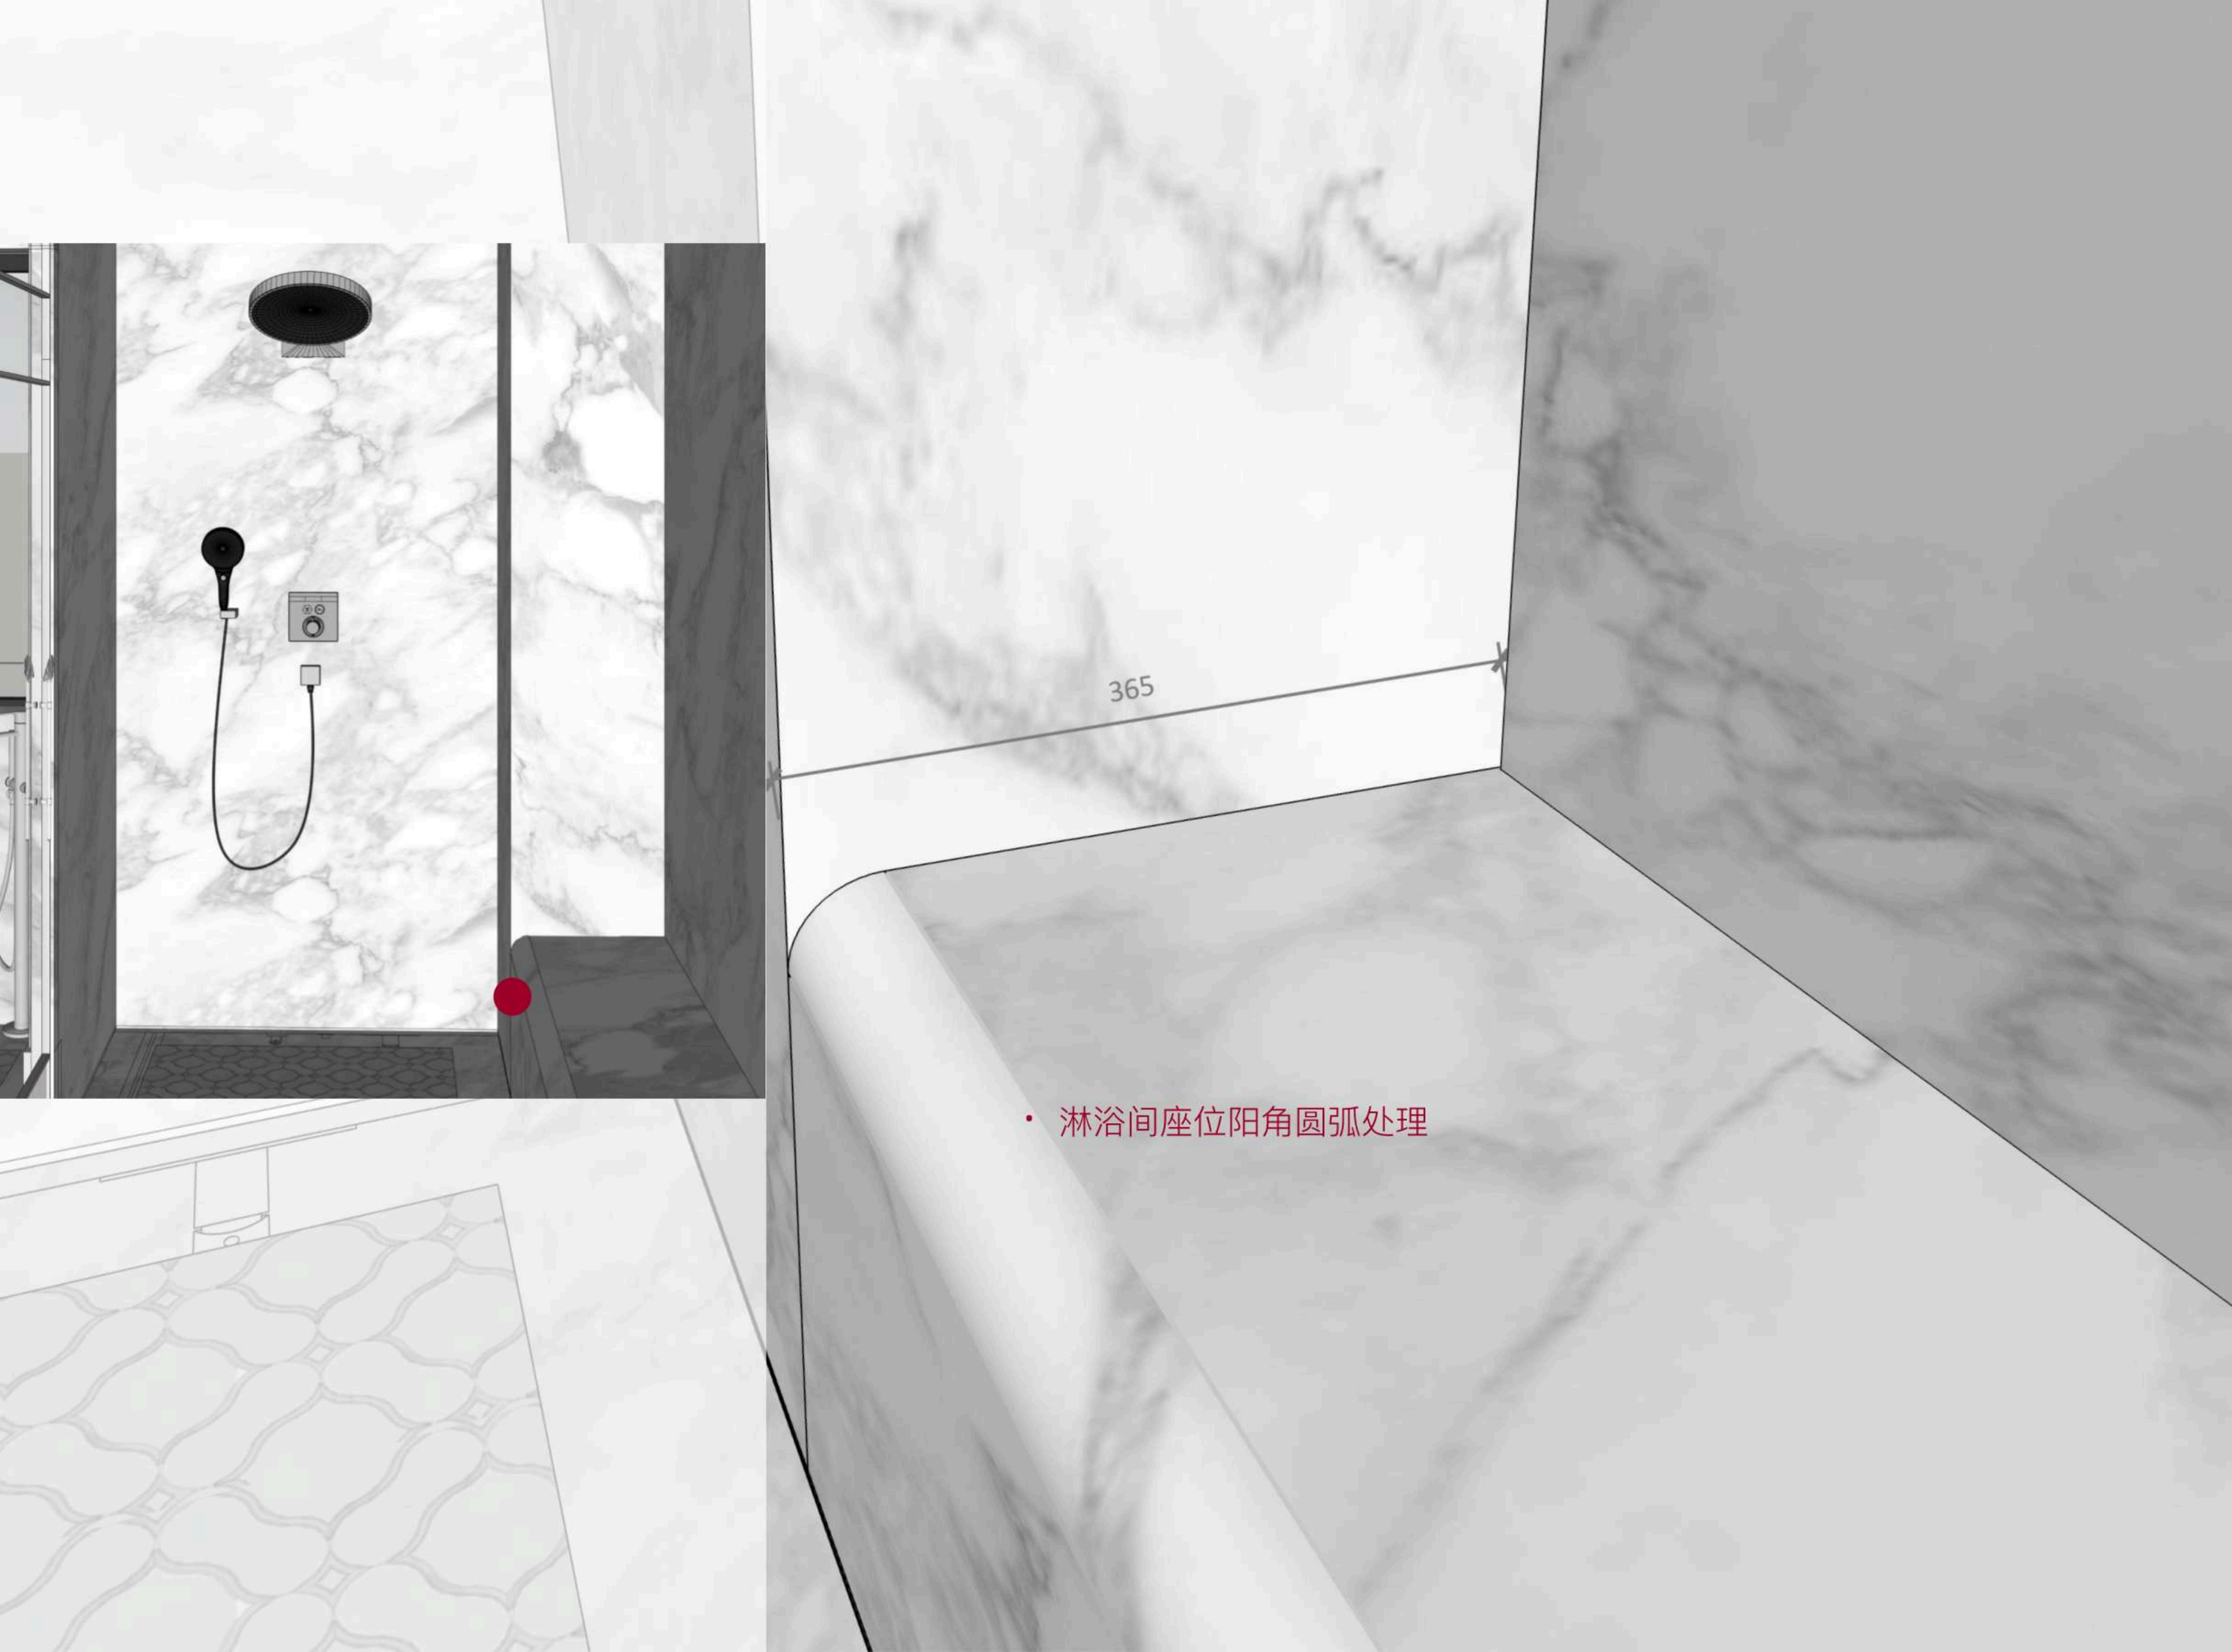

- 淋浴间座位阳角圆弧处理


DETAIL THINKING 细节构想

Master Bathroom
主卫

- 台盆细节构想
- 隔板及灯沟细节构想
- 插座点位分析
- 壁龛细节分析
- 壁灯及镜子安装细节构想
- 淋浴房座凳细节
- 墙面分隔细节构想

三维石材预安装

石材分割 · 拼接构想

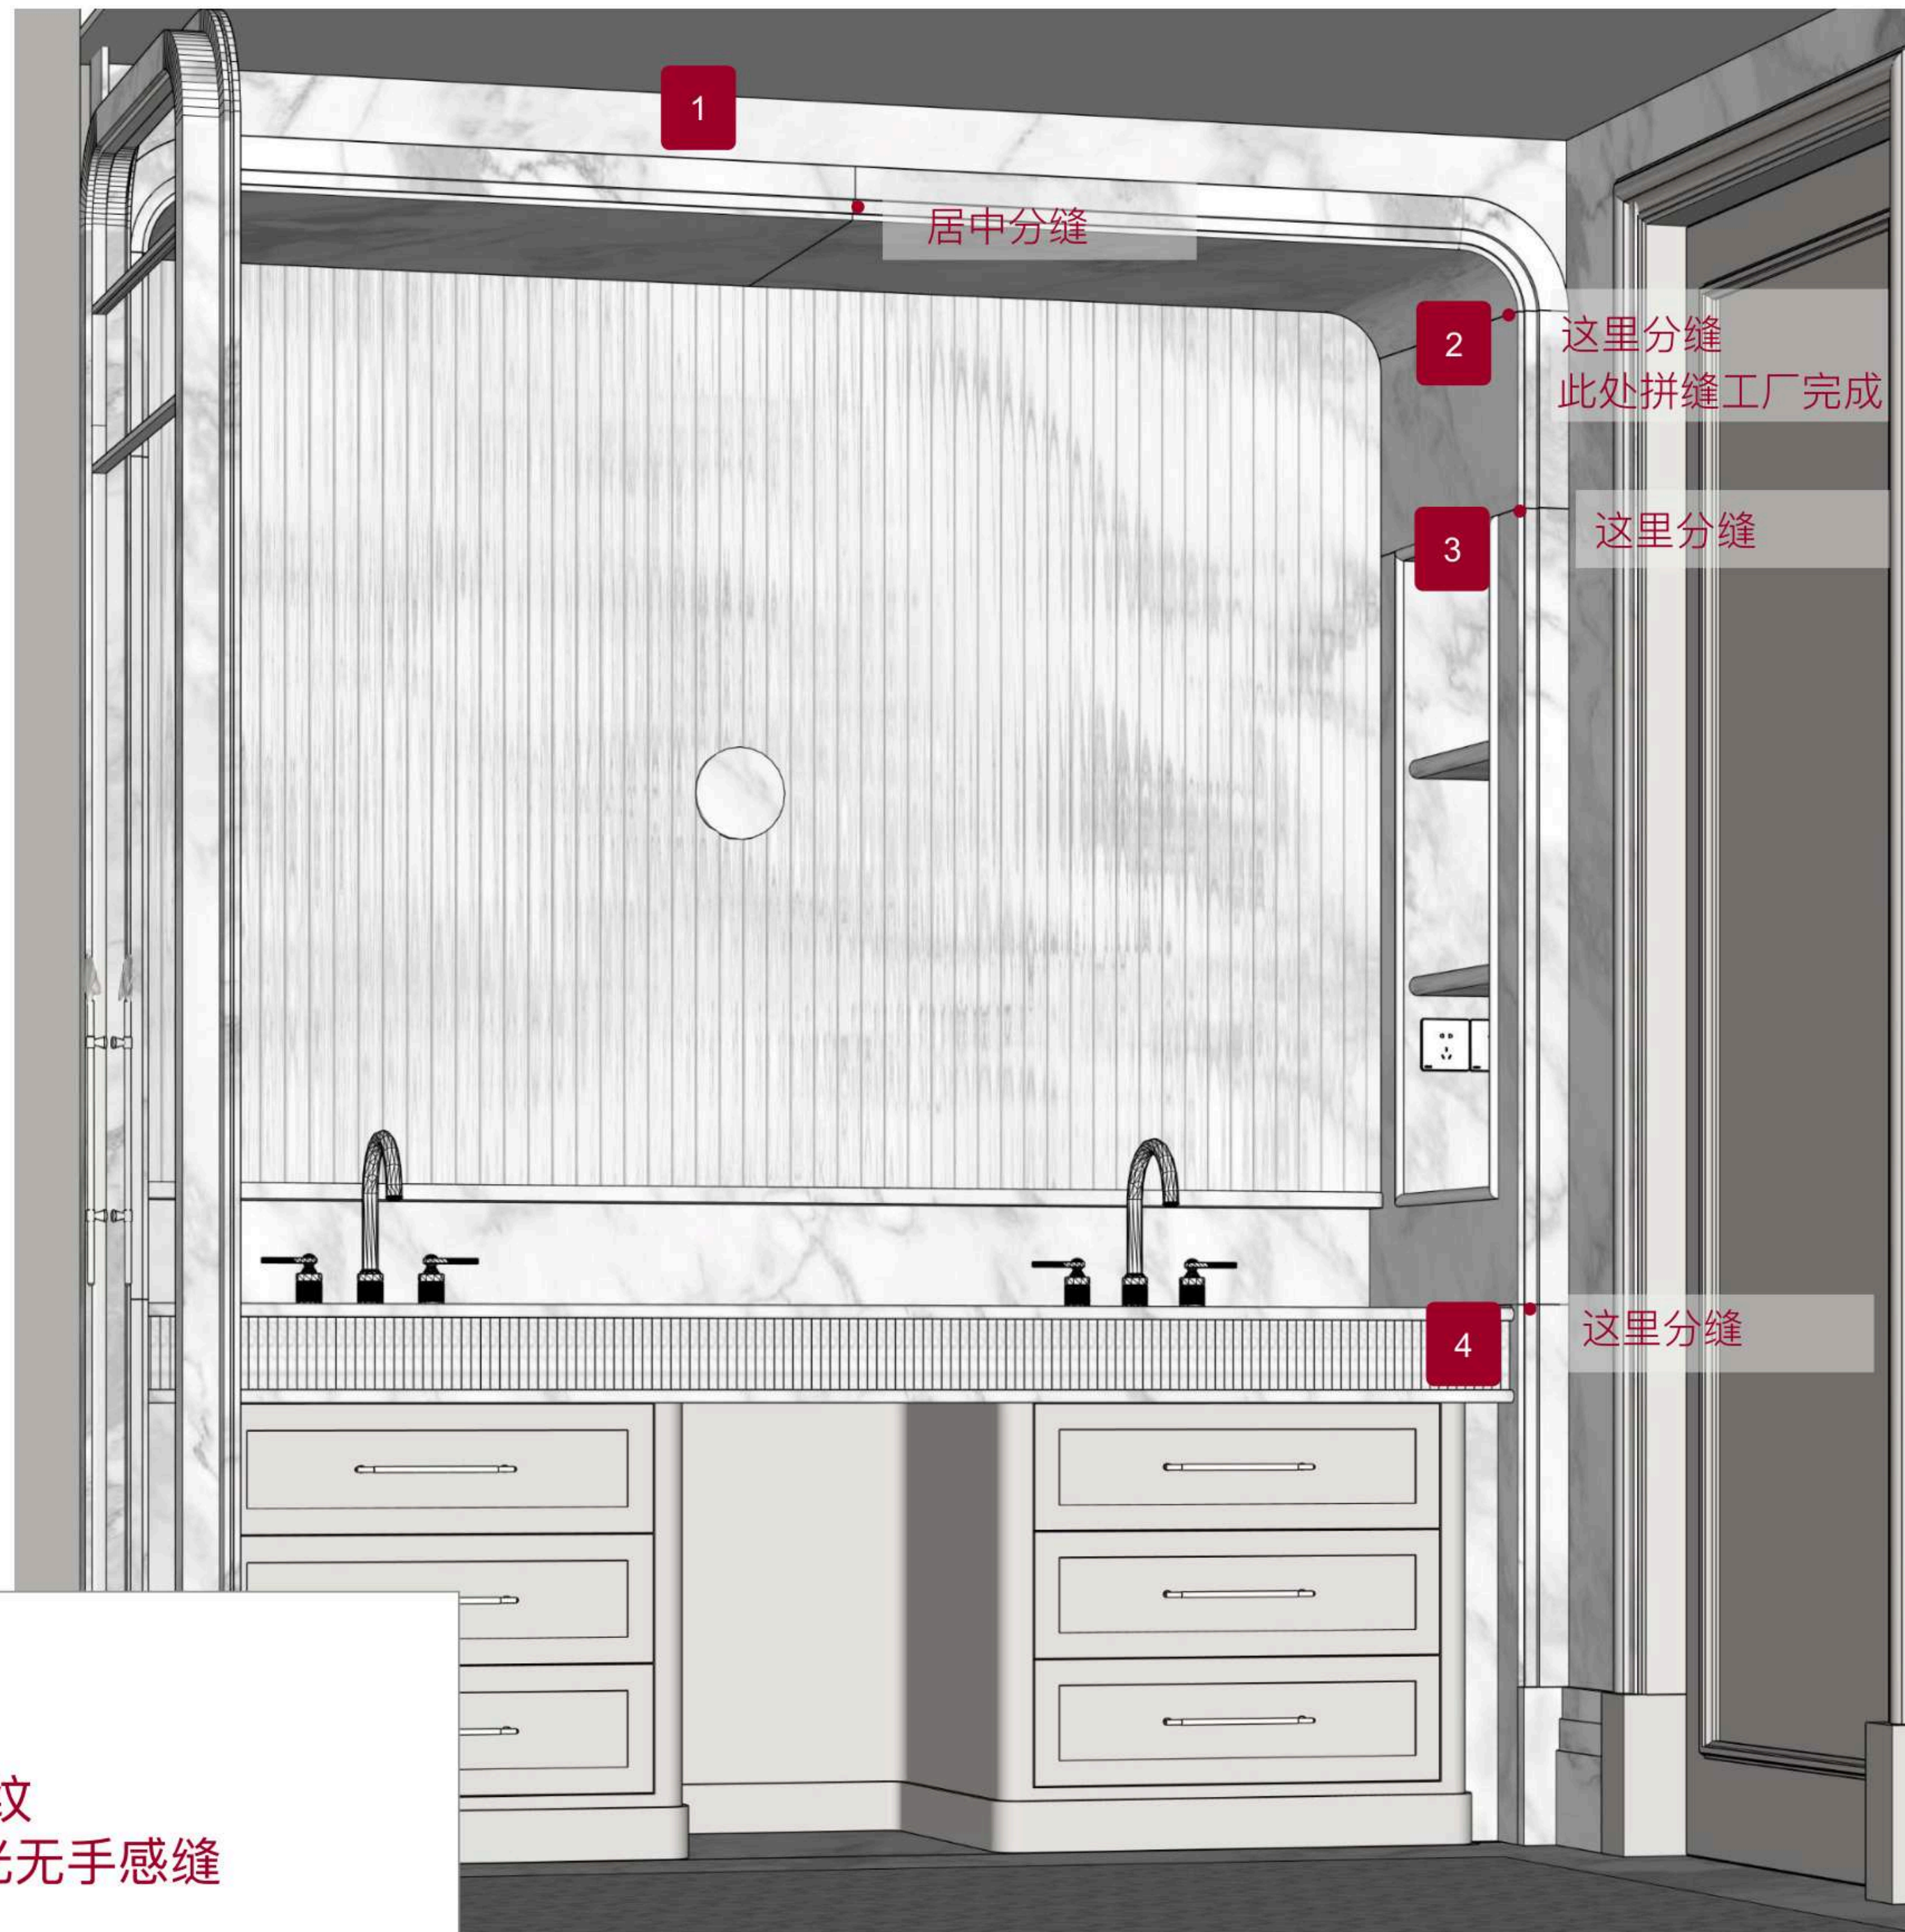

要做到:

- 1、1 2 3 4 石材对纹
- 2、现场追纹密拼后抛光无手感缝


DETAIL THINKING 细节构想

Master Bathroom
主卫

- 台盆细节构想
- 隔板及灯沟细节构想
- 插座点位分析
- 壁龛细节分析
- 壁灯及镜子安装细节构想
- 淋浴房座凳细节
- 墙面分隔细节构想

三维石材预安装

石材分割 · 拼接构想

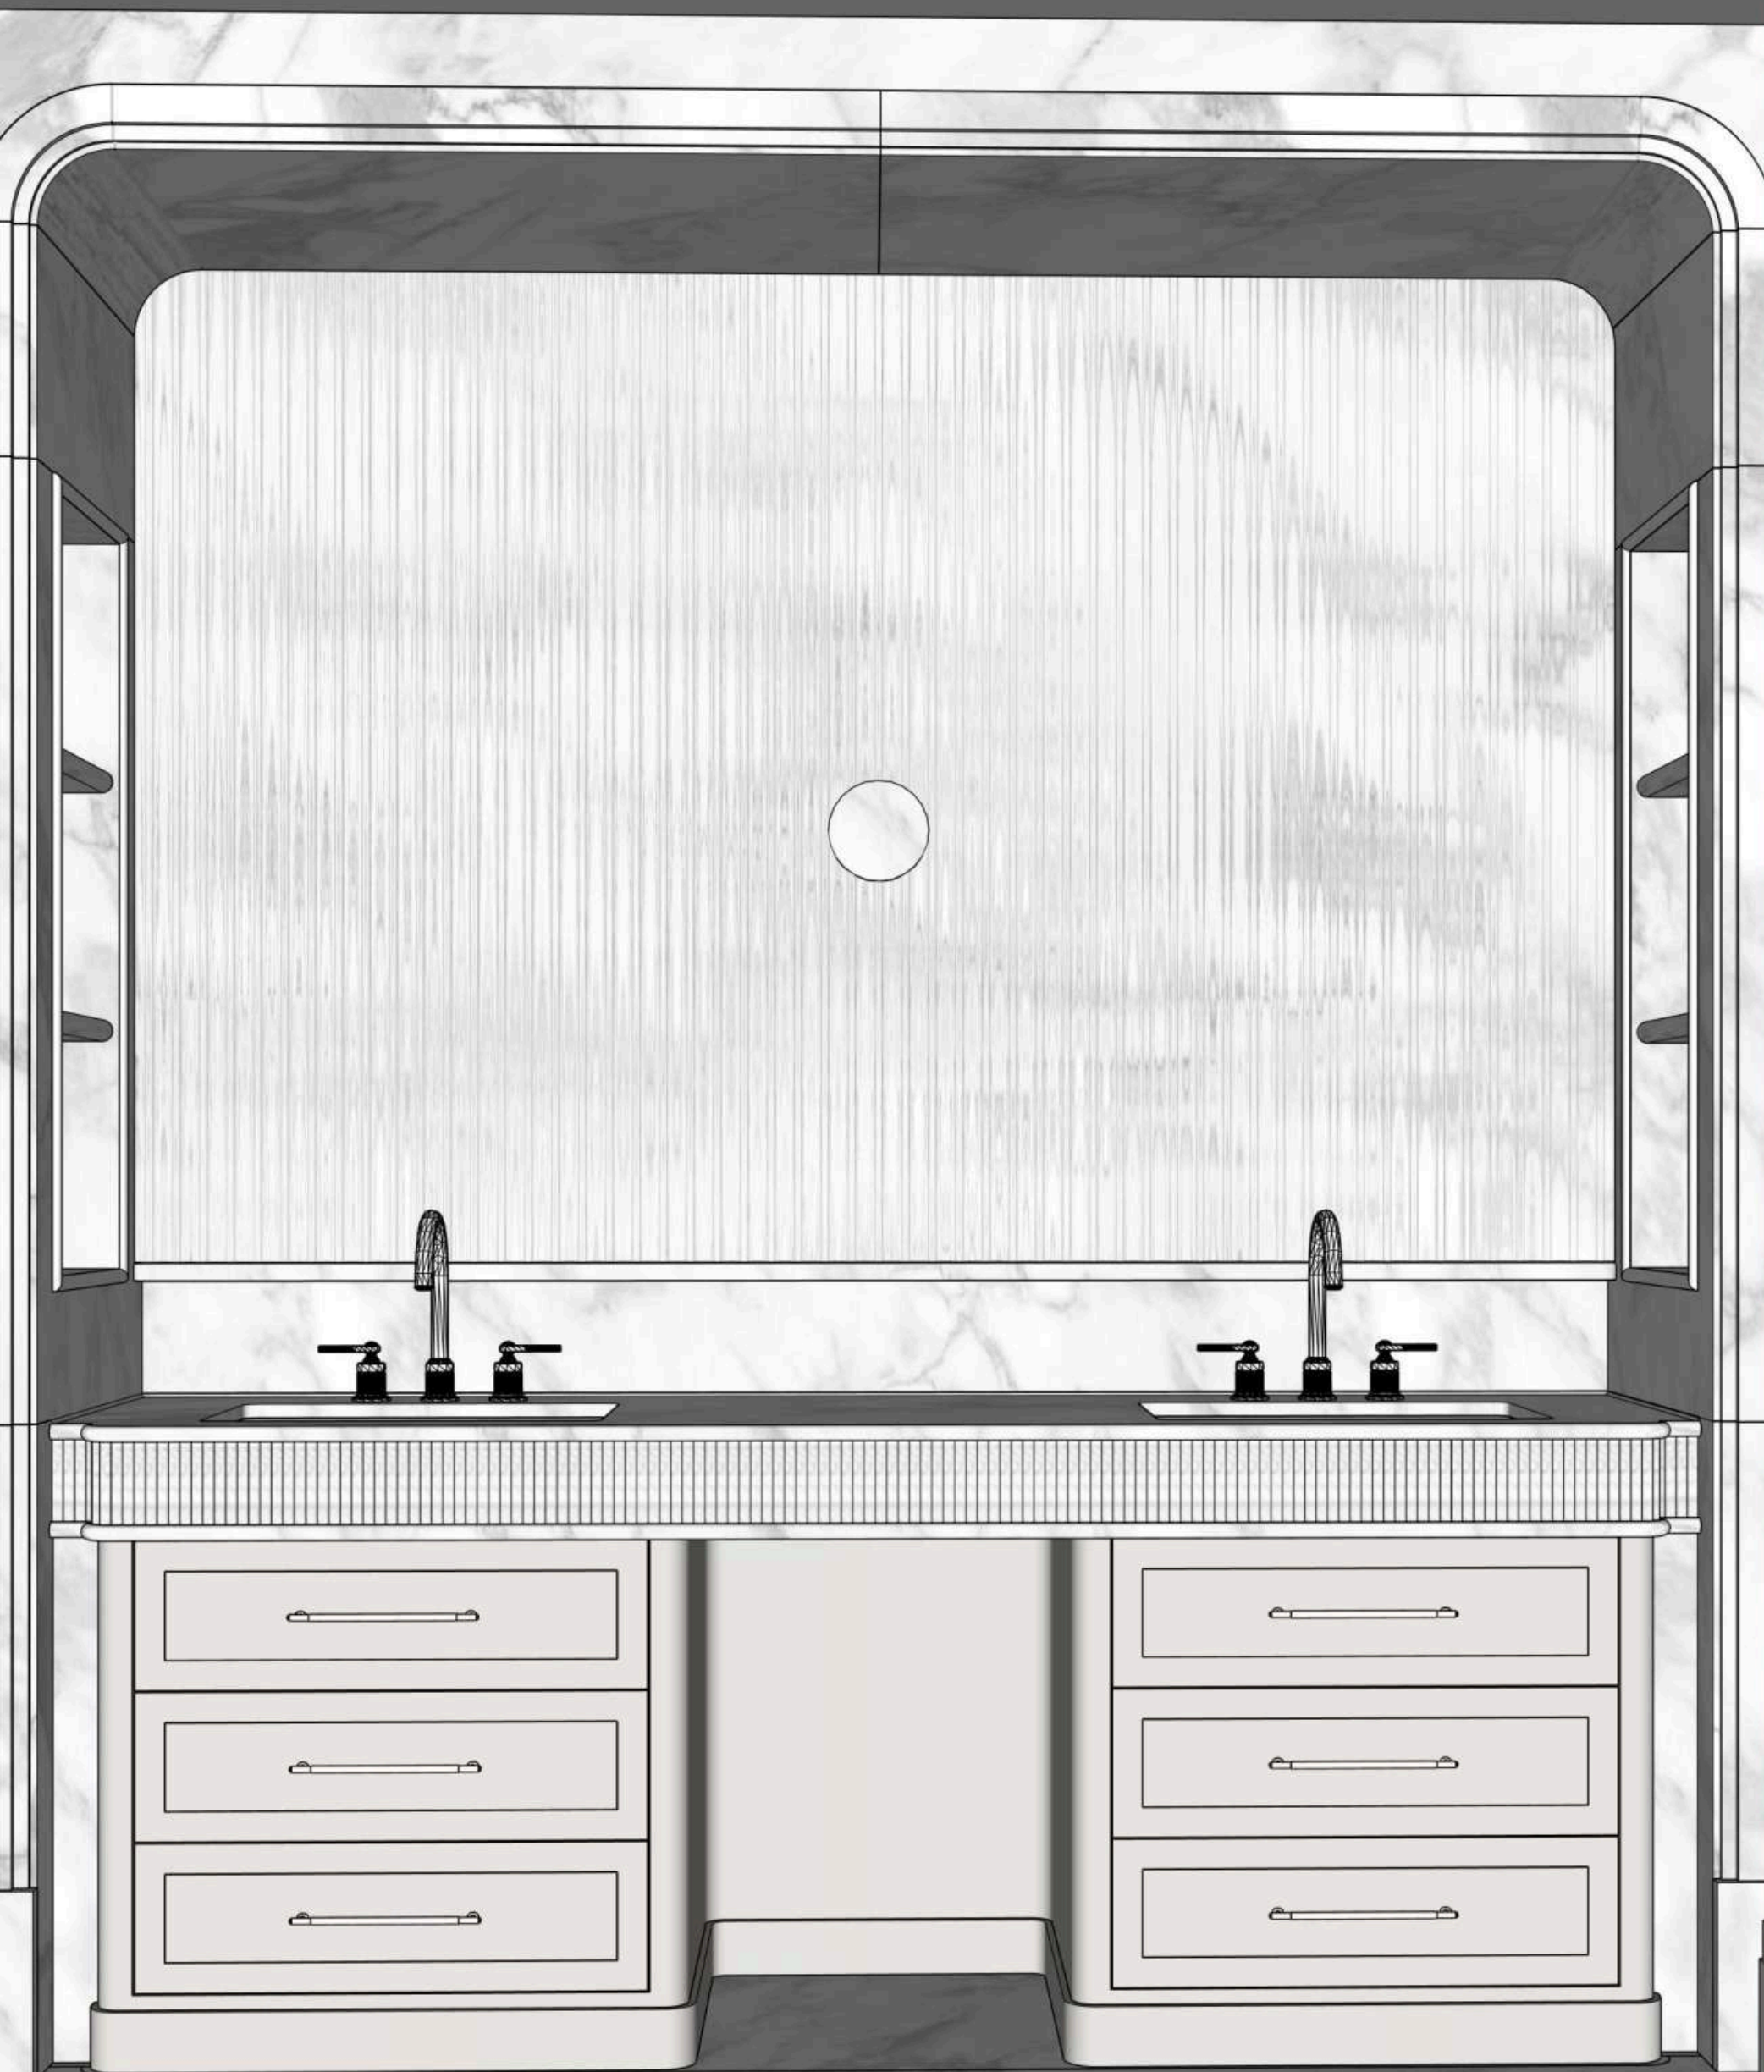

795

壁龛上口高度分割线

1265

台盆高度分割线

850


石材尺寸
1810X2910

DETAIL THINKING 细节构想

Powder room
客卫

- 台盆细节
- 腰线细节
- 窗套细节
- 踢脚细节
- 管井检修口
- 分割原则

三维石材预安装

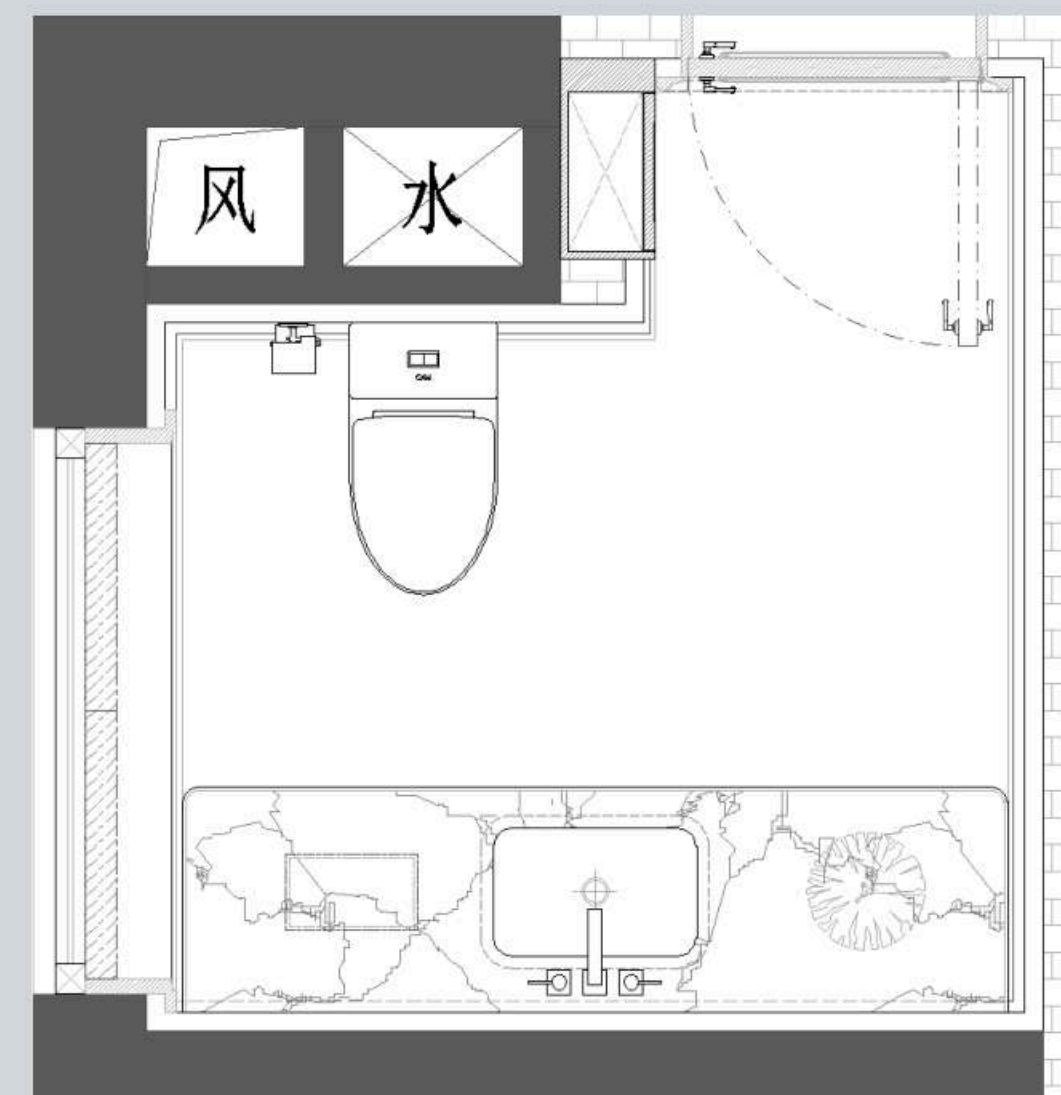

DETAIL THINKING
细节构想

缝隙·进水

1

缝隙·保洁

2

或
洗手台柜是活动家具
放在这的概念

4

隔板·龙头

5




腰线·台面

6

腰线·窗套

3

缝隙·
进水

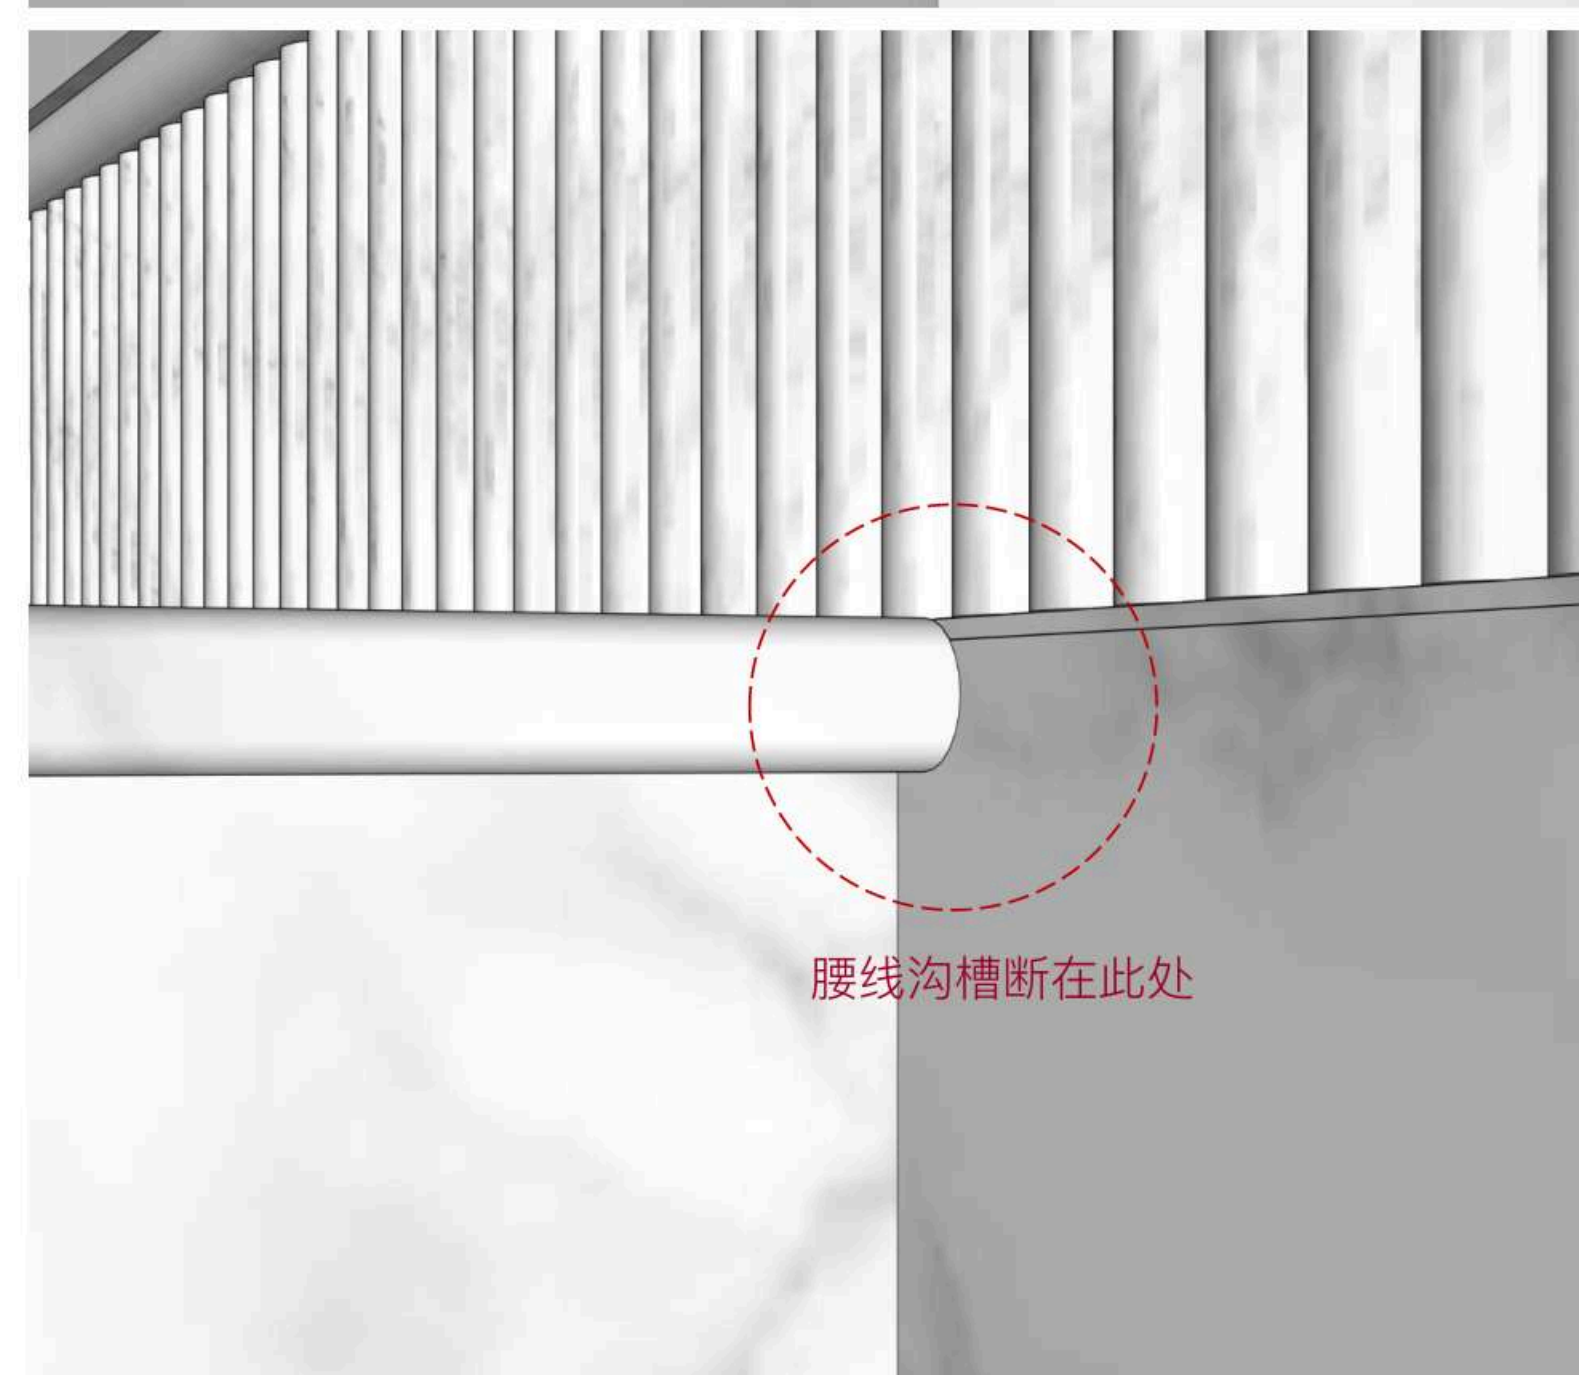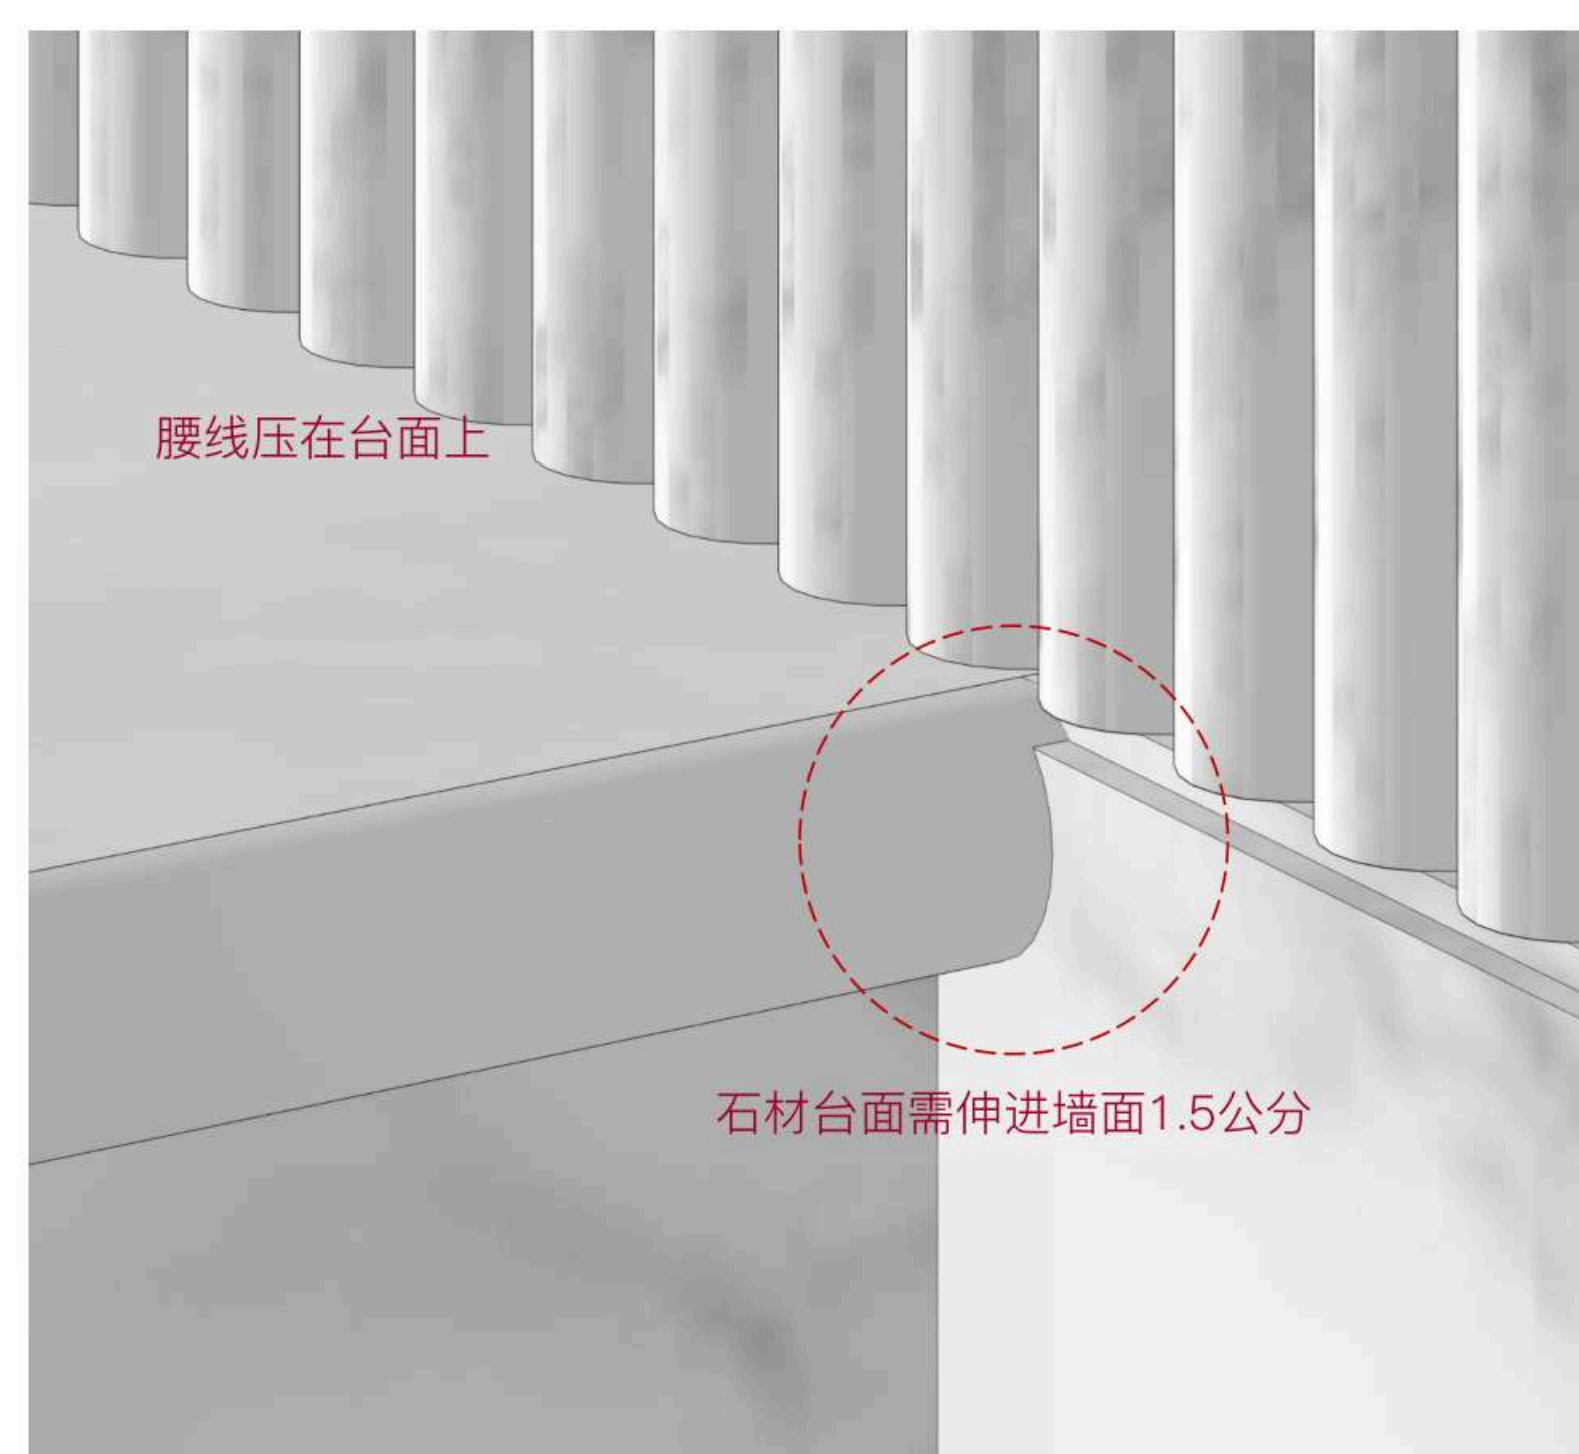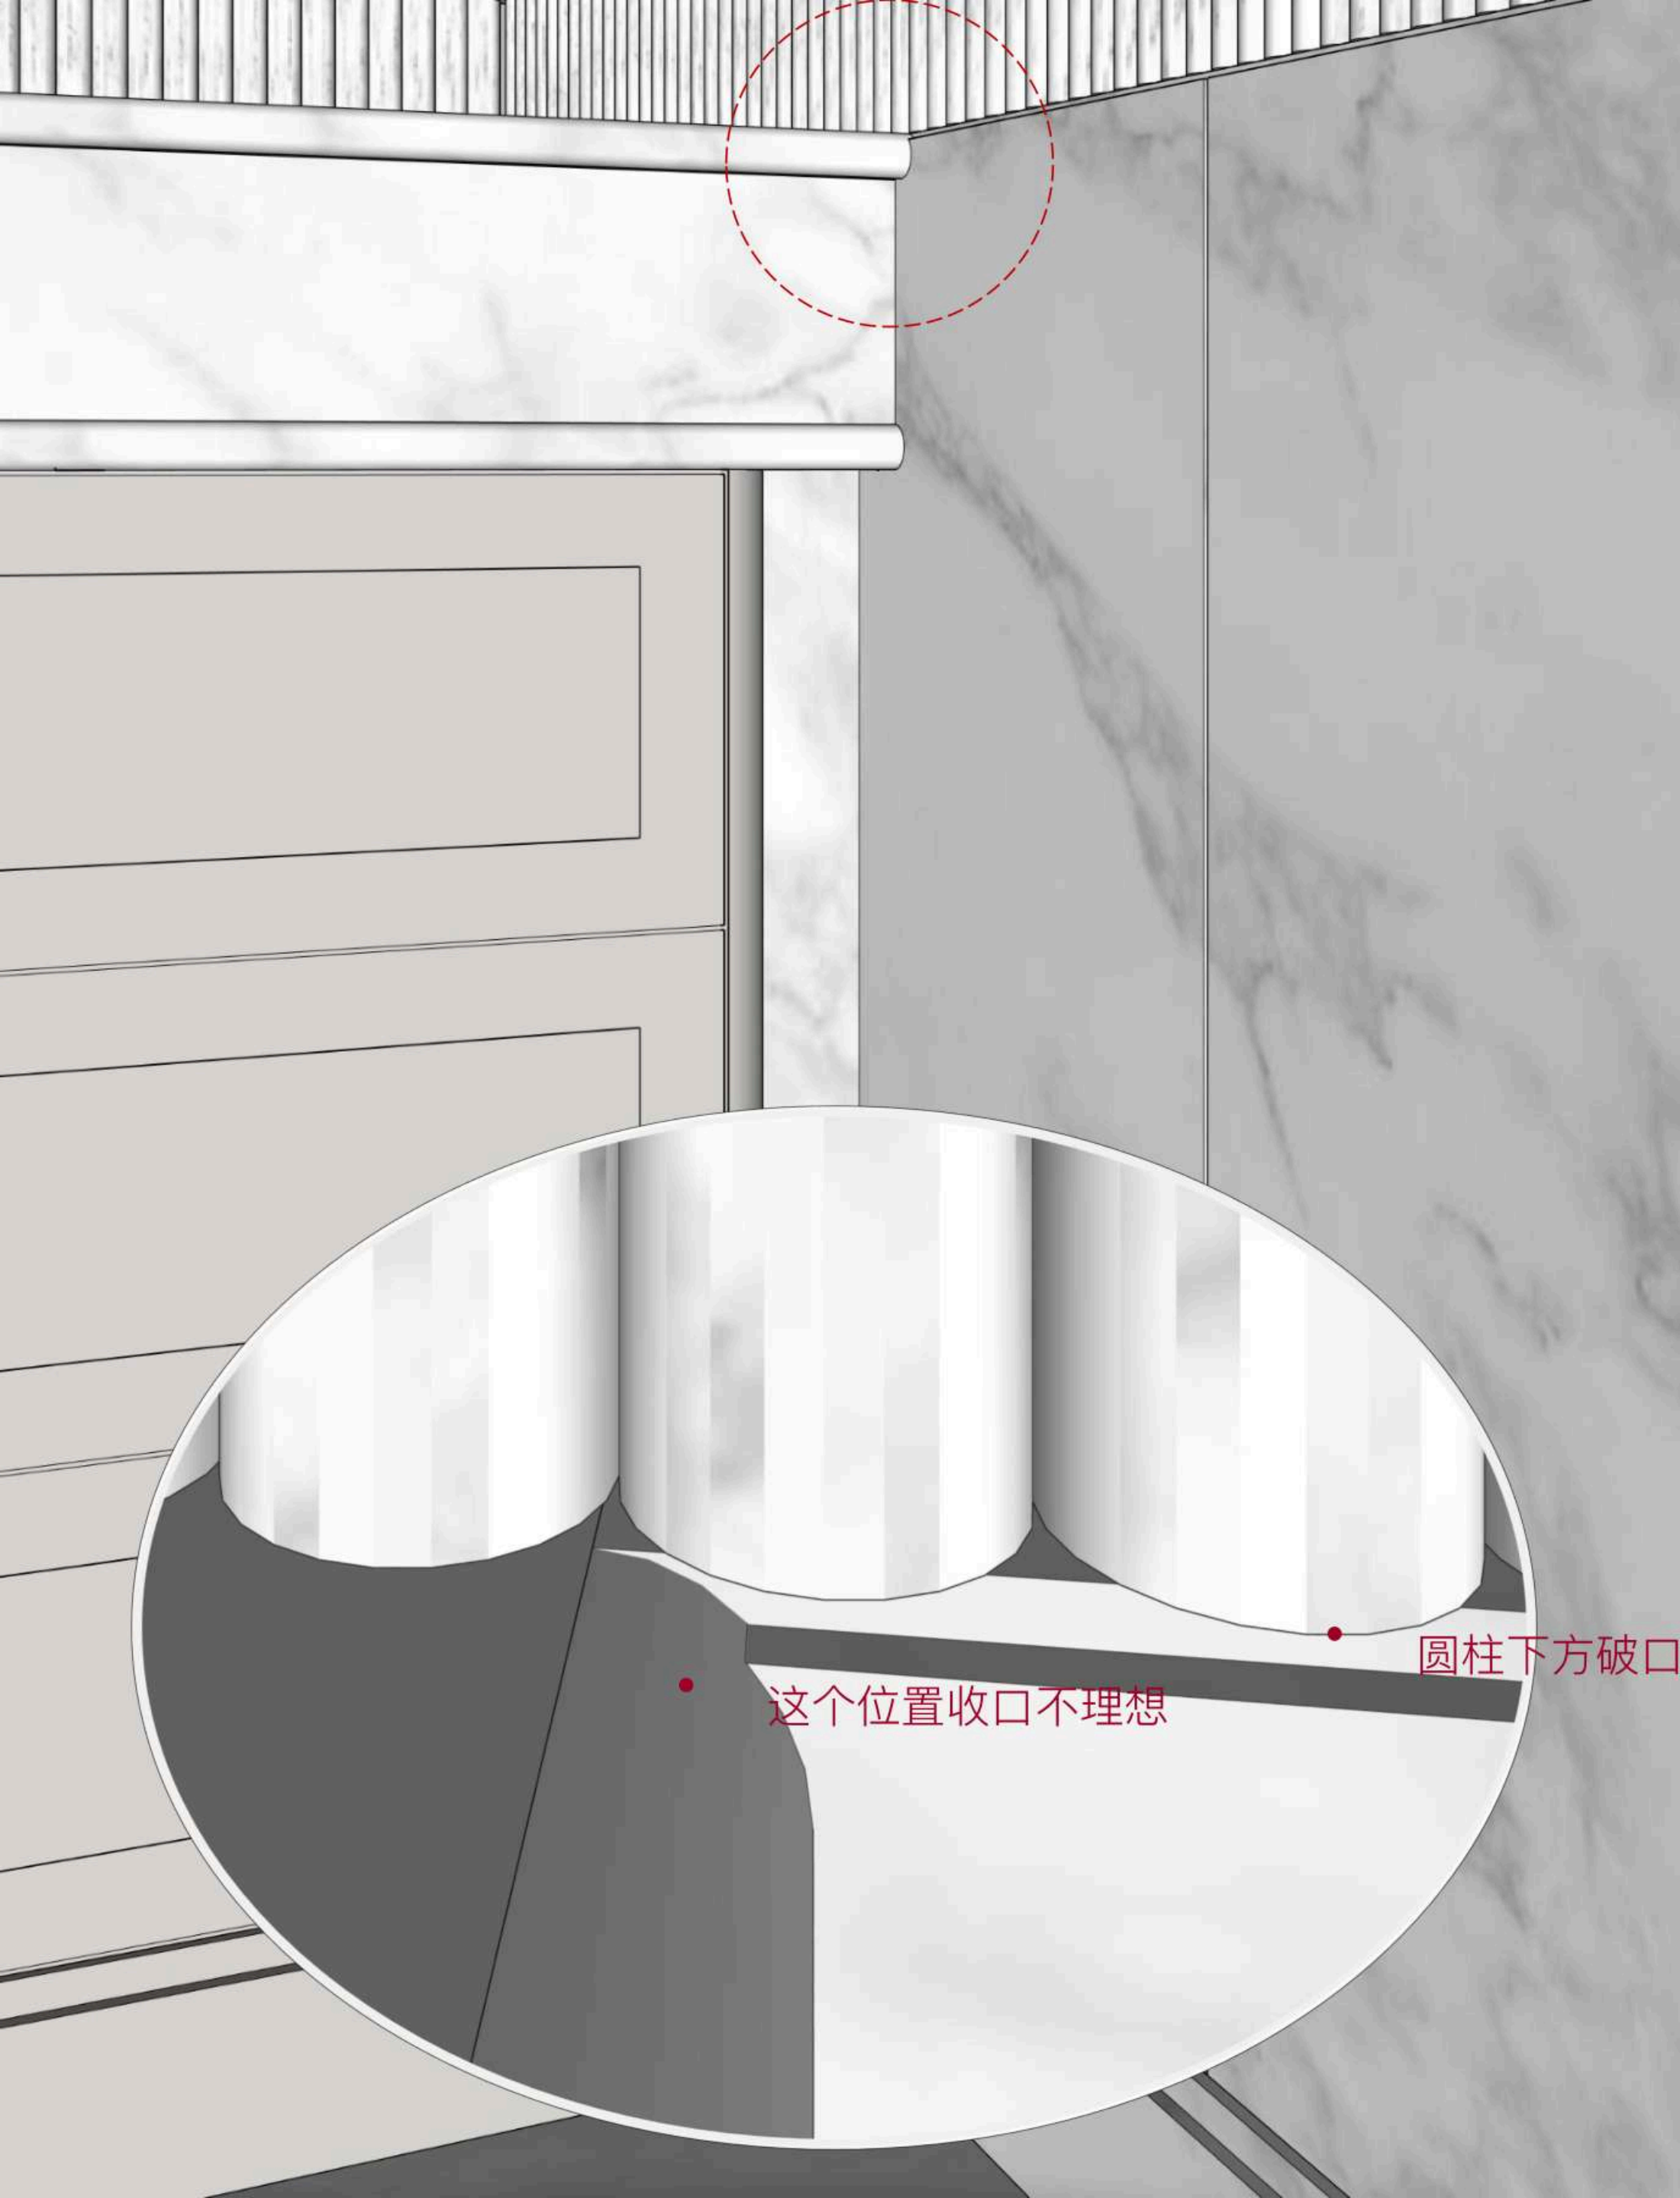

DETAIL THINKING 细节构想

Powder room
客卫


- 台盆细节
- 腰线细节
- 窗套细节
- 踢脚细节
- 管井检修口
- 分割原则



DETAIL THINKING 细节构想

Powder room
客卫




- 台盆细节
- 腰线细节
- 窗套细节
- 踢脚细节
- 管井检修口
- 分割原则

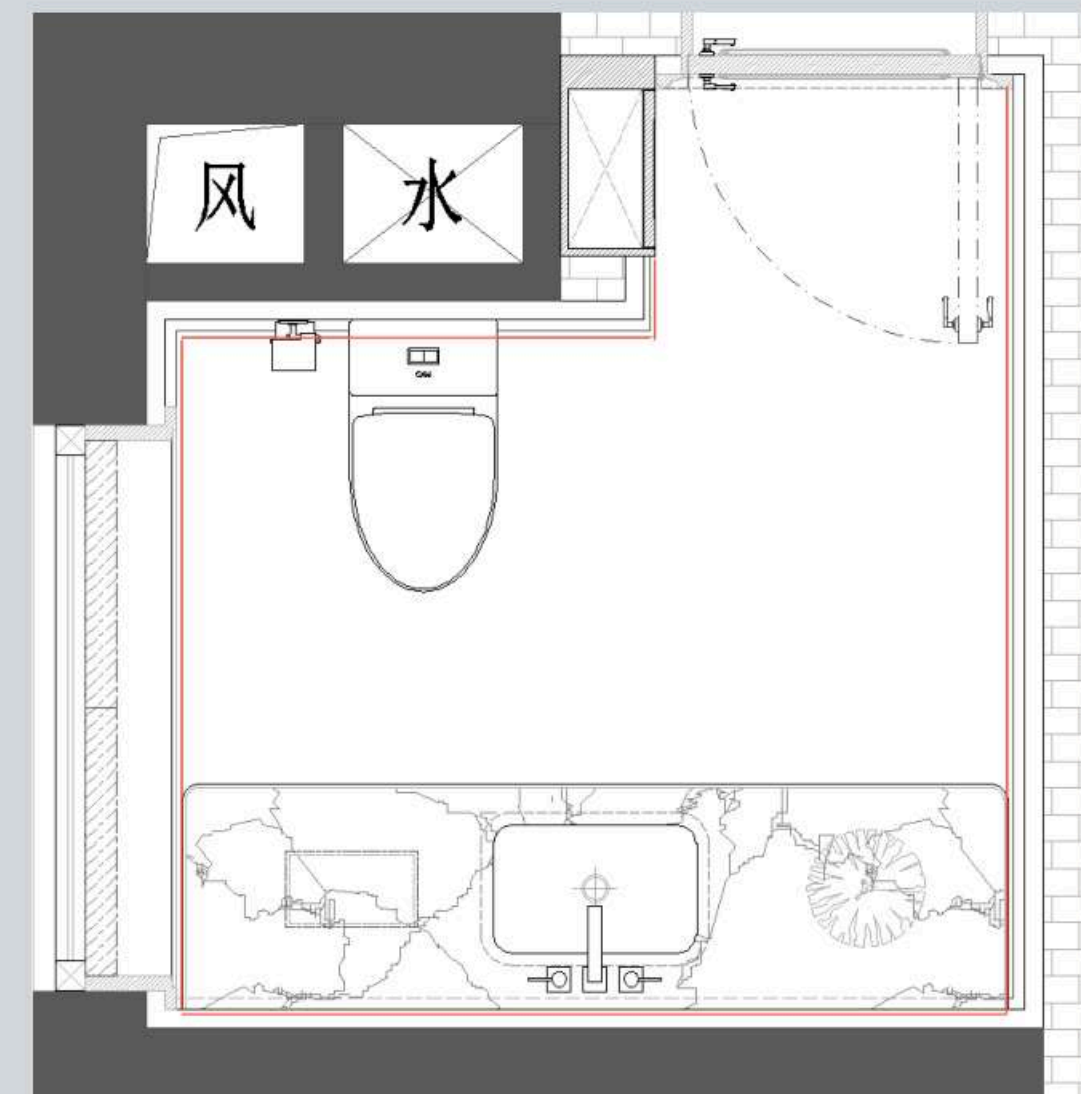

DETAIL THINKING 细节构想

Powder room
客卫




- 台盆细节
- **腰线细节**
- 窗套细节
- 踢脚细节
- 管井检修口
- 分割原则

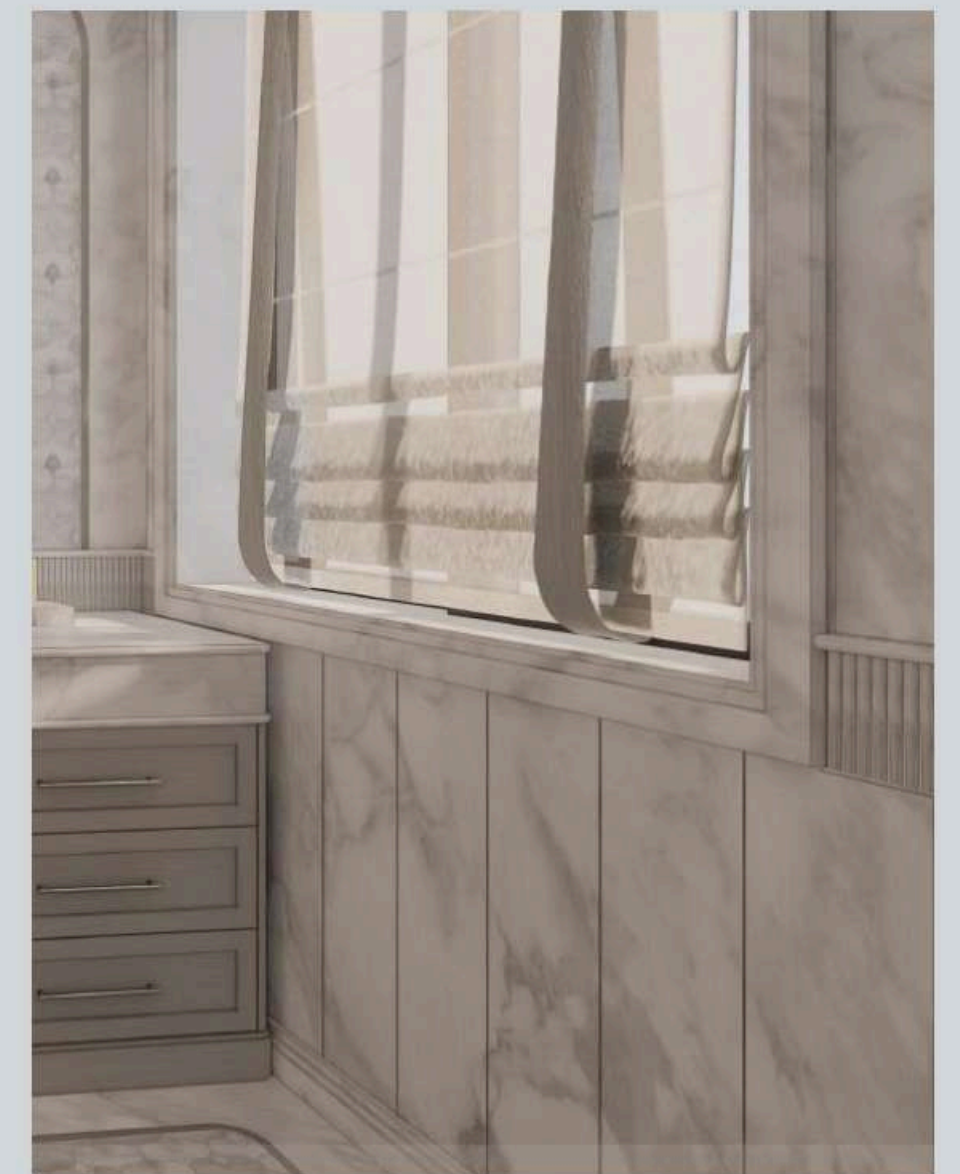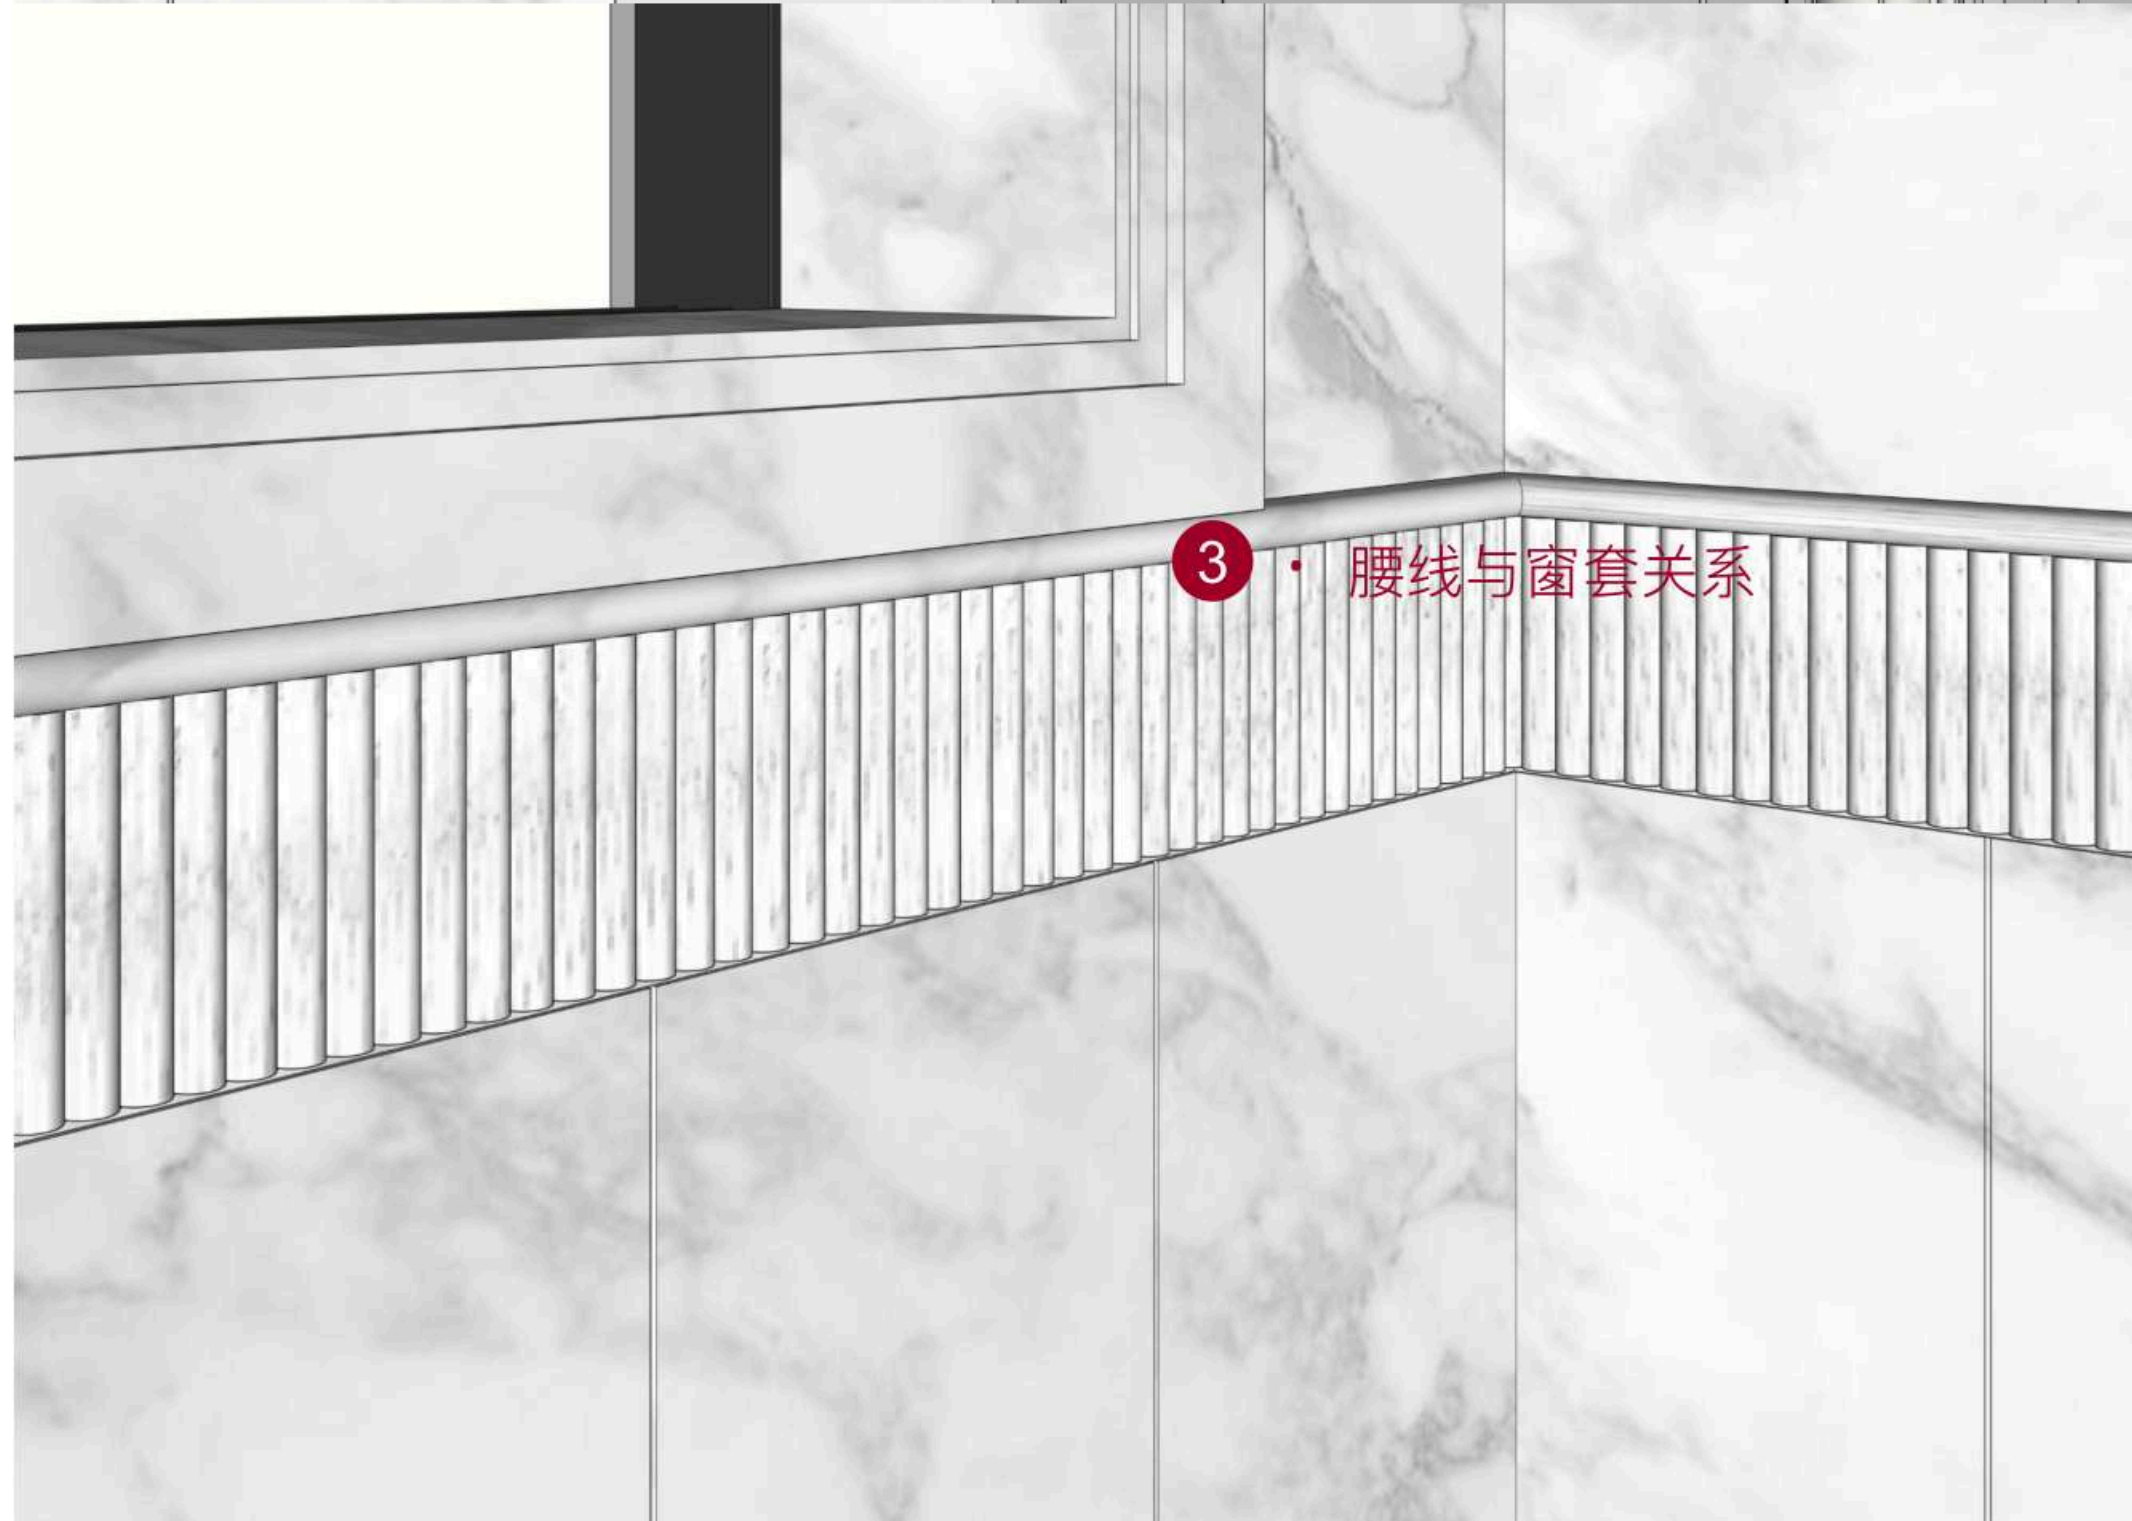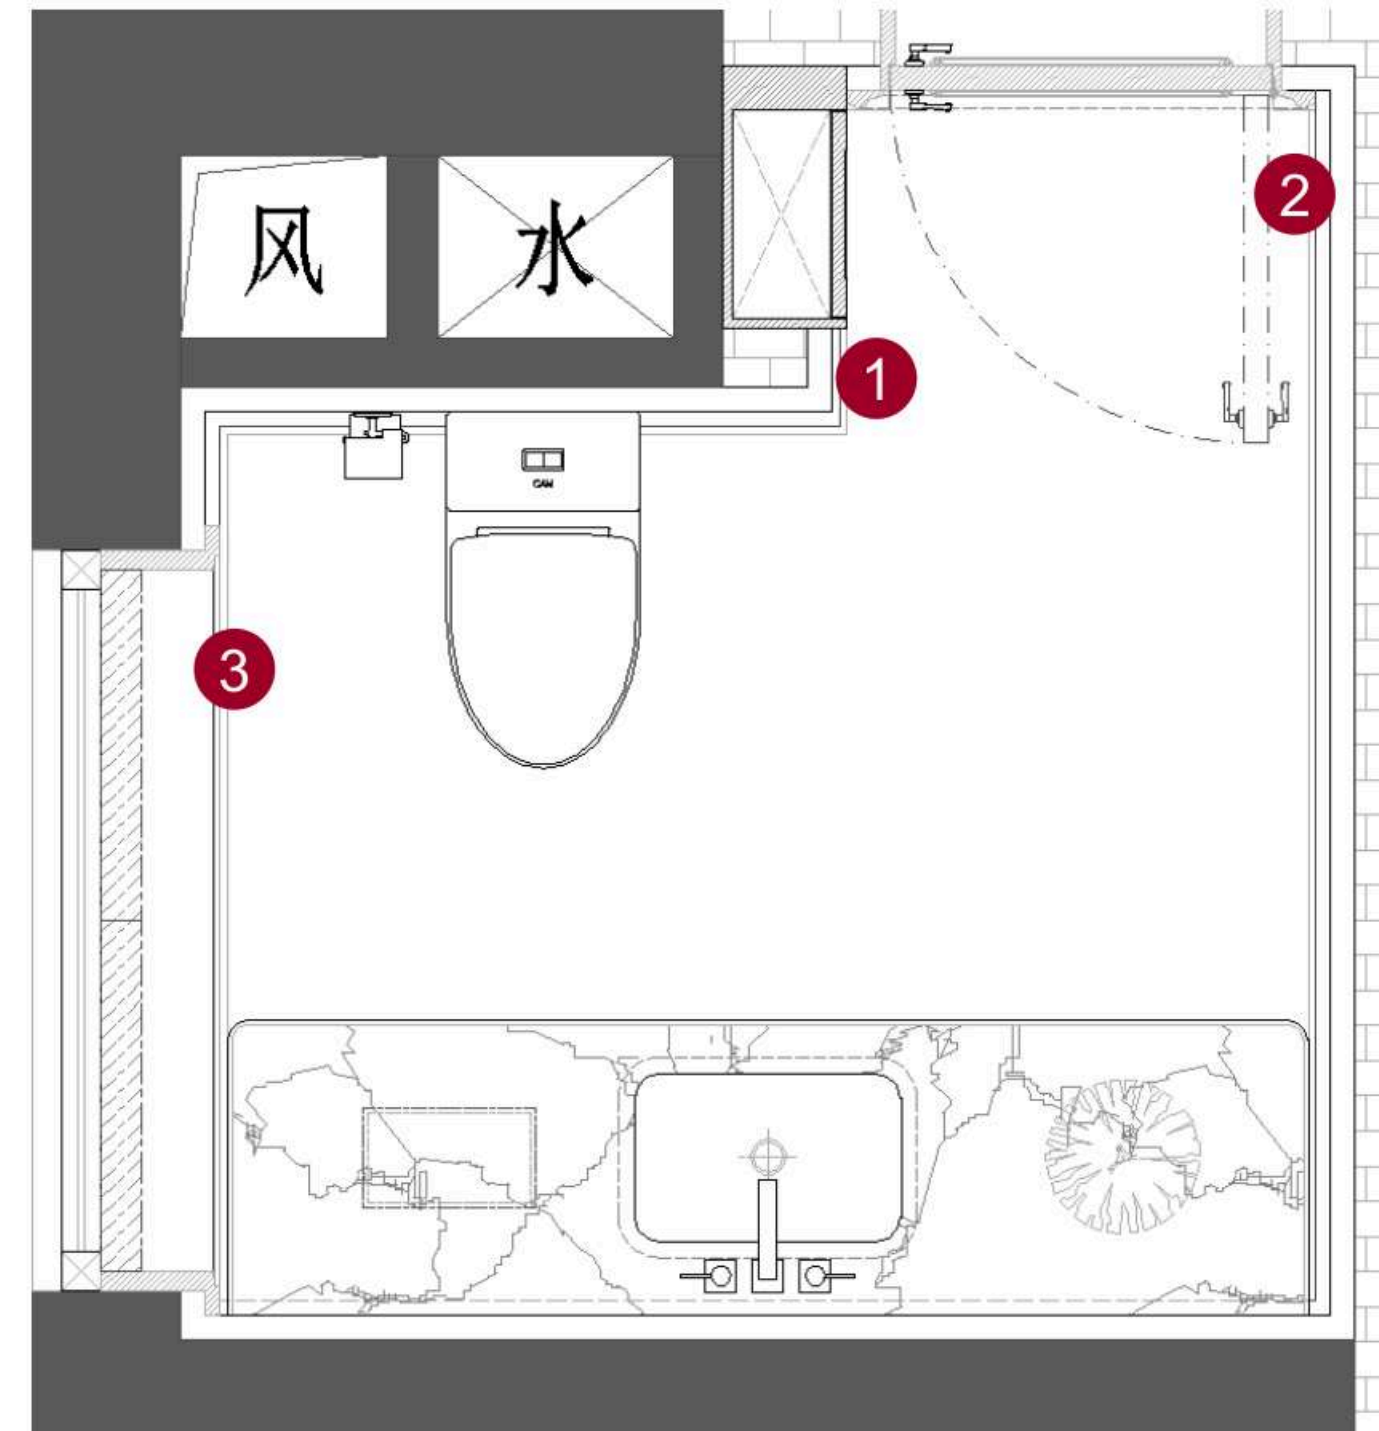


DETAIL THINKING 细节构想

Powder room
客卫


- 台盆细节
- 腰线细节
- **窗套细节**
- 踢脚细节
- 管井检修口
- 分割原则

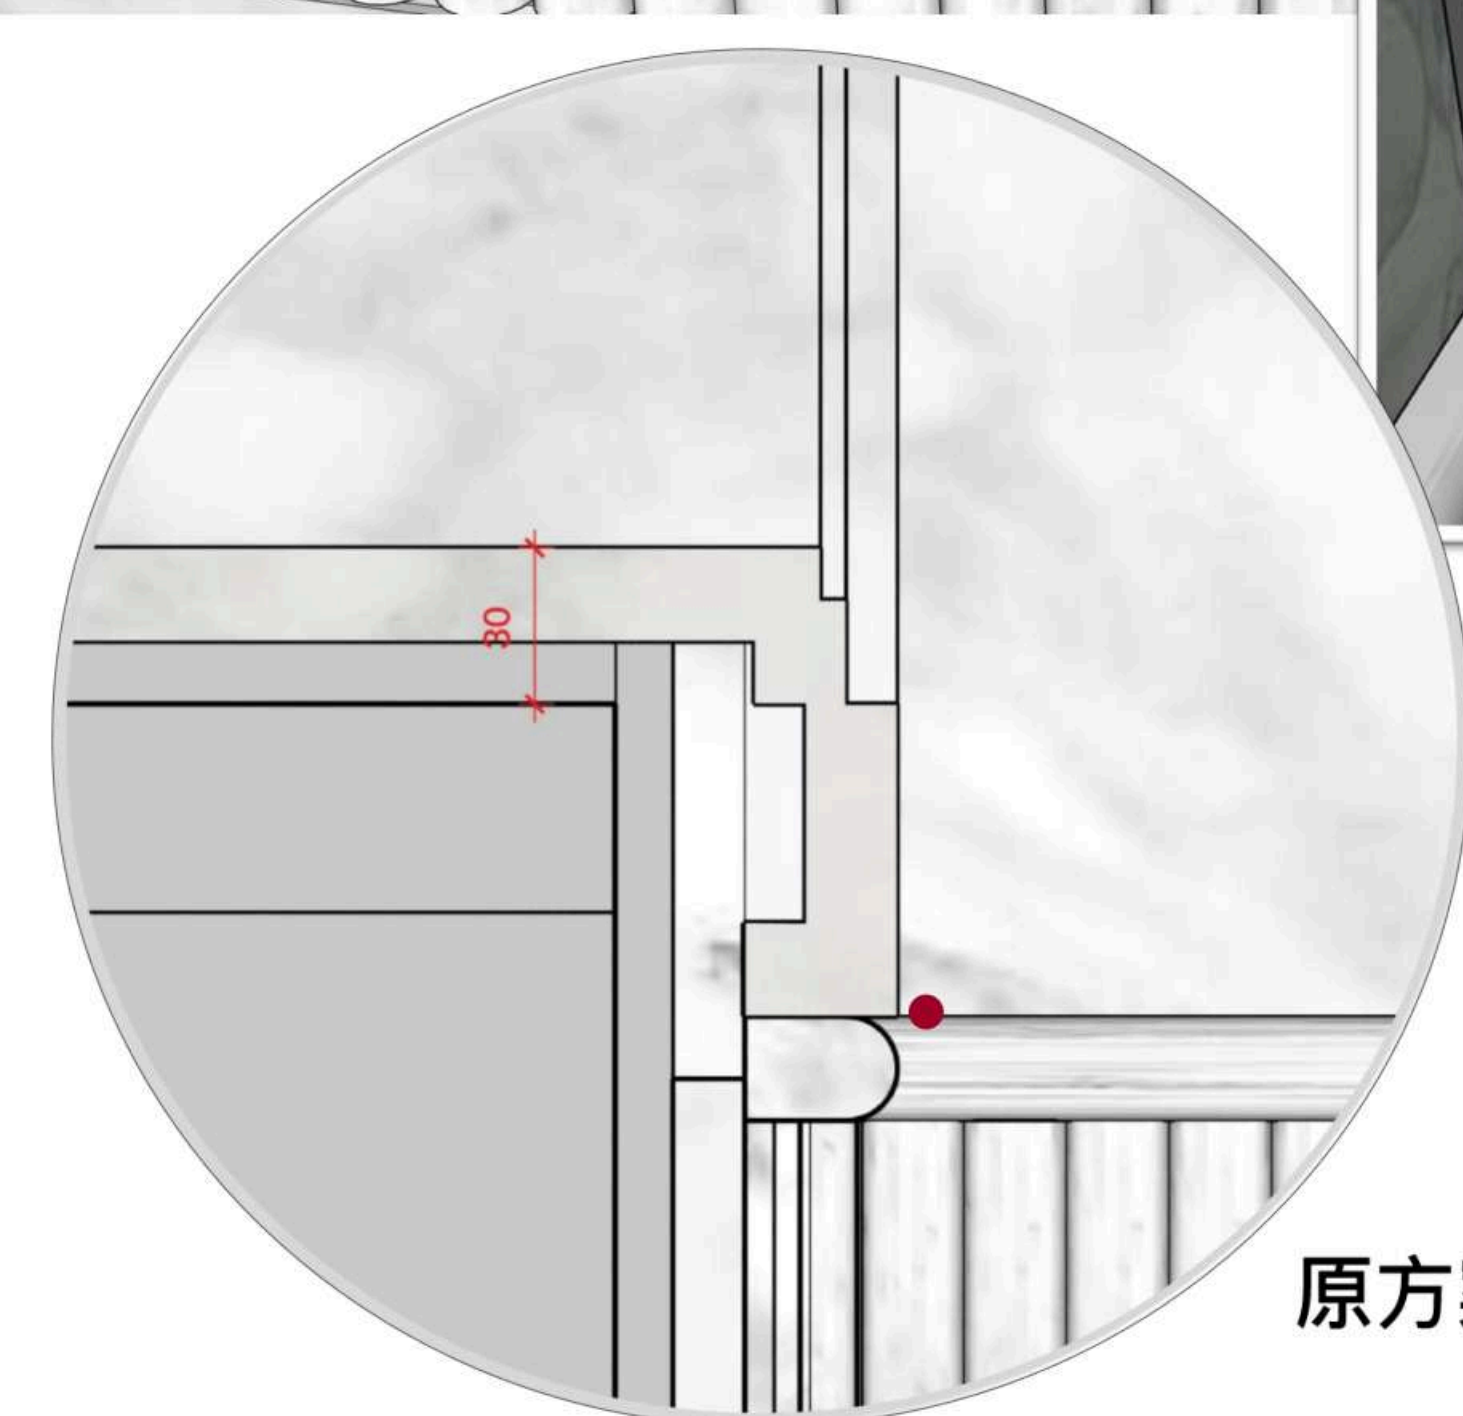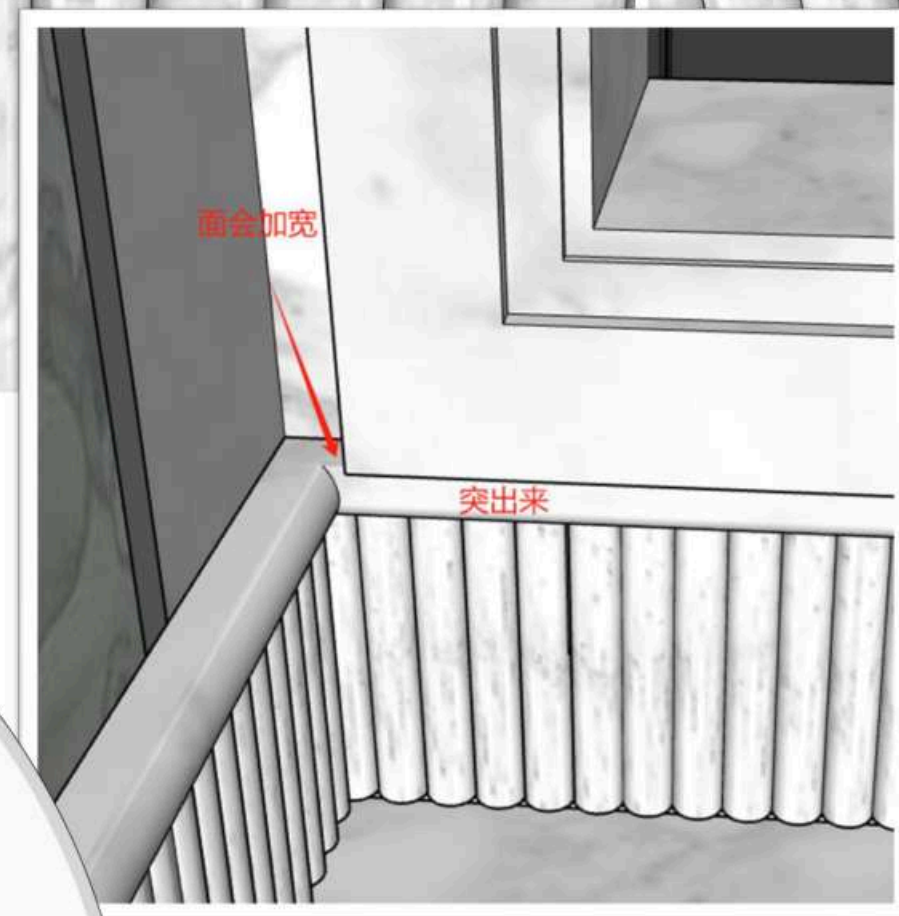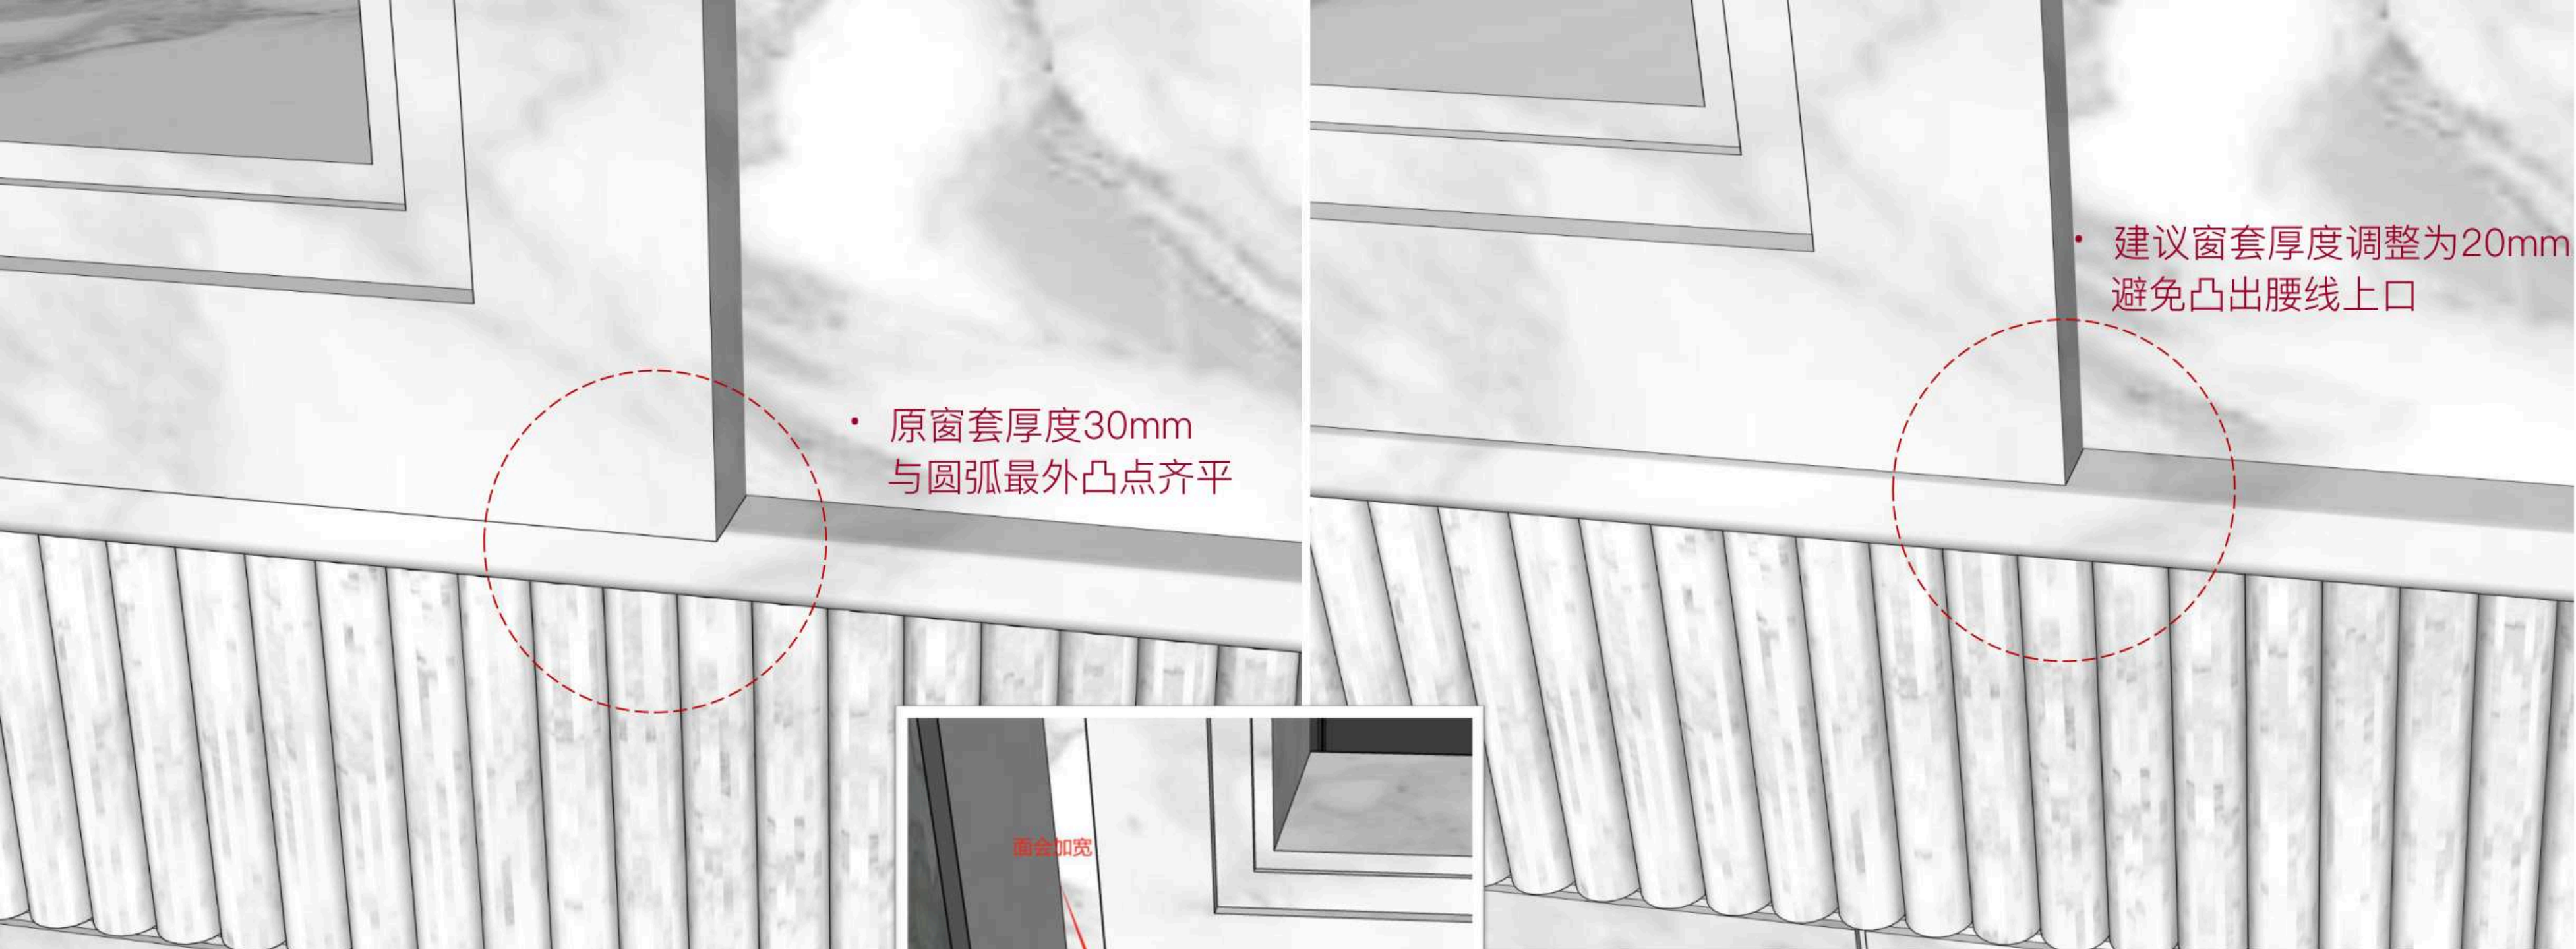

原方案

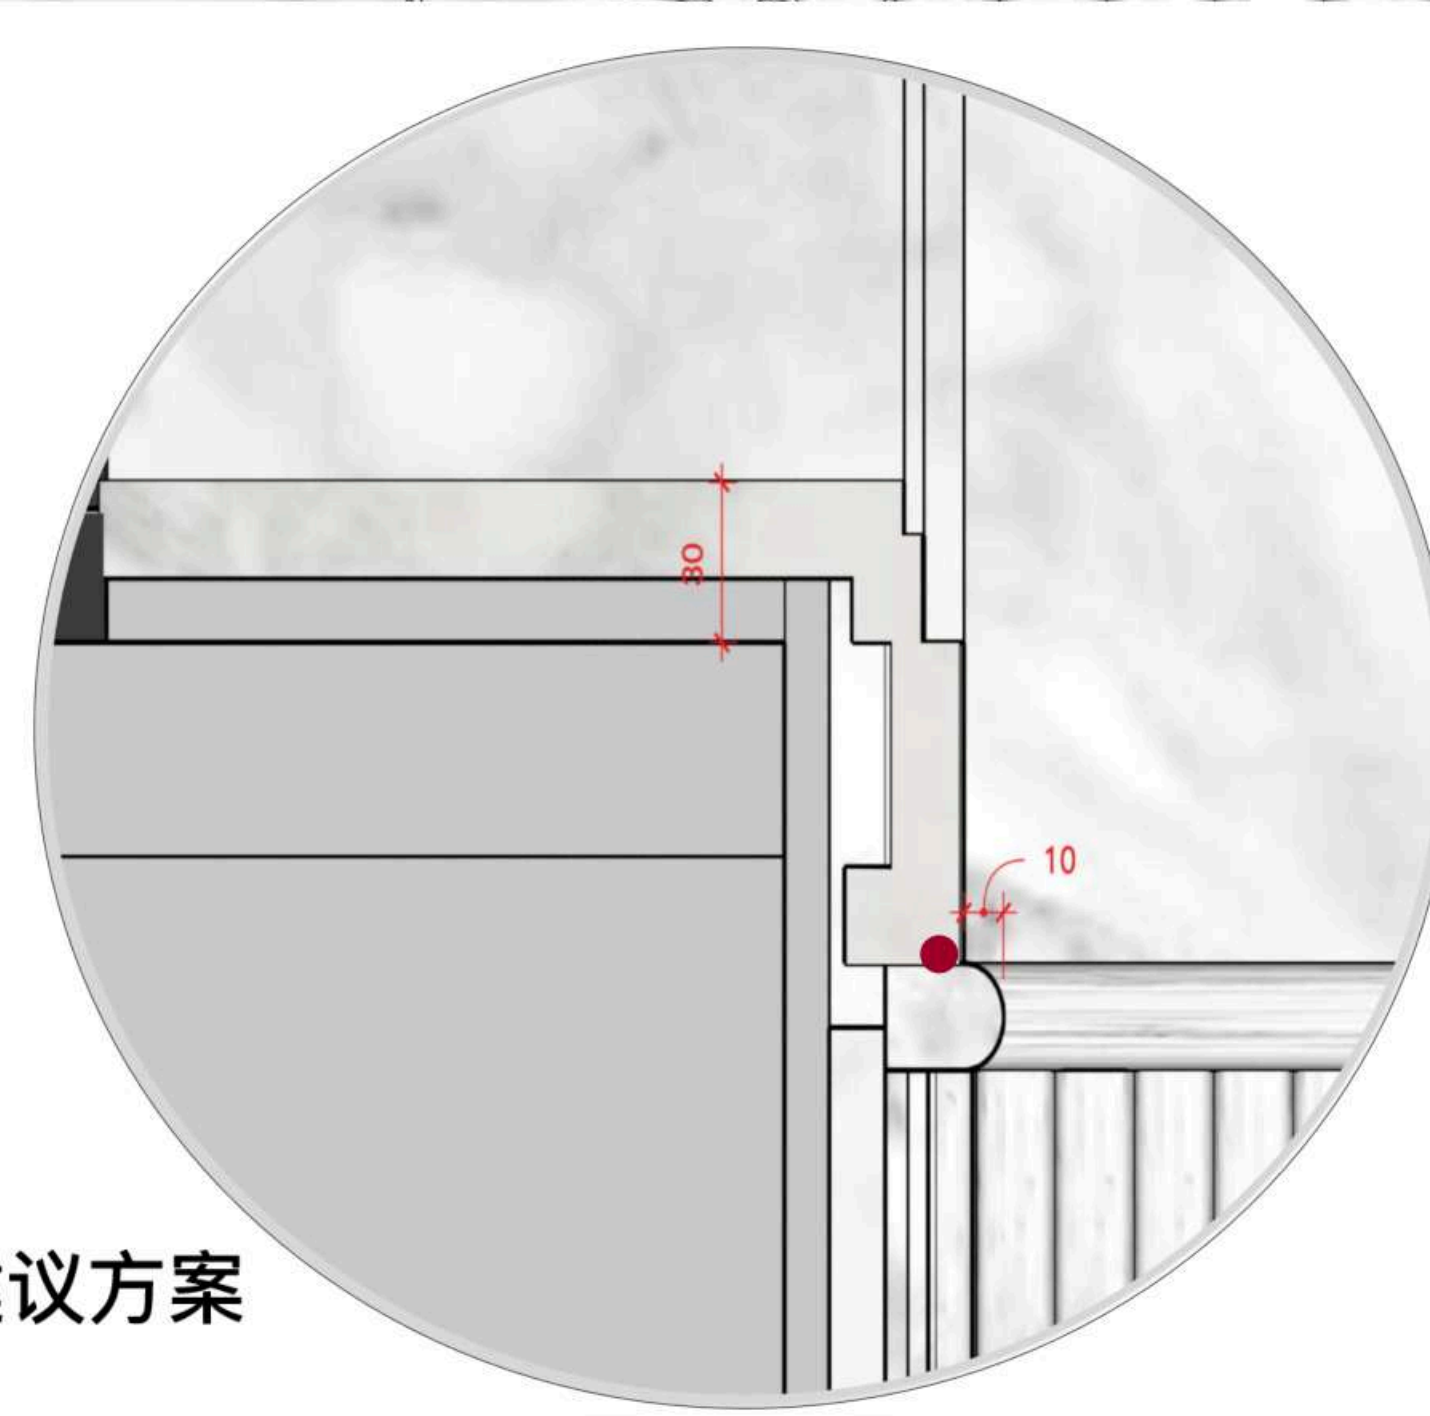


建议方案

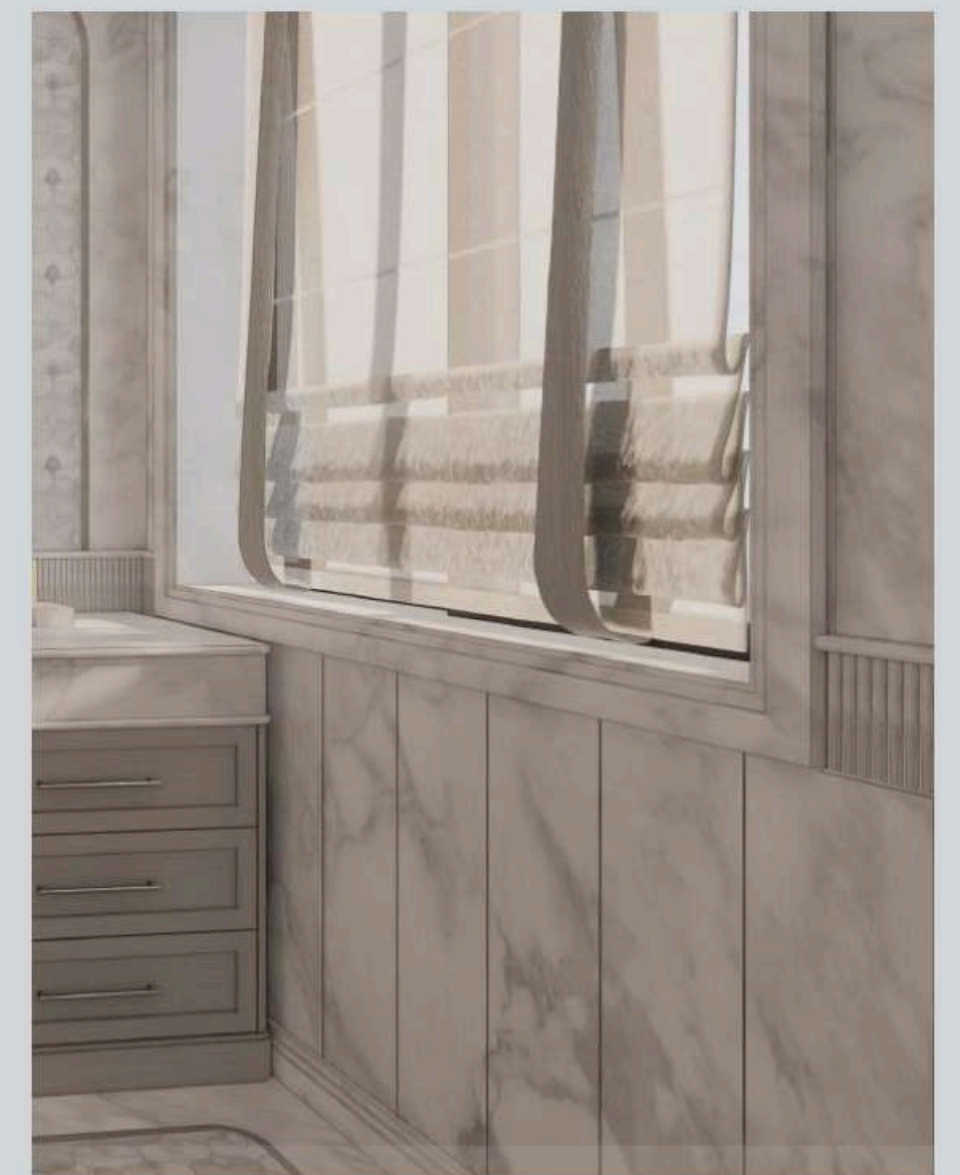

DETAIL THINKING 细节构想

Powder room
客卫

- 台盆细节
- 腰线细节
- 窗套细节
- **踢脚线细节**
- 管井检修口
- 分割原则

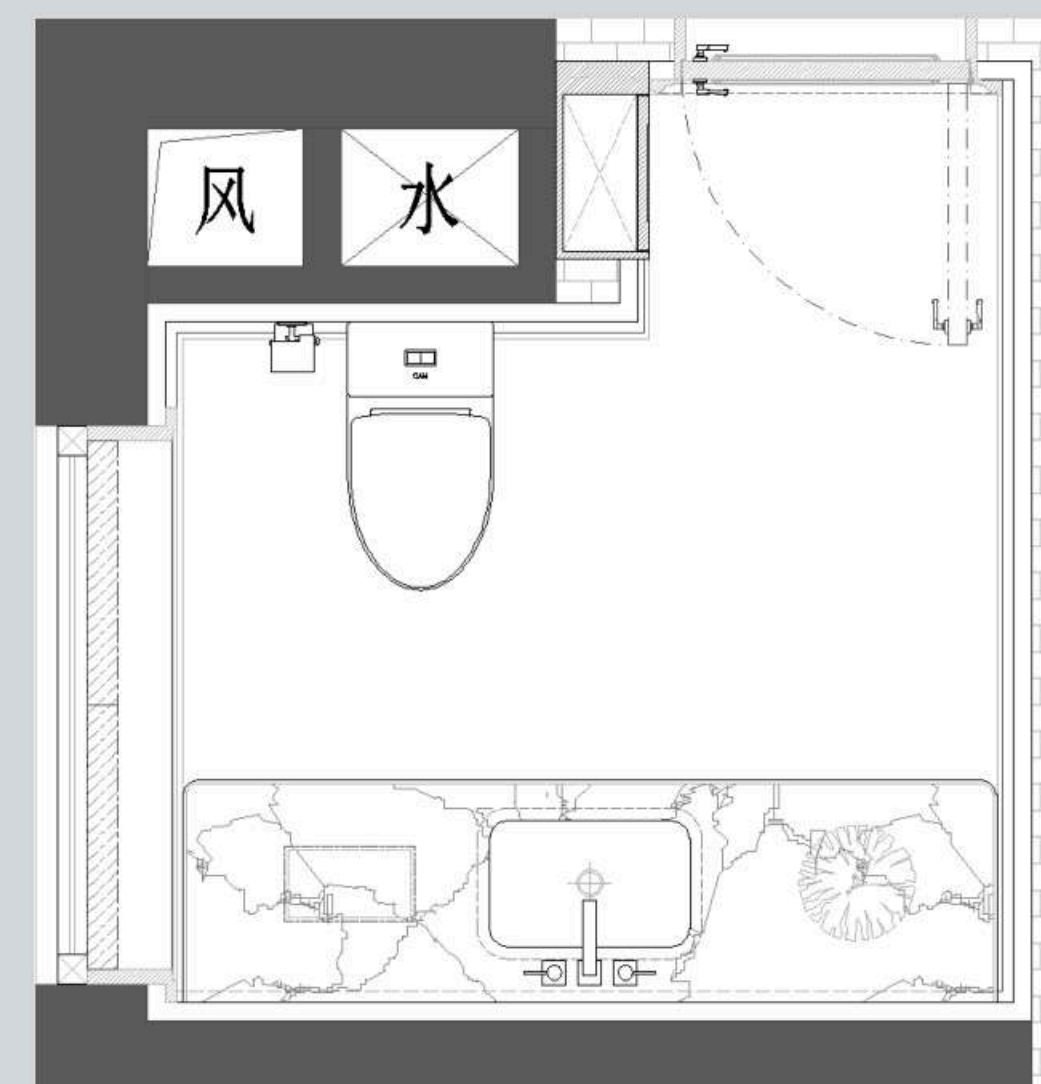

HIBORNI




- 原石材踢脚线高度150mm
柜体踢脚线高度100mm

- 石材踢脚线高度调整100mm
柜体踢脚线高度100mm

DETAIL THINKING 细节构想

Powder room
客卫



- 台盆细节
- 腰线细节
- 窗套细节
- 踢脚线细节
- 管井检修口
- 分割原则

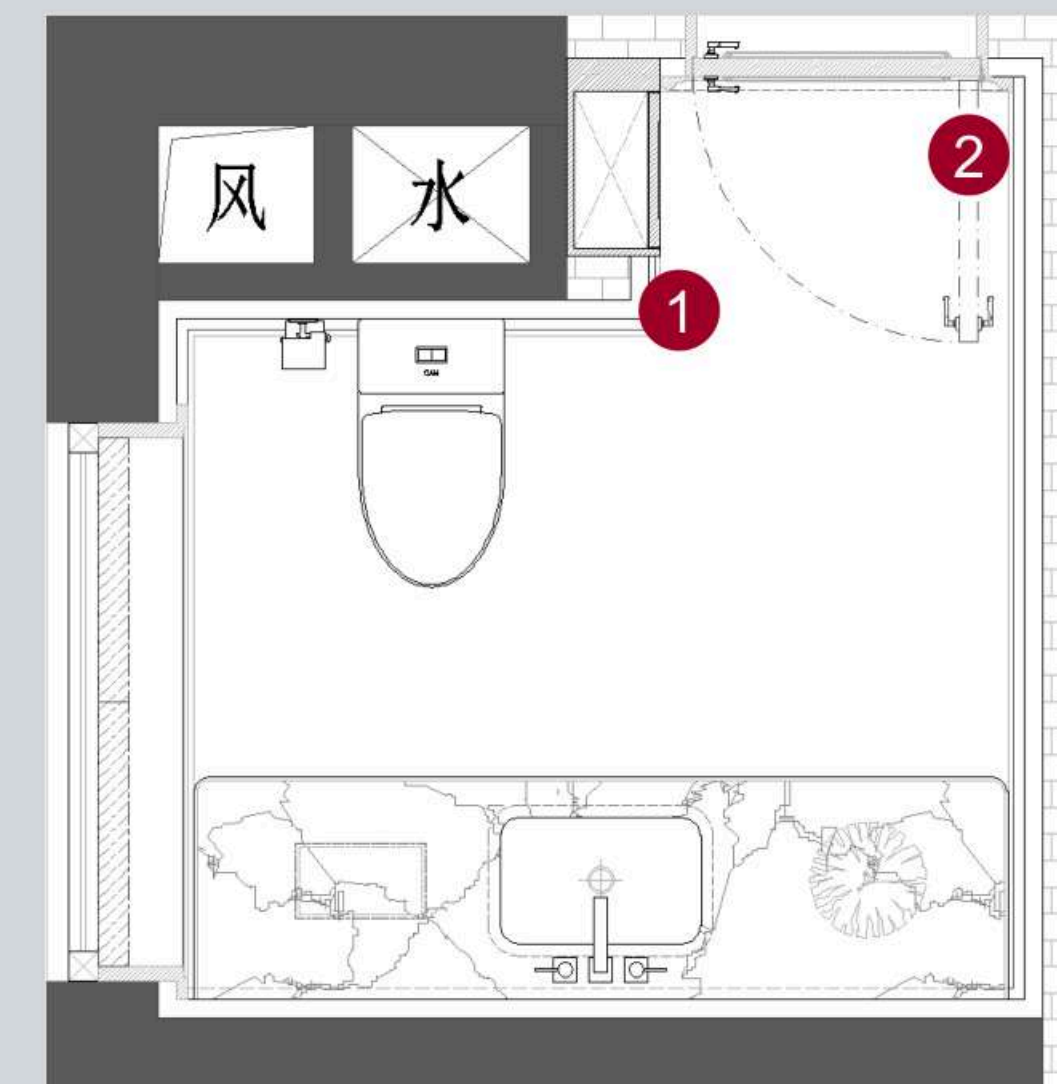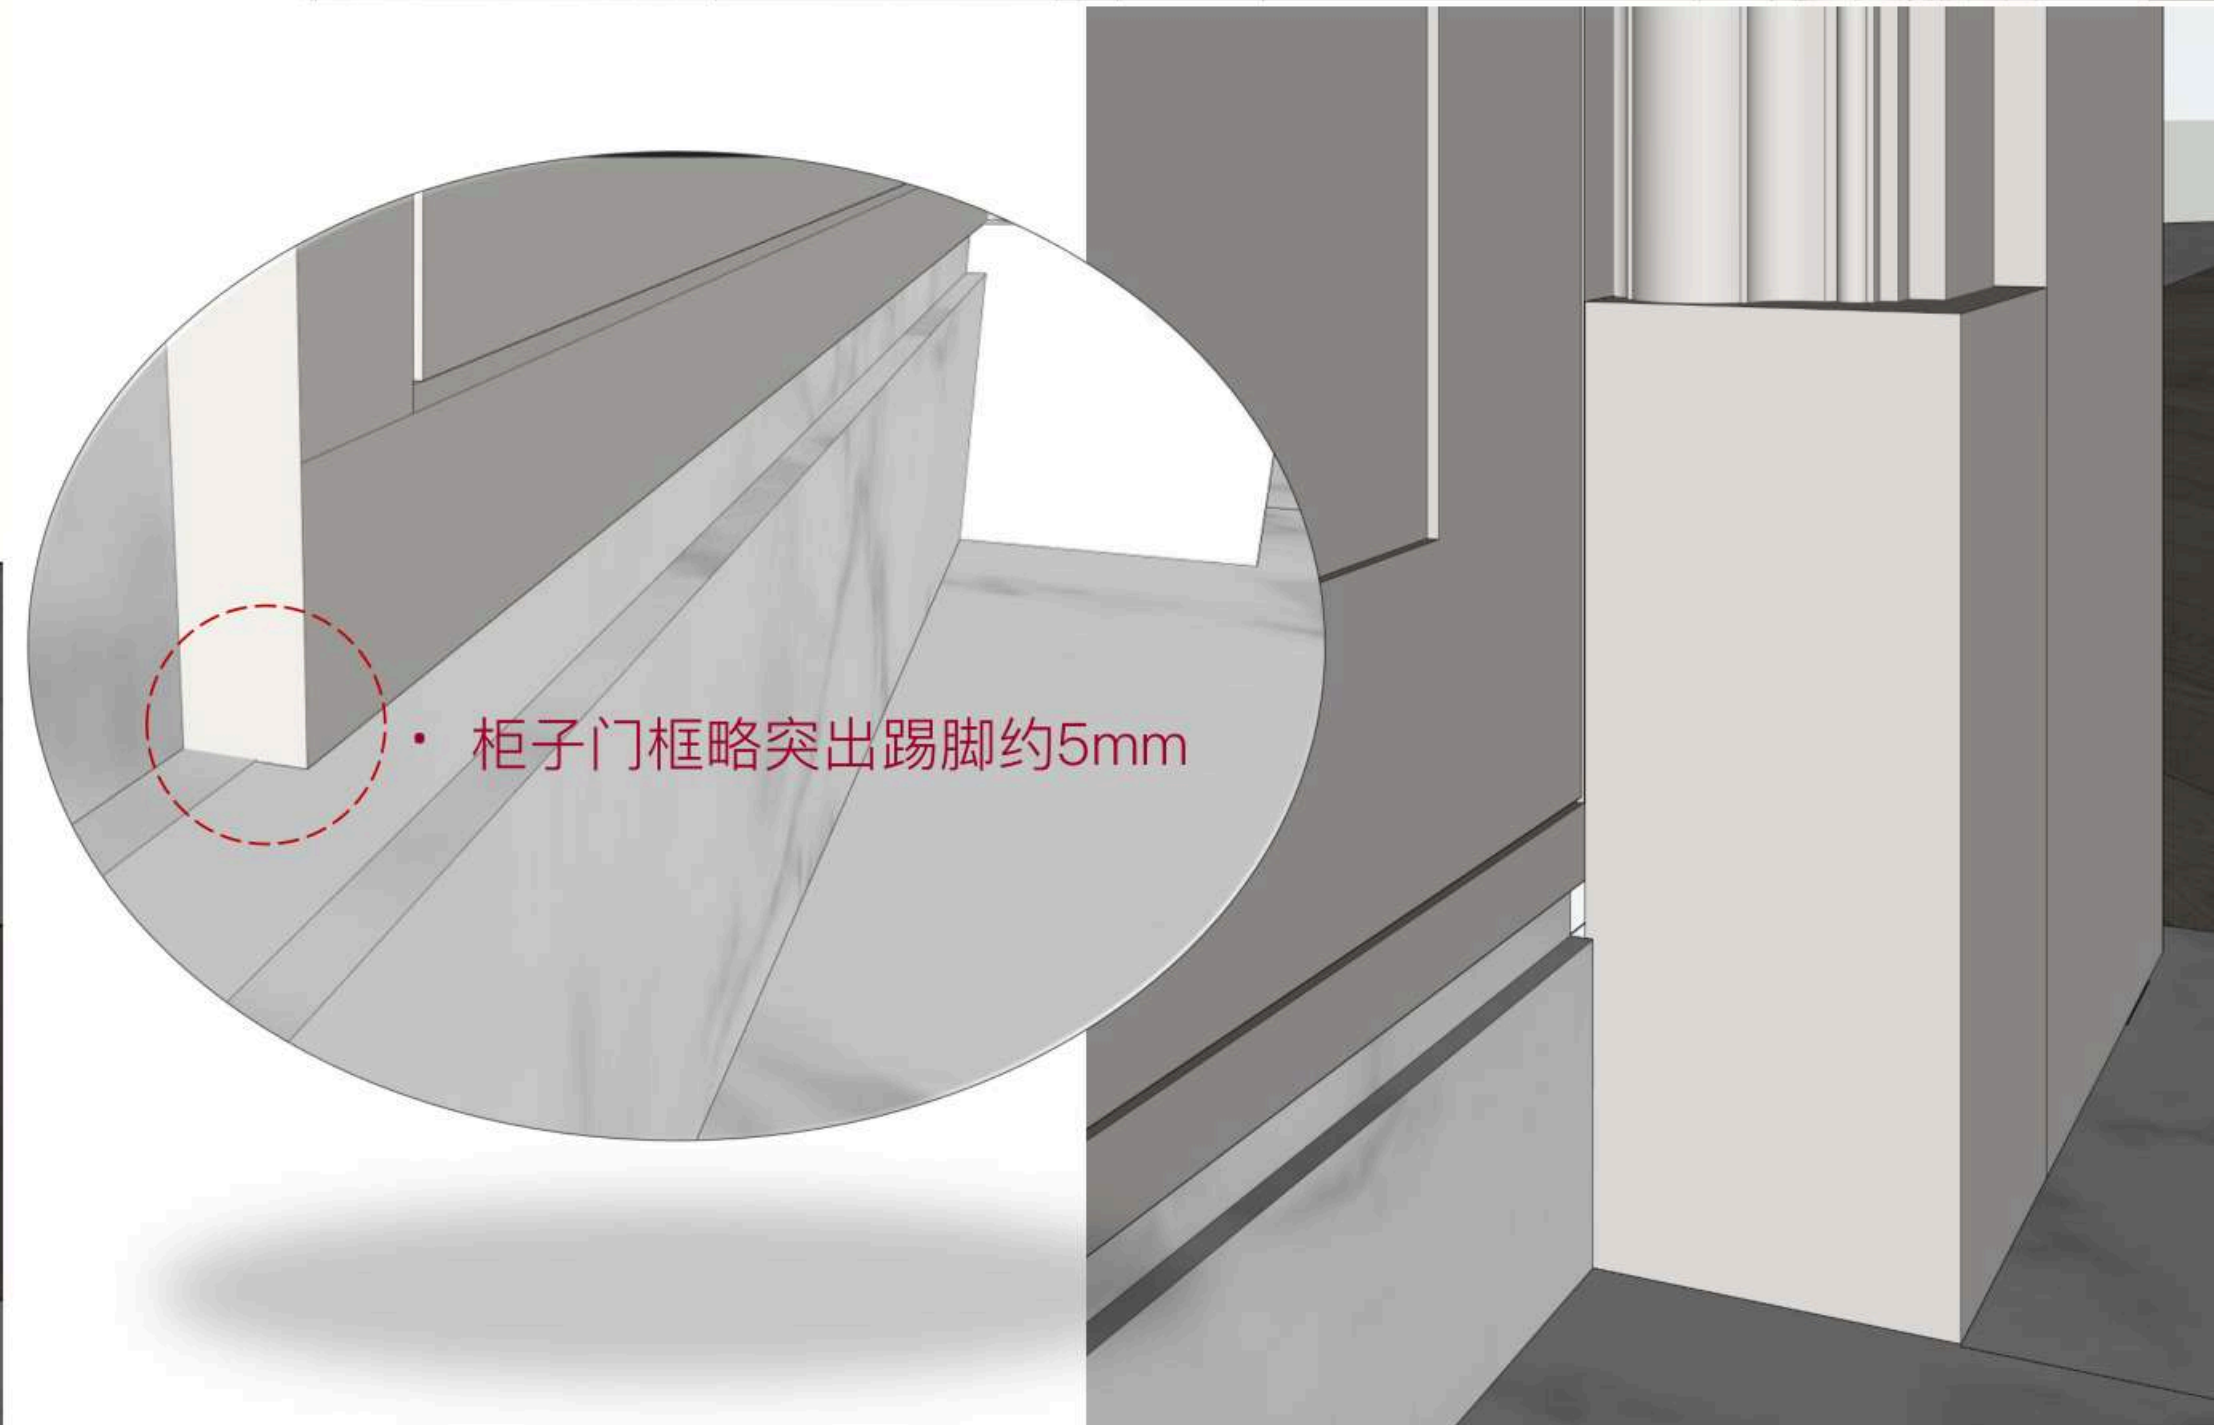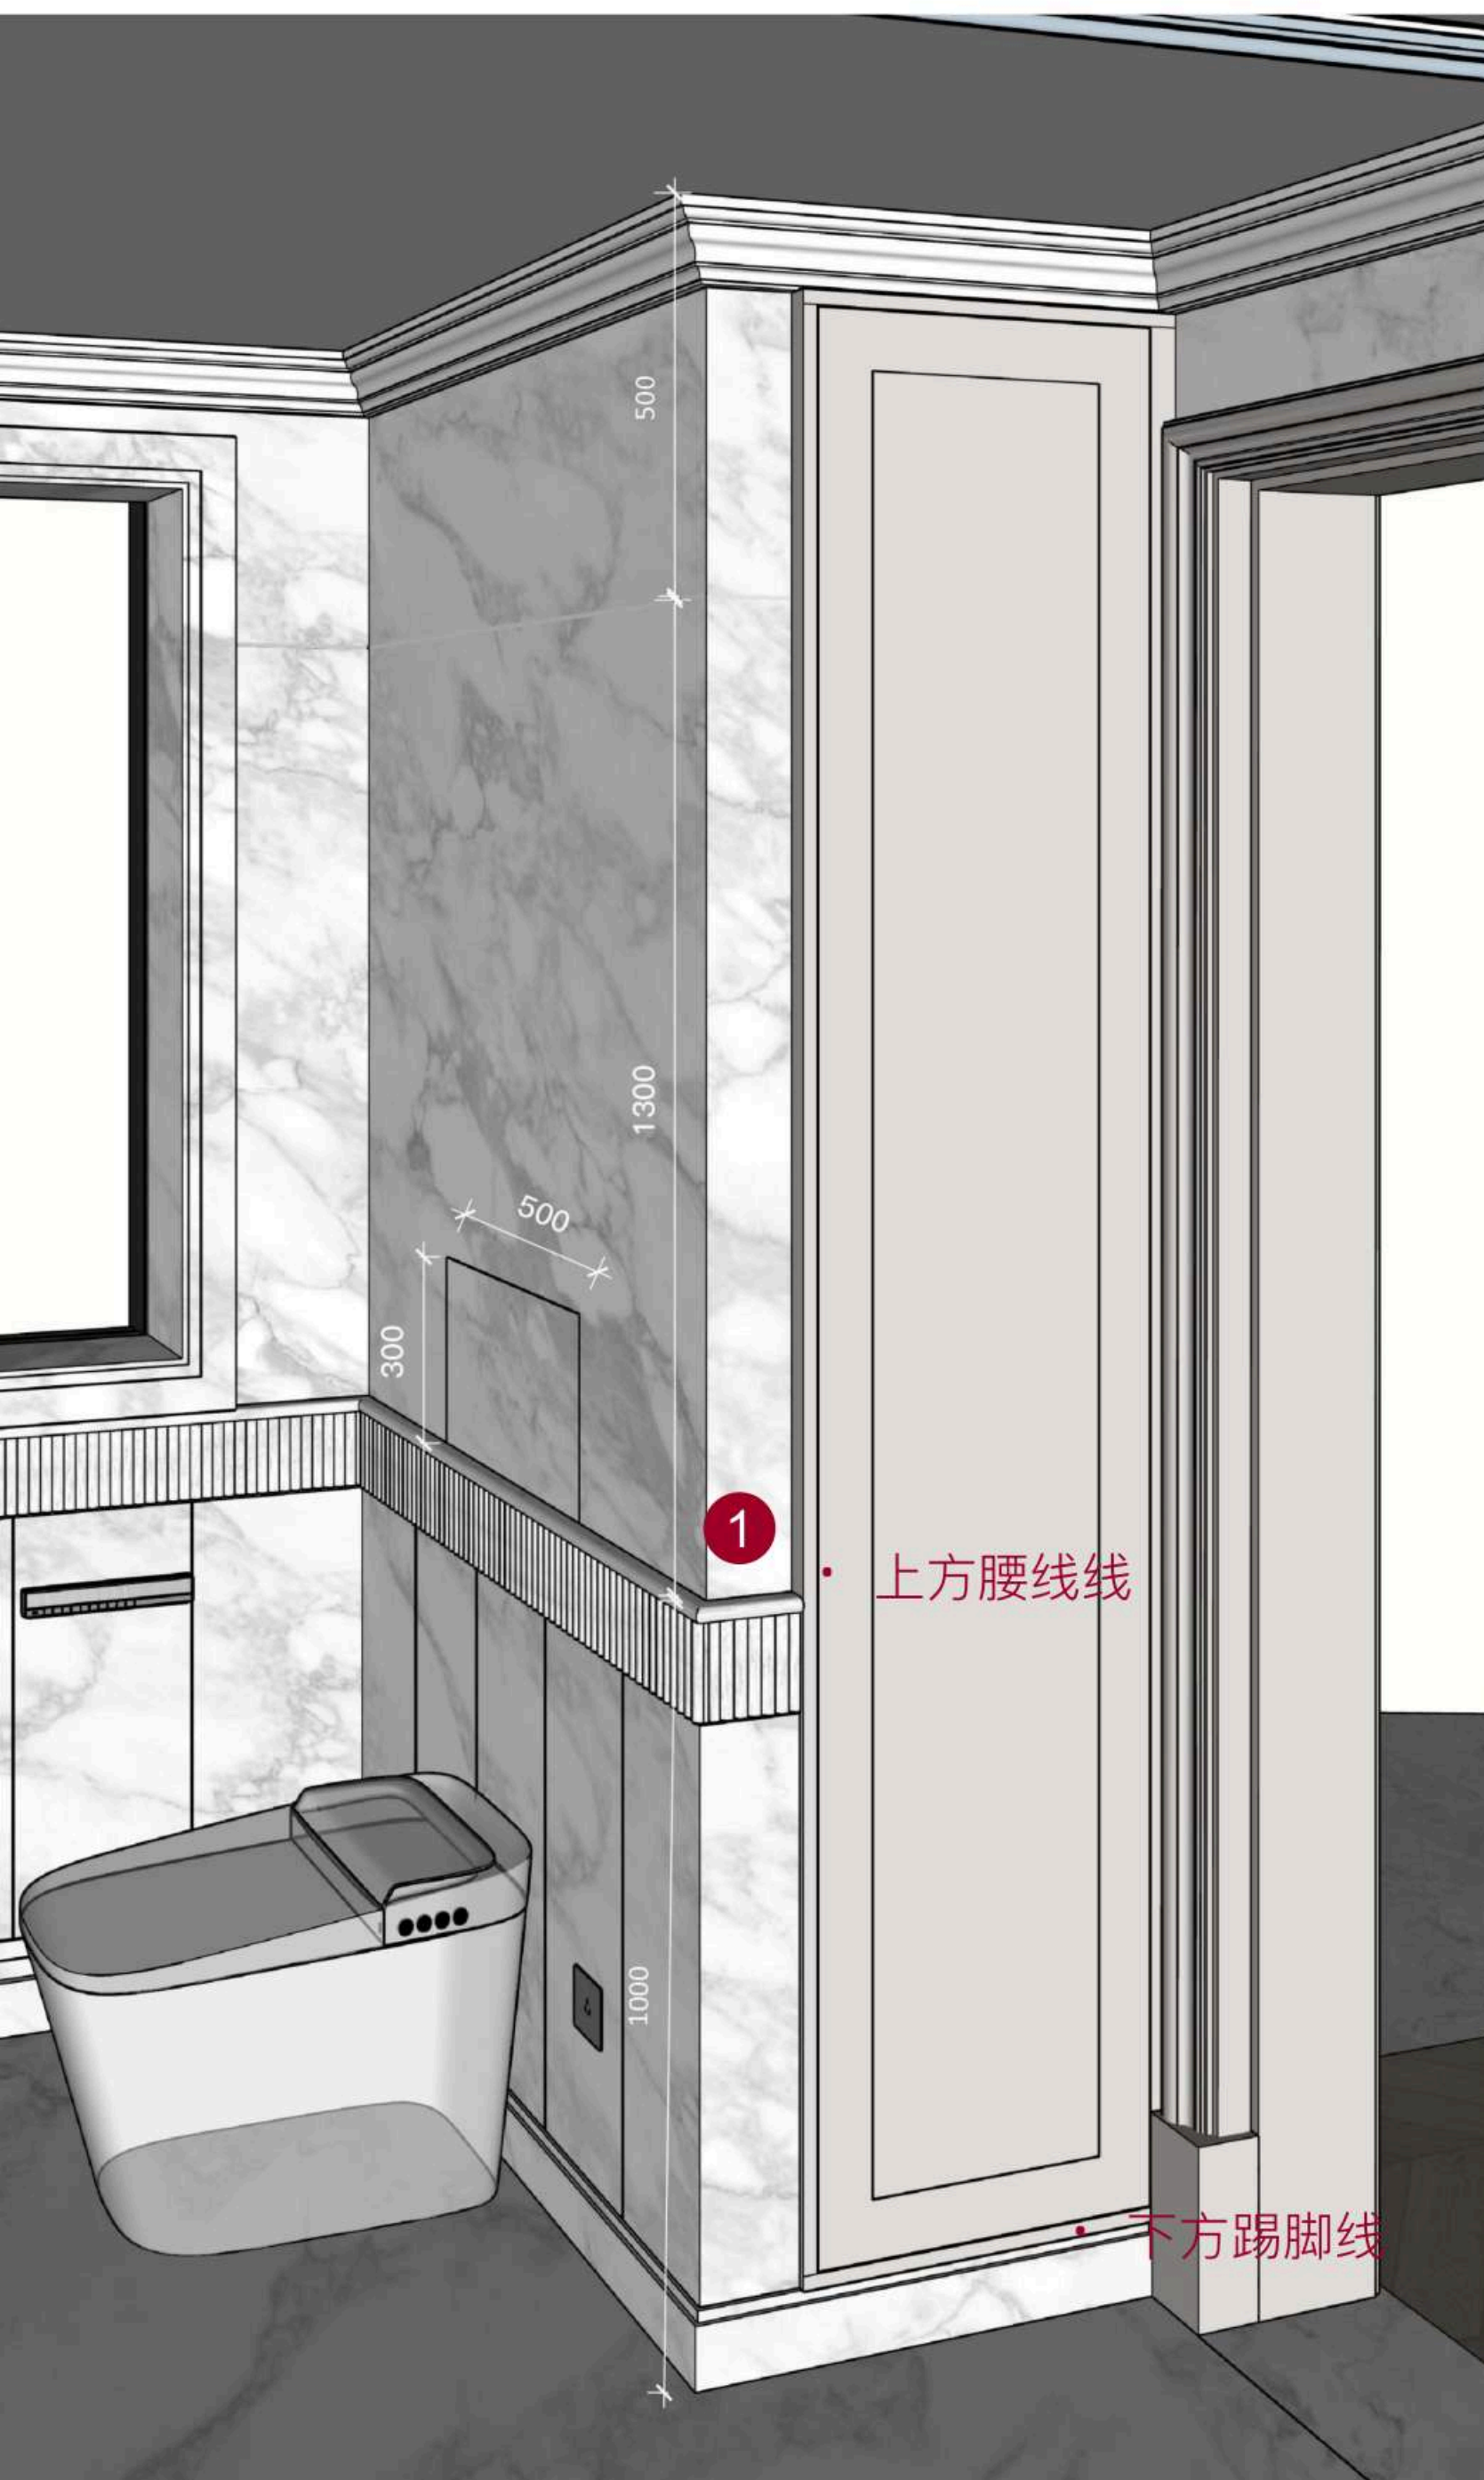

DETAIL THINKING 细节构想

Powder room
客卫

- 台盆细节
- 腰线细节
- 窗套细节
- 踢脚线细节
- 管井检修口
- 分割原则

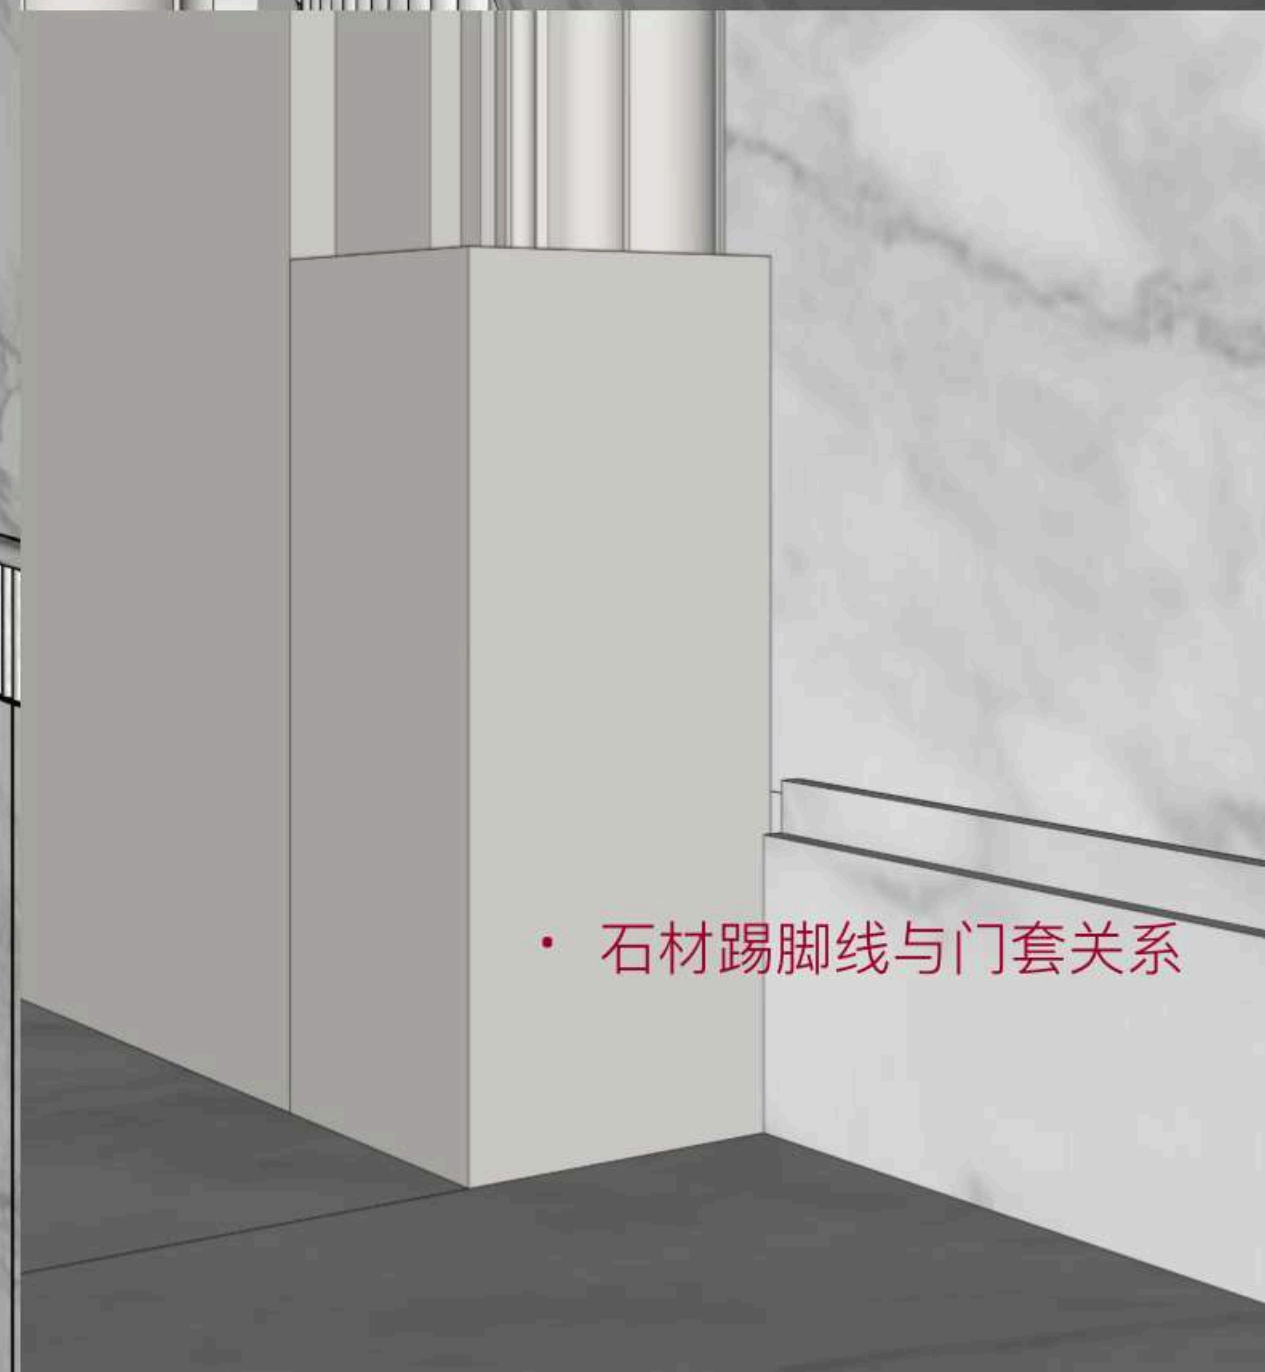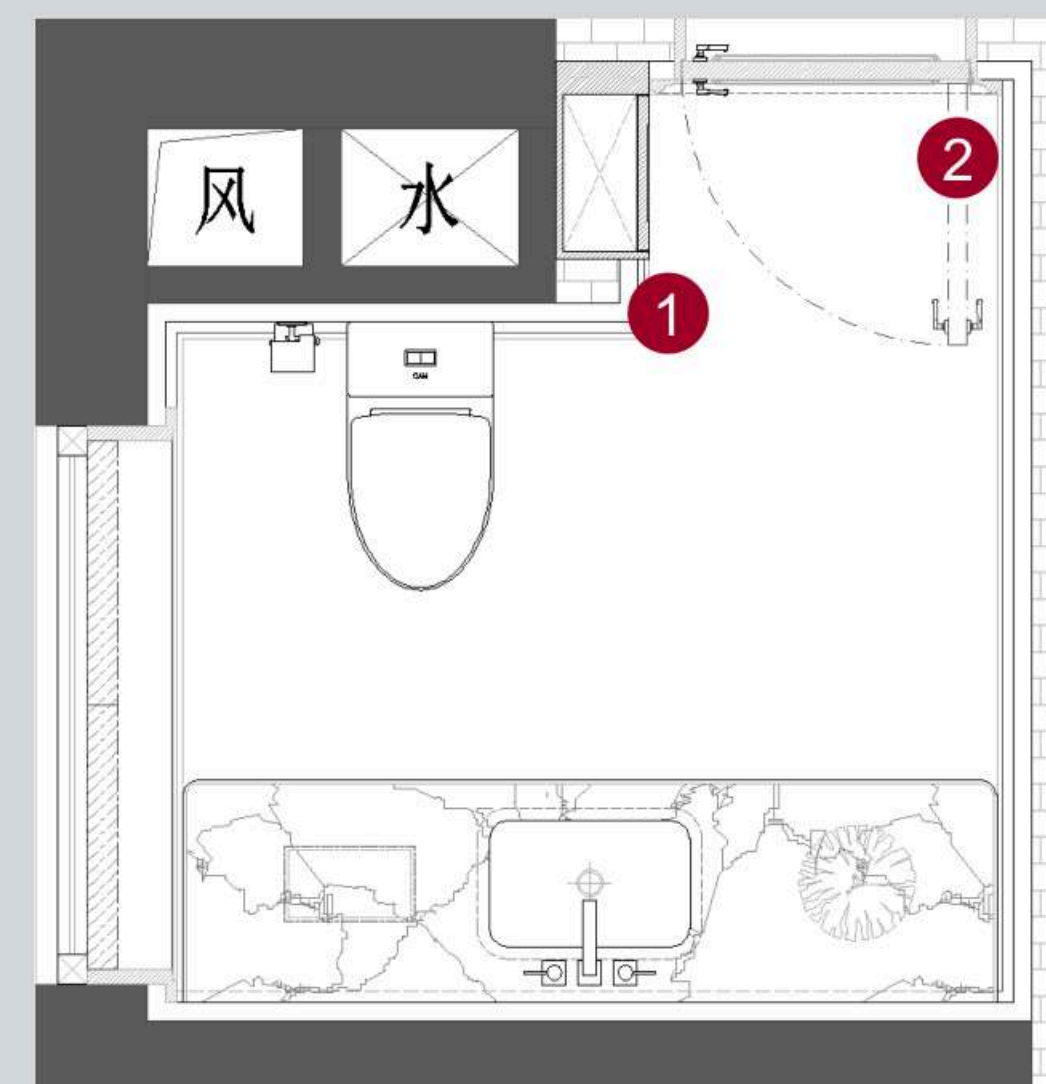


• 石材踢脚线与门套关系

DETAIL THINKING 细节构想

Powder room
客卫



- 台盆细节
- 腰线细节
- 窗套细节
- 踢脚细节
- 管井检修口
- 分割原则

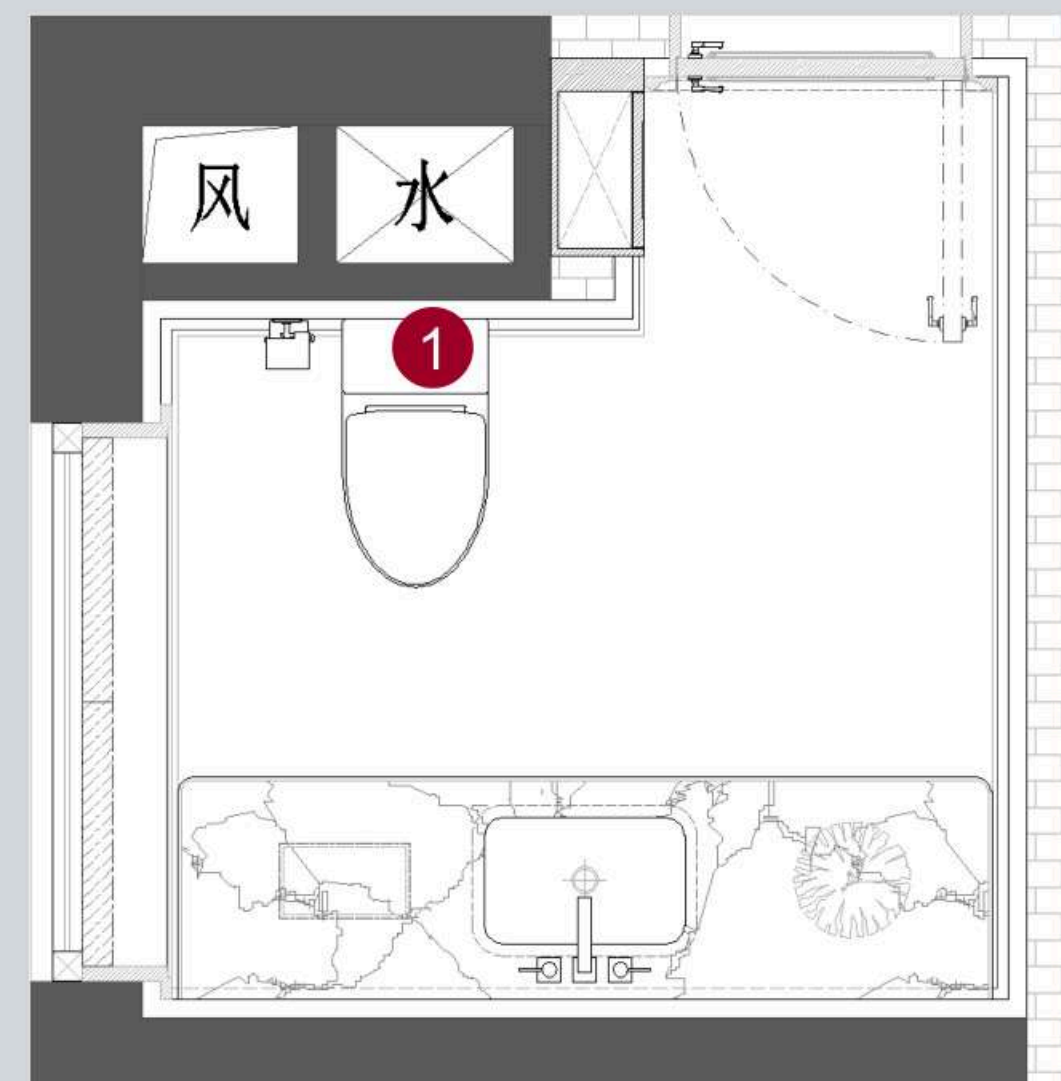

DETAIL THINKING 细节构想

Powder room
客卫


- 台盆细节
- 腰线细节
- 窗套细节
- 踢脚细节
- 管井检修口
- 分割原则

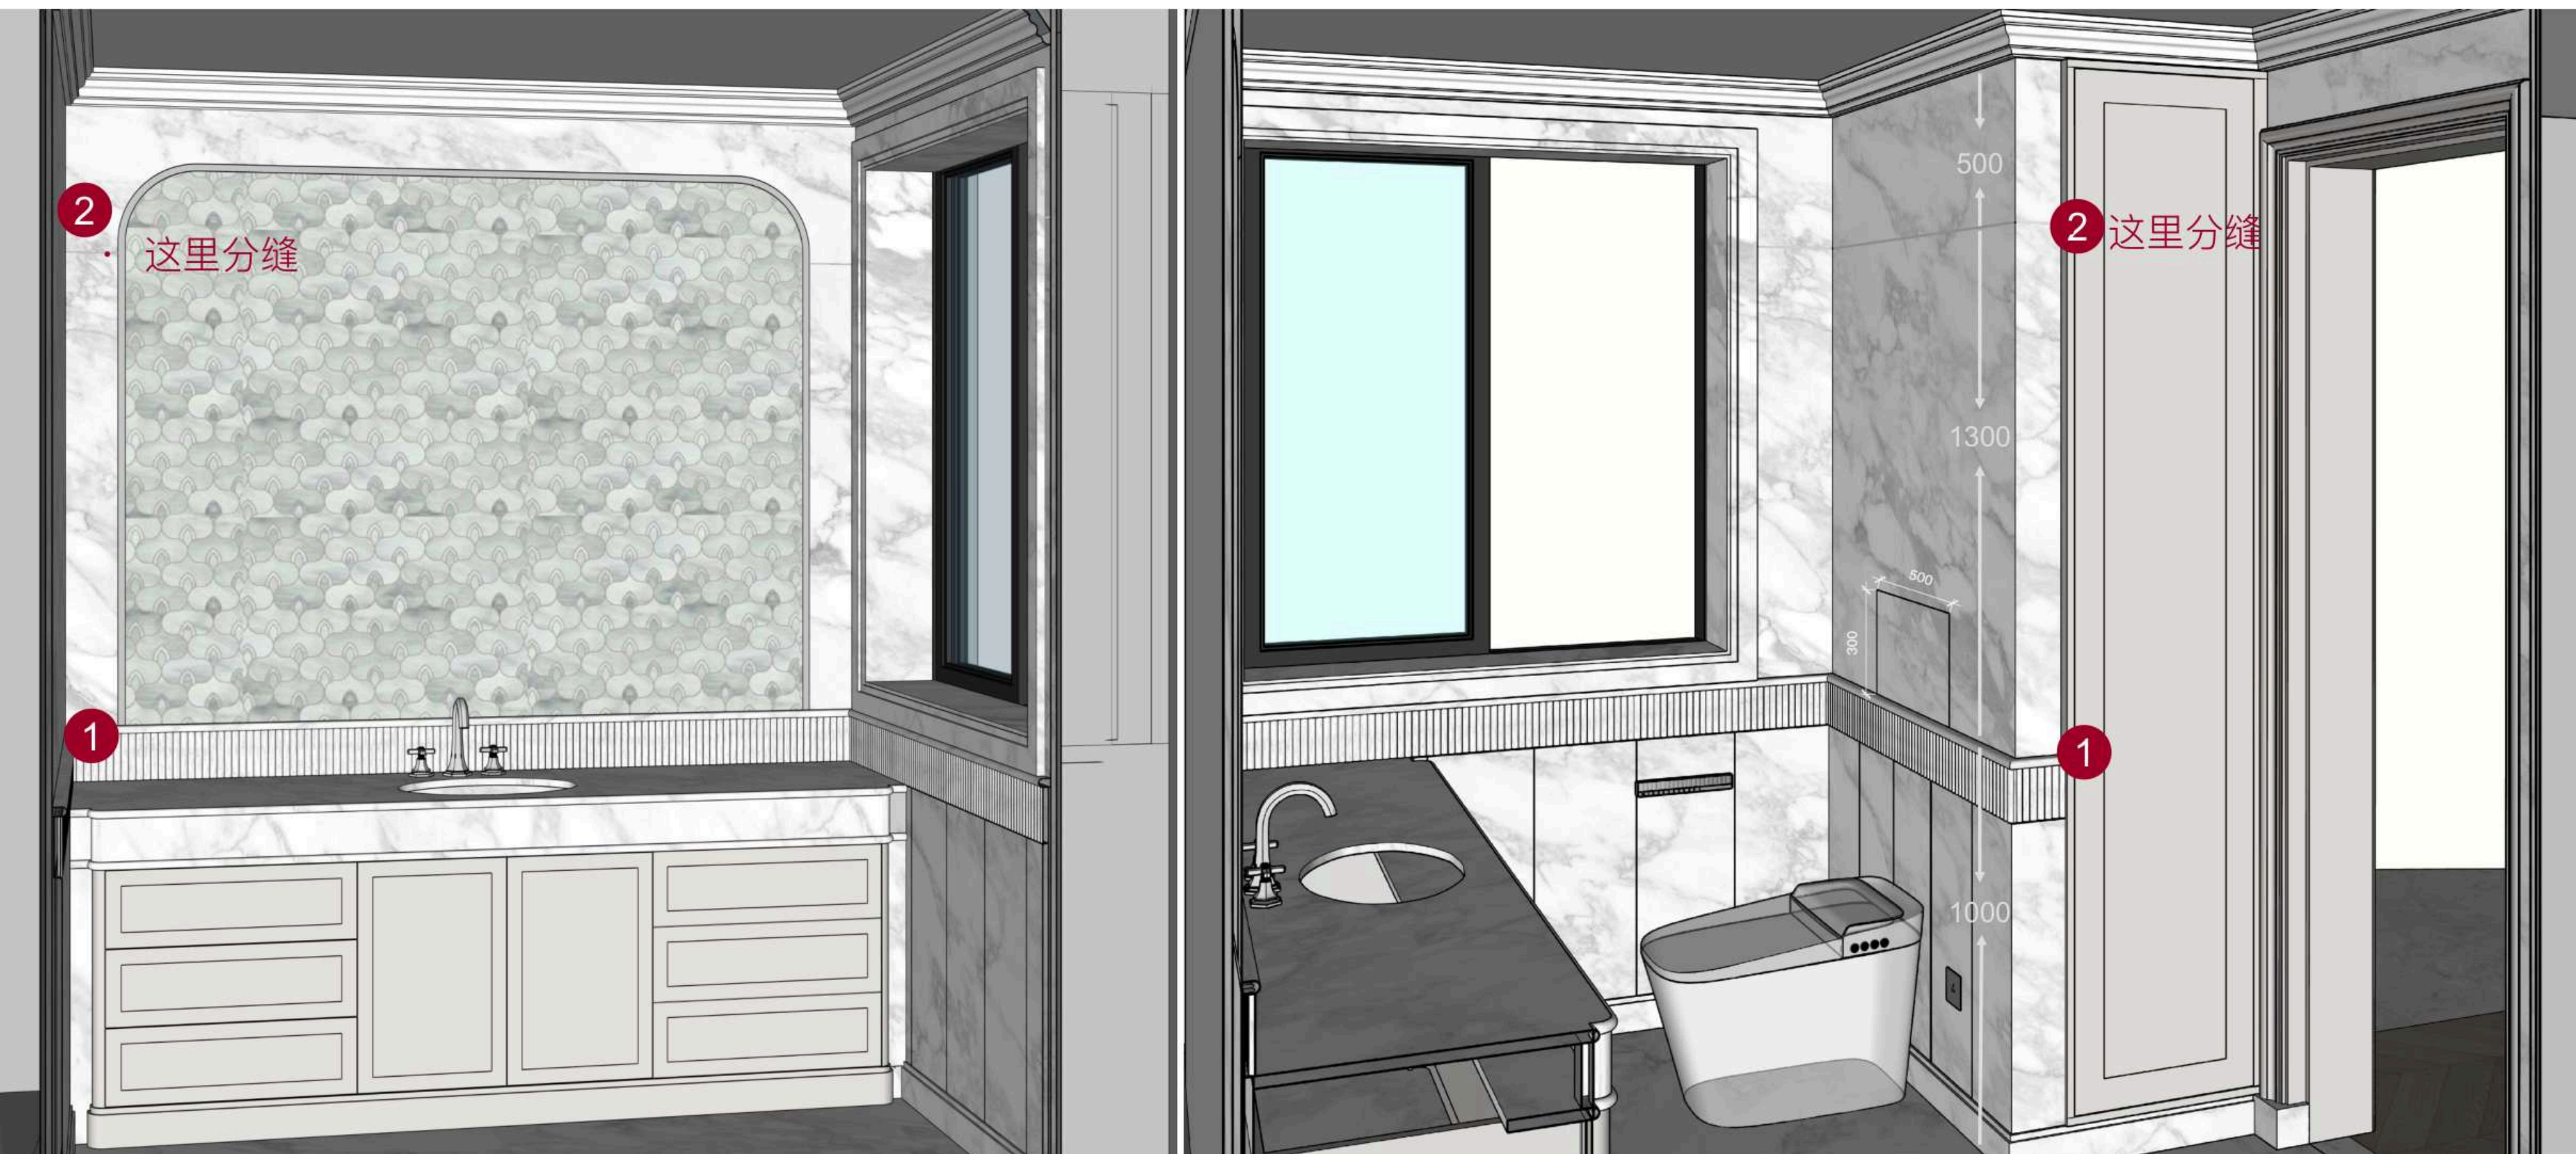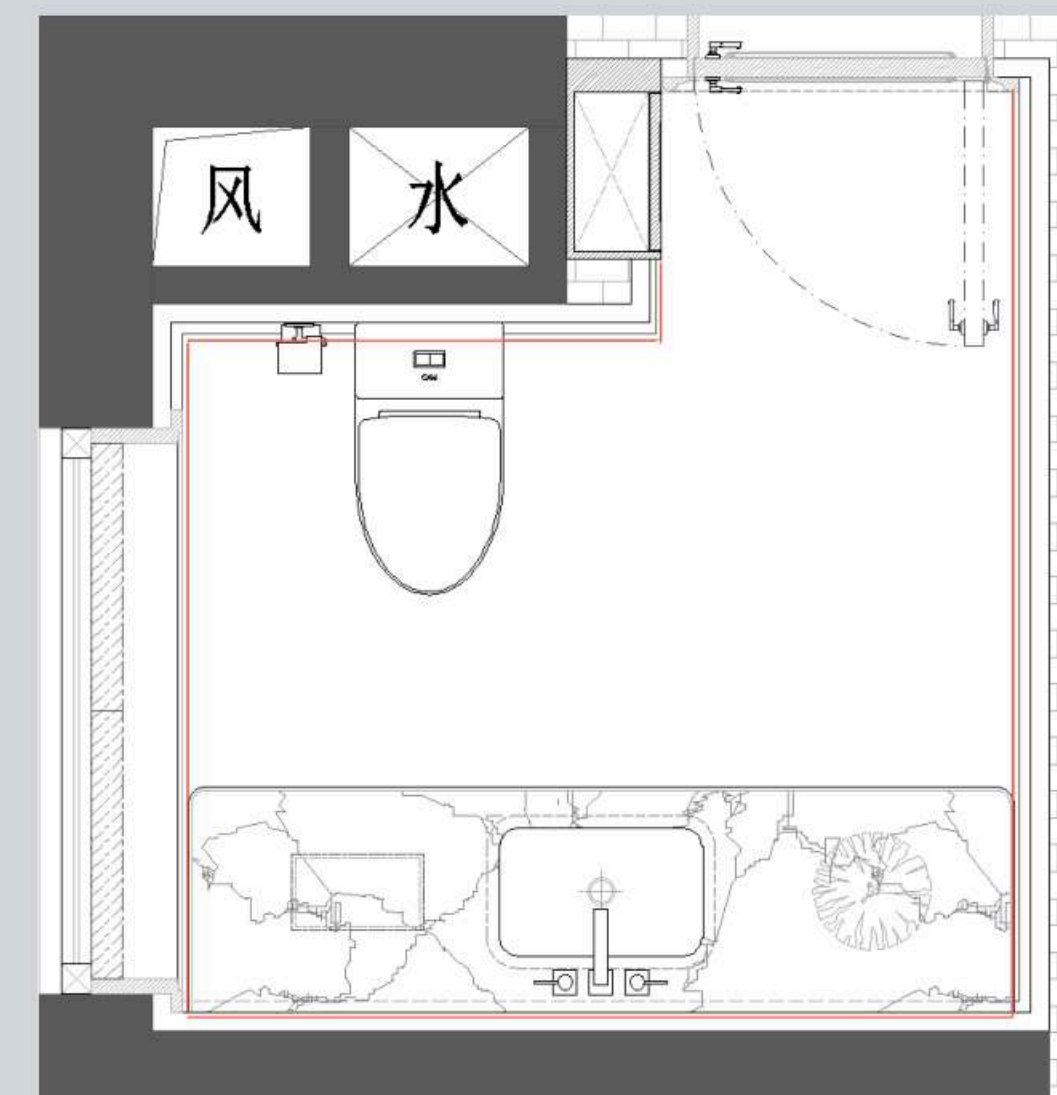

DETAIL THINKING 细节构想

Bathroom for girl
女儿卫


- 台盆柜安装步骤分析
- 腰线细节
- 淋浴房踢脚细节
- 分割原则

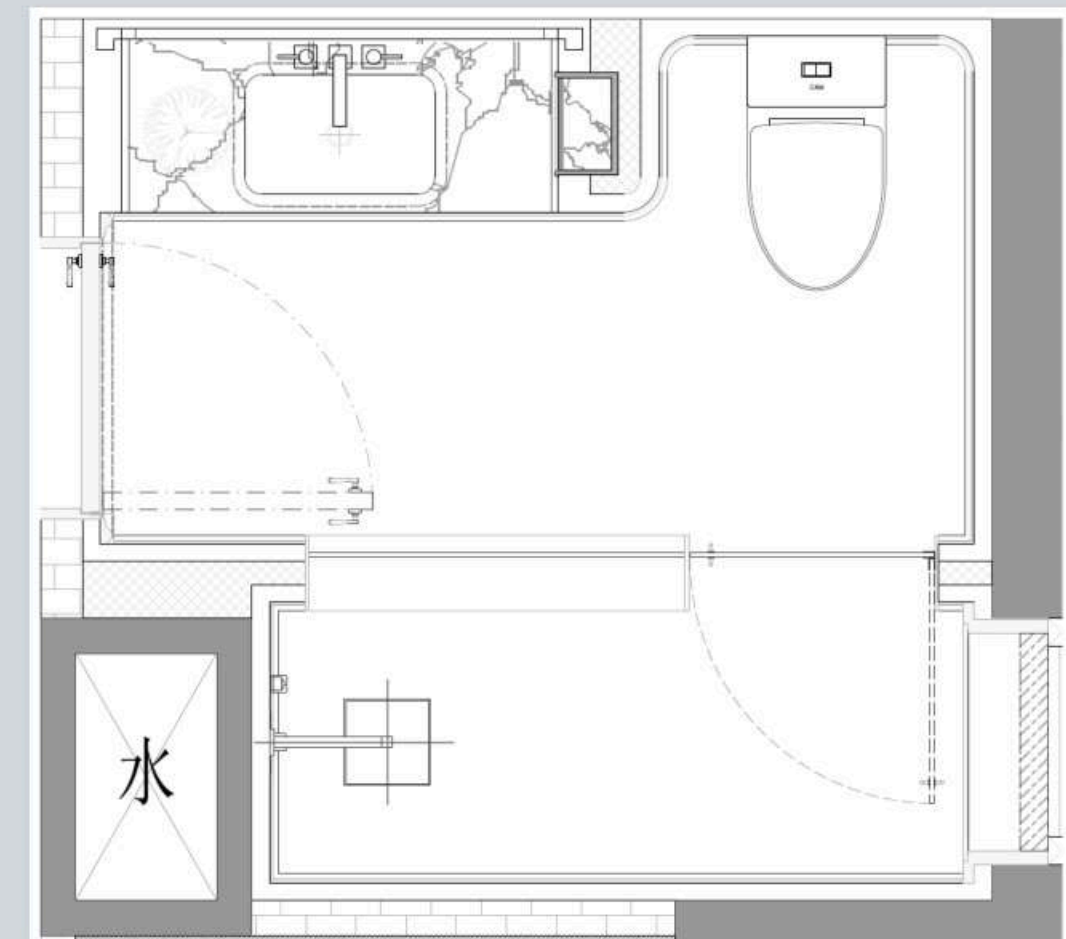


DETAIL THINKING 细节构想

Bathroom for girl
女儿卫


- 台盆柜安装步骤分析
- 腰线细节
- 淋浴房踢脚细节
- 分割原则
- 铝模板

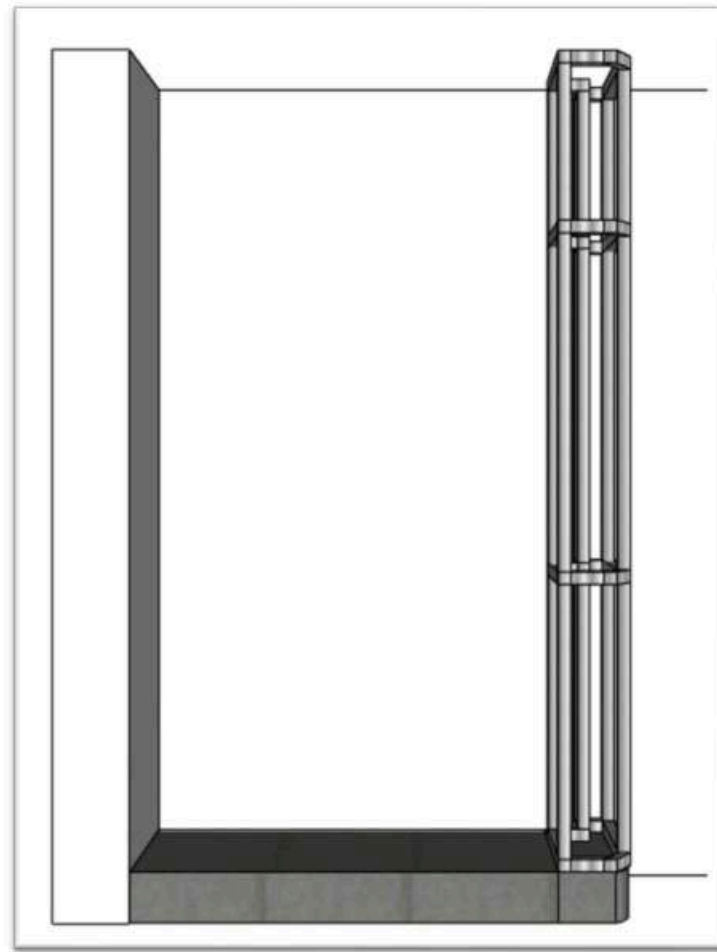


Step.1 浇筑水泥地台
并焊烧钢架

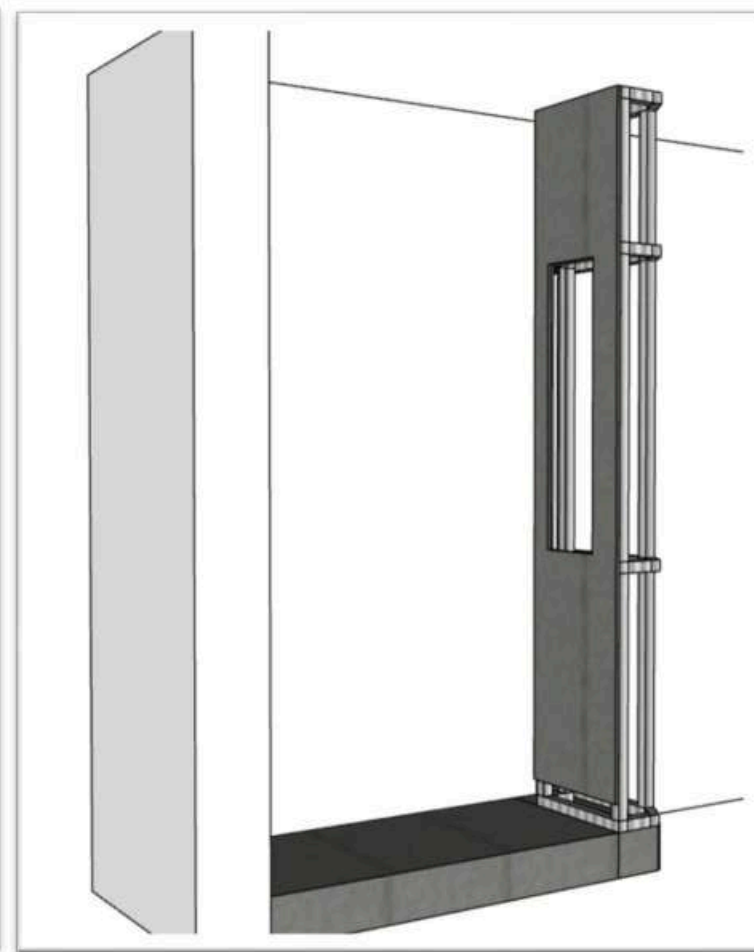

Step.2 水泥板做基层,
留出壁龛位置

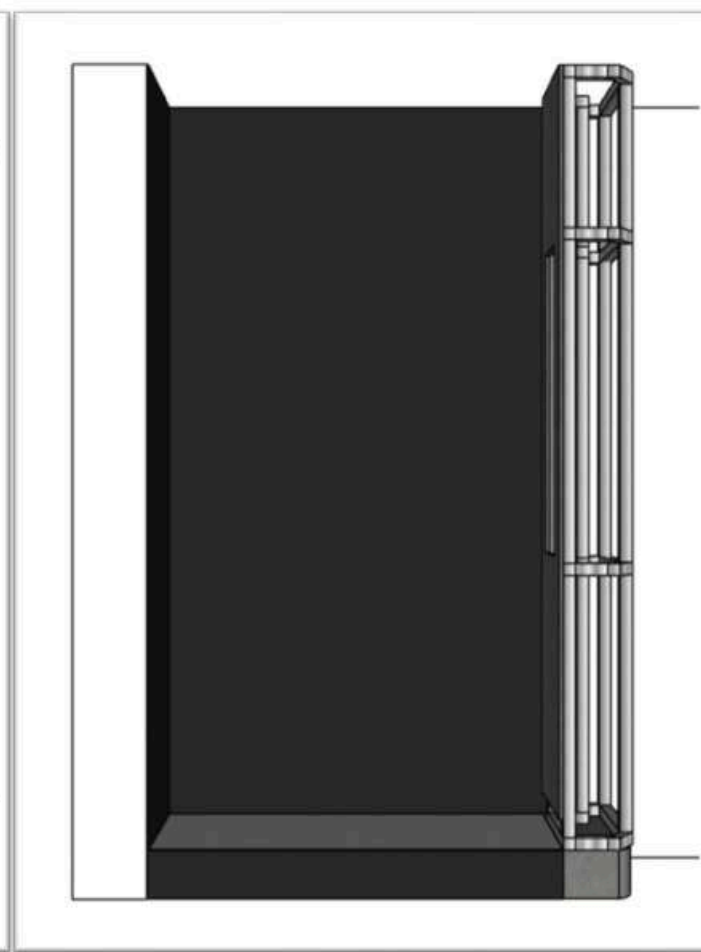

Step.3 通体做防水

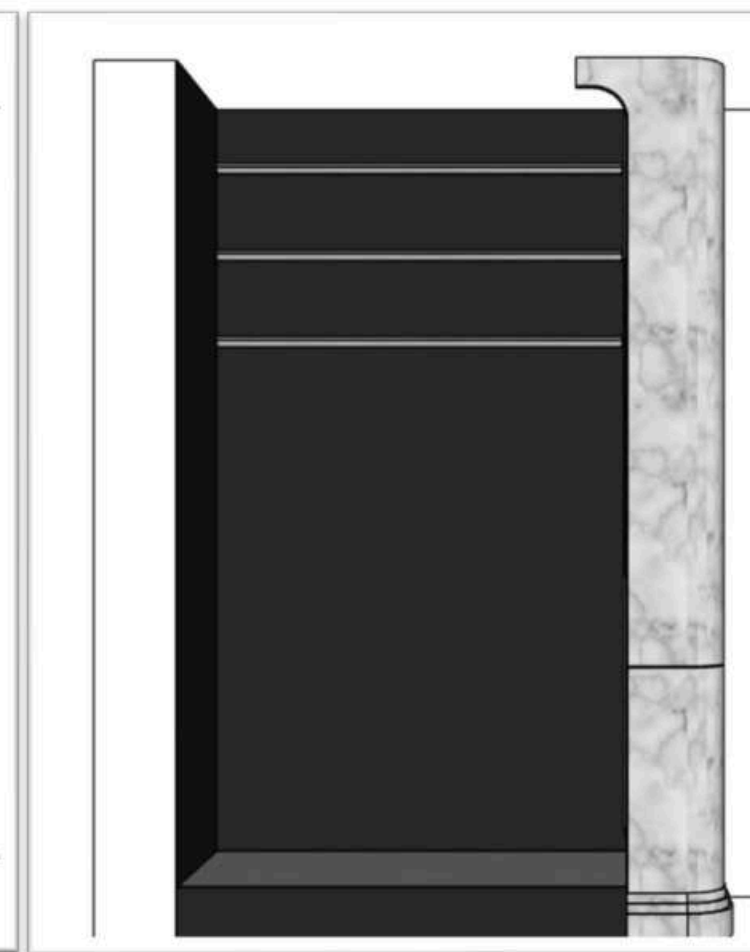

Step.4 安装右侧石材
柜体挂件安装



Step.5 安装木饰面底板



Step.6 整体柜推进去安装




Step.7 上侧及左侧封板
确保收口无缝隙



Step.8 安装石材顶板及侧面封板
缝隙由门套收掉





Step.9 安装下方石材踢脚

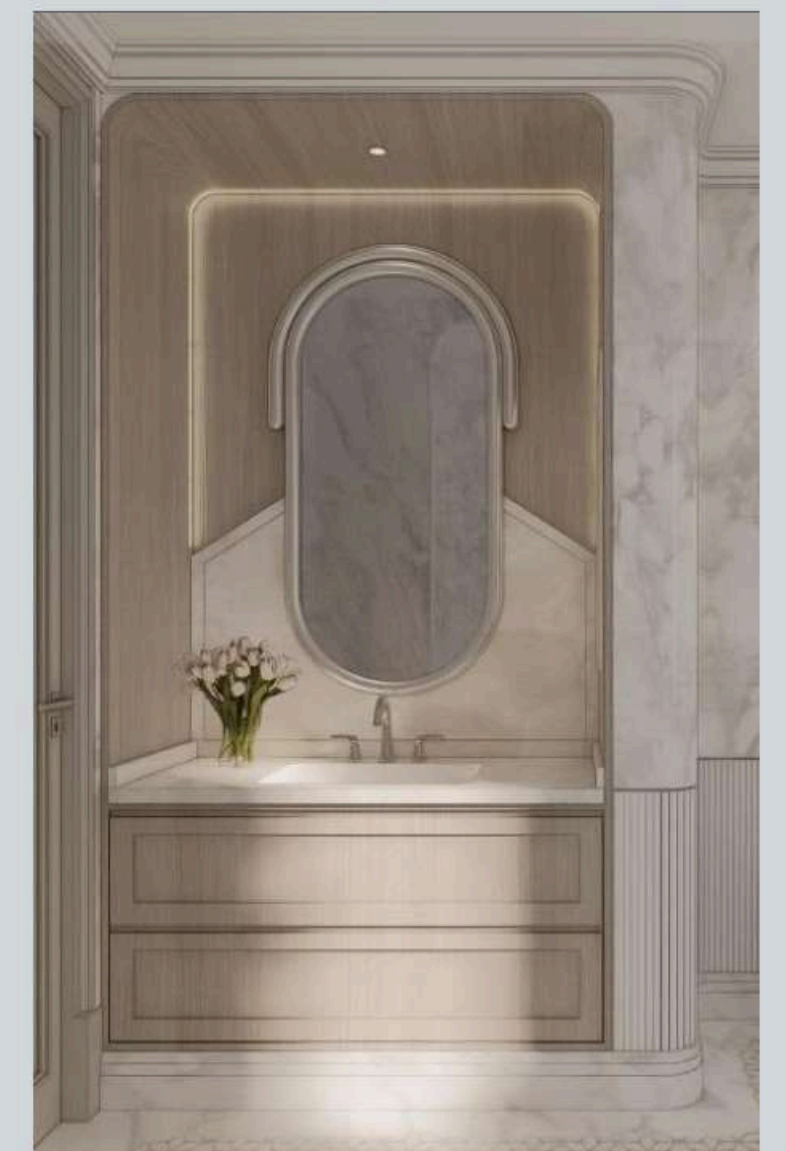

DETAIL THINKING 细节构想

Bathroom for girl
女儿卫

- 台盆柜安装步骤分析
- **腰线细节**
- 淋浴房踢脚细节
- 分割原则
- 铝模板

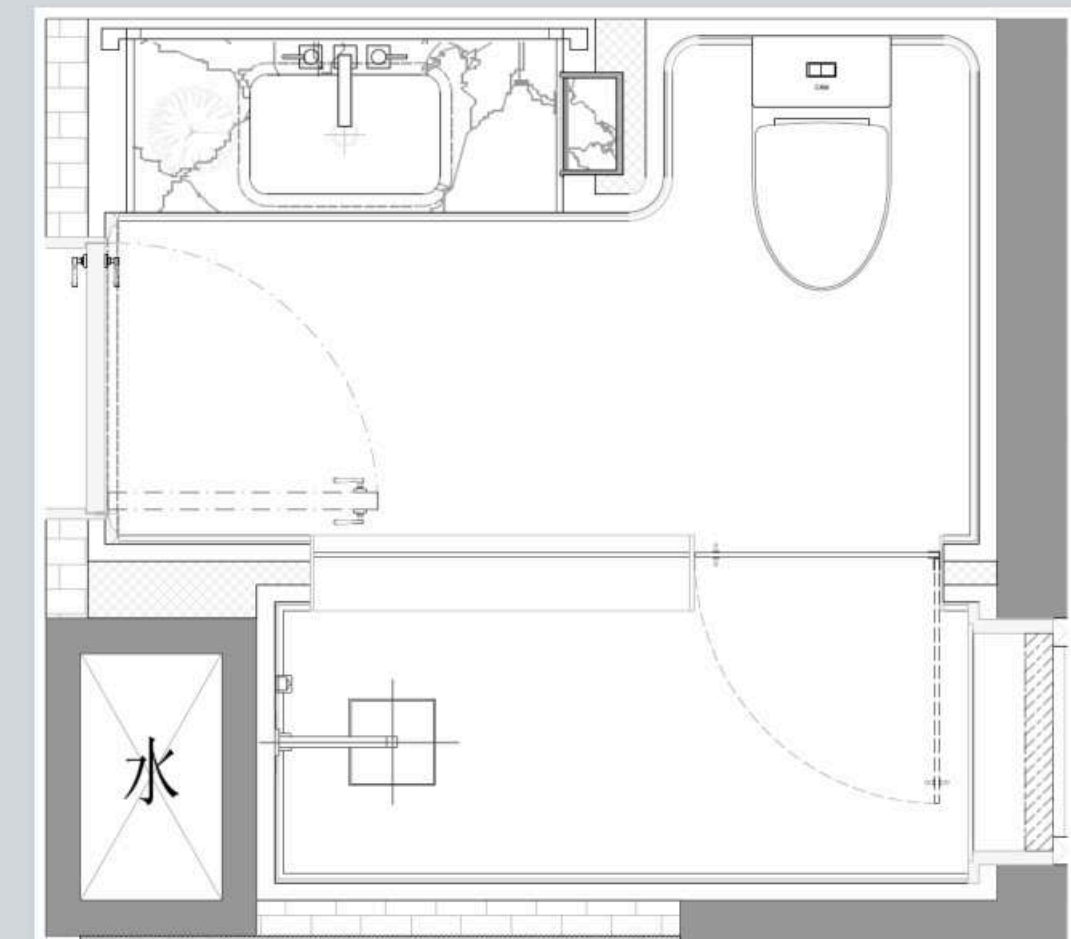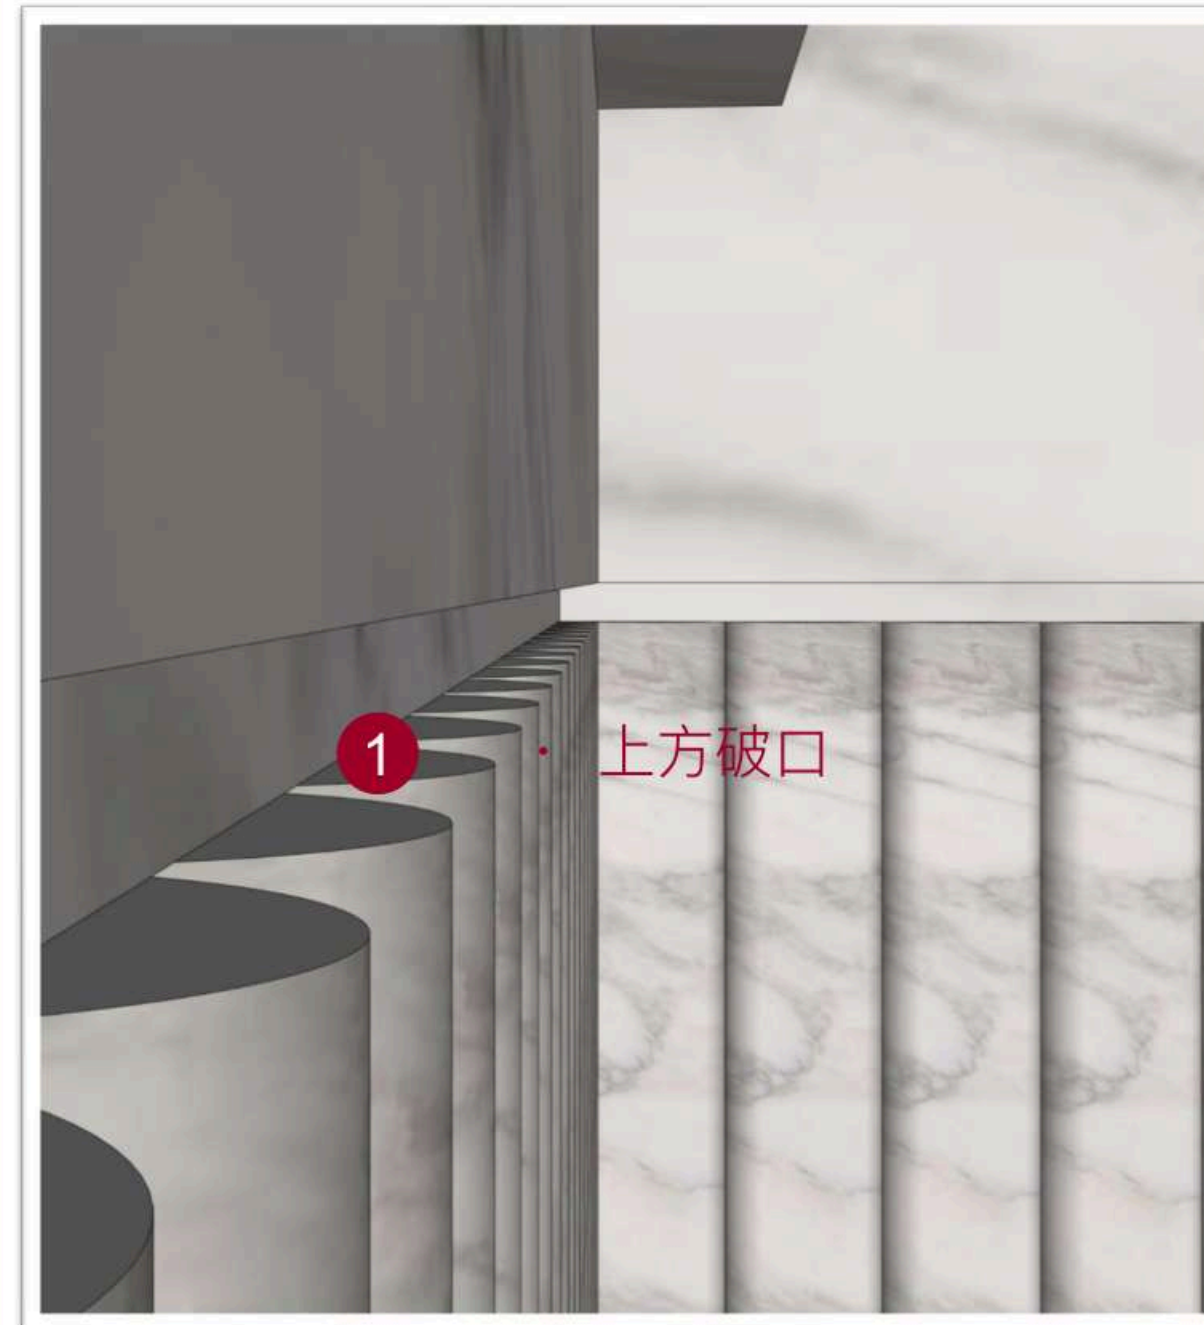


DETAIL THINKING 细节构想


Bathroom for girl
女儿卫

- 台盆柜安装步骤分析
- 腰线细节
- **石材踢脚线细节**
- 分割原则
- 铝模板


石材踢脚线分析

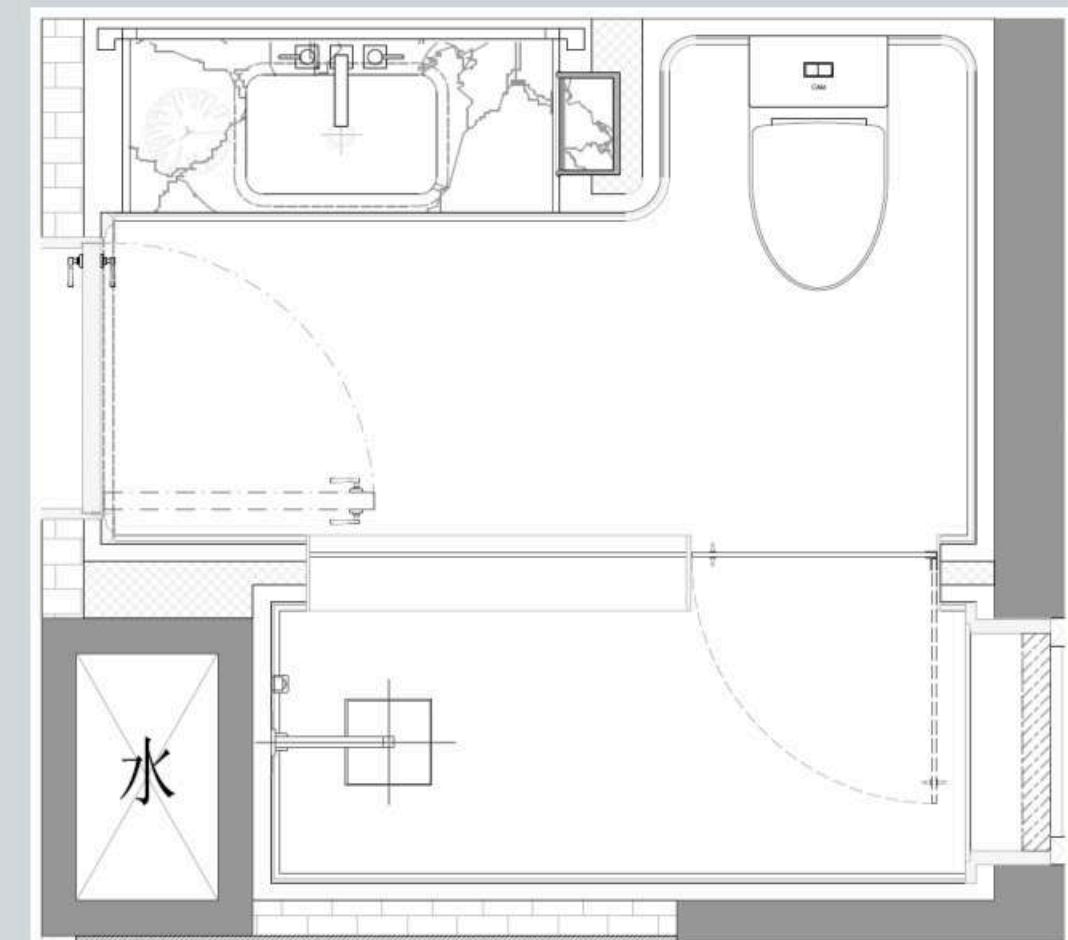

HIBORNI

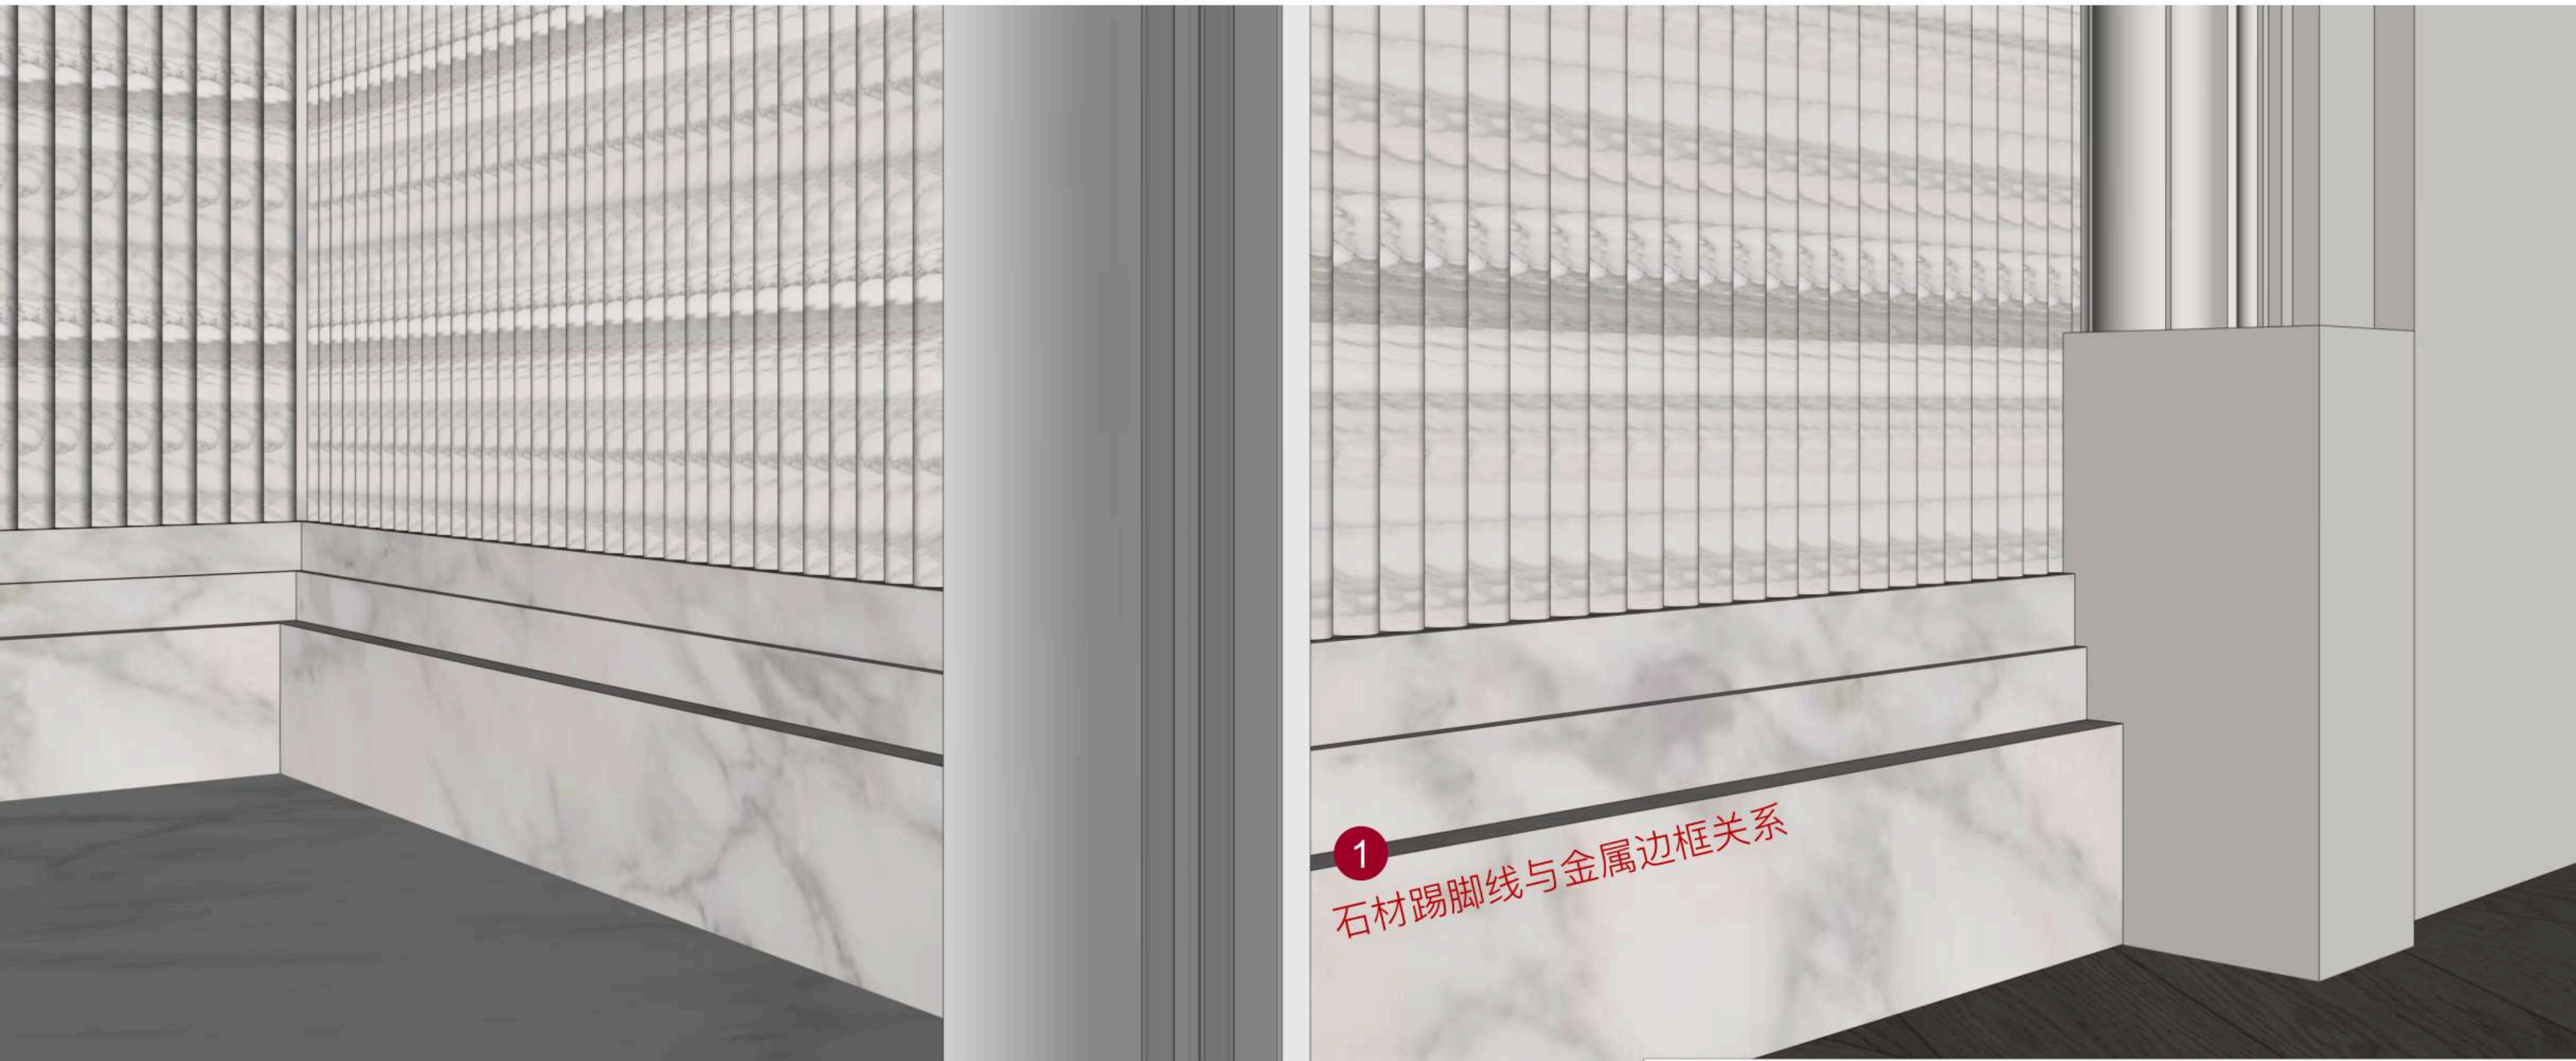


1
石材踢脚线与金属边框关系

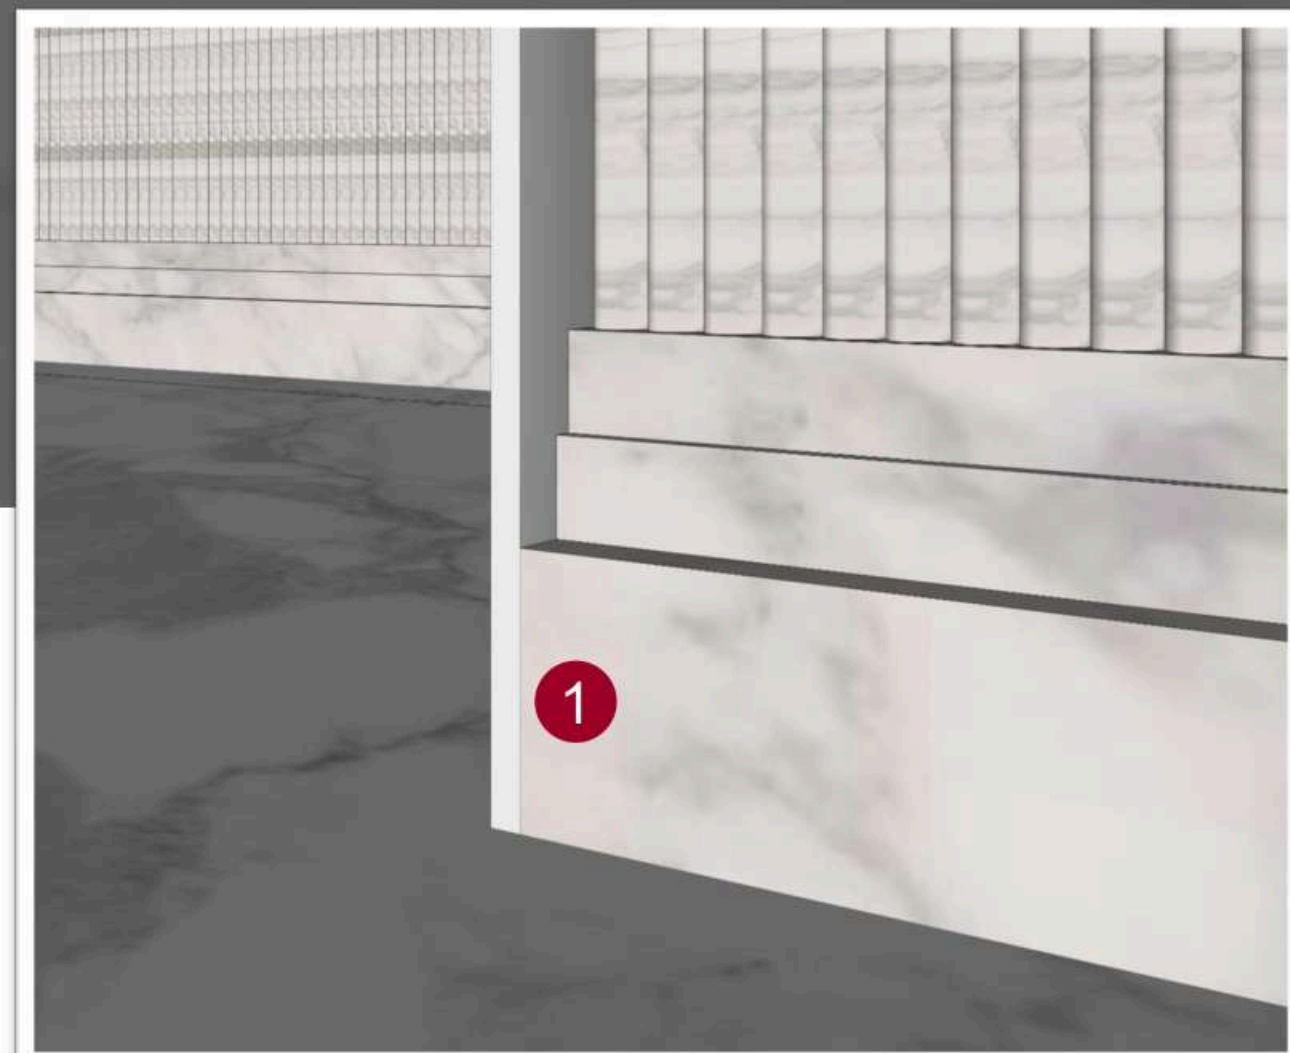

1



1

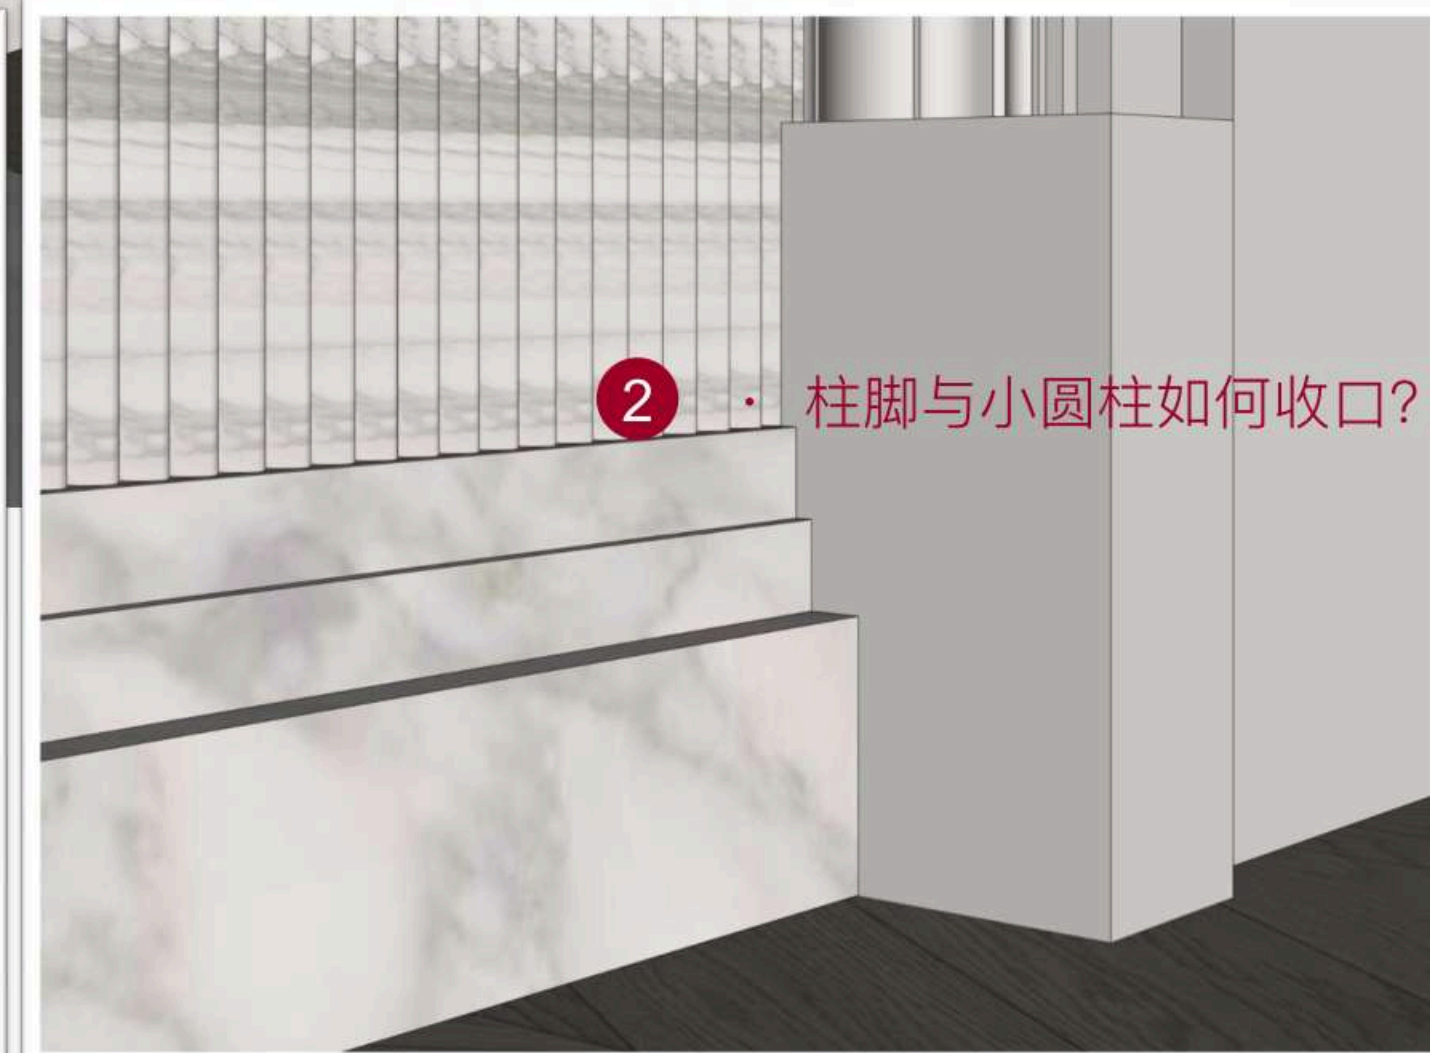


2

柱脚与小圆柱如何收口?

DETAIL THINKING 细节构想

Bathroom for girl
女儿卫








- 台盆柜安装步骤分析
- 腰线细节
- 淋浴房踢脚细节
- **分割原则**
- 铝模板

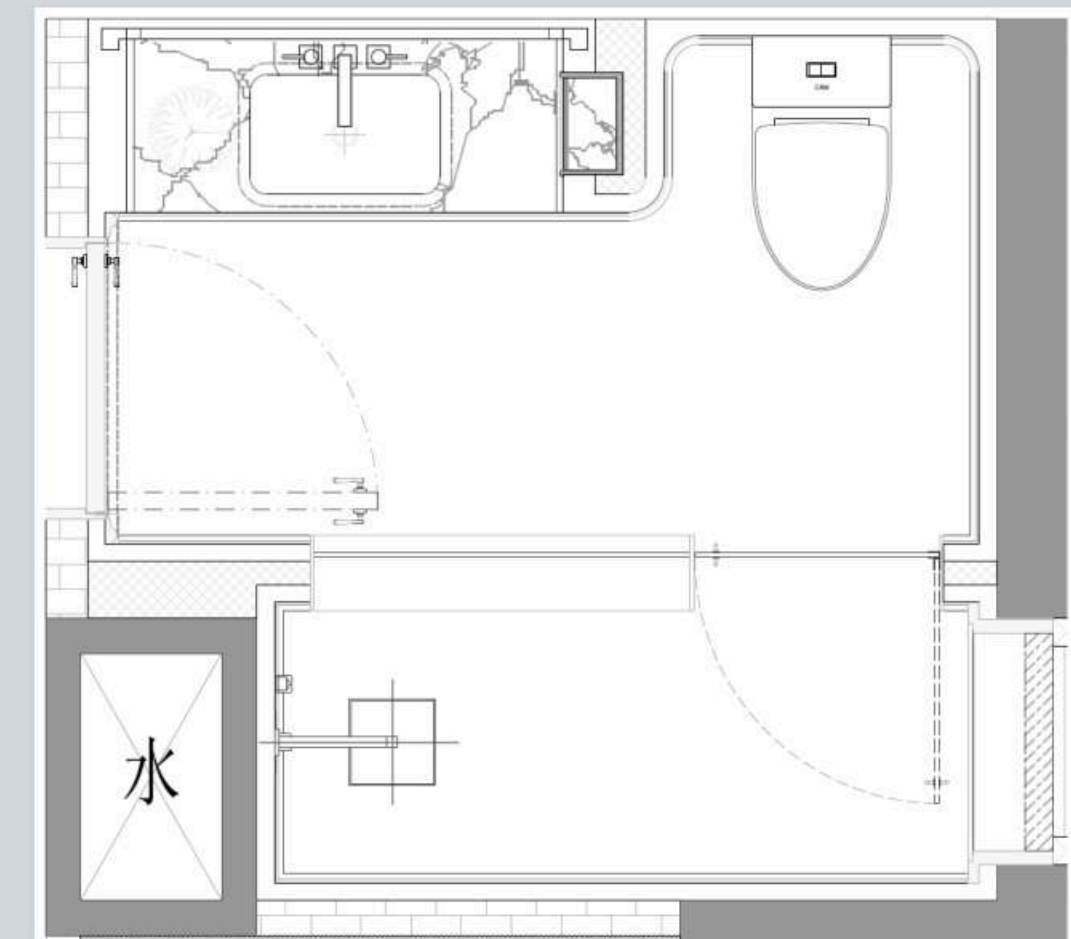

DETAIL THINKING 细节构想

Bathroom for girl
女儿卫



- 台盆柜安装步骤分析
- 腰线细节
- 淋浴房踢脚细节
- 分割原则
- 铝模板

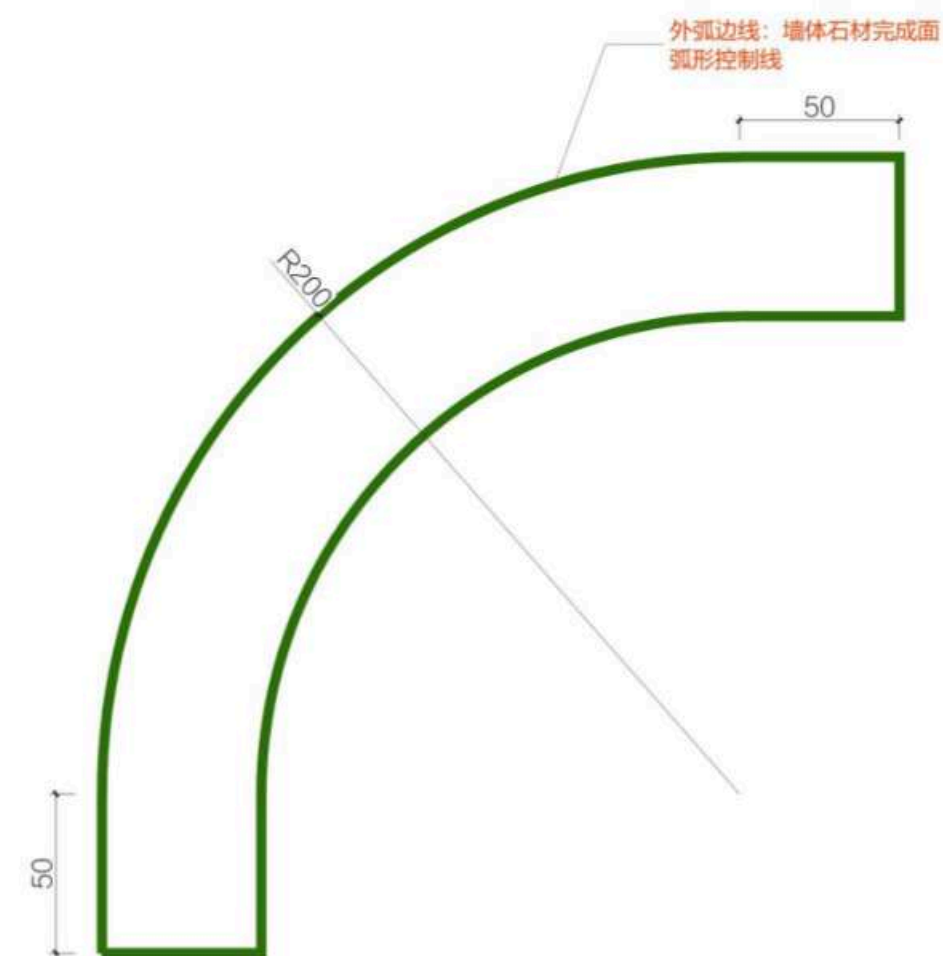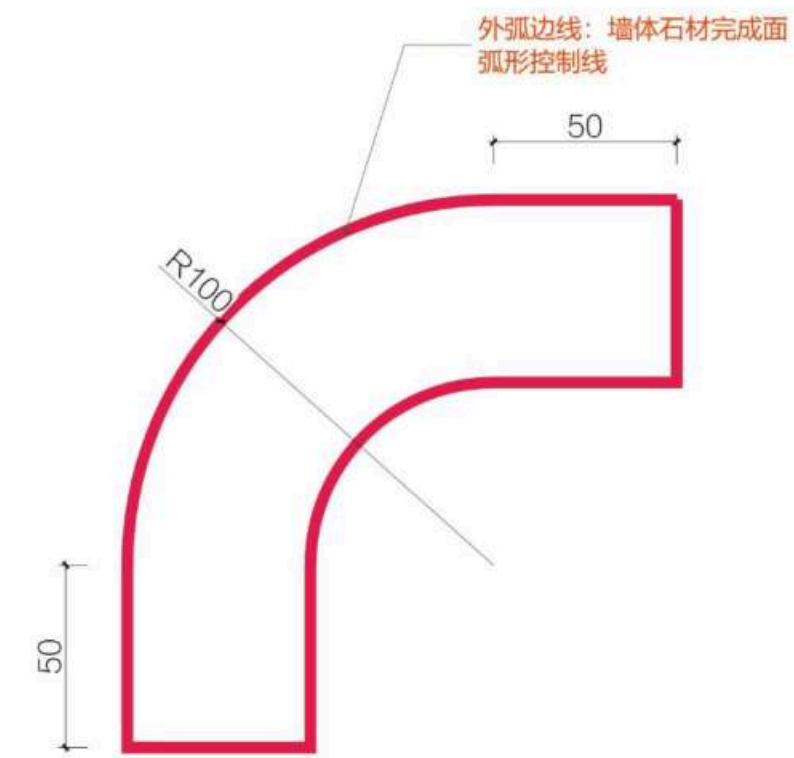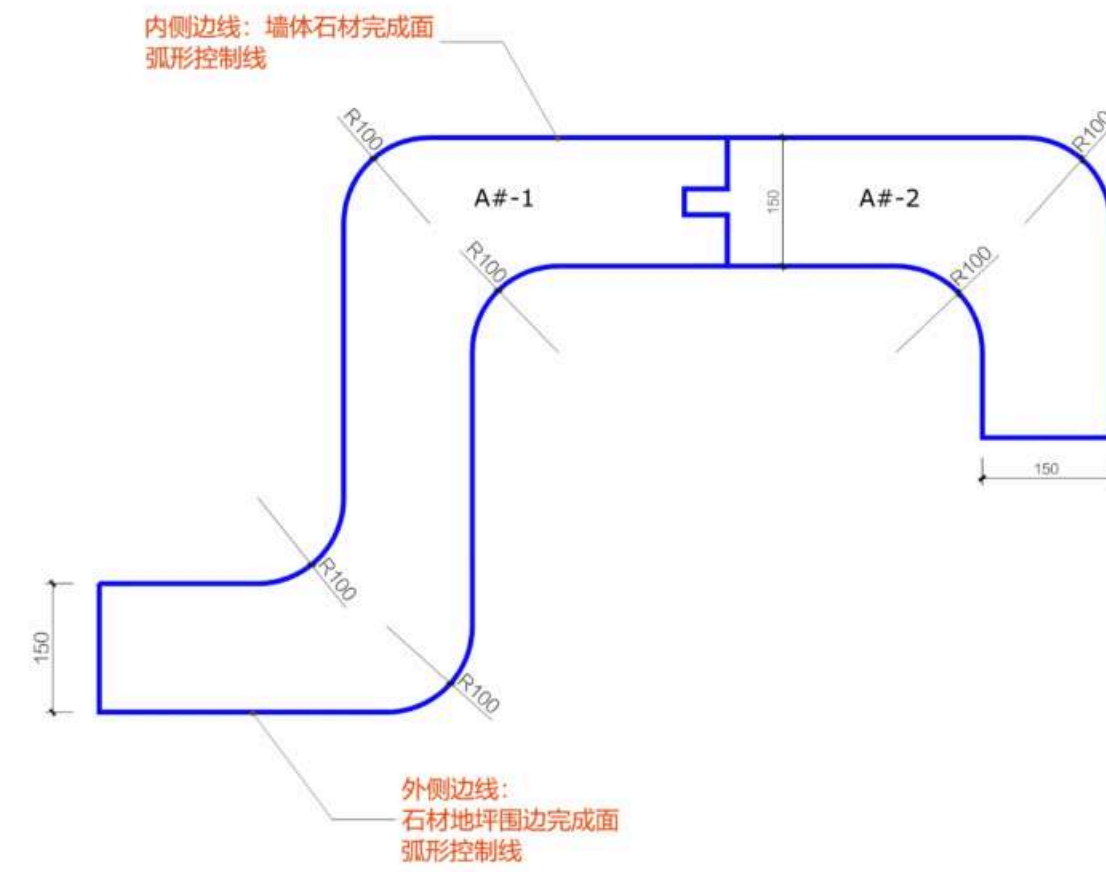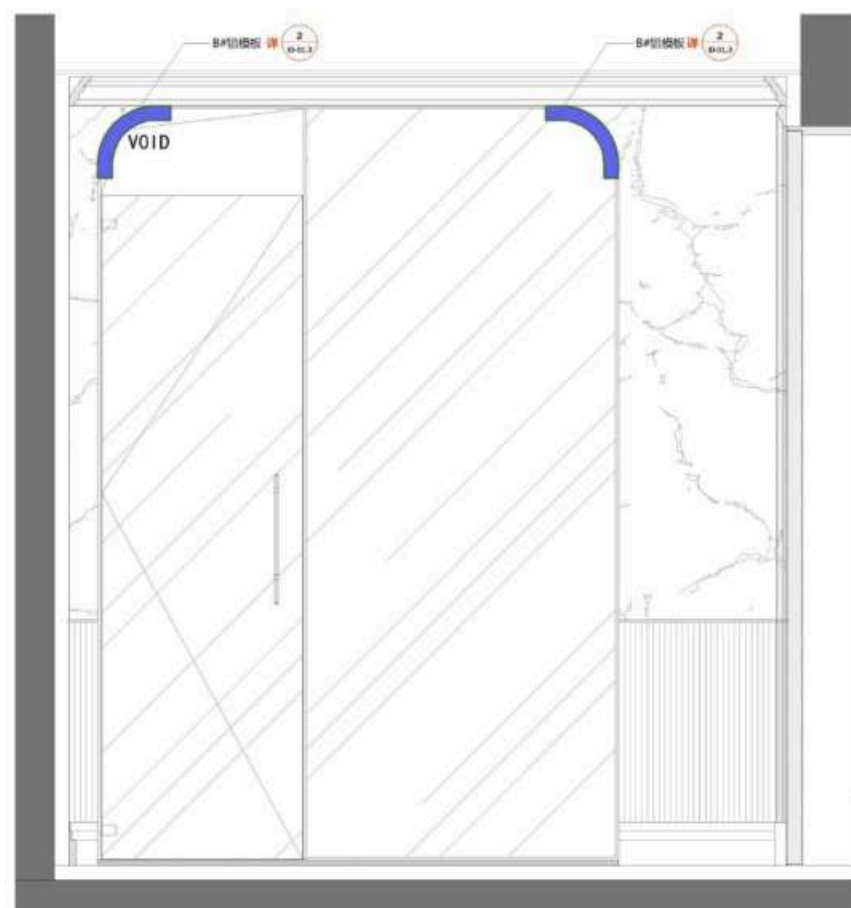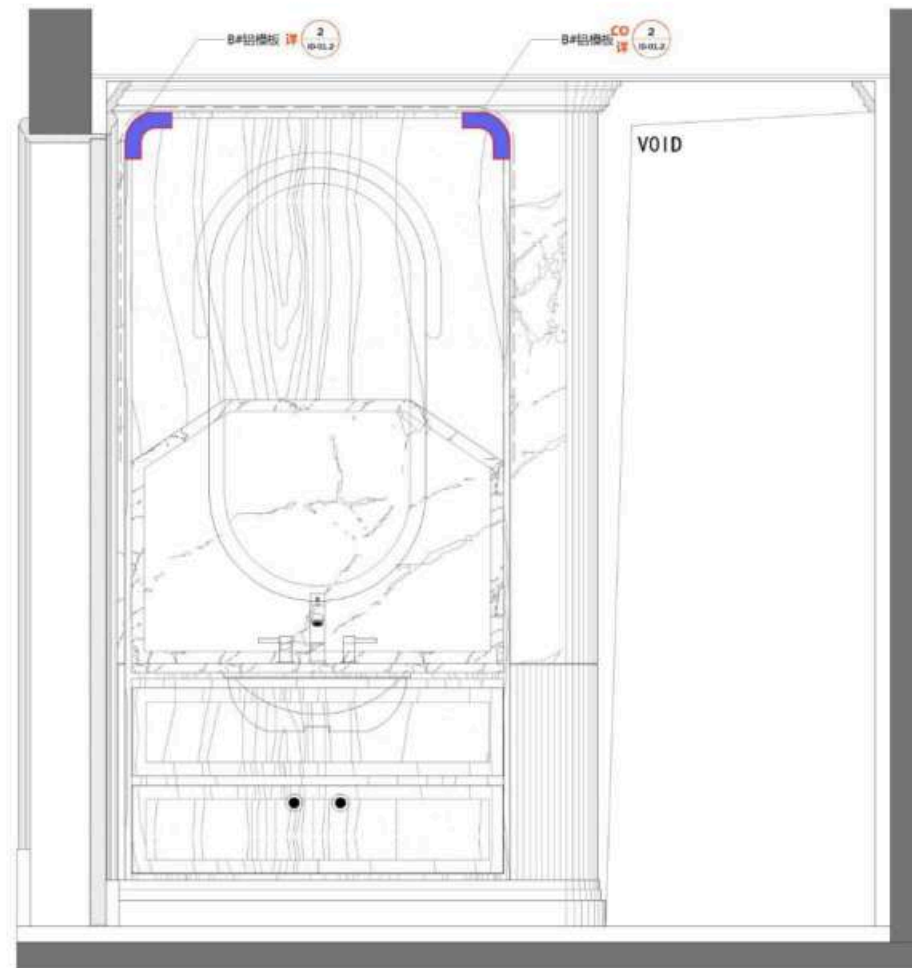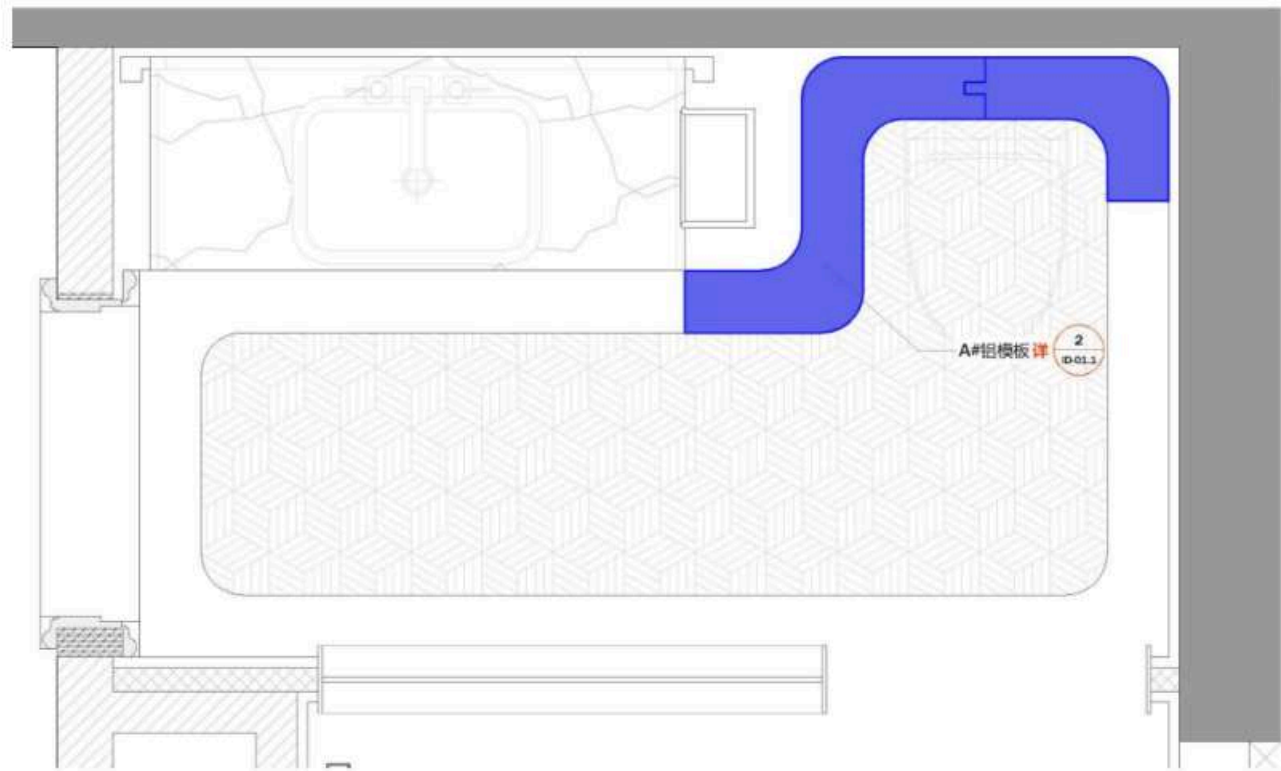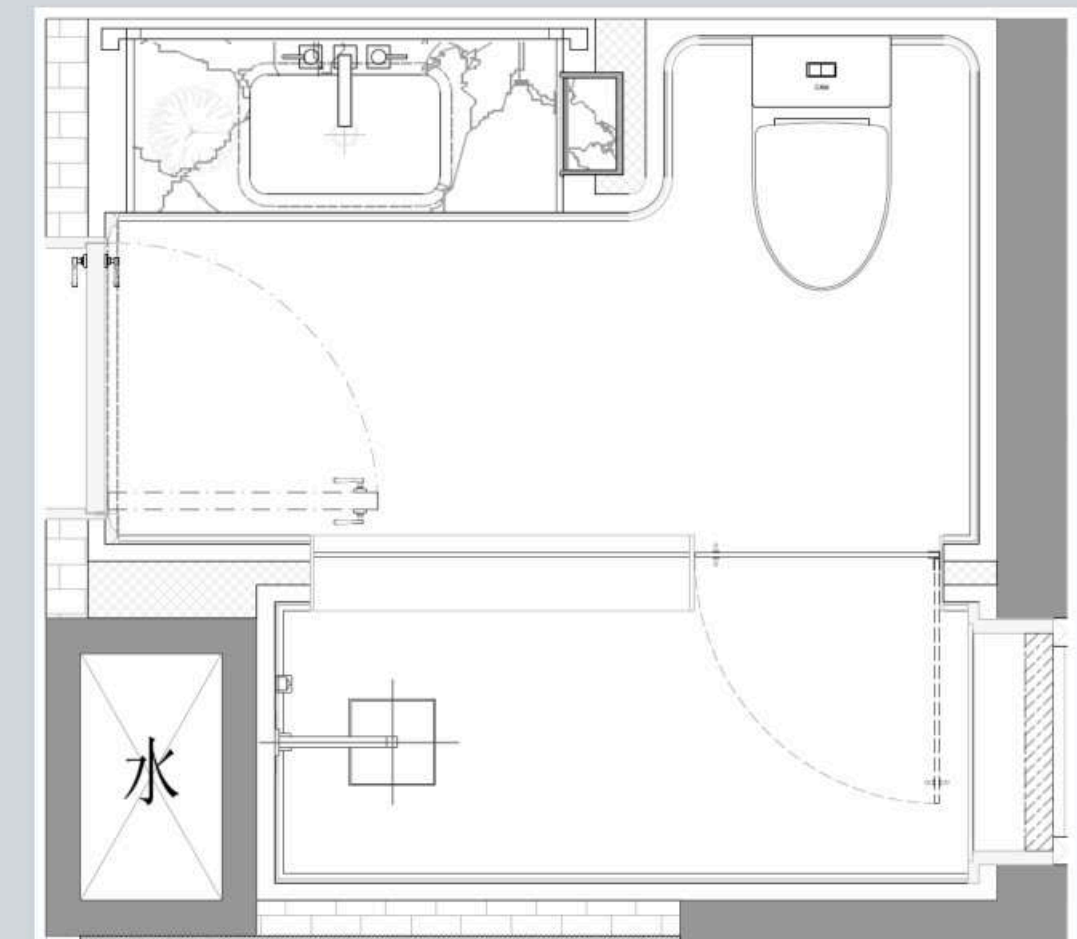

DETAIL THINKING 细节构想

Bathroom for girl
女儿卫

- 台盆柜安装步骤分析
- 腰线细节
- 淋浴房踢脚细节
- 分割原则
- **铝模板**

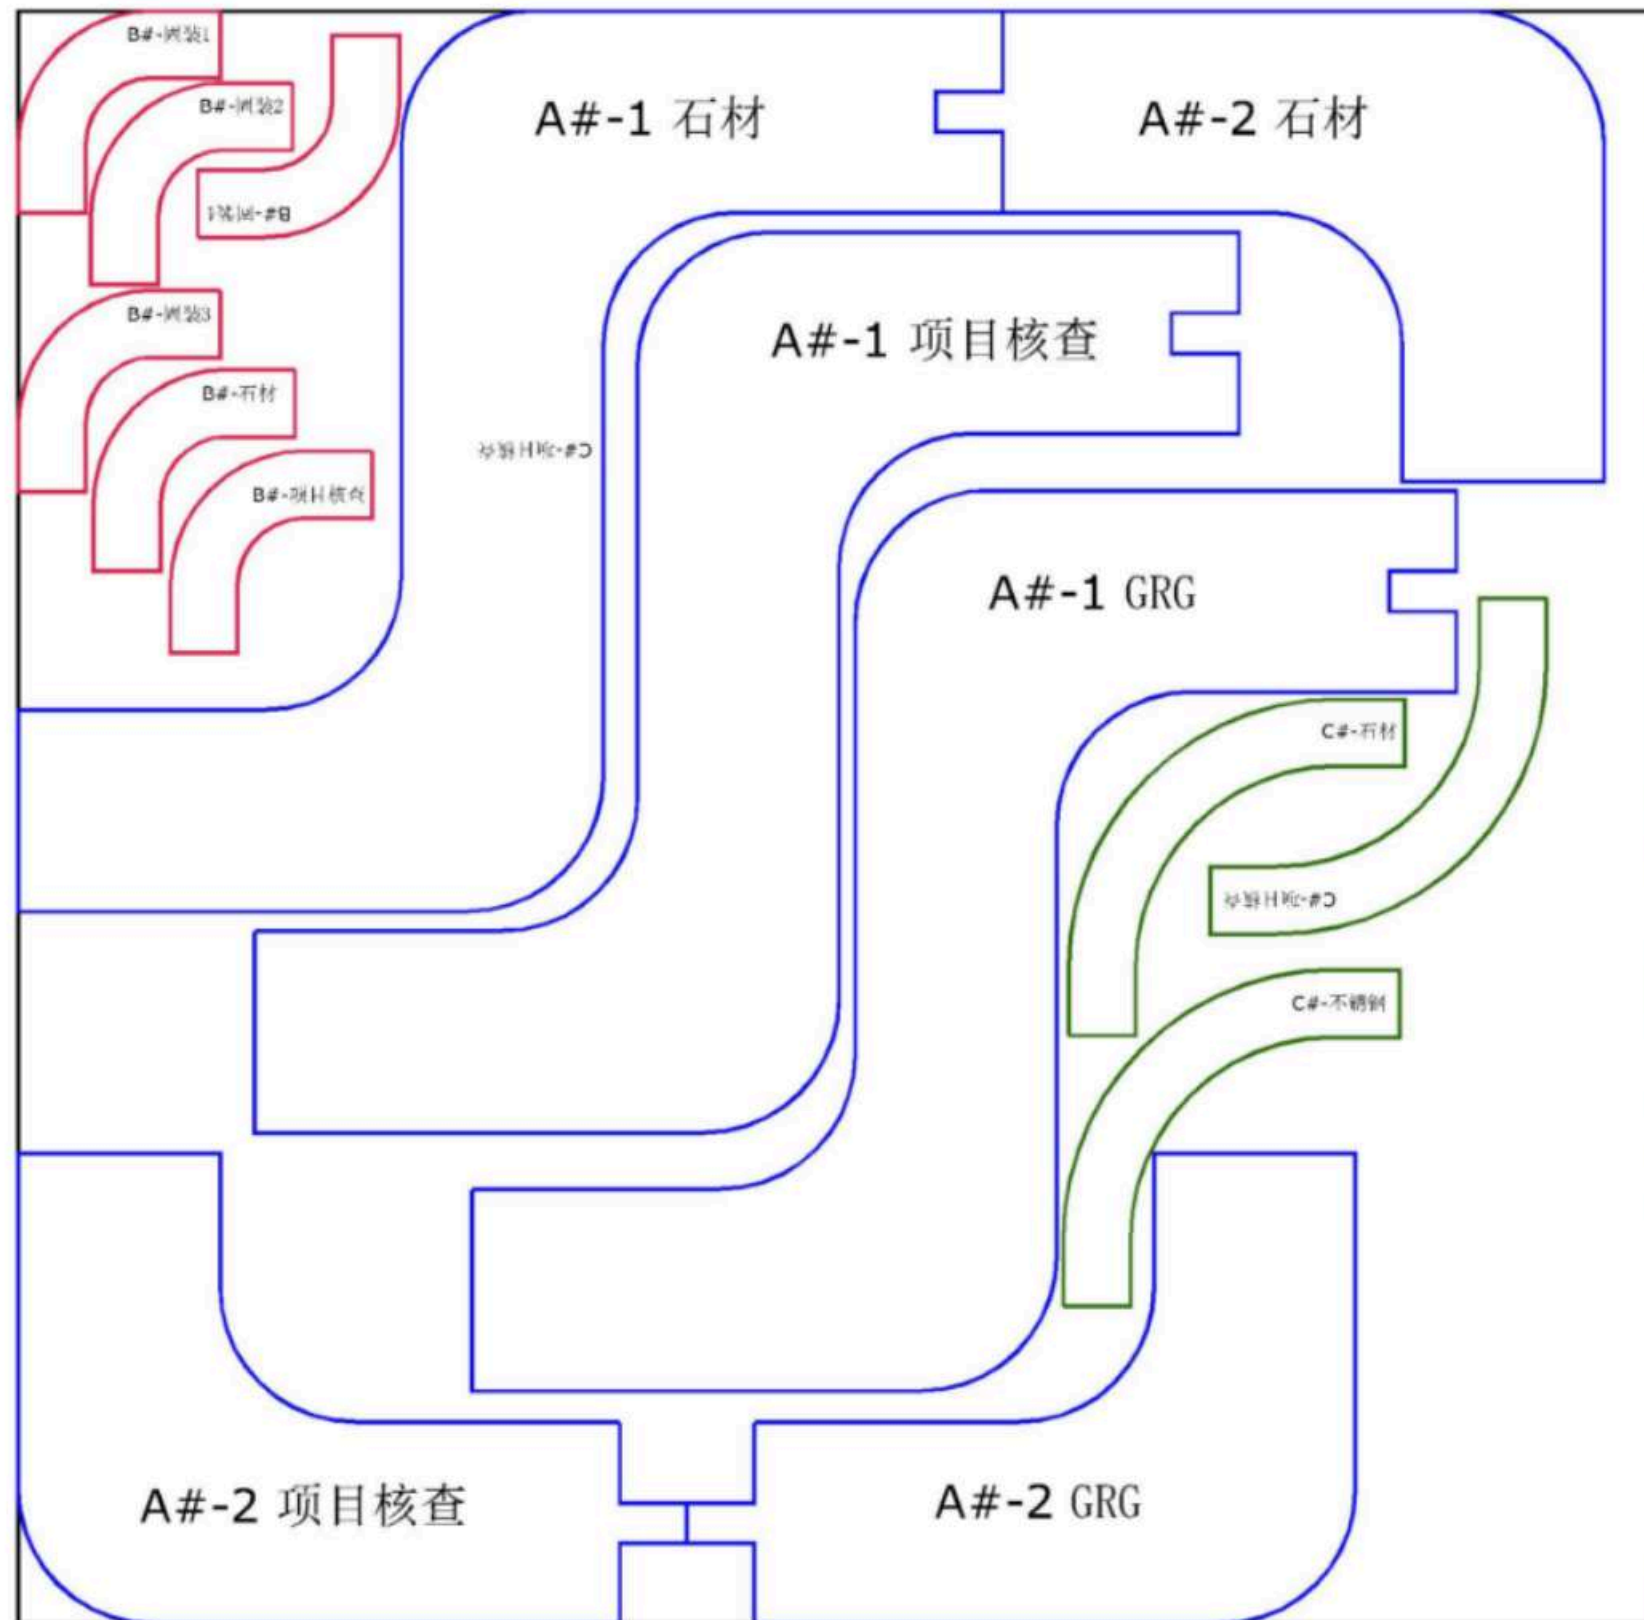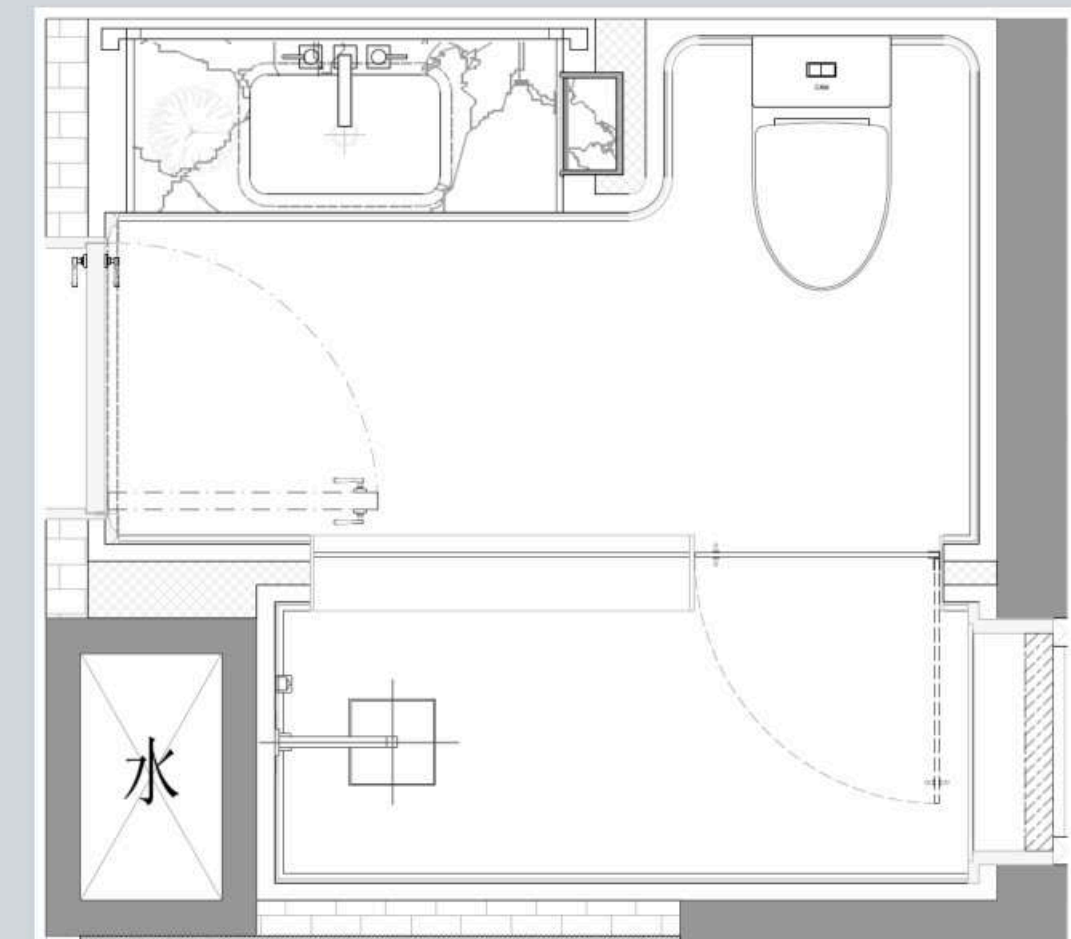


为确保不同材质的圆弧加工后弧度一致，
总包统一加工铝模板作为制作及验收依据。



DETAIL THINKING
细节构想

Bathroom for boy
男孩卫

- 台盆柜细节分析
- 石材与木饰面交接处分析
- 石材踢脚线分析
- 分割原则

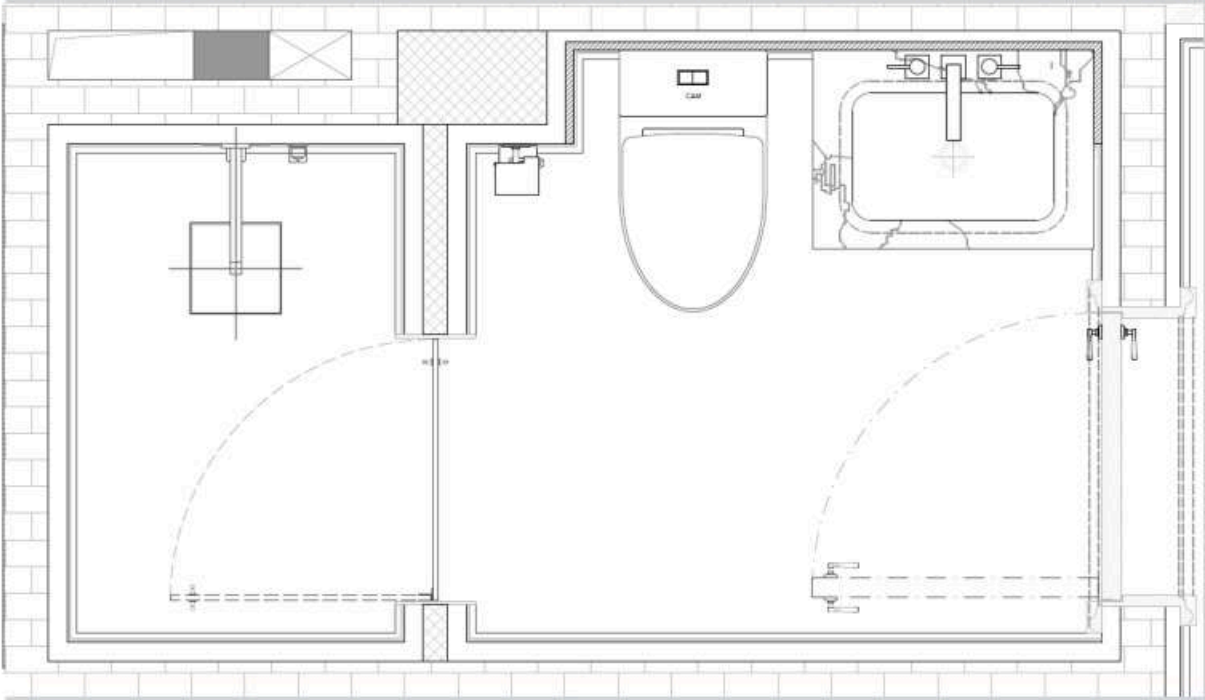


侧边挡水条
是否取消？

2

墙面与台面有缝隙




1

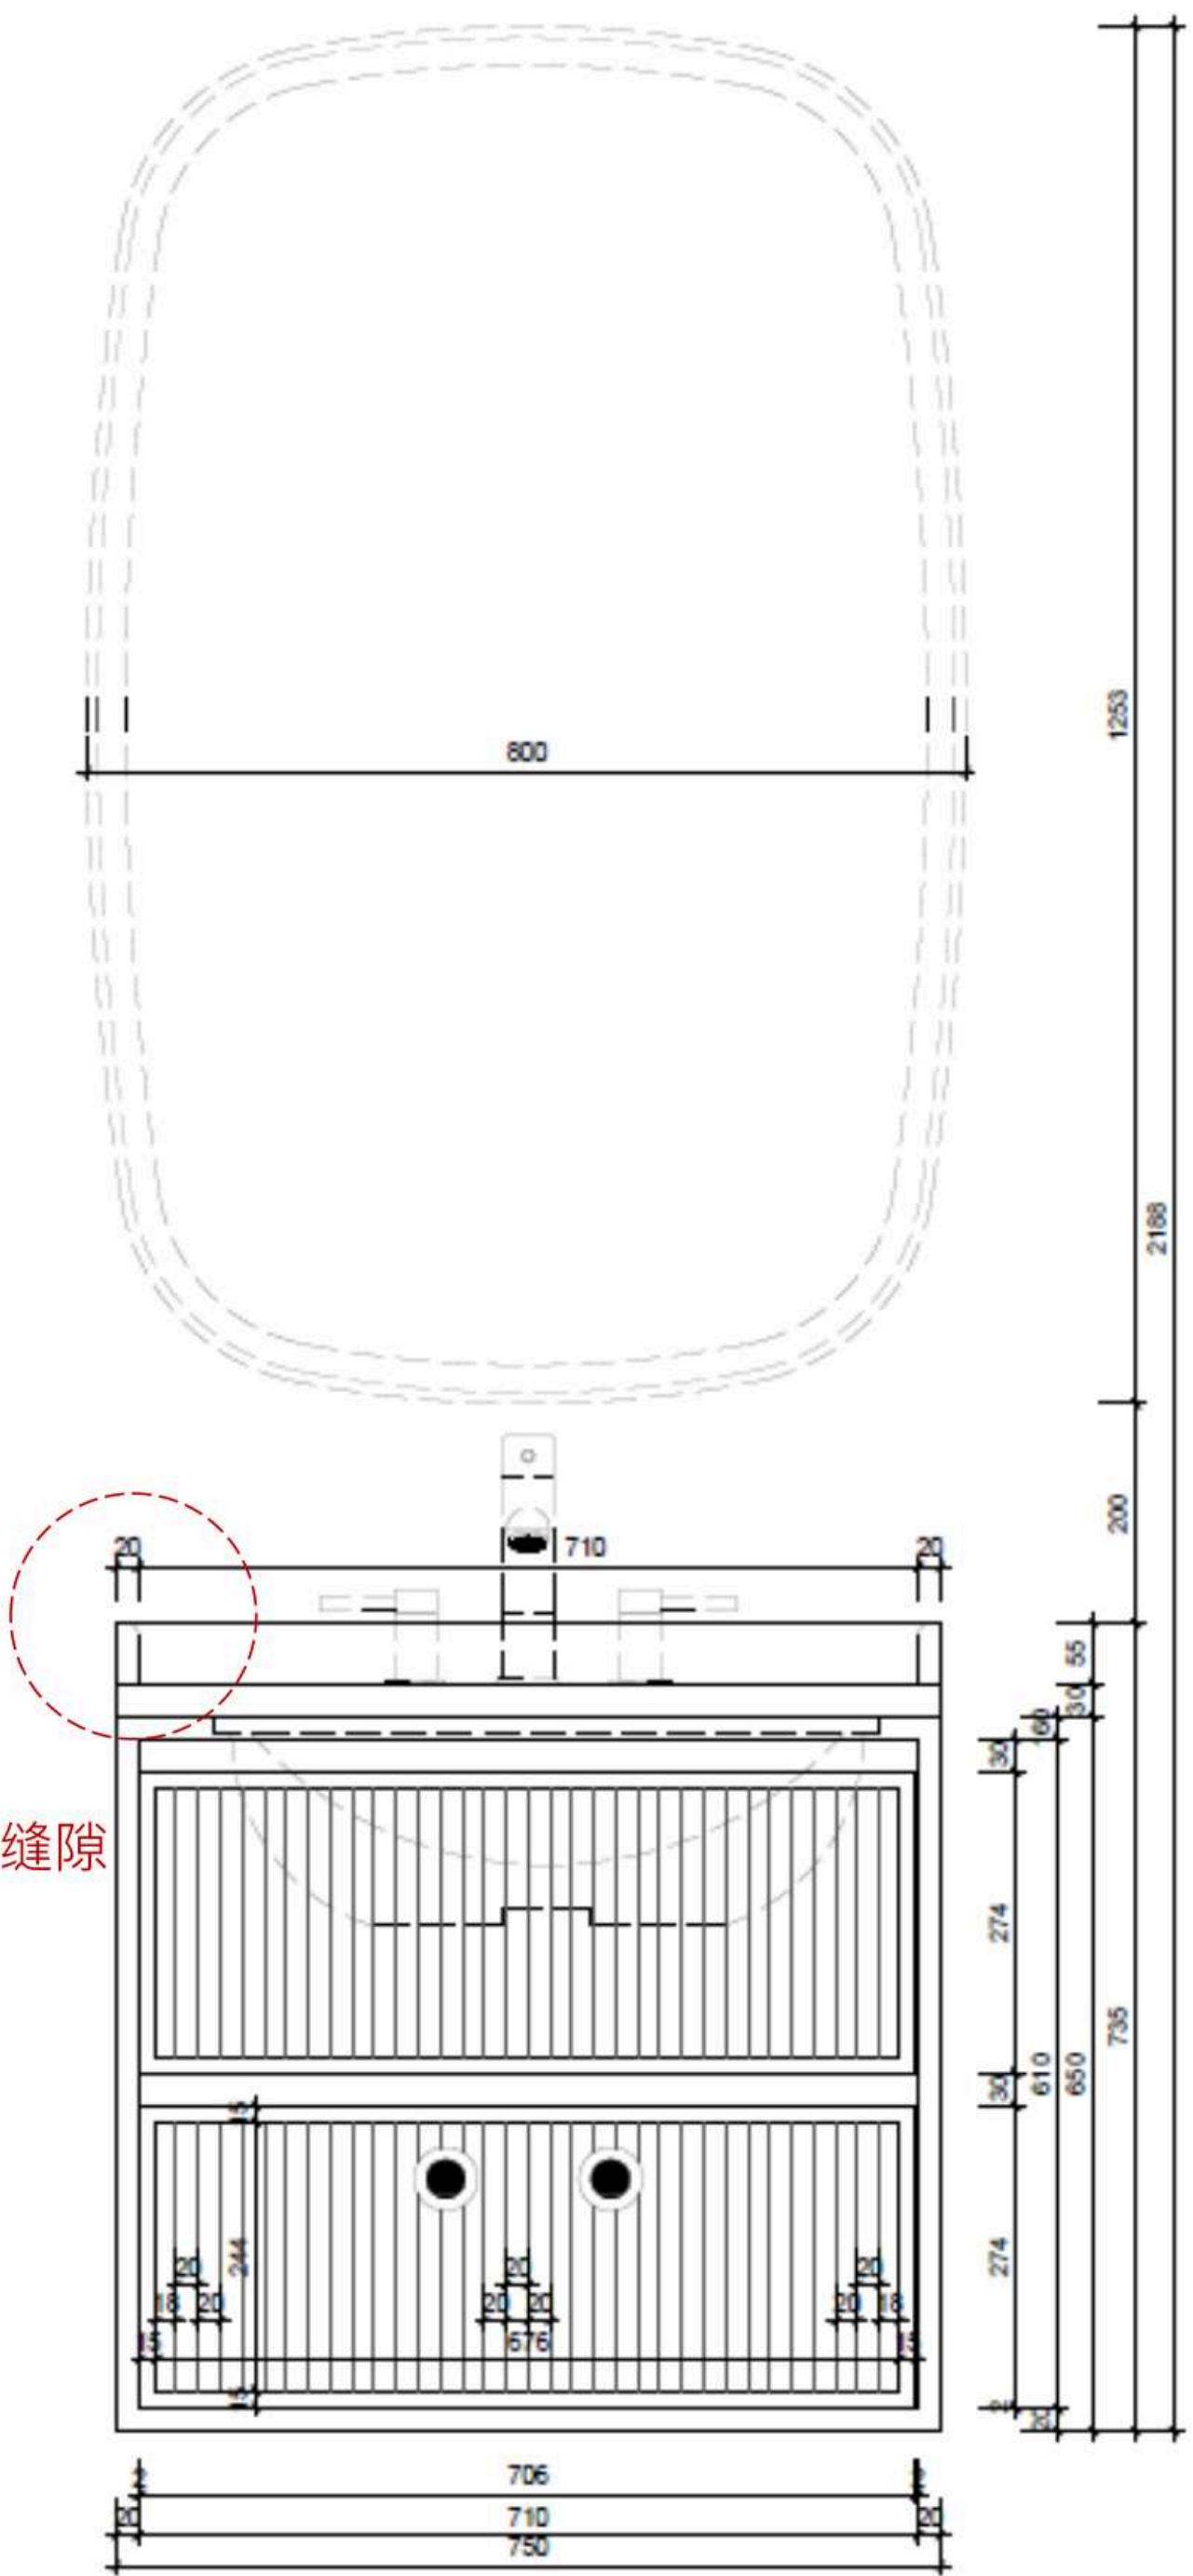

DETAIL THINKING 细节构想

Bathroom for boy
男孩卫


- 台盆柜细节分析
- 石材与木饰面交接处分析
- 石材踢脚线分析
- 分割原则

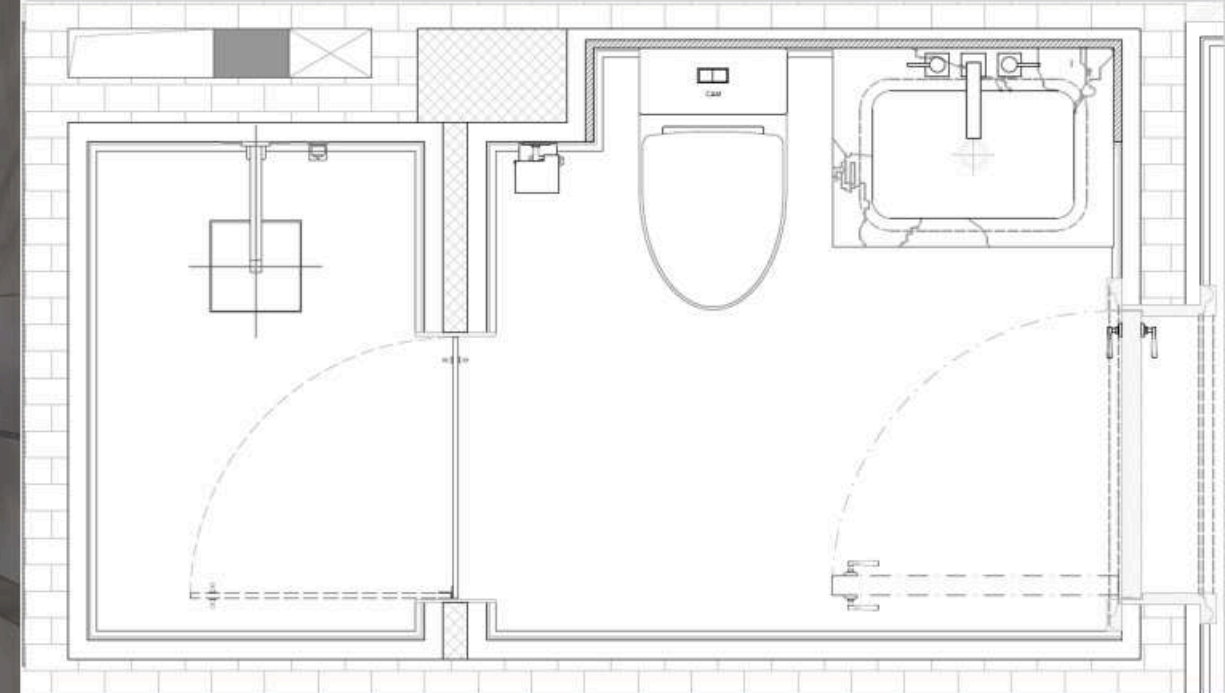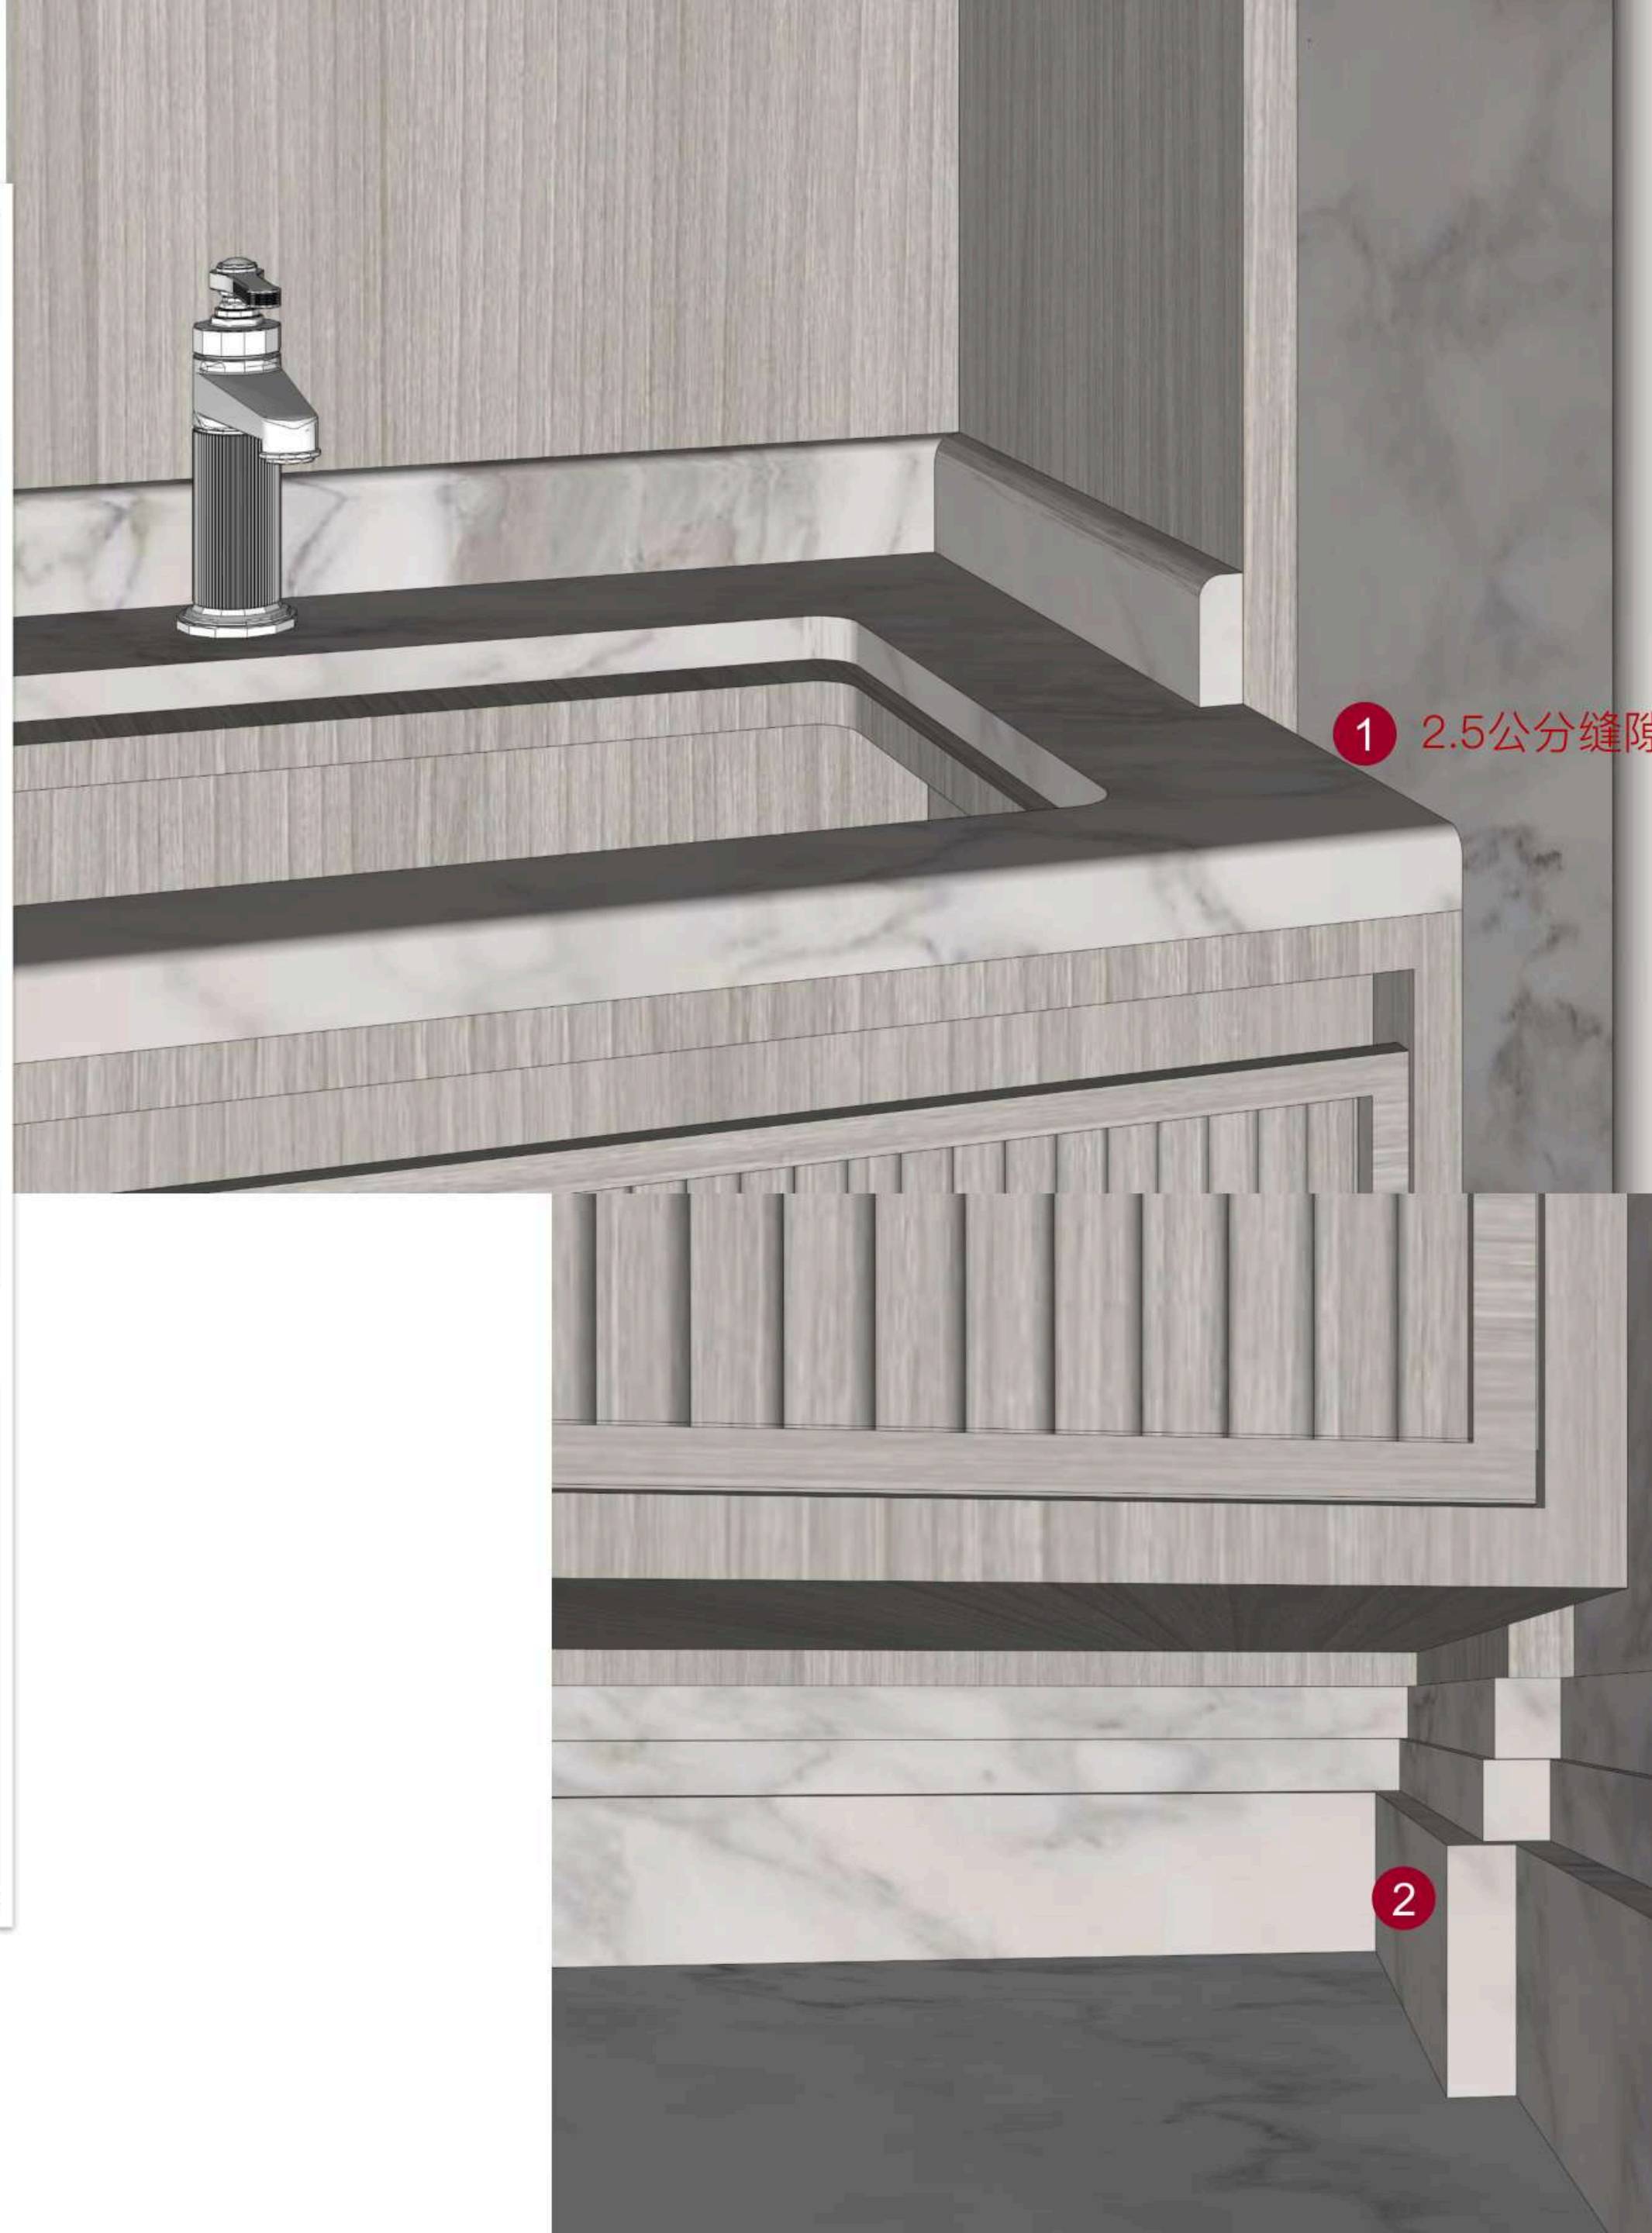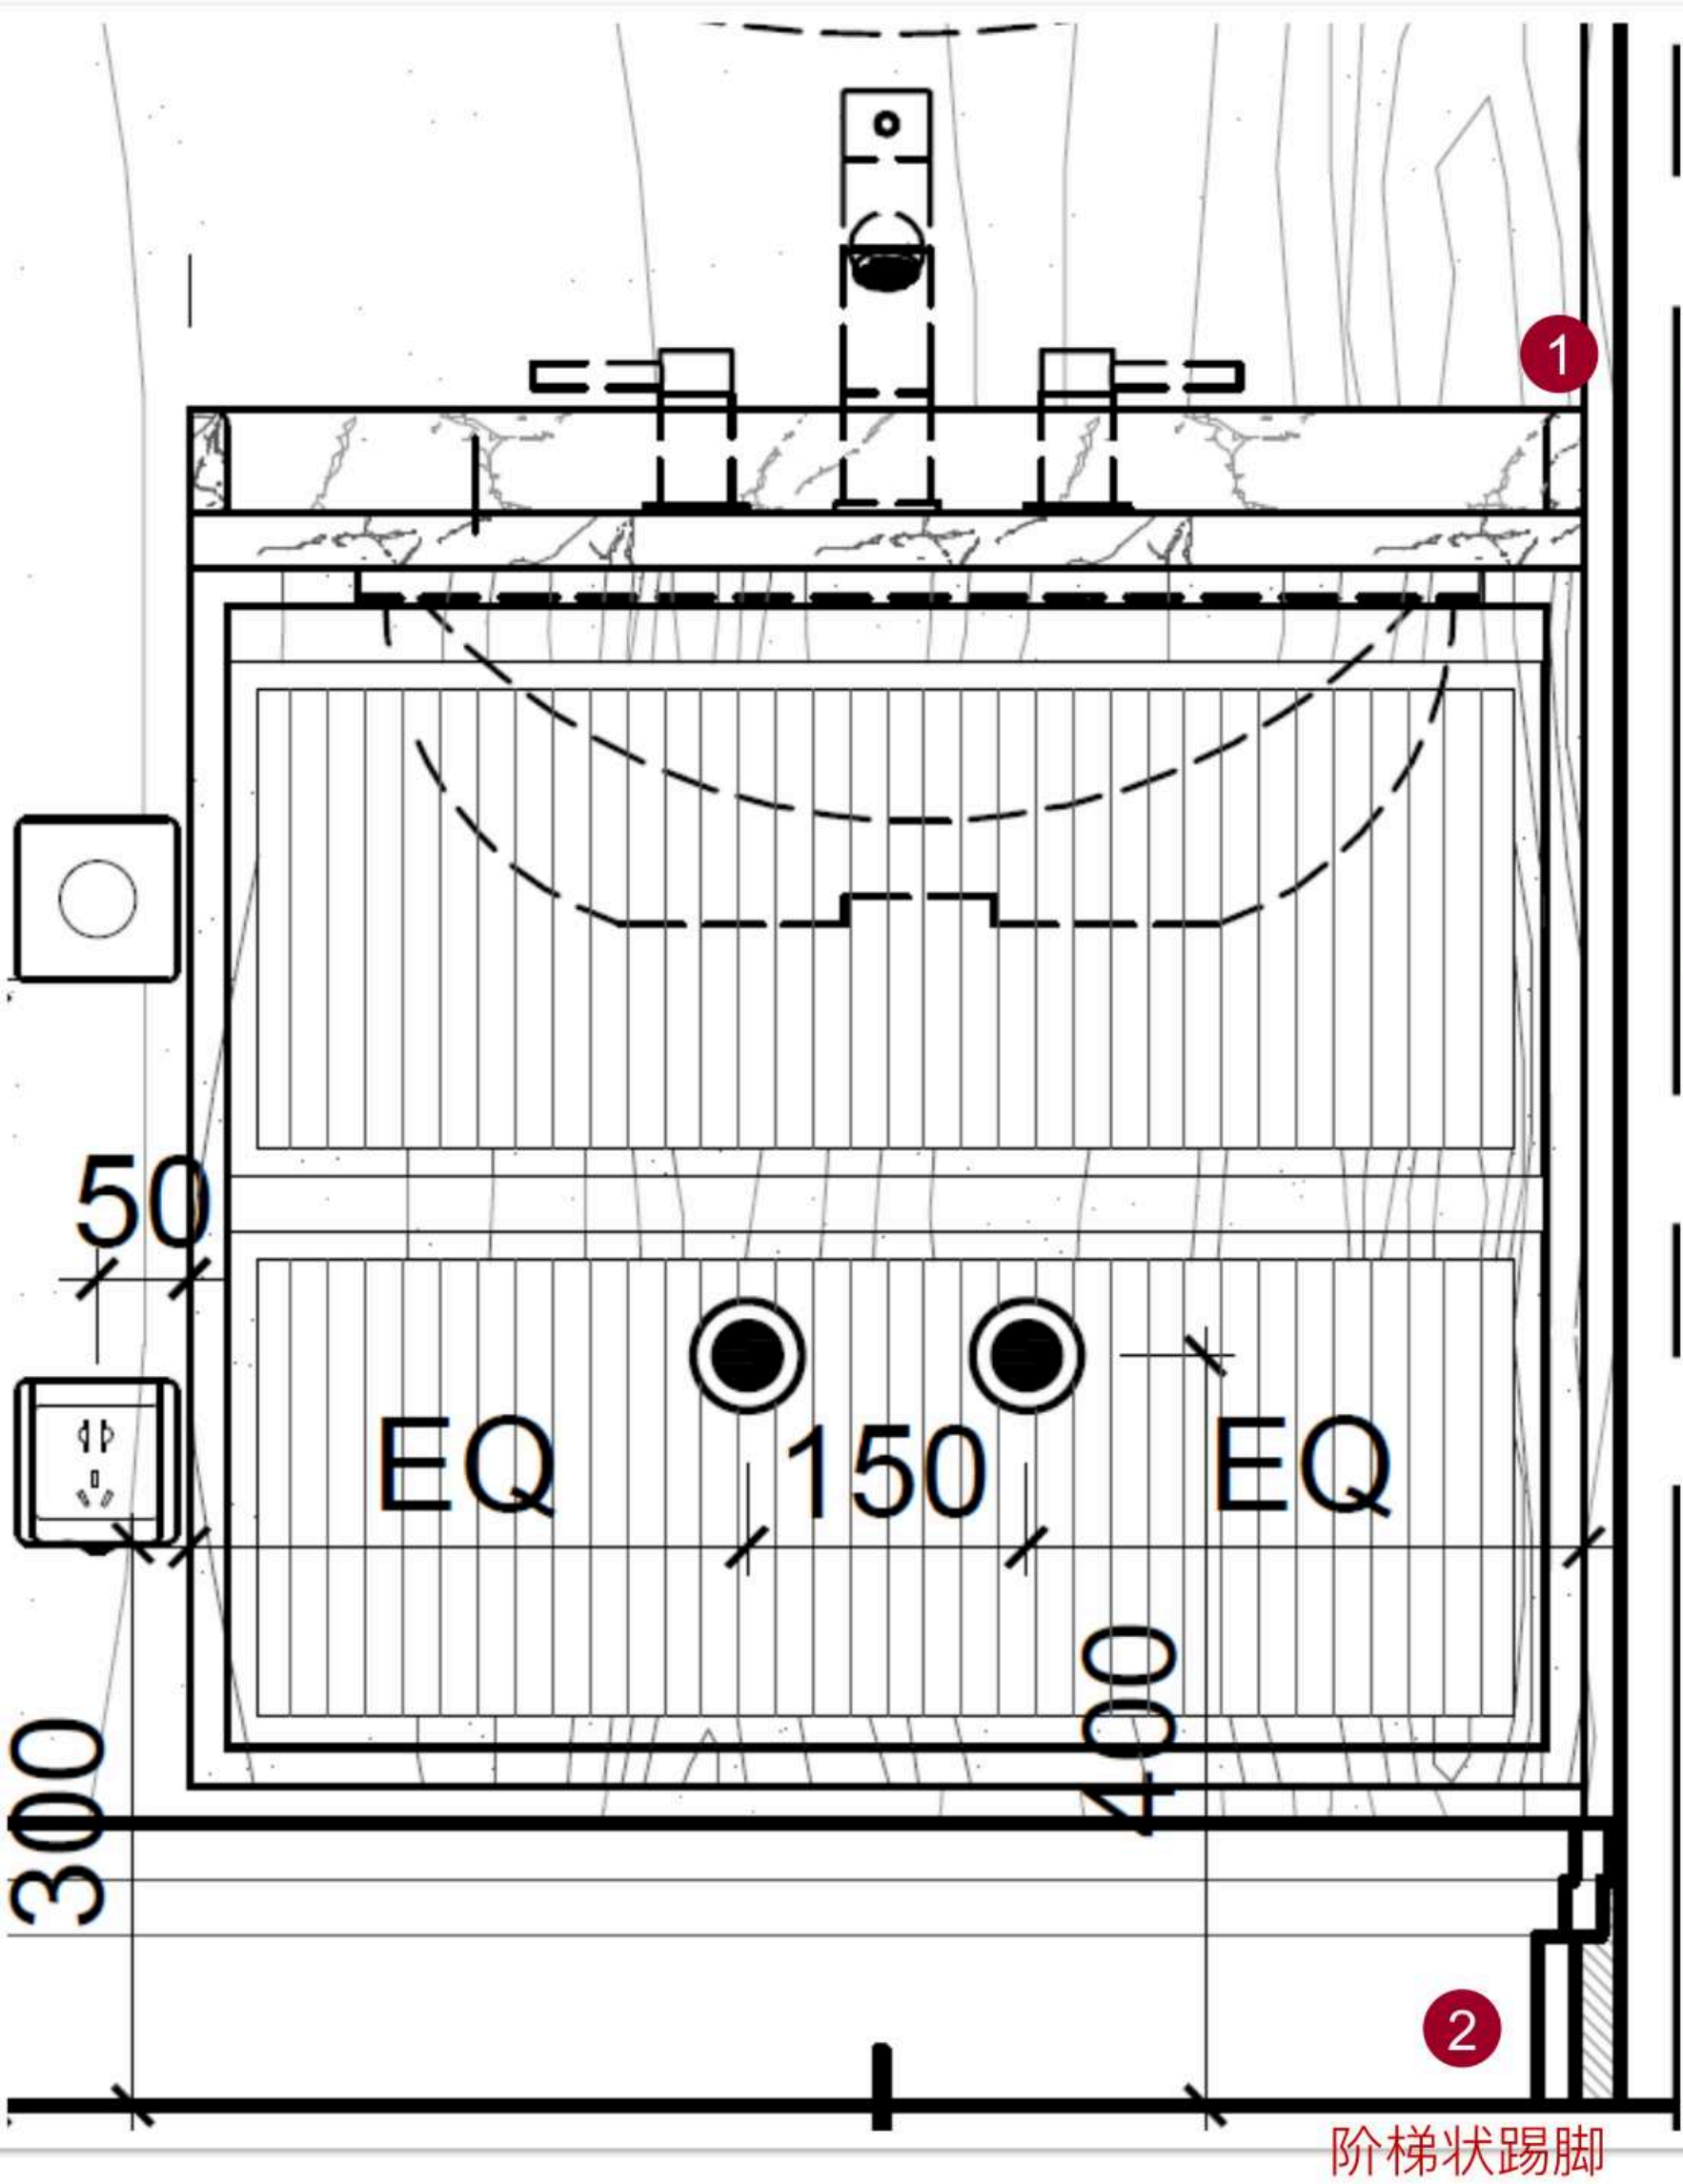

DETAIL THINKING 细节构想

Bathroom for boy
男孩卫



- 台盆柜细节分析
- 石材与木饰面交接处分析
- 石材踢脚线分析
- 分割原则

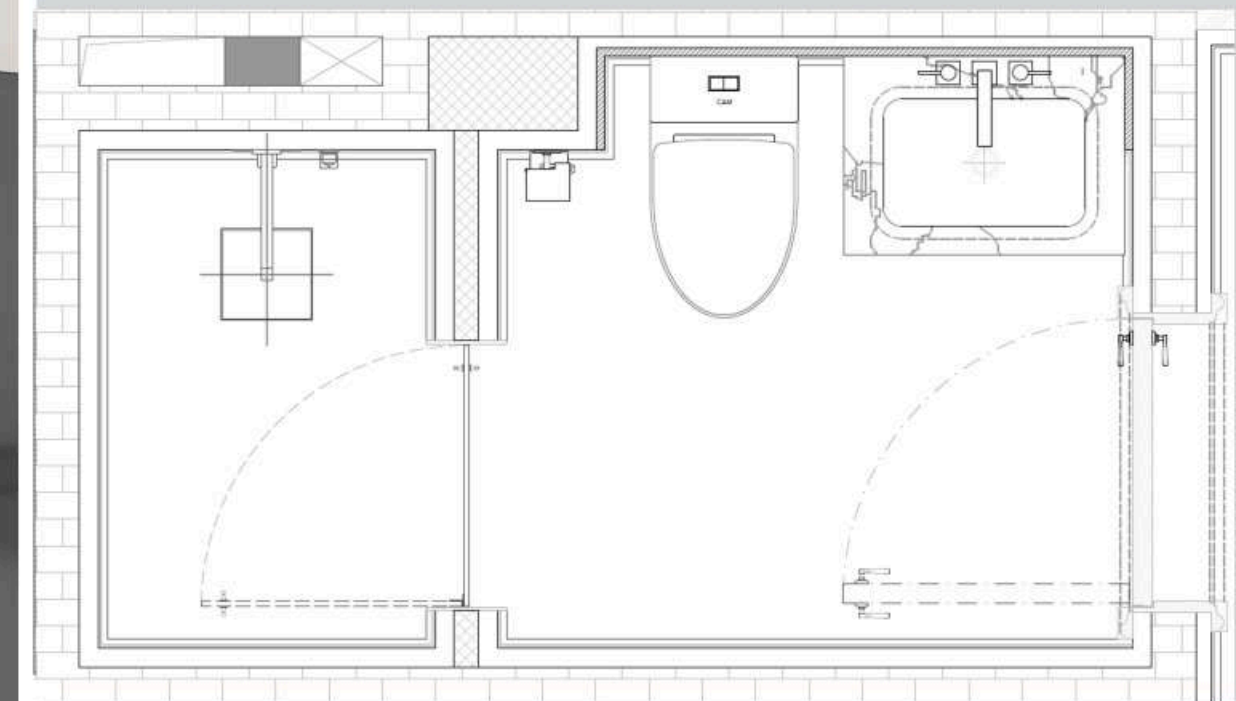

DETAIL THINKING 细节构想

Bathroom for boy
男孩卫

- 台盆柜细节分析
- 石材与木饰面交接处分析
- 石材踢脚线分析
- 分割原则

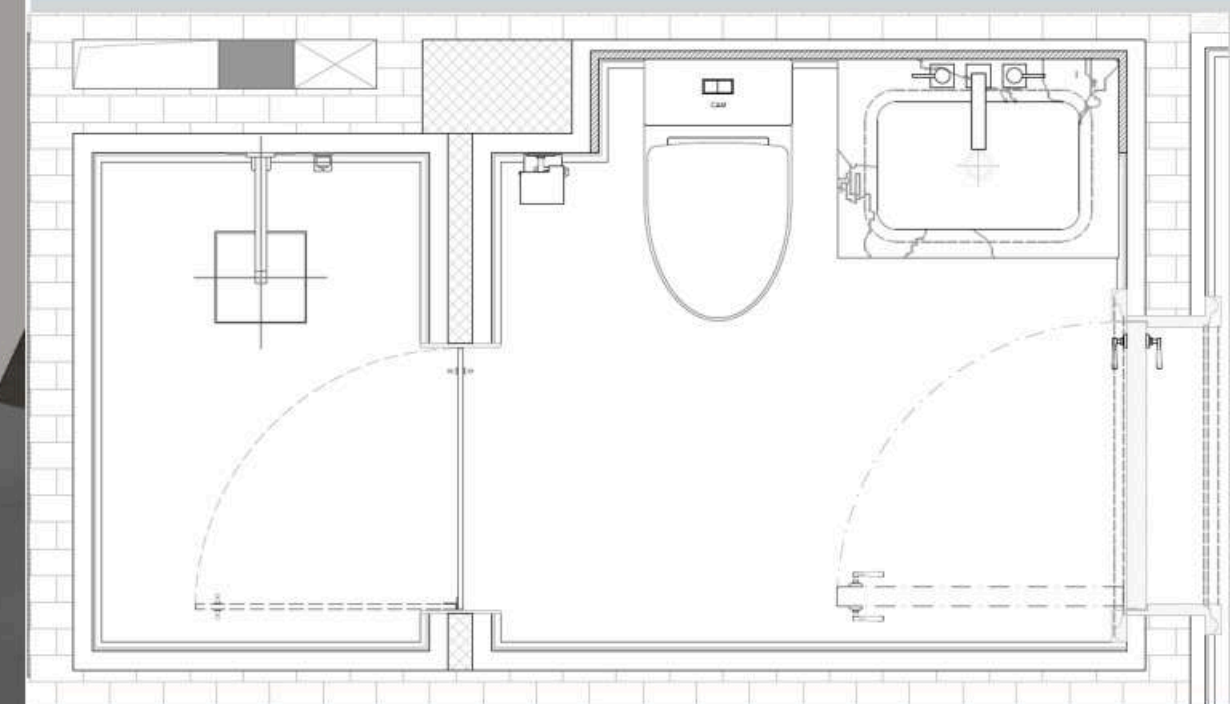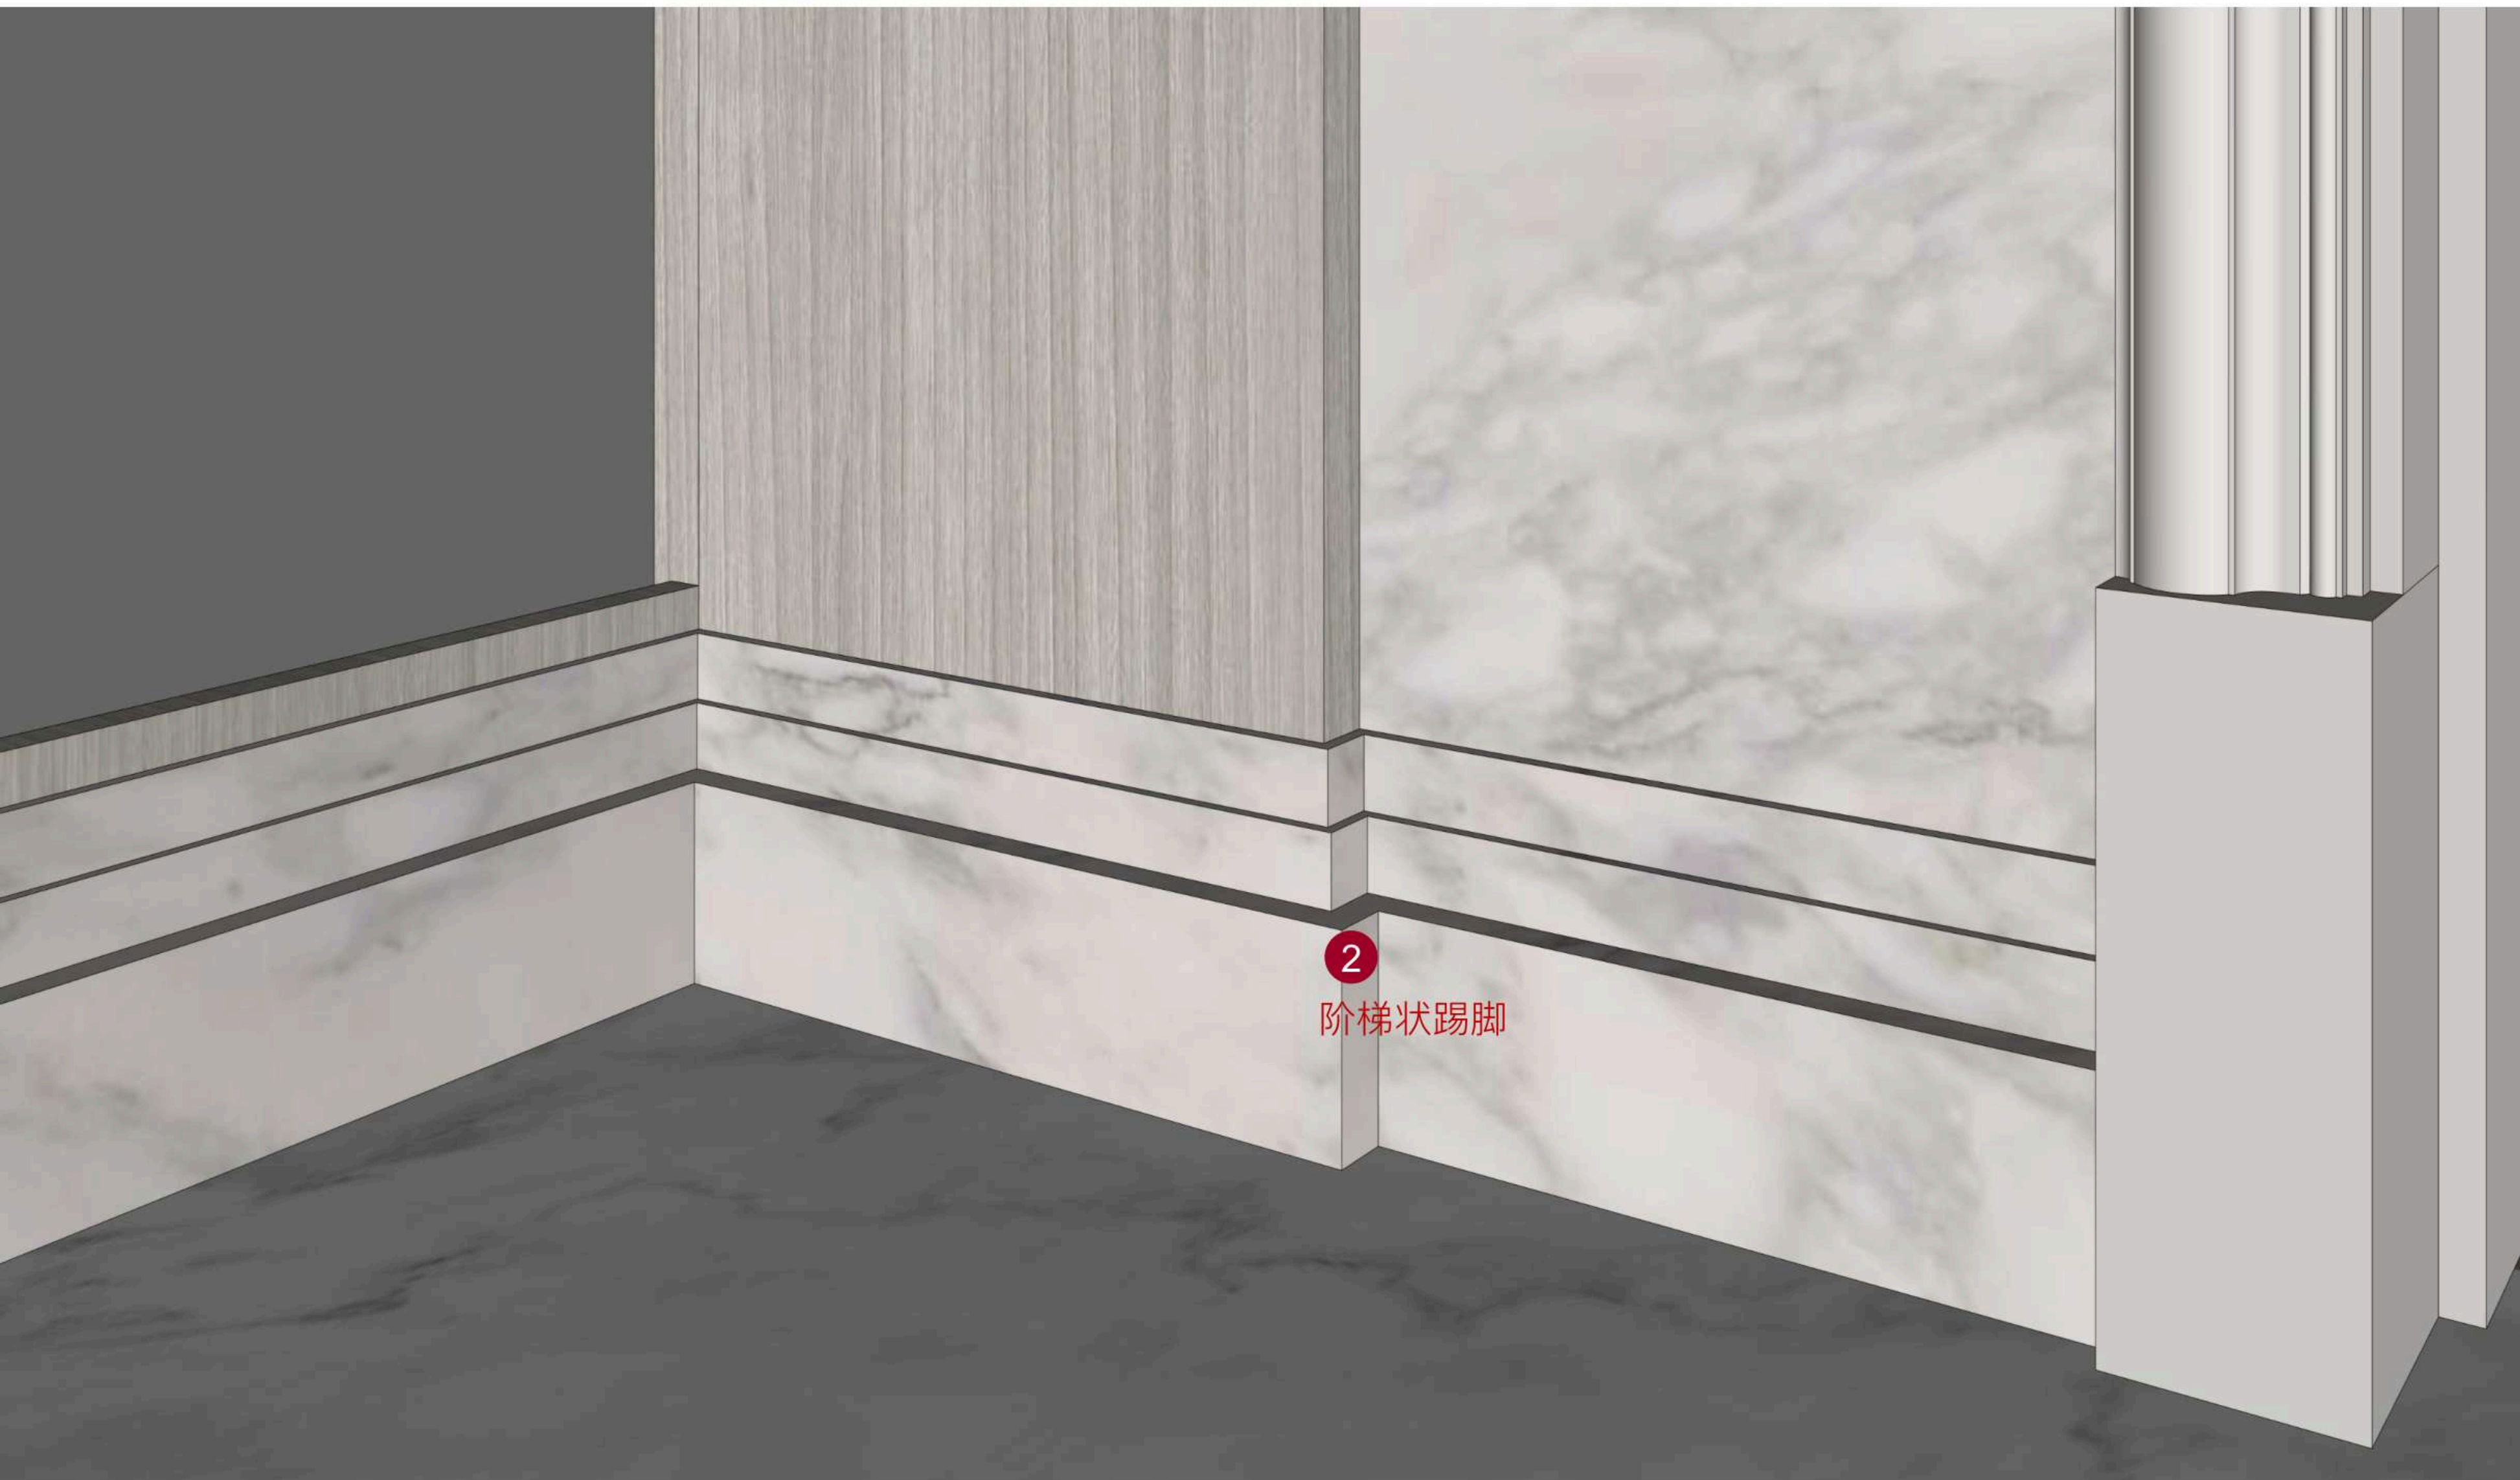

DETAIL THINKING 细节构想

Bathroom for boy
男孩卫

- 台盆柜细节分析
- 石材与木饰面交接处分析
- 石材踢脚线分析
- **分割原则**

